
جدول مساحات الموقع

البند	المقاس	المساحة (م²)
مساحة الأرض (شبه منحرف)	25.00 × 24.27/16.23 م	499.6
مسطح الأكواخ (2)	2 × 7.00 × 9.00 م	126.0
تراس الكوخ	2 × 7.00 × 2.40 م	33.6
مسبح	2 × 2.30 × 4.80 م	22.1
جلسة مدفونة	2 × 3.20 × 3.40 م	21.8
بلاط		19.4
موقف سيارة	2 × 3.00 × 5.50 م	33.0
ممر	2 × 1.00 × 11.17 م	22.3
أحواض زراعة	2 × 6.60 × 0.90 م	11.9
المسطحات الخضراء (حديقة)	الباقي	209.5

الموقع العام وتنسيق الحديقة (لاندسكيب)
الأرض 500 م² | الأبعاد بالسنتيمتر

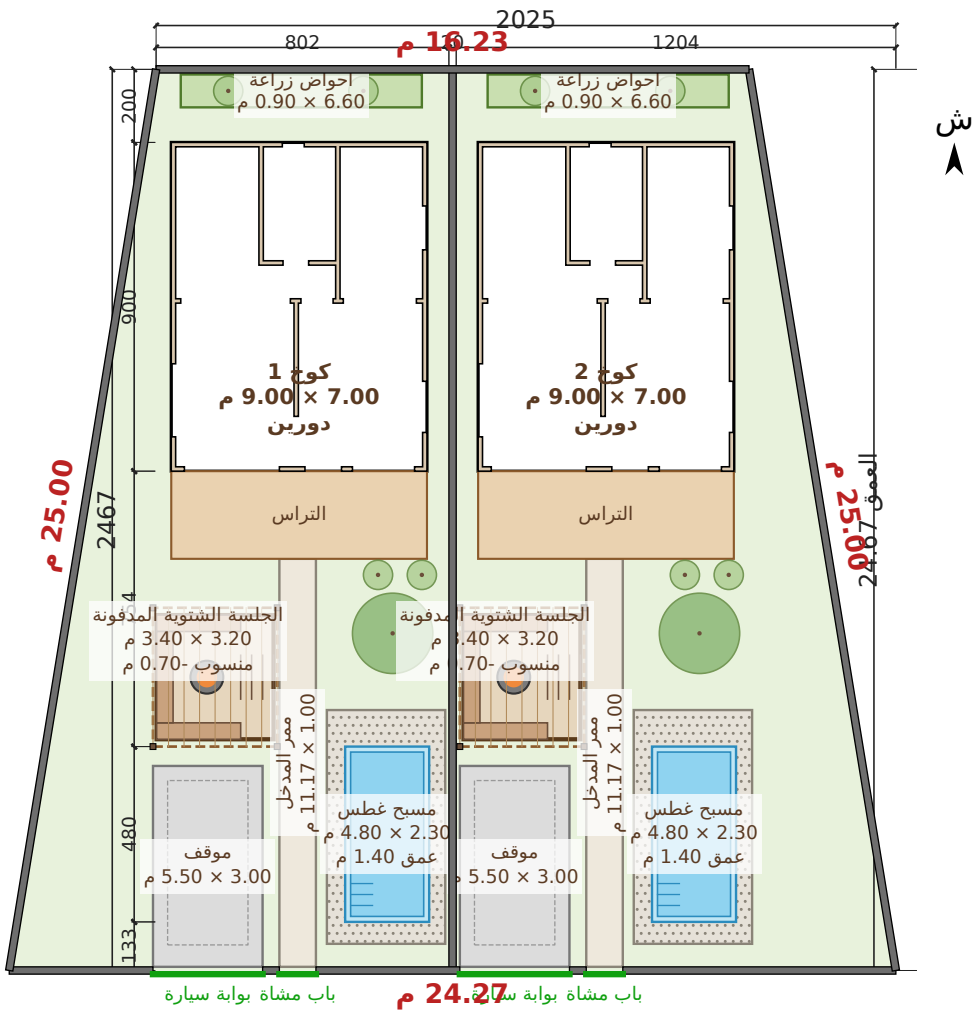


شارع عرض 15 م

- الأرض مقسومة بسور بالنص لوحدتين مستقلتين (≈ 250 م² لكل وحدة) — تأجير مستقل وخصوصية كاملة.
- الشاليه دورين ببصمة 7.00 × 9.00 م — الحوش الأمامي لكل وحدة صار 11.3 م للاندسكيب.
- كل وحدة: بوابة سيارة 3.00 م لموقف + باب مشاة بممر مستقيم لدرج التراس، ومسبح غطس 2.30 × 4.80 م ببلاط حوله.
- جلسة شتوية مدفونة 3.20 × 3.40 م بمنسوب -0.70 م تحت مستوى الأرض: جلسة U مبنية بمساند، درج نزول، ومشب نار بالنص، وفوقها برجولة خشب — محمية من الهوا وتطل على الحديقة.
- سور بلك 2.20 م بغطاء خشب على أضلاع الأرض (شبه منحرف) + السور الفاصل بين الوحدتين، وأحواض زراعة على السور الخلفي.

	المشروع / العميل	عنوان اللوحة	المقياس	التاريخ	رقم اللوحة
مصنع وتد الأخشاب Watad Wood Factory	شاليهين الهدا الاستثماري — دورين — غرفتين وصالة لكل شاليه — 7.00 × 9.00 × 2 دور عميل — الهدا (استثماري)	الموقع العام واللاندسكيب	1:200	2026-10-23	A-01 (1/12)

المسقط الأفقي مع الفرش — الدور الأرضي

الأبعاد بالسنتيمتر - الجدران: قوائم 7×5 + تلبيس 2.5 من الجهتين (12 سم) | منسوب الأرضية +0.00

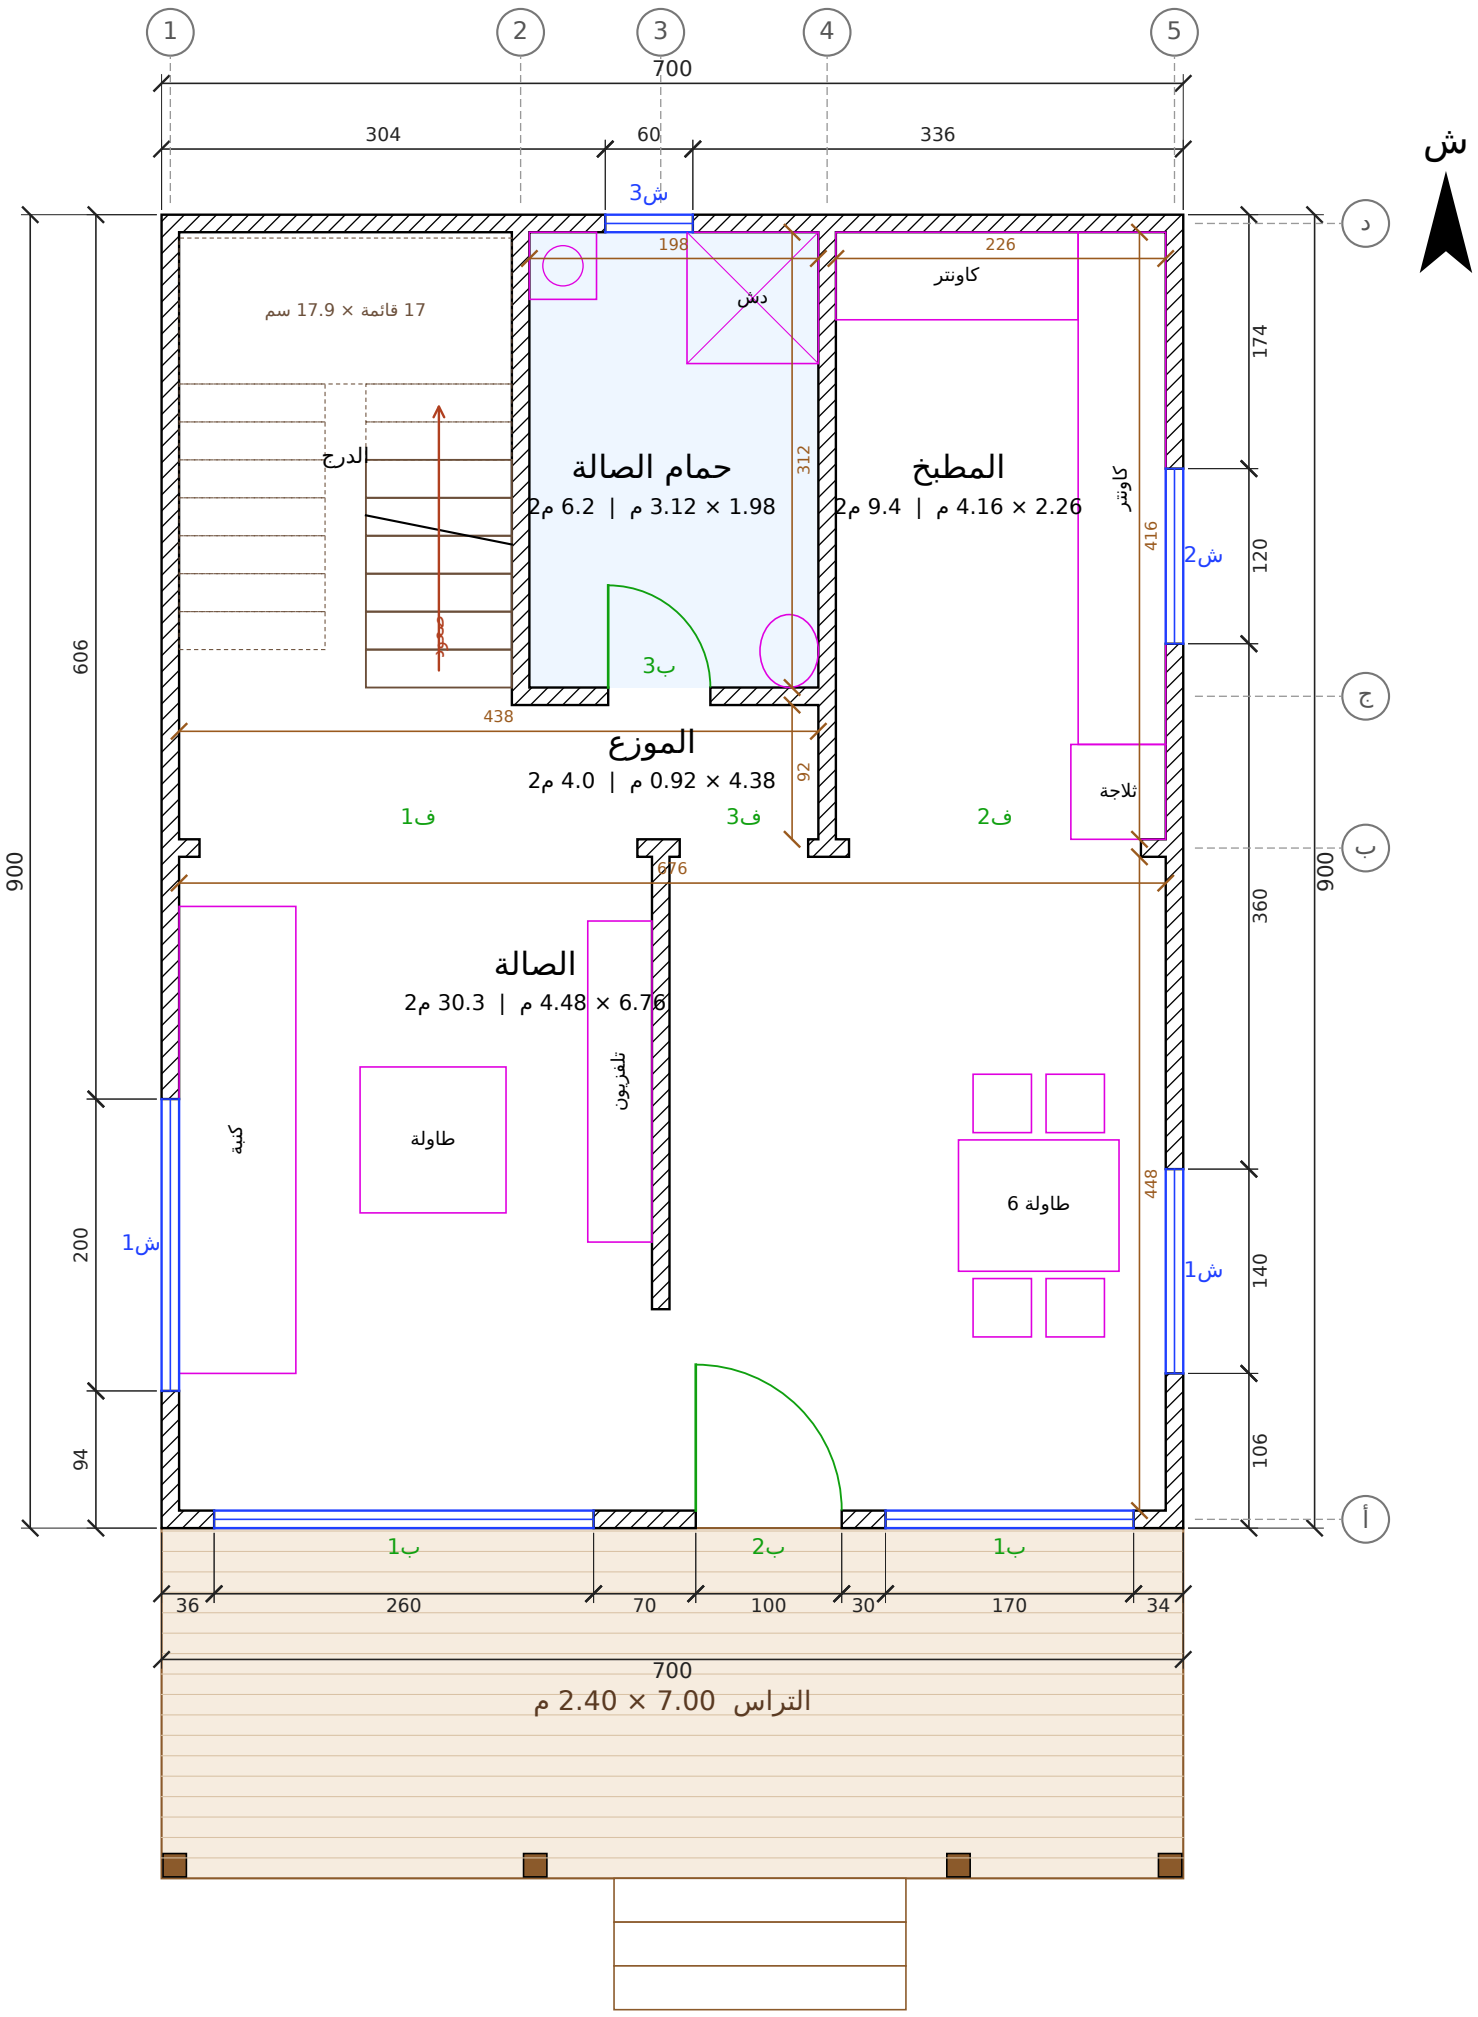


المشروع / العميل	عنوان اللوحة	المقياس	التاريخ	رقم اللوحة
شاليهين الهدا الاستثماري — دورين — غرفتين وصالة لكل شاليه — 7.00 × 9.00 × 2 دور عميل — الهدا (استثماري)	المسقط الأفقي — الدور الأرضي	1:50	2026-10-23	A-02 (2/12)

مصنع وتد الأخشاب
Watad Wood Factory


المسقط الأفقي مع الفرش — الدور الأول

الأبعاد بالسنتيمتر - الجدران: قوائم 7×5 + تلبيس 2.5 من الجهتين (12 سم) | منسوب الأرضية +3.05

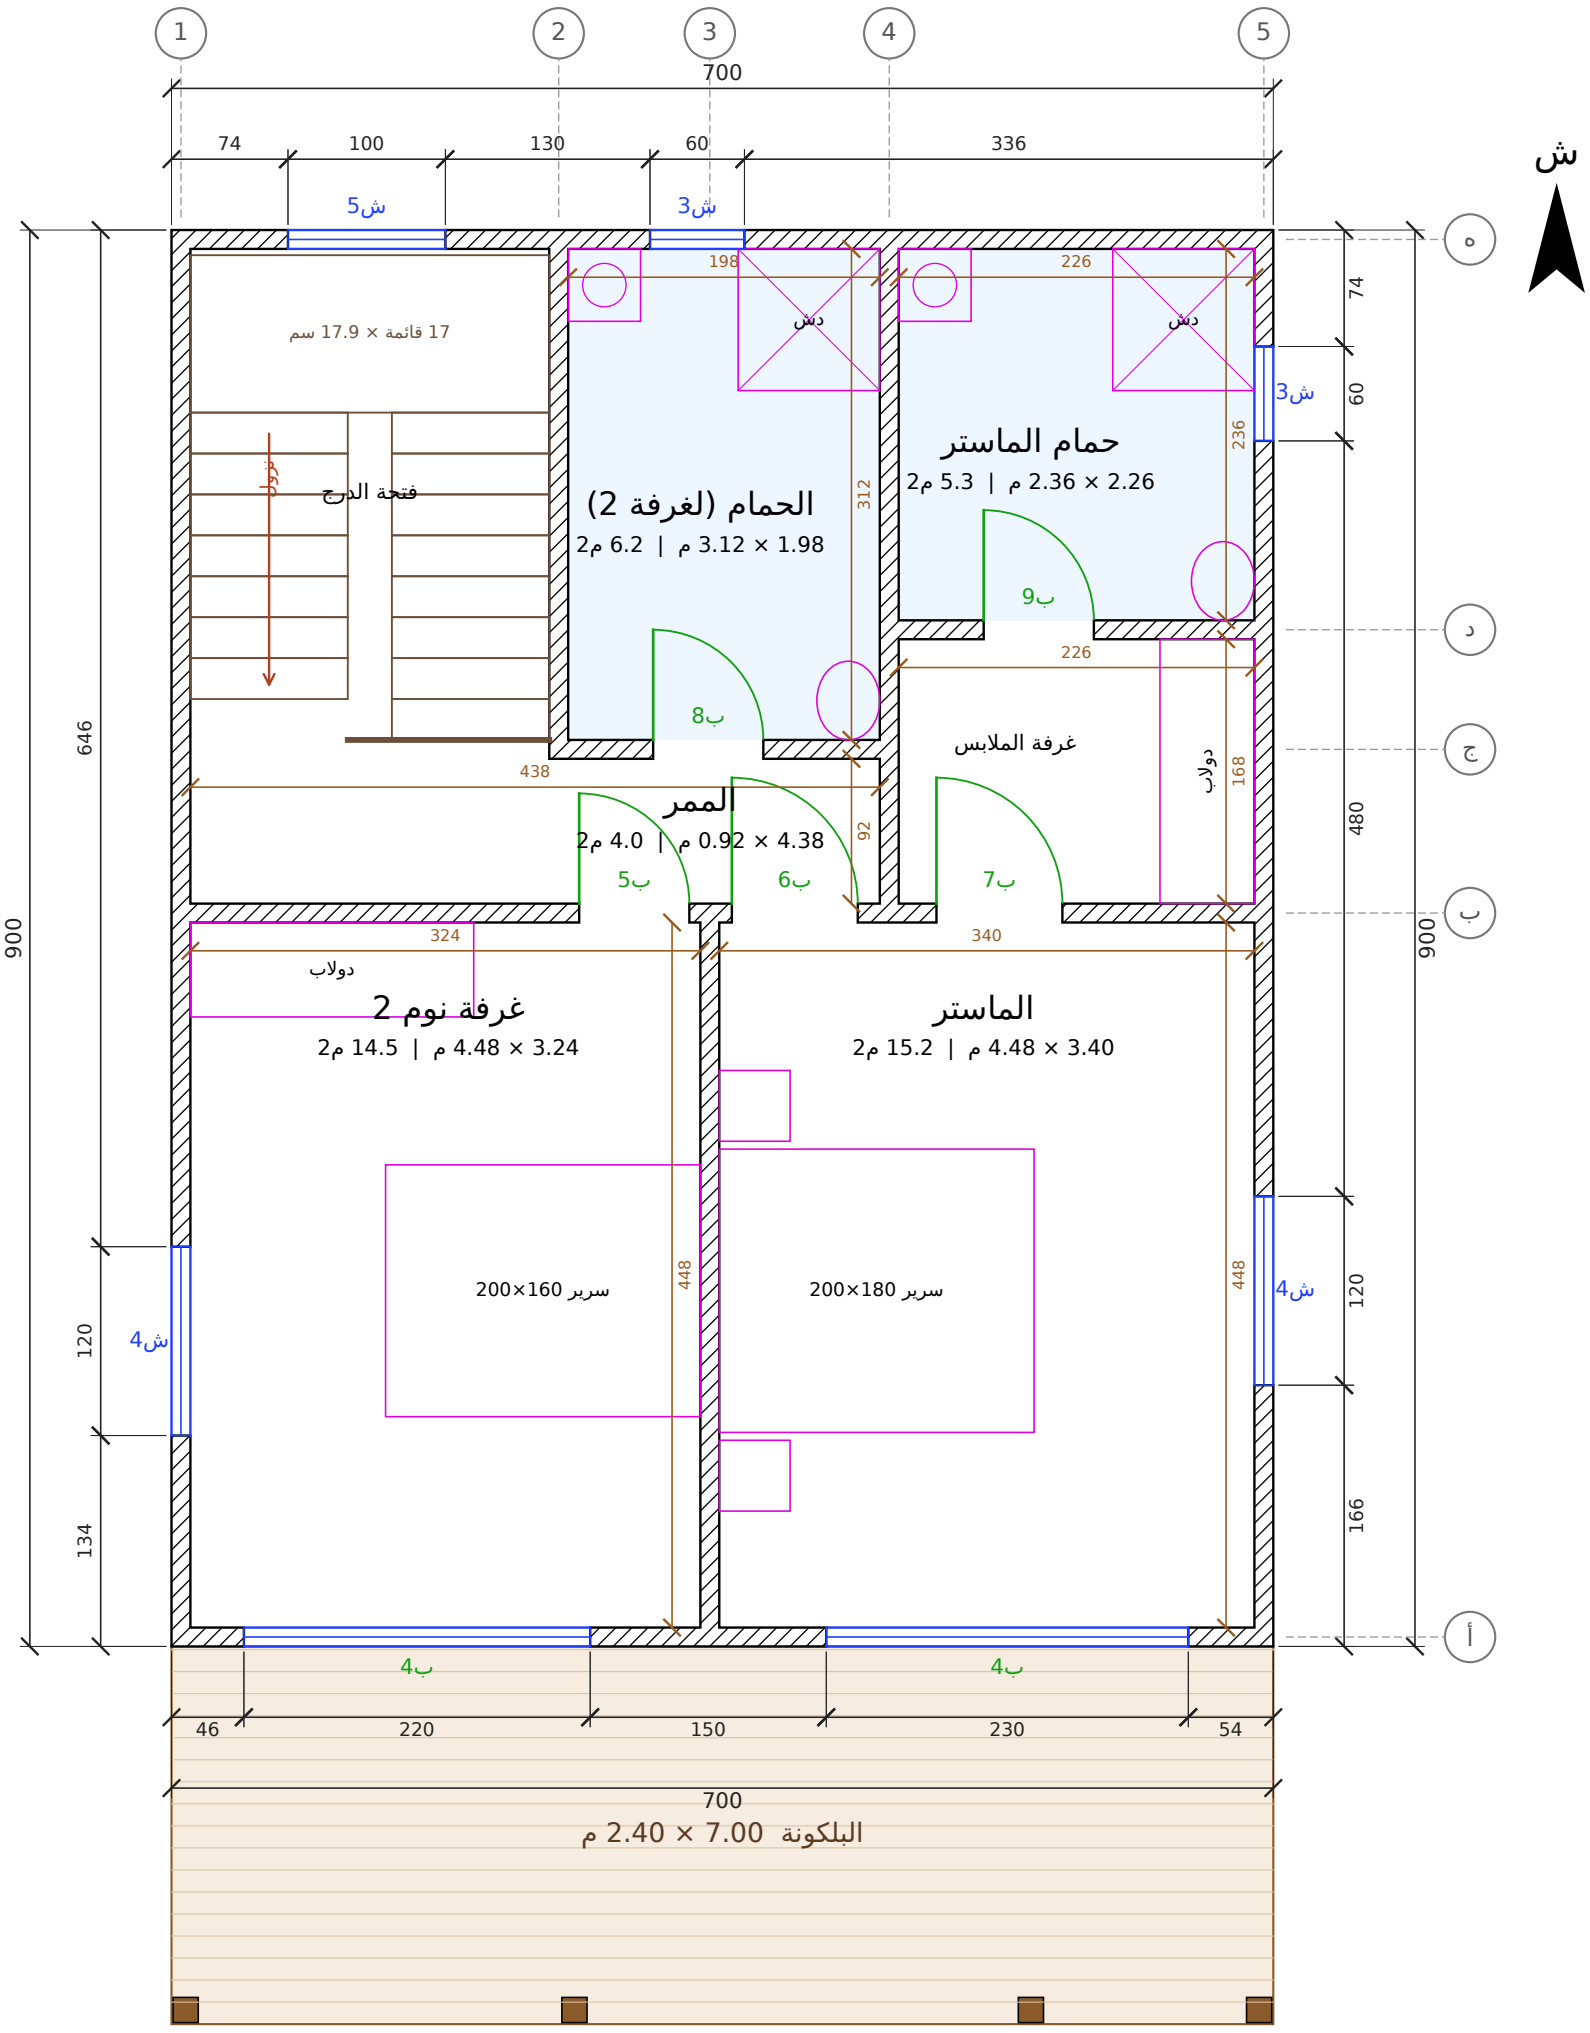


المشروع / العميل	عنوان اللوحة	المقياس	التاريخ	رقم اللوحة
شاليهين الهدا الاستثماري — دورين — غرفتين وصالة لكل شاليه — 7.00 × 9.00 × 2 دور عميل — الهدا (استثماري)	المسقط الأفقي — الدور الأول	1:50	2026-10-23	A-03 (3/12)

مصنع وتد الأخشاب
Watad Wood Factory

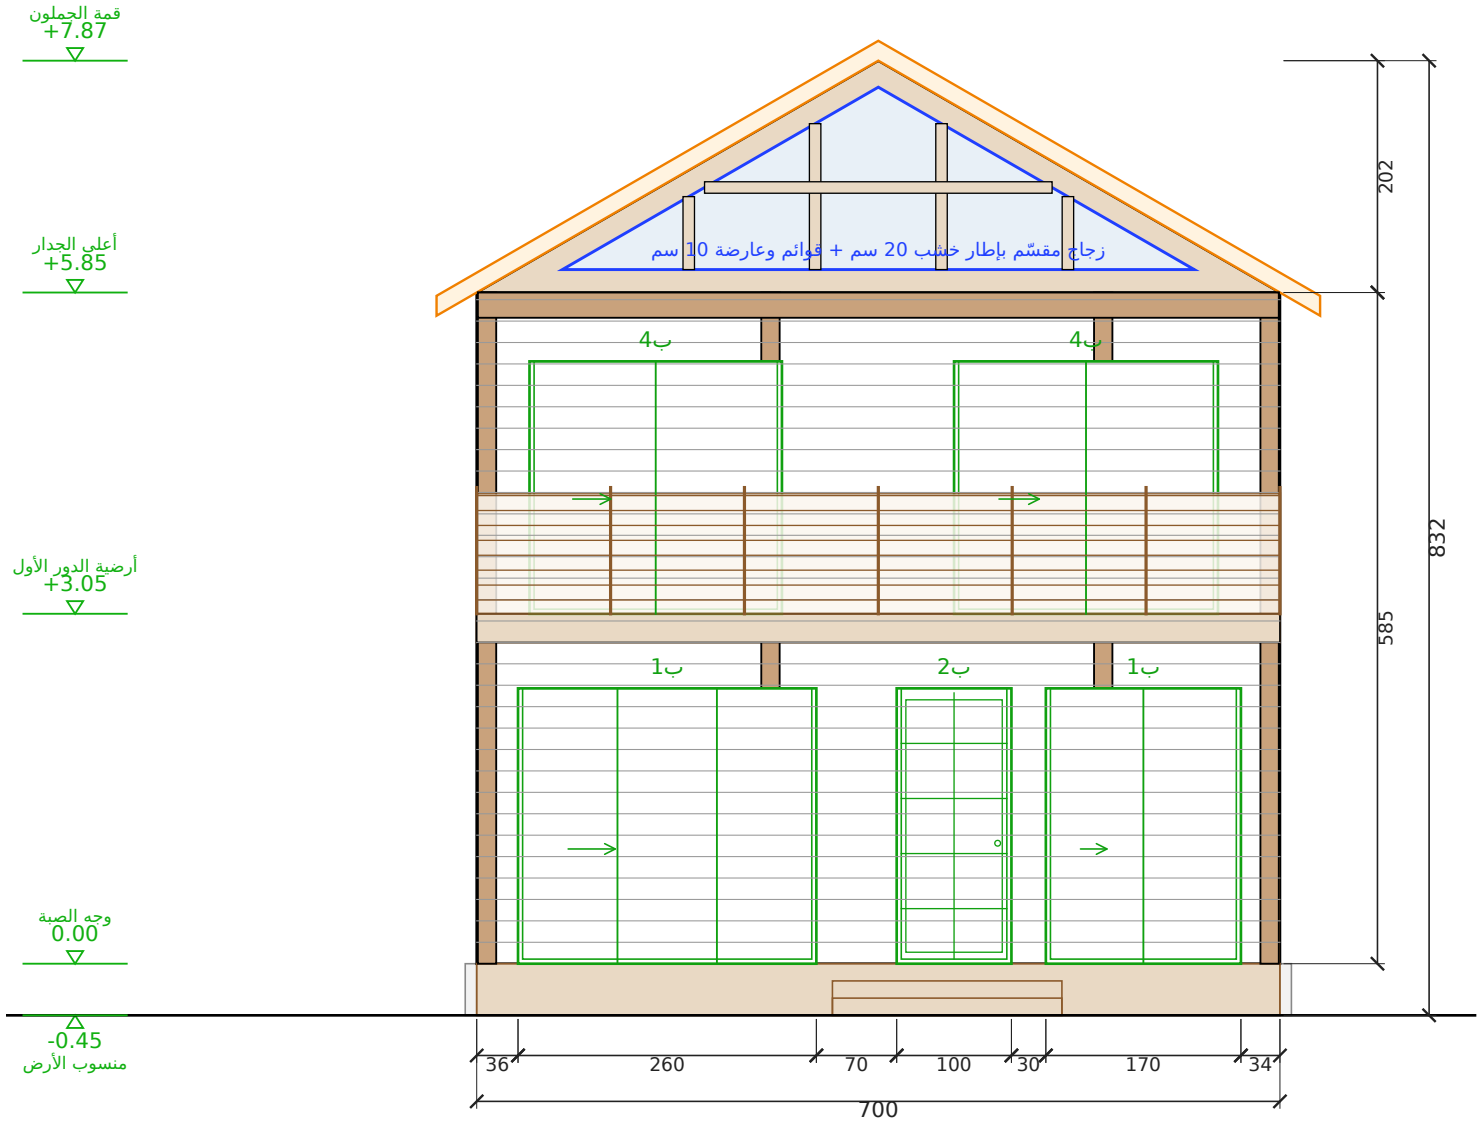

الواجهة الأمامية

مقياس 1:50 | الوحدة: سم

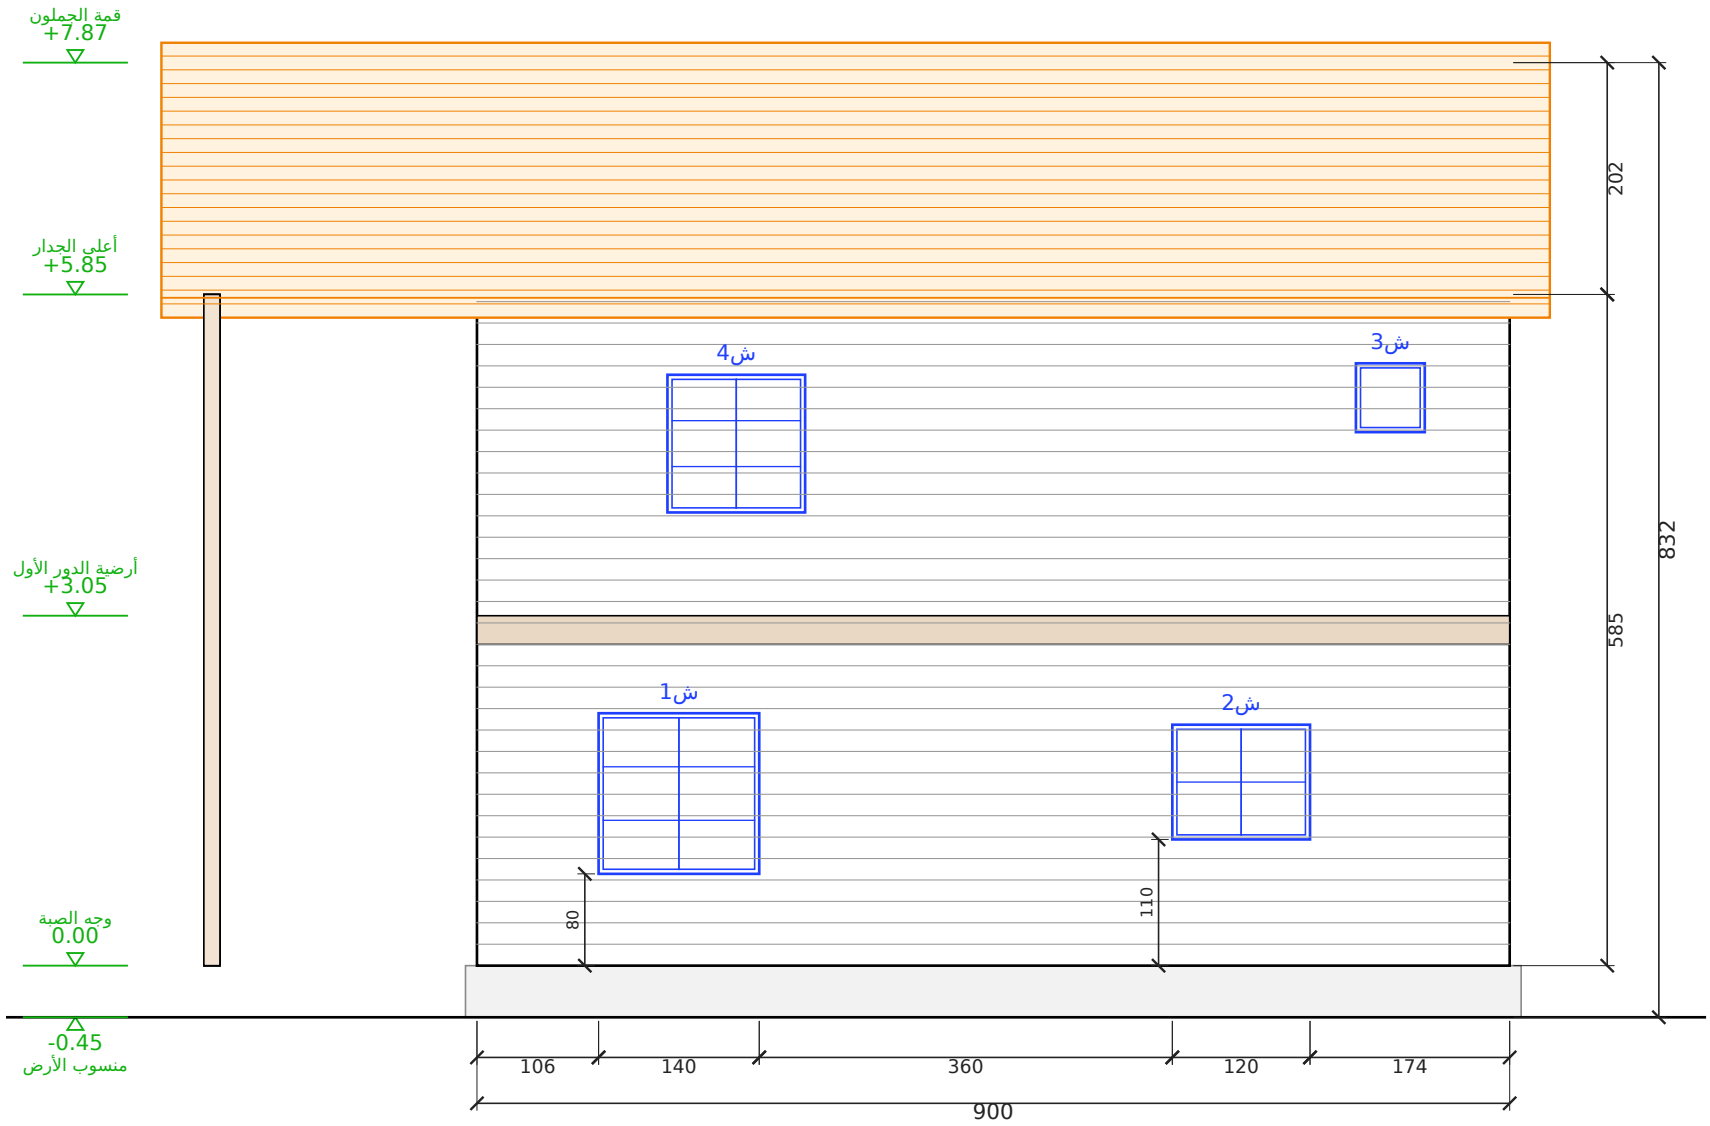


الواجهة الشرقية

مقياس 1:50 | الوحدة: سم


المشروع / العميل	عنوان اللوحة	المقياس	التاريخ	رقم اللوحة
شاليهين الهدا الاستثماري — دورين — غرفتين وصالة لكل شاليه — 7.00 × 9.00 × 2 دور عميل — الهدا (استثماري)	الواجهة الأمامية والواجهة الشرقية	1:50	2026-10-23	A-04 (4/12)

مصنع وتد الأخشاب
Watad Wood Factory

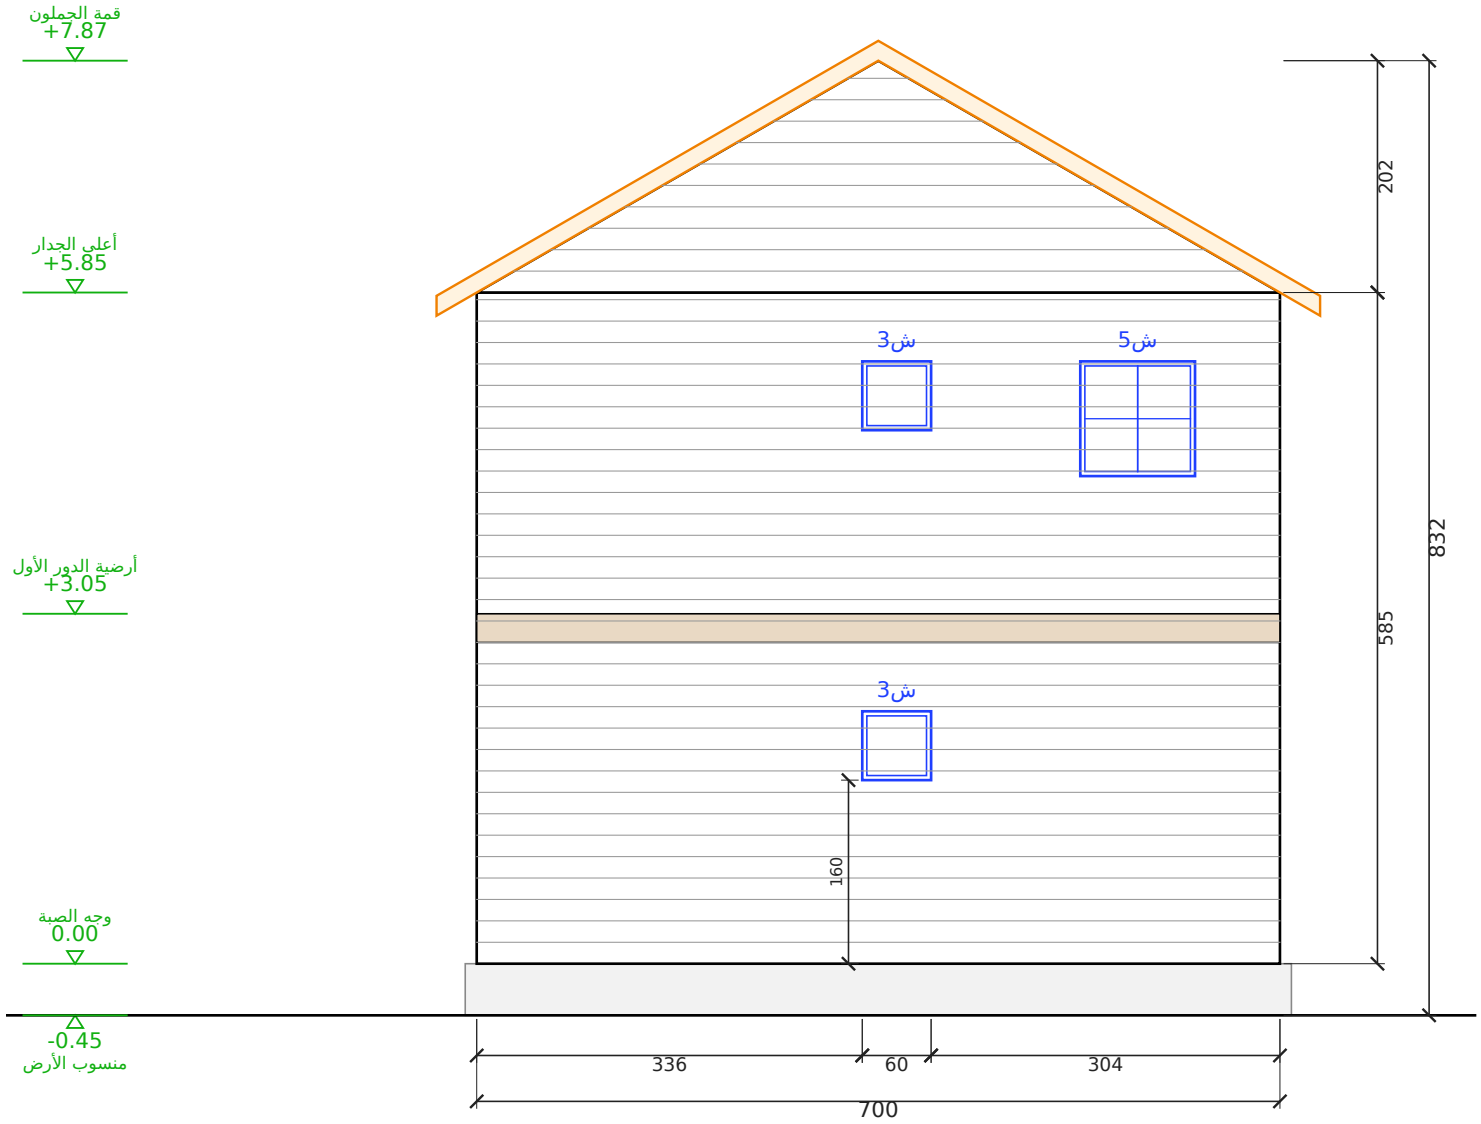

الواجهة الخلفية

مقياس 1:50 | الوحدة: سم

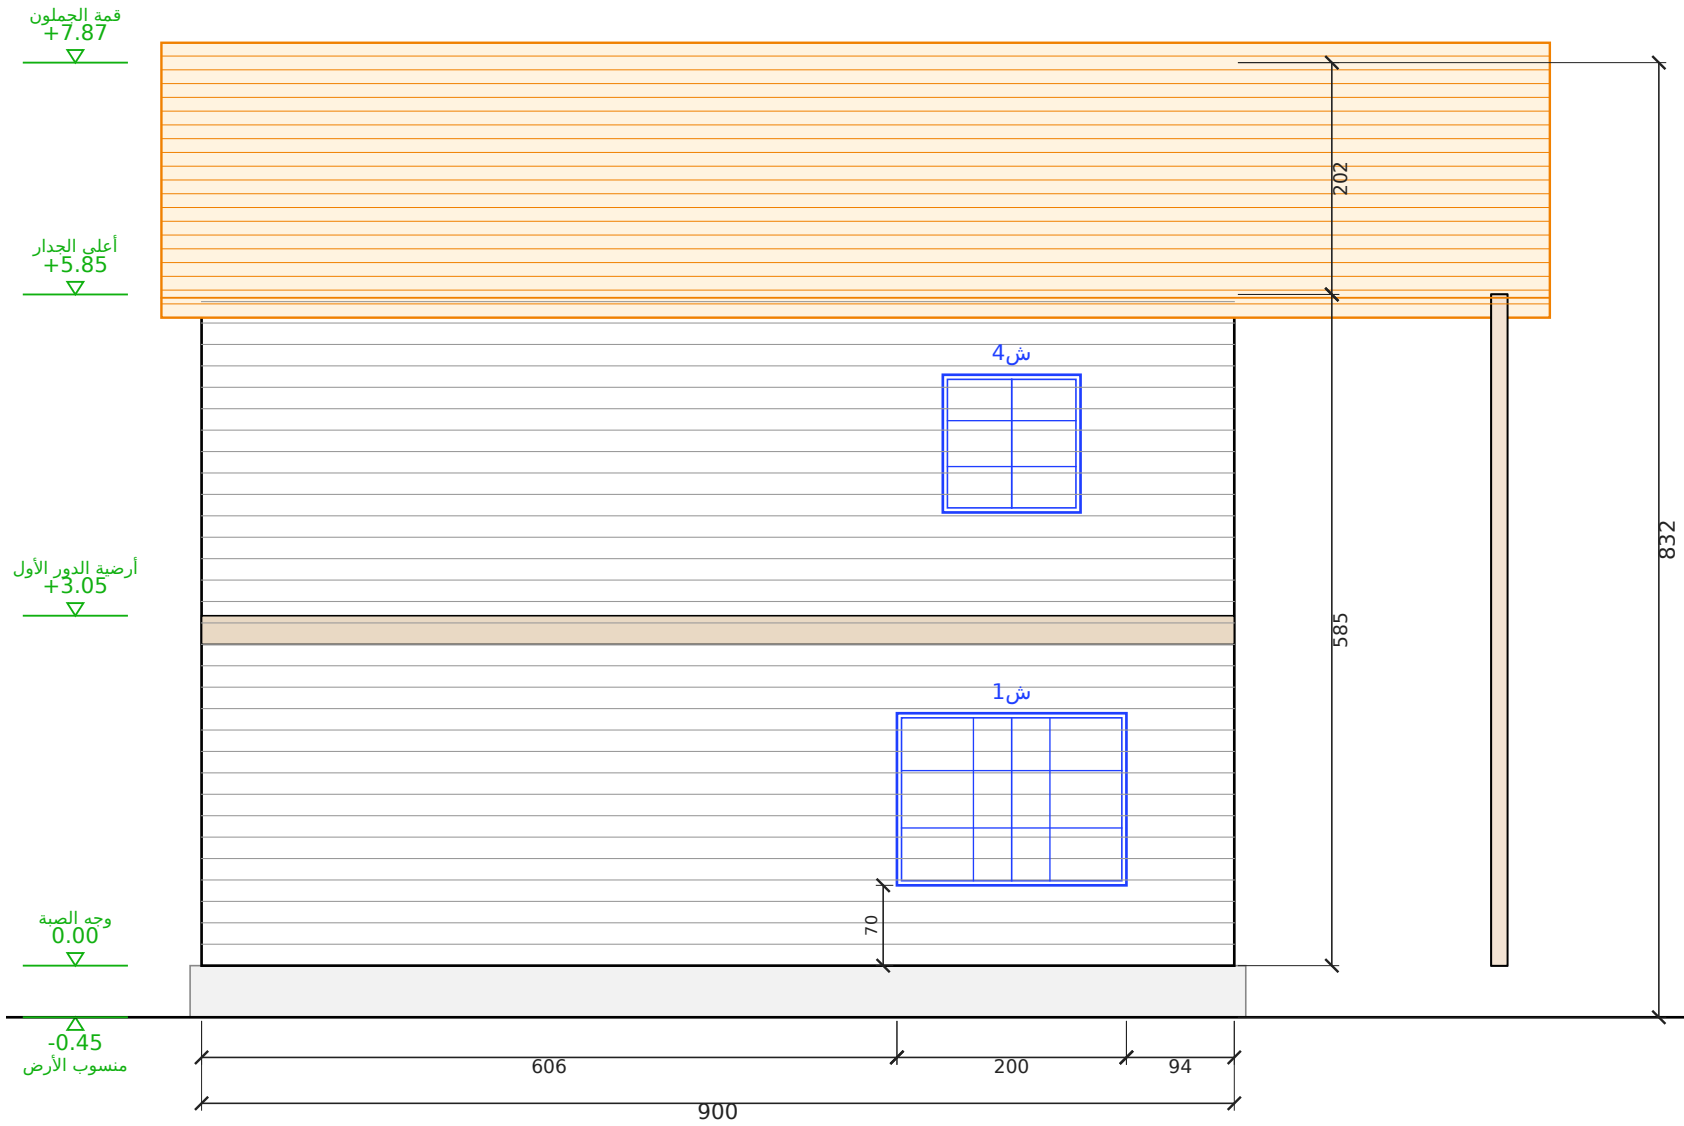


الواجهة الغربية

مقياس 1:50 | الوحدة: سم


المشروع / العميل	عنوان اللوحة	المقياس	التاريخ	رقم اللوحة
شاليهين الهدا الاستثماري — دورين — غرفتين وصالة لكل شاليه — 7.00 × 9.00 × 2 دور عميل — الهدا (استثماري)	الواجهة الخلفية والواجهة الغربية	1:50	2026-10-23	A-05 (5/12)

مصنع وتد الأخشاب
Watad Wood Factory


مسقط السقف (جملون)
رفرف 35 سم من كل جهة | مقياس 1:50

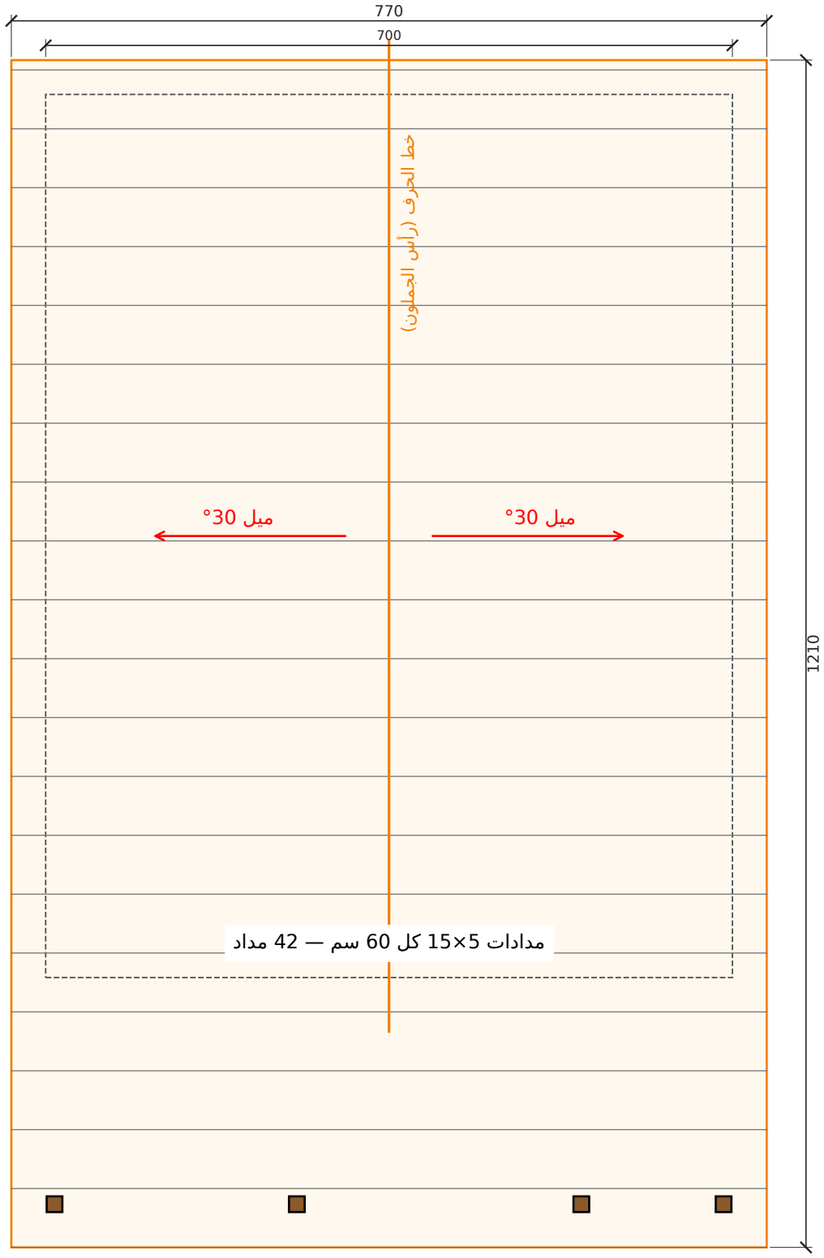

قطاع عرضي أ-أ
مقياس 1:50 | الوحدة: سم

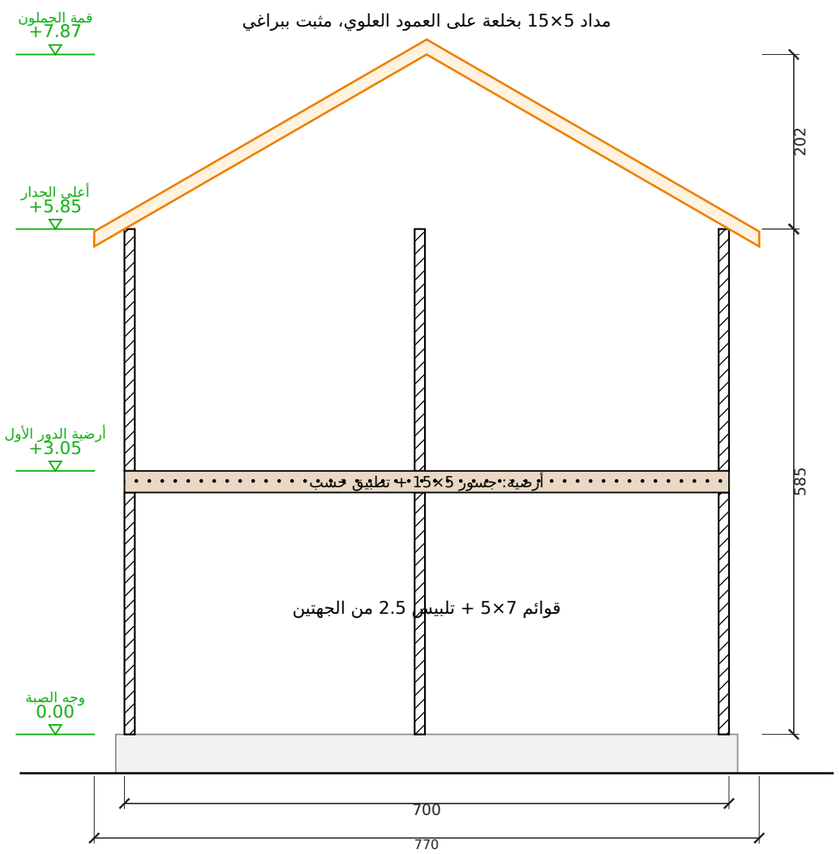

تفصيلة جلوس المداد على العلوي (1:5)

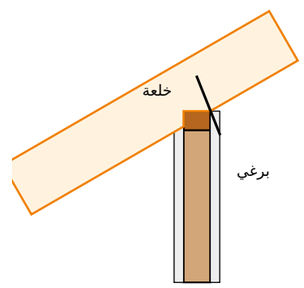

علوي 7×5 على قائم 7×5

مصنع وتد الأخشاب Watad Wood Factory	المشروع / العميل شاليهين الهدا الاستثماري — دورين — غرفتين وصالة لكل شاليه — 9.00 × 7.00 × 2 دور عميل — الهدا (استثماري)	عنوان اللوحة مسقط السقف والقطاع	المقياس 1:50	التاريخ 2026-10-23	رقم اللوحة A-06 (6/12)

جدول مقاسات الأبواب والشبابيك
مقاس الفتحة الصافي في الجدار - الوحدة: سم

الرمز	النوع	العرض (سم)	الارتفاع (سم)	ارتفاع الجلسة (سم)	العدد	الموقع
ب1	باب مزدوج	260	240	-	1	الأمامية
ب1	باب مزدوج	170	240	-	1	الأمامية
ب2	باب	100	240	-	1	الأمامية
ب3	باب	70	210	-	1	حمام الصالة
ب4	باب مزدوج	220	220	-	1	الأمامية (على البلكونة)
ب4	باب مزدوج	230	220	-	1	الأمامية (على البلكونة)
ب5	باب	70	210	-	1	غرفة نوم 2
ب6	باب	80	210	-	1	الماستر
ب7	باب	80	210	-	1	غرفة الملابس
ب8	باب	70	210	-	1	الحمام
ب9	باب	70	210	-	1	حمام الماستر
ف1	باب	300	220	-	1	فتحة الجلسة — الموزع والدرج
ف2	باب	200	220	-	1	فتحة المطبخ
ف3	باب	88	220	-	1	فتحة المدخل — الموزع
ش1	شباك	140	140	80	1	الشرقية
ش1	شباك	200	150	70	1	الغربية
ش2	شباك	120	100	110	1	الشرقية
ش3	شباك	60	60	160	3	الخلفية 2 - الشرقية
ش4	شباك	120	120	90	2	الشرقية - الغربية
ش5	شباك	100	100	120	1	الخلفية

الإجمالي: أبواب 14 - شبابيك 9

جدول المساحات وبيانات المشروع والتسعير

بيانات المشروع

البند	البيان
المشروع	شاليهين الهدا الاستثماري — دورين — غرفتين وصالة لكل شاليه — 7.00 × 9.00 × 2 دور
العميل	عميل — الهدا (استثماري)
الموقع	الهدا — الطائف
الاستخدام	شاليهين استثماري (تأجير)
التاريخ	2026-10-23
نظام البناء	هيكل خشب 7×5 + تلبيس 2.5 سم من الجهتين
السقف	جملون 30° — قرميد معدني

جدول المساحات

م	الفراغ	الأبعاد (م)	المساحة (م2)
1	أرضي — الصالة	6.76 × 4.48	30.28
2	أرضي — الموزع	4.38 × 0.92	4.03
3	أرضي — الدرج	2.28 × 3.00	6.84
4	أرضي — حمام الصالة	1.98 × 3.12	6.18
5	أرضي — المطبخ	2.26 × 4.16	9.40
6	أول — غرفة نوم 2	3.24 × 4.48	14.52
7	أول — الماستر	3.40 × 4.48	15.23
8	أول — الممر	4.38 × 0.92	4.03
9	أول — الحمام (لغرفة 2)	1.98 × 3.12	6.18
10	أول — غرفة الملابس	2.26 × 1.68	3.80
11	أول — حمام الماستر	2.26 × 2.36	5.33
	المساحة الصافية الداخلية		105.82
	التراس	**7.00 × 2.40**	**16.80**
	البلكونة	**7.00 × 2.40**	**16.80**
	المساحة الإجمالية المبنية	**7.00 × 9.00 × 2 دور**	**126.00**
	المساحة الكلية (المبنية + التراس والبلكونة)		**159.60**

التسعير المفصّل

البند	المبلغ (ريال)
الكوخ المبني 126.00 م² × 1,096	138,096
تراس الأرضي + بلكونة الأول للشاليه الأول (7.00 × 2.40 × 2) — 33.60 م² × 1,096	36,826
الشاليه الثاني (مطابق — 126 م² + تراس وبلكونة 33.6 م²) — 159.60 م² × 1,096	174,922
الإجمالي (ريال)	**349,843**

ملاحظات:


- السعر للشاليهين (الدورين) والتراسات والبلكونات حسب المخطط المعتمد — التراس يُسعّر بنفس سعر متر الكوخ.
- أعمال الموقع (السور والبوابات والمسابح والجلسات الشتوية والبلاط والزراعة) عن طريق المقاول وتُسعّر منفصلة.
- الصبة والتمديدات الخارجية على العميل ما لم يُذكر غير ذلك.

لقطات المنظور الخارجي


المنظور الأمامي




منظور أمامي من اليسار

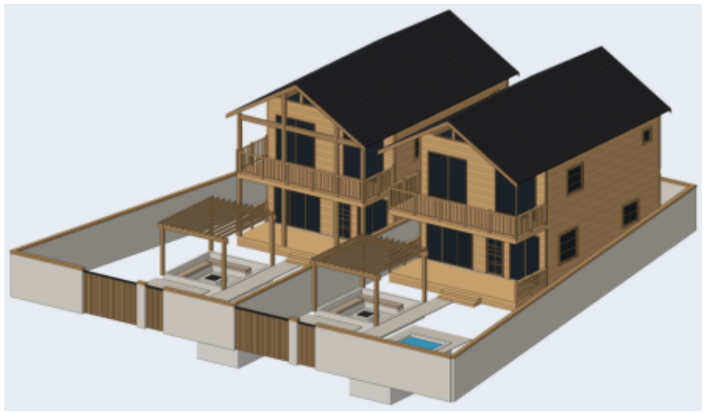


منظور أمامي من اليمين

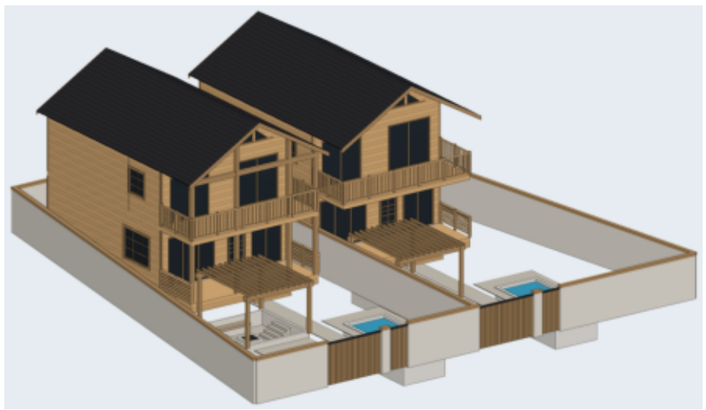


المنظور الخلفي

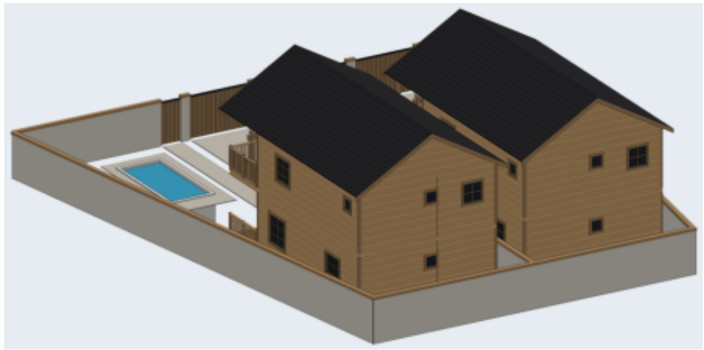

منظور خلفي من اليمين

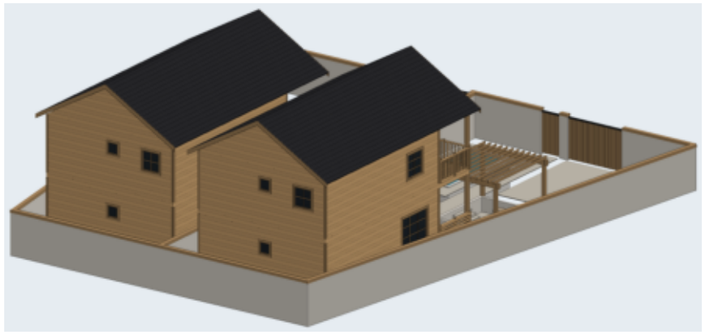


منظر علوي

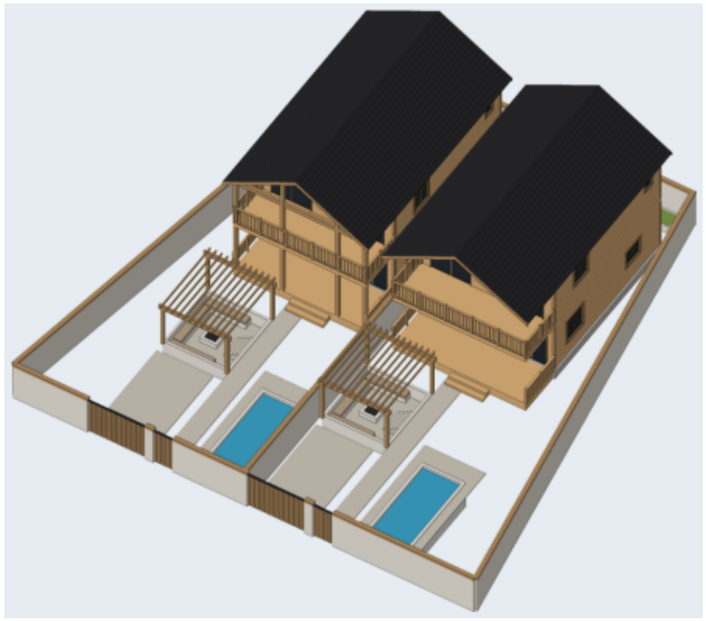

مصنع وتد الأخشاب Watad Wood Factory	المشروع / العميل **شاليهين الهدا الاستثماري — دورين — غرفتين وصالة لكل شاليه — 9.00 × 7.00 × 2 دور** **عميل — الهدا (استثماري)**	عنوان اللوحة **لقطات المنظور**	المقياس **—**	التاريخ **2026-10-23**	رقم اللوحة **A-09 (9/12)**

المقطع العلوي بالفرش — الدور الأرضي


مقطع أفقي على ارتفاع 1.90 م — توزيع الفرش ومسار الحركة

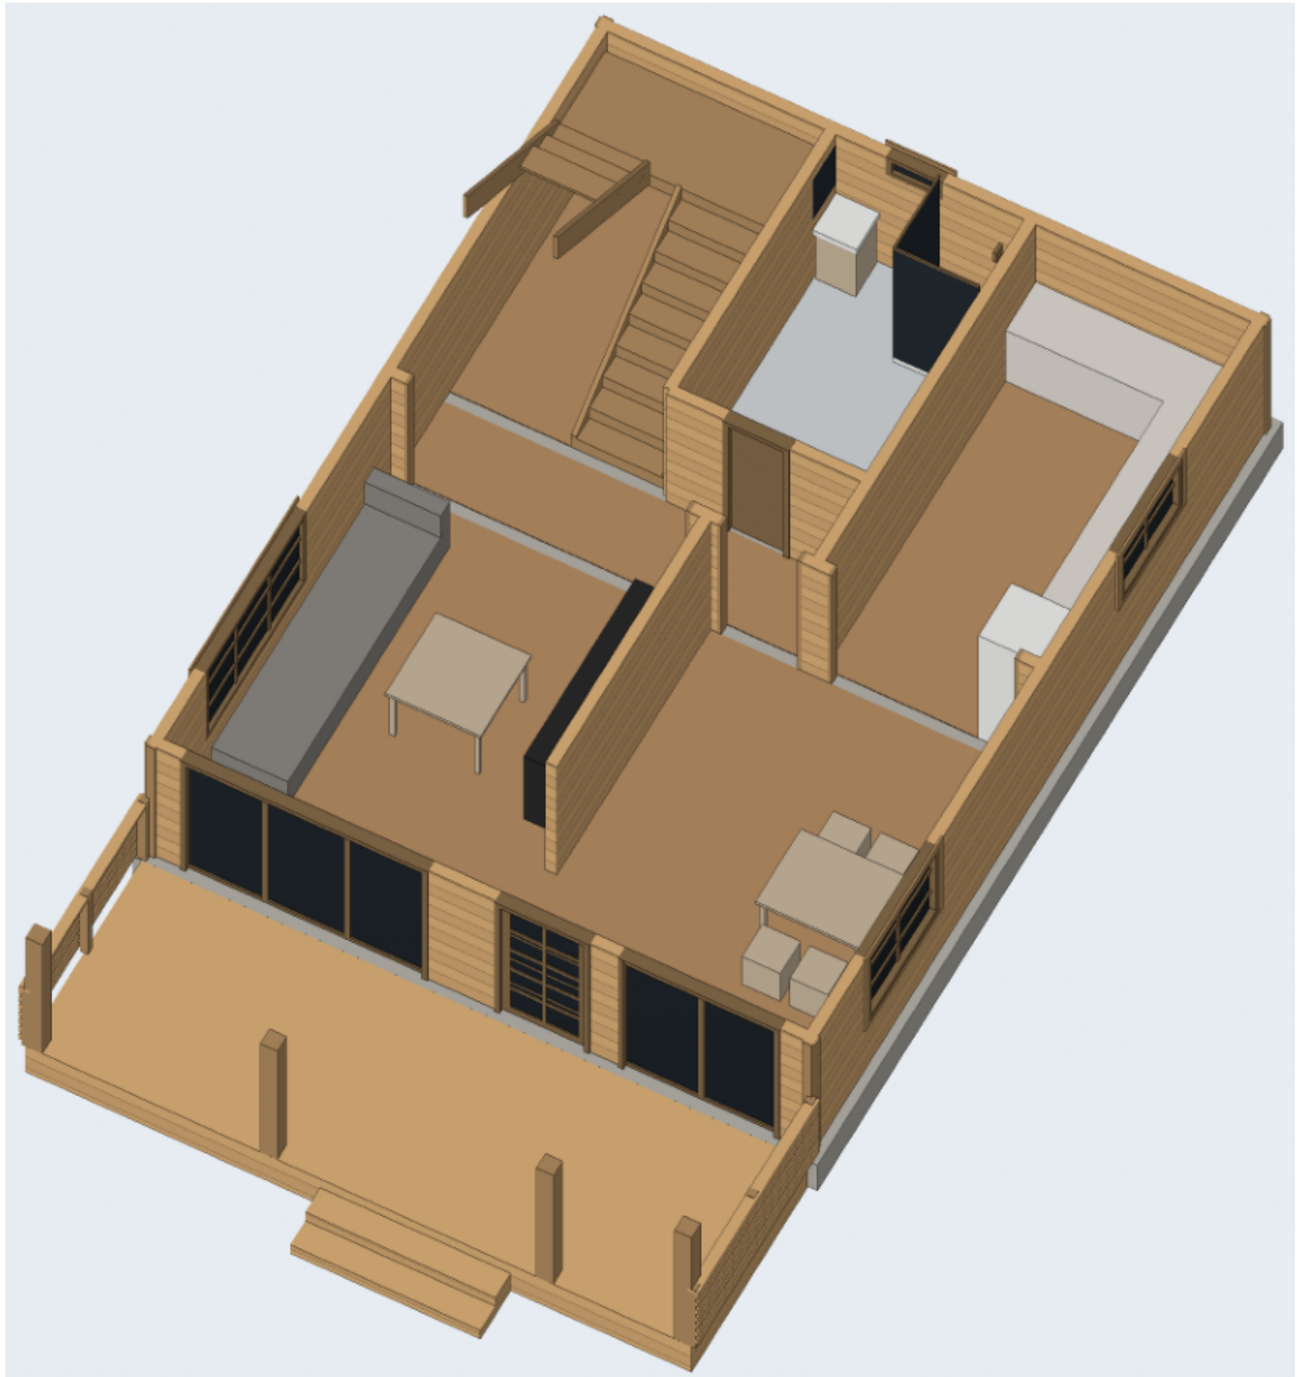

مصنع وتد الأخشاب Watad Wood Factory	المشروع / العميل	عنوان اللوحة	المقياس	التاريخ	رقم اللوحة
شاليهين الهدا الاستثماري — دورين — غرفتين وصالة لكل شاليه — 9.00 × 7.00 × 2 دور عميل — الهدا (استثماري)		المقطع العلوي بالفرش — الدور الأرضي	—	2026-10-23	A-10 (10/12)

المقطع العلوي بالفرش — الدور الأول


مقطع أفقي على ارتفاع 1.90 م — توزيع الفرش ومسار الحركة

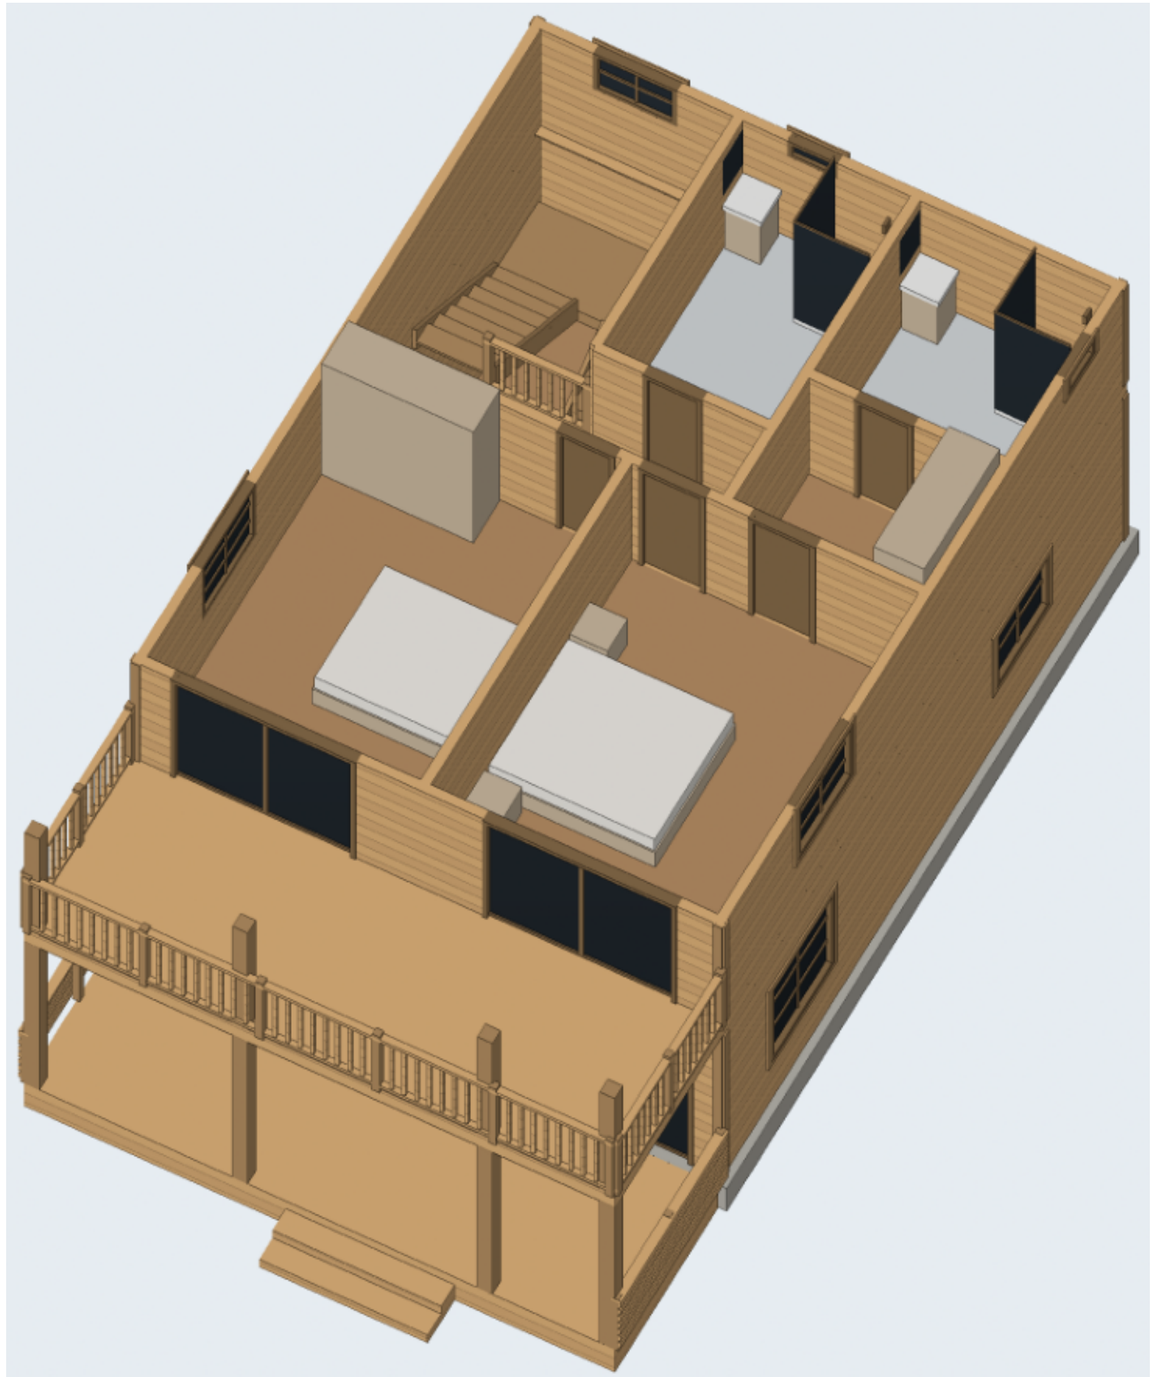

مصنع وتد الأخشاب Watad Wood Factory	المشروع / العميل شاليهين الهدا الاستثماري — دورين — غرفتين وصالة لكل شاليه — 9.00 × 7.00 × 2 دور عميل — الهدا (استثماري)	عنوان اللوحة المقطع العلوي بالفرش — الدور الأول	المقياس —	التاريخ 2026-10-23	رقم اللوحة A-11 (11/12)

المنظور ثلاثي الأبعاد والمواد

النمط: جوزي غامق + إطارات سوداء — رندر واقعي بخامات حقيقية

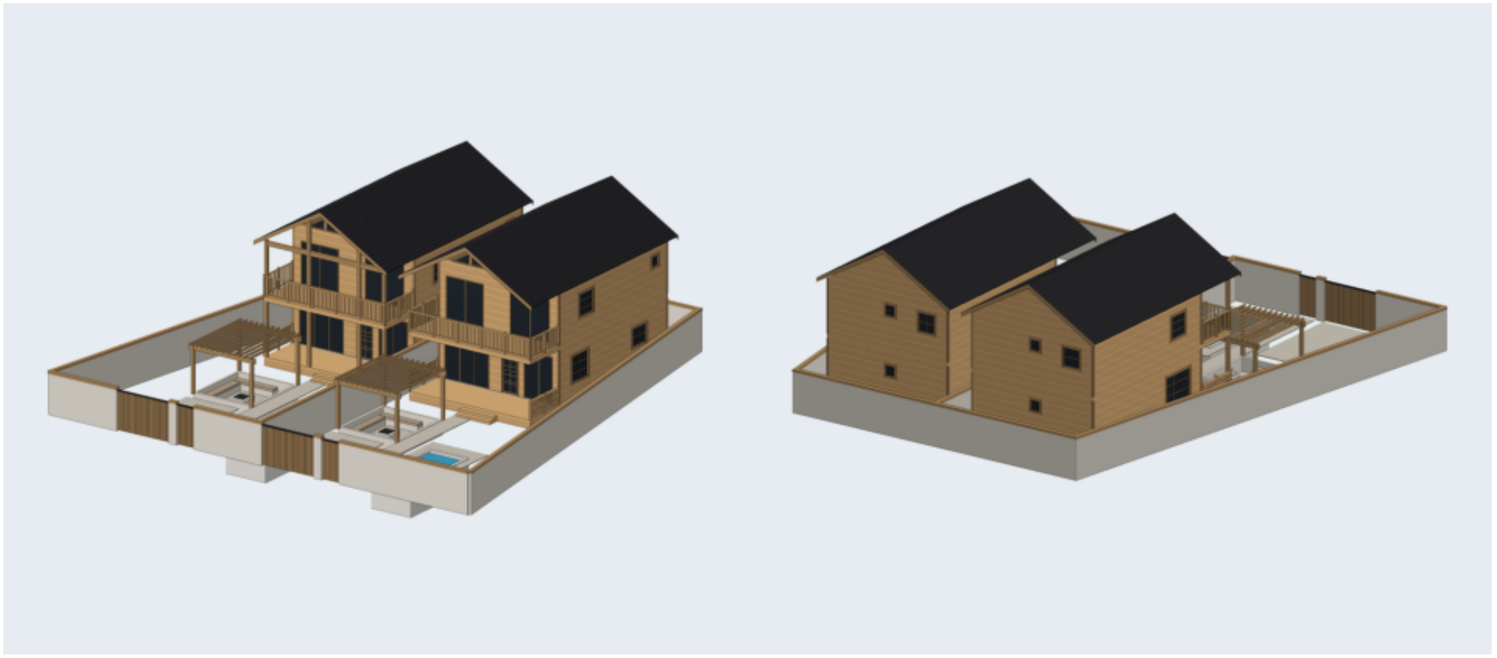

جدول المواد والألوان

الخشب / الصبغة

خشب طبيعي فاتح (بدون صبغة)

القرميد

قرميد رمادي غامق

الزجاج

زجاج عاكس غامق

إطارات الشبابيك والأبواب

إطار خشب بنفس الصبغة أغمق

الكنار والزوايا

نفس الصبغة أغمق درجة


الصبة

خرسانة 45 سم


الدربزين: ألواح أفقية متقاربة (عصري)

تقسيم الشبابيك: بدون | الباب الرئيسي: سحاب زجاج

أنواع الدربزين المعتمدة (من مشاريع المصنع)

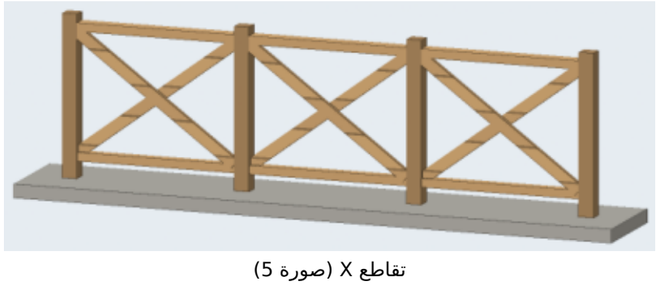

تقاطع X (صورة 5)

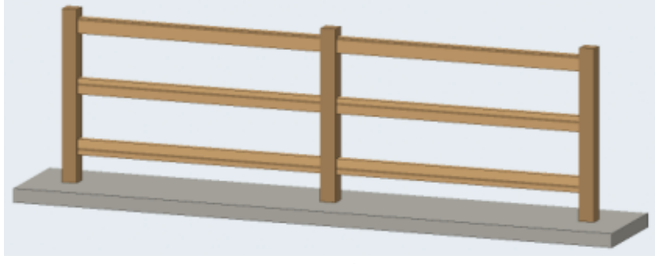

3 مرابيع أفقية (صورة 2)



قوائم رأسية متقاربة (صورة 1)

المشروع / العميل	عنوان اللوحة	المقياس	التاريخ	رقم اللوحة
مصنع وتد الأخشاب Watad Wood Factory — **شاليهين الهدا الاستثماري — دورين — غرفتين وصالة لكل شاليه — 9.00 × 7.00 × 2 دور** عميل — الهدا (استثماري)	**المنظور والمواد**	—	**2026-10-23**	**A-12 (12/12)**