



المسقط الأفقي مع الفرش  
الأبعاد بالسنتيمتر - الجدران: قوائم 5×7 + تليس 2.5 من الجهتين (12 سم)

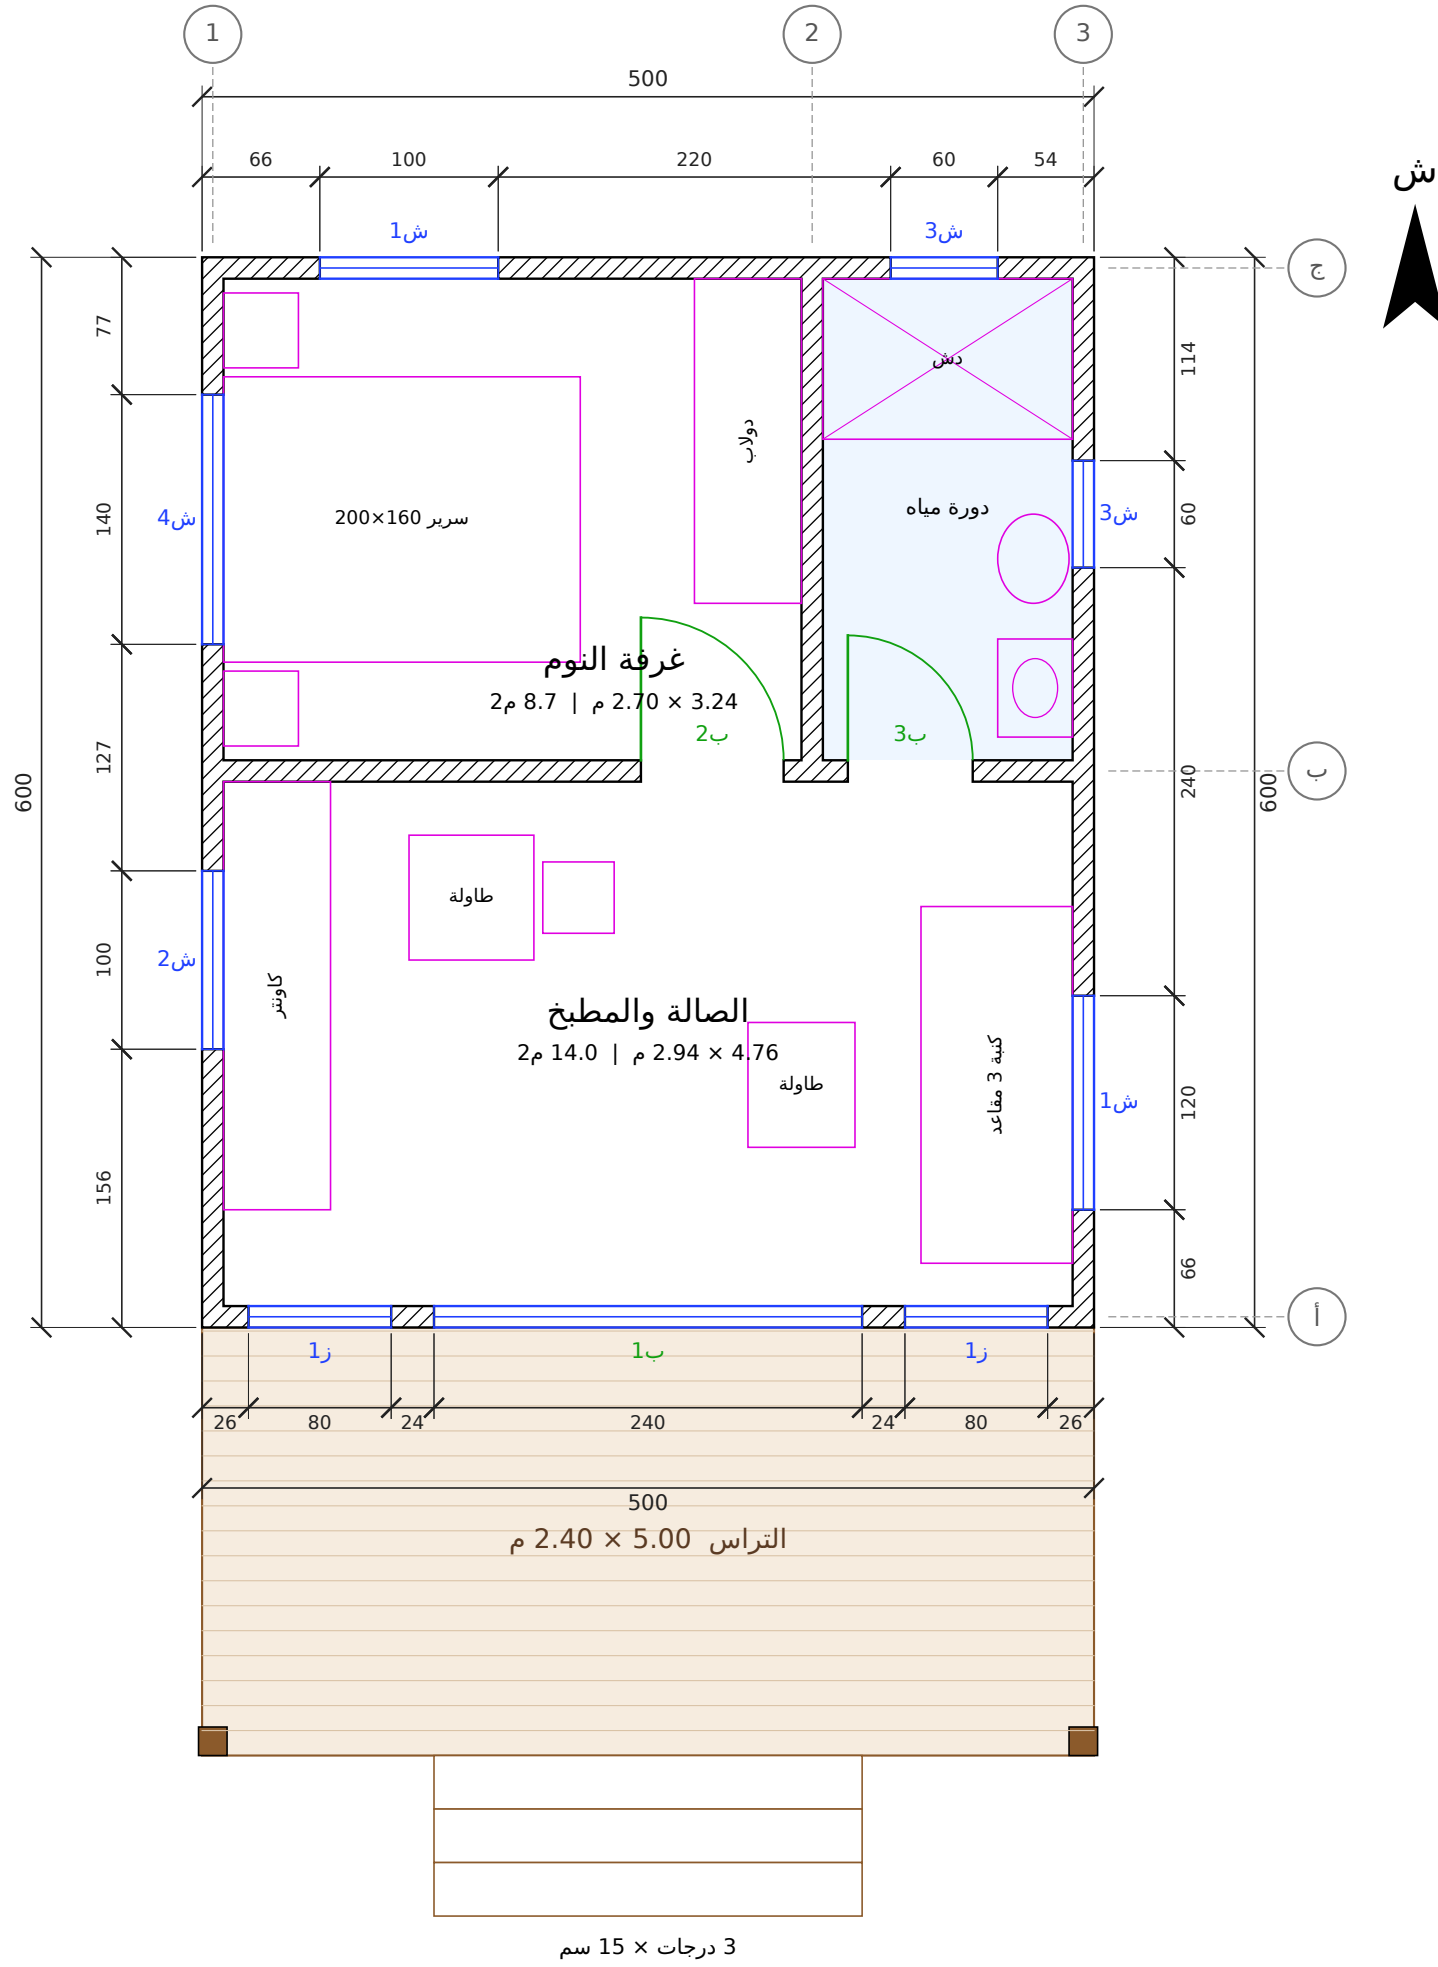


| المشروع / العميل                       | عنوان اللوحة                                        | المقياس       | التاريخ    | رقم اللوحة  |
|----------------------------------------|-----------------------------------------------------|---------------|------------|-------------|
| مصنع وتد الأخشاب<br>Watad Wood Factory | كوخ غرفة وتراس مسقوف 6×5<br>عميل - تصميم حسب الصورة | المسقط الأفقي | 2026-09-29 | A-01 (1/10) |

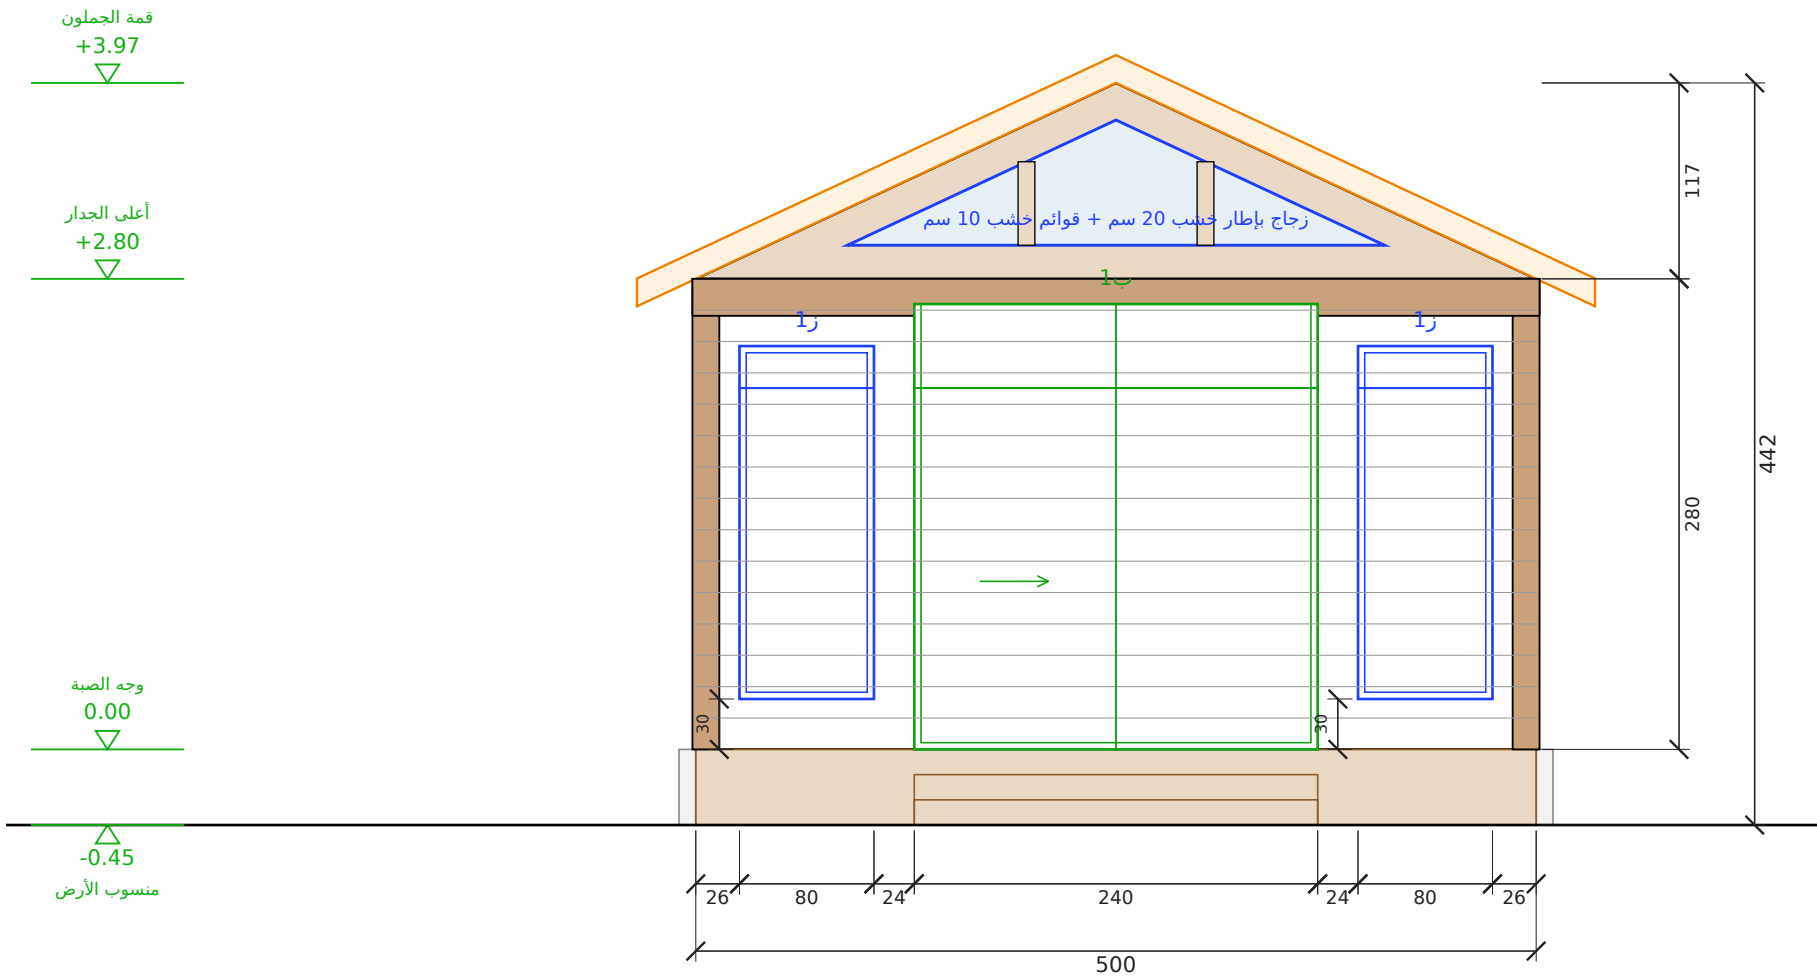

الواجهة الأمامية (التراس)

مقياس 1:50 | الوحدة: سم

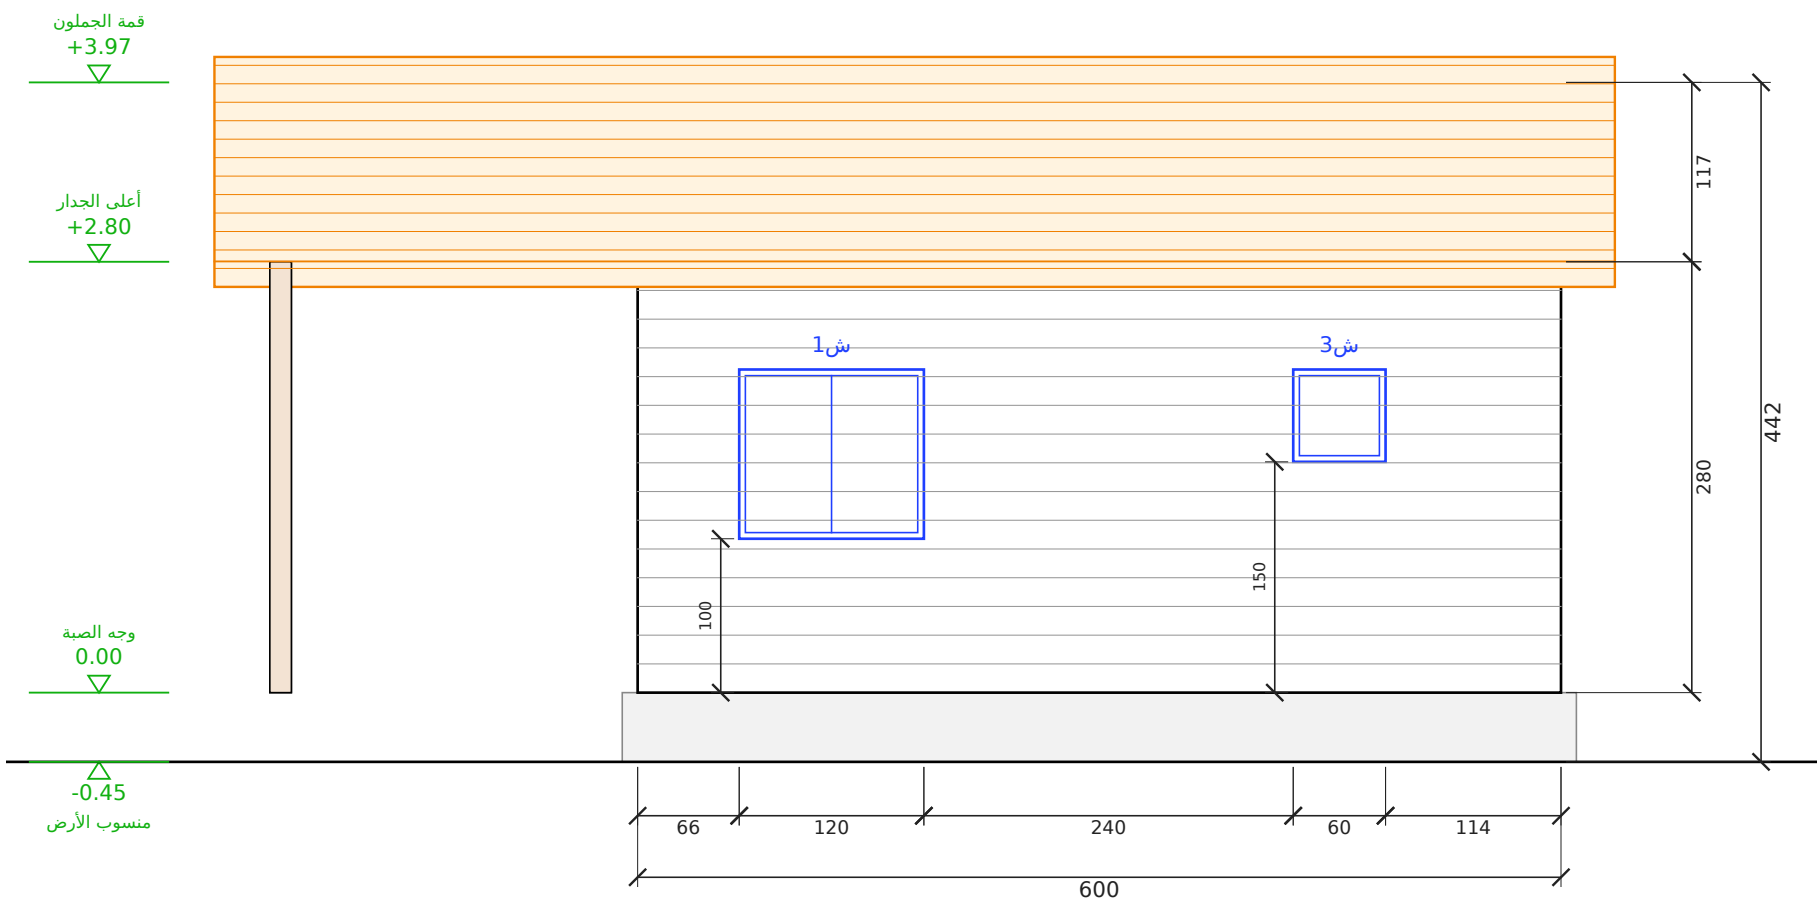

الواجهة الشرقية

مقياس 1:50 | الوحدة: سم

رقم اللوحة

التاريخ

المقياس

عنوان اللوحة

المشروع / العميل

A-02 (2/10)


2026-09-29

الواجهة الأمامية (التراس) والواجهة الشرقية 1:50

كوخ غرفة وتراس مسقوف 6x5  
عميل - تصميم حسب الصورة


مصنع وند الأخشاب  
Watad Wood Factory



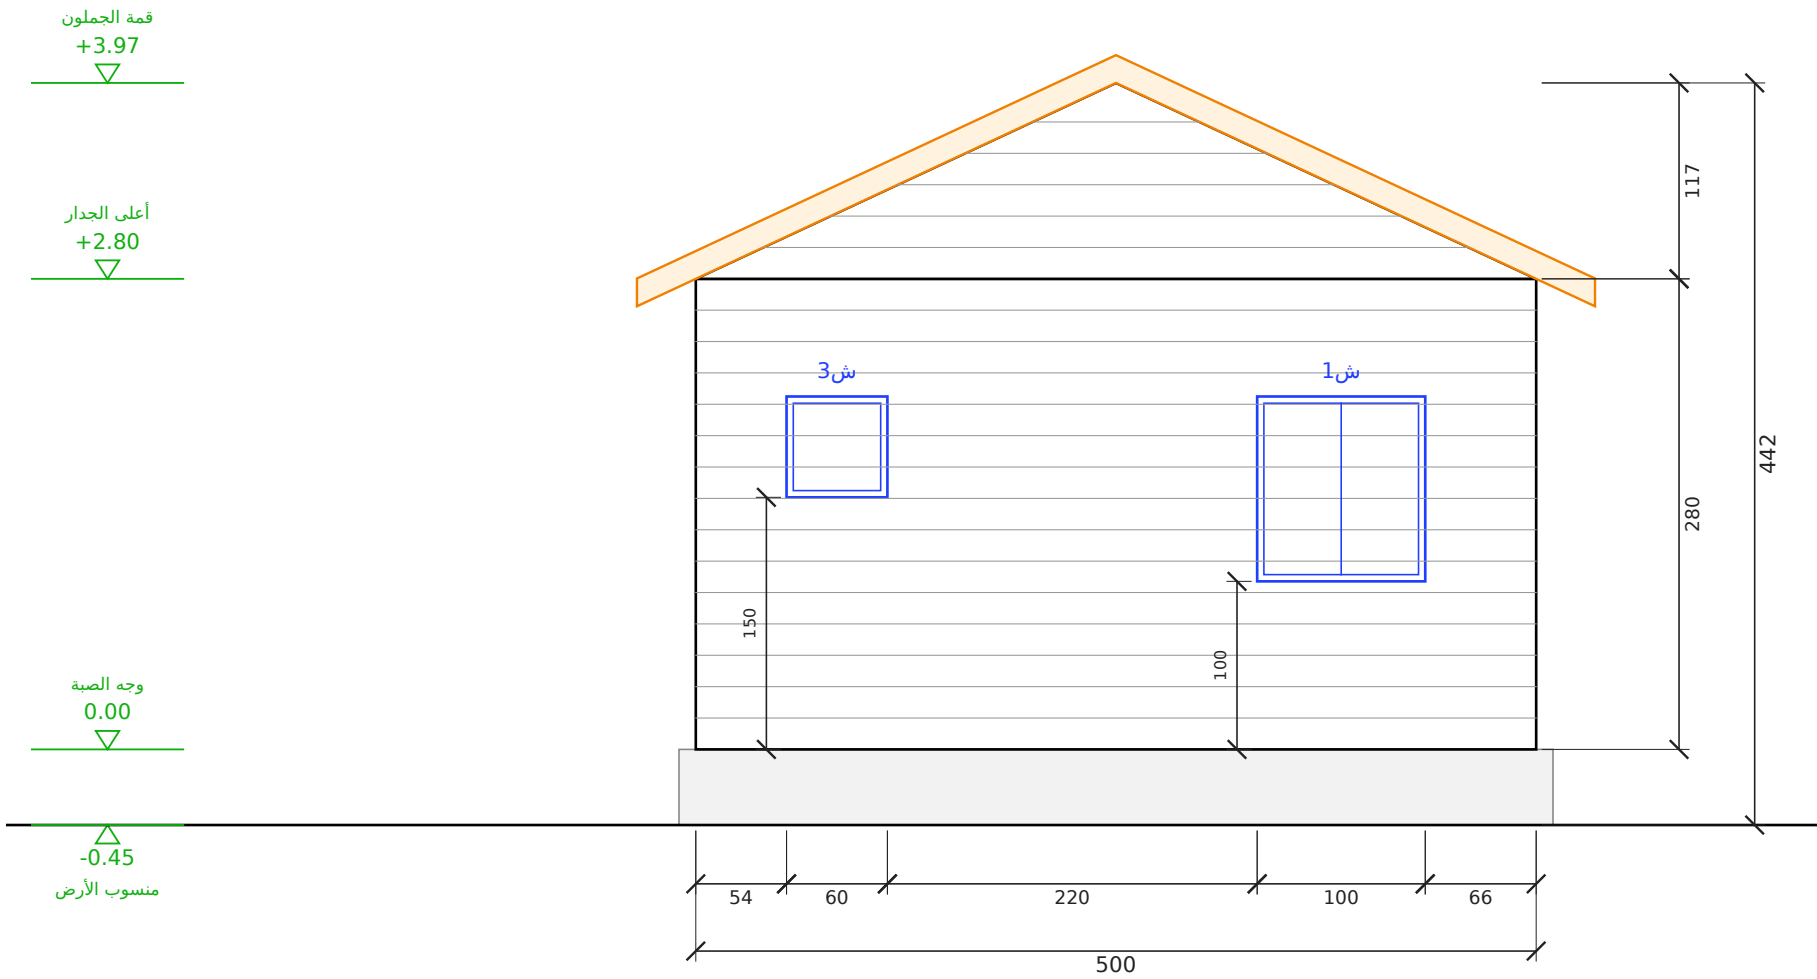

### الواجهة الخلفية

مقياس 1:50 | الوحدة: سم

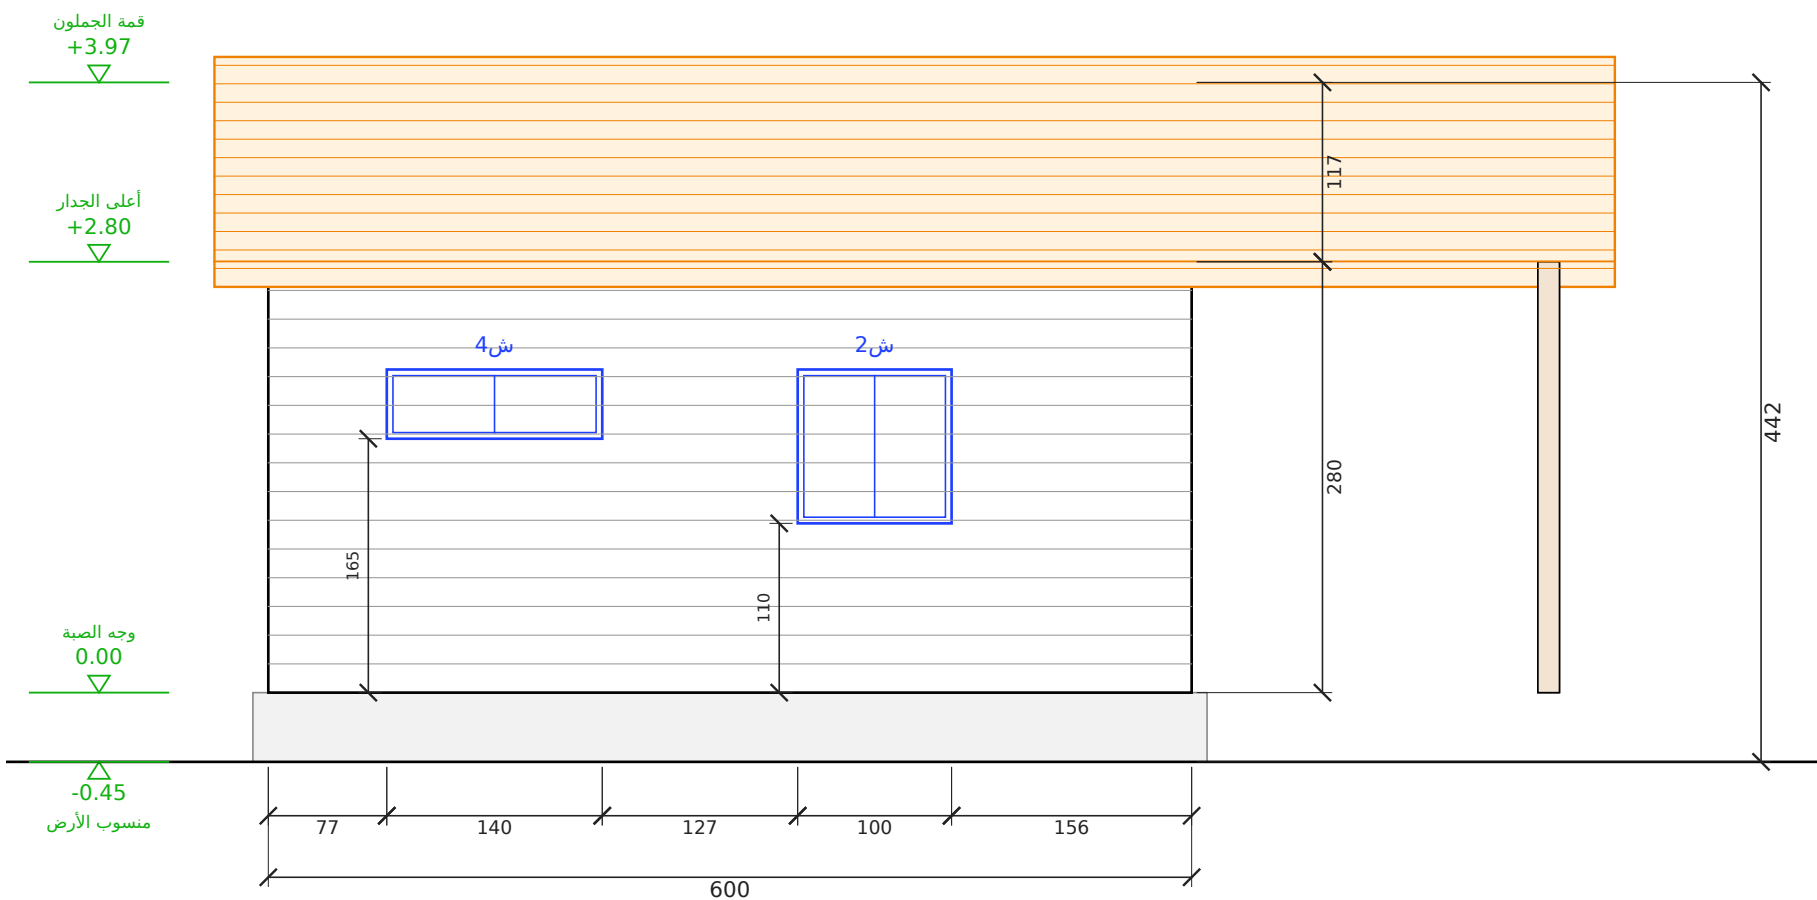


### الواجهة الغربية


مقياس 1:50 | الوحدة: سم

| رقم اللوحة  | التاريخ    | المقياس | عنوان اللوحة                     | المشروع / العميل                                    | مصنع وتد الأخشاب<br>Watad Wood Factory |
|-------------|------------|---------|----------------------------------|-----------------------------------------------------|----------------------------------------|
| A-03 (3/10) | 2026-09-29 | 1:50    | الواجهة الخلفية والواجهة الغربية | كوخ غرفة وتراس مسقوف 6x5<br>عميل - تصميم حسب الصورة |                                        |


مسقط السقف (جملون)  
رفر 35 سم من كل جهة | مقياس 1:50

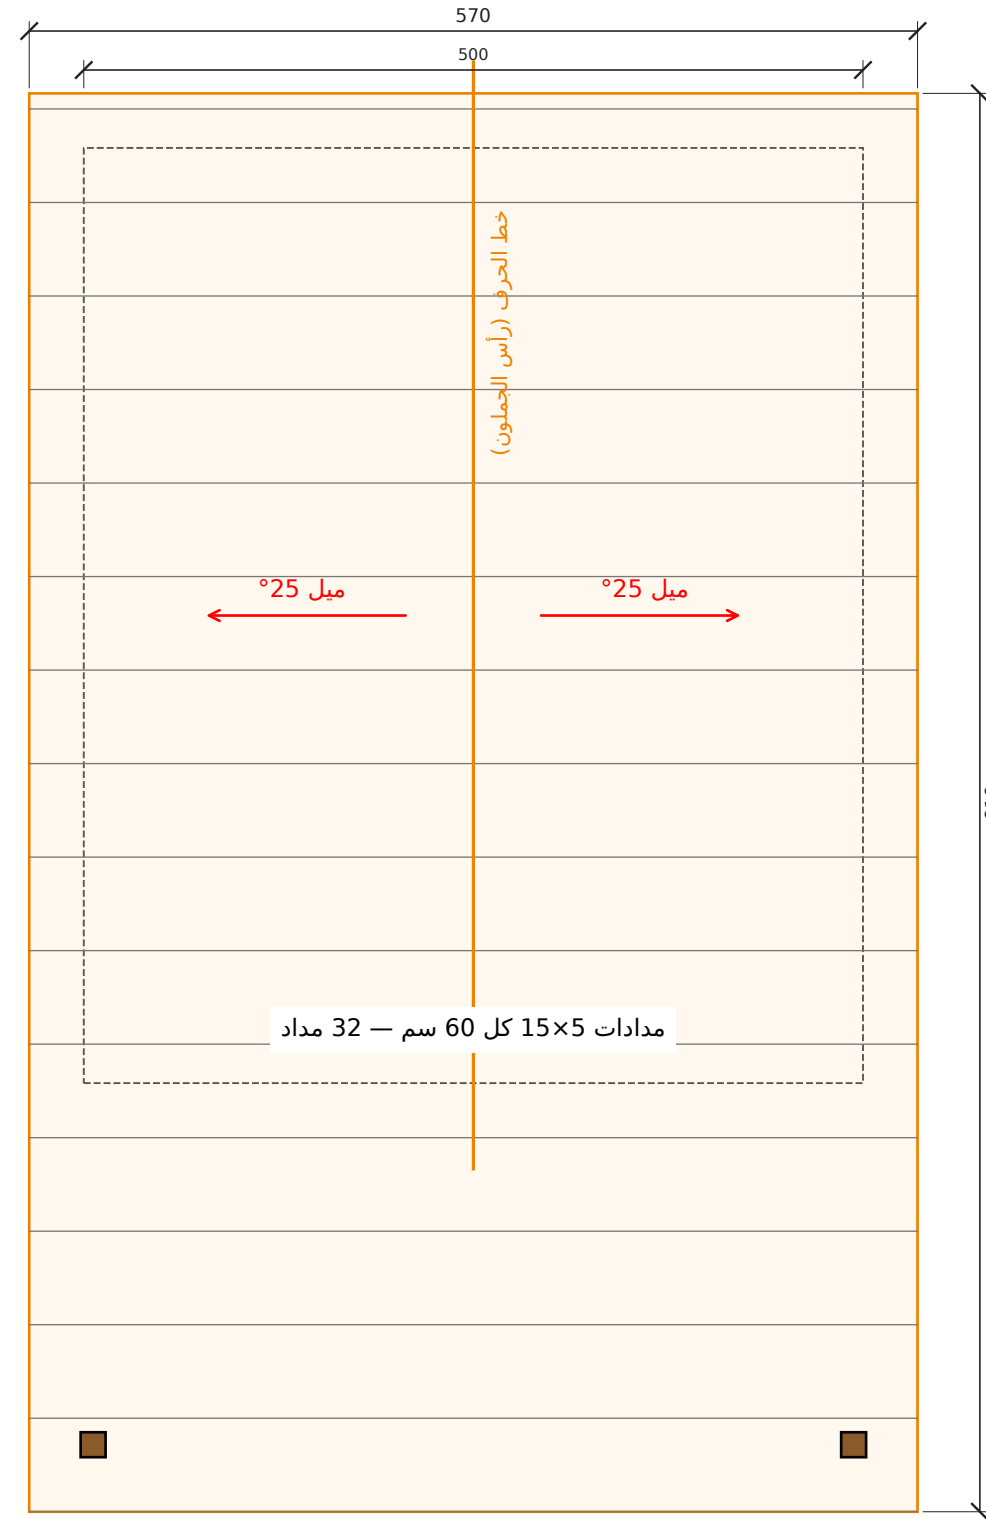

قطاع عرضي أ-أ  
مقياس 1:50 | الوحدة: سم

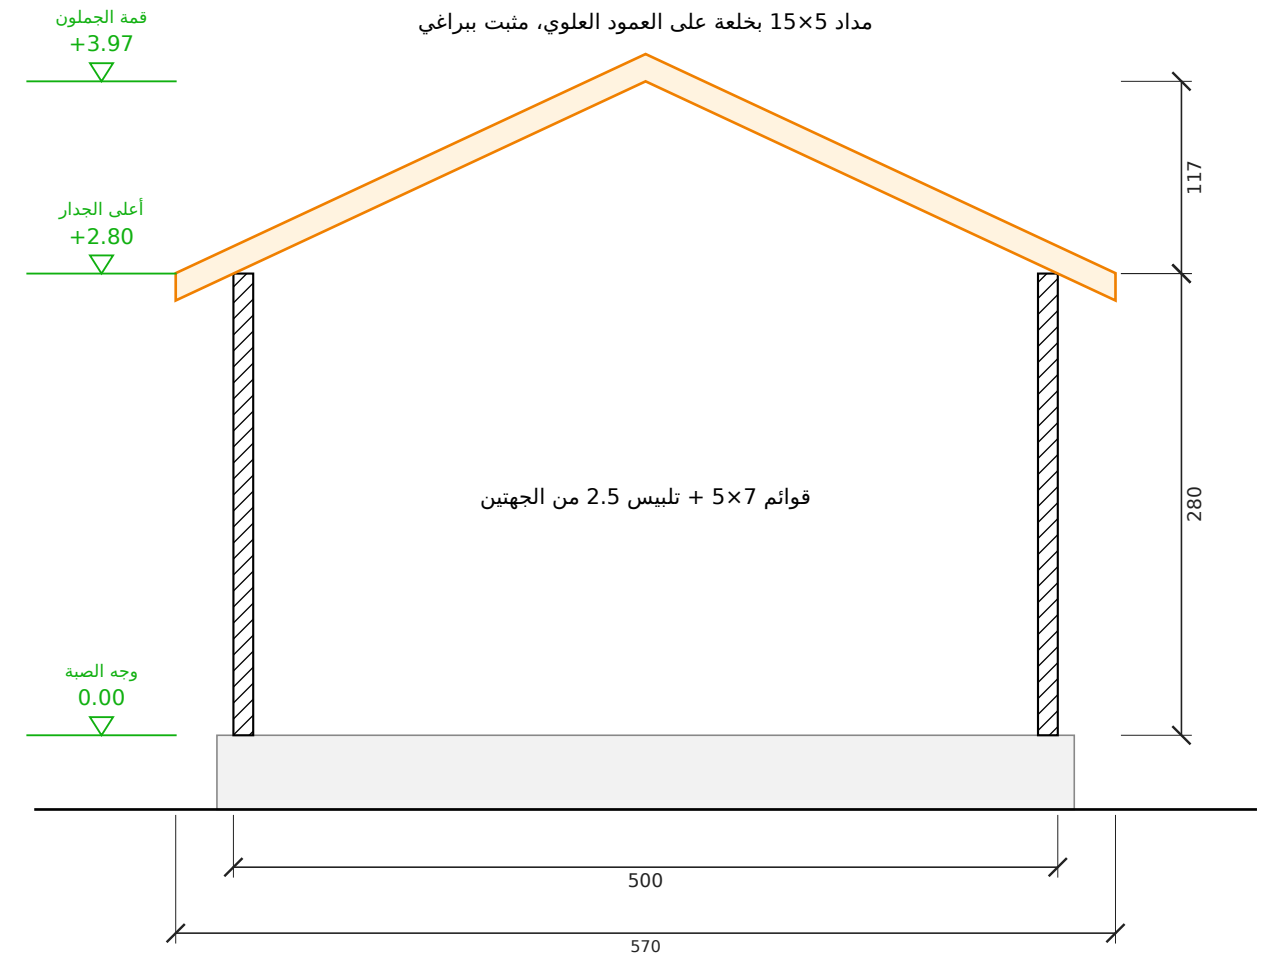

تفصيلة جلوس المداد على العلوي (1:5)

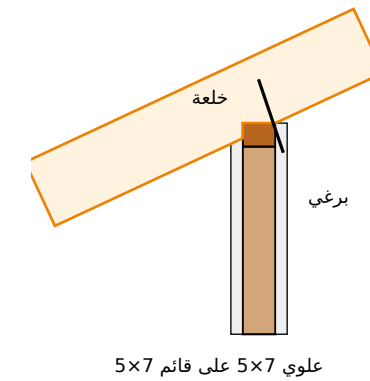

رقم اللوحة

A-04 (4/10)

التاريخ

2026-09-29

المقياس

1:50

عنوان اللوحة

مسقط السقف والقطاع

المشروع / العميل

كوخ غرفة وتراس مسقوف 6×5  
عميل — تصميم حسب الصورة

مصنع وتد الأخشاب  
Watad Wood Factory



جدول مقاسات الأبواب والشبابيك  
مقاس الفتحة الصافي في الجدار - الوحدة: سم

| الرمز | النوع     | العرض (سم) | الارتفاع (سم) | ارتفاع الجلسة (سم) | العدد | الموقع              |
|-------|-----------|------------|---------------|--------------------|-------|---------------------|
| ب1    | باب مزدوج | 240        | 265           | -                  | 1     | الأمامية (التراس)   |
| ب2    | باب       | 80         | 210           | -                  | 1     | غرفة النوم          |
| ب3    | باب       | 70         | 210           | -                  | 1     | حمام                |
| ز1    | شباك      | 80         | 210           | 30                 | 2     | الأمامية (التراس) 2 |
| ش1    | شباك      | 120        | 110           | 100                | 1     | الشرقية             |
| ش1    | شباك      | 100        | 110           | 100                | 1     | الخلفية             |
| ش2    | شباك      | 100        | 100           | 110                | 1     | الغربية             |
| ش3    | شباك      | 60         | 60            | 150                | 2     | الشرقية - الخلفية   |
| ش4    | شباك      | 140        | 45            | 165                | 1     | الغربية             |

الإجمالي: أبواب 3 - شبابيك 8

جدول المساحات وبيانات المشروع والتسعير

جدول المساحات

| م | الفراغ                    | الأبعاد (م) | المساحة (م2) |
|---|---------------------------|-------------|--------------|
| 1 | الصالة والمطبخ            | 4.76 × 2.94 | 13.99        |
| 2 | غرفة النوم                | 3.24 × 2.70 | 8.75         |
| 3 | دورة مياه                 | 1.40 × 2.70 | 3.78         |
|   | المساحة الصافية الداخلية  |             | 26.52        |
|   | التراس المسقوف            | 5.00 × 2.40 | 12.00        |
|   | المساحة الإجمالية المبنية | 5.00 × 6.00 | 30.00        |

بيانات المشروع

| البند       | البيان                                |
|-------------|---------------------------------------|
| المشروع     | كوخ غرفة وتراس مسقوف 6×5              |
| العميل      | عميل — تصميم حسب الصورة               |
| الموقع      | —                                     |
| الاستخدام   | استراحة / استجمام                     |
| التاريخ     | 2026-09-29                            |
| نظام البناء | هيكل خشب 5×7 + تليس 2.5 سم من الجهتين |
| السقف       | جملون 25° — قرميد معدني               |

التسعير

عرض اليوم الوطني


| البند                               | القيمة      |
|-------------------------------------|-------------|
| المساحة المبنية (م2)                | 30.00       |
| سعر المتر المربع — عرض اليوم الوطني | 1,096 ريال  |
| الإجمالي                            | 32,880 ريال |

ملاحظات:


- السعر للمساحة المبنية حسب المخطط المعتمد.
- الصبة والتوريدات الخارجية على العميل ما لم يُذكر غير ذلك.

# الصور الواقعية


أمامي

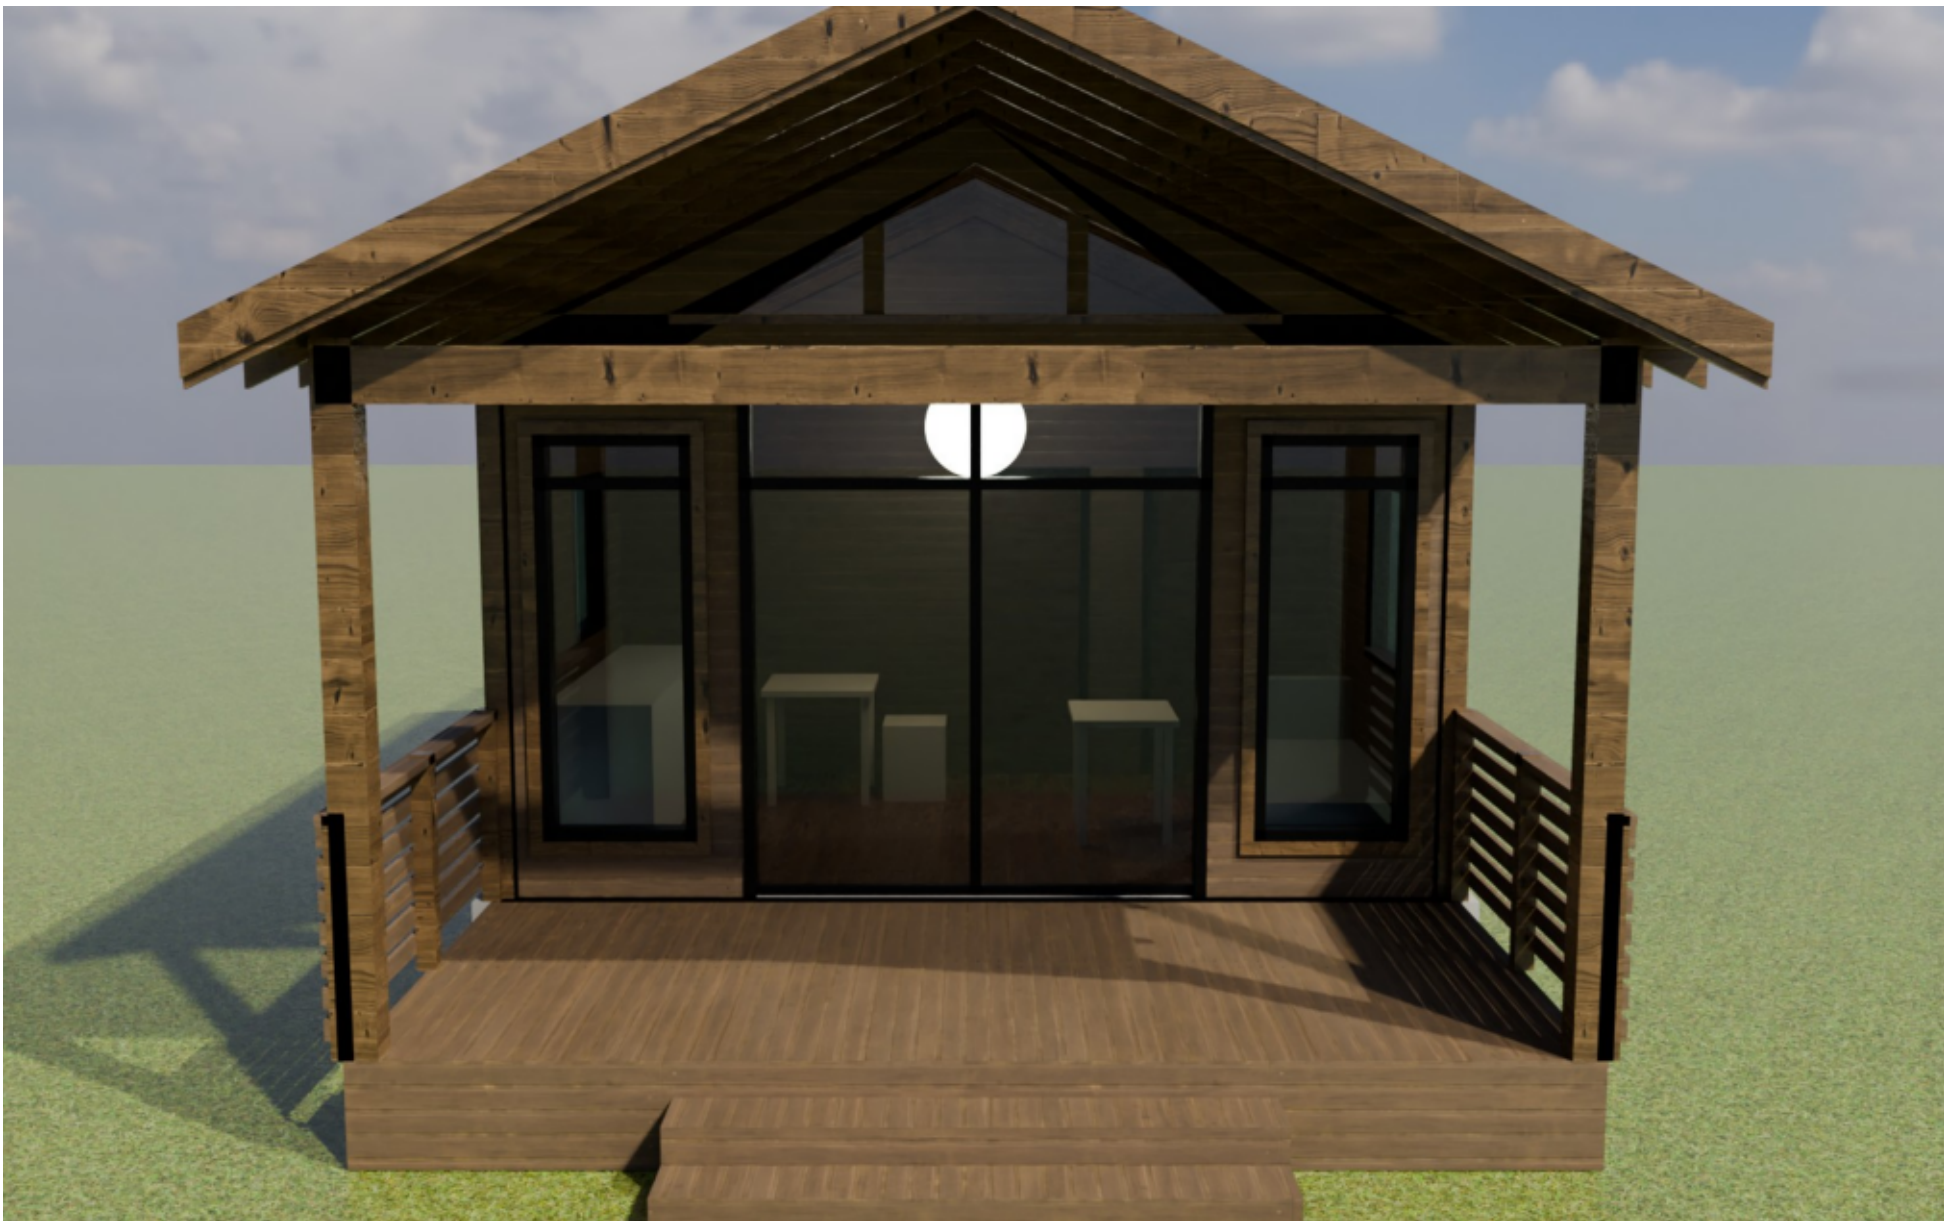

أمامي يسار

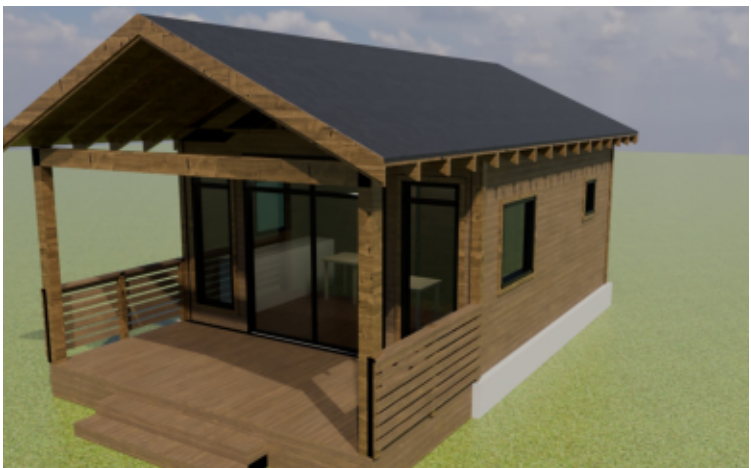

أمامي يمين

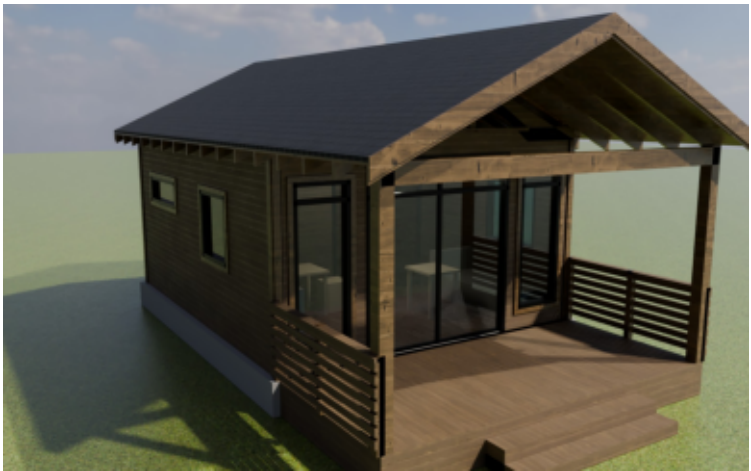

خلفي



رندر واقعي بخامات حقيقية وإضاءة طبيعية — الألوان النهائية حسب عينات المورد


|             |            |         |                |                                                     |                                        |
|-------------|------------|---------|----------------|-----------------------------------------------------|----------------------------------------|
| رقم اللوحة  | التاريخ    | المقياس | عنوان اللوحة   | المشروع / العميل                                    | مصنع وتد الأخشاب<br>Watad Wood Factory |
| A-07 (7/10) | 2026-09-29 | —       | الصور الواقعية | كوخ غرفة وتراس مسقوف 6x5<br>عميل — تصميم حسب الصورة |                                        |

## لقطات المنظور الخارجي


المنظور الأمامي




منظور أمامي من اليسار

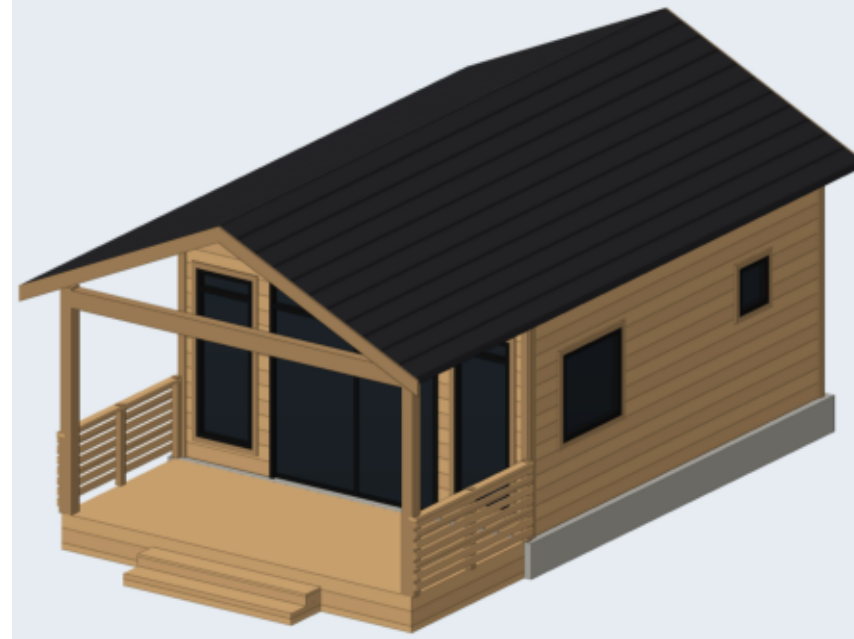

منظور أمامي من اليمين

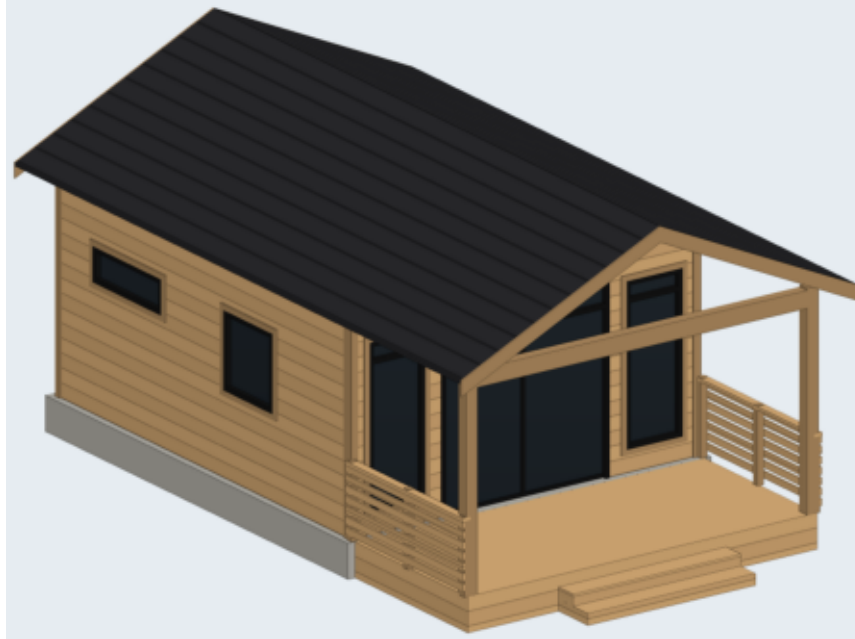


المنظور الخلفي

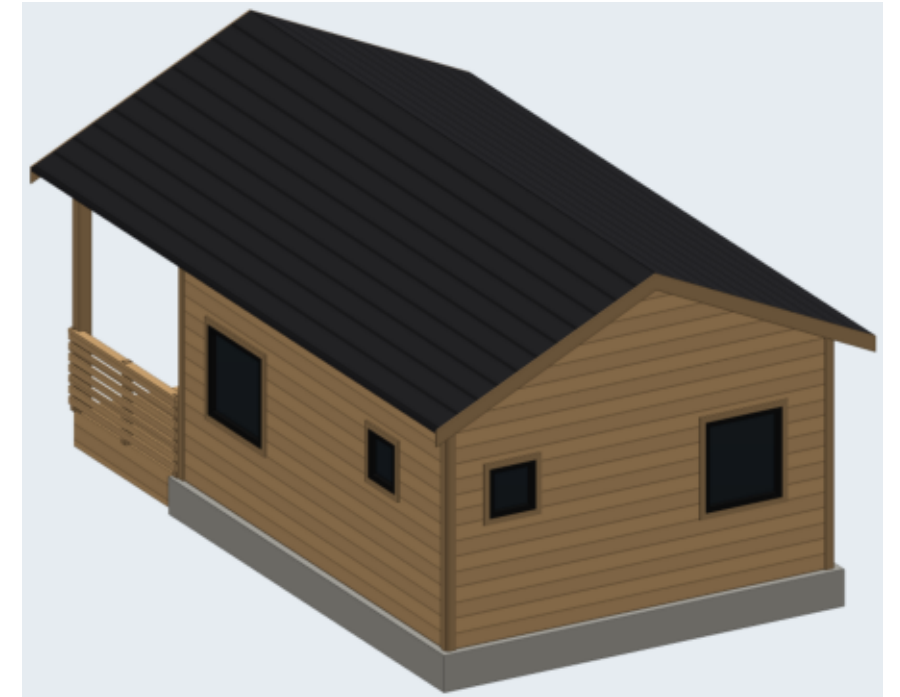

منظور خلفي من اليمين




منظر علوي

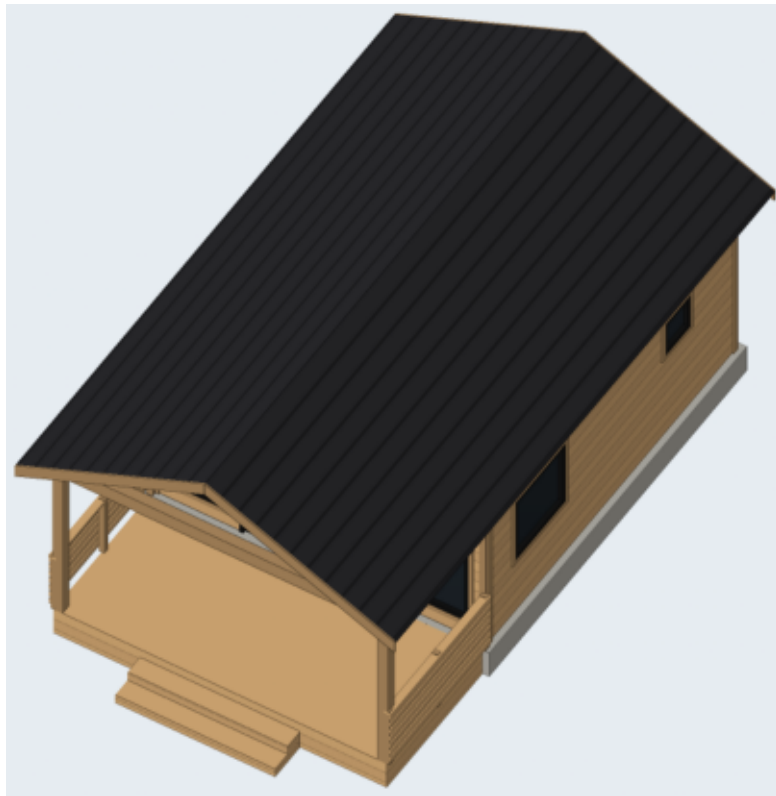

## المقطع العلوي بالفرش

مقطع أفقي على ارتفاع 1.90 م — توزيع الفرش ومسار الحركة

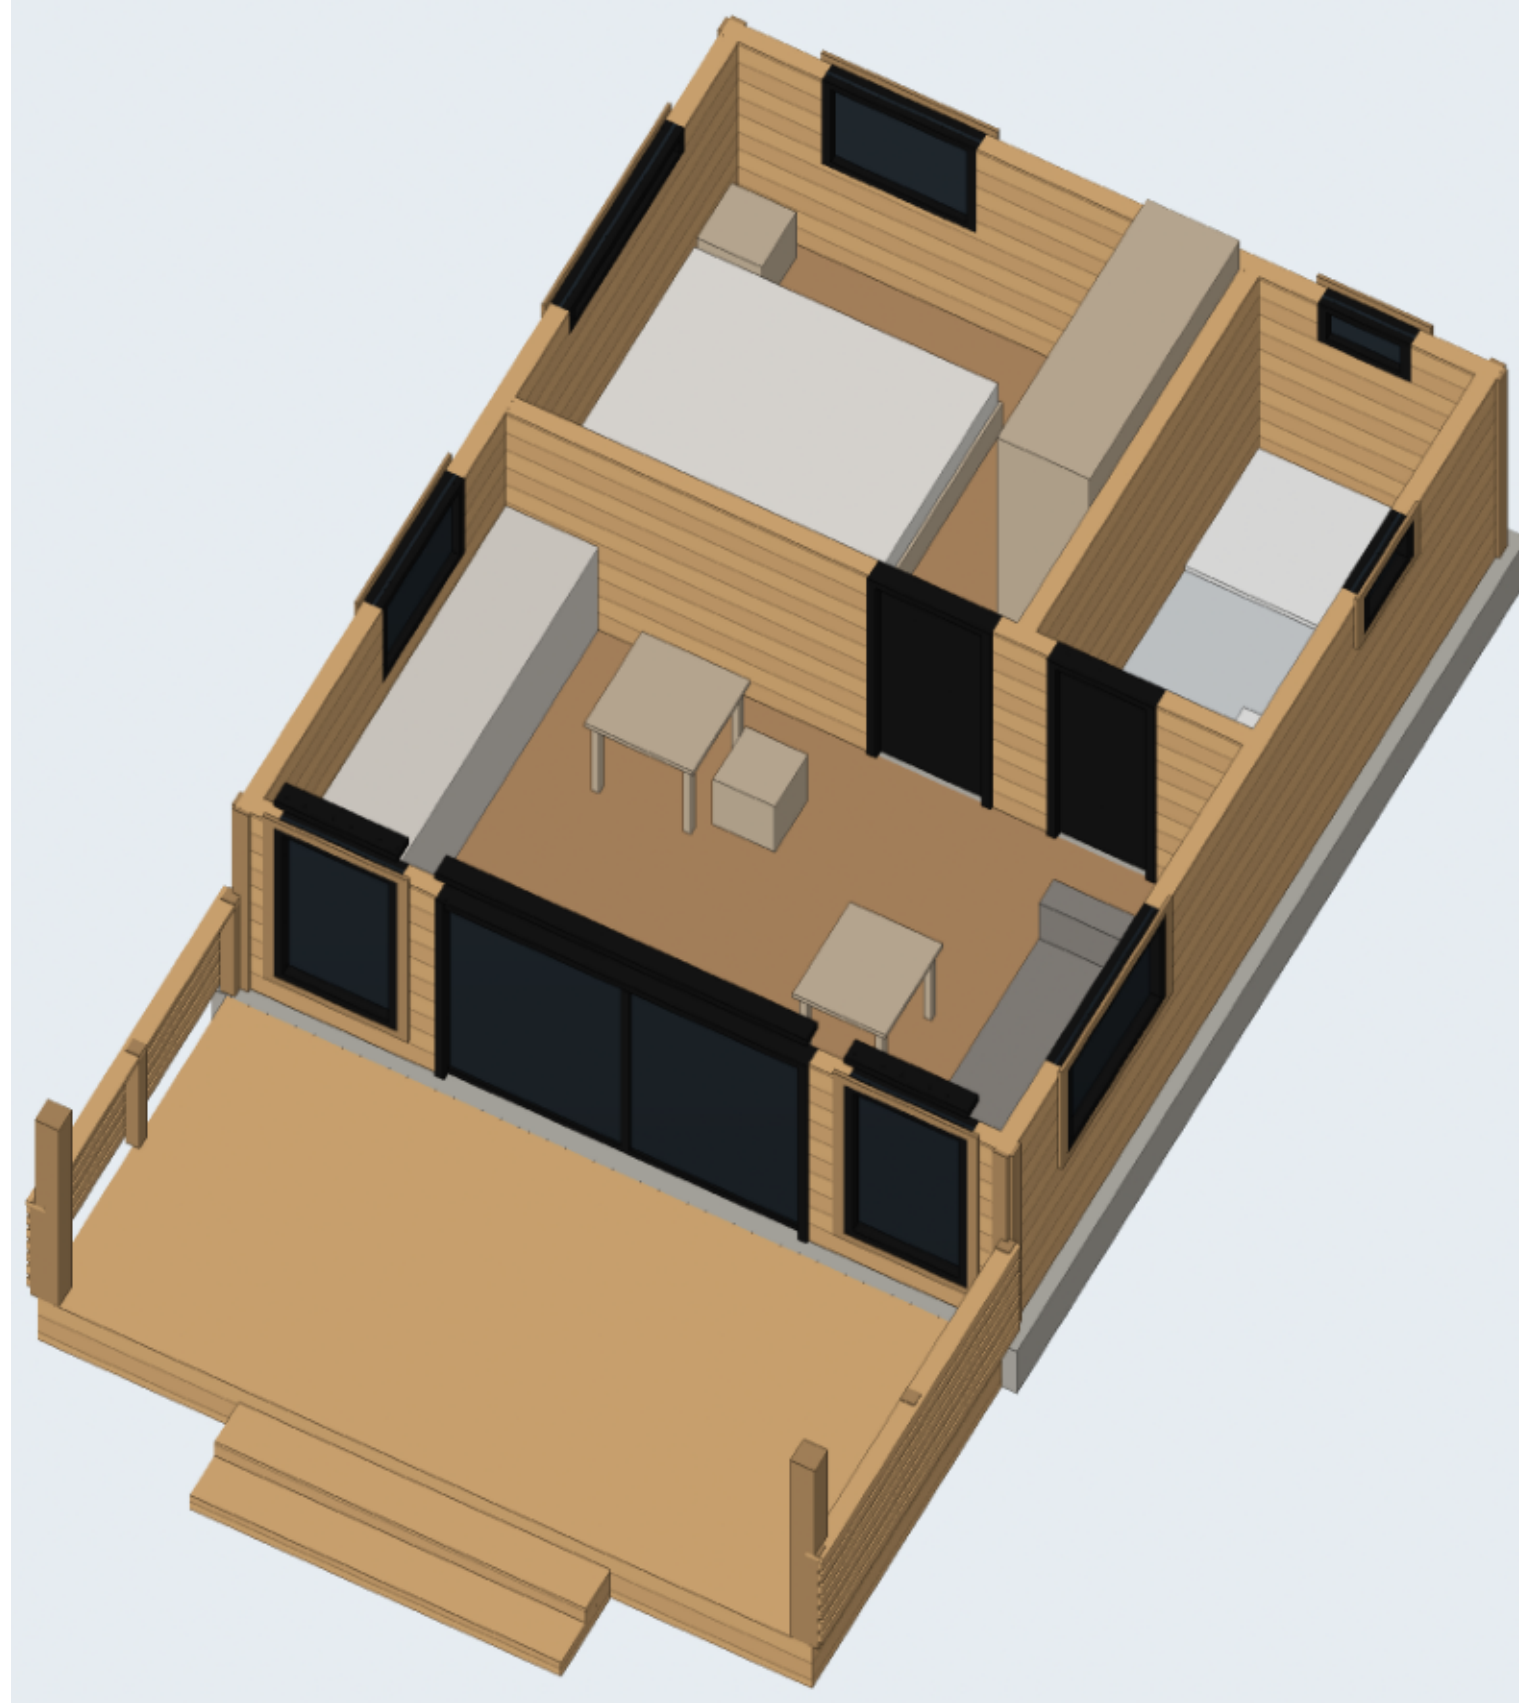

رقم اللوحة

A-09 (9/10)

التاريخ

2026-09-29

المقياس

—

عنوان اللوحة

المقطع العلوي بالفرش

المشروع / العميل

كوخ غرفة وتراس مسقوف 6x5  
عميل — تصميم حسب الصورة


مصنع وتد الأخشاب  
Watad Wood Factory



## المنظور ثلاثي الأبعاد والمواد

النمط: جوزي غامق + إطارات سوداء — معاينة تقريبية، الإخراج النهائي من 3ds Max

### جدول المواد والألوان

 

#### الخشب / الصبغة

خشب طبيعي فاتح (بدون صبغة)



#### القرميد

قرميد رمادي غامق



#### الزجاج

زجاج عاكس غامق



#### إطارات الشبابيك والأبواب

إطار ألومنيوم أسود



#### الكنار والزوايا

نفس الصبغة أعمق درجة



#### الصبغة

خرسانة 45 سم


الدريزين: ألواح أفقية متقاربة (عصري)

تقسيم الشبابيك: بدون | الباب الرئيسي: سحب زجاج


### أنواع الدريزين المعتمدة (من مشاريع المصنع)



قوائم رأسية متقاربة (صورة 1)

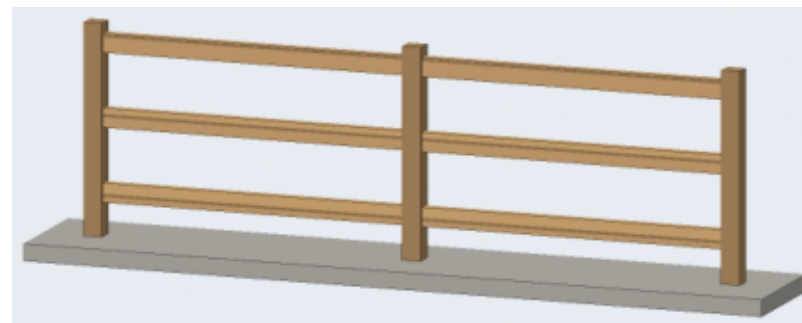

3 مربيع أفقية (صورة 2)

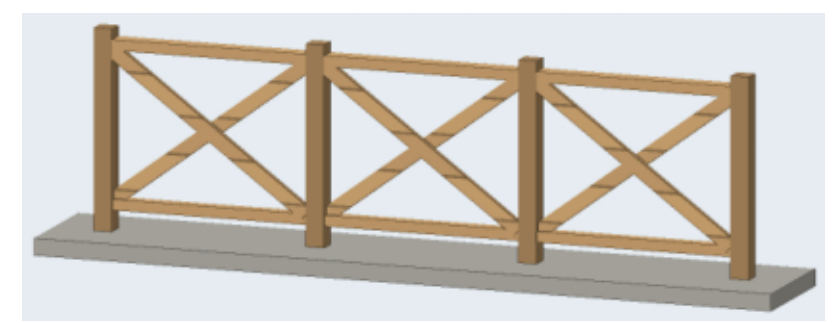

تقاطع X (صورة 5)

رقم اللوحة

A-10 (10/10)

التاريخ

2026-09-29

المقياس

—

عنوان اللوحة

المنظور والمواد

المشروع / العميل

كوخ غرفة وتراس مسقوف 6x5  
عميل — تصميم حسب الصورة

مصنع وتد الأخشاب  
Watad Wood Factory

