
المنظور ثلاثي الأبعاد والمواد

النمط: جوزي غامق + إطارات سوداء — رندر واقعي بخامات حقيقية

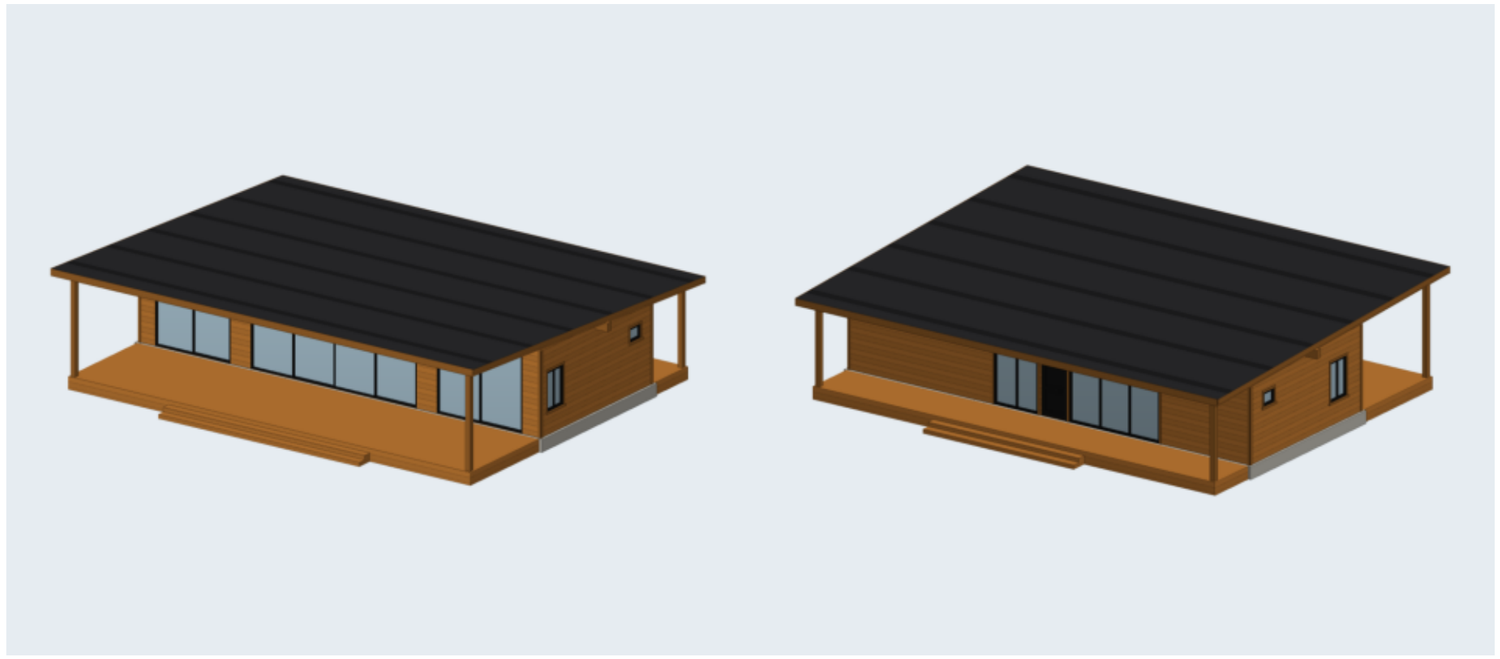

جدول المواد والألوان

الخشب / الصبغة

صبغة عسلي / سيدر

السقف (صاج معدني)

صاج رمادي غامق

الزجاج

زجاج شفاف

إطارات الشبابيك والأبواب

إطار ألمنيوم أسود

الكنار والزوايا

نفس الصبغة أغمق درجة


الصبة

خرسانة 45 سم


الدربزين: ألواح أفقية متقاربة (عصري)

تقسيم الشبابيك: بدون | الباب الرئيسي: سحاب زجاج

أنواع الدربزين المعتمدة (من مشاريع المصنع)

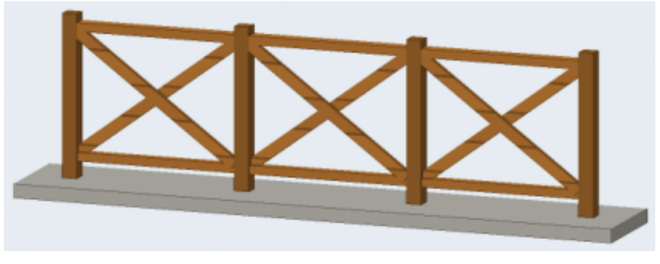

تقاطع X (صورة 5)

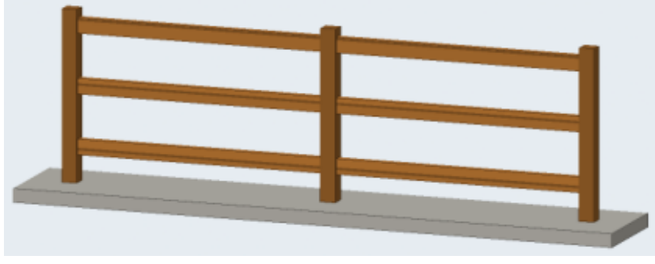

3 مرابيع أفقية (صورة 2)




قوائم رأسية متقاربة (صورة 1)

المشروع / العميل	عنوان اللوحة	المقياس	التاريخ	رقم اللوحة
كوخ الرياض 16.00 × 6.36 م — غرفتين نوم + صالة + حمامين + تراس أمامي 4.00 وخلفي 2.00 **عميل — الرياض**	**المنظور والمواد**	**1:50**	**2026-11-11**	**W-01 (1/15)**

مصنع وتد الأخشاب
Watad Wood Factory


المسقط الأفقي مع الفرش

الأبعاد بالسنتيمتر - الجدران: قوائم 7×5 + تلبيس 2.5 من الجهتين (12 سم)

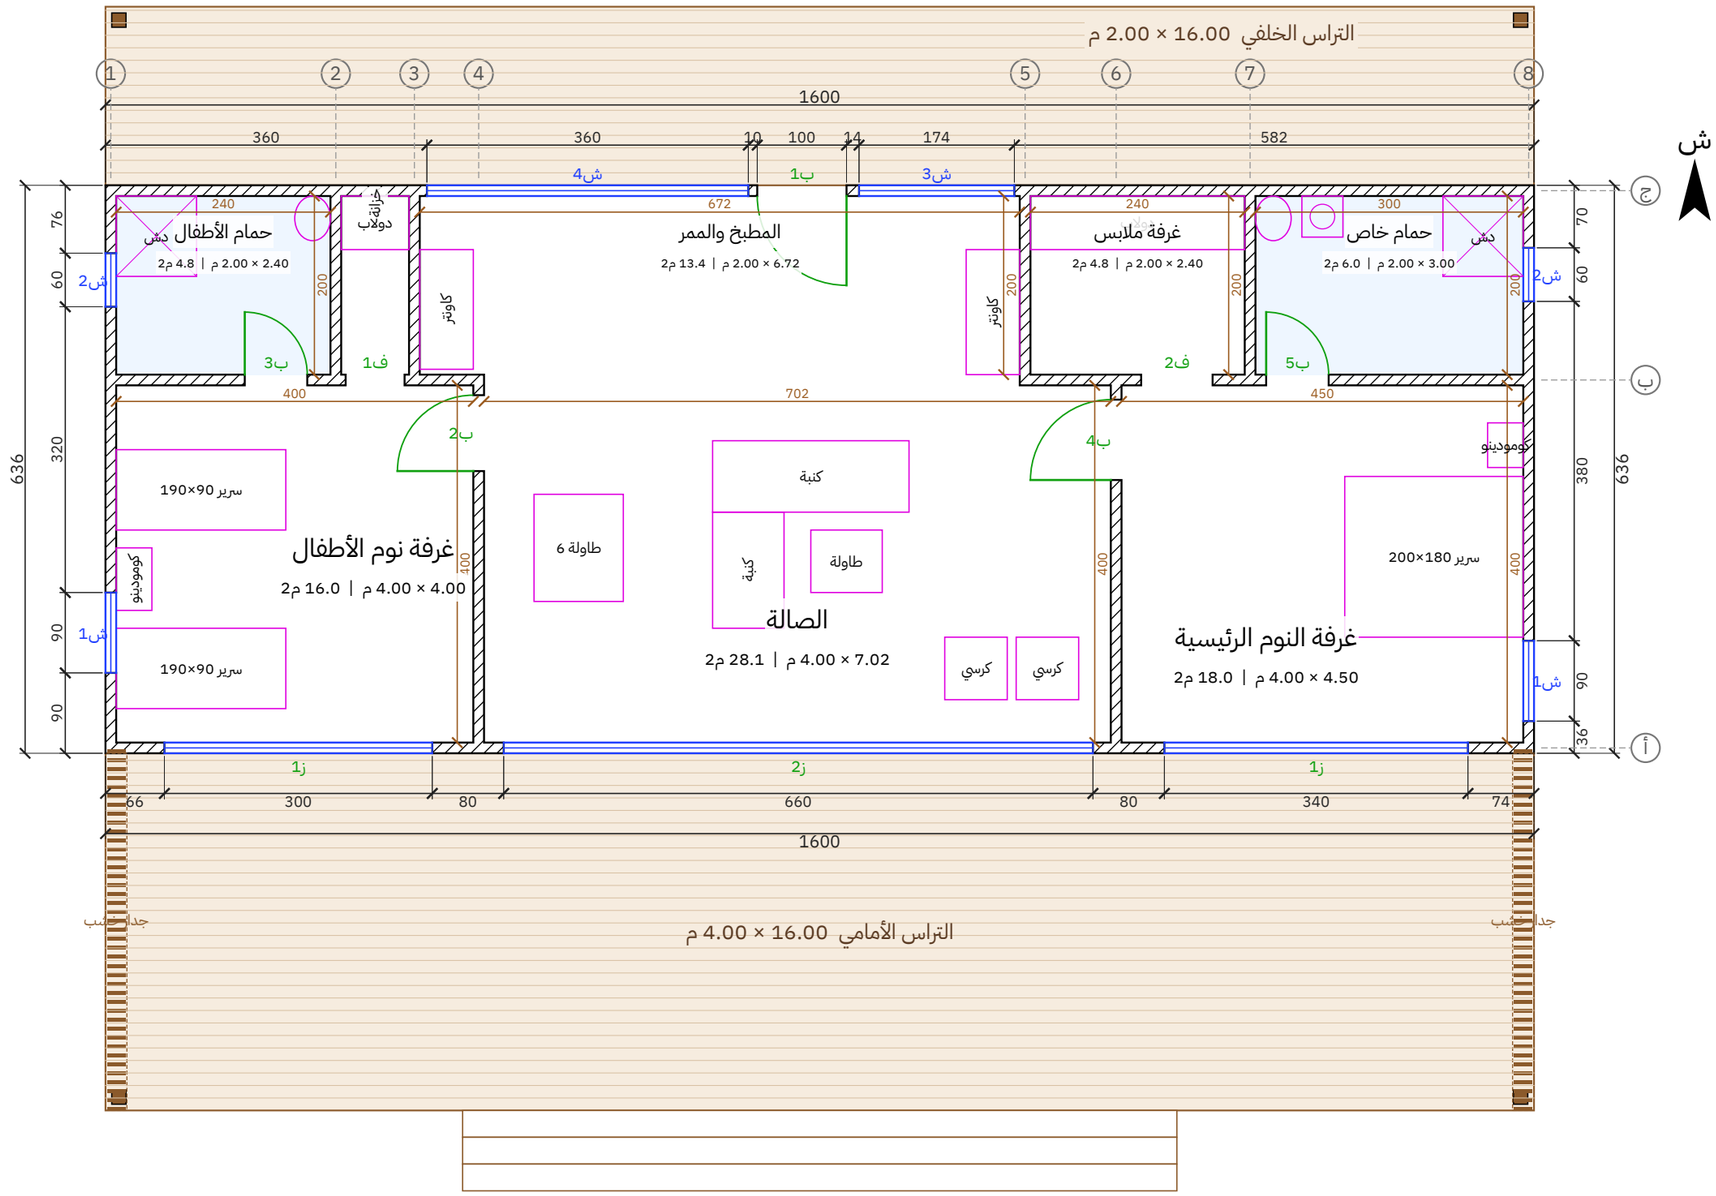


3 درجات × 15 سم

مصنع وتد الأخشاب Watad Wood Factory	المشروع / العميل كوخ الرياض 16.00 × 6.36 م – غرفتين نوم + صالة + حمامين + تراس أمامي 4.00 وخلفي 2.00 عميل – الرياض	عنوان اللوحة المسقط الأفقي	المقياس 1:50	التاريخ 2026-11-11	رقم اللوحة W-02 (2/15)

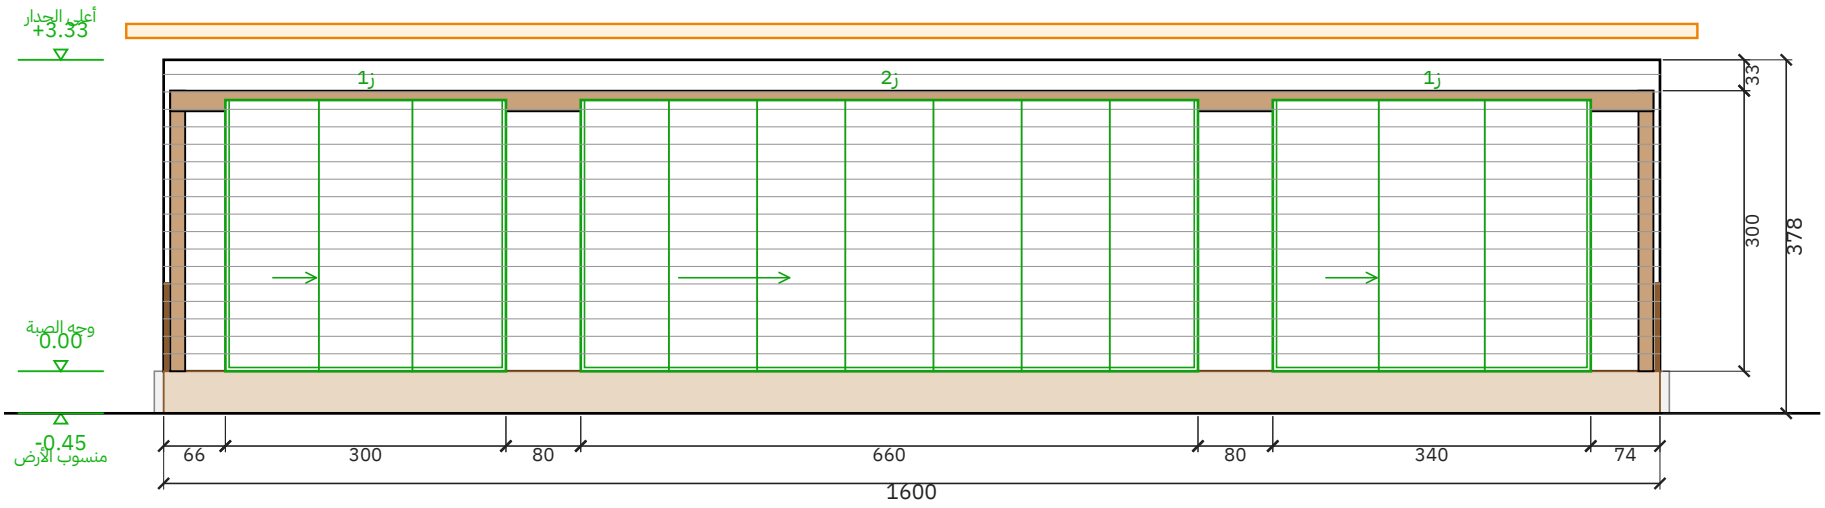

الواجهة الأمامية (على التراس)

مقياس 1:50 | الوحدة: سم

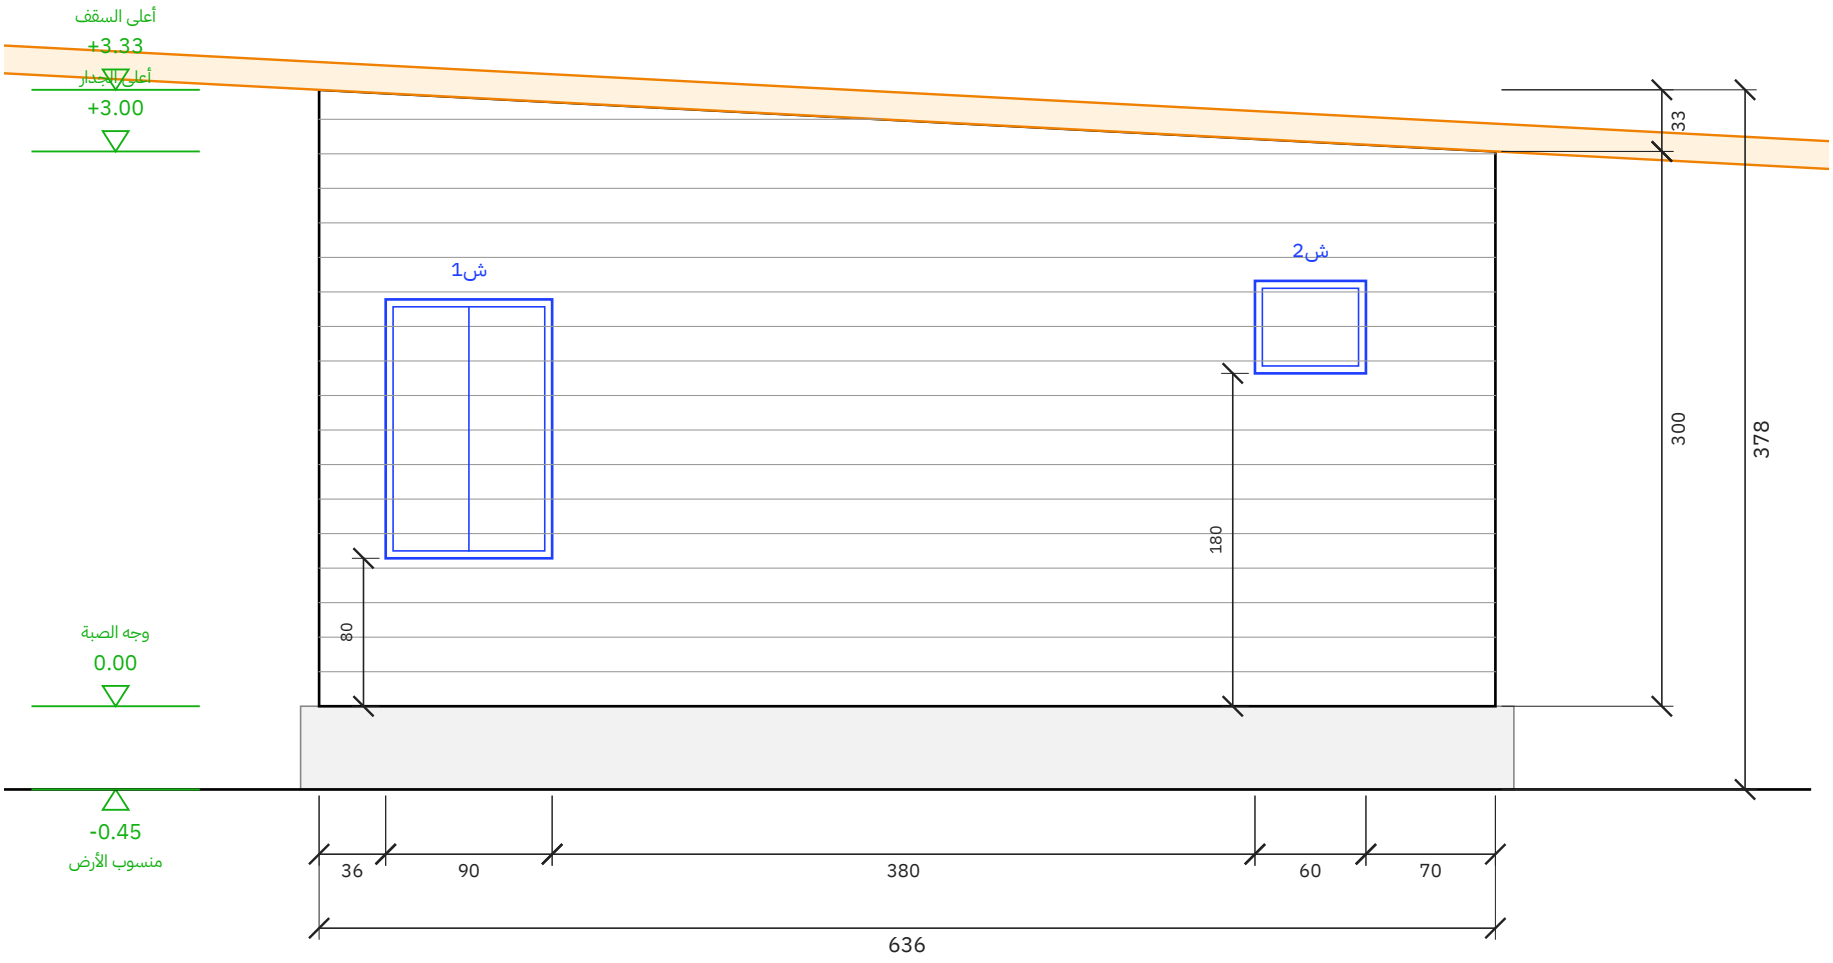


الواجهة الشرقية

مقياس 1:50 | الوحدة: سم


المشروع / العميل	عنوان اللوحة	المقياس	التاريخ	رقم اللوحة
كوخ الرياض 16.00 × 6.36 م — غرفتين نوم + صالة + حمامين + تراس أمامي 4.00 وخلفي 2.00 **عميل — الرياض**	**الواجهة الأمامية (على التراس) والواجهة الشرقية**	**1:50**	**2026-11-11**	**W-03 (3/15)**

مصنع وتد الأخشاب
Watad Wood Factory

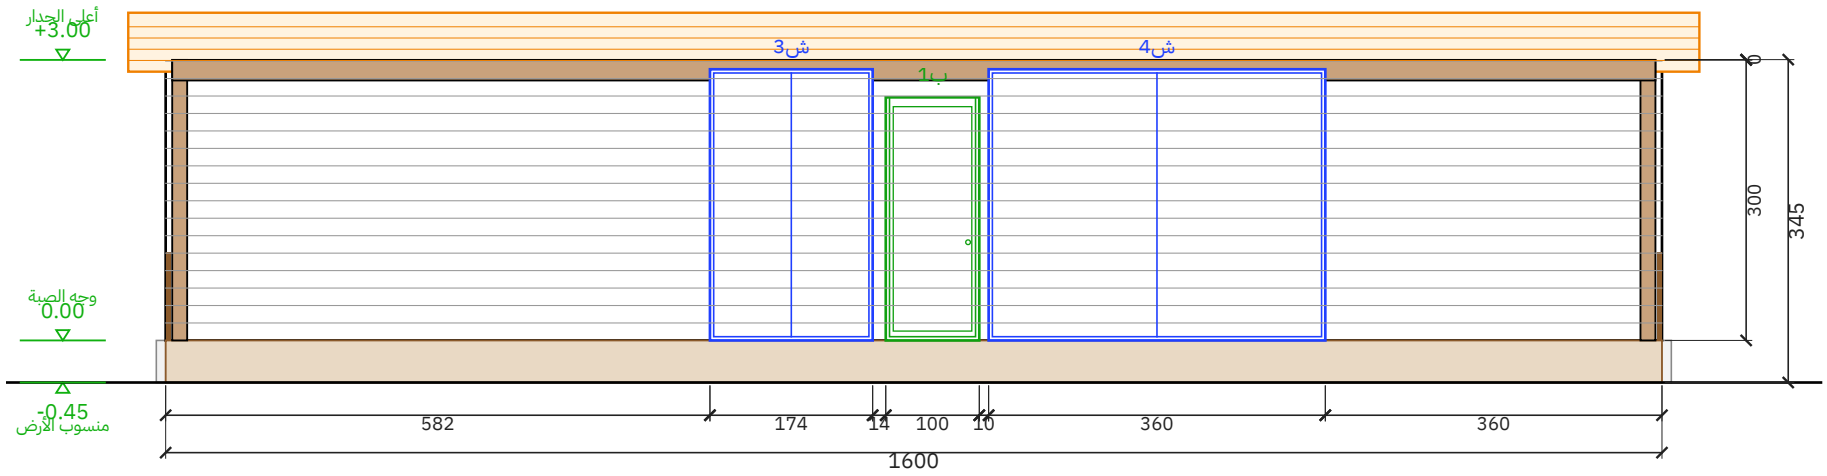

الواجهة الخلفية (المدخل)

مقياس 1:50 | الوحدة: سم

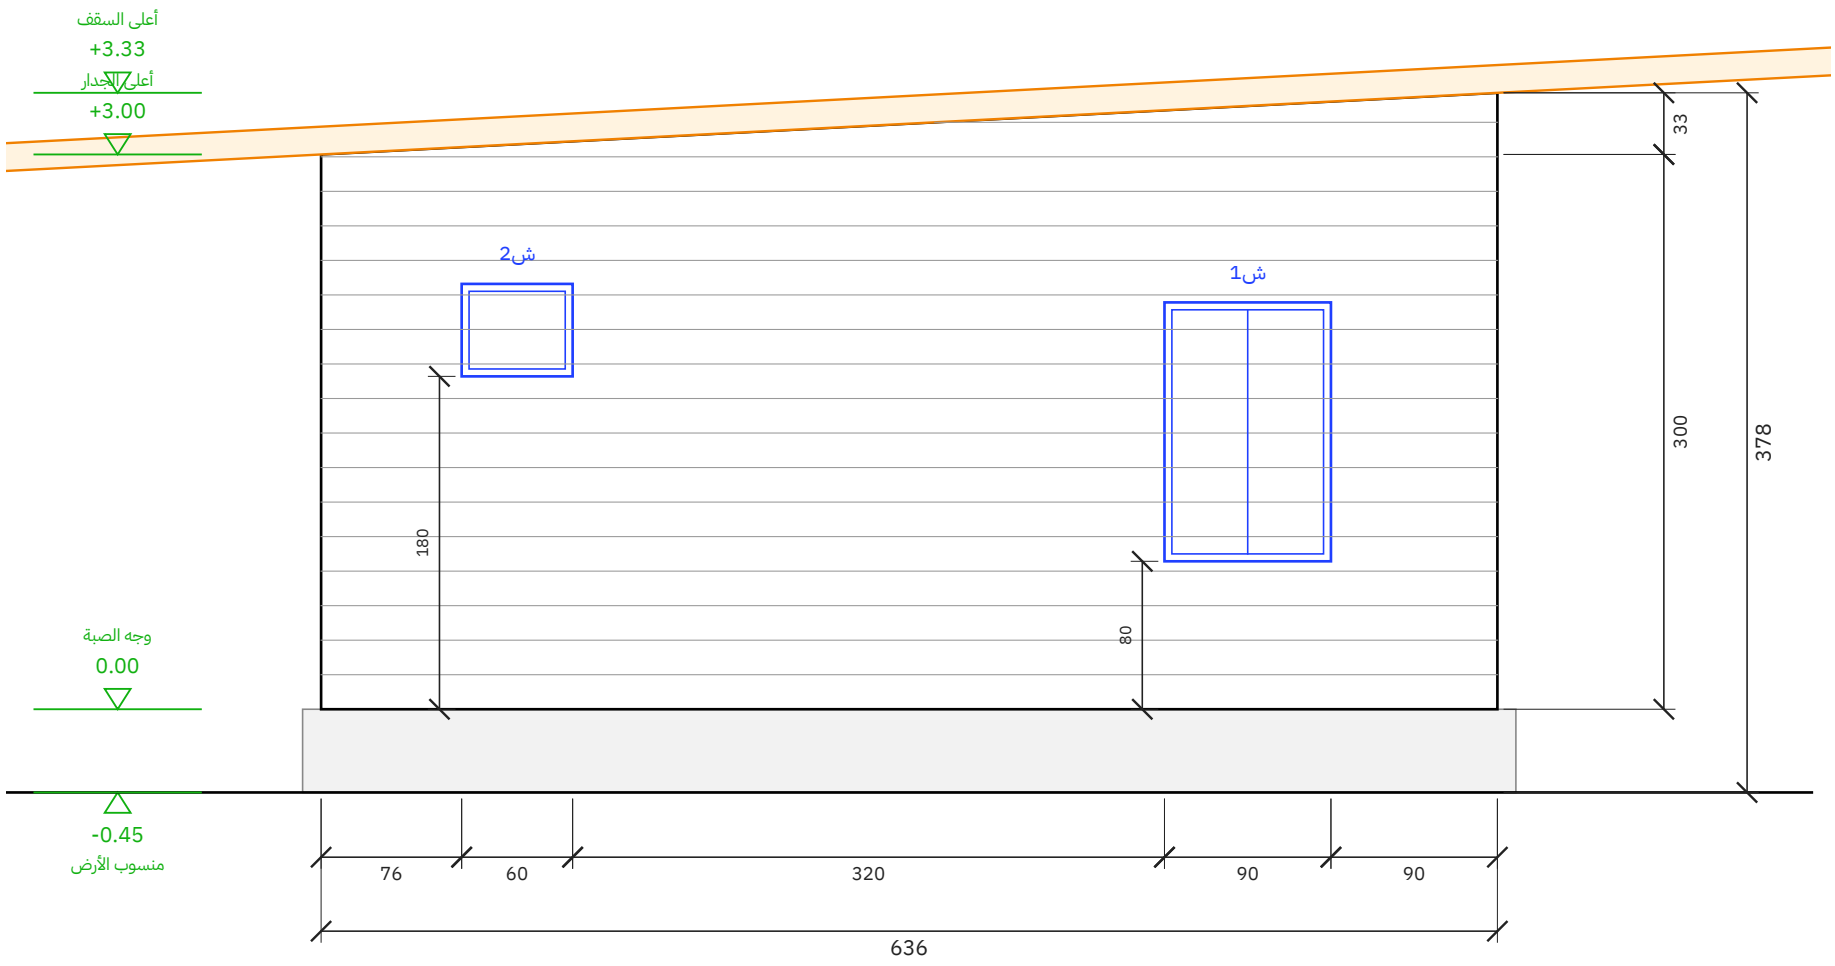

الواجهة الغربية


مقياس 1:50 | الوحدة: سم

المشروع / العميل	عنوان اللوحة	المقياس	التاريخ	رقم اللوحة
دوح الرياض 16.00 × 6.36 م — غرفتين نوم + صالة + حمامين + تراس أمامي 4.00 وخلفي 2.00 **عميل — الرياض**	**الواجهة الخلفية (المدخل) والواجهة الغربية**	**1:50**	**2026-11-11**	**W-04 (4/15)**

مصنع وتد الأخشاب
Watad Wood Factory


مسقط السقف (مائل باتجاه واحد)

رفرف 40 سم من كل جهة | مقياس 1:50

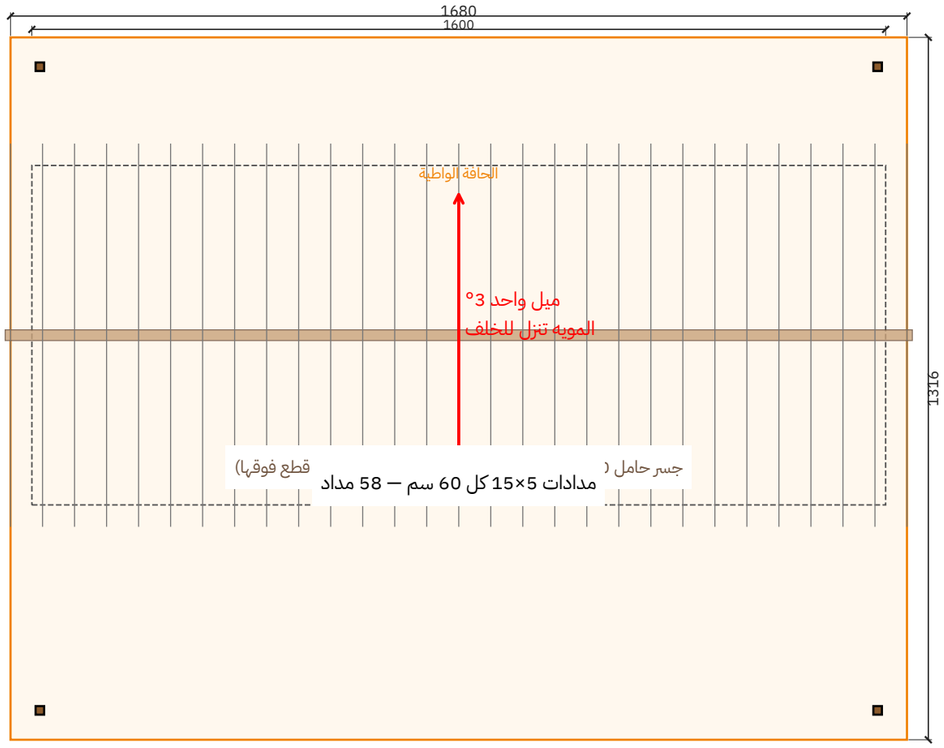


قطاع عرضي أ-أ

مقياس 1:50 | الوحدة: سم

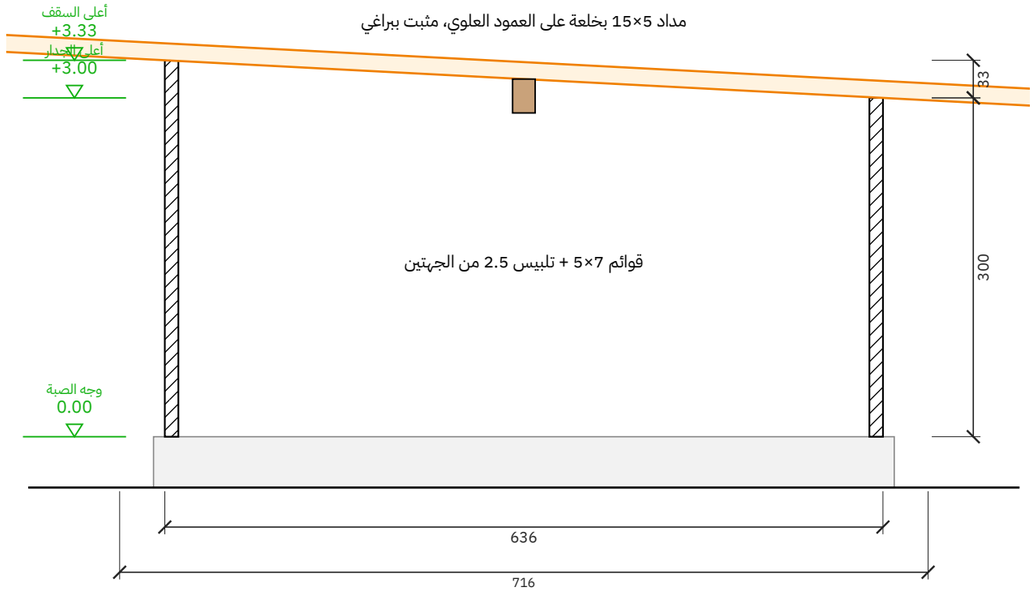

تفصيلة جلوس المداد على العلوي (1:5)

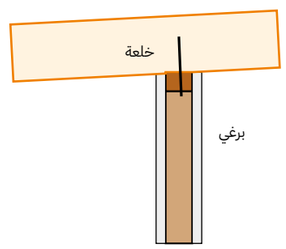

علوي 7×5 على قائم 7×5

المشروع / العميل **كوخ الرياض 16.00 × 6.36 م — غرفتين نوم + صالة + حمامين + تراس أمامي 4.00 وخلفي 2.00** **عميل — الرياض**	عنوان اللوحة **مسقط السقف والقطاع**	المقياس **1:50**	التاريخ **2026-11-11**	رقم اللوحة **W-05 (5/15)**

مصنع وتد الأخشاب
Watad Wood Factory

جدول مقاسات الأبواب والشبابيك

مقاس الفتحة الصافي في الجدار - الوحدة: سم

الرمز	النوع	العرض (سم)	الارتفاع (سم)	ارتفاع الجلسة (سم)	العدد	الموقع
ب1	باب	100	260	-	1	الخلفية (المدخل)
ب2	باب	85	220	-	1	غرفة الأطفال
ب3	باب	70	210	-	1	حمام الأطفال
ب4	باب	90	220	-	1	غرفة النوم الرئيسية
ب5	باب	70	210	-	1	الحمام الخاص
ز1	باب مزدوج	300	290	-	1	الأمامية (على التراس)
ز1	باب مزدوج	340	290	-	1	الأمامية (على التراس)
ز2	باب	660	290	-	1	الأمامية (على التراس)
ف1	باب	66	220	-	1	خزانة غرفة الأطفال
ف2	باب	80	220	-	1	غرفة الملابس
ش1	شباك	90	140	80	2	الشرقية - الغربية
ش2	شباك	60	50	180	2	الشرقية - الغربية
ش3	شباك	174	290	0	1	الخلفية (المدخل)
ش4	شباك	360	290	0	1	الخلفية (المدخل)

الإجمالي: أبواب 10 - شبابيك 6

جدول المساحات وبيانات المشروع


بيانات المشروع

البند	البيان
المشروع	كوخ الرياض 16.00 × 6.36 م — غرفتين نوم + صالة + حمامين + تراس أمامي 4.00 وخلفي 2.00
العميل	عميل — الرياض
الموقع	الرياض
الاستخدام	سكني
التاريخ	2026-11-11
نظام البناء	هيكل خشب 5×7 + تلبيس 2.5 سم من الجهتين
السقف	مائل باتجاه واحد 3° — صاج معدني + عزل مائي


جدول المساحات

م	الفراغ	الأبعاد (م)	المساحة (م2)
1	غرفة نوم الأطفال	4.00 × 4.00	16.00
2	حمام الأطفال	2.40 × 2.00	4.80
3	خزانة	0.76 × 2.00	1.52
4	الصالة	7.02 × 4.00	28.08
5	المطبخ والممر	6.72 × 2.00	13.44
6	غرفة ملابس	2.40 × 2.00	4.80
7	حمام خاص	3.00 × 2.00	6.00
8	غرفة النوم الرئيسية	4.50 × 4.00	18.00
	المساحة الصافية الداخلية		92.64
	المساحة الإجمالية المبنية	**16.00 × 6.36**	**101.76**
	التراس الأمامي (خارج مساحة الكوخ)	**16.00 × 4.00**	**64.00**
	التراس الخلفي (خارج مساحة الكوخ)	**16.00 × 2.00**	**32.00**

تأطير جدار جنوب — الطول 1588 سم، الارتفاع 333 سم

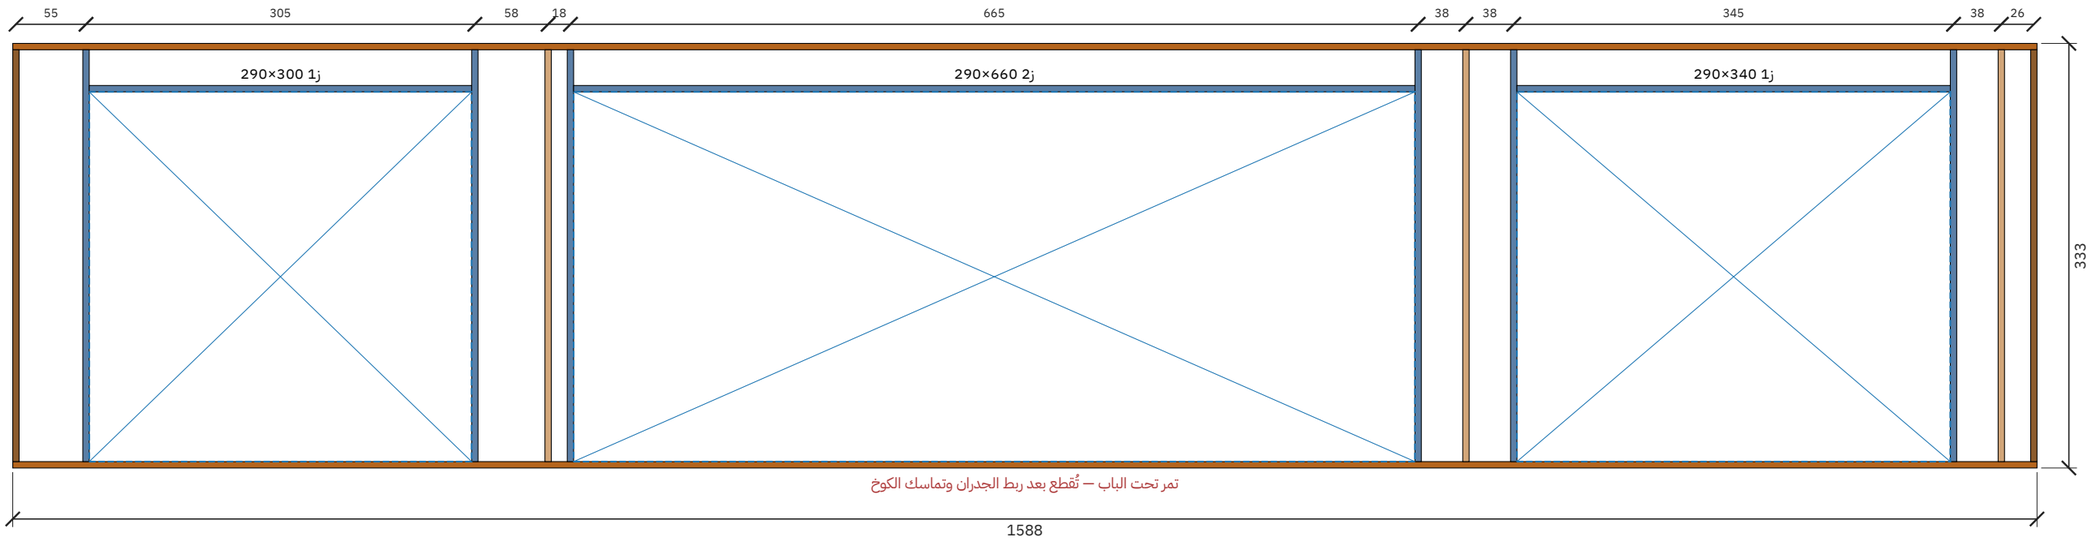


تأطير جدار شرق — الطول 624 سم، الارتفاع 300 سم

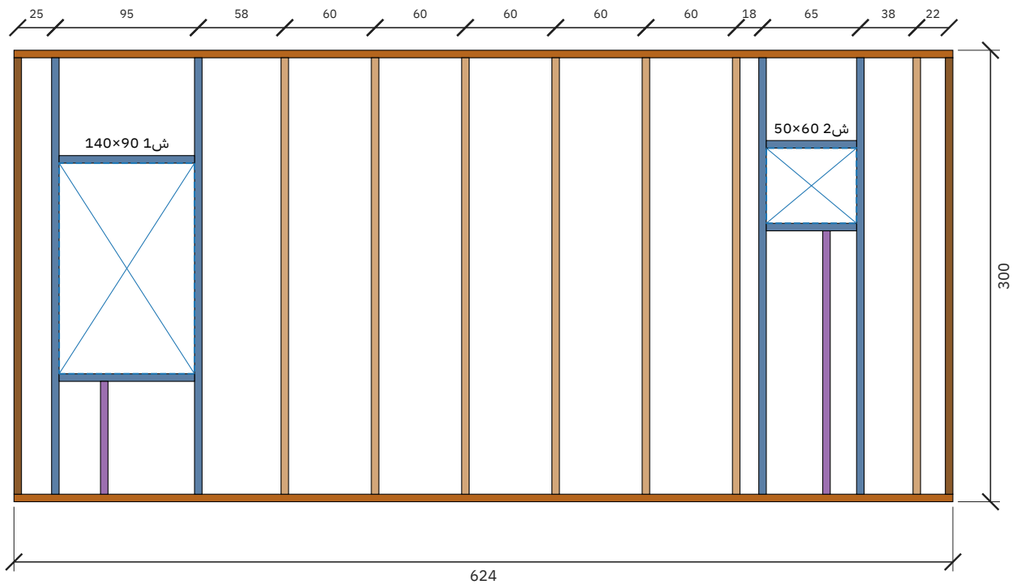


قاعدة سفلية | علوي | عمود | عمود زاوية | جنب فتحة | رأس فتحة | جلسة شباك | عمود قصير

مصنع وتد الأخشاب Watad Wood Factory	المشروع / العميل كوخ الرياض 16.00 × 6.36 م – غرفتين نوم + صالة + حمامين + تراس أمامي 4.00 وخلفي 2.00 عميل – الرياض	عنوان اللوحة لوحات التأطير (للورشة)	المقياس –	التاريخ 2026-11-11	رقم اللوحة W-08 (8/15)

تأطير جدار شمال — الطول 1588 سم، الارتفاع 300 سم

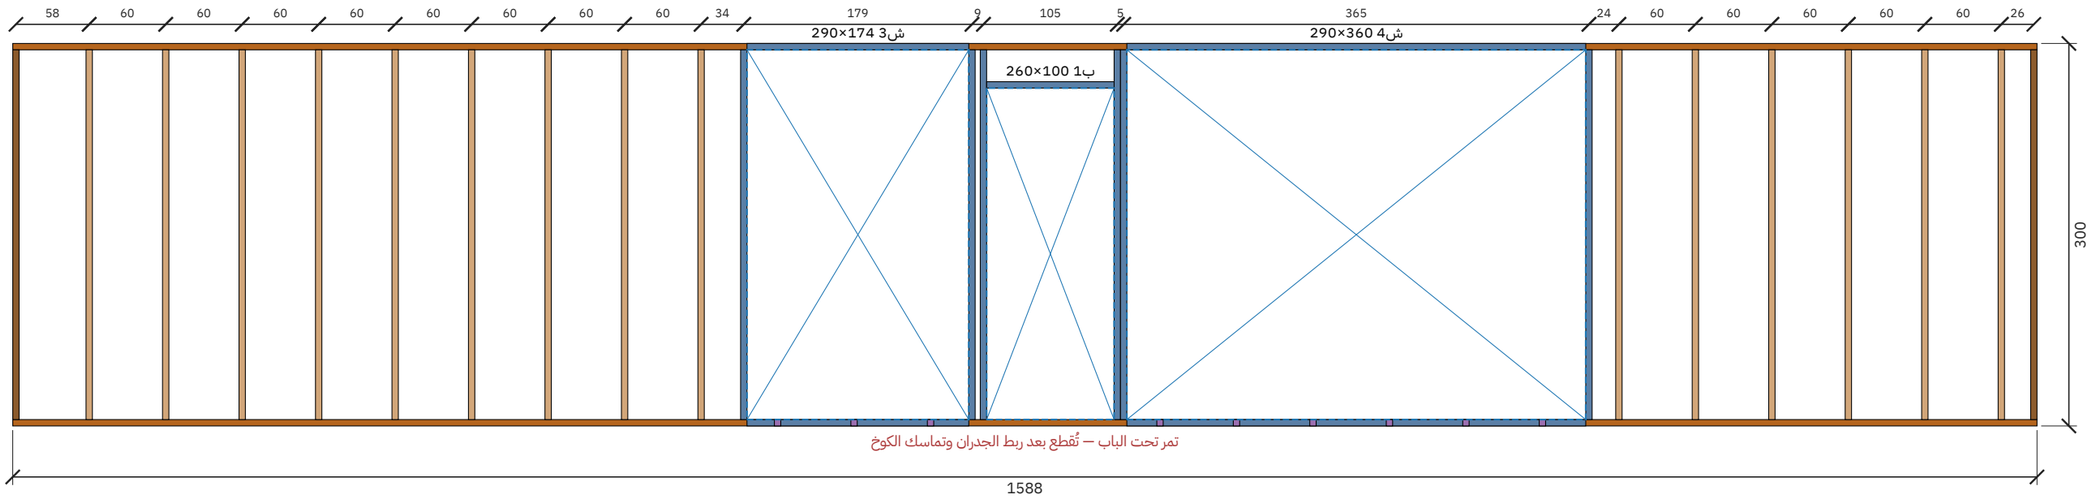


تأطير جدار غرب — الطول 624 سم، الارتفاع 300 سم

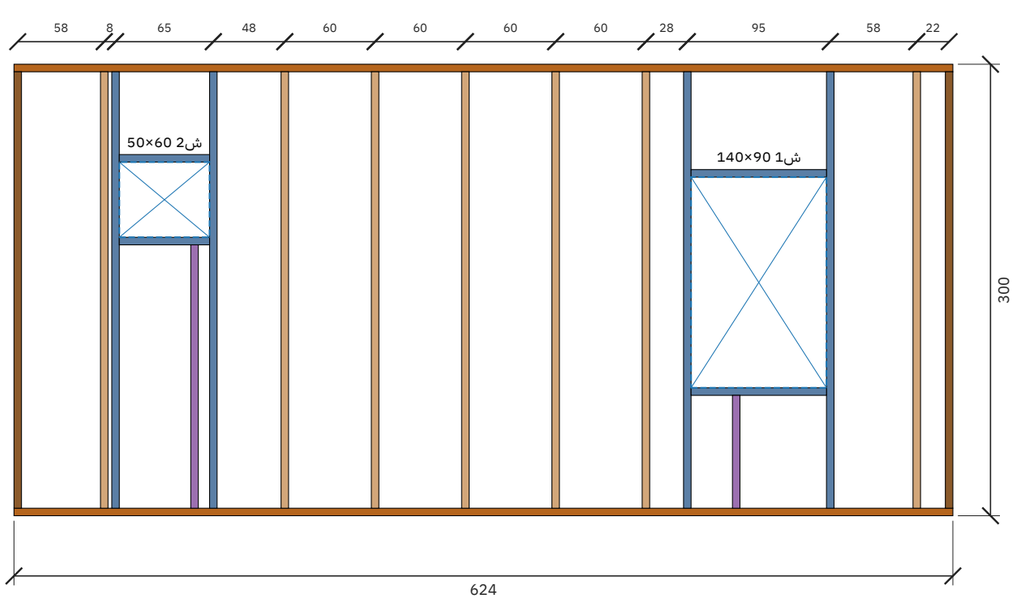


قاعدة سفلية | علوي | عمود | عمود زاوية | جنب فتحة | رأس فتحة | جلسة شباك | عمود قصير

مصنع وتد الأخشاب Watad Wood Factory	المشروع / العميل كوخ الرياض 16.00 × 6.36 م — غرفتين نوم + صالة + حمامين + تراس أمامي 4.00 وخلفي 2.00 عميل — الرياض	عنوان اللوحة لوحات التأطير (للورشة)	المقياس —	التاريخ 2026-11-11	رقم اللوحة W-09 (9/15)

تأطير جدار جدار غرفة الأطفال — الصالة — الطول 412 سم، الارتفاع 300 سم (داخلي)

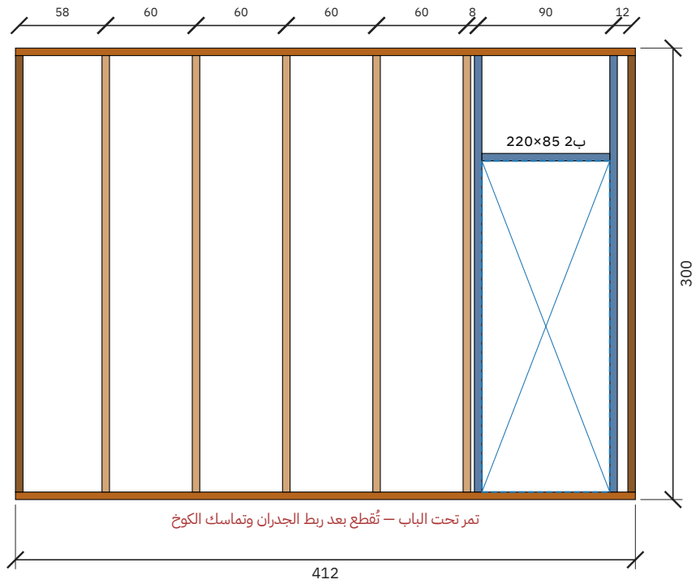


تأطير جدار جدار غرفة الأطفال — الحمام — الطول 412 سم، الارتفاع 300 سم (داخلي)

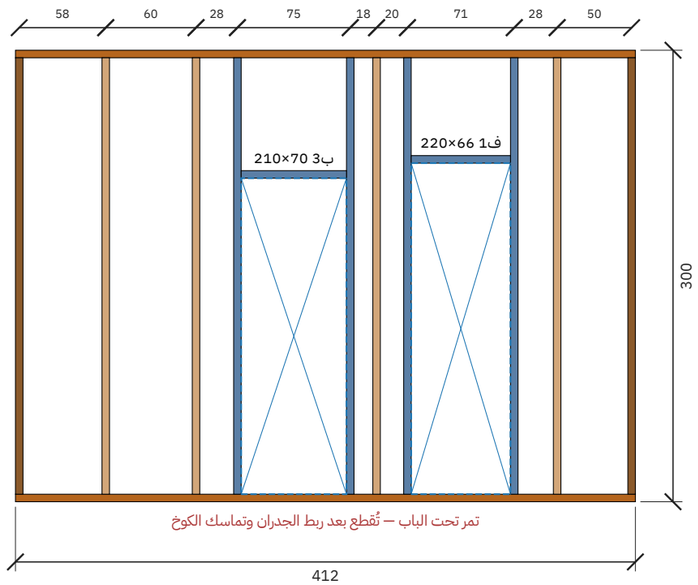


عمود قصير | جلسة شباك | رأس فتحة | جنب فتحة | عمود زاوية | عمود | علوي | قاعدة سفلية

مصنع وتد الأخشاب Watad Wood Factory	المشروع / العميل كوخ الرياض 16.00 × 6.36 م — غرفتين نوم + صالة + حمامين + تراس أمامي 4.00 وخلفي 2.00 عميل — الرياض	عنوان اللوحة لوحات التأطير (للورشة)	المقياس —	التاريخ 2026-11-11	رقم اللوحة W-10 (10/15)

تأطير جدار جدار حمام الأطفال — الخزانة — الطول 212 سم، الارتفاع 300 سم (داخلي)

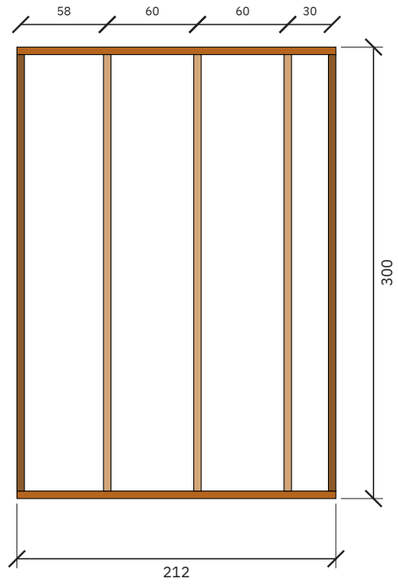


تأطير جدار جدار الخزانة — المطبخ — الطول 212 سم، الارتفاع 300 سم (داخلي)

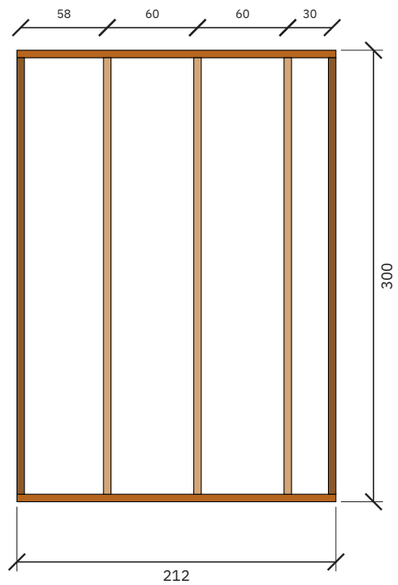


قاعدة سفلية | علوي | عمود | عمود زاوية | جنب فتحة | رأس فتحة | جلسة شباك | عمود قصير

مصنع وتد الأخشاب Watad Wood Factory	المشروع / العميل كوخ الرياض 16.00 × 6.36 م — غرفتين نوم + صالة + حمامين + تراس أمامي 4.00 وخلفي 2.00 عميل — الرياض	عنوان اللوحة لوحات التأطير (للورشة)	المقياس —	التاريخ 2026-11-11	رقم اللوحة W-11 (11/15)

تأطير جدار جدار الغرفة الرئيسية — الصالة — الطول 412 سم، الارتفاع 300 سم (داخلي)

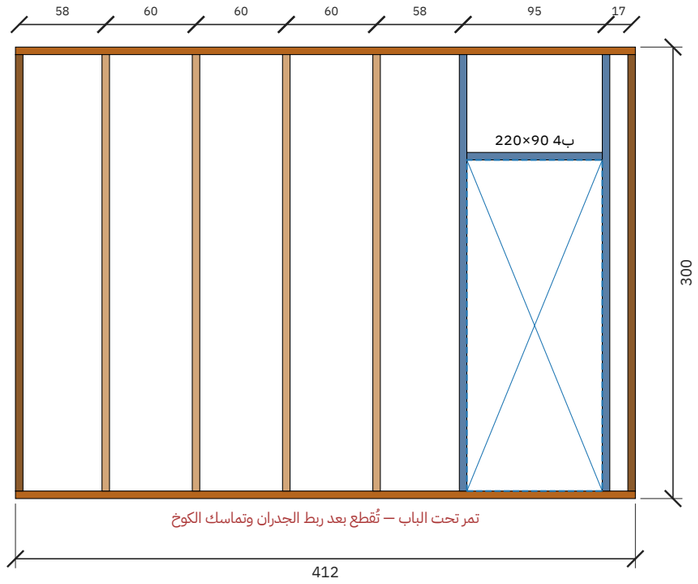


تأطير جدار جدار الغرفة الرئيسية — الملابس والحمام — الطول 564 سم، الارتفاع 300 سم (داخلي)

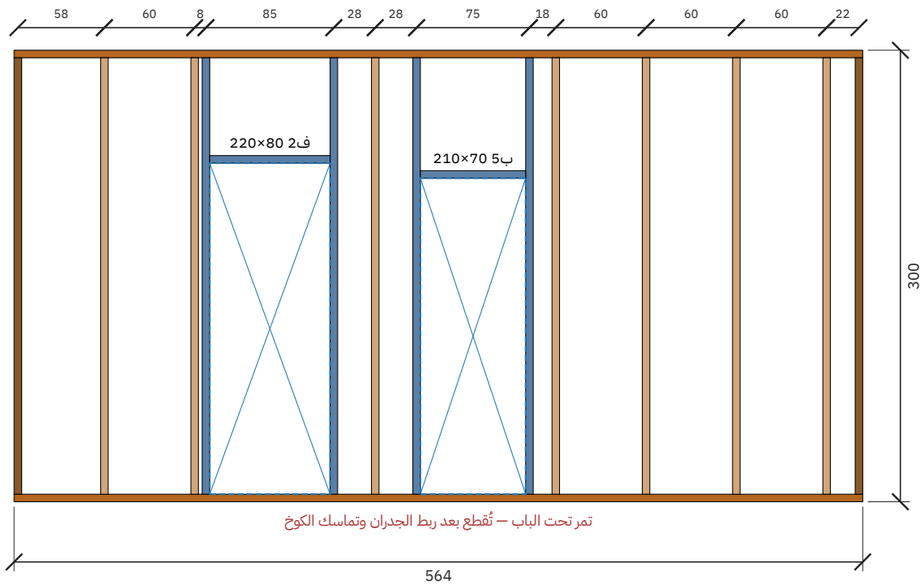


قاعدة سفلية | علوي | عمود | عمود زاوية | جنب فتحة | رأس فتحة | جلسة شباك | عمود قصير

مصنع وتد الأخشاب Watad Wood Factory	المشروع / العميل كوخ الرياض 16.00 × 6.36 م — غرفتين نوم + صالة + حمامين + تراس أمامي 4.00 وخلفي 2.00 عميل — الرياض	عنوان اللوحة لوحات التأطير (للورشة)	المقياس —	التاريخ 2026-11-11	رقم اللوحة W-12 (12/15)

تأطير جدار جدار الملابس — الصالة — الطول 212 سم، الارتفاع 300 سم (داخلي)

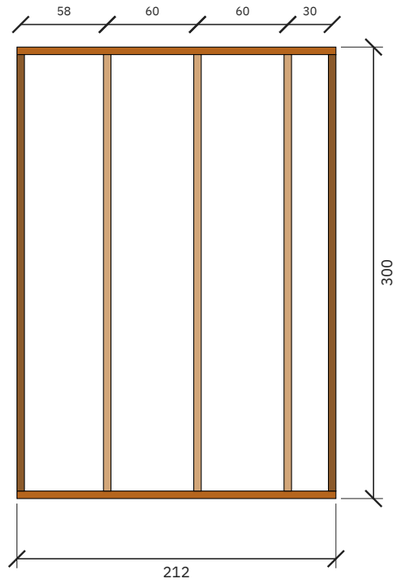

تأطير جدار جدار الملابس — الحمام — الطول 212 سم، الارتفاع 300 سم (داخلي)

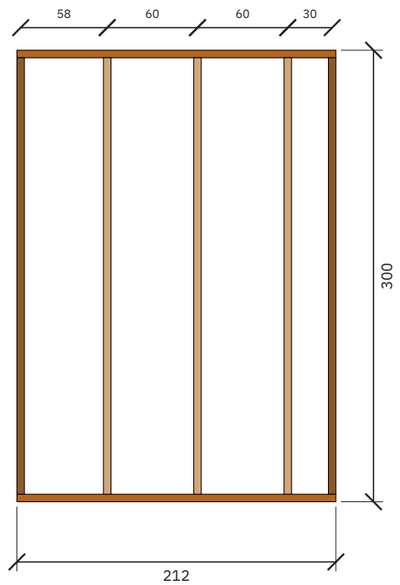

قاعدة سفلية | علوي | عمود | عمود زاوية | جنب فتحة | رأس فتحة | جلسة شباك | عمود قصير

مصنع وتد الأخشاب Watad Wood Factory	المشروع / العميل كوخ الرياض 16.00 × 6.36 م — غرفتين نوم + صالة + حمامين + تراس أمامي 4.00 وخلفي 2.00 عميل — الرياض	عنوان اللوحة لوحات التأطير (للورشة)	المقياس —	التاريخ 2026-11-11	رقم اللوحة W-13 (13/15)

جدول الكميات وخطة تقطيع الطبليات

البند	القيمة
الارتفاع المطلوب / المعتمد	300 / 300 سم
السقف	مائل باتجاه واحد 3° — أعلى نقطة 333 سم من وجه الصبة
المدادات 5×15	58 مداد (29 خط × قطعتين موصولة فوق الجسر الحامل بتراكب 60 سم) × حتى 388 سم — من طبلية 480
طبليات الطريقة الأولى (مداد + عمود)	58 طبلية × 480 سم
طبليات الطريقة الثانية (3 أعمدة)	37 طبلية × 320 سم
إجمالي الطبليات 5×22.5	95
إجمالي قطع 5×7	179
قائمة تقطيع 5×7	1588سم×4 | 660سم×1 | 624سم×4 | 564سم×2 | 412سم×6 | 360سم×2 | 340سم×1 | 323سم×11 | 300سم×1
	290سم×109 | 212سم×8 | 175سم×2 | 174سم×2 | 100سم×1 | 90سم×5 | 85سم×1 | 80سم×1 | 75سم×2
ألواح تلبيس 2.5 سم	417 لوح × 400 سم (مجموع الصفوف 1362.3 م، 24 وجه)
أسمنت بورد 12 مم (122×244)	36 لوح (داخل دورات المياه)
العزل	207 لوح فوم صخري 80
الصبة	يجهزها العميل — 20 سم، مفرغة تحت دورات المياه

مراجعة التصميم مقابل قواعد المصنع

النوع	البند	التفاصيل	المقترح
ملاحظة	بحر المدادات	أطول بحر بدون جدار داخلي يحمل المداد: جهة أ: 636 سم. يحتاج رقم المصنع لأقصى بحر مسموح لتحديد المدادات اللي تُقوّى 20×5.	
ملاحظة	الصبة والدرج	ارتفاع الصبة 45 سم ← 3 درجة بقائمة 15.0 سم.	
ملاحظة	مناسيب رؤوس الفتحات	رؤوس الأبواب والشبابيك على مناسيب مختلفة: 210، 220، 230، 260، 290 سم.	
تنبيه	ميل سقف خفيف (بموافقة المصنع)	ميل 3° أقل من 20° — يصرّف باتجاه واحد بس يحتاج تغطية صاج معدني (مو قرميد) وعزل مائي تحت الصاج ووصلات مختومة.	صاج معدني بطول واحد من الحافة العالية للواطية بدون وصلات عرضية.
سؤال	يحتاج تأكيد	أقصى بحر للمداد بدون جدار داخلي قبل إضافة تقوية 7×5 (مداد 20×5)؟	
سؤال	يحتاج تأكيد	التغطية الصافية للوح التلبيس بعد التعشيق (مستنتجة مؤقتاً 18.67 سم من 280/15)؟	
سؤال	يحتاج تأكيد	هل يوضع أعمدة قصيرة فوق رأس الشباك/الباب إلى العلوي؟	
سؤال	يحتاج تأكيد	مكان الوصلة في القاعدة والعلوي إذا الجدار أطول من الطبلية؟	