
مصنع وتد الأخشاب · ملف التصميم

محمية طيور

30.00 × 15.00 م · 450 م² · حديد مجلفن + شبك · سقف بولي كربونيت بيج · شلال وبحيرة · LED

المسقط الأفقي والتوزيع — محمية الطيور

الأبعاد بالمتر | الأعمدة كل 3.00 م بالطول و 3.75 م بالعرض

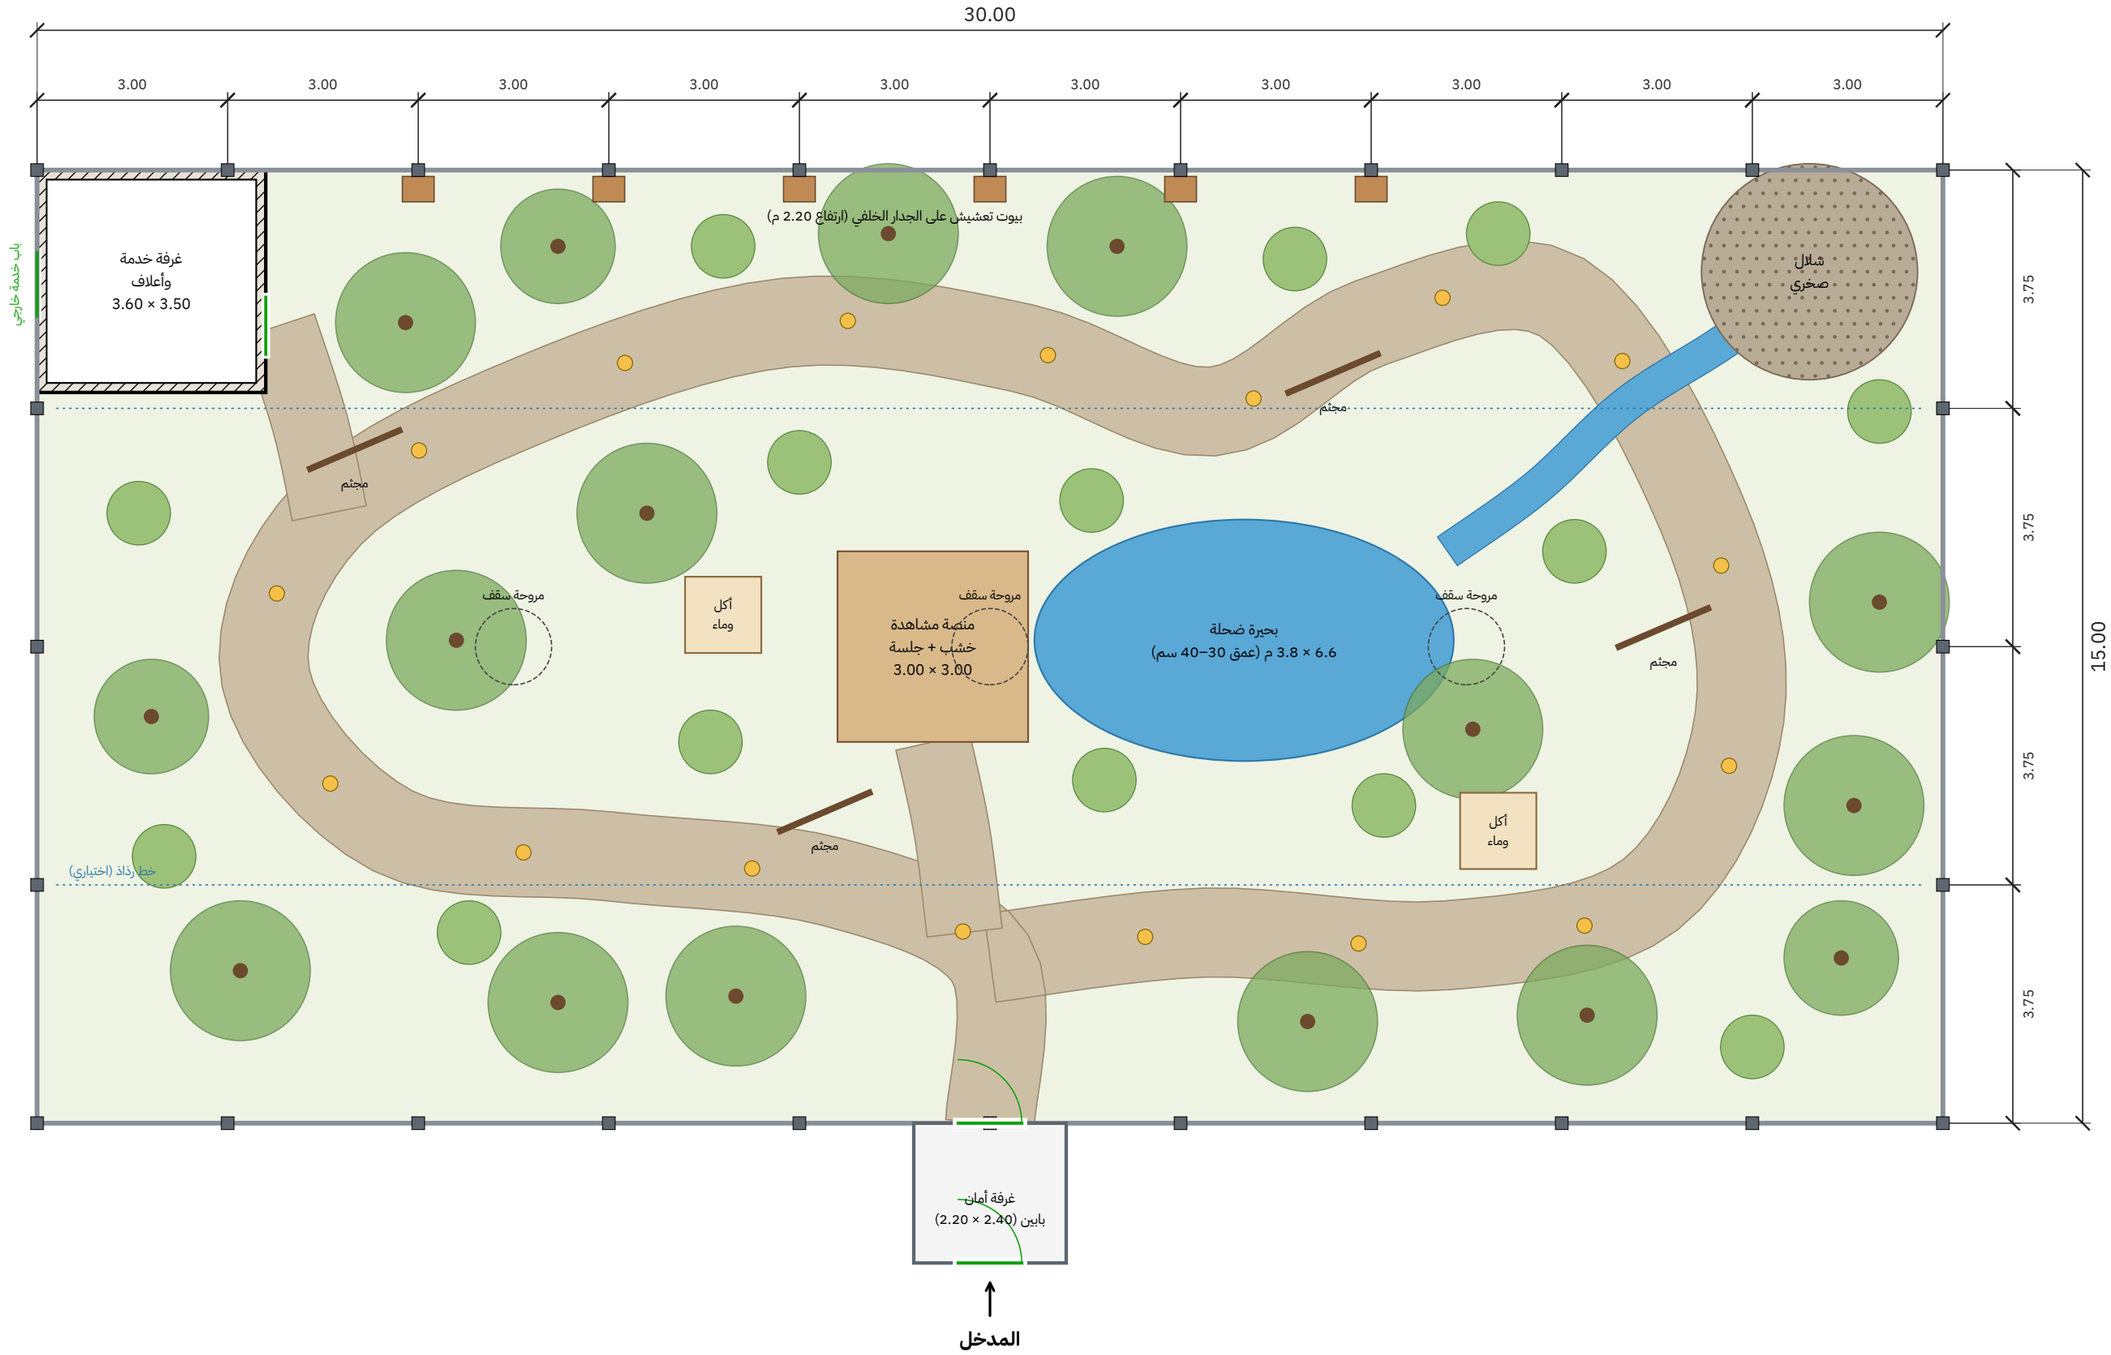


عرض الممر 1.40 م — حجر طبيعي على قاعدة رمل مدكوك


المشروع / العميل	عنوان اللوحة	المقياس	التاريخ	رقم اللوحة
محمية طيور — 30.00 × 15.00 م (450 م²) **مشروع — محمية طيور**	**المسقط الأفقي والتوزيع**	**1:100**	**2026-10-28**	**AV-01 (1/3)**

مصنع وتد الأخشاب
Watad Wood Factory


الواجهة الأمامية (الجنوبية) — المدخل

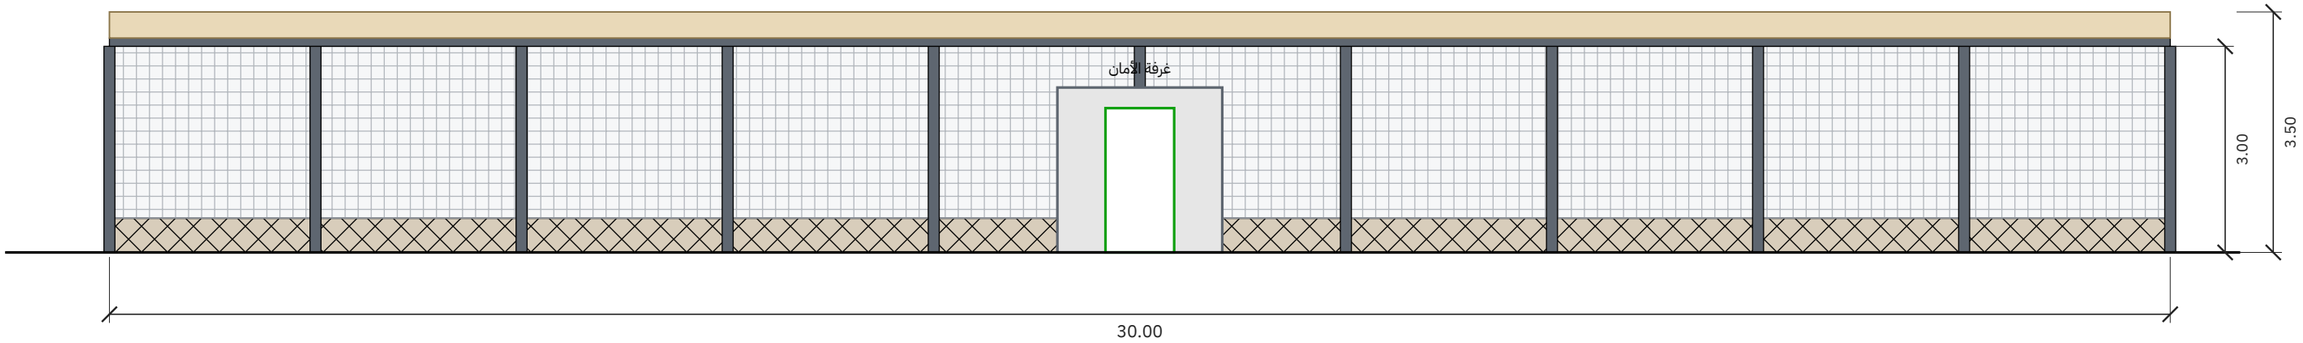

مقطع عرضي

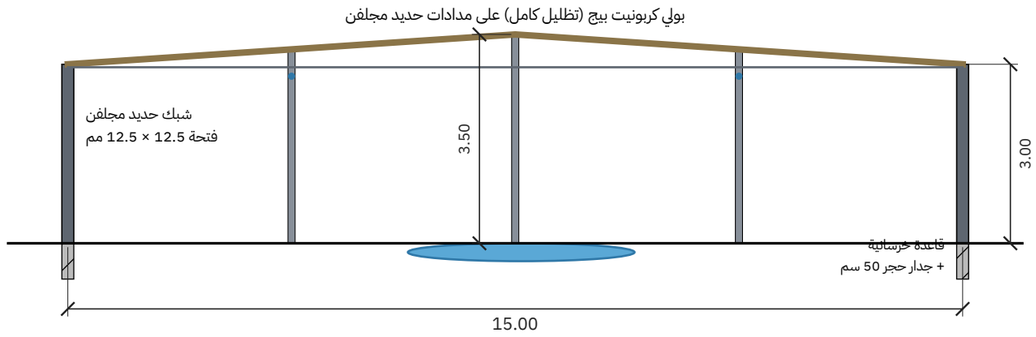

الواجهة الجانبية

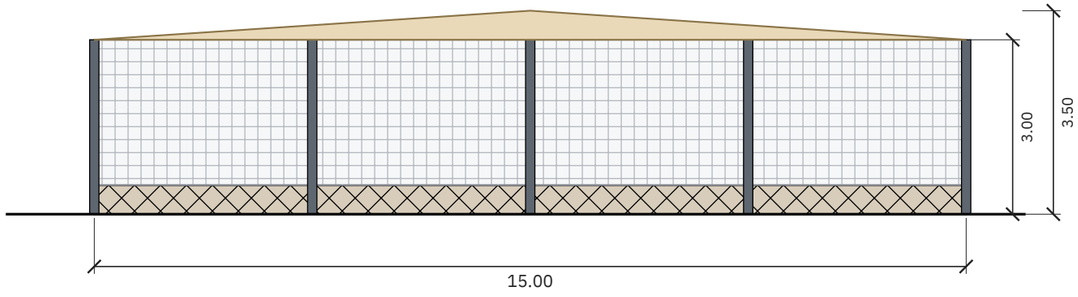


مصنع وتد الأخشاب Watad Wood Factory	المشروع / العميل **محمية طيور — 30.00 × 15.00 م (450 م²)** **مشروع — محمية طيور**	عنوان اللوحة **الواجهات والمقطع**	المقياس **1:100**	التاريخ **2026-10-28**	رقم اللوحة **AV-02 (2/3)**

مواصفات محمية الطيور

البند	المواصفات
المساحة الإجمالية	450 م² (30.00 × 15.00) + غرفة أمان 5.3 م²
ارتفاع السقف	3.00 م عند الأطراف — 3.50 م بالقمة (جملون منخفض يصرّف المطر)
الهيكل	تيوبات حديد مجلفن: أعمدة 100×100×3 مم كل 3.00 م، جسور 100×50، مدادات 50×50
الشبك	شبك حديد مجلفن ملحوم 12.5 × 12.5 مم (يمنع العصافير الصغيرة والثعابين)
القاعدة	قواعد خرسانية + جدار حجر 50 سم على المحيط (ضد الحفر والقوارض)
تغطية السقف	بولي كربونيت بيج متعدد الجدران 10 مم — تظليل كامل + شبك تحته
التهوية والتلطيف	3 مراوح سقف + خطين رذاذ ماء بطول 30 م (اختياري)
الماء	شلال صخري + مجرى 10 م + بحيرة ضحلة 6.6 × 3.8 م (30–40 سم) بمضخة وفلتر
الإضاءة	إنارة أرضية على الممر كل 3.2 م + شريط دافئ تحت الجسور + سبوت للشلال: LED
الزراعة	16 شجرة (برتقال، مانجو، نخل قزم) + 14 شجيرة بأحواض ري بالتنقيط
الممرات	ممر دائري حجر طبيعي عرض 1.40 م ≈ 75 م طولي + منصة مشاهدة خشب 3×3
مرافق الطيور	4 مجاثم جذوع + 2 محطة أكل مظللة + 6 بيوت تعشيش + حمّام رمل
الأمان	غرفة أمان بابين (ما ينفتح الباب الثاني إلا بعد قفل الأول) + غرفة خدمة بباب خارجي


منظر جوي – المحمية كاملة · الخارج – نهاراً

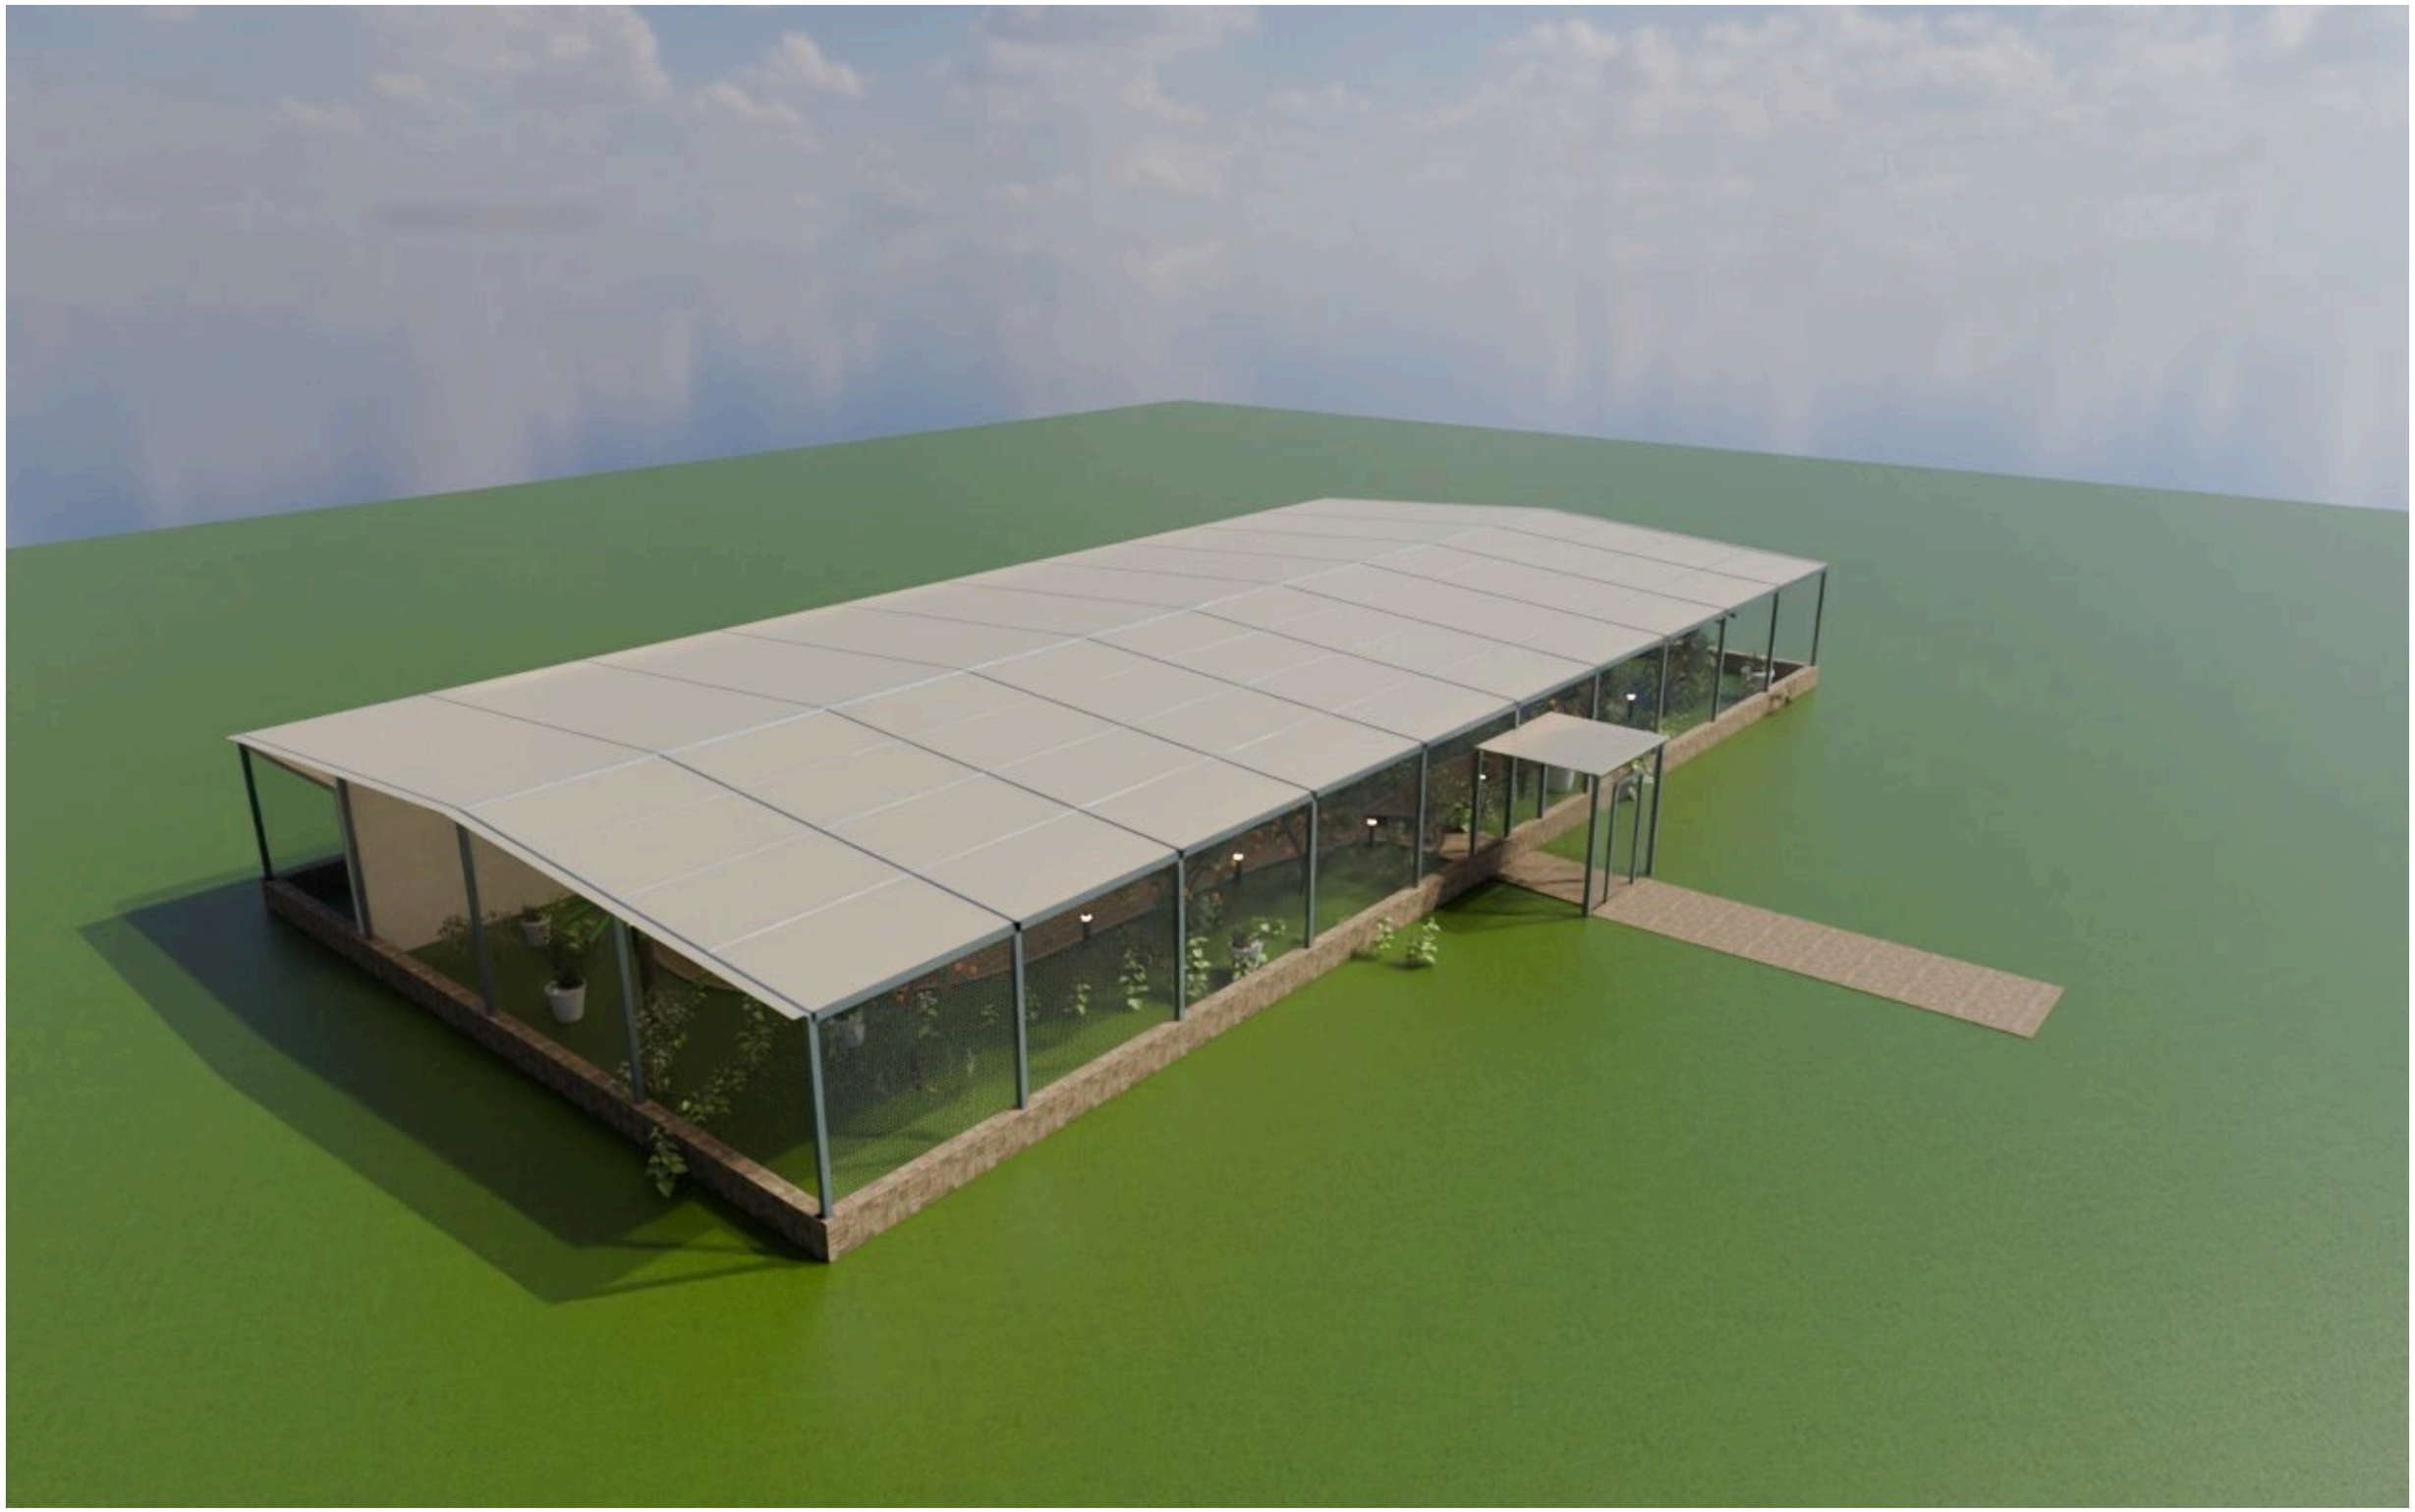

مصنع وتد الأخشاب



مصنع وتد الأخشاب

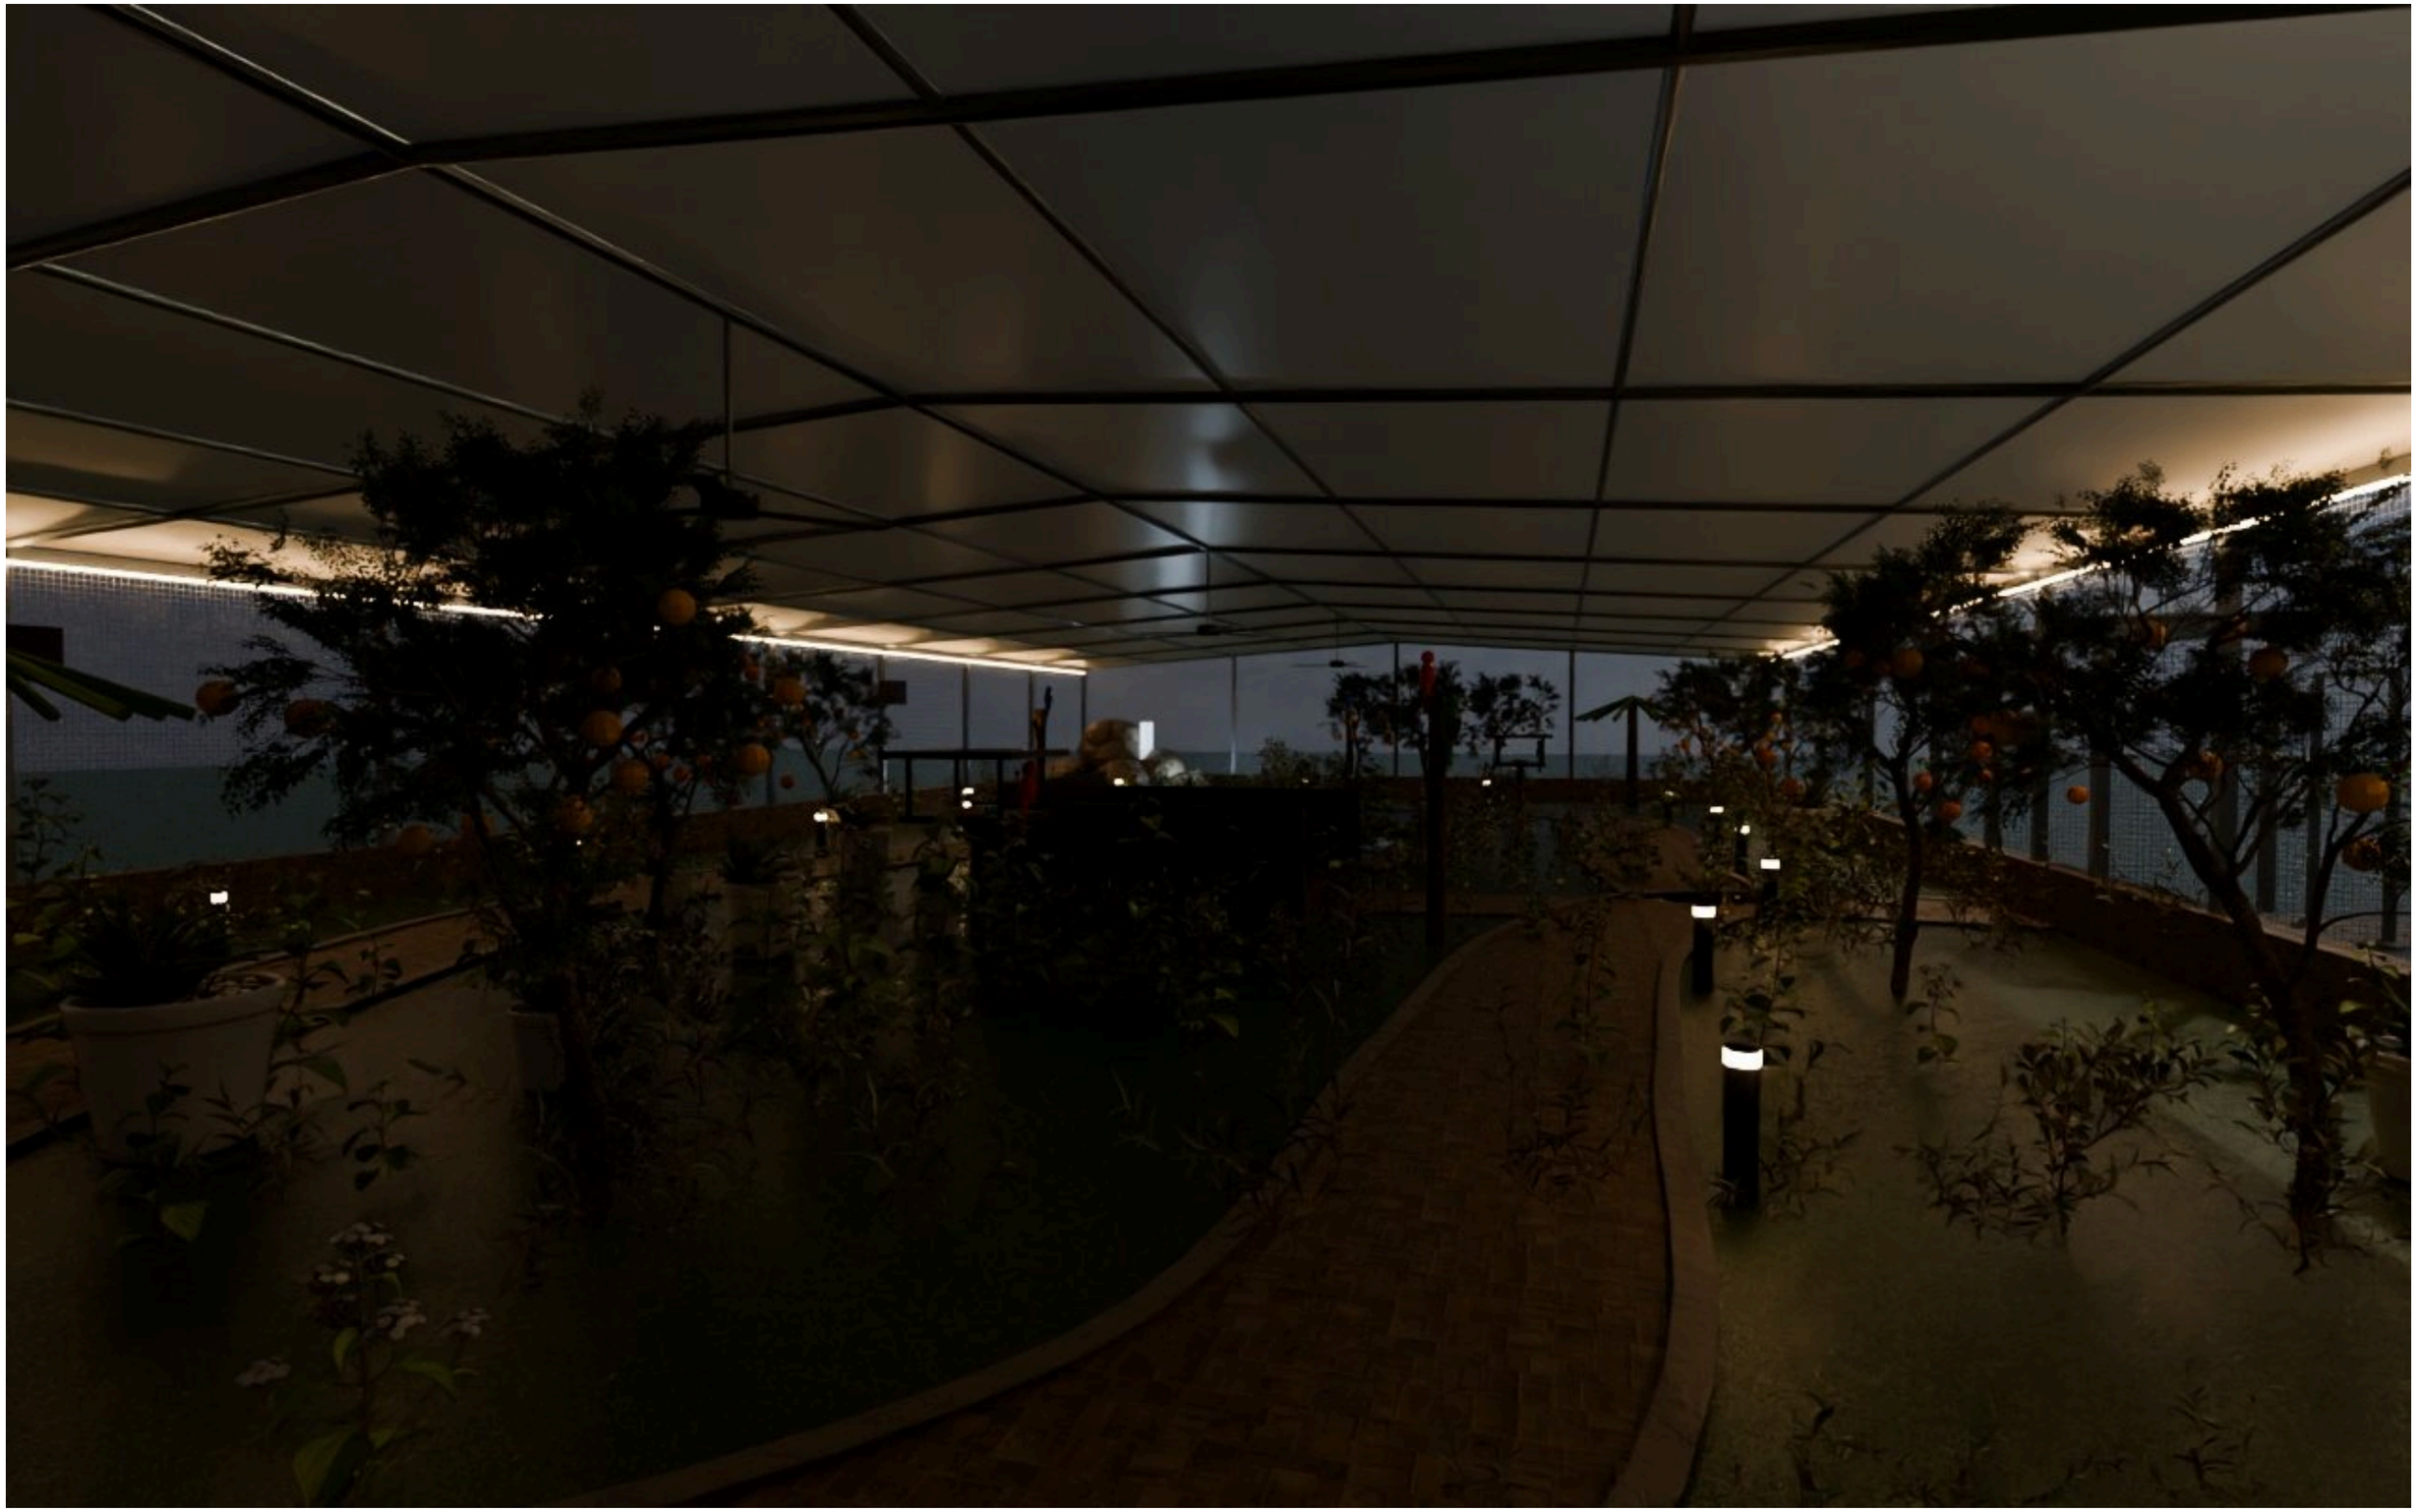

مصنع وتد الأخشاب



مصنع وتد الأخشاب



مصنع وتد الأخشاب



مصنع وتد الأخشاب