



[illegible]

المشروع / العمل	عنوان اللوحة	المقياس	التاريخ	رقم اللوحة
مصنع وتد الأخشاب Watad Wood Factory	كوخ غرفتين بواجهة زجاج – 76 م² عمل – تصميم رقم 5	المسقط الأفقي 1:50	2026-10-09	A-01 (1/9)

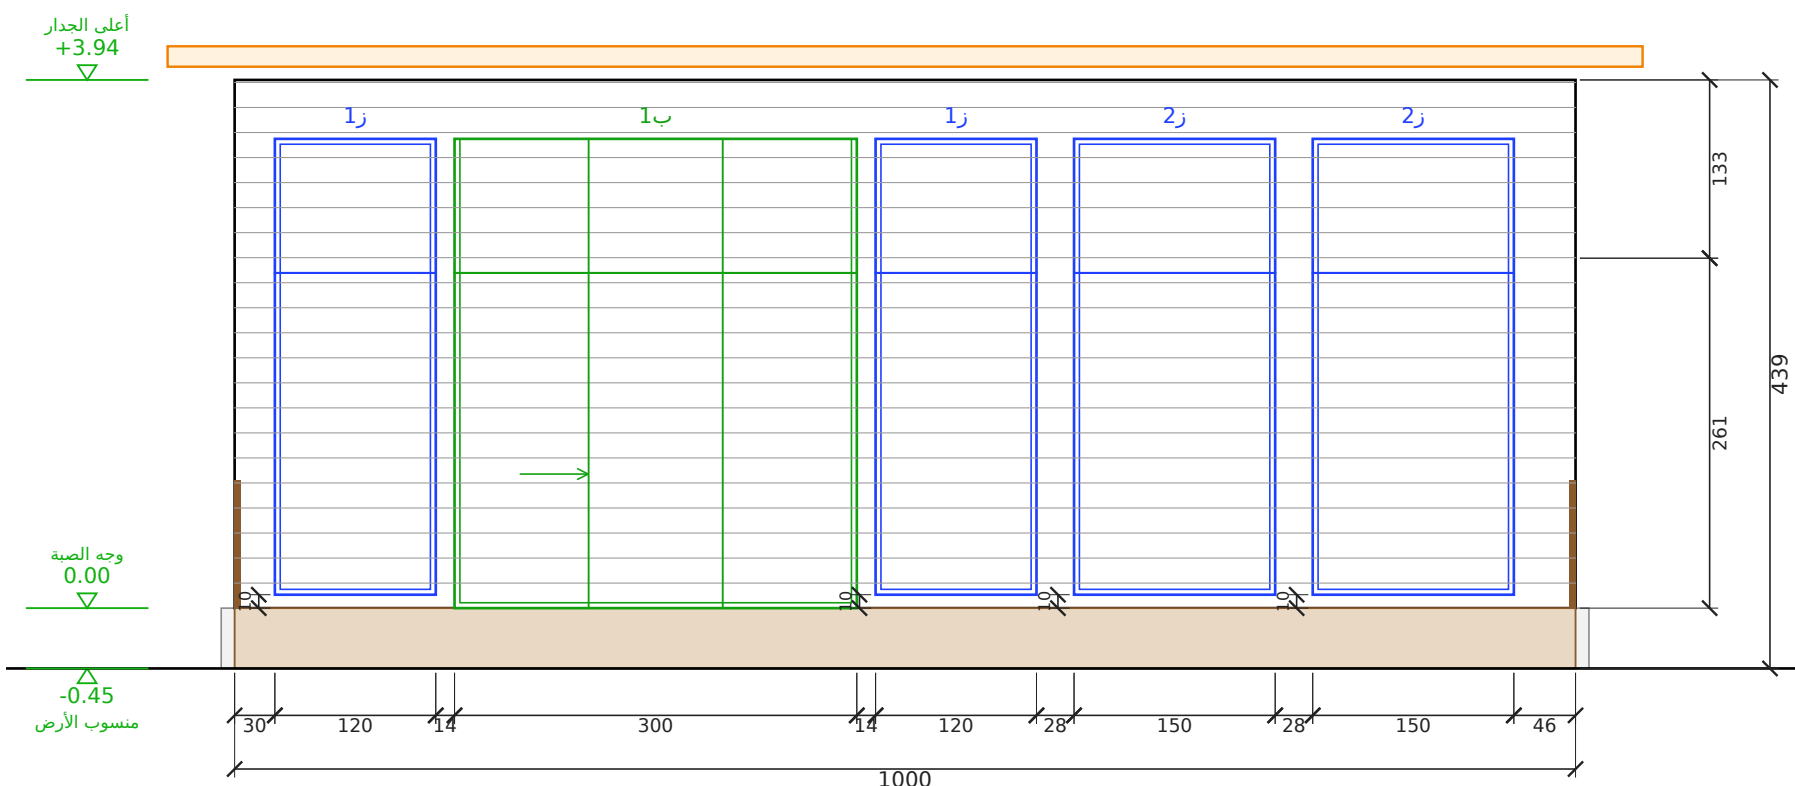

الواجهة الأمامية


مقياس 1:50 | الوحدة: سم

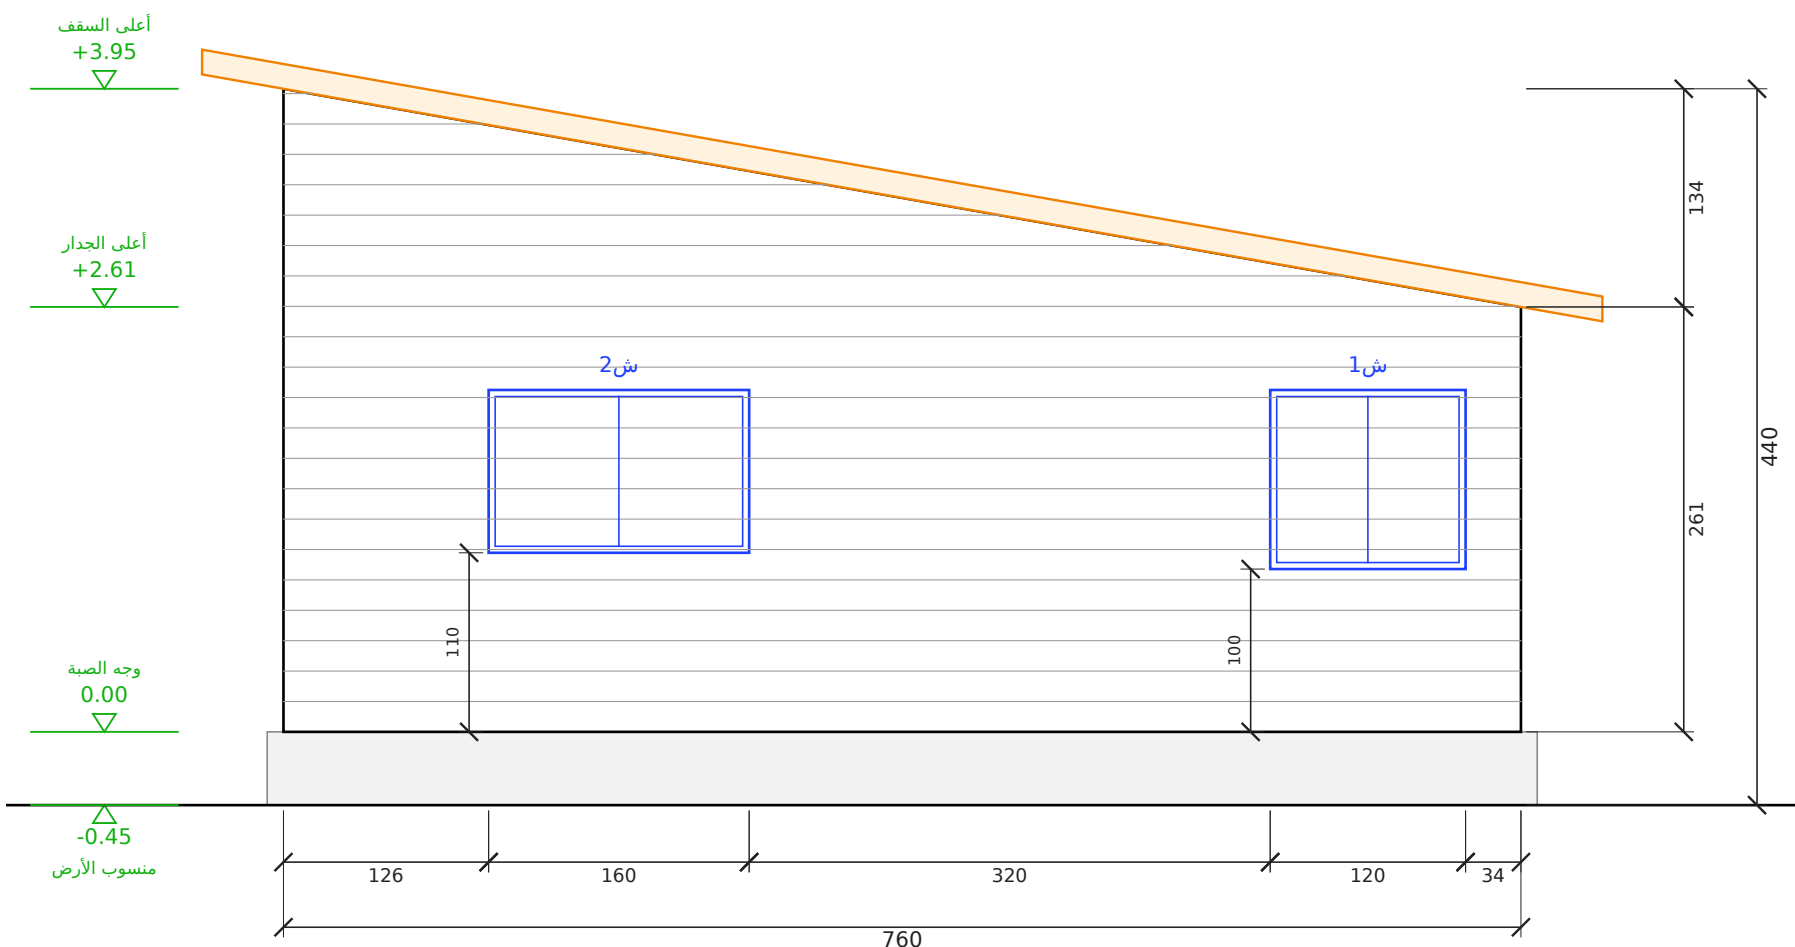

الواجهة الشرقية


مقياس 1:50 | الوحدة: سم

رقم اللوحة	التاريخ	المقياس	عنوان اللوحة	المشروع / العميل	مصنع وتد الأخشاب Watad Wood Factory
A-02 (2/9)	2026-10-09	1:50	الواجهة الأمامية والواجهة الشرقية	كوخ غرفتين بواجهة زجاج - 76 م ² عميل - تصميم رقم 5	

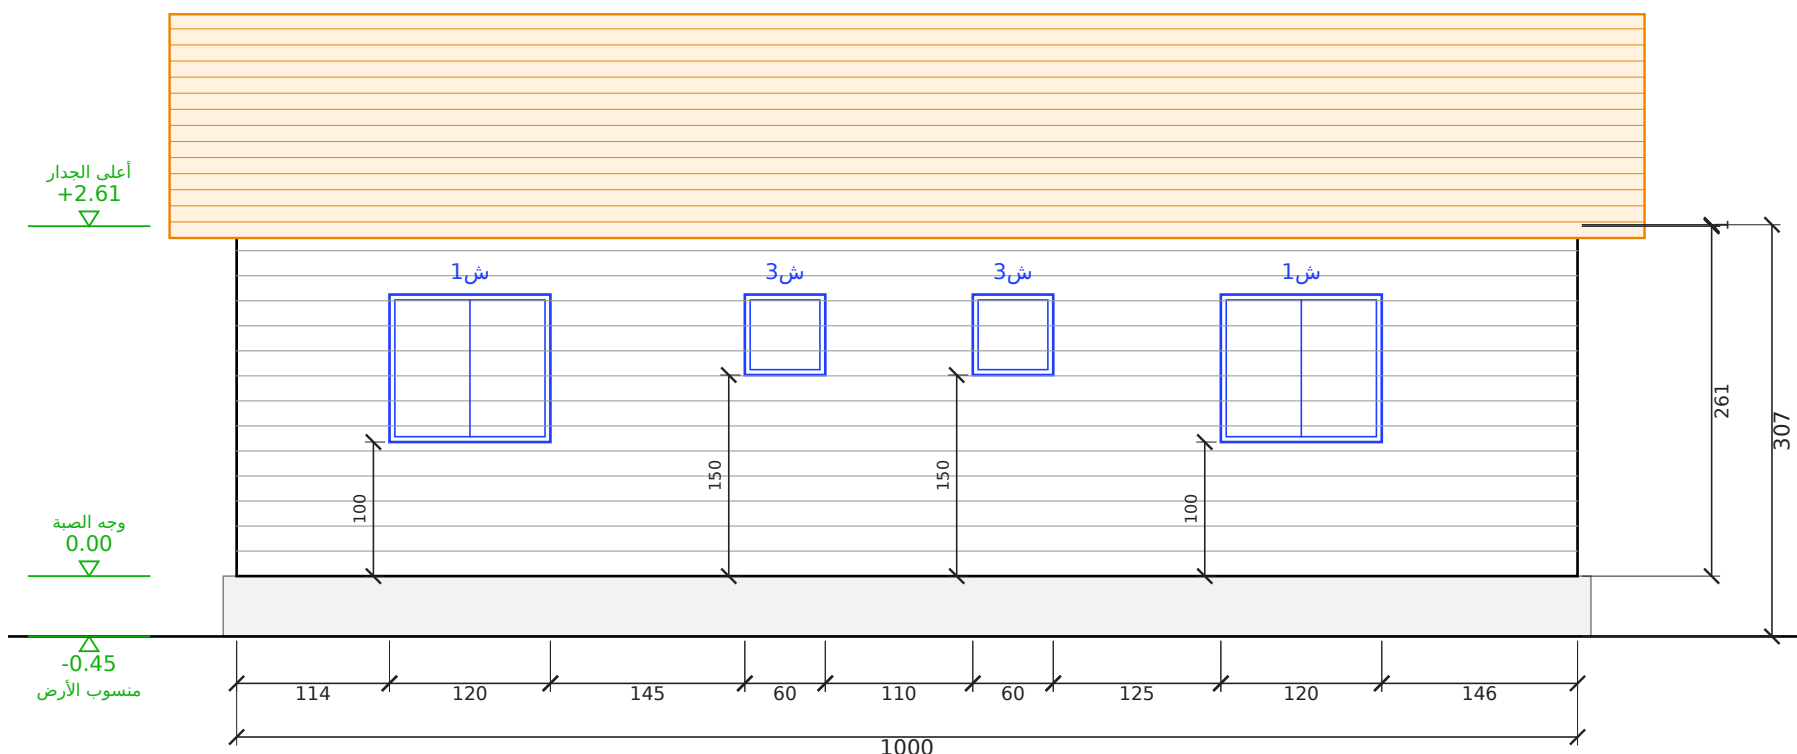

الواجهة الخلفية

مقياس 1:50 | الوحدة: سم

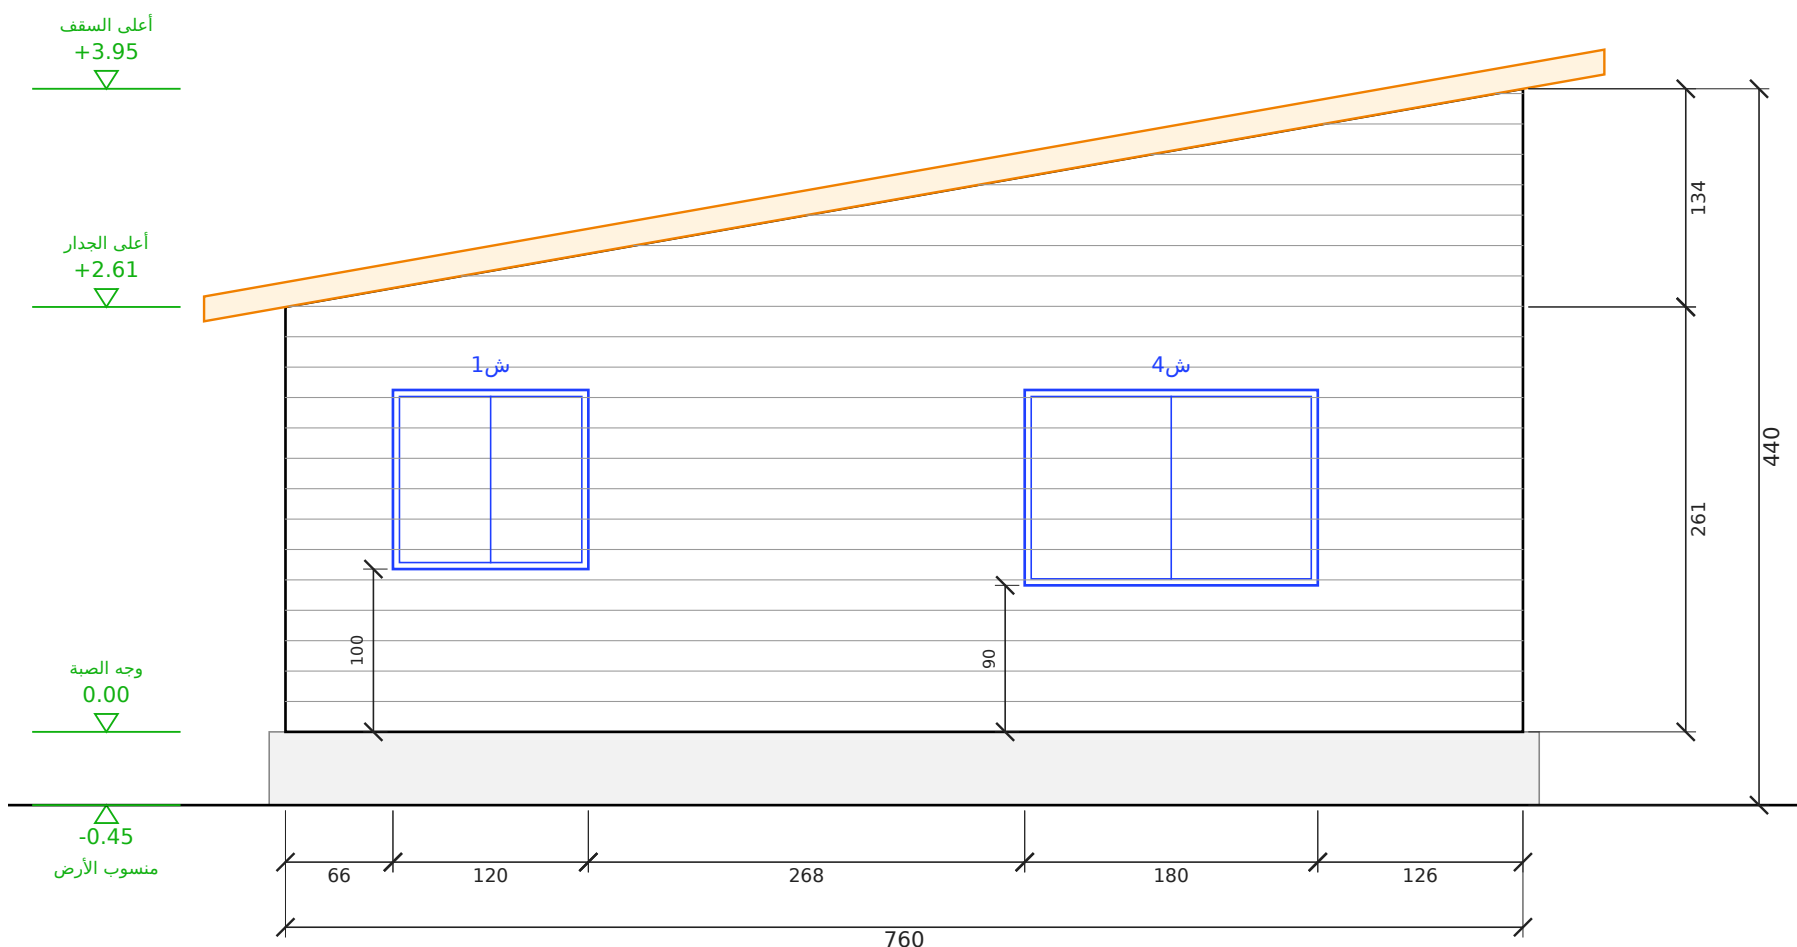


الواجهة الغربية


مقياس 1:50 | الوحدة: سم

رقم اللوحة	التاريخ	المقياس	عنوان اللوحة	المشروع / العميل	مصنع وتد الأخشاب Watad Wood Factory
A-03 (3/9)	2026-10-09	1:50	الواجهة الخلفية والواجهة الغربية	كوخ غرفتين بواجهة زجاج - 76 م ² عميل - تصميم رقم 5	


مسقط السقف (مائل باتجاه واحد)
رفرف 50 سم من كل جهة | مقياس 1:50

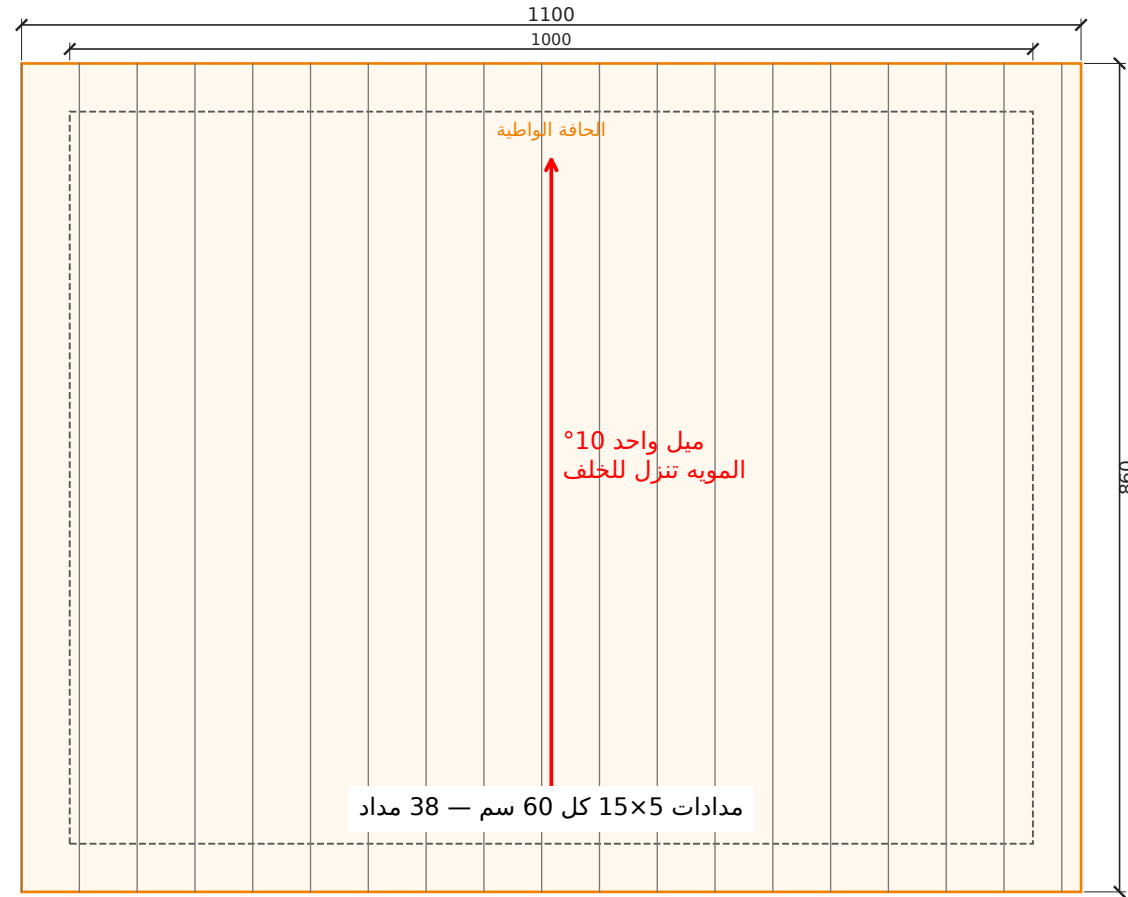

قطاع عرضي أ-أ
مقياس 1:50 | الوحدة: سم

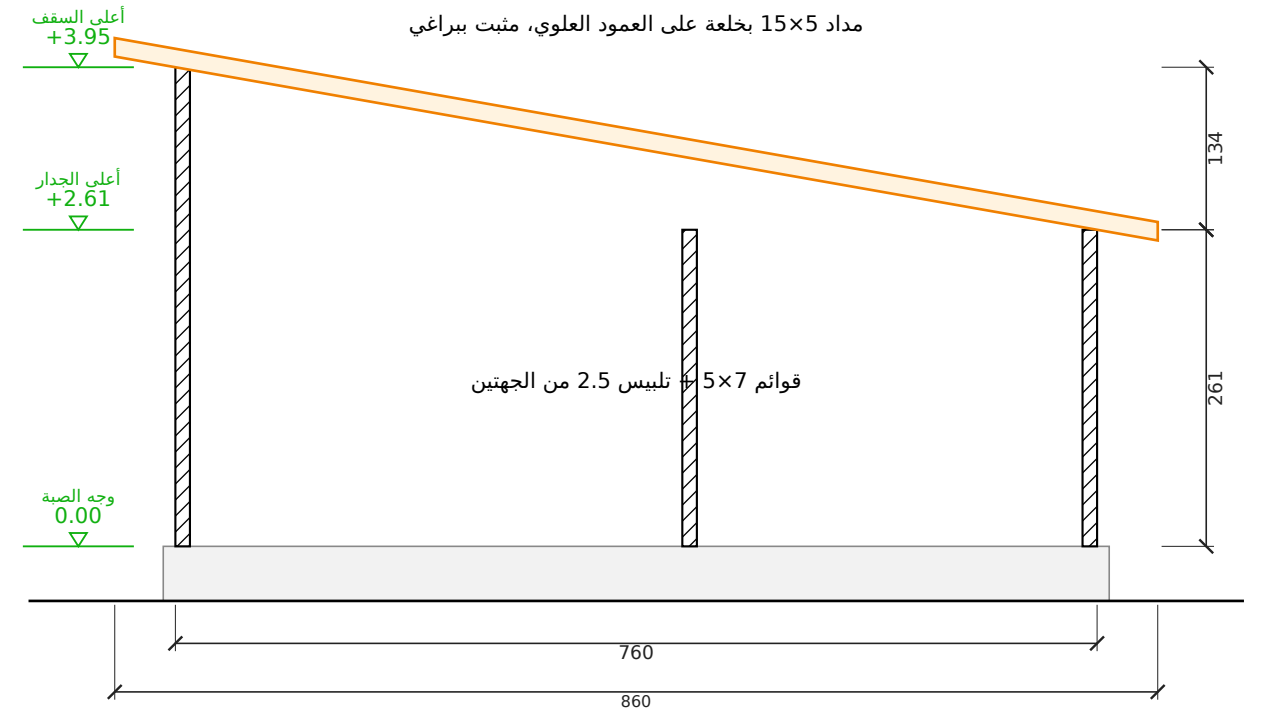

تفصيلة جلوس المداد على العلوي (1:5)

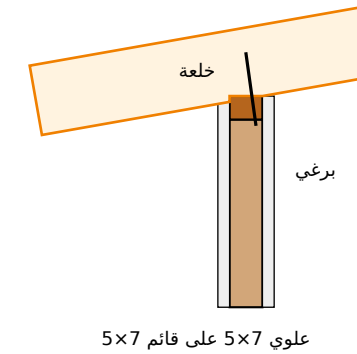

رقم اللوحة

A-04 (4/9)

التاريخ

2026-10-09

المقياس

1:50

عنوان اللوحة

مسقط السقف والقطاع

المشروع / العميل

كوخ غرفتين بواجهة زجاج — 76 م²
عميل — تصميم رقم 5

مصنع وتد الأخشاب
Watad Wood Factory



جدول مقاسات الأبواب والشبابيك
مقاس الفتحة الصافي في الجدار - الوحدة: سم

الرمز	النوع	العرض (سم)	الارتفاع (سم)	ارتفاع الجلسة (سم)	العدد	الموقع
ب1	باب	300	350	-	1	الأمامية
ب2	باب	80	210	-	2	غرفة النوم - الماستر
ب3	باب	70	210	-	2	الحمام المشترك - حمام الماستر
ز1	شباك	120	340	10	2	الأمامية 2
ز2	شباك	150	340	10	2	الأمامية 2
ش1	شباك	120	110	100	4	الشرقية - الخلفية 2 - الغربية
ش2	شباك	160	100	110	1	الشرقية
ش3	شباك	60	60	150	2	الخلفية 2
ش4	شباك	180	120	90	1	الغربية

الإجمالي: أبواب 5 - شبابيك 12

جدول المساحات وبيانات المشروع

جدول المساحات

م	الفراغ	الأبعاد (م)	المساحة (م2)
1	الصالة	6.28 × 4.06	25.50
2	المطبخ الأمريكي	3.48 × 4.06	14.13
3	غرفة النوم	3.18 × 3.18	10.11
4	حمام	1.58 × 3.18	5.02
5	حمام ماستر	1.58 × 3.18	5.02
6	غرفة الماستر	3.06 × 3.18	9.73
	المساحة الصافية الداخلية		69.52
	التراس المسقوف	10.00 × 1.80	18.00
	المساحة الإجمالية المبنية	10.00 × 7.60	76.00

بيانات المشروع


البند	البيان
المشروع	كوخ غرفتين بواجهة زجاج — 76 م ²
العميل	عميل — تصميم رقم 5
الموقع	—
الاستخدام	سكن
التاريخ	2026-10-09
نظام البناء	هيكل خشب 5×7 + تليس 2.5 سم من الجهتين
السقف	مائل باتجاه واحد 10° — قرميد معدني

لقطات المنظور الخارجي

منظور أمامي من اليمين



منظور أمامي من اليسار

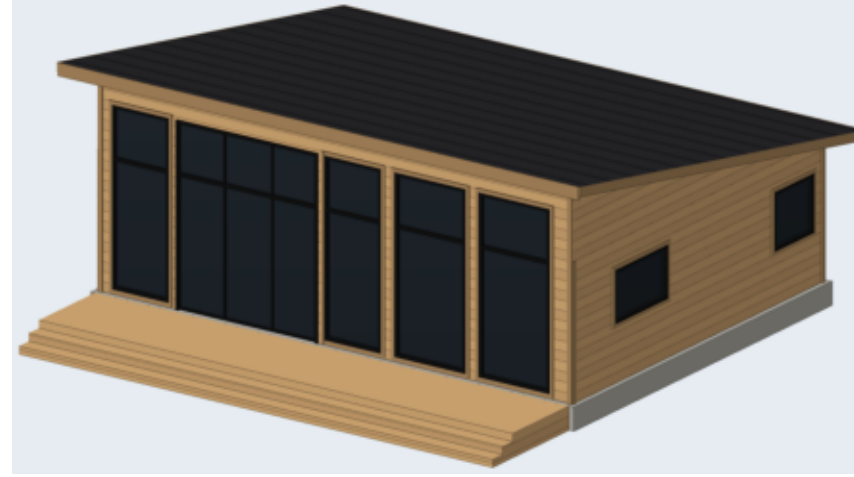


المنظور الأمامي




منظر علوي



منظور خلفي من اليمين

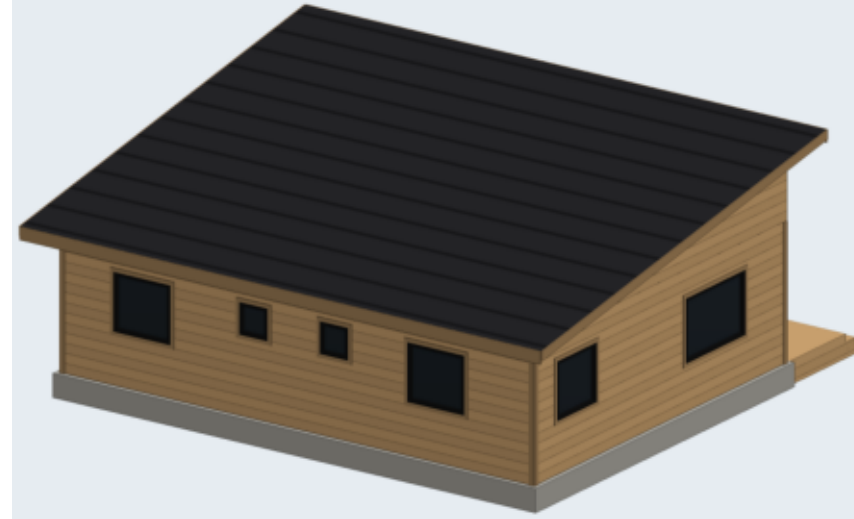

المنظور الخلفي

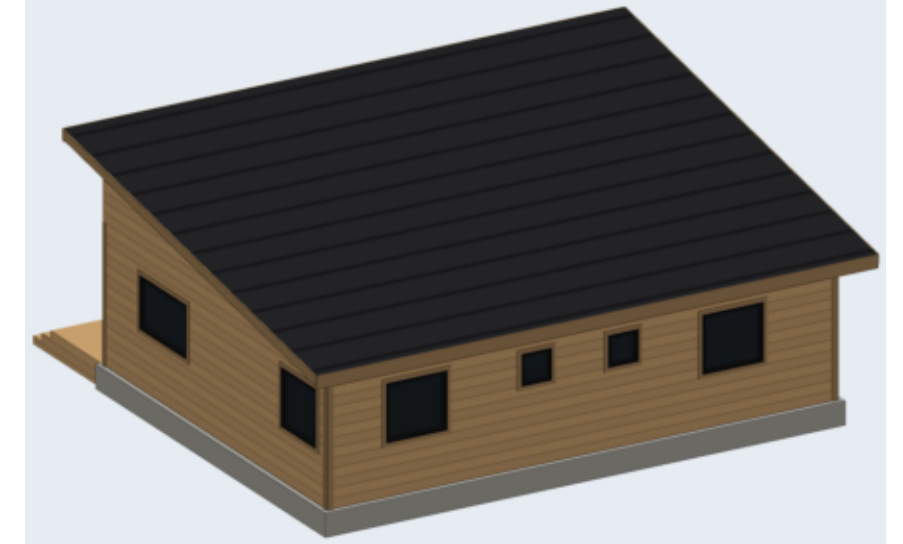

رقم اللوحة

A-07 (7/9)

التاريخ

2026-10-09

المقياس

—

عنوان اللوحة

لقطات المنظور

المشروع / العميل


كوخ غرفتين بواجهة زجاج — 76 م²
عميل — تصميم رقم 5

مصنع وتد الأخشاب
Watad Wood Factory



المقطع العلوي بالفرش

مقطع أفقي على ارتفاع 1.90 م — توزيع الفرش ومسار الحركة

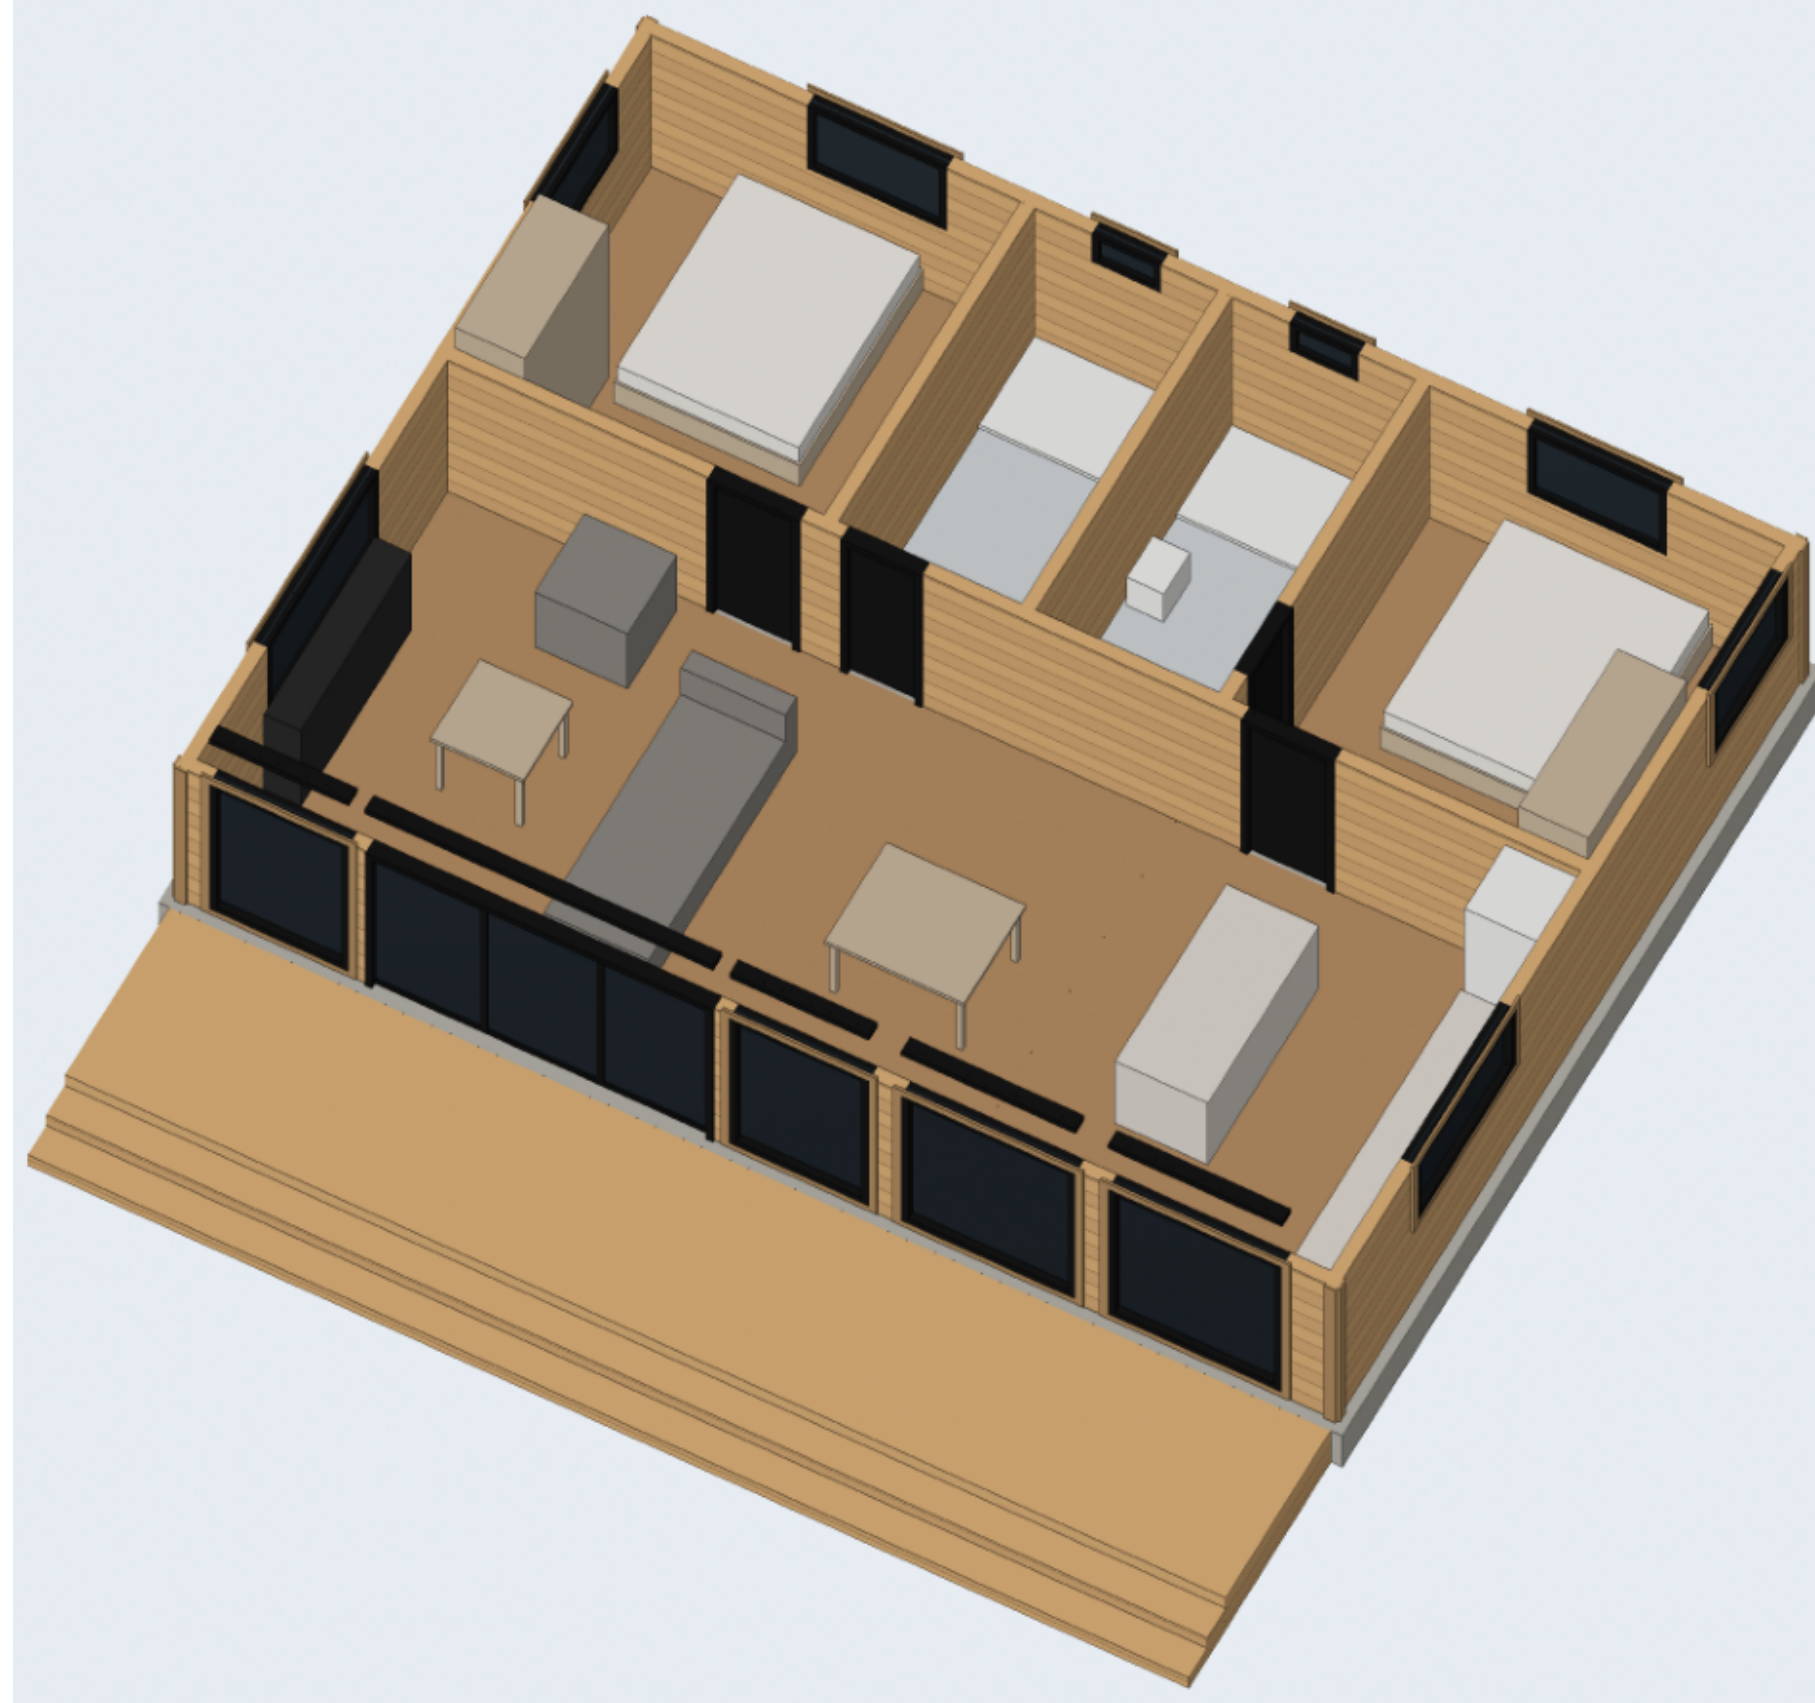

رقم اللوحة

A-08 (8/9)

التاريخ

2026-10-09

المقياس

—

عنوان اللوحة

المقطع العلوي بالفرش

المشروع / العميل

كوخ غرفتين بواجهة زجاج — 76 م²
عميل — تصميم رقم 5

مصنع وتد الأخشاب
Watad Wood Factory



المنظور ثلاثي الأبعاد والمواد

النمط: جوزي غامق + إطارات سوداء — رندر واقعي بخامات حقيقية

جدول المواد والألوان

الخشب / الصبغة

خشب طبيعي فاتح (بدون صبغة)

القرميد

قرميد رمادي غامق

الزجاج

زجاج عاكس غامق

إطارات الشبابيك والأبواب

إطار ألومنيوم أسود

الكنار والزوايا


نفس الصبغة أعمق درجة

الصبغة

خرسانة 45 سم

الدريزين: ألواح أفقية متقاربة (عصري)


تقسيم الشبابيك: بدون | الباب الرئيسي: سحب زجاج

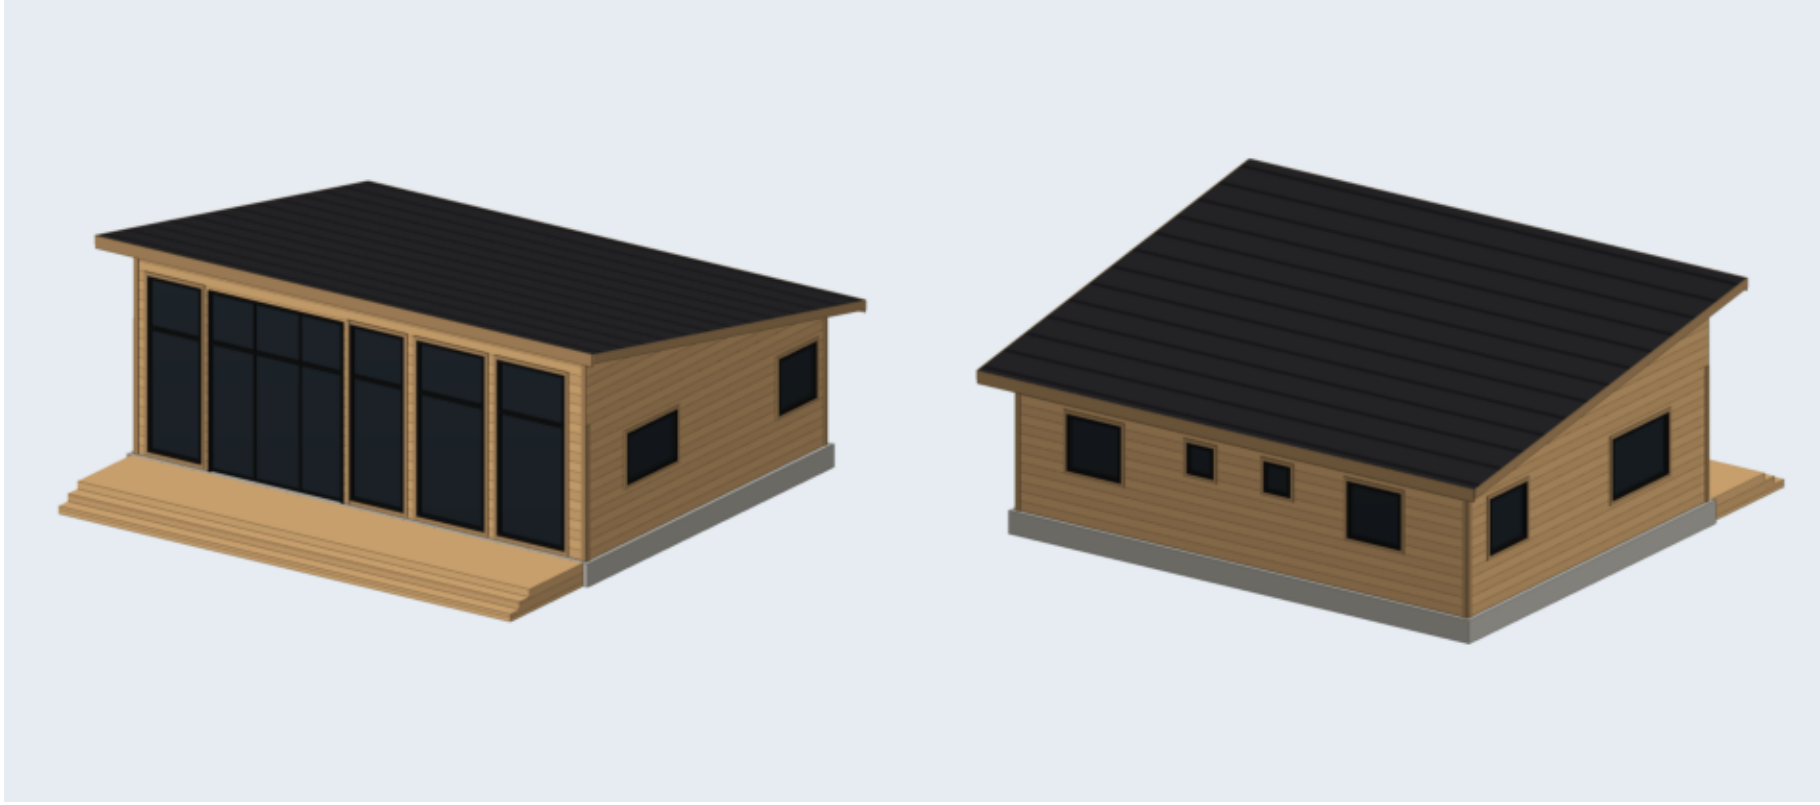


أنواع الدريزين المعتمدة (من مشاريع المصنع)



قوائم رأسية متقاربة (صورة 1)

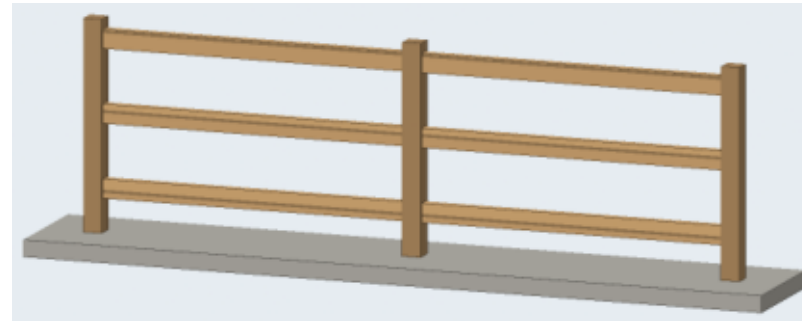

3 مربيع أفقية (صورة 2)

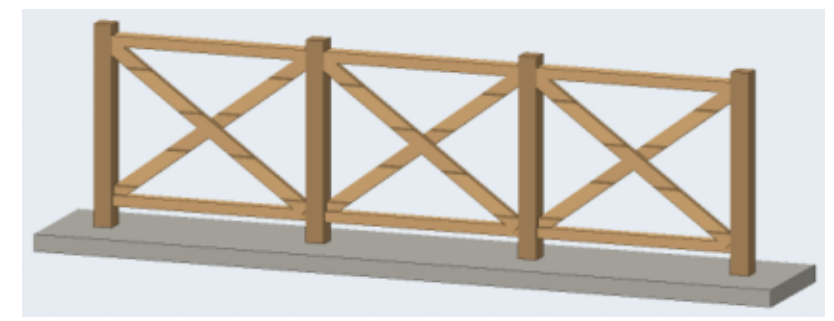

تقاطع X (صورة 5)

رقم اللوحة

A-09 (9/9)

التاريخ

2026-10-09

المقياس

—

عنوان اللوحة

المنظور والمواد

المشروع / العميل

كوخ غرفتين بواجهة زجاج — 76 م²
عميل — تصميم رقم 5

مصنع وتد الأخشاب

Watad Wood Factory

