

## المنظور ثلاثي الأبعاد والمواد

النمط: جوزي غامق + إطارات سوداء — معاينة تقريبية، الإخراج النهائي من 3ds Max

### جدول المواد والألوان



#### الخشب / الصبغة

صبغة جوزي غامق



#### القرميد

قرميد رمادي غامق



#### الزجاج

زجاج عاكس غامق




#### إطارات الشبابيك والأبواب

إطار ألومنيوم أسود



#### الكنار والزوايا

نفس الصبغة أغمق درجة

 

#### الصبغة

خرسانة 45 سم


الدريزين: ألواح أفقية متقاربة (عصري)

تقسيم الشبابيك: بدون | الباب الرئيسي: سحب زجاج


### أنواع الدريزين المعتمدة (من مشاريع المصنع)



قوائم رأسية متقاربة (صورة 1)

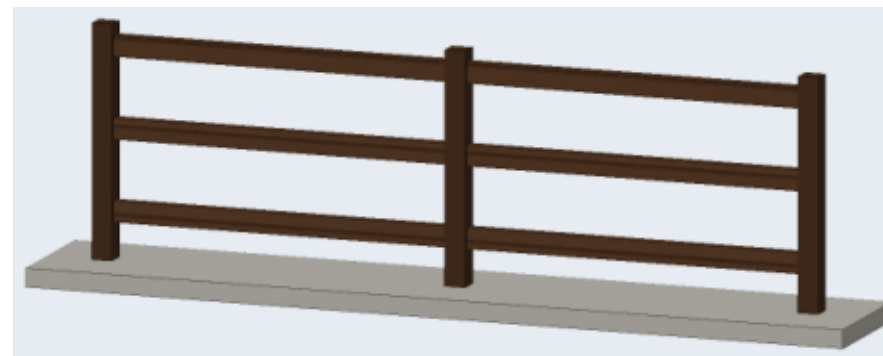



3 مربيع أفقية (صورة 2)

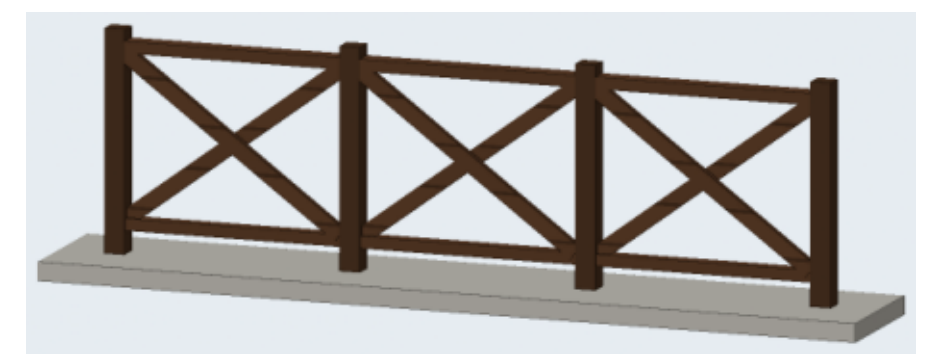

تقاطع X (صورة 5)


المسقط الأفقي مع الفرش  
الأبعاد بالسنتيمتر - الجدران: قوائم 5×7 + تليس 2.5 من الجهتين (12 سم)

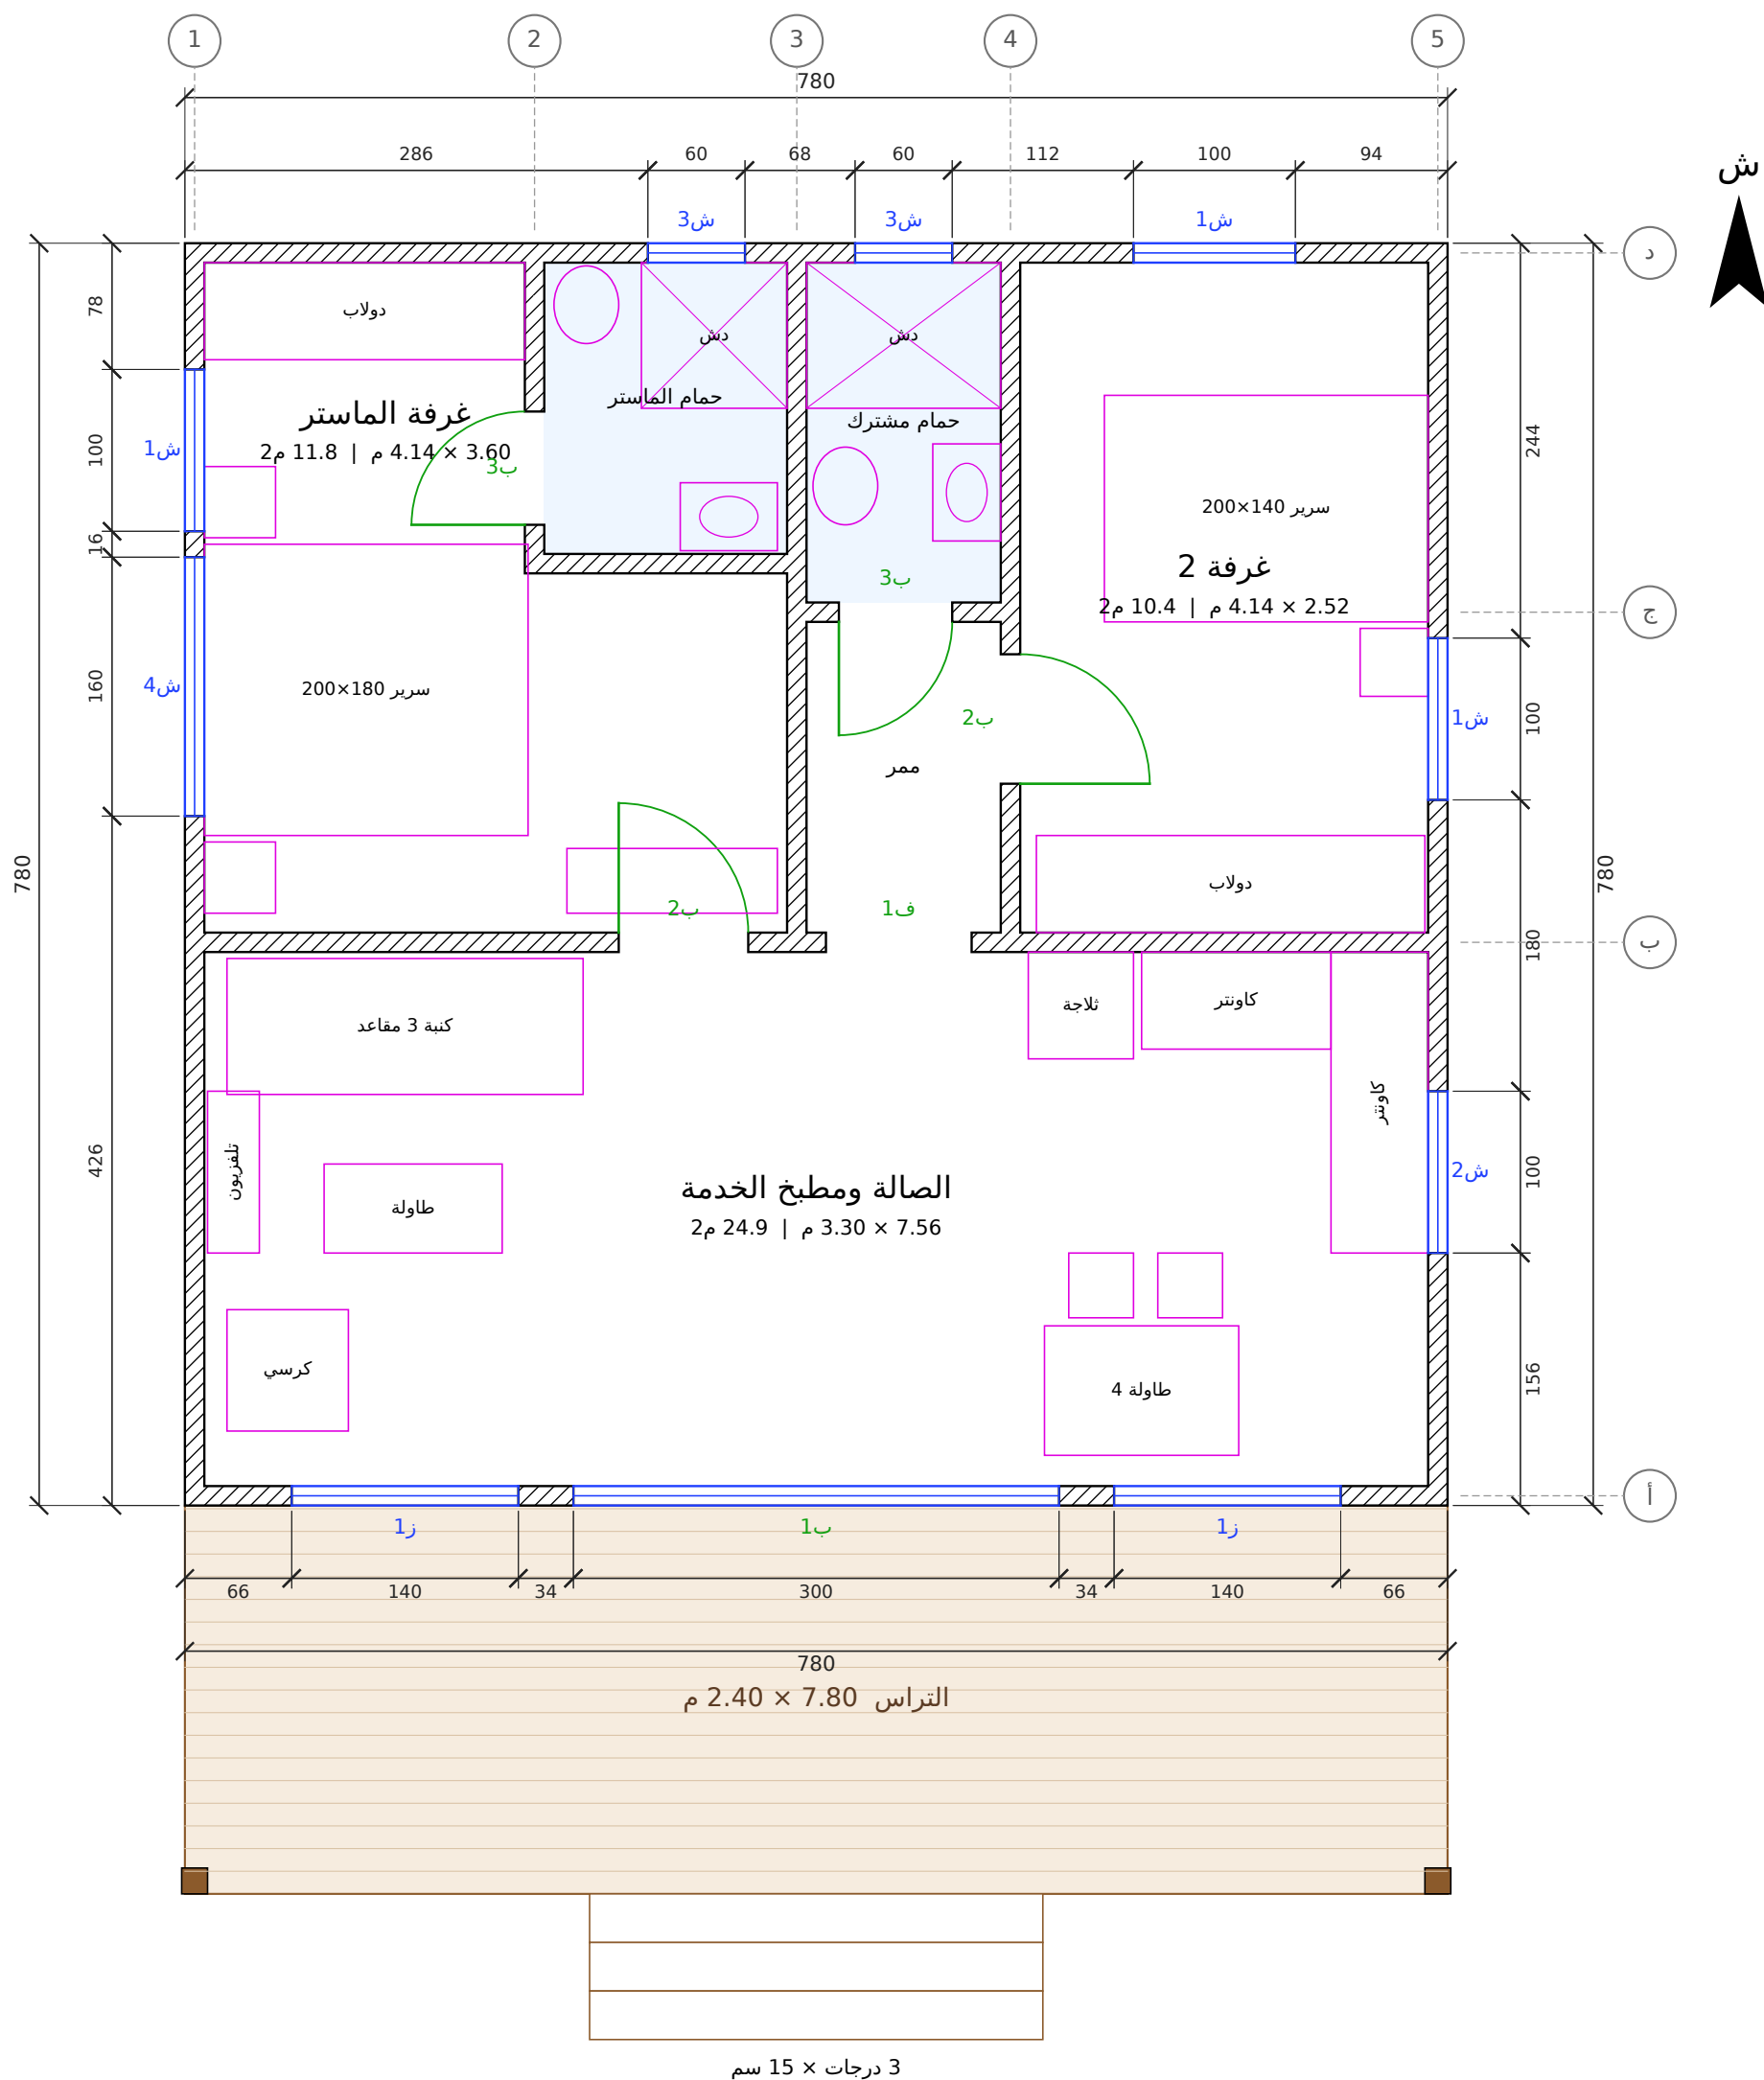

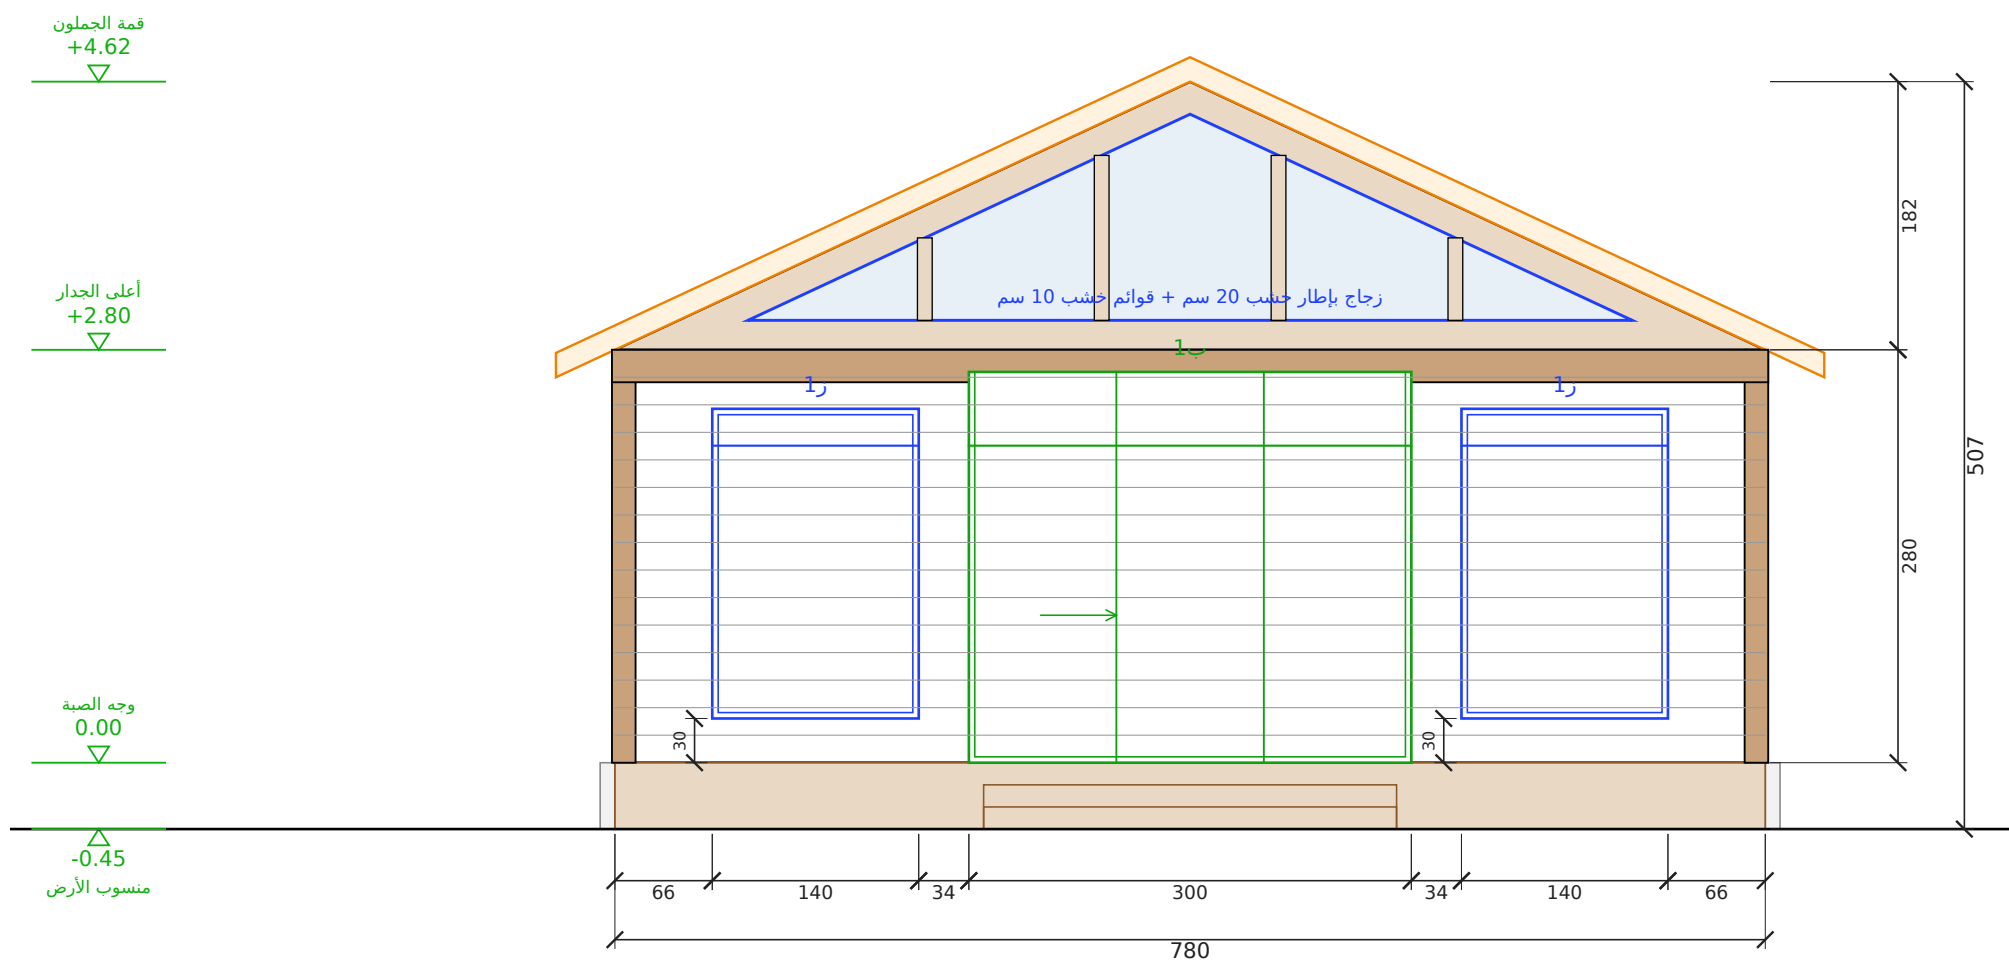


الواجهة الأمامية (التراس)

مقياس 1:50 | الوحدة: سم

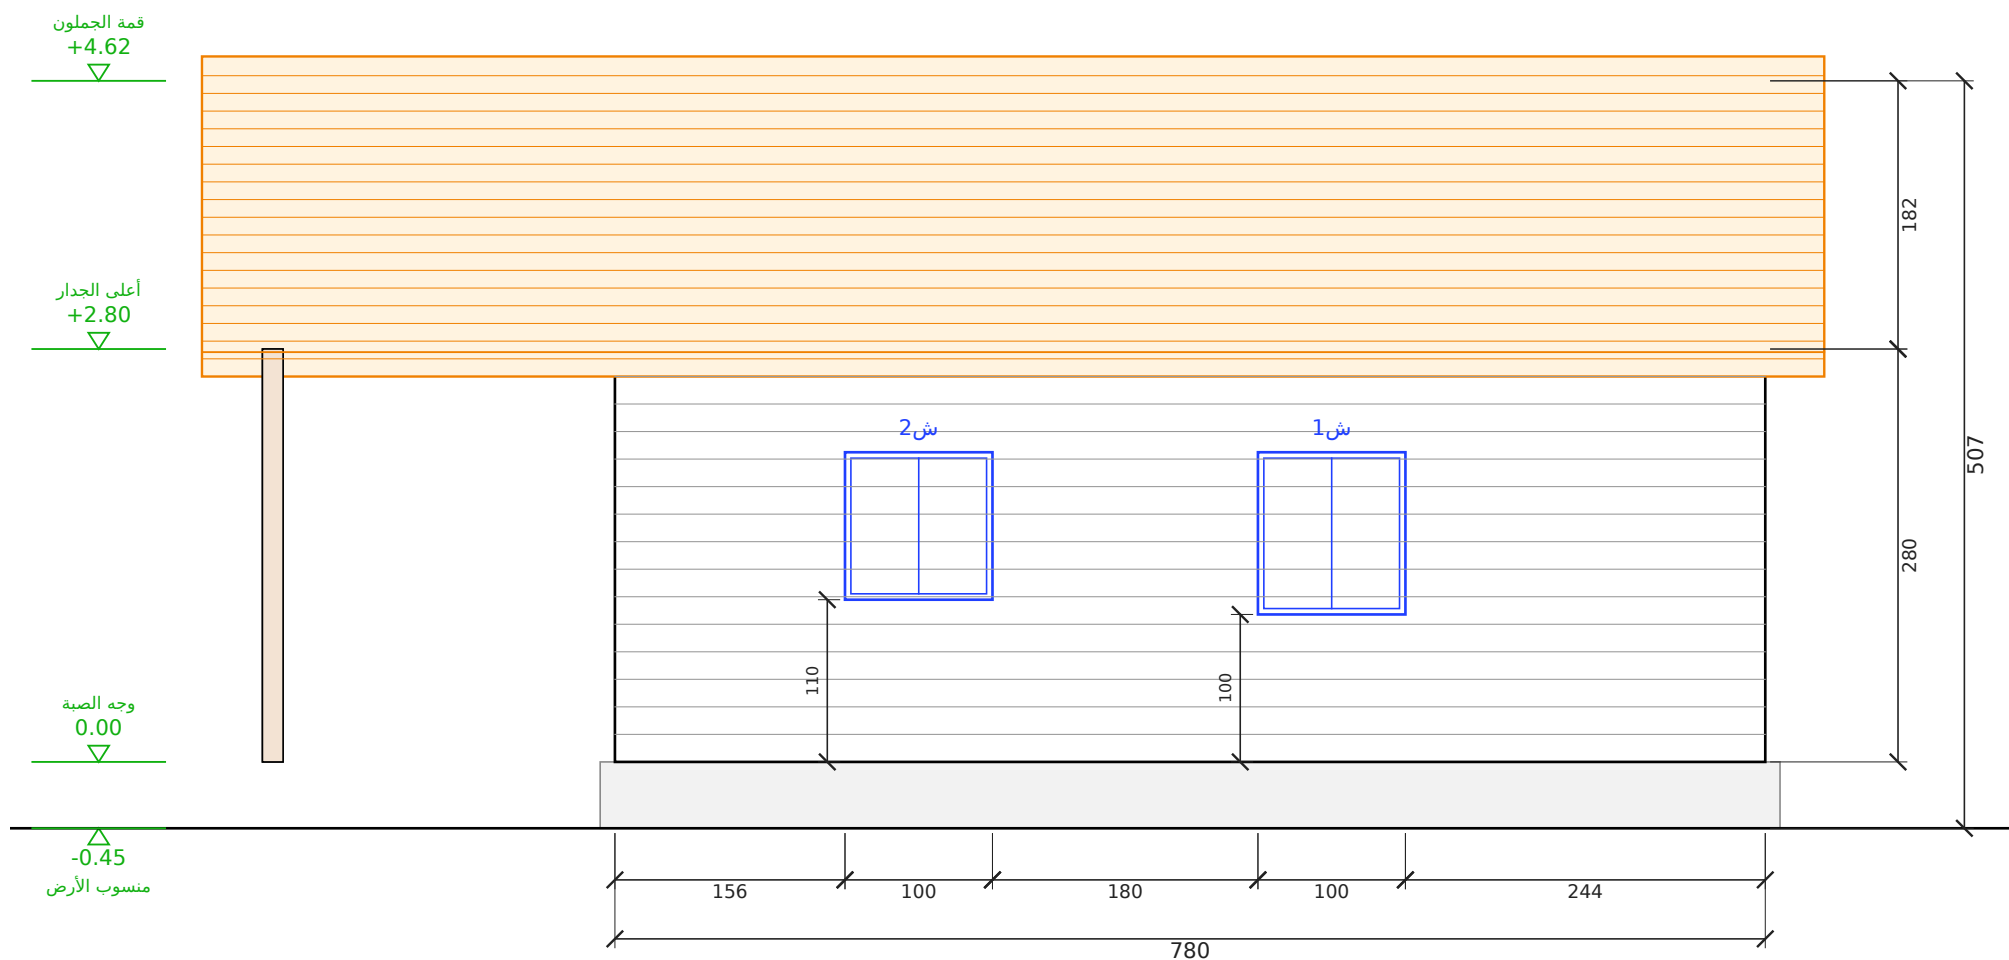


الواجهة الشرقية

مقياس 1:50 | الوحدة: سم

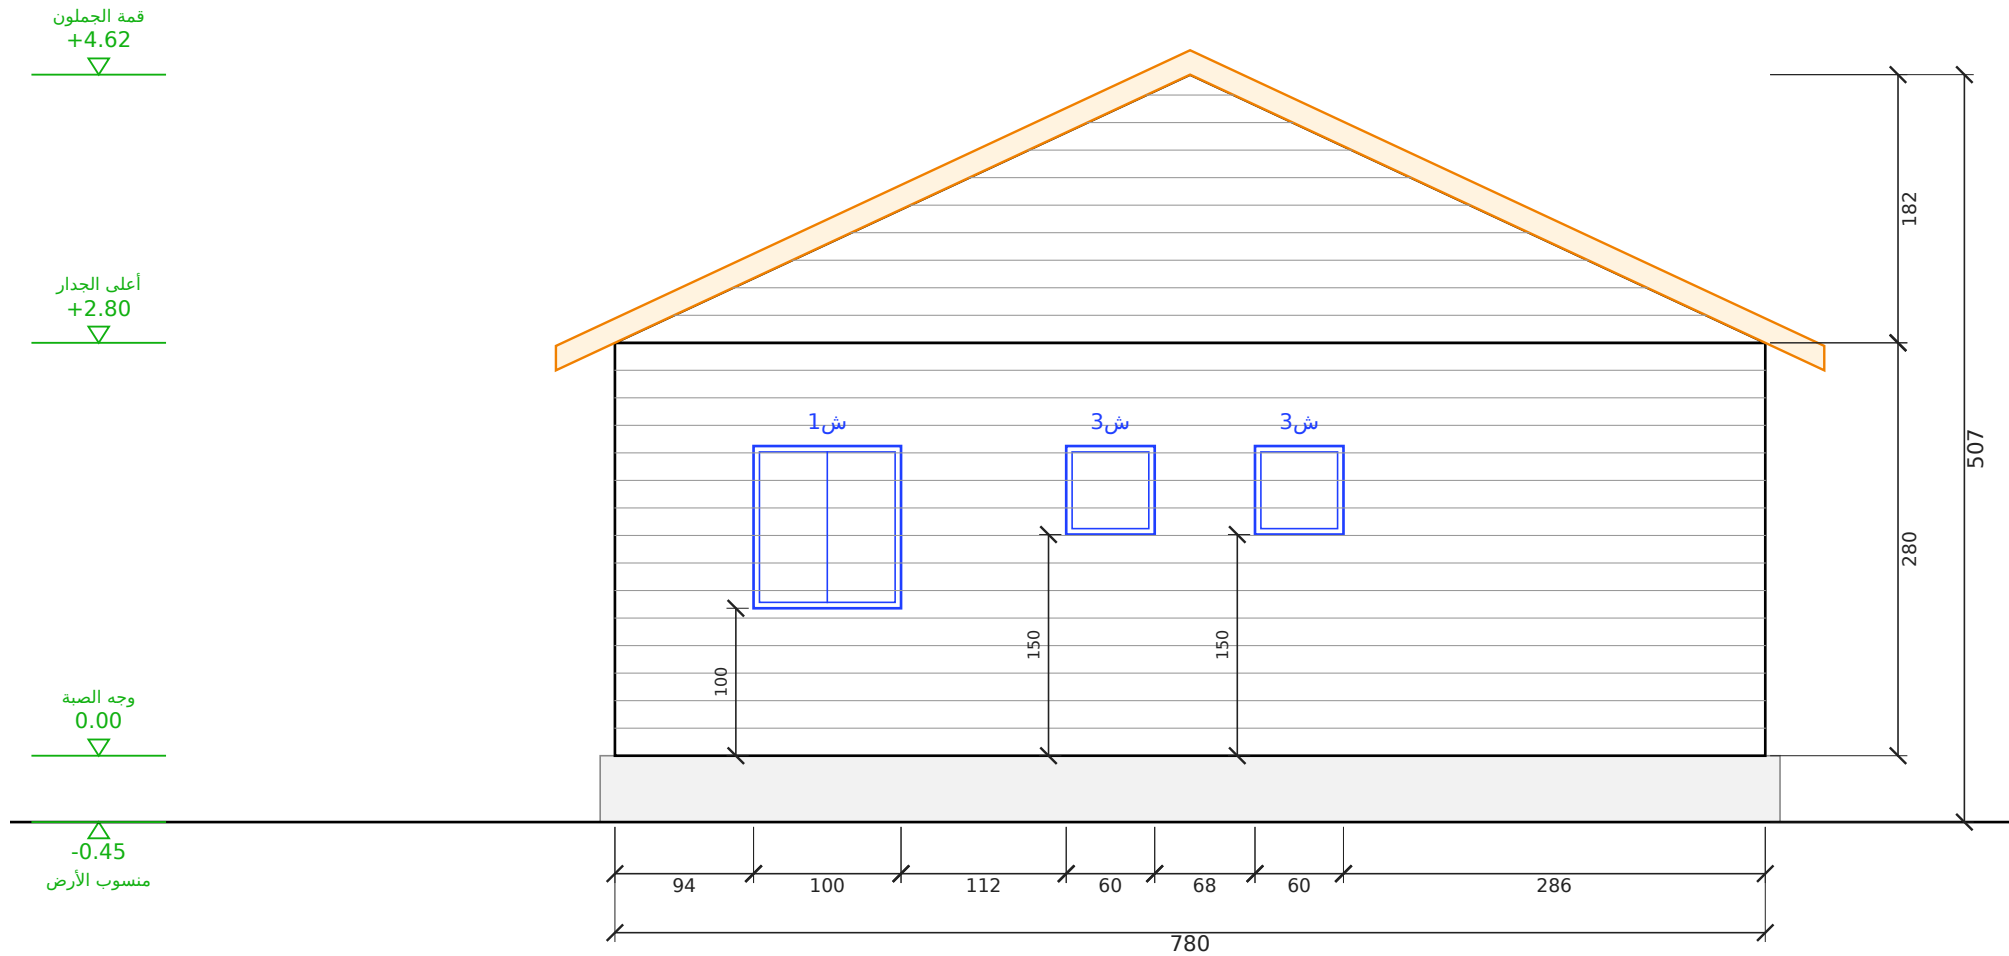

### الواجهة الخلفية


مقياس 1:50 | الوحدة: سم

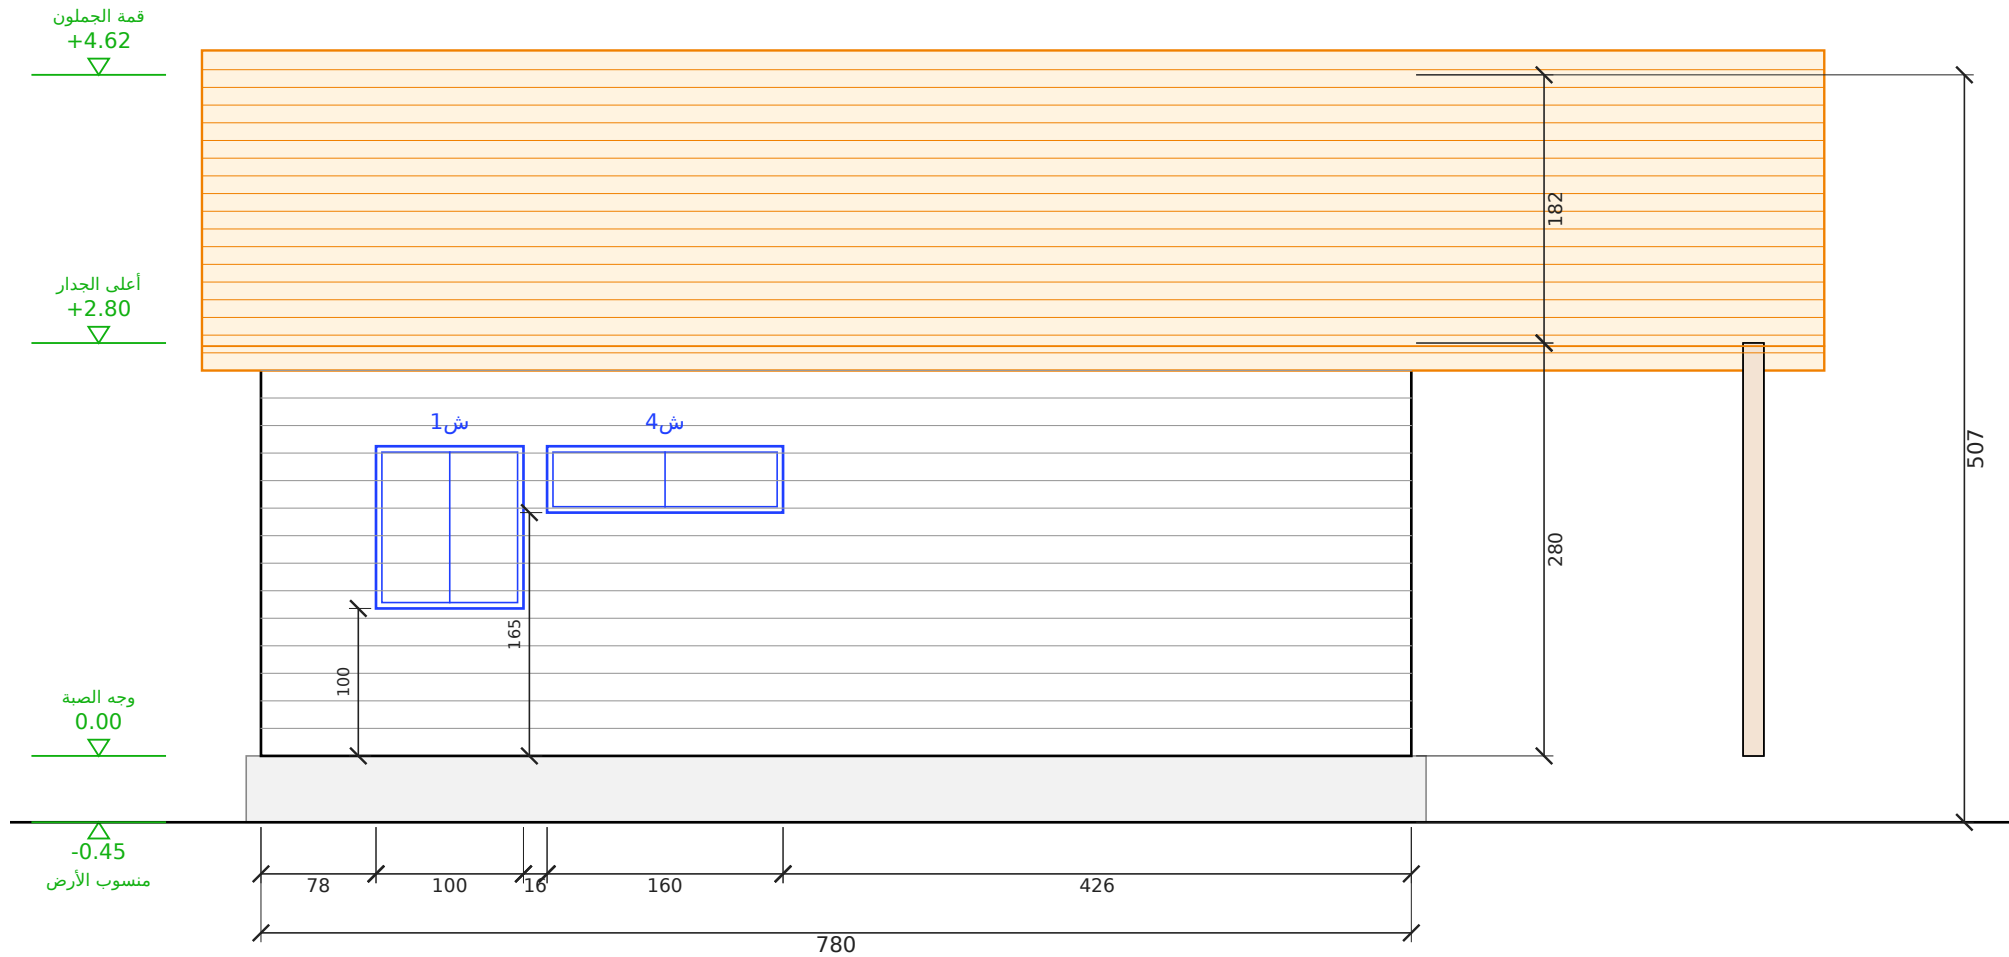


### الواجهة الغربية

مقياس 1:50 | الوحدة: سم


مسقط السقف (جملون)  
رفر 40 سم من كل جهة | مقياس 1:50

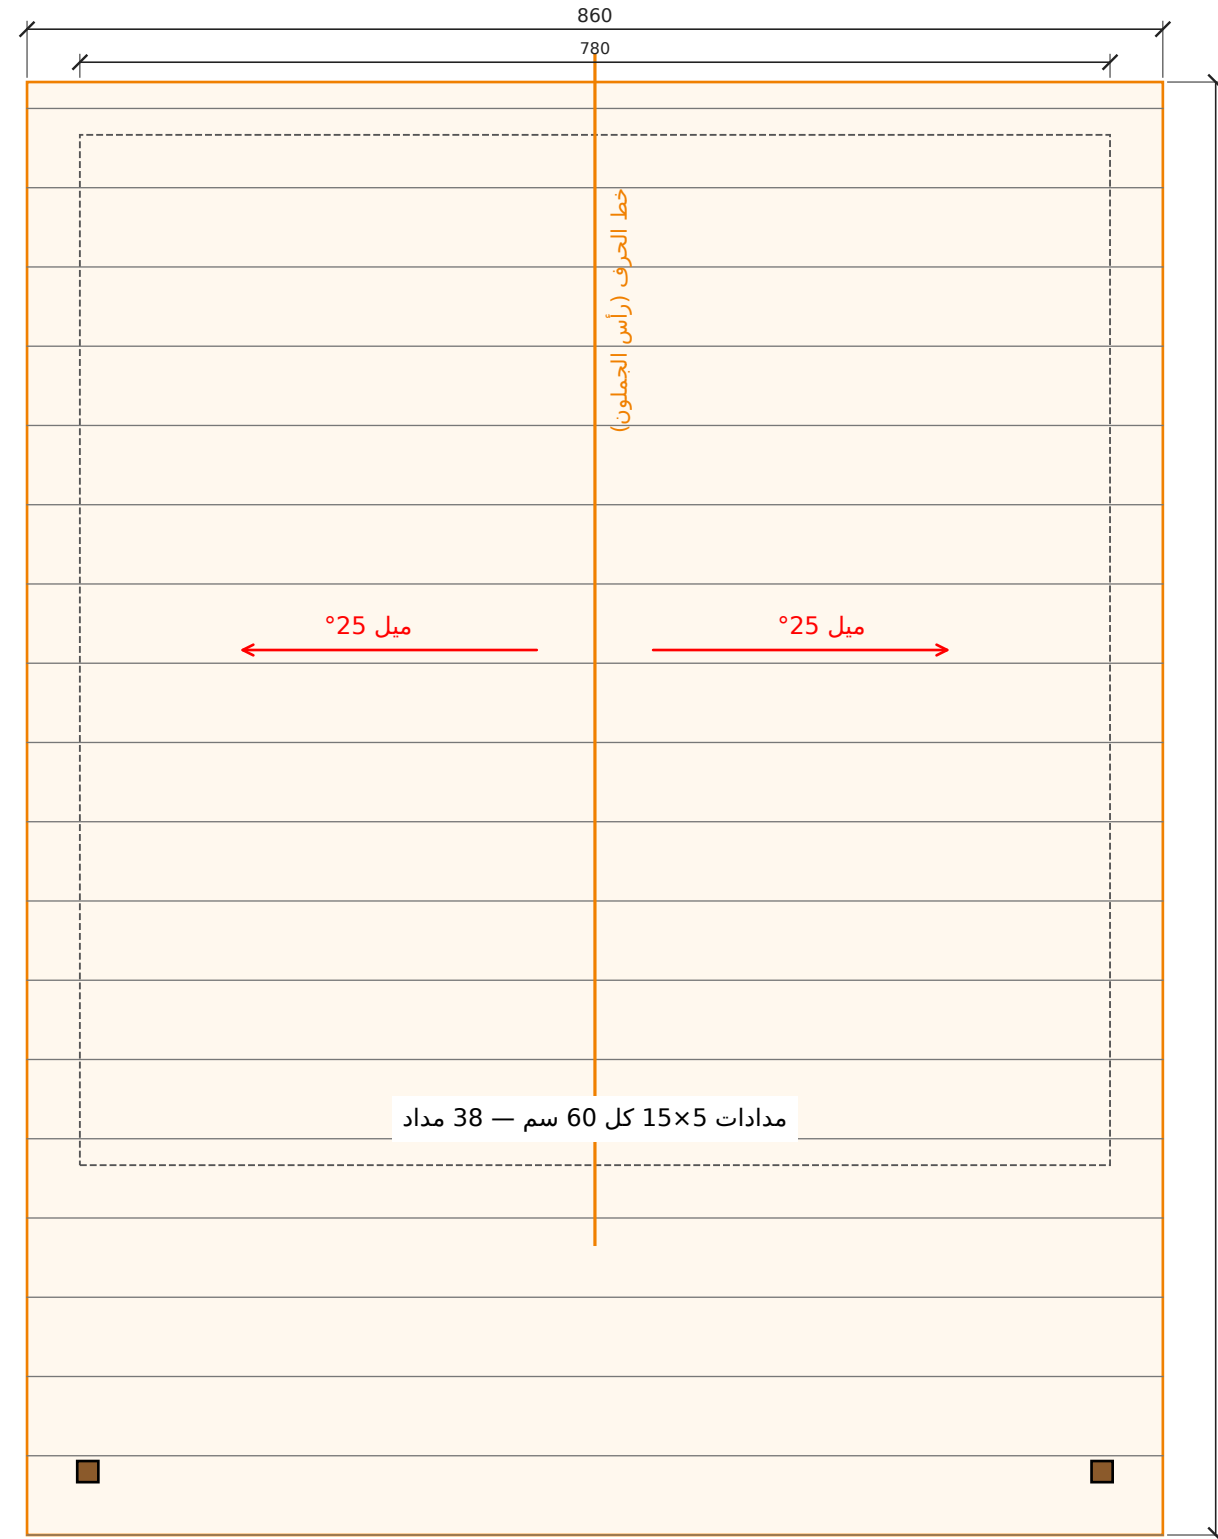

قطاع عرضي أ-أ  
مقياس 1:50 | الوحدة: سم

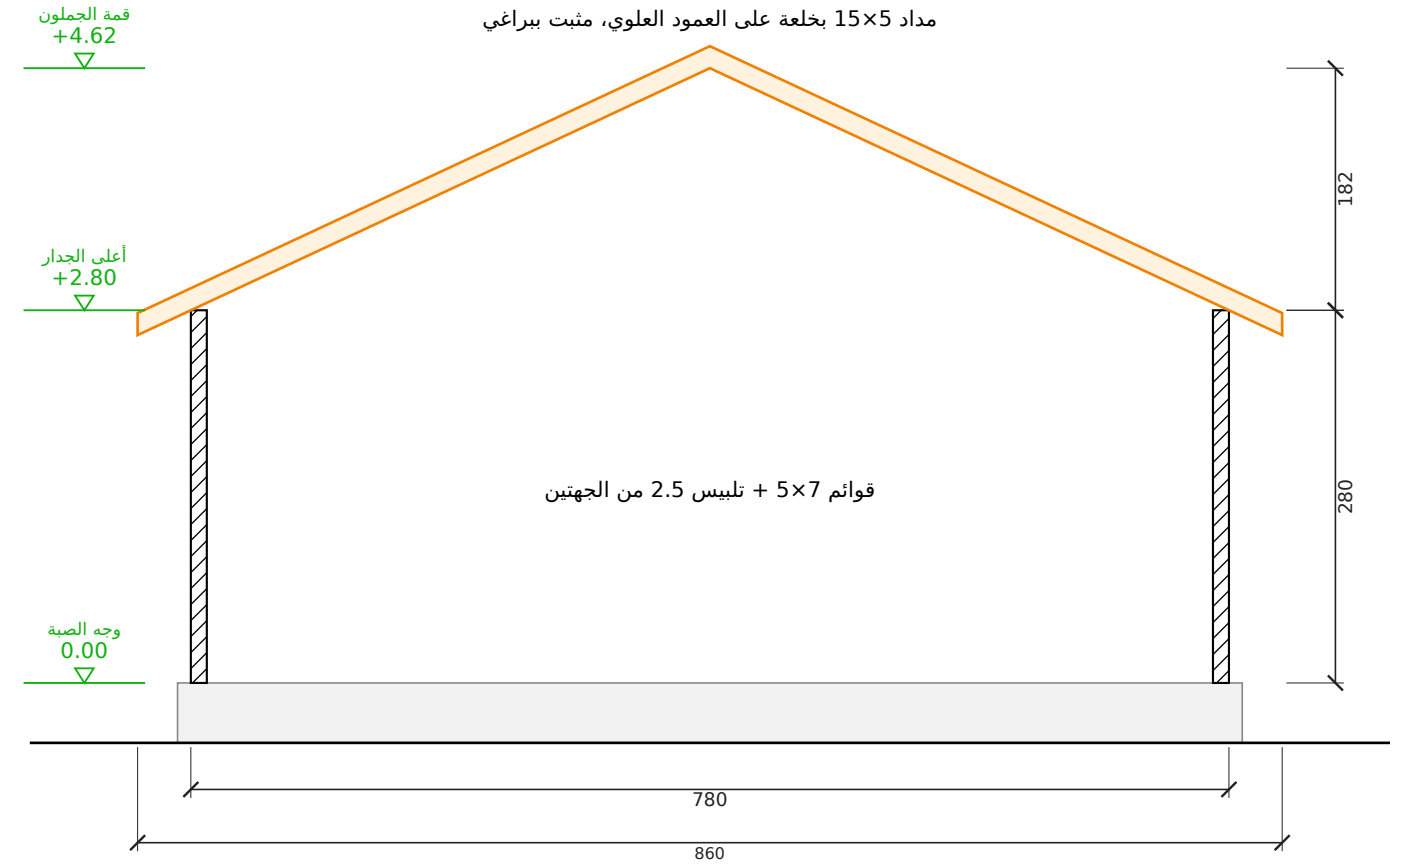

تفصيلة جلوس المداد على العلوي (1:5)

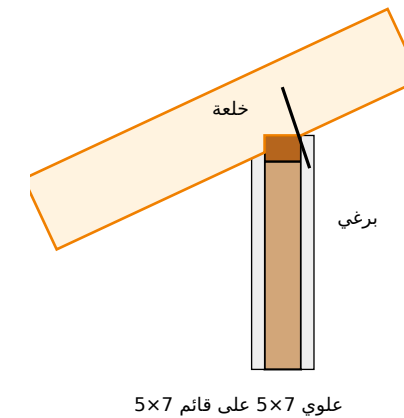

جدول مقاسات الأبواب والشبابيك  
مقاس الفتحة الصافي في الجدار - الوحدة: سم

| الرمز | النوع | العرض (سم) | الارتفاع (سم) | ارتفاع الجلسة (سم) | العدد | الموقع                      |
|-------|-------|------------|---------------|--------------------|-------|-----------------------------|
| ب1    | باب   | 300        | 265           | -                  | 1     | الأمامية (التراس)           |
| ب2    | باب   | 80         | 210           | -                  | 2     | ماستر - غرفة 2              |
| ب3    | باب   | 70         | 210           | -                  | 2     | حمام مشترك - حمام ماستر     |
| ف1    | باب   | 90         | 210           | -                  | 1     | فتحة الممر                  |
| ز1    | شباك  | 140        | 210           | 30                 | 2     | الأمامية (التراس) 2         |
| ش1    | شباك  | 100        | 110           | 100                | 3     | الشرقية - الخلفية - الغربية |
| ش2    | شباك  | 100        | 100           | 110                | 1     | الشرقية                     |
| ش3    | شباك  | 60         | 60            | 150                | 2     | الخلفية 2                   |
| ش4    | شباك  | 160        | 45            | 165                | 1     | الغربية                     |

الإجمالي: أبواب 6 - شبابيك 9

مصنع وتد الأخشاب  
Watad Wood Factory

| البند     | القيمة                         |
|-----------|--------------------------------|
| المشروع   | كوخ غرفتين وتراس مسقوف 7.8×7.8 |
| العميل    | عميل — تصميم حسب الصورة        |
| الموقع    | —                              |
| الاستخدام | استراحة / استجمام              |
| المدير    | —                              |
| التاريخ   | 2026-09-29                     |
| المقياس   | 1:50                           |
| الوحدة    | سم                             |


التسعير

| البند                     | القيمة             |
|---------------------------|--------------------|
| المساحة الإجمالية (م2)    | 60.84              |
| مساحة التراس المسقوف (م2) | 18.72              |
| سعر المتر (ريال)          | يُحدد بعد الاعتماد |
| الإجمالي (ريال)           | —                  |


جدول المساحات

| م | الفراغ                     | الأبعاد الداخلية (م) | المساحة (م2) |
|---|----------------------------|----------------------|--------------|
| 1 | الصالة ومطبخ الخدمة        | 7.56 × 3.30          | 24.95        |
| 2 | غرفة الماستر               | 3.60 × 4.14          | 11.79        |
| 3 | حمام الماستر               | 1.50 × 1.80          | 2.70         |
| 4 | ممر                        | 1.20 × 1.92          | 2.30         |
| 5 | حمام مشترك                 | 1.20 × 2.10          | 2.52         |
| 6 | غرفة 2                     | 2.52 × 4.14          | 10.43        |
|   | المساحة الصافية الداخلية   |                      | 54.70        |
|   | المساحة الإجمالية الخارجية | 7.80 × 7.80          | 60.84        |

تأطير جدار جنوب — الطول 768 سم، الارتفاع 280 سم

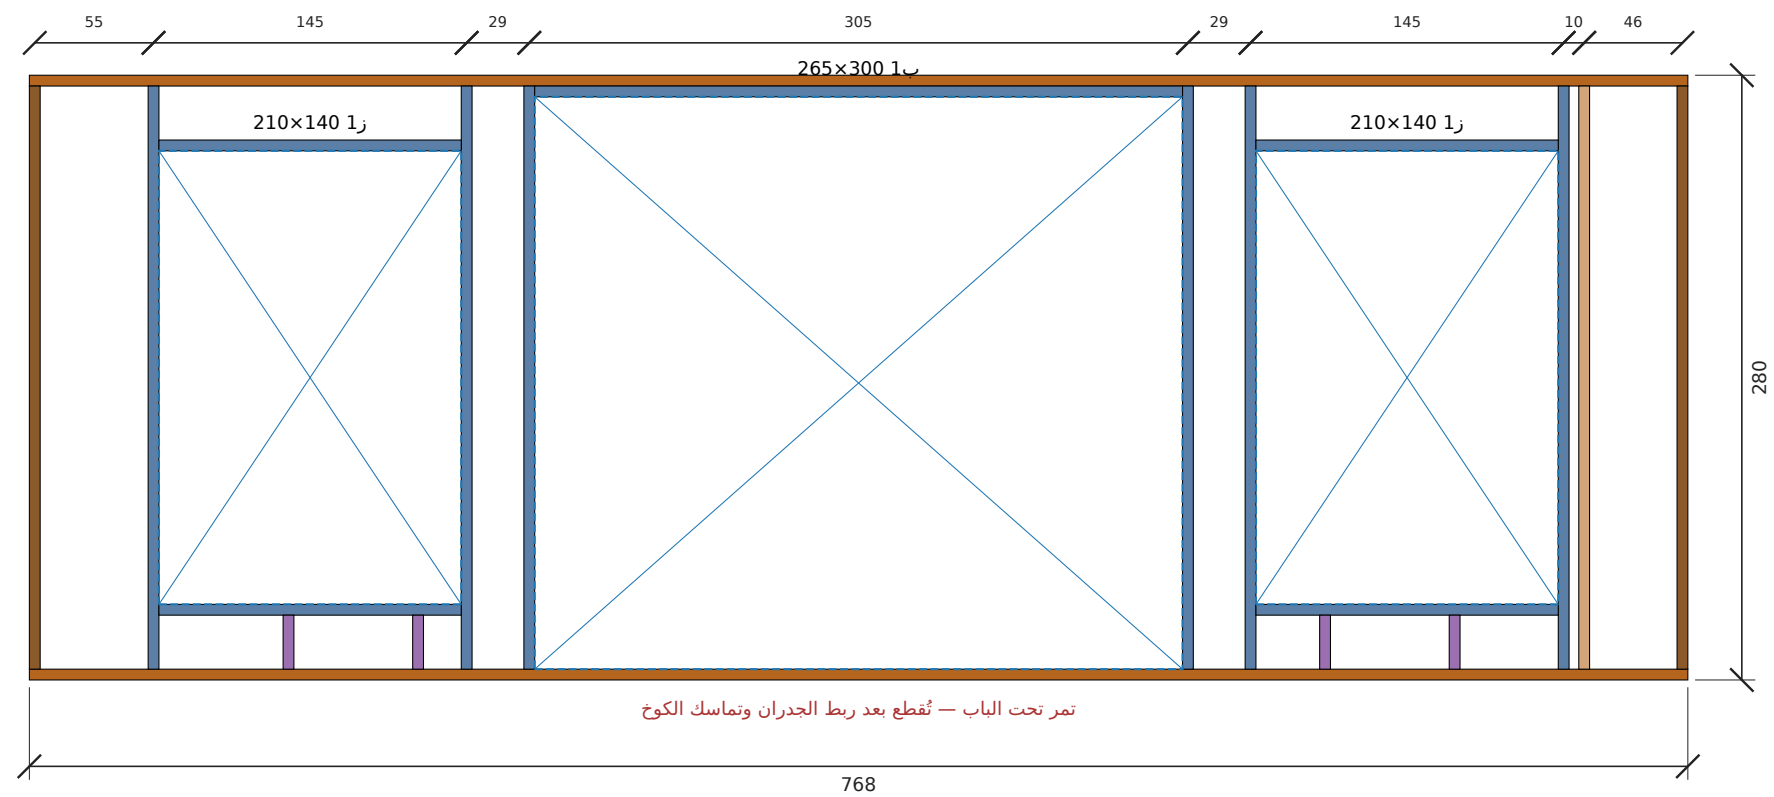


تأطير جدار شرق — الطول 768 سم، الارتفاع 280 سم

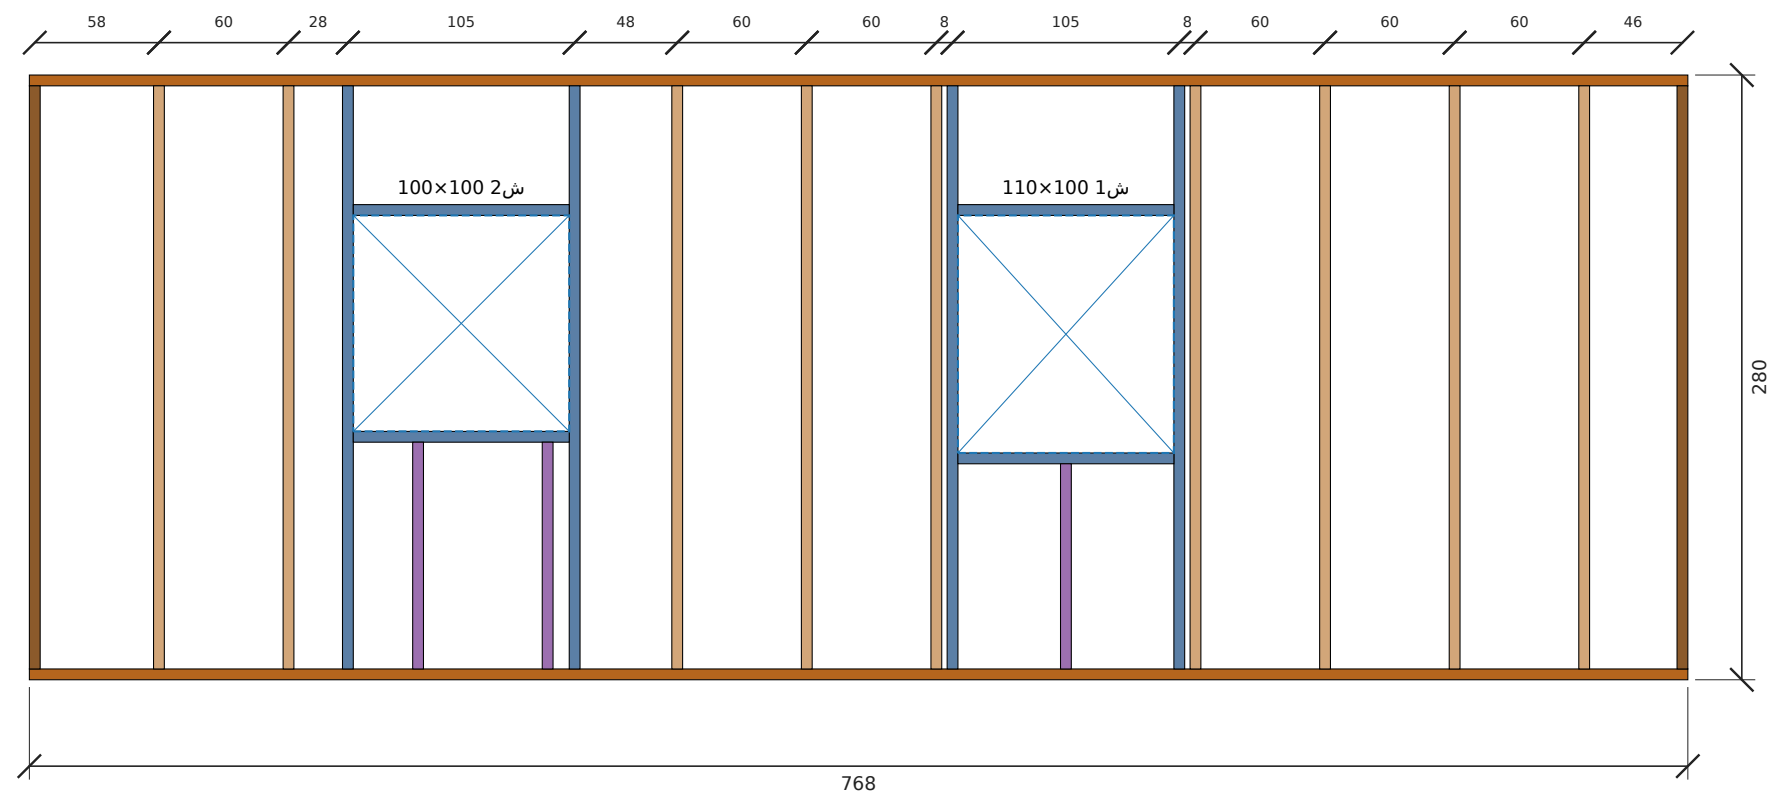


عمود قصير   جلسة شباك   رأس فتحة   جنب فتحة   عمود زاوية   عمود   علوي   قاعدة سفلية

تأطير جدار شمال — الطول 768 سم، الارتفاع 280 سم

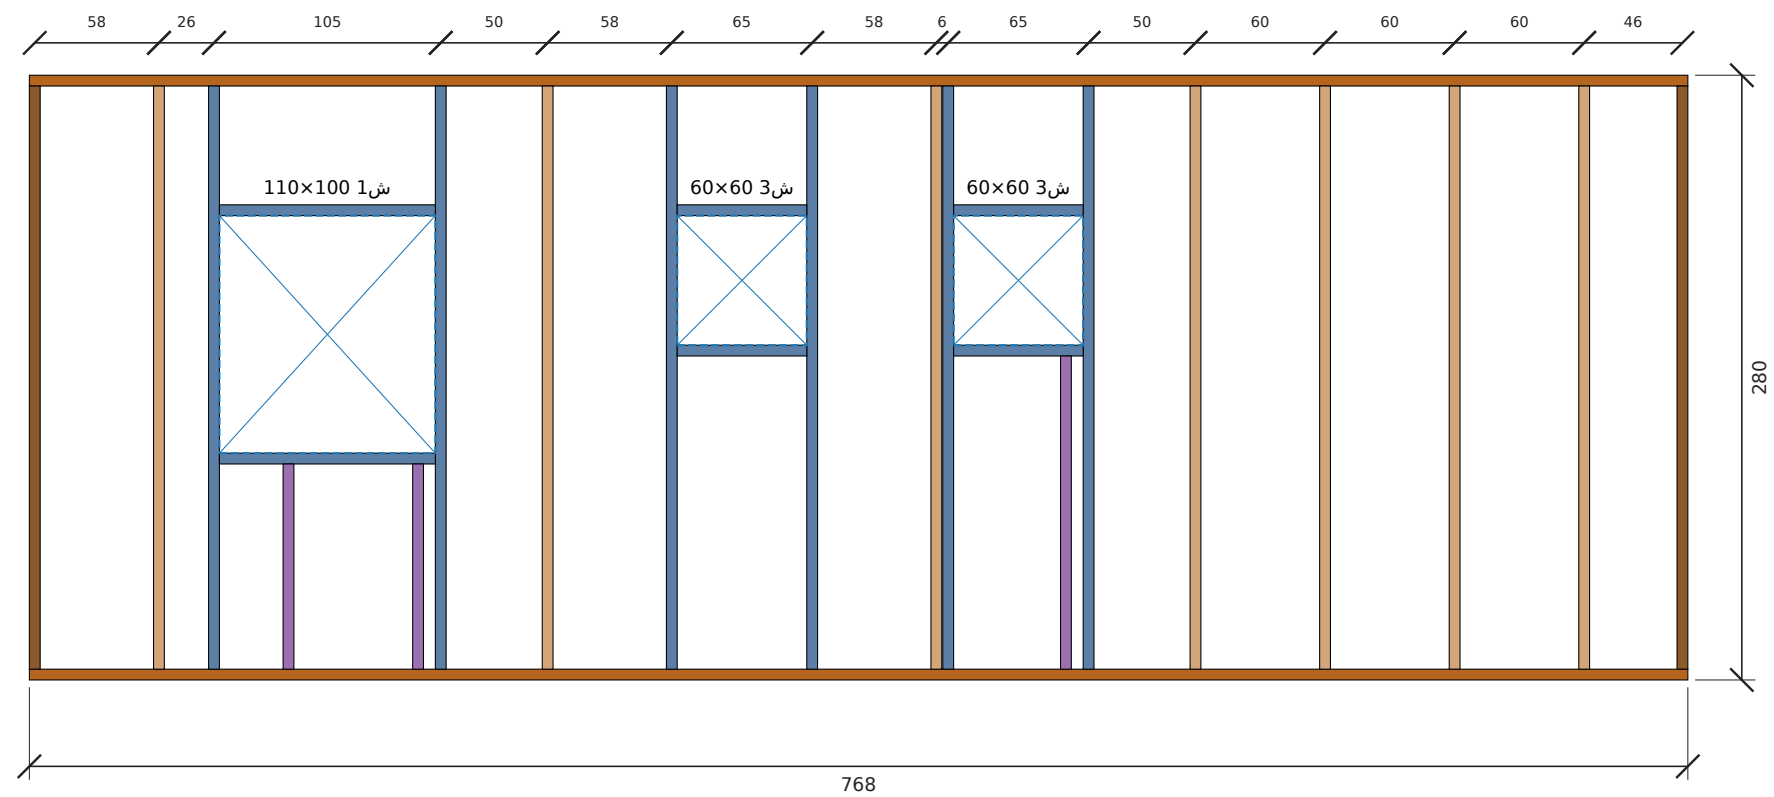


تأطير جدار غرب — الطول 768 سم، الارتفاع 280 سم

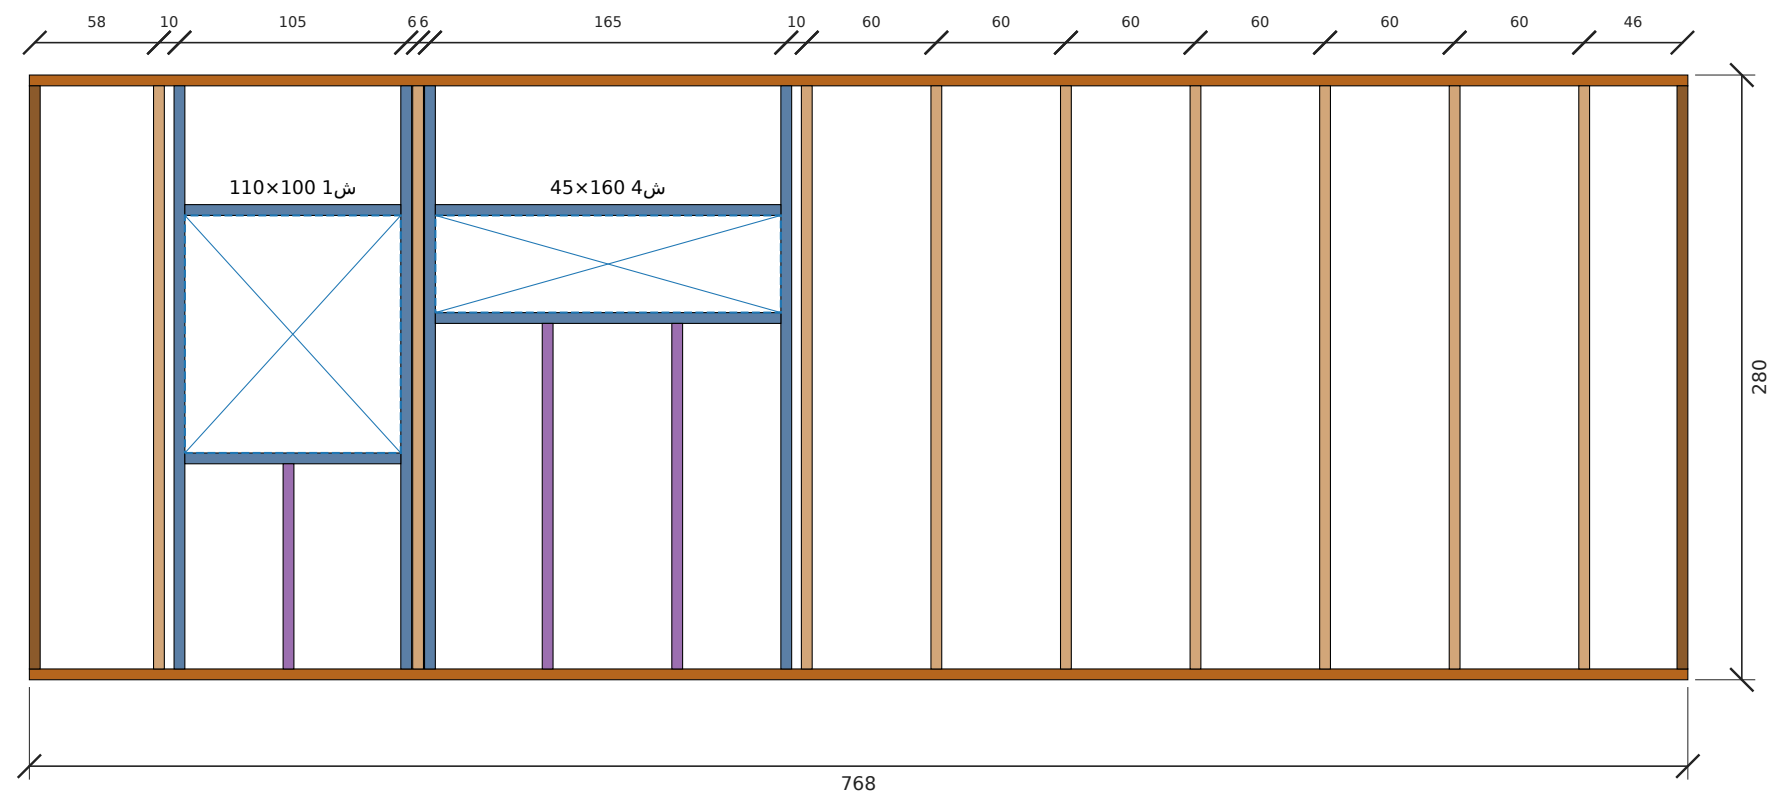


عمود قصير عمود زاوية عمود علوي قاعدة سفلية رأس فتحة جنب فتحة جلسة شباك

تأطير جدار د1-فاصل الصالة — الطول 768 سم، الارتفاع 280 سم (داخلي)

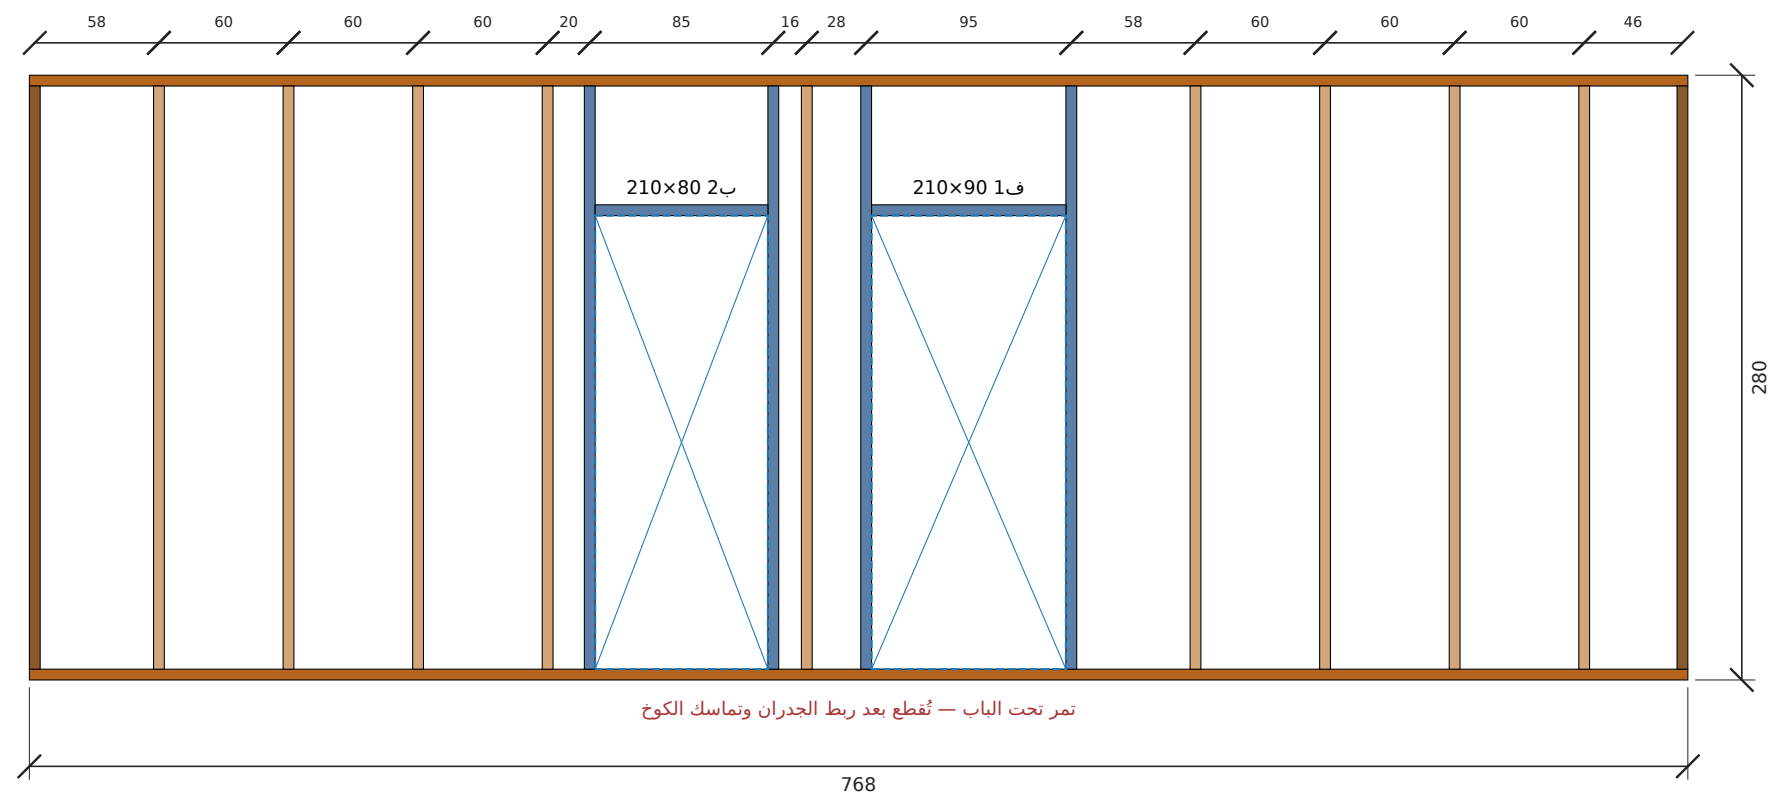


تأطير جدار د2-جدار النواة — الطول 426 سم، الارتفاع 280 سم (داخلي)

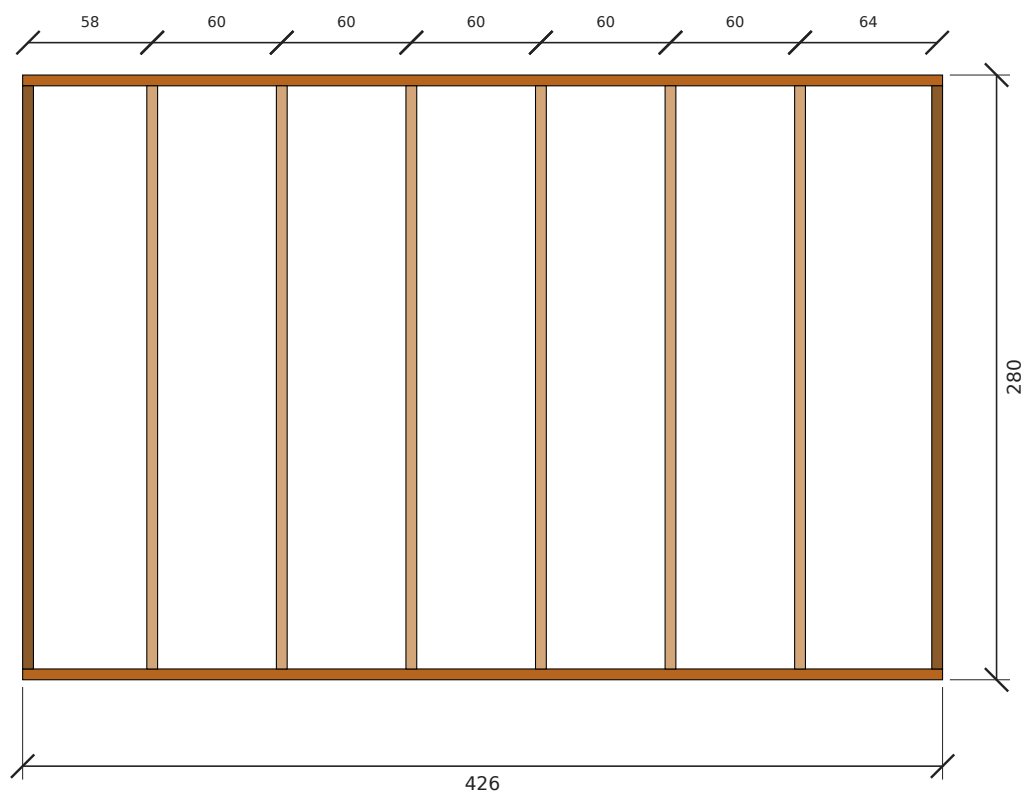


عمود قصير عمود زاوية عمود عمود علوي قاعدة سفلية رأس فتحة جنب فتحة جلسة شباك

تأطير جدار د3-غرفة 2 — الطول 426 سم، الارتفاع 280 سم (داخلي)

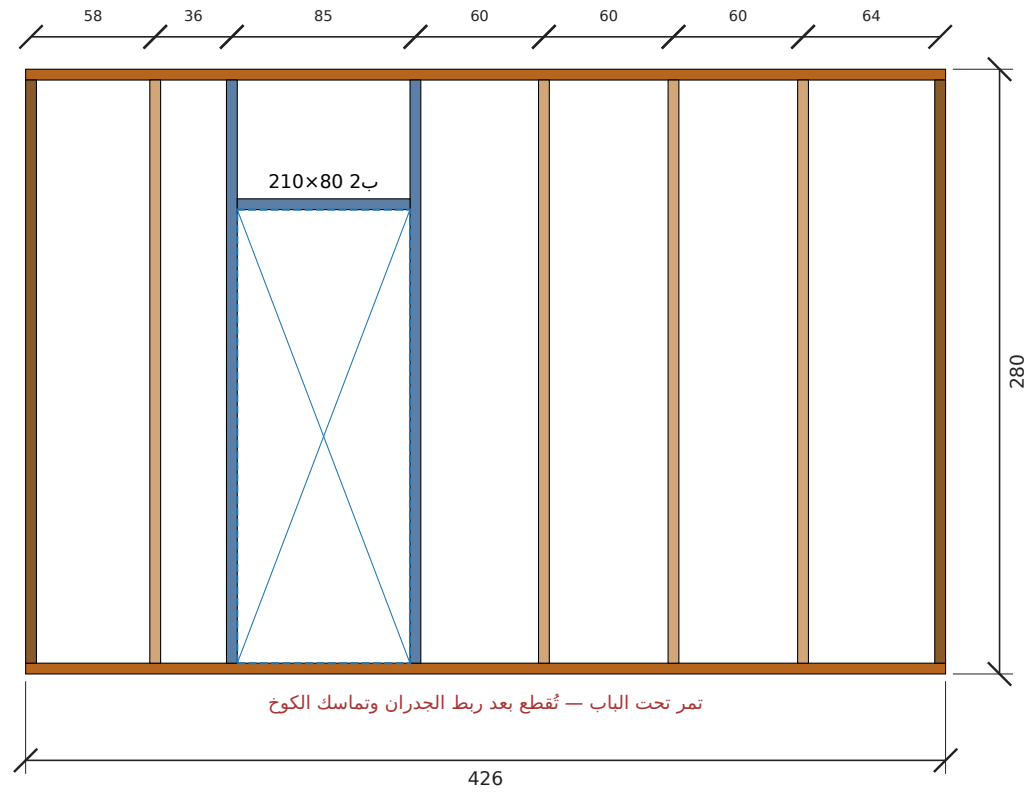


تأطير جدار د4-حمام مشترك — الطول 132 سم، الارتفاع 280 سم (داخلي)

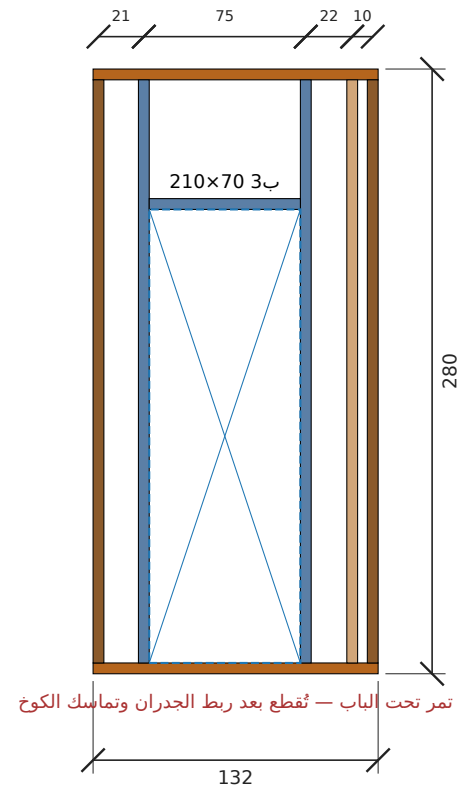


عمود قصير عمود زاوية عمود علوي قاعدة سفلية جنب فتحة رأس فتحة جلسة شباك رأس فتحة جنب فتحة عمود علوي قاعدة سفلية

تأطير جدار د5-حمام ماستر جنوب — الطول 162 سم، الارتفاع 280 سم (داخلي)

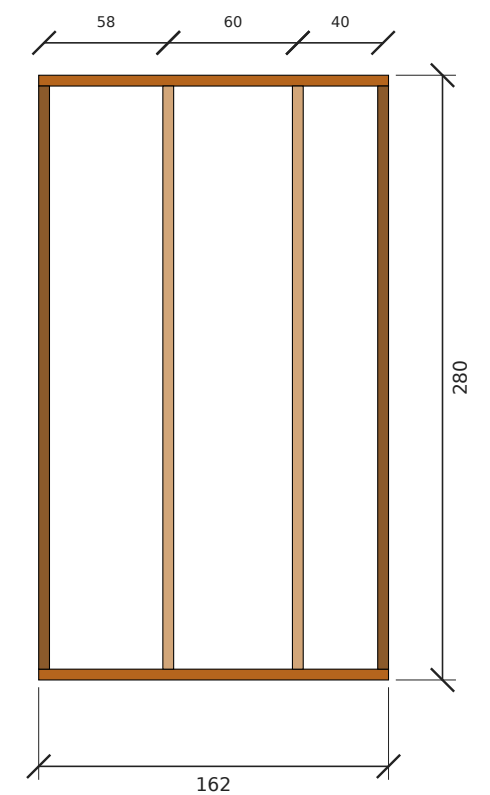

تأطير جدار د6-حمام ماستر غرب — الطول 192 سم، الارتفاع 280 سم (داخلي)

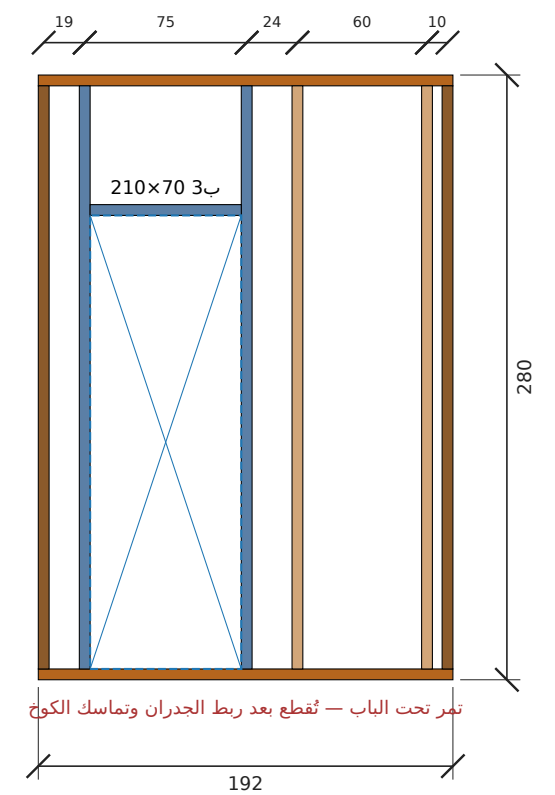

عمود قصير عمود زاوية عمود عمود علوي قاعدة سفلية جلسة شباك رأس فتحة جنب فتحة

جدول الكميات وخطة تقطيع الطبلیات

| البند                               | القيمة                                                                                     |
|-------------------------------------|--------------------------------------------------------------------------------------------|
| الارتفاع المطلوب / المعتمد          | 280 / 280 سم                                                                               |
| السقف                               | جملون 25° — قمة 462 سم من وجه الصبة                                                        |
| المدادات 15×5                       | 38 مداد (19 لكل جهة) × 474 سم — من طبلية 480                                               |
| طبلیات الطريقة الأولى (مداد + عمود) | 38 طبلية × 480 سم                                                                          |
| طبلیات الطريقة الثانية (3 أعمدة)    | 31 طبلية × 320 سم                                                                          |
| إجمالي الطبلیات 22.5×5              | 69                                                                                         |
| إجمالي قطع 5×7                      | 157                                                                                        |
| فائمة تقطيع 5×7                     | 768سم×10   426سم×4   300سم×1   270سم×100   192سم×2   162سم×2   160سم×4   145سم×1   140سم×4 |
|                                     | 132سم×2   105سم×2   100سم×8   95سم×4   90سم×1   80سم×2   70سم×2   60سم×4   25سم×4          |
| ألواح تلبیس 2.5 سم                  | 280 لوح × 400 سم (مجموع الصفوف 1047.4 م، 20 وجه)                                           |
| أسمنت بورد 12 مم (244×122)          | 28 لوح (داخل دورات المياه)                                                                 |
| العزل                               | بدون (غير مطلوب)                                                                           |
| الصبة                               | يجهزها العميل — 20 سم، مفرغة تحت دورات المياه                                              |

مراجعة التصميم مقابل قواعد المصنع

| النوع  | البند               | التفاصيل   | المقترح |
|--------|---------------------|---|---------|
| ملاحظة | بحر المدادات        | أطول بحر بدون جدار داخلي يحمل المداد: جهة أ: 390 سم،<br>جهة ب: 390 سم. يحتاج رقم المصنع لأقصى بحر مسموح لتحديد<br>المدادات اللي تُقوّى 5×20. |         |
| ملاحظة | الصبة والدرج        | ارتفاع الصبة 45 سم ← 3 درجة بقائمة 15.0 سم.                                                                                                  |         |
| ملاحظة | مناسيب رؤوس الفتحات | رؤوس الأبواب والشبايك على مناسيب مختلفة: 265 ،240 ،210 سم.                                                                                   |         |
| سؤال   | يحتاج تأكيد         | أقصى بحر للمداد بدون جدار داخلي قبل إضافة تقوية 5×7<br>(مداد 5×20)؟                                                                          |         |
| سؤال   | يحتاج تأكيد         | التغطية الصافية للوح التلبيس بعد التعشيق (مستنتجة<br>مؤقتاً 18.67 سم من 280/15)؟                                                             |         |
| سؤال   | يحتاج تأكيد         | هل يوضع أعمدة قصيرة فوق رأس الشباك/الباب إلى العلوي؟                                                                                         |         |
| سؤال   | يحتاج تأكيد         | مكان الوصلة في القاعدة والعلوي إذا الجدار أطول من<br>الطلبية؟                                                                                |         |