




المسقط الأفقي مع الفرش
الأبعاد بالسنتيمتر - الجدران: قوائم 5×7 + تليس 2.5 من الجهتين (12 سم)

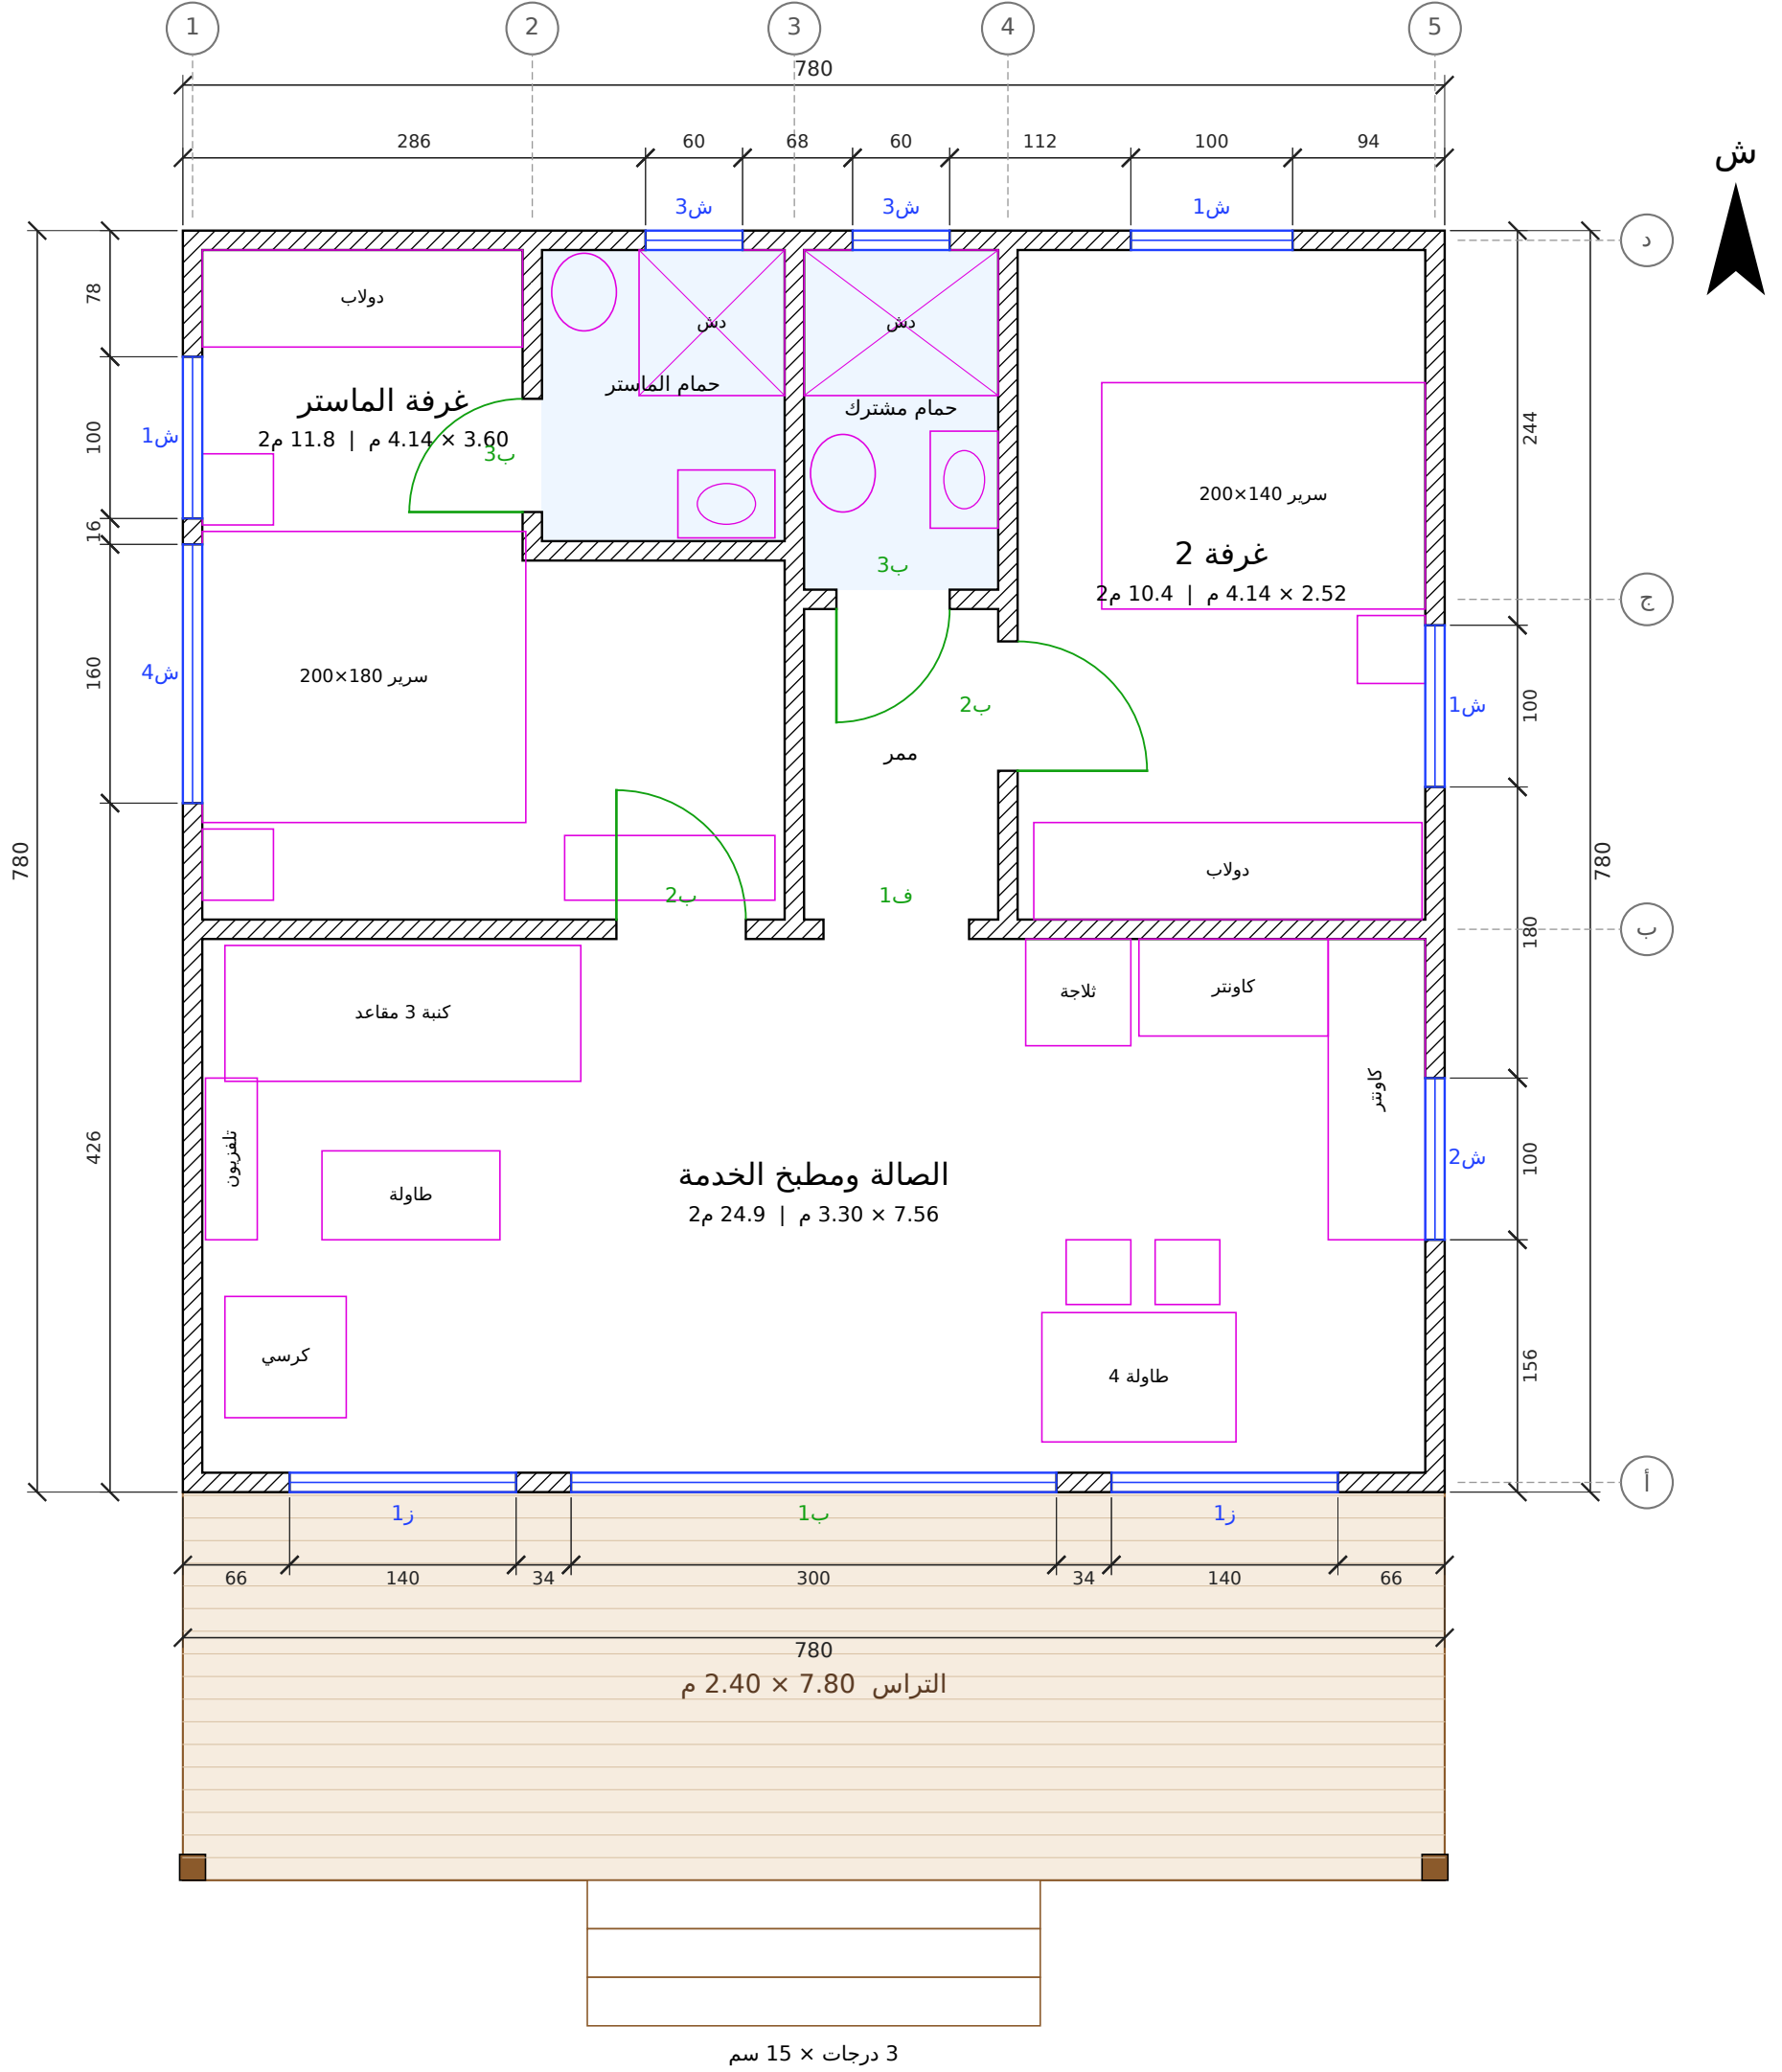

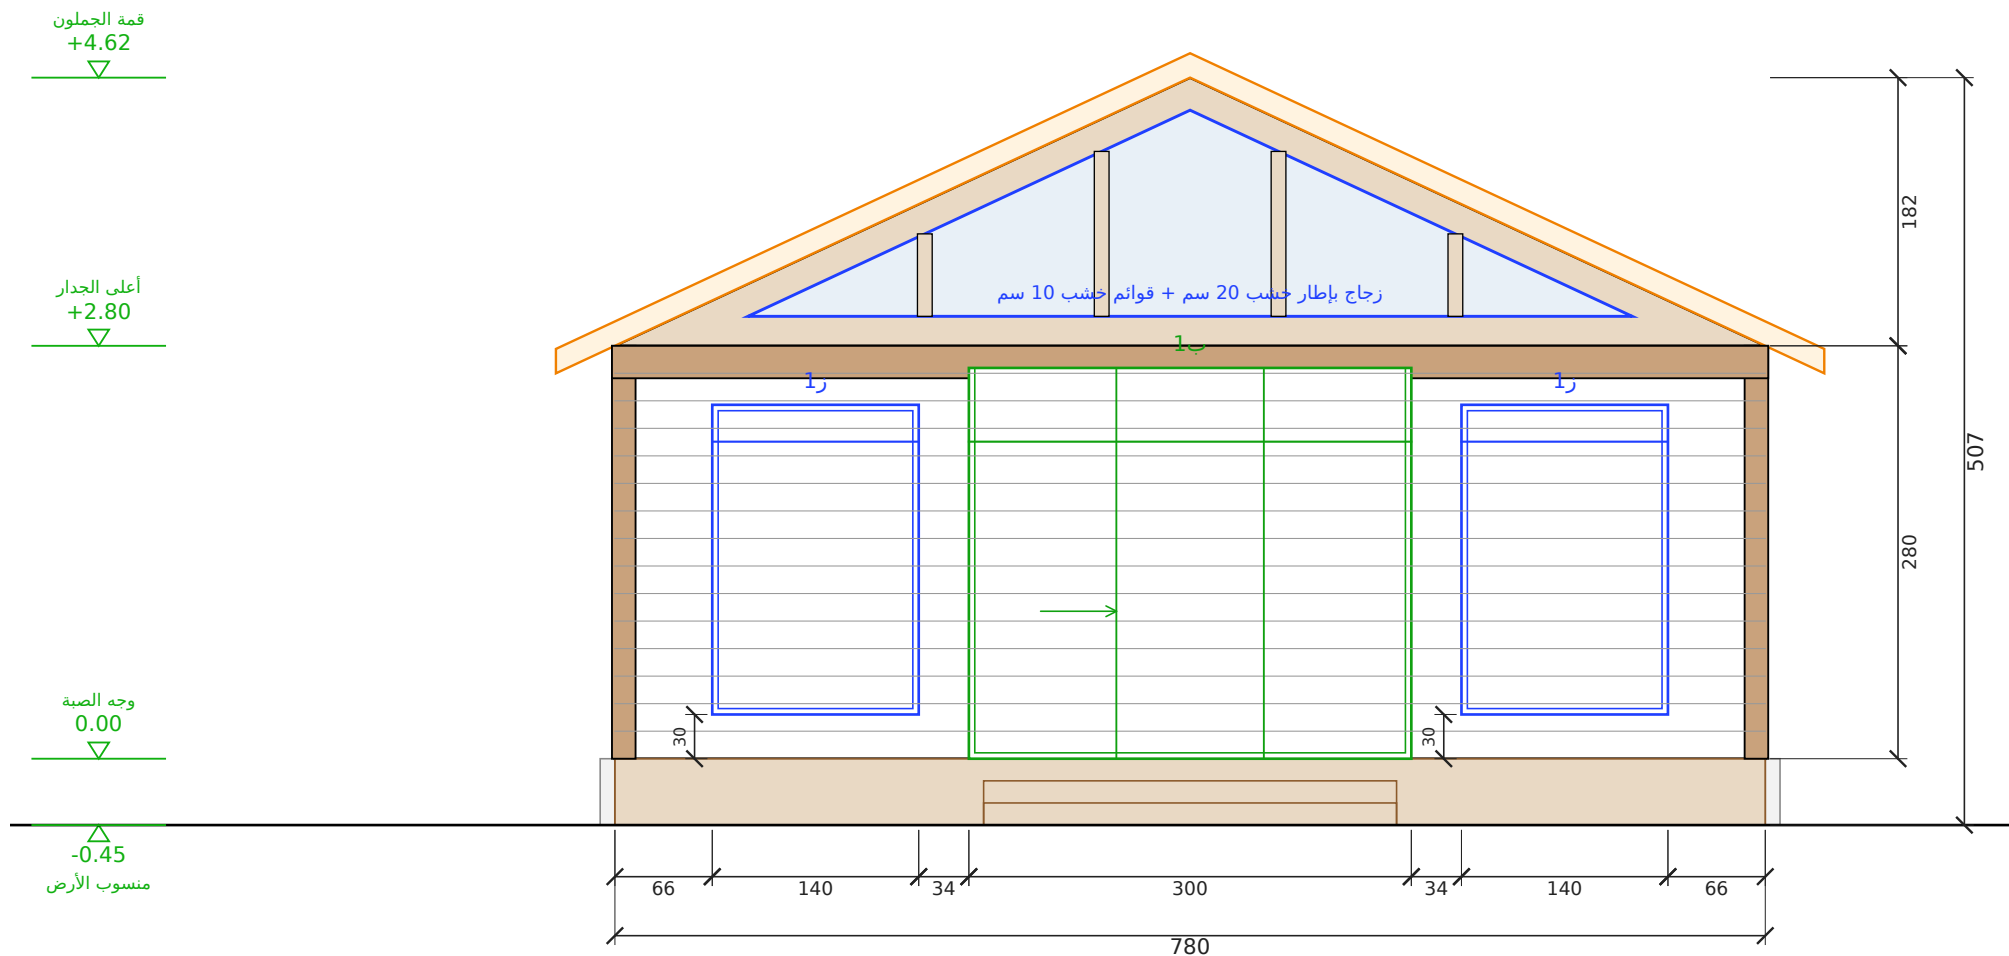


الواجهة الأمامية (التراس)

مقياس 1:50 | الوحدة: سم

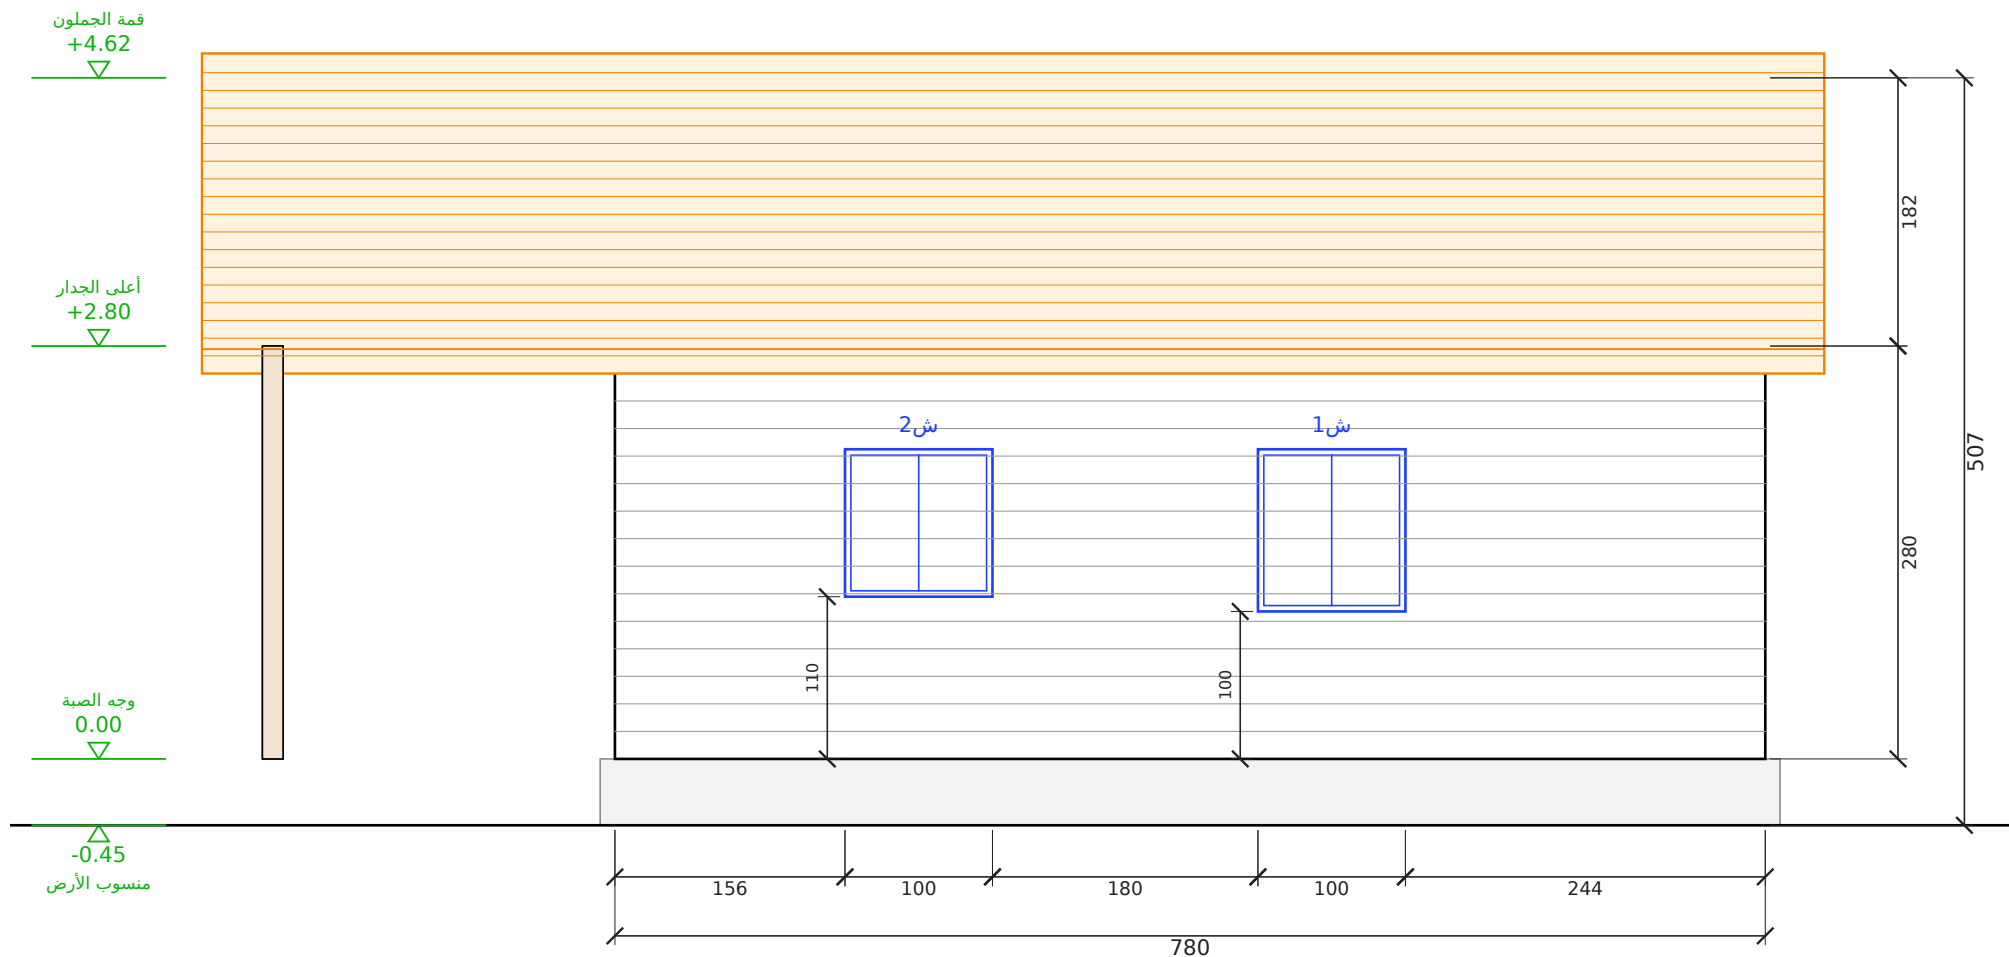


الواجهة الشرقية

مقياس 1:50 | الوحدة: سم

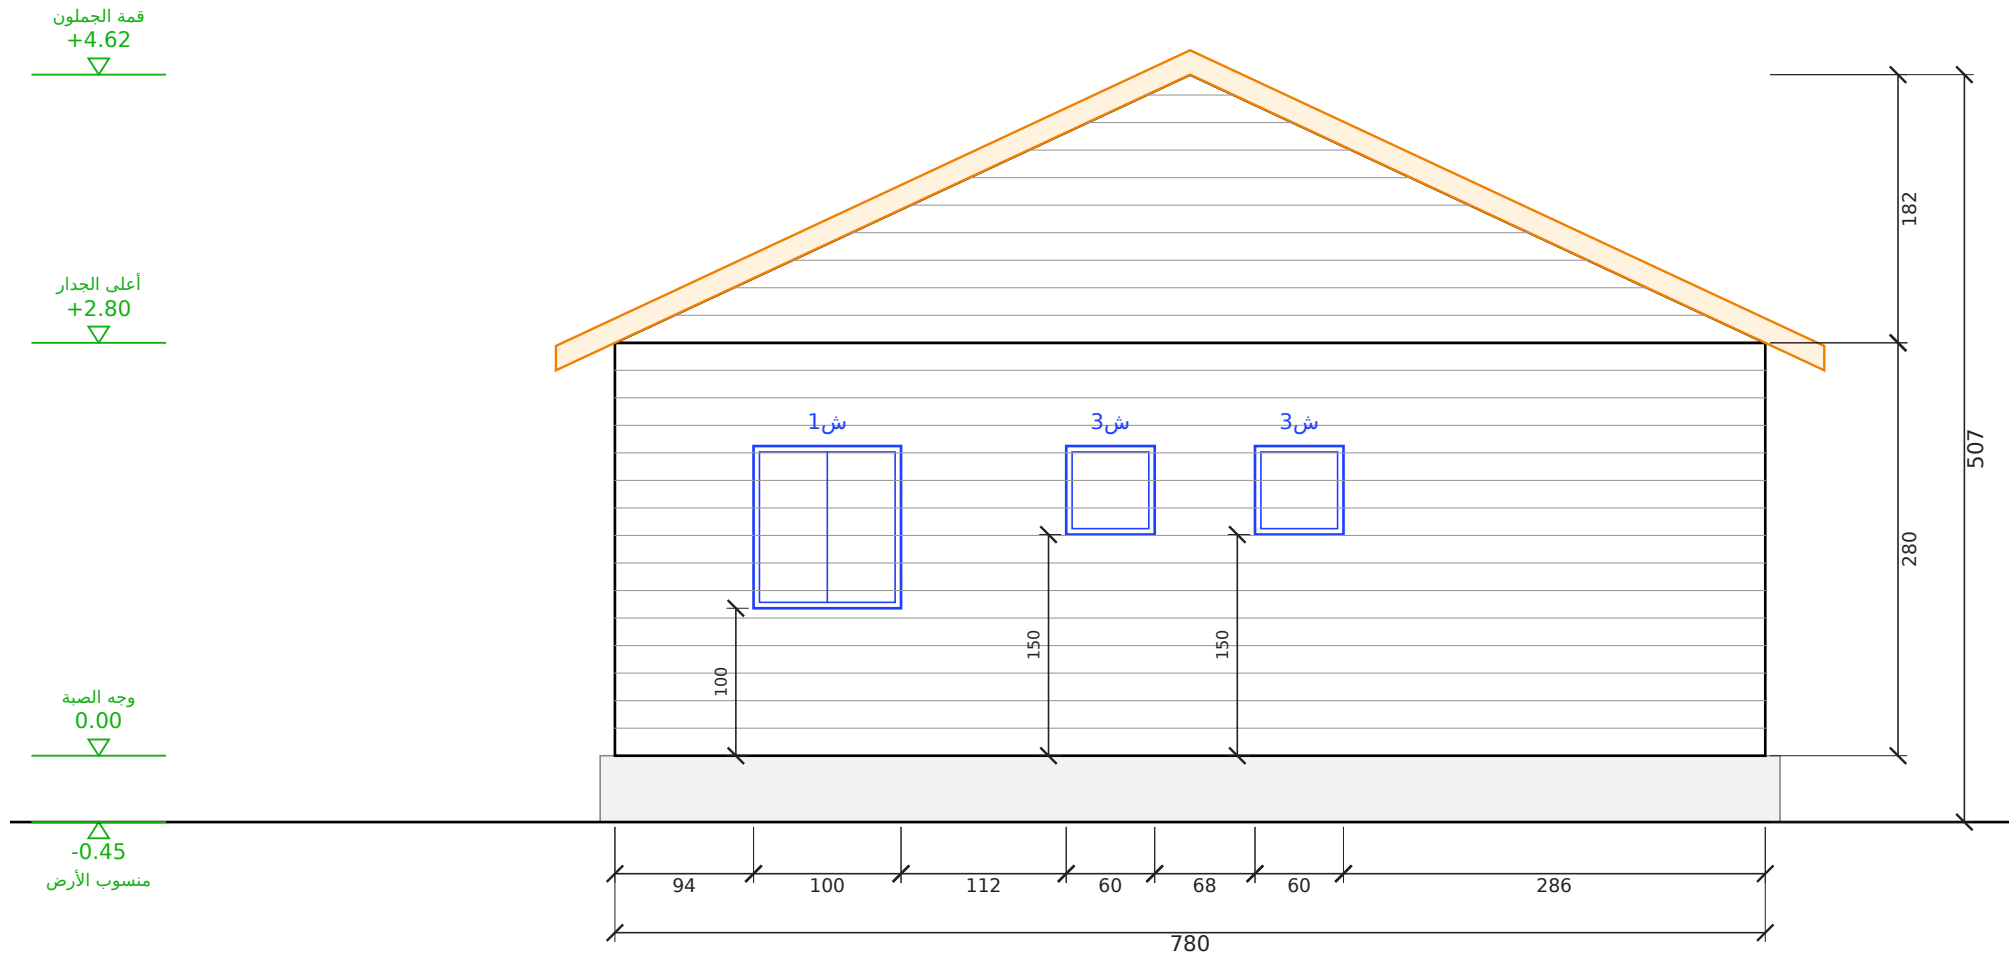

الواجهة الخلفية


مقياس 1:50 | الوحدة: سم

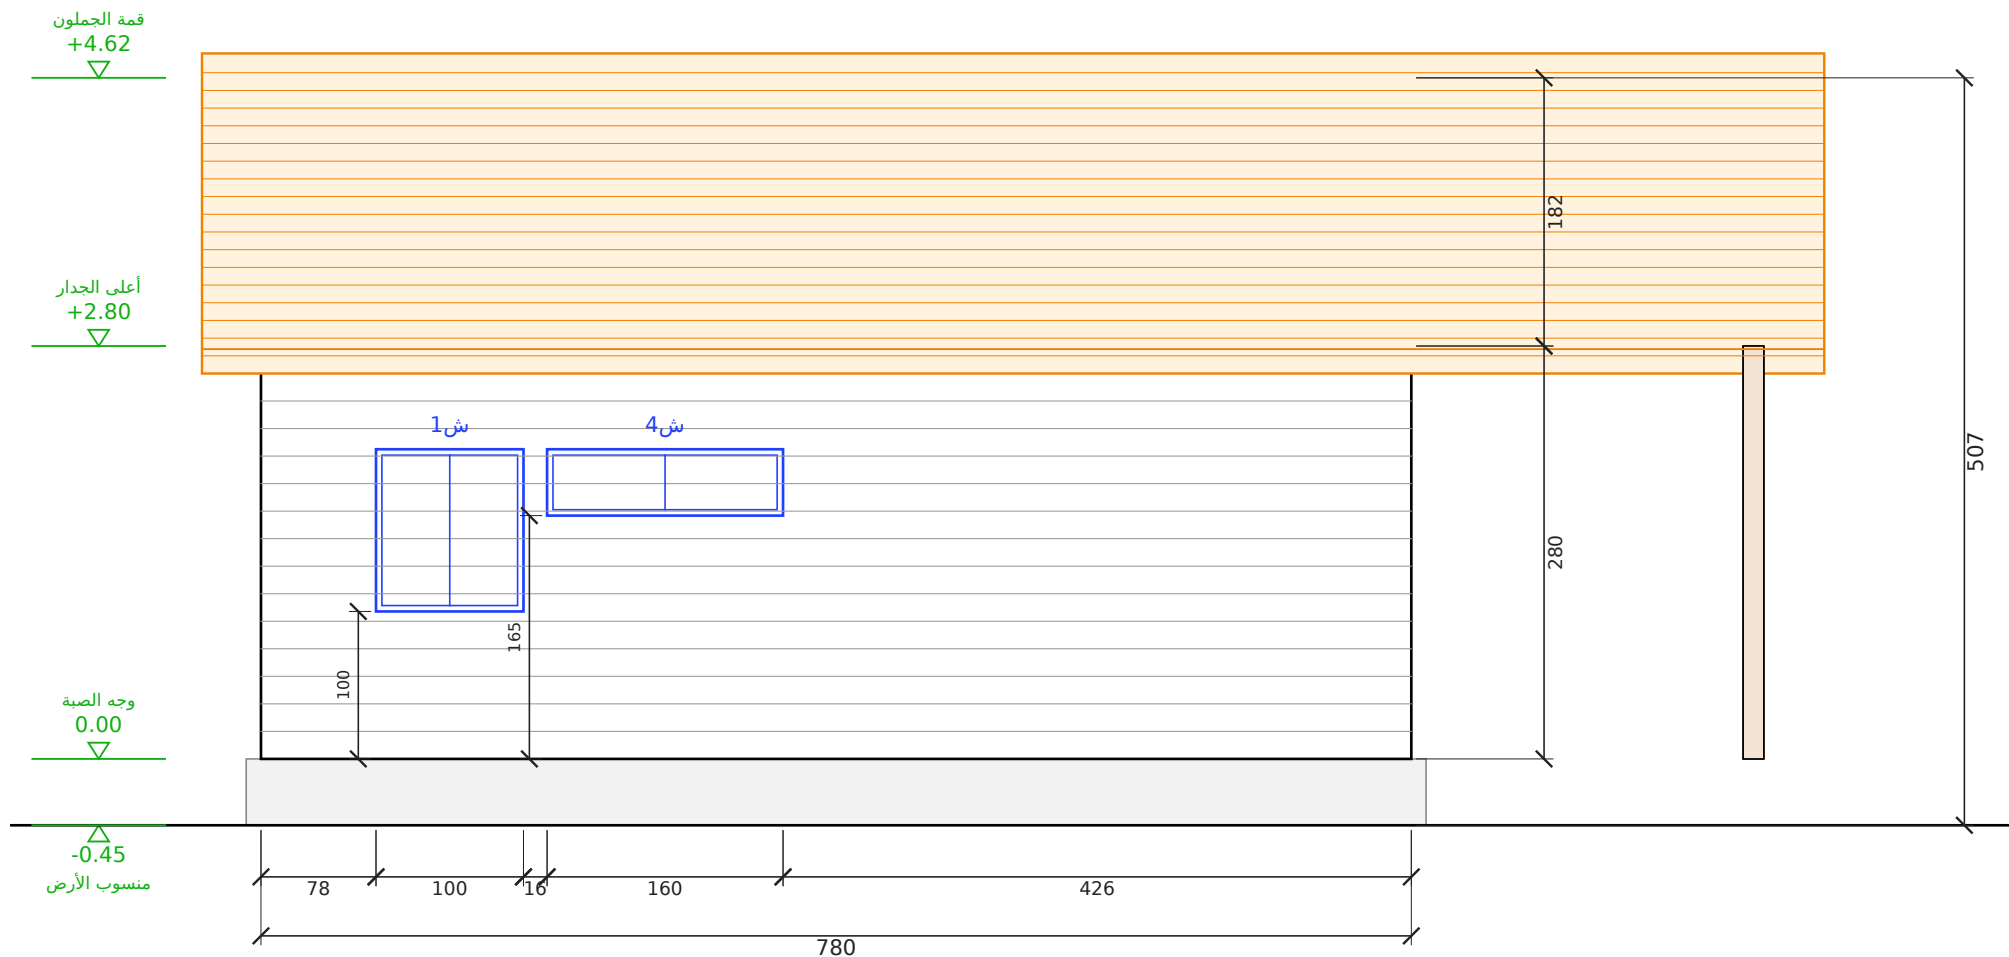

الواجهة الغربية


مقياس 1:50 | الوحدة: سم

مسقط السقف (جملون)
رفر 40 سم من كل جهة | مقياس 1:50

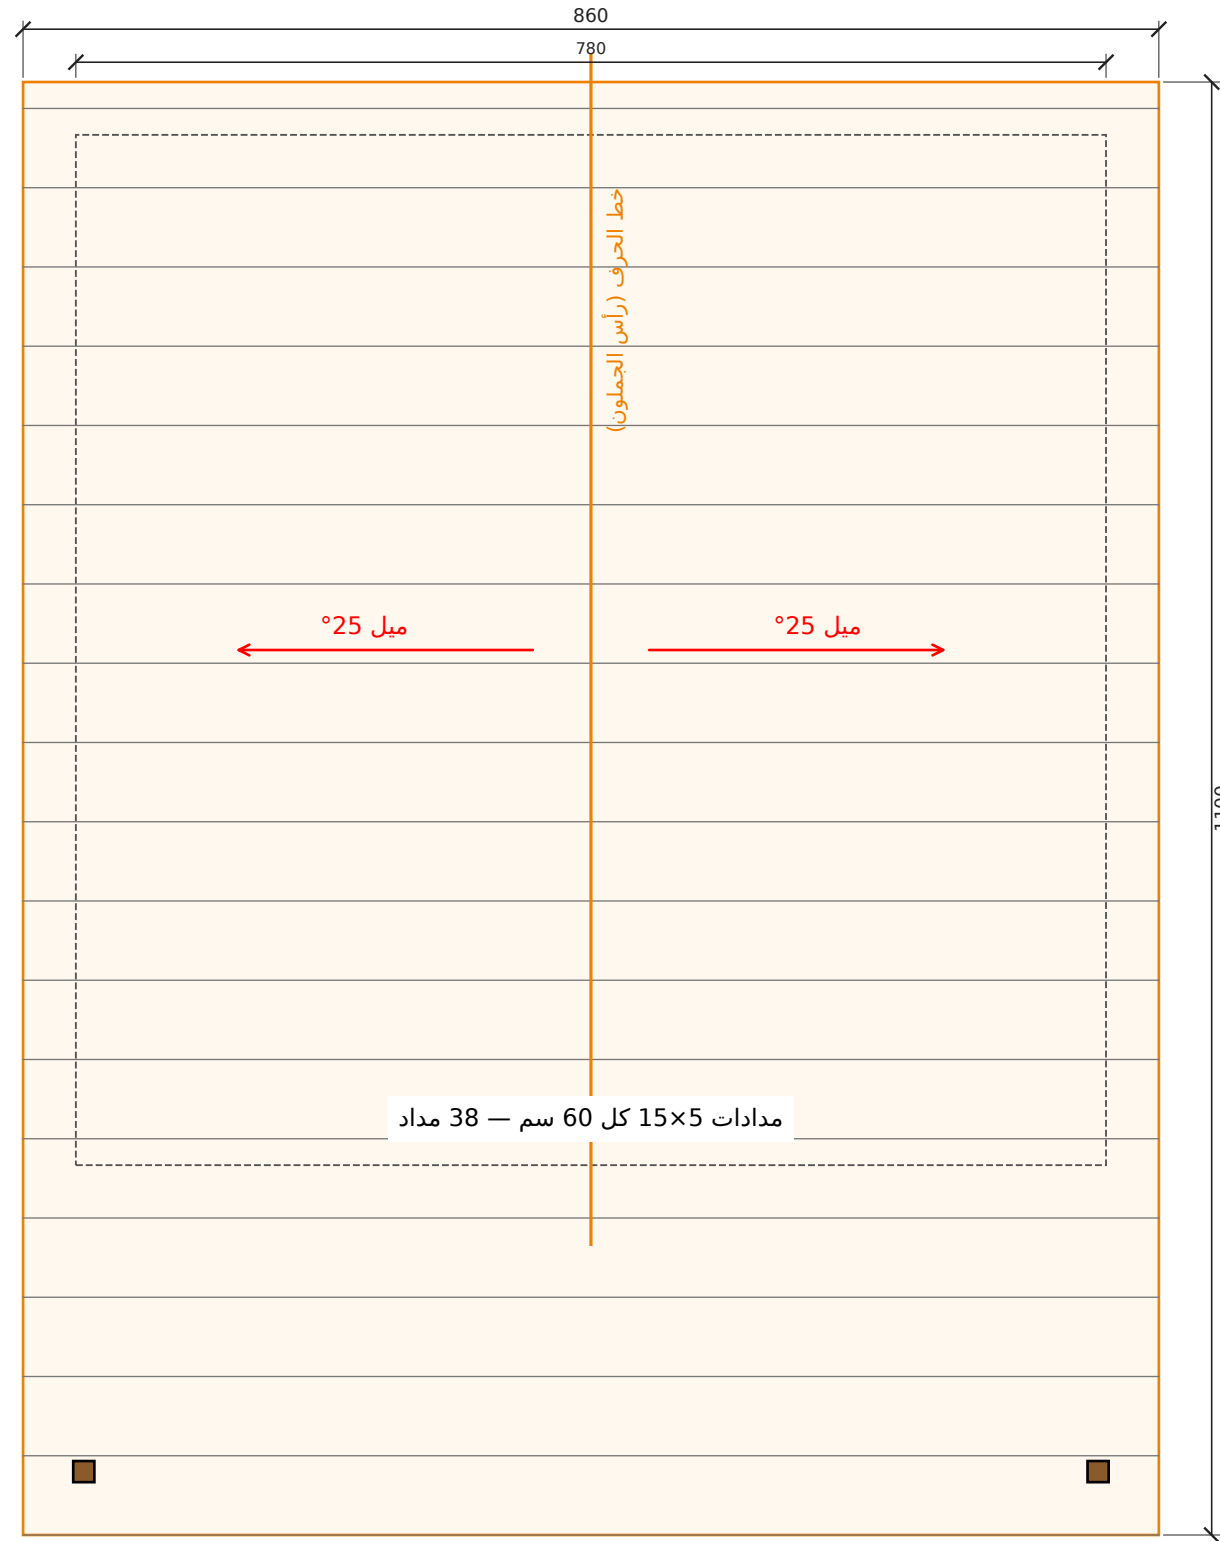


قطاع عرضي أ-أ
مقياس 1:50 | الوحدة: سم

مداد 15x5 بخلعة على العمود العلوي، مثبت ببرغي

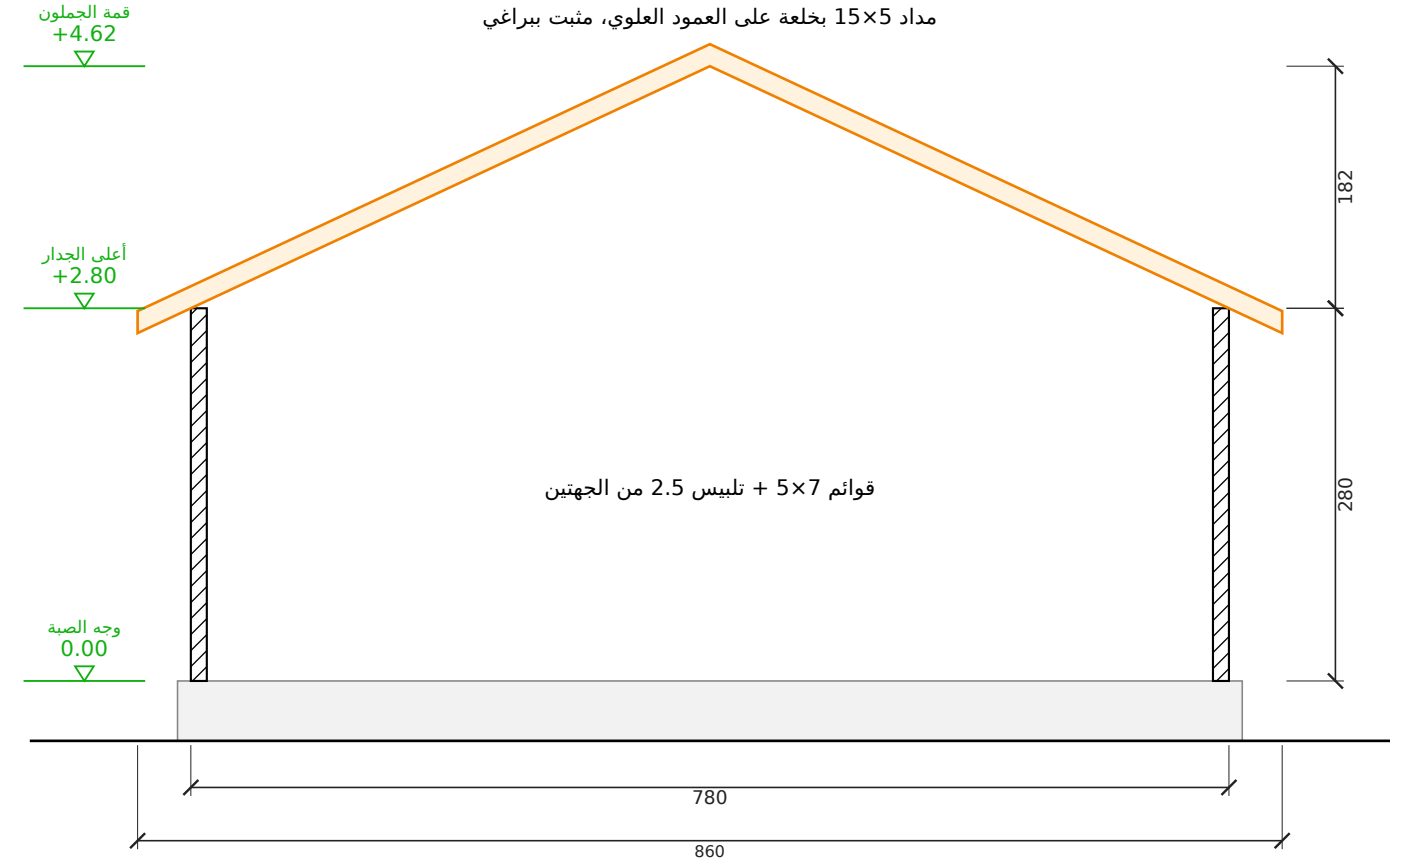

تفصيلة جلوس المداد على العلوي (1:5)

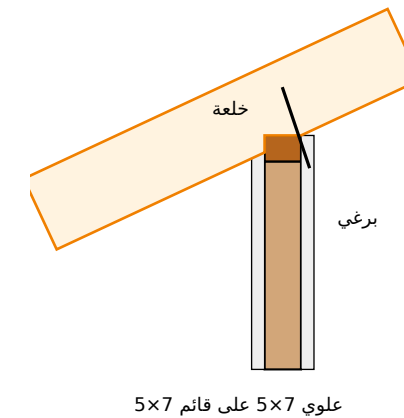

جدول مقاسات الأبواب والشبابيك
مقاس الفتحة الصافي في الجدار - الوحدة: سم

الرمز	النوع	العرض (سم)	الارتفاع (سم)	ارتفاع الجلسة (سم)	العدد	الموقع
ب1	باب	300	265	-	1	الأمامية (التراس)
ب2	باب	80	210	-	2	ماستر - غرفة 2
ب3	باب	70	210	-	2	حمام مشترك - حمام ماستر
ف1	باب	90	210	-	1	فتحة الممر
ز1	شباك	140	210	30	2	الأمامية (التراس) 2
ش1	شباك	100	110	100	3	الشرقية - الخلفية - الغربية
ش2	شباك	100	100	110	1	الشرقية
ش3	شباك	60	60	150	2	الخلفية 2
ش4	شباك	160	45	165	1	الغربية

الإجمالي: أبواب 6 - شبابيك 9

مصنع وتد الأخشاب
Watad Wood Factory

البند	القيمة
المشروع	كوخ غرفتين وتراس مسقوف 7.8×7.8
العميل	عميل — تصميم حسب الصورة
الموقع	—
الاستخدام	استراحة / استجمام
المدير	—
التاريخ	2026-09-29
المقياس	1:50
الوحدة	سم

التسعير

البند	القيمة
المساحة الإجمالية (م2)	60.84
مساحة التراس المسقوف (م2)	18.72
سعر المتر (ريال)	يُحدد بعد الاعتماد
الإجمالي (ريال)	—

جدول المساحات

م	الفراغ	الأبعاد الداخلية (م)	المساحة (م2)
1	الصالة ومطبخ الخدمة	7.56 × 3.30	24.95
2	غرفة الماستر	3.60 × 4.14	11.79
3	حمام الماستر	1.50 × 1.80	2.70
4	ممر	1.20 × 1.92	2.30
5	حمام مشترك	1.20 × 2.10	2.52
6	غرفة 2	2.52 × 4.14	10.43
	المساحة الصافية الداخلية		54.70
	المساحة الإجمالية الخارجية	7.80 × 7.80	60.84

المنظور ثلاثي الأبعاد والمواد

النمط: جوزي غامق + إطارات سوداء — معاينة تقريبية، الإخراج النهائي من 3ds Max

جدول المواد والألوان



الخشب / الصبغة

صبغة جوزي غامق



القرميد

قرميد رمادي غامق



الزجاج

زجاج عاكس غامق




إطارات الشبابيك والأبواب

إطار ألومنيوم أسود



الكنار والزوايا

نفس الصبغة أغمق درجة

 

الصبغة

خرسانة 45 سم


الدريزين: ألواح أفقية متقاربة (عصري)

تقسيم الشبابيك: بدون | الباب الرئيسي: سحب زجاج


أنواع الدريزين المعتمدة (من مشاريع المصنع)



قوائم رأسية متقاربة (صورة 1)

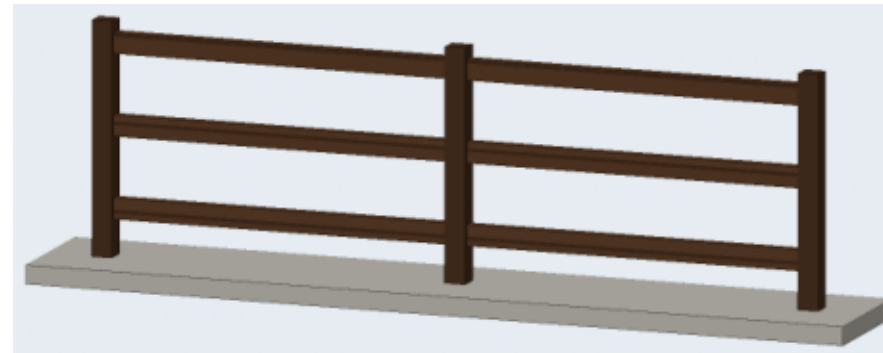

3 مرباع أفقية (صورة 2)

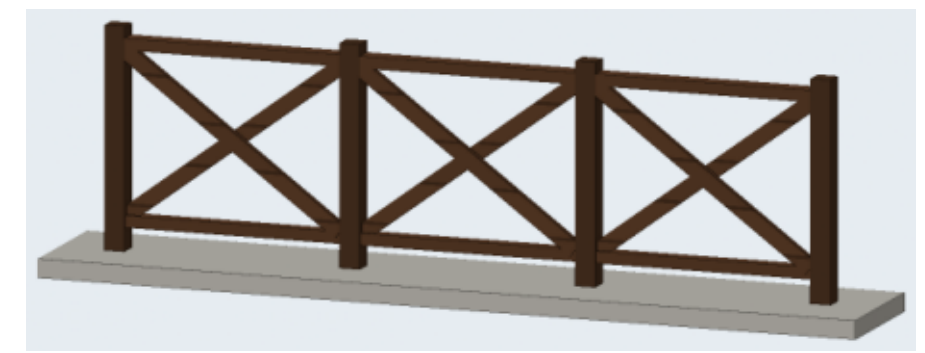

تقاطع X (صورة 5)