



المسقط الأفقي مع الفرش — الدور الأرضي
الأبعاد بالسنتيمتر - الجدران: قوائم 5×7 + تليس 2.5 من الجهتين (12 سم) | منسوب الأرضية 0.00+

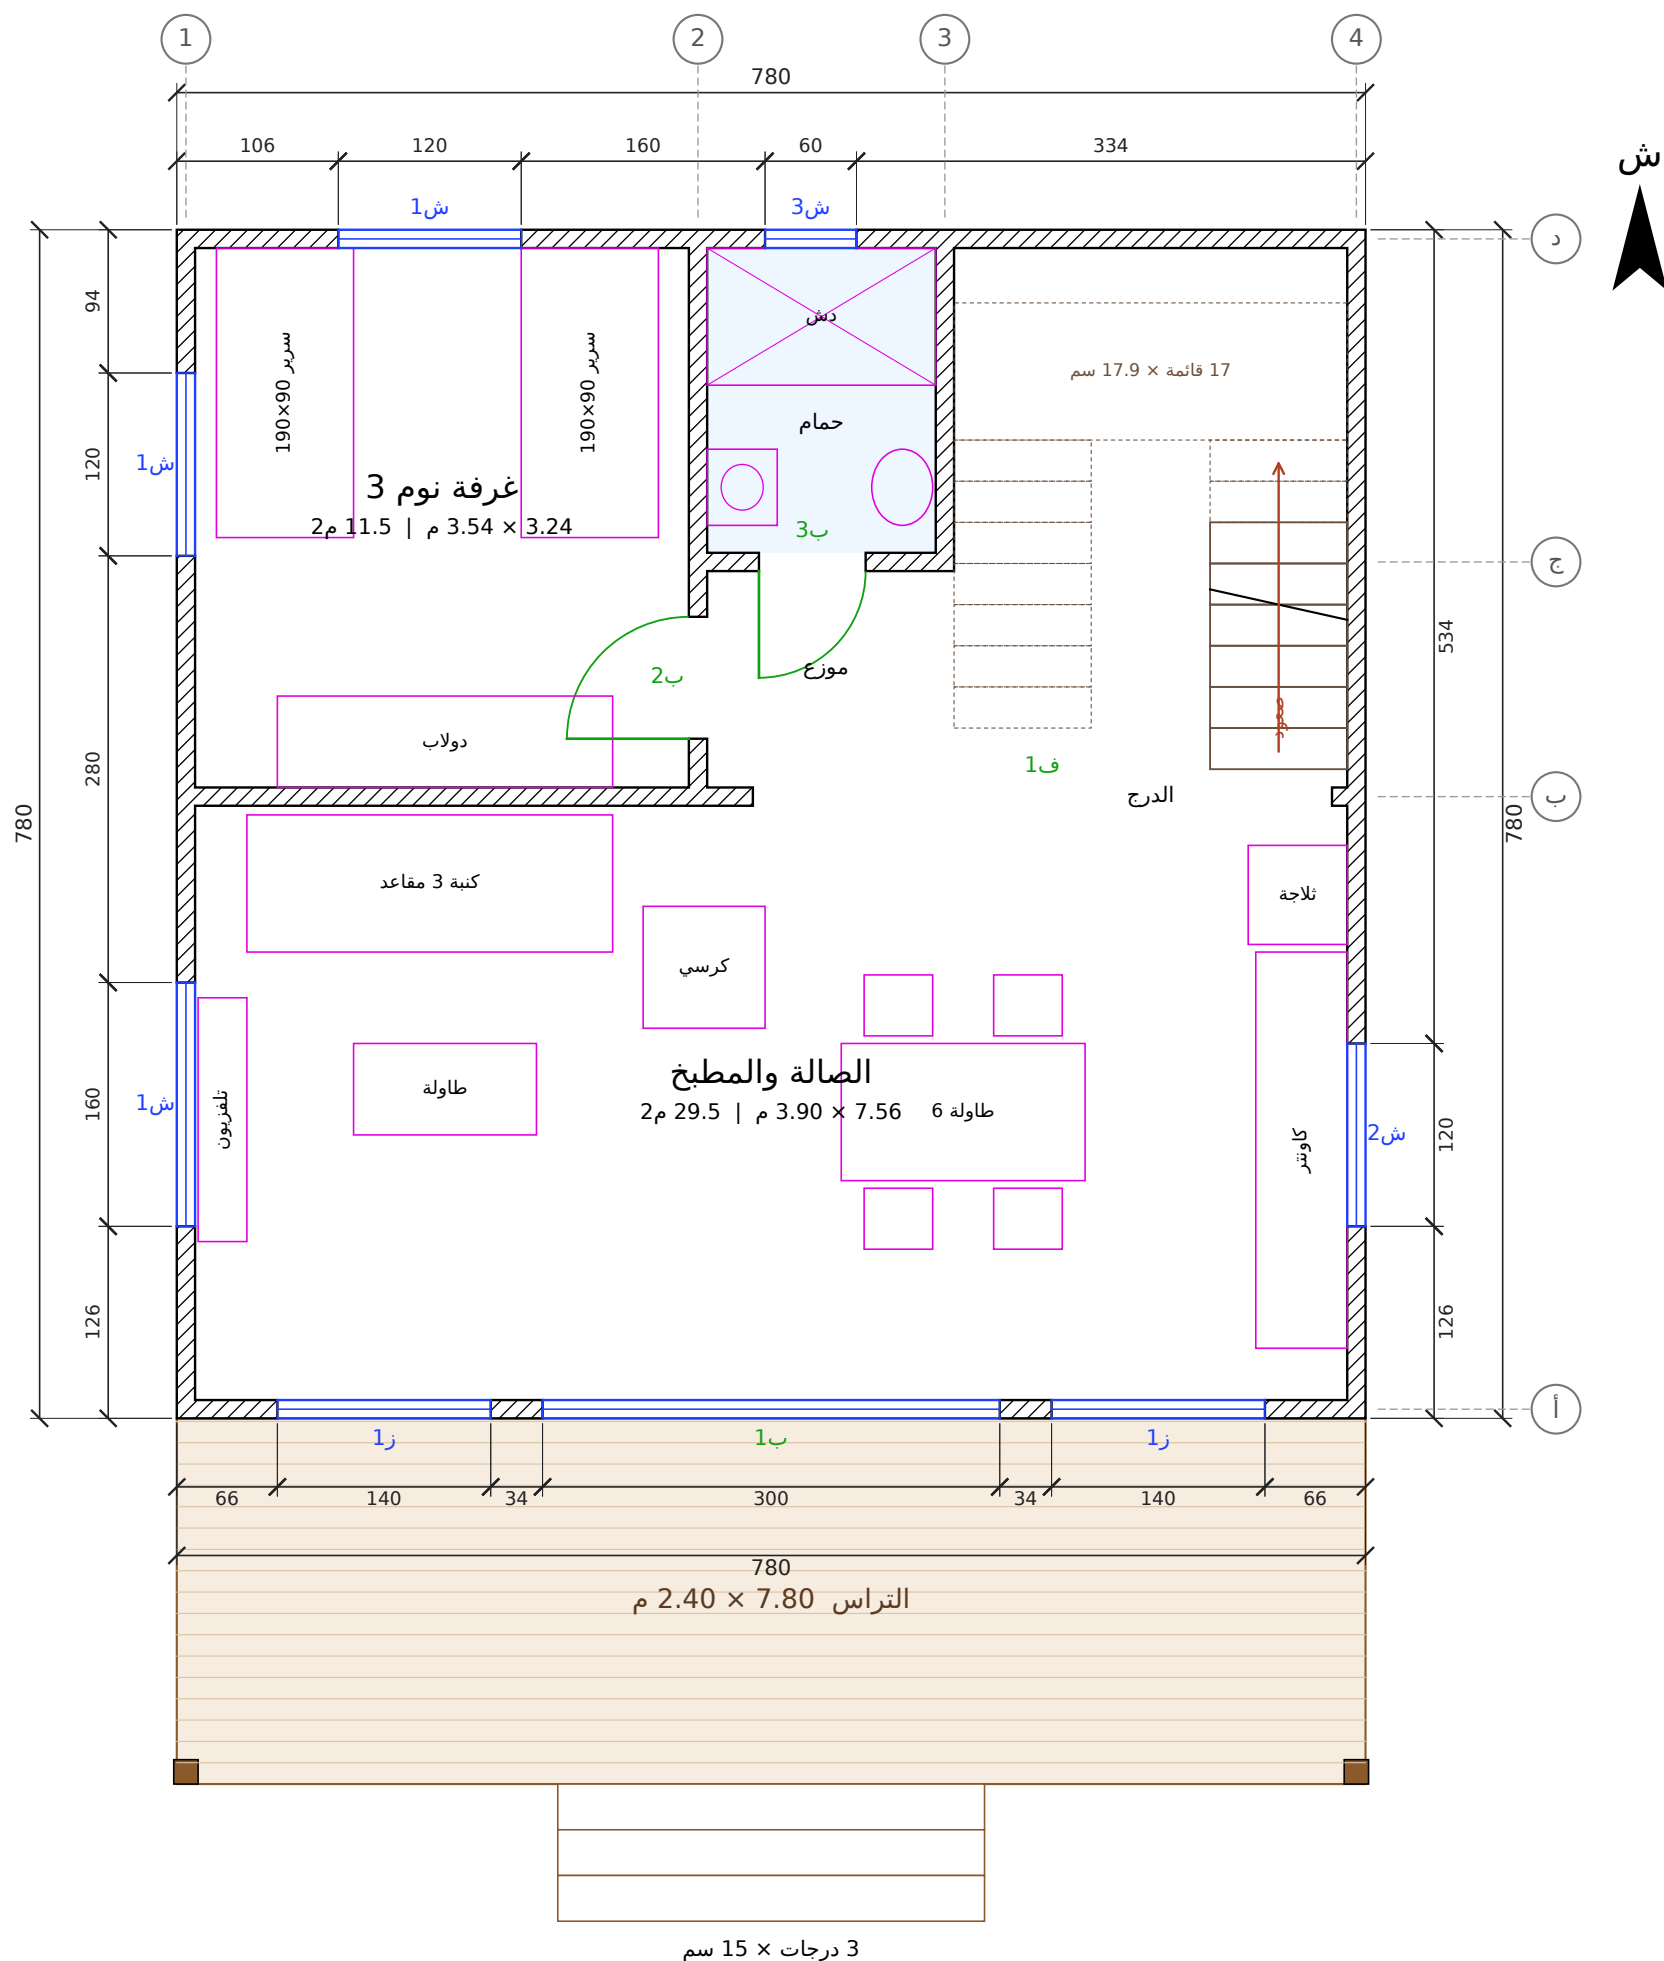


رقم اللوحة	التاريخ	المقياس	عنوان اللوحة	المشروع / العميل	مصنع وتد الأخشاب Watad Wood Factory
A-01 (1/14)	2026-09-29	1:50	المسقط الأفقي — الدور الأرضي	كوخ دورين 3 غرف نوم — 120 م ² عميل جديد	

المسقط الأفقي مع الفرش - الدور الأول
الأبعاد بالسنتيمتر - الجدران: قوائم 5×7 + تليس 2.5 من الجهتين (12 سم) | منسوب الأرضية +3.05

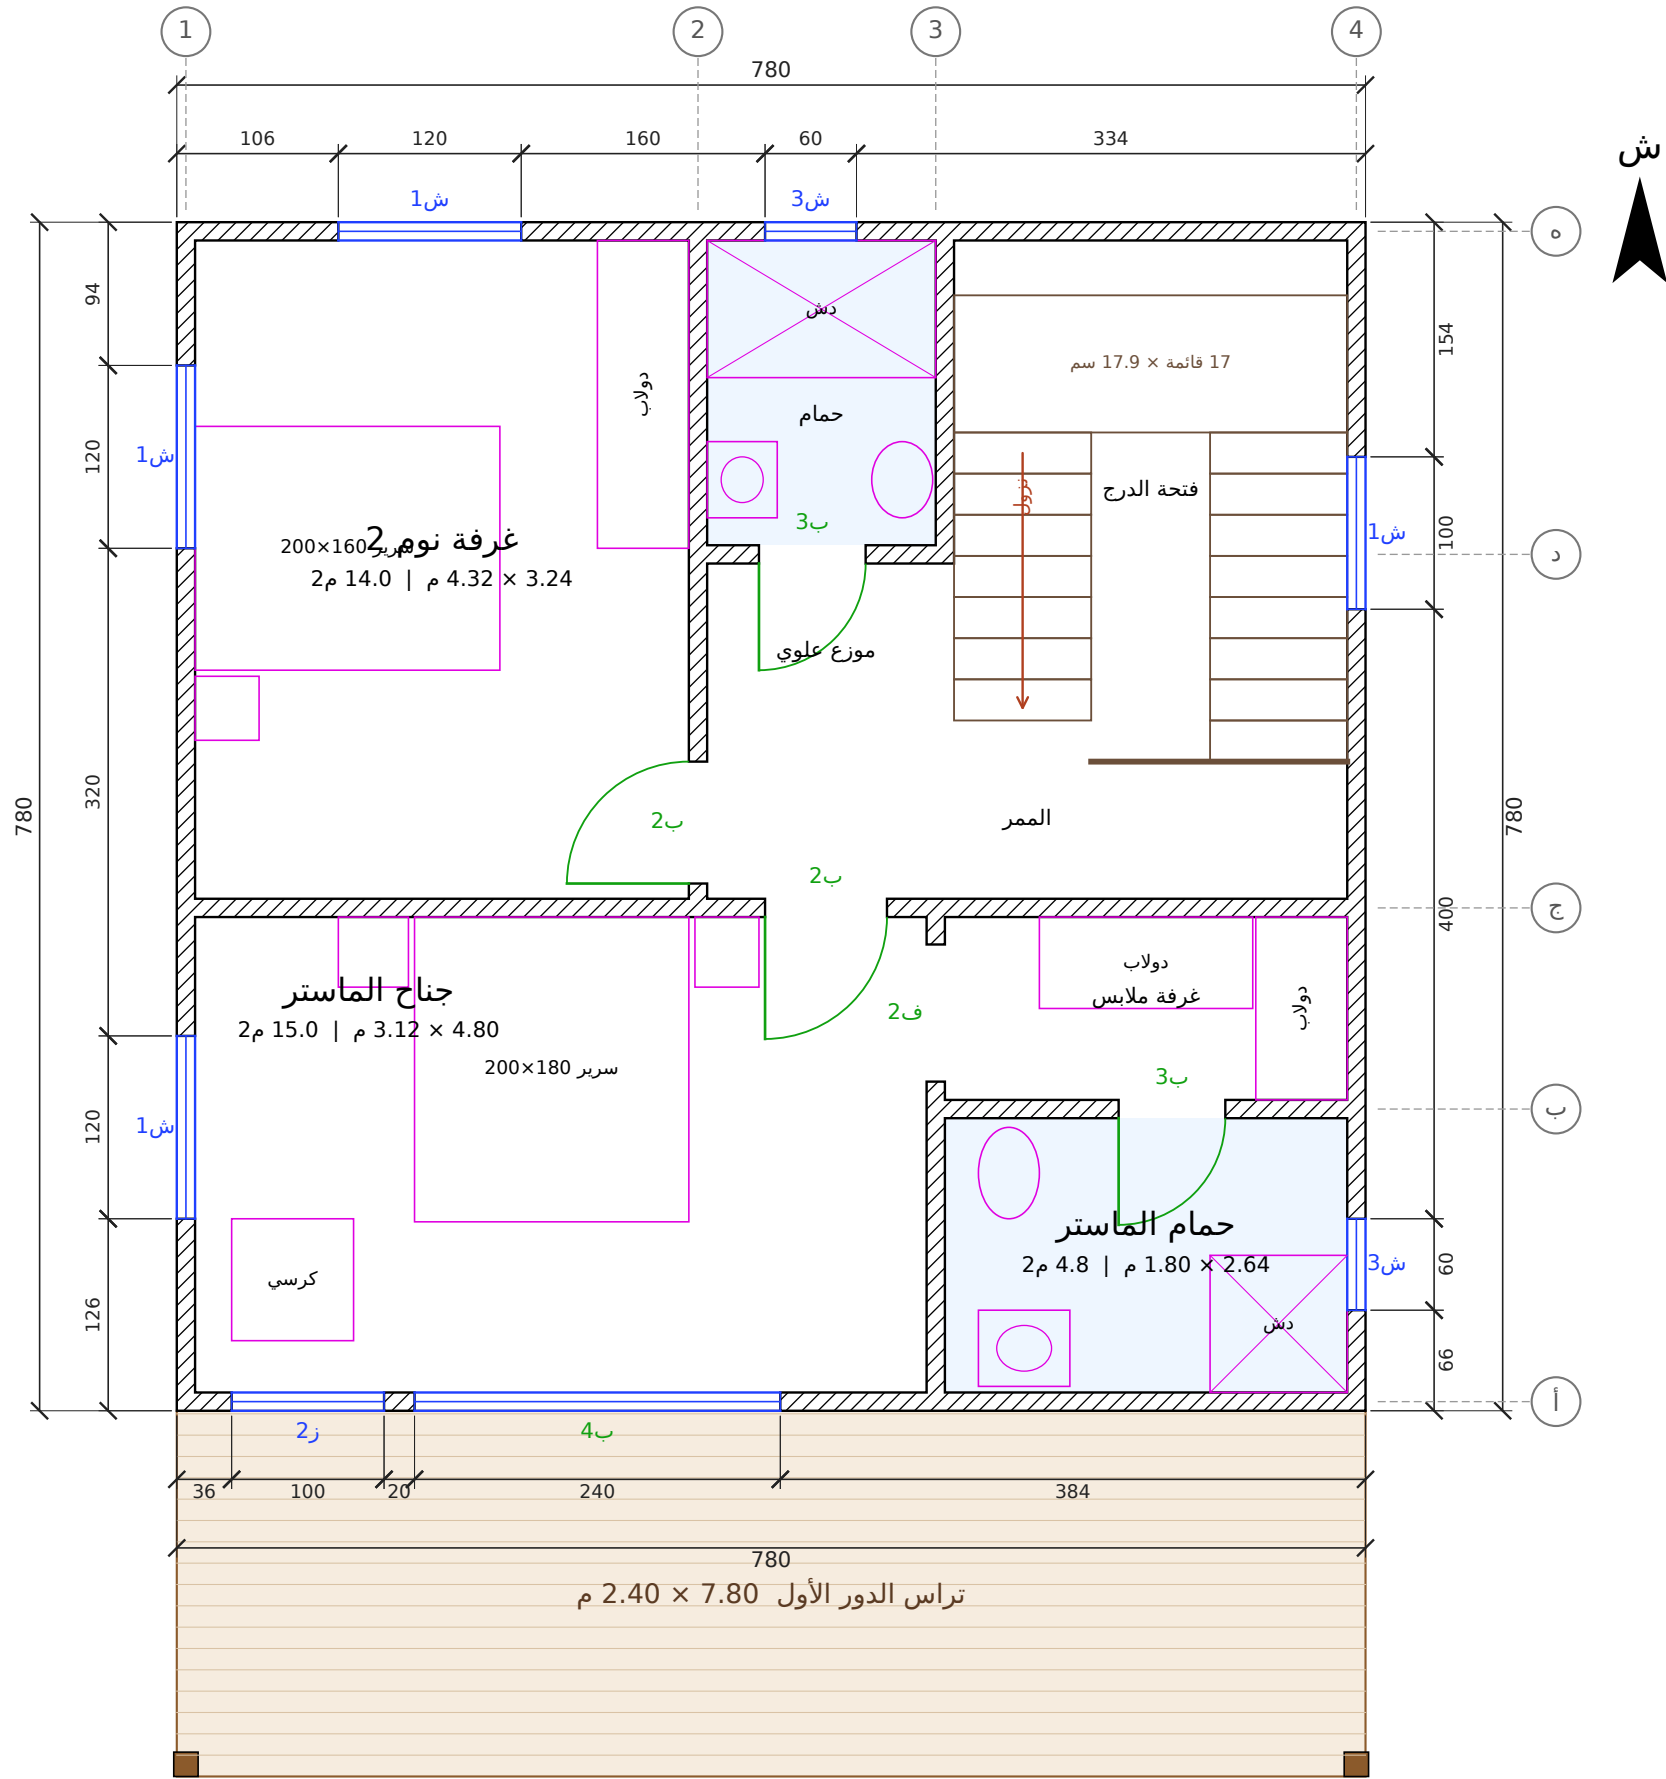


رقم اللوحة	التاريخ	المقياس	عنوان اللوحة	المشروع / العميل	مصنع وتد الأخشاب Watad Wood Factory
A-02 (2/14)	2026-09-29	1:50	المسقط الأفقي - الدور الأول	كوخ دورين 3 غرف نوم - 120 م ² عميل جديد	

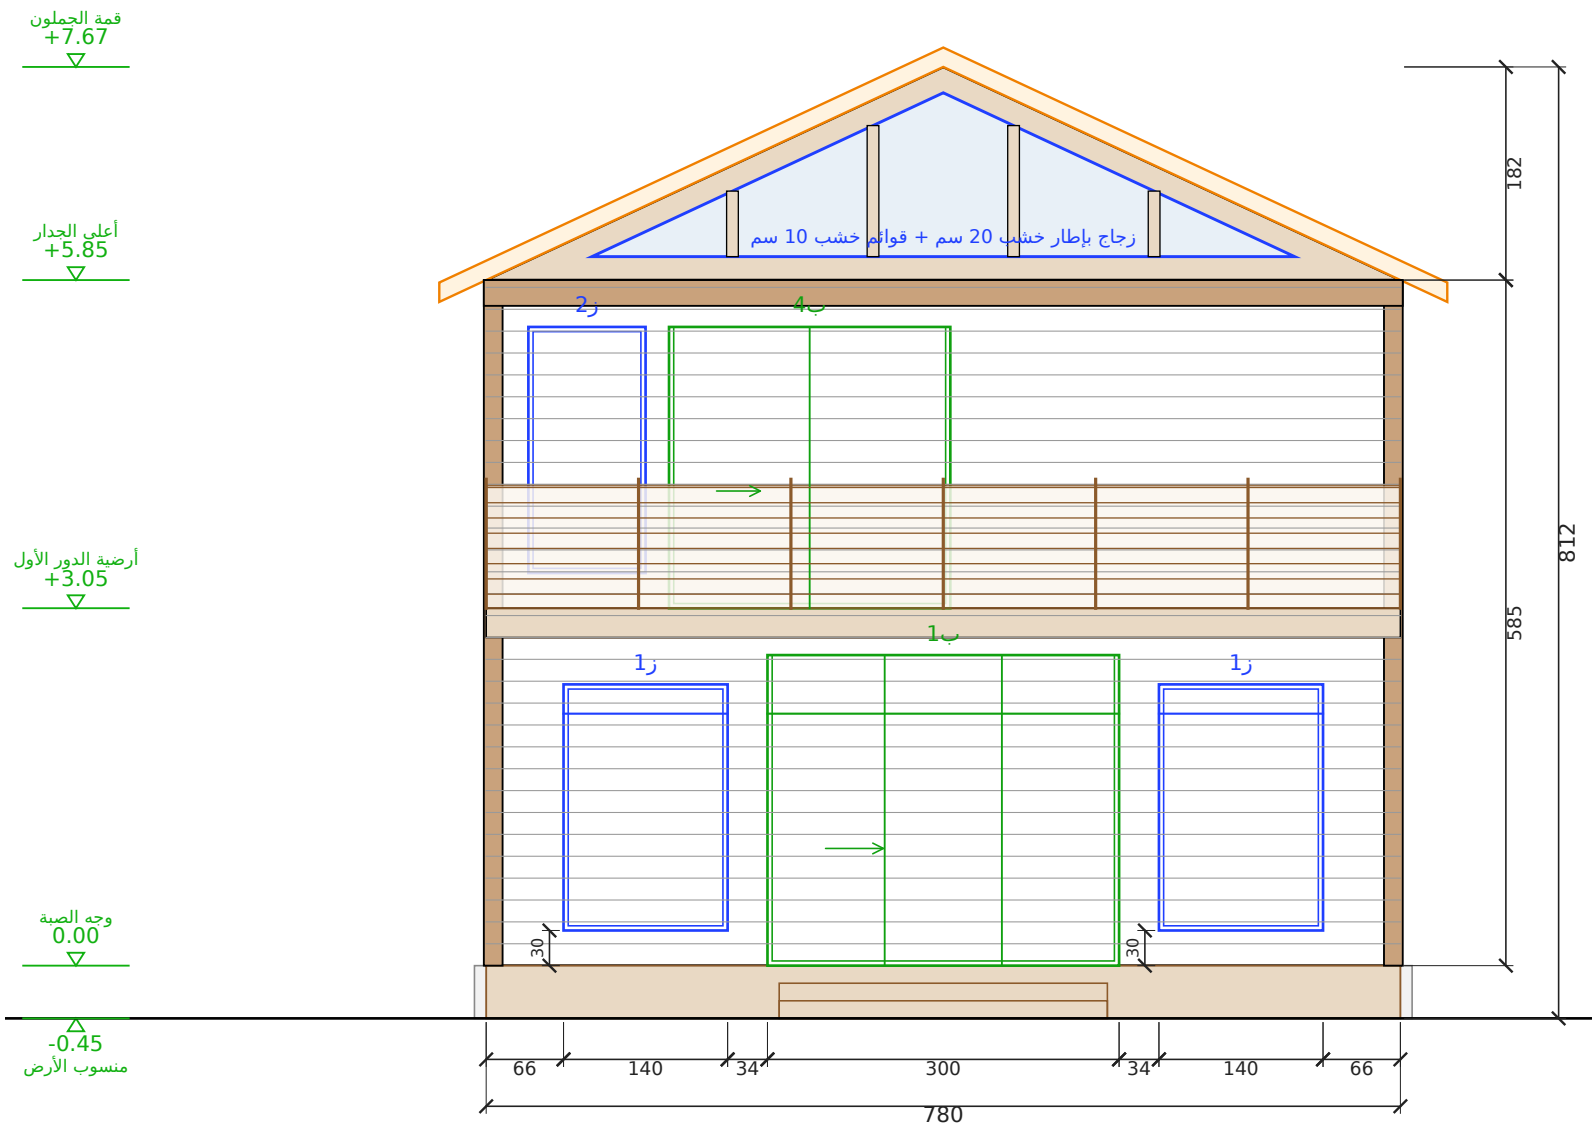

الواجهة الأمامية (التراس)


مقياس 1:50 | الوحدة: سم

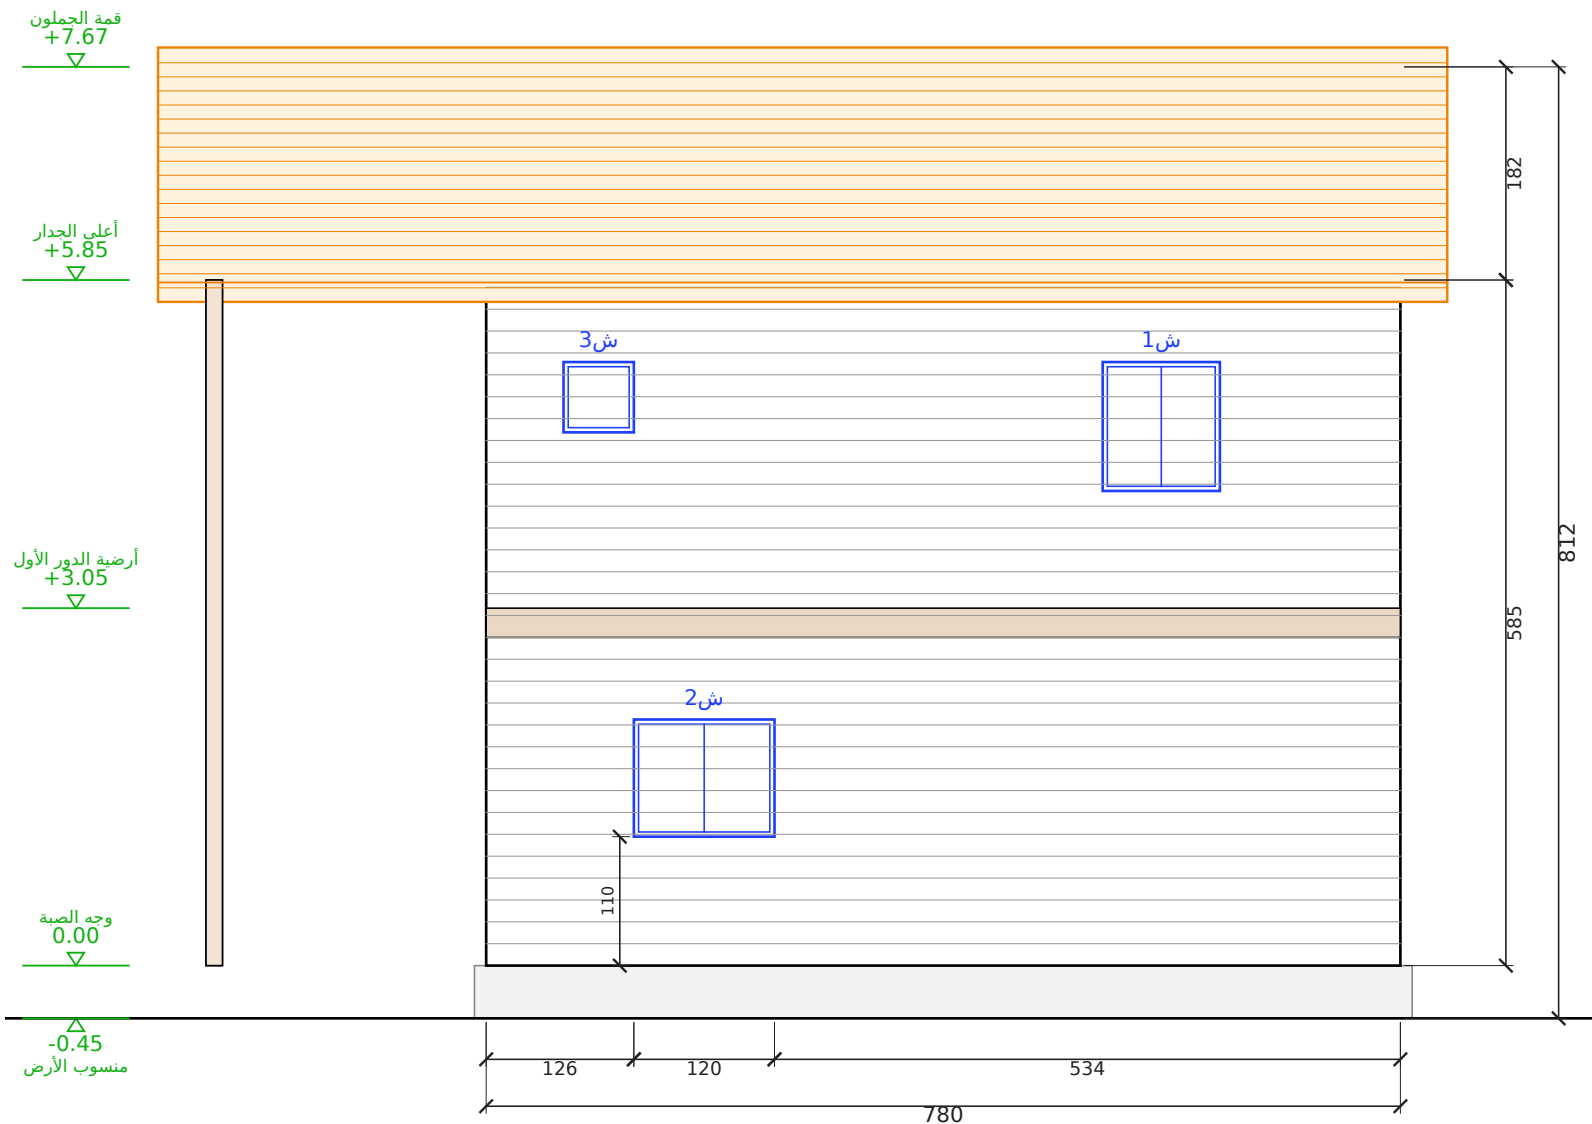

الواجهة الشرقية


مقياس 1:50 | الوحدة: سم

رقم اللوحة	التاريخ	المقياس	عنوان اللوحة	المشروع / العميل	مصنع وتد الأخشاب Watad Wood Factory
A-03 (3/14)	2026-09-29	1:50	الواجهة الأمامية (التراس) والواجهة الشرقية	كوخ دورين 3 غرف نوم — 120 م ² عميل جديد	

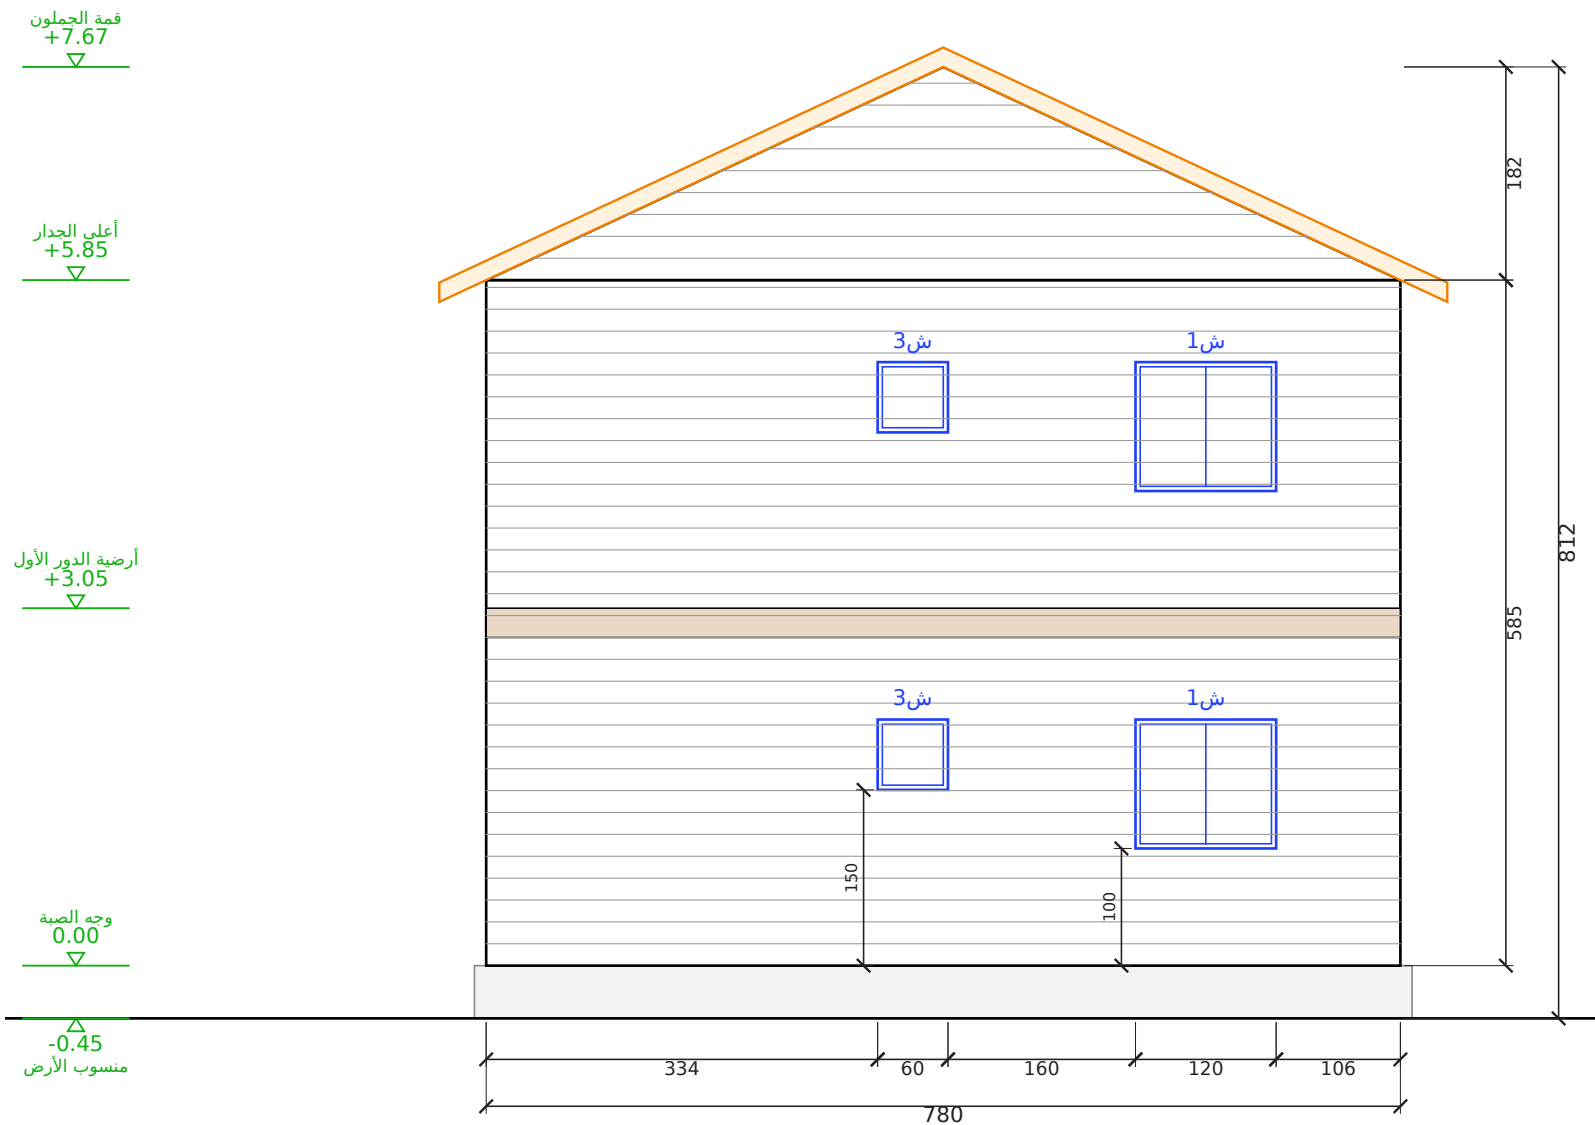

الواجهة الخلفية

مقياس 1:50 | الوحدة: سم

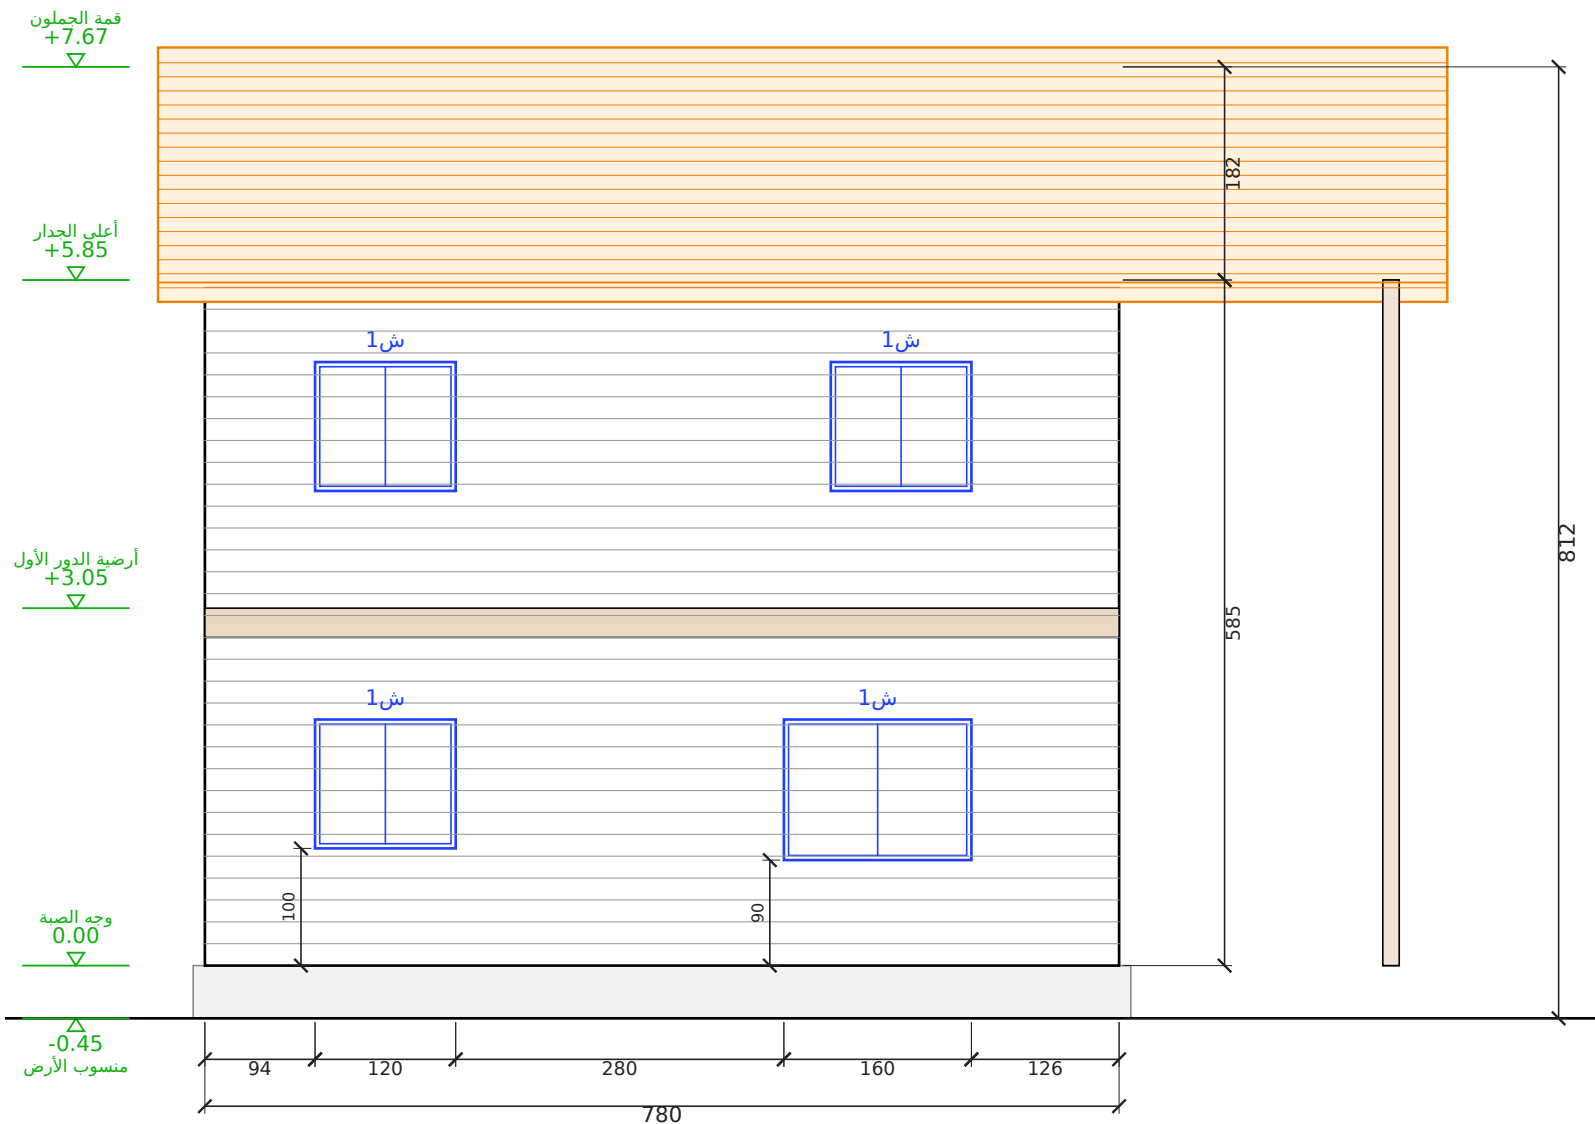


الواجهة الغربية


مقياس 1:50 | الوحدة: سم

رقم اللوحة	التاريخ	المقياس	عنوان اللوحة	المشروع / العميل	مصنع وتد الأخشاب Watad Wood Factory
A-04 (4/14)	2026-09-29	1:50	الواجهة الخلفية والواجهة الغربية	كوخ دورين 3 غرف نوم — 120 م ² عميل جديد	


مسقط السقف (جملون)
رفر 40 سم من كل جهة | مقياس 1:50

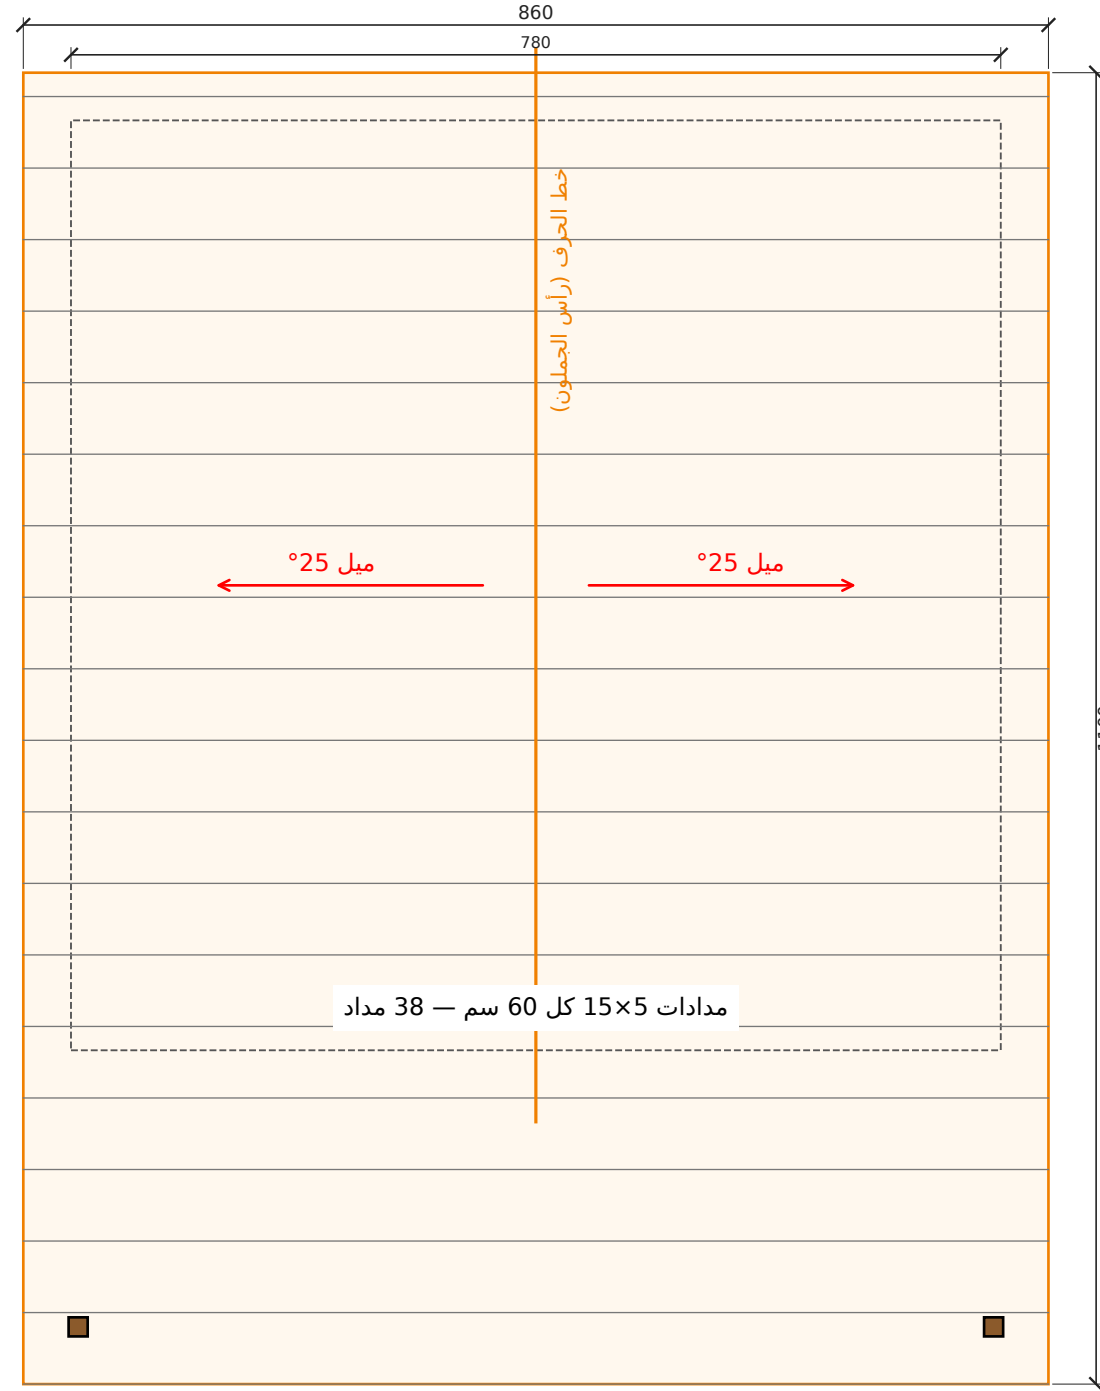

قطاع عرضي أ-أ
مقياس 1:50 | الوحدة: سم

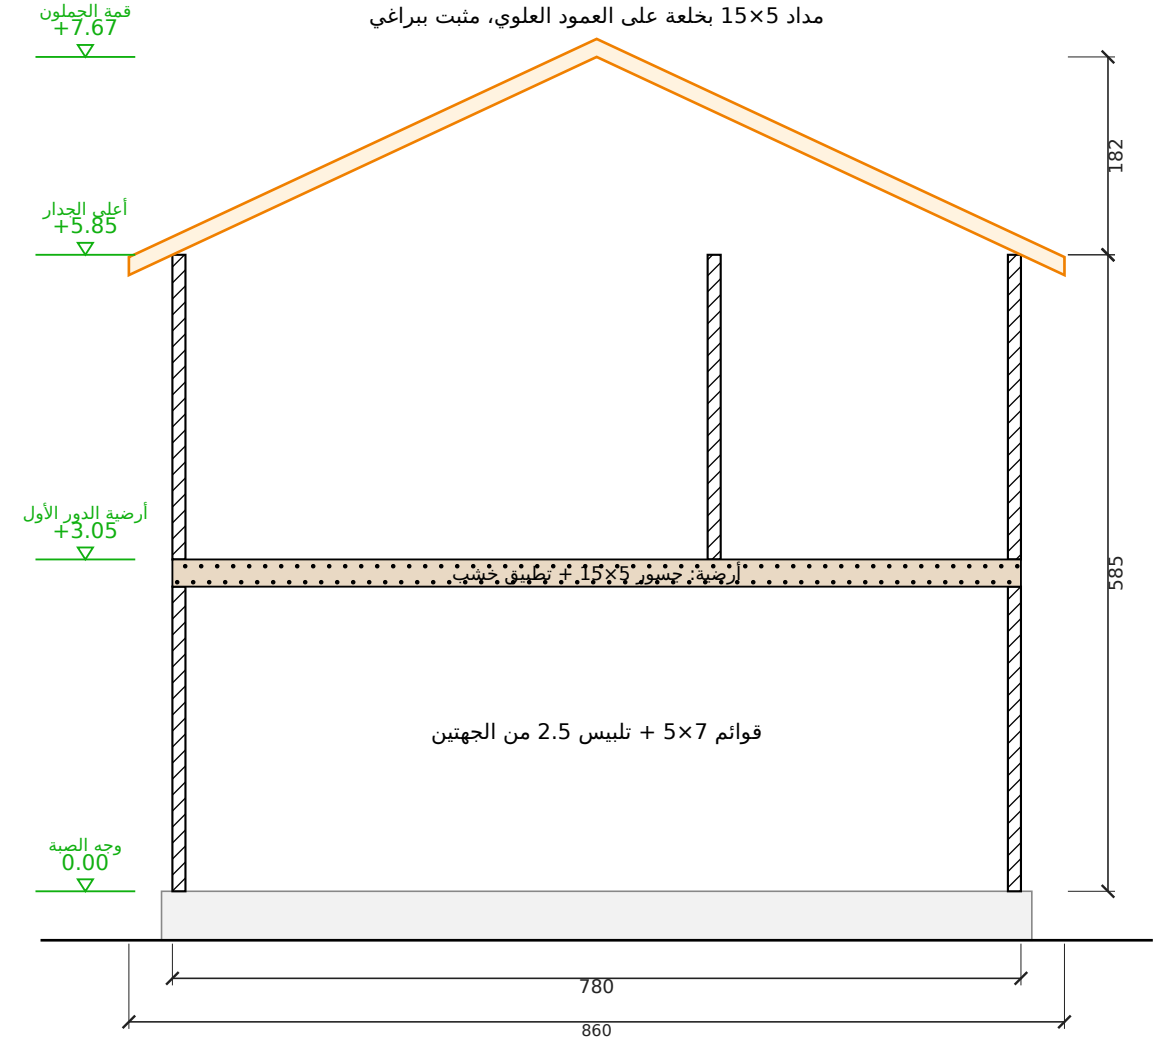

تفصيلة جلوس المداد على العلوي (1:5)

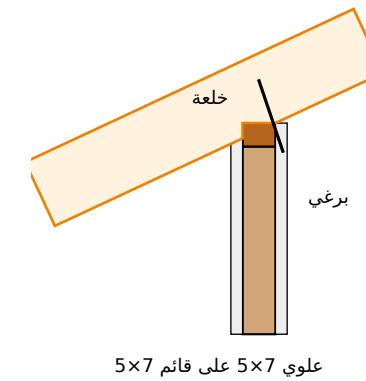

رقم اللوحة

A-05 (5/14)

التاريخ

2026-09-29

المقياس

1:50

عنوان اللوحة

مسقط السقف والقطاع

المشروع / العميل

كوخ دورين 3 غرف نوم - 120 م²
عميل جديد

مصنع وتد الأخشاب
Watad Wood Factory



جدول مقاسات الأبواب والشبابيك
مقاس الفتحة الصافي في الجدار - الوحدة: سم

الرمز	النوع	العرض (سم)	الارتفاع (سم)	ارتفاع الجلسة (سم)	العدد	الموقع
ب1	باب	300	265	-	1	الأمامية (التراس)
ب2	باب	80	210	-	3	غرفة 3 - ماستر - غرفة 2
ب3	باب	70	210	-	3	حمام 2 - حمام ماستر
ب4	باب مزدوج	240	240	-	1	الأمامية (التراس)
ف1	باب	380	240	-	1	فتحة الموزع والدرج
ف2	باب	90	210	-	1	فتحة غرفة الملابس
ز1	شباك	140	210	30	2	الأمامية (التراس) 2
ز2	شباك	100	210	30	1	الأمامية (التراس)
ش1	شباك	120	110	100	5	الخلفية 2 - الغربية 3
ش1	شباك	160	120	90	1	الغربية
ش1	شباك	100	110	100	1	الشرقية
ش2	شباك	120	100	110	1	الشرقية
ش3	شباك	60	60	150	3	الخلفية 2 - الشرقية

الإجمالي: أبواب 10 - شبابيك 14

جدول المساحات وبيانات المشروع والتسعير

جدول المساحات

م	الفراغ	الأبعاد (م)	المساحة (م2)
1	أرضي — الصالة والمطبخ	7.56 × 3.90	29.48
2	أرضي — غرفة نوم 3	3.24 × 3.54	11.47
3	أرضي — موزع	1.56 × 1.42	2.22
4	أرضي — حمام	1.50 × 2.00	3.00
5	أرضي — الدرج	2.58 × 3.54	9.13
6	أول — جناح الماستر	4.80 × 3.12	14.98
7	أول — حمام الماستر	2.64 × 1.80	4.75
8	أول — غرفة ملابس	2.64 × 1.20	3.17
9	أول — غرفة نوم 2	3.24 × 4.32	14.00
10	أول — الممر	4.20 × 0.90	3.78
11	أول — موزع علوي	1.56 × 1.30	2.03
12	أول — حمام	1.50 × 2.00	3.00
	المساحة الصافية الداخلية		101.00
	التراس المسقوف + تراس الدور الأول	7.80 × 2.40 × 2	37.44
	المساحة الإجمالية المبنية	2 × 7.80 × 7.80 دور	121.68

بيانات المشروع

البند	البيان
المشروع	كوخ دورين 3 غرف نوم — 120 م ²
العميل	عميل جديد
الموقع	—
الاستخدام	سكن / استجمام
التاريخ	2026-09-29
نظام البناء	هيكل خشب 5×7 + تليس 2.5 سم من الجهتين
السقف	جملون 25° — قرميد معدني

التسعير

البند	القيمة
المساحة الكلية — الكوخ + التراس (م2)	159.12
سعر المتر المربع — عرض اليوم الوطني	1,096 ريال
الإجمالي	174,396 ريال

ملاحظات:

- السعر لكامل المساحة (الكوخ + التراس المسقوف) حسب المخطط المعتمد.
- الصبة والتמידات الخارجية على العميل ما لم يُذكر غير ذلك.

الصور الواقعية – الخارج

أمامي من اليسار



أمامي من اليمين



الواجهة الأمامية



خلفي من اليسار



رندر واقعي بخامات حقيقية وإضاءة طبيعية – الألوان النهائية حسب عينات المورد

رقم اللوحة	التاريخ	المقياس	عنوان اللوحة	المشروع / العميل	مصنع وتد الأخشاب Watad Wood Factory
A-08 (8/14)	2026-09-29	—	الصور الواقعية – الخارج	كوخ دورين 3 غرف نوم – 120 م ² عميل جديد	



الصور الواقعية — وقت الغروب

أمامي من اليمين — وقت الغروب



أمامي من اليسار — وقت الغروب



رقم اللوحة	التاريخ	المقياس	عنوان اللوحة	المشروع / العميل	مصنع وتد الأخشاب Watad Wood Factory
A-09 (9/14)	2026-09-29	—	الصور الواقعية — الغروب	كوخ دورين 3 غرف نوم — 120 م ² عميل جديد	

الصور الواقعية – الداخل

جناح الماستر



الصالة والمطبخ – منظر 2



الصالة والمطبخ



غرفة نوم 3



غرفة نوم 2



الأثاث للتوضيح فقط — مواقع القطع ومقاساتها حسب المسقط


رقم اللوحة	التاريخ	المقياس	عنوان اللوحة	المشروع / العميل	مصنع وتد الأخشاب Watad Wood Factory
A-10 (10/14)	2026-09-29	—	الصور الواقعية – الداخل	كوخ دورين 3 غرف نوم — 120 م ² عميل جديد	

لقطات المنظور الخارجي


المنظور الأمامي




منظور أمامي من اليسار

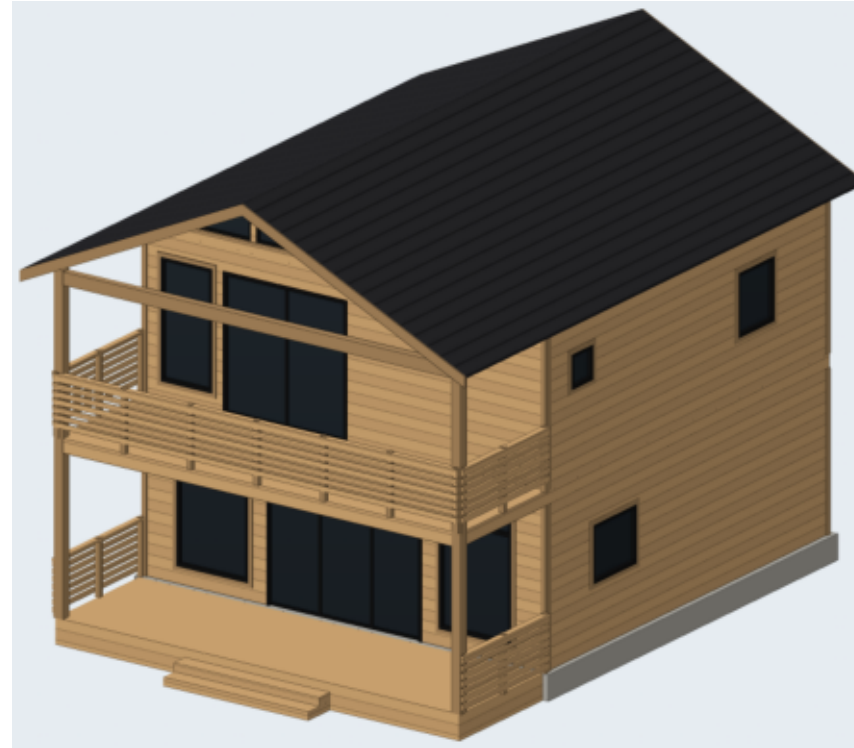


منظور أمامي من اليمين

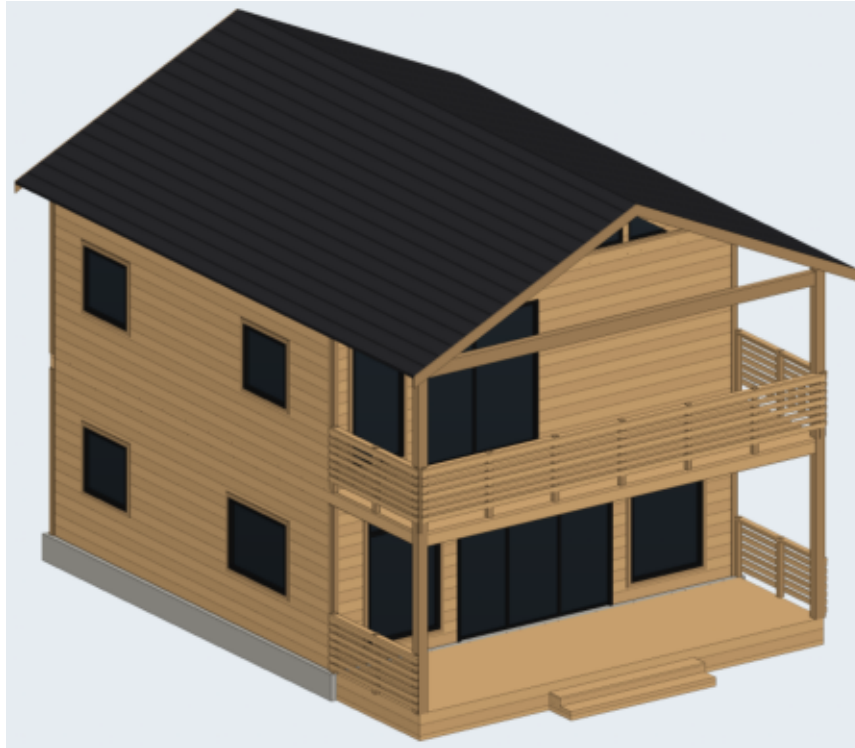


المنظور الخلفي

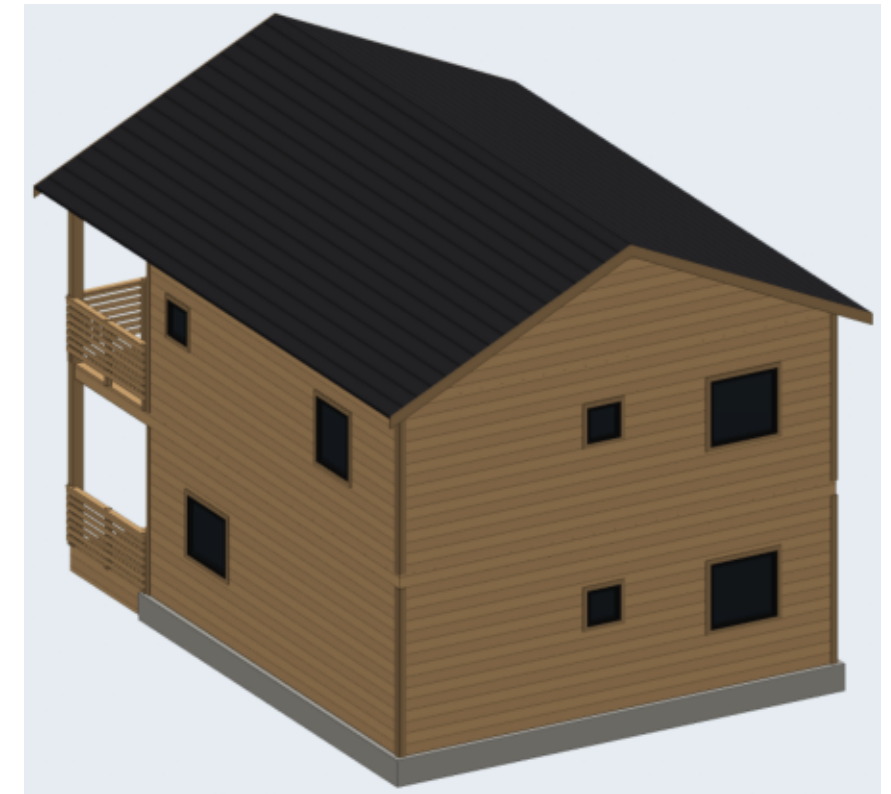

منظور خلفي من اليمين

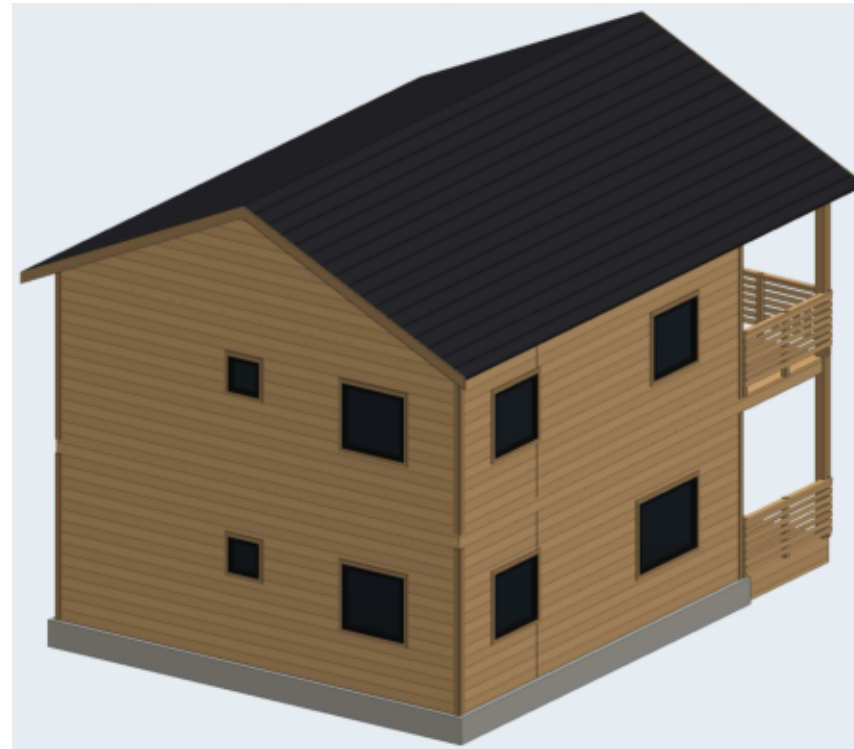

منظر علوي

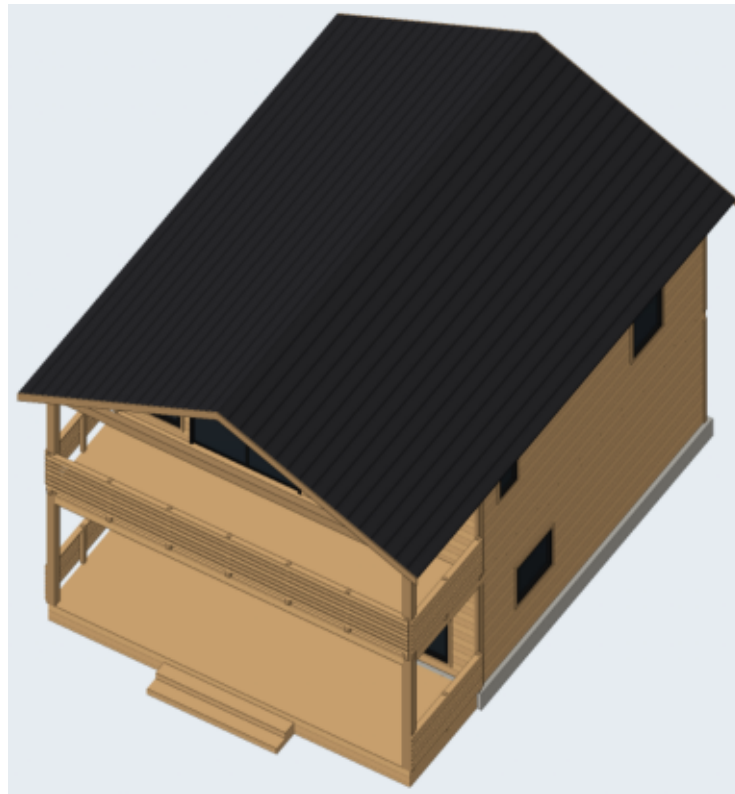


رقم اللوحة	التاريخ	المقياس	عنوان اللوحة	المشروع / العميل	مصنع وتد الأخشاب Watad Wood Factory
A-11 (11/14)	2026-09-29	—	لقطات المنظور	كوخ دورين 3 غرف نوم — 120 م ² عميل جديد	



المقطع العلوي بالفرش – الدور الأرضي

مقطع أفقي على ارتفاع 1.90 م – توزيع الفرش ومسار الحركة

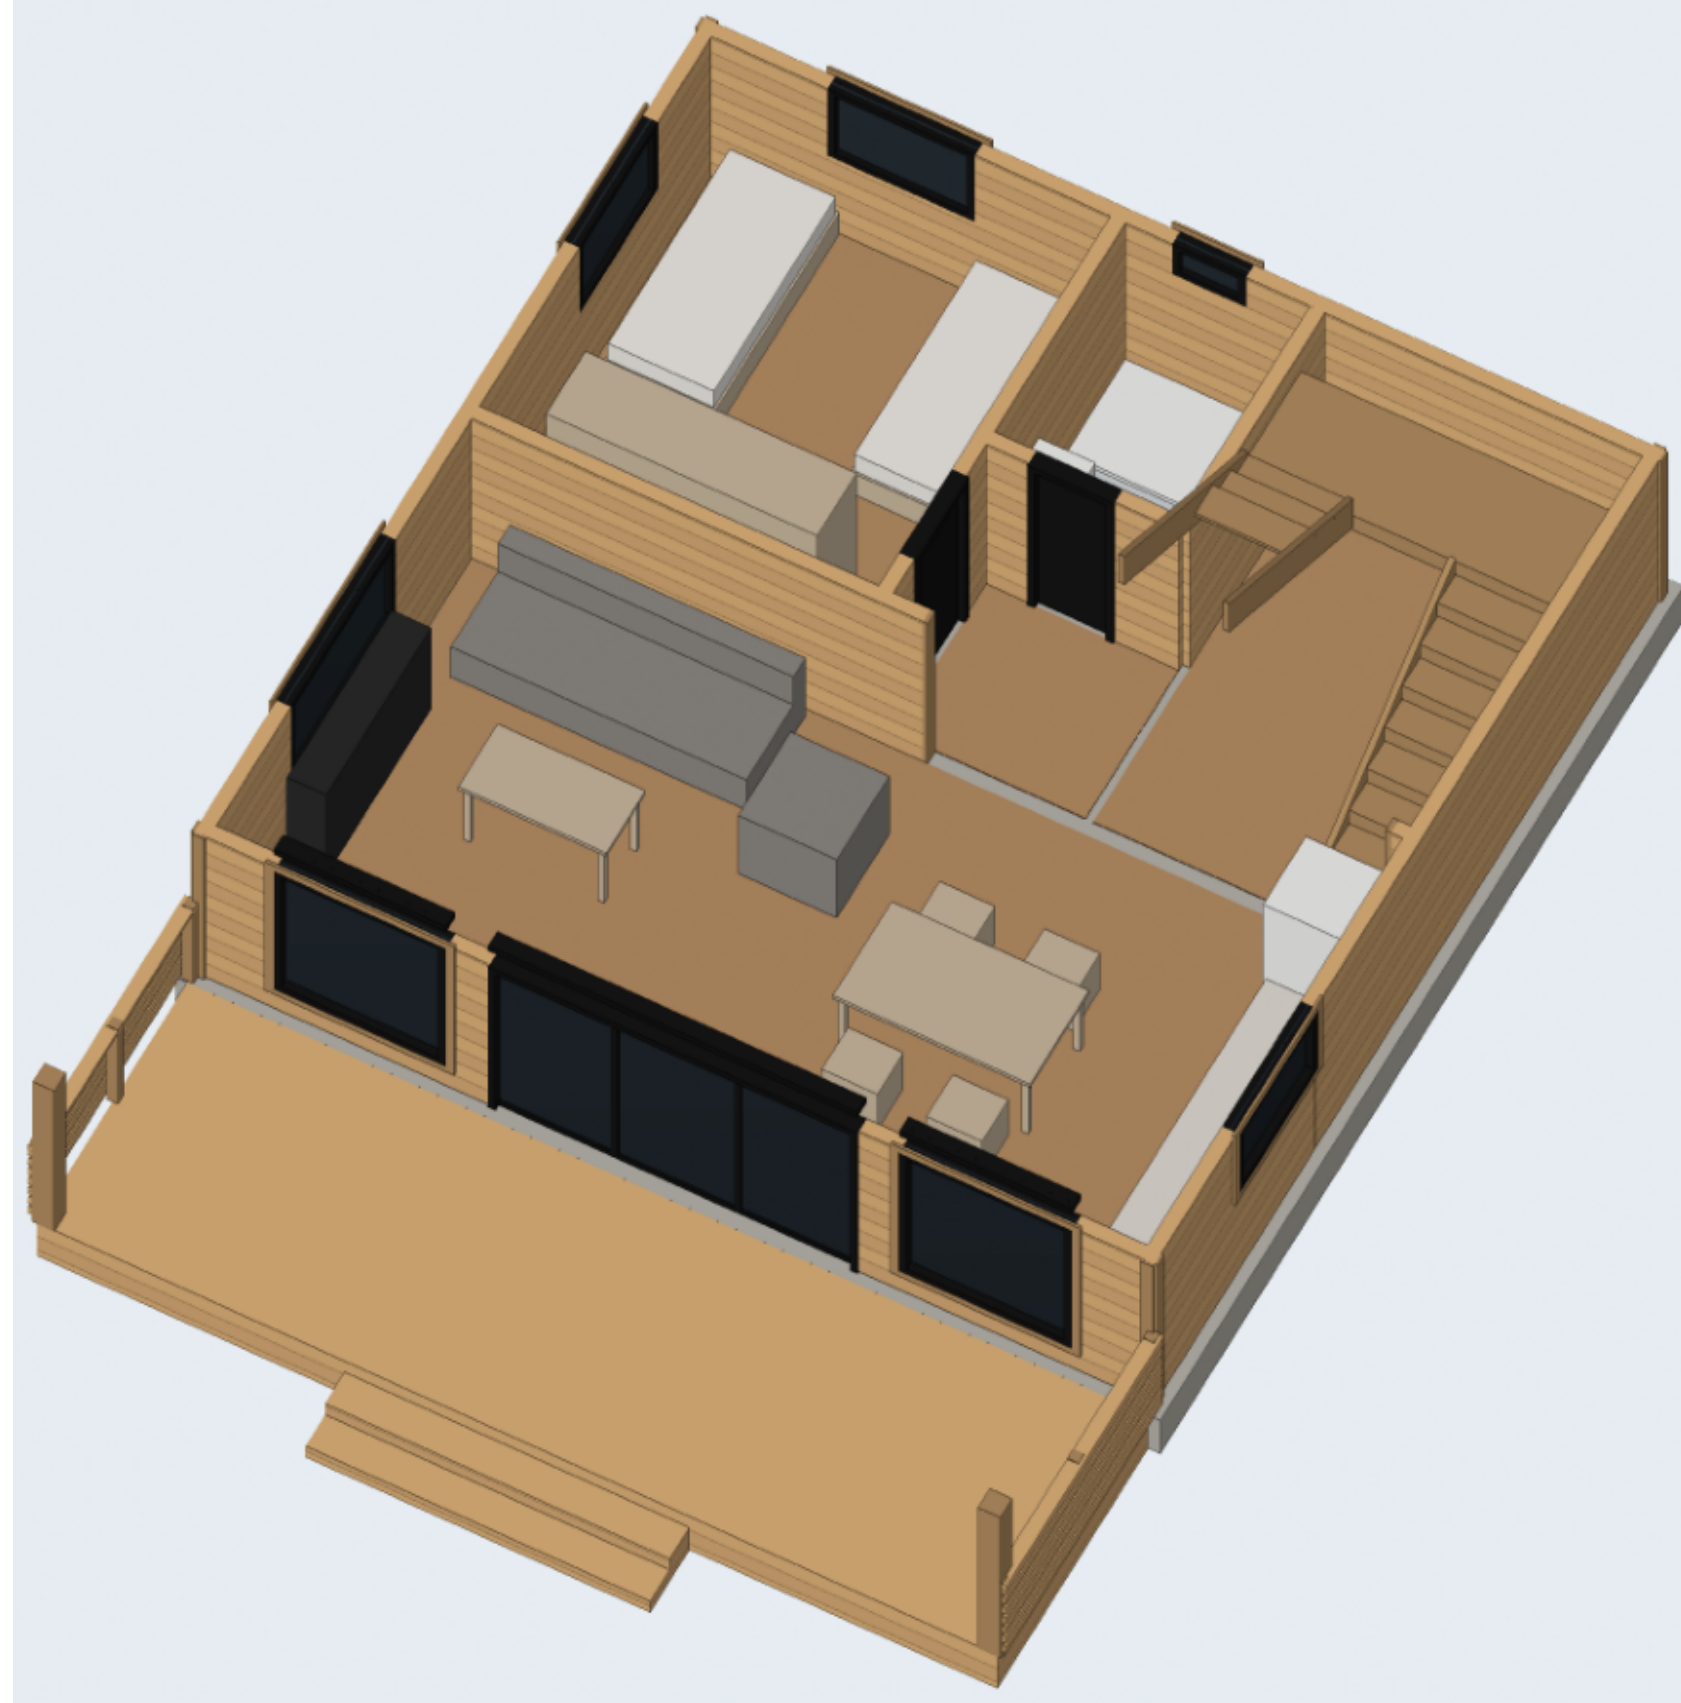

رقم اللوحة

A-12 (12/14)

التاريخ

2026-09-29

المقياس

—

عنوان اللوحة

المقطع العلوي بالفرش – الدور الأرضي

المشروع / العميل


كوخ دورين 3 غرف نوم – 120 م²
عميل جديد

مصنع وتد الأخشاب
Watad Wood Factory



المقطع العلوي بالفرش – الدور الأول

مقطع أفقي على ارتفاع 1.90 م – توزيع الفرش ومسار الحركة

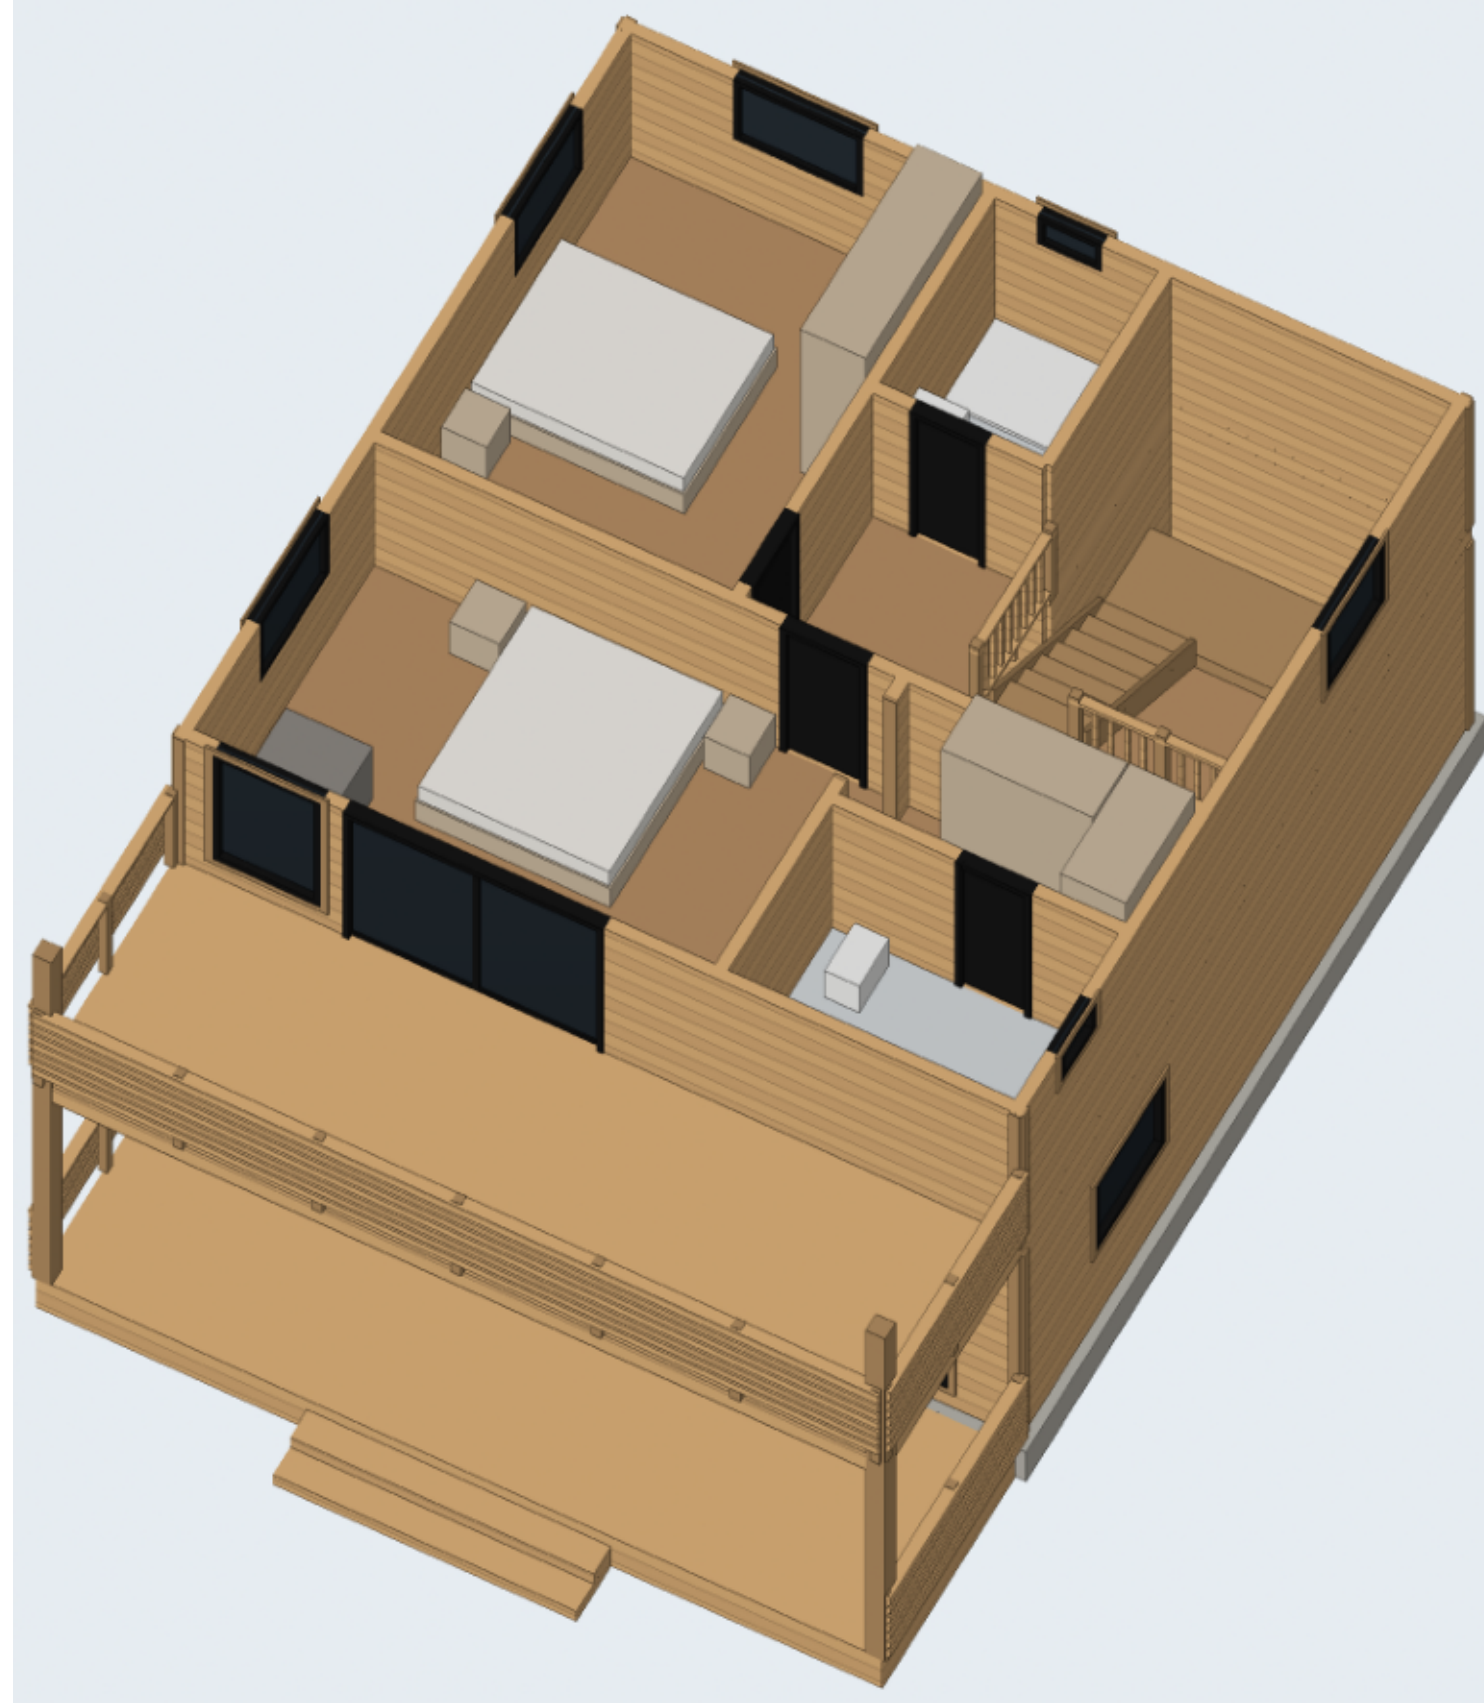

رقم اللوحة

A-13 (13/14)

التاريخ

2026-09-29

المقياس

—

عنوان اللوحة

المقطع العلوي بالفرش – الدور الأول

المشروع / العميل

كوخ دورين 3 غرف نوم – 120 م²
عميل جديد


مصنع وتد الأخشاب
Watad Wood Factory



المنظور ثلاثي الأبعاد والمواد

النمط: جوزي غامق + إطارات سوداء — معاينة تقريبية، الإخراج النهائي من 3ds Max

جدول المواد والألوان

 

الخشب / الصبغة
خشب طبيعي فاتح (بدون صبغة)



القرميد
قرميد رمادي غامق




الزجاج
زجاج عاكس غامق



إطارات الشبابيك والأبواب
إطار ألومنيوم أسود



الكنار والزوايا
نفس الصبغة أعمق درجة

 

الصبة
خرسانة 45 سم


الدريزين: ألواح أفقية متقاربة (عصري)

تقسيم الشبابيك: بدون | الباب الرئيسي: سحب زجاج


أنواع الدريزين المعتمدة (من مشاريع المصنع)



قوائم رأسية متقاربة (صورة 1)

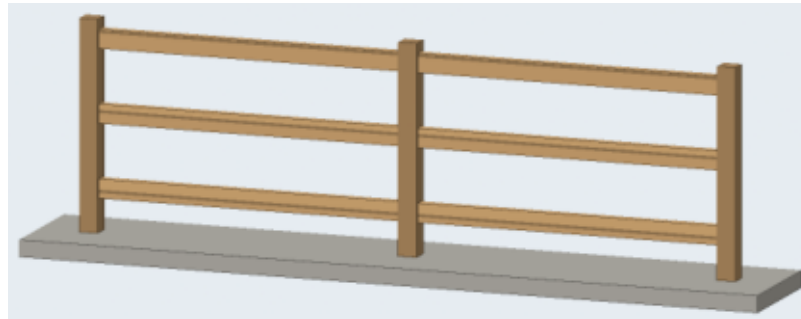

3 مربيع أفقية (صورة 2)

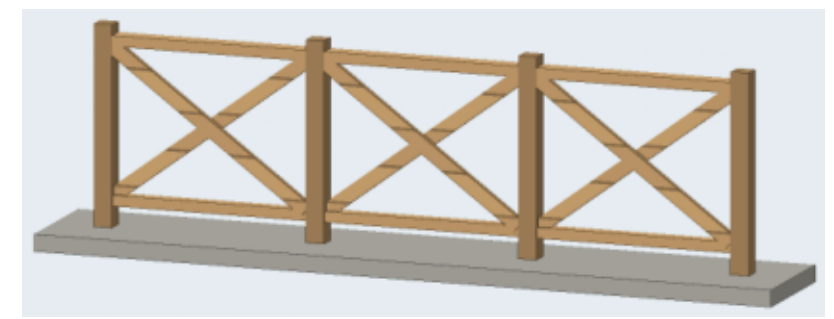

تقاطع X (صورة 5)

رقم اللوحة

A-14 (14/14)

التاريخ

2026-09-29

المقياس

—

عنوان اللوحة

المنظور والمواد

المشروع / العميل

كوخ دورين 3 غرف نوم — 120 م²
عميل جديد

مصنع وتد الأخشاب
Watad Wood Factory

