
المسقط الأفقي مع الفرش — الدور الأرضي

الأبعاد بالسنتيمتر - الجدران: قوائم 7×5 + تلبيس 2.5 من الجهتين (12 سم) | منسوب الأرضية +0.00

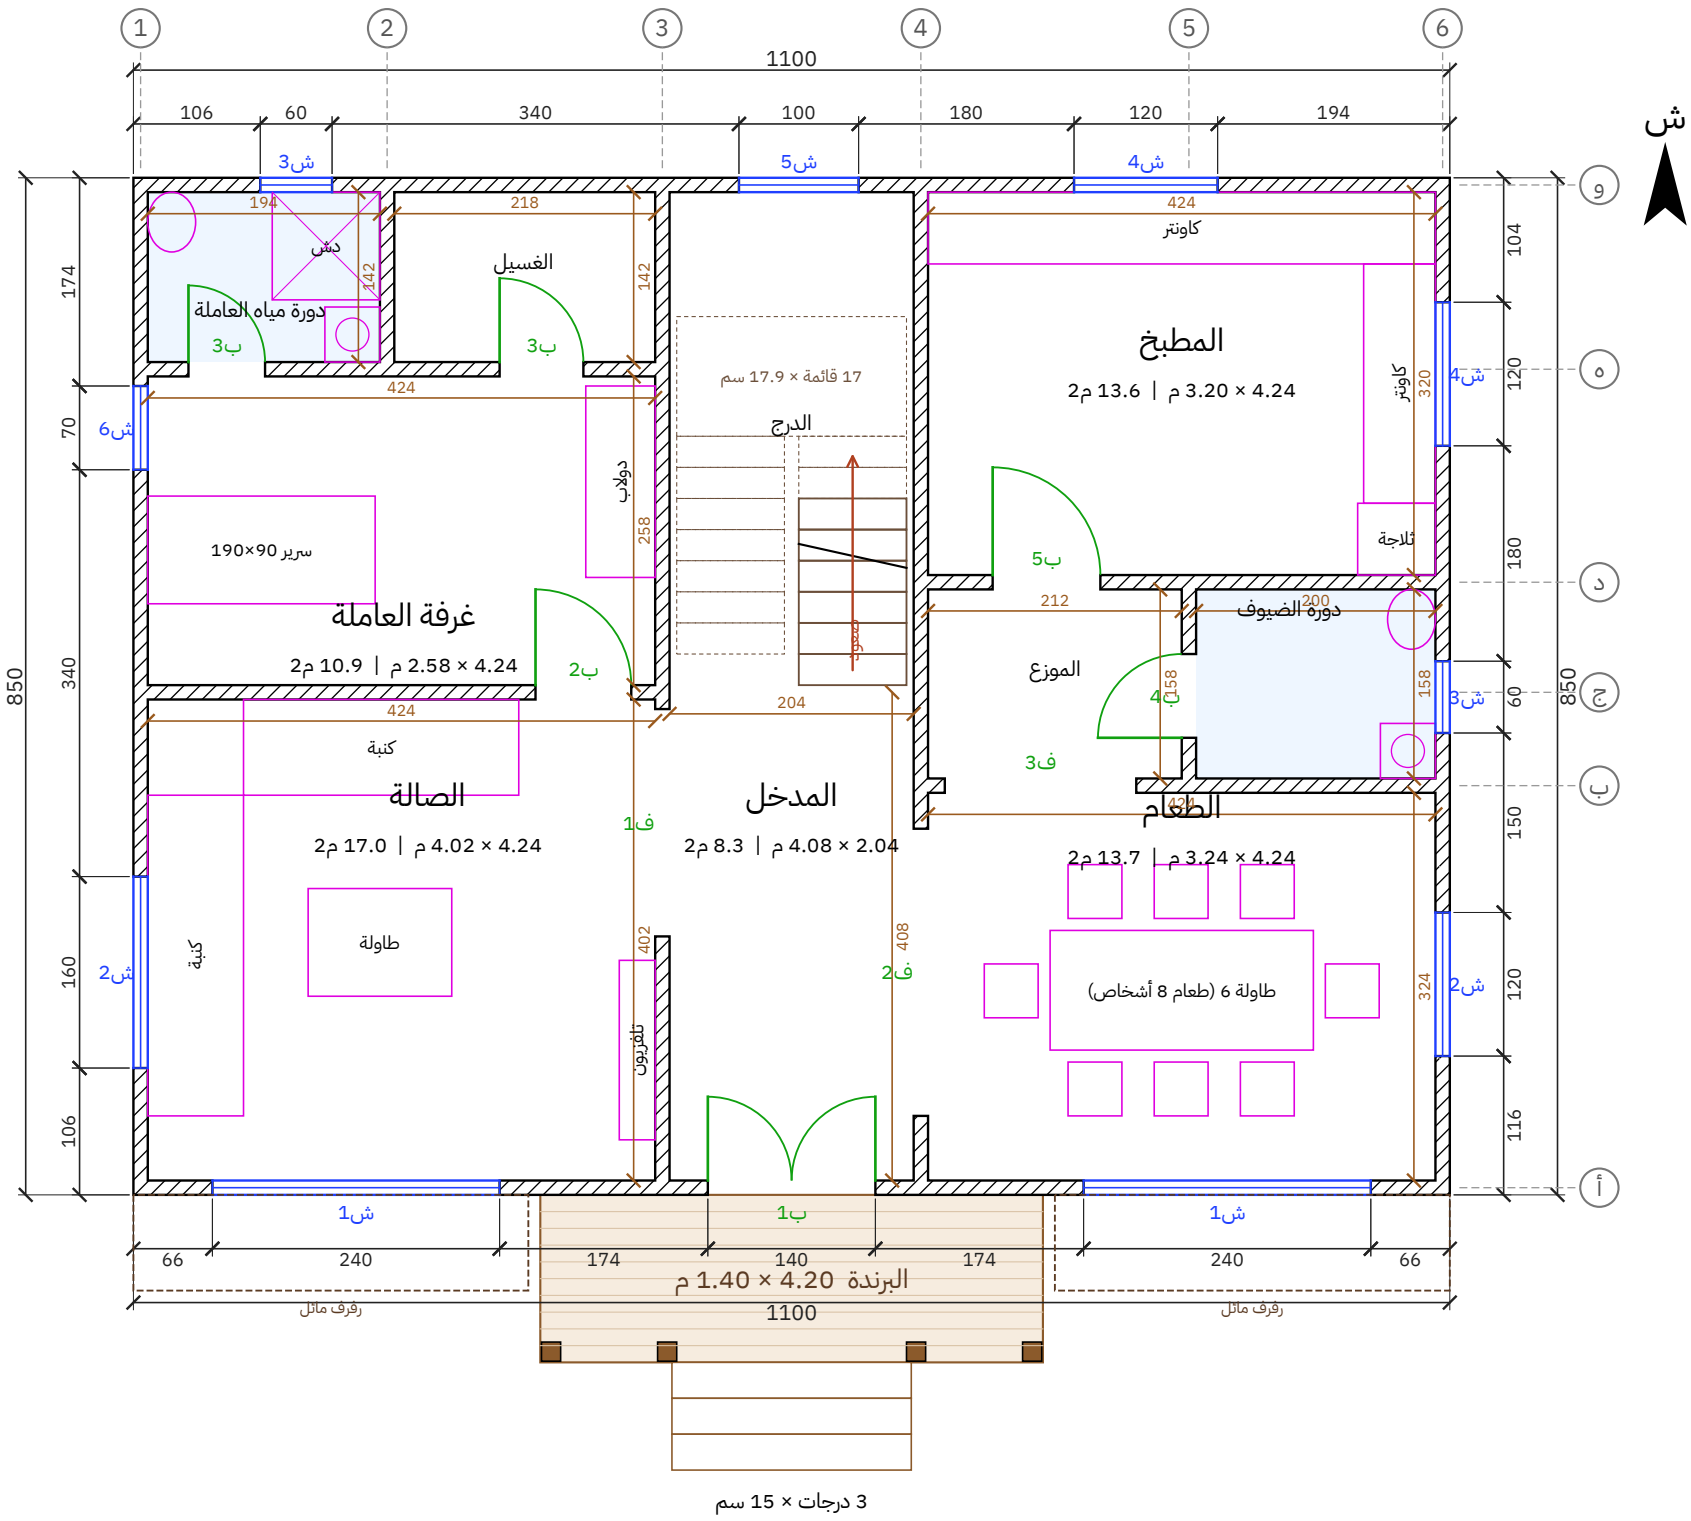


المشروع / العميل	عنوان اللوحة	المقياس	التاريخ	رقم اللوحة
فيلا خشب دورين — واجهة جملون زجاج وبلكونة — 3 غرف (ماستر) — 11.00 × 8.50 م عميل — الباحة	المسقط الأفقي — الدور الأرضي	1:50	2026-10-23	A-01 (1/11)

مصنع وتد الأخشاب
Watad Wood Factory


المسقط الأفقي مع الفرش — الدور الأول

الأبعاد بالسنتيمتر - الجدران: قوائم 7×5 + تلبيس 2.5 من الجهتين (12 سم) | منسوب الأرضية +3.05

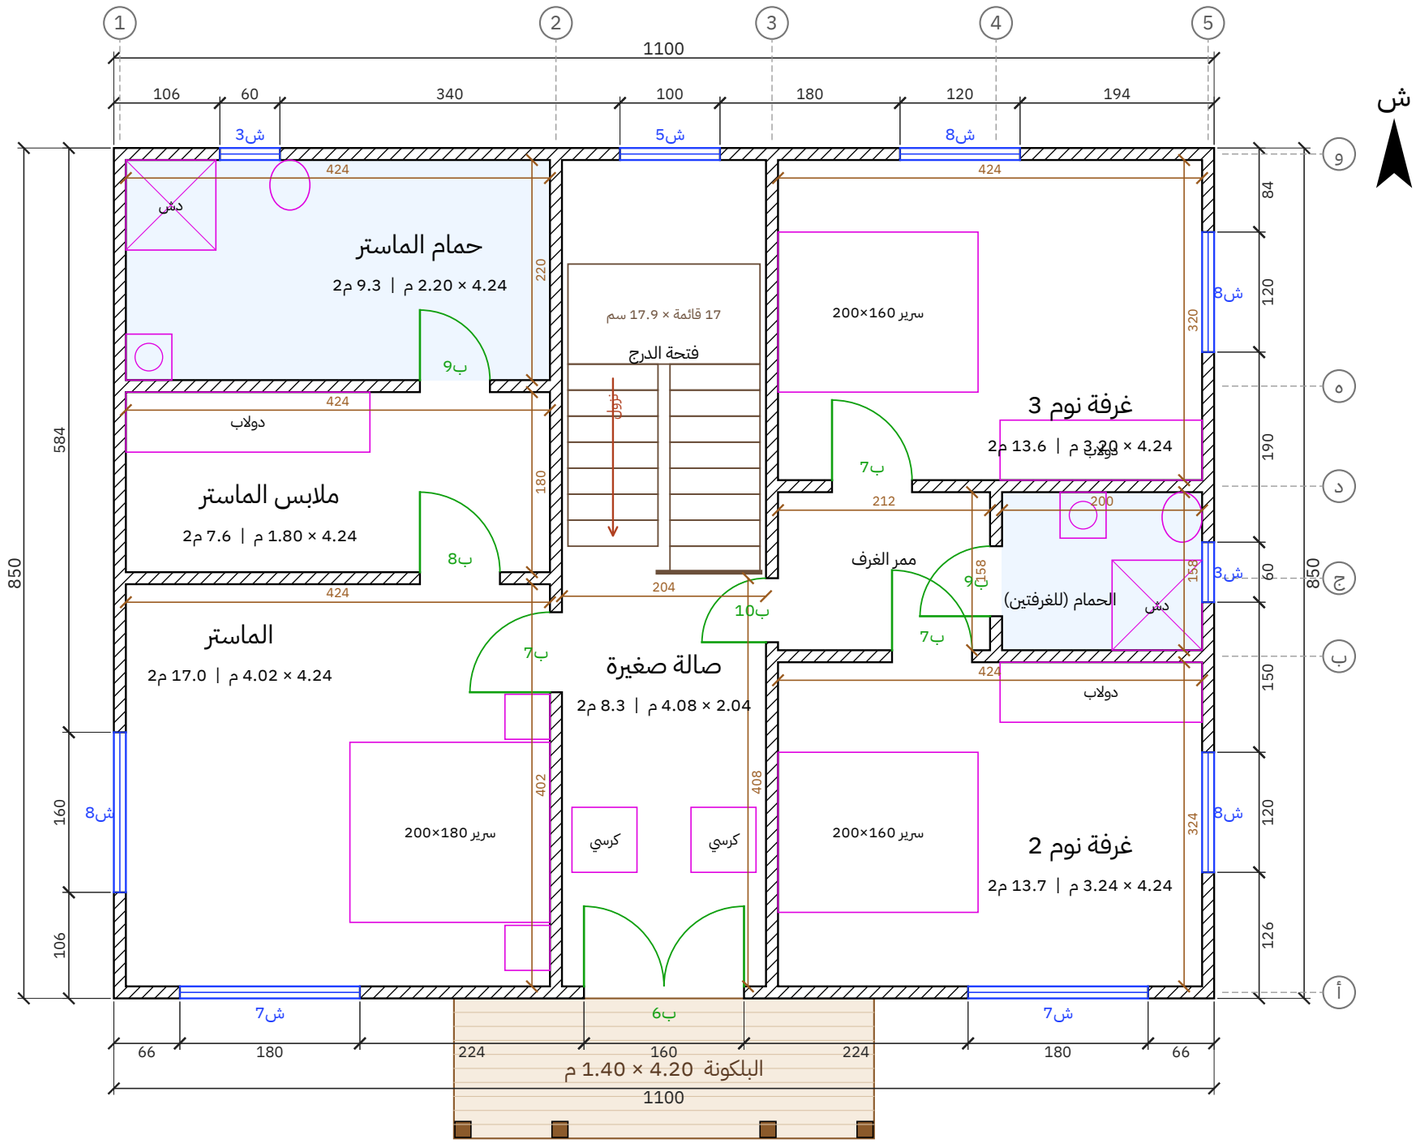


المشروع / العميل	عنوان اللوحة	المقياس	التاريخ	رقم اللوحة
فيلا خشب دورين — واجهة جملون زجاج وبلكونة — 3 غرف (ماستر) — 11.00 × 8.50 م عميل — الباحة	المسقط الأفقي — الدور الأول	1:50	2026-10-23	A-02 (2/11)

مصنع وتد الأخشاب
Watad Wood Factory

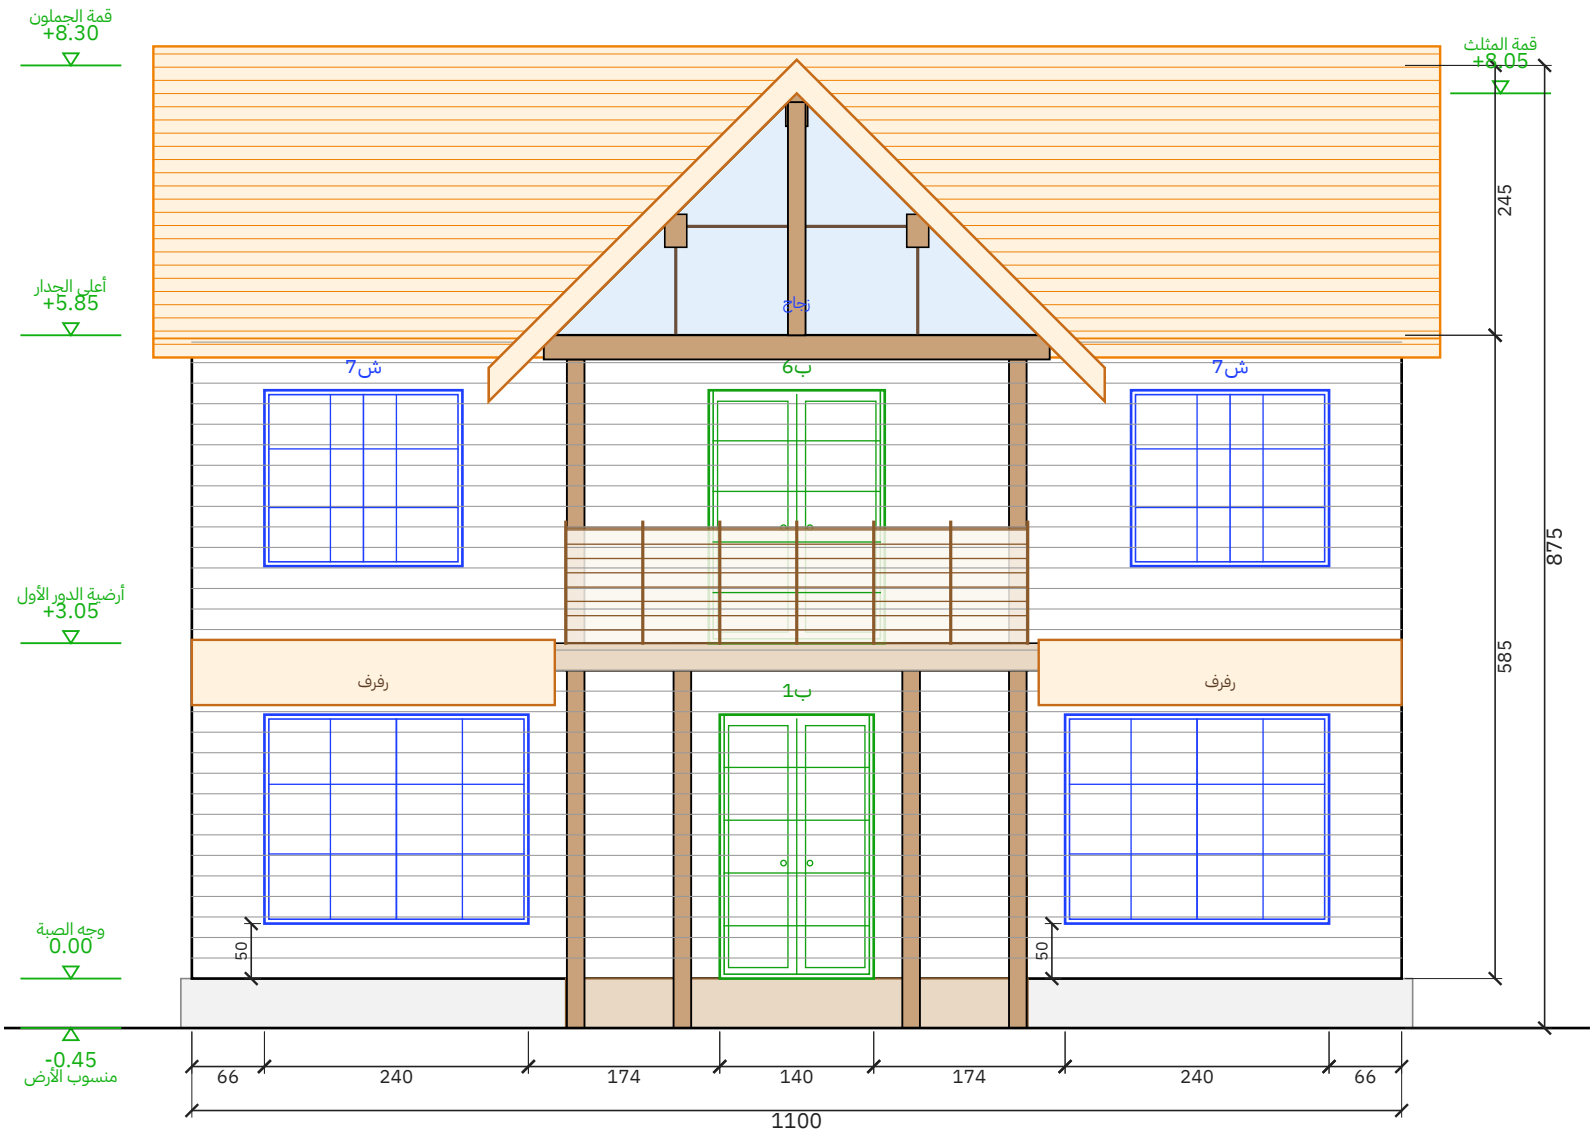

الواجهة الأمامية


مقياس 1:50 | الوحدة: سم

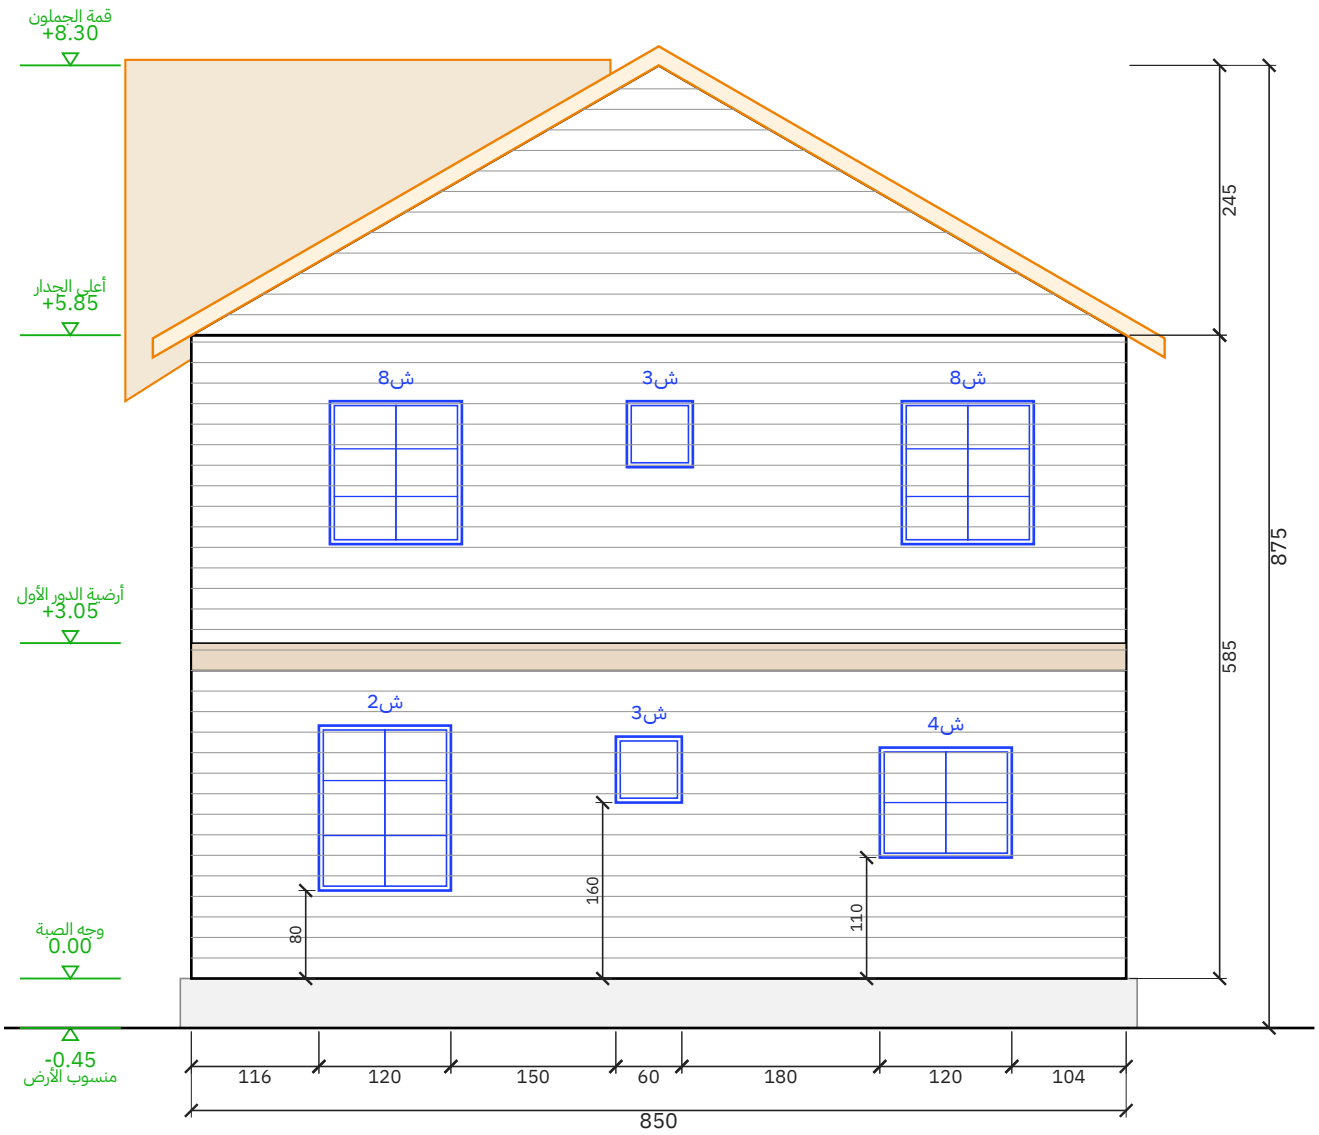

الواجهة الشرقية


مقياس 1:50 | الوحدة: سم

مصنع وتد الأخشاب Watad Wood Factory	المشروع / العميل فيلا خشب دورين – واجهة جملون زجاج وبلكونة – 3 غرف (ماستر) – 11.00 × 8.50 م عميل – الباحة	عنوان اللوحة الواجهة الأمامية والواجهة الشرقية	المقياس 1:50	التاريخ 2026-10-23	رقم اللوحة A-03 (3/11)

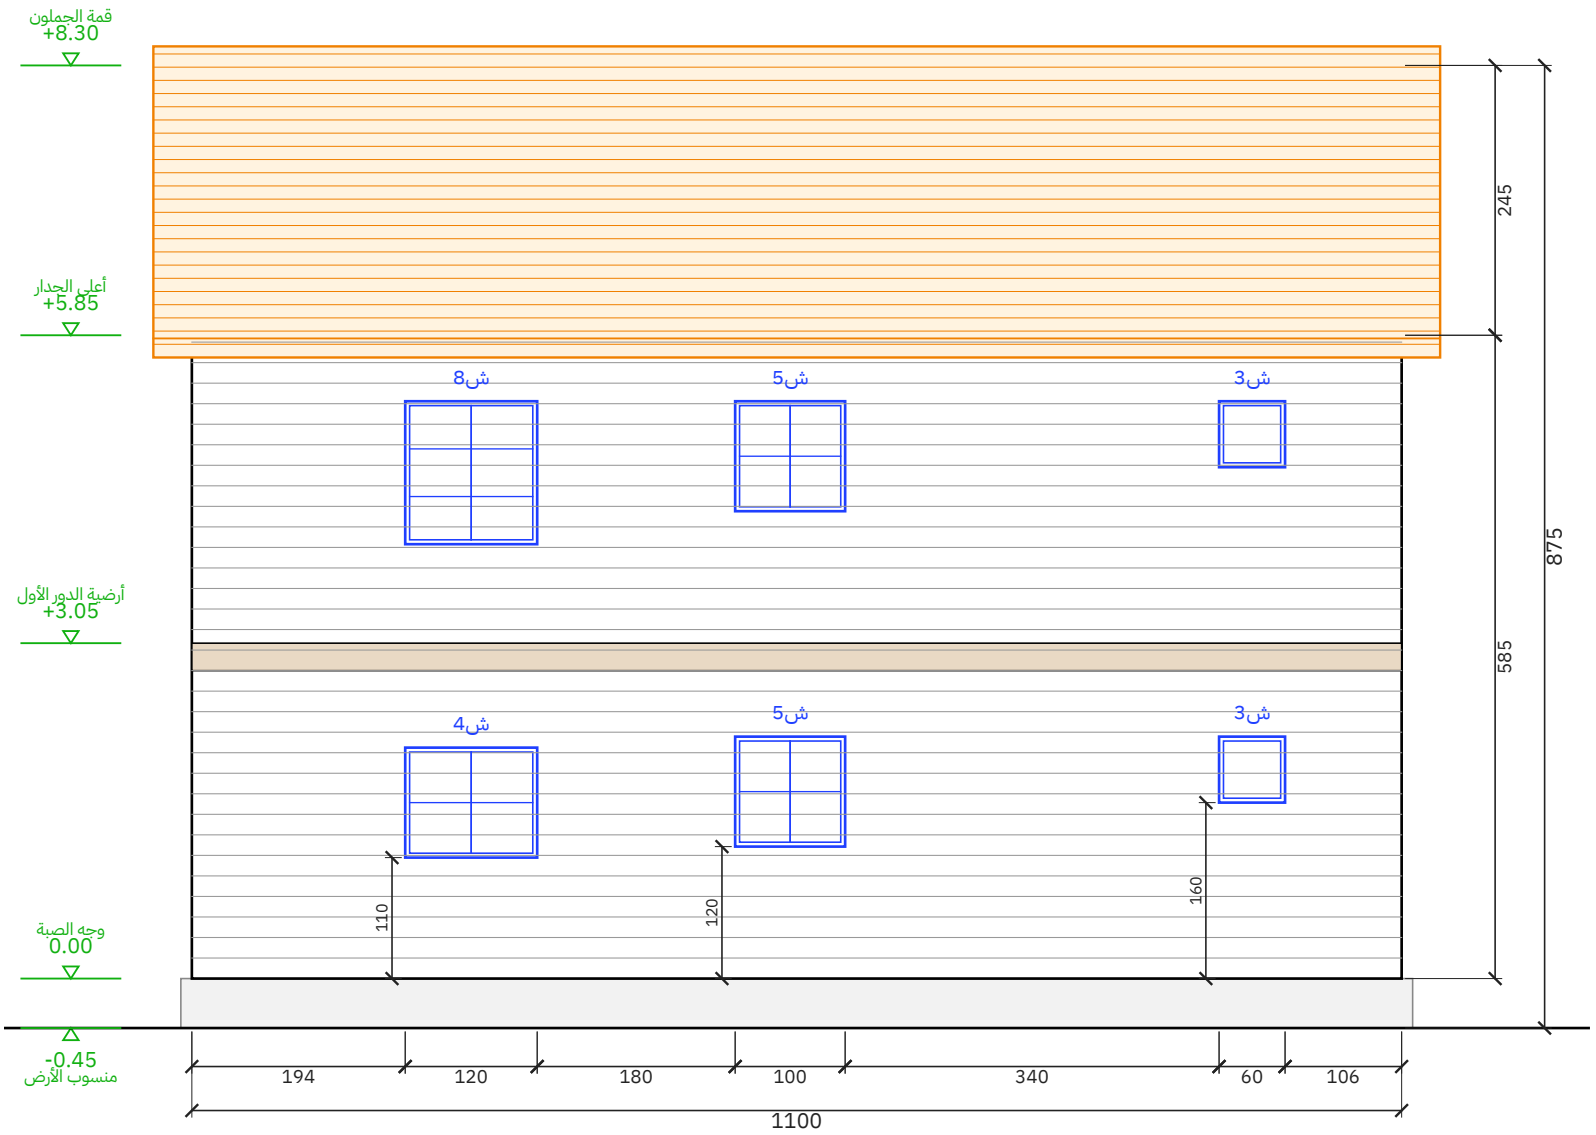

الواجهة الخلفية

مقياس 1:50 | الوحدة: سم

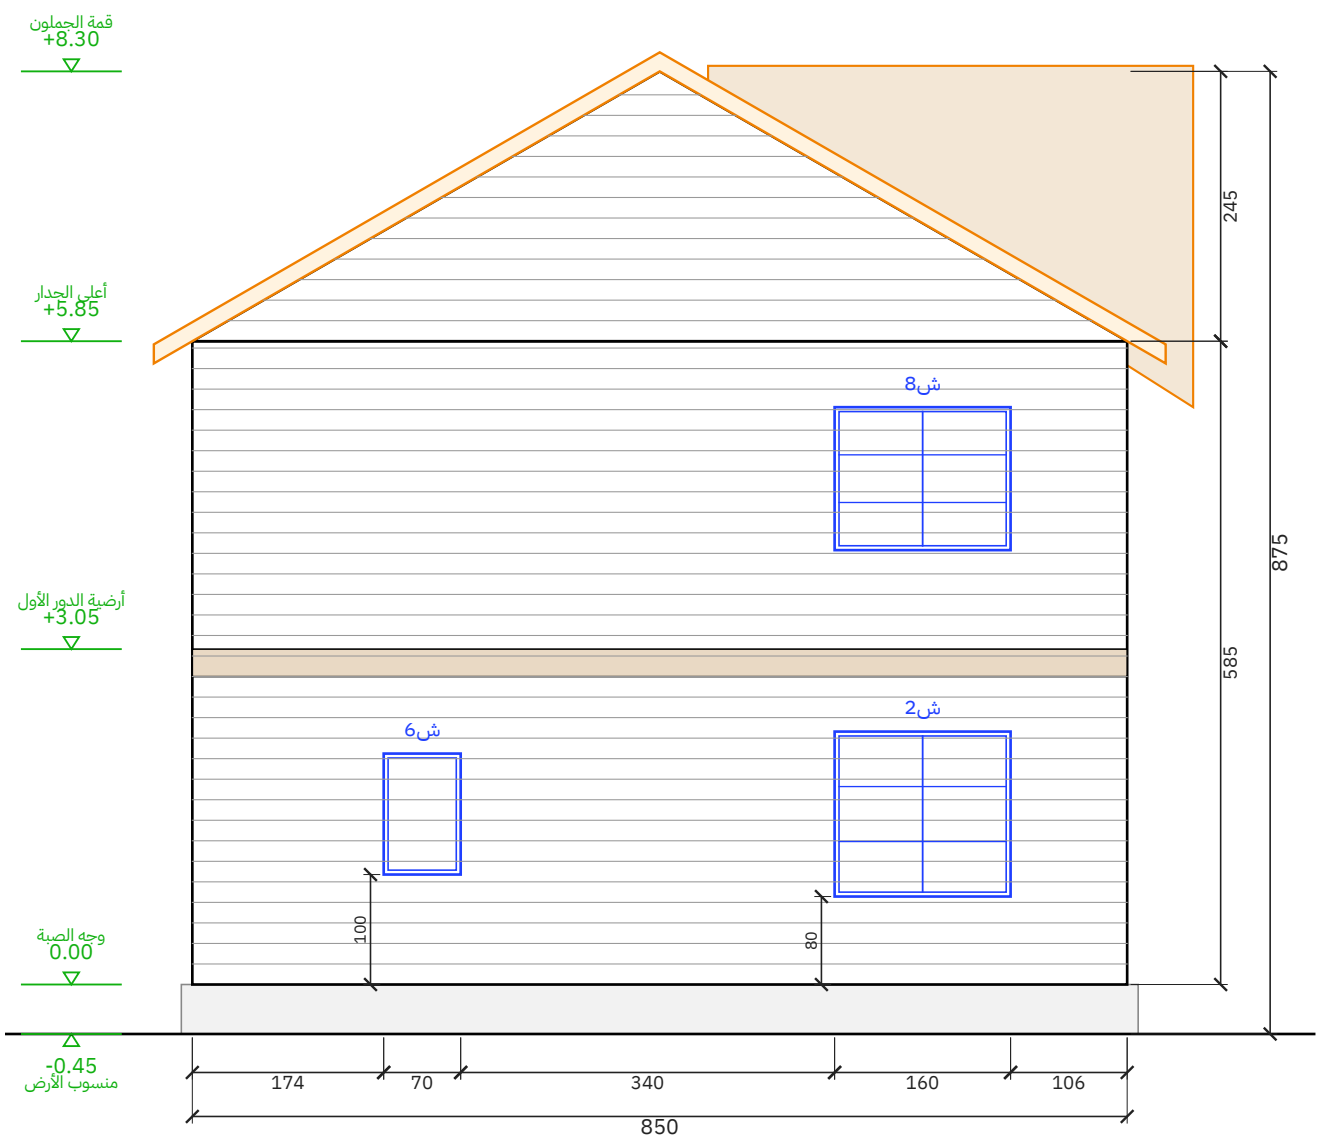

الواجهة الغربية


مقياس 1:50 | الوحدة: سم

المشروع / العميل	عنوان اللوحة	المقياس	التاريخ	رقم اللوحة
فيلا خشب دورين – واجهة جملون زجاج وبلكونة – 3 غرف (ماستر) – 11.00 × 8.50 م عميل – الباحة	الواجهة الخلفية والواجهة الغربية	1:50	2026-10-23	A-04 (4/11)


مصنع وتد الأخشاب
Watad Wood Factory

قطاع عرضي أ-أ

مقياس 1:50 | الوحدة: سم

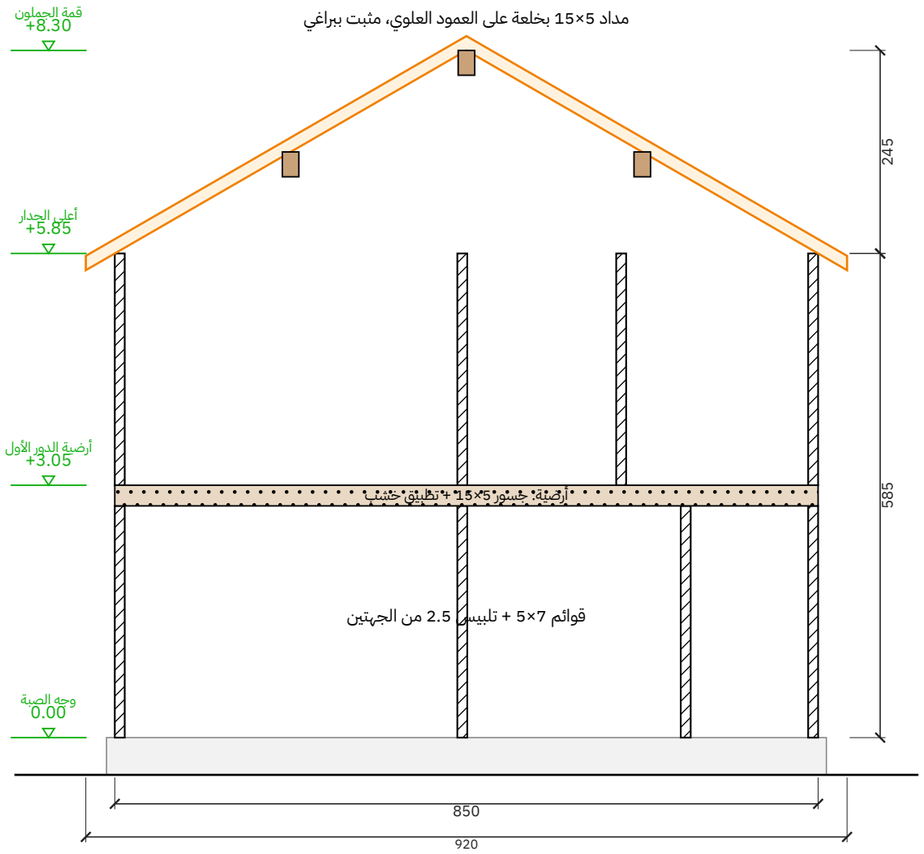


تفصيلة جلوس المداد على العلوي (1:5)

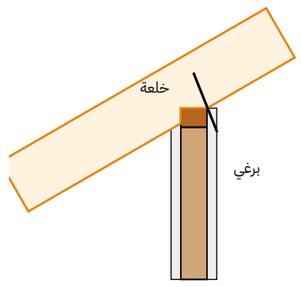

علوي 7×5 على قائم 7×5

مسقط السقف (جملون)

رفرف 35 سم من كل جهة | مقياس 1:50

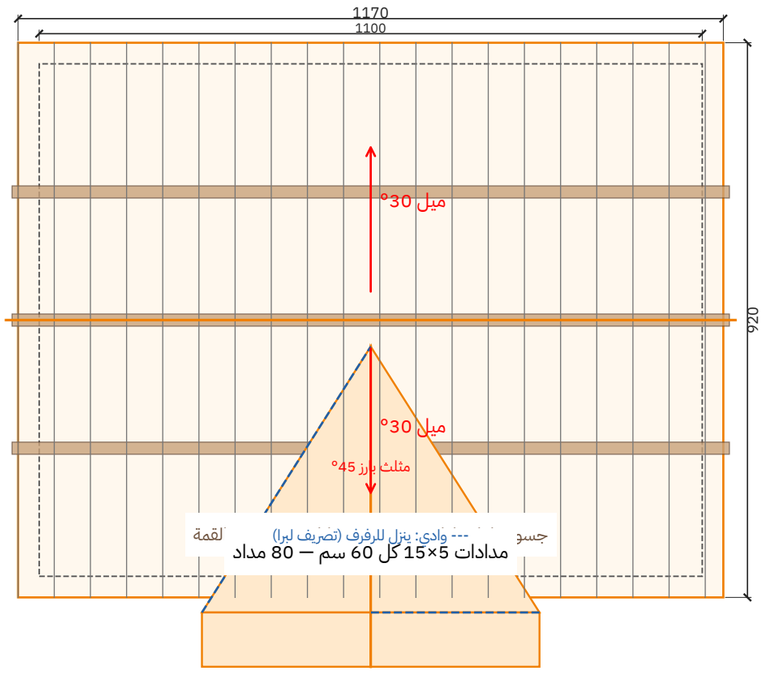

المشروع / العميل: فيلا خشب دورين — واجهة جملون زجاج وبلكونة — 3 غرف (ماستر) — 11.00 × 8.50 م — عميل — الباحة	عنوان اللوحة: مسقط السقف والقطاع	المقياس: 1:50	التاريخ: 2026-10-23	رقم اللوحة: A-05 (5/11)

مصنع وتد الأخشاب
Watad Wood Factory

جدول مقاسات الأبواب والشبابيك

مقاس الفتحة الصافي في الجدار - الوحدة: سم

الرمز	النوع	العرض (سم)	الارتفاع (سم)	ارتفاع الجلسة (سم)	العدد	الموقع
ب1	باب مزدوج	140	240	-	1	الأمامية
ب10	باب	64	210	-	1	ممر الغرف
ب2	باب	80	210	-	1	غرفة العاملة
ب3	باب	64	210	-	1	دورة مياه العاملة
ب3	باب	70	210	-	1	الغسيل
ب4	باب	70	210	-	1	دورة الضيوف
ب5	باب	90	210	-	1	المطبخ
ب6	باب مزدوج	160	230	-	1	الأمامية (البلكونة)
ب7	باب	80	210	-	3	الماستر - غرفة 2 - غرفة 3
ب8	باب	80	210	-	1	ملابس الماستر
ب9	باب	70	210	-	2	حمام الماستر - الحمام (للغرفتين)
ف1	باب	190	240	-	1	الصالة — المدخل
ف2	باب	240	240	-	1	الطعام — المدخل
ف3	باب	160	220	-	1	الطعام — الموزع
ش1	شباك	240	190	50	2	الأمامية 2
ش2	شباك	120	150	80	1	الشرقية
ش2	شباك	160	150	80	1	الغربية
ش3	شباك	60	60	160	4	الشرقية 2 - الخلفية 2
ش4	شباك	120	100	110	2	الشرقية - الخلفية
ش5	شباك	100	100	120	2	الخلفية 2
ش6	شباك	70	110	100	1	الغربية
ش7	شباك	180	160	70	2	الأمامية (البلكونة) 2
ش8	شباك	120	130	90	3	الشرقية 2 - الخلفية
ش8	شباك	160	130	90	1	الغربية

الإجمالي: أبواب 17 - شبابيك 19

جدول المساحات وبيانات المشروع والتسعير

بيانات المشروع

البند	البيان
المشروع	فيلا خشب دورين — واجهة جملون زجاج وبلكونة — 3 غرف (ماستر) — 11.00 × 8.50 م
العميل	عميل — الباحة
الموقع	الباحة
الاستخدام	سكن عائلي
التاريخ	2026-10-23
نظام البناء	هيكل خشب 5×7 + تلبيس 2.5 سم من الجهتين
السقف	جملون 30° — قرميد معدني + 1 مثلث بارز

جدول المساحات

م	الفراغ	الأبعاد (م)	المساحة (م2)
1	أرضي — الصالة	4.24 × 4.02	17.04
2	أرضي — المدخل	2.04 × 4.08	8.32
3	أرضي — الطعام	4.24 × 3.24	13.74
4	أرضي — الموزع	2.12 × 1.58	3.35
5	أرضي — دورة الضيوف	2.00 × 1.58	3.16
6	أرضي — المطبخ	4.24 × 3.20	13.57
7	أرضي — الدرج	1.92 × 4.12	7.91
8	أرضي — غرفة العاملة	4.24 × 2.58	10.94
9	أرضي — دورة مياه العاملة	1.94 × 1.42	2.75
10	أرضي — الغسيل	2.18 × 1.42	3.10
11	أول — الماستر	4.24 × 4.02	17.04
12	أول — صالة صغيرة	2.04 × 4.08	8.32
13	أول — ملابس الماستر	4.24 × 1.80	7.63
14	أول — حمام الماستر	4.24 × 2.20	9.33
15	أول — غرفة نوم 2	4.24 × 3.24	13.74
16	أول — ممر الغرف	2.12 × 1.58	3.35
17	أول — الحمام (للغرفتين)	2.00 × 1.58	3.16
18	أول — غرفة نوم 3	4.24 × 3.20	13.57
	المساحة الصافية الداخلية		160.03
	البرندة	**4.20 × 1.40**	**5.88**
	البلكونة	**4.20 × 1.40**	**5.88**
	المساحة الإجمالية المبنية	**11.00 × 8.50 × 2 دور**	**187.00**
	المساحة الكلية (المبنية + التراس والبلكونة)		**198.76**

التسعير المفصّل

البند	المبلغ (ريال)
الكوخ المبني 187.00 م² × 1,500	280,500
البرندة + البلكونة (4.20 × 1.40 × 2) — 11.76 م² × 1,500	17,640
الإجمالي (ريال)	**298,140**

ملاحظات:


- السعر 1,500 ر.س/م² للدورين حسب المخطط المعتمد — شامل الصبة (بصمة المبنى 11.00 × 8.50 م).
- شامل أدوات التأسيس للسباكة والكهرباء (التمديدات الداخلية).
- التوصيلات الخارجية (عداد الكهرباء والمويه والصرف) على العميل.

لقطات المنظور الخارجي


المنظور الأمامي



منظور أمامي من اليسار

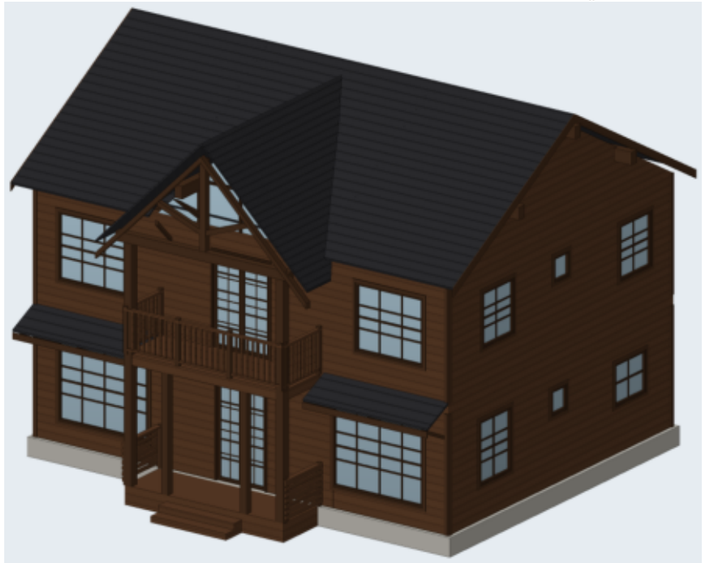

منظور أمامي من اليمين

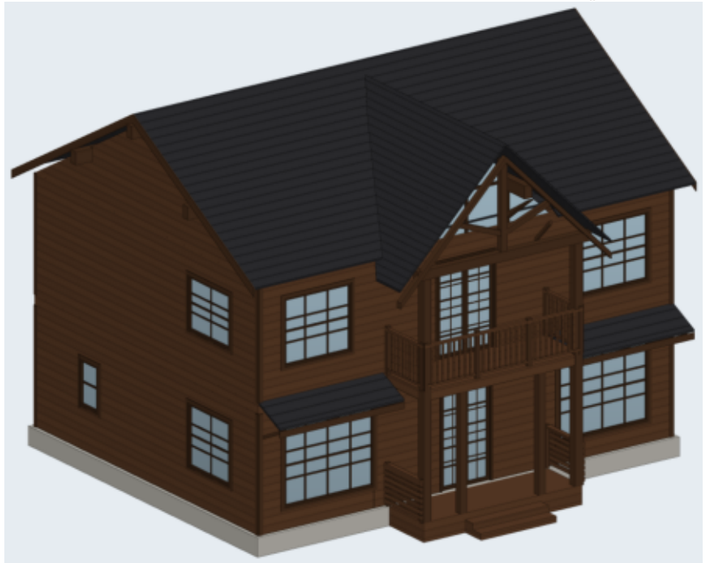

المنظور الخلفي



منظور خلفي من اليمين



منظر علوي



مصنع وتد الأخشاب Watad Wood Factory	المشروع / العميل فيلا خشب دورين – واجهة جملون زجاج وبلكونة – 3 غرف (ماستر) – 11.00 × 8.50 م عميل – الباحة	عنوان اللوحة لقطات المنظور	المقياس –	التاريخ 2026-10-23	رقم اللوحة A-08 (8/11)

المقطع العلوي بالفرش — الدور الأرضي


مقطع أفقي على ارتفاع 1.90 م — توزيع الفرش ومسار الحركة



المشروع / العميل	عنوان اللوحة	المقياس	التاريخ	رقم اللوحة
مصنع وتد الأخشاب Watad Wood Factory **فيلا خشب دورين — واجهة جملون زجاج وبلكونة — 3 غرف (ماستر) — 11.00 × 8.50 م** **عميل — الباحة**	**المقطع العلوي بالفرش — الدور الأرضي**	—	2026-10-23	A-09 (9/11)

المقطع العلوي بالفرش — الدور الأول

مقطع أفقي على ارتفاع 1.90 م — توزيع الفرش ومسار الحركة

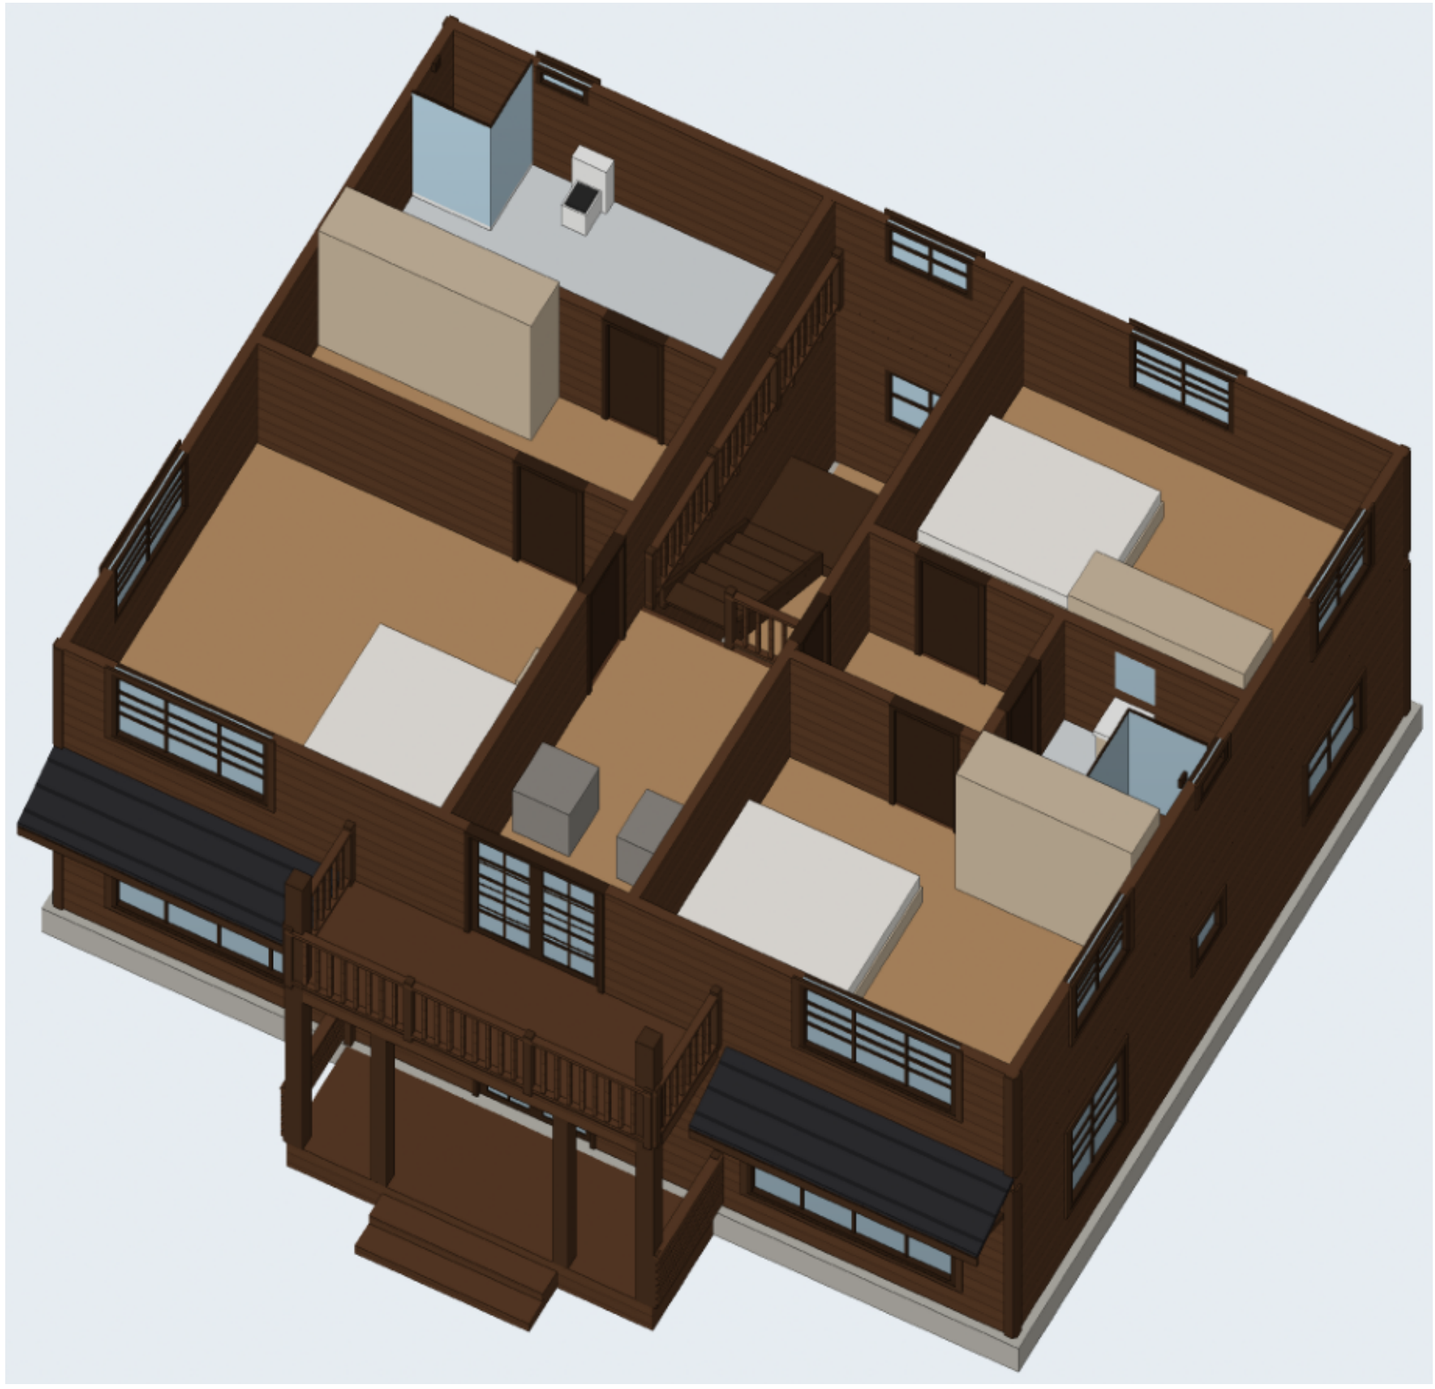

المشروع / العميل	عنوان اللوحة	المقياس	التاريخ	رقم اللوحة
مصنع وتد الأخشاب Watad Wood Factory فيلا خشب دورين — واجهة جملون زجاج وبلكونة — 3 غرف (ماستر) — 11.00 × 8.50 م عميل — الباحة	المقطع العلوي بالفرش — الدور الأول	—	2026-10-23	A-10 (10/11)

المنظور ثلاثي الأبعاد والمواد

النمط: جوزي غامق + إطارات سوداء — رندر واقعي بخامات حقيقية



جدول المواد والألوان

الخشب / الصبغة

صبغة جوزي غامق

القرميد

قرميد رمادي غامق

الزجاج

زجاج شفاف

إطارات الشبابيك والأبواب

إطار خشب بنفس الصبغة أغمق

الكنار والزوايا

نفس الصبغة أغمق درجة


الصبة

خرسانة 45 سم


الدربزين: ألواح أفقية متقاربة (عصري)

تقسيم الشبابيك: شبكة | الباب الرئيسي: زجاج بتقسيمات (فرنسي)

أنواع الدربزين المعتمدة (من مشاريع المصنع)

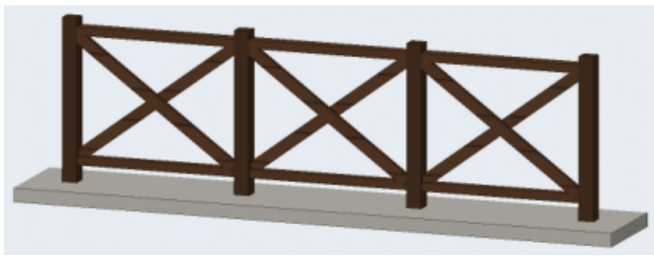

تقاطع X (صورة 5)

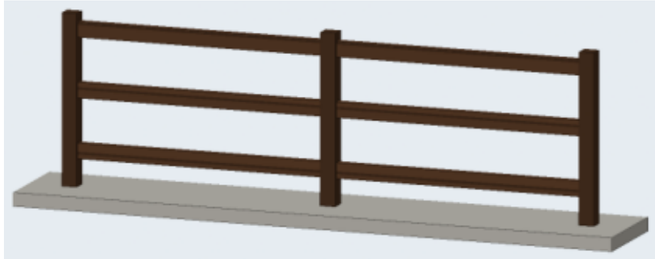

3 مرابيع أفقية (صورة 2)



قوائم رأسية متقاربة (صورة 1)

المشروع / العميل	عنوان اللوحة	المقياس	التاريخ	رقم اللوحة
مصنع وتد الأخشاب Watad Wood Factory — **فيلا خشب دورين — واجهة جملون زجاج وبلكونة — 3 غرف (ماستر) — 11.00 × 8.50 م** — **عميل — الباحة**	**المنظور والمواد**	—	**2026-10-23**	**A-11 (11/11)**