


المسقط الأفقي مع الفرش - الدور الأرضي

الأبعاد بالسنتيمتر - الجدران: قوائم 5×7 + تليس 2.5 من الجهتين (12 سم)

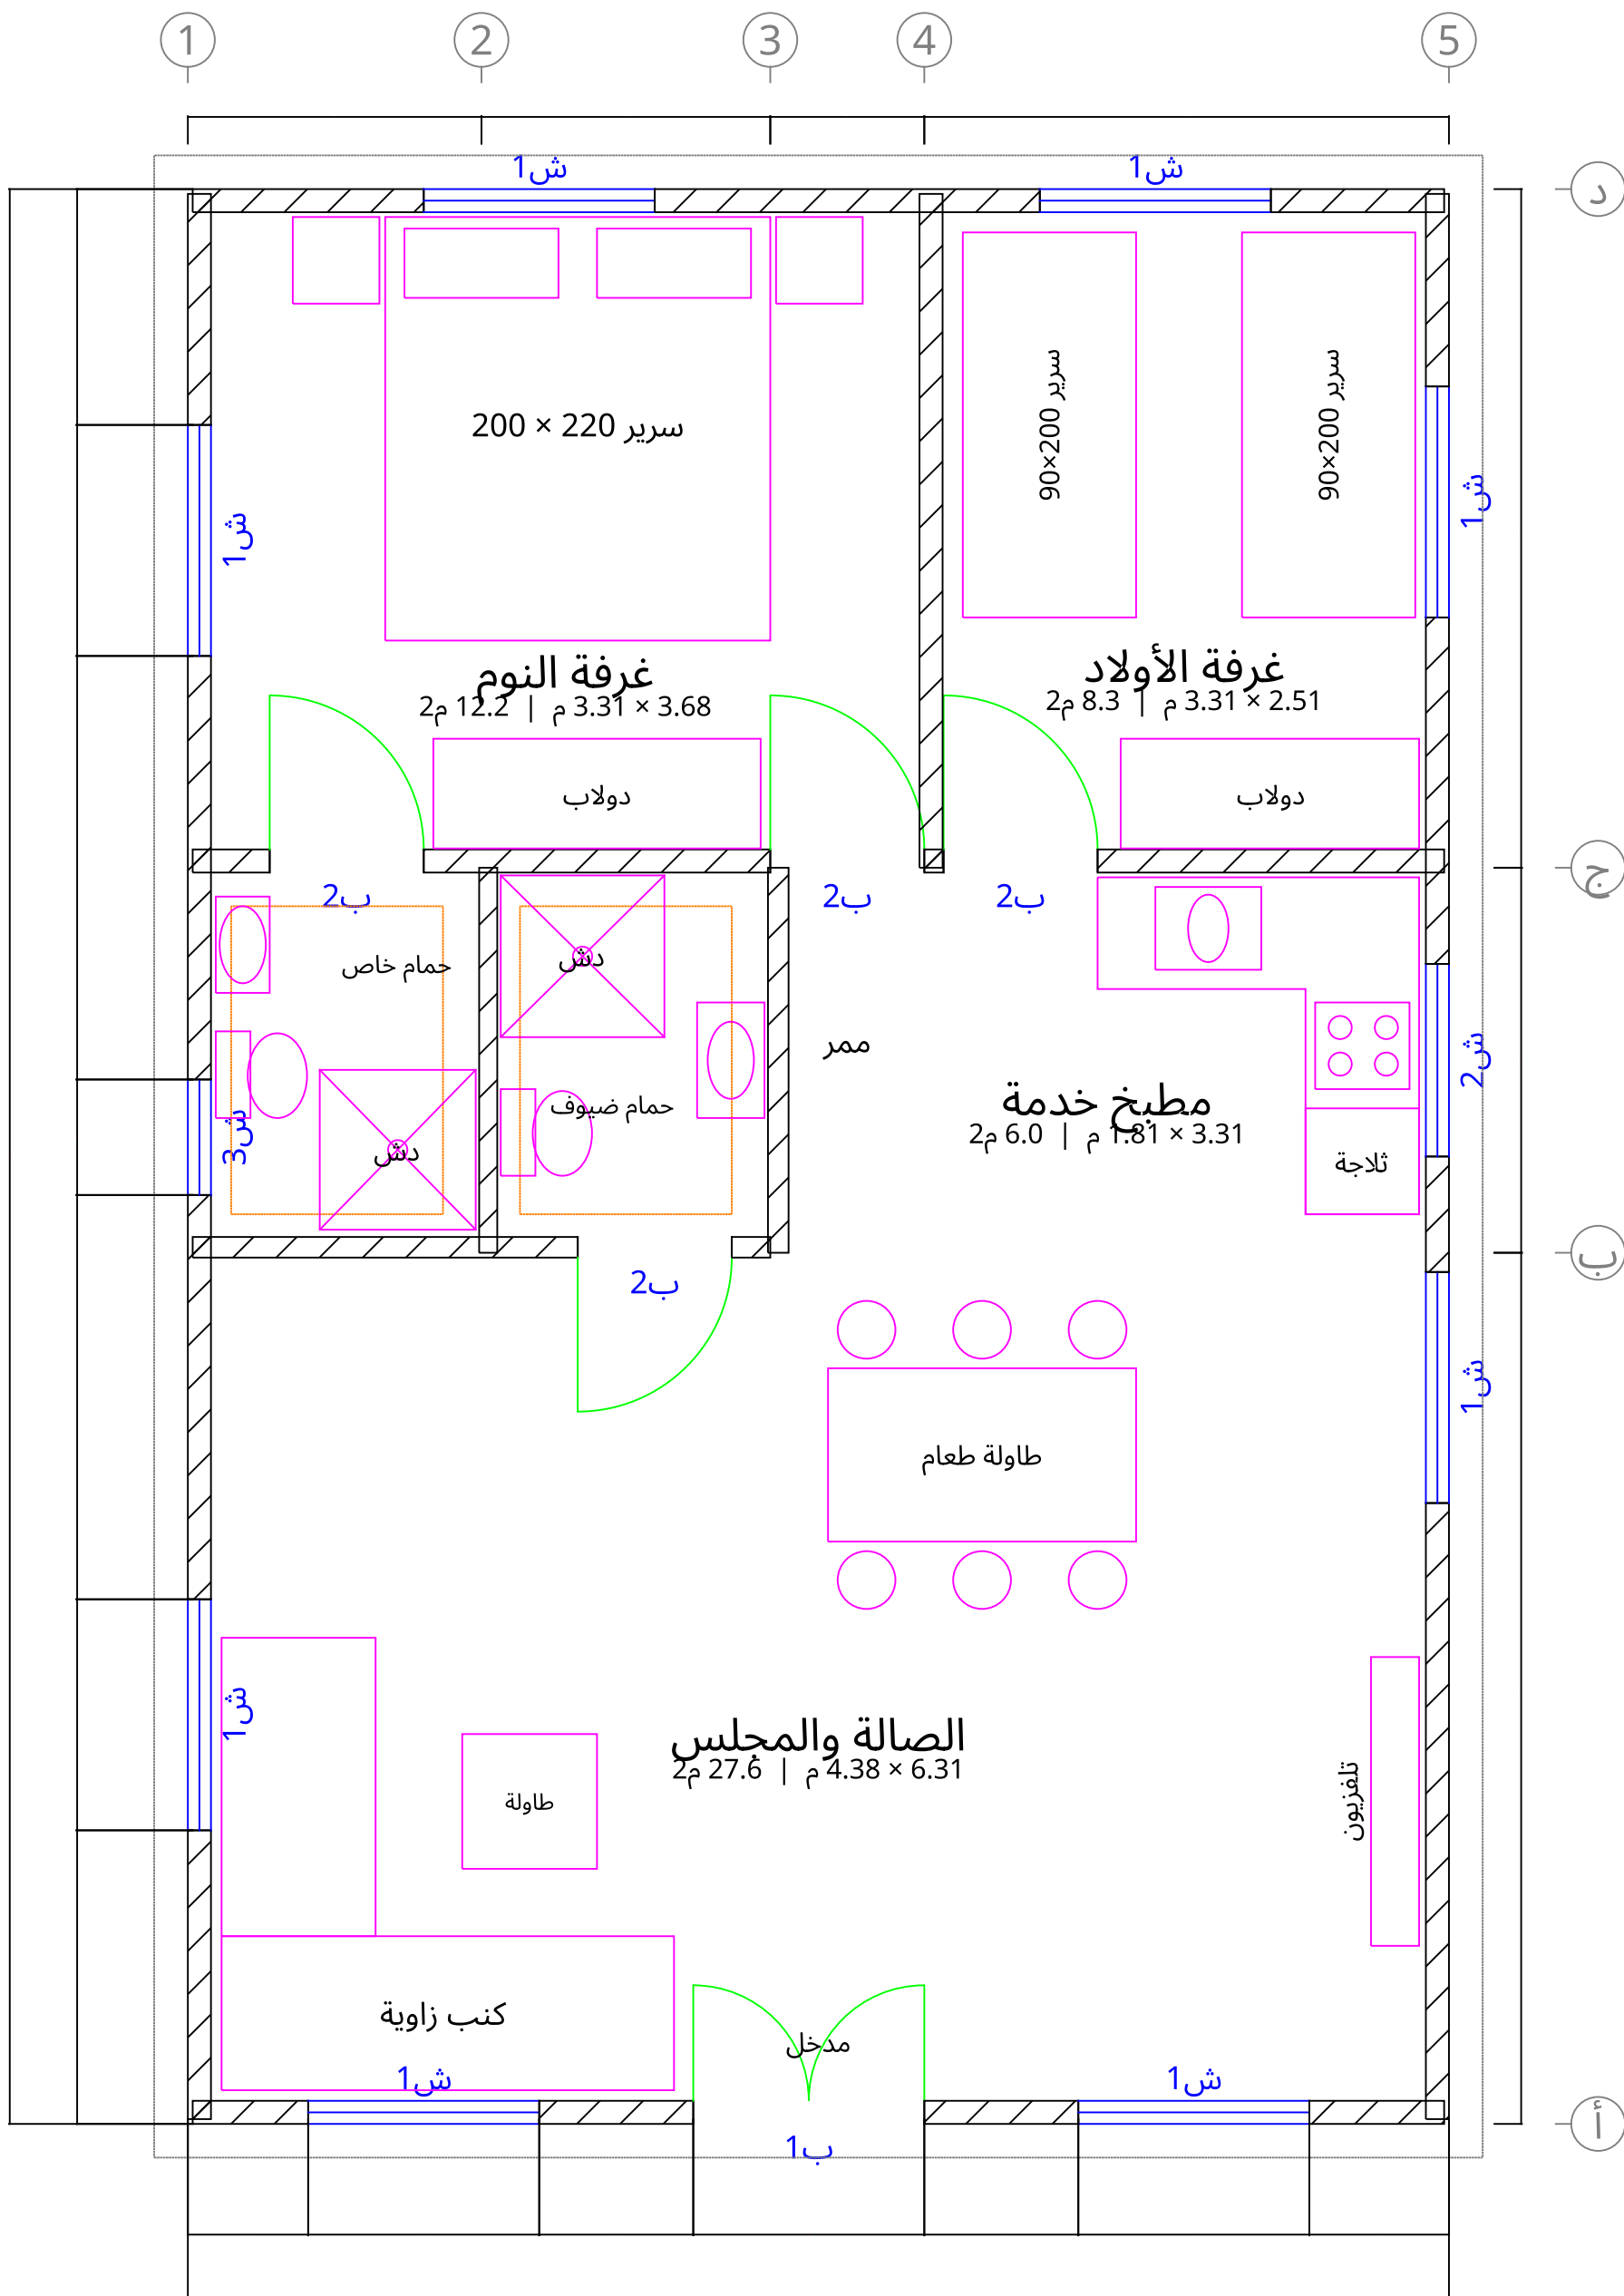

+4.60
▽
قمة الجملون

+2.80
▽
أعلى الجدار

وجه الصبة
0.00
▽
▽
-0.20
منسوب الأرض



الواجهة الجنوبية (الرئيسية)

مقياس 1:50 | الوحدة: سم

+4.60
▽
قمة الجملون

+2.80
▽
أعلى الجدار


وجه الصبة
0.00
▽
▽
-0.20
منسوب الأرض




الواجهة الشمالية

مقياس 1:50 | الوحدة: سم



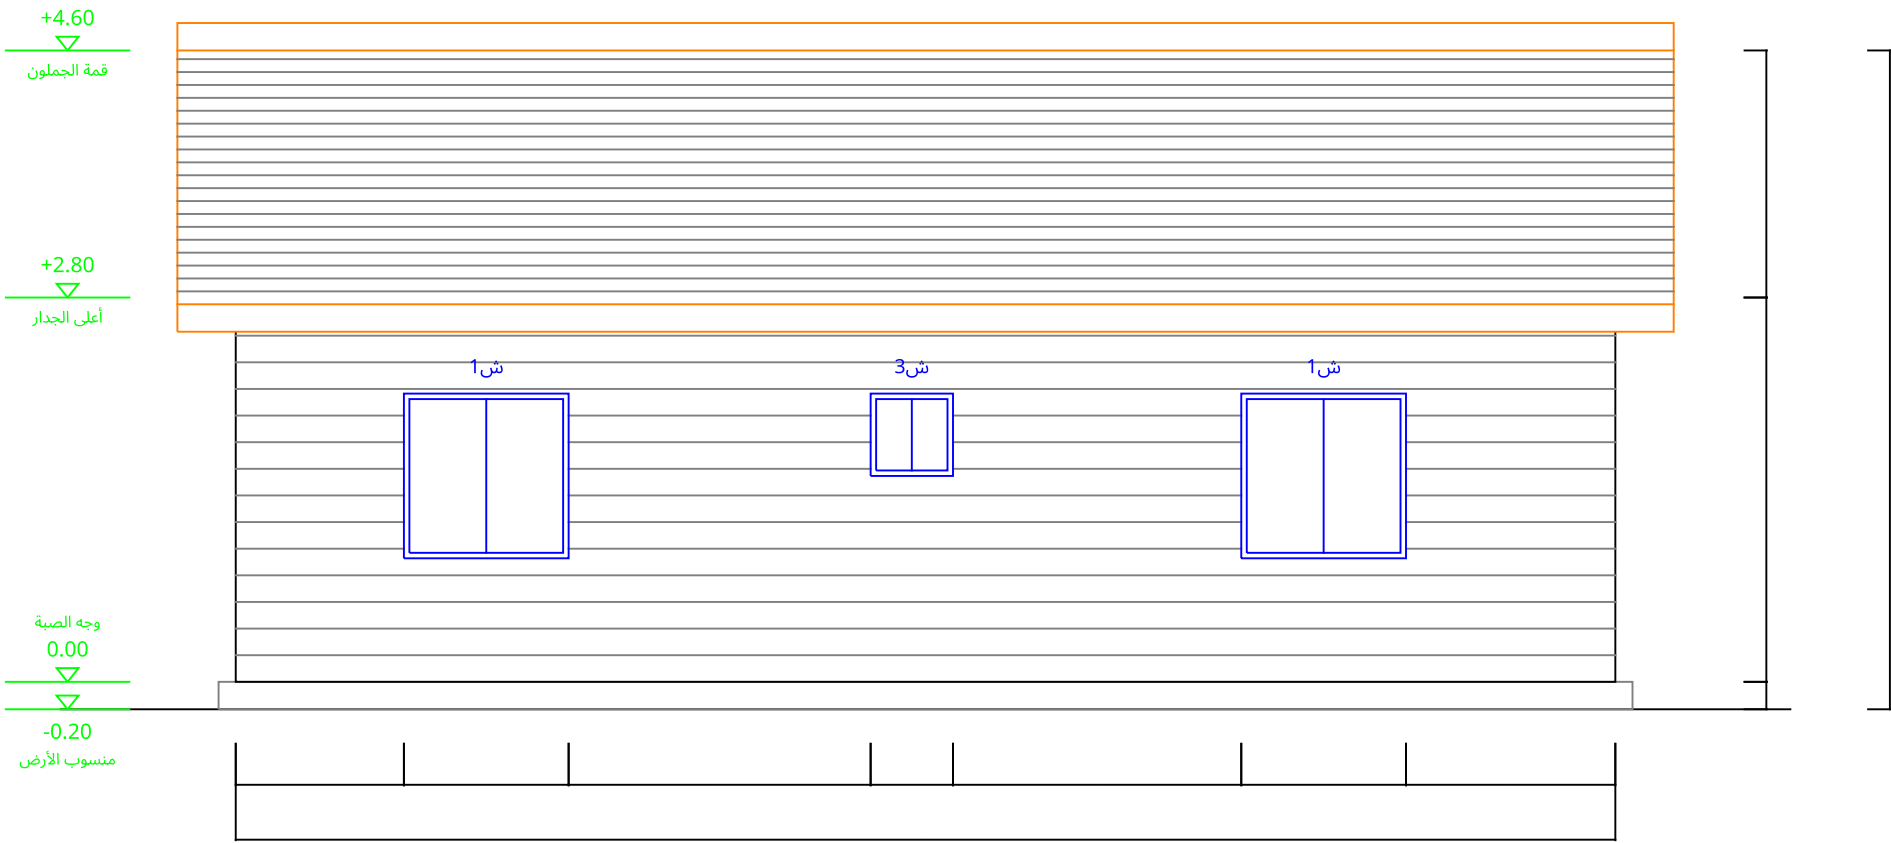


الواجهة الغربية
مقياس 1:50 | الوحدة: سم

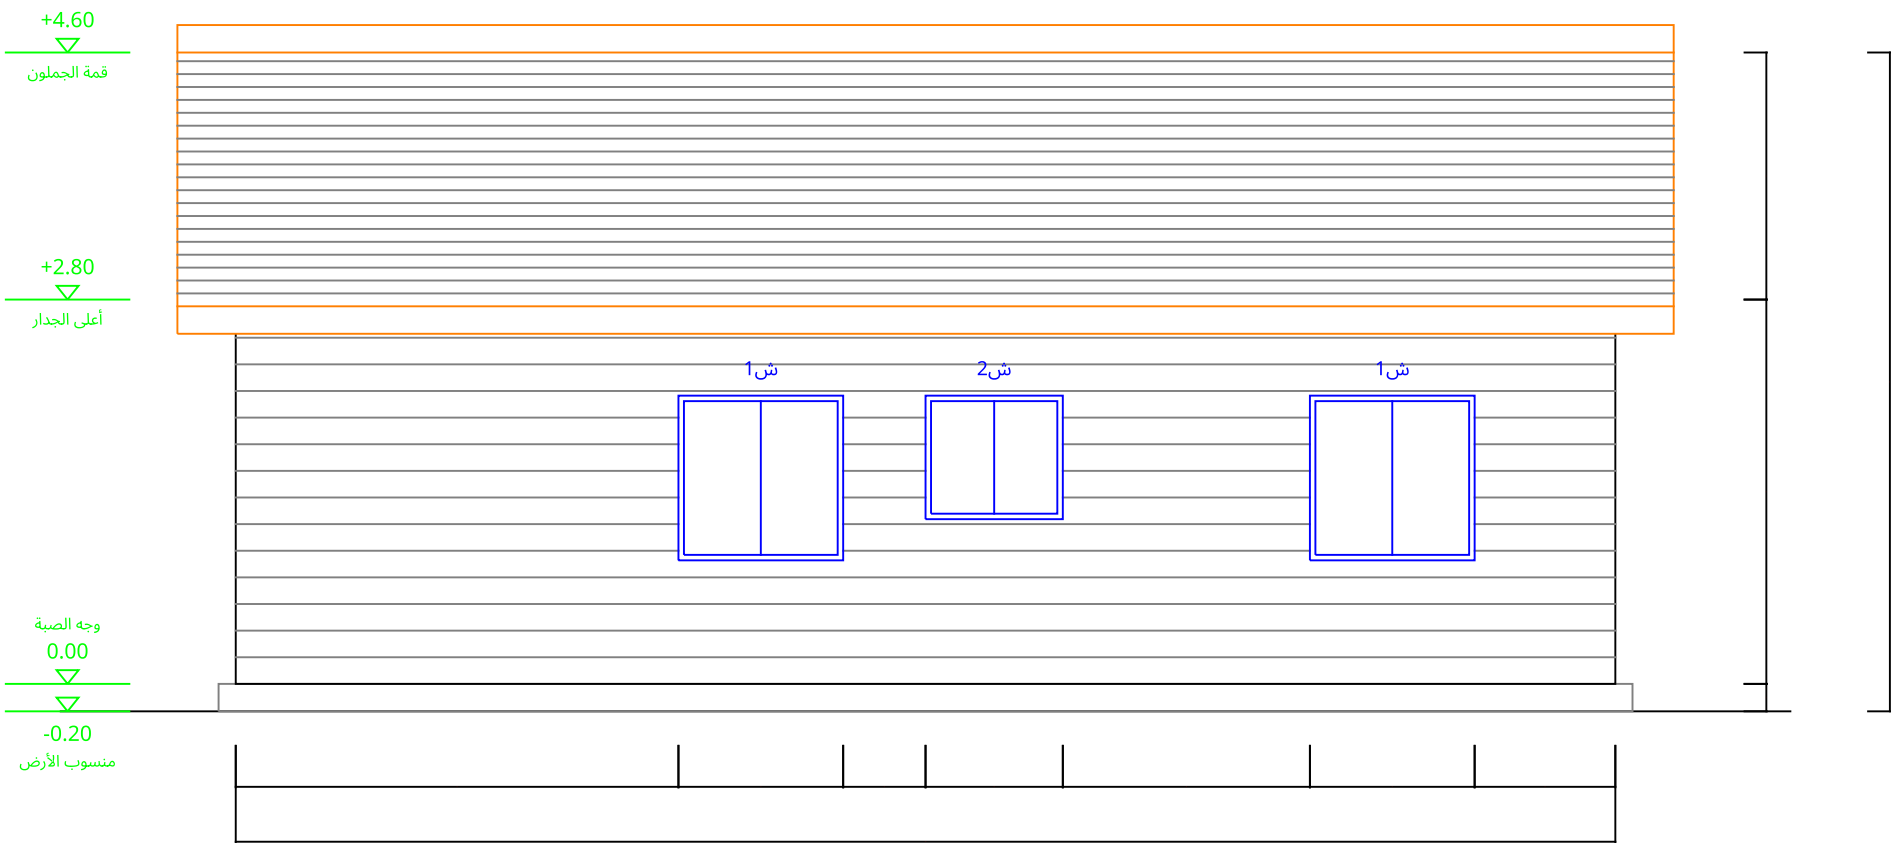


الواجهة الشرقية
مقياس 1:50 | الوحدة: سم



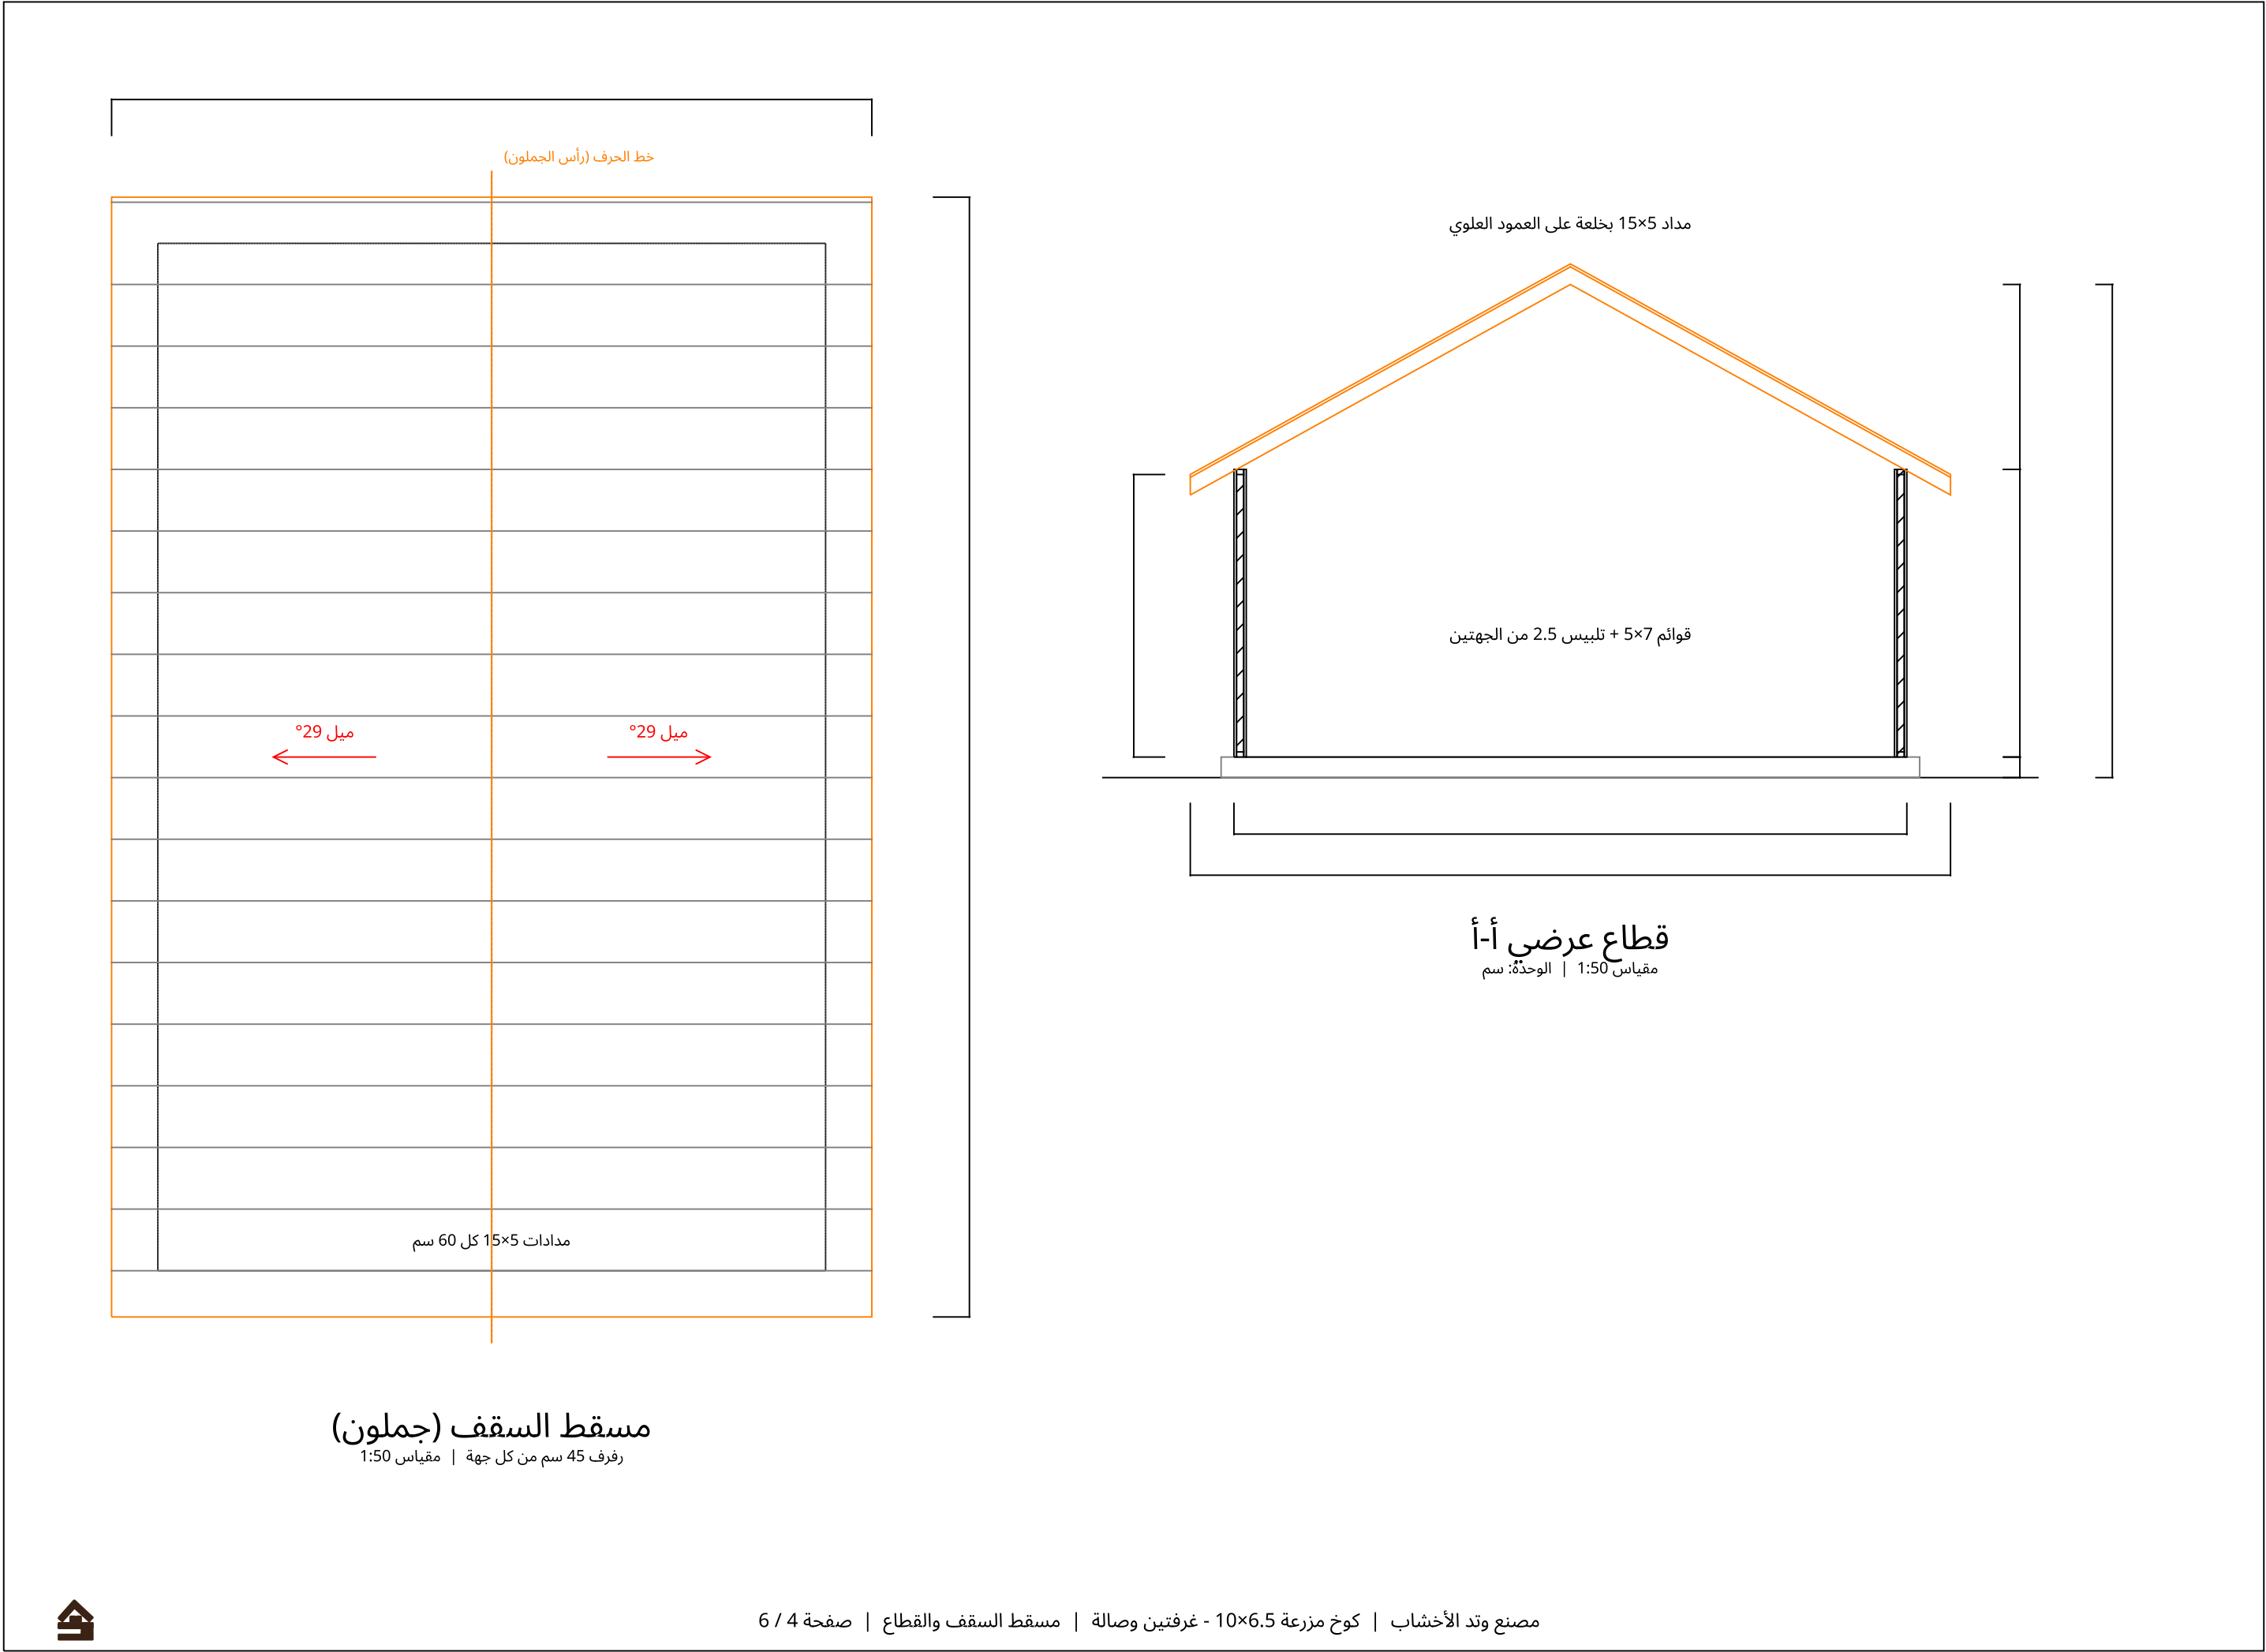

جدول مقاسات الأبواب والشبابيك

مقاس الفتحة الصافي في الجدار - الوحدة: سم

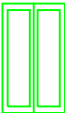الرمز	النوع	العرض (سم)	الارتفاع (سم)	ارتفاع الجلسة (سم)	العدد	الموقع	الرسم
ب1	باب رئيسي مزدوج	120	210	-	1	المدخل - الواجهة الجنوبية	
ب2	باب داخلي	80	210	-	4	حمام ضيوف - حمام خاص - غرفة النوم - غرفة الأولاد	
ش1	شباك	120	120	90	8	جنوب 2 - شمال 2 - غرب 2 - شرق 2	
ش2	شباك مطبخ	100	90	120	1	المطبخ - الواجهة الشرقية	
ش3	شباك حمام	60	60	150	1	الحمام الخاص - الواجهة الغربية	

الإجمالي: أبواب 5 - شبابيك 10



جدول المساحات

م	الفراغ	الأبعاد الداخلية (م)	المساحة (م2)
1	الصالة والمجلس	6.31 × 4.38	27.64
2	مطبخ خدمة	3.31 × 1.81	5.99
3	حمام ضيوف	1.40 × 1.81	2.54
4	حمام خاص	1.39 × 1.81	2.52
5	غرفة النوم	3.68 × 3.31	12.18
6	غرفة الأولاد	2.51 × 3.31	8.31
7	الممر	0.68 × 1.81	1.23
المساحة الصافية الداخلية			60.41
المساحة الإجمالية الخارجية			65.83



مصنع وتد الأخشاب

Watad Wood Factory

المشروع	كوخ مزرعة 10×6.5 - غرفتين وصالة
العميل	
الموقع	مزرعة ريفية
الاستخدام	شخصي واستثماري
المدير	م. أحمد
التاريخ	2026-09-28
المقياس	1:50
الوحدة	سم

التسعير

البند	القيمة
المساحة الإجمالية (م2)	65.83
سعر المتر (ريال)	1,096
الإجمالي (ريال)	72,147

