




المسقط الأفقي مع الفرش
الأبعاد بالسنتيمتر - الجدران: قوائم 5×7 + تليس 2.5 من الجهتين (12 سم)

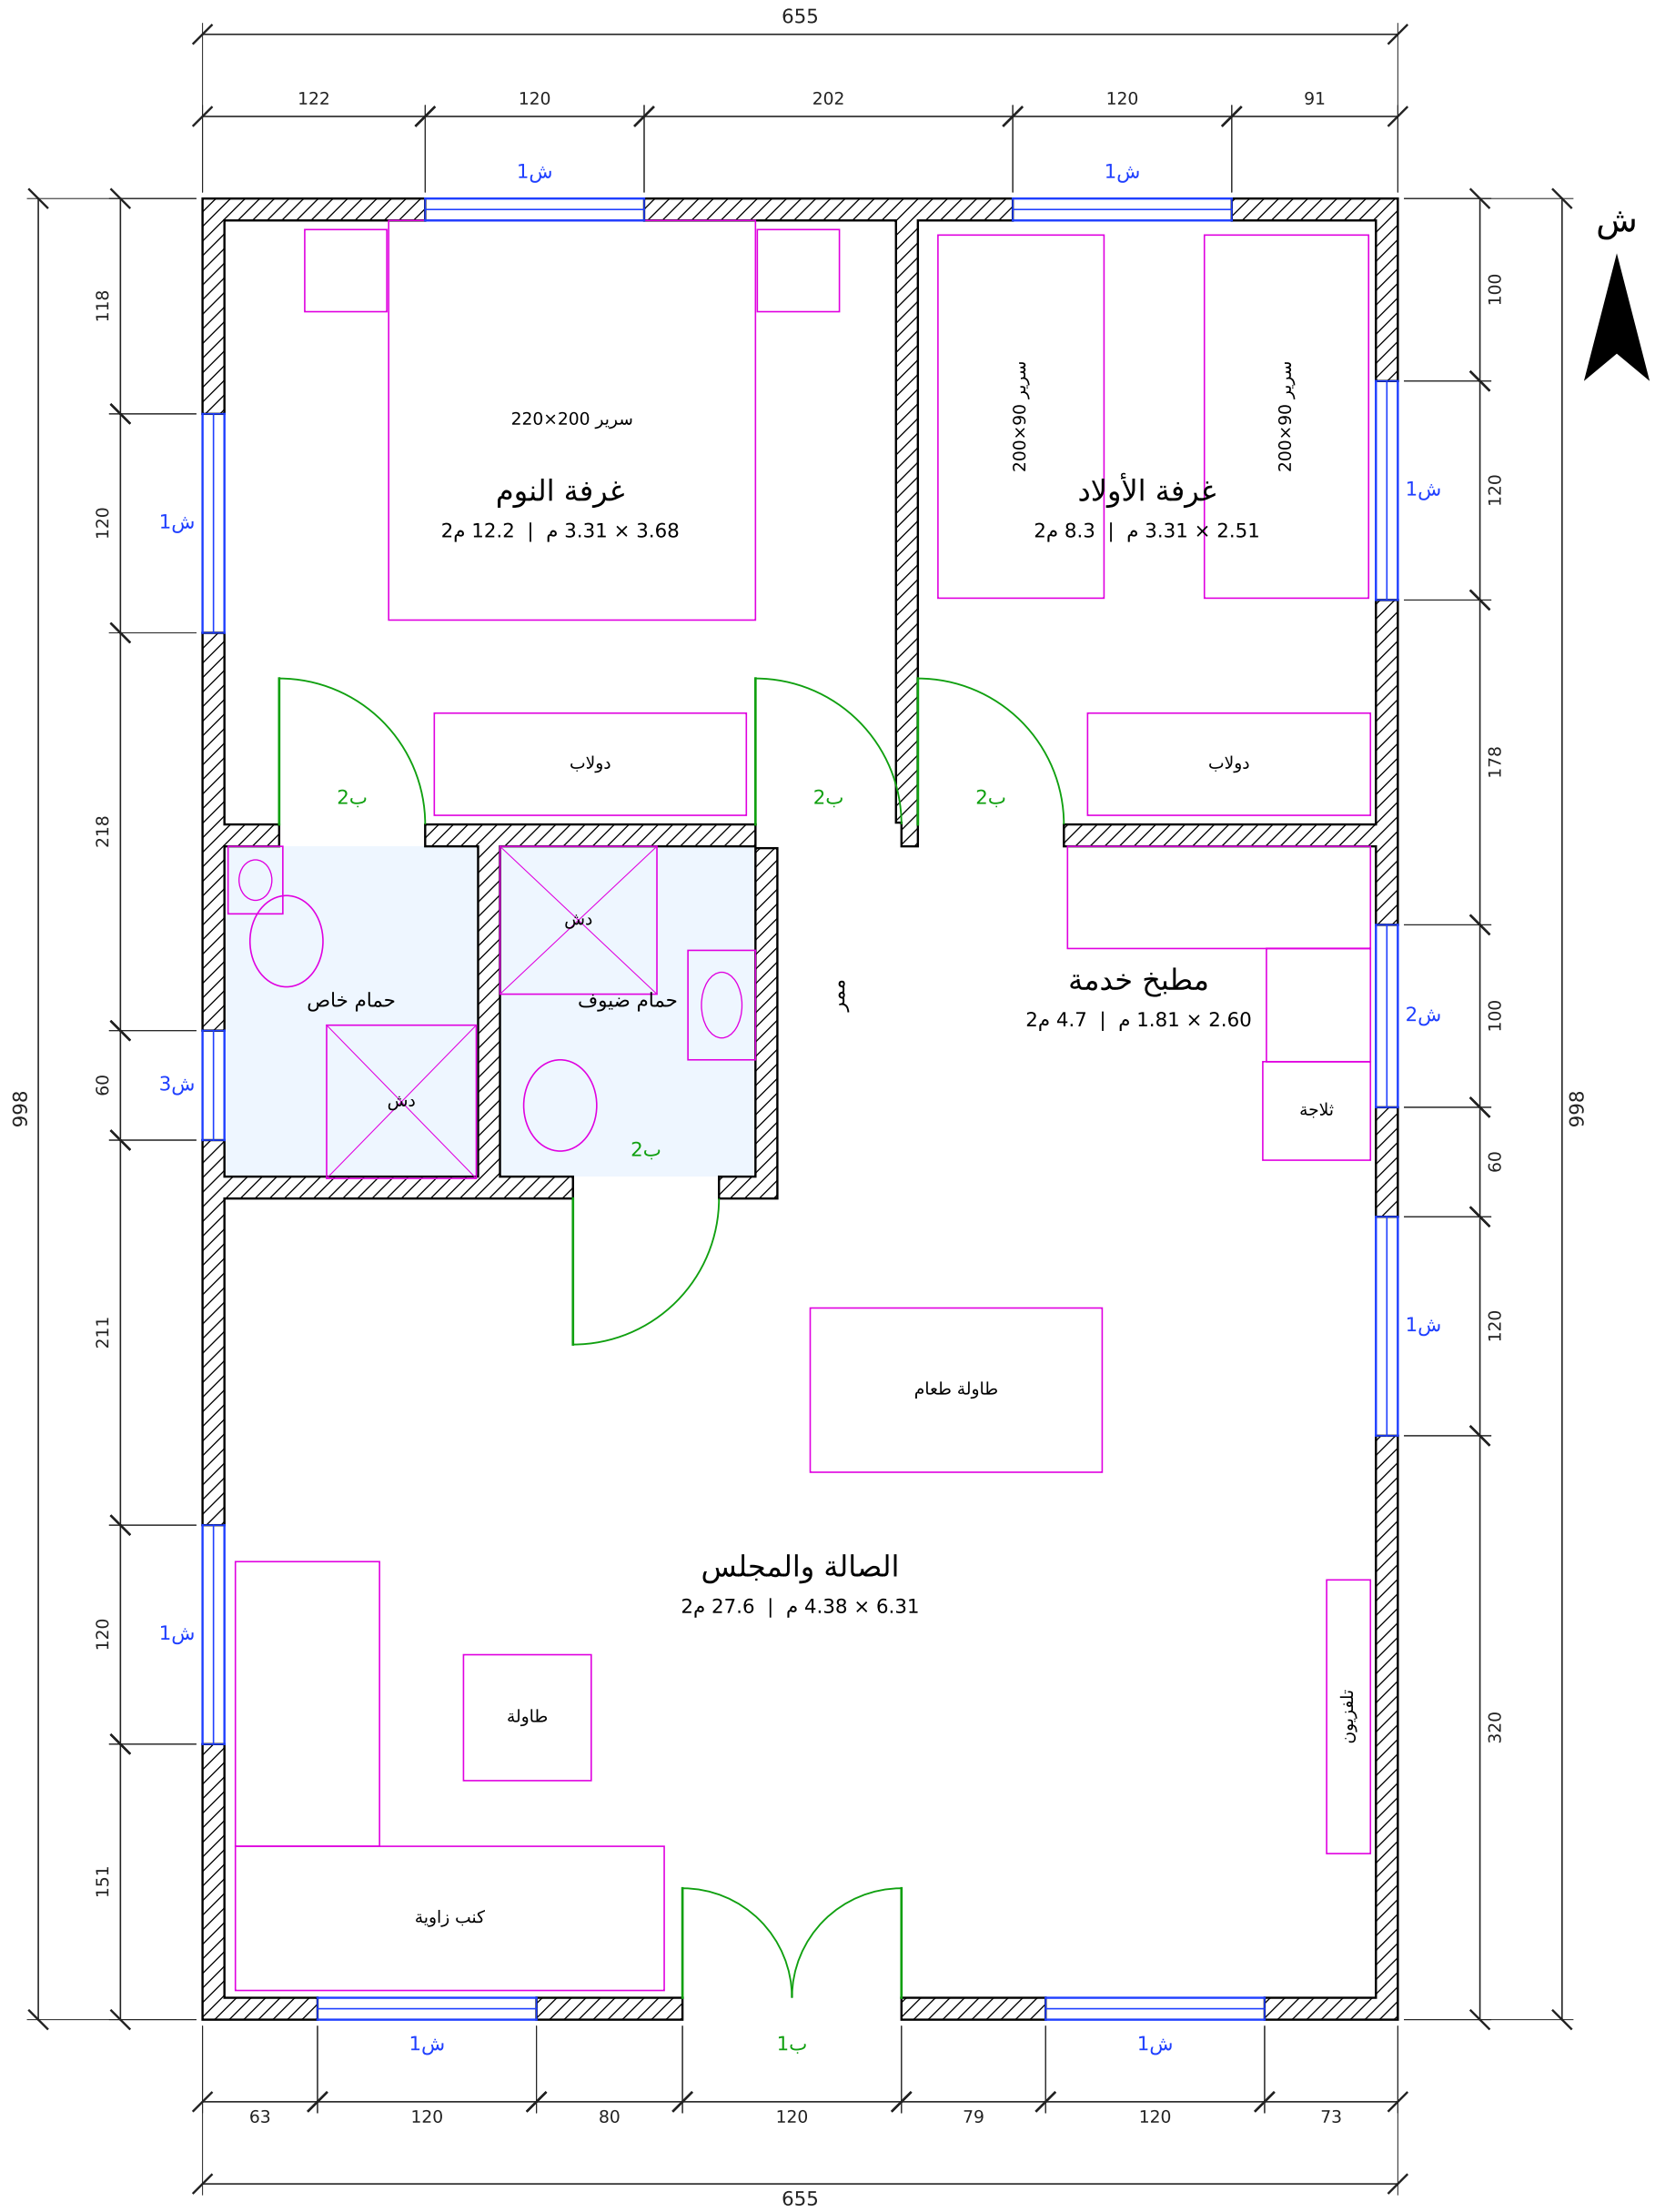

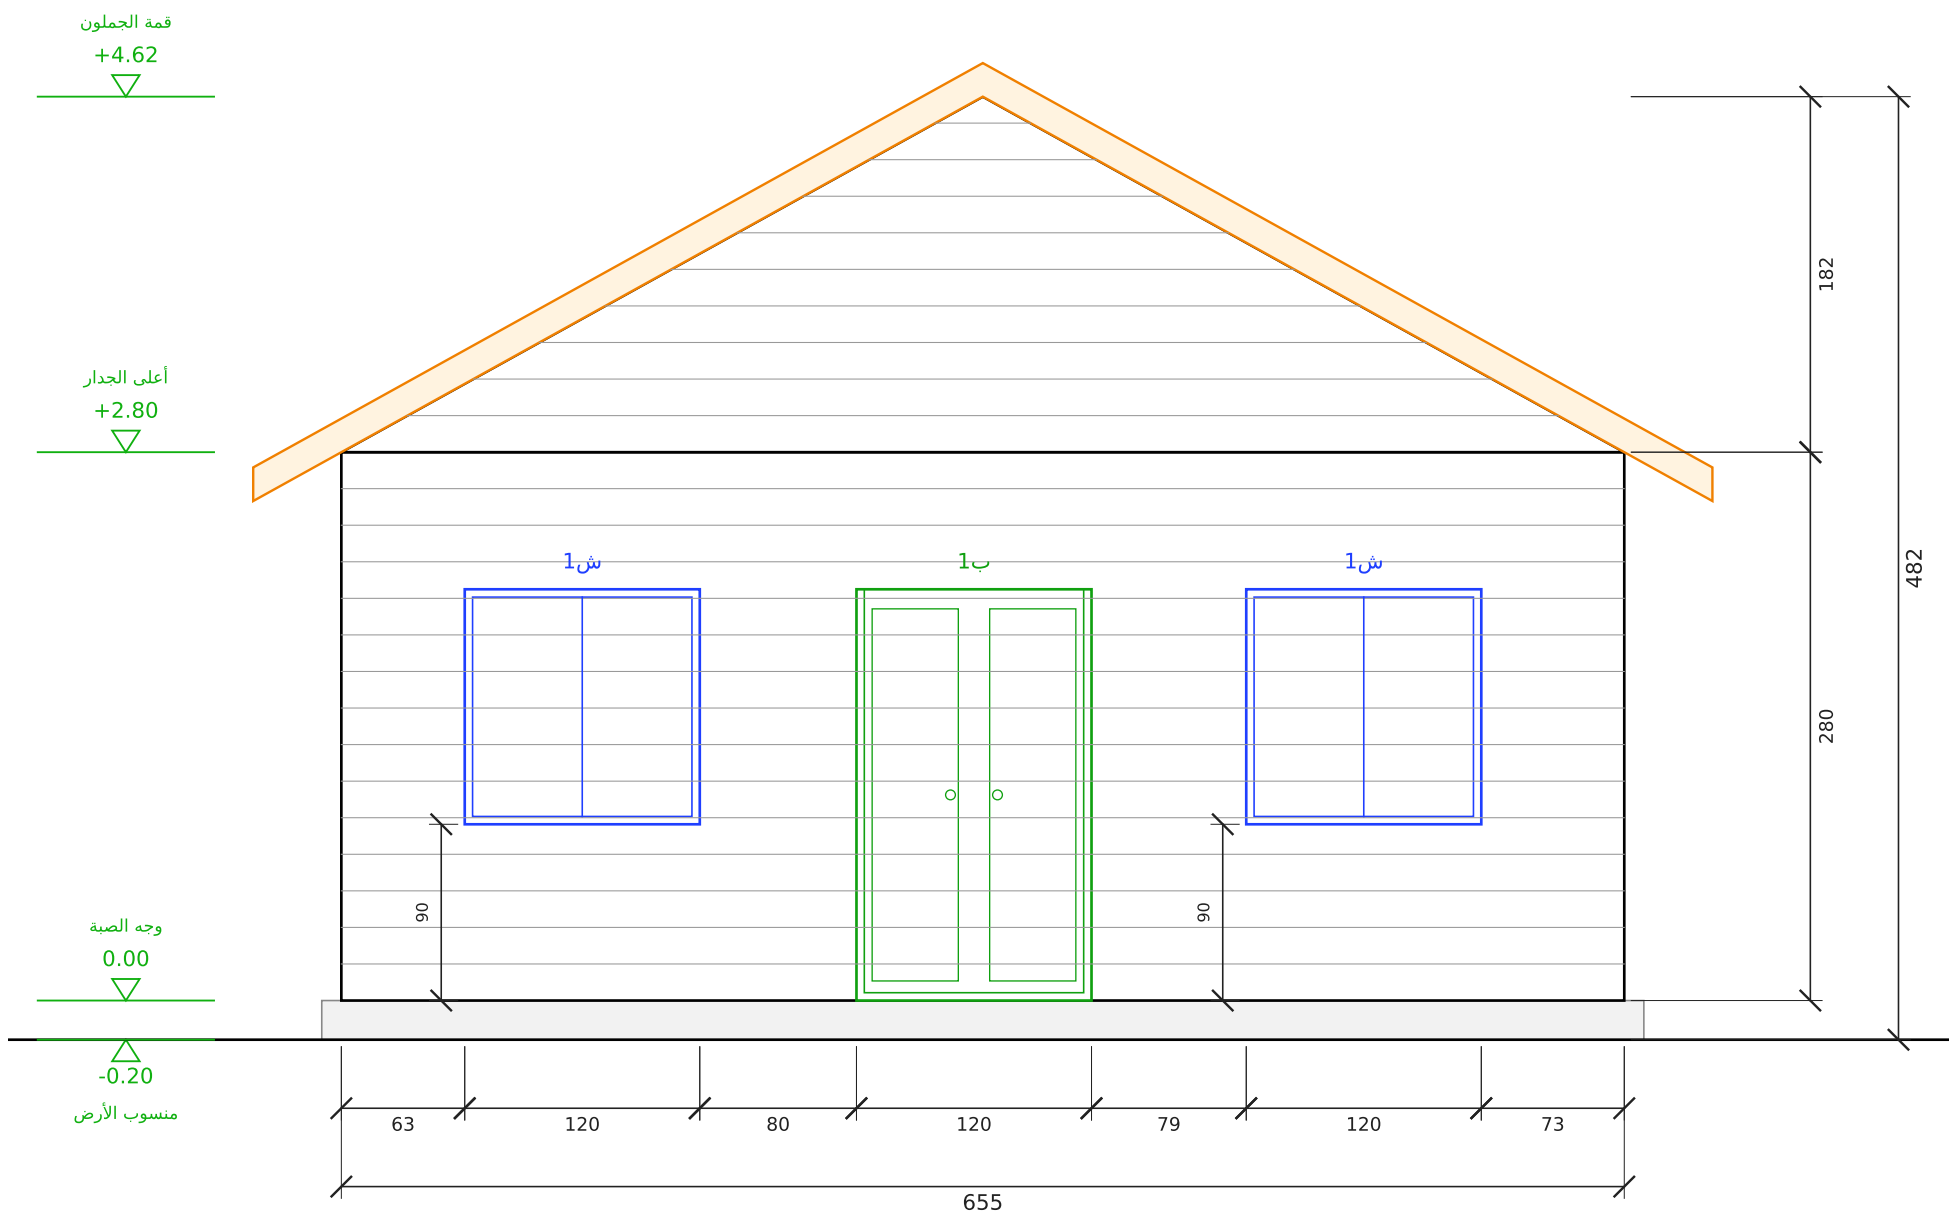


الواجهة الجنوبية (الرئيسية)

مقياس 1:50 | الوحدة: سم

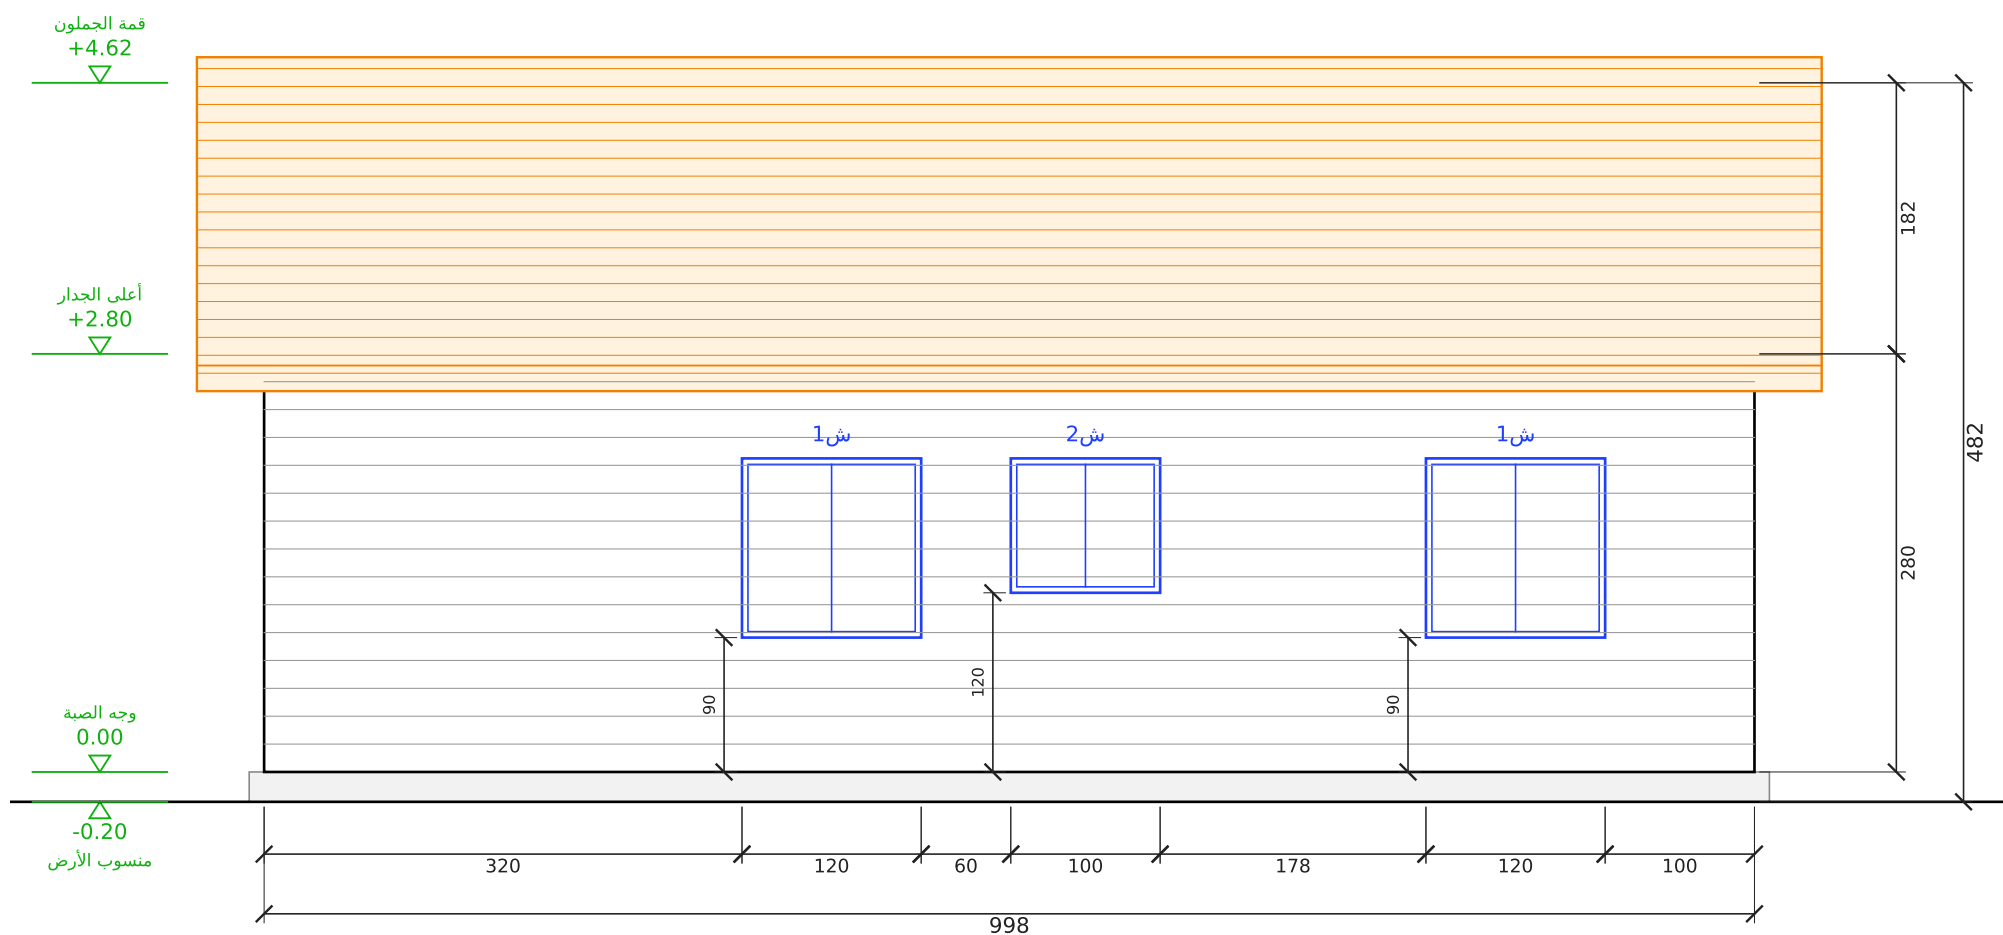


الواجهة الشرقية

مقياس 1:50 | الوحدة: سم

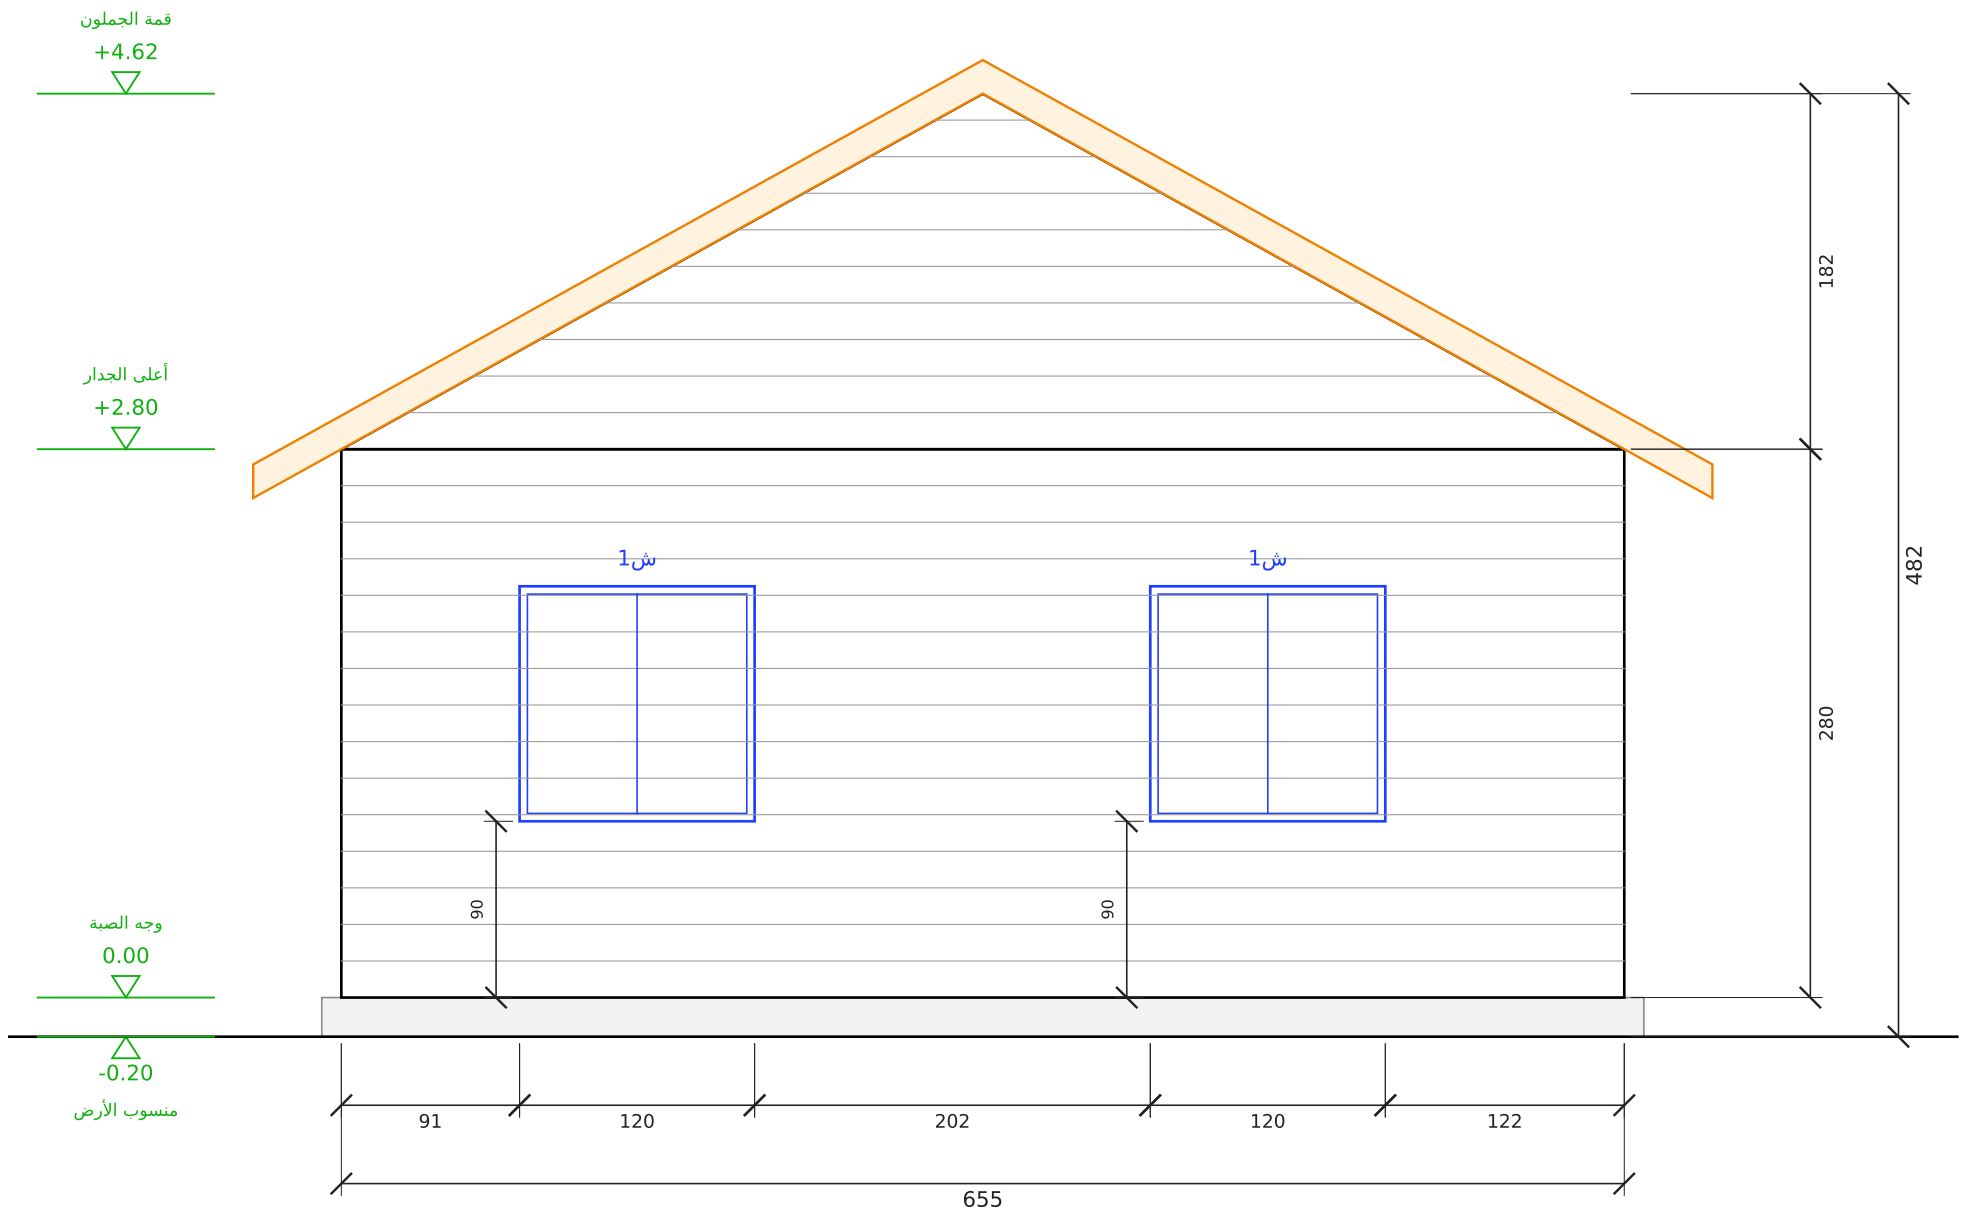

الواجهة الشمالية


مقياس 1:50 | الوحدة: سم

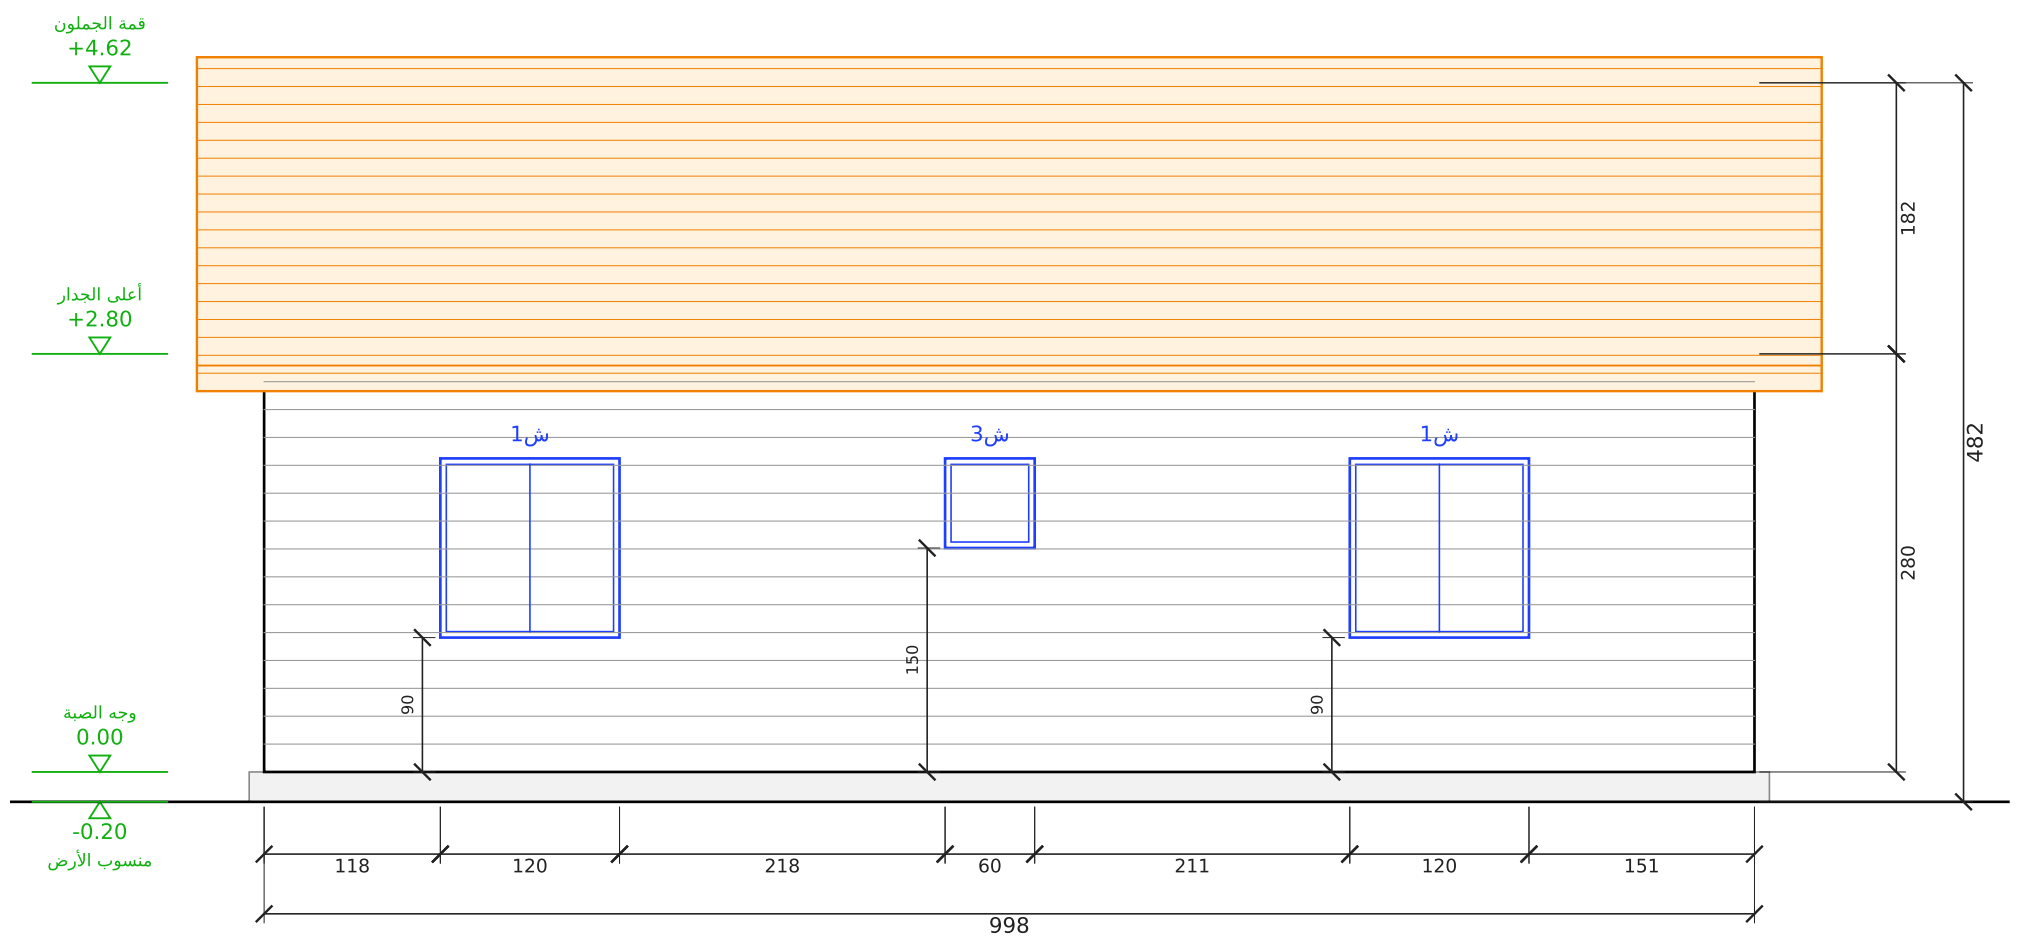


الواجهة الغربية

مقياس 1:50 | الوحدة: سم


مسقط السقف (جملون)
رفر 45 سم من كل جهة | مقياس 1:50

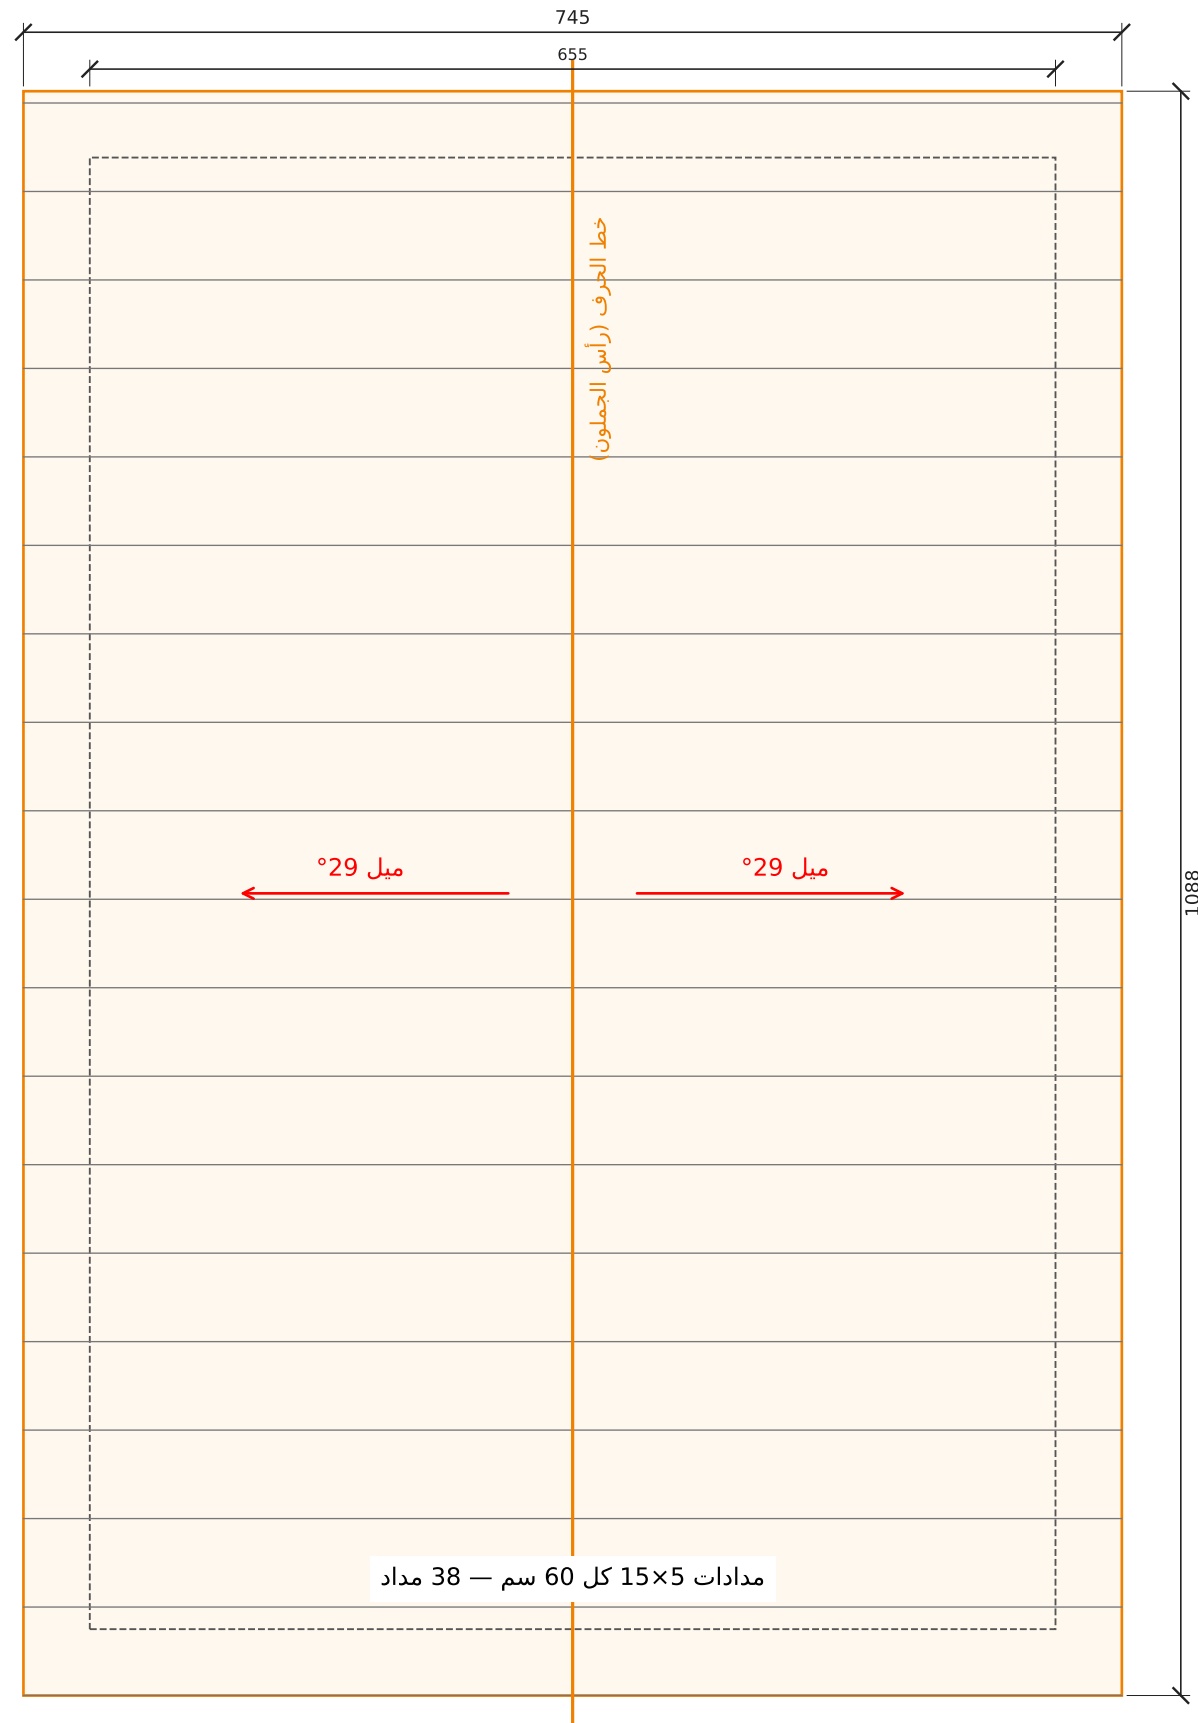

قطاع عرضي أ-أ
مقياس 1:50 | الوحدة: سم

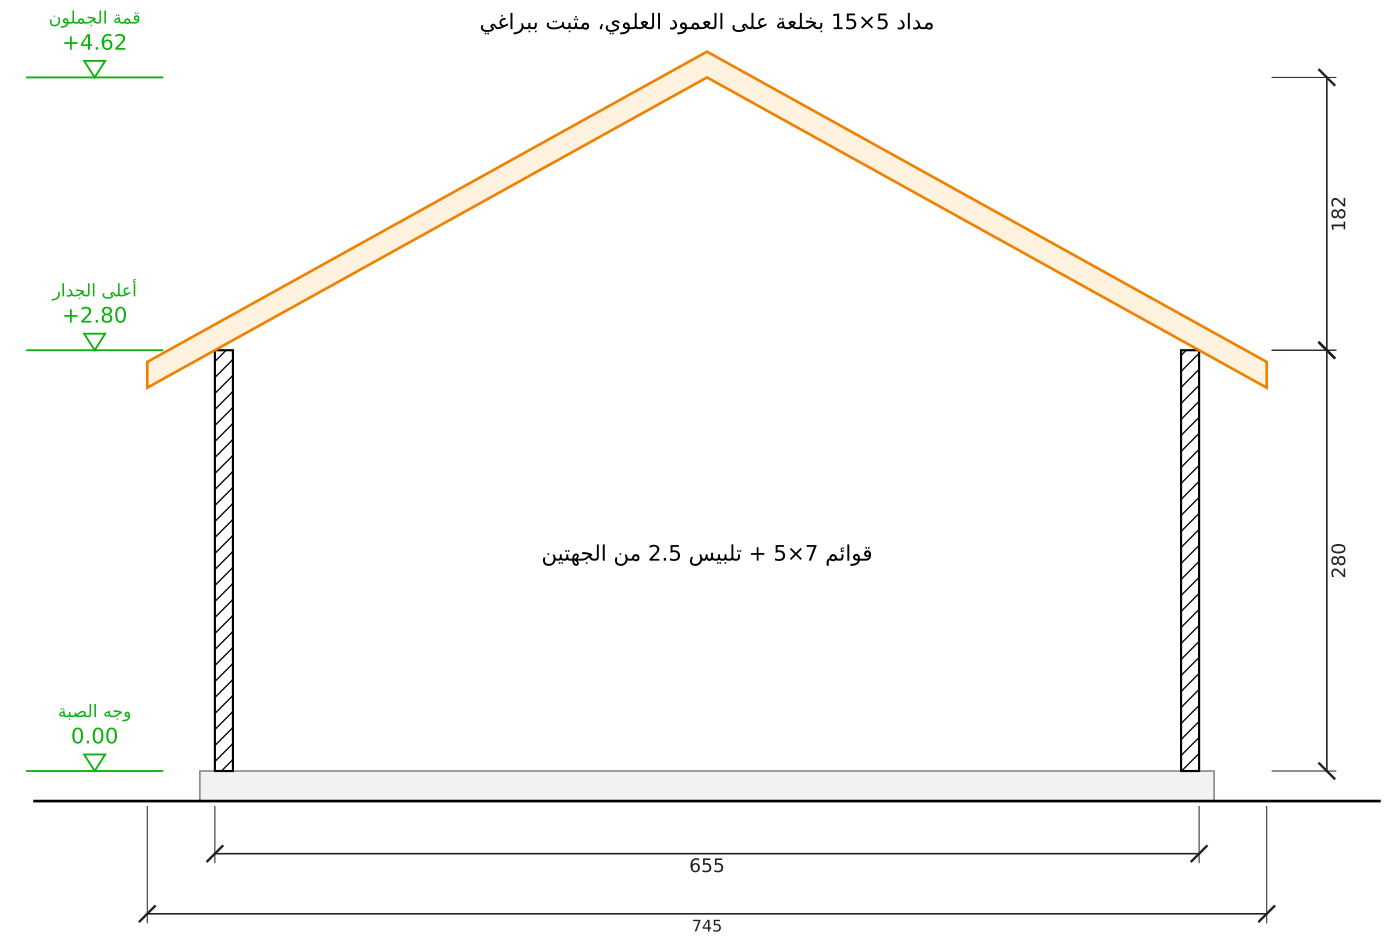

تفصيلة جلوس المداد على العلوي (1:5)

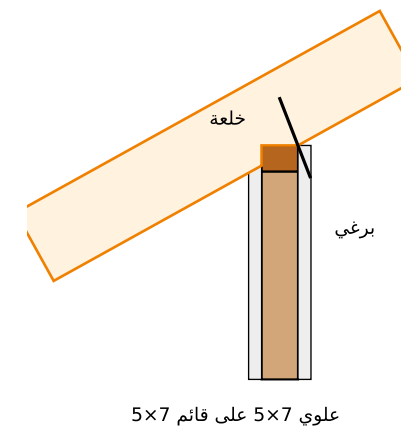

جدول مقاسات الأبواب والشبابيك
مقاس الفتحة الصافي في الجدار - الوحدة: سم

الرمز	النوع	العرض (سم)	الارتفاع (سم)	ارتفاع الجلسة (سم)	العدد	الموقع
ب1	باب مزدوج	120	210	-	1	الجنوبية (الرئيسية)
ب2	باب	80	210	-	4	حمام ضيوف - حمام خاص - غرفة النوم - غرفة الأولاد
ش1	شباك	120	120	90	8	الجنوبية (الرئيسية) 2 - الشرقية 2 - الشمالية 2 - الغربية 2
ش2	شباك	100	90	120	1	الشرقية
ش3	شباك	60	60	150	1	الغربية

الإجمالي: أبواب 5 - شبابيك 10

مصنع وتد الأخشاب
Watad Wood Factory

البند	القيمة
المشروع	كوخ مزرعة 10×6.5 - غرفتين وصالة
العميل	
الموقع	مزرعة ريفية
الاستخدام	شخصي واستثماري
المدير	م. أحمد
التاريخ	2026-09-28
المقياس	1:50
الوحدة	سم


التسعير

البند	القيمة
المساحة الإجمالية (م2)	65.37
سعر المتر (ريال)	1,096
الإجمالي (ريال)	71,646


جدول المساحات

م	الفراغ	الأبعاد الداخلية (م)	المساحة (م2)
1	الصالة والمجلس	6.31 × 4.38	27.64
2	حمام خاص	1.39 × 1.81	2.52
3	حمام ضيوف	1.40 × 1.81	2.53
4	ممر	0.68 × 1.81	1.23
5	مطبخ خدمة	2.60 × 1.81	4.71
6	غرفة النوم	3.68 × 3.31	12.18
7	غرفة الأولاد	2.51 × 3.31	8.31
	المساحة الصافية الداخلية		59.11
	المساحة الإجمالية الخارجية	6.55 × 9.98	65.37

تأطير جدار جنوب — الطول 643 سم، الارتفاع 280 سم

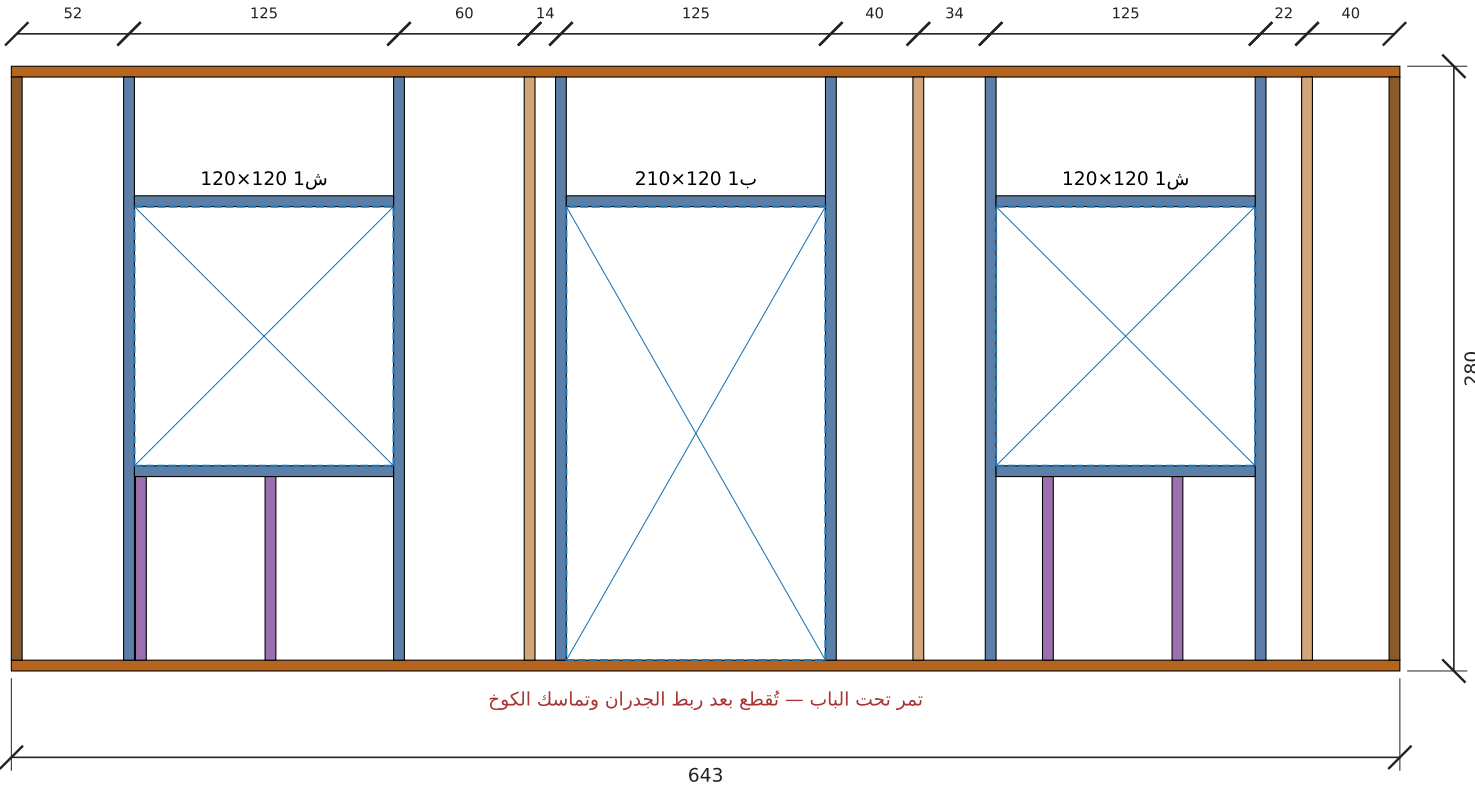


تأطير جدار شرق — الطول 986 سم، الارتفاع 280 سم

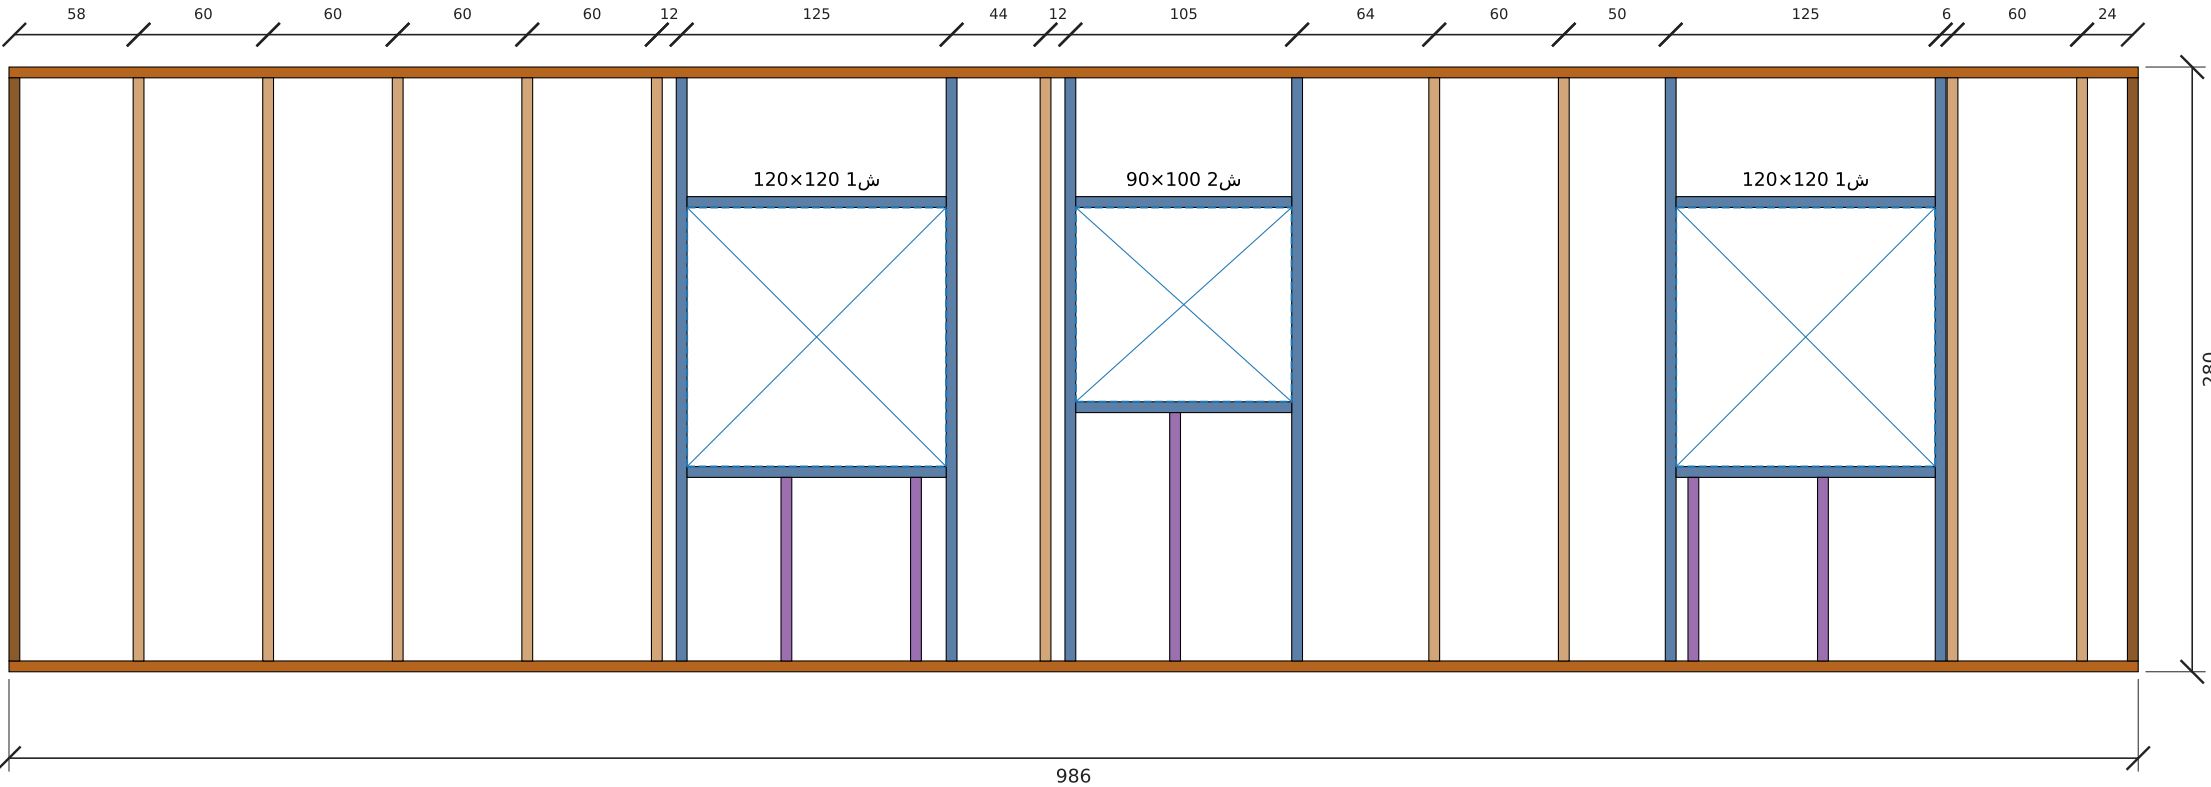


عمود قصير جلسة شباك رأس فتحة جنب فتحة عمود زاوية عمود عمود علوي قاعدة سفلية

تأطير جدار شمال — الطول 643 سم، الارتفاع 280 سم

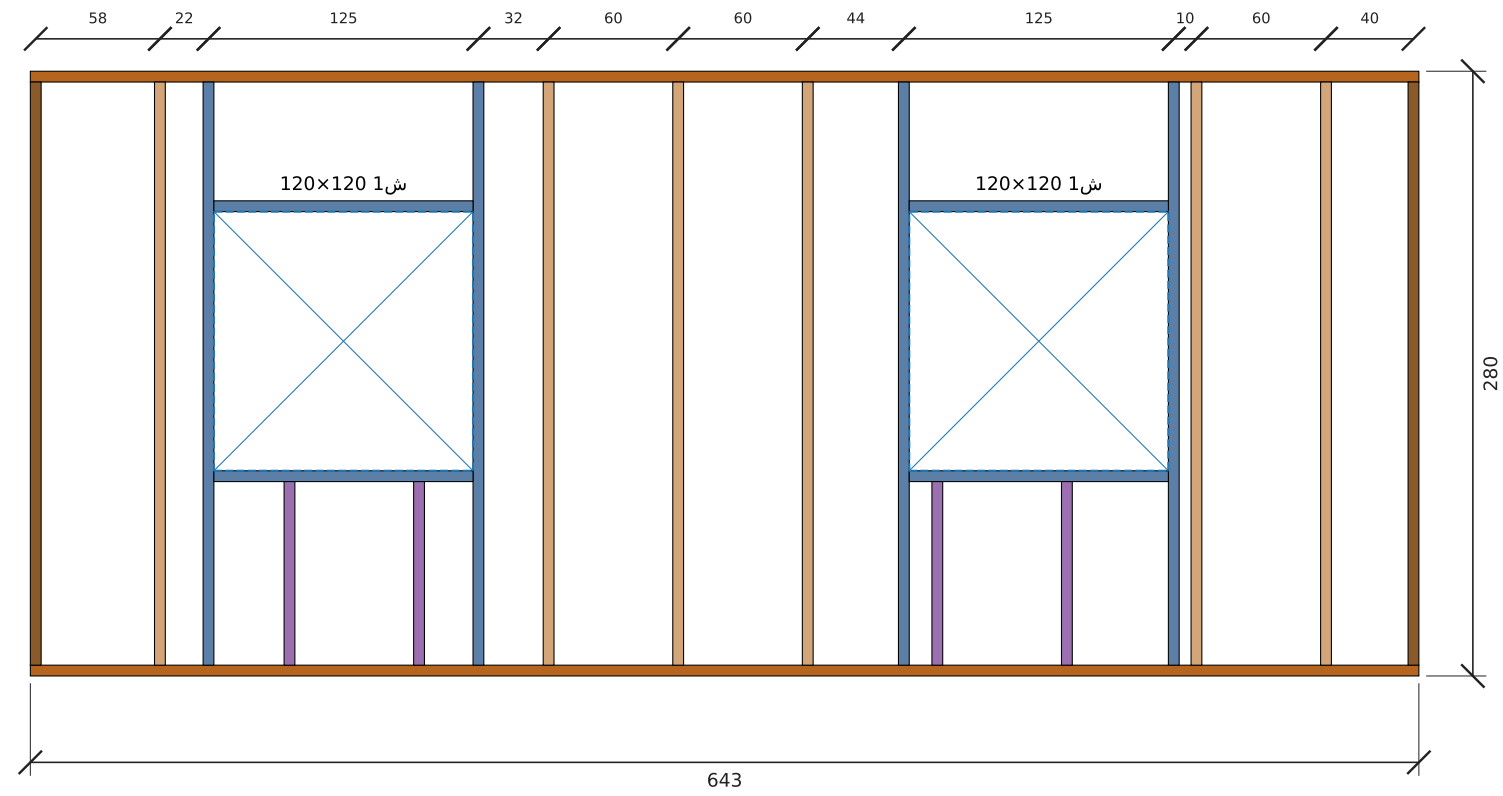


تأطير جدار غرب — الطول 986 سم، الارتفاع 280 سم

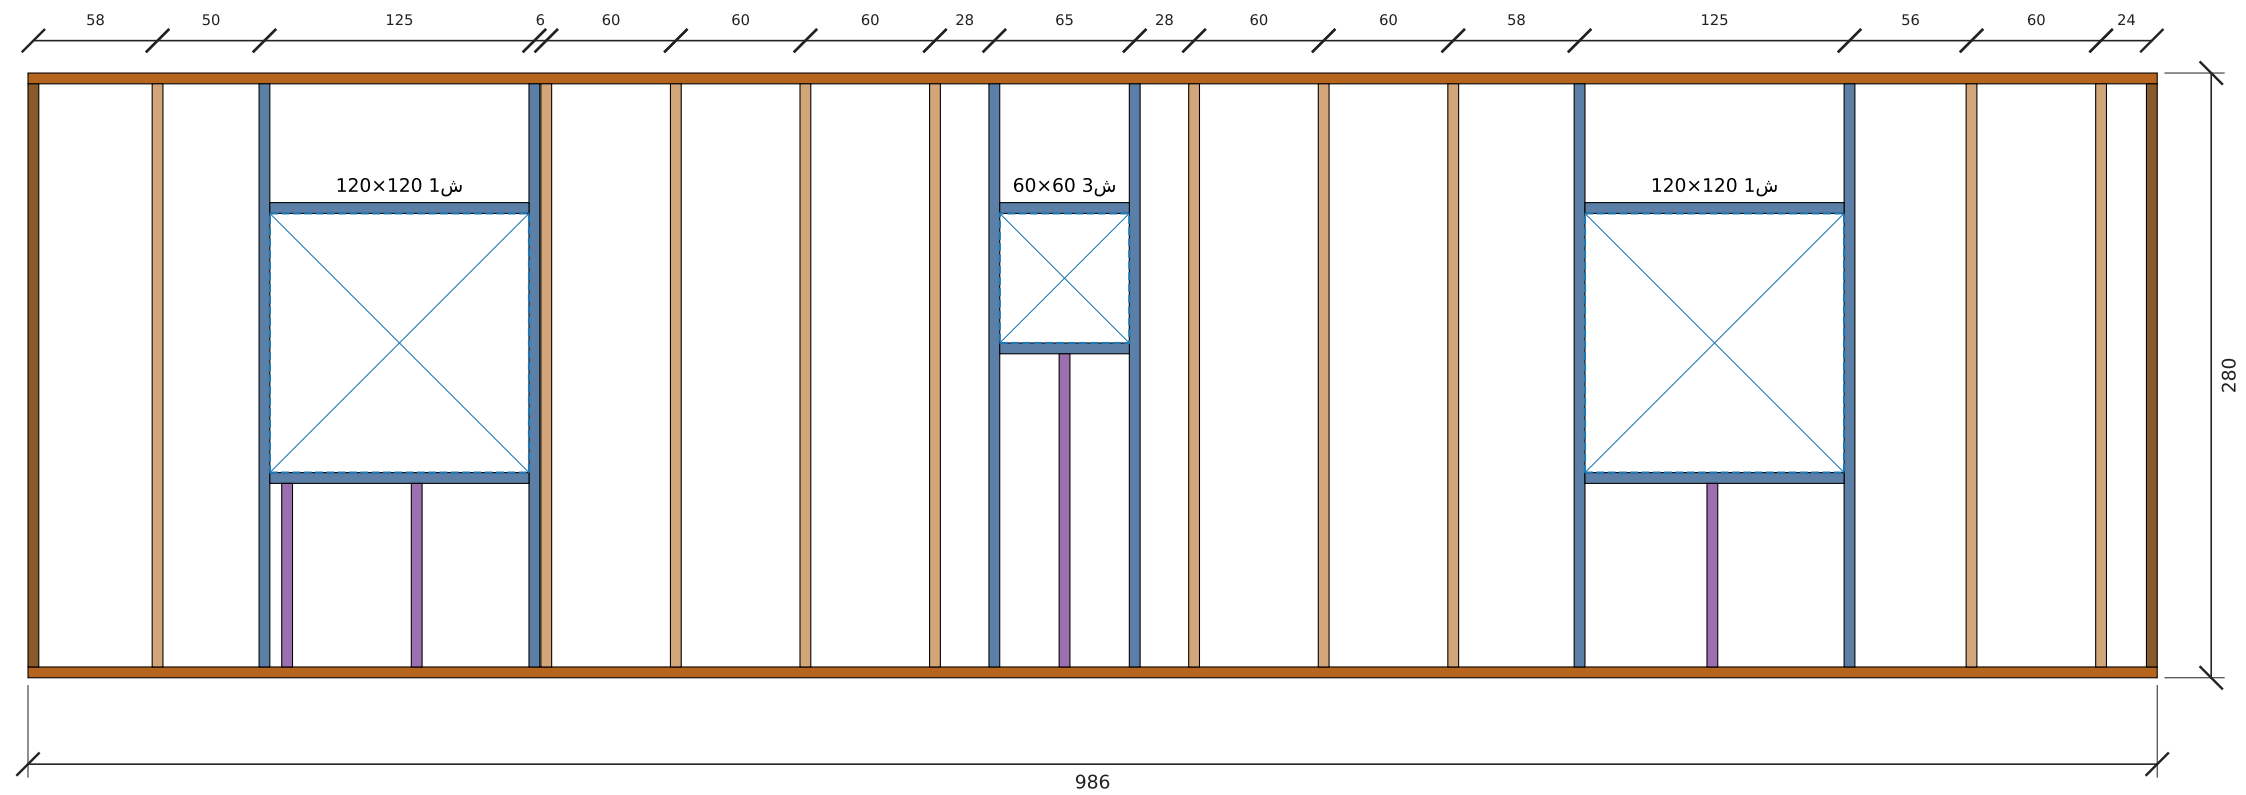


عمود قصير جلسة شباك رأس فتحة جنب فتحة عمود زاوية عمود علوي قاعدة سفلية

تأطير جدار د1-جنوب الحمامات — الطول 303 سم، الارتفاع 280 سم (داخلي)

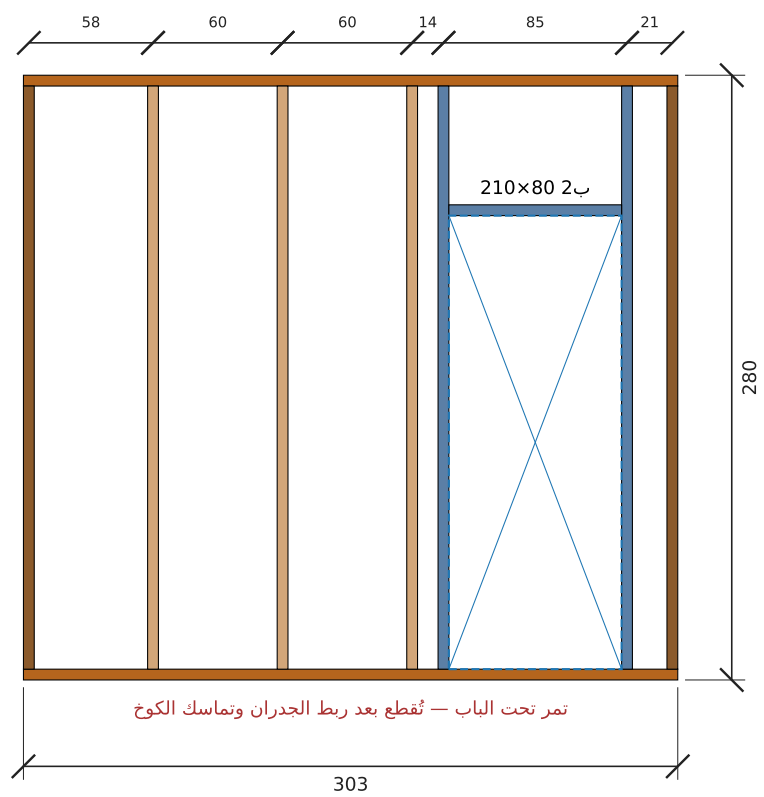


تأطير جدار د2-بين الحمامين — الطول 193 سم، الارتفاع 280 سم (داخلي)

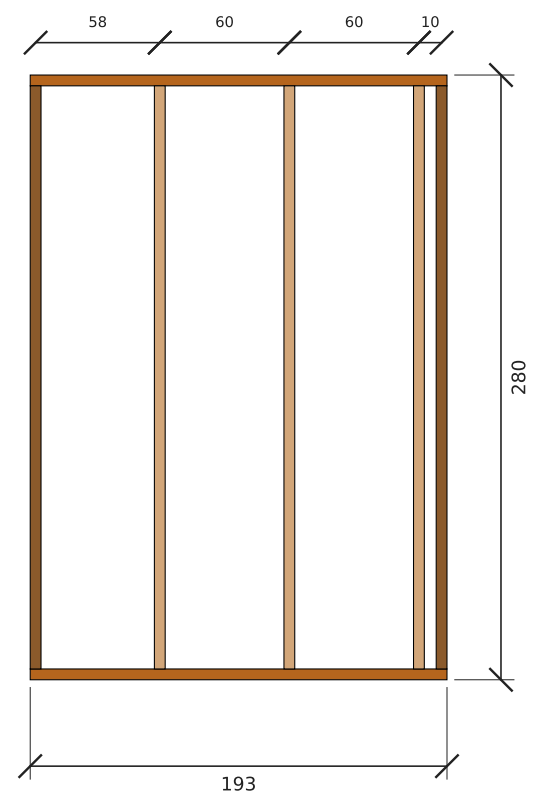


عمود قصير عمود زاوية عمود علوي قاعدة سفلية رأس فتحة جنب فتحة جلسة شباك

تأطير جدار د3-شرق حمام الضيوف — الطول 193 سم، الارتفاع 280 سم (داخلي)

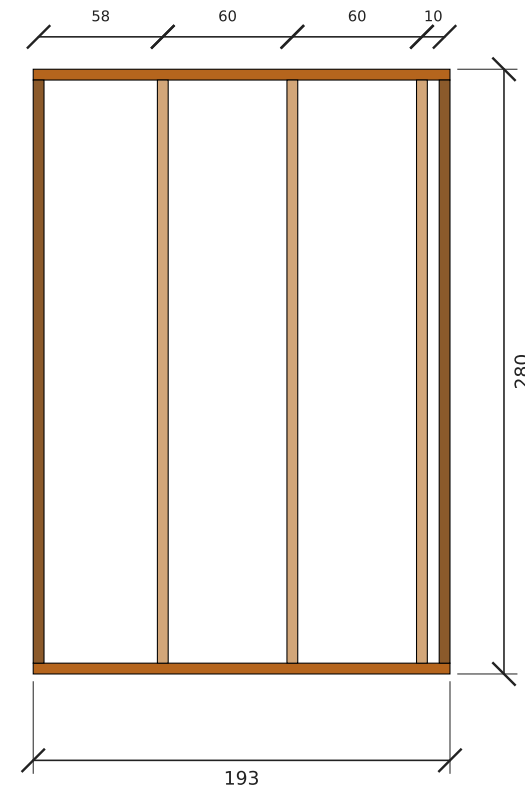


تأطير جدار 4-جنوب الغرف — الطول 643 سم، الارتفاع 280 سم (داخلي)

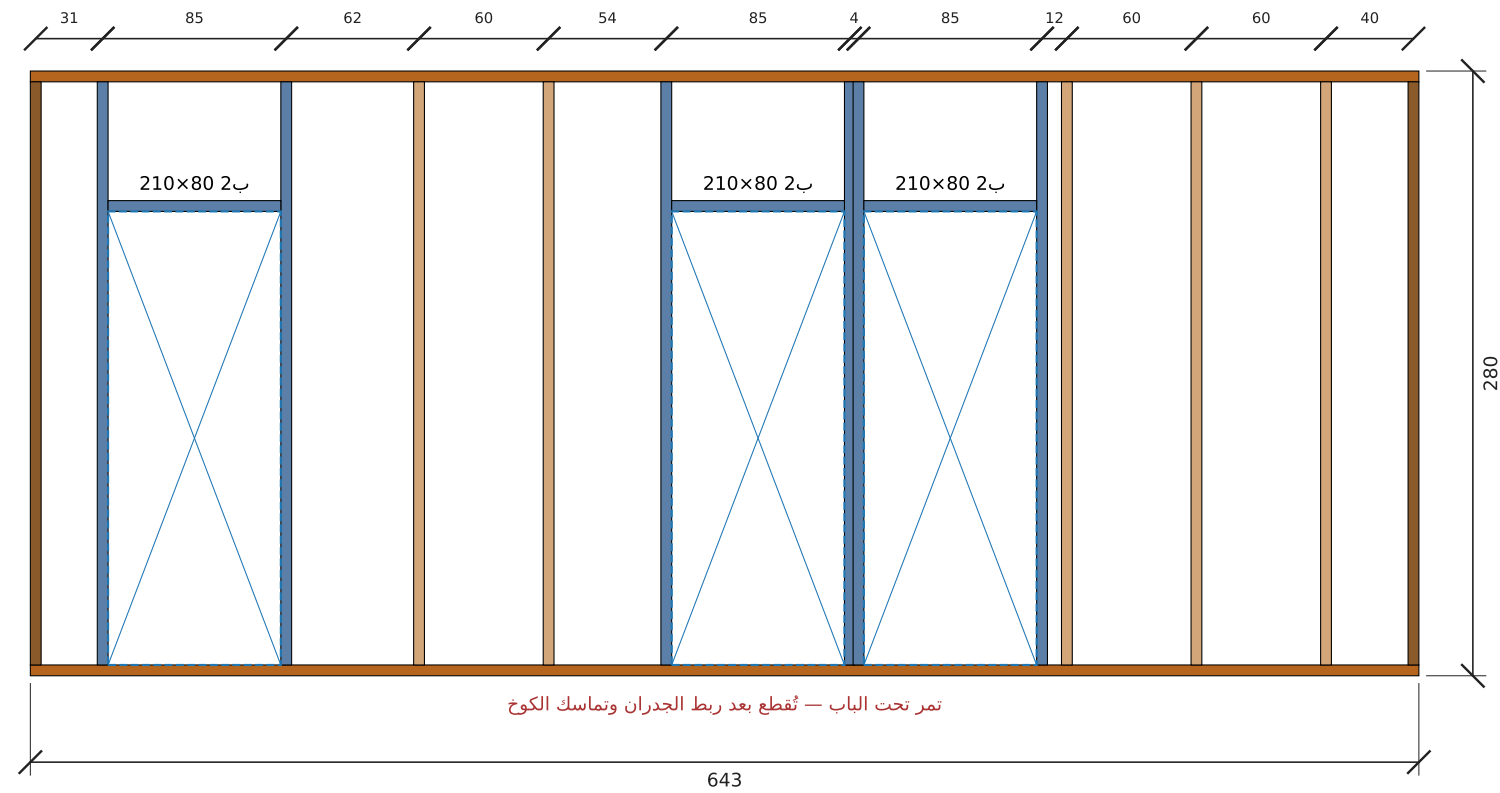

عمود قصير جلسة شباك رأس فتحة جنب فتحة عمود زاوية عمود علوي قاعدة سفلية

تأطير جدار د5-بين الغرفتين — الطول 343 سم، الارتفاع 280 سم (داخلي)

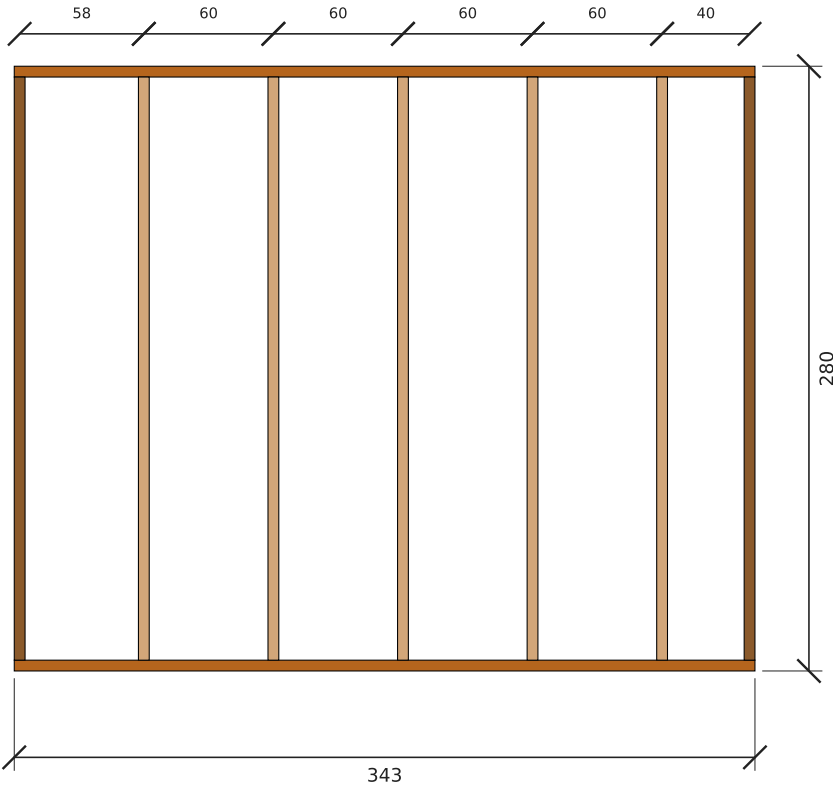

جدول الكميات وخطة تقطيع الطبلیات

البند	القيمة
الارتفاع المطلوب / المعتمد	280 / 280 سم
السقف	جملون 29° — قمة 462 سم من وجه الصبة
المدادات 15×5	38 مداد (19 لكل جهة) × 426 سم — من طبلية 480
طبلیات الطريقة الأولى (مداد + عمود)	38 طبلية × 480 سم
طبلیات الطريقة الثانية (3 أعمدة)	29 طبلية × 320 سم
إجمالي الطبلیات 22.5×5	67
إجمالي قطع 5×7	156
قائمة تقطيع 5×7	986سم 4 × 643سم 6 × 343سم 2 × 303سم 2 × 270سم 96 × 193سم 4 × 145سم 1 × 120سم 17 × 115سم 1 ×
	100سم 2 × 85سم 15 × 80سم 4 × 60سم 2 ×
ألواح تلبیس 2.5 سم	287 لوح × 400 سم (مجموع الصفوف 1052.4 م، 18 وجه)
أسمنت بورد 12 مم (244×122)	32 لوح (داخل دورات المياه)
العزل	بدون (غير مطلوب)
الصبة	یجهزها العميل — 20 سم، مفرغة تحت دورات المياه

مراجعة التصميم مقابل قواعد المصنع

النوع	البند	التفاصيل	المقترح
خطأ	ب2 غرفة النوم في د4-جنوب الغرف	الفتحة تقع على التقاء الجدار د3-شرق حمام الضيوف (عند 303 سم)، د5-بين الغرفتين (عند 380 سم) — الباب يصطدم بالجدار ولا يوجد مكان لجنب الإطار 5×7.	تُبعد حافة الفتحة 11 سم على الأقل عن محور الجدار الملتقي، أو يُعاد توزيع الجدران الداخلية.
خطأ	ب2 غرفة الأولاد في د4-جنوب الغرف	الفتحة تقع على التقاء الجدار د5-بين الغرفتين (عند 380 سم) — الباب يصطدم بالجدار ولا يوجد مكان لجنب الإطار 7×5.	تُبعد حافة الفتحة 11 سم على الأقل عن محور الجدار الملتقي، أو يُعاد توزيع الجدران الداخلية.
خطأ	ب2 غرفة النوم و ب2 غرفة الأولاد	فتحتين متلاصقتين في د4-جنوب الغرف — المسافة بينهما أقل من إطارين 5×7 (10 سم).	
تنبيه	عرض ممر	العرض الصافي 68 سم أقل من 90 سم (ضيق للحركة ولفتح باب 80 سم).	يُوسَّع الممر إلى 90 سم على الأقل.
خطأ	حمام ضيوف بدون جدار خارجي	السياكة في المصنع تمشي من الخارج والصبة مفرغة تحت دورات المياه — هذا الحمام محصور داخل المبنى.	يُنقل الحمام ليلمس جدار خارجي، أو يُعتمد مسار سياكة تحت الصبة بقرار من المصنع.
تنبيه	تهوية حمام ضيوف	لا يوجد شباك — يحتاج شفاط هواء.	إضافة شفاط أو شباك صغير.
ملاحظة	بحر المدادات	أطول بحر بدون جدار داخلي يحمل المداد: جهة أ: 328 سم، جهة ب: 328 سم. يحتاج رقم المصنع لأقصى بحر مسموح لتحديد المدادات اللي تُقوَّى 5×20.	
سؤال	يحتاج تأكيد	أقصى بحر للمداد بدون جدار داخلي قبل إضافة تقوية 5×7 (مداد 5×20)؟	
سؤال	يحتاج تأكيد	التغطية الصافية للوح التليس بعد التعشيق (مستنتجة مؤقتاً 18.67 سم من 280/15)؟	
سؤال	يحتاج تأكيد	هل يوضع أعمدة قصيرة فوق رأس الشباك/الباب إلى العلوي؟	
سؤال	يحتاج تأكيد	مكان الوصلة في القاعدة والعلوي إذا الجدار أطول من الطيلية؟	