




المسقط الأفقي مع الفرش
الأبعاد بالسنتيمتر - الجدران: قوائم 5×7 + تليس 2.5 من الجهتين (12 سم)

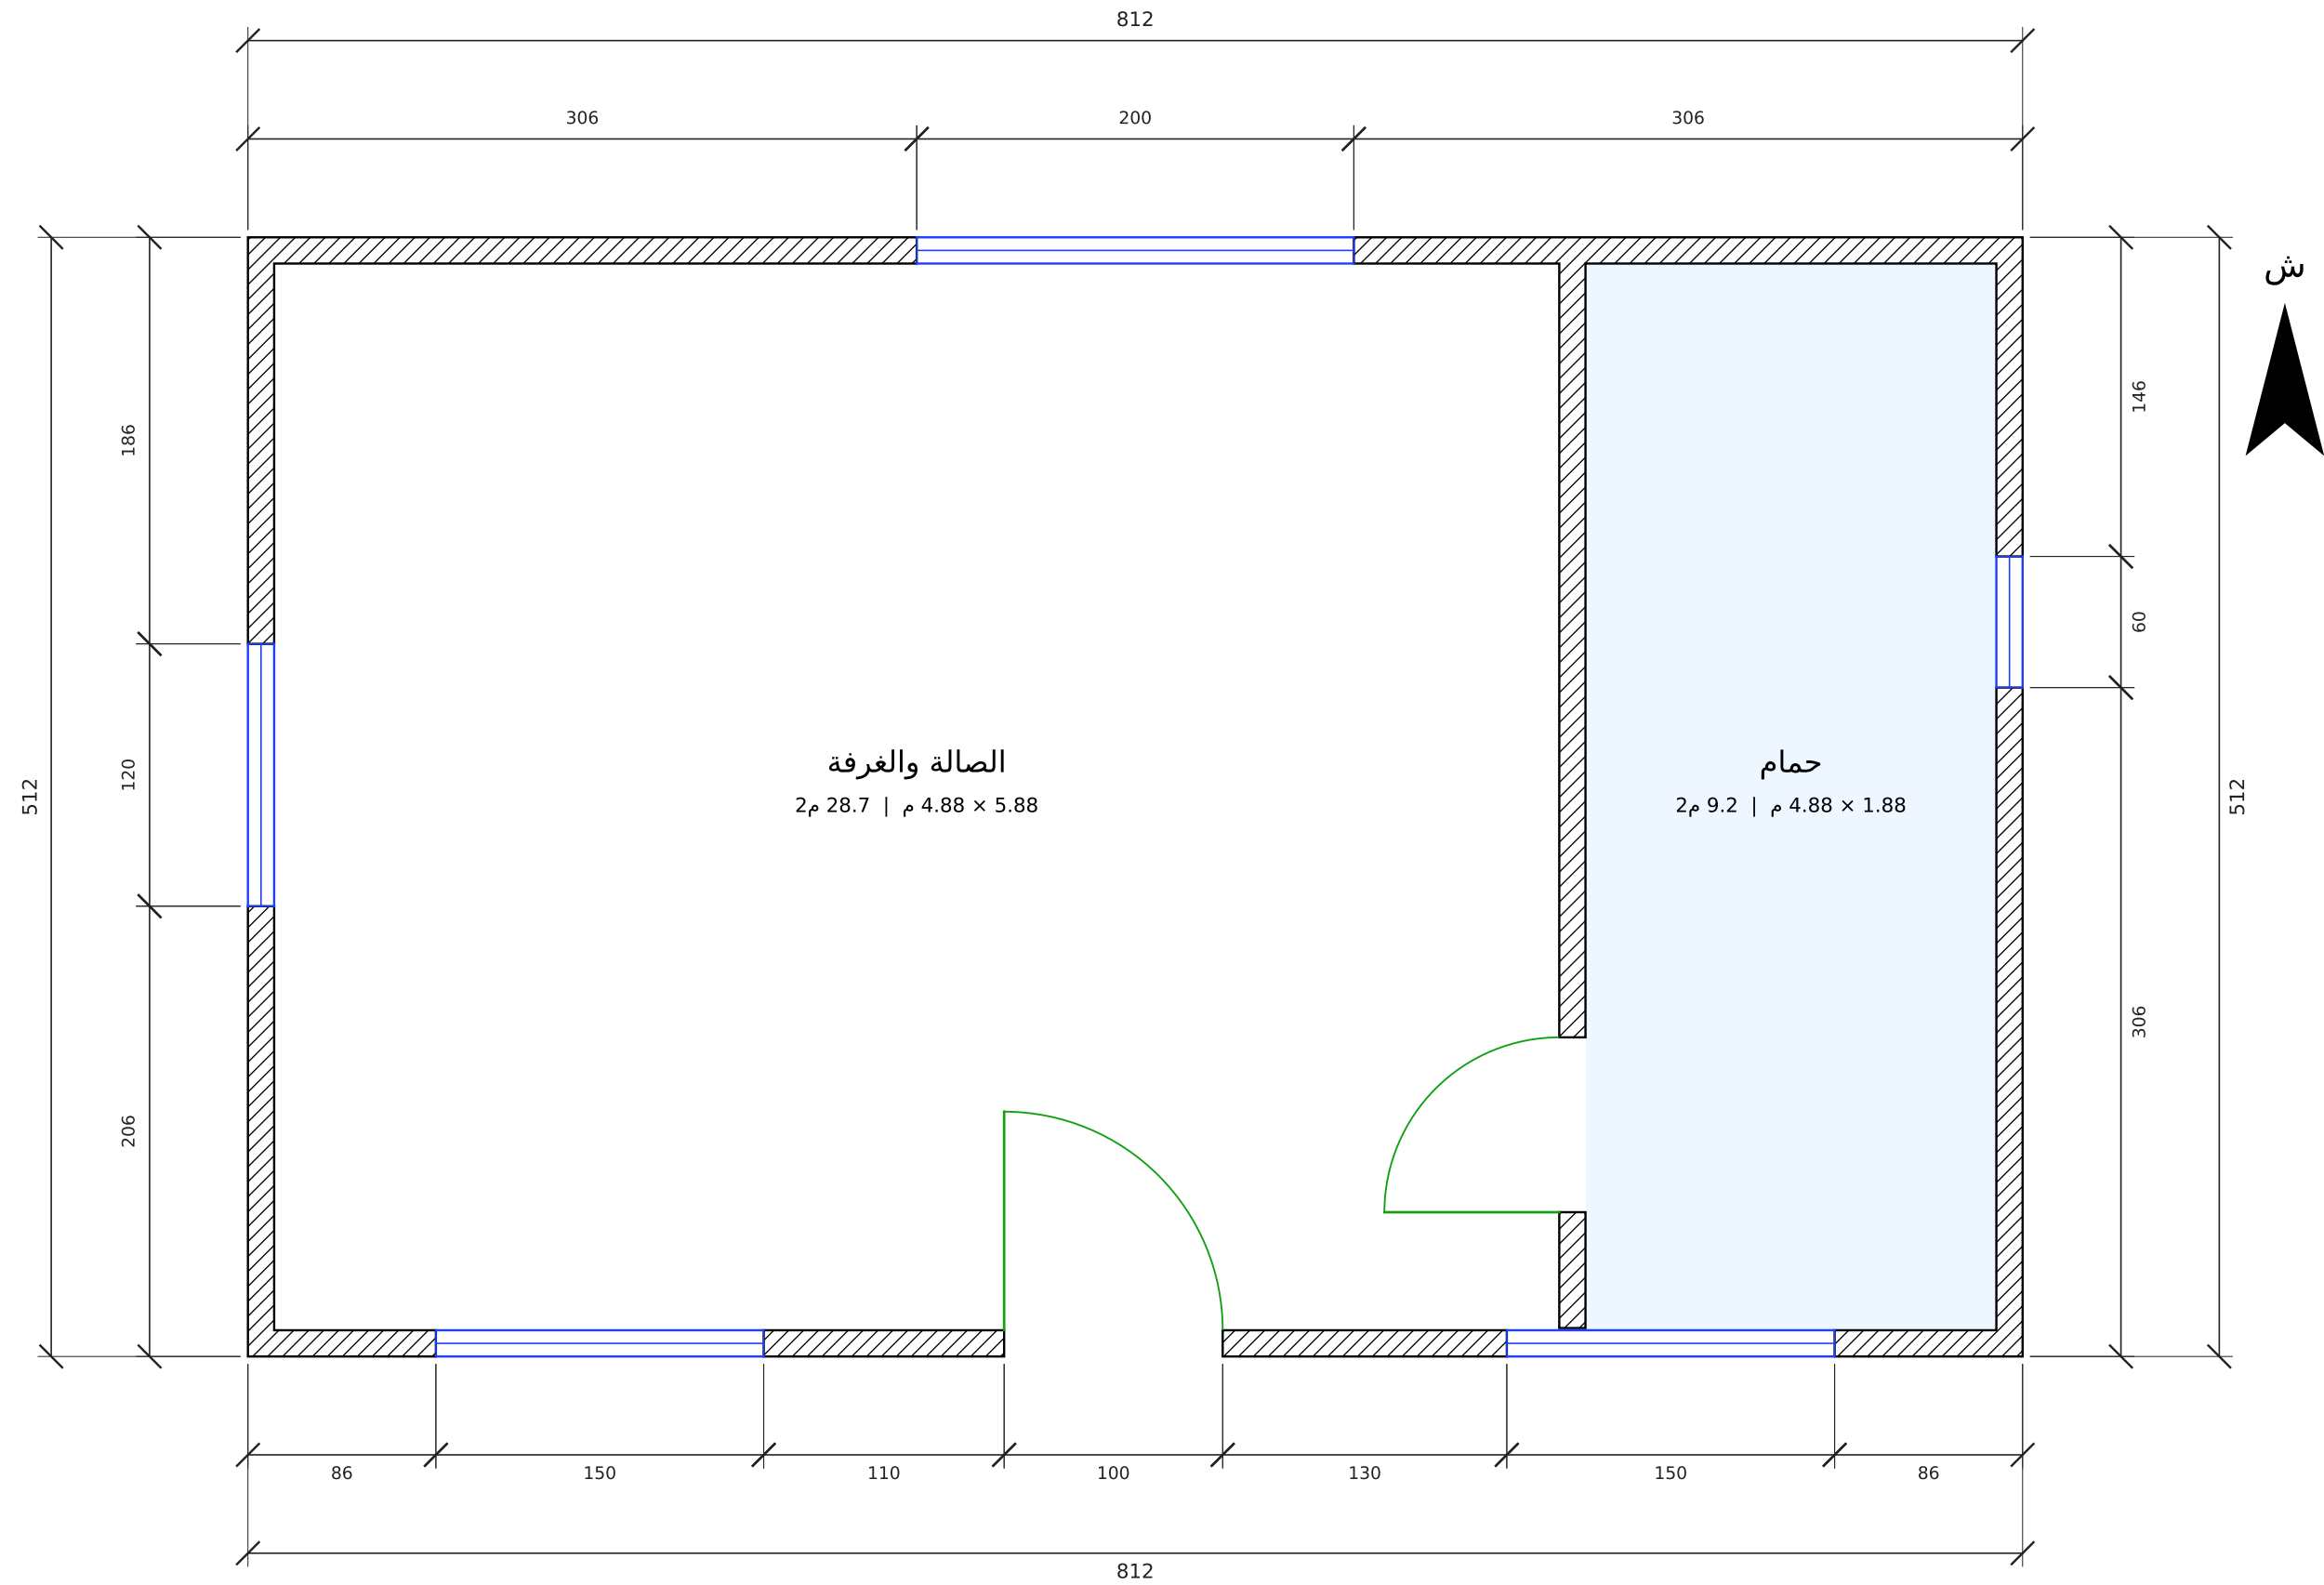

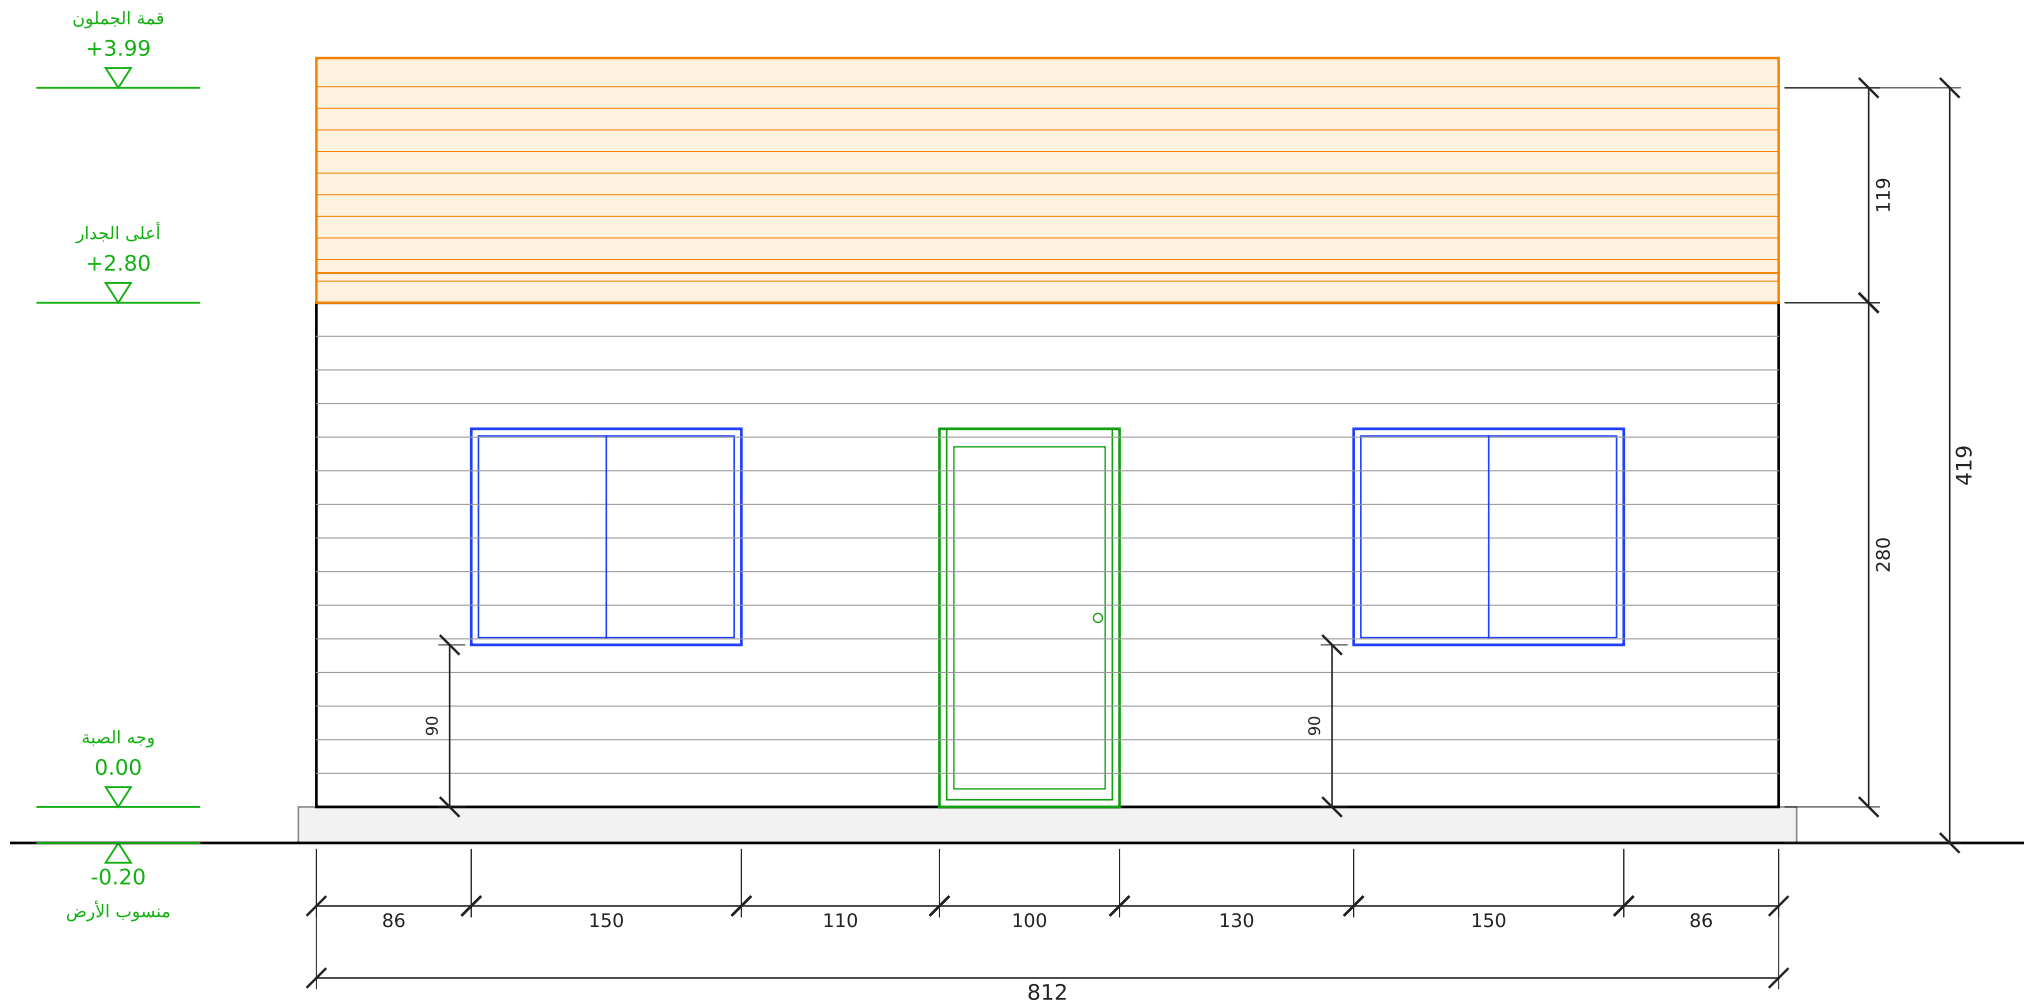


جنوب-W1

مقياس 1:50 | الوحدة: سم

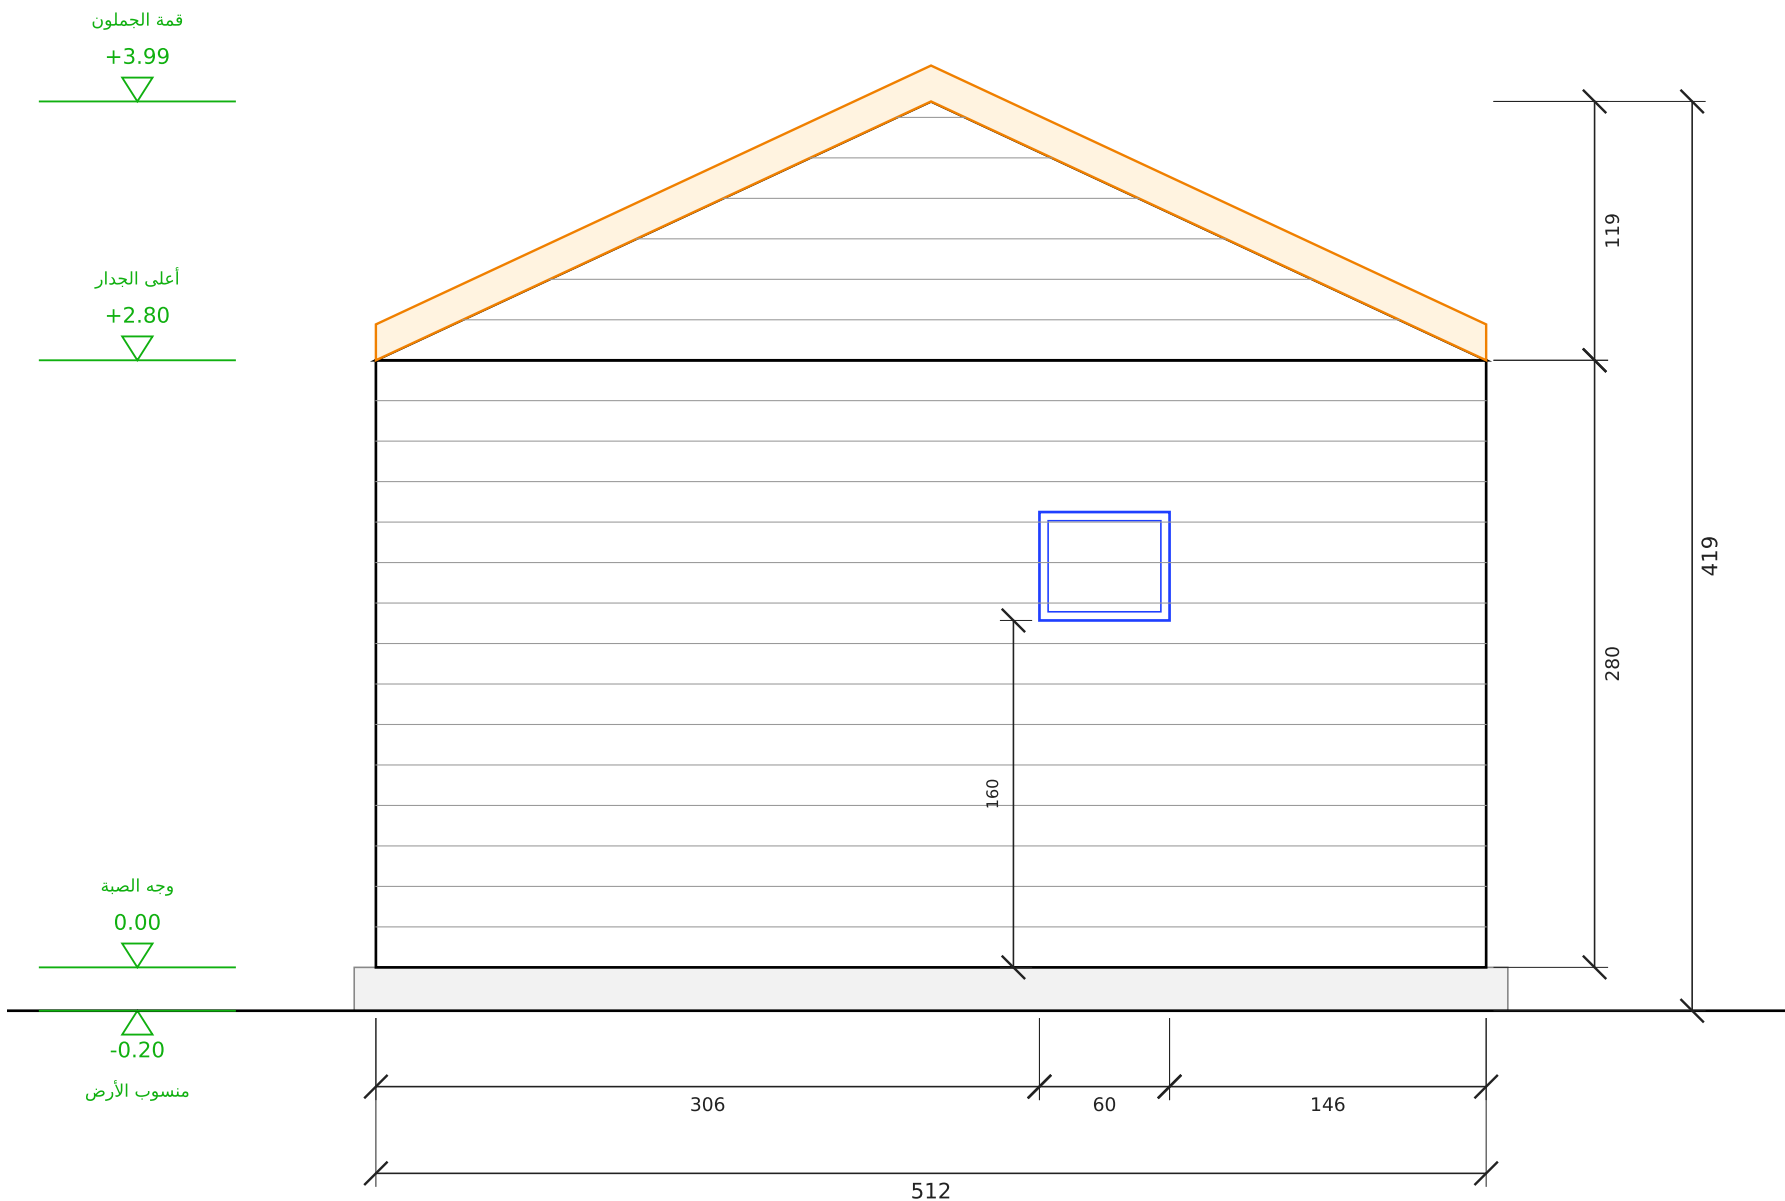


شرق-W2

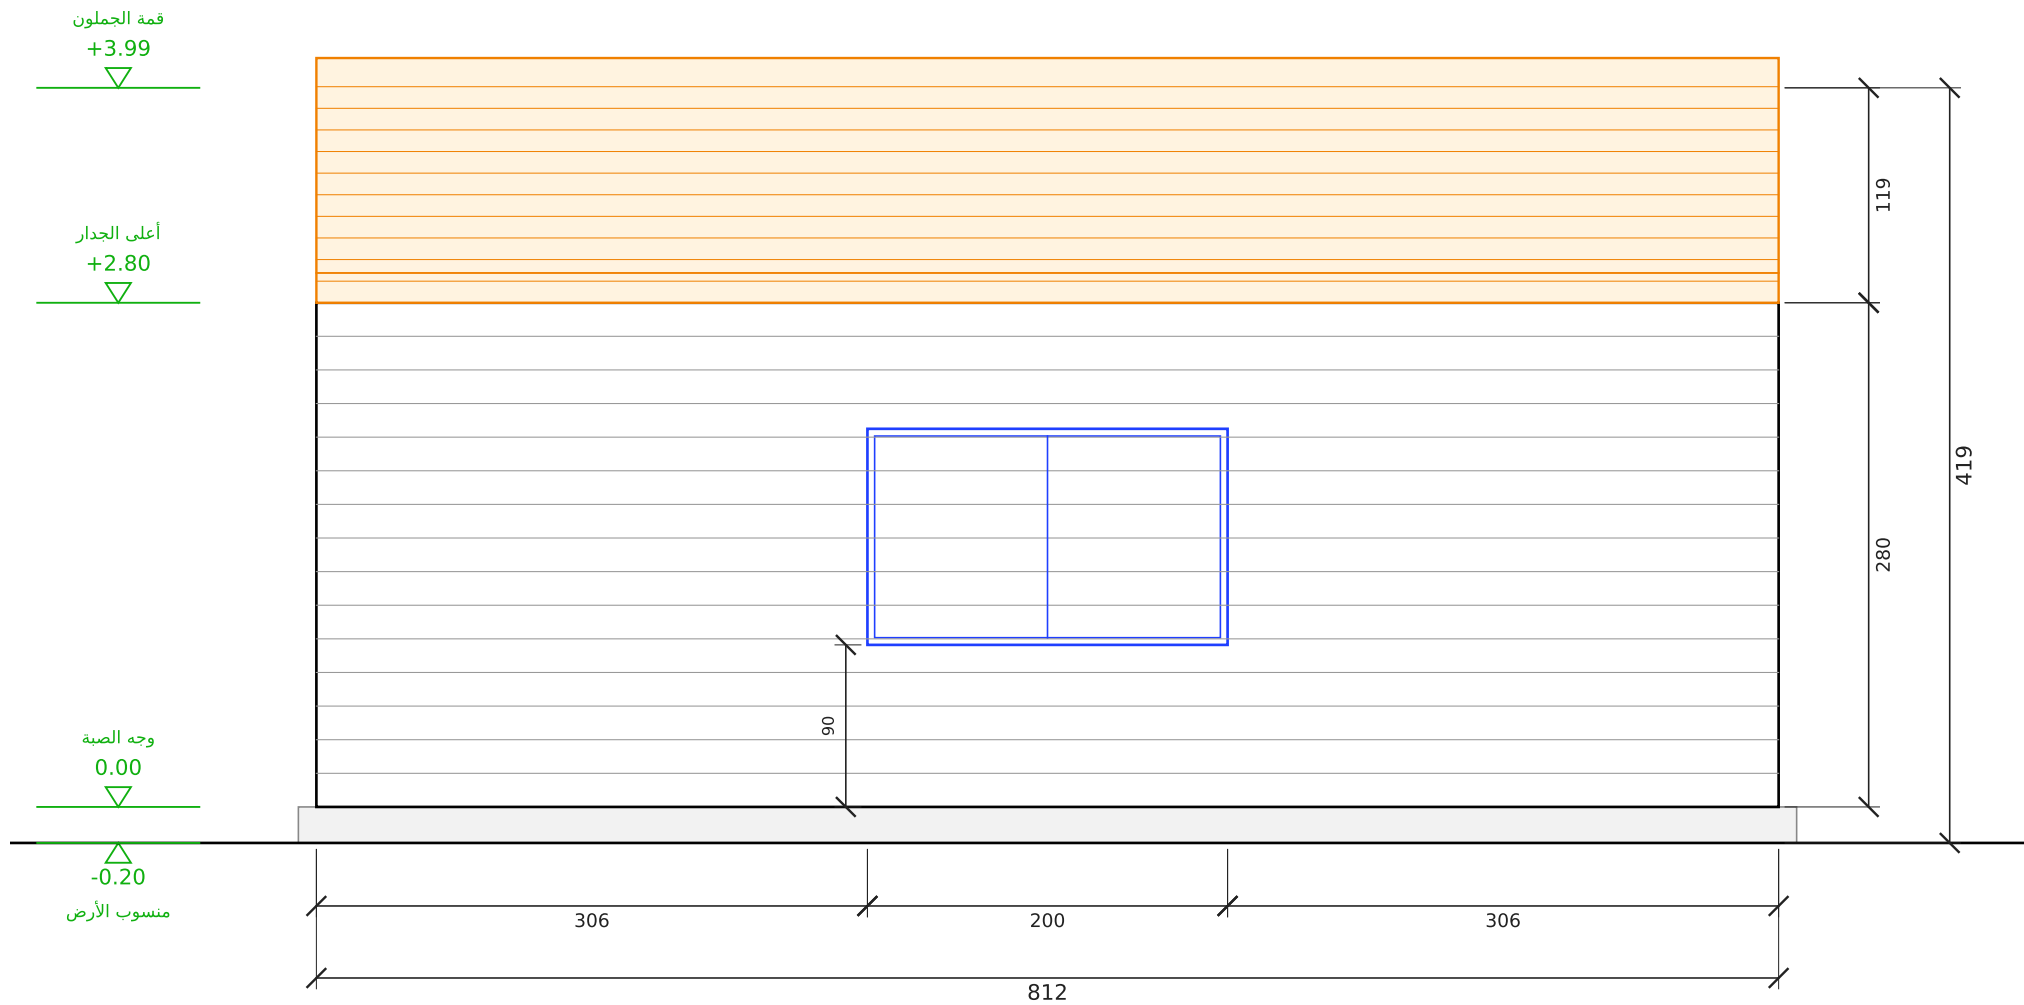


شمال-W3

مقياس 1:50 | الوحدة: سم

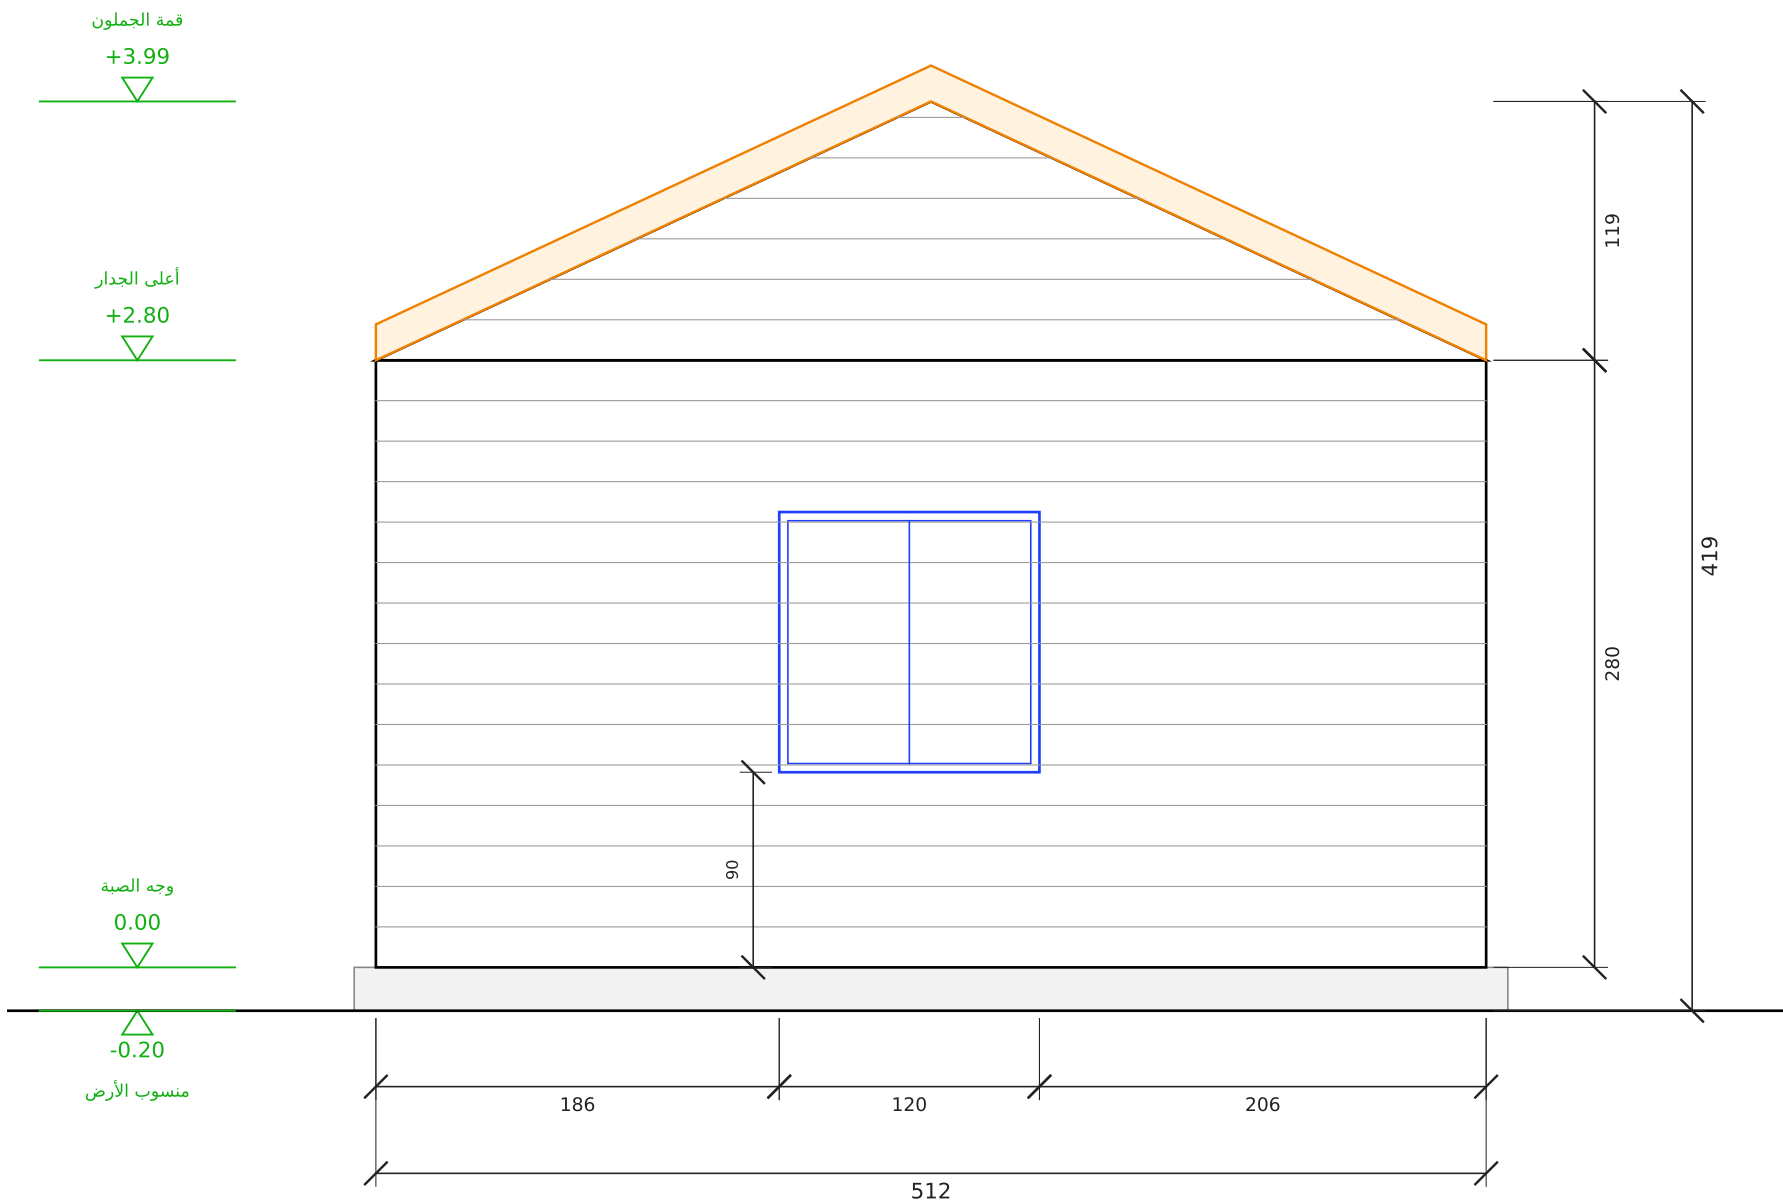


غرب-W4


مسقط السقف (جملون)
رفف 0 سم من كل جهة | مقياس 1:50

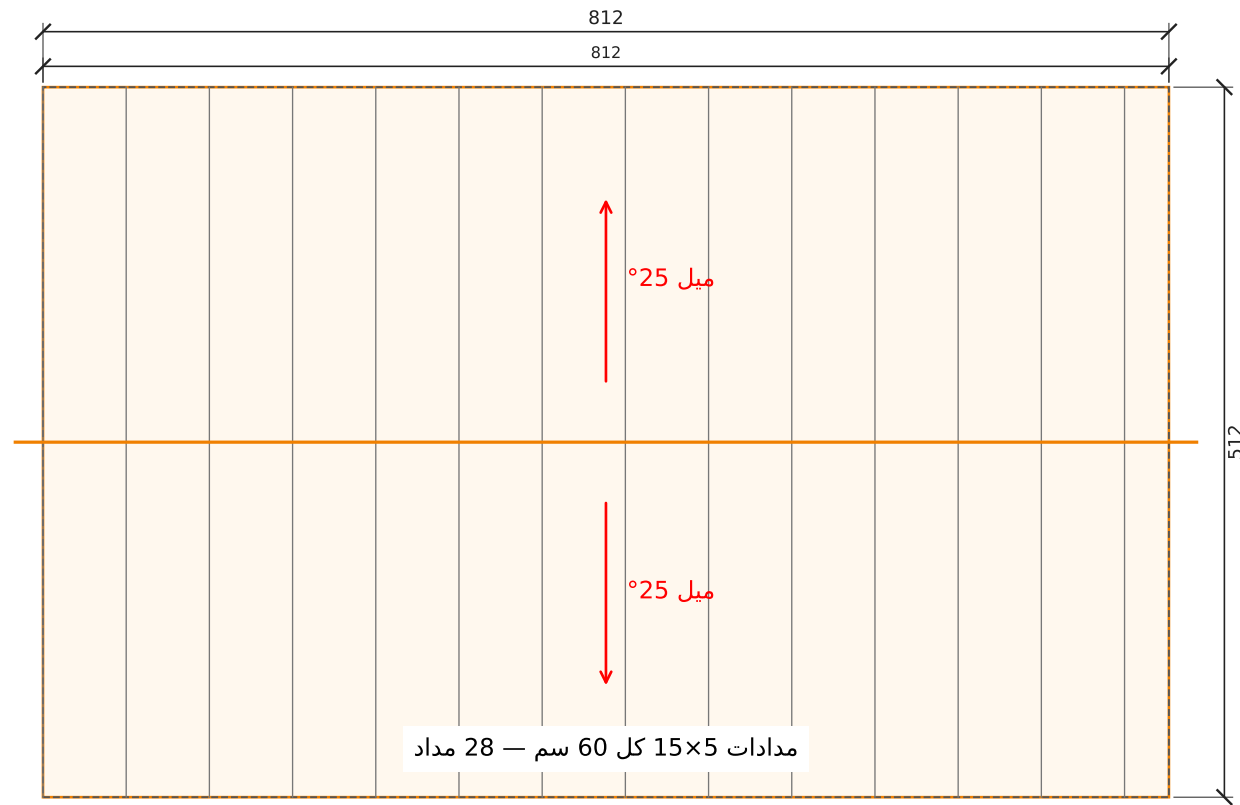

قطاع عرضي أ-أ
مقياس 1:50 | الوحدة: سم

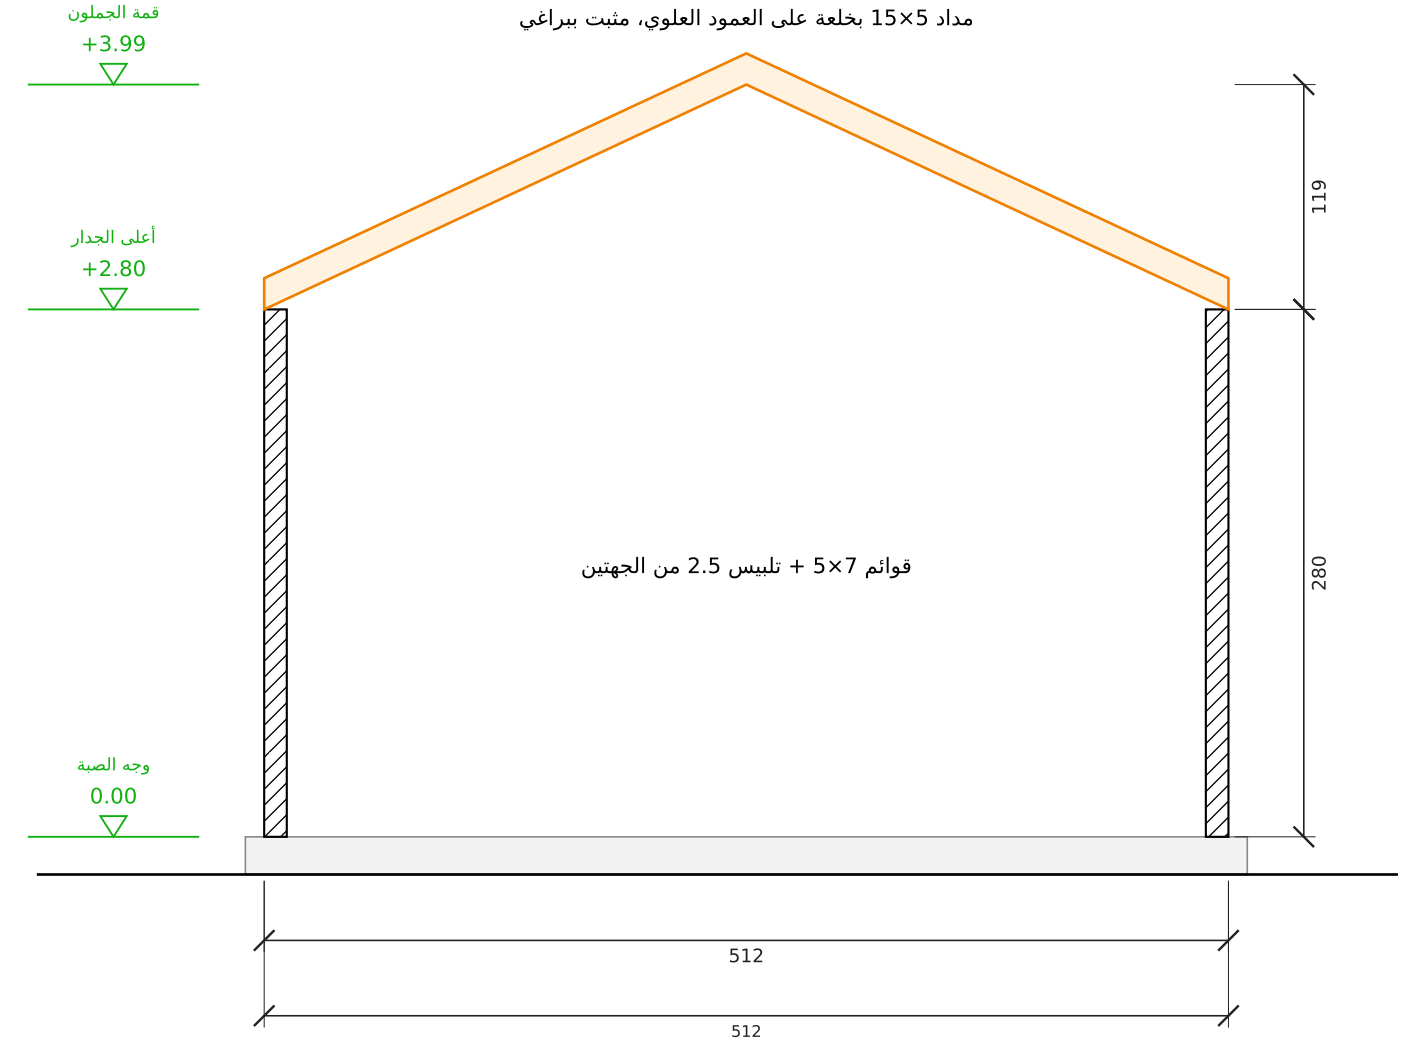

تفصيلة جلوس المدا على العلوي (1:5)

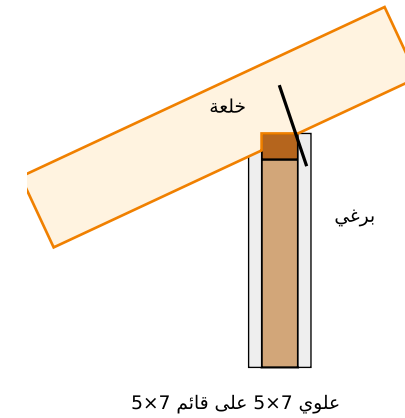

جدول مقاسات الأبواب والشبابيك
مقاس الفتحة الصافي في الجدار - الوحدة: سم

الرمز	النوع	العرض (سم)	الارتفاع (سم)	ارتفاع الجلسة (سم)	العدد	الموقع
	باب	100	210	-	1	جنوب-W1
	باب	80	210	-	1	باب حمام
	شباك	150	120	90	2	جنوب W1-2
	شباك	60	50	160	1	شرق-W2
	شباك	200	120	90	1	شمال-W3
	شباك	120	120	90	1	غرب-W4

الإجمالي: أبواب 2 - شبابيك 5


مصنع وتد الأخشاب
Watad Wood Factory

البند	القيمة
المشروع	sample-cabin
العميل	مثال تجريبي
الموقع	
الاستخدام	
المدير	
التاريخ	
المقياس	1:50
الوحدة	سم


جدول المساحات

م	الفراغ	الأبعاد الداخلية (م)	المساحة (م2)
1	الصالة والغرفة	5.88 × 4.88	28.69
2	حمام	1.88 × 4.88	9.17
	المساحة الصافية الداخلية		37.87
	المساحة الإجمالية الخارجية	8.12 × 5.12	41.57

تأطير جدار W1-جنوب — الطول 800 سم، الارتفاع 280 سم

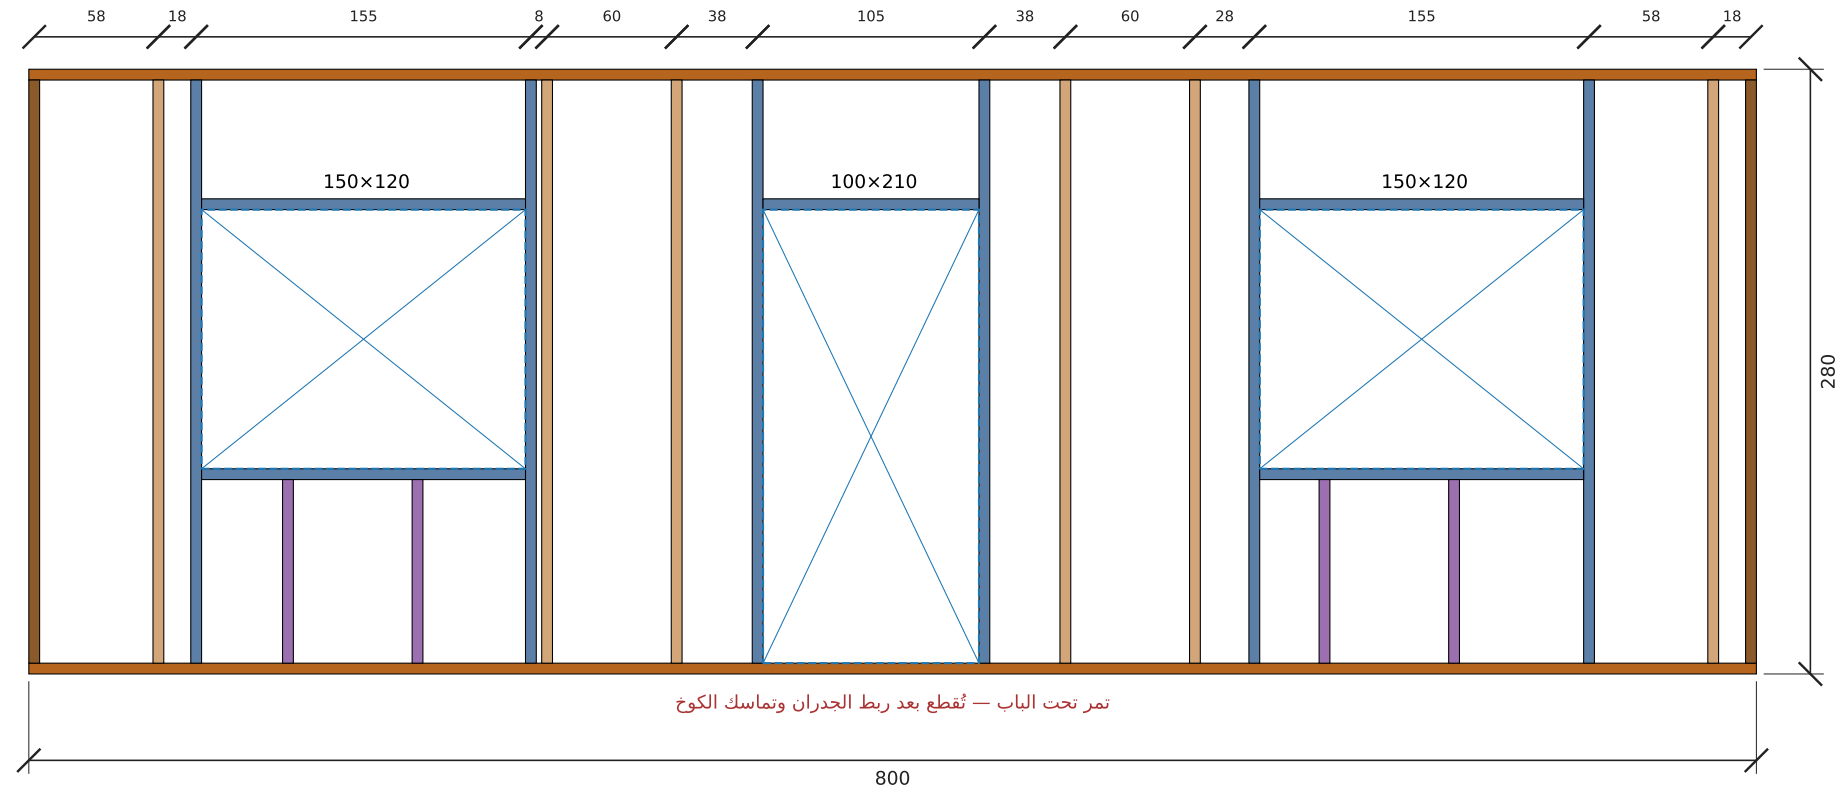


تأطير جدار W2-شرق — الطول 500 سم، الارتفاع 280 سم

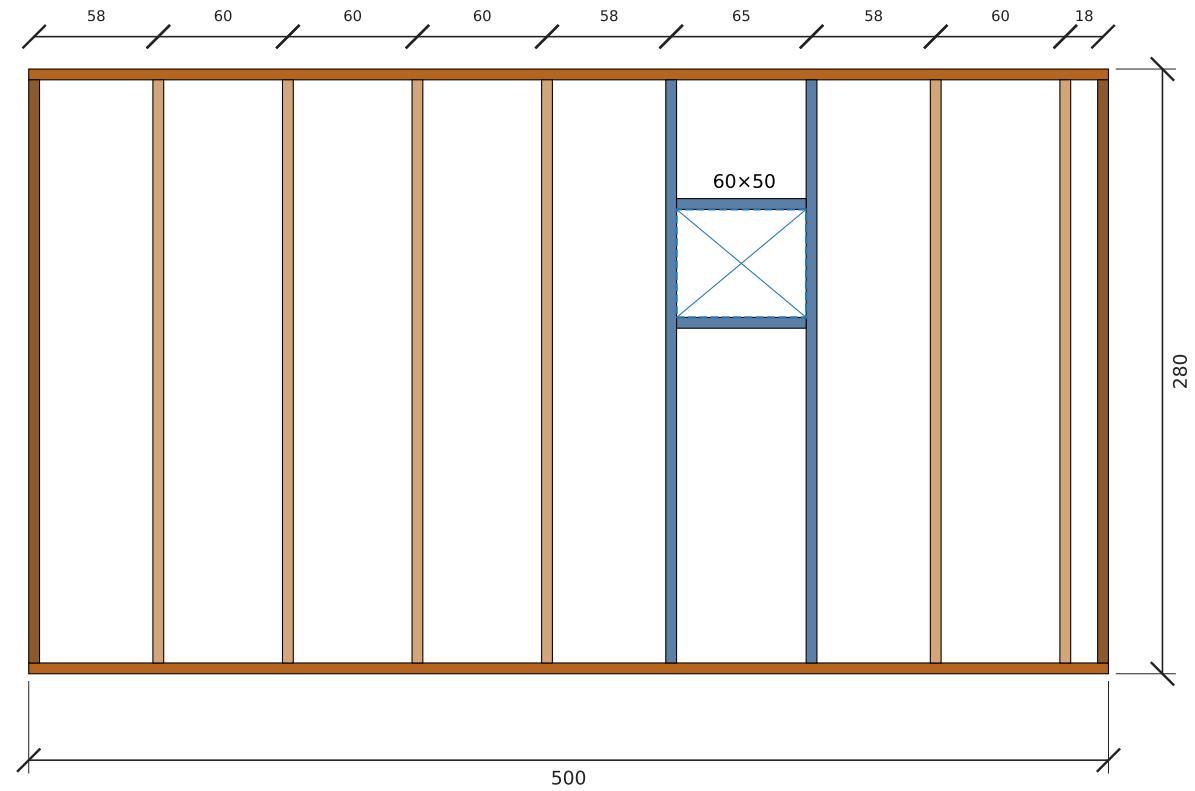


قاعدة سفلية علوي عمود عمود زاوية جنب فتحة رأس فتحة جلسة شباك عمود قصير

تأطير جدار W3-شمال — الطول 800 سم، الارتفاع 280 سم

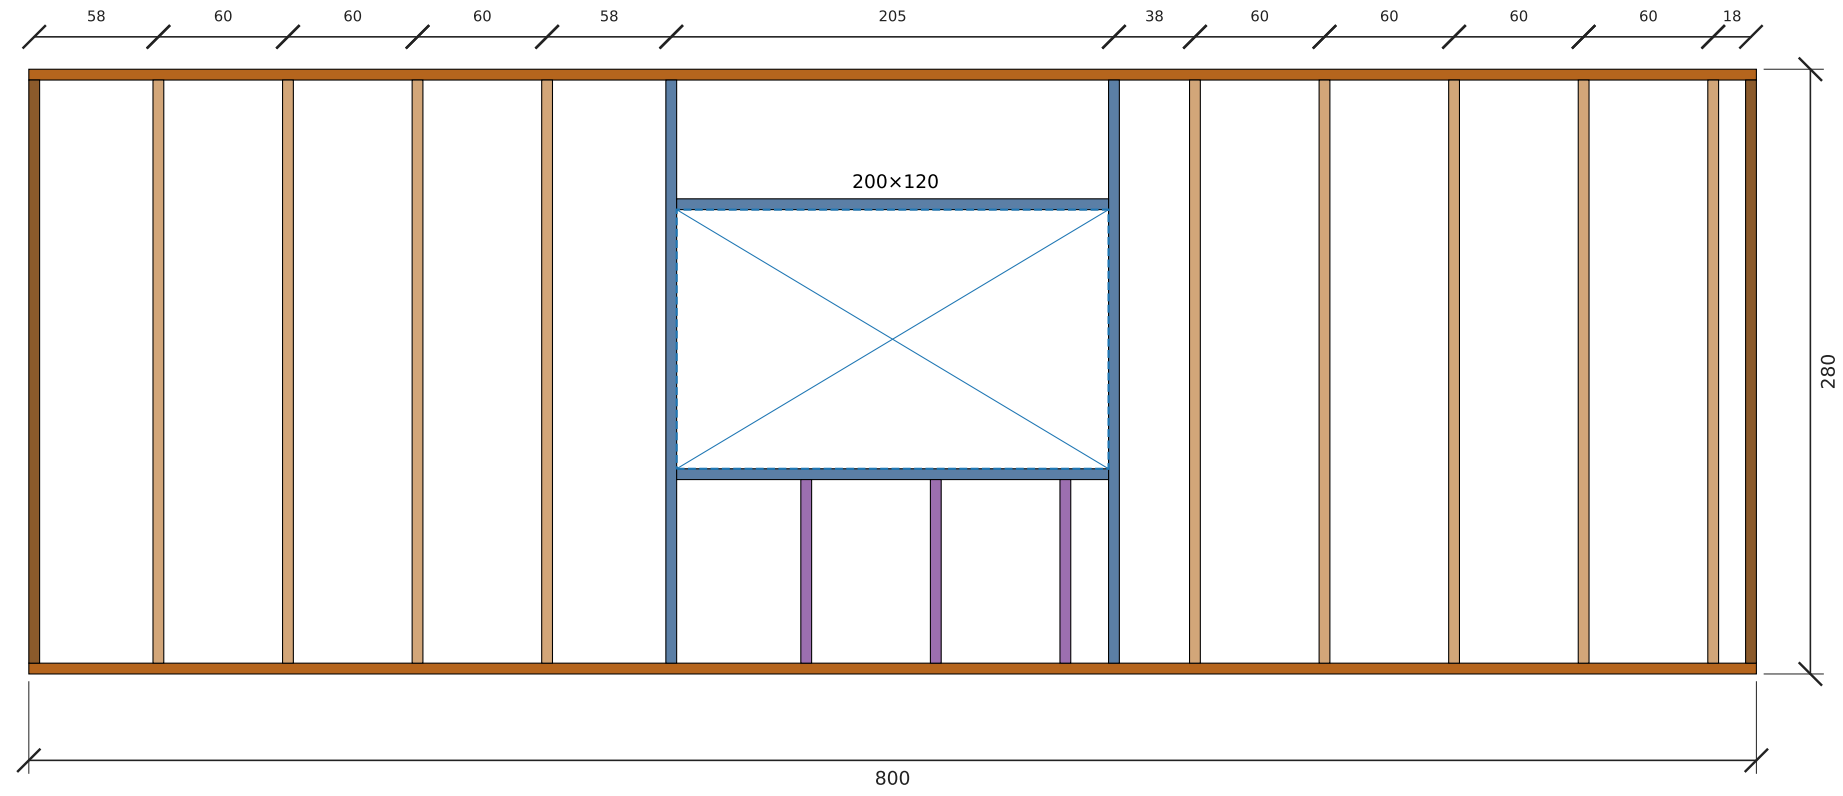


تأطير جدار W4-غرب — الطول 500 سم، الارتفاع 280 سم

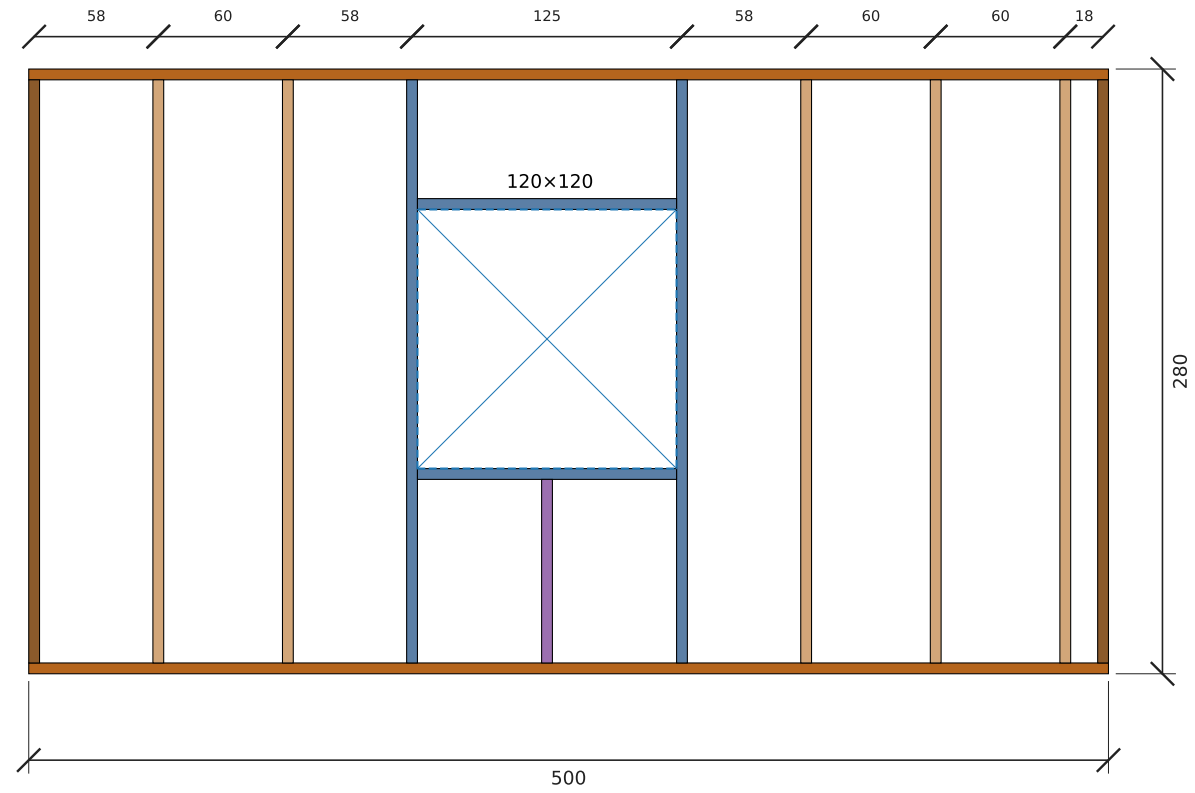

■ قاعدة سفلية
 ■ علوي
 ■ عمود
 ■ عمود زاوية
 ■ جنب فتحة
 ■ رأس فتحة
 ■ جلسة شباك
 ■ عمود قصير

تأطير جدار W5-داخلي — الطول 500 سم، الارتفاع 280 سم (داخلي)

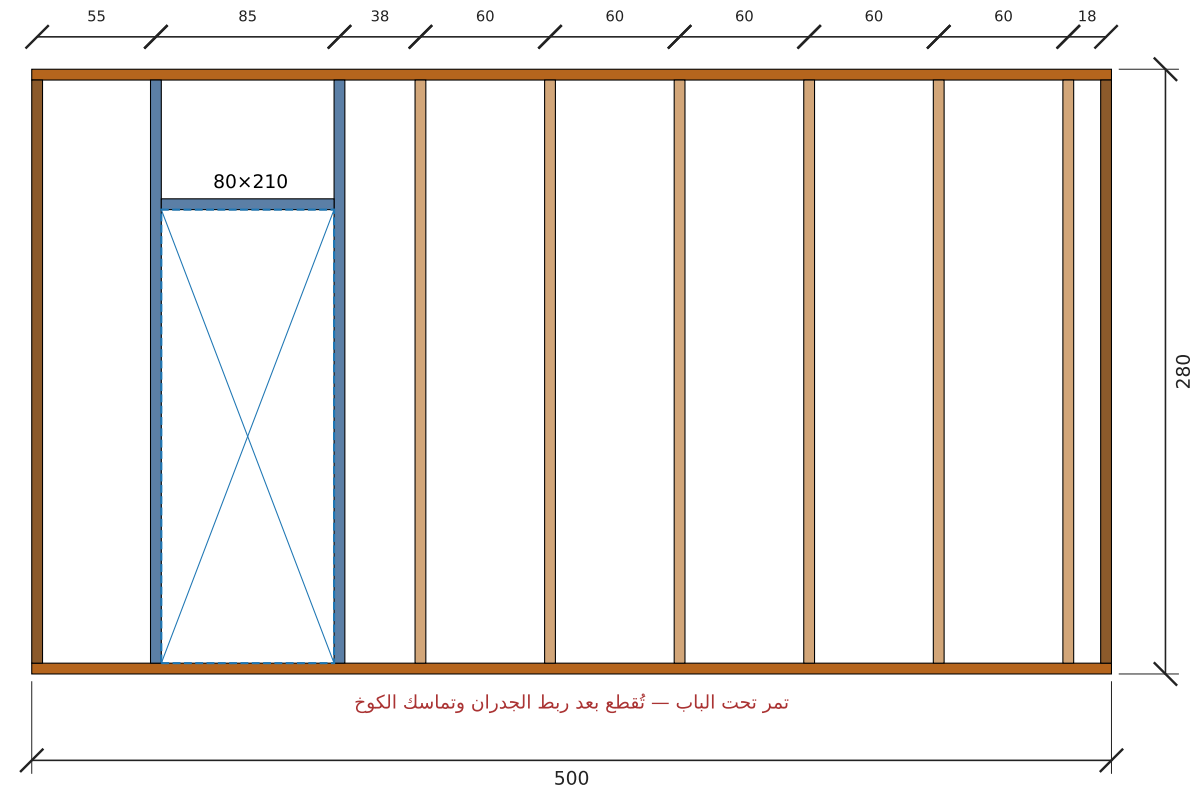

عمود قصير عمود زاوية عمود علوي قاعدة سفلية جنب فتحة رأس فتحة جلسة شباك رأس فتحة جنب فتحة

جدول الكميات وخطة تقطيع الطبلیات

البند	القيمة
الارتفاع المطلوب / المعتمد	280 / 280 سم
السقف	جملون 25° — قمة 399 سم من وجه الصبة
المدادات 15×5	28 مداد (14 لكل جهة) × 282 سم — من طبلية 320
طبلیات الطريقة الأولى (مداد + عمود)	28 طبلية × 320 سم
طبلیات الطريقة الثانية (3 أعمدة)	20 طبلية × 320 سم
إجمالي الطبلیات 22.5×5	48
إجمالي قطع 5×7	86
قائمة تقطيع 5×7	800سم×4 500سم×6 270سم×56 200سم×2 150سم×4 120سم×2 100سم×1 85سم×8 80سم×1
	60سم×2
ألواح تلبیس 2.5 سم	173 لوح × 400 سم (مجموع الصفوف 612.4 م، 10 وجه)
أسمنت بورد 12 مم (244×122)	24 لوح (داخل دورات المياه)
العزل	بدون (غير مطلوب)
الصبة	یجهزها العميل — 20 سم، مفرغة تحت دورات المياه

مراجعة التصميم مقابل قواعد المصنع

النوع	البند	التفاصيل	المقترح
خطأ	ش2 في W1-جنوب	الفتحة تقع على التقاء الجدار W5-داخلي (عند 600 سم) — الباب يصطدم بالجدار ولا يوجد مكان لجنب الإطار 5×7.	تُبعد حافة الفتحة 11 سم على الأقل عن محور الجدار الملتقي، أو يُعاد توزيع الجدران الداخلية.
ملاحظة	بحر المدادات	أطول بحر بدون جدار داخلي يحمل المداد: جهة أ: 256 سم، جهة ب: 256 سم. يحتاج رقم المصنع لأقصى بحر مسموح لتحديد المدادات اللي تُقوّى 5×20.	
سؤال	يحتاج تأكيد	أقصى بحر للمداد بدون جدار داخلي قبل إضافة تقوية 5×7 (مداد 5×20)؟	
سؤال	يحتاج تأكيد	التغطية الصافية للوح التليس بعد التعشيق (مستنتجة مؤقتاً 18.67 سم من 280/15)؟	
سؤال	يحتاج تأكيد	هل يوضع أعمدة قصيرة فوق رأس الشباك/الباب إلى العلوي؟	
سؤال	يحتاج تأكيد	مكان الوصلة في القاعدة والعلوي إذا الجدار أطول من الطيلية؟	