
المسقط الأفقي مع الفرش — الدور الأرضي


الأبعاد بالسنتيمتر - الجدران: قوائم 7×5 + تلبيس 2.5 من الجهتين (12 سم) | منسوب الأرضية +0.00

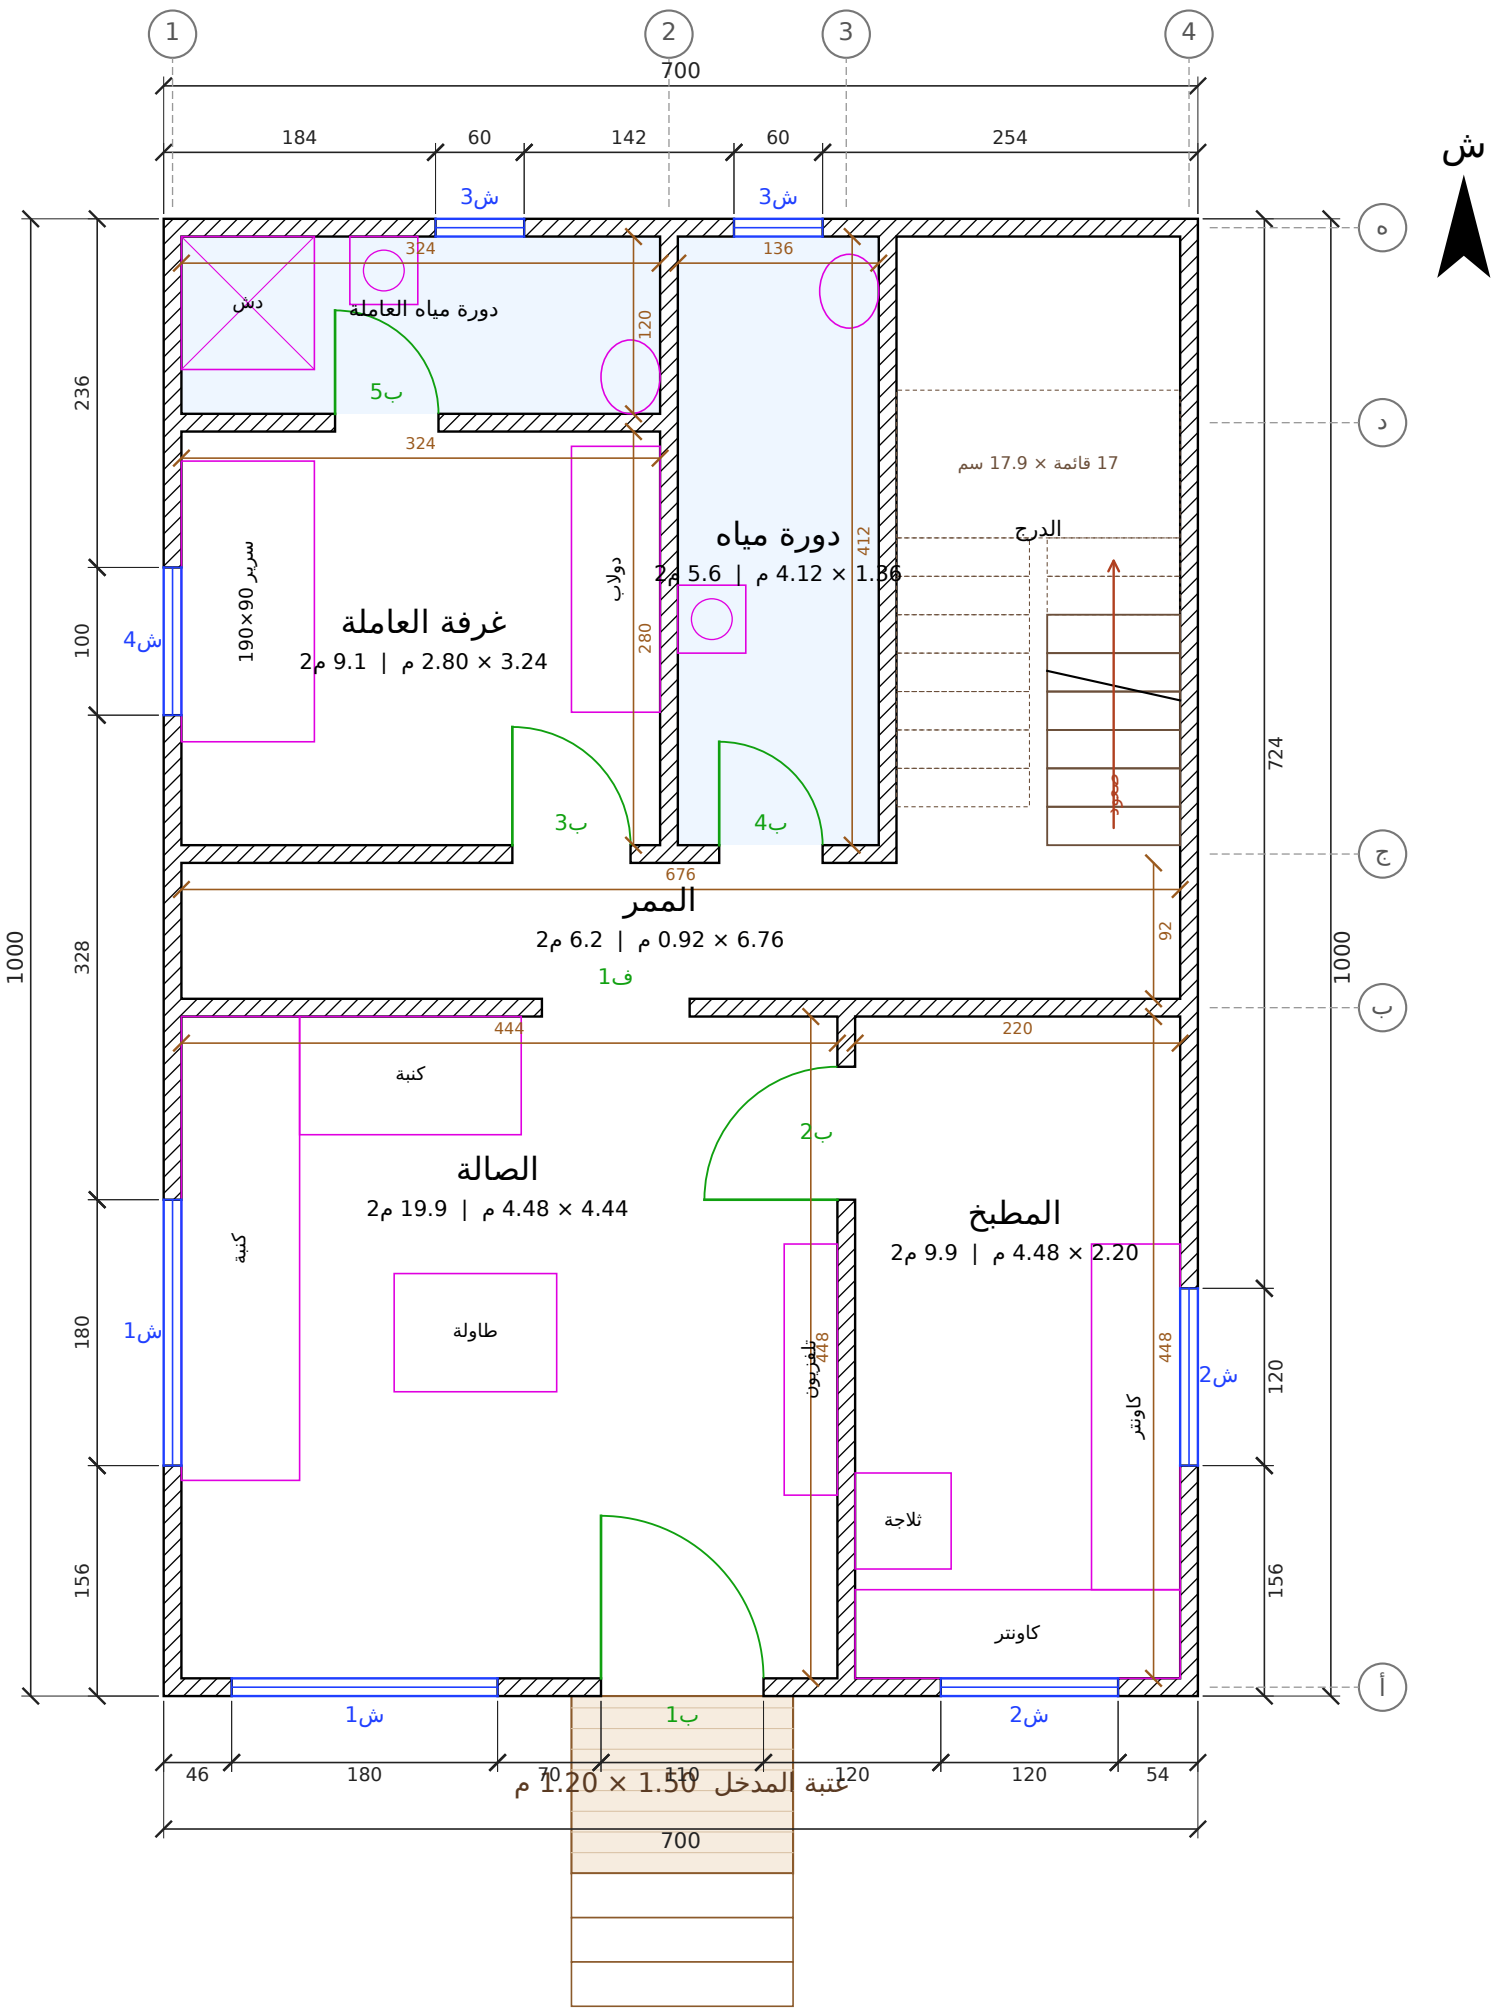

مصنع وتد الأخشاب Watad Wood Factory	المشروع / العميل فيلا خشب دورين — صالة ومطبخ وغرفة عاملة + 3 غرف (ماستر) — عميل — الباحة 7.00 × 10.00 م	عنوان اللوحة المسقط الأفقي — الدور الأرضي	المقياس 1:50	التاريخ 2026-10-23	رقم اللوحة A-01 (1/11)


المسقط الأفقي مع الفرش — الدور الأول

الأبعاد بالسنتيمتر - الجدران: قوائم 7×5 + تلبيس 2.5 من الجهتين (12 سم) | منسوب الأرضية +3.05

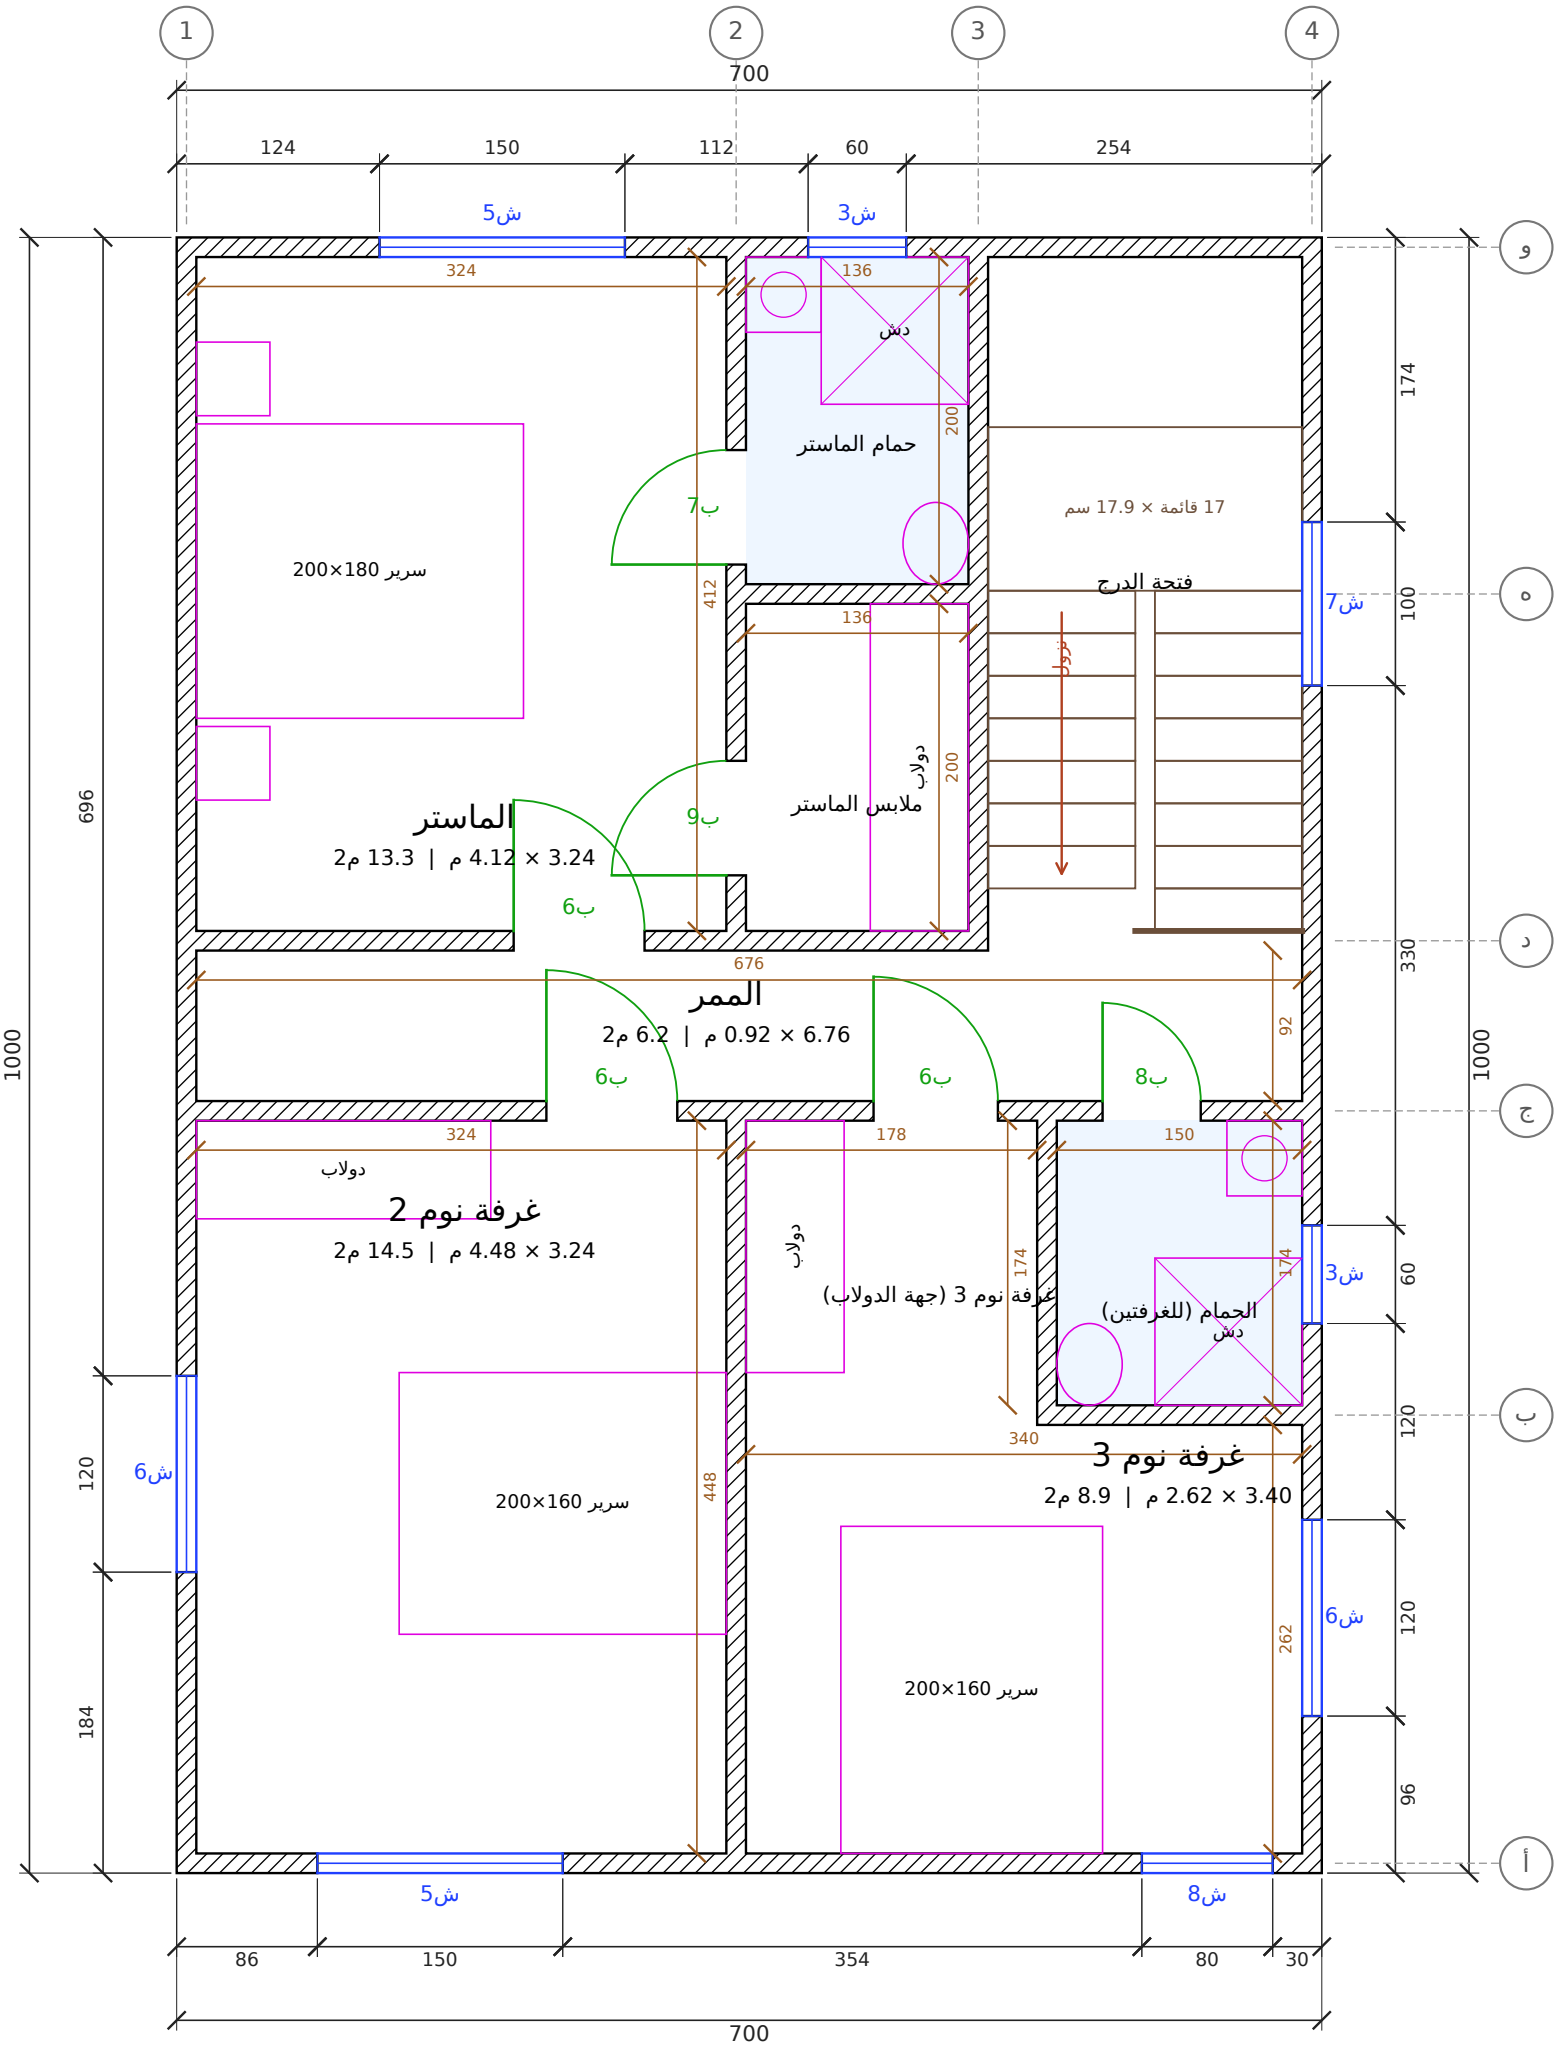


المشروع / العميل	عنوان اللوحة	المقياس	التاريخ	رقم اللوحة
فيلا خشب دورين — صالة ومطبخ وغرفة عاملة + 3 غرف (ماستر) — عميل — الباحة 10.00 × 7.00 م	المسقط الأفقي — الدور الأول	1:50	2026-10-23	A-02 (2/11)

مصنع وتد الأخشاب
Watad Wood Factory

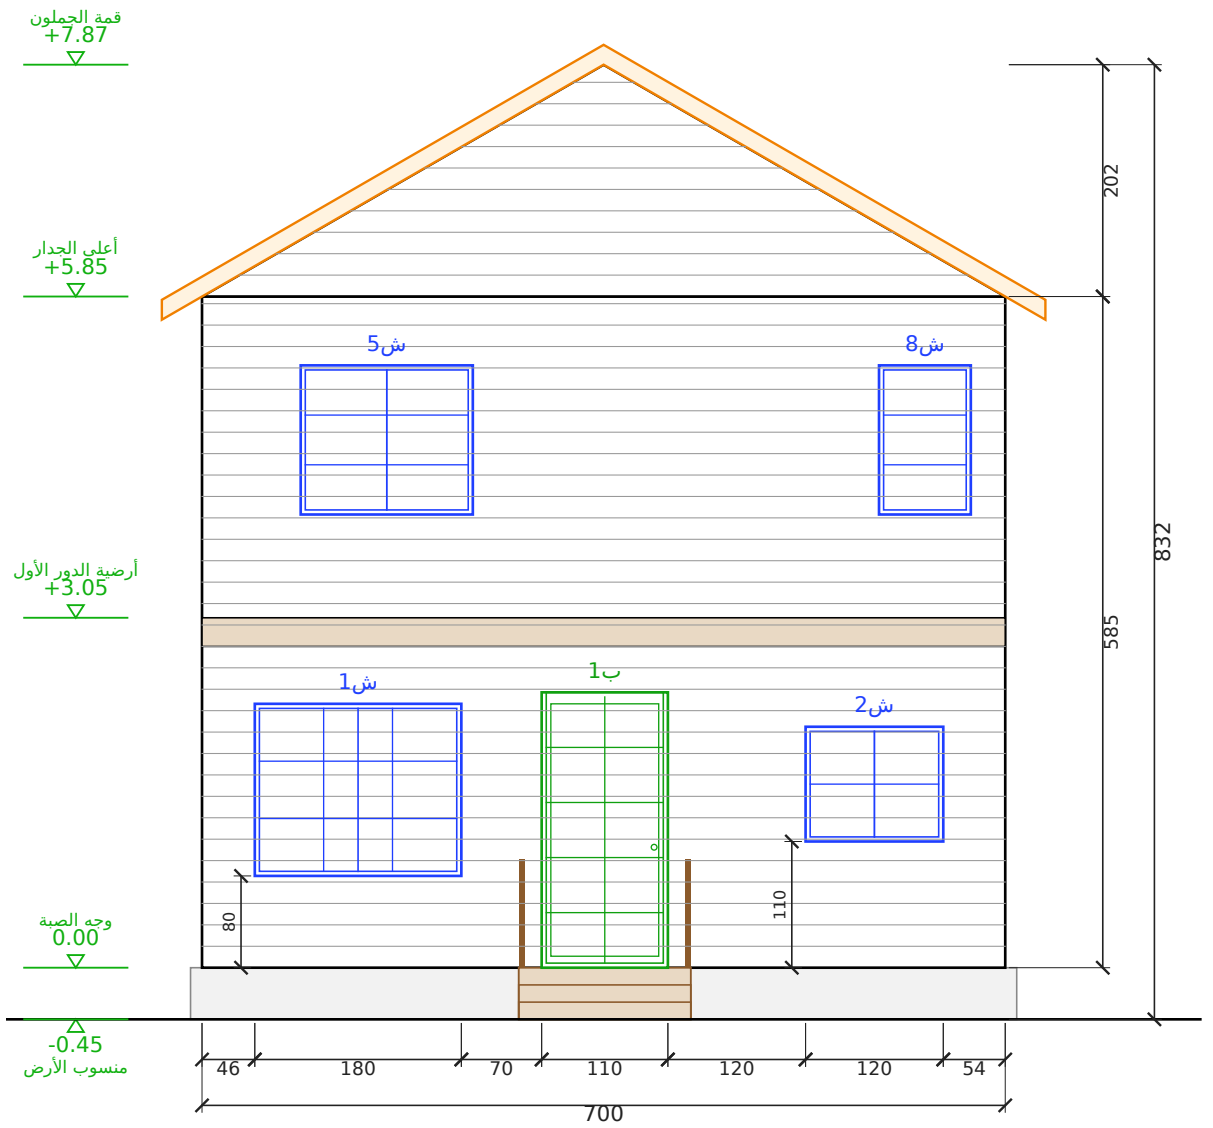

الواجهة الأمامية

مقياس 1:50 | الوحدة: سم

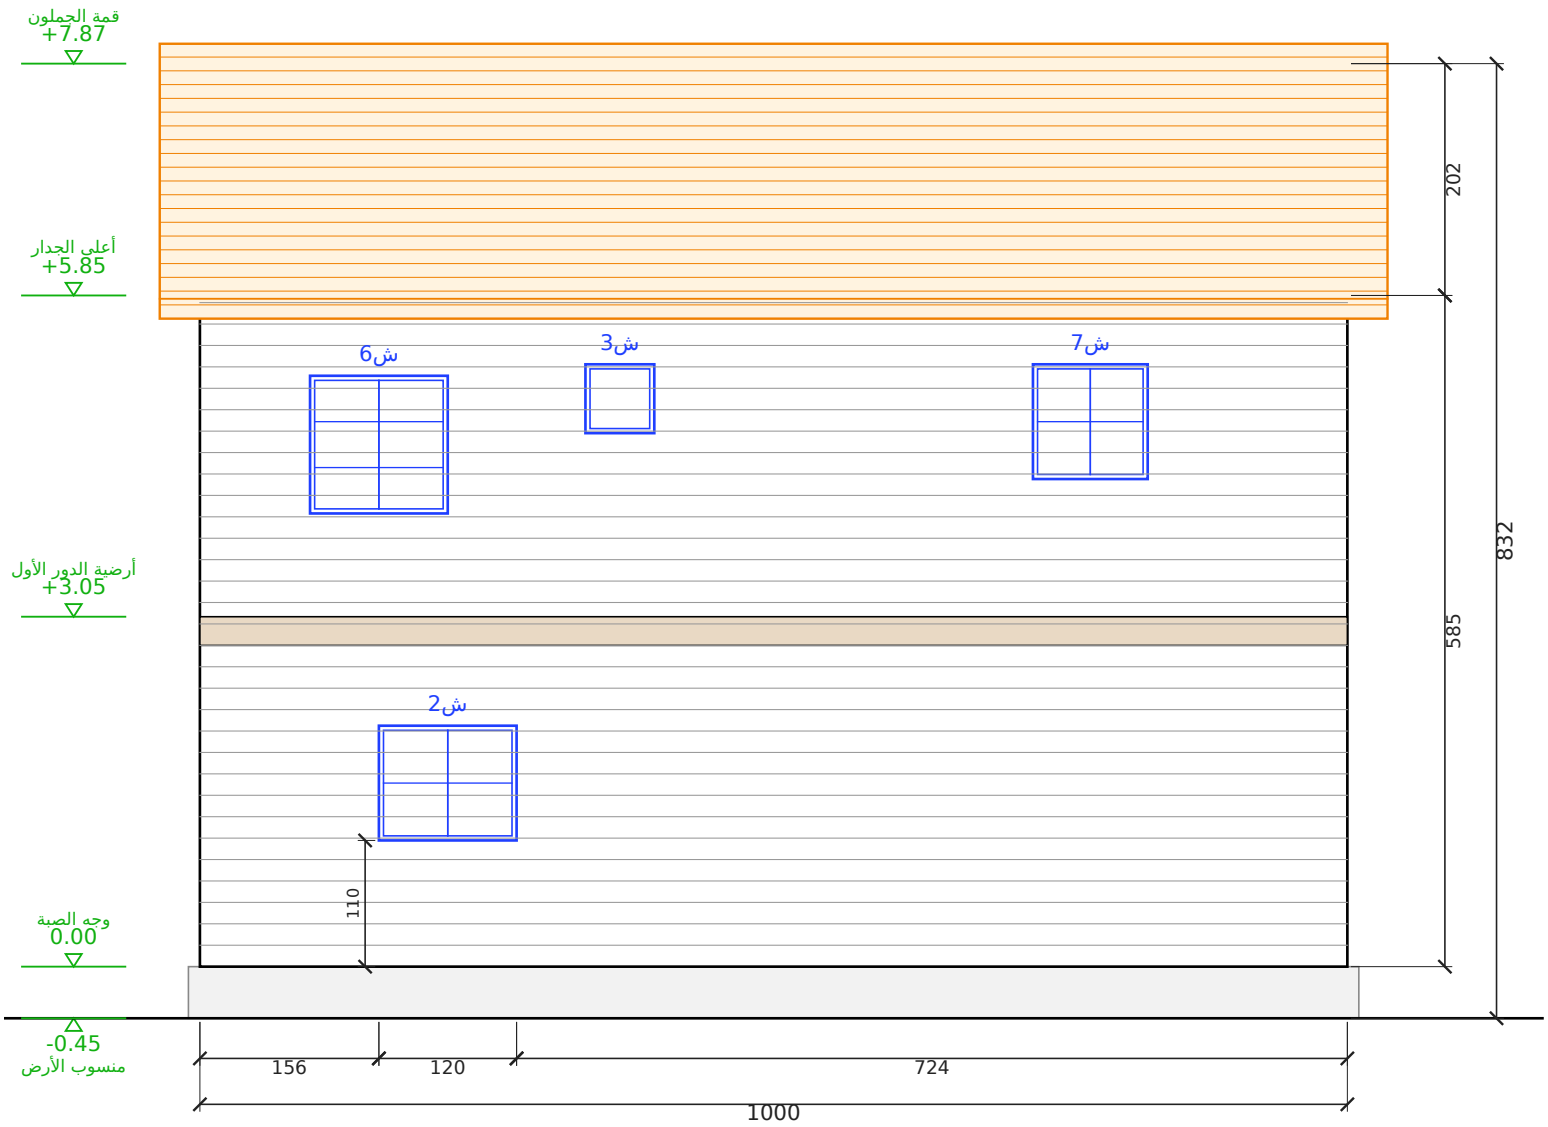


الواجهة الشرقية

مقياس 1:50 | الوحدة: سم


المشروع / العميل	عنوان اللوحة	المقياس	التاريخ	رقم اللوحة
فيلا خشب دورين — صالة ومطبخ وغرفة عاملة + 3 غرف (ماستر) — 7.00 × 10.00 م **عميل — الباحة**	**الواجهة الأمامية والواجهة الشرقية**	**1:50**	**2026-10-23**	**A-03 (3/11)**

مصنع وتد الأخشاب
Watad Wood Factory

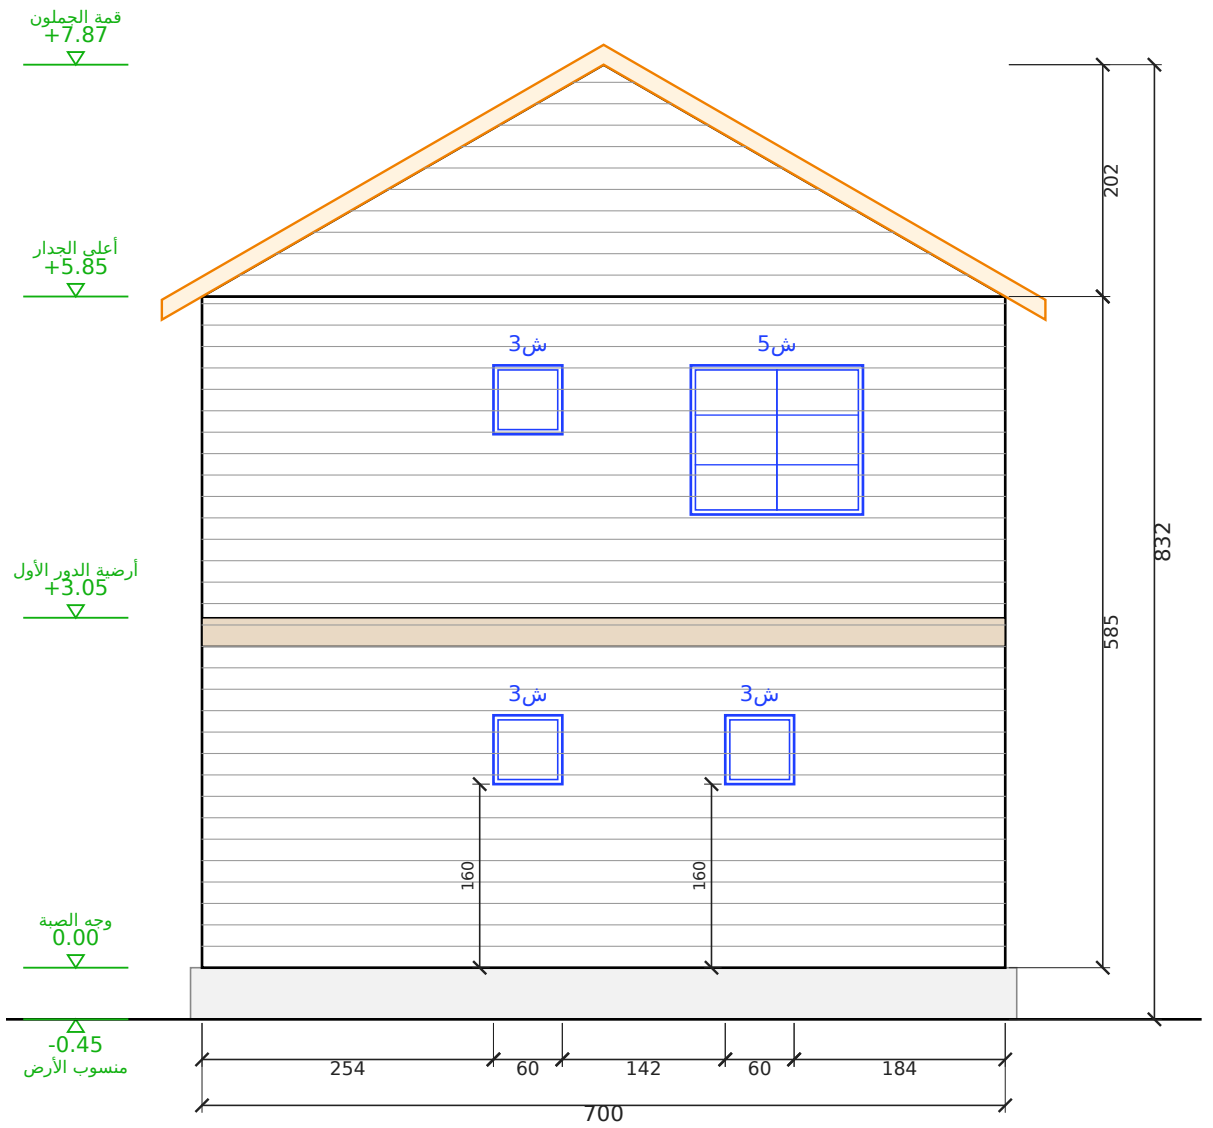

الواجهة الخلفية

مقياس 1:50 | الوحدة: سم

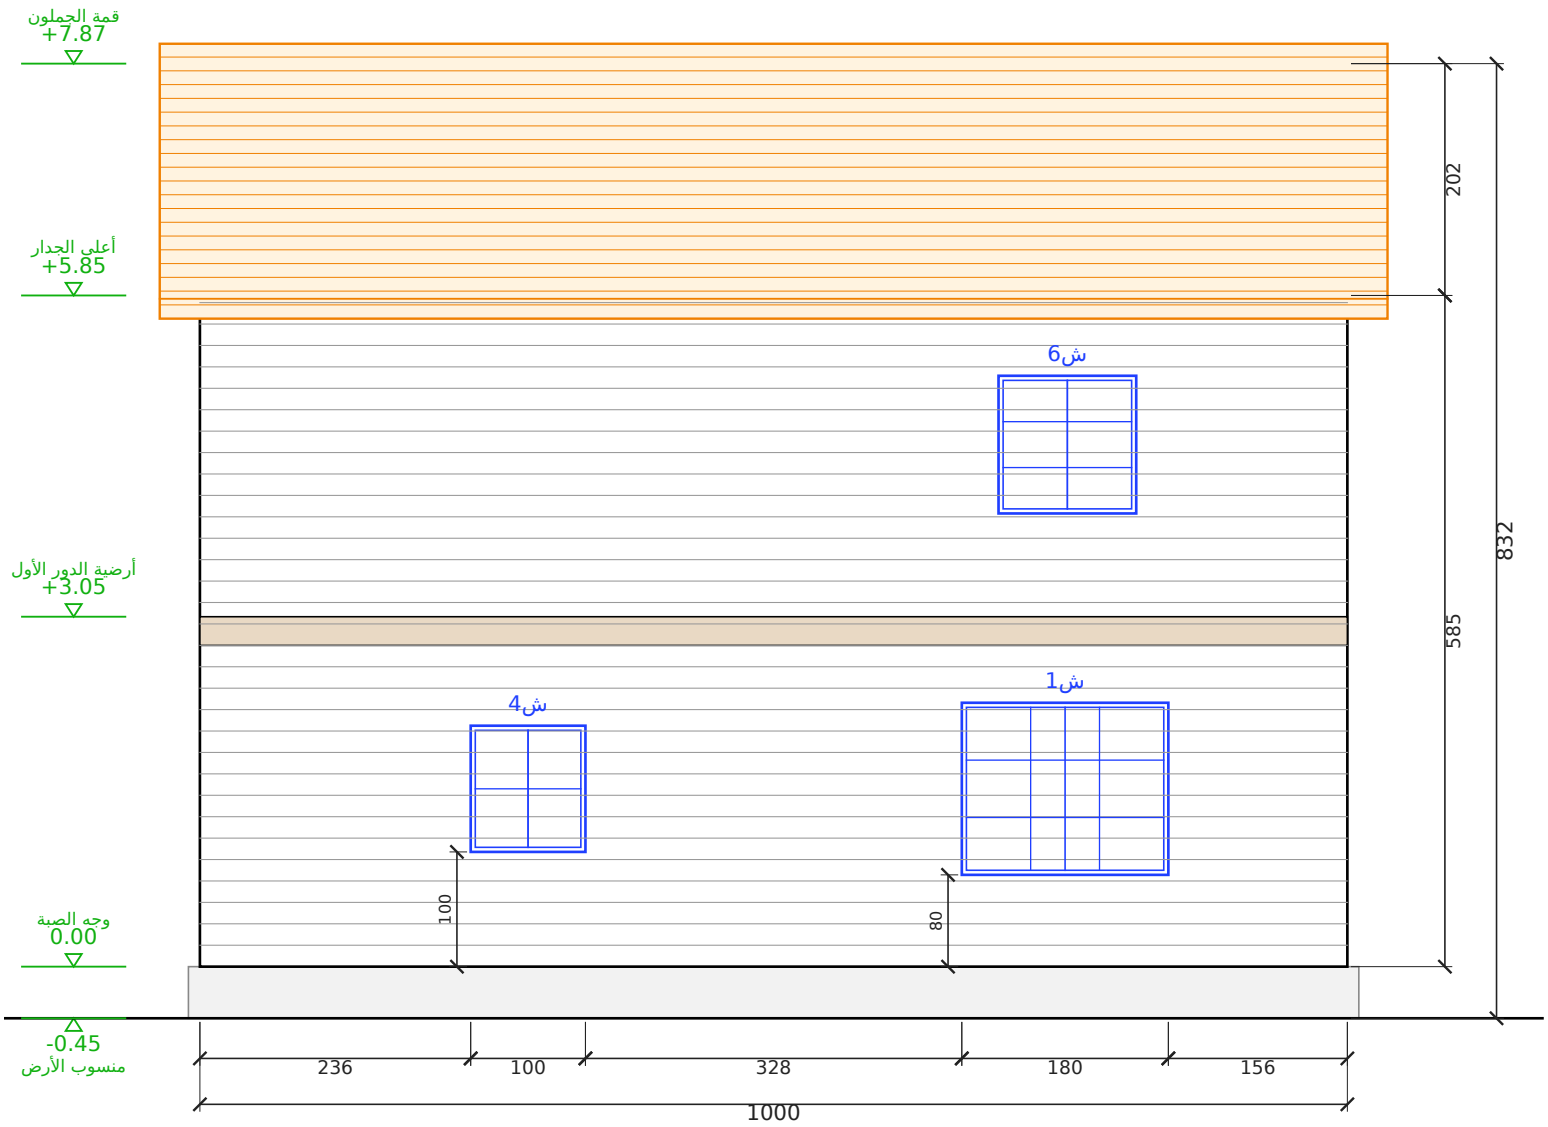


الواجهة الغربية

مقياس 1:50 | الوحدة: سم


المشروع / العميل	عنوان اللوحة	المقياس	التاريخ	رقم اللوحة
فيلا خشب دورين — صالة ومطبخ وغرفة عاملة + 3 غرف (ماستر) — 10.00 × 7.00 م **عميل — الباحة**	**الواجهة الخلفية والواجهة الغربية**	**1:50**	**2026-10-23**	**A-04 (4/11)**

مصنع وتد الأخشاب
Watad Wood Factory


مسقط السقف (جملون)
رفرف 35 سم من كل جهة | مقياس 1:50

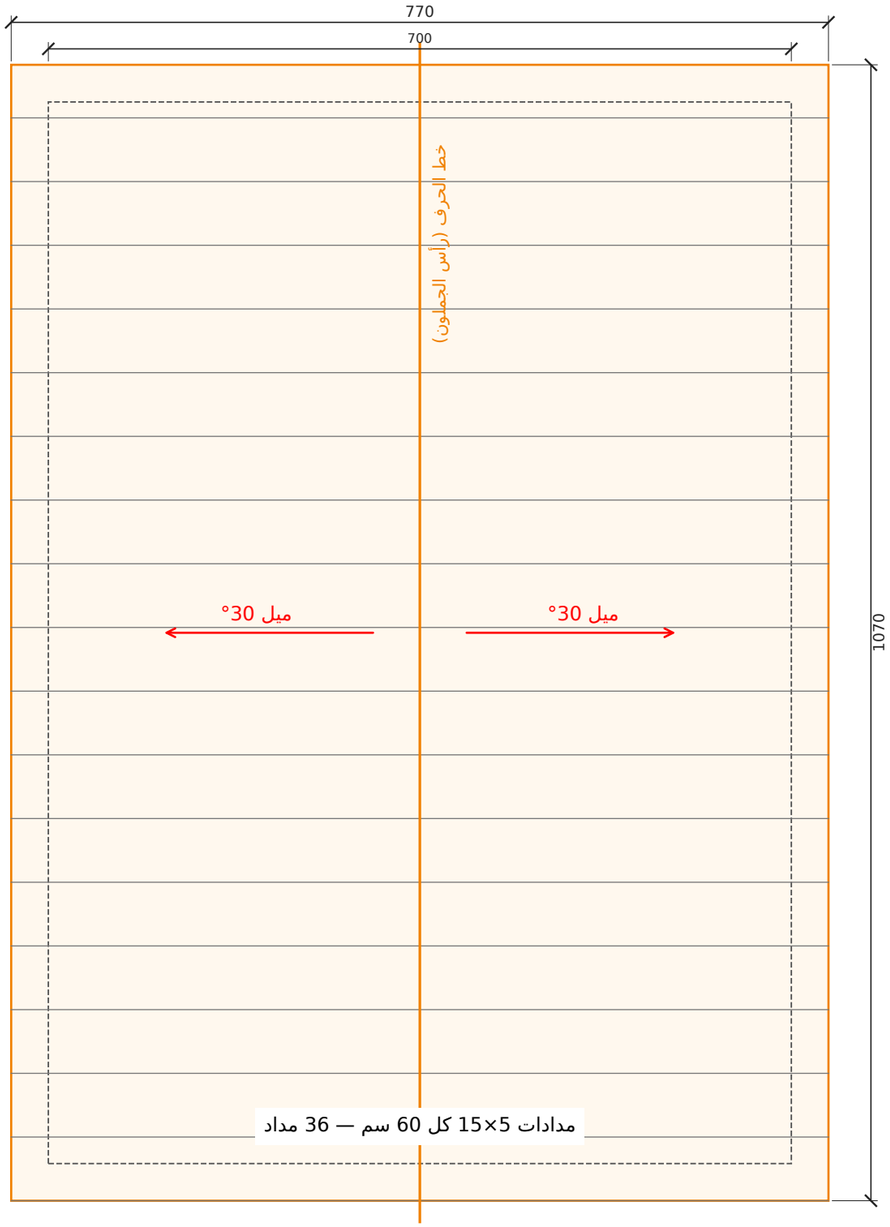

قطاع عرضي أ-أ
مقياس 1:50 | الوحدة: سم

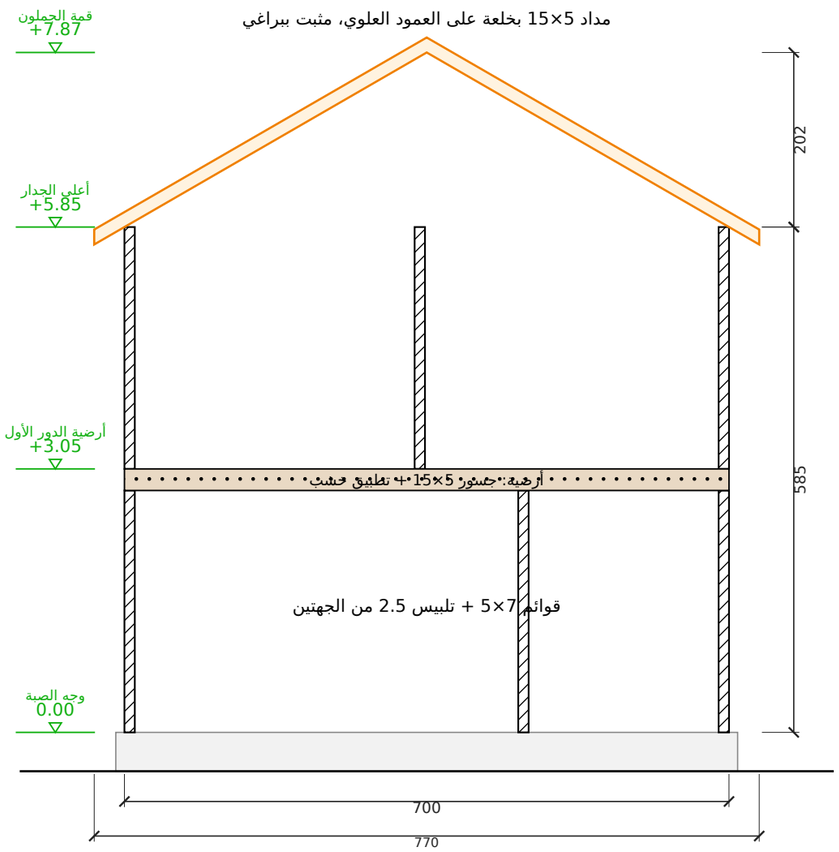

تفصيلة جلوس المداد على العلوي (1:5)

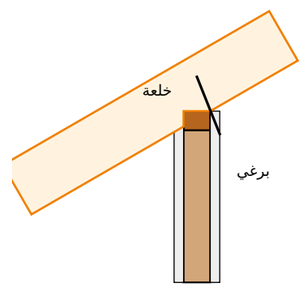

علوي 7×5 على قائم 7×5

المشروع / العميل	عنوان اللوحة	المقياس	التاريخ	رقم اللوحة
فيلا خشب دورين — صالة ومطبخ وغرفة عاملة + 3 غرف (ماستر) — 7.00 × 10.00 م **عميل — الباحة**	**مسقط السقف والقطاع**	**1:50**	**2026-10-23**	**A-05 (5/11)**

مصنع وتد الأخشاب
Watad Wood Factory

جدول مقاسات الأبواب والشبابيك
مقاس الفتحة الصافي في الجدار - الوحدة: سم

الرمز	النوع	العرض (سم)	الارتفاع (سم)	ارتفاع الجلسة (سم)	العدد	الموقع
ب1	باب	110	240	-	1	الأمامية
ب2	باب	90	210	-	1	المطبخ
ب3	باب	80	210	-	1	غرفة العاملة
ب4	باب	70	210	-	1	دورة المياه
ب5	باب	70	210	-	1	دورة مياه العاملة
ب6	باب	80	210	-	2	غرفة 2 - الماستر
ب6	باب	76	210	-	1	غرفة 3
ب7	باب	70	210	-	1	حمام الماستر
ب8	باب	60	210	-	1	الحمام (للغرفتين)
ب9	باب	70	210	-	1	ملابس الماستر
ف1	باب	100	220	-	1	الصالة — الممر
ش1	شباك	180	150	80	2	الأمامية - الغربية
ش2	شباك	120	100	110	2	الأمامية - الشرقية
ش3	شباك	60	60	160	4	الخلفية 3 - الشرقية
ش4	شباك	100	110	100	1	الغربية
ش5	شباك	150	130	90	2	الأمامية - الخلفية
ش6	شباك	120	120	90	2	الشرقية - الغربية
ش7	شباك	100	100	120	1	الشرقية
ش8	شباك	80	130	90	1	الأمامية

الإجمالي: أبواب 12 - شبابيك 15

مصنع وتد الأخشاب Watad Wood Factory	المشروع / العميل فيلا خشب دورين — صالة ومطبخ وغرفة عاملة + 3 غرف (ماستر) — 7.00 × 10.00 م عميل — الباحة	عنوان اللوحة جدول الأبواب والشبابيك	المقياس —	التاريخ 2026-10-23	رقم اللوحة A-06 (6/11)

جدول المساحات وبيانات المشروع والتسعير

بيانات المشروع

البند	البيان
المشروع	فيلا خشب دورين — صالة ومطبخ وغرفة عاملة + 3 غرف (ماستر) — 7.00 × 10.00 م
العميل	عميل — الباحة
الموقع	الباحة
الاستخدام	سكن عائلي
التاريخ	2026-10-23
نظام البناء	هيكل خشب 7×5 + تلبيس 2.5 سم من الجهتين
السقف	جملون 30° — قرميد معدني

جدول المساحات

م	الفراغ	الأبعاد (م)	المساحة (م2)
1	أرضي — الصالة	4.48 × 4.44	19.89
2	أرضي — المطبخ	4.48 × 2.20	9.86
3	أرضي — الممر	6.76 × 0.92	6.22
4	أرضي — غرفة العاملة	2.80 × 3.24	9.07
5	أرضي — دورة مياه العاملة	1.20 × 3.24	3.89
6	أرضي — دورة مياه	4.12 × 1.36	5.60
7	أرضي — الدرج	4.12 × 1.92	7.91
8	أول — غرفة نوم 2	4.48 × 3.24	14.52
9	أول — غرفة نوم 3	2.62 × 3.40	8.91
10	أول — غرفة نوم 3 (جهة الدولاب)	1.74 × 1.78	3.10
11	أول — الممر	0.92 × 6.76	6.22
12	أول — الماستر	4.12 × 3.24	13.35
13	أول — الحمام (للغرفتين)	1.74 × 1.50	2.61
14	أول — ملابس الماستر	2.00 × 1.36	2.72
15	أول — حمام الماستر	2.00 × 1.36	2.72
	المساحة الصافية الداخلية		**116.58**
	عتبة المدخل	**1.20 × 1.50**	**1.80**
	المساحة الإجمالية المبنية	**2 دور × 10.00 × 7.00**	**140.00**
	المساحة الكلية (المبنية + التراس)		**141.80**

التسعير المفصّل

البند	المبلغ (ريال)
الكوخ المبني 140.00 م² × 1,500	210,000
عتبة المدخل بدرجها (1.50 × 1.20) — 1.80 م² × 1,500	2,700
الإجمالي (ريال)	**212,700**

ملاحظات:


- السعر 1,500 ر.س/م² للدورين حسب المخطط المعتمد — شامل الصبة (بصمة المبنى 7.00 × 10.00 م).
- شامل أدوات التأسيس للسباكة والكهرباء (التمديدات الداخلية).
- التوصيلات الخارجية (عداد الكهرباء والمويه والصرف) على العميل.

لقطات المنظور الخارجي

المنظور الأمامي




منظور أمامي من اليسار

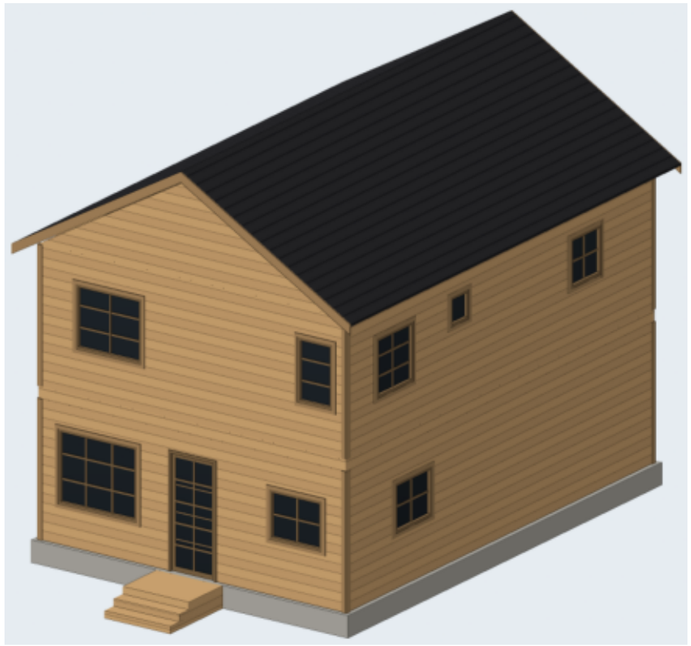


منظور أمامي من اليمين




المنظور الخلفي

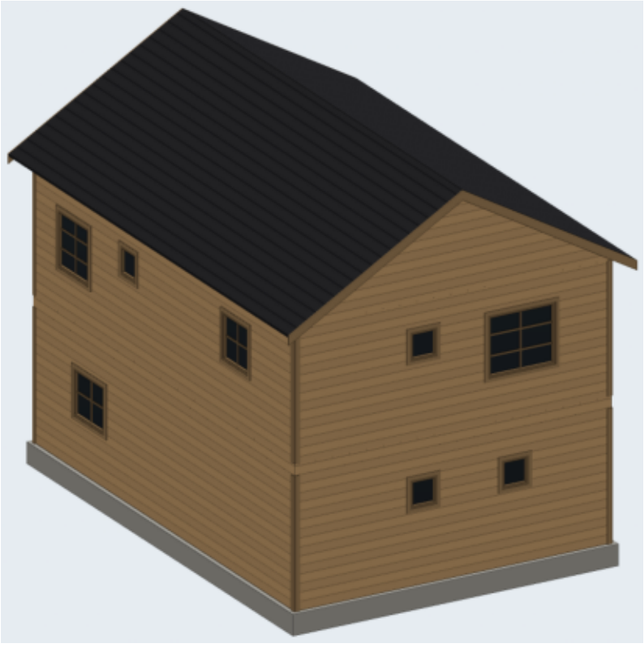

منظور خلفي من اليمين

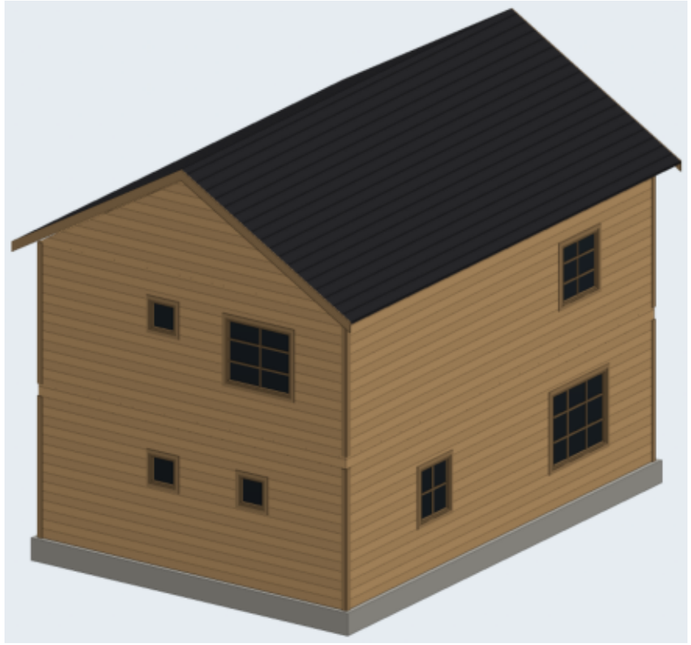

منظر علوي

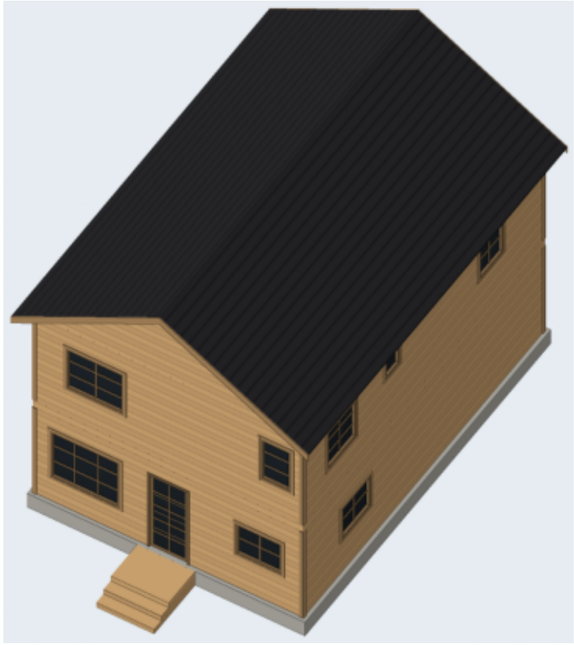


المشروع / العميل	عنوان اللوحة	المقياس	التاريخ	رقم اللوحة
فيلا خشب دورين — صالة ومطبخ وغرفة عاملة + 3 غرف (ماستر) — 7.00 × 10.00 م **عميل — الباحة**	**لقطات المنظور**	**—**	**2026-10-23**	**A-08 (8/11)**

مصنع وتد الأخشاب
Watad Wood Factory

المقطع العلوي بالفرش — الدور الأرضي


مقطع أفقي على ارتفاع 1.90 م — توزيع الفرش ومسار الحركة

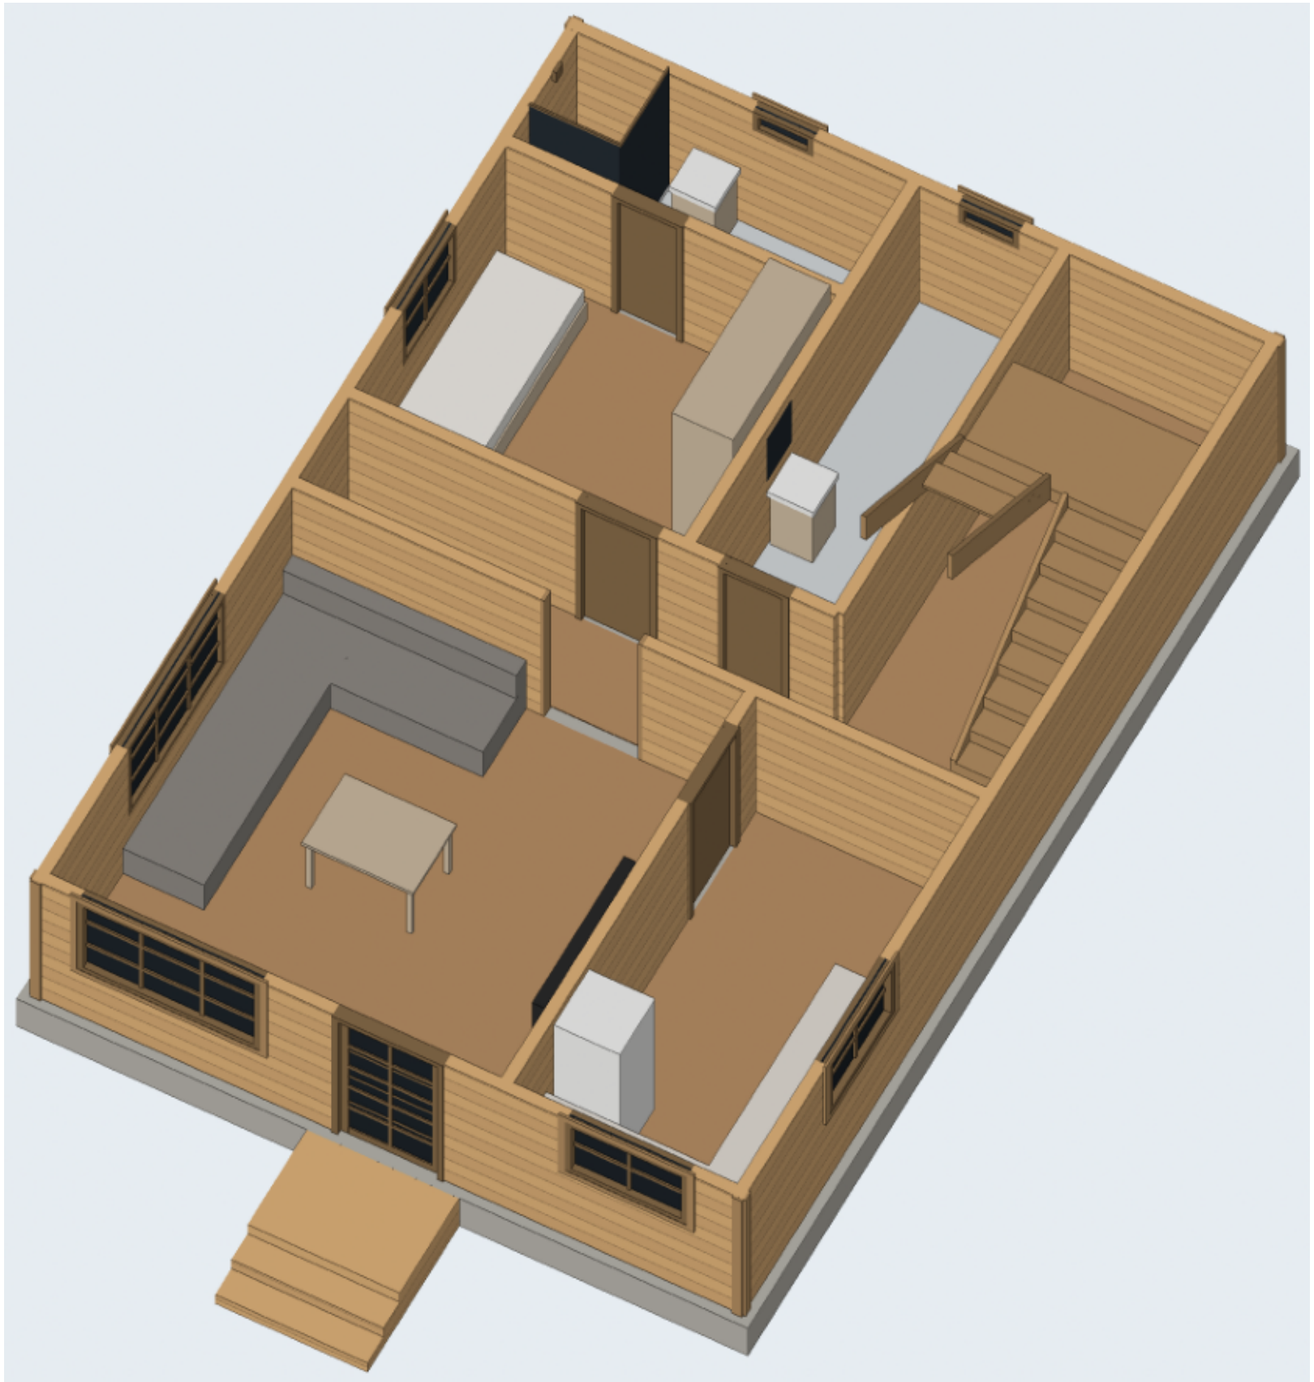

مصنع وتد الأخشاب Watad Wood Factory	المشروع / العميل **فيلا خشب دورين — صالة ومطبخ وغرفة عاملة + 3 غرف (ماستر) — 10.00 × 7.00 م** **عميل — الباحة**	عنوان اللوحة **المقطع العلوي بالفرش — الدور الأرضي**	المقياس **—**	التاريخ **2026-10-23**	رقم اللوحة **A-09 (9/11)**

المقطع العلوي بالفرش — الدور الأول


مقطع أفقي على ارتفاع 1.90 م — توزيع الفرش ومسار الحركة

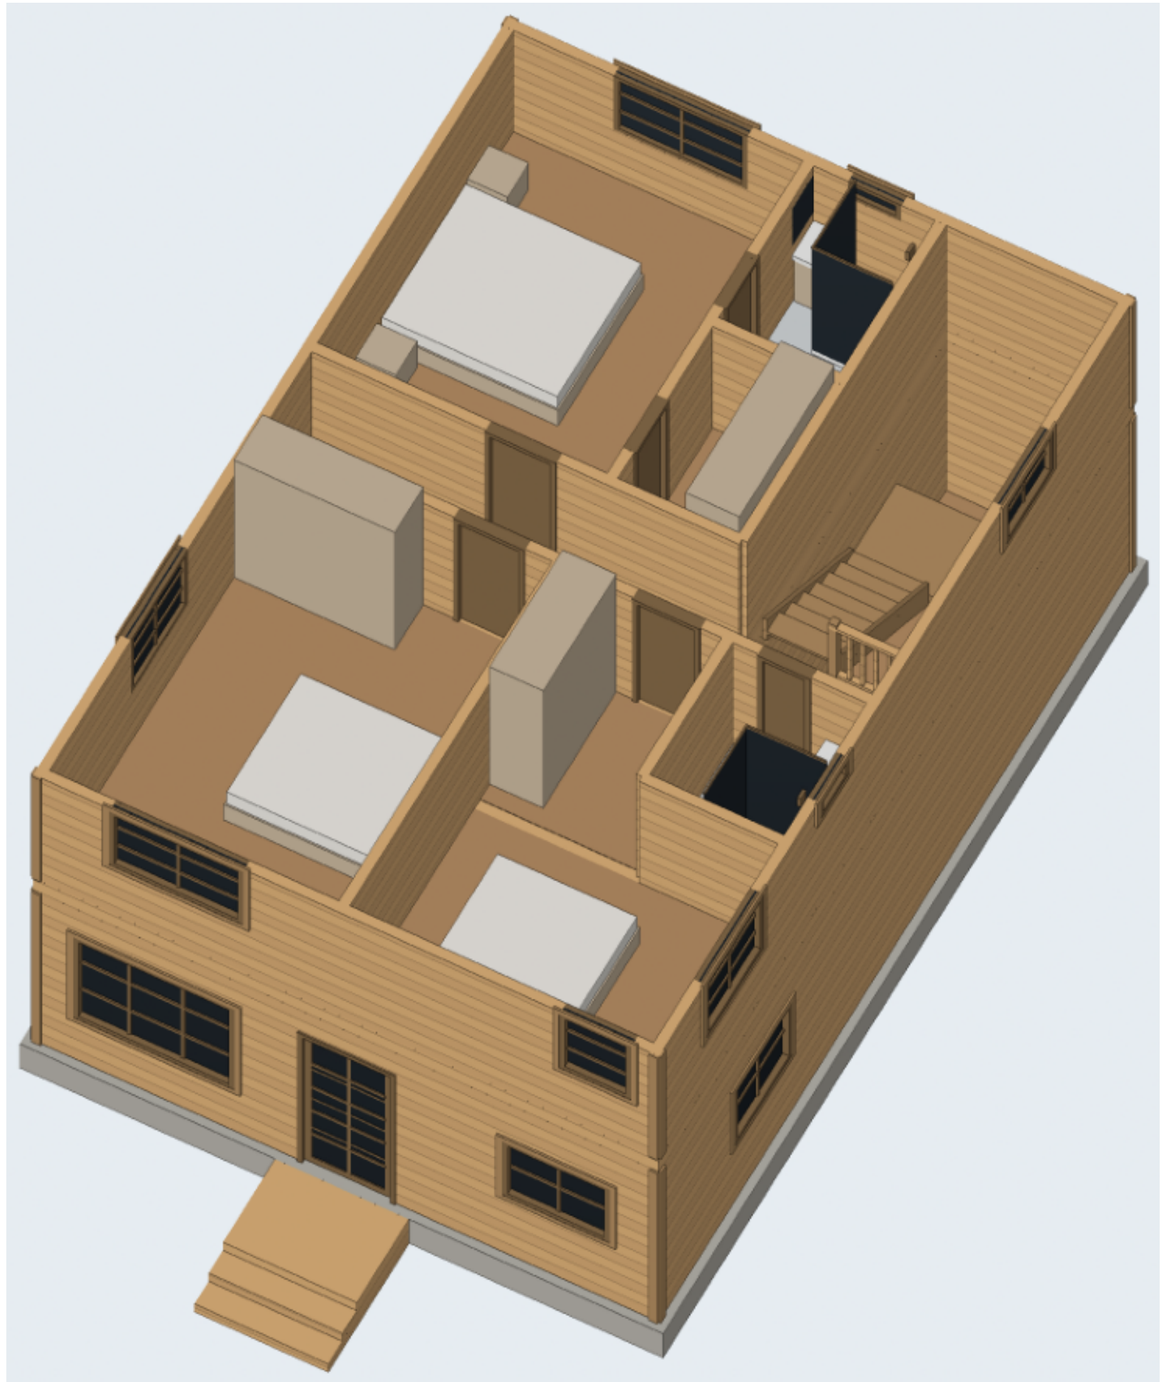

مصنع وتد الأخشاب Watad Wood Factory	المشروع / العميل فيلا خشب دورين — صالة ومطبخ وغرفة عاملة + 3 غرف (ماستر) — 10.00 × 7.00 م عميل — الباحة	عنوان اللوحة المقطع العلوي بالفرش — الدور الأول	المقياس —	التاريخ 2026-10-23	رقم اللوحة A-10 (10/11)

المنظور ثلاثي الأبعاد والمواد

النمط: جوزي غامق + إطارات سوداء — رندر واقعي بخامات حقيقية

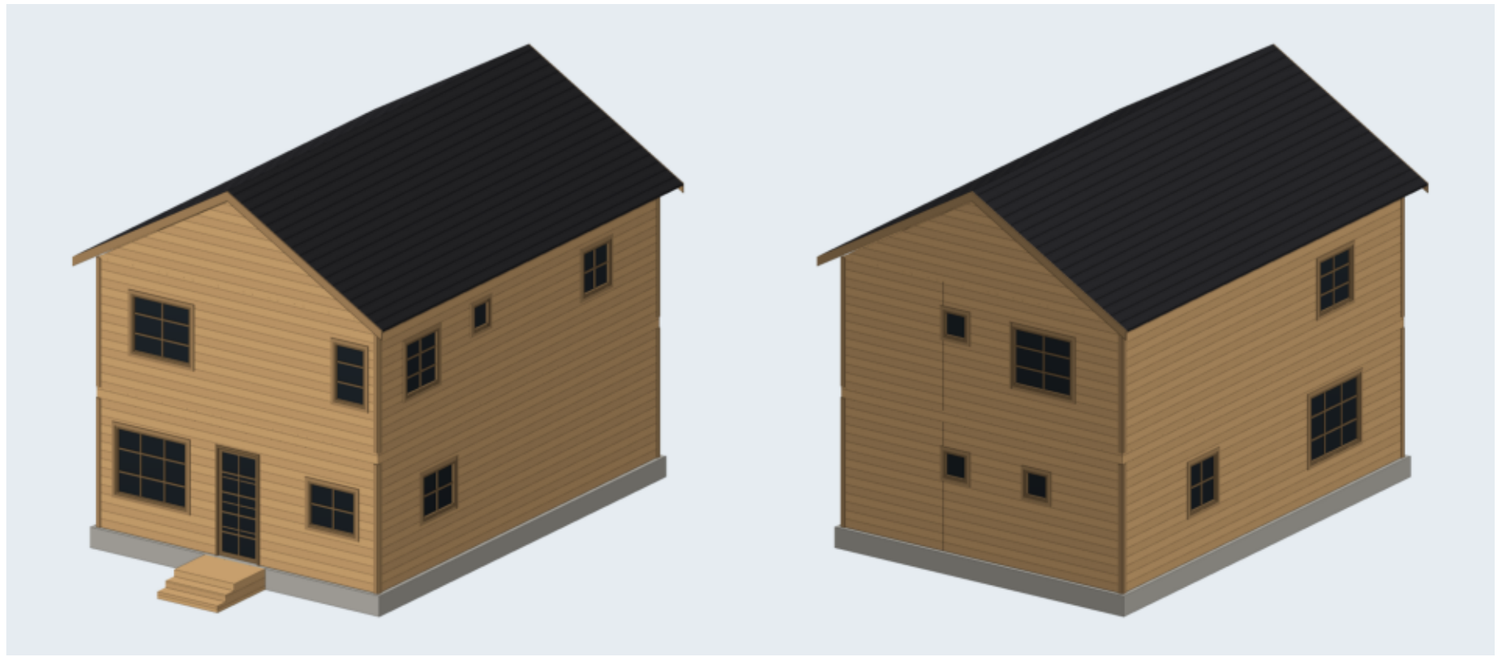

جدول المواد والألوان

الخشب / الصبغة

خشب طبيعي فاتح (بدون صبغة)

القرميد

قرميد رمادي غامق

الزجاج

زجاج عاكس غامق

إطارات الشبابيك والأبواب

إطار خشب بنفس الصبغة أغمق

الكنار والزوايا

نفس الصبغة أغمق درجة


الصبة

خرسانة 45 سم


الدربزين: ألواح أفقية متقاربة (عصري)

تقسيم الشبابيك: بدون | الباب الرئيسي: زجاج بتقسيمات (فرنسي)

أنواع الدربزين المعتمدة (من مشاريع المصنع)

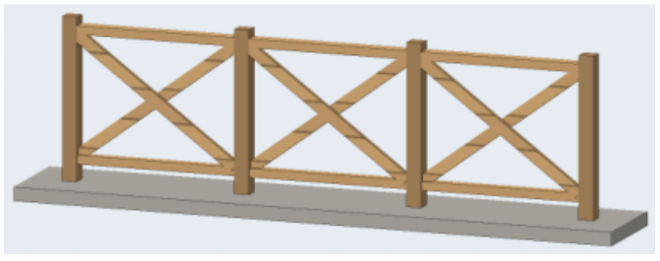

تقاطع X (صورة 5)

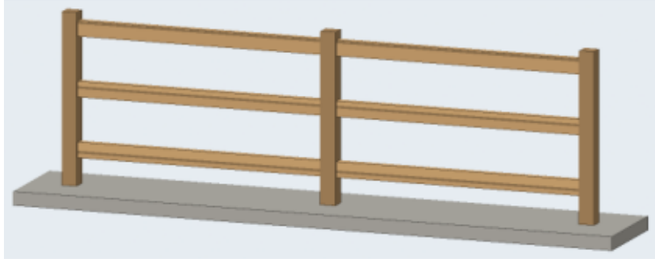

3 مرابيع أفقية (صورة 2)



قوائم رأسية متقاربة (صورة 1)

المشروع / العميل	عنوان اللوحة	المقياس	التاريخ	رقم اللوحة
فيلا خشب دورين — صالة ومطبخ وغرفة عاملة + 3 غرف (ماستر) — 7.00 × 10.00 م **عميل — الباحة**	**المنظور والمواد**	**—**	**2026-10-23**	**A-11 (11/11)**

مصنع وتد الأخشاب
Watad Wood Factory

الخارج — نهاراً · أمامي من اليسار



(مصنع وتد الأخشاب — الواقع الافتراضي في آخر صفحة (أو اضغط هنا

الخارج — نهاراً · أمامي من اليمين



(مصنع وتد الأخشاب — الواقع الافتراضي في آخر صفحة (أو اضغط هنا

الخارج — نهاراً · الواجهة الأمامية



(مصنع وتد الأخشاب — الواقع الافتراضي في آخر صفحة (أو اضغط هنا

الخارج — نهاراً · خلفي من اليسار



(مصنع وتد الأخشاب — الواقع الافتراضي في آخر صفحة (أو اضغط هنا

وقت الغروب وبالليل · أمامي من اليسار — وقت الغروب



(مصنع وتد الأخشاب — الواقع الافتراضي في آخر صفحة (أو اضغط هنا

وقت الغروب وبالليل · أمامي من اليمين — وقت الغروب



(مصنع وتد الأخشاب — الواقع الافتراضي في آخر صفحة (أو اضغط هنا

وقت الغروب وبالليل · الصالة — بالليل والإنارة شغالة



(مصنع وتد الأخشاب — الواقع الافتراضي في آخر صفحة (أو اضغط هنا

وقت الغروب وبالليل · الماستر — بالليل والإنارة شغالة



(مصنع وتد الأخشاب — الواقع الافتراضي في آخر صفحة (أو اضغط هنا



(مصنع وتد الأخشاب — الواقع الافتراضي في آخر صفحة (أو اضغط هنا



(مصنع وتد الأخشاب — الواقع الافتراضي في آخر صفحة (أو اضغط هنا



(مصنع وتد الأخشاب — الواقع الافتراضي في آخر صفحة (أو اضغط هنا

(صور 360° — تنعرض متحركة في الجولة الافتراضية (اضغط هنا






(صور 360° — تنعرض متحركة في الجولة الافتراضية (اضغط هنا






(صور 360° — تنعرض متحركة في الجولة الافتراضية (اضغط هنا

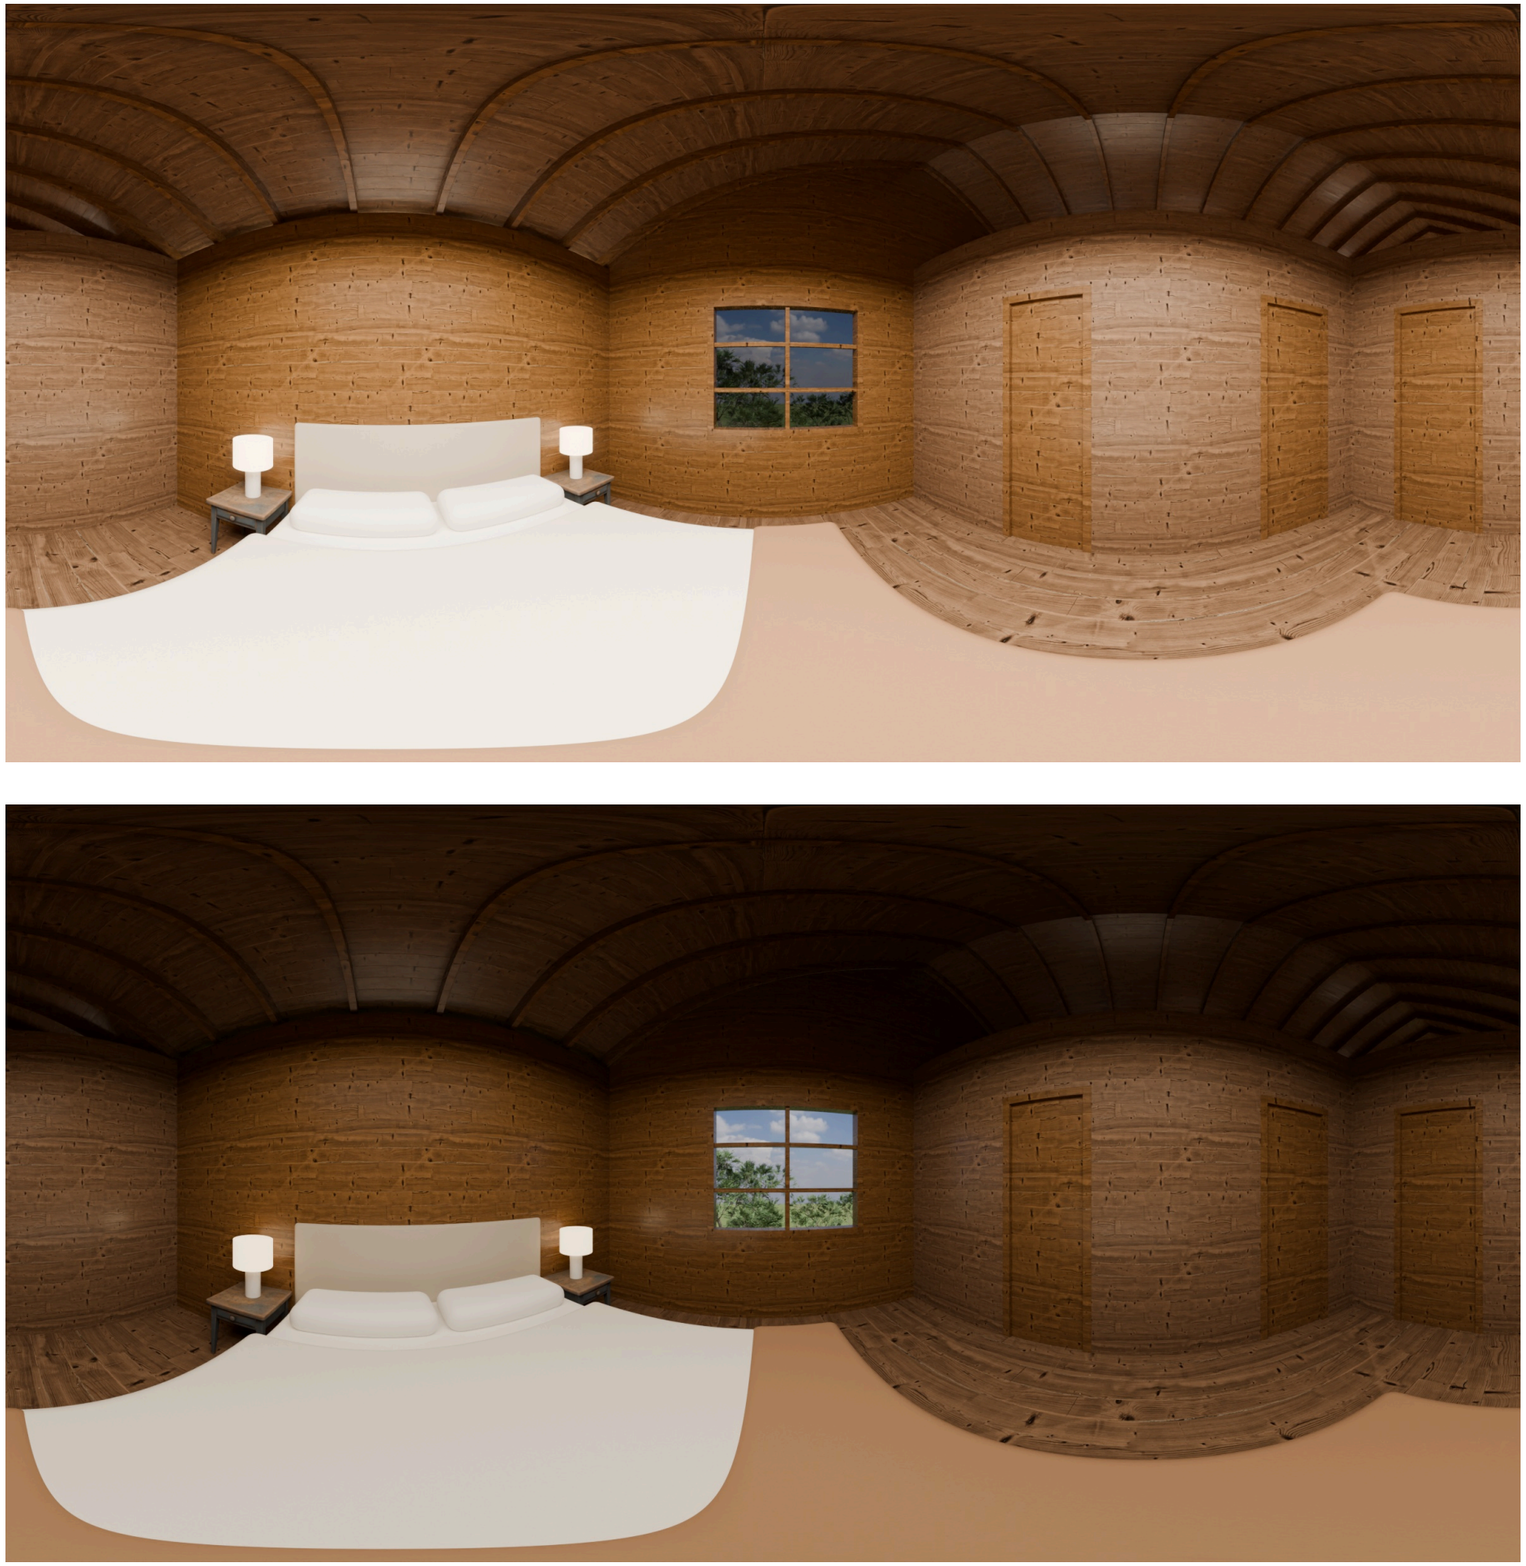

(صور 360° — تنعرض متحركة في الجولة الافتراضية (اضغط هنا

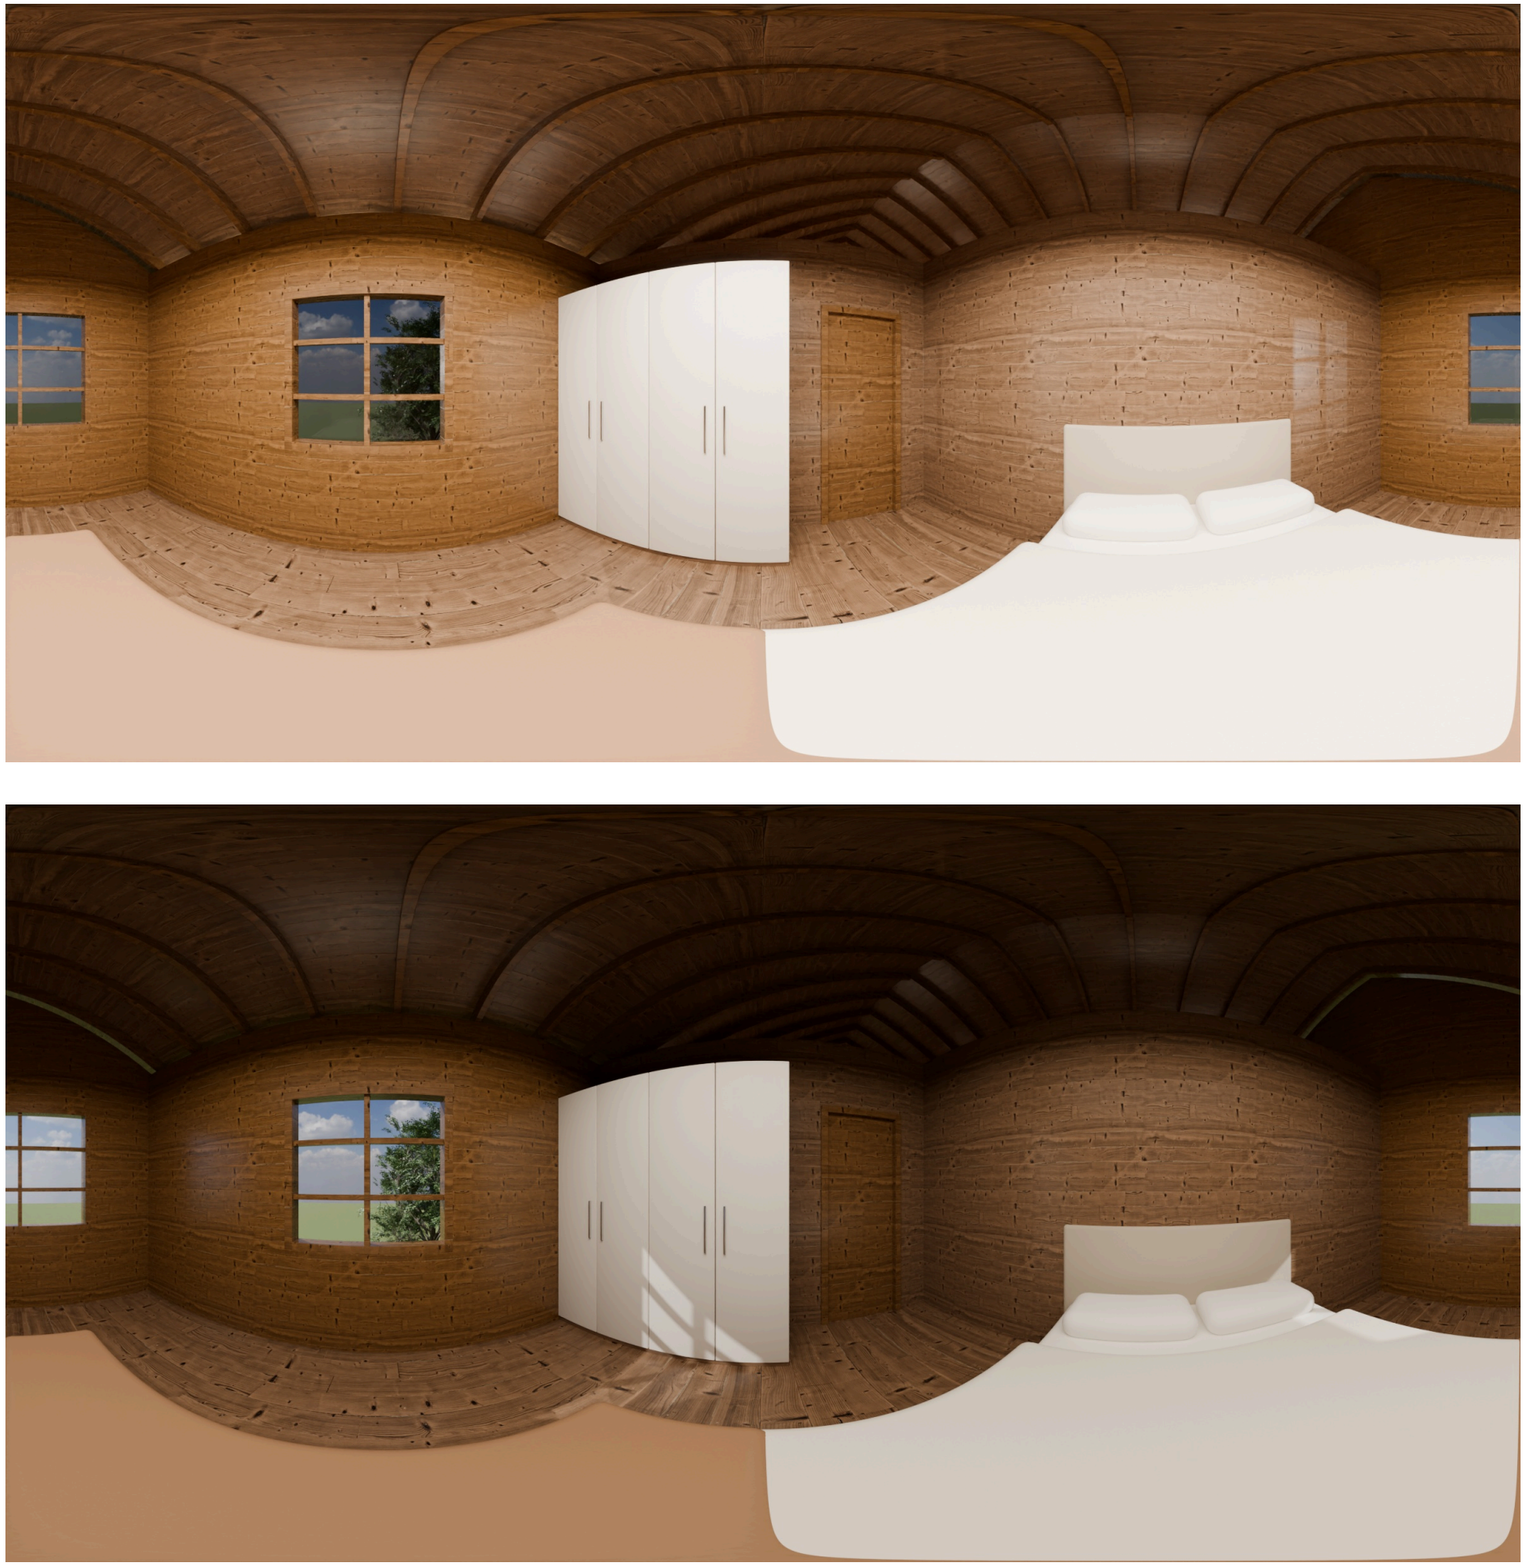

مصنع وتد الأخشاب

جرّب الواقع الافتراضي

.فيلا الباحة — امشِ داخل التصميم: الحوش والجلسات والدورين، ولف 360° بكل غرفة. امسح الرمز بكاميرا الجوال أو اضغط على الزر



افتح الجولة بالنهار

افتح الجولة بالليل والإنارة شغالة

الرابط: https://watad-wood.com/baha/