
المنظور ثلاثي الأبعاد والمواد

النمط: جوزي غامق + إطارات سوداء — رندر واقعي بخامات حقيقية

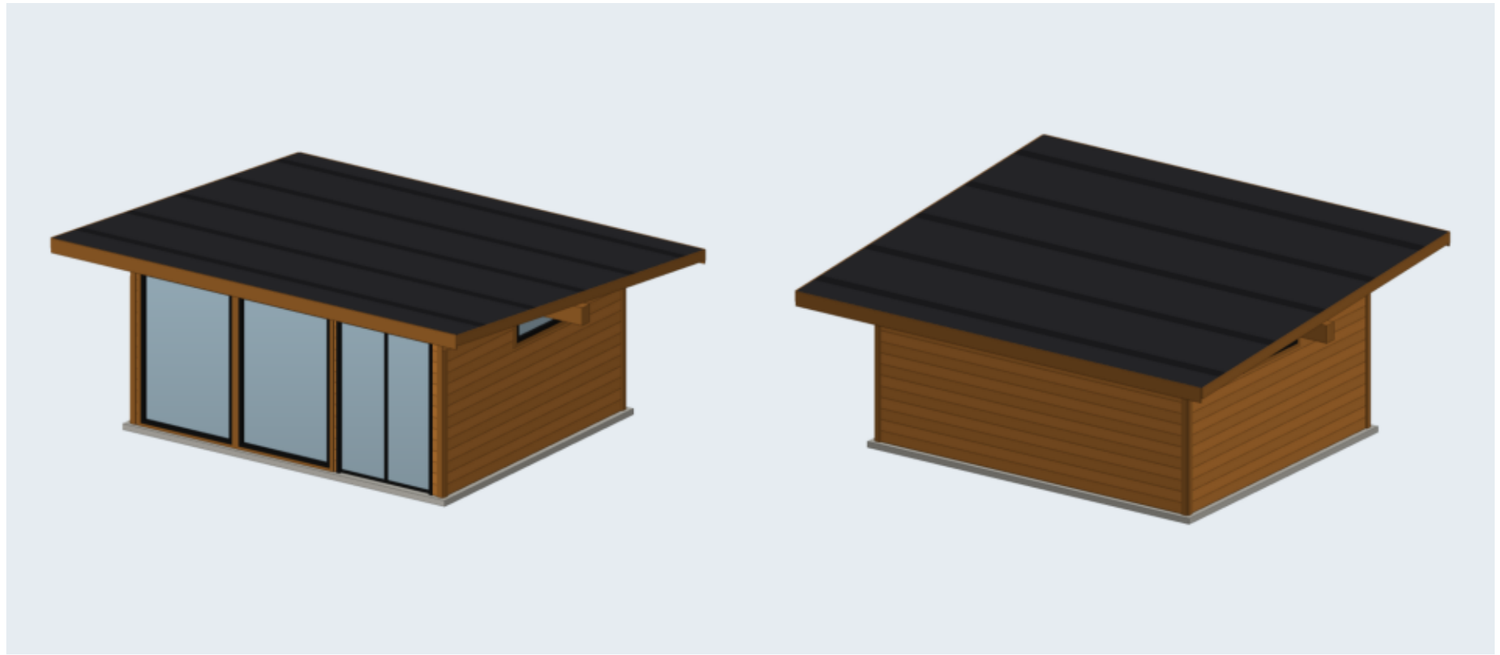

جدول المواد والألوان

الخشب / الصبغة

صبغة عسلي / سيدر

السقف (صاج معدني)

صاج رمادي غامق

الزجاج

زجاج شفاف

إطارات الشبابيك والأبواب

إطار ألمنيوم أسود

الكنار والزوايا

نفس الصبغة أغمق درجة


القاعدة

قواعد حديد 10 سم (متنقل — بدون صبة)


الدربزين: قوائم رأسية متقاربة (صورة 1)

تقسيم الشبابيك: بدون | الباب الرئيسي: سحاب زجاج

أنواع الدربزين المعتمدة (من مشاريع المصنع)

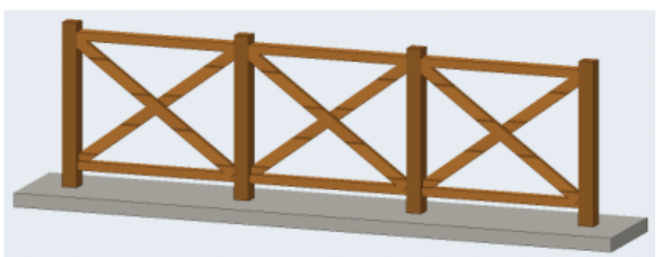

تقاطع X (صورة 5)

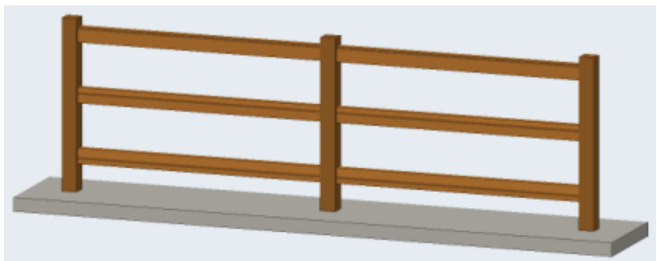

3 مرابيع أفقية (صورة 2)




قوائم رأسية متقاربة (صورة 1)

المشروع / العميل	عنوان اللوحة	المقياس	التاريخ	رقم اللوحة
مجلس حديث بواجهة زجاج كاملة — 6.00 × 5.00 = 30 م² **عميل — مجلس حديث 5×6**	**المنظور والمواد**	**1:50**	**2026-10-23**	**W-01 (1/11)**

مصنع وتد الأخشاب
Watad Wood Factory


المسقط الأفقي مع الفرش

الأبعاد بالسنتيمتر - الجدران: قوائم 7×5 + تلبيس 2.5 من الجهتين (12 سم)

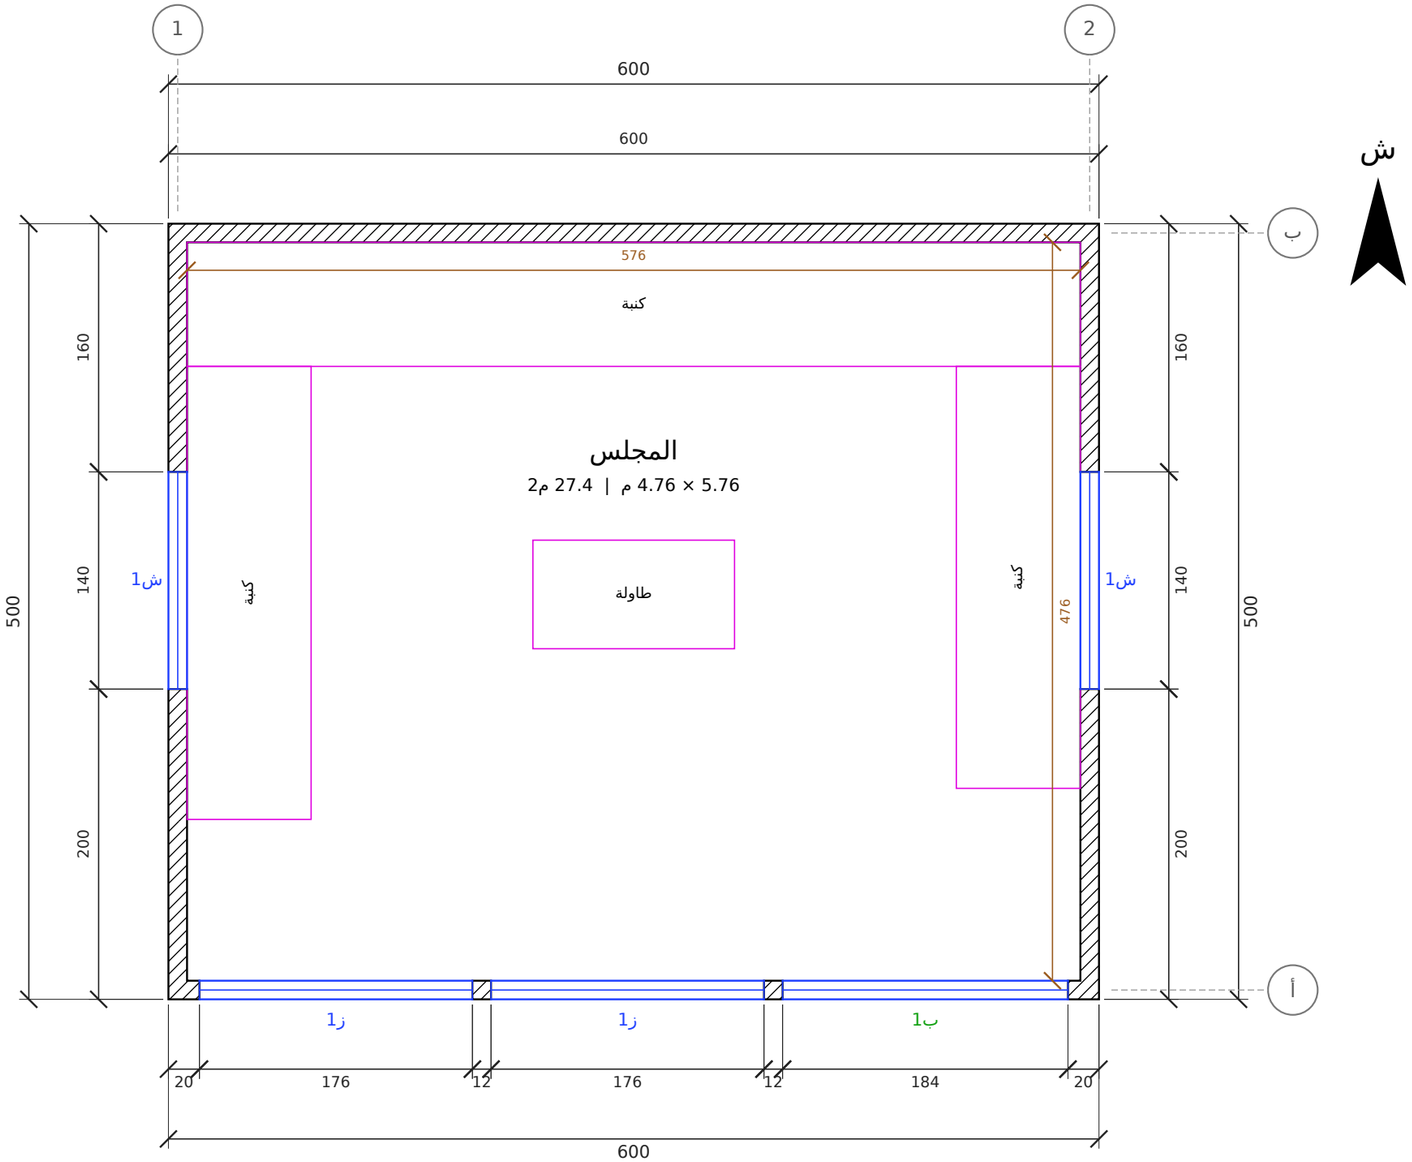


المشروع / العميل	عنوان اللوحة	المقياس	التاريخ	رقم اللوحة
مجلس حديث بواجهة زجاج كاملة — 6.00 × 5.00 = 30 م² **عميل — مجلس حديث 5×6**	**المسقط الأفقي**	**1:50**	**2026-10-23**	**W-02 (2/11)**

مصنع وتد الأخشاب
Watad Wood Factory

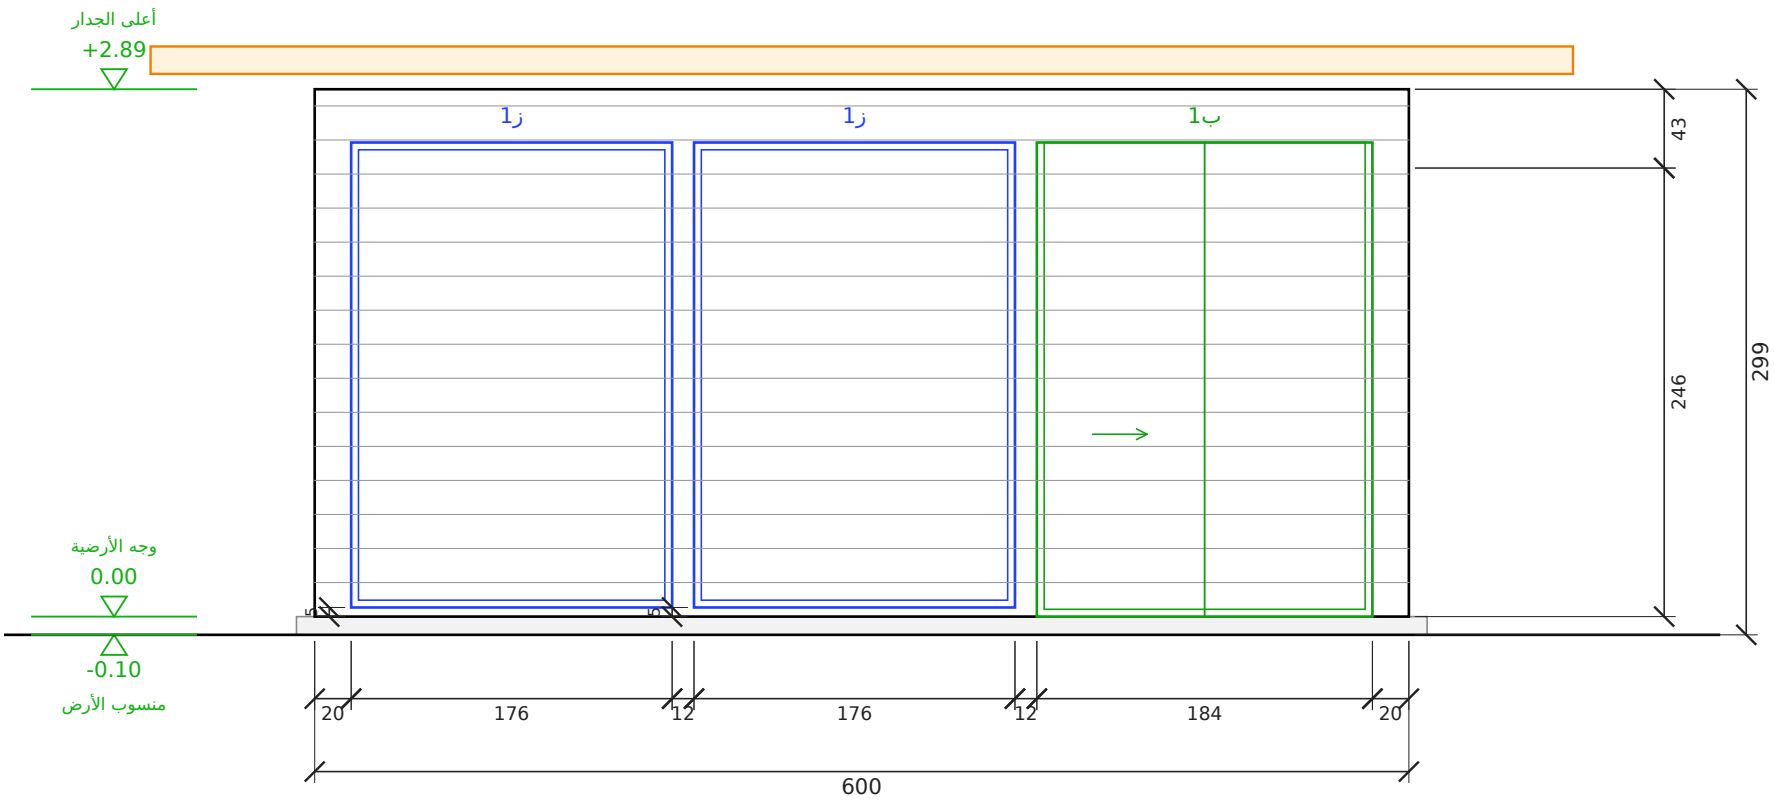

الواجهة الأمامية (زجاج كامل)


مقياس 1:50 | الوحدة: سم

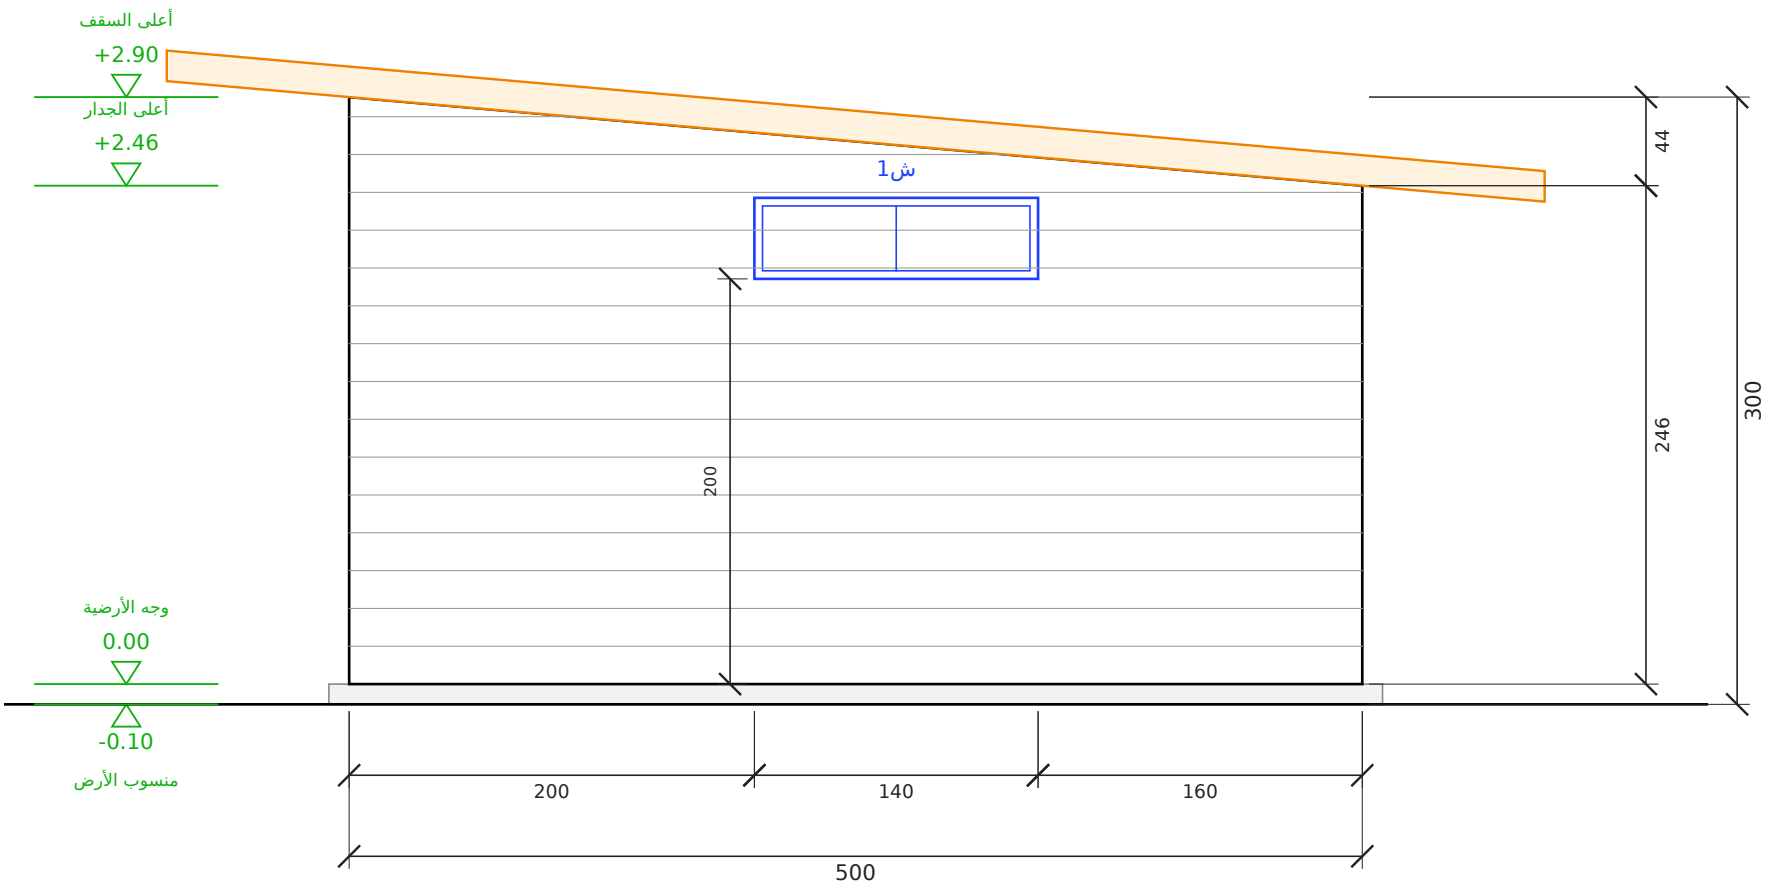

الواجهة الشرقية


مقياس 1:50 | الوحدة: سم

المشروع / العميل	عنوان اللوحة	المقياس	التاريخ	رقم اللوحة
مصنع وتد الأخشاب Watad Wood Factory **مجلس حديث بواجهة زجاج كاملة — 6.00 × 5.00 = 30 م²** **عميل — مجلس حديث 5×6**	**الواجهة الأمامية (زجاج كامل) والواجهة الشرقية**	**1:50**	**2026-10-23**	**W-03 (3/11)**

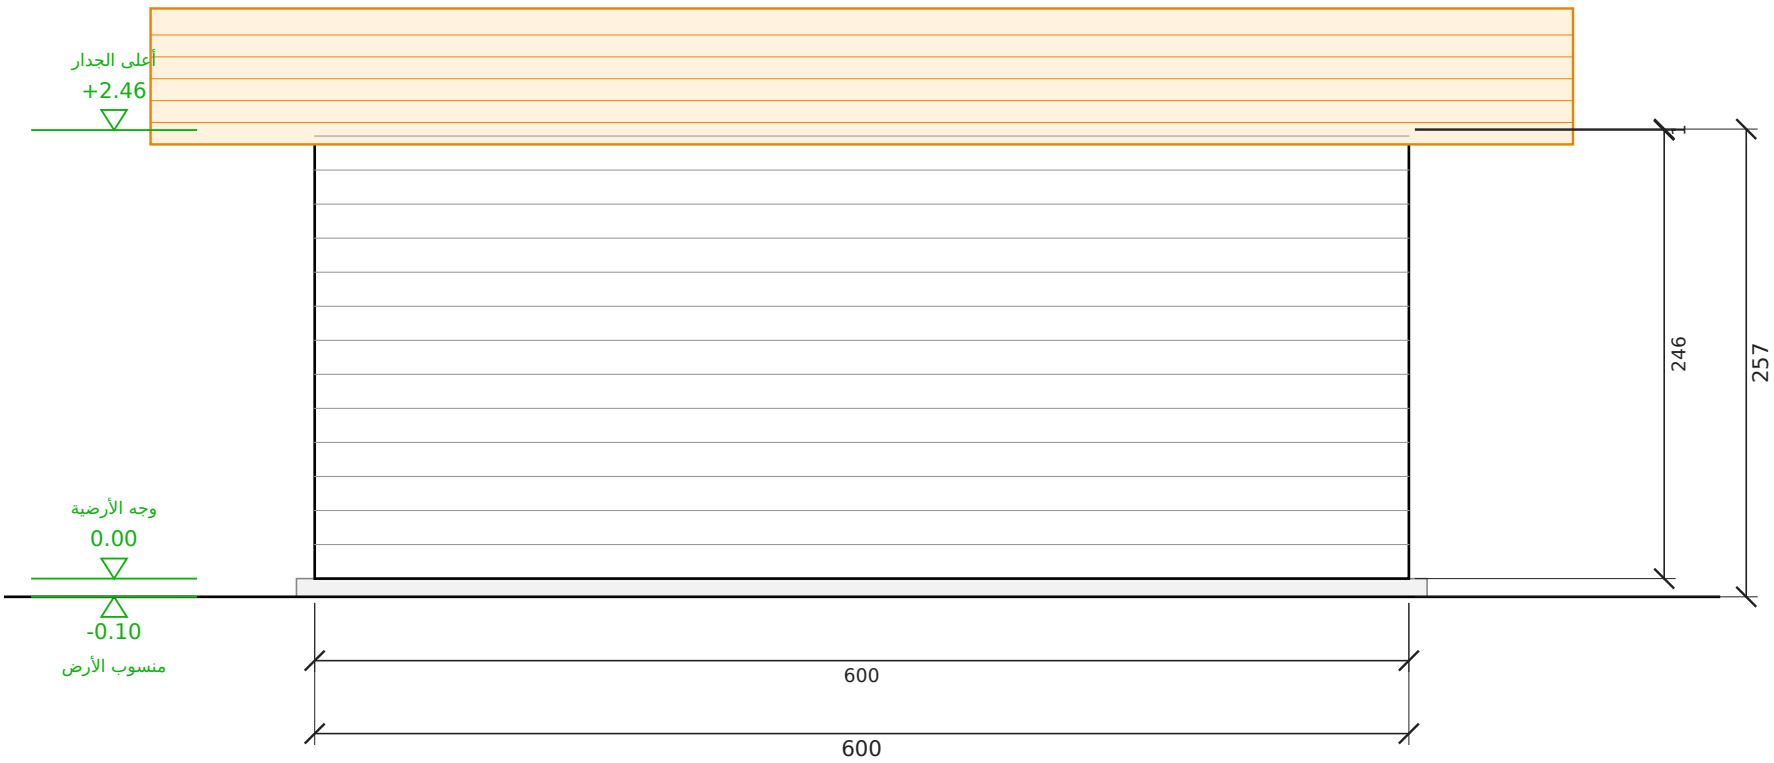

الواجهة الخلفية

مقياس 1:50 | الوحدة: سم

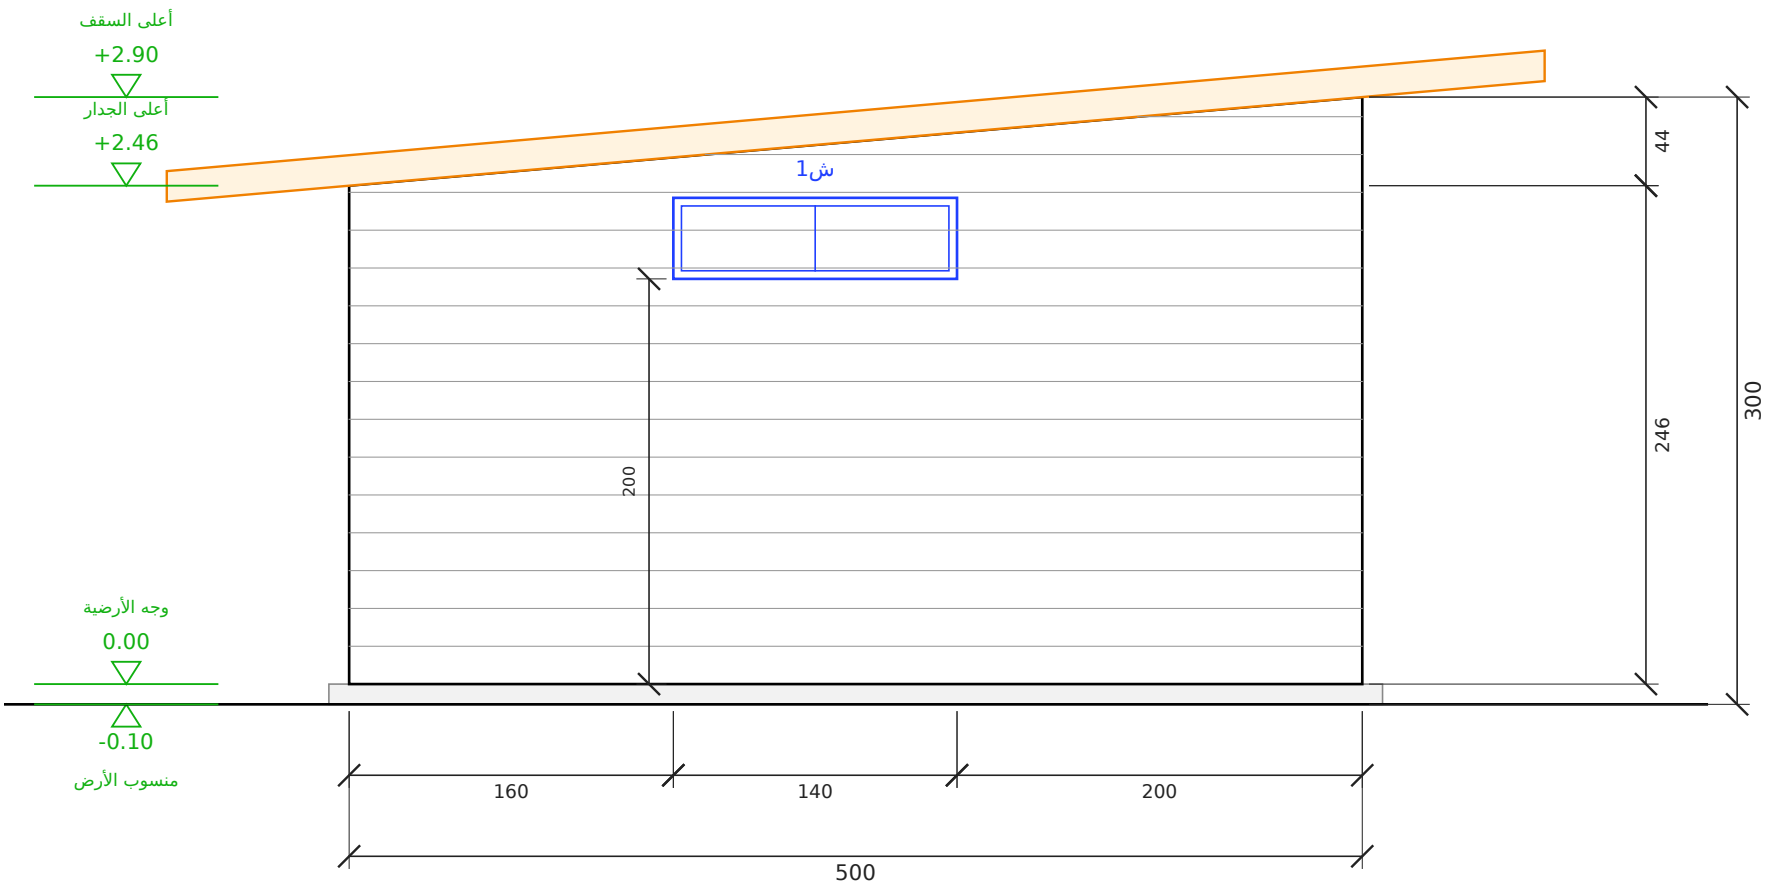


الواجهة الغربية

مقياس 1:50 | الوحدة: سم


المشروع / العميل	عنوان اللوحة	المقياس	التاريخ	رقم اللوحة
مجلس حديث بواجهة زجاج كاملة — 6.00 × 5.00 = 30 م² عميل — مجلس حديث 5×6	الواجهة الخلفية والواجهة الغربية	1:50	2026-10-23	W-04 (4/11)

مصنع وتد الأخشاب
Watad Wood Factory


مسقط السقف (مائل باتجاه واحد)
رفرف 90 سم من كل جهة | مقياس 1:50

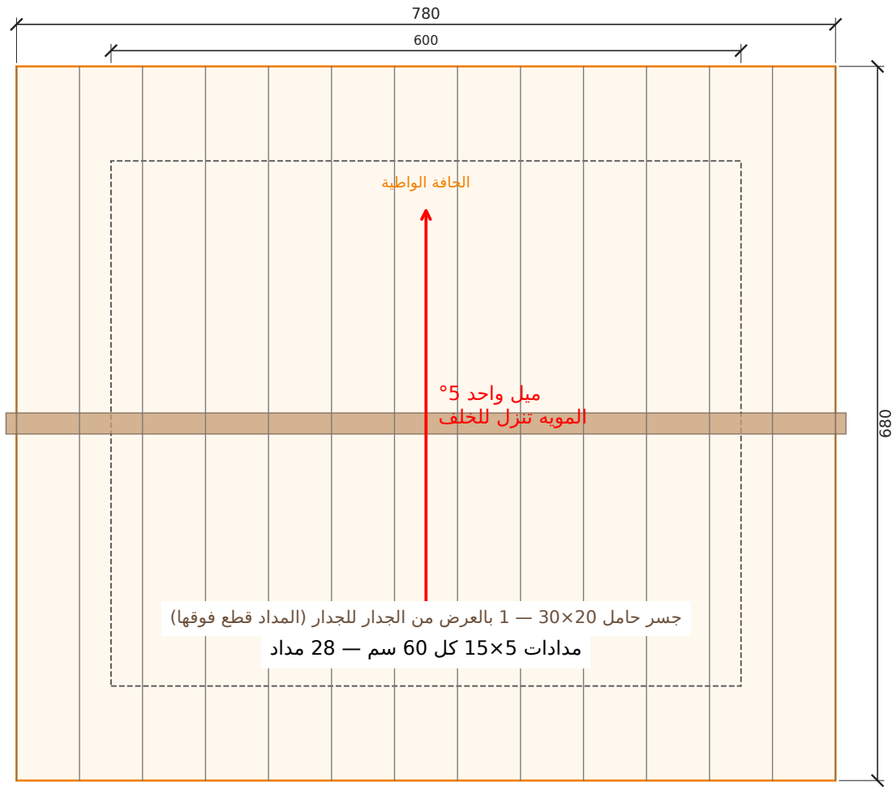

قطاع عرضي أ-أ
مقياس 1:50 | الوحدة: سم

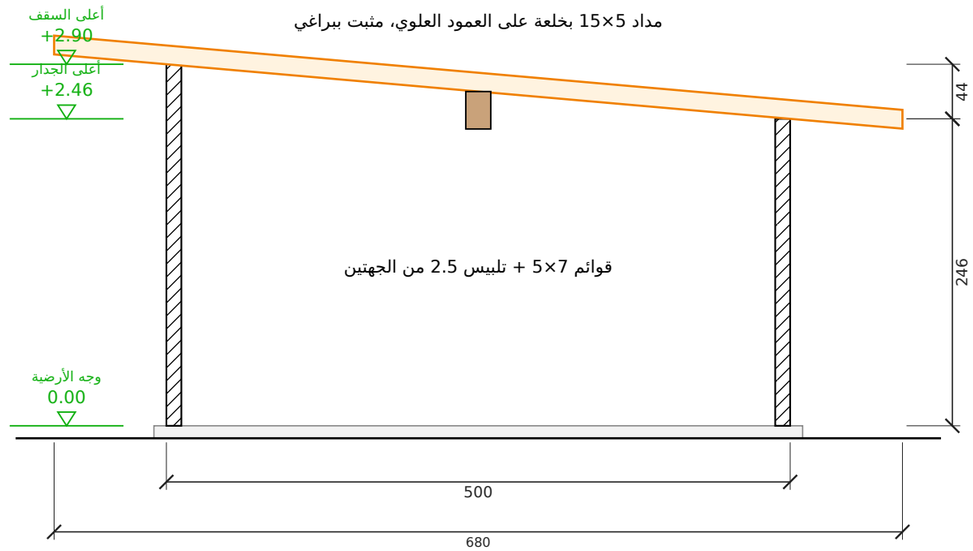

تفصيلة جلوس المداد على العلوي (1:5)

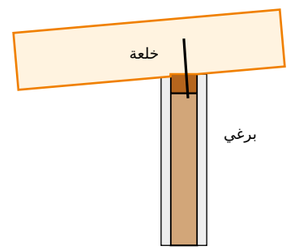

المشروع / العميل **مجلس حديث بواجهة زجاج كاملة — 6.00 × 5.00 = 30 م²** **عميل — مجلس حديث 5×6**	عنوان اللوحة **مسقط السقف والقطاع**	المقياس **1:50**	التاريخ **2026-10-23**	رقم اللوحة **W-05 (5/11)**

مصنع وتد الأخشاب
Watad Wood Factory

جدول مقاسات الأبواب والشبابيك
مقاس الفتحة الصافي في الجدار - الوحدة: سم

الرمز	النوع	العرض (سم)	الارتفاع (سم)	ارتفاع الجلسة (سم)	العدد	الموقع
ب1	باب مزدوج	184	260	-	1	الأمامية (زجاج كامل)
ز1	شباك	176	255	5	2	الأمامية (زجاج كامل) 2
ش1	شباك	140	40	200	2	الشرقية - الغربية

الإجمالي: أبواب 1 - شبابيك 4

جدول المساحات وبيانات المشروع


بيانات المشروع

البند	البيان
المشروع	مجلس حديث بواجهة زجاج كاملة — 6.00 × 5.00 = 30 م²
العميل	عميل — مجلس حديث 5×6
الموقع	—
الاستخدام	مجلس
التاريخ	2026-10-23
نظام البناء	هيكل خشب 5×7 + تلبيس 2.5 سم من الجهتين
السقف	مائل باتجاه واحد 5° — صاج معدني + عزل مائي


جدول المساحات

م	الفراغ	الأبعاد (م)	المساحة (م2)
1	المجلس	5.76 × 4.76	27.42
	المساحة الصافية الداخلية		**27.42**
	المساحة الإجمالية المبنية	**6.00 × 5.00**	**30.00**

تأطير جدار جنوب — الطول 588 سم، الارتفاع 290 سم

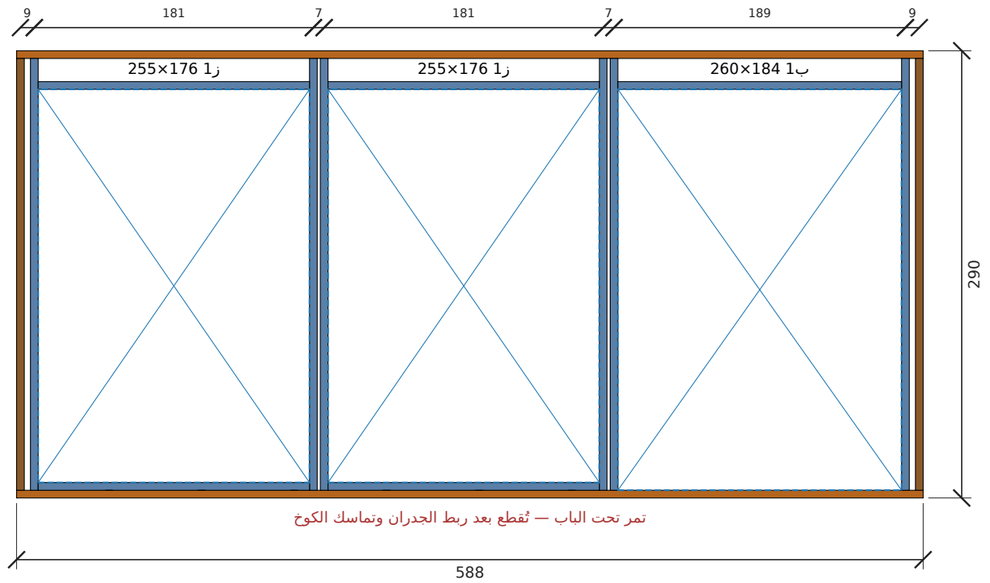

تأطير جدار شرق — الطول 488 سم، الارتفاع 246 سم

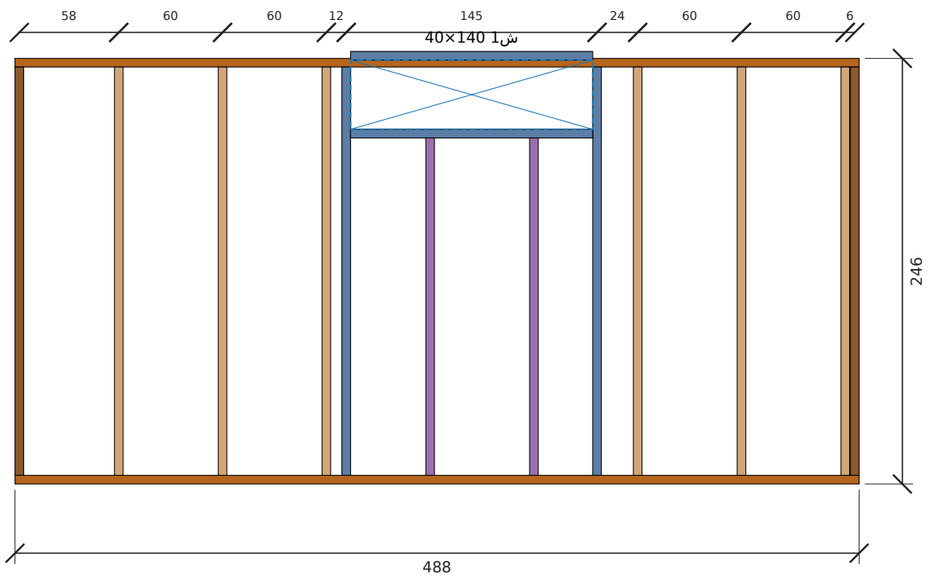


قاعدة سفلية | علوي | عمود | عمود زاوية | جنب فتحة | رأس فتحة | جلسة شباك | عمود قصير


المشروع / العميل	عنوان اللوحة	المقياس	التاريخ	رقم اللوحة
مجلس حديث بواجهة زجاج كاملة — 6.00 × 5.00 = 30 م² **عميل — مجلس حديث 5×6**	**لوحات التأطير (للورشة)**	**—**	**2026-10-23**	**W-08 (8/11)**

مصنع وتد الأخشاب
Watad Wood Factory

تأطير جدار شمال — الطول 588 سم، الارتفاع 246 سم

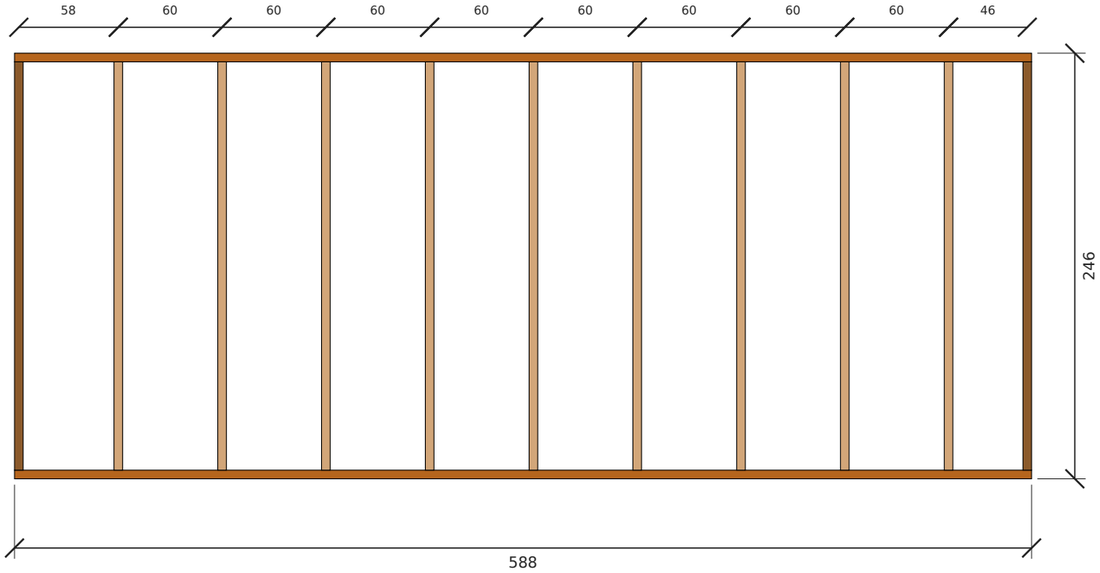

تأطير جدار غرب — الطول 488 سم، الارتفاع 246 سم

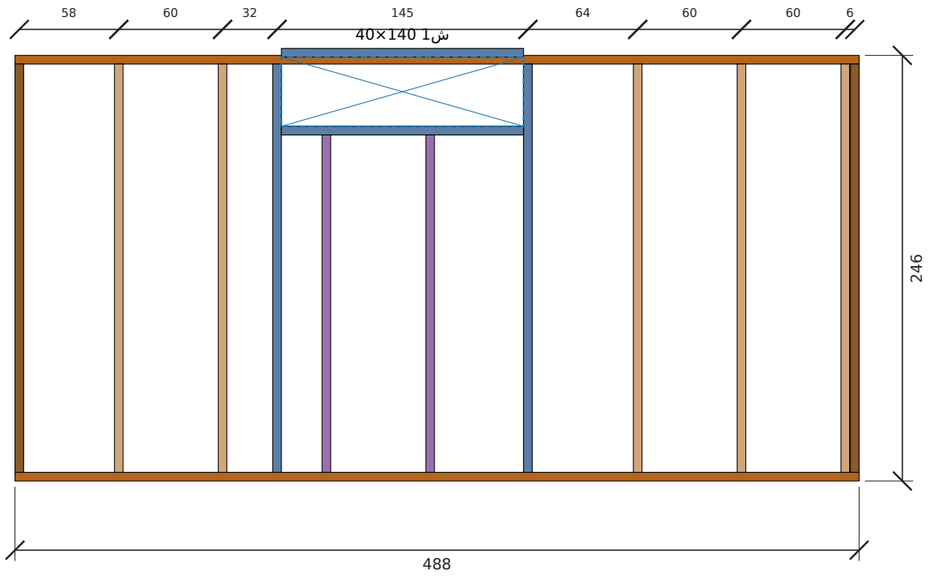

قاعدة سفلية | علوي | عمود | عمود زاوية | جنب فتحة | رأس فتحة | جلسة شباك | عمود قصير

المشروع / العميل	عنوان اللوحة	المقياس	التاريخ	رقم اللوحة
مجلس حديث بواجهة زجاج كاملة — 6.00 × 5.00 = 30 م² **عميل — مجلس حديث 5×6**	**لوحات التأطير (للورشة)**	**—**	**2026-10-23**	**W-09 (9/11)**

مصنع وتد الأخشاب
Watad Wood Factory

جدول الكميات وخطة تقطيع الطبليات

البند	القيمة
الارتفاع المطلوب / المعتمد	246 / 246 سم
السقف	مائل باتجاه واحد 5° — أعلى نقطة 290 سم من وجه الأرضية
المدادات 5×15	28 مداد (14 خط × قطعتين موصولة فوق الجسر الحامل بتراكب 60 سم) × حتى 371 سم — من طبلية 480
طبليات الطريقة الأولى (مداد + عمود)	28 طبلية × 480 سم
طبليات الطريقة الثانية (3 أعمدة)	8 طبلية × 320 سم
إجمالي الطبليات 5×22.5	36
إجمالي قطع 5×7	65
قائمة تقطيع 5×7	588سم×4 | 488سم×4 | 280سم×8 | 236سم×30 | 195سم×4 | 184سم×1 | 176سم×4 | 140سم×4 | 5سم×6
ألواح تلبيس 2.5 سم	148 لوح × 400 سم (مجموع الصفوف 442.9 م، 8 وجه)
أسمنت بورد 12 مم (122×244)	0 لوح (داخل دورات المياه)
العزل	بدون (غير مطلوب)
القاعدة	قواعد حديد 10 سم من المصنع (متنقل — بدون صبة)

مراجعة التصميم مقابل قواعد المصنع

النوع	البند	التفاصيل	المقترح
ملاحظة	بحر المدادات	أطول بحر بدون جدار داخلي يحمل المداد: جهة أ: 500 سم. يحتاج رقم المصنع لأقصى بحر مسموح لتحديد المدادات اللي تُقوّى 20×5.	
ملاحظة	الصبة والدرج	ارتفاع الصبة 10 سم ← 1 درجة بقائمة 10.0 سم. بارتفاع 20 سم ما يطلع إلا درجة وحدة؛ للدكة المرتفعة 45 سم = 3 درجات.	
ملاحظة	مناسيب رؤوس الفتحات	رؤوس الأبواب والشبابيك على مناسيب مختلفة: 240، 260 سم.	
تنبيه	ميل سقف خفيف (بموافقة المصنع)	ميل 5° أقل من 20° — يصرّف باتجاه واحد بس يحتاج تغطية صاج معدني (مو قرميد) وعزل مائي تحت الصاج ووصلات مختومة.	صاج معدني بطول واحد من الحافة العالية للواطية بدون وصلات عرضية.
سؤال	يحتاج تأكيد	أقصى بحر للمداد بدون جدار داخلي قبل إضافة تقوية 5×7 (مداد 20×5)؟	
سؤال	يحتاج تأكيد	التغطية الصافية للوح التلبيس بعد التعشيق (مستنتجة مؤقتاً 18.67 سم من 280/15)؟	
سؤال	يحتاج تأكيد	هل يوضع أعمدة قصيرة فوق رأس الشباك/الباب إلى العلوي؟	
سؤال	يحتاج تأكيد	مكان الوصلة في القاعدة والعلوي إذا الجدار أطول من الطبلية؟	