
المنظور ثلاثي الأبعاد والمواد

النمط: جوزي غامق + إطارات سوداء — رندر واقعي بخامات حقيقية

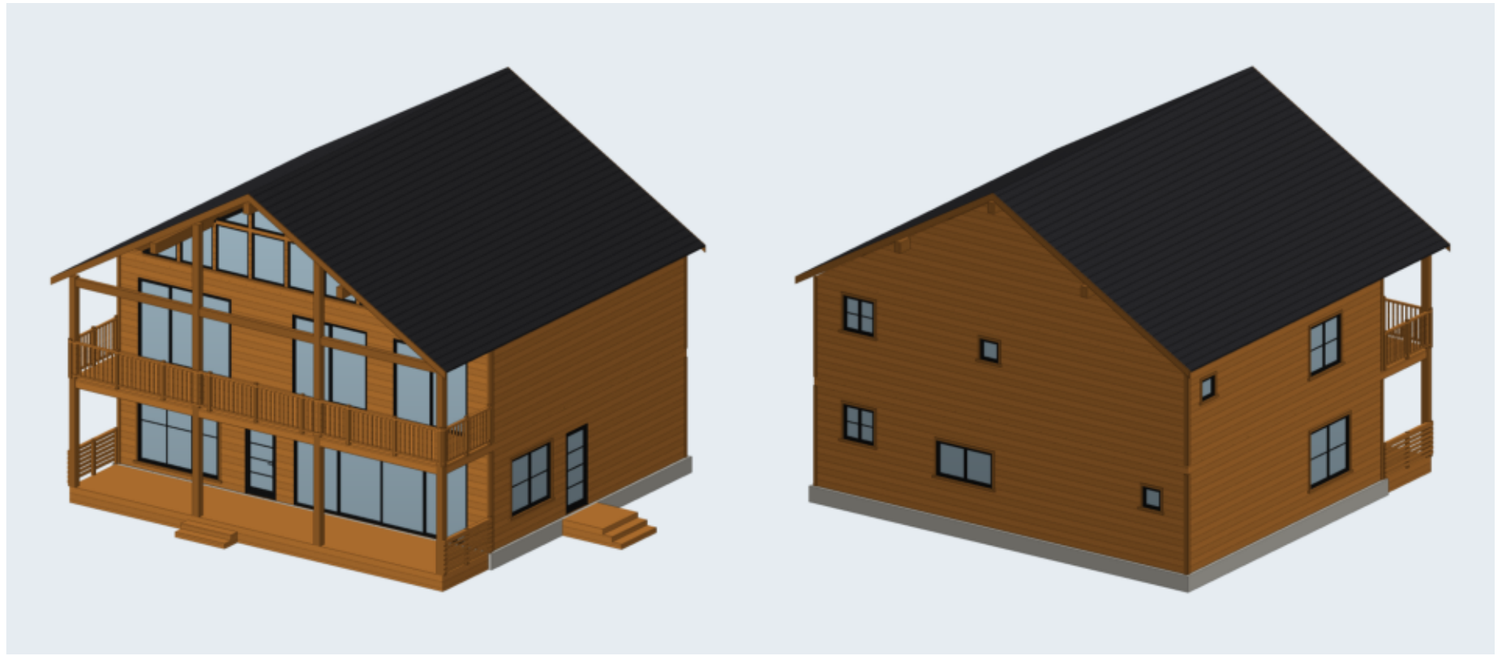

جدول المواد والألوان

الخشب / الصبغة

صبغة عسلي / سيدر

القرميد

قرميد رمادي غامق

الزجاج

زجاج شفاف

إطارات الشبابيك والأبواب

إطار ألمنيوم أسود

الكنار والزوايا

نفس الصبغة أغمق درجة


الصبة

خرسانة 45 سم


الدربزين: ألواح أفقية متقاربة (عصري)

تقسيم الشبابيك: بدون | الباب الرئيسي: زجاج بتقسيمات (فرنسي)

أنواع الدربزين المعتمدة (من مشاريع المصنع)

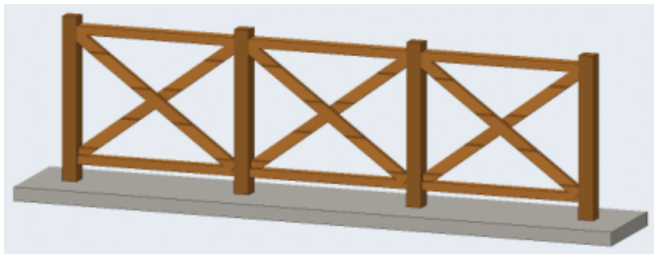

تقاطع X (صورة 5)

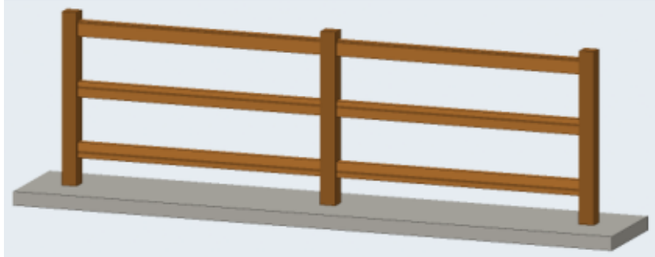

3 مرابيع أفقية (صورة 2)




قوائم رأسية متقاربة (صورة 1)

المشروع / العميل	عنوان اللوحة	المقياس	التاريخ	رقم اللوحة
فيلا خشب دورين بواجهة زجاج وشرفة — 12.00 × 9.00 م **عميل — فيلا دورين**	**المنظور والمواد**	**1:50**	**2026-10-31**	**W-01 (1/21)**

مصنع وتد الأخشاب
Watad Wood Factory

المسقط الأفقي مع الفرش — الدور الأرضي

الأبعاد بالسنتيمتر - الجدران: قوائم 7×5 + تلبيس 2.5 من الجهتين (12 سم) | منسوب الأرضية +0.00

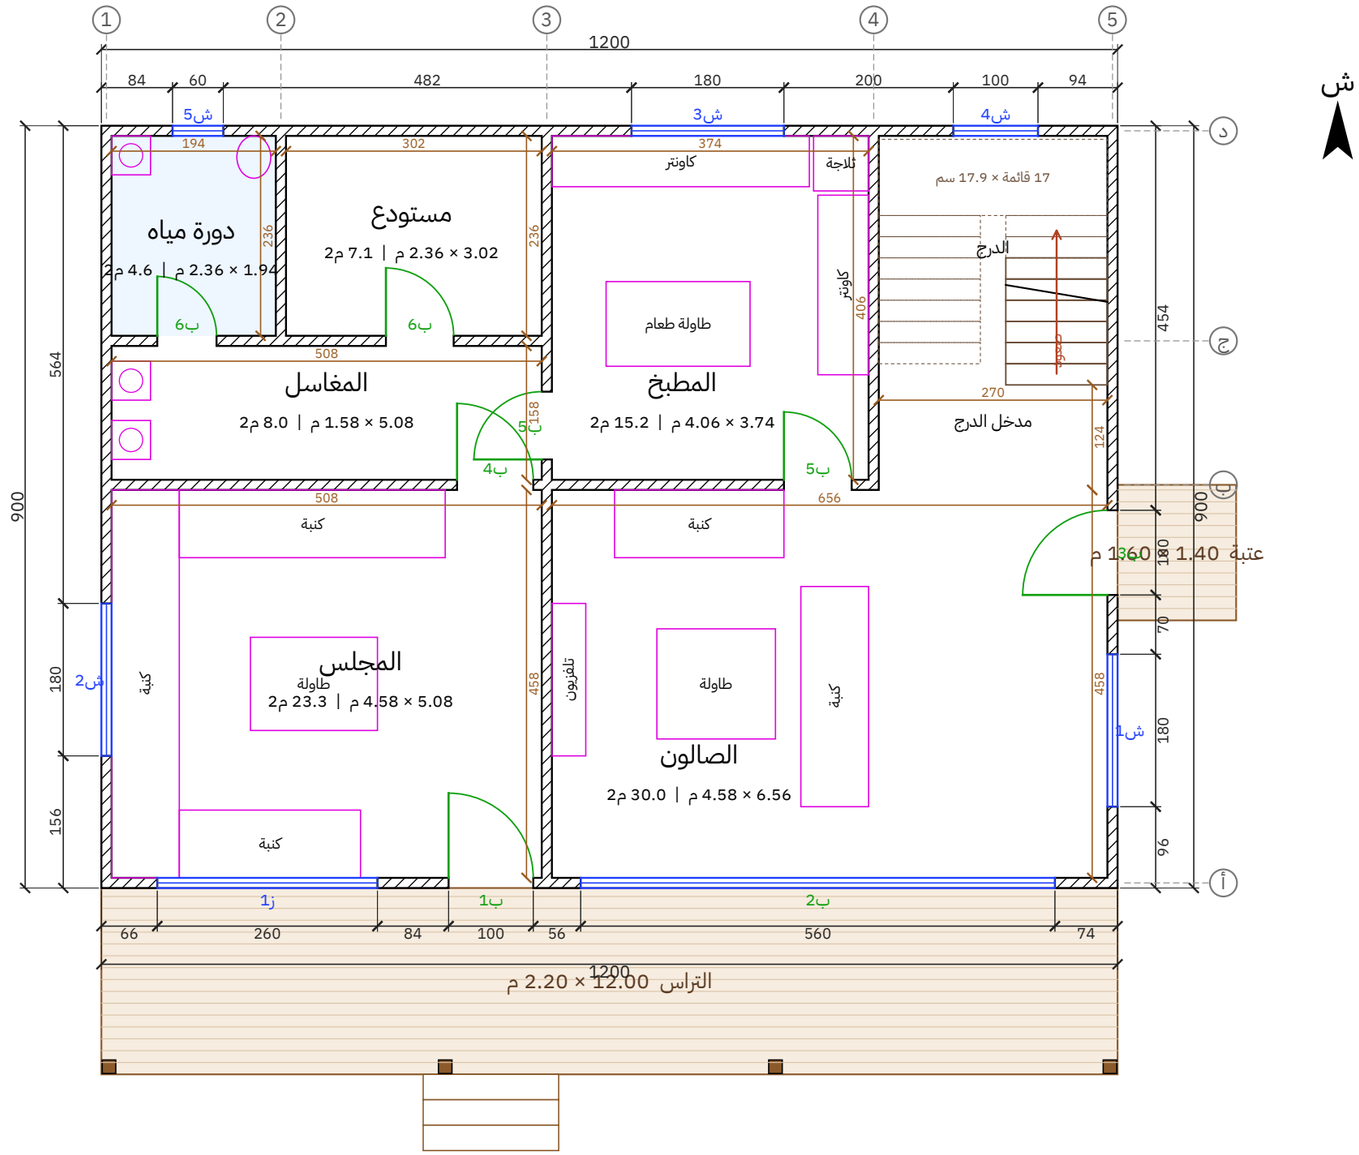


المشروع / العميل	عنوان اللوحة	المقياس	التاريخ	رقم اللوحة
فيلا خشب دورين بواجهة زجاج وشرفة — 12.00 × 9.00 م عميل — فيلا دورين	المسقط الأفقي — الدور الأرضي	1:50	2026-10-31	W-02 (2/21)

مصنع وتد الأخشاب
Watad Wood Factory


المسقط الأفقي مع الفرش — الدور الأول

الأبعاد بالسنتيمتر - الجدران: قوائم 7×5 + تلبيس 2.5 من الجهتين (12 سم) | منسوب الأرضية +3.05

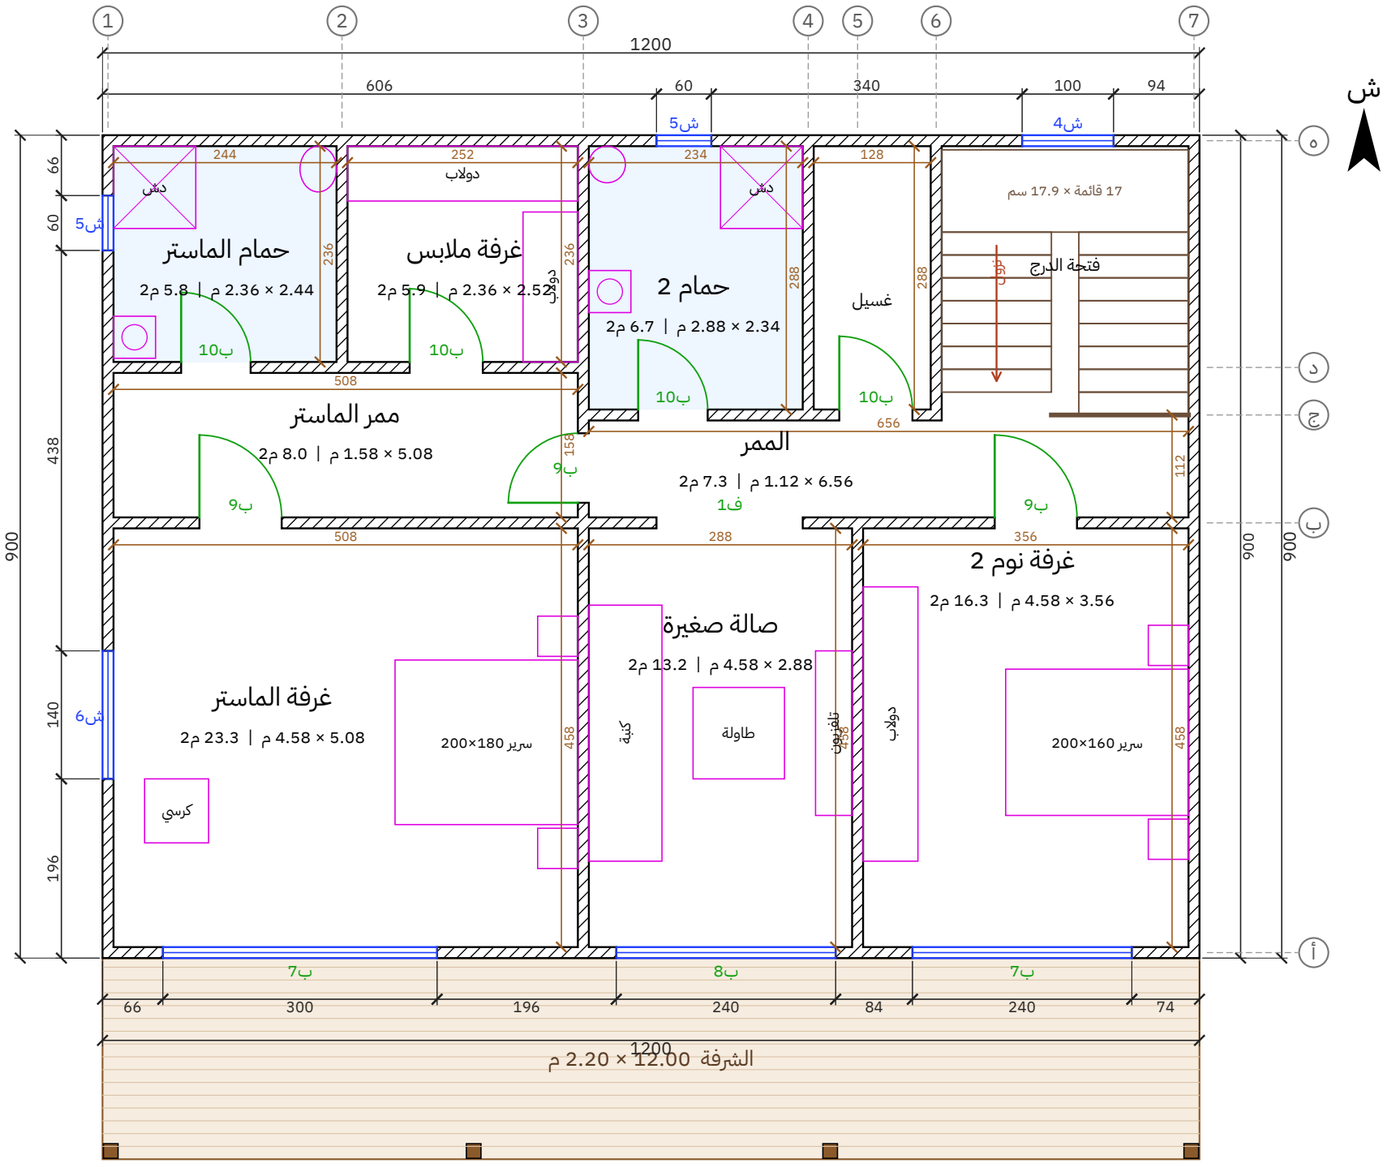


المشروع / العميل	عنوان اللوحة	المقياس	التاريخ	رقم اللوحة
فيلا خشب دورين بواجهة زجاج وشرفة — 12.00 × 9.00 م عميل — فيلا دورين	المسقط الأفقي — الدور الأول	1:50	2026-10-31	W-03 (3/21)

مصنع وتد الأخشاب
Watad Wood Factory

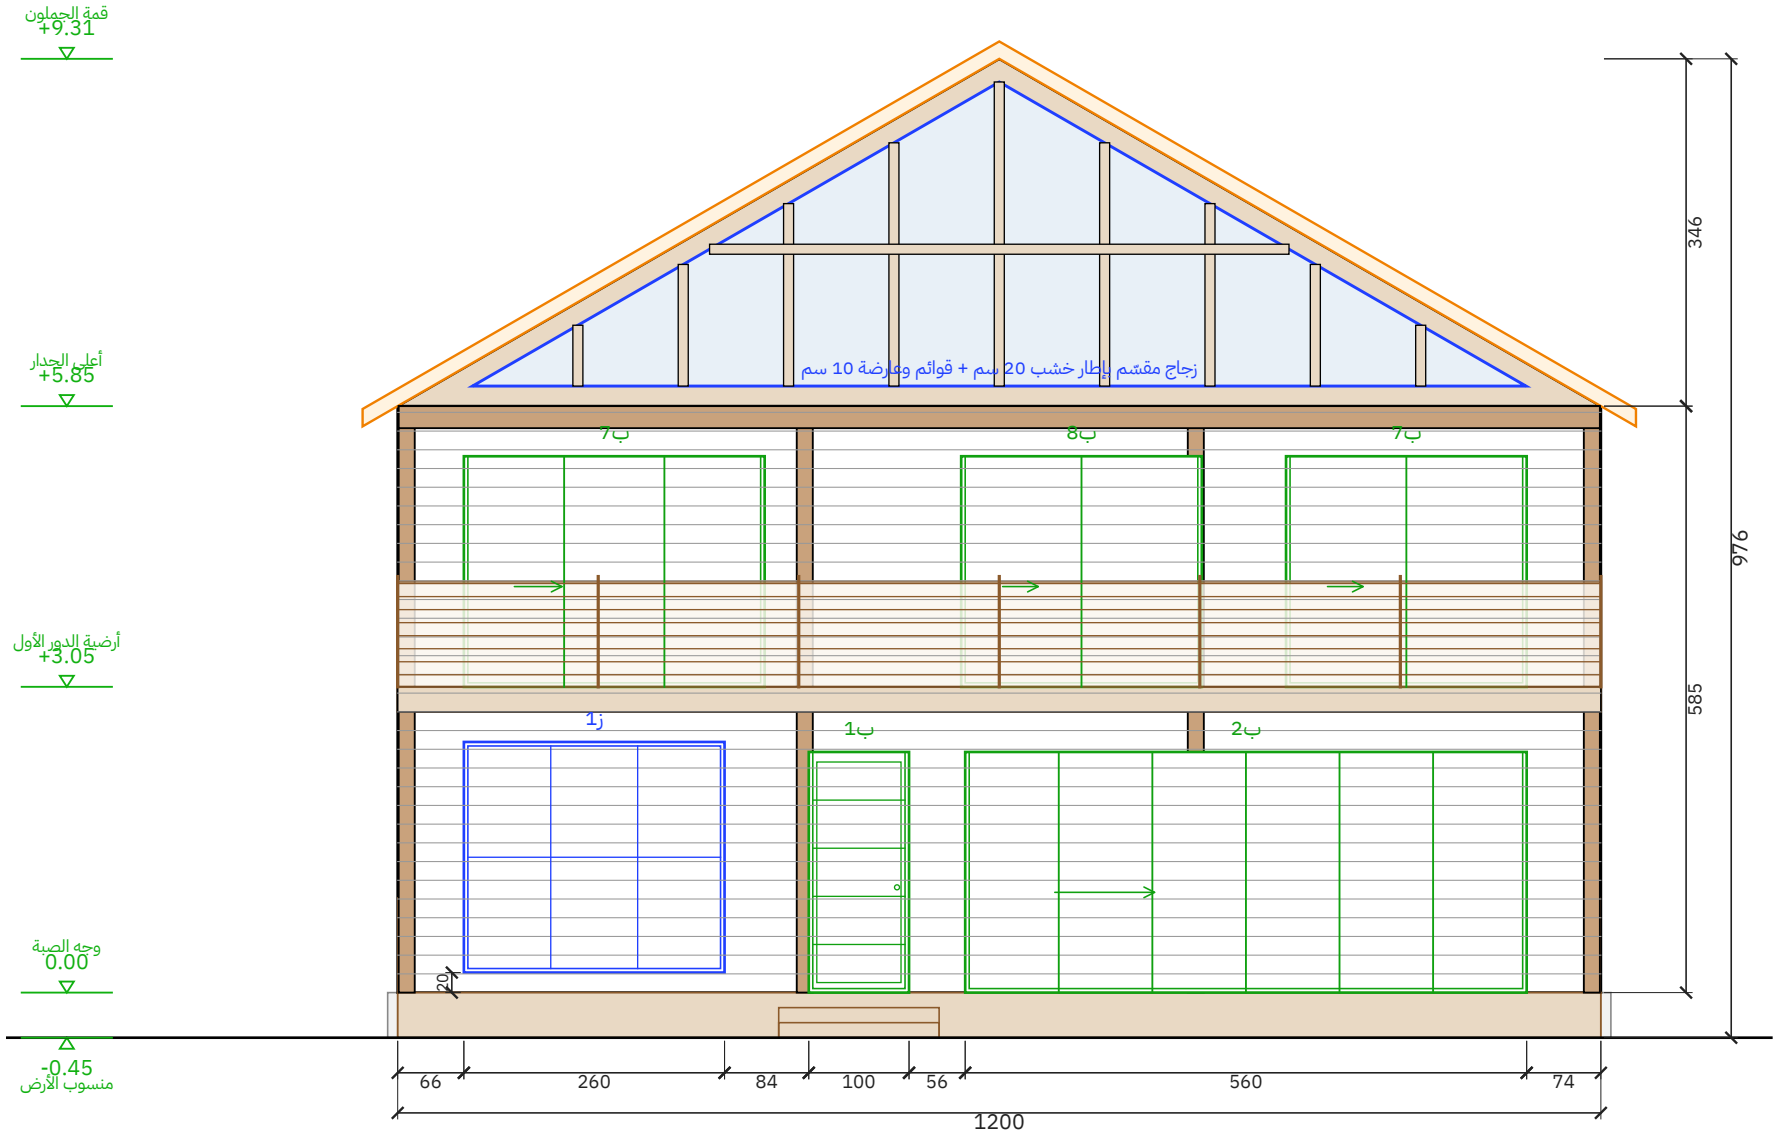

الواجهة الأمامية (زجاج)

مقياس 1:50 | الوحدة: سم

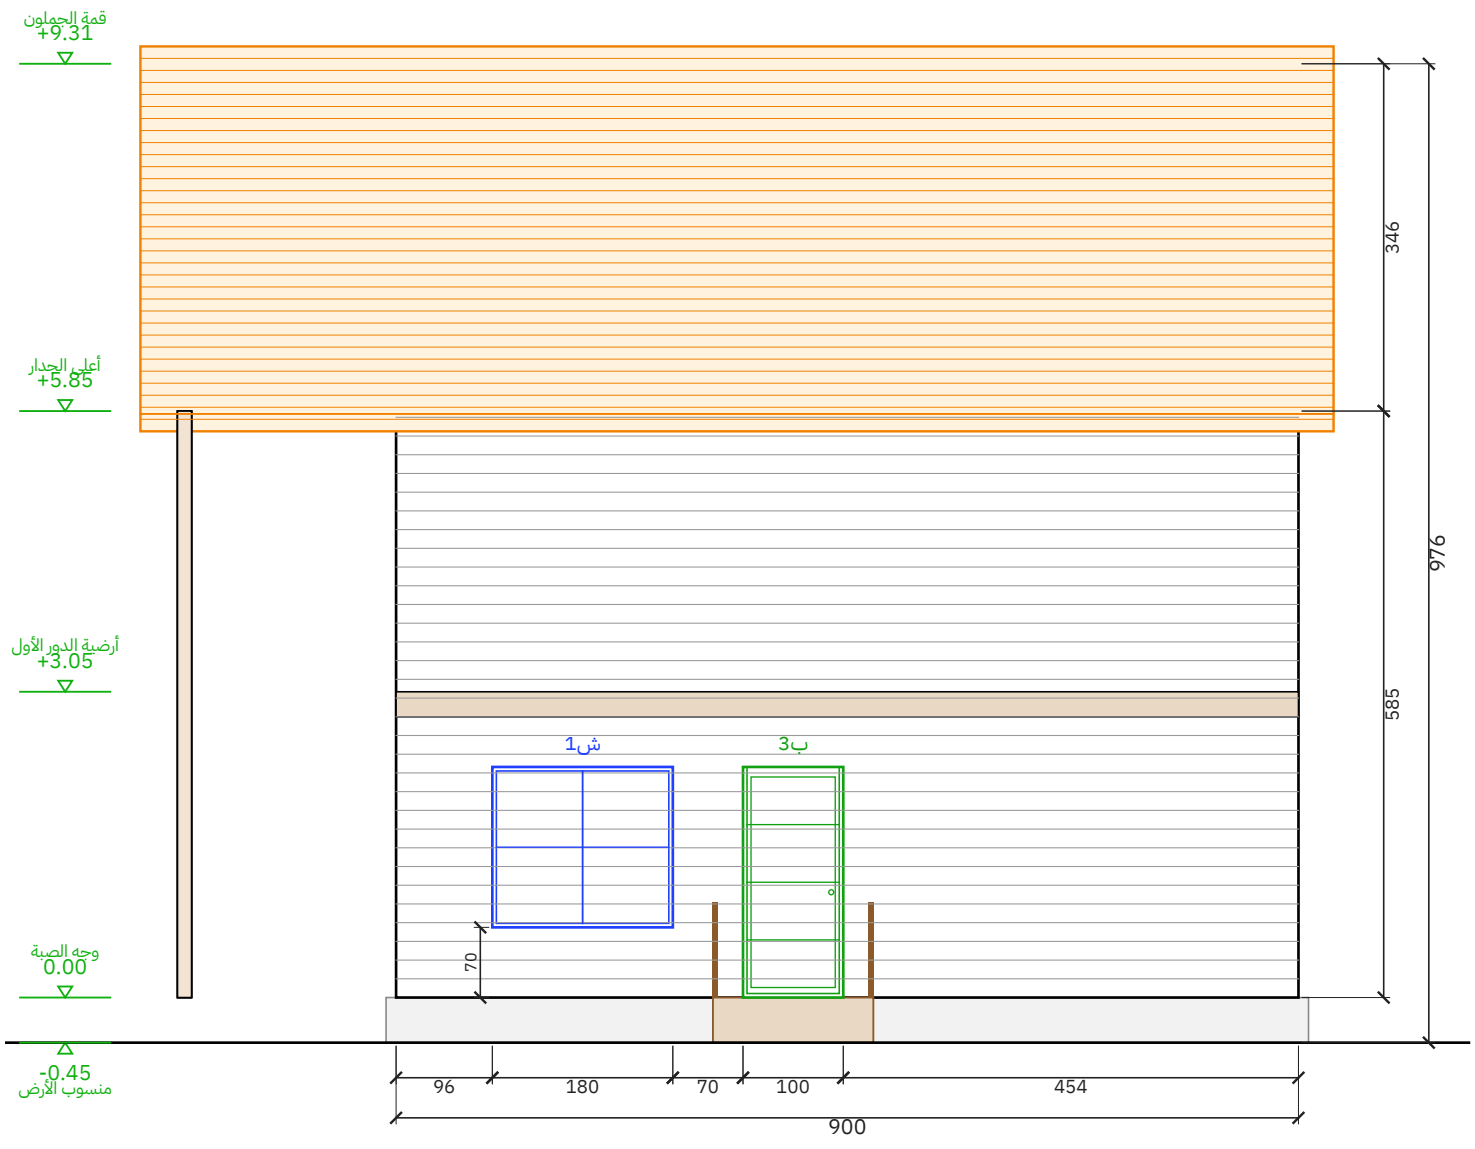


الواجهة الشرقية

مقياس 1:50 | الوحدة: سم


المشروع / العميل	عنوان اللوحة	المقياس	التاريخ	رقم اللوحة
فيلا خشب دورين بواجهة زجاج وشرفة – 12.00 × 9.00 م عميل – فيلا دورين	الواجهة الأمامية (زجاج) والواجهة الشرقية	1:50	2026-10-31	W-04 (4/21)

مصنع وتد الأخشاب
Watad Wood Factory

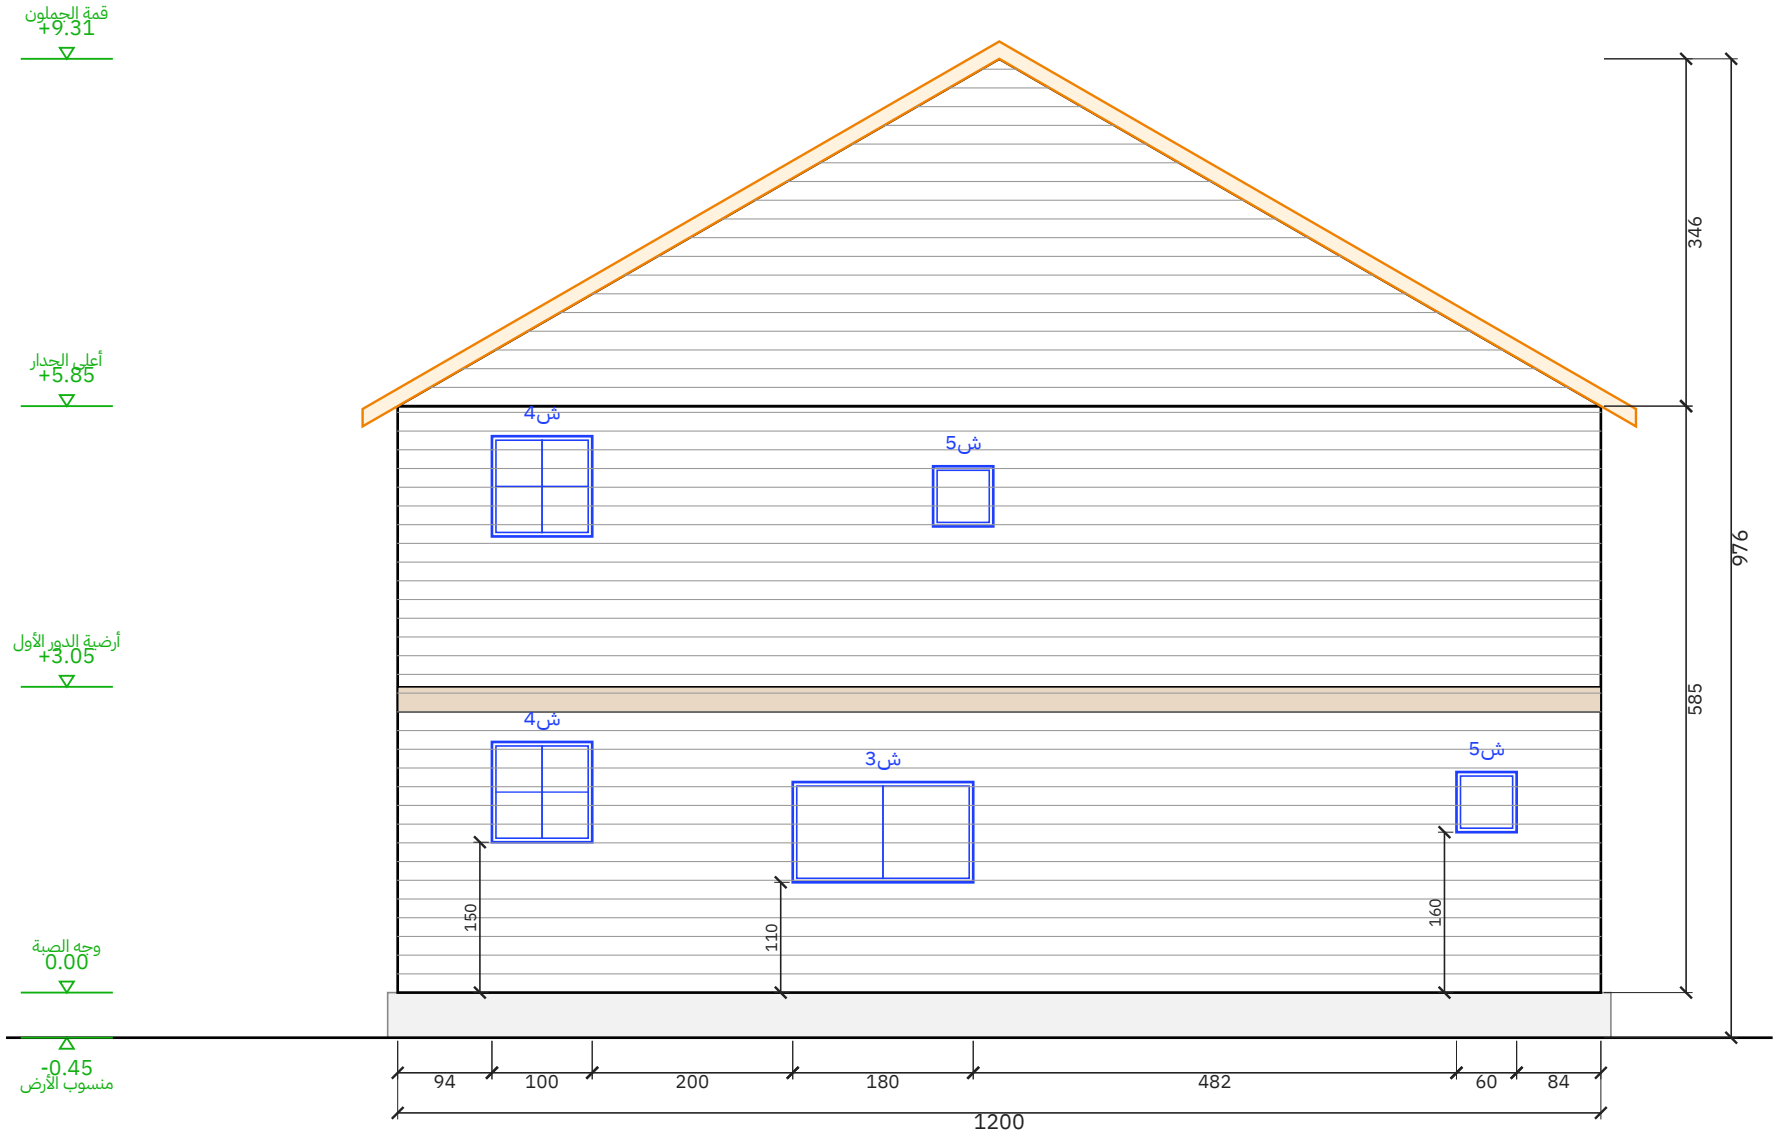

الواجهة الخلفية

مقياس 1:50 | الوحدة: سم

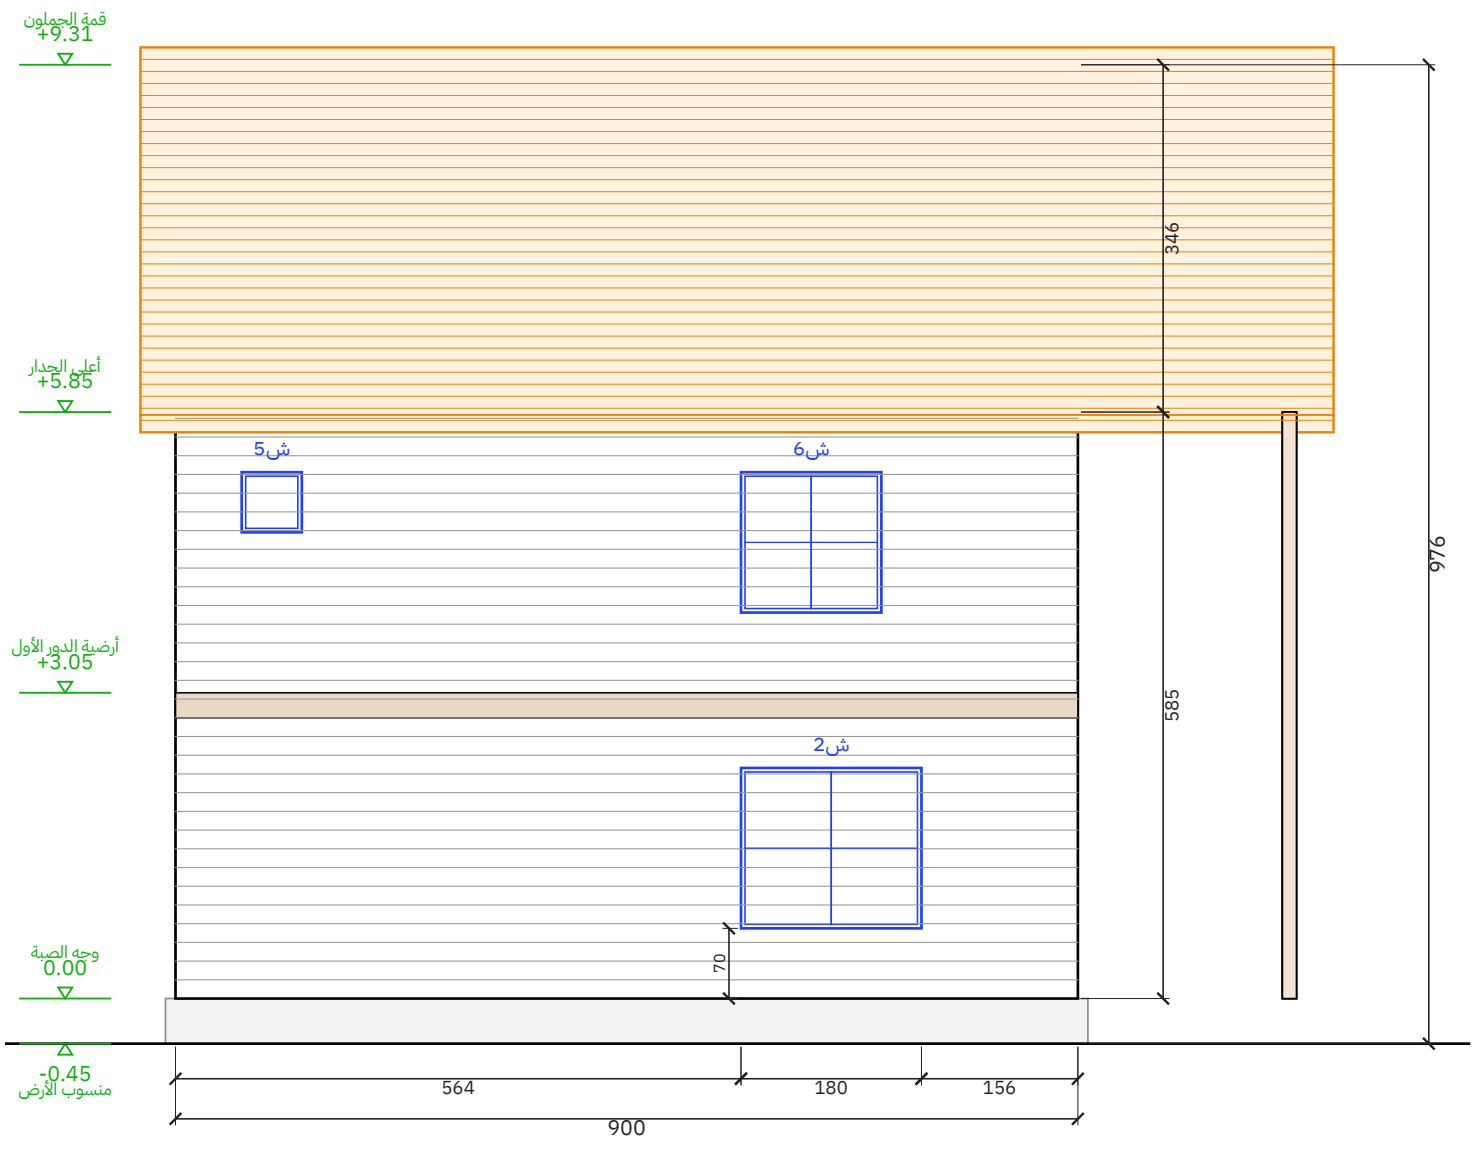


الواجهة الغربية

مقياس 1:50 | الوحدة: سم

المشروع / العميل	عنوان اللوحة	المقياس	التاريخ	رقم اللوحة
مصنع وتد الأخشاب Watad Wood Factory فيلا خشب دورين بواجهة زجاج وشرفة — 12.00 × 9.00 م عميل — فيلا دورين	الواجهة الخلفية والواجهة الغربية	1:50	2026-10-31	W-05 (5/21)


مسقط السقف (جملون)

رفرف 35 سم من كل جهة | مقياس 1:50

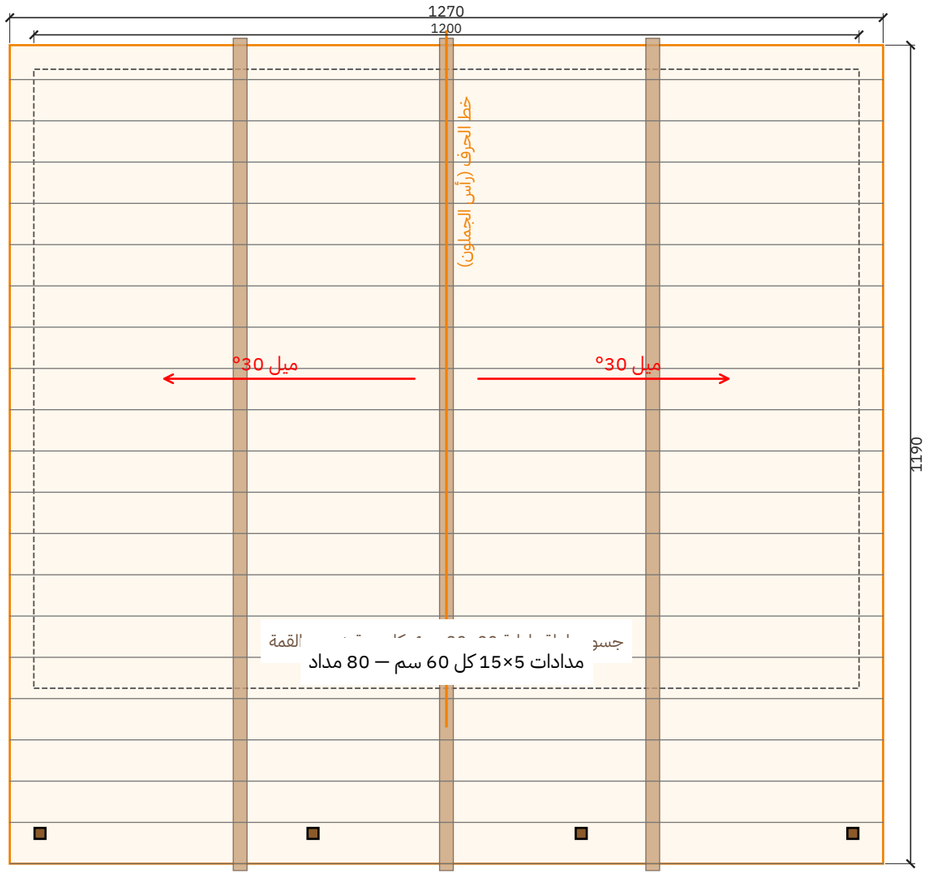


قطاع عرضي أ-أ

مقياس 1:50 | الوحدة: سم

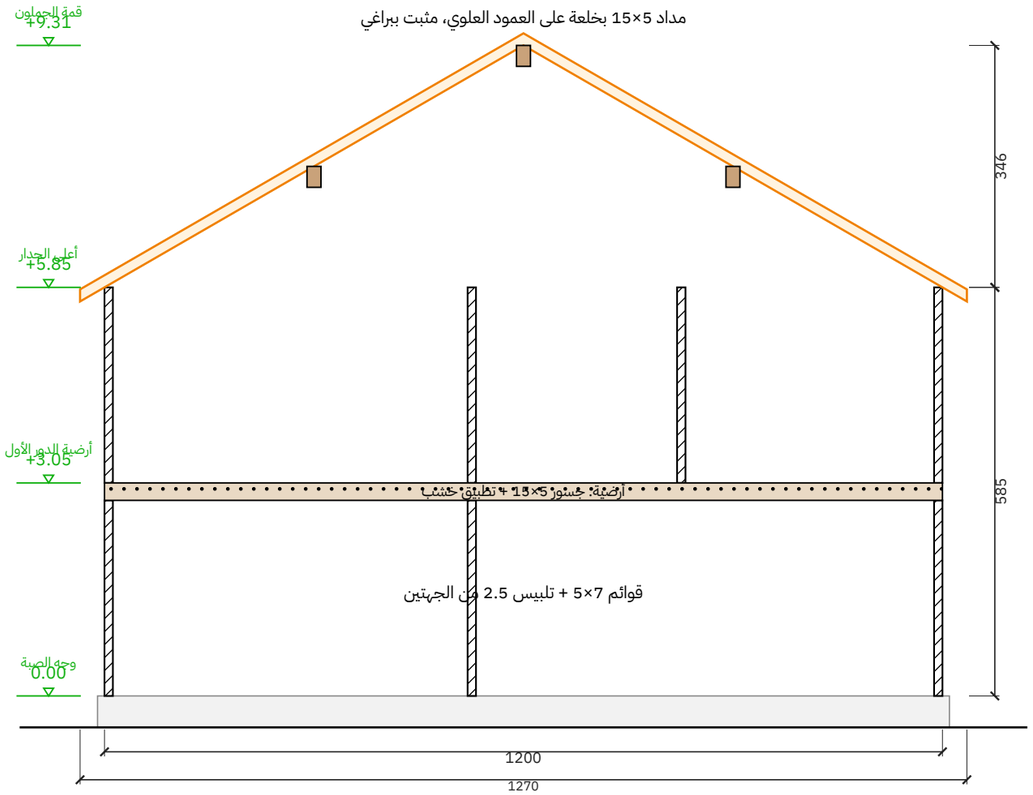

تفصيلة جلوس المداد على العلوي (1:5)

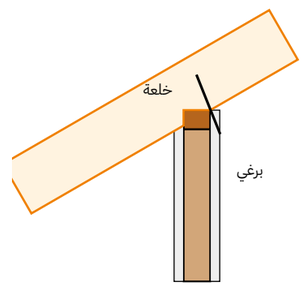

علوي 7×5 على قائم 7×5

المشروع / العميل	عنوان اللوحة	المقياس	التاريخ	رقم اللوحة
فيلا خشب دورين بواجهة زجاج وشرفة — 12.00 × 9.00 م عميل — فيلا دورين	مسقط السقف والقطاع	—	2026-10-31	W-06 (6/21)

مصنع وتد الأخشاب
Watad Wood Factory

جدول مقاسات الأبواب والشبابيك

مقاس الفتحة الصافي في الجدار - الوحدة: سم

الرمز	النوع	العرض (سم)	الارتفاع (سم)	ارتفاع الجلسة (سم)	العدد	الموقع
ب1	باب	100	240	-	1	الأمامية (زجاج)
ب10	باب	76	210	-	2	حمام الماستر - حمام 2
ب10	باب	80	210	-	2	غرفة الملابس - الغسيل
ب2	باب	560	240	-	1	الأمامية (زجاج)
ب3	باب	100	230	-	1	الشرقية
ب4	باب	90	220	-	1	المجلس — المغاسل
ب5	باب	80	220	-	2	المطبخ — الصالون - المطبخ — المغاسل
ب6	باب	70	210	-	1	دورة المياه
ب6	باب	80	210	-	1	المستودع
ب7	باب	300	230	-	1	الأمامية (على الشرفة)
ب7	باب مزدوج	240	230	-	1	الأمامية (على الشرفة)
ب8	باب مزدوج	240	230	-	1	الأمامية (على الشرفة)
ب9	باب	76	210	-	1	جناح الماستر
ب9	باب	90	210	-	2	الماستر — الملابس - غرفة 2
ف1	باب	160	220	-	1	فتحة الصالة الصغيرة
ز1	شباك	260	230	20	1	الأمامية (زجاج)
ش1	شباك	180	160	70	1	الشرقية
ش2	شباك	180	160	70	1	الغربية
ش3	شباك	180	100	110	1	الخلفية
ش4	شباك	100	100	150	2	الخلفية 2
ش5	شباك	60	60	160	3	الخلفية 2 - الغربية
ش6	شباك	140	140	80	1	الغربية

الإجمالي: أبواب 19 - شبابيك 10

جدول المساحات وبيانات المشروع


بيانات المشروع

البند	البيان
المشروع	فيلا خشب دورين بواجهة زجاج وشرفة — 12.00 × 9.00 م
العميل	عميل — فيلا دورين
الموقع	—
الاستخدام	سكن عائلي — مجلس + صالون + غرفتين
التاريخ	2026-10-31
نظام البناء	هيكل خشب 5×7 + تلبيس 2.5 سم من الجهتين
السقف	جملون 30° — قرميد معدني


جدول المساحات

م	الفراغ	الأبعاد (م)	المساحة (م2)
1	أرضي — المجلس	4.58 × 5.08	23.27
2	أرضي — الصالون	4.58 × 6.56	30.04
3	أرضي — المغاسل	1.58 × 5.08	8.03
4	أرضي — دورة مياه	2.36 × 1.94	4.58
5	أرضي — مستودع	2.36 × 3.02	7.13
6	أرضي — المطبخ	4.06 × 3.74	15.18
7	أرضي — مدخل الدرج	1.24 × 2.70	3.35
8	أرضي — الدرج	2.94 × 2.70	7.94
9	أول — غرفة الماستر	4.58 × 5.08	23.27
10	أول — صالة صغيرة	4.58 × 2.88	13.19
11	أول — غرفة نوم 2	4.58 × 3.56	16.30
12	أول — ممر الماستر	1.58 × 5.08	8.03
13	أول — حمام الماستر	2.36 × 2.44	5.76
14	أول — غرفة ملابس	2.36 × 2.52	5.95
15	أول — الممر	1.12 × 6.56	7.35
16	أول — حمام 2	2.88 × 2.34	6.74
17	أول — غسيل	2.88 × 1.28	3.69
	المساحة الصافية الداخلية		189.78
	التراس	2.20 × 12.00	26.40
	عتبة	**1.60 × 1.40**	**2.24**
	الشرفة	**2.20 × 12.00**	**26.40**
	المساحة الإجمالية المبنية	**12.00 × 9.00 × 2 دور**	**216.00**
	المساحة الكلية (المبنية + التراسات)		**271.04**

تأطير جدار أ-جنوب — الطول 1188 سم، الارتفاع 280 سم

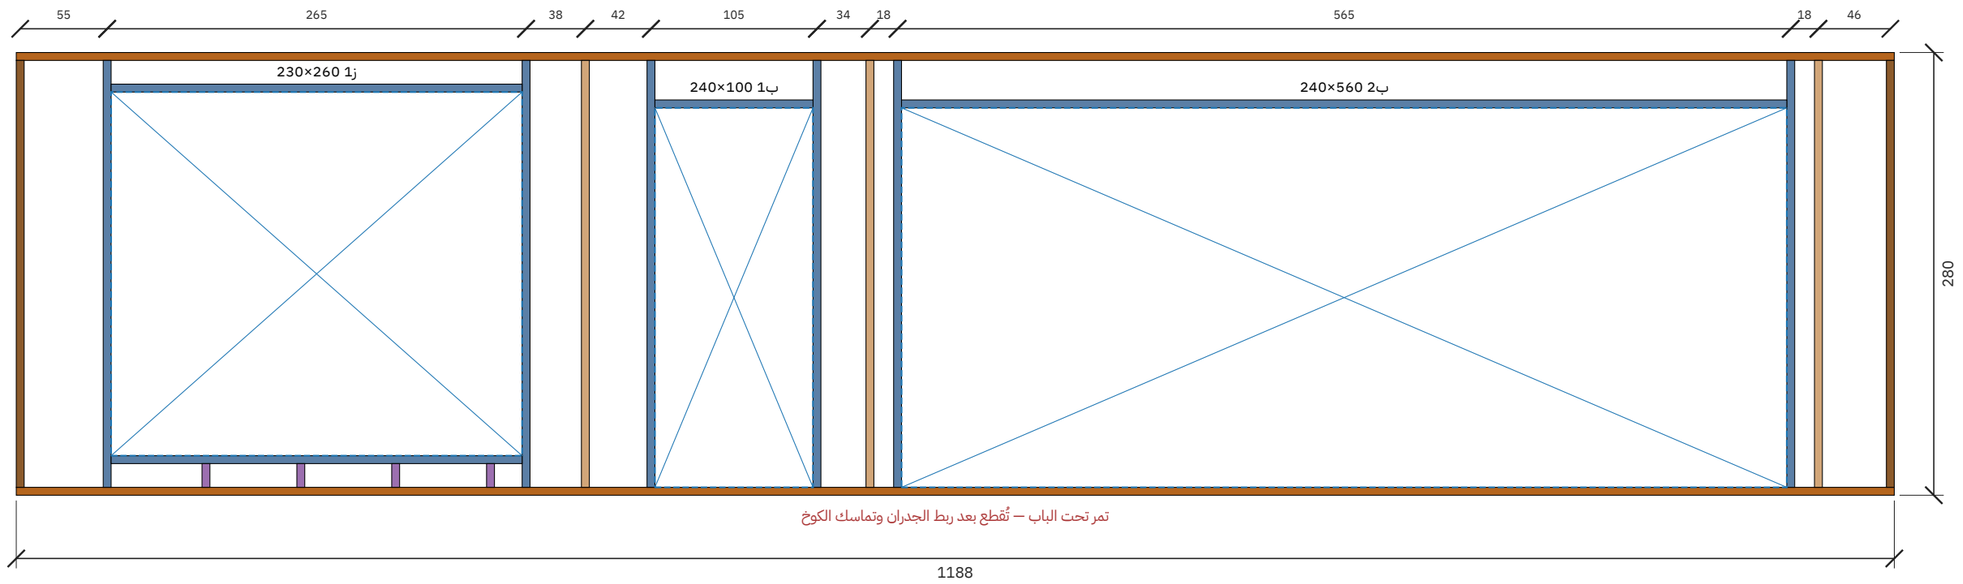

تأطير جدار أ-شرق — الطول 888 سم، الارتفاع 280 سم

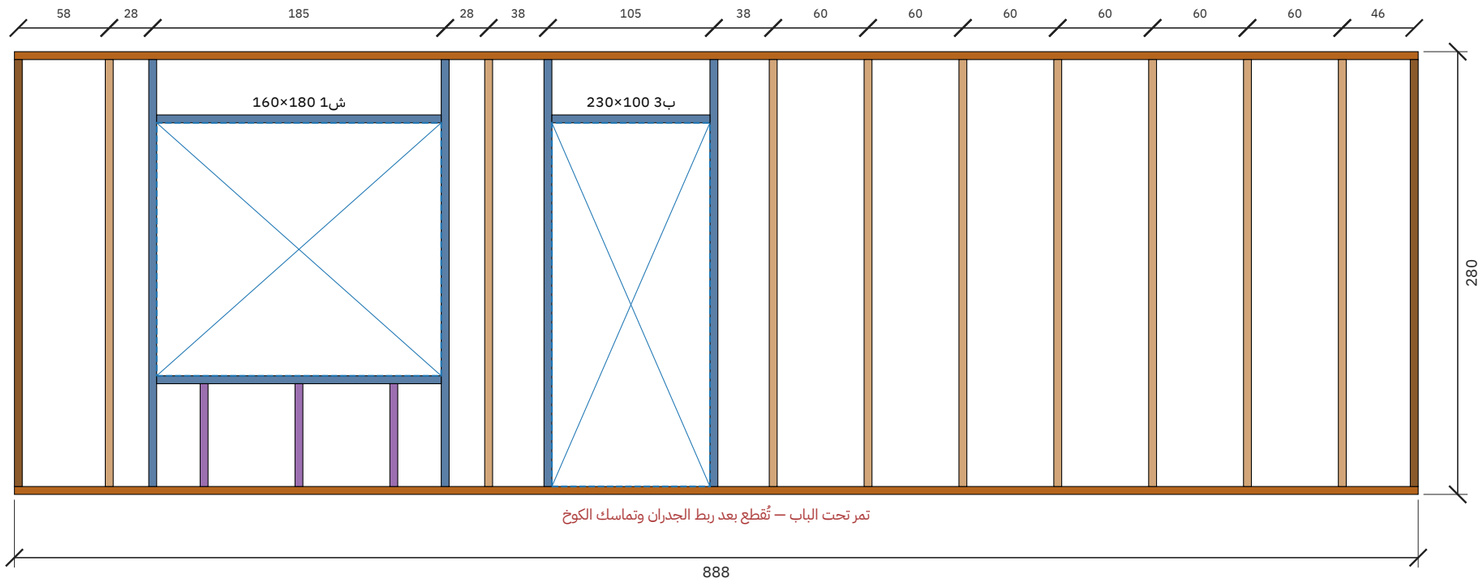


قاعدة سفلية | علوي | عمود | عمود زاوية | جنب فتحة | رأس فتحة | جلسة شباك | عمود قصير


المشروع / العميل	عنوان اللوحة	المقياس	التاريخ	رقم اللوحة
فيلا خشب دورين بواجهة زجاج وشرفة — 12.00 × 9.00 م **عميل — فيلا دورين**	**لوحات التأطير (للورشة)**	**—**	**2026-10-31**	**W-09 (9/21)**

مصنع وتد الأخشاب
Watad Wood Factory

تأطير جدار أ-شمال — الطول 1188 سم، الارتفاع 280 سم

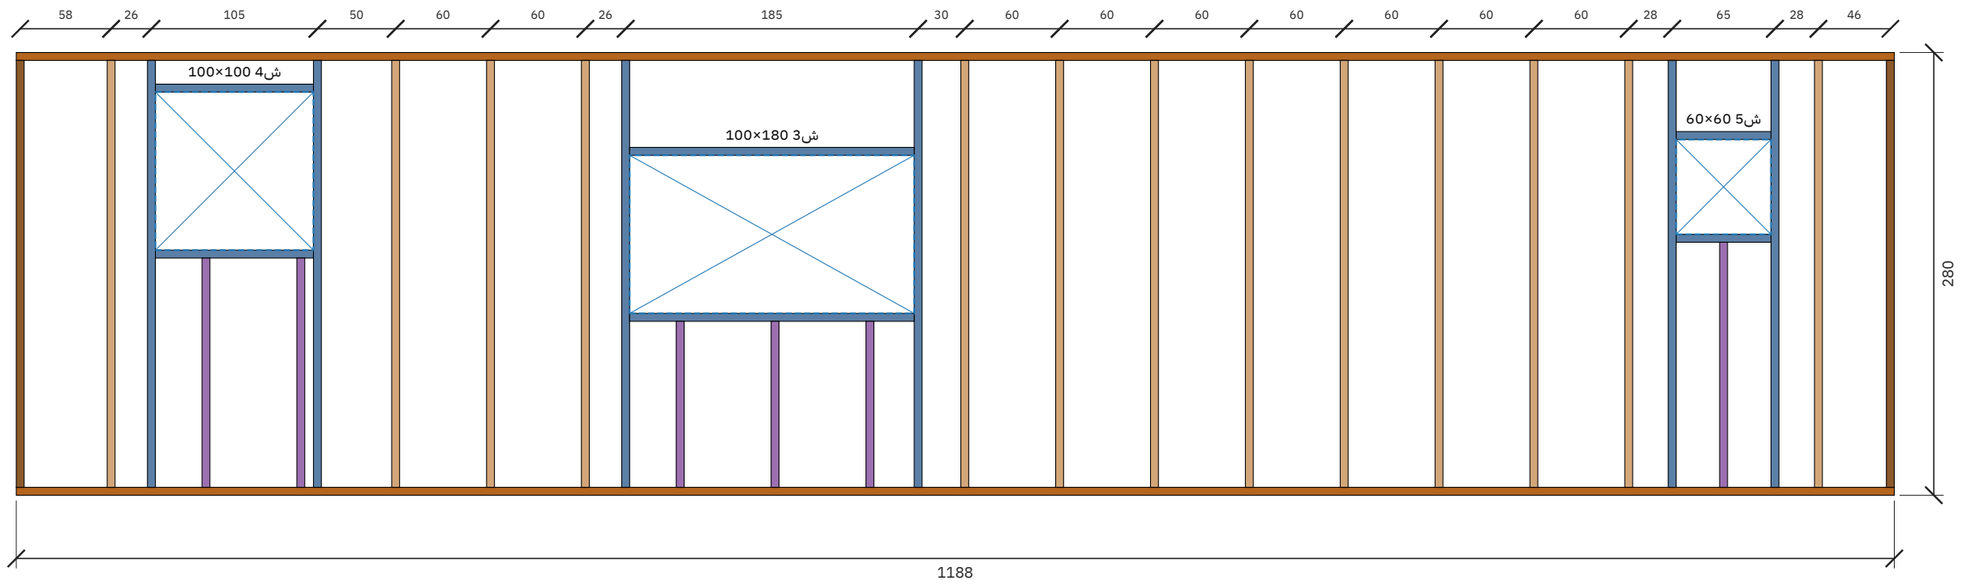

تأطير جدار أ-غرب — الطول 888 سم، الارتفاع 280 سم

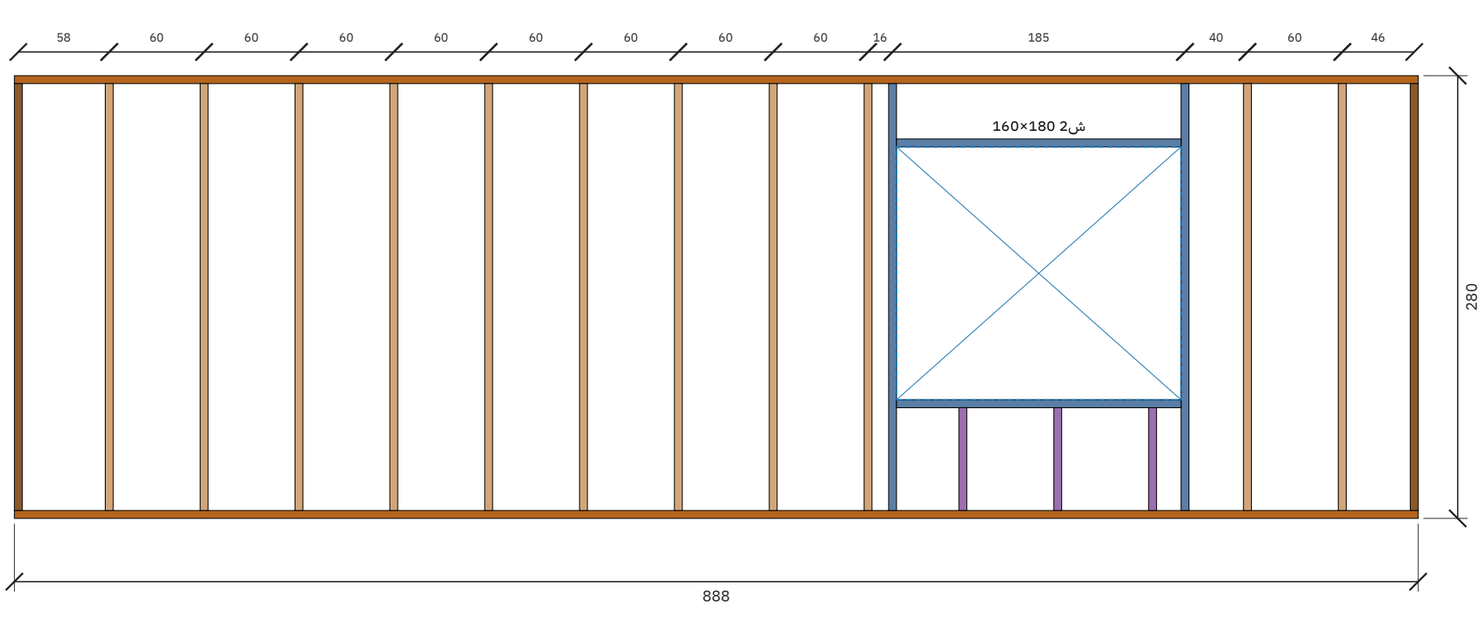


قاعدة سفلية | علوي | عمود | عمود زاوية | جنب فتحة | رأس فتحة | جلسة شباك | عمود قصير


المشروع / العميل	عنوان اللوحة	المقياس	التاريخ	رقم اللوحة
فيلا خشب دورين بواجهة زجاج وشرفة — 12.00 × 9.00 م **عميل — فيلا دورين**	**لوحات التأطير (للورشة)**	**—**	**2026-10-31**	**W-10 (10/21)**

مصنع وتد الأخشاب
Watad Wood Factory

تأطير جدار أ-المجلس/الصالون — الطول 470 سم، الارتفاع 280 سم (داخلي)

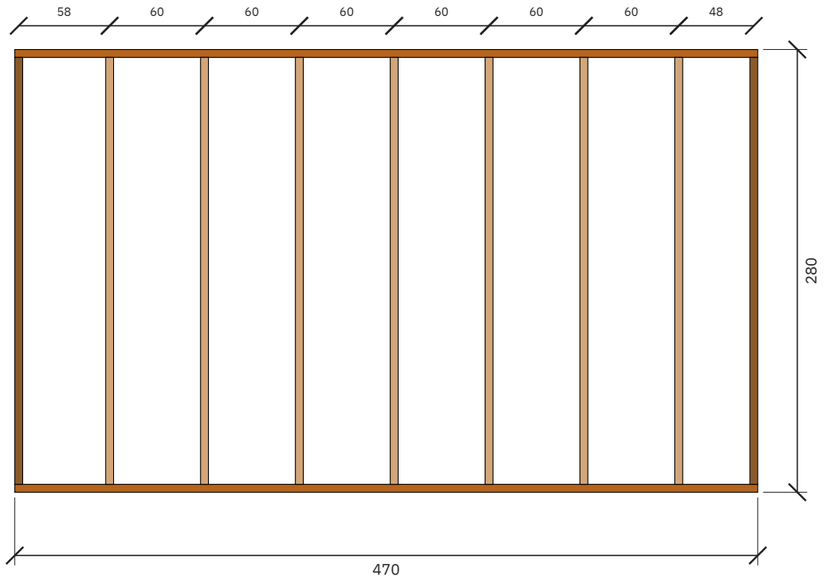

تأطير جدار أ-خلف المجلس والصالون — الطول 906 سم، الارتفاع 280 سم (داخلي)

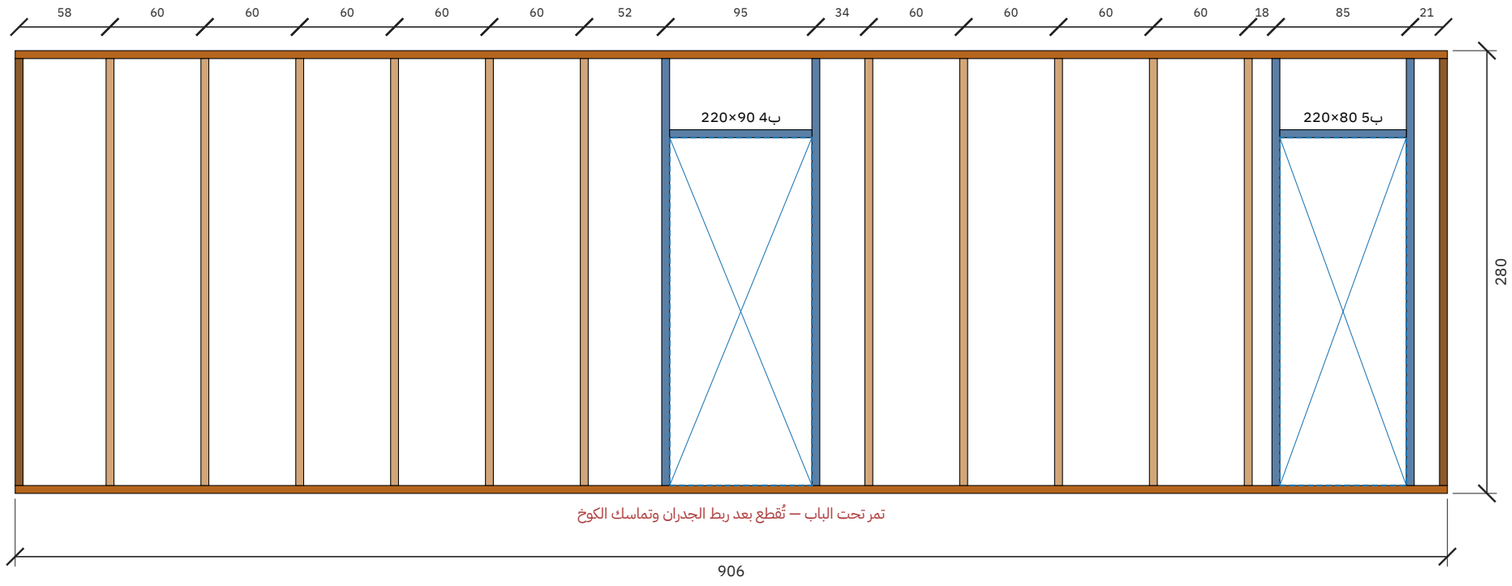


قاعدة سفلية | علوي | عمود | عمود زاوية | جنب فتحة | رأس فتحة | جلسة شباك | عمود قصير


المشروع / العميل	عنوان اللوحة	المقياس	التاريخ	رقم اللوحة
فيلا خشب دورين بواجهة زجاج وشرفة — 12.00 × 9.00 م **عميل — فيلا دورين**	**لوحات التأطير (للورشة)**	**—**	**2026-10-31**	**W-11 (11/21)**

مصنع وتد الأخشاب
Watad Wood Factory

تأطير جدار أ-جدار المطبخ الغربي — الطول 418 سم، الارتفاع 280 سم (داخلي)

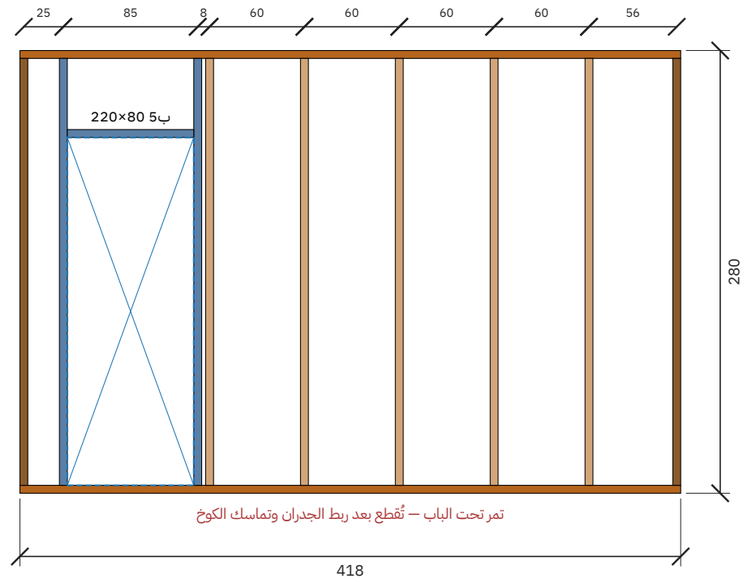

تأطير جدار أ-فاصل الدورة — الطول 520 سم، الارتفاع 280 سم (داخلي)

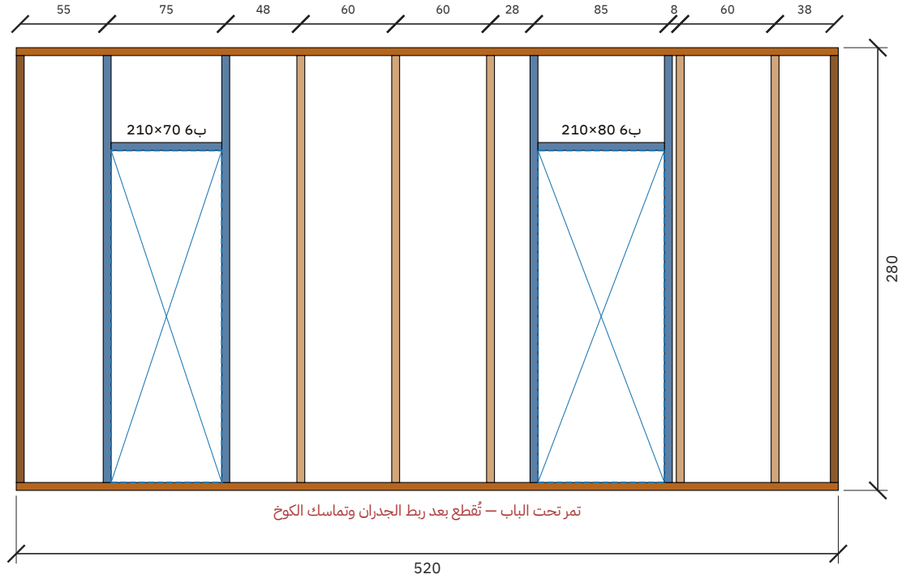


قاعدة سفلية | علوي | عمود | عمود زاوية | جنب فتحة | رأس فتحة | جلسة شباك | عمود قصير


المشروع / العميل	عنوان اللوحة	المقياس	التاريخ	رقم اللوحة
فيلا خشب دورين بواجهة زجاج وشرفة — 12.00 × 9.00 م **عميل — فيلا دورين**	**لوحات التأطير (للورشة)**	**—**	**2026-10-31**	**W-12 (12/21)**

مصنع وتد الأخشاب
Watad Wood Factory

تأطير جدار أ-جدار الدورة — الطول 248 سم، الارتفاع 280 سم (داخلي)

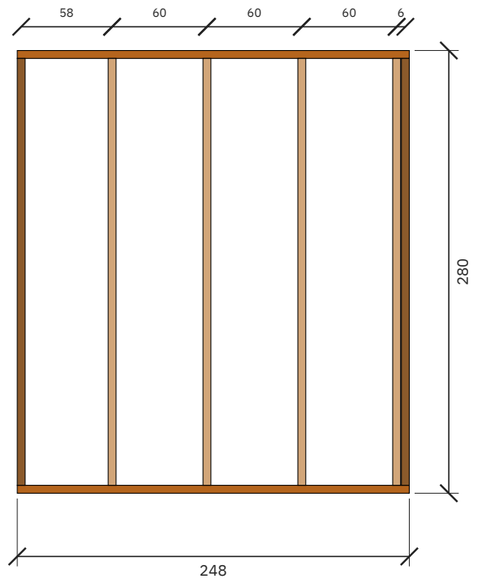

تأطير جدار أ-جدار الدرج — الطول 418 سم، الارتفاع 280 سم (داخلي)

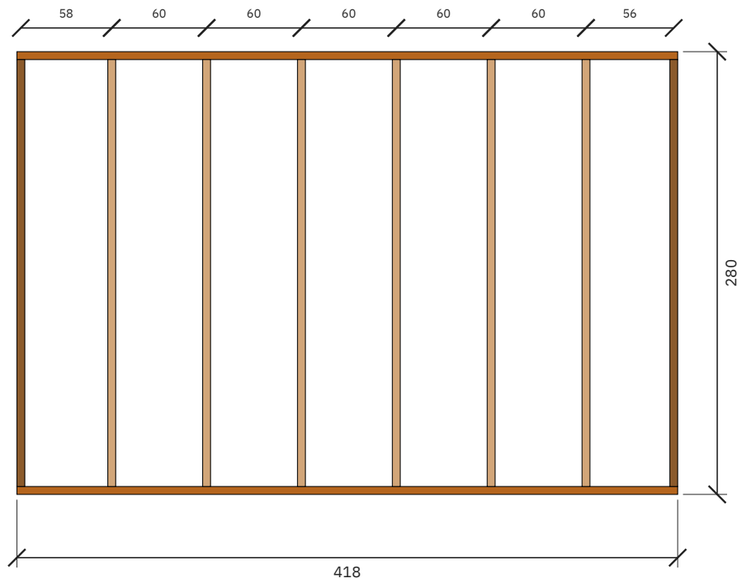


قاعدة سفلية | علوي | عمود | عمود زاوية | جنب فتحة | رأس فتحة | جلسة شباك | عمود قصير


المشروع / العميل	عنوان اللوحة	المقياس	التاريخ	رقم اللوحة
فيلا خشب دورين بواجهة زجاج وشرفة — 12.00 × 9.00 م عميل — فيلا دورين	لوحات التأطير (للورشة)	—	2026-10-31	W-13 (13/21)

مصنع وتد الأخشاب
Watad Wood Factory

تأطير جدار ب-جنوب — الطول 1188 سم، الارتفاع 280 سم

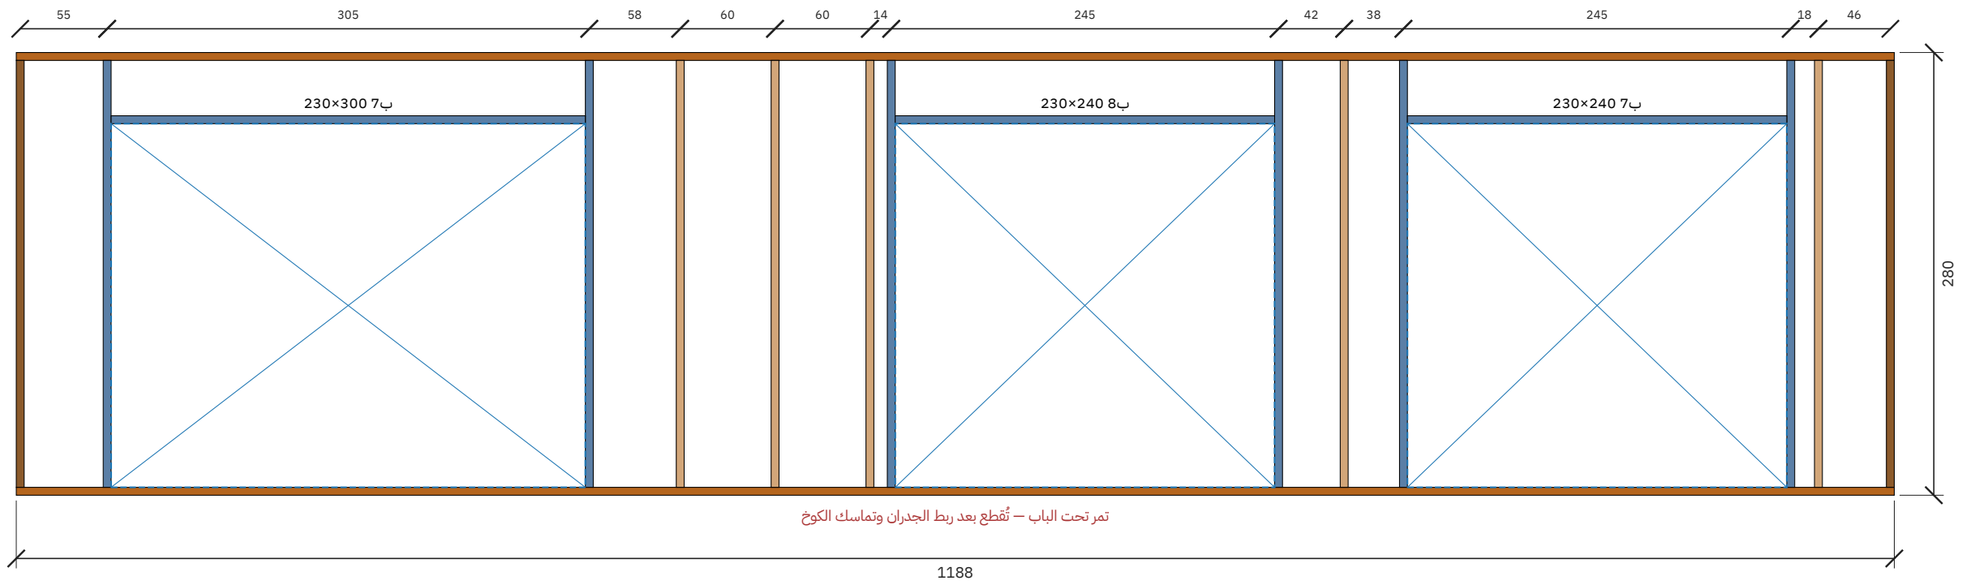

تأطير جدار ب-شرق — الطول 888 سم، الارتفاع 280 سم

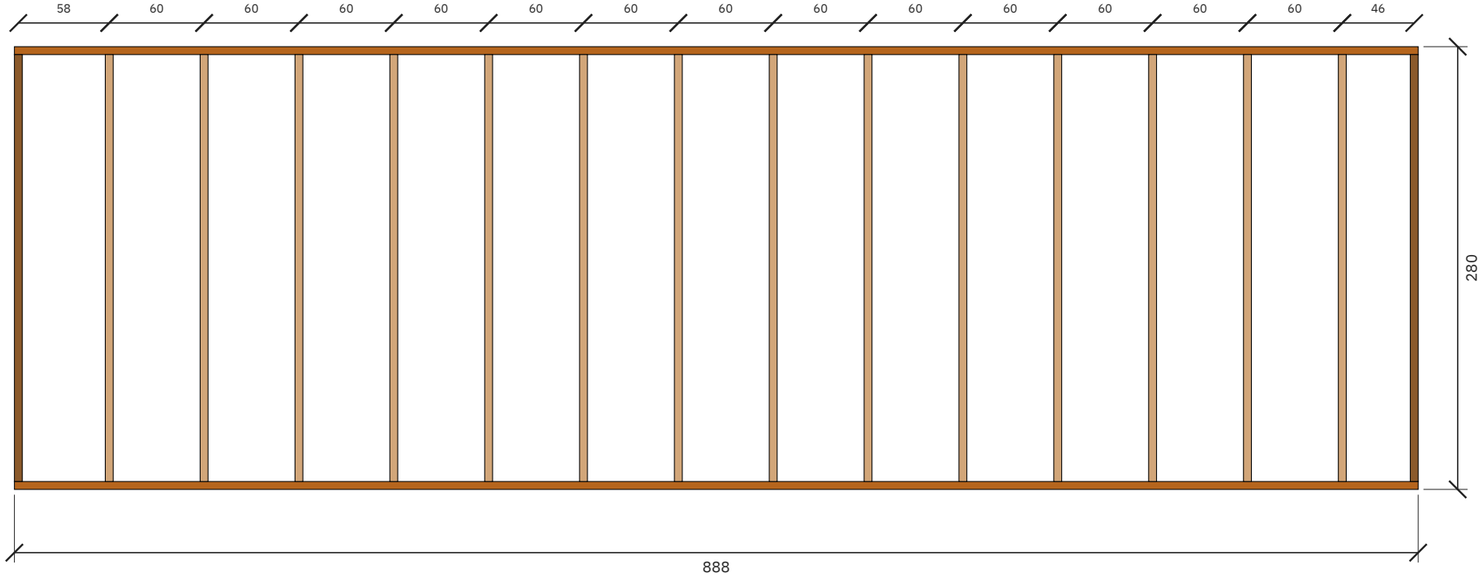


قاعدة سفلية | علوي | عمود | عمود زاوية | جنب فتحة | رأس فتحة | جلسة شباك | عمود قصير


المشروع / العميل	عنوان اللوحة	المقياس	التاريخ	رقم اللوحة
فيلا خشب دورين بواجهة زجاج وشرفة — 12.00 × 9.00 م **عميل — فيلا دورين**	**لوحات التأطير (للورشة)**	**—**	**2026-10-31**	**W-14 (14/21)**

مصنع وتد الأخشاب
Watad Wood Factory

تأطير جدار ب-شمال — الطول 1188 سم، الارتفاع 280 سم

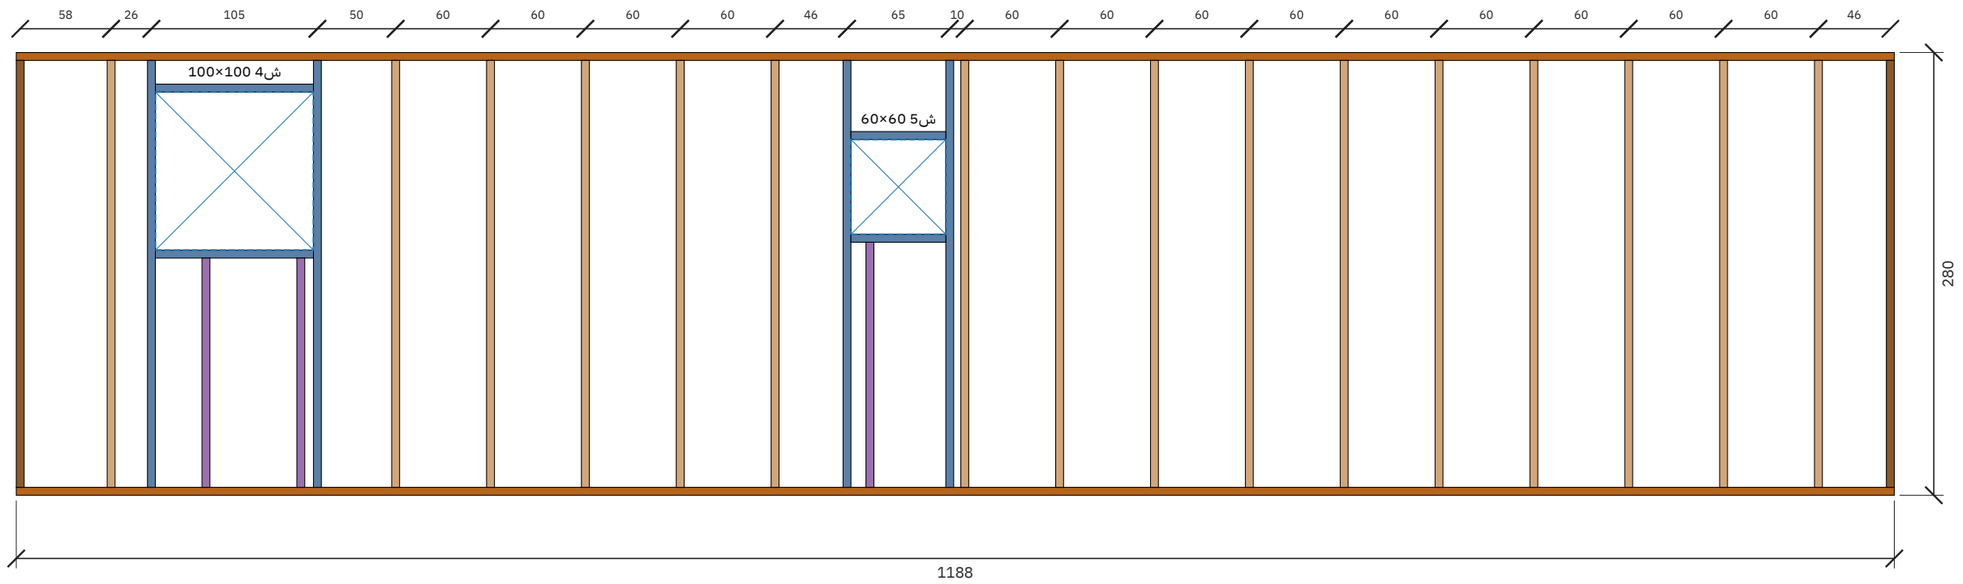

تأطير جدار ب-غرب — الطول 888 سم، الارتفاع 280 سم

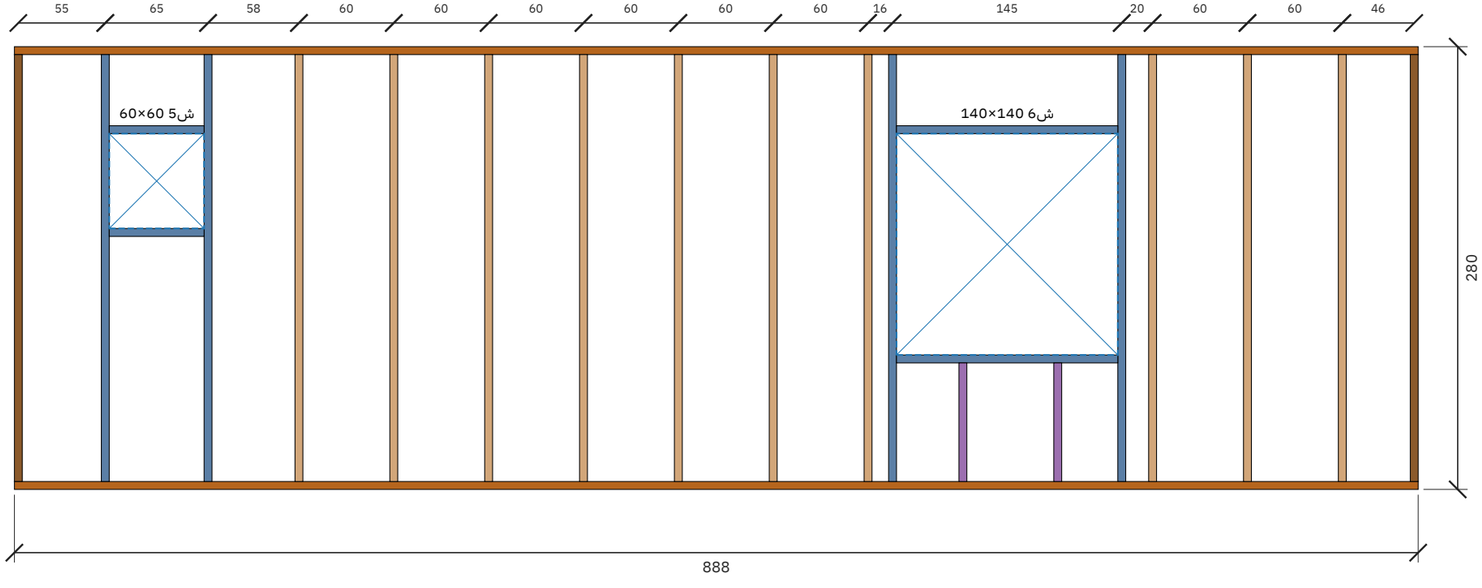


قاعدة سفلية | علوي | عمود | عمود زاوية | جنب فتحة | رأس فتحة | جلسة شباك | عمود قصير


المشروع / العميل	عنوان اللوحة	المقياس	التاريخ	رقم اللوحة
فيلا خشب دورين بواجهة زجاج وشرفة — 12.00 × 9.00 م **عميل — فيلا دورين**	**لوحات التأطير (للورشة)**	**—**	**2026-10-31**	**W-15 (15/21)**

مصنع وتد الأخشاب
Watad Wood Factory

تأطير جدار ب-جدار الماستر الشرقي — الطول 888 سم، الارتفاع 280 سم (داخلي)

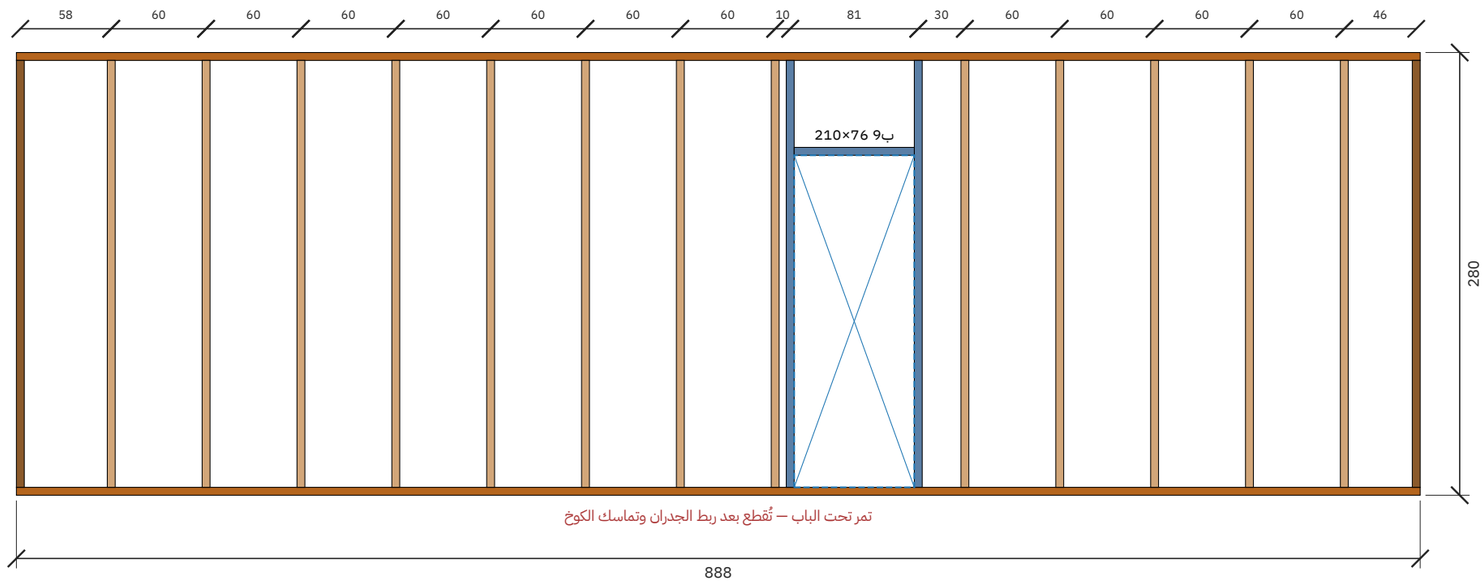

تأطير جدار ب-خلف الغرف — الطول 1188 سم، الارتفاع 280 سم (داخلي)

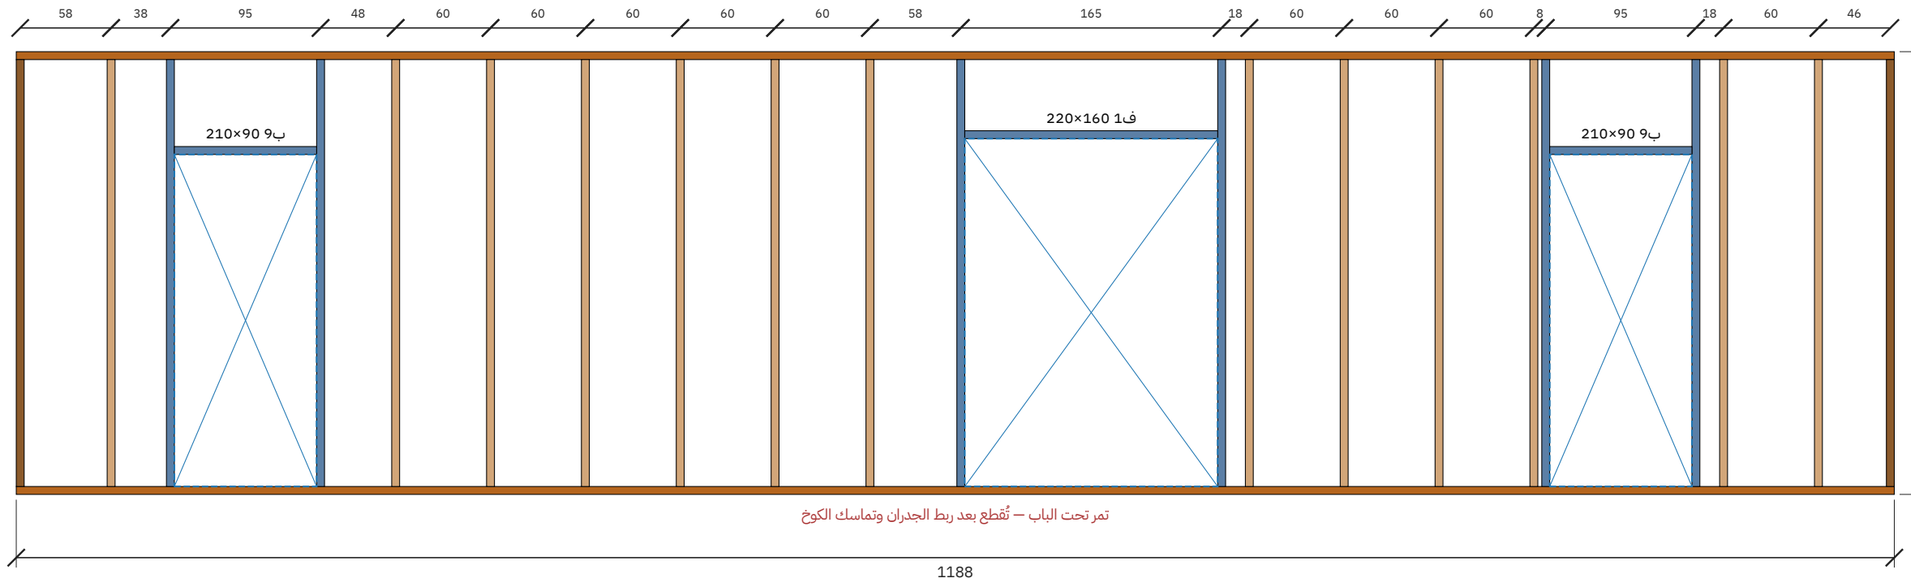


قاعدة سفلية | علوي | عمود | عمود زاوية | جنب فتحة | رأس فتحة | جلسة شباك | عمود قصير


المشروع / العميل	عنوان اللوحة	المقياس	التاريخ	رقم اللوحة
فيلا خشب دورين بواجهة زجاج وشرفة — 12.00 × 9.00 م **عميل — فيلا دورين**	**لوحات التأطير (للورشة)**	**—**	**2026-10-31**	**W-16 (16/21)**

مصنع وتد الأخشاب
Watad Wood Factory

تأطير جدار ب-جدار غرفة 2 — الطول 470 سم، الارتفاع 280 سم (داخلي)

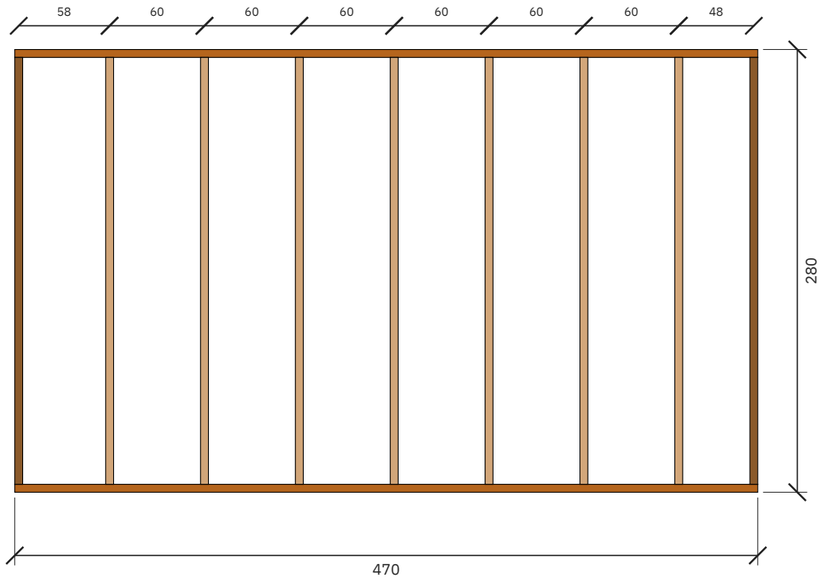


تأطير جدار ب-فاصل حمام الماستر — الطول 520 سم، الارتفاع 280 سم (داخلي)

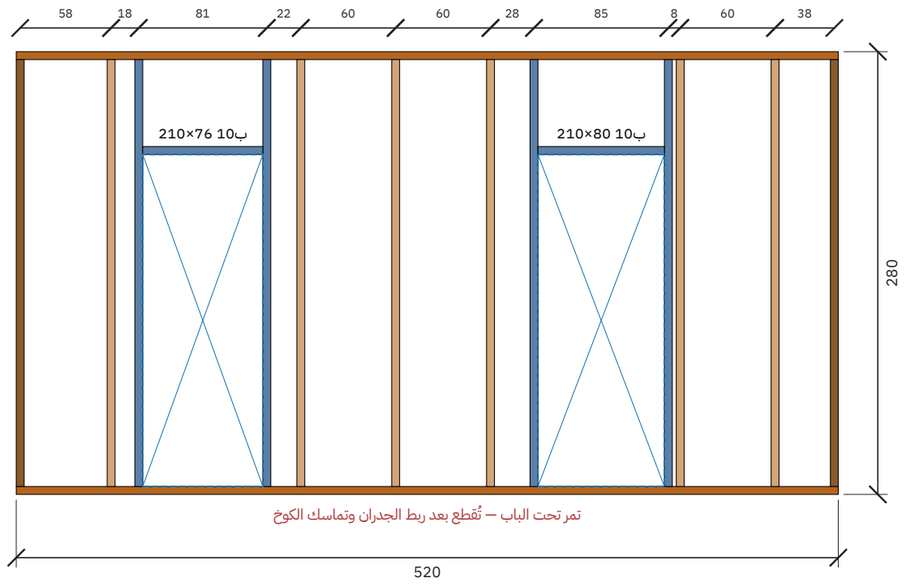


قاعدة سفلية | علوي | عمود | عمود زاوية | جنب فتحة | رأس فتحة | جلسة شباك | عمود قصير

مصنع وتد الأخشاب Watad Wood Factory	المشروع / العميل فيلا خشب دورين بواجهة زجاج وشرفة — 12.00 × 9.00 م عميل — فيلا دورين	عنوان اللوحة لوحات التأطير (للورشة)	المقياس —	التاريخ 2026-10-31	رقم اللوحة W-17 (17/21)

تأطير جدار ب-جدار الملابس — الطول 248 سم، الارتفاع 280 سم (داخلي)

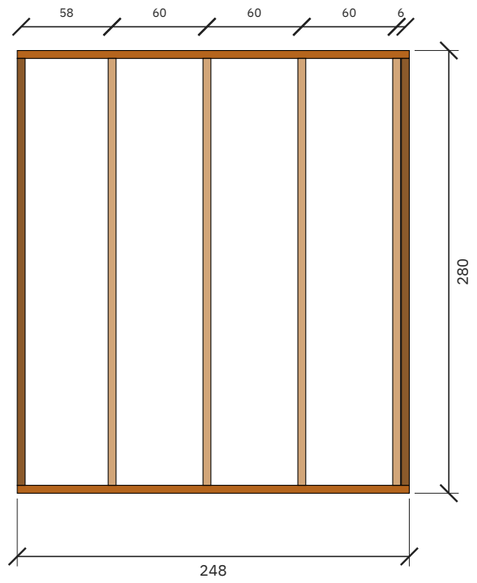

تأطير جدار ب-فاصل حمام 2 — الطول 386 سم، الارتفاع 280 سم (داخلي)

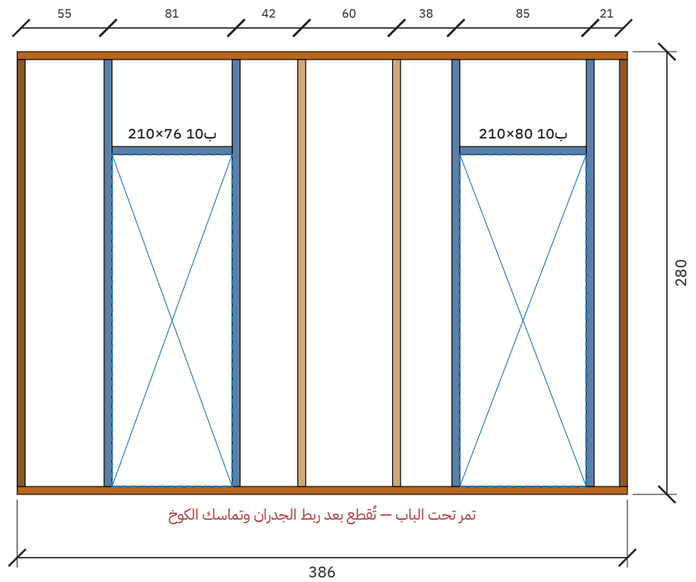


قاعدة سفلية | علوي | عمود | عمود زاوية | جنب فتحة | رأس فتحة | جلسة شباك | عمود قصير


المشروع / العميل	عنوان اللوحة	المقياس	التاريخ	رقم اللوحة
فيلا خشب دورين بواجهة زجاج وشرفة — 12.00 × 9.00 م **عميل — فيلا دورين**	**لوحات التأطير (للورشة)**	**—**	**2026-10-31**	**W-18 (18/21)**

مصنع وتد الأخشاب
Watad Wood Factory

تأطير جدار ب-جدار الغسيل — الطول 300 سم، الارتفاع 280 سم (داخلي)

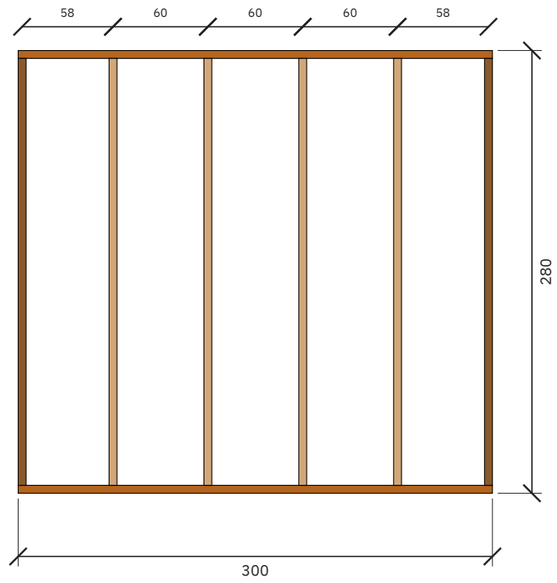

تأطير جدار ب-جدار الدرج — الطول 300 سم، الارتفاع 280 سم (داخلي)

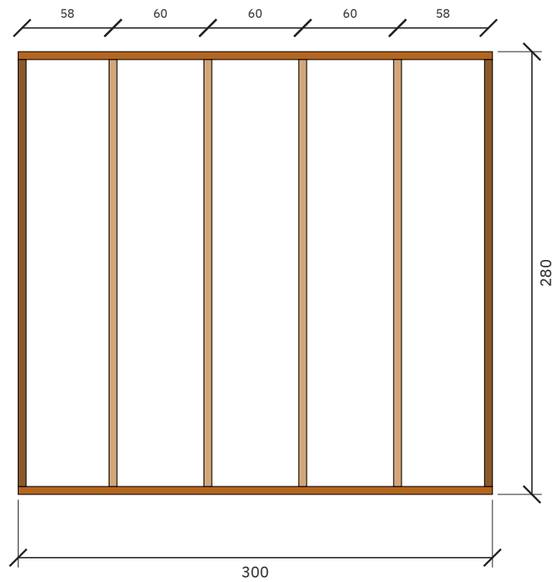

عمود قصير
جلسة شباك
رأس فتحة
جنب فتحة
عمود زاوية
عمود
علوي
قاعدة سفلية

مصنع وتد الأخشاب Watad Wood Factory	المشروع / العميل **فيلا خشب دورين بواجهة زجاج وشرفة — 12.00 × 9.00 م** **عميل — فيلا دورين**	عنوان اللوحة **لوحات التأطير (للورشة)**	المقياس **—**	التاريخ **2026-10-31**	رقم اللوحة **W-19 (19/21)**

جدول الكميات وخطة تقطيع الطبليات

البند	القيمة
الارتفاع المطلوب / المعتمد	280 / 280 سم
السقف	جملون 30° — أعلى نقطة 931 سم من وجه الصبة
المدادات 5×15	80 مداد (20 خط × قطعتين موصولة فوق الجسر الحامل بتراكب 60 سم) × حتى 422 سم — من طبلية 480
طبليات الطريقة الأولى (مداد + عمود)	80 طبلية × 480 سم
طبليات الطريقة الثانية (3 أعمدة)	95 طبلية × 320 سم
مدادات أرضية الدور العلوي 5×15 كل 60 سم	60 مداد — 216سم×15، 292سم×15، 324سم×15، 396سم×15 (طبلية 480 بالطريقة الأولى)
إجمالي الطبليات 5×22.5	235
إجمالي قطع 5×7	378
قائمة تقطيع 5×7	1188سم×10 | 906سم×2 | 888سم×10 | 560سم×1 | 520سم×4 | 470سم×4 | 418سم×4 | 386سم×2 | 300سم×5
	270سم×274 | 260سم×2 | 248سم×4 | 240سم×2 | 180سم×6 | 160سم×1 | 155سم×2 | 145سم×4 | 140سم×2
ألواح تلبيس 2.5 سم	1050 لوح × 400 سم (مجموع الصفوف 3367.5 م، 44 وجه)
أسمنت بورد 12 مم (122×244)	52 لوح (داخل دورات المياه)
العزل	497 لوح فوم صخري 80
الصبة	يجهزها العميل — 20 سم، مفرغة تحت دورات المياه

مراجعة التصميم مقابل قواعد المصنع

النوع	البند	التفاصيل	المقترح
ملاحظة	حمام 2 غير مكدّس	دورة المياه العلوية ليست فوق دورة مياه أرضية — تحتاج خط صرف خارجي مستقل على الجدار.	يُفضّل تكديس الحمامات فوق بعض (قاعدة المصنع).
ملاحظة	بحر المدادات	أطول بحر بدون جدار داخلي يحمل المداد: جهة أ: 526 سم، جهة ب: 600 سم. يحتاج رقم المصنع لأقصى بحر مسموح لتحديد المدادات اللي تُقوّى 20×5.	
ملاحظة	الصبة والدرج	ارتفاع الصبة 45 سم ← 3 درجة بقائمة 15.0 سم.	
ملاحظة	مناسيب رؤوس الفتحات	رؤوس الأبواب والشبابيك على مناسيب مختلفة: 210، 220، 230، 240، 250 سم.	
سؤال	يحتاج تأكيد	أقصى بحر للمداد بدون جدار داخلي قبل إضافة تقوية 7×5 (مداد 20×5)؟	
سؤال	يحتاج تأكيد	التغطية الصافية للوح التلبيس بعد التعشيق (مستنتجة مؤقتاً 18.67 سم من 280/15)؟	
سؤال	يحتاج تأكيد	هل يوضع أعمدة قصيرة فوق رأس الشباك/الباب إلى العلوي؟	
سؤال	يحتاج تأكيد	مكان الوصلة في القاعدة والعلوي إذا الجدار أطول من الطبلية؟	