
المسقط الأفقي مع الفرش — الدور الأرضي

الأبعاد بالسنتيمتر - الجدران: قوائم 7×5 + تلبيس 2.5 من الجهتين (12 سم) | منسوب الأرضية +0.00

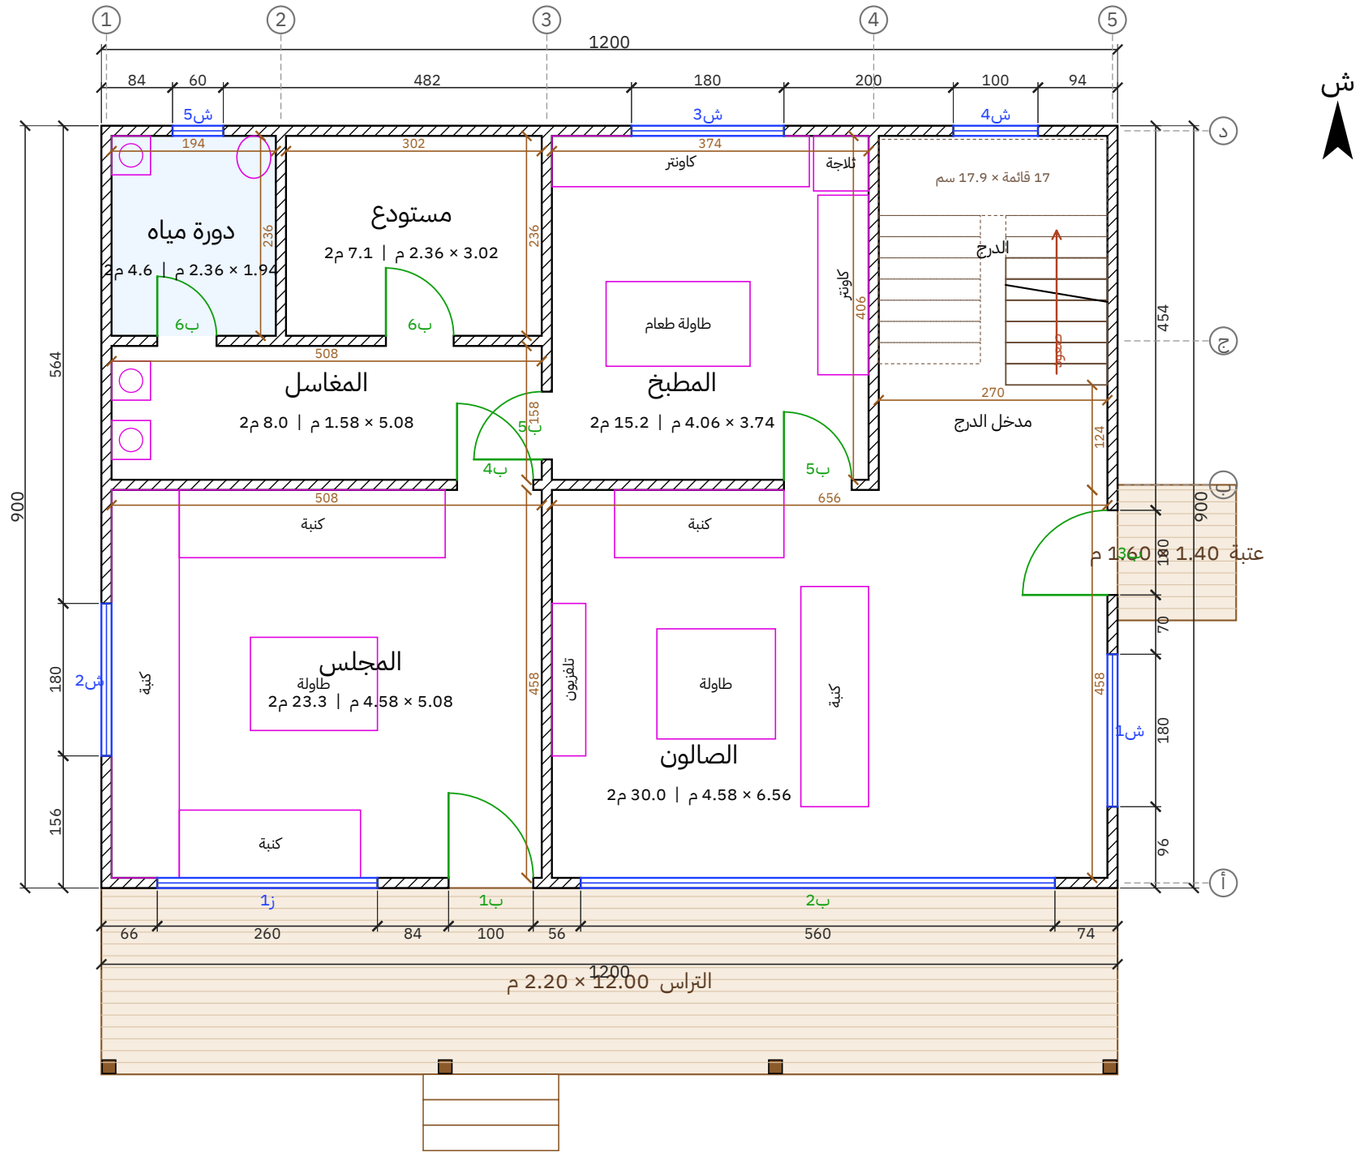


المشروع / العميل	عنوان اللوحة	المقياس	التاريخ	رقم اللوحة
فيلا خشب دورين بواجهة زجاج وشرفة — 12.00 × 9.00 م عميل — فيلا دورين	المسقط الأفقي — الدور الأرضي	1:50	2026-10-31	A-01 (1/11)

مصنع وتد الأخشاب
Watad Wood Factory


المسقط الأفقي مع الفرش — الدور الأول

الأبعاد بالسنتيمتر - الجدران: قوائم 7×5 + تلبيس 2.5 من الجهتين (12 سم) | منسوب الأرضية +3.05

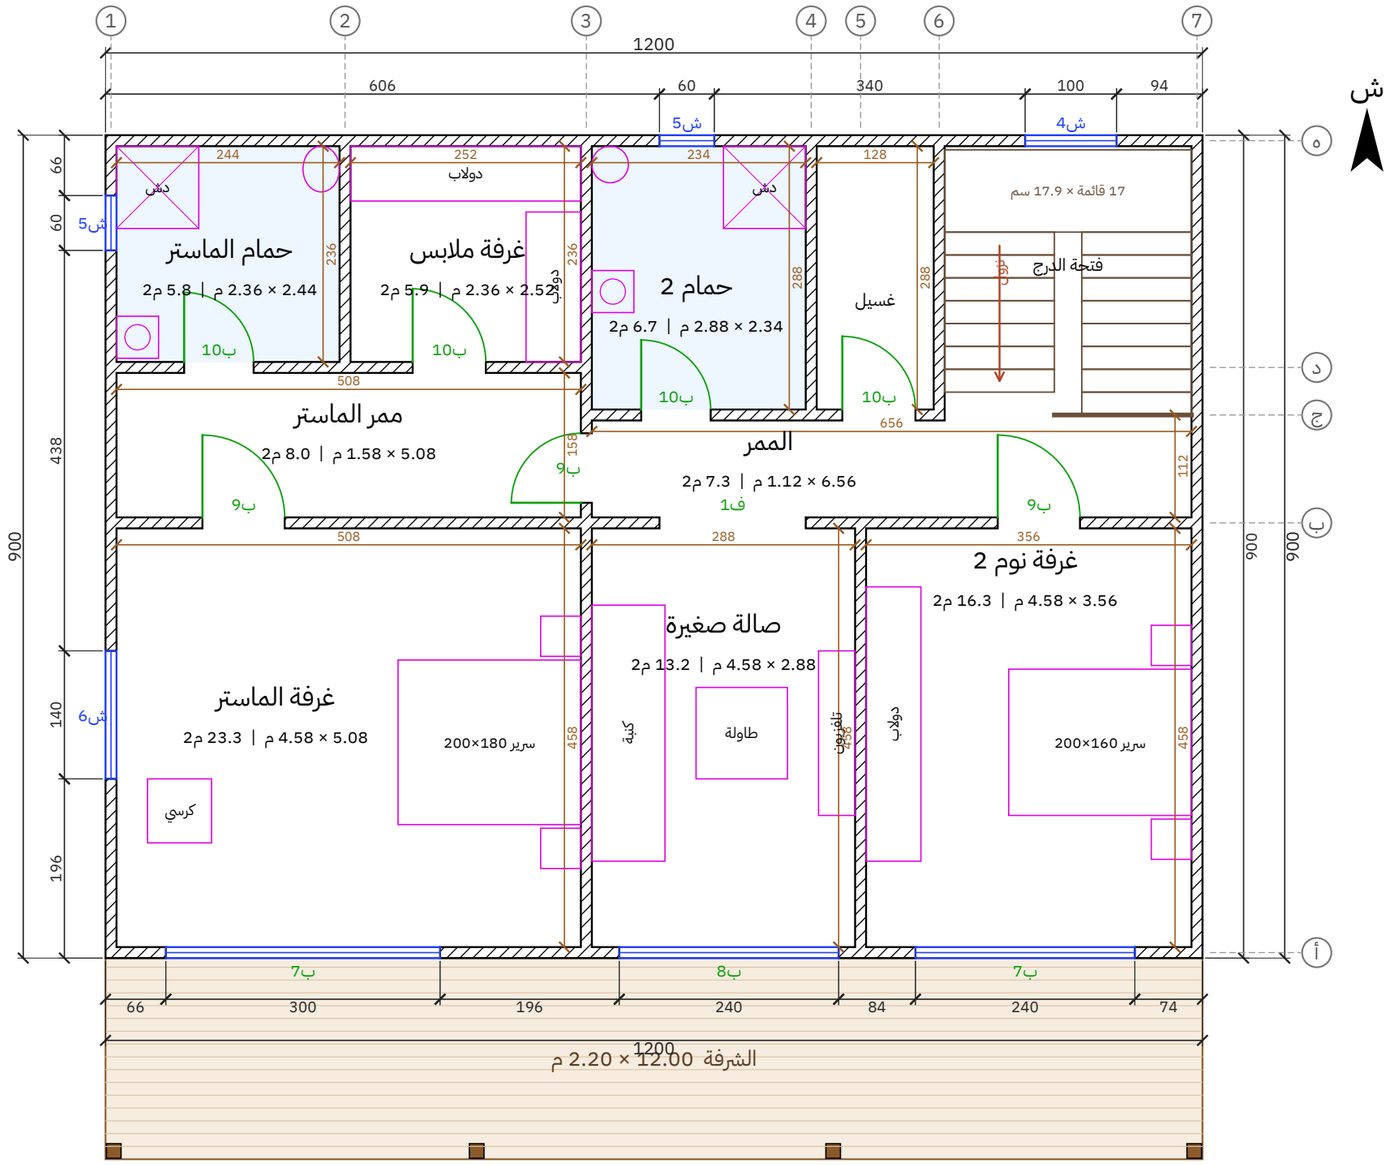


المشروع / العميل	عنوان اللوحة	المقياس	التاريخ	رقم اللوحة
فيلا خشب دورين بواجهة زجاج وشرفة — 12.00 × 9.00 م عميل — فيلا دورين	المسقط الأفقي — الدور الأول	1:50	2026-10-31	A-02 (2/11)

مصنع وتد الأخشاب
Watad Wood Factory

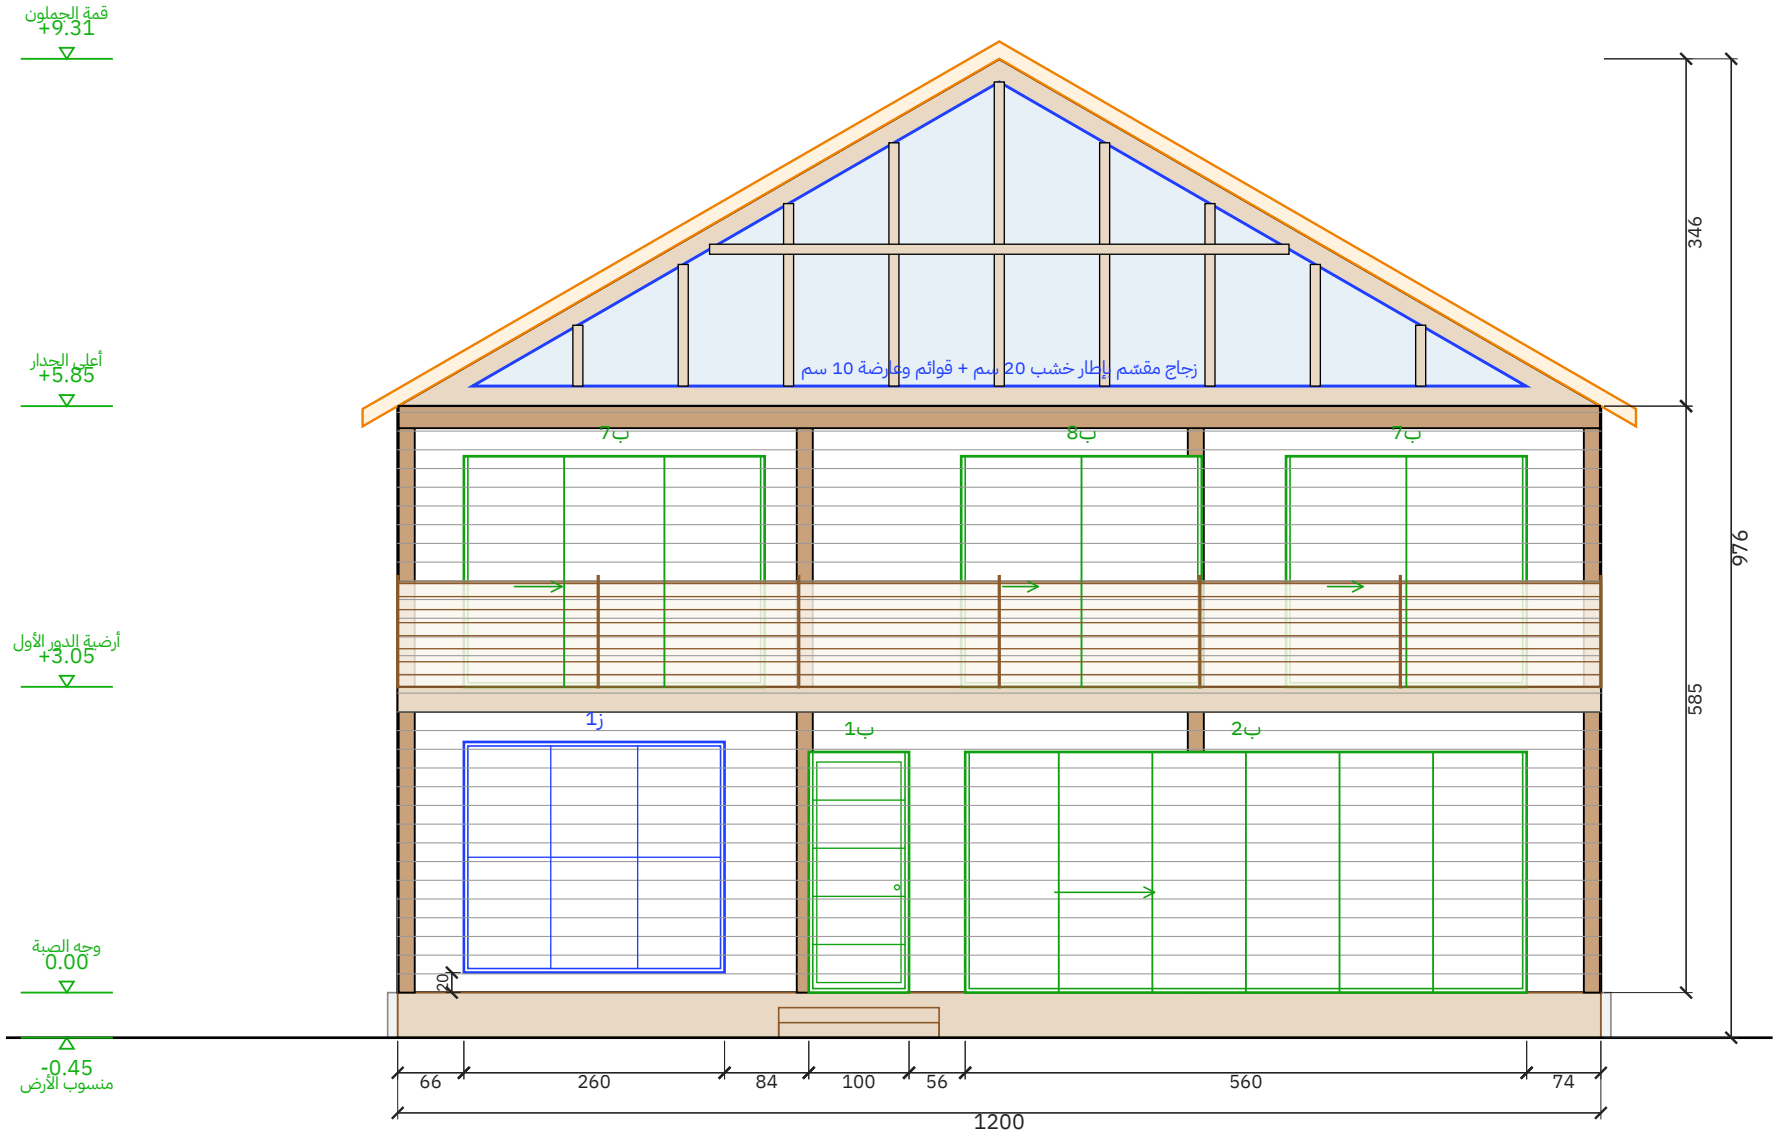

الواجهة الأمامية (زجاج)

مقياس 1:50 | الوحدة: سم

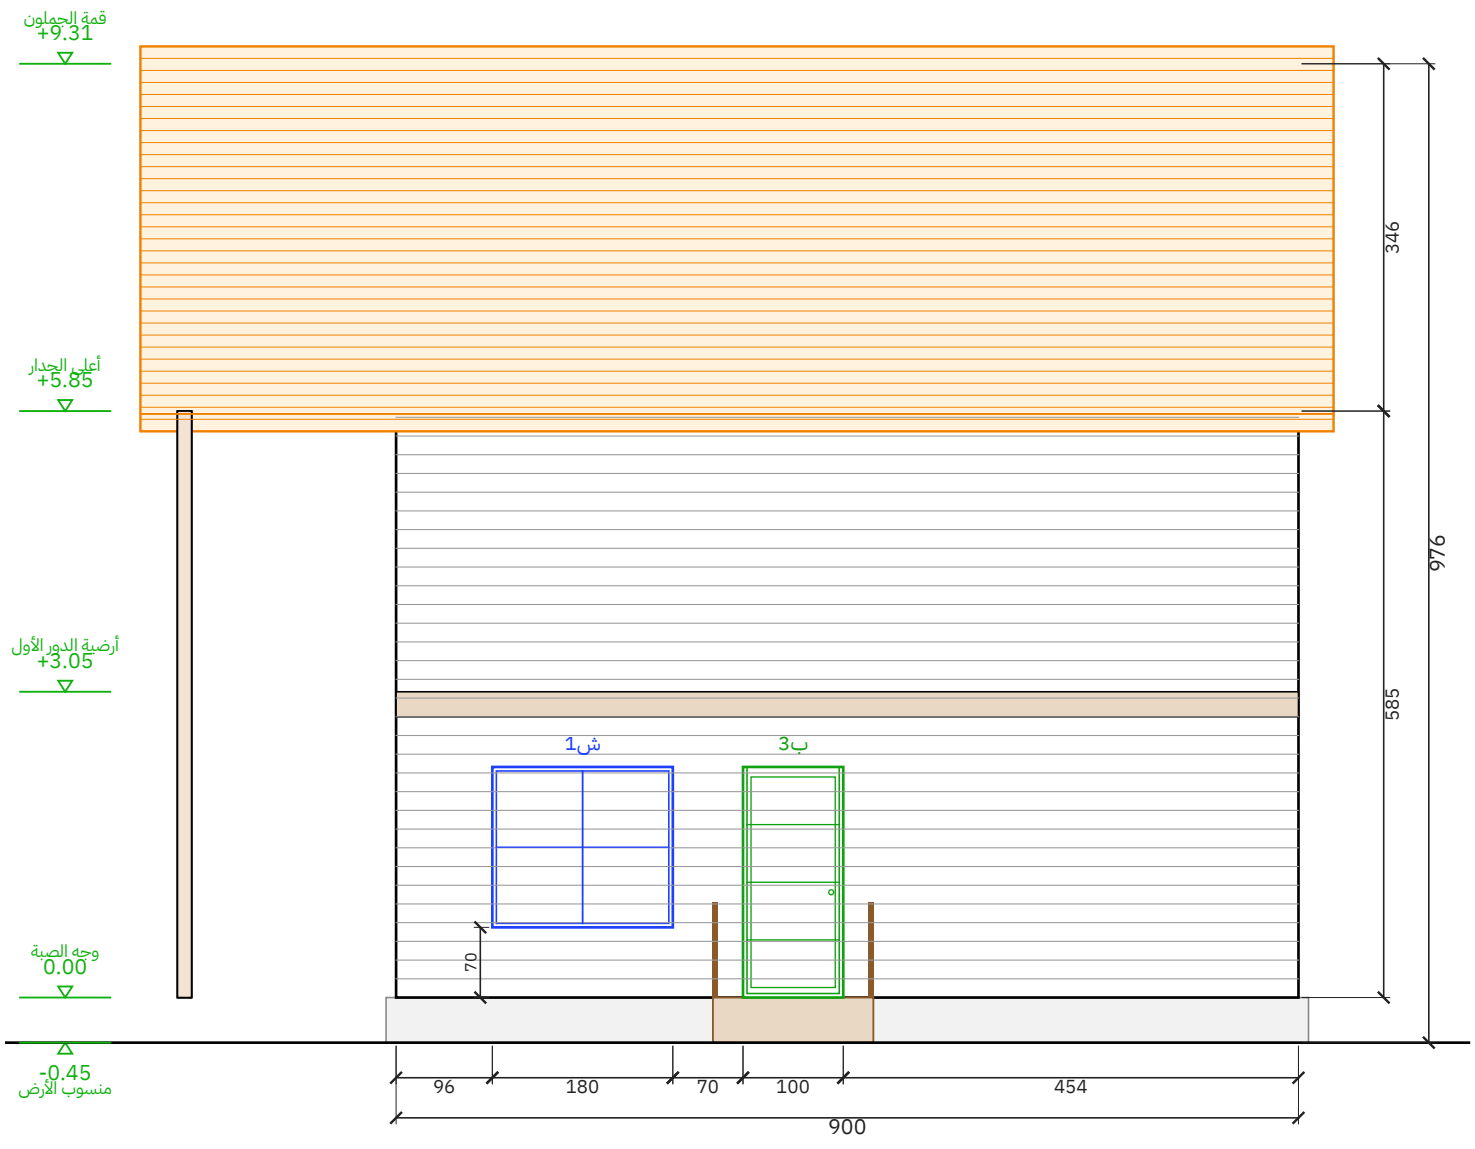


الواجهة الشرقية

مقياس 1:50 | الوحدة: سم


المشروع / العميل	عنوان اللوحة	المقياس	التاريخ	رقم اللوحة
فيلا خشب دورين بواجهة زجاج وشرفة — 12.00 × 9.00 م عميل — فيلا دورين	الواجهة الأمامية (زجاج) والواجهة الشرقية	1:50	2026-10-31	A-03 (3/11)

مصنع وتد الأخشاب
Watad Wood Factory

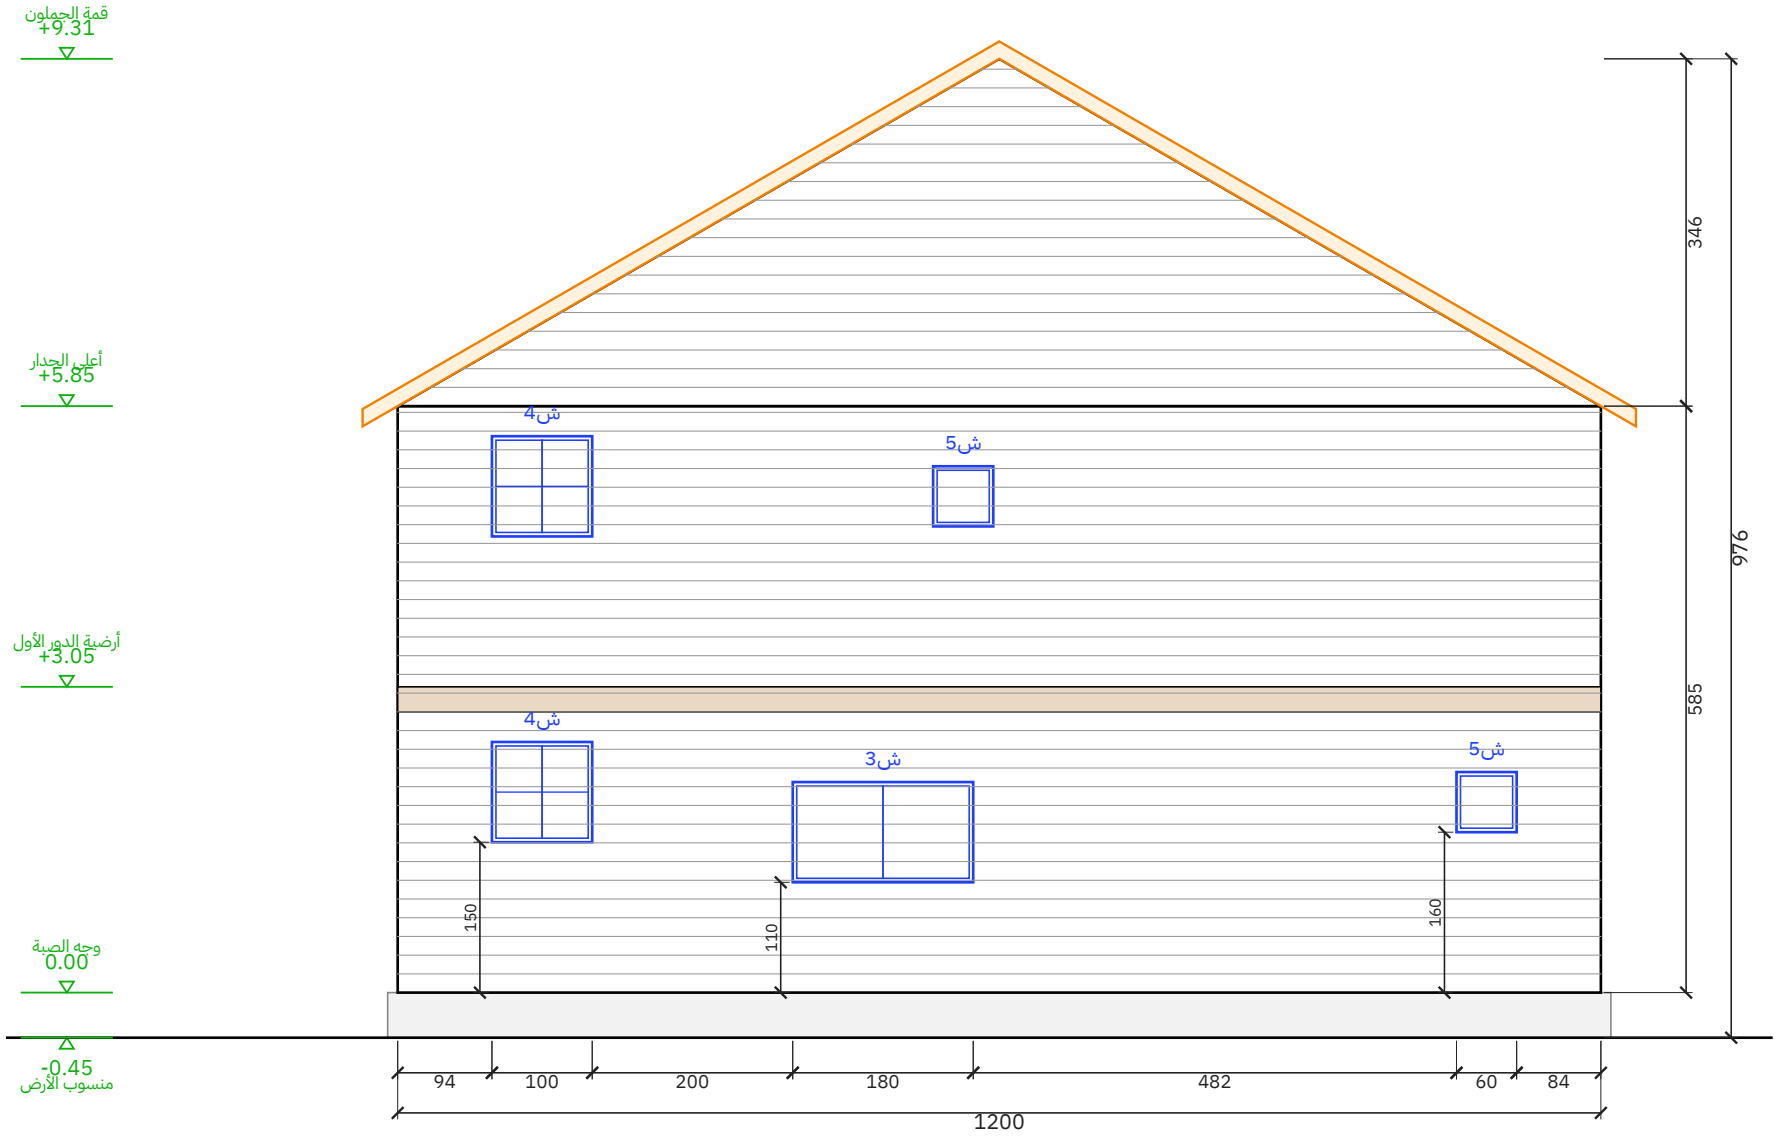

الواجهة الخلفية

مقياس 1:50 | الوحدة: سم

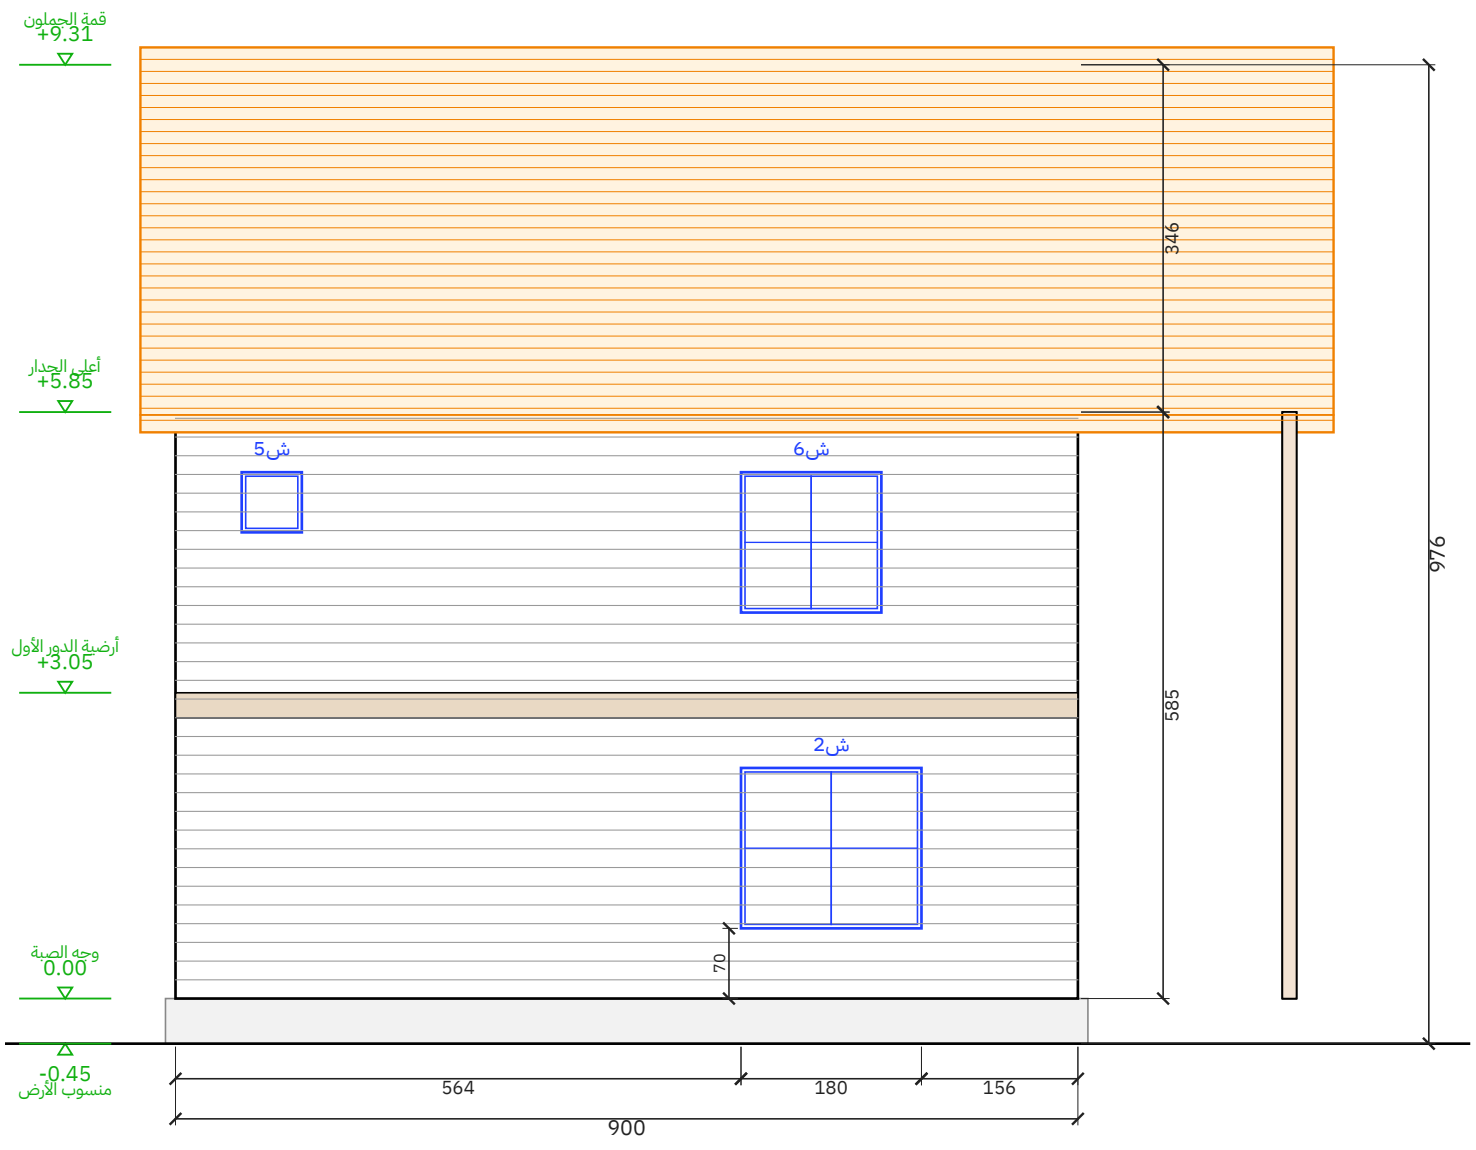


الواجهة الغربية

مقياس 1:50 | الوحدة: سم

المشروع / العميل	عنوان اللوحة	المقياس	التاريخ	رقم اللوحة
مصنع وتد الأخشاب Watad Wood Factory فيلا خشب دورين بواجهة زجاج وشرفة — 12.00 × 9.00 م عميل — فيلا دورين	الواجهة الخلفية والواجهة الغربية	1:50	2026-10-31	A-04 (4/11)


مسقط السقف (جملون)

رفرف 35 سم من كل جهة | مقياس 1:50

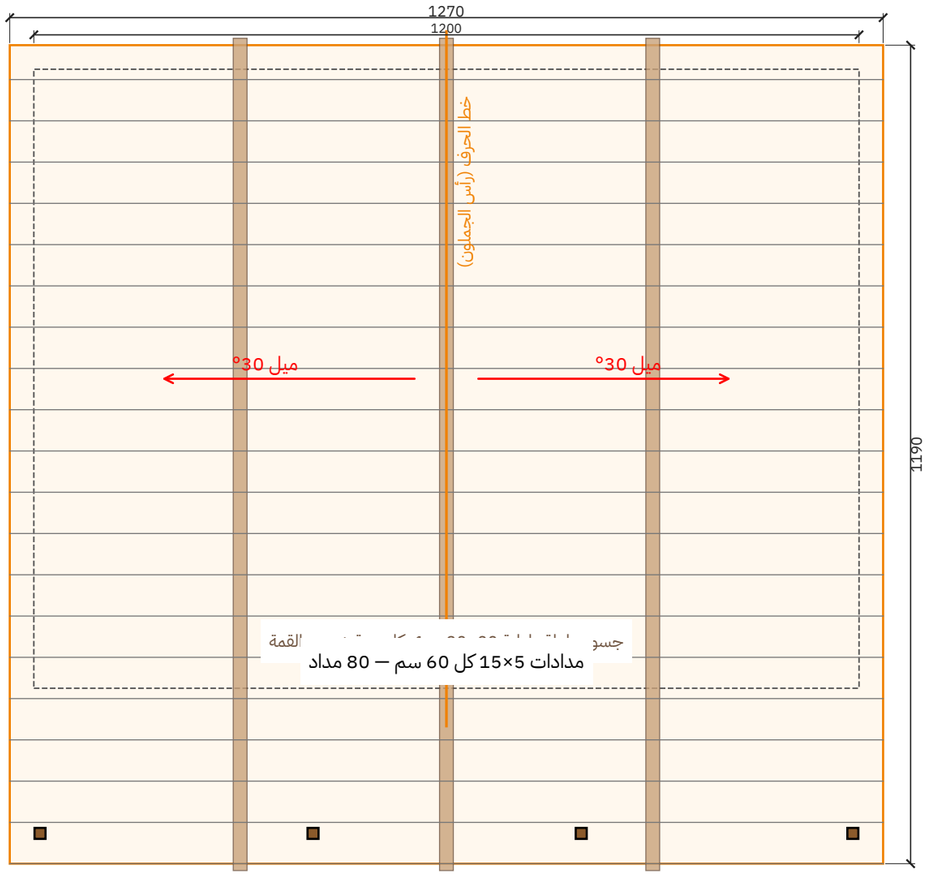


قطاع عرضي أ-أ

مقياس 1:50 | الوحدة: سم

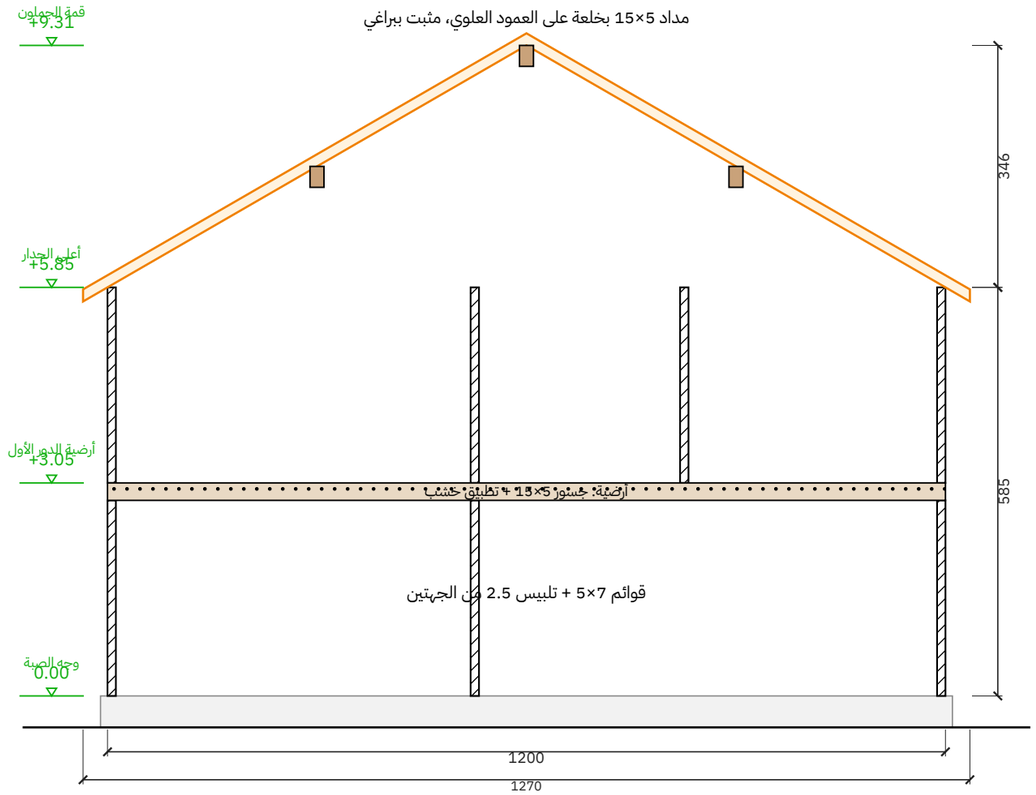

تفصيلة جلوس المداد على العلوي (1:5)

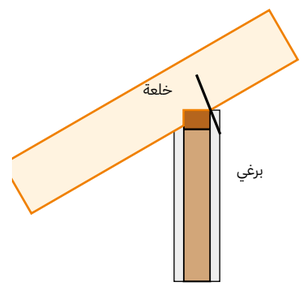

علوي 7×5 على قائم 7×5

المشروع / العميل	عنوان اللوحة	المقياس	التاريخ	رقم اللوحة
مصنع وتد الأخشاب Watad Wood Factory فيلا خشب دورين بواجهة زجاج وشرفة — 12.00 × 9.00 م عميل — فيلا دورين	مسقط السقف والقطاع	1:50	2026-10-31	A-05 (5/11)

جدول مقاسات الأبواب والشبابيك

مقاس الفتحة الصافي في الجدار - الوحدة: سم

الرمز	النوع	العرض (سم)	الارتفاع (سم)	ارتفاع الجلسة (سم)	العدد	الموقع
ب1	باب	100	240	-	1	الأمامية (زجاج)
ب10	باب	76	210	-	2	حمام الماستر - حمام 2
ب10	باب	80	210	-	2	غرفة الملابس - الغسيل
ب2	باب	560	240	-	1	الأمامية (زجاج)
ب3	باب	100	230	-	1	الشرقية
ب4	باب	90	220	-	1	المجلس — المغاسل
ب5	باب	80	220	-	2	المطبخ — الصالون - المطبخ — المغاسل
ب6	باب	70	210	-	1	دورة المياه
ب6	باب	80	210	-	1	المستودع
ب7	باب	300	230	-	1	الأمامية (على الشرفة)
ب7	باب مزدوج	240	230	-	1	الأمامية (على الشرفة)
ب8	باب مزدوج	240	230	-	1	الأمامية (على الشرفة)
ب9	باب	76	210	-	1	جناح الماستر
ب9	باب	90	210	-	2	الماستر — الملابس - غرفة 2
ف1	باب	160	220	-	1	فتحة الصالة الصغيرة
ز1	شباك	260	230	20	1	الأمامية (زجاج)
ش1	شباك	180	160	70	1	الشرقية
ش2	شباك	180	160	70	1	الغربية
ش3	شباك	180	100	110	1	الخلفية
ش4	شباك	100	100	150	2	الخلفية 2
ش5	شباك	60	60	160	3	الخلفية 2 - الغربية
ش6	شباك	140	140	80	1	الغربية

الإجمالي: أبواب 19 - شبابيك 10

جدول المساحات وبيانات المشروع

بيانات المشروع

البند	البيان
المشروع	فيلا خشب دورين بواجهة زجاج وشرفة — 12.00 × 9.00 م
العميل	عميل — فيلا دورين
الموقع	—
الاستخدام	سكن عائلي — مجلس + صالون + غرفتين
التاريخ	2026-10-31
نظام البناء	هيكل خشب 5×7 + تلبيس 2.5 سم من الجهتين
السقف	جملون 30° — قرميد معدني

جدول المساحات

م	الفراغ	الأبعاد (م)	المساحة (م2)
1	أرضي — المجلس	4.58 × 5.08	23.27
2	أرضي — الصالون	4.58 × 6.56	30.04
3	أرضي — المغاسل	1.58 × 5.08	8.03
4	أرضي — دورة مياه	2.36 × 1.94	4.58
5	أرضي — مستودع	2.36 × 3.02	7.13
6	أرضي — المطبخ	4.06 × 3.74	15.18
7	أرضي — مدخل الدرج	1.24 × 2.70	3.35
8	أرضي — الدرج	2.94 × 2.70	7.94
9	أول — غرفة الماستر	4.58 × 5.08	23.27
10	أول — صالة صغيرة	4.58 × 2.88	13.19
11	أول — غرفة نوم 2	4.58 × 3.56	16.30
12	أول — ممر الماستر	1.58 × 5.08	8.03
13	أول — حمام الماستر	2.36 × 2.44	5.76
14	أول — غرفة ملابس	2.36 × 2.52	5.95
15	أول — الممر	1.12 × 6.56	7.35
16	أول — حمام 2	2.88 × 2.34	6.74
17	أول — غسيل	2.88 × 1.28	3.69
	المساحة الصافية الداخلية		189.78
	التراس	2.20 × 12.00	26.40
	عتبة	**1.60 × 1.40**	**2.24**
	الشرفة	**2.20 × 12.00**	**26.40**
	المساحة الإجمالية المبنية	**12.00 × 9.00 × 2 دور**	**216.00**
	المساحة الكلية (المبنية + التراسات)		**271.04**

لقطات المنظور الخارجي

المنظور الأمامي




منظور أمامي من اليسار




منظور أمامي من اليمين




المنظور الخلفي

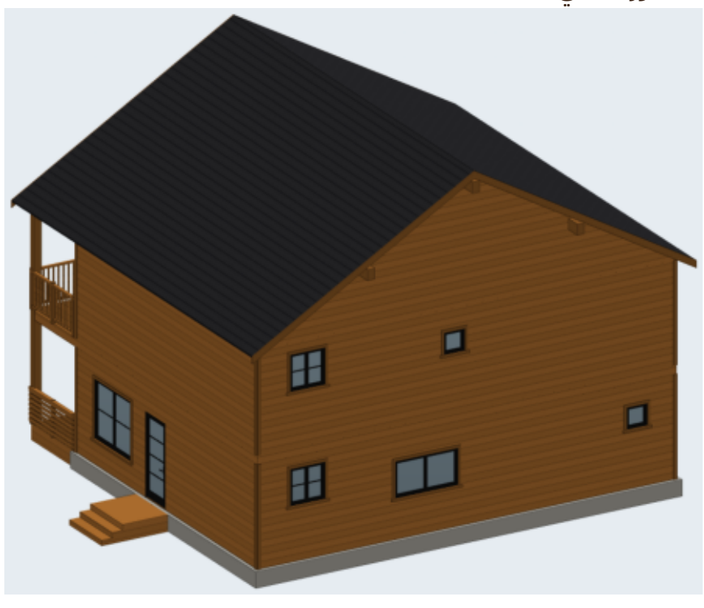

منظور خلفي من اليمين

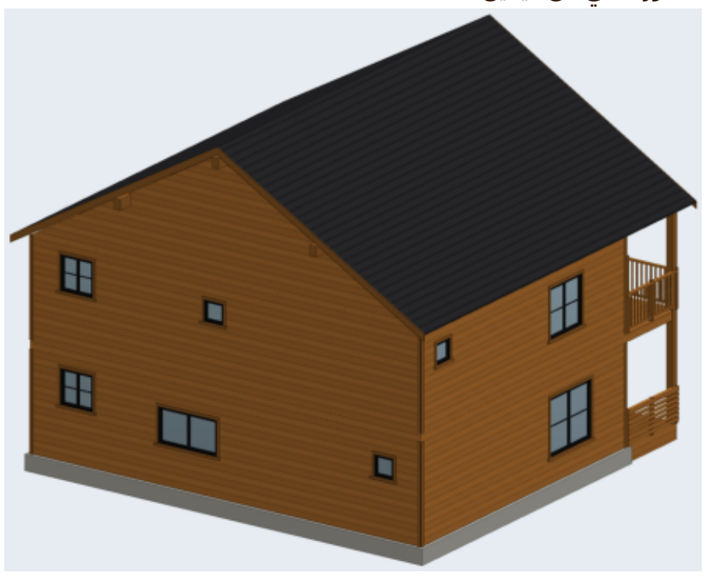

منظر علوي

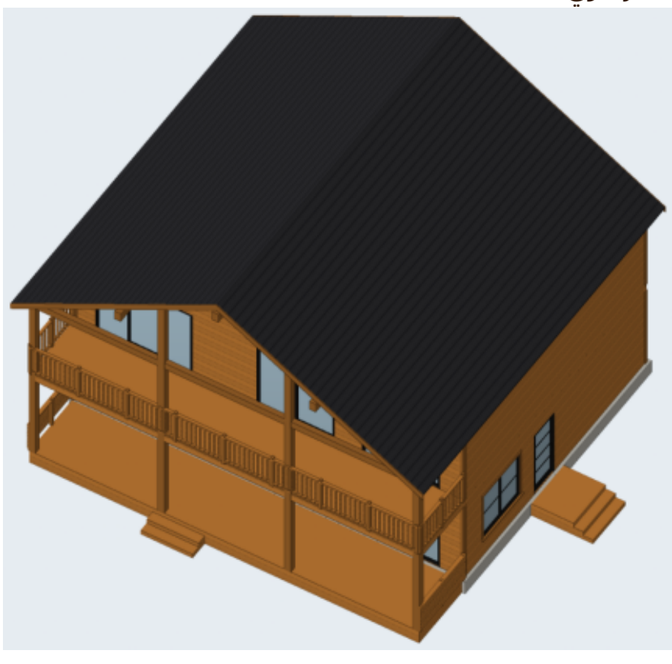


المشروع / العميل	عنوان اللوحة	المقياس	التاريخ	رقم اللوحة
فيلا خشب دورين بواجهة زجاج وشرفة — 12.00 × 9.00 م **عميل — فيلا دورين**	**لقطات المنظور**	**—**	**2026-10-31**	**A-08 (8/11)**

مصنع وتد الأخشاب
Watad Wood Factory

المقطع العلوي بالفرش — الدور الأرضي


مقطع أفقي على ارتفاع 1.90 م — توزيع الفرش ومسار الحركة

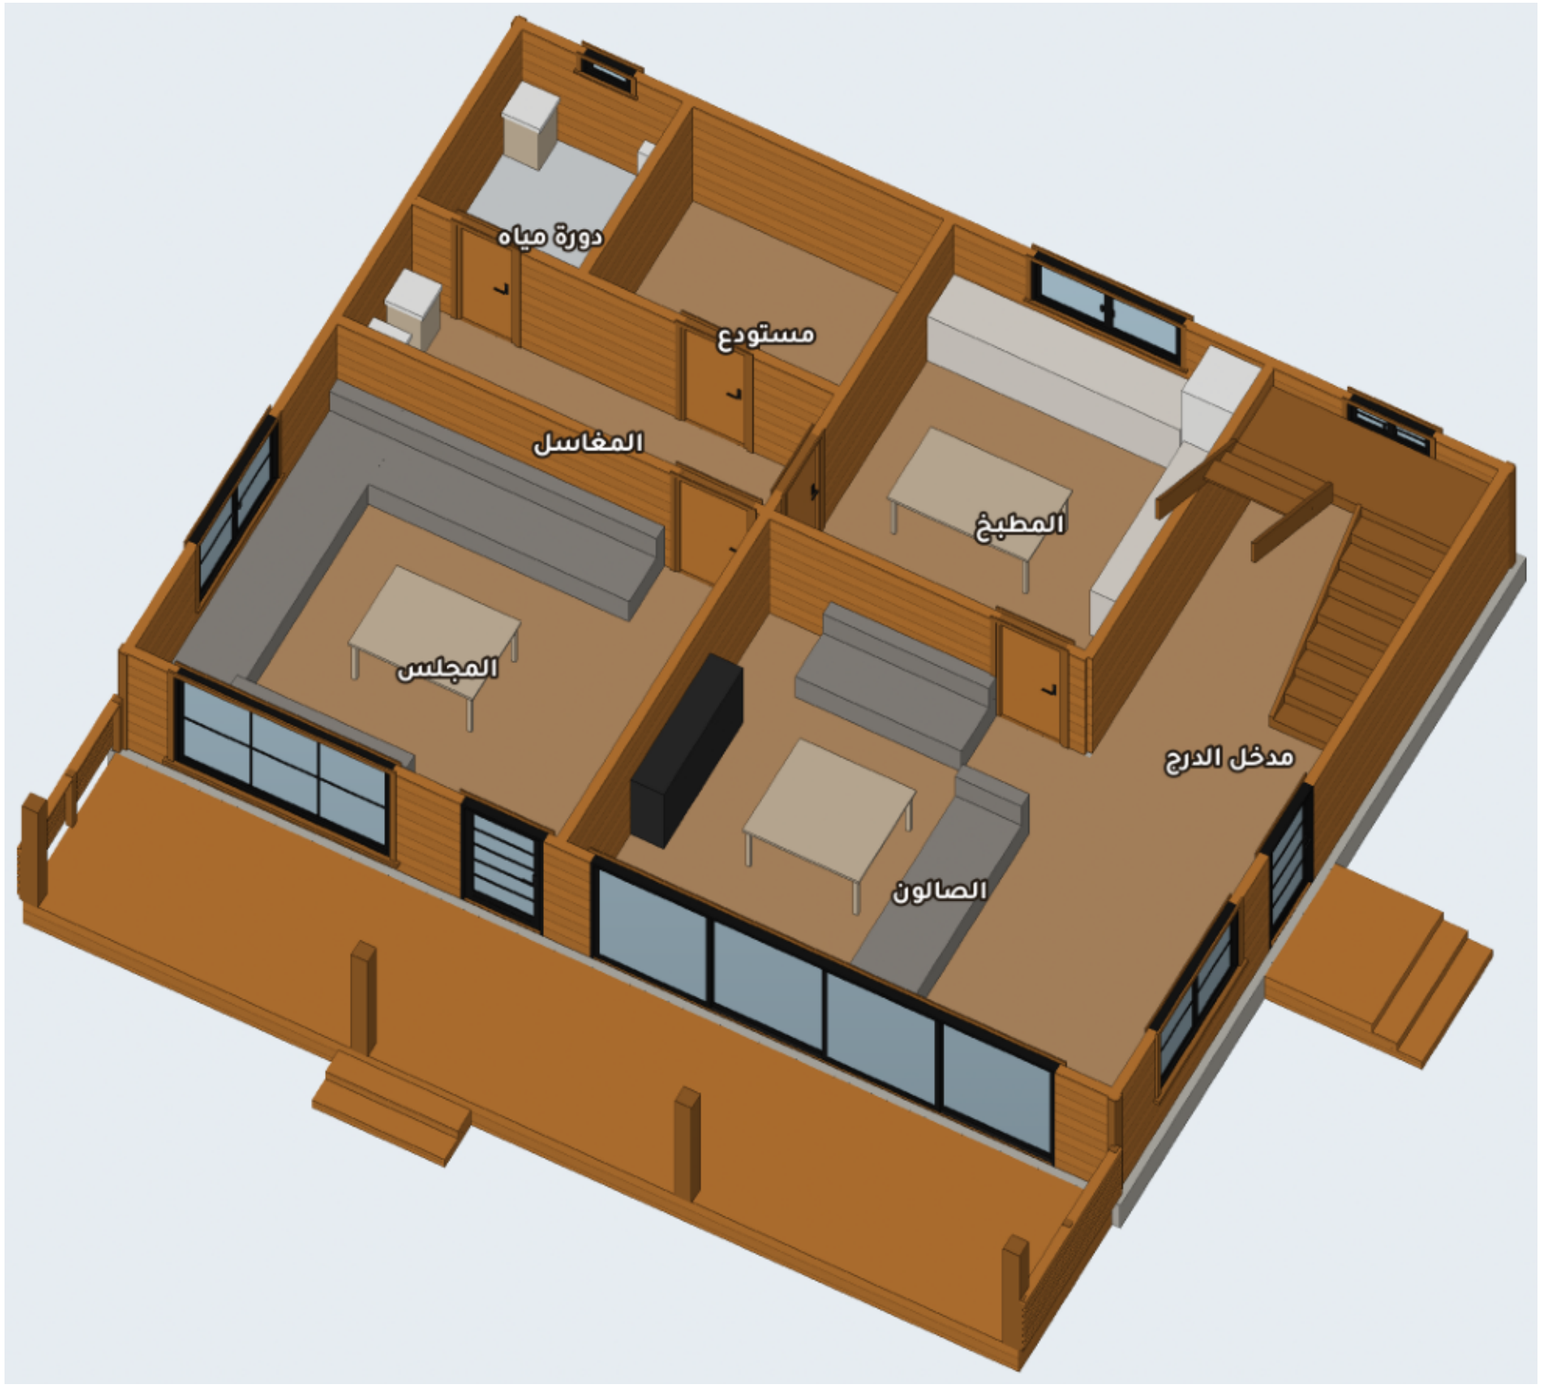

المشروع / العميل	عنوان اللوحة	المقياس	التاريخ	رقم اللوحة
مصنع وتد الأخشاب — Watad Wood Factory فيلا خشب دورين بواجهة زجاج وشرفة — 12.00 × 9.00 م عميل — فيلا دورين	المقطع العلوي بالفرش — الدور الأرضي	—	2026-10-31	A-09 (9/11)

المقطع العلوي بالفرش — الدور الأول

مقطع أفقي على ارتفاع 1.90 م — توزيع الفرش ومسار الحركة

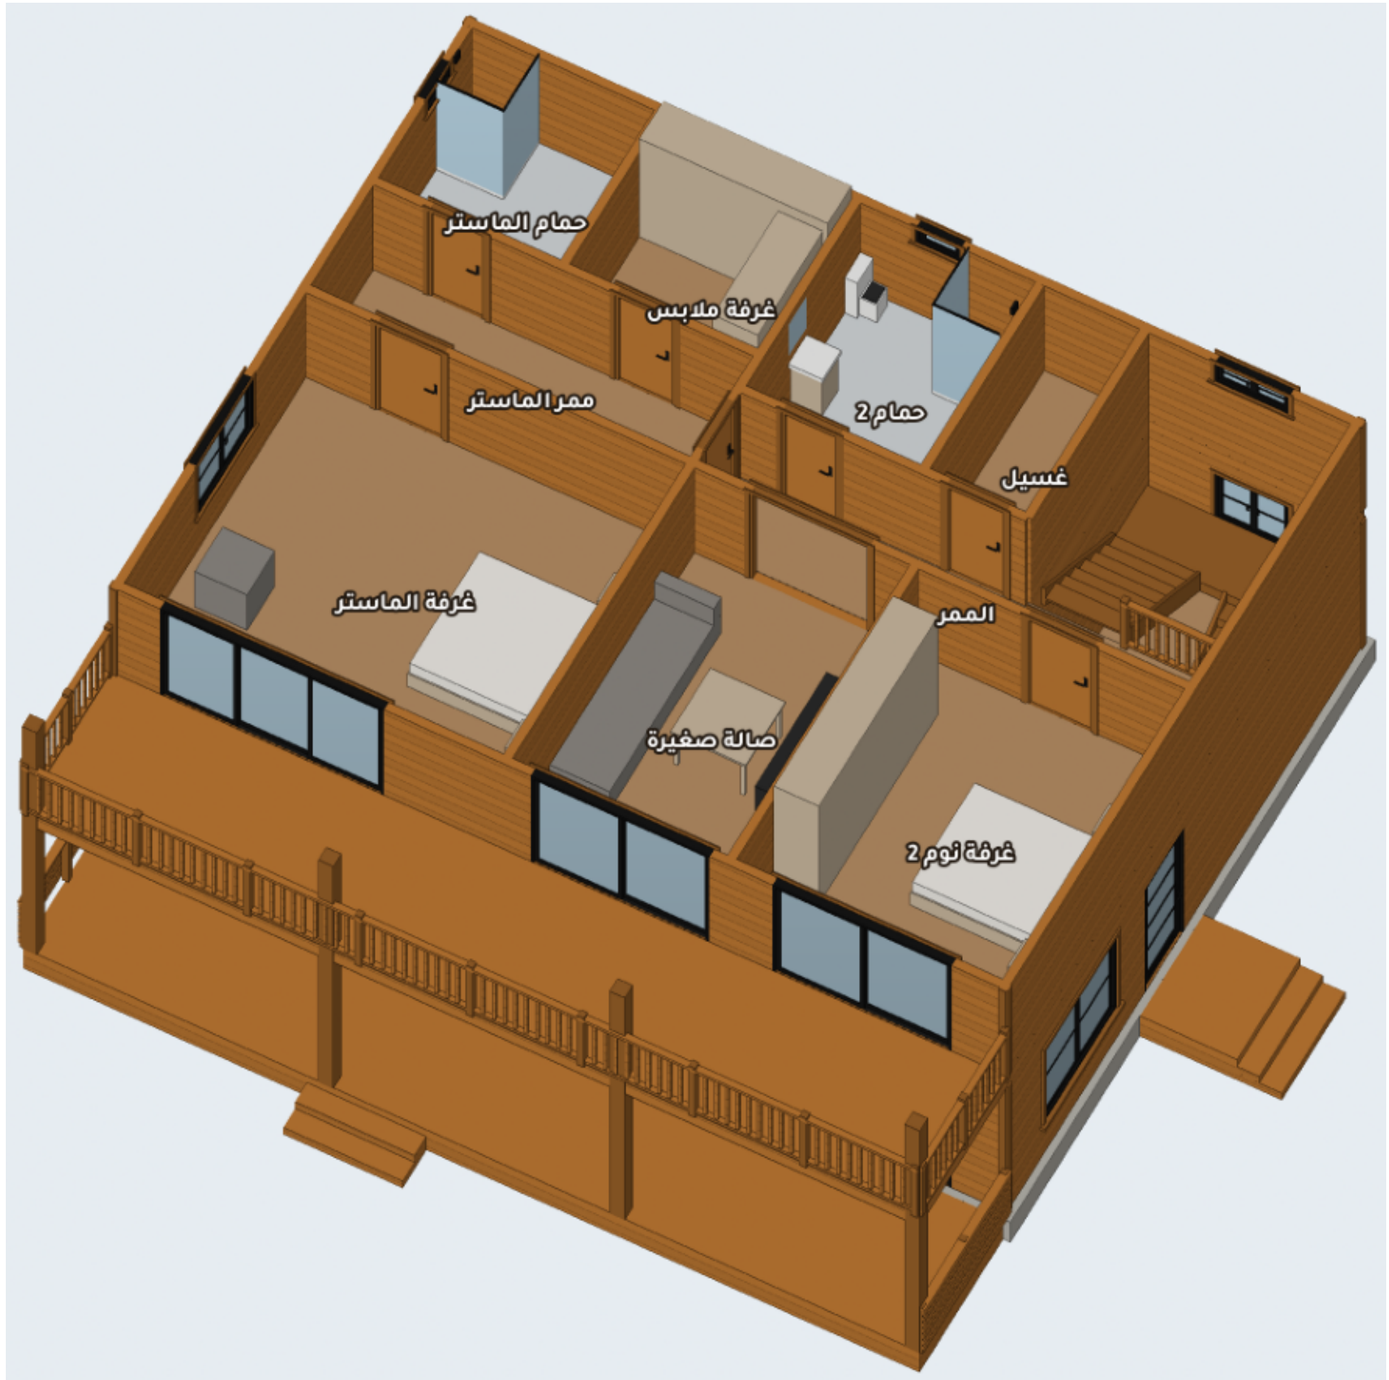


المشروع / العميل	عنوان اللوحة	المقياس	التاريخ	رقم اللوحة
فيلا خشب دورين بواجهة زجاج وشرفة — 12.00 × 9.00 م عميل — فيلا دورين	المقطع العلوي بالفرش — الدور الأول	—	2026-10-31	A-10 (10/11)

مصنع وتد الأخشاب
Watad Wood Factory

المنظور ثلاثي الأبعاد والمواد

النمط: جوزي غامق + إطارات سوداء — رندر واقعي بخامات حقيقية

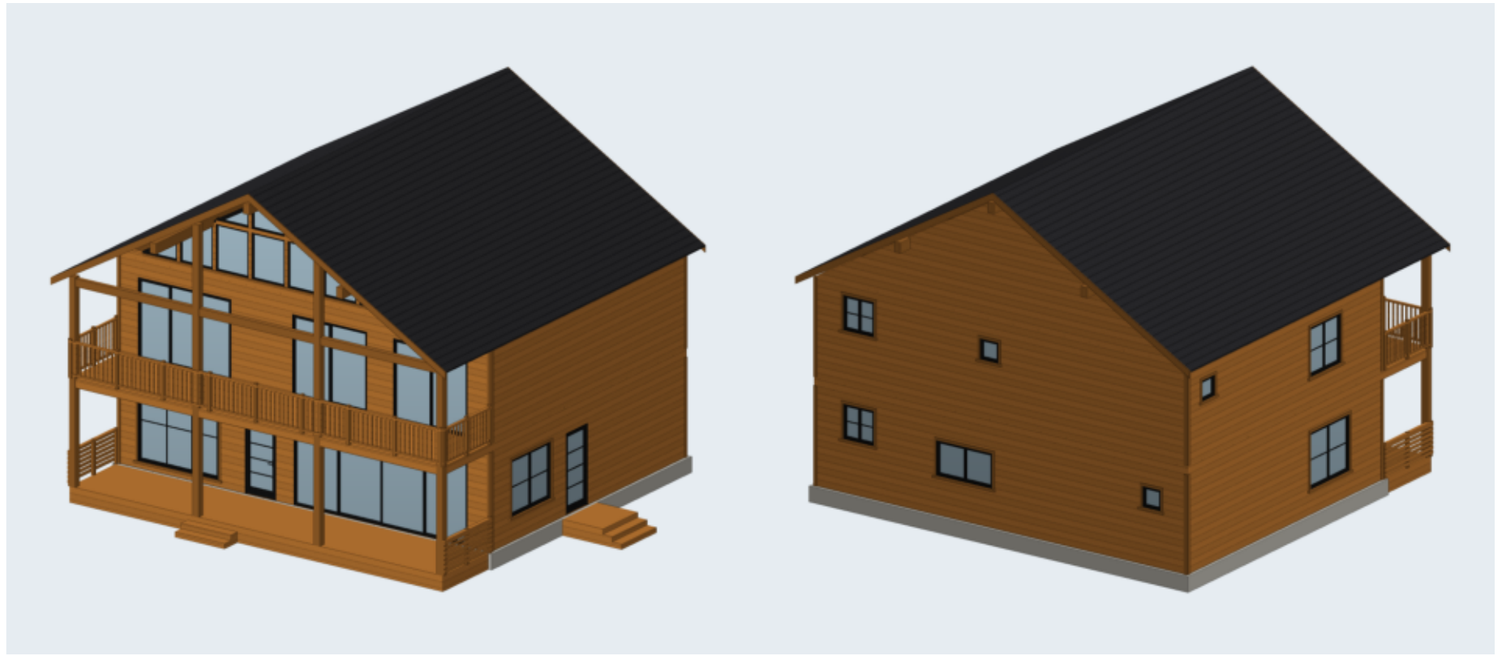

جدول المواد والألوان

الخشب / الصبغة

صبغة عسلي / سيدر

القرميد

قرميد رمادي غامق

الزجاج

زجاج شفاف

إطارات الشبابيك والأبواب

إطار ألمنيوم أسود

الكنار والزوايا

نفس الصبغة أغمق درجة


الصبة

خرسانة 45 سم


الدربزين: ألواح أفقية متقاربة (عصري)

تقسيم الشبابيك: بدون | الباب الرئيسي: زجاج بتقسيمات (فرنسي)

أنواع الدربزين المعتمدة (من مشاريع المصنع)

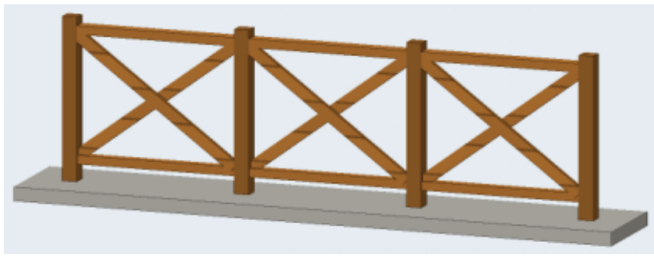

تقاطع X (صورة 5)

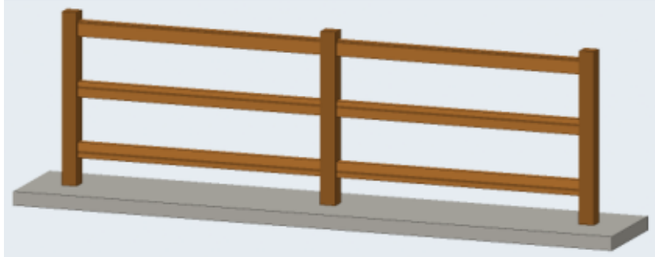

3 مرابيع أفقية (صورة 2)



قوائم رأسية متقاربة (صورة 1)

المشروع / العميل	عنوان اللوحة	المقياس	التاريخ	رقم اللوحة
فيلا خشب دورين بواجهة زجاج وشرفة — 12.00 × 9.00 م **عميل — فيلا دورين**	**المنظور والمواد**	—	**2026-10-31**	**A-11 (11/11)**

مصنع وتد الأخشاب
Watad Wood Factory