
جدول مساحات الموقع

البند	المقاس	المساحة (م²)
مساحة الأرض	19.00 × 27.00 م	513.0
مسطح الكوخ (البصمة)	9.00 × 9.00 م	81.0
تراس الكوخ	1.50 × 5.58 م	8.4
جلسة خارجية	3.20 × 7.60 م	24.3
بلاط		47.1
موقف سيارة	4.70 × 11.40 م	53.6
ممر	1.10 × 11.34 م	12.5
المسطحات الخضراء (حديقة)	الباقي	286.1

الموقع العام وتنسيق الحديقة (لاندسكيب)

الأرض 19 × 27 م = 513 م² | الأبعاد بالسنتيمتر

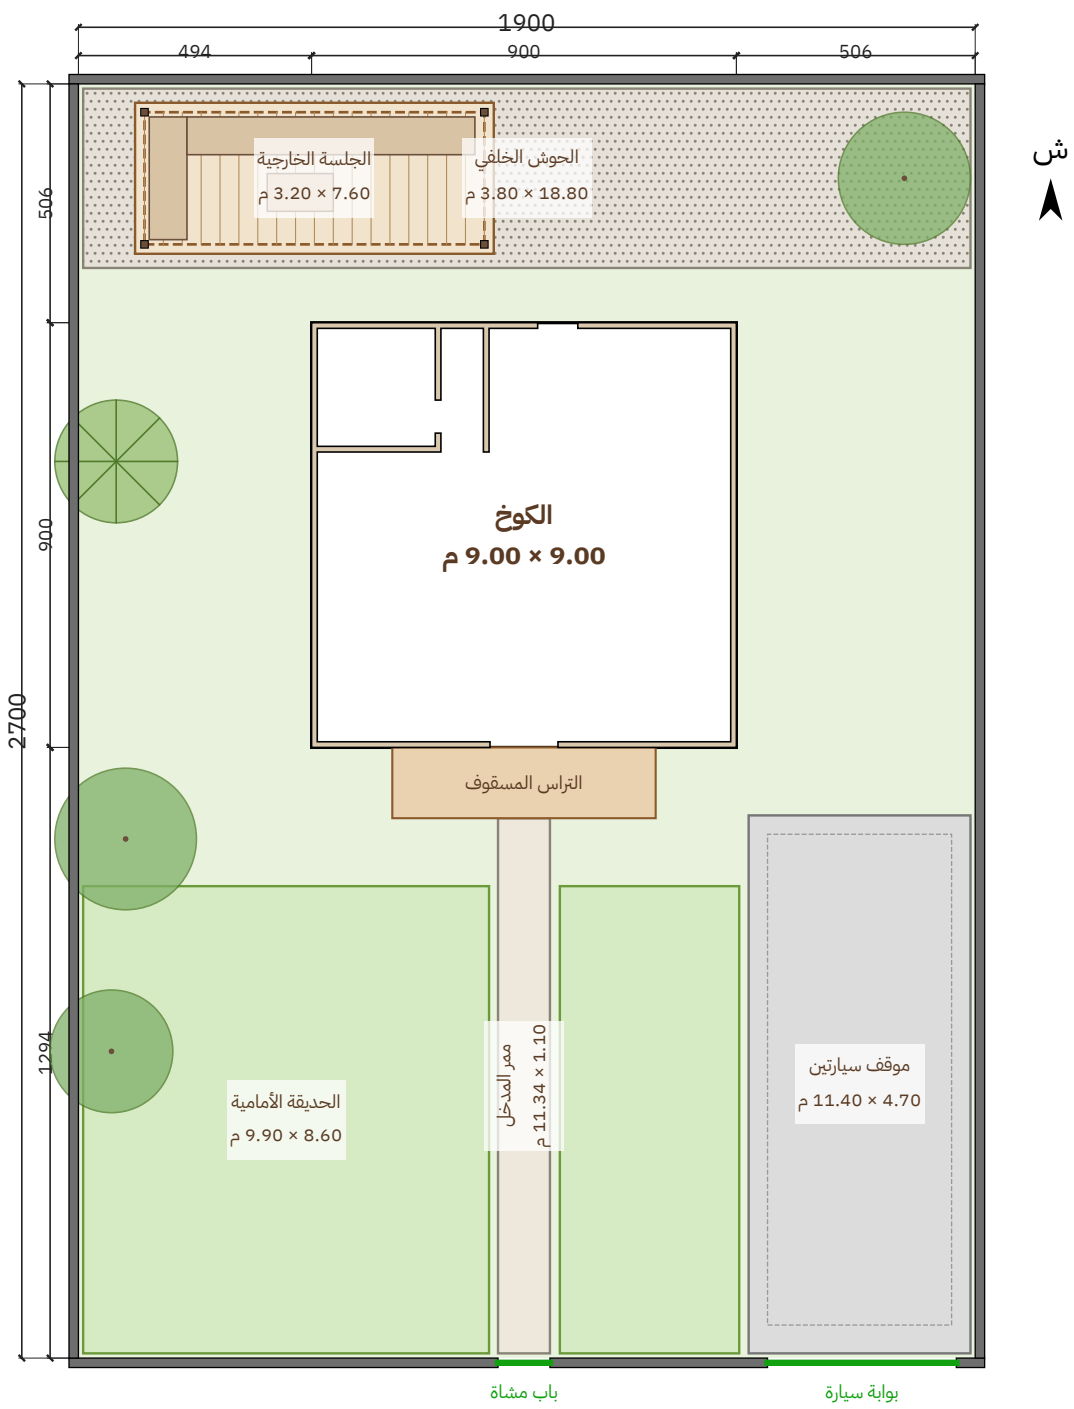


شارع عرض 16 م

المشروع / العميل	عنوان اللوحة	المقياس	التاريخ	رقم اللوحة
كوخ A-frame دورين — صالة ومطبخ وحمام + غرفتين وحمام وشرفة داخلية — 9.00 × 9.00 م عميل — A-frame 9×9	الموقع العام واللاندسكيب	1:200	2026-10-26	A-01 (1/11)

مصنع وتد الأخشاب
Watad Wood Factory

المسقط الأفقي مع الفرش


الأبعاد بالسنتيمتر - الجدران: قوائم 5×7 + تلبيس 2.5 من الجهتين (12 سم)

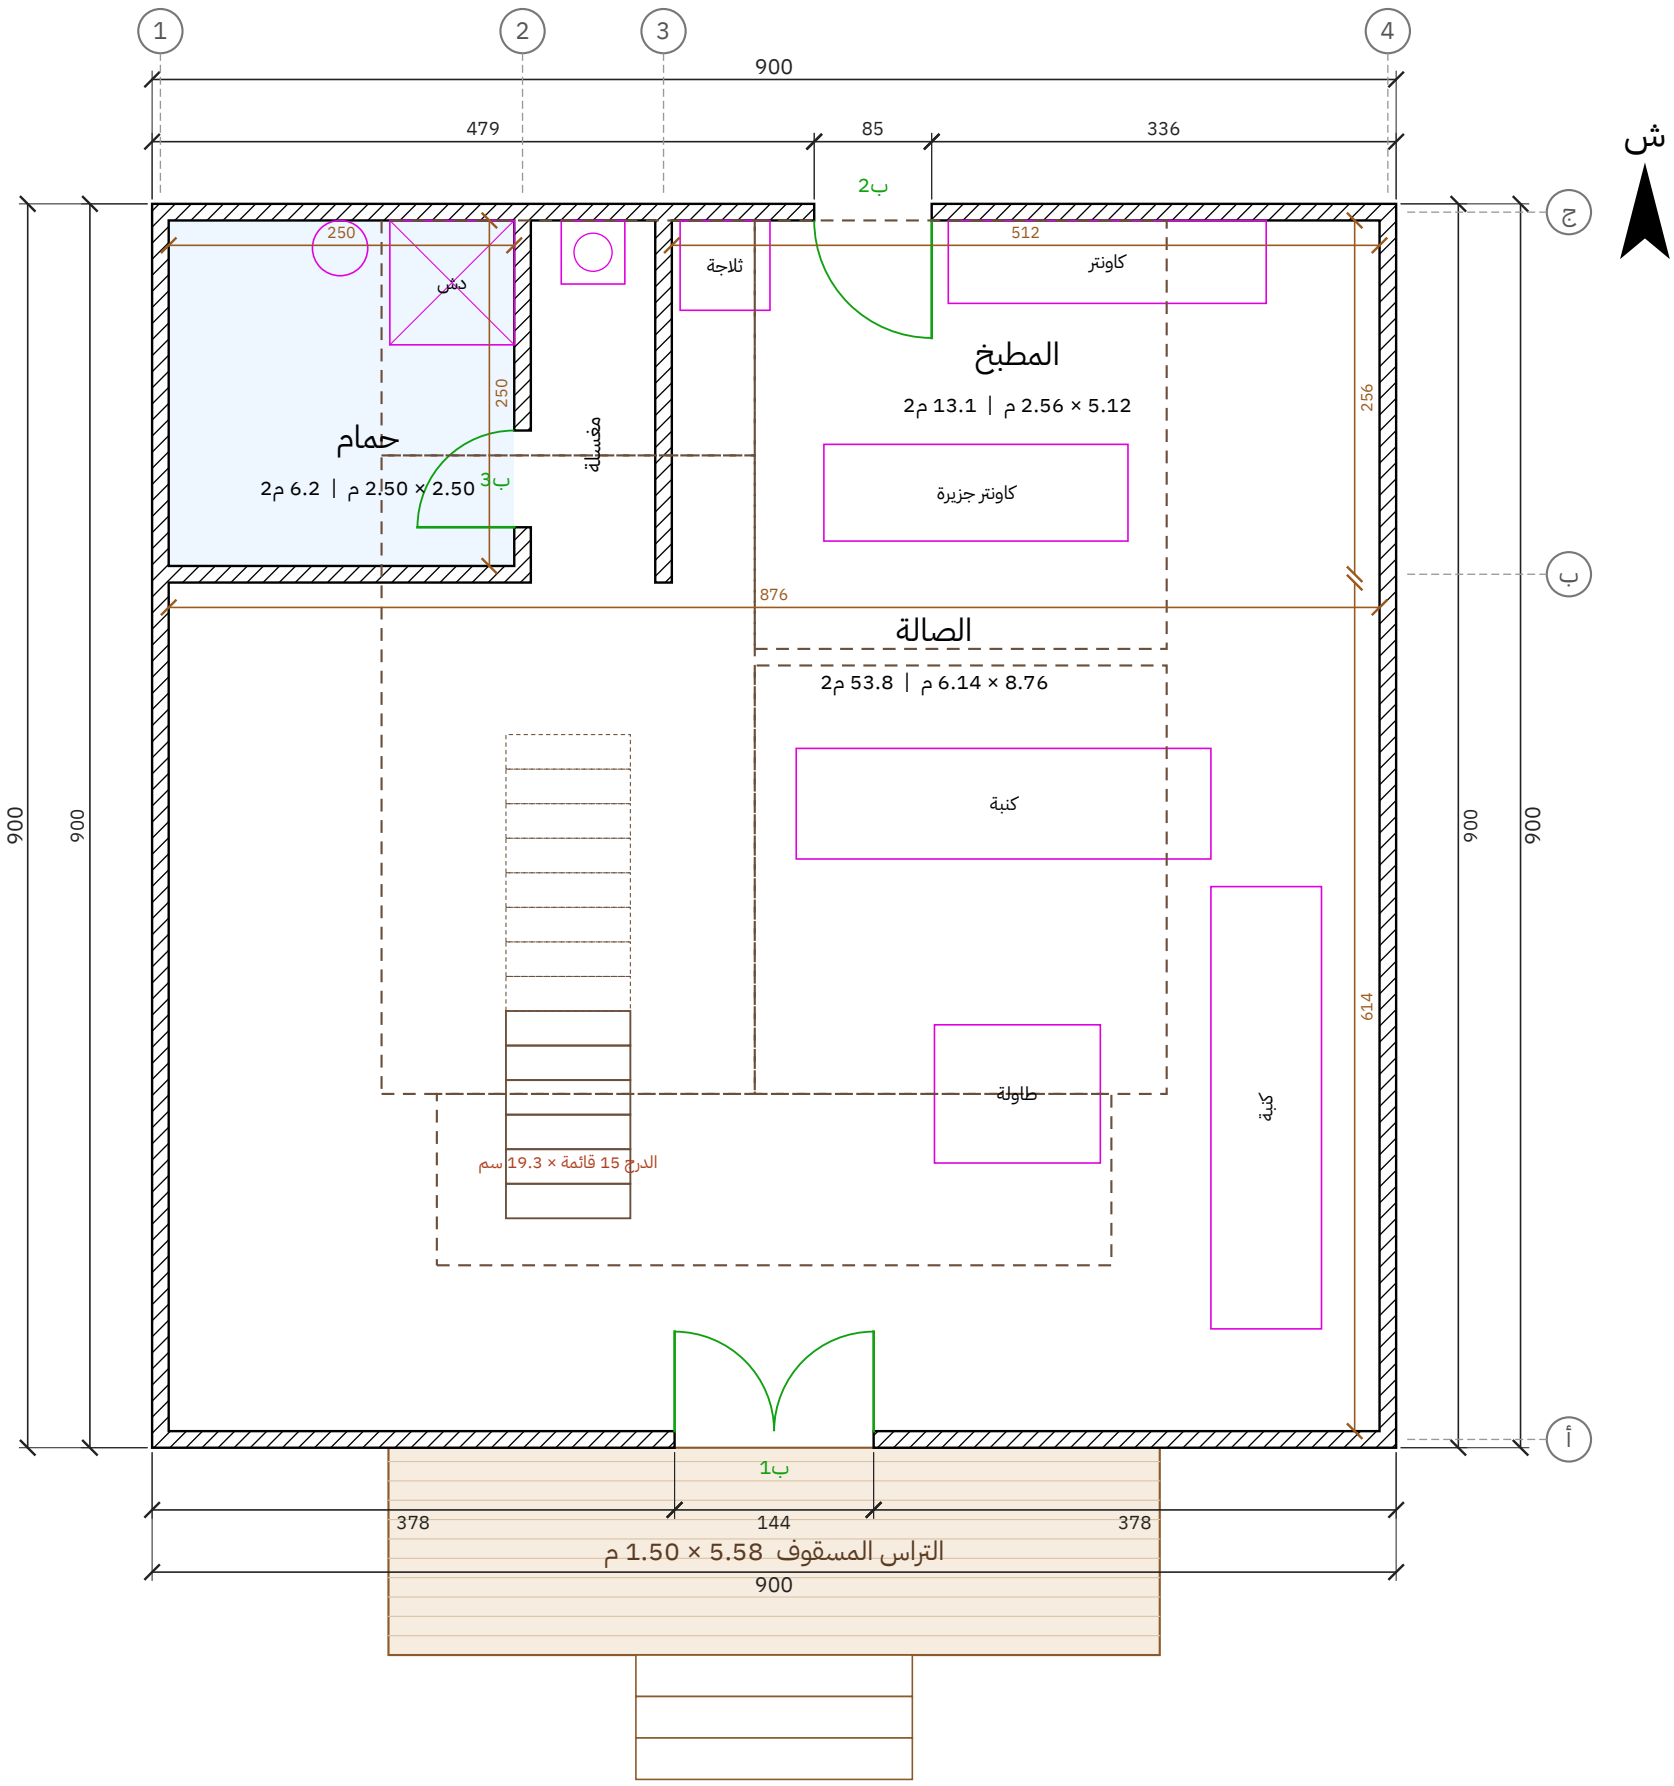


مصنع وتد الأخشاب Watad Wood Factory	المشروع / العميل كوخ A-frame دورين — صالة ومطبخ وحمام + غرفتين وحمام وشرفة داخلية — 9.00 × 9.00 م عميل — A-frame 9×9	عنوان اللوحة المسقط الأفقي	المقياس 1:50	التاريخ 2026-10-26	رقم اللوحة A-02 (2/11)

المسقط الأفقي مع الفرش — الدور الأول (شرفة داخلية بعد الزجاج 1.20 م)

منسوب الأرضية +2.90 | الأبعاد بالسنتيمتر | الوقفة الكاملة ≥ 2.10 م بين الخطين المتقطعين

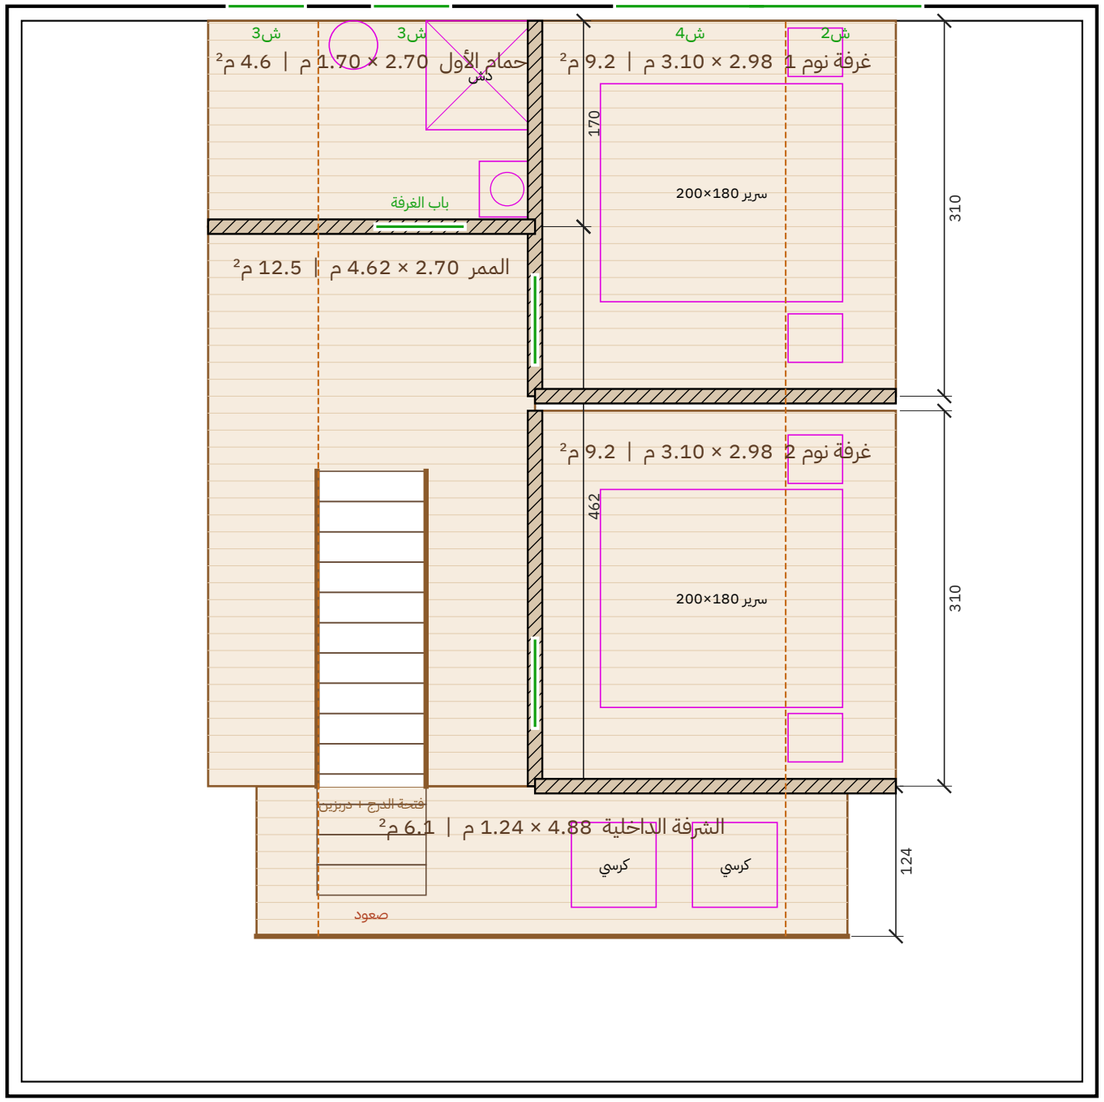


مصنع وتد الأخشاب Watad Wood Factory	المشروع / العميل كوخ A-frame دورين — صالة ومطبخ وحمام + غرفتين وحمام وشرفة داخلية — 9.00 × 9.00 م عميل — A-frame 9×9	عنوان اللوحة المسقط الأفقي مع الفرش — الدور الأول (شرفة داخلية بعد الزجاج 1.20 م)	المقياس 1:50	التاريخ 2026-10-26	رقم اللوحة A-03 (3/11)

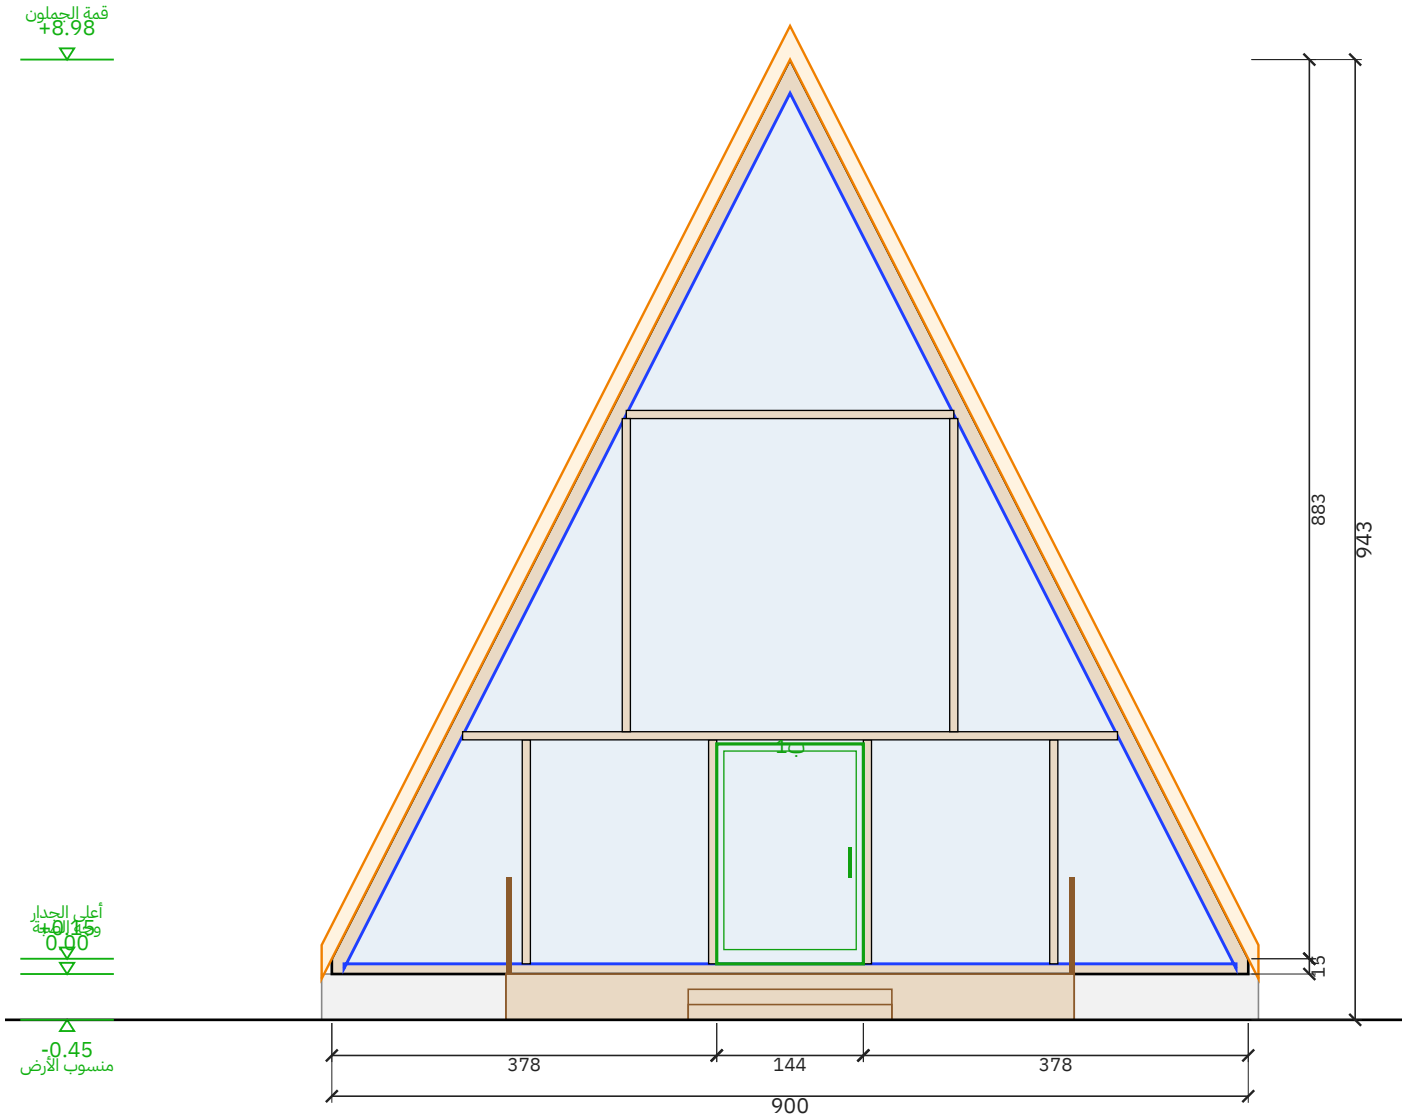

الواجهة الأمامية (مثلث زجاج كامل)

مقياس 1:50 | الوحدة: سم

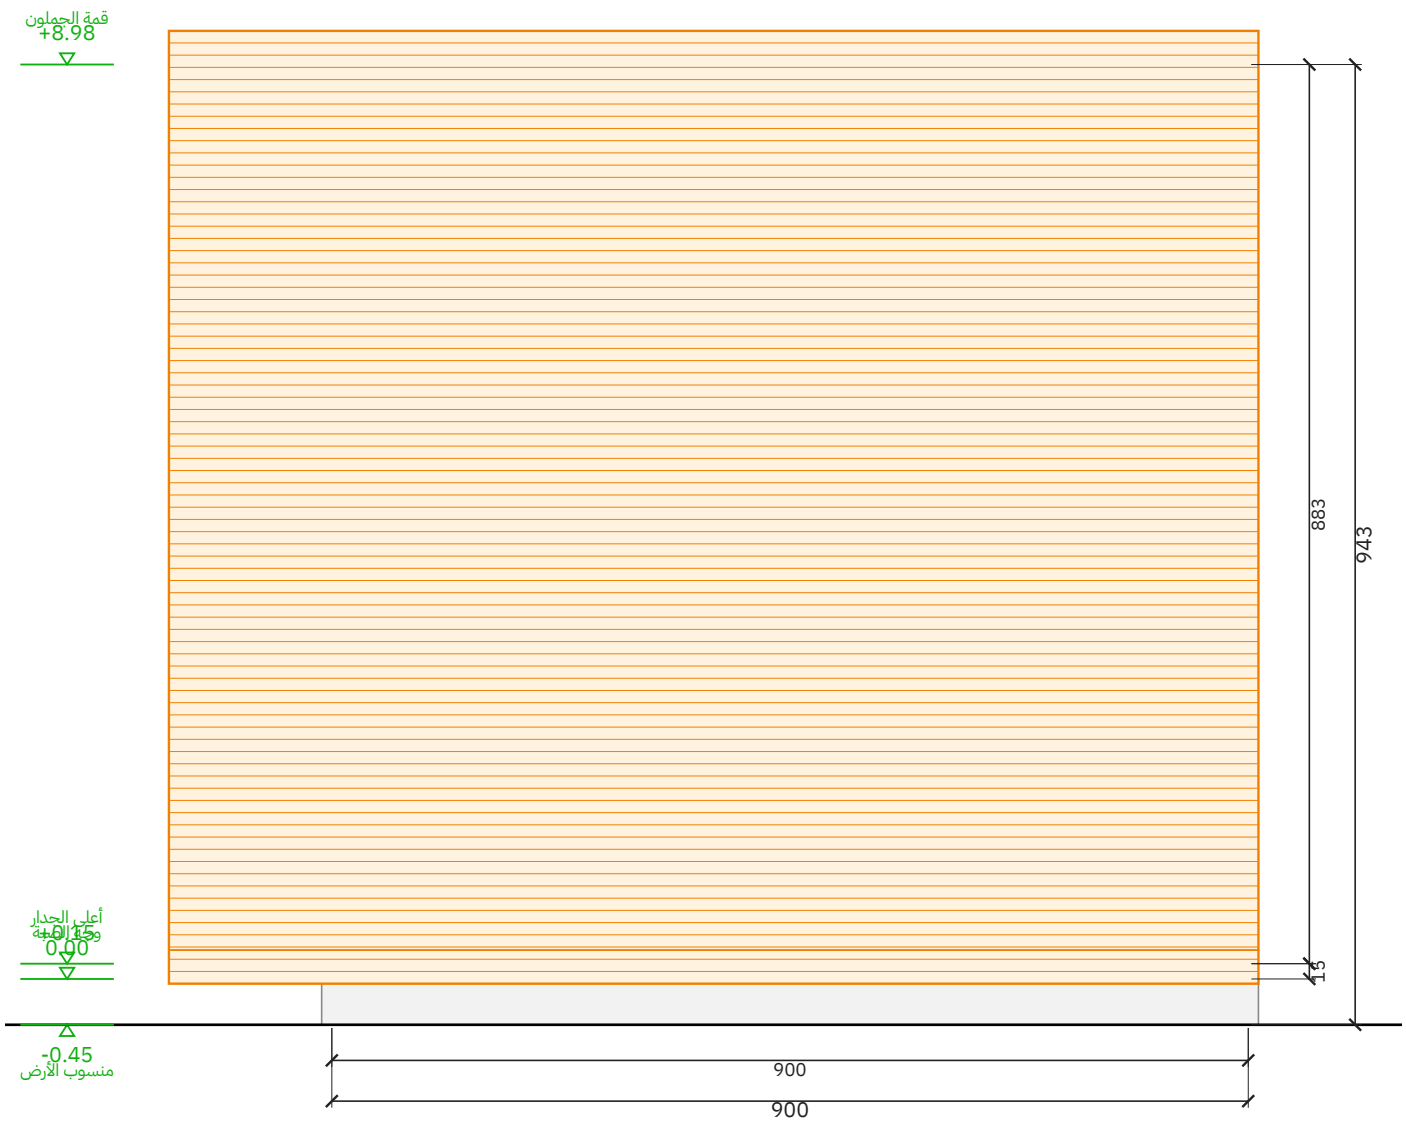


الواجهة الشرقية (السقف لين الأرض)

مقياس 1:50 | الوحدة: سم


المشروع / العميل	عنوان اللوحة	المقياس	التاريخ	رقم اللوحة
كوخ A-frame دورين — صالة ومطبخ وحمام + غرفتين وحمام وشرفة داخلية — 9.00 × 9.00 م عميل — A-frame 9×9	الواجهة الأمامية (مثلث زجاج كامل) والواجهة الشرقية (السقف لين الأرض)	1:50	2026-10-26	A-04 (4/11)

مصنع وتد الأخشاب
Watad Wood Factory

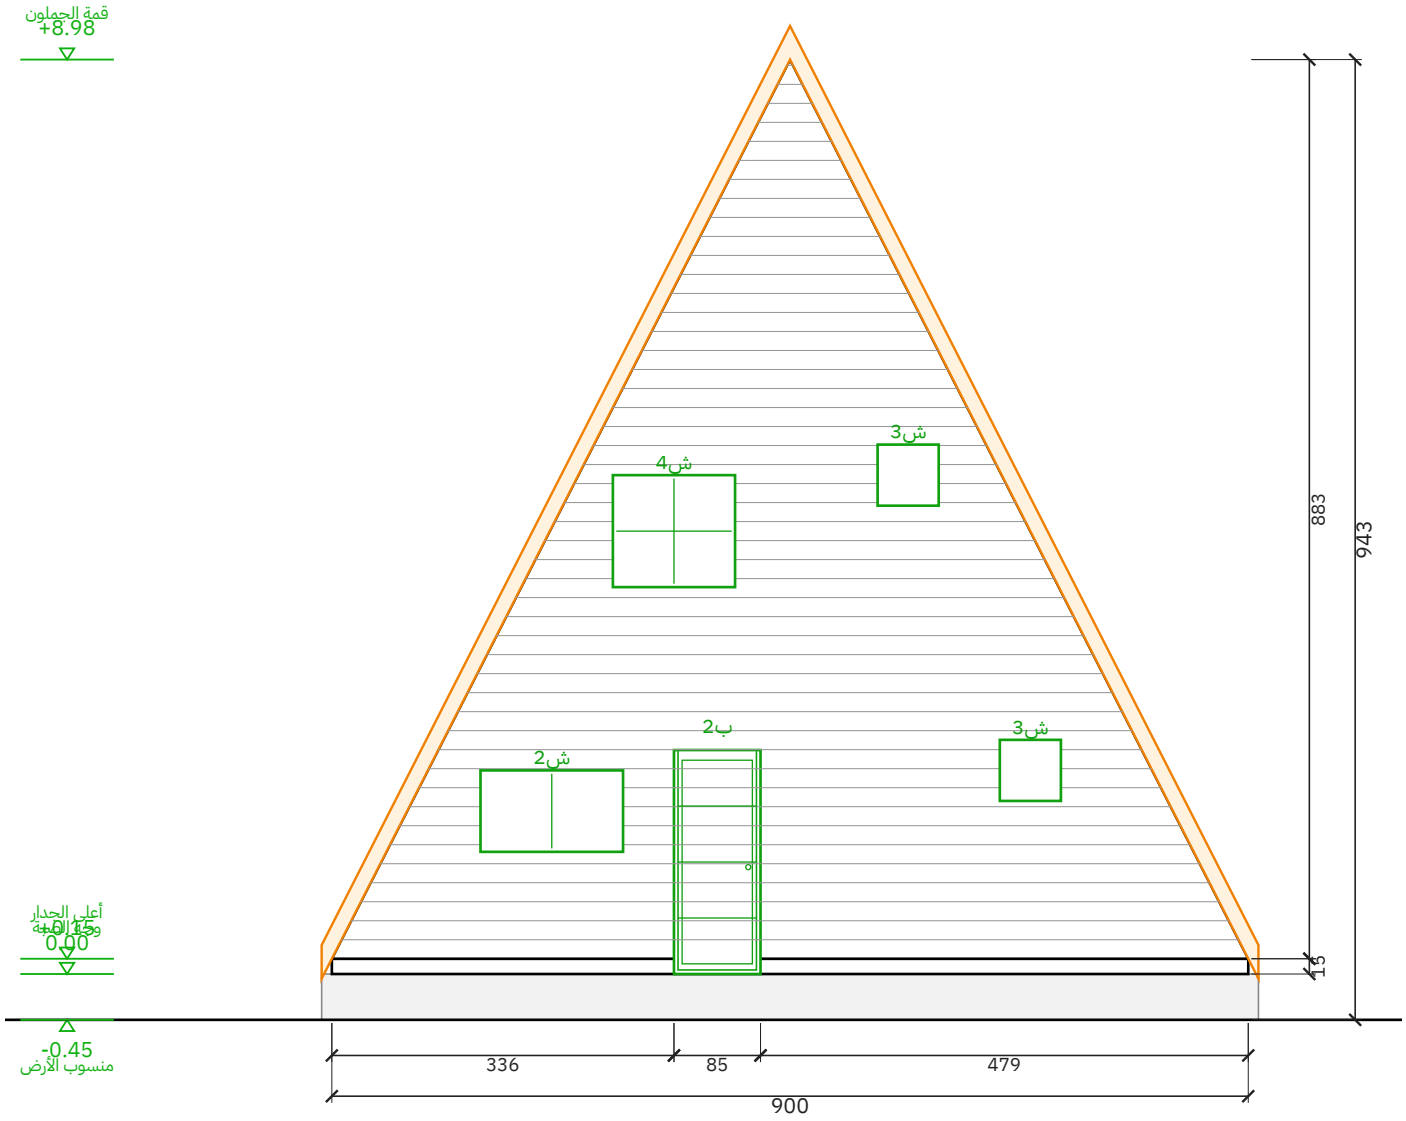

الواجهة الخلفية

مقياس 1:50 | الوحدة: سم

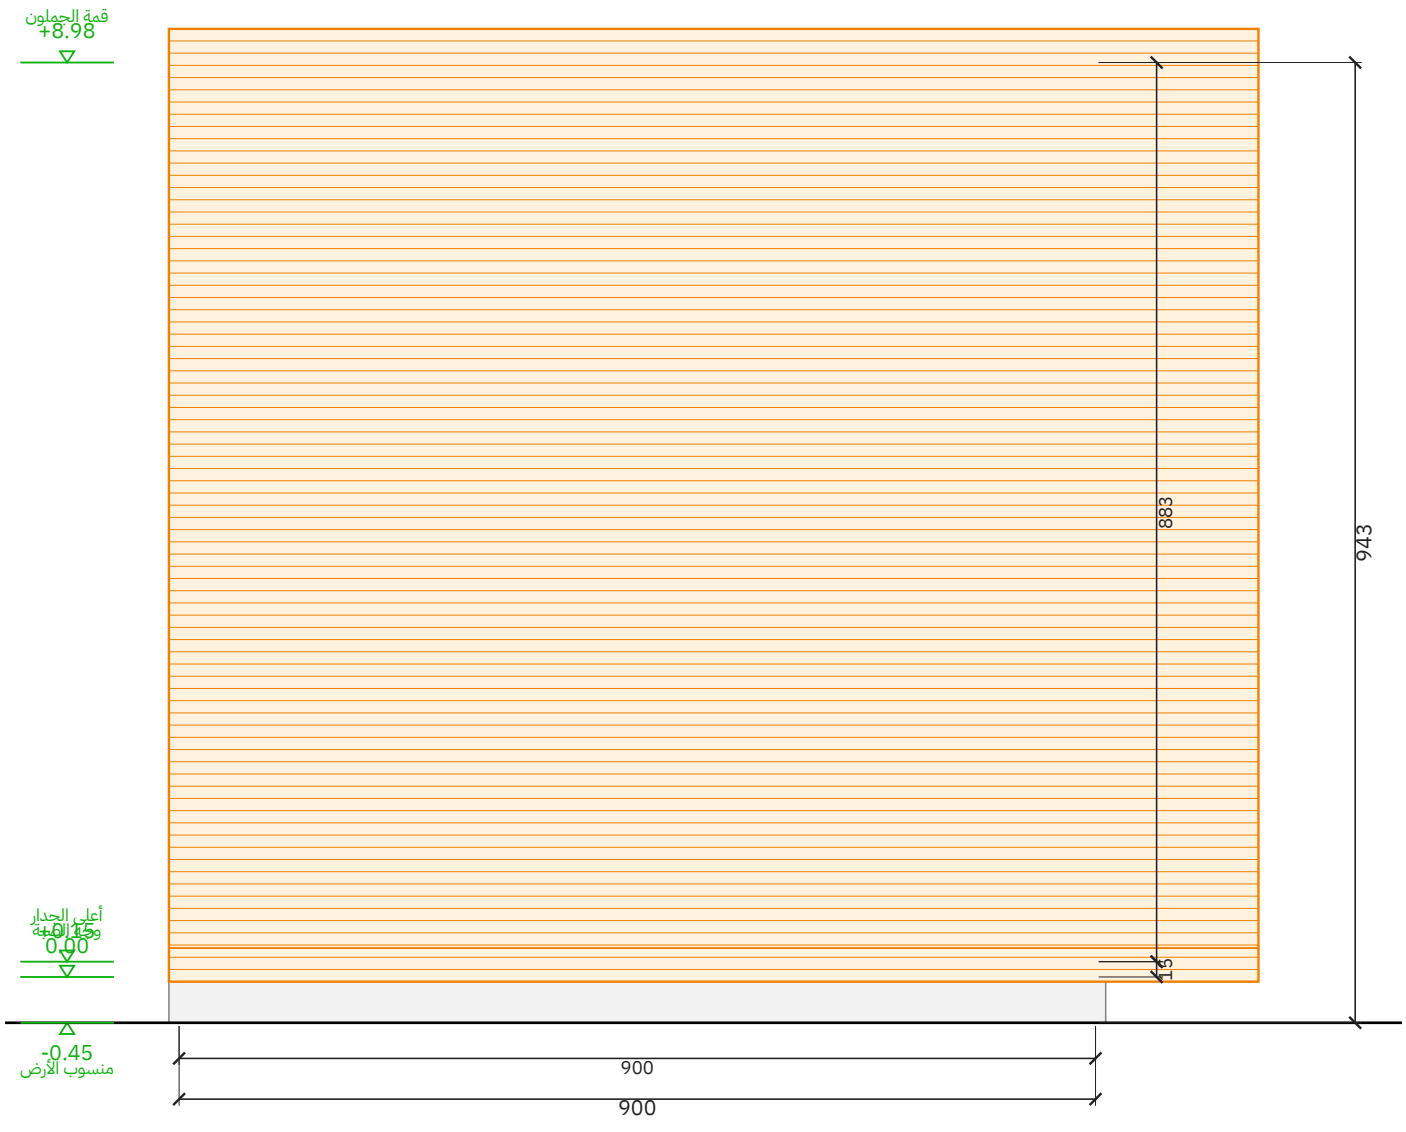

الواجهة الغربية (السقف لين الأرض)


مقياس 1:50 | الوحدة: سم

المشروع / العميل	عنوان اللوحة	المقياس	التاريخ	رقم اللوحة
كوخ A-frame دورين — صالة ومطبخ وحمام + غرفتين وحمام وشرفة داخلية — 9.00 × 9.00 م عميل — A-frame 9×9	الواجهة الخلفية والواجهة الغربية (السقف لين الأرض)	1:50	2026-10-26	A-05 (5/11)

مصنع وتد الأخشاب
Watad Wood Factory


مسقط السقف (جملون)

رفرف 10 سم من كل جهة | مقياس 1:50

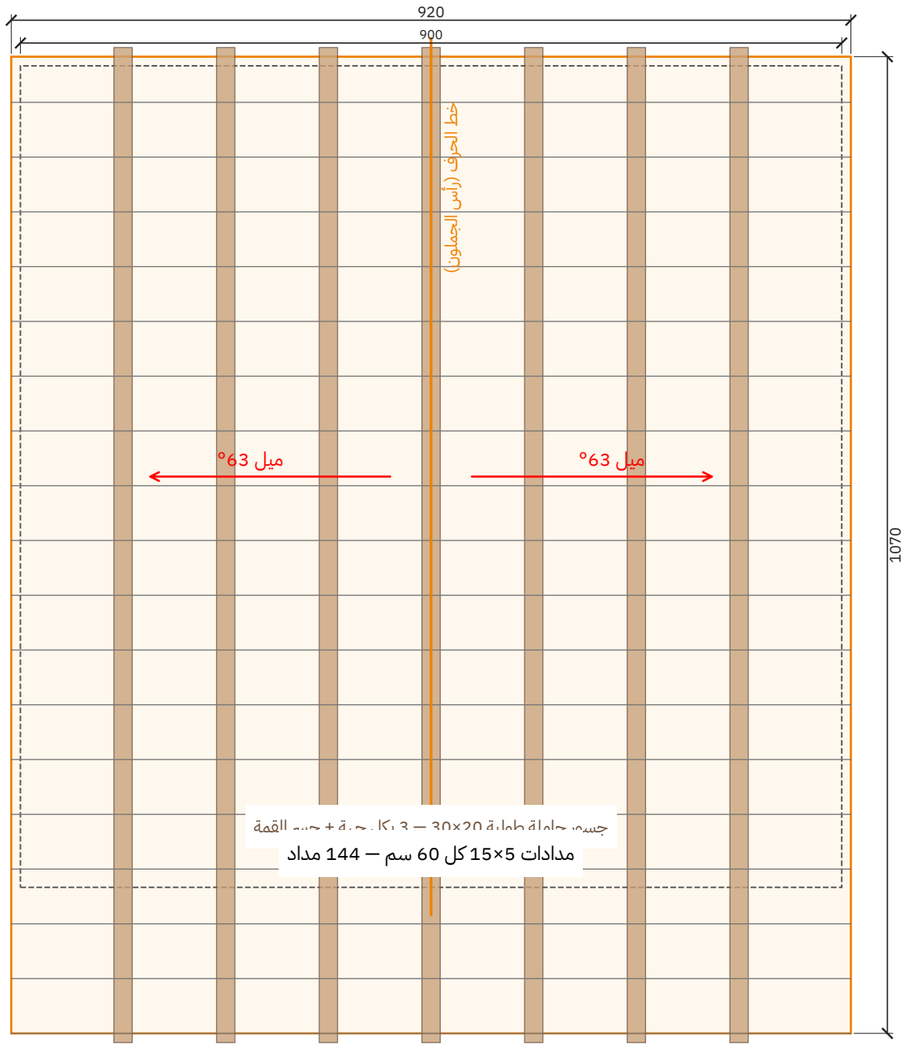


قطاع عرضي أ-أ

مقياس 1:50 | الوحدة: سم

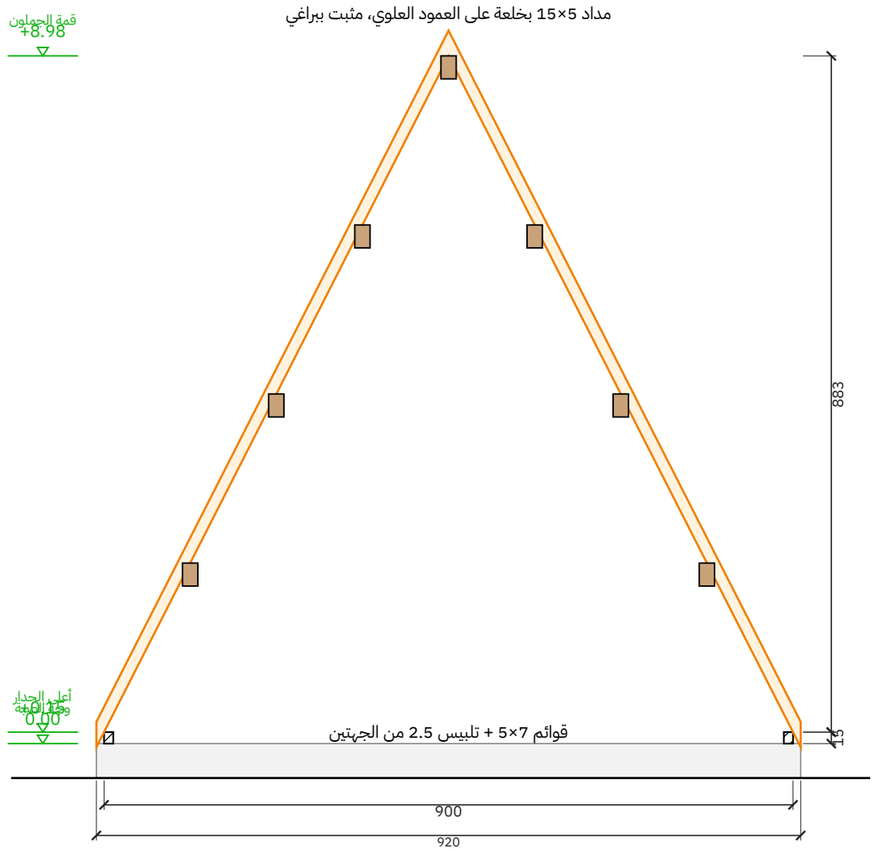

تفصيلة جلوس المداد على العلوي (1:5)

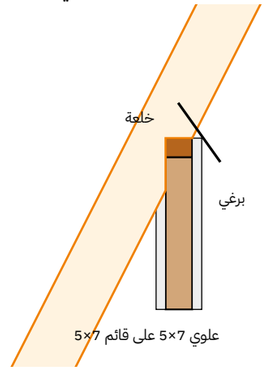

المشروع / العميل كوخ A-frame دورين — صالة ومطبخ وحمام + غرفتين وحمام وشرفة داخلية — 9.00 × 9.00 م عميل — A-frame 9×9	عنوان اللوحة مسقط السقف والقطاع	المقياس 1:50	التاريخ 2026-10-26	رقم اللوحة A-06 (6/11)

مصنع وتد الأخشاب
Watad Wood Factory

جدول مقاسات الأبواب والشبابيك

مقاس الفتحة الصافي في الجدار - الوحدة: سم

الرمز	النوع	العرض (سم)	الارتفاع (سم)	ارتفاع الجلسة (سم)	العدد	الموقع
ب1	باب مزدوج	144	230	-	1	الأمامية (مثلث زجاج كامل)
ب2	باب	85	220	-	1	الخلفية
ب3	باب	70	210	-	1	الحمام (من المغسلة)
ش2	باب	140	80	-	1	الخلفية
ش3	باب	60	60	-	2	الخلفية 2
ش4	باب	120	110	-	1	الخلفية

الإجمالي: أبواب 7 - شبابيك 0

جدول المساحات وبيانات المشروع

بيانات المشروع


البند	البيان
المشروع	كوخ A-frame دورين — صالة ومطبخ وحمام + غرفتين وحمام وشرفة داخلية — 9.00 × 9.00 م
العميل	عميل — A-frame 9×9
الموقع	—
الاستخدام	سكن / استراحة
التاريخ	2026-10-26
نظام البناء	هيكل خشب 5×7 + تلبيس 2.5 سم من الجهتين
السقف	جملون 63° — قرميد معدني

جدول المساحات


م	الفراغ	الأبعاد (م)	المساحة (م2)
1	الصالة	6.14 × 8.76	53.79
2	حمام	2.50 × 2.50	6.25
3	مغسلة	0.90 × 2.50	2.25
4	المطبخ	2.56 × 5.12	13.11
5	أول — الشرفة الداخلية	1.24 × 4.88	6.05
6	أول — الممر	2.70 × 4.62 – فتحة الدرج	10.13
7	أول — غرفة نوم 2	3.10 × 2.98	9.24
8	أول — غرفة نوم 1	3.10 × 2.98	9.24
9	أول — حمام الأول	1.70 × 2.70	4.59
	المساحة الصافية الداخلية		114.64
	التراس المسقوف	1.50 × 5.58	8.37
	مسطح الأرضي	**9.00 × 9.00**	**81.00**
	مسطح الدور الأول (داخل المثلث)		**39.25**
	المساحة الإجمالية المبنية (الأرضي + الأول)	**مجموع الأدوار**	**120.25**
	المساحة الكلية (المبنية + التراس)		**128.62**

لقطات المنظور الخارجي


المنظور الأمامي

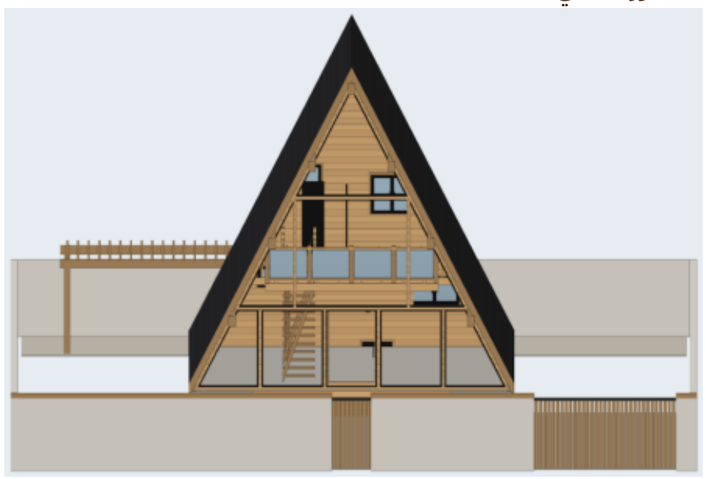


منظور أمامي من اليسار

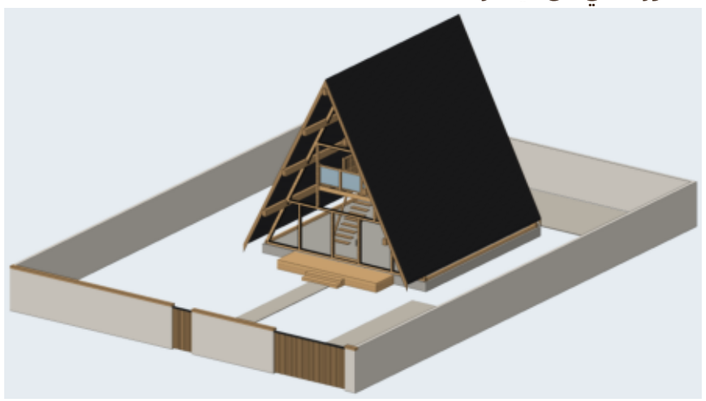


منظور أمامي من اليمين

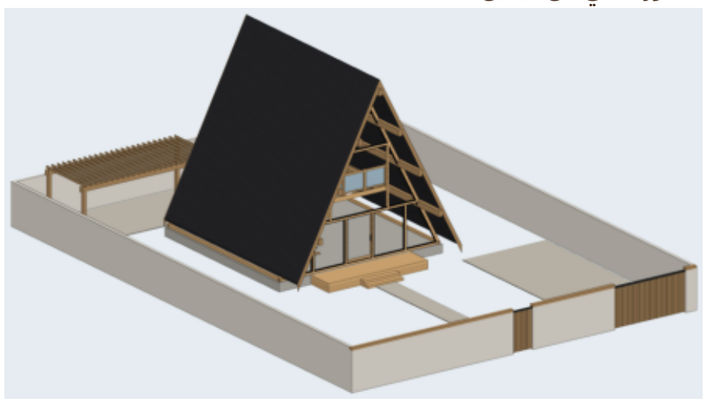


المنظور الخلفي

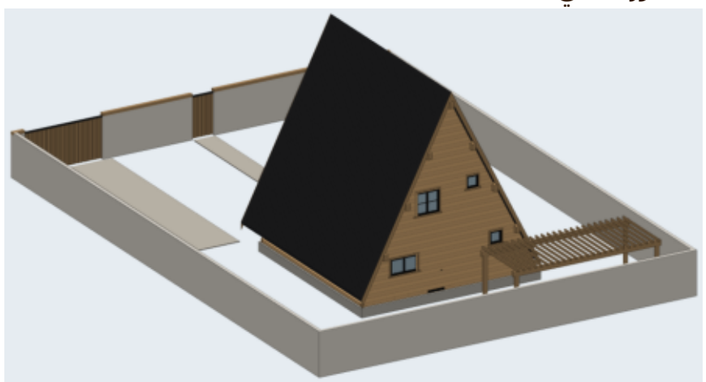

منظور خلفي من اليمين

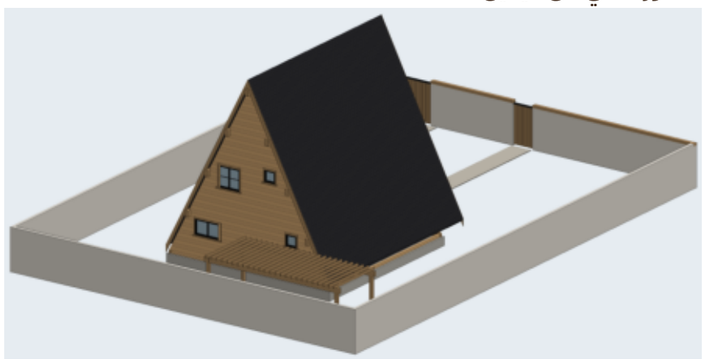

منظر علوي

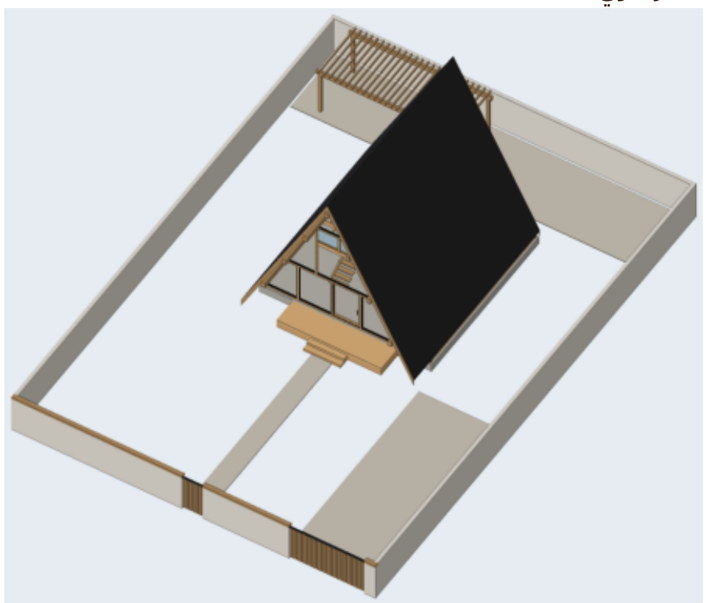


المشروع / العميل	عنوان اللوحة	المقياس	التاريخ	رقم اللوحة
كوخ A-frame دورين — صالة ومطبخ وحمام + غرفتين وحمام وشرفة داخلية — 9.00 × 9.00 م عميل — A-frame 9×9	لقطات المنظور	—	2026-10-26	A-09 (9/11)

مصنع وتد الأخشاب
Watad Wood Factory

المقطع العلوي بالفرش


مقطع أفقي على ارتفاع 1.90 م — توزيع الفرش ومسار الحركة

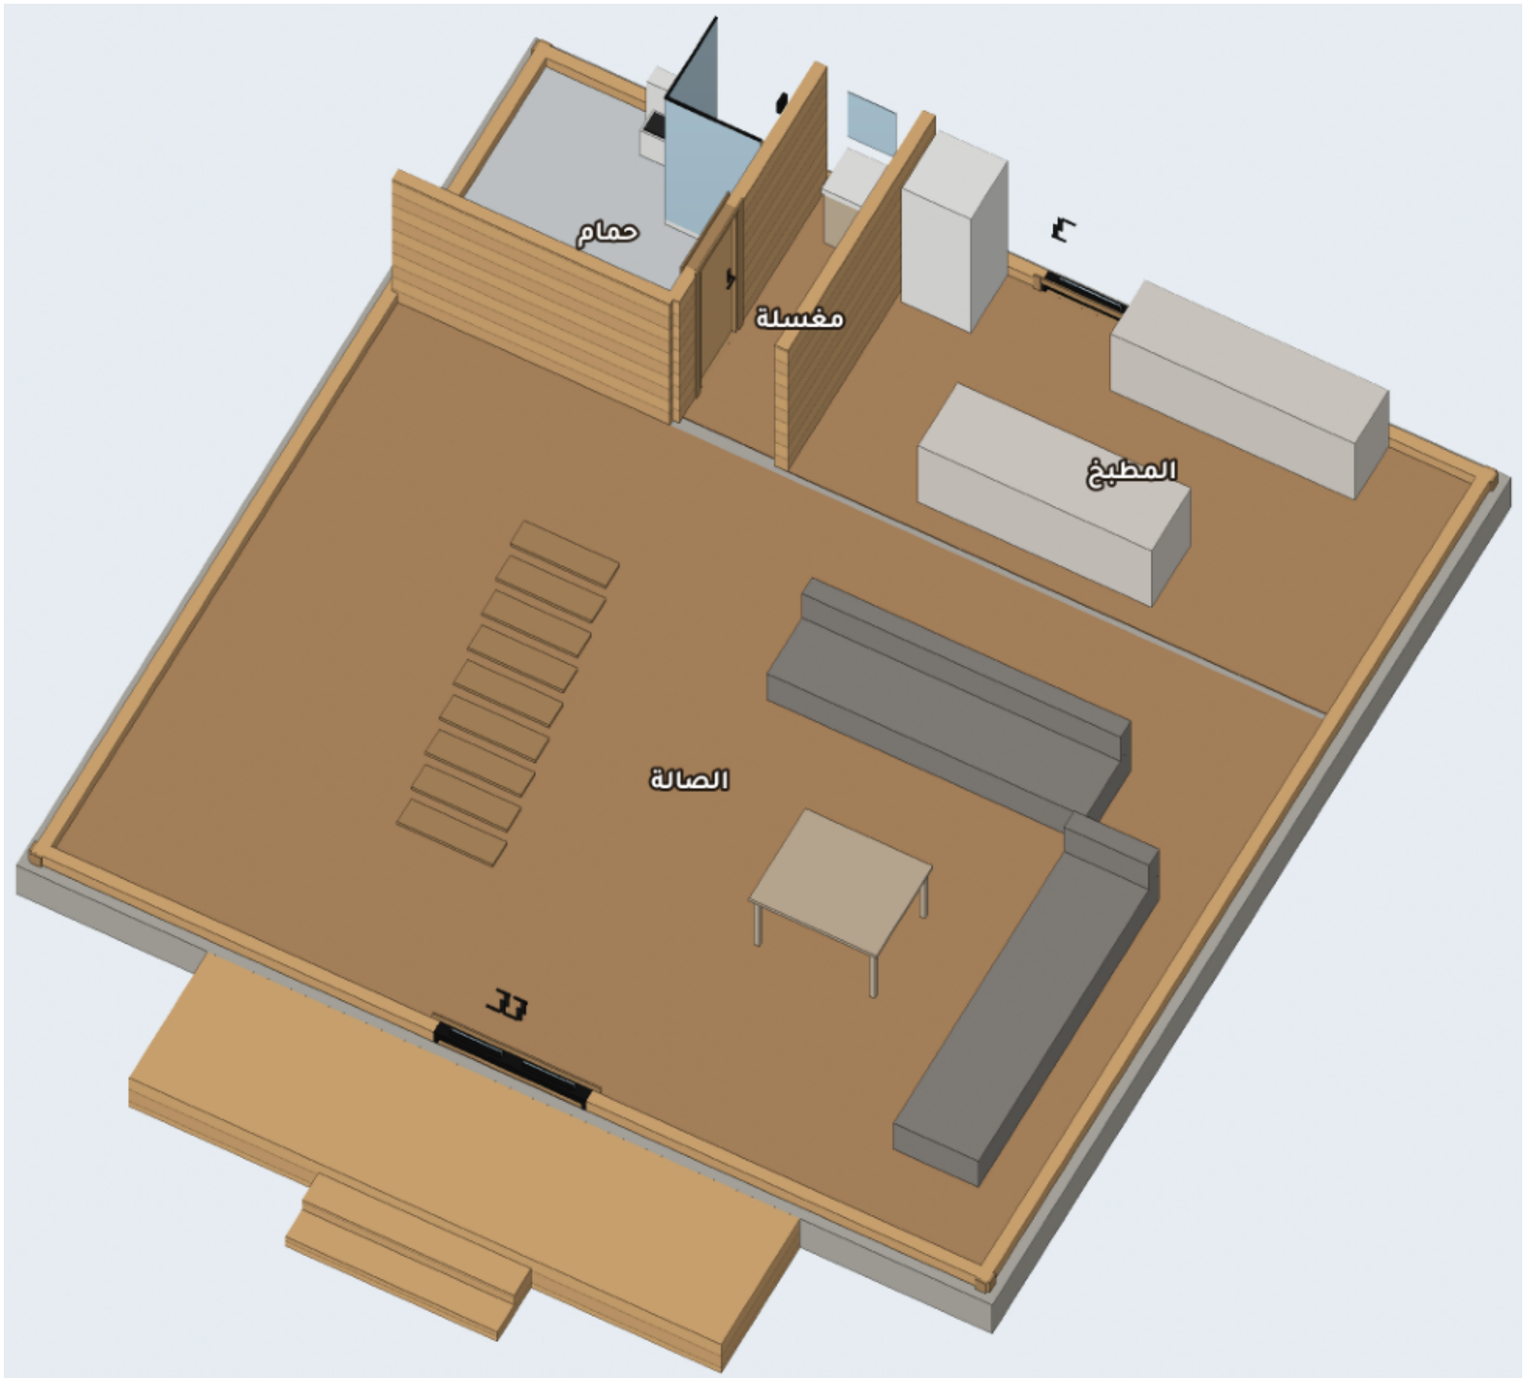

مصنع وتد الأخشاب Watad Wood Factory	المشروع / العميل كوخ A-frame دورين — صالة ومطبخ وحمام + غرفتين وحمام وشرفة داخلية — 9.00 × 9.00 م عميل — A-frame 9×9	عنوان اللوحة المقطع العلوي بالفرش	المقياس —	التاريخ 2026-10-26	رقم اللوحة A-10 (10/11)

المنظور ثلاثي الأبعاد والمواد

النمط: جوزي غامق + إطارات سوداء — رندر واقعي بخامات حقيقية

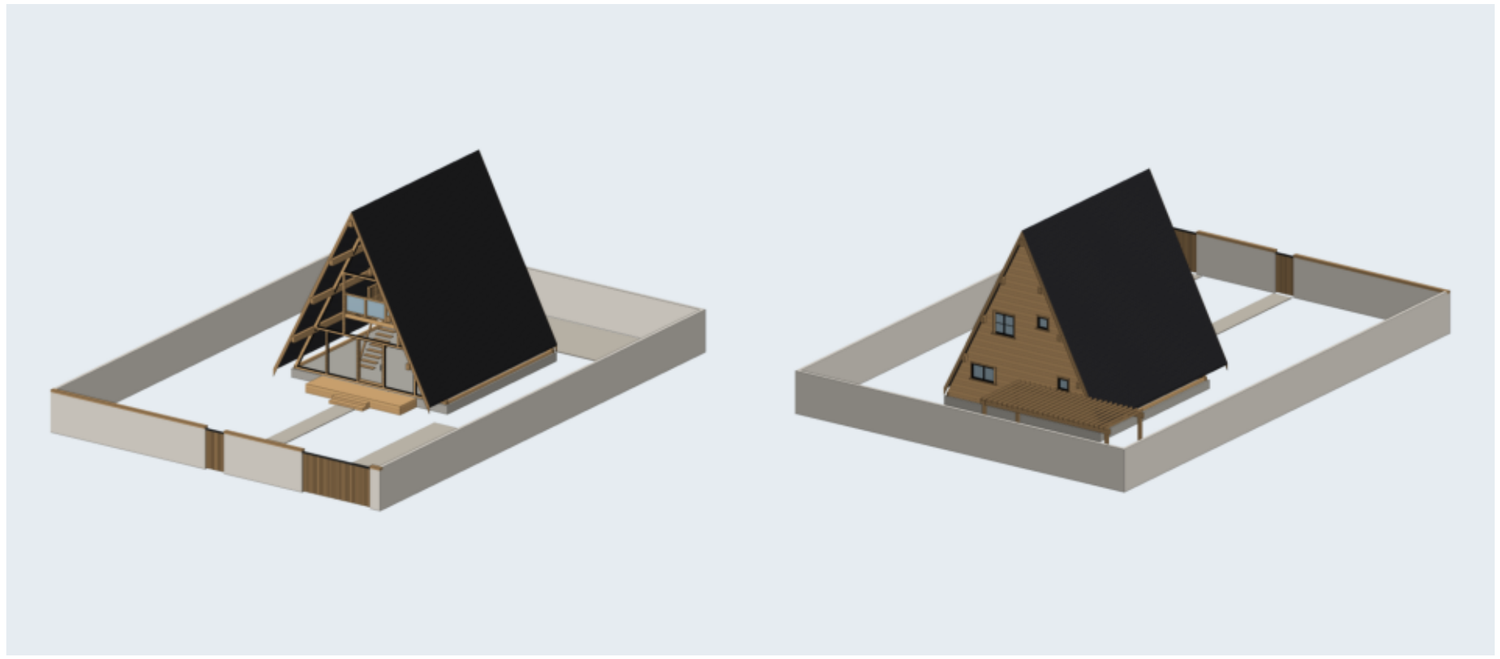

جدول المواد والألوان

الخشب / الصبغة

خشب طبيعي فاتح (بدون صبغة)

القرميد

قرميد رمادي غامق

الزجاج

زجاج شفاف

إطارات الشبابيك والأبواب

إطار ألمنيوم أسود

الكنار والزوايا

نفس الصبغة أغمق درجة


الصبة

خرسانة 45 سم


الدربزين: ألواح أفقية متقاربة (عصري)

تقسيم الشبابيك: بدون | الباب الرئيسي: زجاج بتقسيمات (فرنسي)

أنواع الدربزين المعتمدة (من مشاريع المصنع)

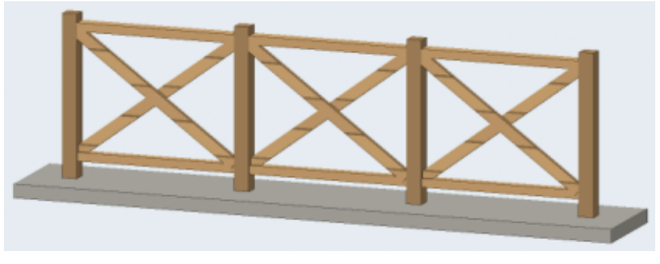

تقاطع X (صورة 5)

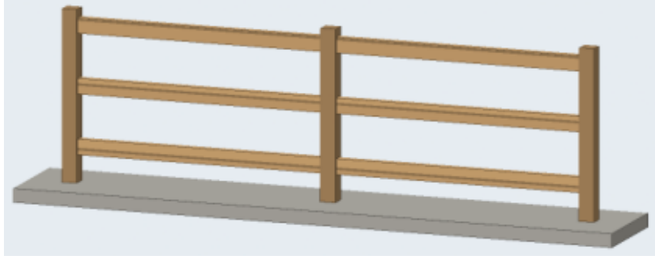

3 مرابيع أفقية (صورة 2)



قوائم رأسية متقاربة (صورة 1)

مصنع وتد الأخشاب Watad Wood Factory	المشروع / العميل كوخ A-frame دورين — صالة ومطبخ وحمام + غرفتين وحمام وشرفة داخلية — 9.00 × 9.00 م عميل — A-frame 9×9	عنوان اللوحة المنظور والمواد	المقياس —	التاريخ 2026-10-26	رقم اللوحة A-11 (11/11)