
# المسقط الأفقي مع الفرش — الدور الأرضي

الأبعاد بالسنتيمتر - الجدران: قوائم 7×5 + تلبيس 2.5 من الجهتين (12 سم) | منسوب الأرضية +0.00

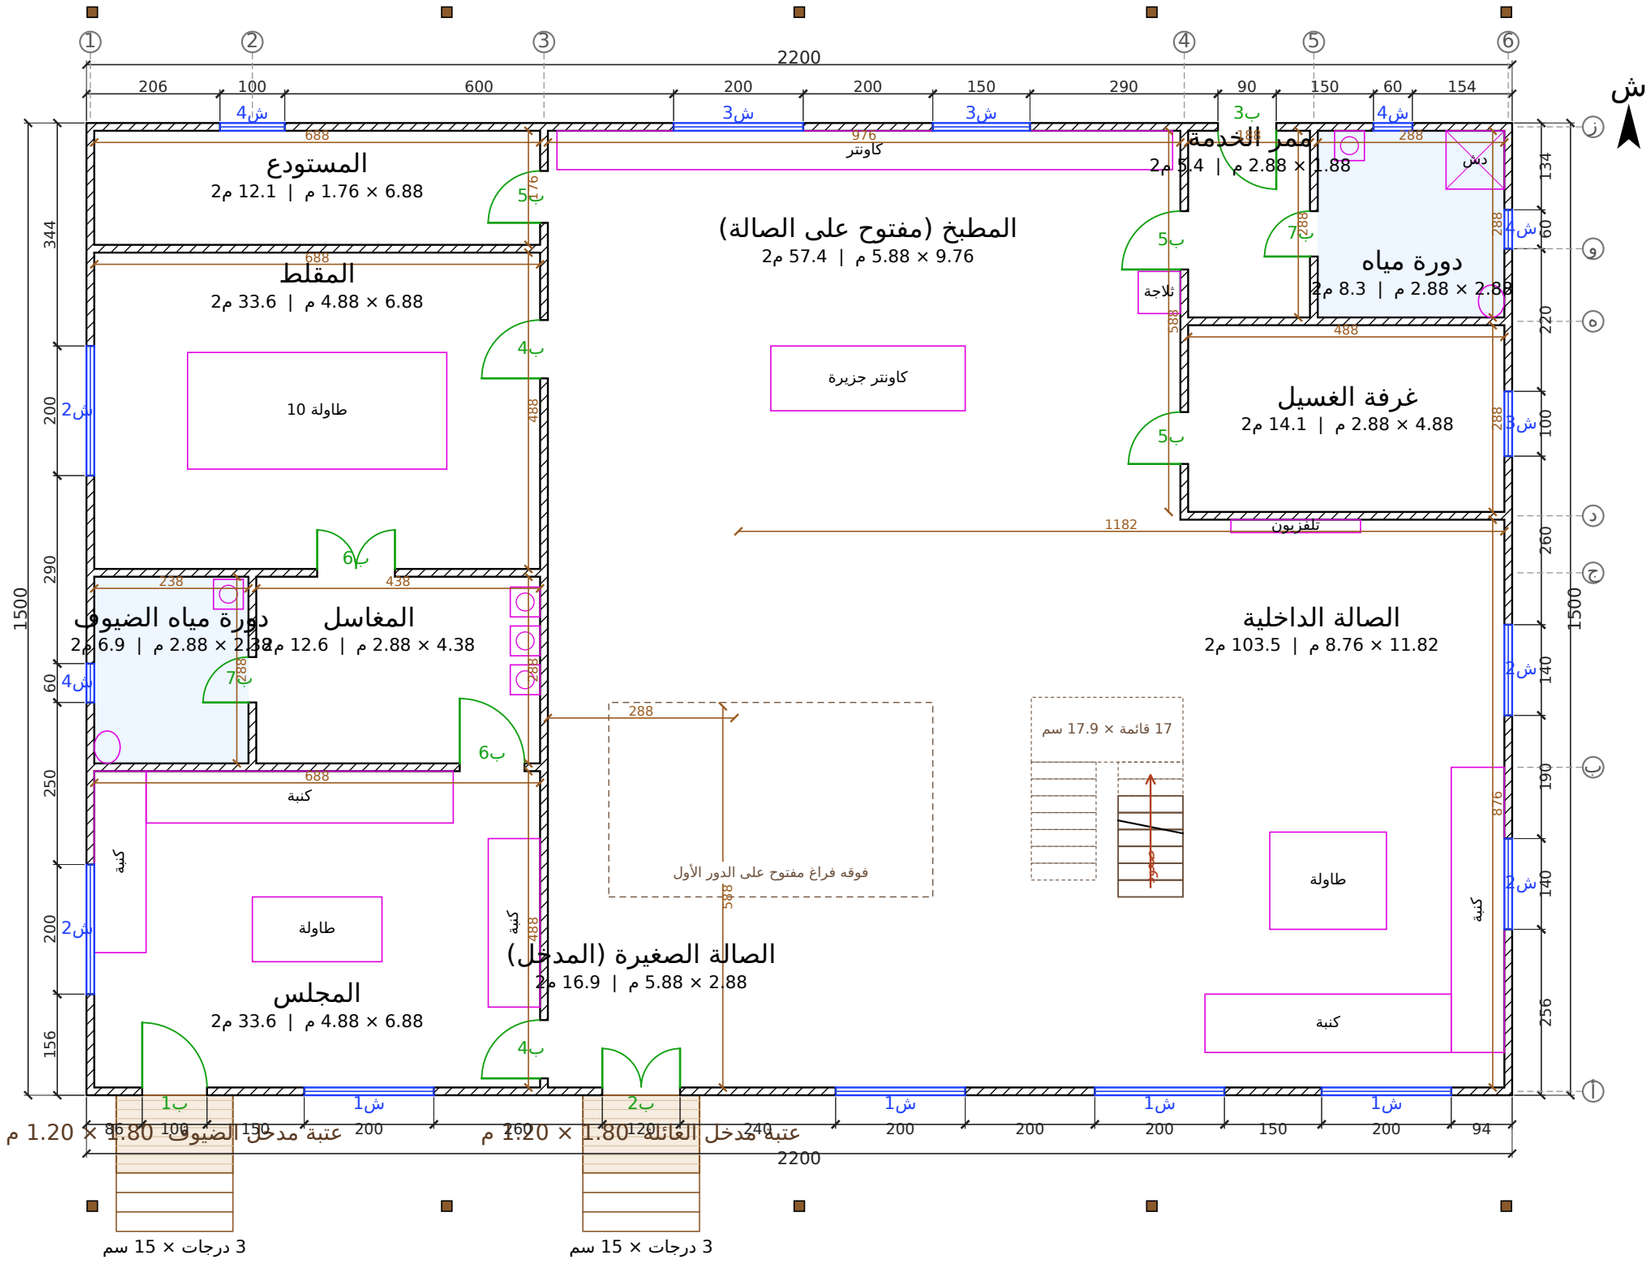



| المشروع / العميل | عنوان اللوحة | المقياس | التاريخ | رقم اللوحة |
|---|---|---|---|---|
| **فيلا دورين — مجلس ومقلط + 6 غرف — 15.00 × 22.00**<br>**عميل — فيلا 6 غرف** | **المسقط الأفقي — الدور الأرضي** | **1:50** | **2026-10-21** | **A-01 (1/11)** |

**مصنع وتد الأخشاب**
Watad Wood Factory


# المسقط الأفقي مع الفرش — الدور الأول

الأبعاد بالسنتيمتر - الجدران: قوائم 7×5 + تلبيس 2.5 من الجهتين (12 سم) | منسوب الأرضية +3.05

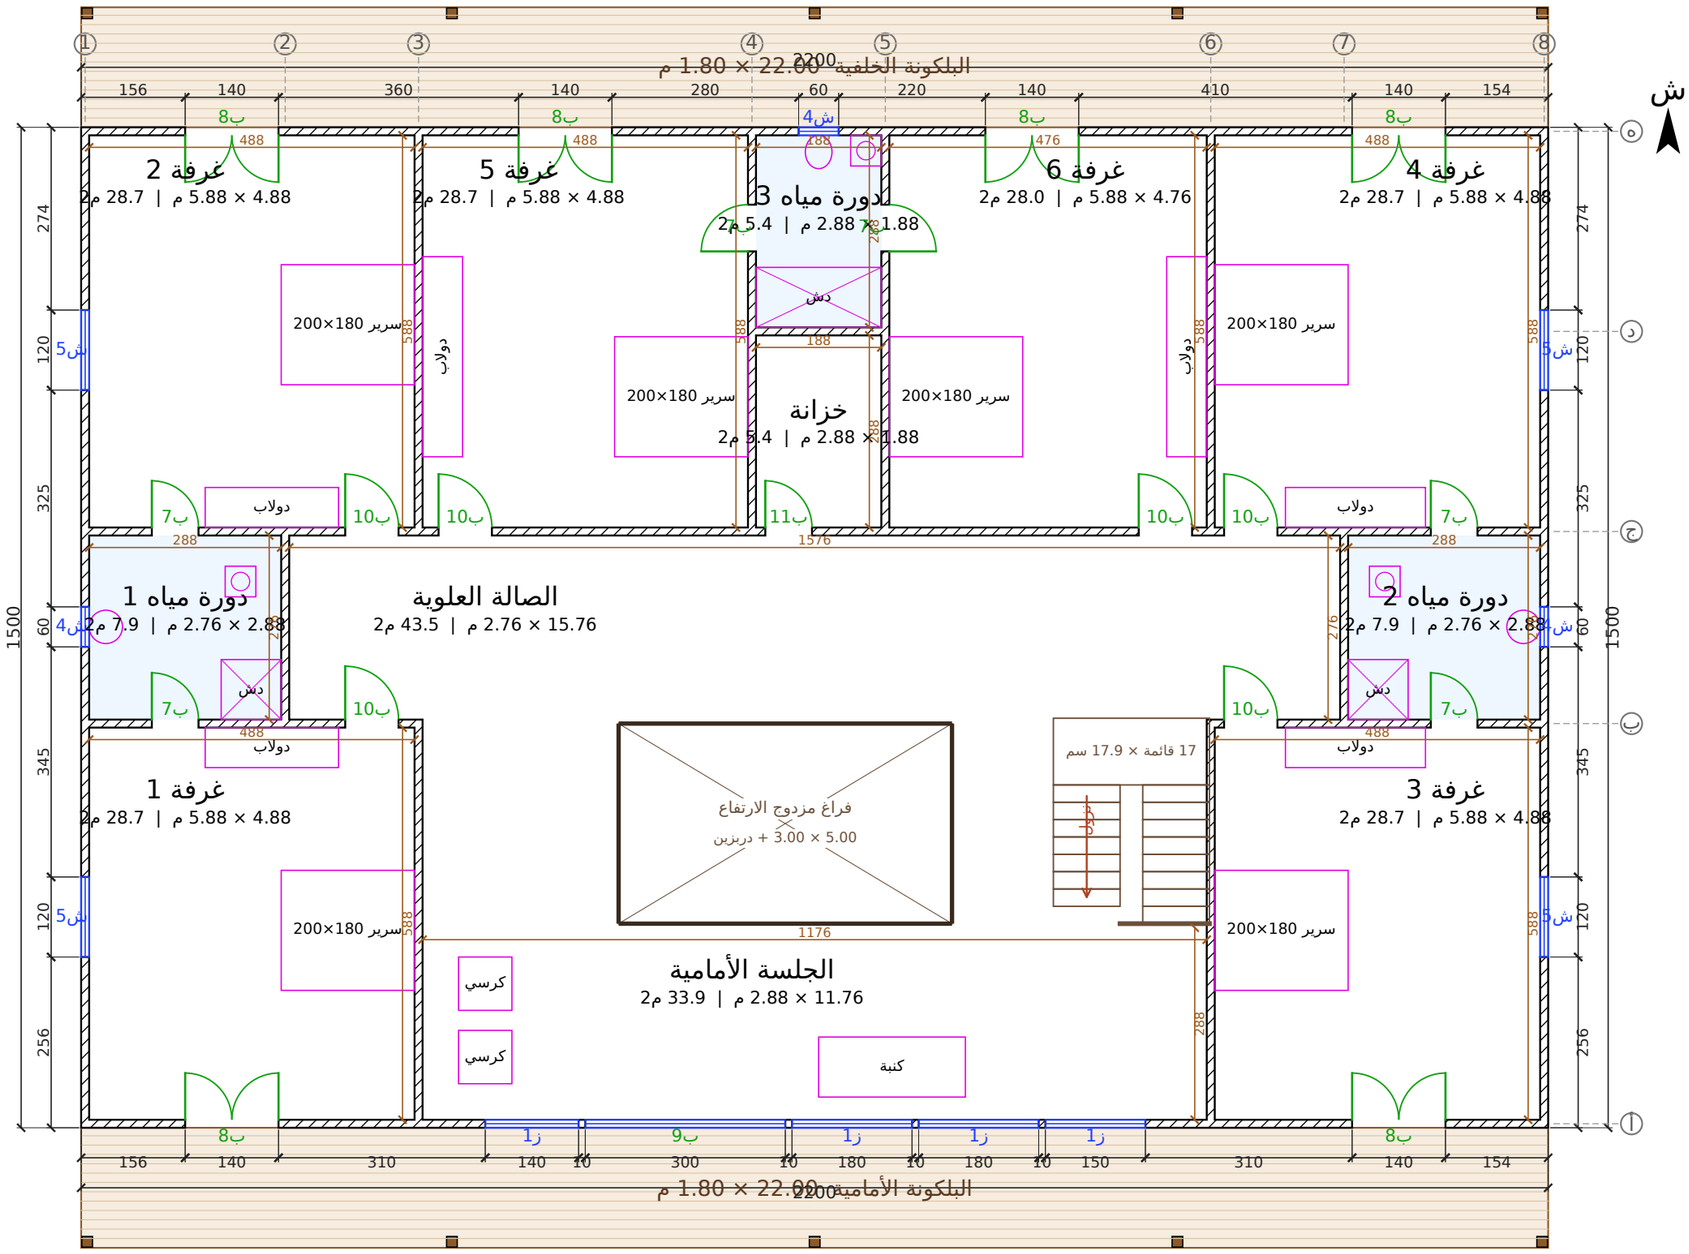



| المشروع / العميل | عنوان اللوحة | المقياس | التاريخ | رقم اللوحة |
|---|---|---|---|---|
| **فيلا دورين — مجلس ومقلط + 6 غرف — 15.00 × 22.00**<br>**عميل — فيلا 6 غرف** | **المسقط الأفقي — الدور الأول** | **1:50** | **2026-10-21** | **A-02 (2/11)** |

**مصنع وتد الأخشاب**
Watad Wood Factory

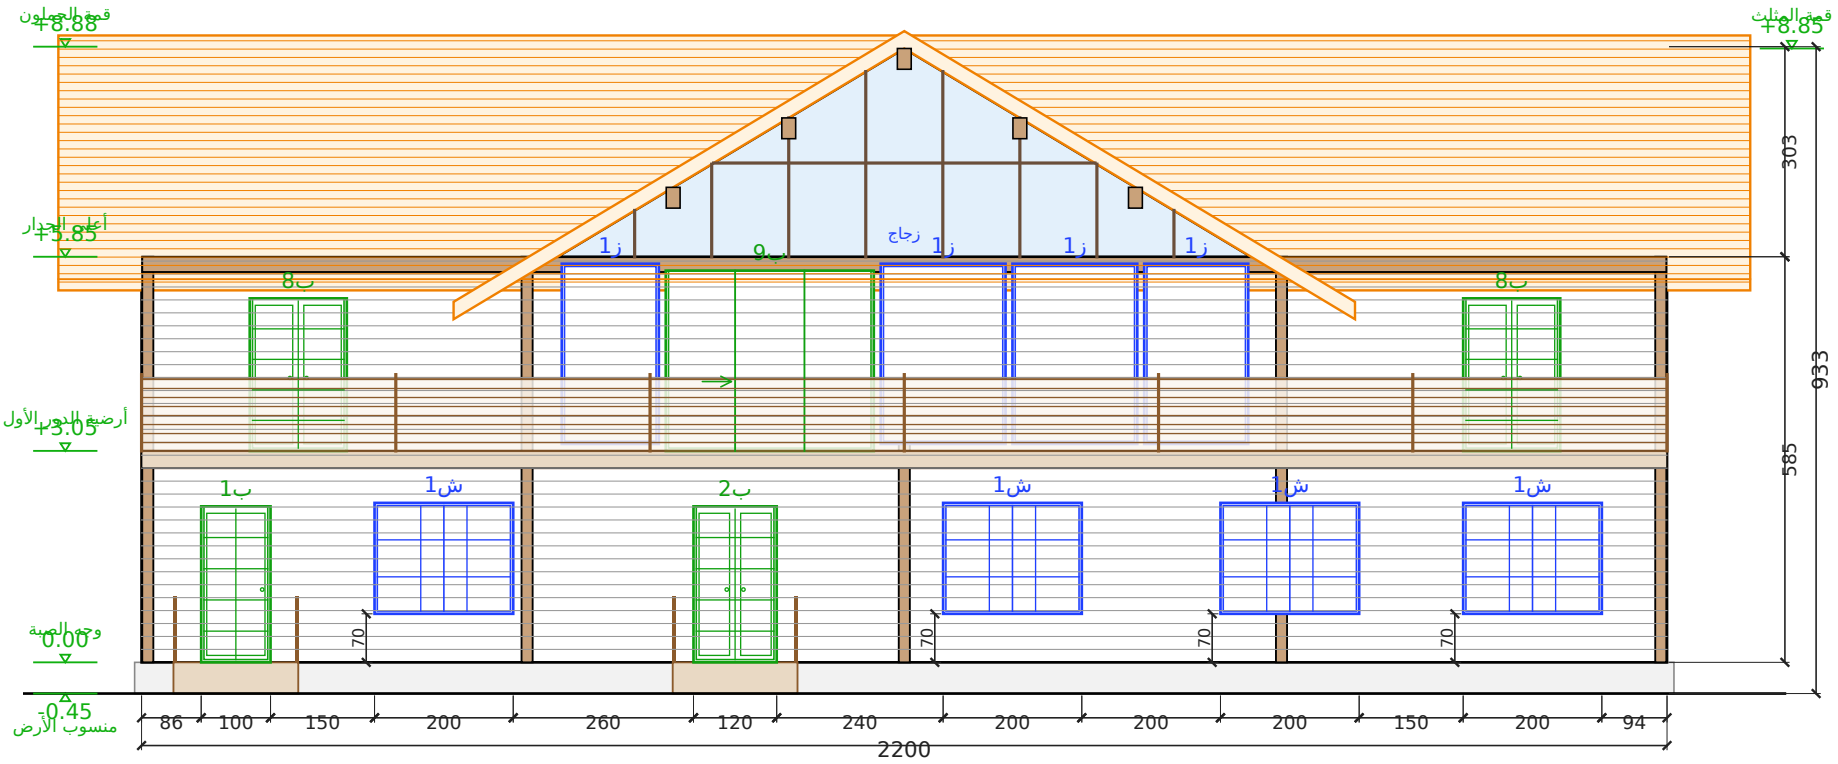


## الواجهة الأمامية

مقياس 1:50 | الوحدة: سم

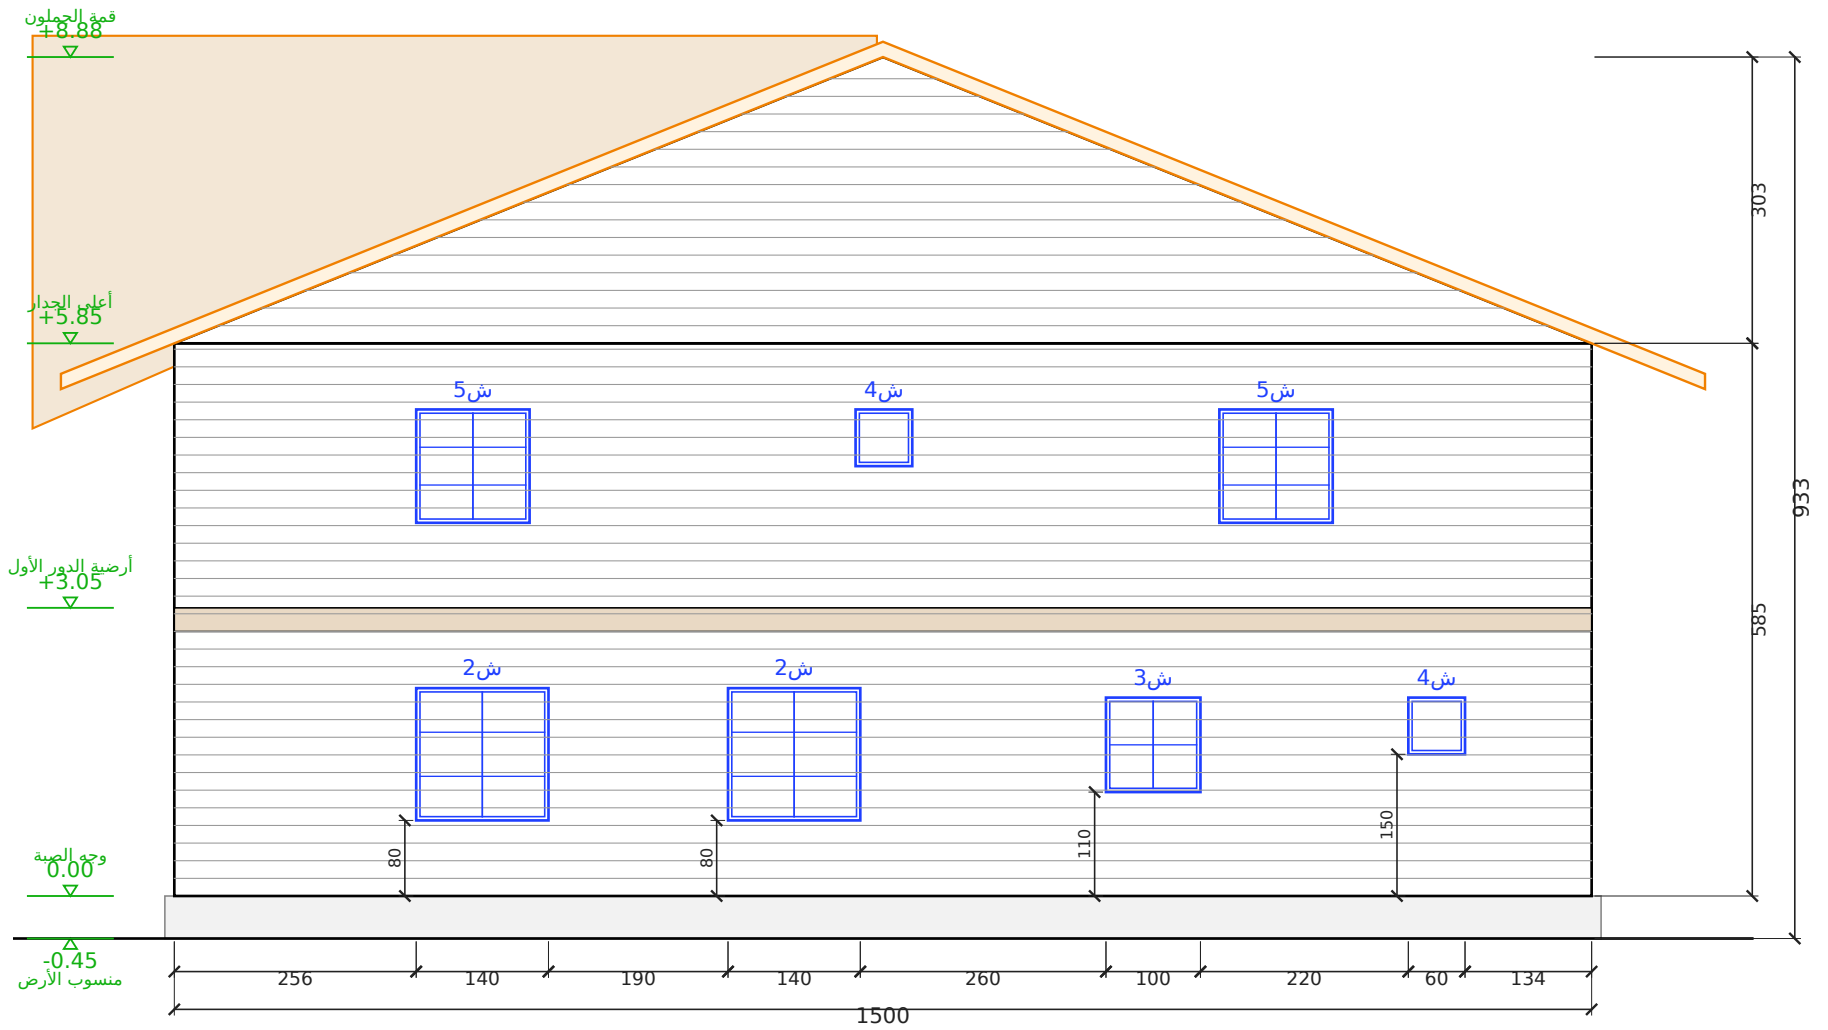



## الواجهة الشرقية

مقياس 1:50 | الوحدة: سم


| المشروع / العميل | عنوان اللوحة | المقياس | التاريخ | رقم اللوحة |
|---|---|---|---|---|
| **فيلا دورين — مجلس ومقلط + 6 غرف — 15.00 × 22.00**<br>**عميل — فيلا 6 غرف** | **الواجهة الأمامية والواجهة الشرقية** | **1:50** | **2026-10-21** | **A-03 (3/11)** |

**مصنع وتد الأخشاب**
Watad Wood Factory

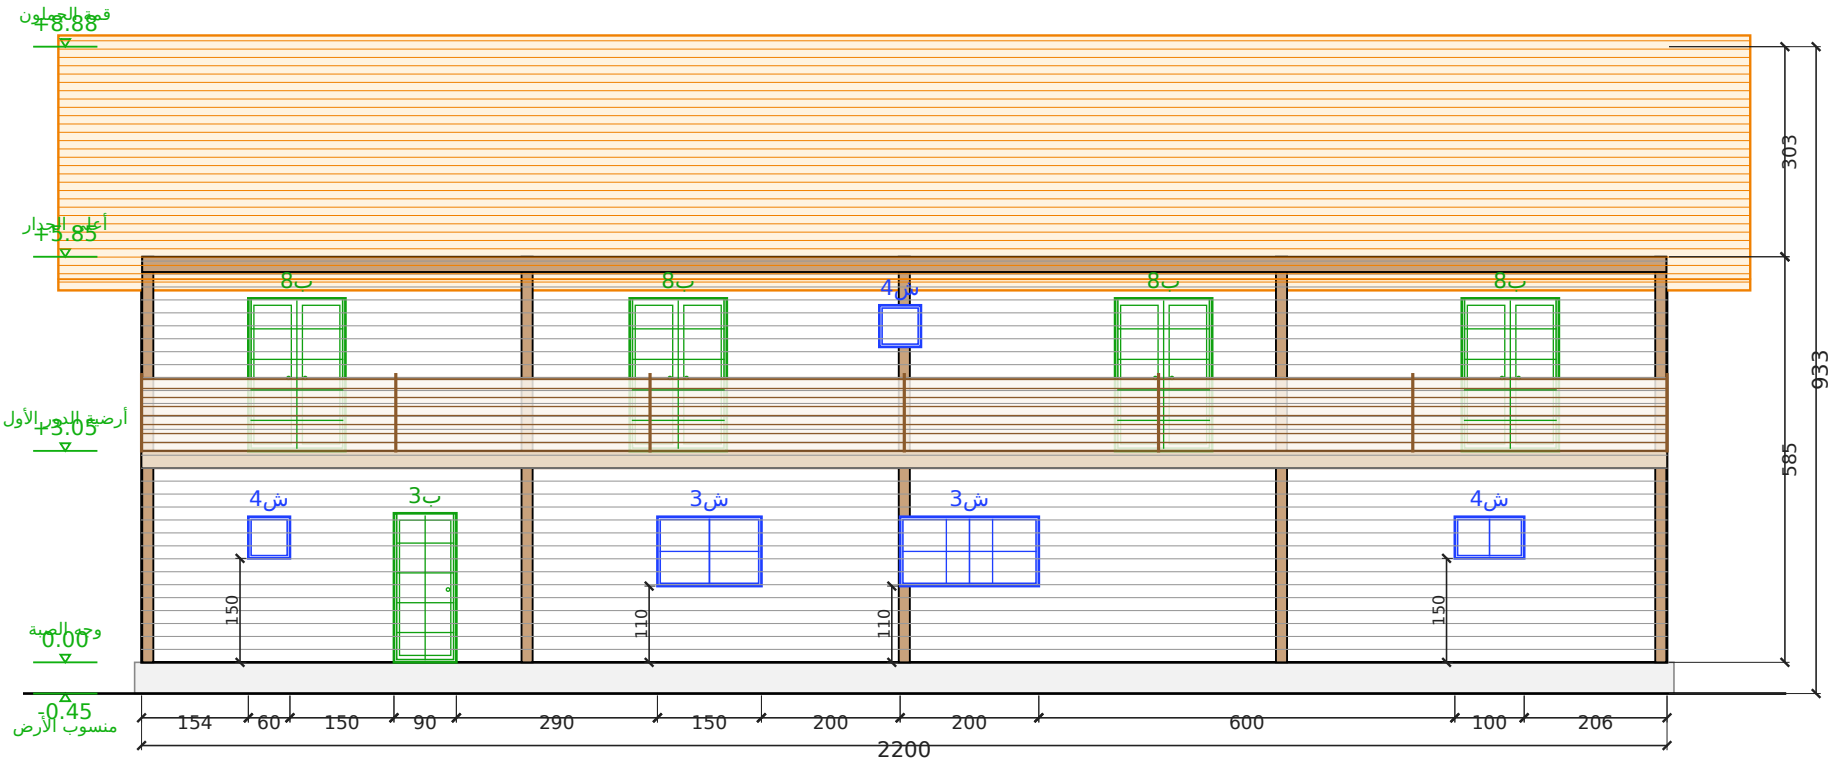


## الواجهة الخلفية

مقياس 1:50 | الوحدة: سم

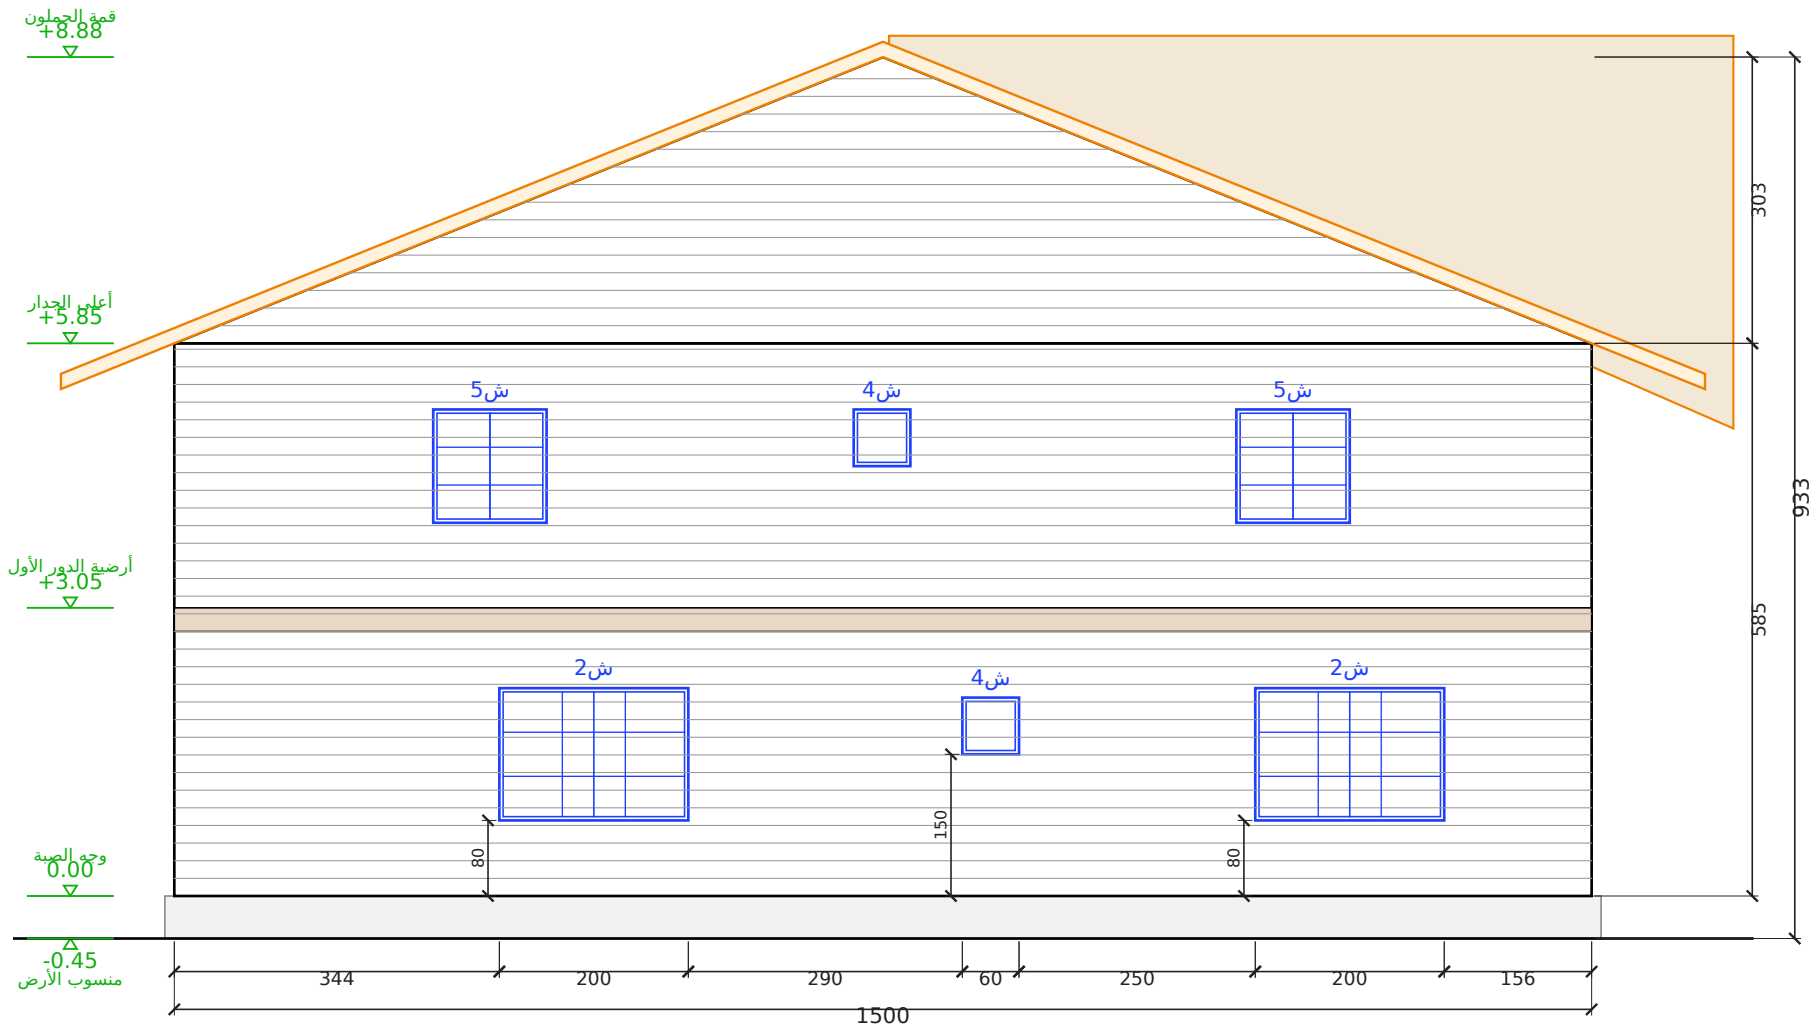



## الواجهة الغربية


مقياس 1:50 | الوحدة: سم

| | | | | | |
|---|---|---|---|---|---|
| **مصنع وتد الأخشاب**<br>Watad Wood Factory | المشروع / العميل<br>**فيلا دورين — مجلس ومقلط + 6 غرف — 15.00 × 22.00**<br>**عميل — فيلا 6 غرف** | عنوان اللوحة<br>**الواجهة الخلفية والواجهة الغربية** | المقياس<br>**1:50** | التاريخ<br>**2026-10-21** | رقم اللوحة<br>**A-04 (4/11)** |


## مسقط السقف (جملون)
رفرف 120 سم من كل جهة | مقياس 1:50

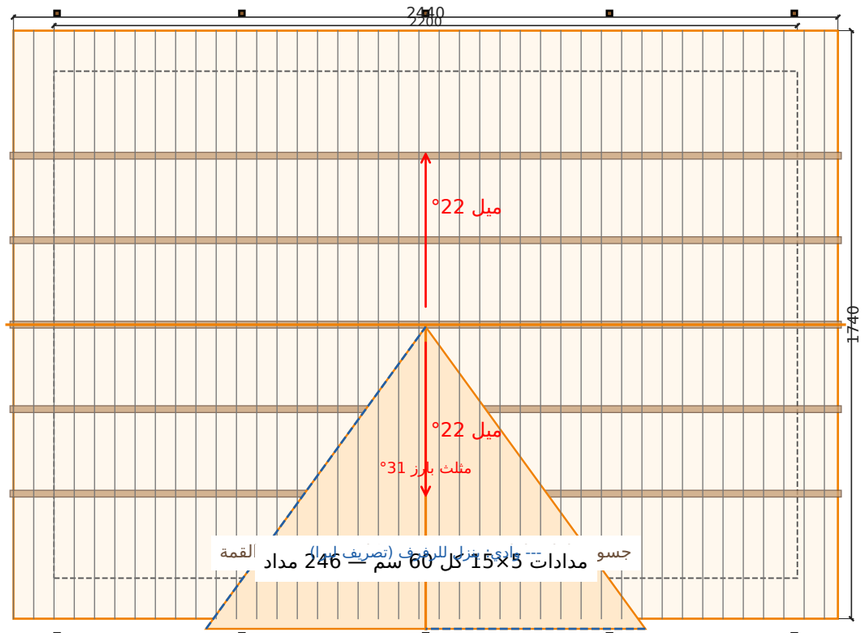


## قطاع عرضي أ-أ
مقياس 1:50 | الوحدة: سم

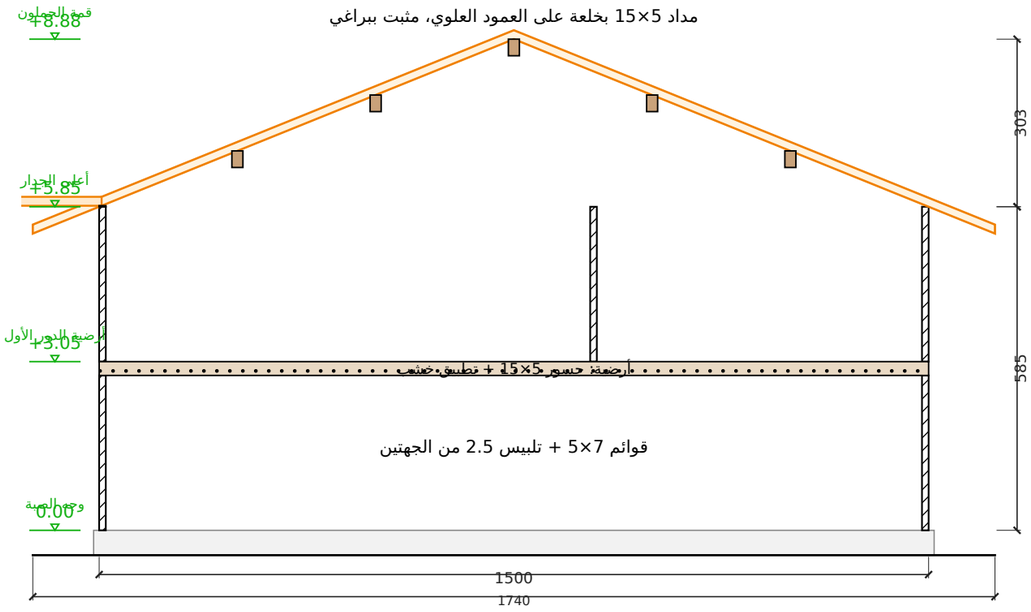


### تفصيلة جلوس المداد على العلوي (1:5)

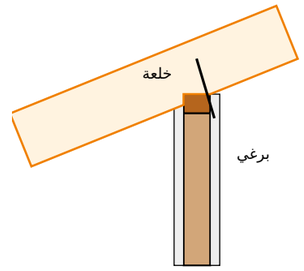


| المشروع / العميل | عنوان اللوحة | المقياس | التاريخ | رقم اللوحة |
|---|---|---|---|---|
| **فيلا دورين — مجلس ومقلط + 6 غرف — 15.00 × 22.00**<br>**عميل — فيلا 6 غرف** | **مسقط السقف والقطاع** | **1:50** | **2026-10-21** | **A-05 (5/11)** |

**مصنع وتد الأخشاب**
Watad Wood Factory

# جدول مقاسات الأبواب والشبابيك

## مقاس الفتحة الصافي في الجدار - الوحدة: سم

| الرمز | النوع | العرض (سم) | الارتفاع (سم) | ارتفاع الجلسة (سم) | العدد | الموقع |
|---|---|---|---|---|---|---|
| ب1 | باب | 100 | 225 | - | 1 | الأمامية |
| ب10 | باب | 80 | 210 | - | 6 | غرفة 1 - غرفة 2 - غرفة 5 - غرفة 6 - غرفة 3 - غرفة 4 |
| ب11 | باب | 70 | 210 | - | 1 | خزانة |
| ب2 | باب مزدوج | 120 | 225 | - | 1 | الأمامية |
| ب3 | باب | 90 | 215 | - | 1 | الخلفية |
| ب4 | باب | 90 | 210 | - | 2 | المجلس — الصالة الصغيرة - المقلط — المطبخ (تقديم) |
| ب5 | باب | 80 | 210 | - | 2 | المستودع - غرفة الغسيل |
| ب5 | باب | 90 | 210 | - | 1 | ممر الخدمة |
| ب6 | باب | 100 | 210 | - | 1 | المجلس — المغاسل |
| ب6 | باب مزدوج | 120 | 210 | - | 1 | المغاسل — المقلط |
| ب7 | باب | 70 | 210 | دورة مياه الضيوف - دورة مياه - | 8 | غرفة 1 — دورة مياه 1 - غرفة 2 — دورة مياه 1 - غرفة 5 — دورة مياه 3 - غرفة 6 — دورة مياه 3 - غرفة 3 — دورة مياه 2 - غرفة |
| ب8 | باب مزدوج | 140 | 220 | - | 6 | الأمامية 2 - الخلفية 4 |
| ب9 | باب | 300 | 260 | - | 1 | الأمامية |
| ز1 | شباك | 140 | 260 | 10 | 1 | الأمامية |
| ز1 | شباك | 180 | 260 | 10 | 2 | الأمامية 2 |
| ز1 | شباك | 150 | 260 | 10 | 1 | الأمامية |
| ش1 | شباك | 200 | 160 | 70 | 4 | الأمامية 4 |
| ش2 | شباك | 140 | 140 | 80 | 2 | الشرقية 2 |
| ش2 | شباك | 200 | 140 | 80 | 2 | الغربية 2 |
| ش3 | شباك | 100 | 100 | 110 | 1 | الشرقية |
| ش3 | شباك | 150 | 100 | 110 | 1 | الخلفية |
| ش3 | شباك | 200 | 100 | 110 | 1 | الخلفية |
| ش3 | شباك | 150 | 100 | 110 | 1 | الخلفية |
| ش3 | شباك | 200 | 100 | 110 | 1 | الخلفية |
| ش4 | شباك | 60 | 60 | 150 | 6 | الشرقية 2 - الخلفية 2 - الغربية 2 |
| ش4 | شباك | 100 | 60 | 150 | 1 | الخلفية |
| ش5 | شباك | 120 | 120 | 90 | 4 | الشرقية 2 - الغربية 2 |

الإجمالي: أبواب 32 - شبابيك 26

# جدول المساحات وبيانات المشروع

## بيانات المشروع

| البند | البيان |
|---|---|
| المشروع | فيلا دورين — مجلس ومقلط + 6 غرف — 15.00 × 22.00 |
| العميل | عميل — فيلا 6 غرف |
| الموقع | — |
| الاستخدام | سكن خاص |
| التاريخ | 2026-10-21 |
| نظام البناء | هيكل خشب 5×7 + تلبيس 2.5 سم من الجهتين |
| السقف | جملون 22° — قرميد معدني + 1 مثلث بارز |

## جدول المساحات


| م | الفراغ | الأبعاد (م) | المساحة (م2) |
|---|---|---|---|
| 1 | أرضي — المجلس | 4.88 × 6.88 | 33.57 |
| 2 | أرضي — دورة مياه الضيوف | 2.38 × 2.88 | 6.85 |
| 3 | أرضي — المغاسل | 2.88 × 4.38 | 12.61 |
| 4 | أرضي — المقلط | 4.88 × 6.88 | 33.57 |
| 5 | أرضي — المستودع | 1.76 × 6.88 | 12.11 |
| 6 | أرضي — الصالة الصغيرة (المدخل) | 2.88 × 5.88 | 16.93 |
| 7 | أرضي — الصالة الداخلية | 8.76 × 11.82 | 103.54 |
| 8 | أرضي — المطبخ (مفتوح على الصالة) | 5.88 × 9.76 | 57.39 |
| 9 | أرضي — غرفة الغسيل | 2.88 × 4.88 | 14.05 |
| 10 | أرضي — ممر الخدمة | 2.88 × 1.88 | 5.41 |
| 11 | أرضي — دورة مياه | 2.88 × 2.88 | 8.29 |
| 12 | أول — غرفة 1 | 5.88 × 4.88 | 28.69 |
| 13 | أول — دورة مياه 1 | 2.76 × 2.88 | 7.95 |
| 14 | أول — غرفة 2 | 5.88 × 4.88 | 28.69 |
| 15 | أول — غرفة 3 | 5.88 × 4.88 | 28.69 |
| 16 | أول — دورة مياه 2 | 2.76 × 2.88 | 7.95 |
| 17 | أول — غرفة 4 | 5.88 × 4.88 | 28.69 |
| 18 | أول — غرفة 5 | 5.88 × 4.88 | 28.69 |
| 19 | أول — غرفة 6 | 5.88 × 4.76 | 27.99 |
| 20 | أول — دورة مياه 3 | 2.88 × 1.88 | 5.41 |
| 21 | أول — خزانة | 2.88 × 1.88 | 5.41 |
| 22 | أول — الجلسة الأمامية | 2.88 × 11.76 | 33.87 |
| 23 | أول — الصالة العلوية | 2.76 × 15.76 | 43.50 |
|  | المساحة الصافية الداخلية |  | 579.91 |
|  | عتبة مدخل الضيوف | 1.20 × 1.80 | 2.16 |
|  | عتبة مدخل العائلة | 1.20 × 1.80 | 2.16 |
|  | **البلكونة الأمامية** | **1.80 × 22.00** | **39.60** |
|  | **البلكونة الخلفية** | **1.80 × 22.00** | **39.60** |
|  | **المساحة الإجمالية المبنية** | **2 دور × 15.00 × 22.00** | **660.00** |
|  | **المساحة الكلية (المبنية + التراس والبلكونة)** |  | **743.52** |

# لقطات المنظور الخارجي


المنظور الأمامي




منظور أمامي من اليسار

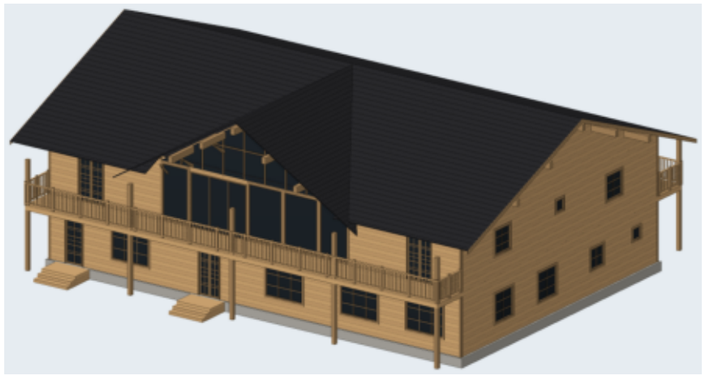

منظور أمامي من اليمين

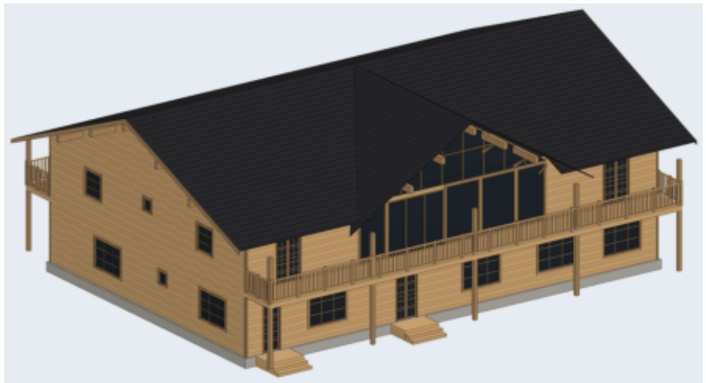


المنظور الخلفي

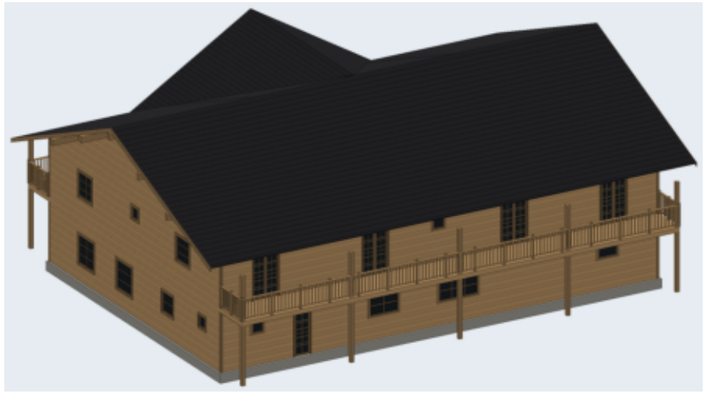

منظور خلفي من اليمين



منظر علوي

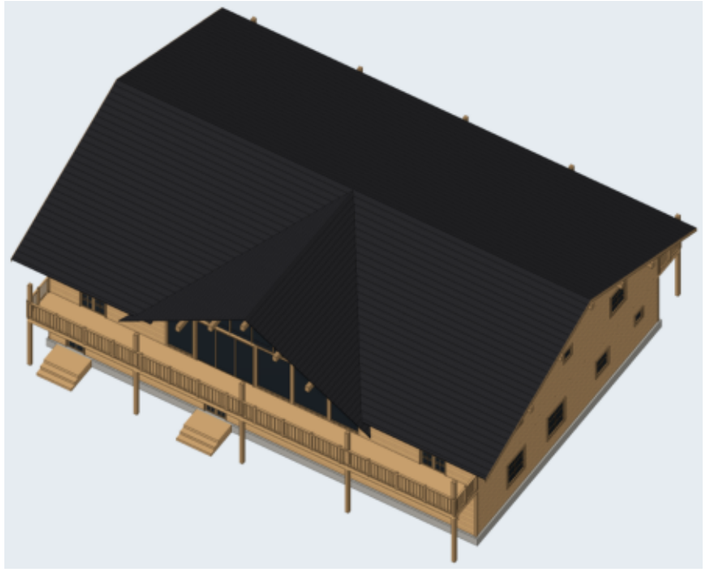


| المشروع / العميل | عنوان اللوحة | المقياس | التاريخ | رقم اللوحة |
|---|---|---|---|---|
| **فيلا دورين — مجلس ومقلط + 6 غرف — 15.00 × 22.00**<br>**عميل — فيلا 6 غرف** | **لقطات المنظور** | **—** | **2026-10-21** | **A-08 (8/11)** |

**مصنع وتد الأخشاب**
Watad Wood Factory

# المقطع العلوي بالفرش — الدور الأرضي

مقطع أفقي على ارتفاع 1.90 م — توزيع الفرش ومسار الحركة

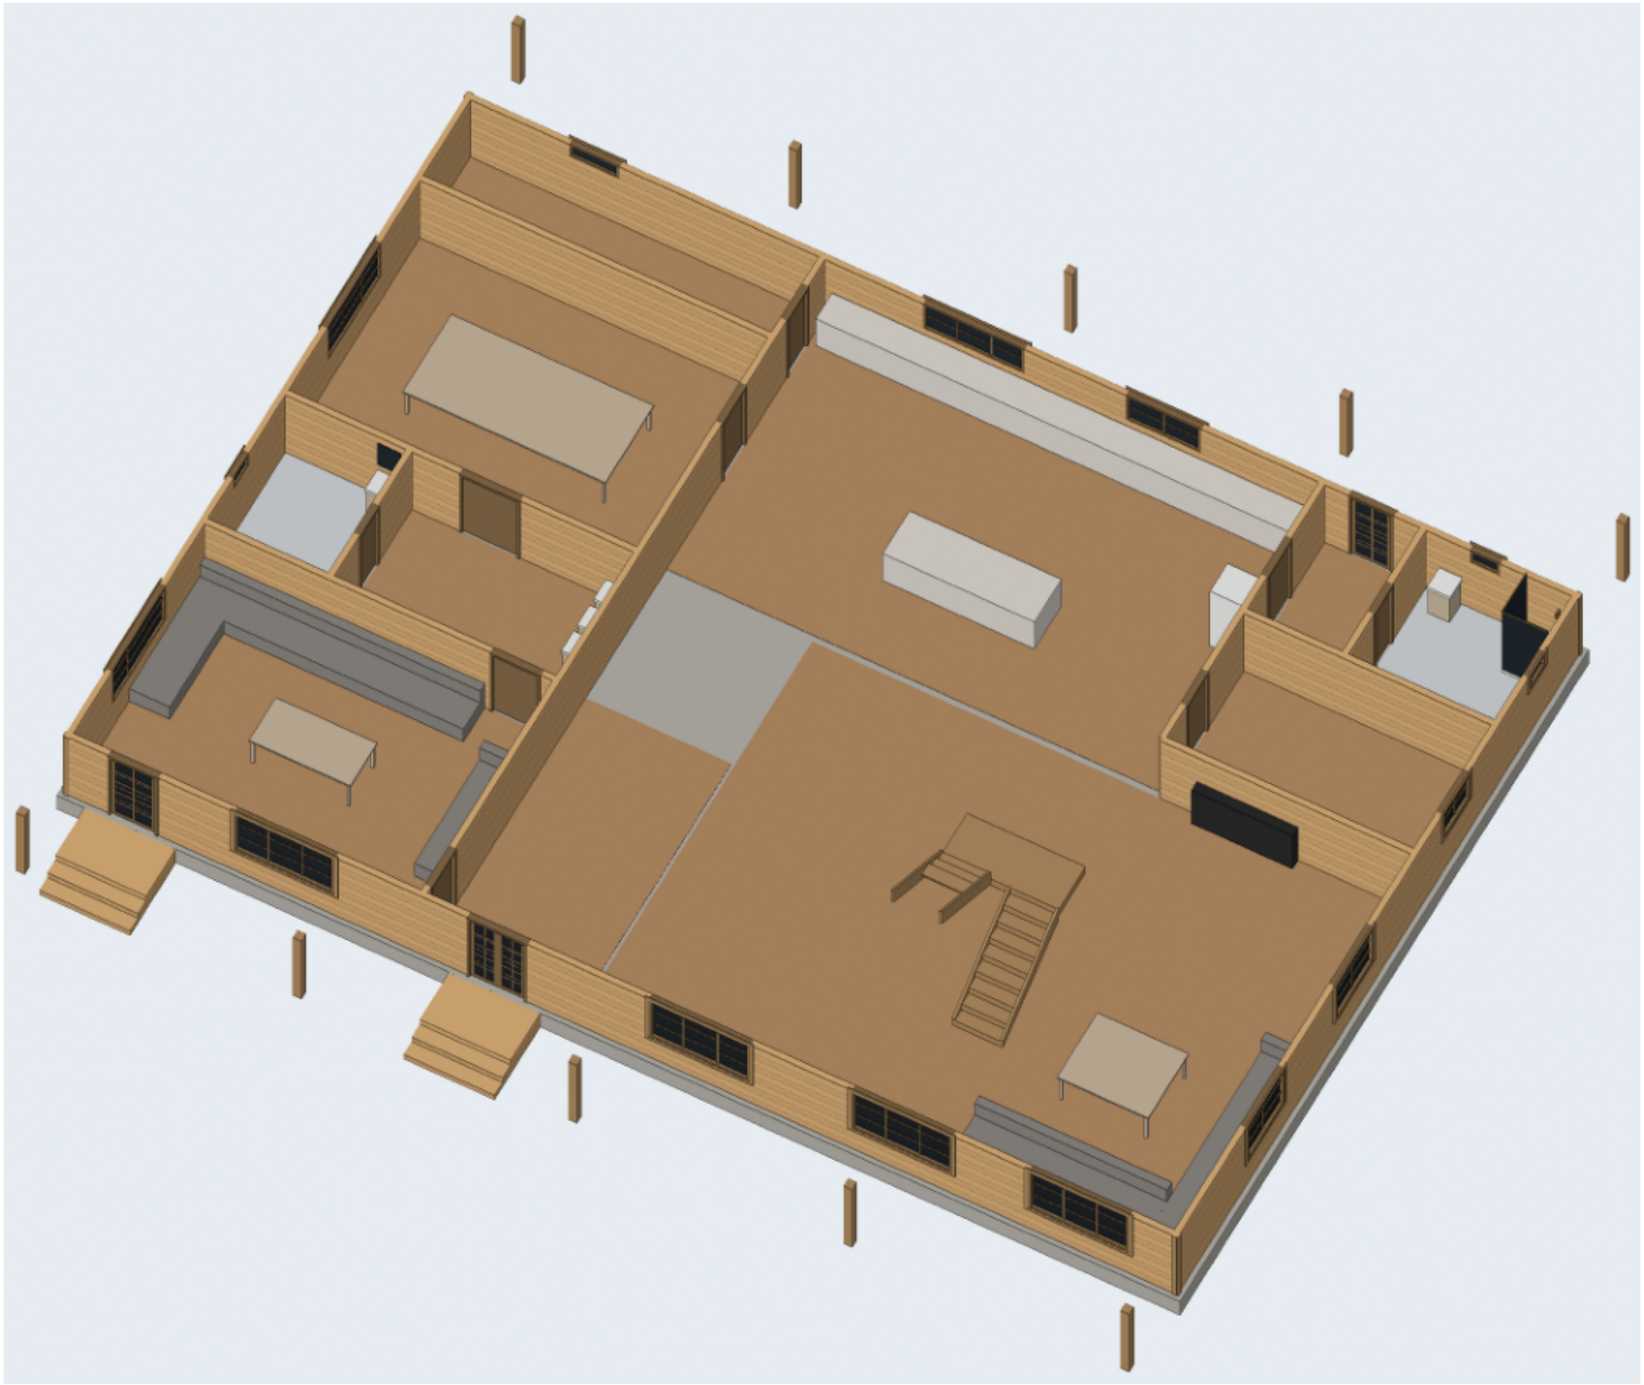


| المشروع / العميل | عنوان اللوحة | المقياس | التاريخ | رقم اللوحة |
|---|---|---|---|---|
| **فيلا دورين — مجلس ومقلط + 6 غرف — 15.00 × 22.00**<br>**عميل — فيلا 6 غرف** | **المقطع العلوي بالفرش — الدور الأرضي** | **—** | **2026-10-21** | **A-09 (9/11)** |

**مصنع وتد الأخشاب**
Watad Wood Factory

# المقطع العلوي بالفرش — الدور الأول


مقطع أفقي على ارتفاع 1.90 م — توزيع الفرش ومسار الحركة

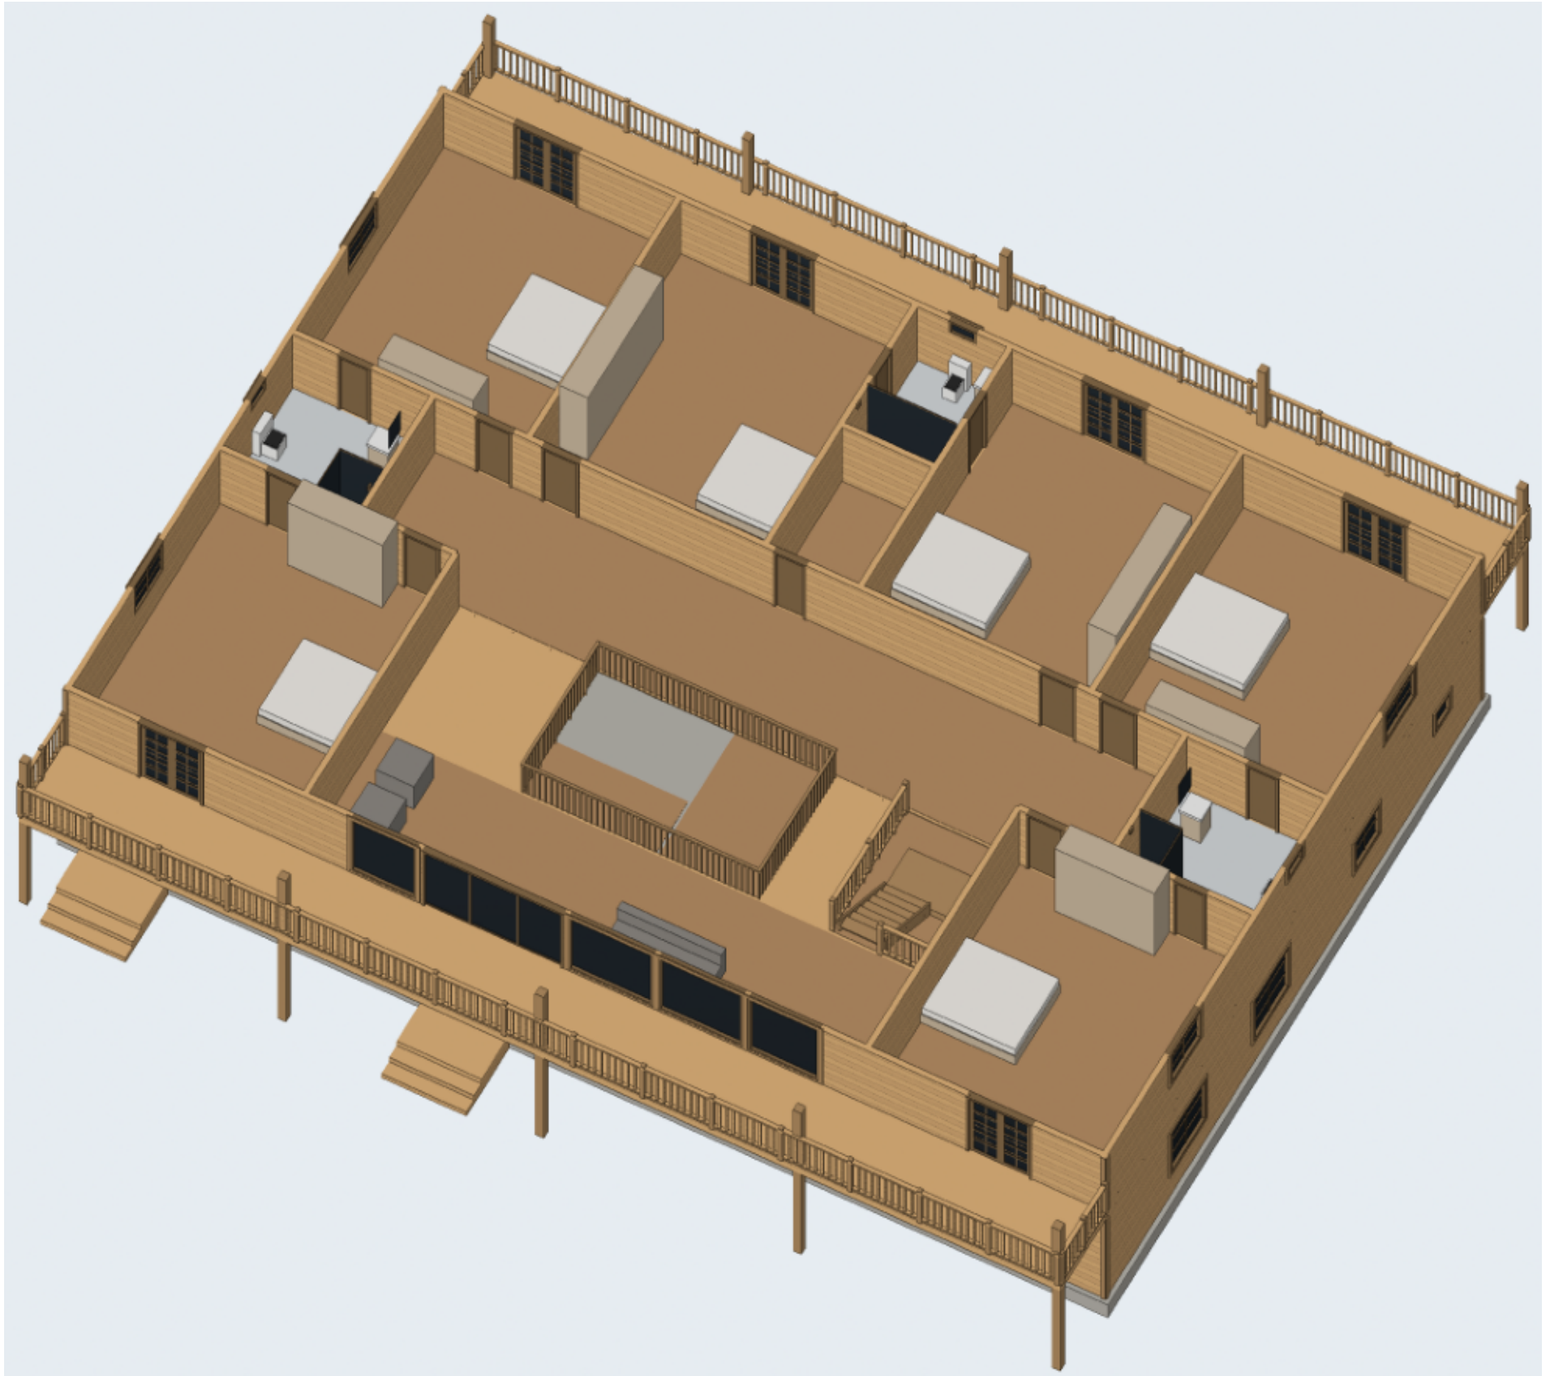

| المشروع / العميل | عنوان اللوحة | المقياس | التاريخ | رقم اللوحة |
|---|---|---|---|---|
| **مصنع وتد الأخشاب**<br>Watad Wood Factory | **فيلا دورين — مجلس ومقلط + 6 غرف — 15.00 × 22.00**<br>**عميل — فيلا 6 غرف** | **المقطع العلوي بالفرش — الدور الأول** | **—** | **2026-10-21** | **A-10 (10/11)** |

# المنظور ثلاثي الأبعاد والمواد

النمط: جوزي غامق + إطارات سوداء — رندر واقعي بخامات حقيقية

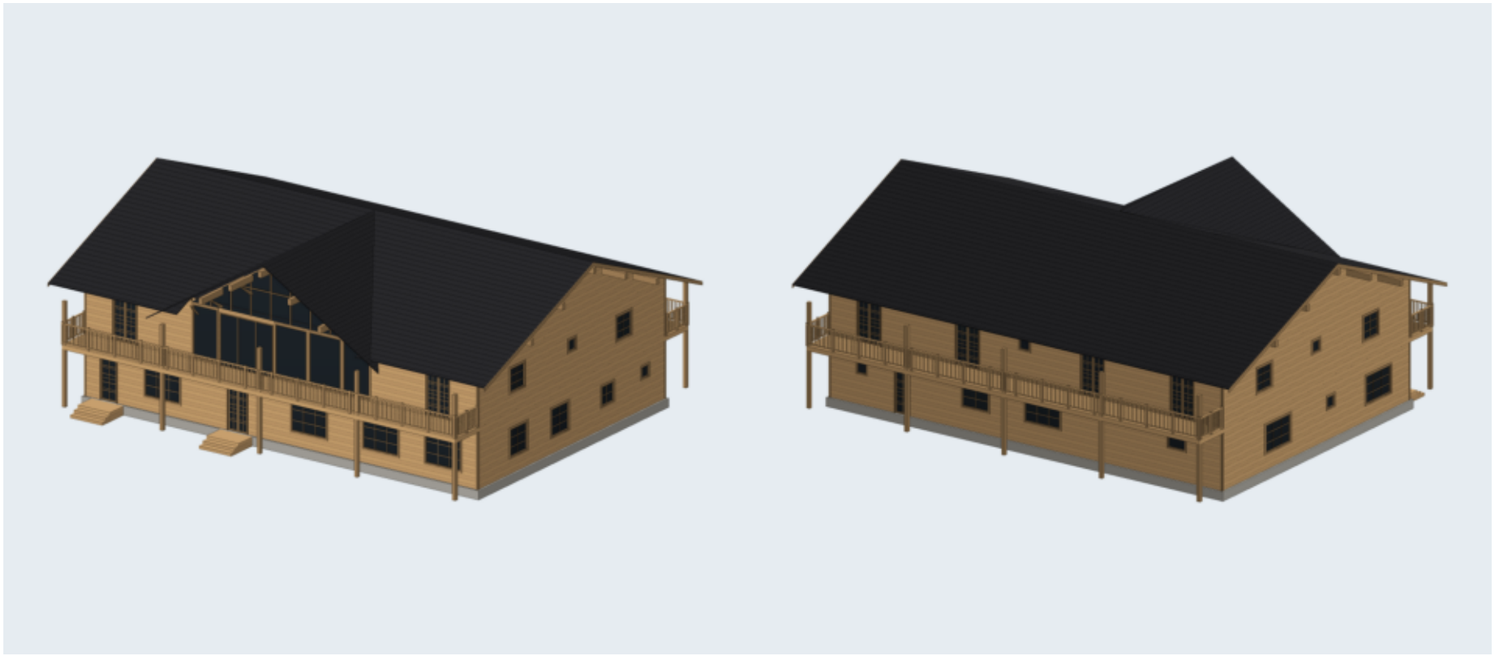

## جدول المواد والألوان

**الخشب / الصبغة**

خشب طبيعي فاتح (بدون صبغة)

**القرميد**

قرميد رمادي غامق

**الزجاج**

زجاج عاكس غامق

**إطارات الشبابيك والأبواب**

إطار خشب بنفس الصبغة أغمق

**الكنار والزوايا**

نفس الصبغة أغمق درجة


**الصبة**

خرسانة 45 سم


الدربزين: ألواح أفقية متقاربة (عصري)

تقسيم الشبابيك: بدون | الباب الرئيسي: زجاج بتقسيمات (فرنسي)

## أنواع الدربزين المعتمدة (من مشاريع المصنع)

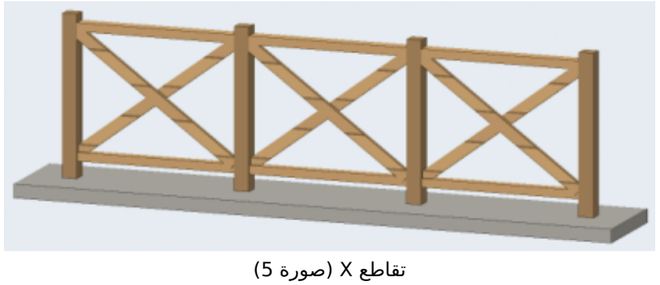

تقاطع X (صورة 5)

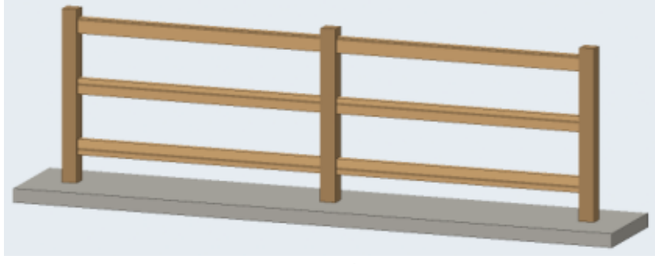

3 مرابيع أفقية (صورة 2)



قوائم رأسية متقاربة (صورة 1)

| المشروع / العميل | عنوان اللوحة | المقياس | التاريخ | رقم اللوحة |
|---|---|---|---|---|
| **فيلا دورين — مجلس ومقلط + 6 غرف — 15.00 × 22.00**<br>**عميل — فيلا 6 غرف** | **المنظور والمواد** | — | **2026-10-21** | **A-11 (11/11)** |

**مصنع وتد الأخشاب**
Watad Wood Factory