
مصنع وتد الأخشاب · ملف التصميم

كوخ A-frame دورين

9.00 × 10.00 م · مثلث حاد 61° · القمة 8.27 م · صالة ومطبخ أمريكي وحمامين · غرفتين وحمام · أرض بسور

المسقط الأفقي مع الفرش


الأبعاد بالسنتيمتر - الجدران: قوائم 7×5 + تلبيس 2.5 من الجهتين (12 سم)

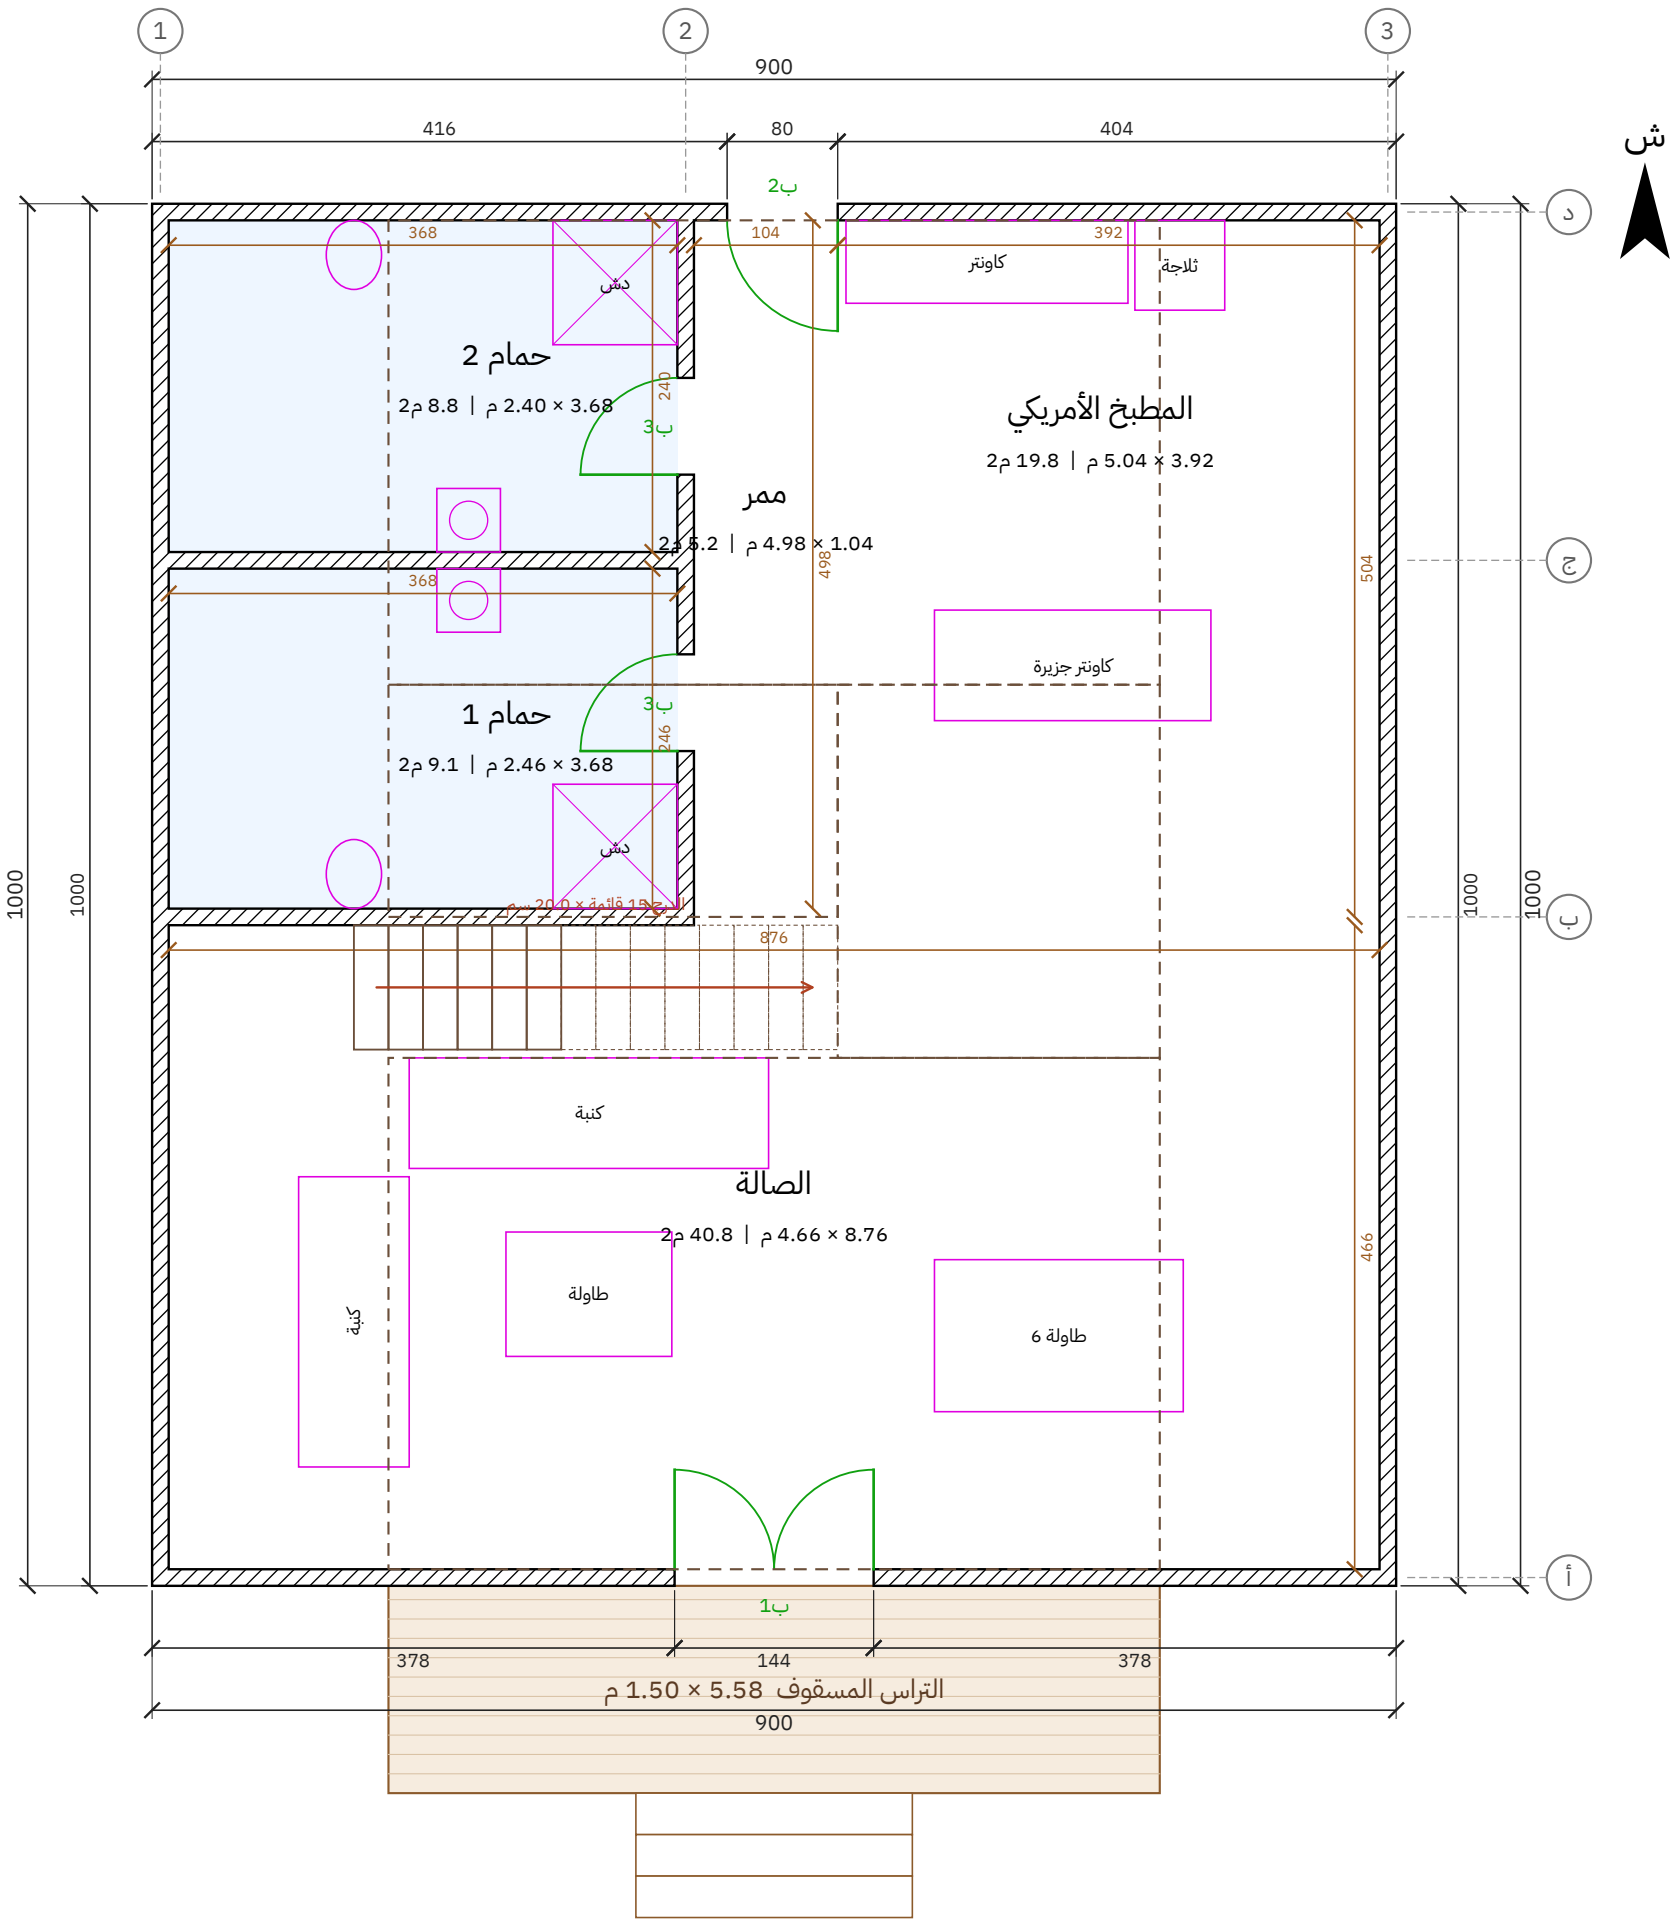

مصنع وتد الأخشاب Watad Wood Factory	المشروع / العميل كوخ A-frame دورين — صالة ومطبخ أمريكي وحمامين + غرفتين وحمام — 9.00 × 10.00 م عميل — A-frame دورين	عنوان اللوحة المسقط الأفقي	المقياس 1:50	التاريخ 2026-10-24	رقم اللوحة A-02 (2/11)


المسقط الأفقي مع الفرش — الدور الأول (داخل المثلث)

منسوب الأرضية +3.00 | الأبعاد بالسنتيمتر | الوقفة الكاملة ≥ 2.10 م بين الخطين المتقطعين

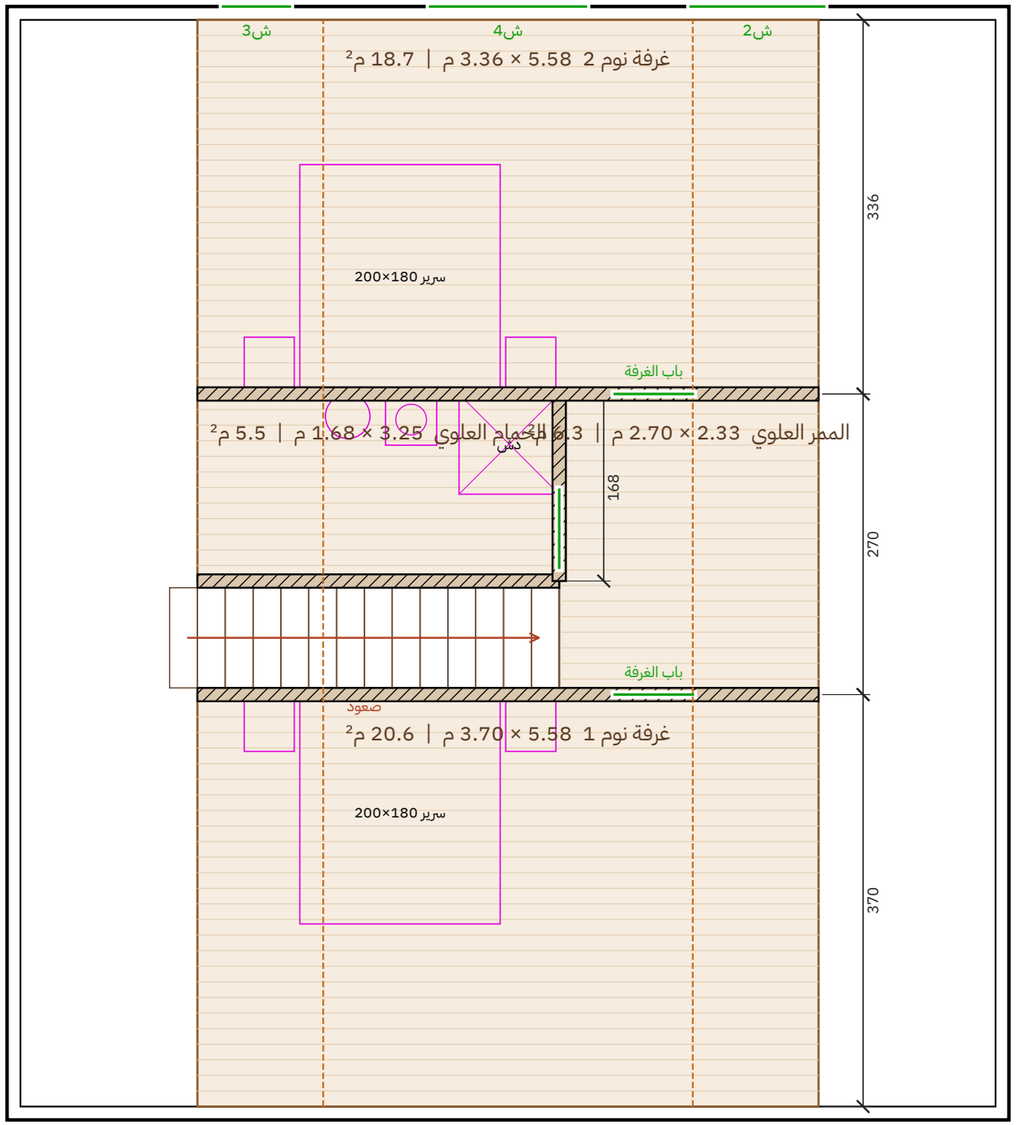

المشروع / العميل	عنوان اللوحة	المقياس	التاريخ	رقم اللوحة
كوخ A-frame دورين — صالة ومطبخ أمريكي وحمامين + غرفتين وحمام — 9.00 × 10.00 م عميل — A-frame دورين	المسقط الأفقي مع الفرش — الدور الأول (داخل المثلث)	1:50	2026-10-24	A-03 (3/11)

مصنع وتد الأخشاب
Watad Wood Factory

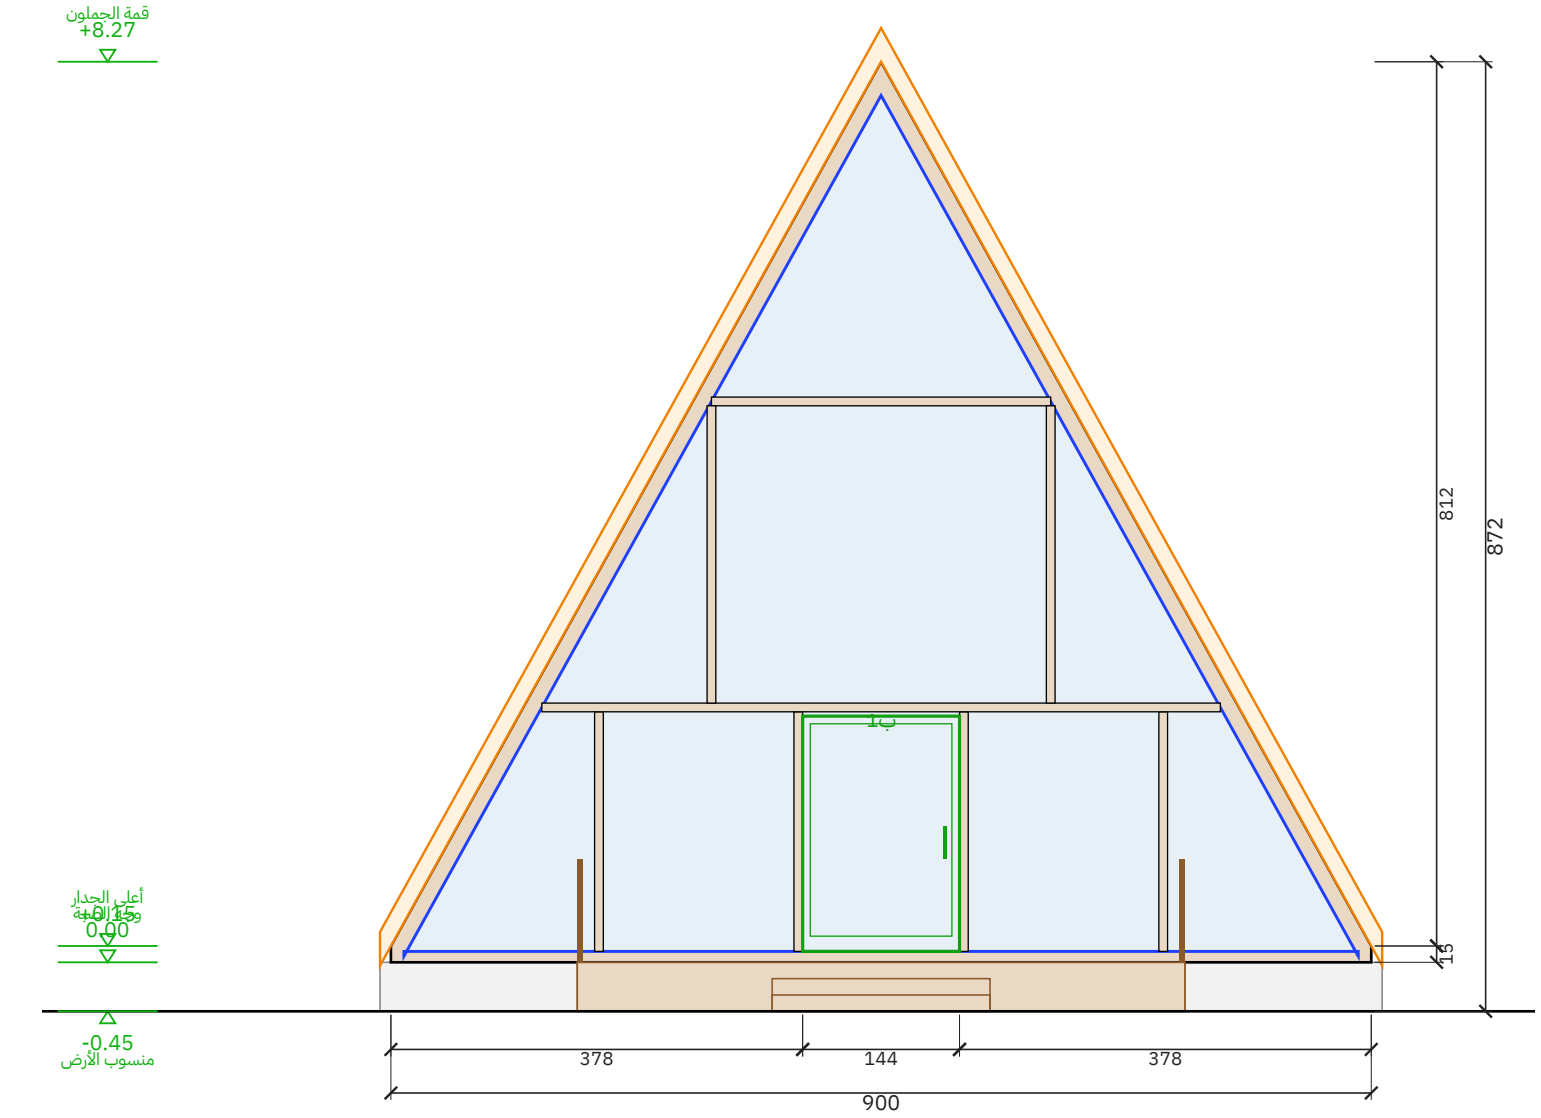

الواجهة الأمامية (مثلث زجاج كامل)

مقياس 1:50 | الوحدة: سم




الواجهة الشرقية (السقف لين الأرض)

مقياس 1:50 | الوحدة: سم


المشروع / العميل	عنوان اللوحة	المقياس	التاريخ	رقم اللوحة
نوع A-frame دورين — صالة ومطبخ أمريكي وحمامين + غرفتين وحمام — 9.00 × 10.00 م عميل — A-frame دورين	الواجهة الأمامية (مثلث زجاج كامل) والواجهة الشرقية (السقف لين الأرض)	1:50	2026-10-24	A-04 (4/11)

مصنع وتد الأخشاب
Watad Wood Factory

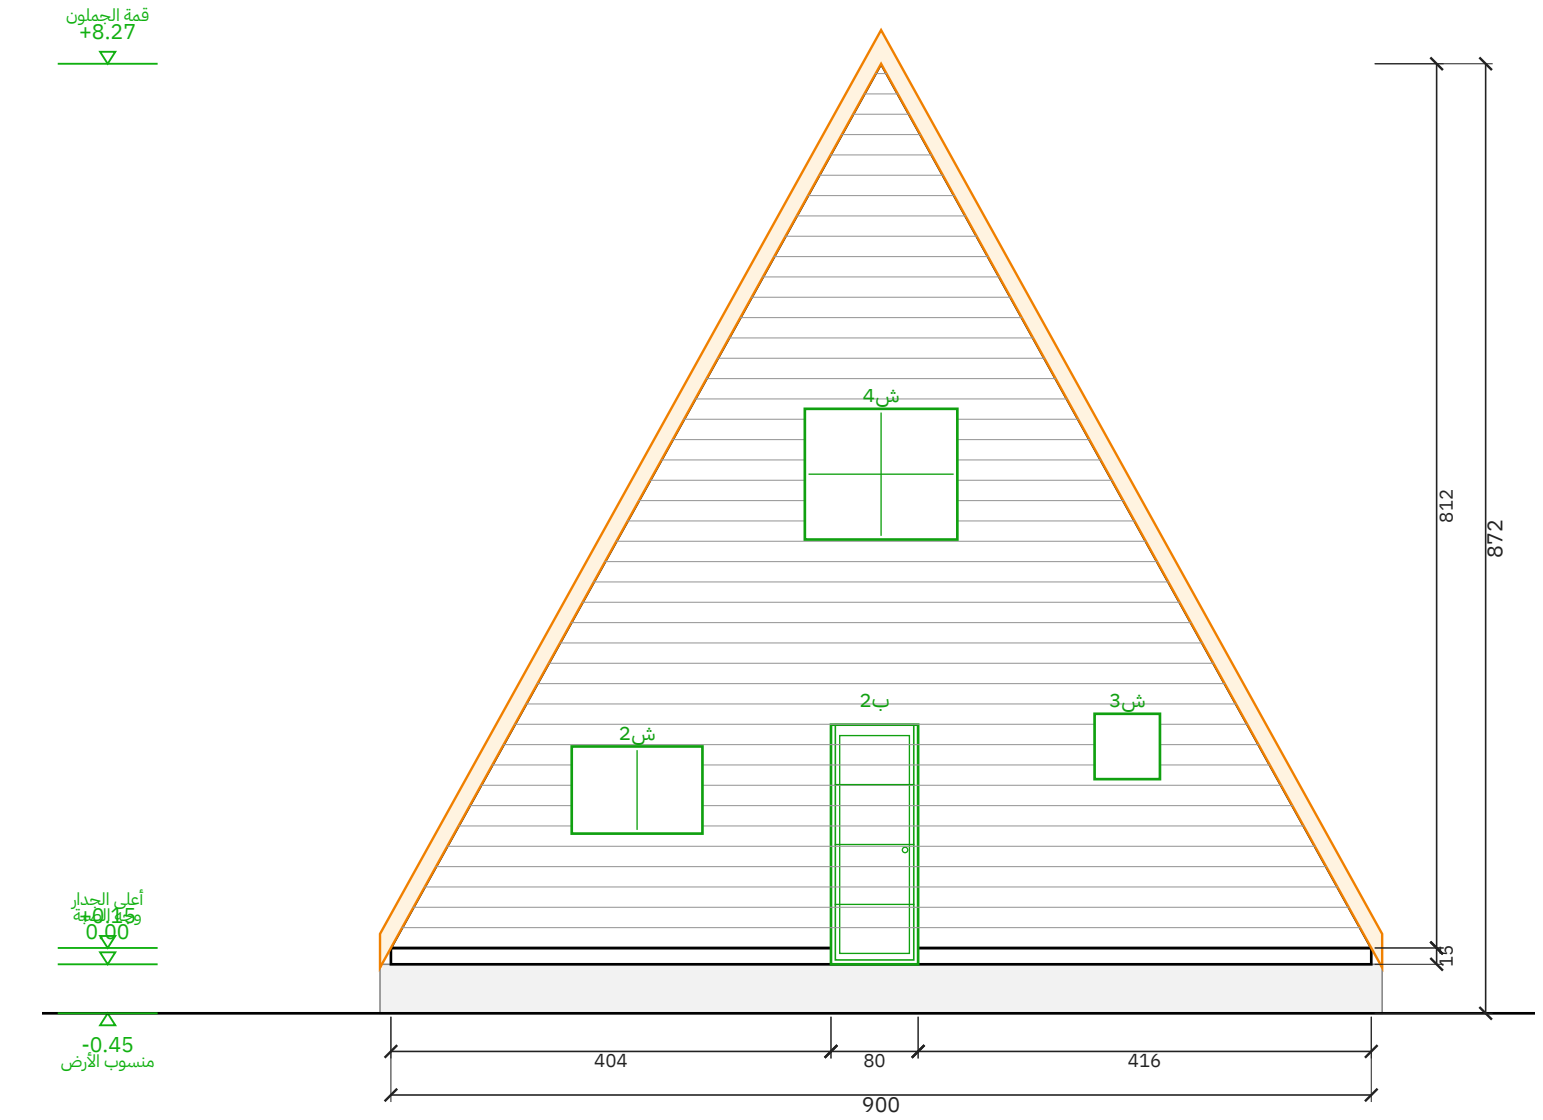

الواجهة الخلفية

مقياس 1:50 | الوحدة: سم

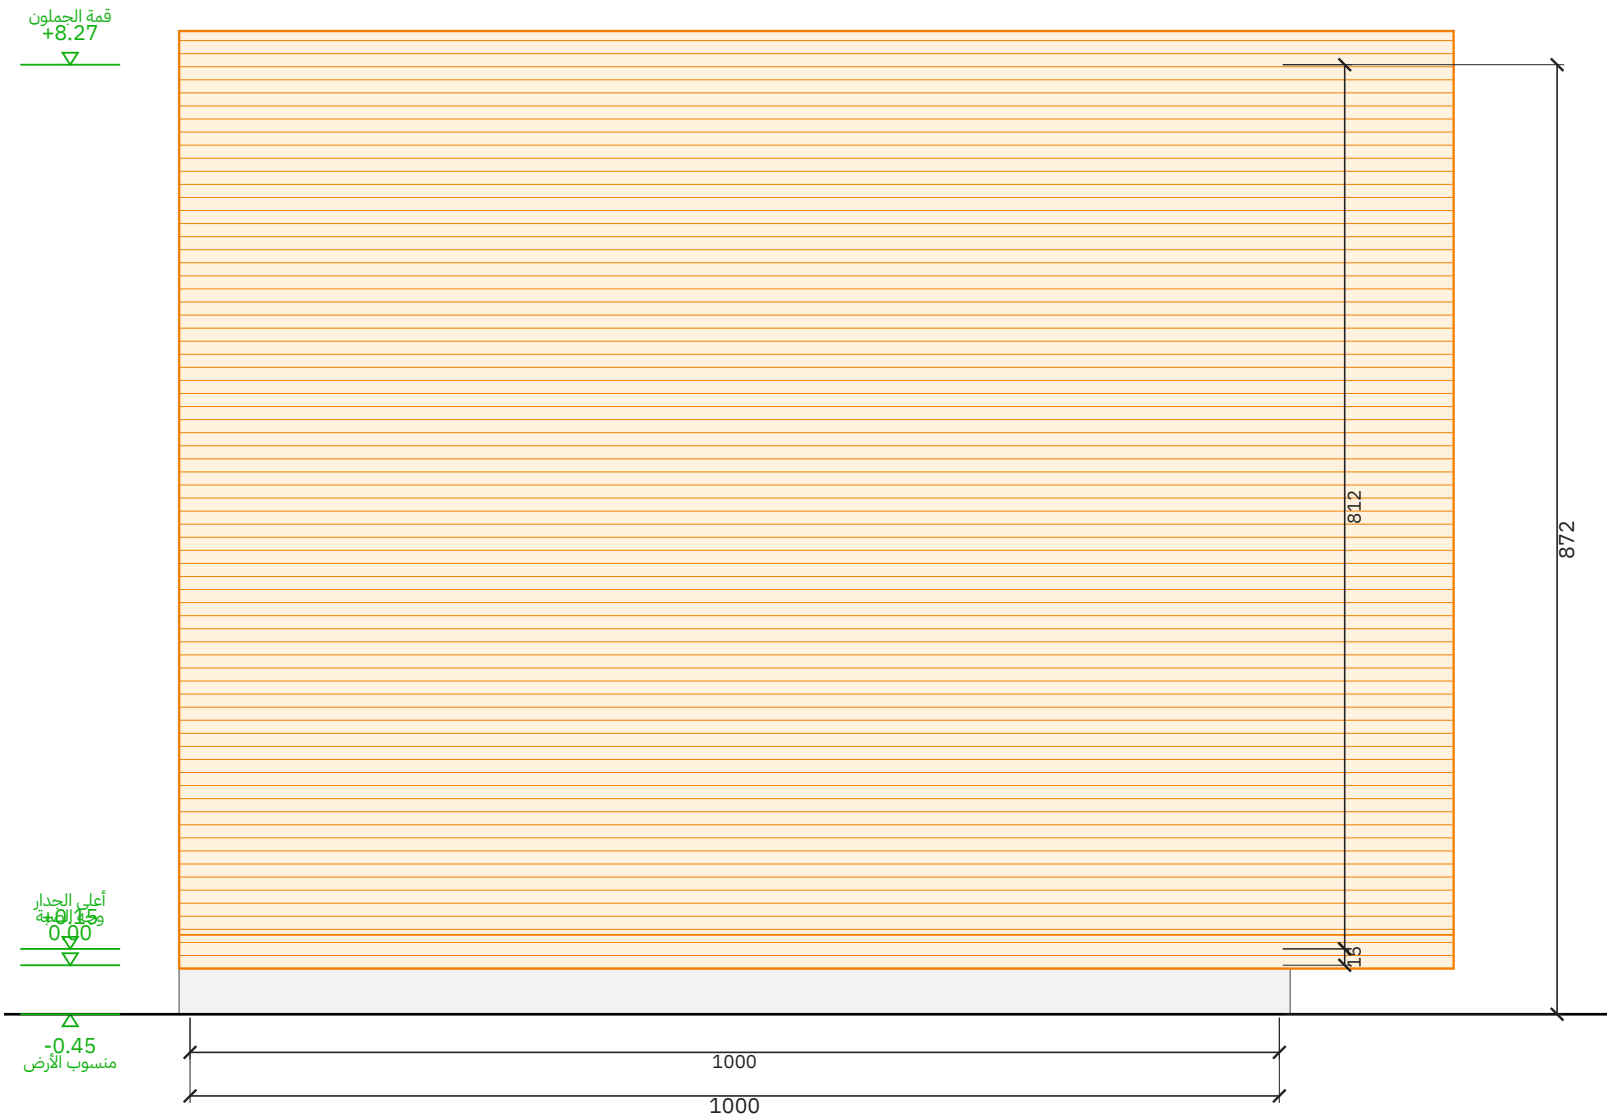

الواجهة الغربية (السقف لين الأرض)


مقياس 1:50 | الوحدة: سم

المشروع / العميل	عنوان اللوحة	المقياس	التاريخ	رقم اللوحة
نوع A-frame دورين — صالة ومطبخ أمريكي وحمامين + غرفتين وحمام — 9.00 × 10.00 م عميل — A-frame دورين	الواجهة الخلفية والواجهة الغربية (السقف لين الأرض)	1:50	2026-10-24	A-05 (5/11)

مصنع وتد الأخشاب
Watad Wood Factory


مسقط السقف (جملون)

رفرف 10 سم من كل جهة | مقياس 1:50

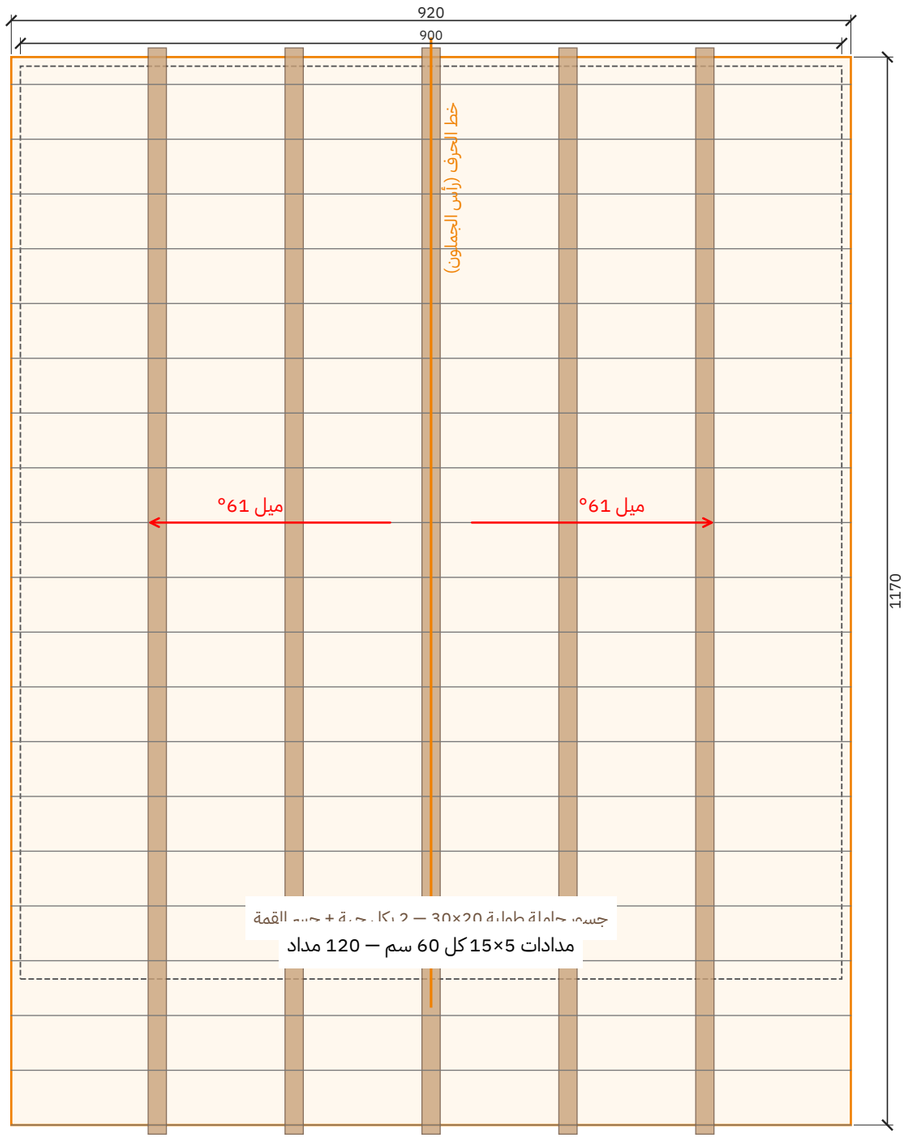


قطاع عرضي أ-أ

مقياس 1:50 | الوحدة: سم

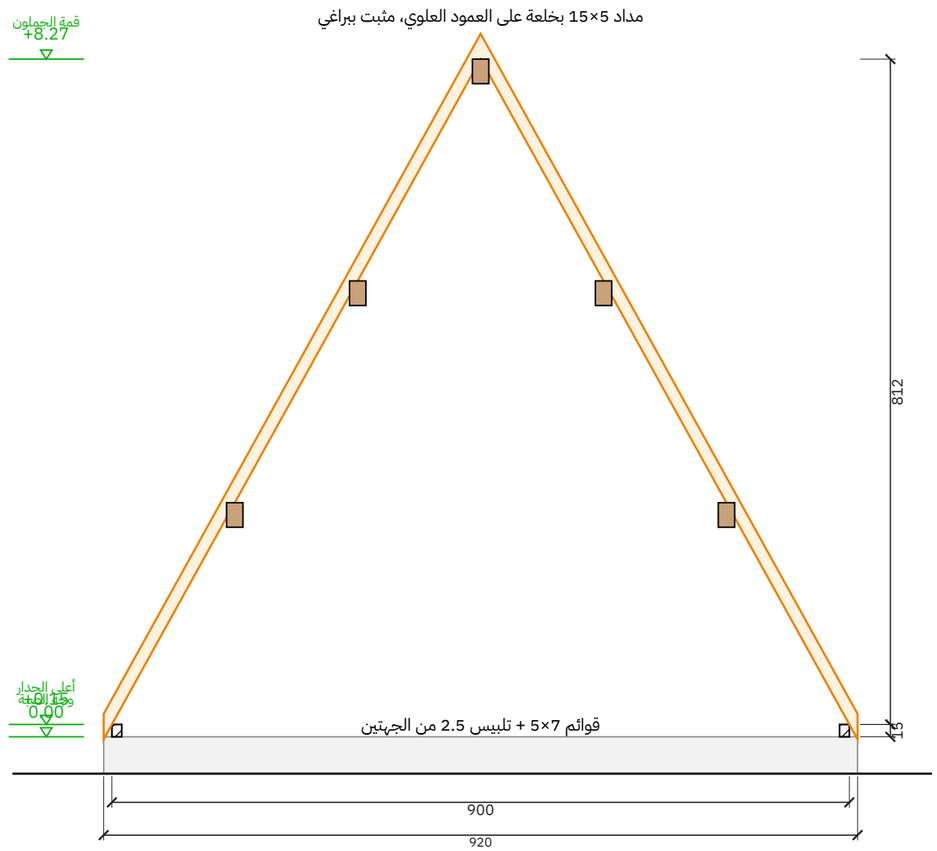

تفصيلة جلوس المداد على العلوي (1:5)

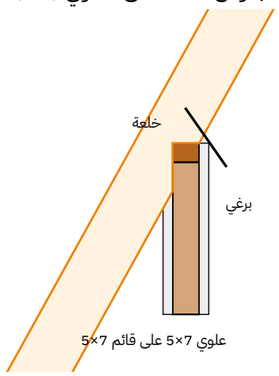


المشروع / العميل	عنوان اللوحة	المقياس	التاريخ	رقم اللوحة
كوخ A-frame دورين — صالة ومطبخ أمريكي وحمامين + غرفتين وحمام — 9.00 × 10.00 م **عميل — A-frame دورين**	**مسقط السقف والقطاع**	**1:50**	**2026-10-24**	**A-06 (6/11)**


مصنع وتد الأخشاب
Watad Wood Factory

لقطات المنظور الخارجي


المنظور الأمامي

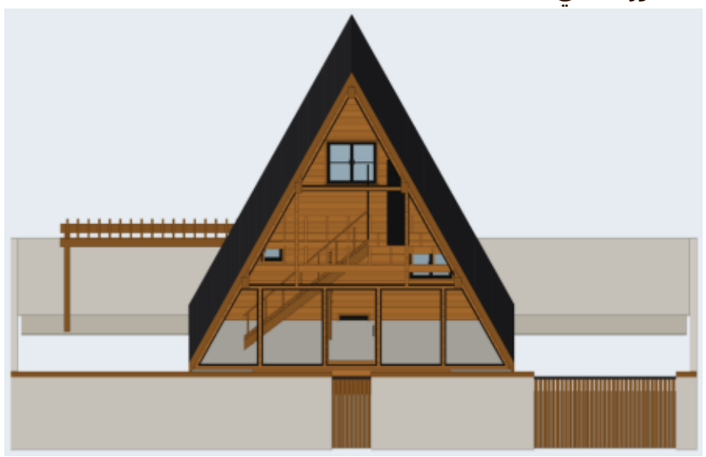


منظور أمامي من اليسار

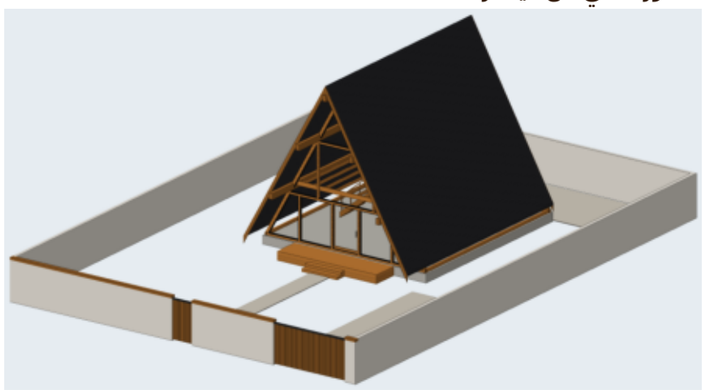


منظور أمامي من اليمين

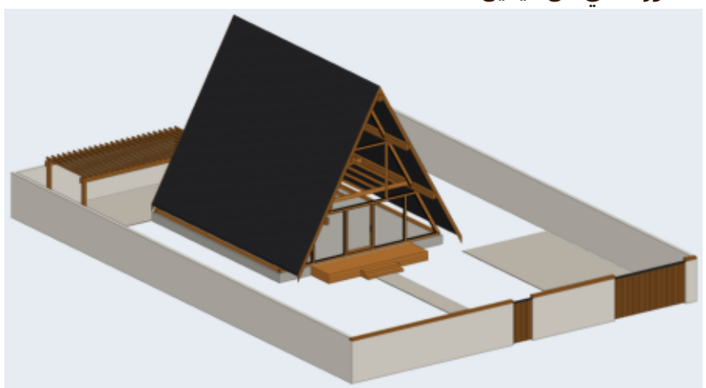


المنظور الخلفي

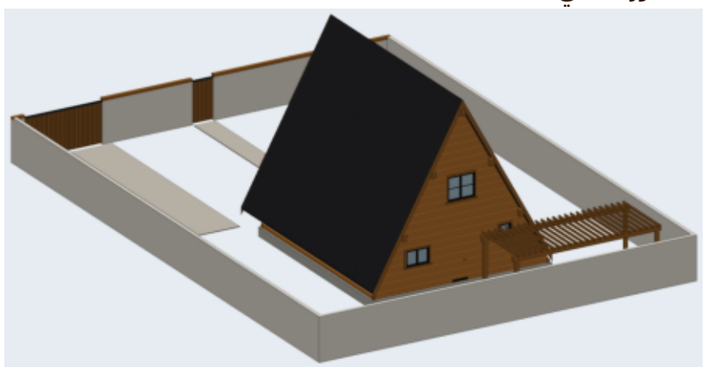

منظور خلفي من اليمين

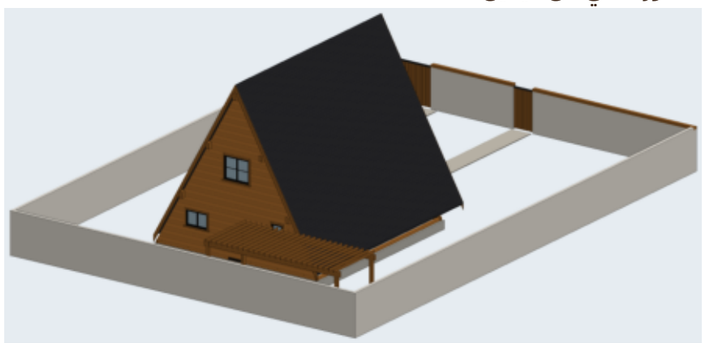

منظر علوي

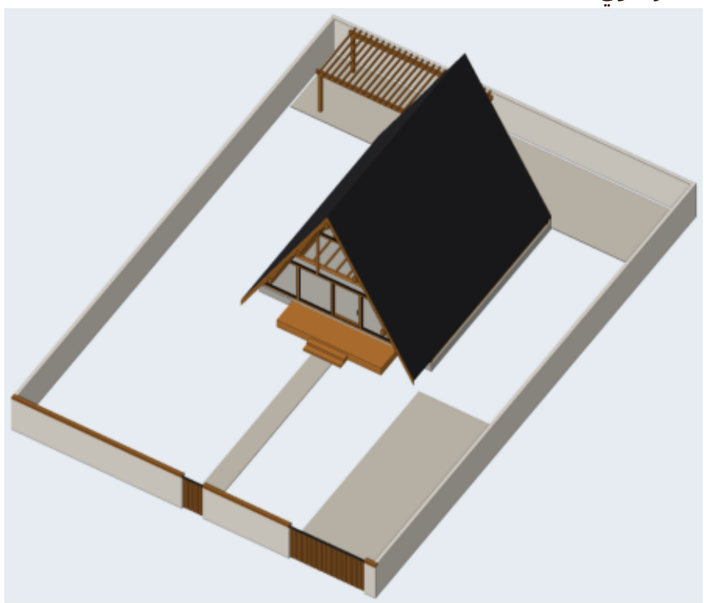


المشروع / العميل	عنوان اللوحة	المقياس	التاريخ	رقم اللوحة
كوخ A-frame دورين – صالة ومطبخ أمريكي وحمامين + غرفتين وحمام – 9.00 × 10.00 م **عميل – A-frame دورين**	**لقطات المنظور**	**–**	**2026-10-24**	**A-09 (9/11)**

مصنع وتد الأخشاب
Watad Wood Factory

المقطع العلوي بالفرش

مقطع أفقي على ارتفاع 1.90 م — توزيع الفرش ومسار الحركة

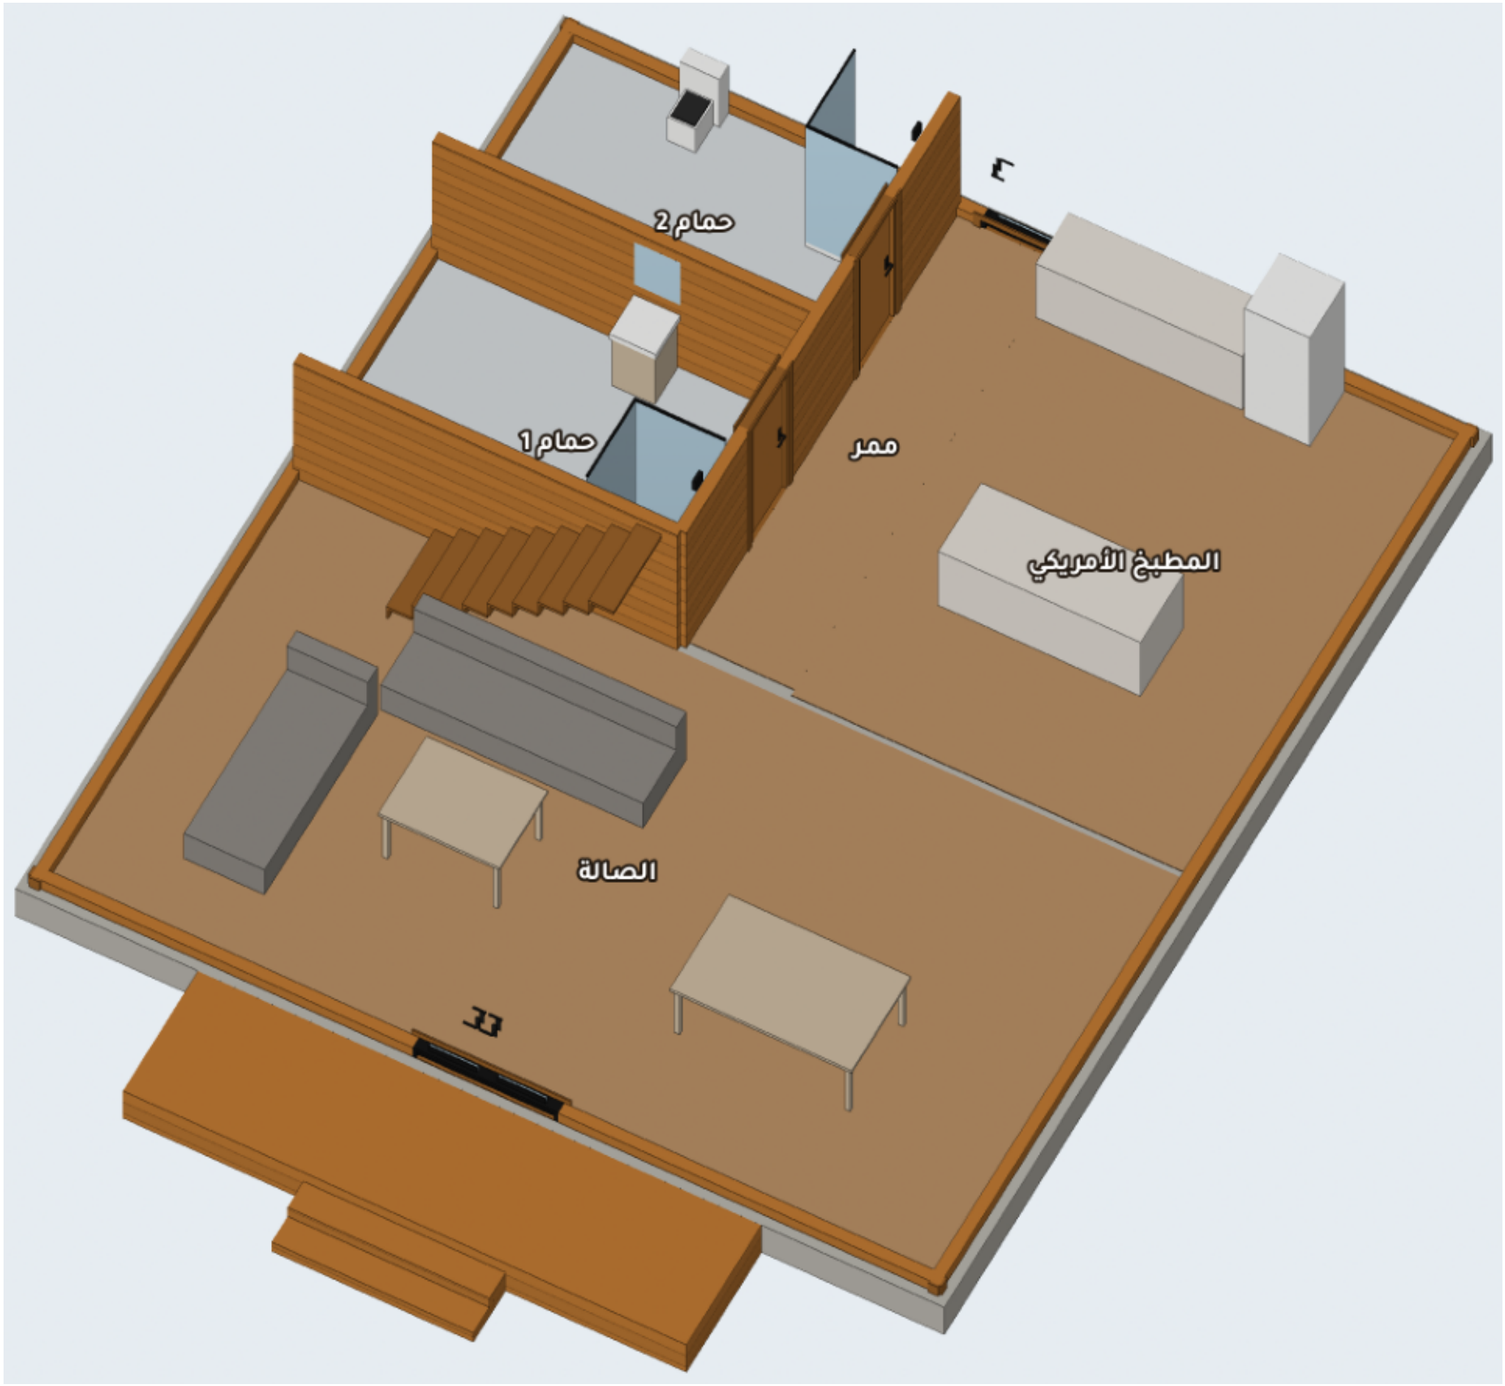

المشروع / العميل	عنوان اللوحة	المقياس	التاريخ	رقم اللوحة
كوخ A-frame دورين — صالة ومطبخ أمريكي وحمامين + غرفتين وحمام — 9.00 × 10.00 م **عميل — A-frame دورين**	**المقطع العلوي بالفرش**	**—**	**2026-10-24**	**A-10 (10/11)**

مصنع وتد الأخشاب
Watad Wood Factory



مصنع وتد الأخشاب



مصنع وتد الأخشاب



مصنع وتد الأخشاب

منظر علوي – الأرض والسور · الخارج – نهاراً



مصنع وتد الأخشاب



مصنع وتد الأخشاب



مصنع وتد الأخشاب



مصنع وتد الأخشاب



مصنع وتد الأخشاب



مصنع وتد الأخشاب



مصنع وتد الأخشاب



مصنع وتد الأخشاب



مصنع وتد الأخشاب




مصنع وتد الأخشاب

جدول مساحات الموقع

البند	المقاس	المساحة (م²)
مساحة الأرض	19.00 × 27.00 م	513.0
مسطح الكوخ (البصمة)	9.00 × 10.00 م	90.0
تراس الكوخ	1.50 × 5.58 م	8.4
جلسة خارجية	3.20 × 7.60 م	24.3
بلاط		47.1
موقف سيارة	4.70 × 11.40 م	53.6
ممر	1.10 × 11.34 م	12.5
المسطحات الخضراء (حديقة)	الباقي	277.1

الموقع العام وتنسيق الحديقة (لاندسكيب)

الأرض 19 × 27 م = 513 م² | الأبعاد بالسنتيمتر

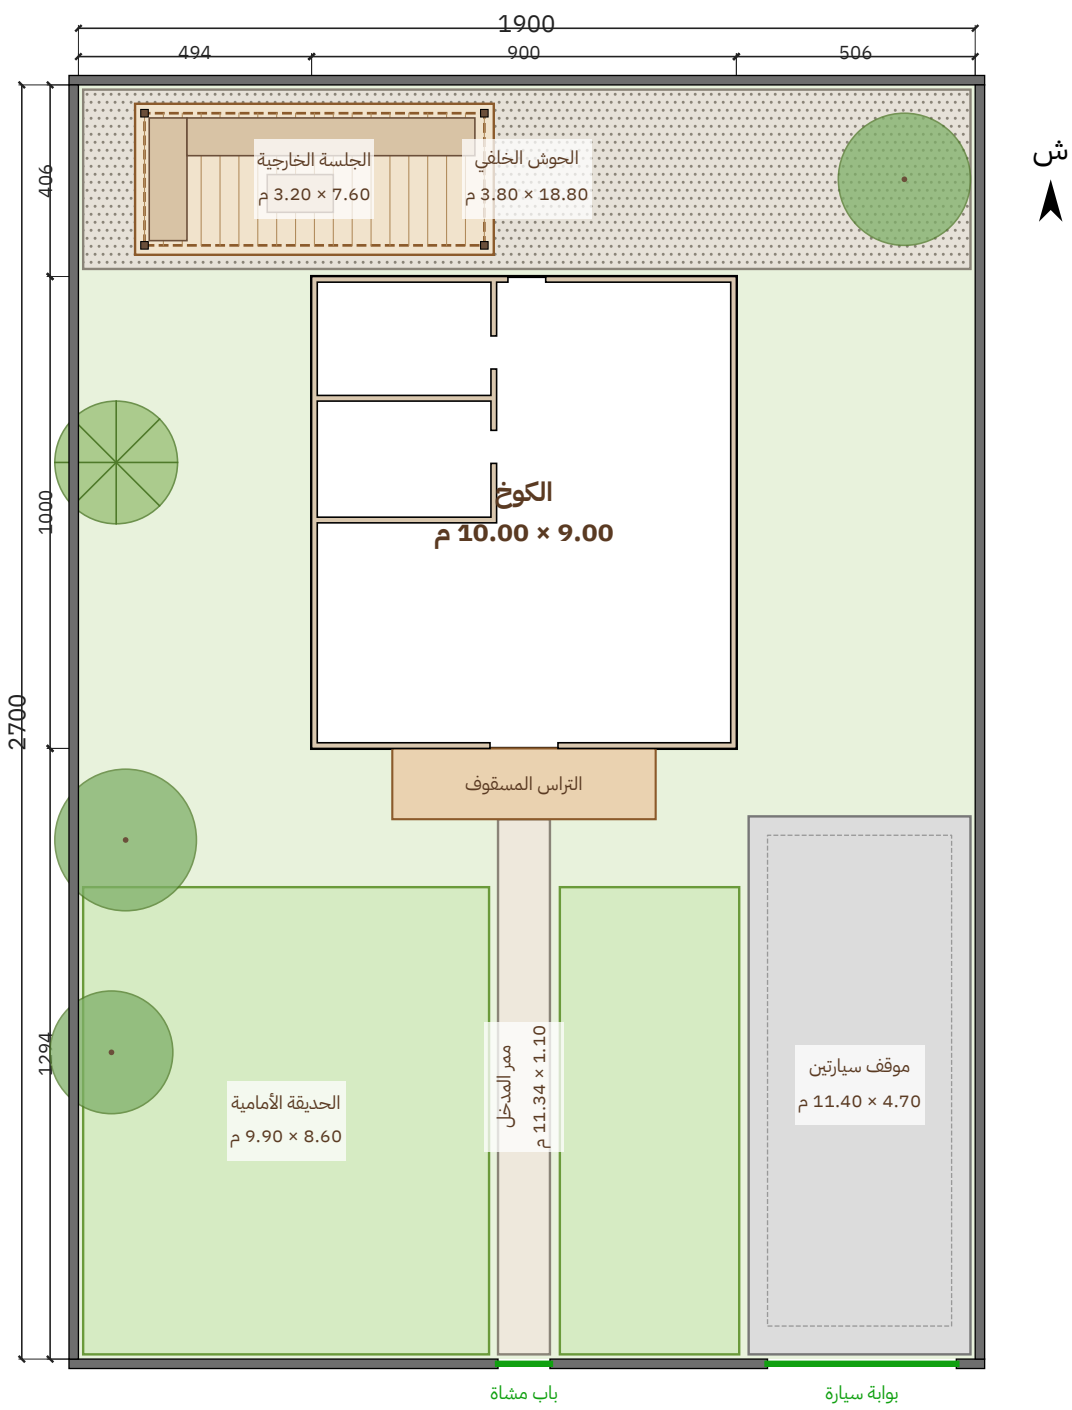

شارع عرض 16 م

المشروع / العميل	عنوان اللوحة	المقياس	التاريخ	رقم اللوحة
كوخ A-frame دورين — صالة ومطبخ أمريكي وحمامين + غرفتين وحمام — 9.00 × 10.00 م عميل — A-frame دورين	الموقع العام واللاندسكيب	1:200	2026-10-24	A-01 (1/11)

مصنع وتد الأخشاب
Watad Wood Factory

جدول مقاسات الأبواب والشبابيك


مقاس الفتحة الصافي في الجدار - الوحدة: سم

الرمز	النوع	العرض (سم)	الارتفاع (سم)	ارتفاع الجلسة (سم)	العدد	الموقع
ب1	باب مزدوج	144	230	-	1	الأمامية (مثلث زجاج كامل)
ب2	باب	80	220	-	1	الخلفية
ب3	باب	70	210	-	2	حمام 1 - حمام 2
ش2	باب	120	80	-	1	الخلفية
ش3	باب	60	60	-	1	الخلفية
ش4	باب	140	120	-	1	الخلفية

الإجمالي: أبواب 7 - شبابيك 0

المنظور ثلاثي الأبعاد والمواد

النمط: جوزي غامق + إطارات سوداء — رندر واقعي بخامات حقيقية

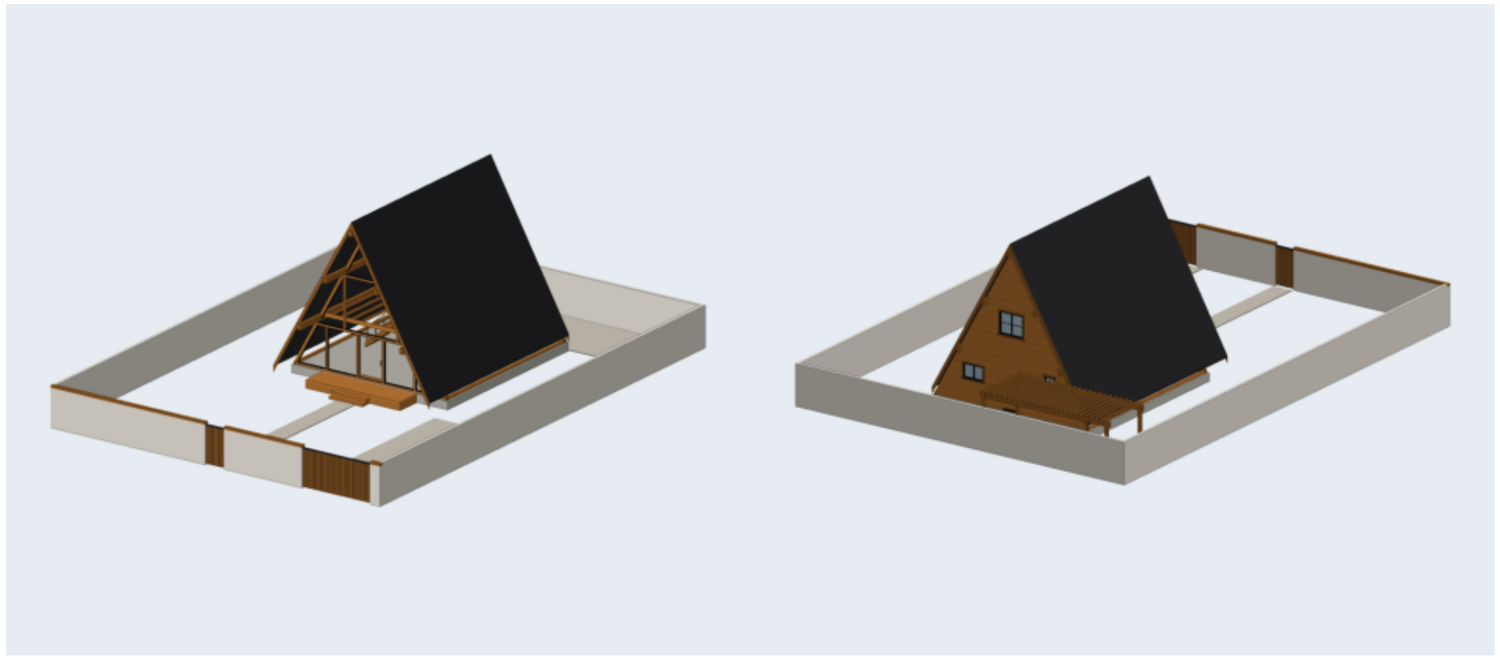

جدول المواد والألوان

الخشب / الصبغة

صبغة عسلي / سيدر

القرميد

قرميد رمادي غامق

الزجاج

زجاج شفاف

إطارات الشبابيك والأبواب

إطار ألمنيوم أسود

الكنار والزوايا

نفس الصبغة أغمق درجة


الصبة

خرسانة 45 سم


الدربزين: ألواح أفقية متقاربة (عصري)

تقسيم الشبابيك: بدون | الباب الرئيسي: زجاج بتقسيمات (فرنسي)

أنواع الدربزين المعتمدة (من مشاريع المصنع)

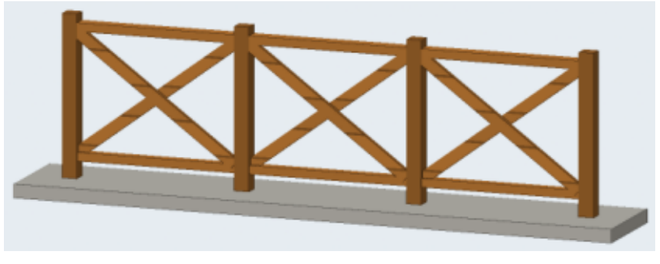

تقاطع X (صورة 5)

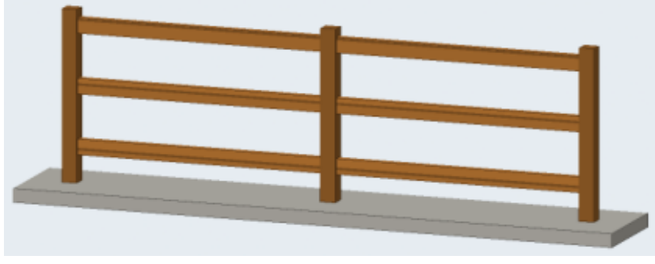

3 مرابيع أفقية (صورة 2)



قوائم رأسية متقاربة (صورة 1)

المشروع / العميل	عنوان اللوحة	المقياس	التاريخ	رقم اللوحة
كوخ A-frame دورين — صالة ومطبخ أمريكي وحمامين + غرفتين وحمام — 9.00 × 10.00 م **عميل — A-frame دورين**	**المنظور والمواد**	**—**	**2026-10-24**	**A-11 (11/11)**

مصنع وتد الأخشاب
Watad Wood Factory

جدول المساحات وبيانات المشروع

بيانات المشروع

البند	البيان
المشروع	كوخ A-frame دورين — صالة ومطبخ أمريكي وحمامين + غرفتين وحمام — 9.00 × 10.00 م
العميل	عميل — A-frame دورين
الموقع	—
الاستخدام	سكن / استراحة
التاريخ	2026-10-24
نظام البناء	هيكل خشب 5×7 + تلبيس 2.5 سم من الجهتين
السقف	جملون 61° — قرميد معدني

جدول المساحات

م	الفراغ	الأبعاد (م)	المساحة (م2)
1	الصالة	4.66 × 8.76	40.82
2	حمام 1	2.46 × 3.68	9.05
3	حمام 2	2.40 × 3.68	8.83
4	ممر	4.98 × 1.04	5.18
5	المطبخ الأمريكي	5.04 × 3.92	19.76
6	أول — غرفة نوم 1	3.70 × 5.58	20.65
7	أول — الممر العلوي	2.70 × 2.33	6.29
8	أول — الحمام العلوي	1.68 × 3.25	5.46
9	أول — غرفة نوم 2	3.36 × 5.58	18.75
	المساحة الصافية الداخلية		134.79
	التراس المسقوف	1.50 × 5.58	8.37
	مسطح الأرضي	**10.00 × 9.00**	**90.00**
	مسطح الدور الأول (داخل المثلث)		**51.15**
	المساحة الإجمالية المبنية (الأرضي + الأول)	**مجموع الأدوار**	**141.15**
	المساحة الكلية (المبنية + التراس)		**149.52**