
## جدول مساحات الموقع

| البند | المقاس | المساحة (م²) |
|---|---|---|
| مساحة الأرض | 19.00 × 27.00 م | 513.0 |
| مسطح الكوخ (البصمة) | 9.00 × 10.00 م | 90.0 |
| تراس الكوخ | 1.50 × 5.58 م | 8.4 |
| جلسة خارجية | 3.20 × 7.60 م | 24.3 |
| بلاط | | 47.1 |
| موقف سيارة | 4.70 × 11.40 م | 53.6 |
| ممر | 1.10 × 11.34 م | 12.5 |
| المسطحات الخضراء (حديقة) | الباقي | 277.1 |

الموقع العام وتنسيق الحديقة (لاندسكيب)

الأرض 19 × 27 م = 513 م² | الأبعاد بالسنتيمتر

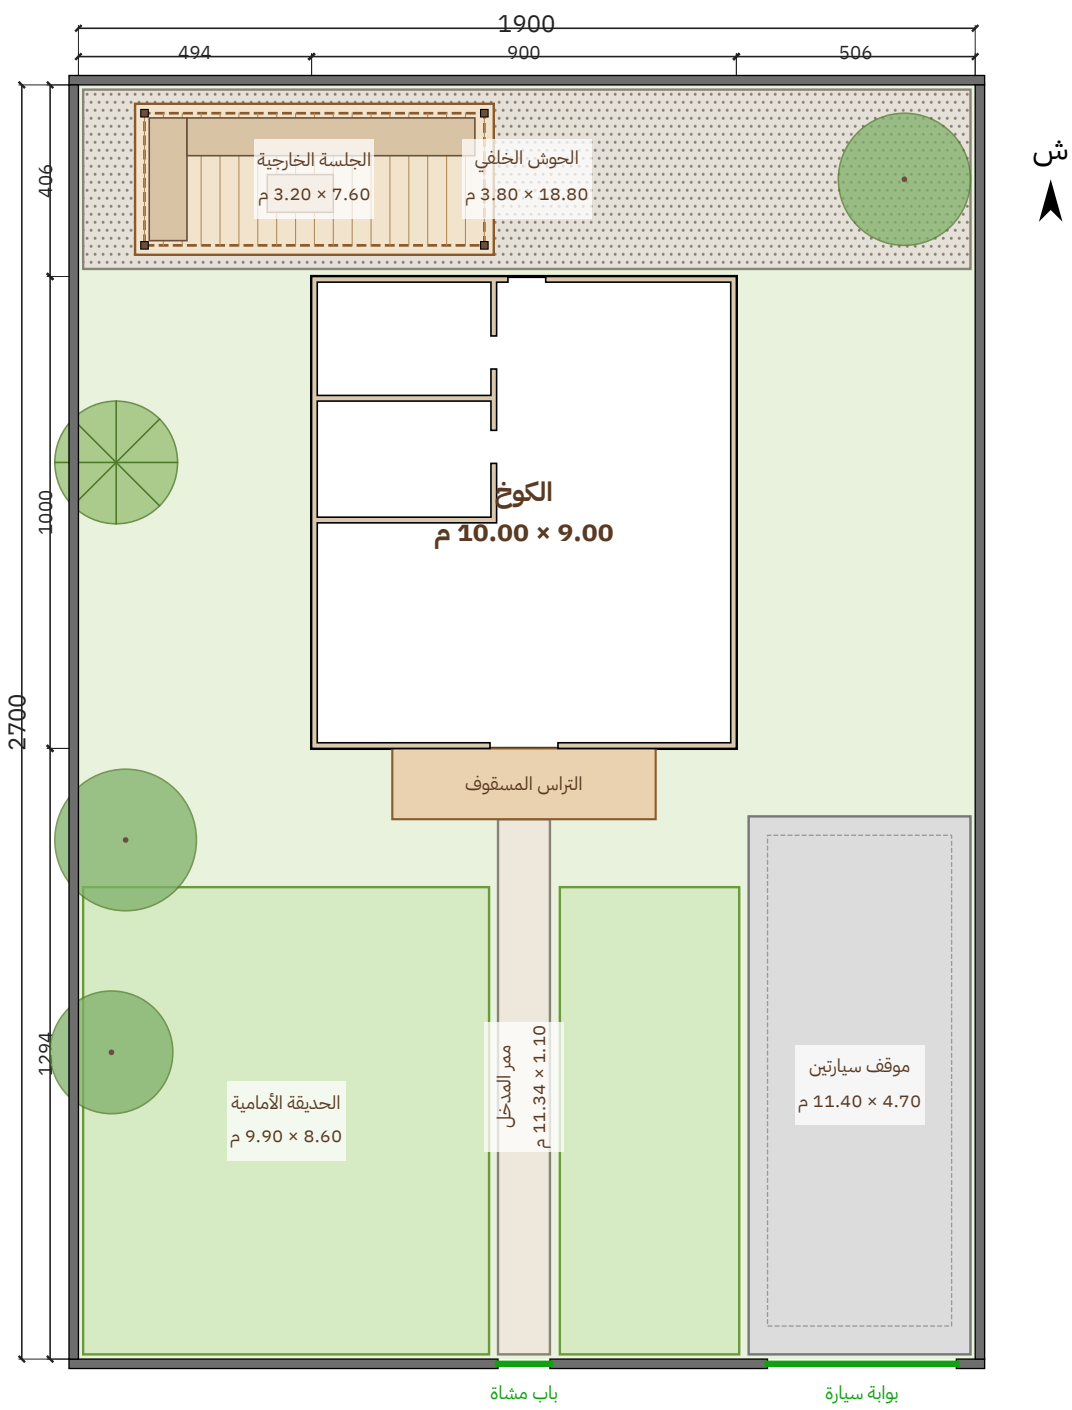



شارع عرض 16 م

| المشروع / العميل | عنوان اللوحة | المقياس | التاريخ | رقم اللوحة |
|---|---|---|---|---|
| كوخ A-frame دورين — صالة ومطبخ أمريكي وحمامين + غرفتين وحمام — 9.00 × 10.00 م<br>عميل — A-frame دورين | الموقع العام واللاندسكيب | 1:200 | 2026-10-24 | A-01 (1/11) |

مصنع وتد الأخشاب
Watad Wood Factory

المسقط الأفقي مع الفرش


الأبعاد بالسنتيمتر - الجدران: قوائم 7×5 + تلبيس 2.5 من الجهتين (12 سم)

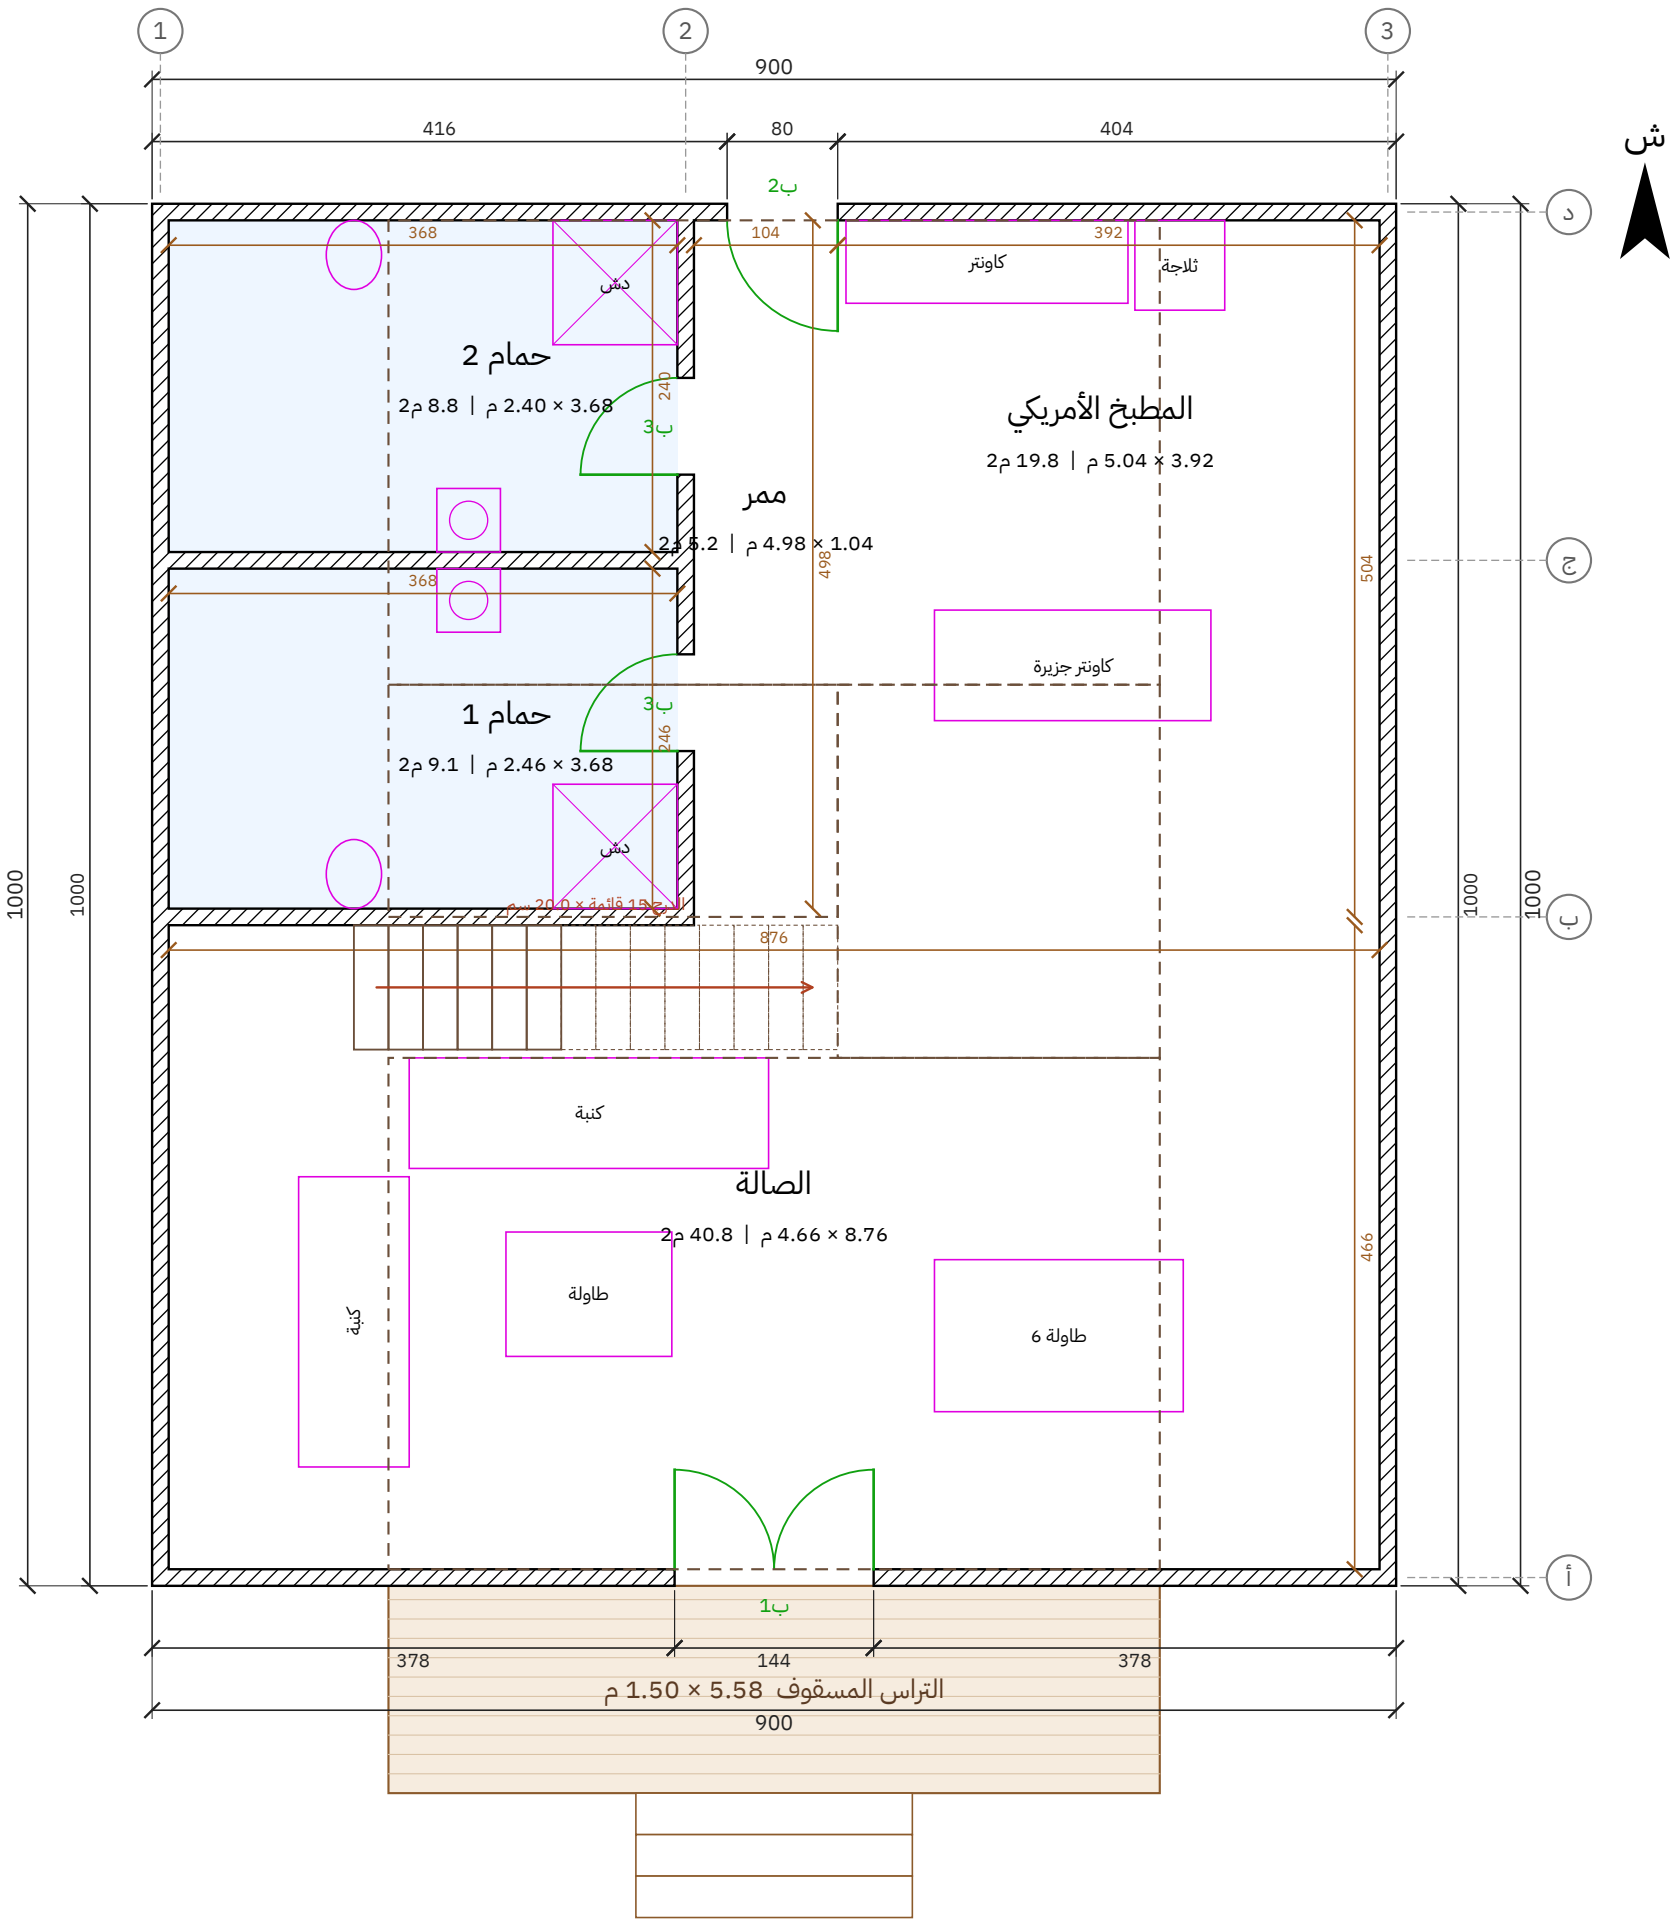


| | | | | | |
|---|---|---|---|---|---|
| مصنع وتد الأخشاب<br>Watad Wood Factory | المشروع / العميل<br>كوخ A-frame دورين — صالة ومطبخ أمريكي وحمامين + غرفتين وحمام — 9.00 × 10.00 م<br>عميل — A-frame دورين | عنوان اللوحة<br>المسقط الأفقي | المقياس<br>1:50 | التاريخ<br>2026-10-24 | رقم اللوحة<br>A-02 (2/11) |


# المسقط الأفقي مع الفرش — الدور الأول (داخل المثلث)

منسوب الأرضية +3.00 | الأبعاد بالسنتيمتر | الوقفة الكاملة ≥ 2.10 م بين الخطين المتقطعين

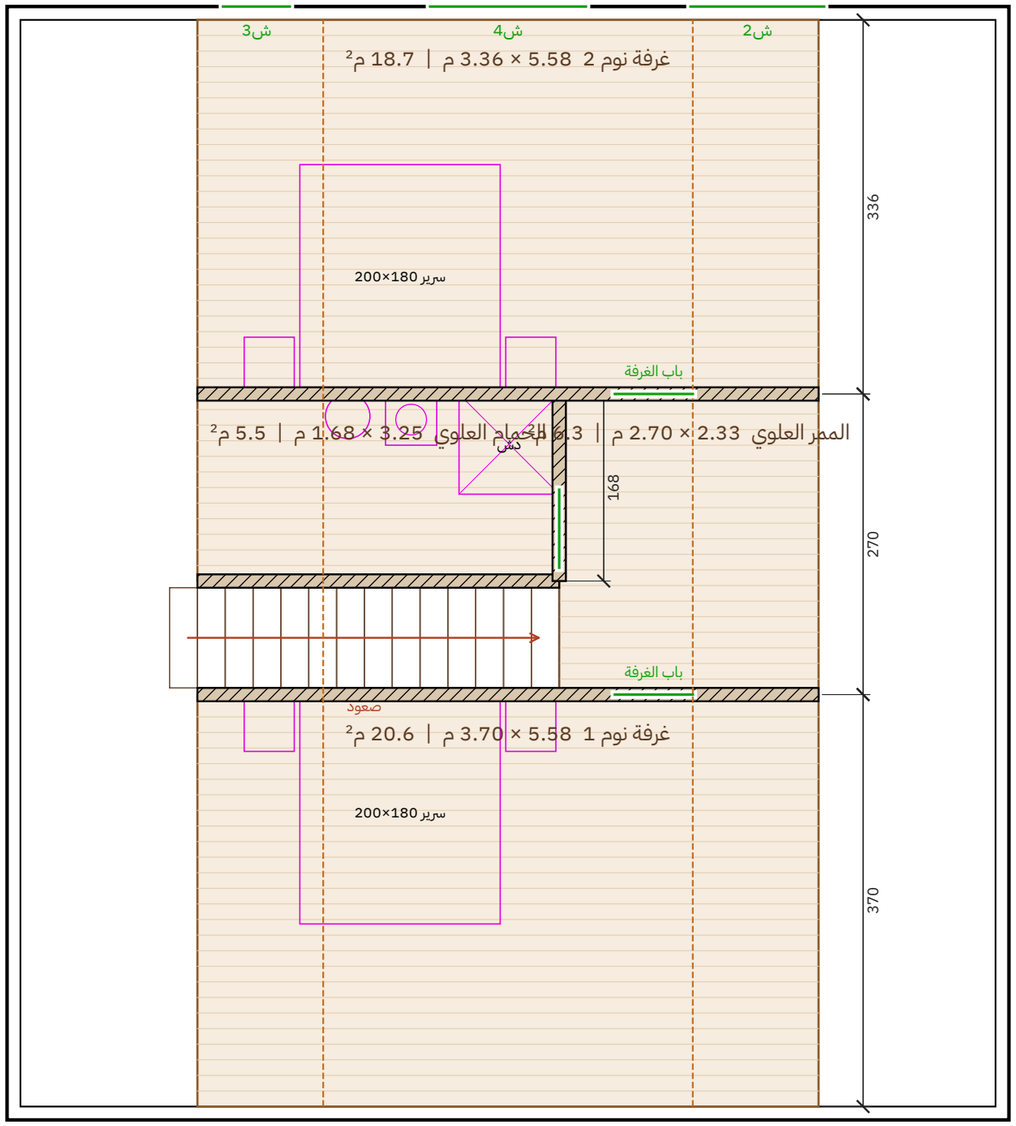


| المشروع / العميل | عنوان اللوحة | المقياس | التاريخ | رقم اللوحة |
|---|---|---|---|---|
| كوخ A-frame دورين — صالة ومطبخ أمريكي وحمامين + غرفتين وحمام — 9.00 × 10.00 م<br>عميل — A-frame دورين | المسقط الأفقي مع الفرش — الدور الأول (داخل المثلث) | 1:50 | 2026-10-24 | A-03 (3/11) |

مصنع وتد الأخشاب
Watad Wood Factory

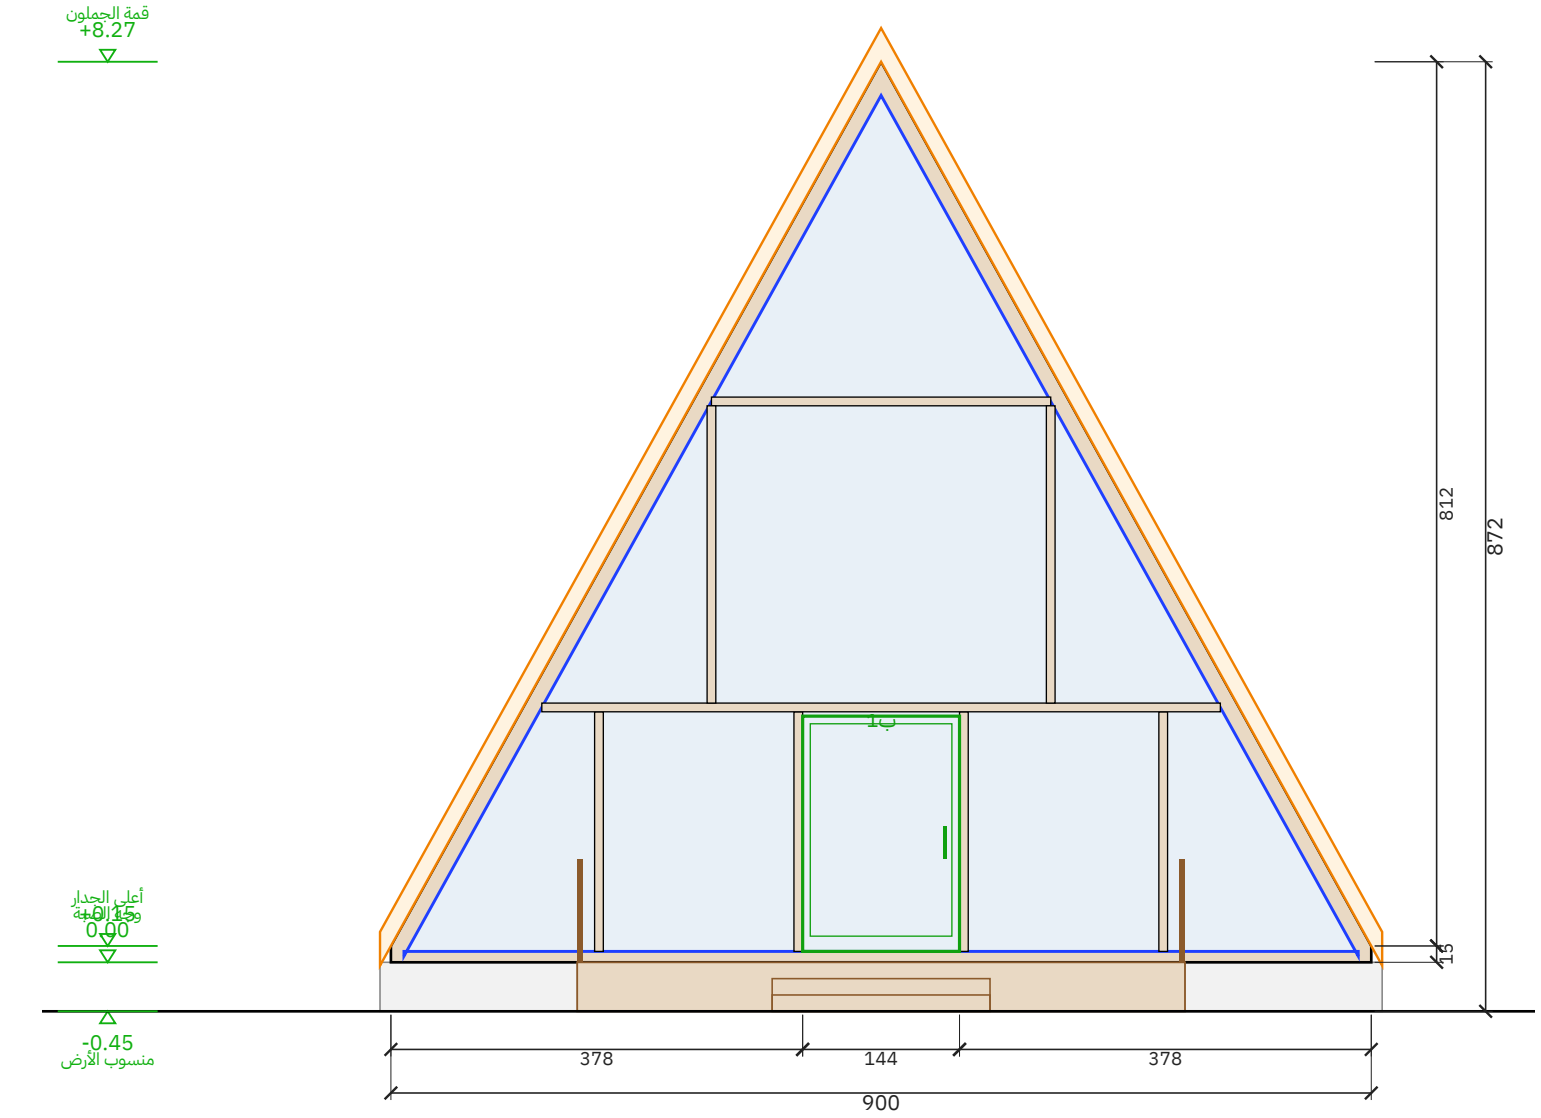


## الواجهة الأمامية (مثلث زجاج كامل)

مقياس 1:50 | الوحدة: سم





## الواجهة الشرقية (السقف لين الأرض)

مقياس 1:50 | الوحدة: سم


| المشروع / العميل | عنوان اللوحة | المقياس | التاريخ | رقم اللوحة |
|---|---|---|---|---|
| نوع A-frame دورين — صالة ومطبخ أمريكي وحمامين + غرفتين وحمام — 9.00 × 10.00 م<br>عميل — A-frame دورين | الواجهة الأمامية (مثلث زجاج كامل) والواجهة الشرقية (السقف لين الأرض) | 1:50 | 2026-10-24 | A-04 (4/11) |

مصنع وتد الأخشاب
Watad Wood Factory

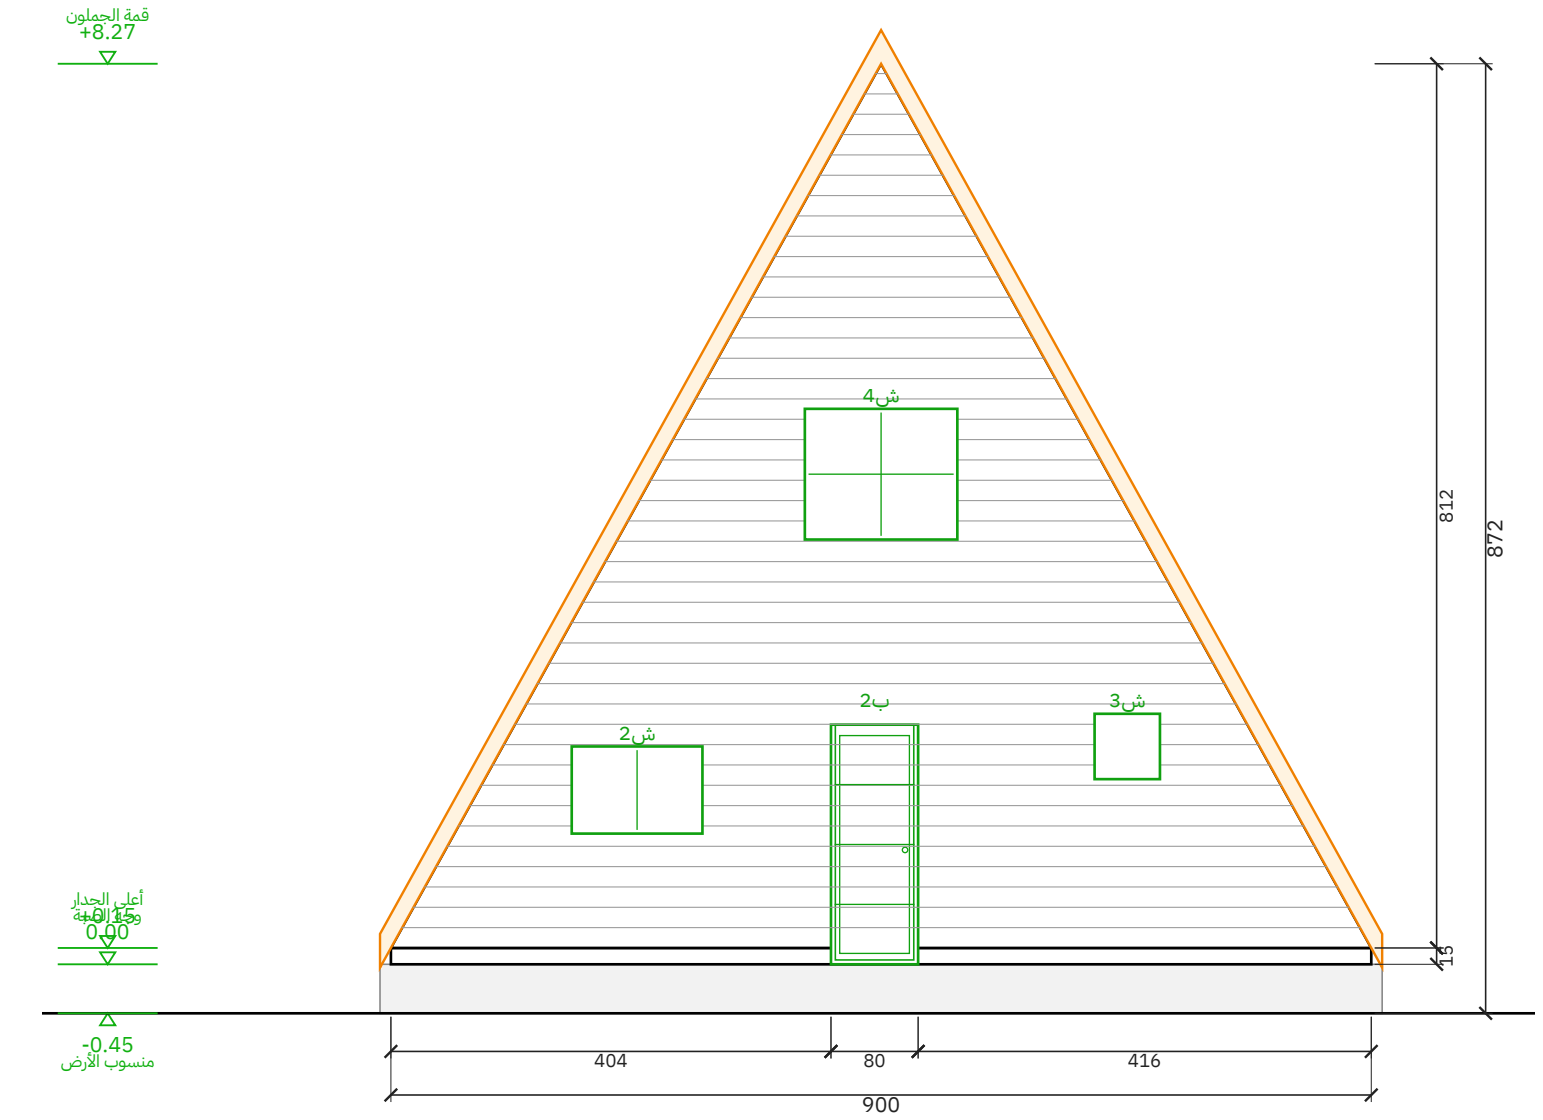


## الواجهة الخلفية

مقياس 1:50 | الوحدة: سم

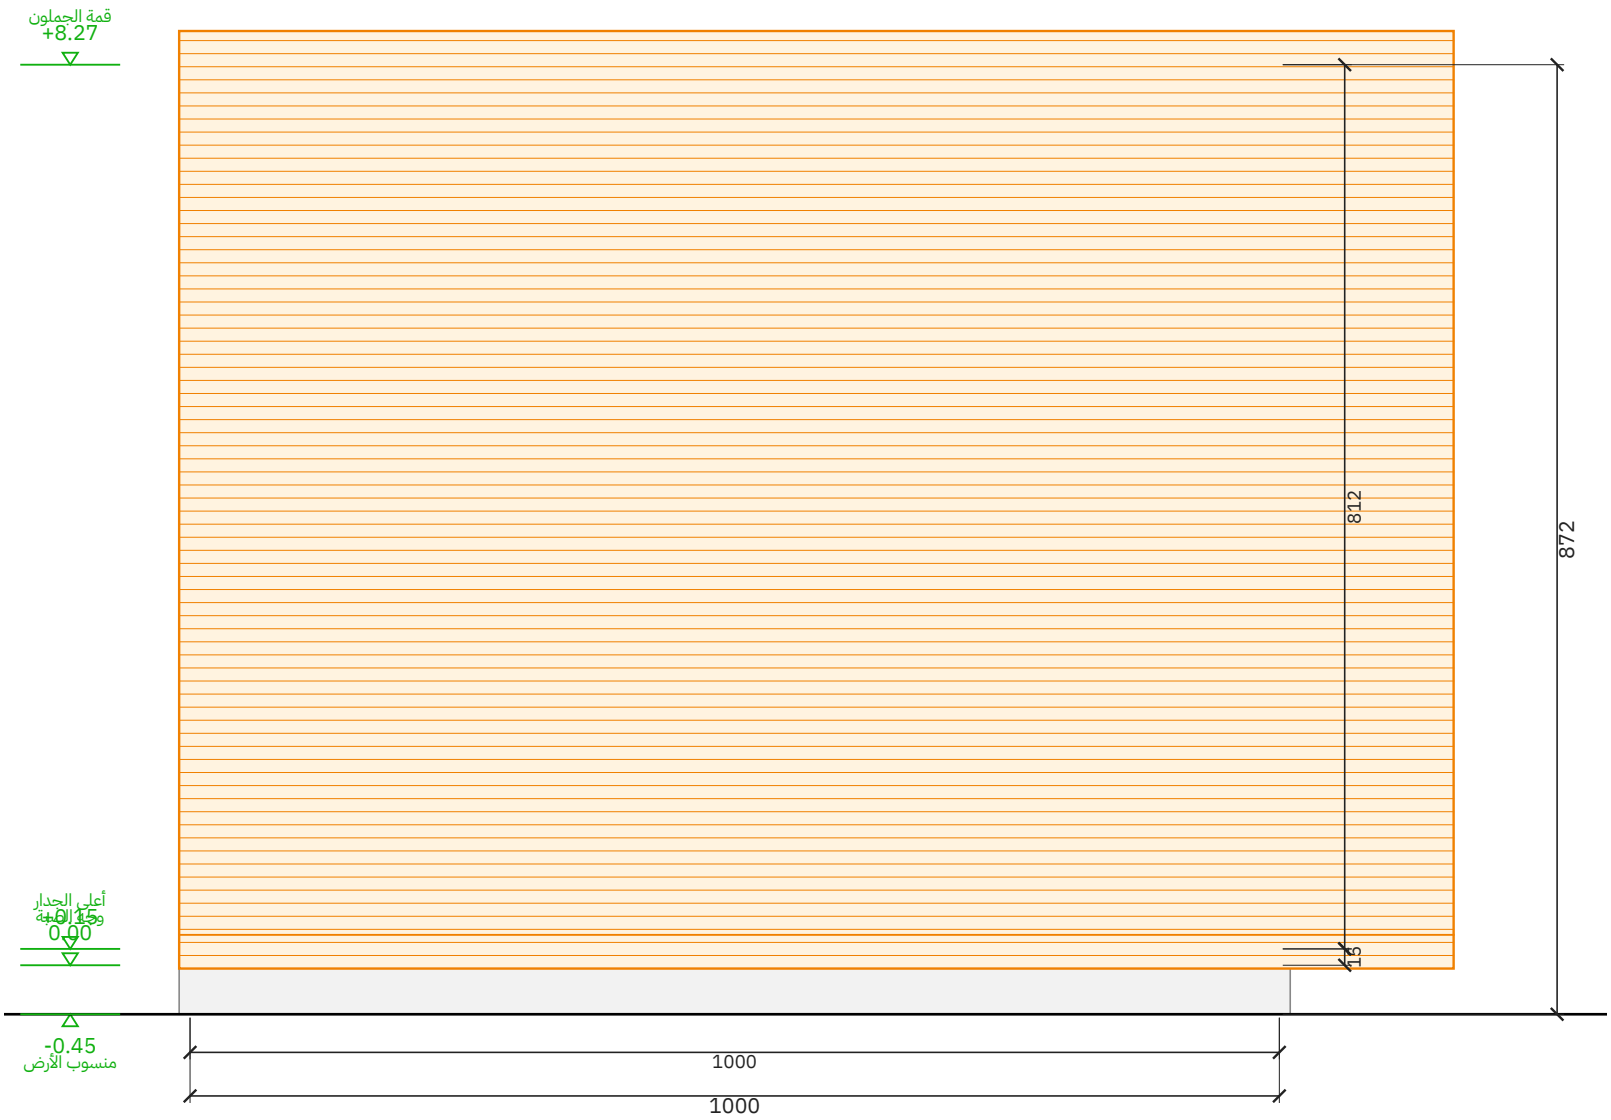


## الواجهة الغربية (السقف لين الأرض)


مقياس 1:50 | الوحدة: سم

| المشروع / العميل | عنوان اللوحة | المقياس | التاريخ | رقم اللوحة |
|---|---|---|---|---|
| نوع A-frame دورين — صالة ومطبخ أمريكي وحمامين + غرفتين وحمام — 9.00 × 10.00 م<br>عميل — A-frame دورين | الواجهة الخلفية والواجهة الغربية (السقف لين الأرض) | 1:50 | 2026-10-24 | A-05 (5/11) |

مصنع وتد الأخشاب
Watad Wood Factory


## مسقط السقف (جملون)

رفرف 10 سم من كل جهة | مقياس 1:50

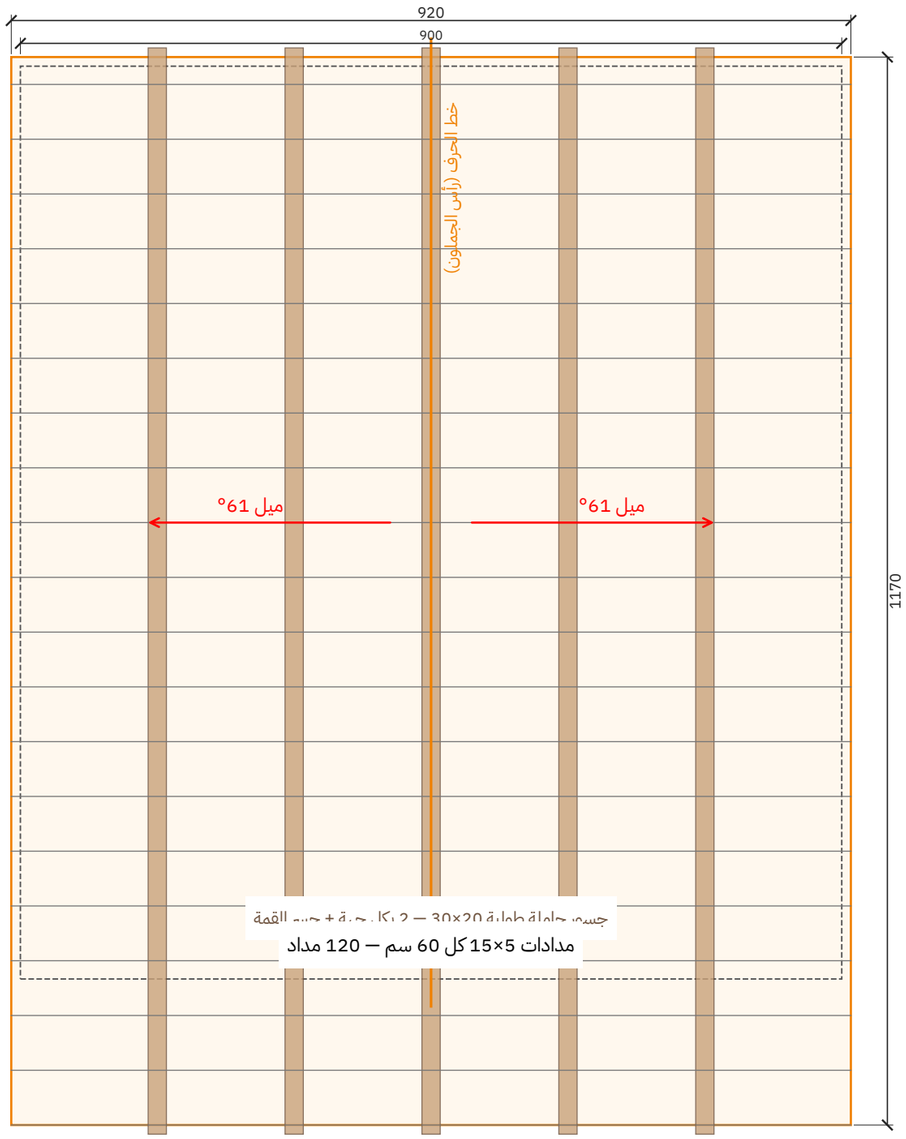



## قطاع عرضي أ-أ

مقياس 1:50 | الوحدة: سم

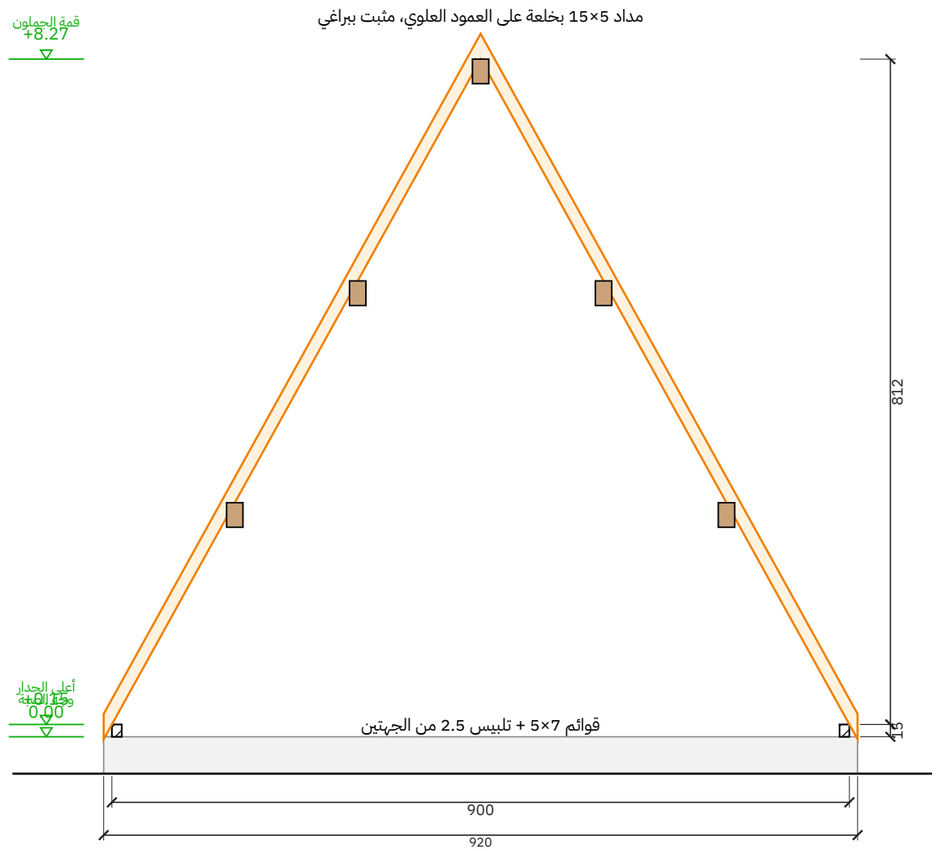


### تفصيلة جلوس المداد على العلوي (1:5)

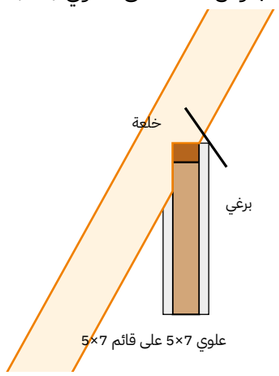


| المشروع / العميل | عنوان اللوحة | المقياس | التاريخ | رقم اللوحة |
|---|---|---|---|---|
| **كوخ A-frame دورين — صالة ومطبخ أمريكي وحمامين + غرفتين وحمام — 9.00 × 10.00 م**<br>**عميل — A-frame دورين** | **مسقط السقف والقطاع** | **1:50** | **2026-10-24** | **A-06 (6/11)** |

**مصنع وتد الأخشاب**
Watad Wood Factory

## جدول مقاسات الأبواب والشبابيك

### مقاس الفتحة الصافي في الجدار - الوحدة: سم

| الرمز | النوع | العرض (سم) | الارتفاع (سم) | ارتفاع الجلسة (سم) | العدد | الموقع |
|---|---|---|---|---|---|---|
| ب1 | باب مزدوج | 144 | 230 | - | 1 | الأمامية (مثلث زجاج كامل) |
| ب2 | باب | 80 | 220 | - | 1 | الخلفية |
| ب3 | باب | 70 | 210 | - | 2 | حمام 1 - حمام 2 |
| ش2 | باب | 120 | 80 | - | 1 | الخلفية |
| ش3 | باب | 60 | 60 | - | 1 | الخلفية |
| ش4 | باب | 140 | 120 | - | 1 | الخلفية |

الإجمالي: أبواب 7 - شبابيك 0

# جدول المساحات وبيانات المشروع

## بيانات المشروع


| البند | البيان |
|---|---|
| المشروع | كوخ A-frame دورين — صالة ومطبخ أمريكي وحمامين + غرفتين وحمام — 9.00 × 10.00 م |
| العميل | عميل — A-frame دورين |
| الموقع | — |
| الاستخدام | سكن / استراحة |
| التاريخ | 2026-10-24 |
| نظام البناء | هيكل خشب 5×7 + تلبيس 2.5 سم من الجهتين |
| السقف | جملون 61° — قرميد معدني |

## جدول المساحات


| م | الفراغ | الأبعاد (م) | المساحة (م2) |
|---|---|---|---|
| 1 | الصالة | 4.66 × 8.76 | 40.82 |
| 2 | حمام 1 | 2.46 × 3.68 | 9.05 |
| 3 | حمام 2 | 2.40 × 3.68 | 8.83 |
| 4 | ممر | 4.98 × 1.04 | 5.18 |
| 5 | المطبخ الأمريكي | 5.04 × 3.92 | 19.76 |
| 6 | أول — غرفة نوم 1 | 3.70 × 5.58 | 20.65 |
| 7 | أول — الممر العلوي | 2.70 × 2.33 | 6.29 |
| 8 | أول — الحمام العلوي | 1.68 × 3.25 | 5.46 |
| 9 | أول — غرفة نوم 2 | 3.36 × 5.58 | 18.75 |
| | المساحة الصافية الداخلية | | 134.79 |
| | التراس المسقوف | 1.50 × 5.58 | 8.37 |
| | **مسطح الأرضي** | **10.00 × 9.00** | **90.00** |
| | **مسطح الدور الأول (داخل المثلث)** | | **51.15** |
| | **المساحة الإجمالية المبنية (الأرضي + الأول)** | **مجموع الأدوار** | **141.15** |
| | **المساحة الكلية (المبنية + التراس)** | | **149.52** |

# لقطات المنظور الخارجي


المنظور الأمامي

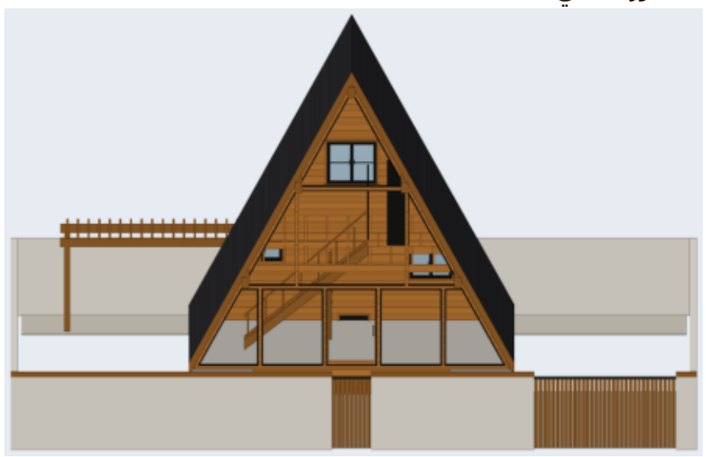


منظور أمامي من اليسار

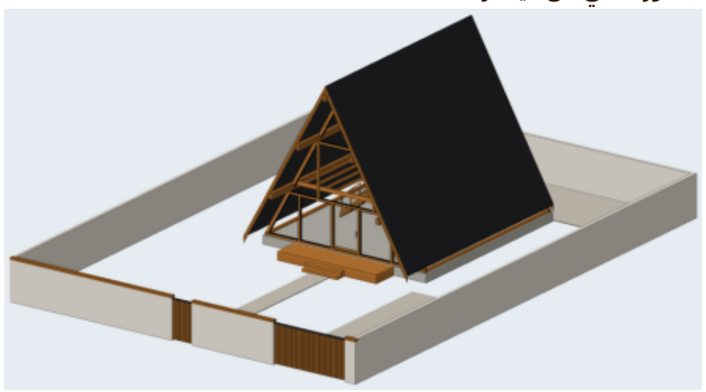


منظور أمامي من اليمين

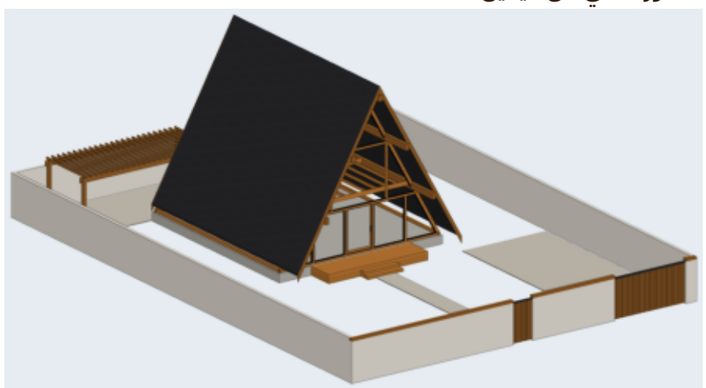


المنظور الخلفي

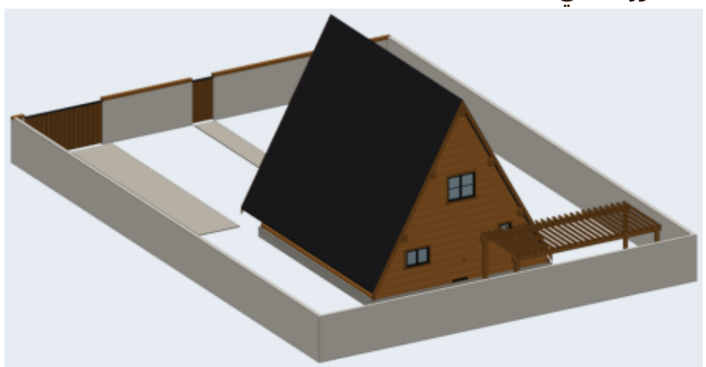

منظور خلفي من اليمين

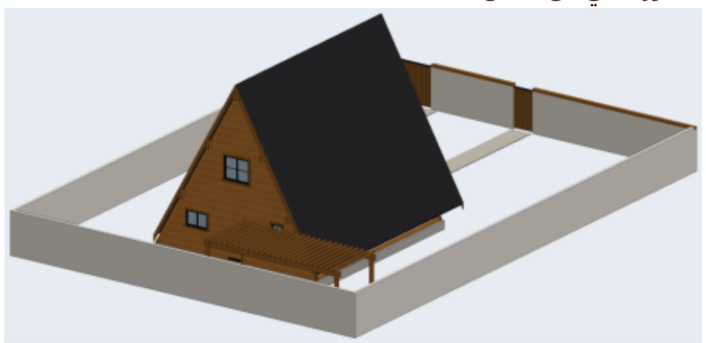

منظر علوي

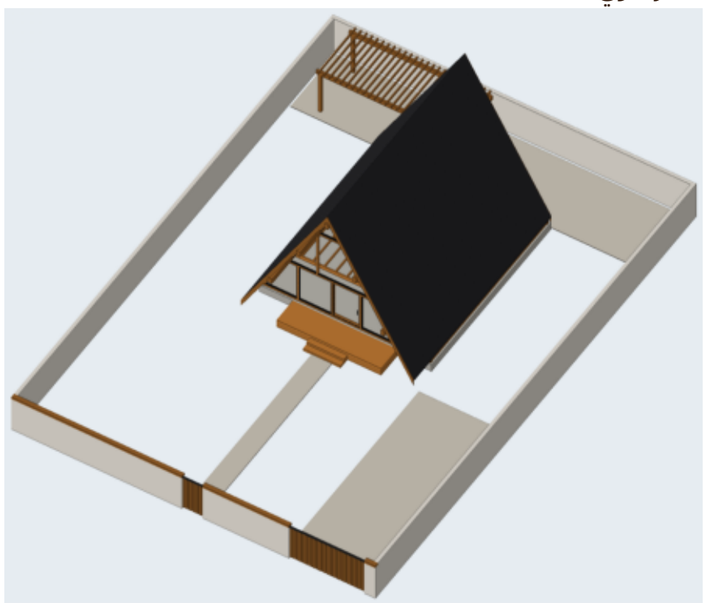


| المشروع / العميل | عنوان اللوحة | المقياس | التاريخ | رقم اللوحة |
|---|---|---|---|---|
| **كوخ A-frame دورين – صالة ومطبخ أمريكي وحمامين + غرفتين وحمام – 9.00 × 10.00 م**<br>**عميل – A-frame دورين** | **لقطات المنظور** | **–** | **2026-10-24** | **A-09 (9/11)** |

**مصنع وتد الأخشاب**
Watad Wood Factory

# المقطع العلوي بالفرش

مقطع أفقي على ارتفاع 1.90 م — توزيع الفرش ومسار الحركة

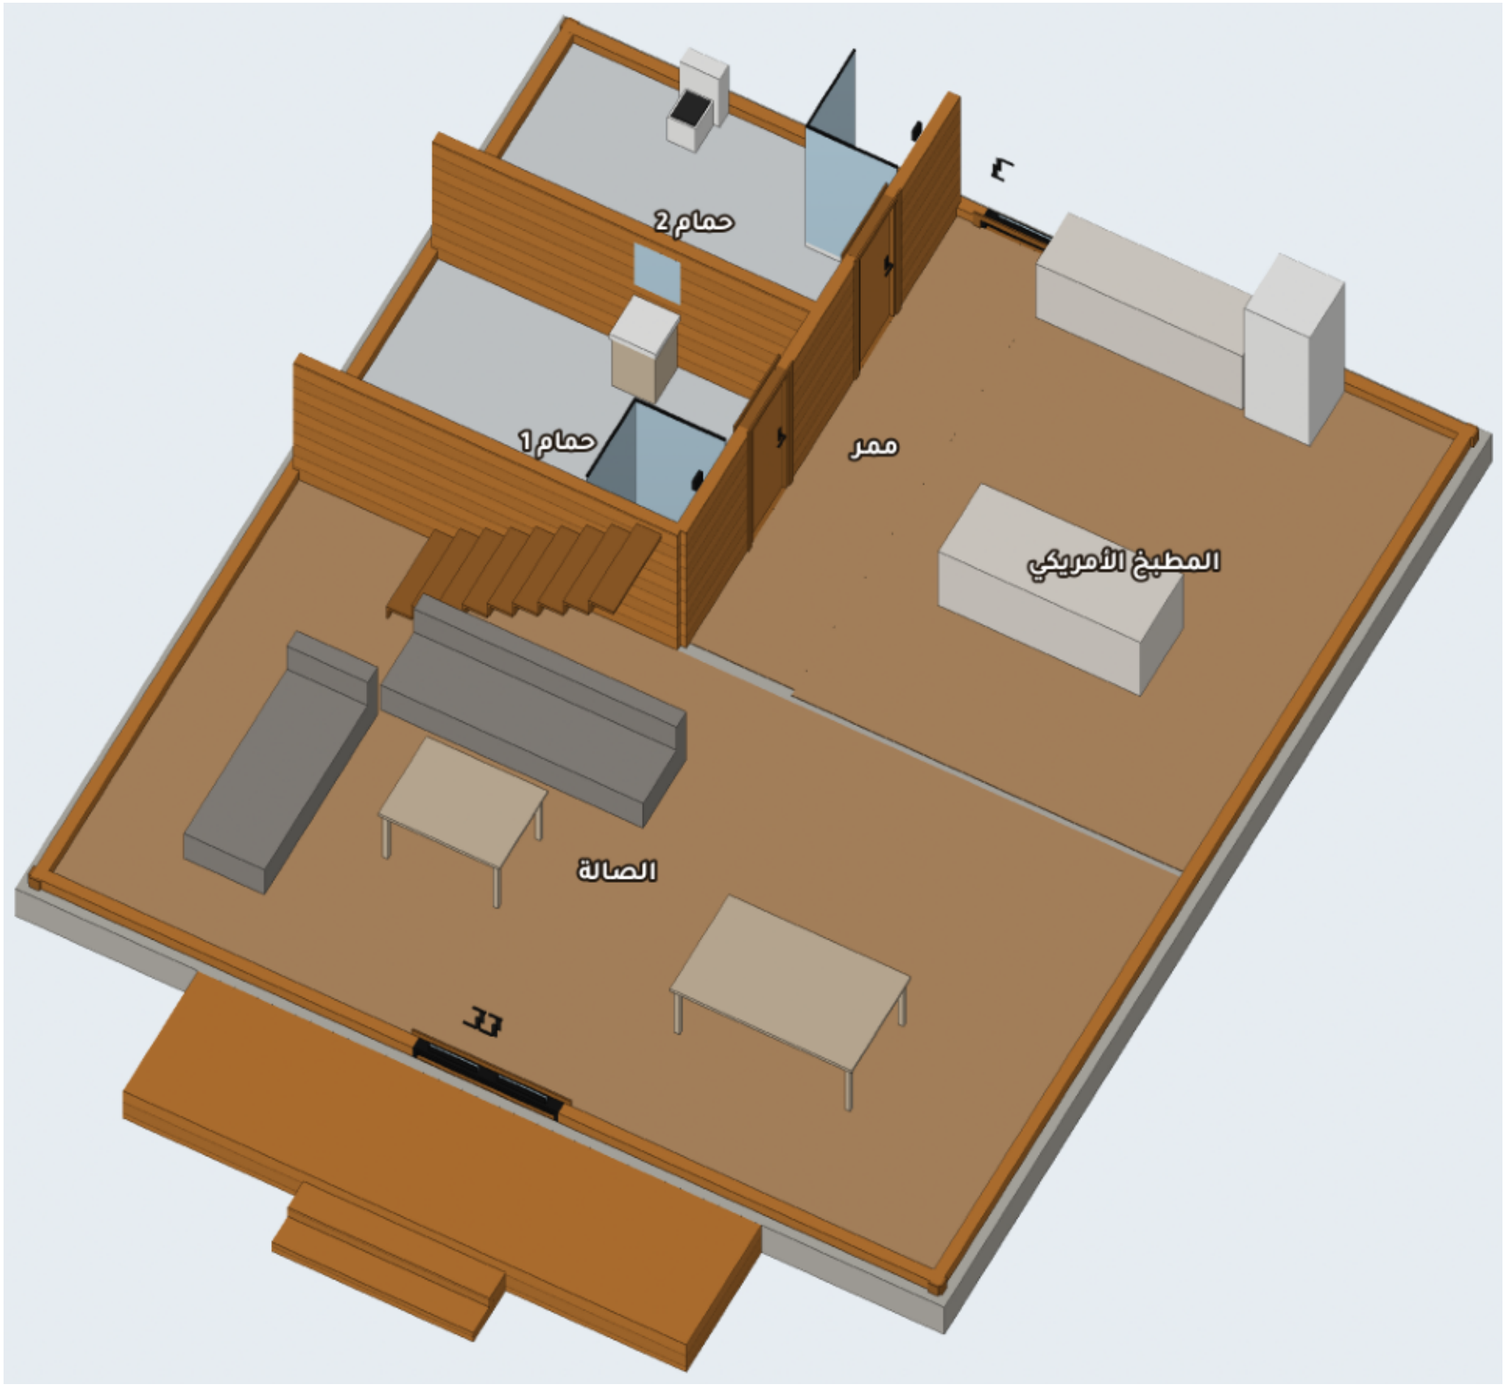



| المشروع / العميل | عنوان اللوحة | المقياس | التاريخ | رقم اللوحة |
|---|---|---|---|---|
| **كوخ A-frame دورين — صالة ومطبخ أمريكي وحمامين + غرفتين وحمام — 9.00 × 10.00 م**<br>**عميل — A-frame دورين** | **المقطع العلوي بالفرش** | **—** | **2026-10-24** | **A-10 (10/11)** |

مصنع وتد الأخشاب
Watad Wood Factory

# المنظور ثلاثي الأبعاد والمواد

النمط: جوزي غامق + إطارات سوداء — رندر واقعي بخامات حقيقية

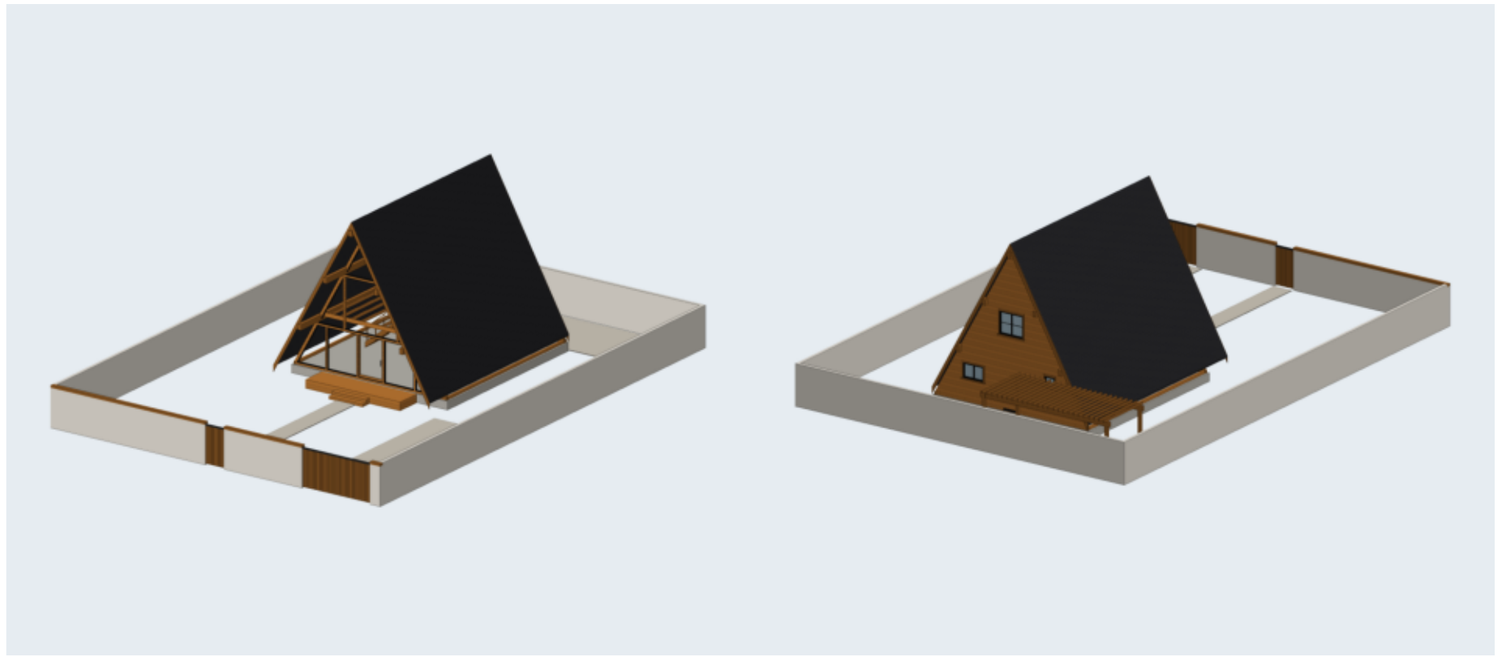

## جدول المواد والألوان

**الخشب / الصبغة**

صبغة عسلي / سيدر

**القرميد**

قرميد رمادي غامق

**الزجاج**

زجاج شفاف

**إطارات الشبابيك والأبواب**

إطار ألمنيوم أسود

**الكنار والزوايا**

نفس الصبغة أغمق درجة


**الصبة**

خرسانة 45 سم


الدربزين: ألواح أفقية متقاربة (عصري)

تقسيم الشبابيك: بدون | الباب الرئيسي: زجاج بتقسيمات (فرنسي)

## أنواع الدربزين المعتمدة (من مشاريع المصنع)

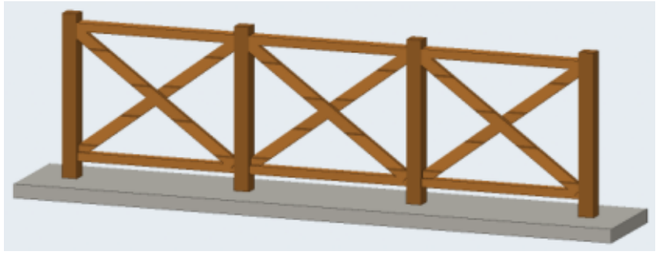

تقاطع X (صورة 5)

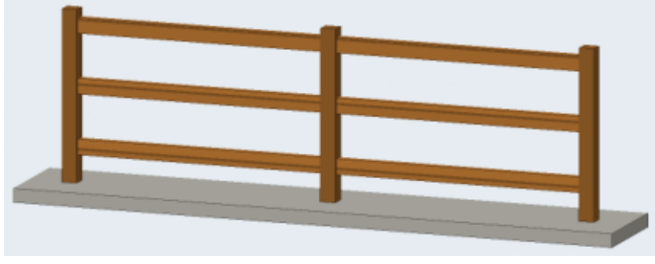

3 مرابيع أفقية (صورة 2)



قوائم رأسية متقاربة (صورة 1)

| المشروع / العميل | عنوان اللوحة | المقياس | التاريخ | رقم اللوحة |
|---|---|---|---|---|
| **كوخ A-frame دورين — صالة ومطبخ أمريكي وحمامين + غرفتين وحمام — 9.00 × 10.00 م**<br>**عميل — A-frame دورين** | **المنظور والمواد** | **—** | **2026-10-24** | **A-11 (11/11)** |

**مصنع وتد الأخشاب**
Watad Wood Factory