

# المسقط الأفقي مع الفرش
## الأبعاد بالسنتيمتر - الجدران: قوائم 5×7 + تلبيس 2.5 من الجهتين (12 سم)

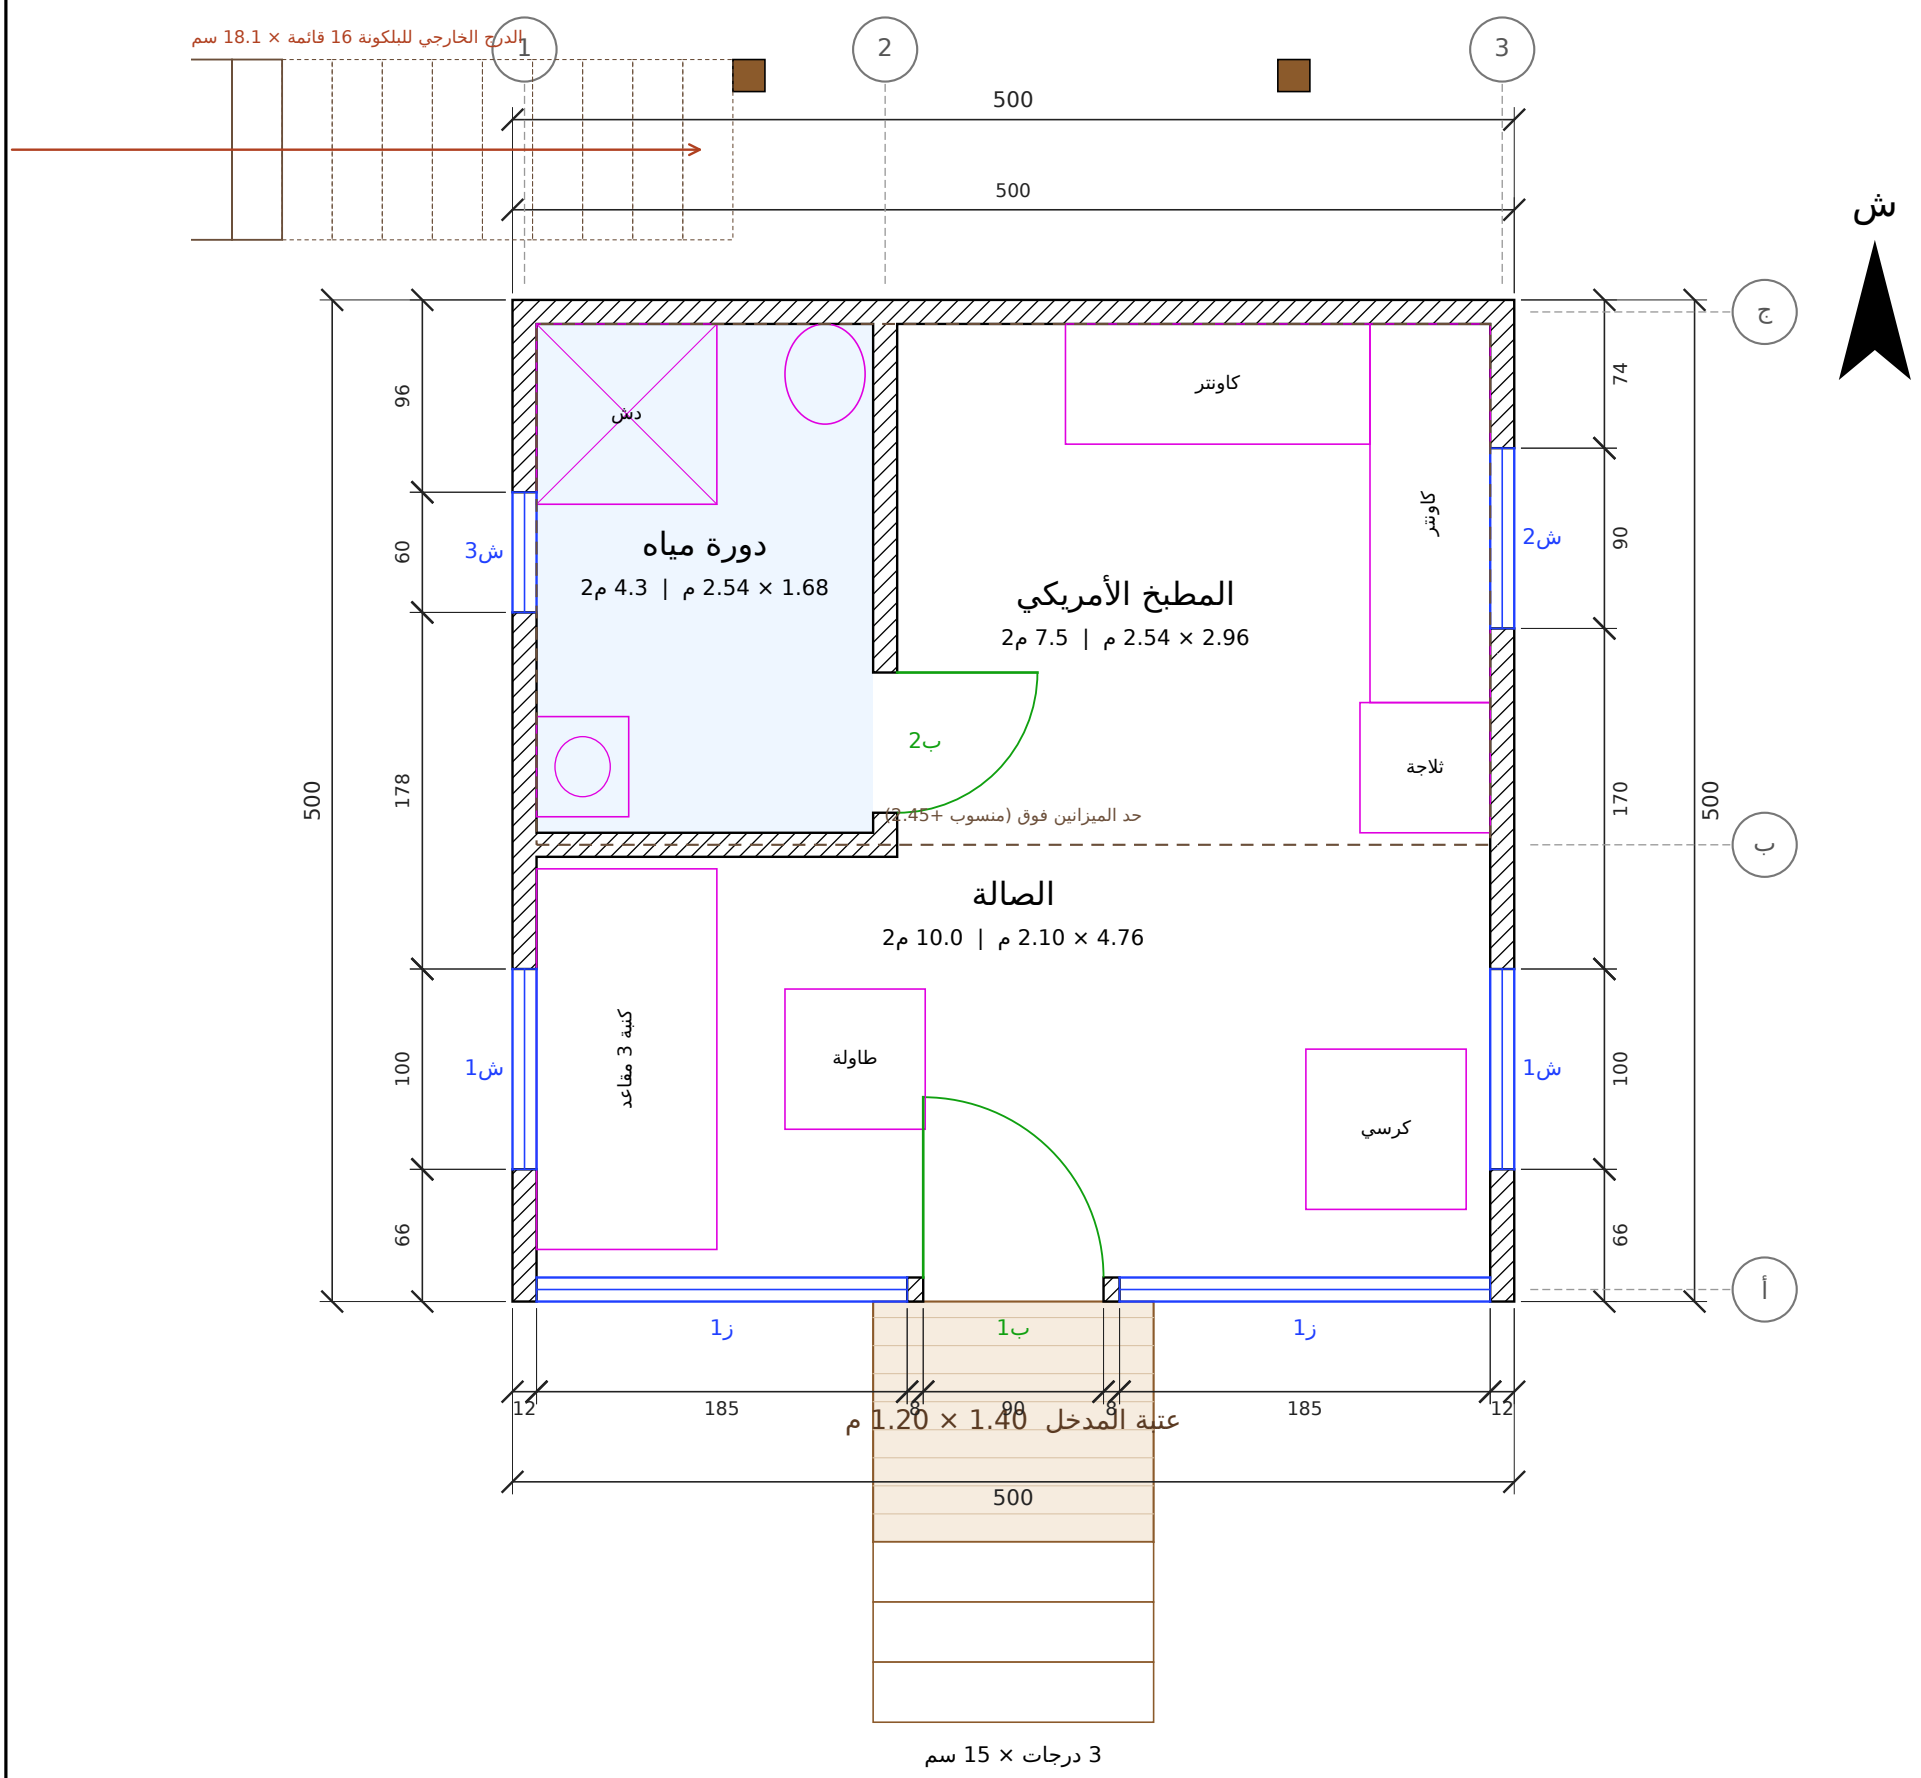



| | | | | | |
|---|---|---|---|---|---|
| **مصنع وتد الأخشاب**<br>Watad Wood Factory | المشروع / العميل<br>**كوخ A-frame بواجهة زجاج + ميزانين — 25 م²**<br>**عميل — الهدا** | عنوان اللوحة<br>**المسقط الأفقي** | المقياس<br>**1:50** | التاريخ<br>**2026-10-18** | رقم اللوحة<br>**A-01 (1/10)** |

# مسقط الميزانين (نص الدور) — غرفة النوم
## منسوب أرضية الميزانين +2.45  |  الأبعاد بالسنتيمتر

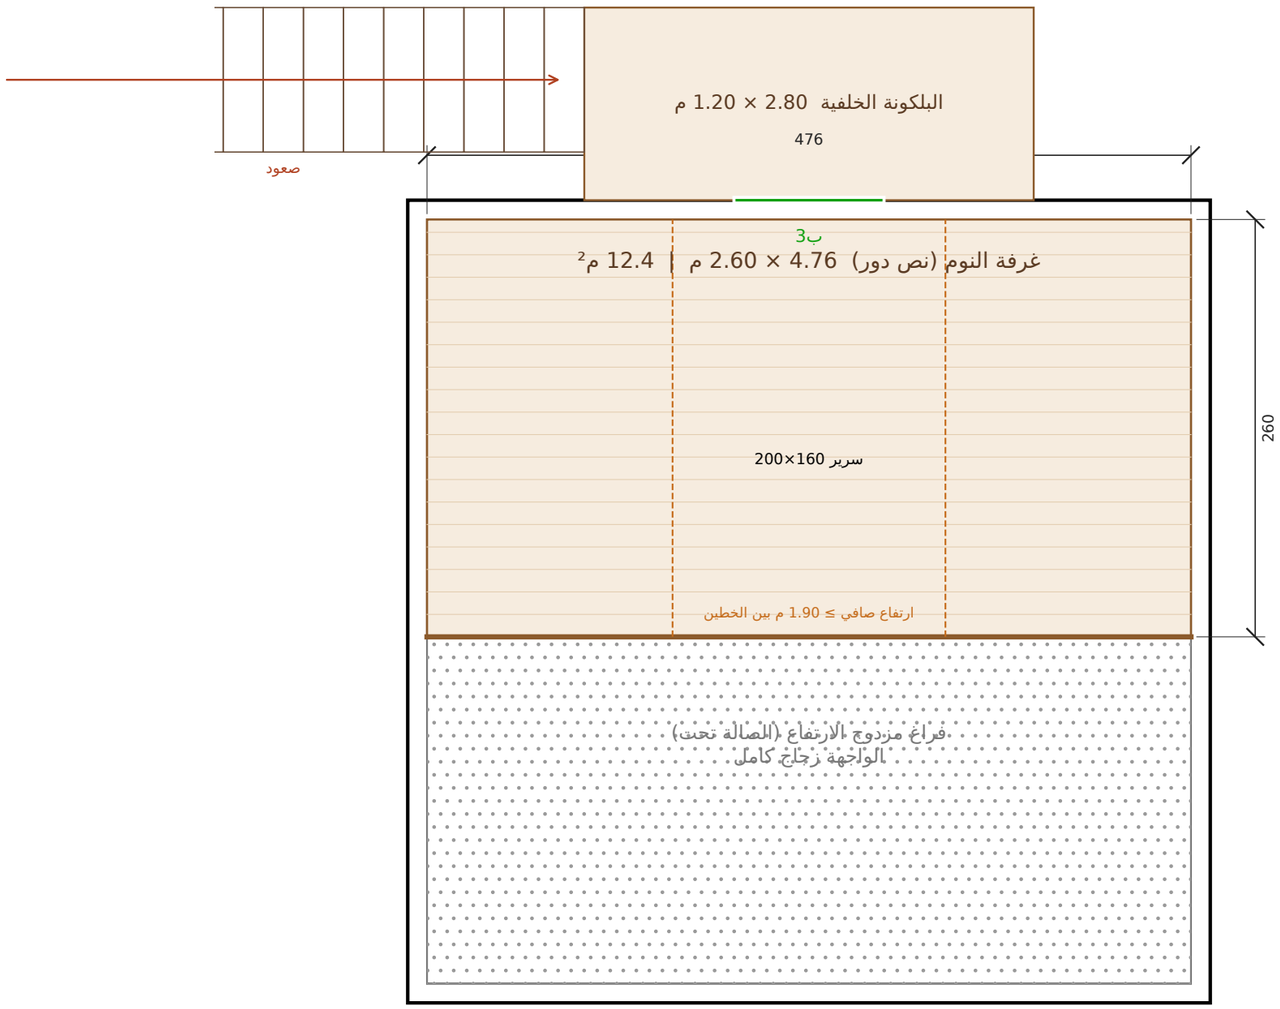



| المشروع / العميل | عنوان اللوحة | المقياس | التاريخ | رقم اللوحة |
|---|---|---|---|---|
| **كوخ A-frame بواجهة زجاج + ميزانين — 25 م²**<br>**عميل — الهدا** | **مسقط الميزانين** | **1:50** | **2026-10-18** | **A-02  (2/10)** |

**مصنع وتد الأخشاب**
Watad Wood Factory

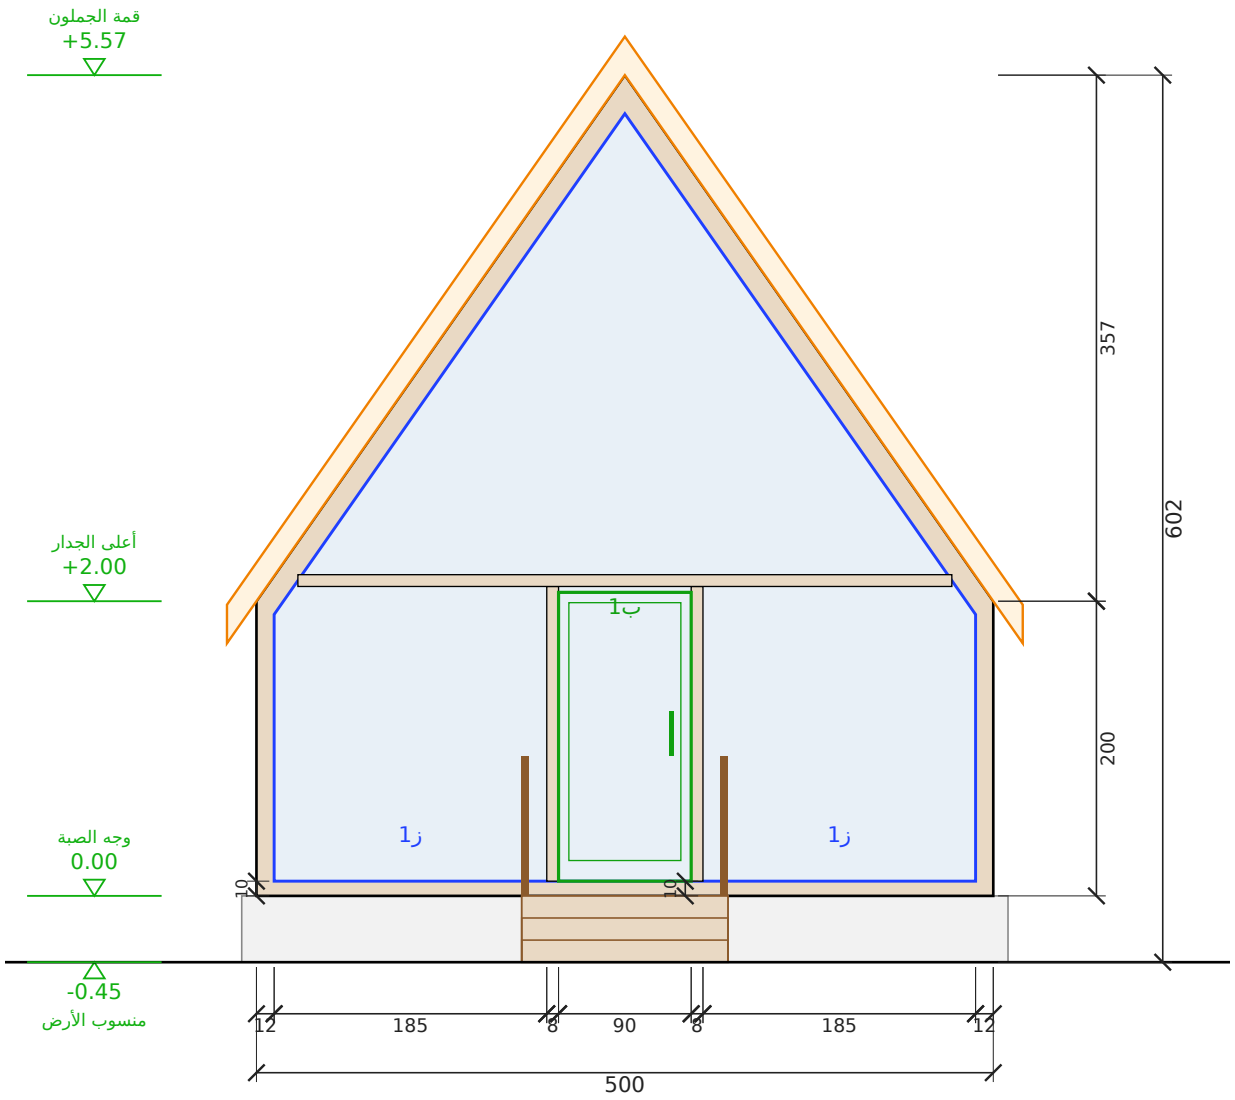


## الواجهة الأمامية

مقياس 1:50 | الوحدة: سم

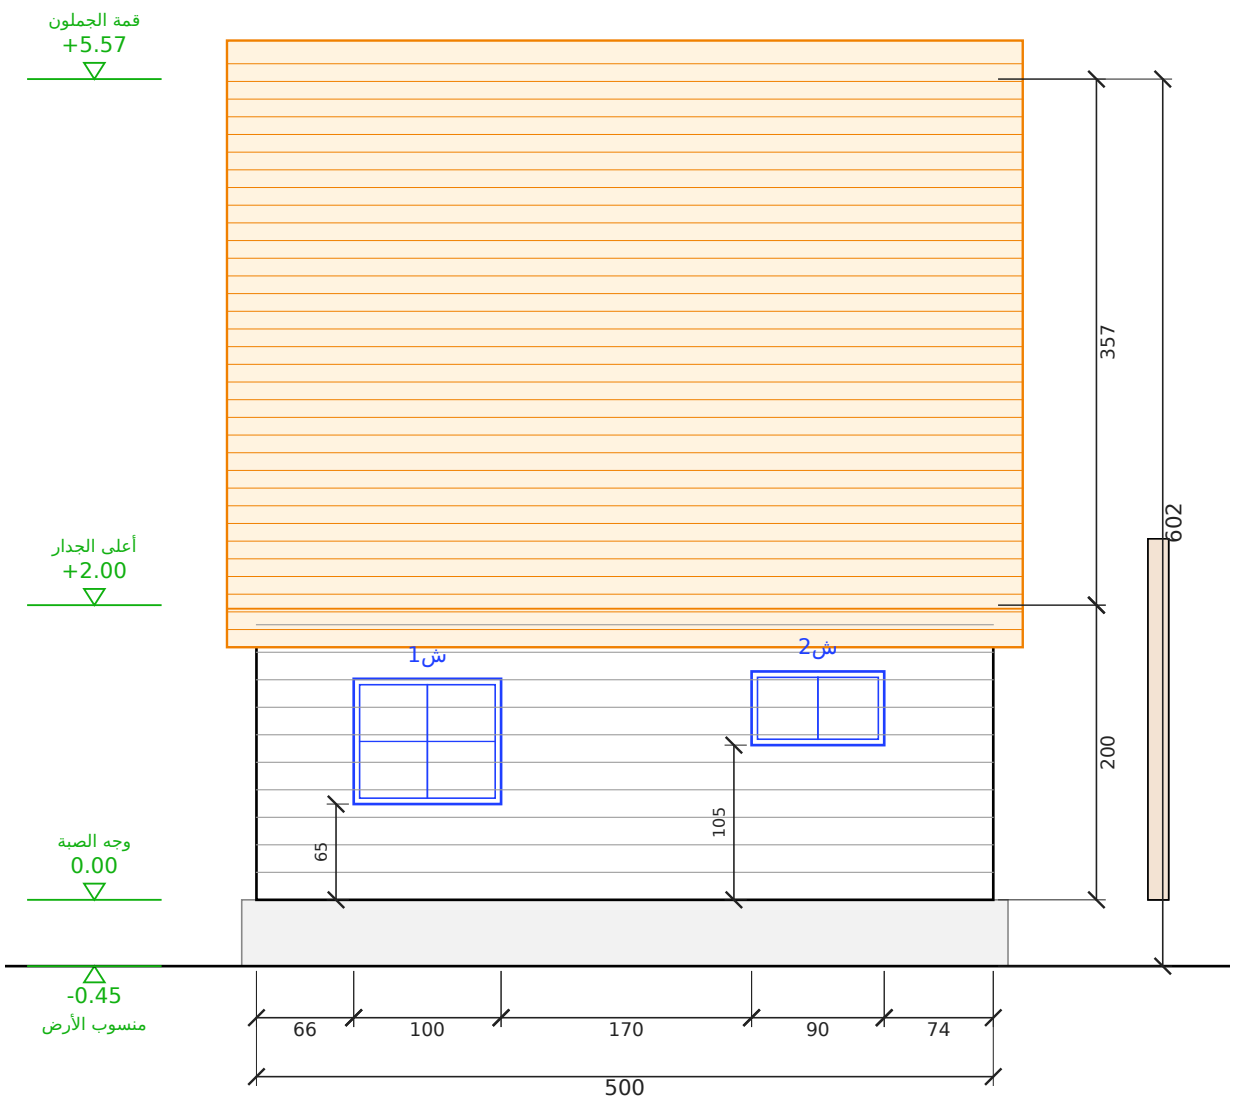



## الواجهة الشرقية

مقياس 1:50 | الوحدة: سم


| المشروع / العميل | عنوان اللوحة | المقياس | التاريخ | رقم اللوحة |
|---|---|---|---|---|
| **كوخ A-frame بواجهة زجاج + ميزانين — 25 م²**<br>**عميل — الهدا** | **الواجهة الأمامية والواجهة الشرقية** | **1:50** | **2026-10-18** | **A-03 (3/10)** |

**مصنع وتد الأخشاب**
Watad Wood Factory

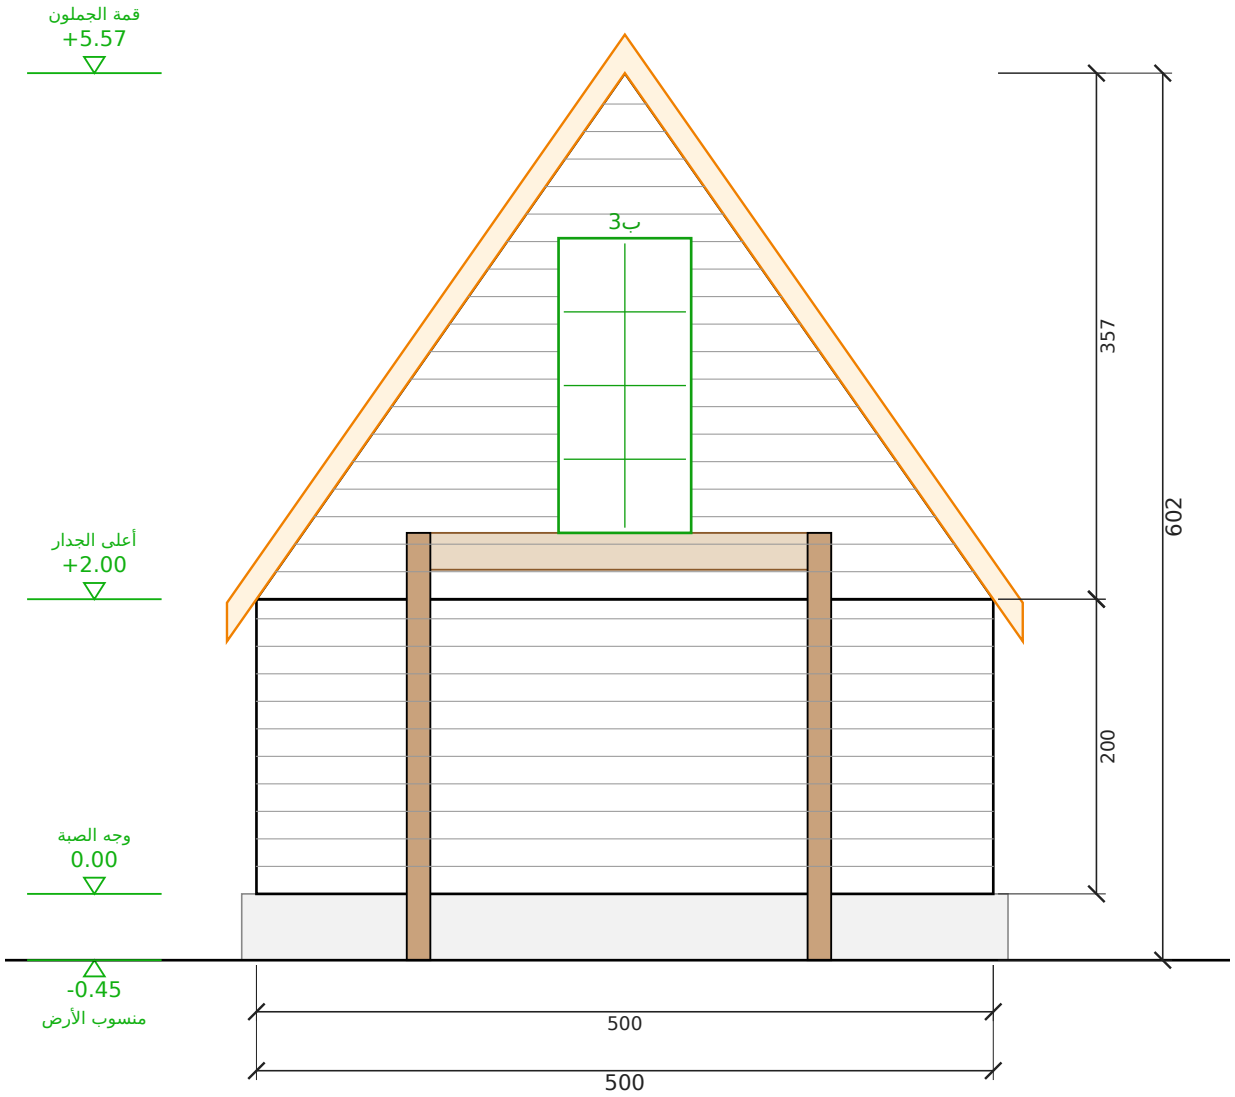


## الواجهة الخلفية

مقياس 1:50 | الوحدة: سم

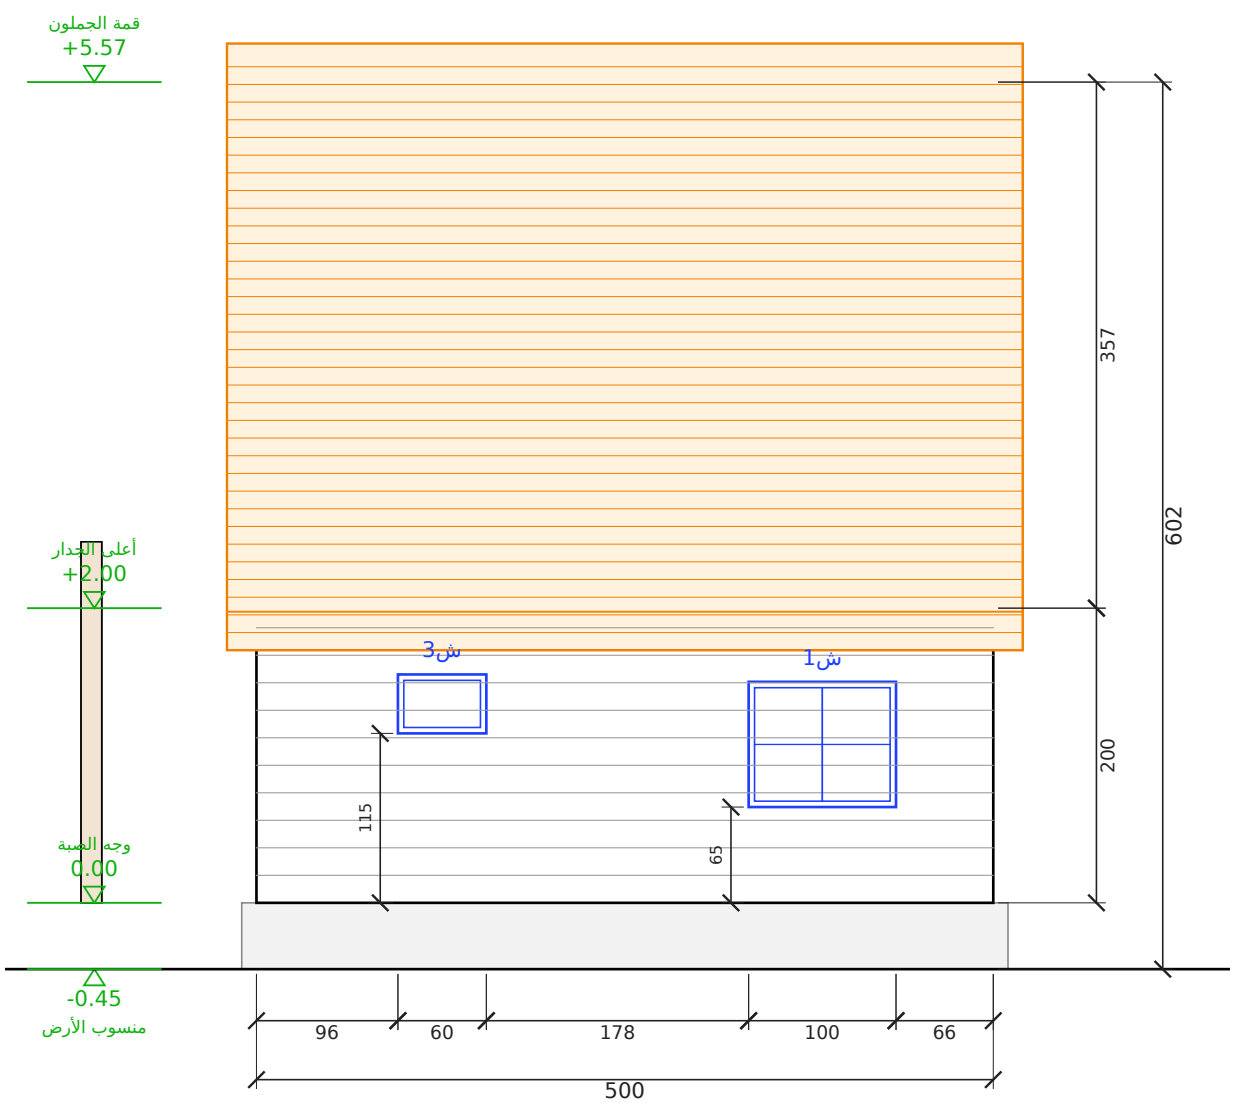



## الواجهة الغربية

مقياس 1:50 | الوحدة: سم


| المشروع / العميل | عنوان اللوحة | المقياس | التاريخ | رقم اللوحة |
|---|---|---|---|---|
| **كوخ A-frame بواجهة زجاج + ميزانين — 25 م²**<br>**عميل — الهدا** | **الواجهة الخلفية والواجهة الغربية** | **1:50** | **2026-10-18** | **A-04 (4/10)** |

**مصنع وتد الأخشاب**
Watad Wood Factory


## مسقط السقف (جملون)
## رفرف 20 سم من كل جهة | مقياس 1:50

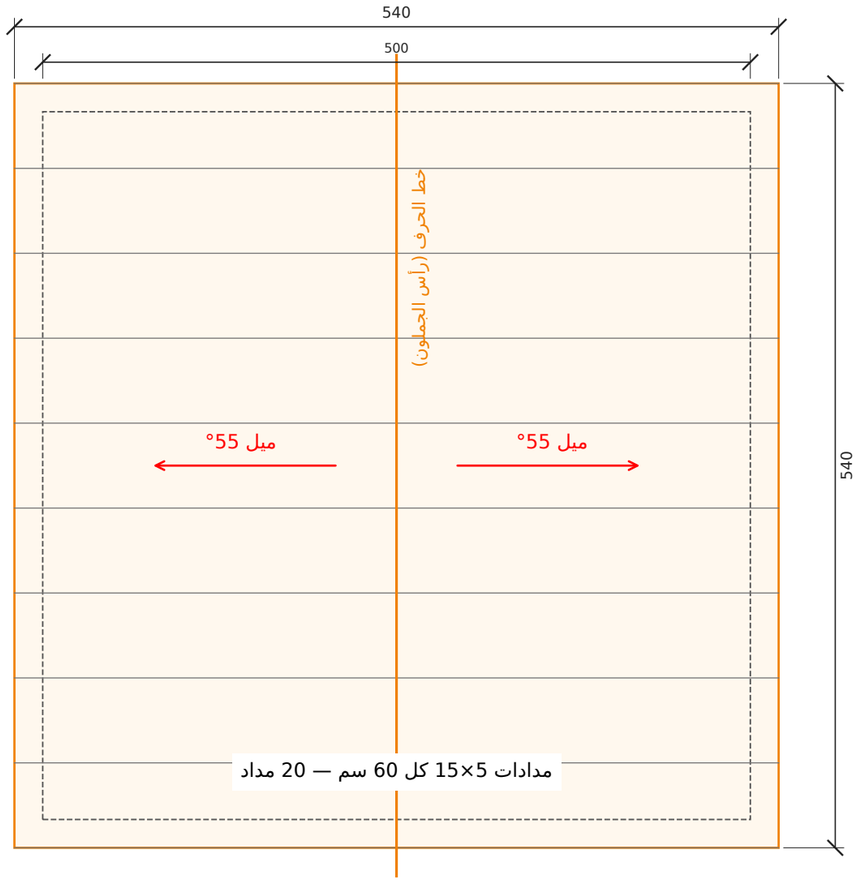


## قطاع عرضي أ-أ
## مقياس 1:50 | الوحدة: سم

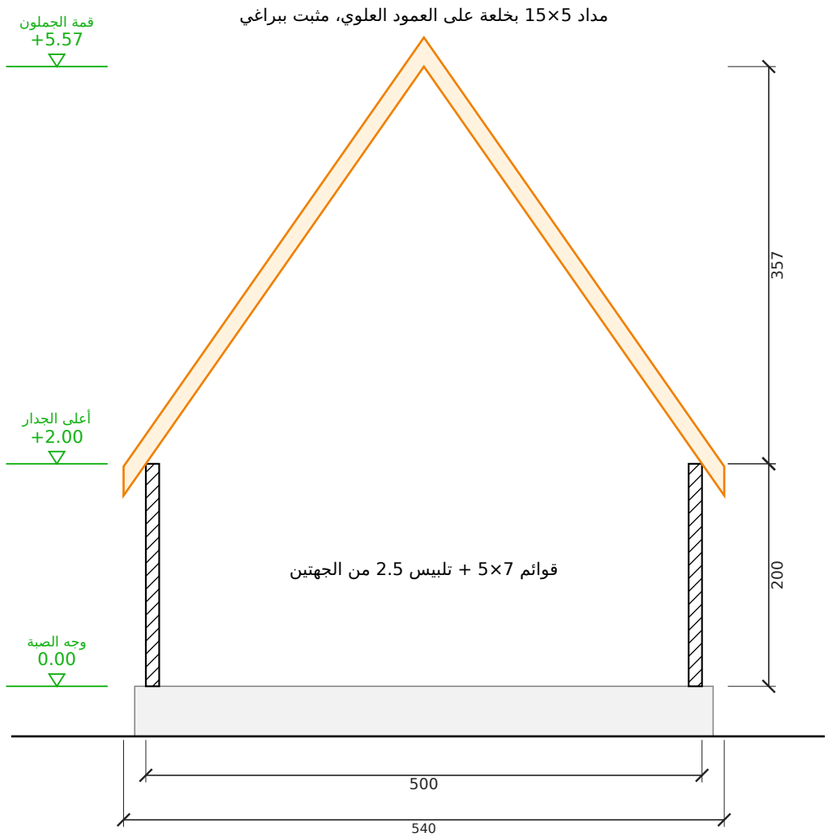


### تفصيلة جلوس المداد على العلوي (1:5)

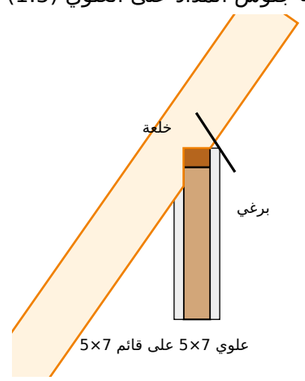


| المشروع / العميل | عنوان اللوحة | المقياس | التاريخ | رقم اللوحة |
|---|---|---|---|---|
| كوخ A-frame بواجهة زجاج + ميزانين — 25 م²<br>عميل — الهدا | مسقط السقف والقطاع | 1:50 | 2026-10-18 | A-05 (5/10) |

مصنع وتد الأخشاب
Watad Wood Factory

## جدول مقاسات الأبواب والشبابيك
### مقاس الفتحة الصافي في الجدار - الوحدة: سم

| الرمز | النوع | العرض (سم) | الارتفاع (سم) | ارتفاع الجلسة (سم) | العدد | الموقع |
|---|---|---|---|---|---|---|
| ب1 | باب | 90 | 210 | - | 1 | الأمامية |
| ب2 | باب | 70 | 205 | - | 1 | دورة المياه |
| ب3 | باب | 90 | 200 | - | 1 | الخلفية |
| ز1 | شباك | 185 | 200 | 10 | 2 | الأمامية 2 |
| ش1 | شباك | 100 | 85 | 65 | 2 | الشرقية - الغربية |
| ش2 | شباك | 90 | 50 | 105 | 1 | الشرقية |
| ش3 | شباك | 60 | 40 | 115 | 1 | الغربية |

الإجمالي: أبواب 3 - شبابيك 6

| المشروع / العميل | عنوان اللوحة | المقياس | التاريخ | رقم اللوحة |
|---|---|---|---|---|
| **كوخ A-frame بواجهة زجاج + ميزانين — 25 م²**<br>**عميل — الهدا** | **جدول الأبواب والشبابيك** | **—** | **2026-10-18** | **A-06 (6/10)** |

مصنع وتد الأخشاب
Watad Wood Factory

# جدول المساحات وبيانات المشروع

## بيانات المشروع


| البند | البيان |
|---|---|
| المشروع | كوخ A-frame بواجهة زجاج + ميزانين — 25 م² |
| العميل | عميل — الهدا |
| الموقع | الهدا |
| الاستخدام | استراحة / سكن |
| التاريخ | 2026-10-18 |
| نظام البناء | هيكل خشب 5×7 + تلبيس 2.5 سم من الجهتين |
| السقف | جملون 55° — قرميد معدني |

## جدول المساحات

| م | الفراغ | الأبعاد (م) | المساحة (م2) |
|---|---|---|---|
| 1 | الصالة | 4.76 × 2.10 | 10.00 |
| 2 | المطبخ الأمريكي | 2.96 × 2.54 | 7.52 |
| 3 | دورة مياه | 1.68 × 2.54 | 4.27 |
| | **المساحة الصافية الداخلية** | | **21.78** |
| | **التراس المسقوف + تراس الدور الأول** | **1.40 × 1.20 × 2** | **5.04** |
| | **المساحة الإجمالية المبنية** | **5.00 × 5.00** | **25.00** |

# لقطات المنظور الخارجي

المنظور الأمامي

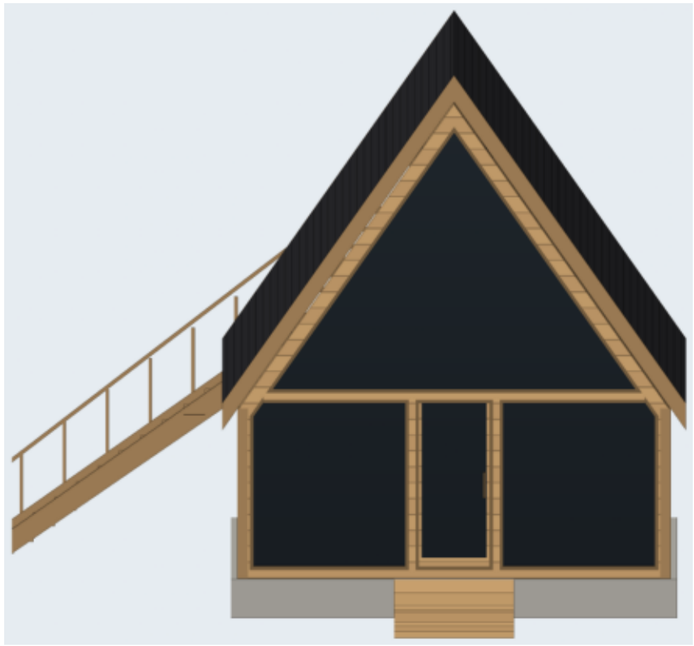

منظور أمامي من اليسار



منظور أمامي من اليمين



المنظور الخلفي



منظور خلفي من اليمين



منظر علوي




| المشروع / العميل | عنوان اللوحة | المقياس | التاريخ | رقم اللوحة |
|---|---|---|---|---|
| **كوخ A-frame بواجهة زجاج + ميزانين — 25 م²**<br>**عميل — الهدا** | **لقطات المنظور** | **—** | **2026-10-18** | **A-08 (8/10)** |

**مصنع وتد الأخشاب**
Watad Wood Factory

# المقطع العلوي بالفرش

مقطع أفقي على ارتفاع 1.90 م — توزيع الفرش ومسار الحركة

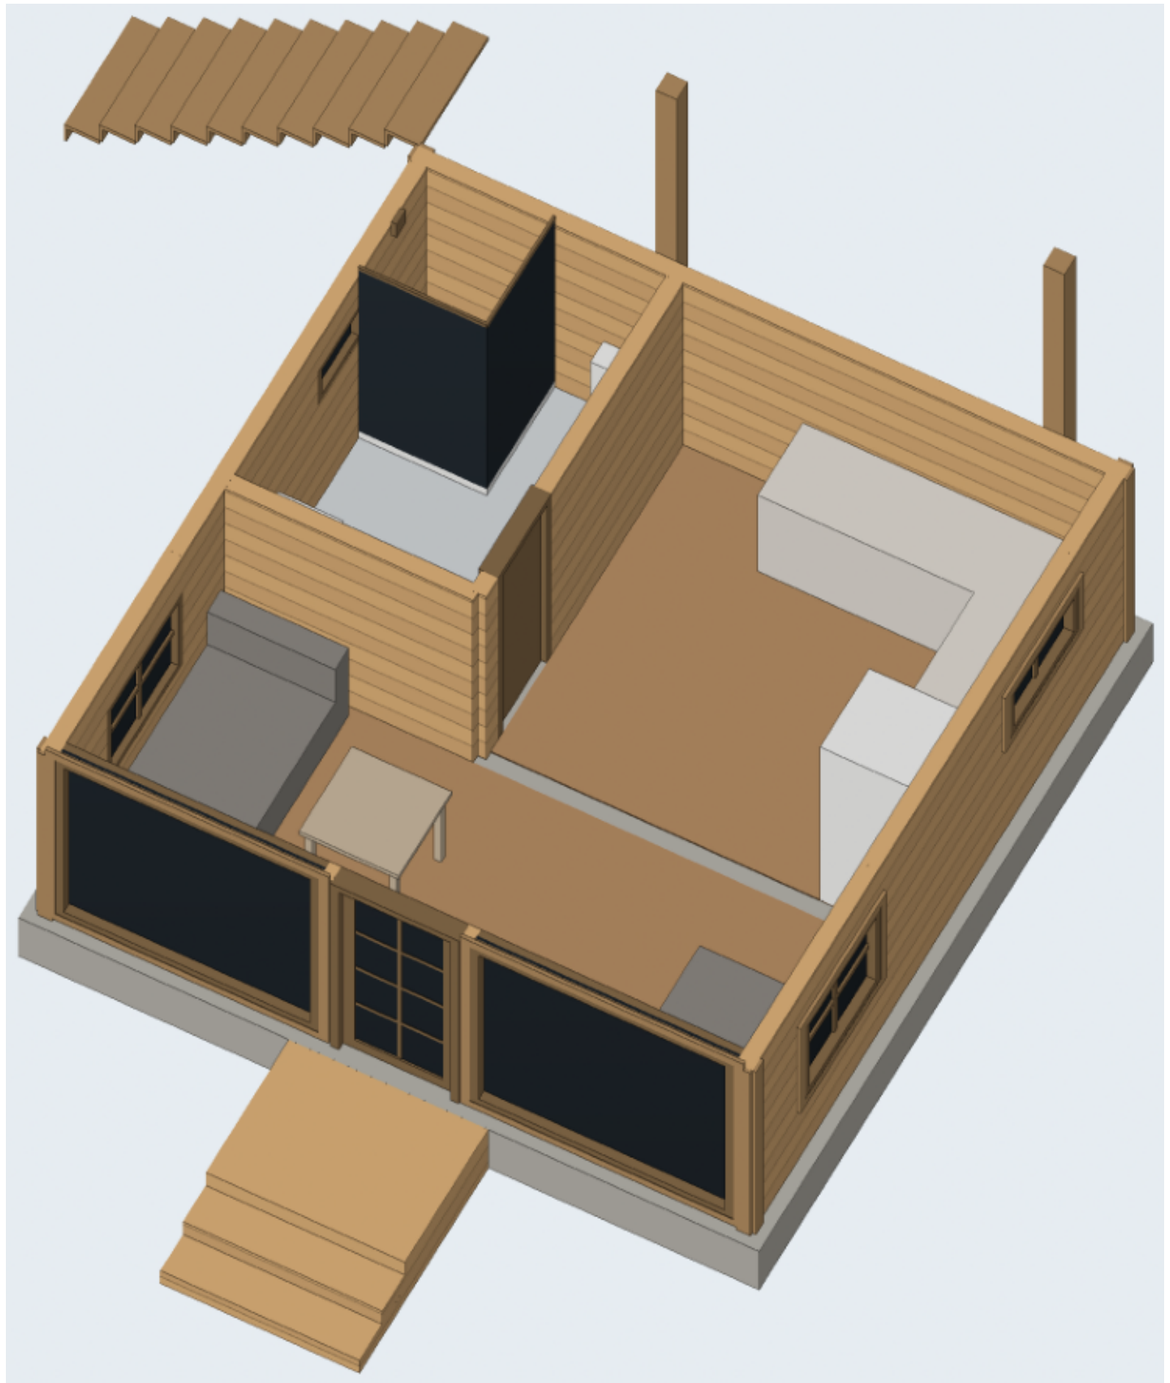


| المشروع / العميل | عنوان اللوحة | المقياس | التاريخ | رقم اللوحة |
|---|---|---|---|---|
| **كوخ A-frame بواجهة زجاج + ميزانين — 25 م²**<br>**عميل — الهدا** | **المقطع العلوي بالفرش** | **—** | **2026-10-18** | **A-09 (9/10)** |

**مصنع وتد الأخشاب**
Watad Wood Factory

# المنظور ثلاثي الأبعاد والمواد

النمط: جوزي غامق + إطارات سوداء — رندر واقعي بخامات حقيقية

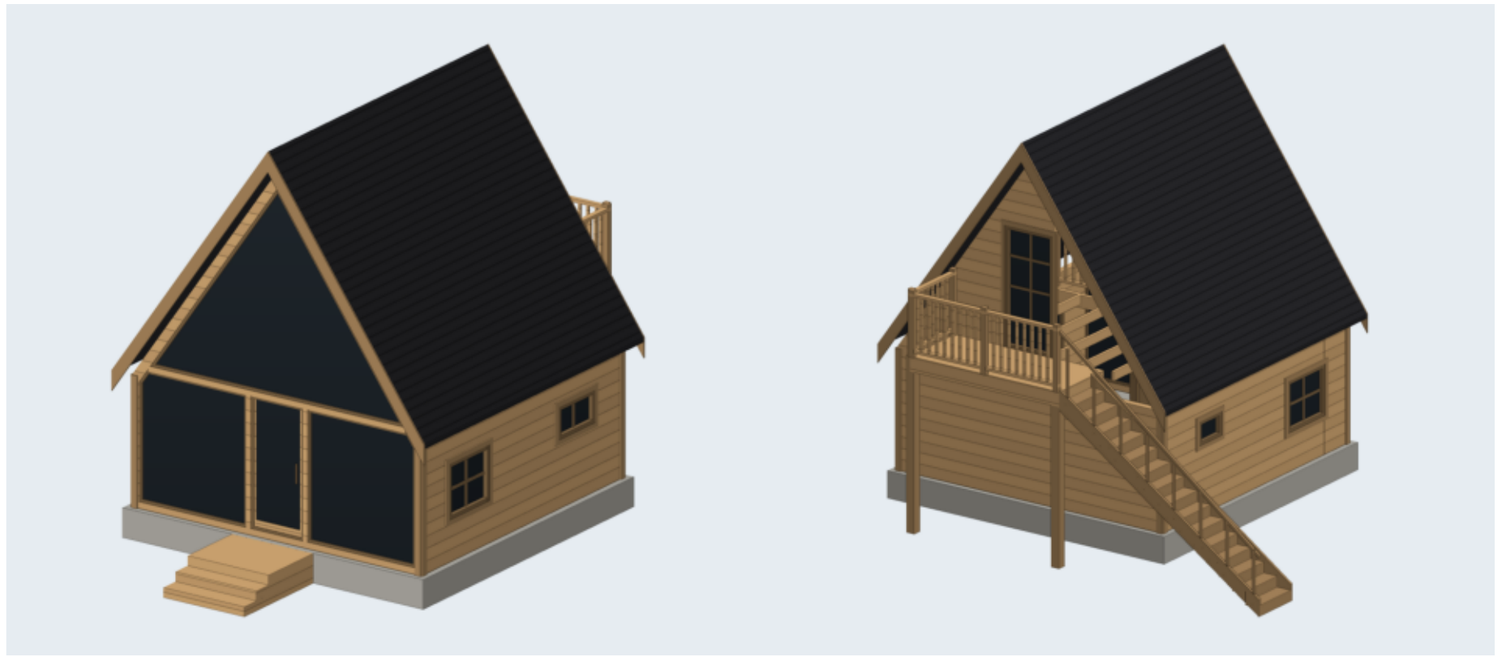

## جدول المواد والألوان

**الخشب / الصبغة**

خشب طبيعي فاتح (بدون صبغة)

**القرميد**

قرميد رمادي غامق

**الزجاج**

زجاج عاكس غامق

**إطارات الشبابيك والأبواب**

إطار خشب بنفس الصبغة أغمق

**الكنار والزوايا**

نفس الصبغة أغمق درجة


**الصبة**

خرسانة 45 سم


الدربزين: ألواح أفقية متقاربة (عصري)

تقسيم الشبابيك: بدون | الباب الرئيسي: زجاج بتقسيمات (فرنسي)

## أنواع الدربزين المعتمدة (من مشاريع المصنع)

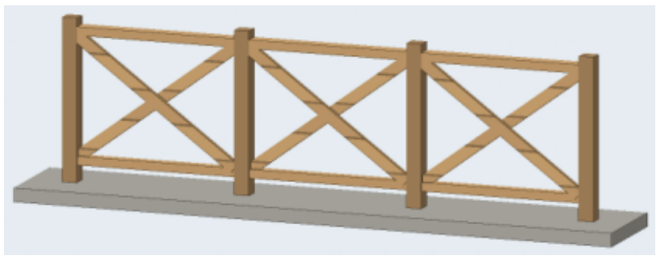

تقاطع X (صورة 5)

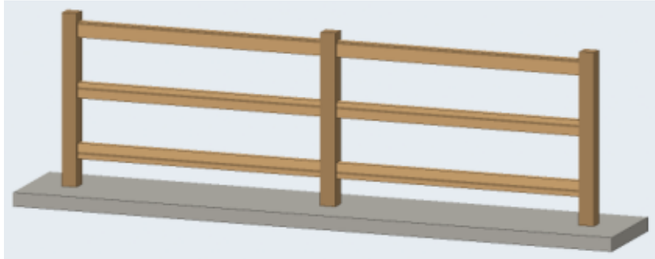

3 مرابيع أفقية (صورة 2)



قوائم رأسية متقاربة (صورة 1)

| المشروع / العميل | عنوان اللوحة | المقياس | التاريخ | رقم اللوحة |
|---|---|---|---|---|
| **كوخ A-frame بواجهة زجاج + ميزانين — 25 م²**<br>**عميل — الهدا** | **المنظور والمواد** | **—** | **2026-10-18** | **A-10 (10/10)** |

**مصنع وتد الأخشاب**
Watad Wood Factory