
المنظور ثلاثي الأبعاد والمواد

النمط: جوزي غامق + إطارات سوداء — رندر واقعي بخامات حقيقية

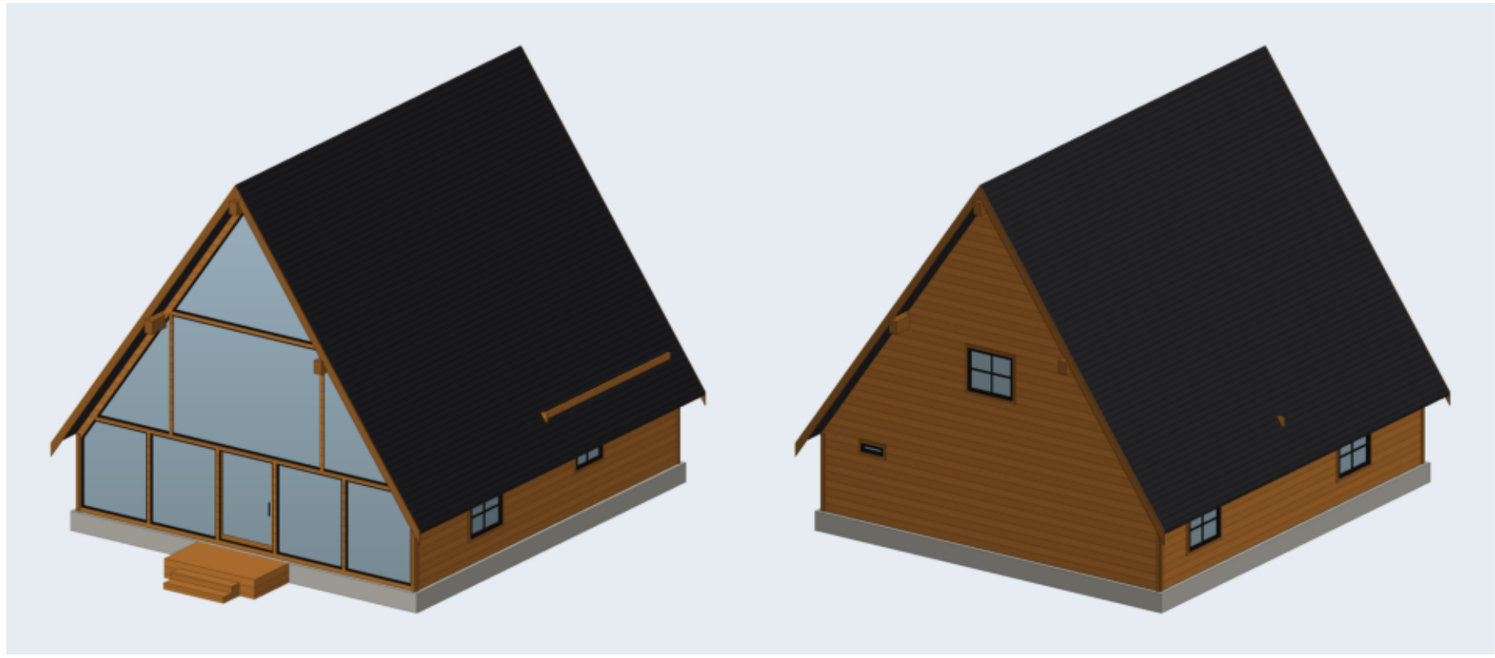

جدول المواد والألوان

الخشب / الصبغة

صبغة عسلي / سيدر

القرميد

قرميد رمادي غامق

الزجاج

زجاج شفاف

إطارات الشبابيك والأبواب

إطار ألمنيوم أسود

الكنار والزوايا

نفس الصبغة أغمق درجة


الصبة

خرسانة 45 سم


الدربزين: ألواح أفقية متقاربة (عصري)

تقسيم الشبابيك: بدون | الباب الرئيسي: زجاج بتقسيمات (فرنسي)

أنواع الدربزين المعتمدة (من مشاريع المصنع)

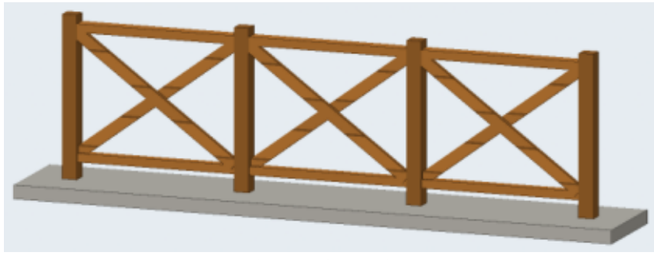

تقاطع X (صورة 5)

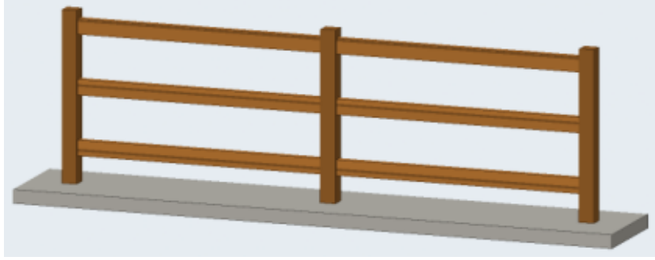

3 مرابيع أفقية (صورة 2)




قوائم رأسية متقاربة (صورة 1)


مصنع وتد الأخشاب Watad Wood Factory	المشروع / العميل كوخ A-frame بواجهة زجاج + ميزانين — صالة وغرفة ومطبخ أمريكي وحمام — 9.00 × 10.00 م عميل — A-frame 9×10	عنوان اللوحة المنظور والمواد	المقياس 1:50	التاريخ 2026-10-23	رقم اللوحة W-01 (1/13)

المسقط الأفقي مع الفرش

الأبعاد بالسنتيمتر - الجدران: قوائم 5×7 + تلبيس 2.5 من الجهتين (12 سم)

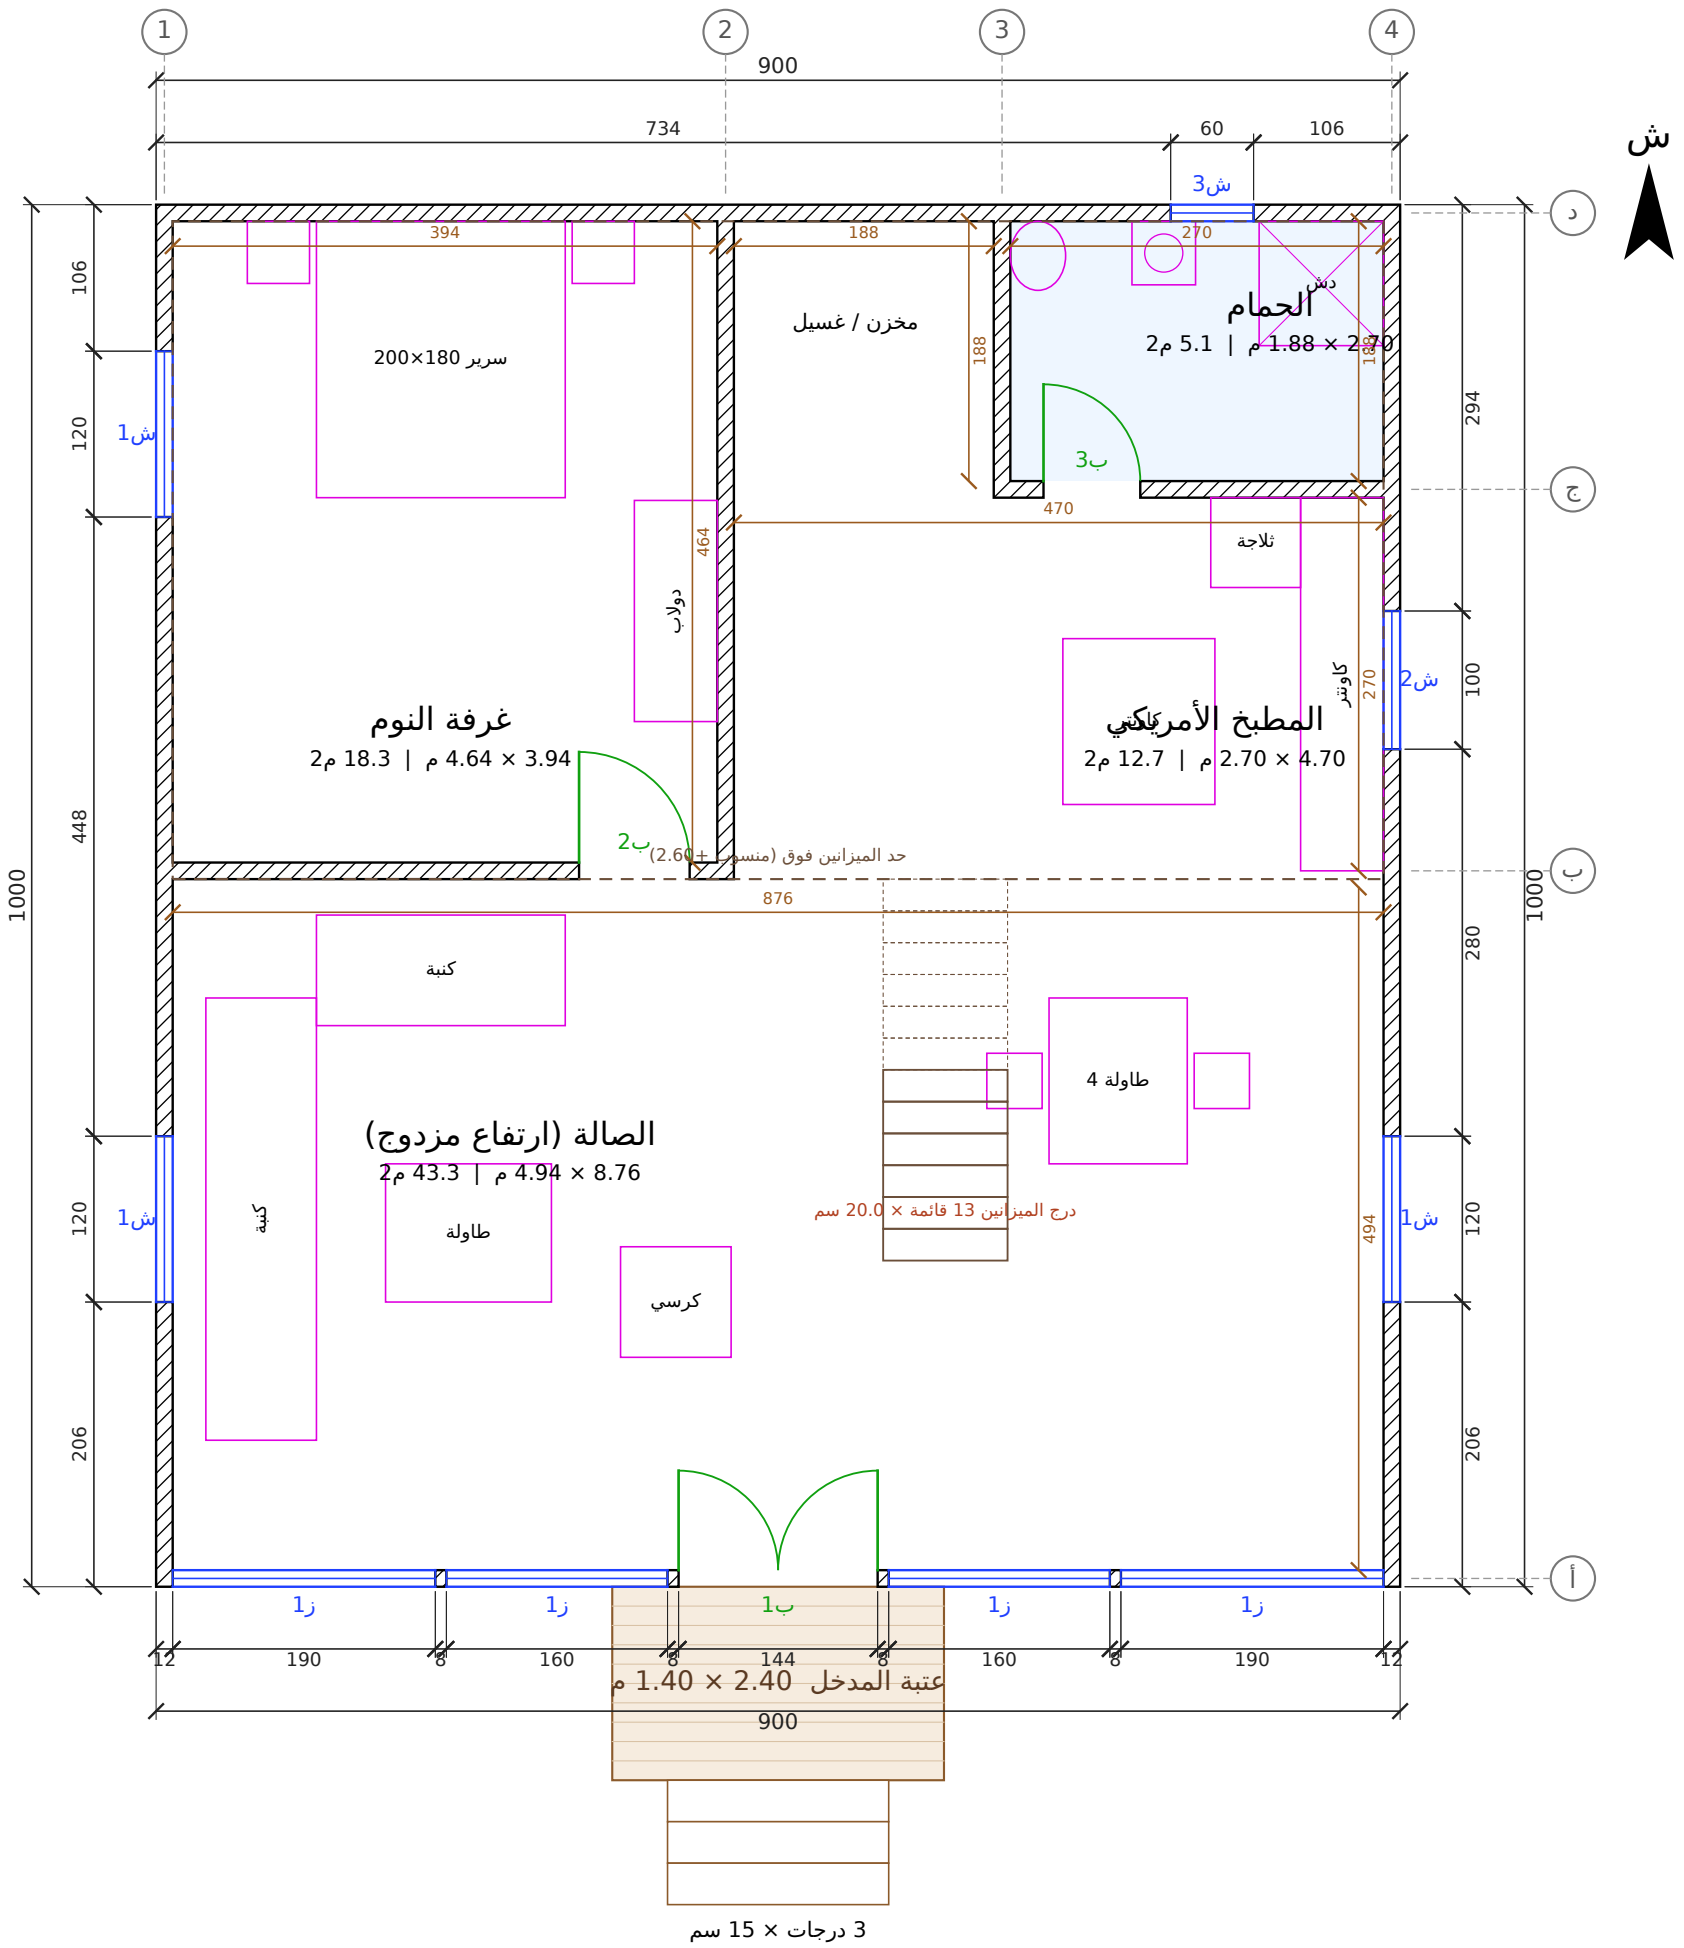


المشروع / العميل	عنوان اللوحة	المقياس	التاريخ	رقم اللوحة
مصنع وتد الأخشاب Watad Wood Factory **كوخ A-frame بواجهة زجاج + ميزانين — صالة وغرفة ومطبخ أمريكي وحمام — 9.00 × 10.00 م** **عميل — A-frame 9×10**	**المسقط الأفقي**	**1:50**	**2026-10-23**	**W-02 (2/13)**

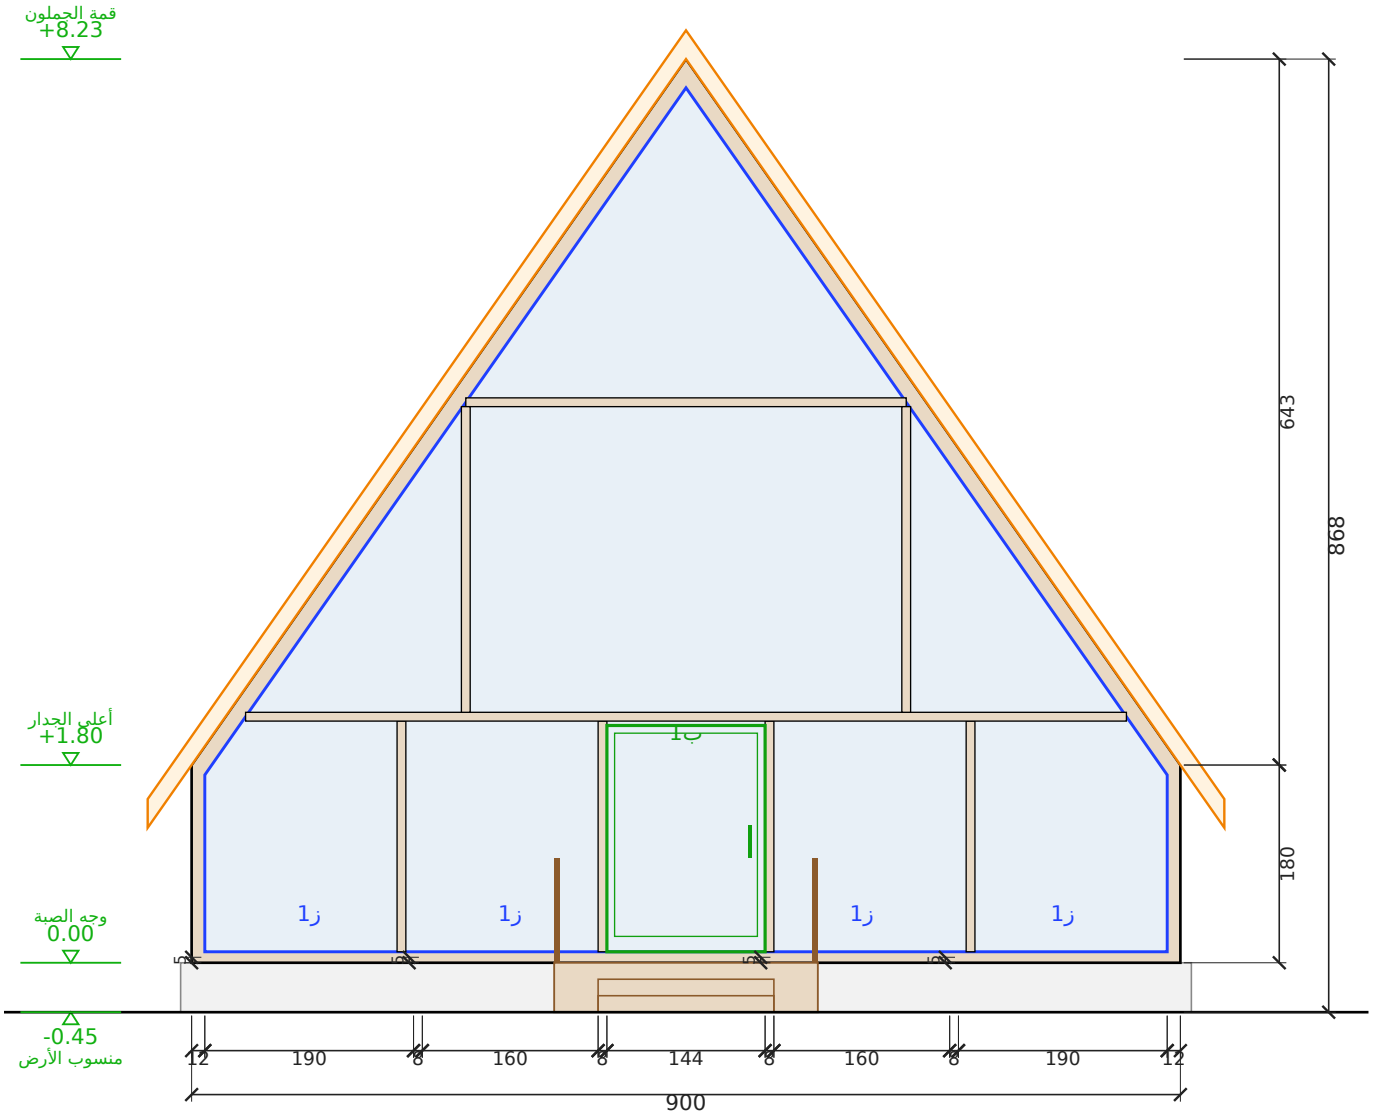

الواجهة الأمامية (زجاج كامل)

مقياس 1:50 | الوحدة: سم

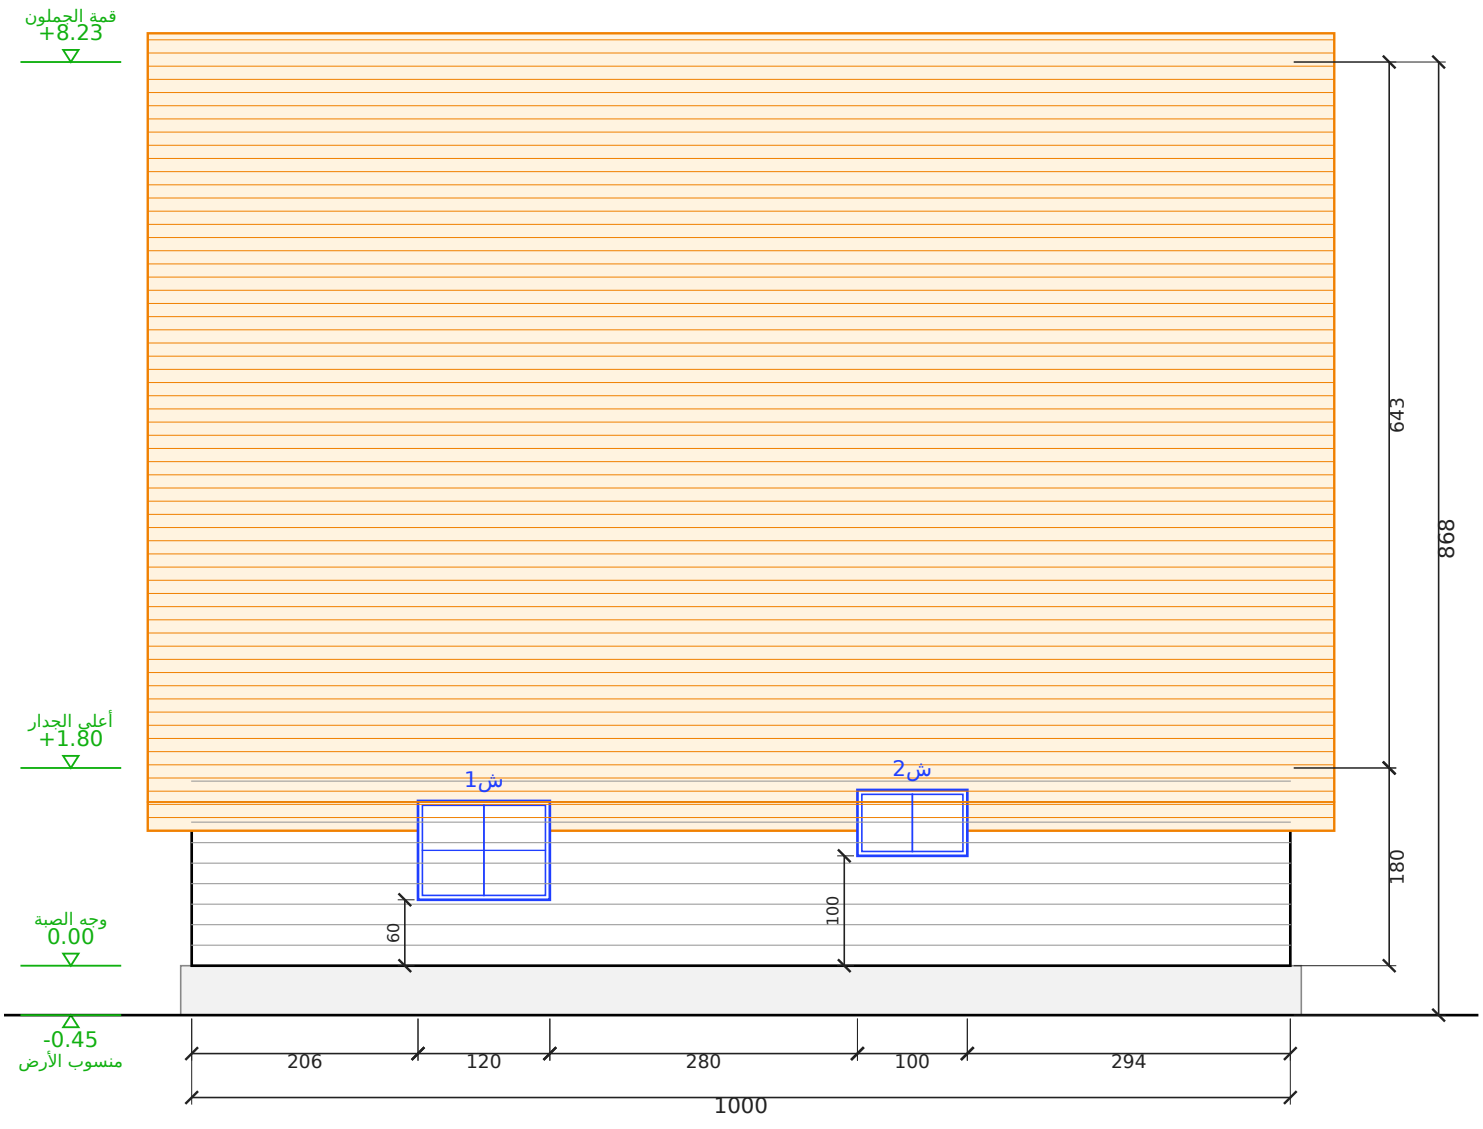


الواجهة الشرقية

مقياس 1:50 | الوحدة: سم


المشروع / العميل	عنوان اللوحة	المقياس	التاريخ	رقم اللوحة
كوخ A-frame بواجهة زجاج + ميزانين — صالة وغرفة ومطبخ أمريكي وحمام — 10.00 × 9.00 م **عميل — A-frame 9×10**	**الواجهة الأمامية (زجاج كامل) والواجهة الشرقية**	**1:50**	**2026-10-23**	**W-03 (3/13)**

مصنع وتد الأخشاب
Watad Wood Factory

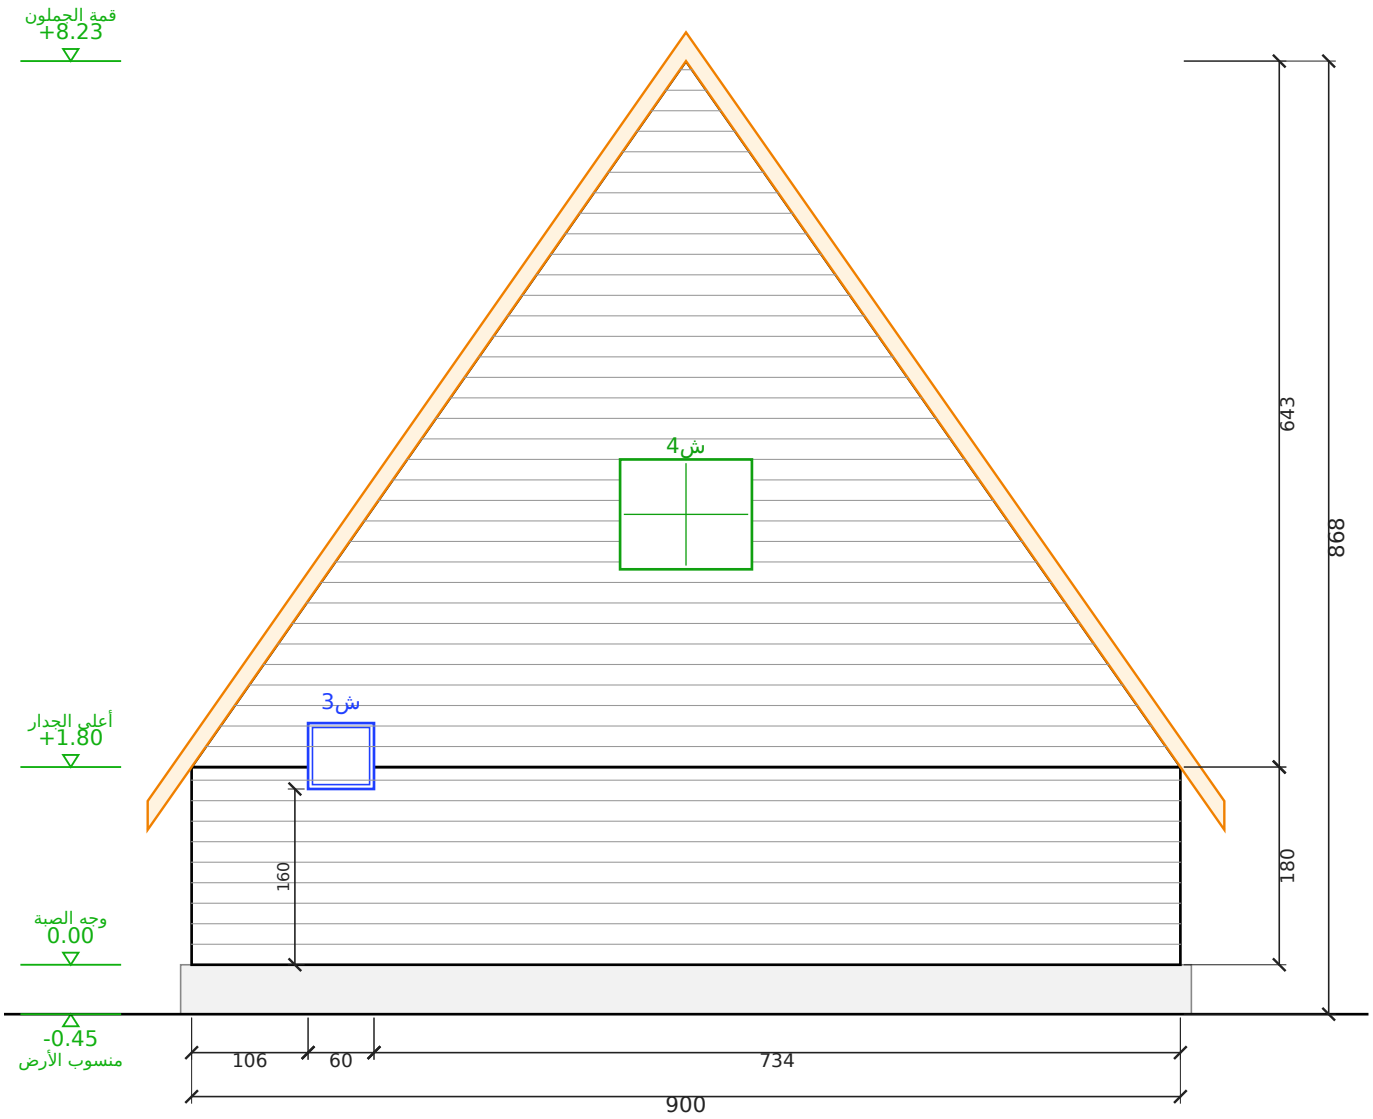

الواجهة الخلفية

مقياس 1:50 | الوحدة: سم

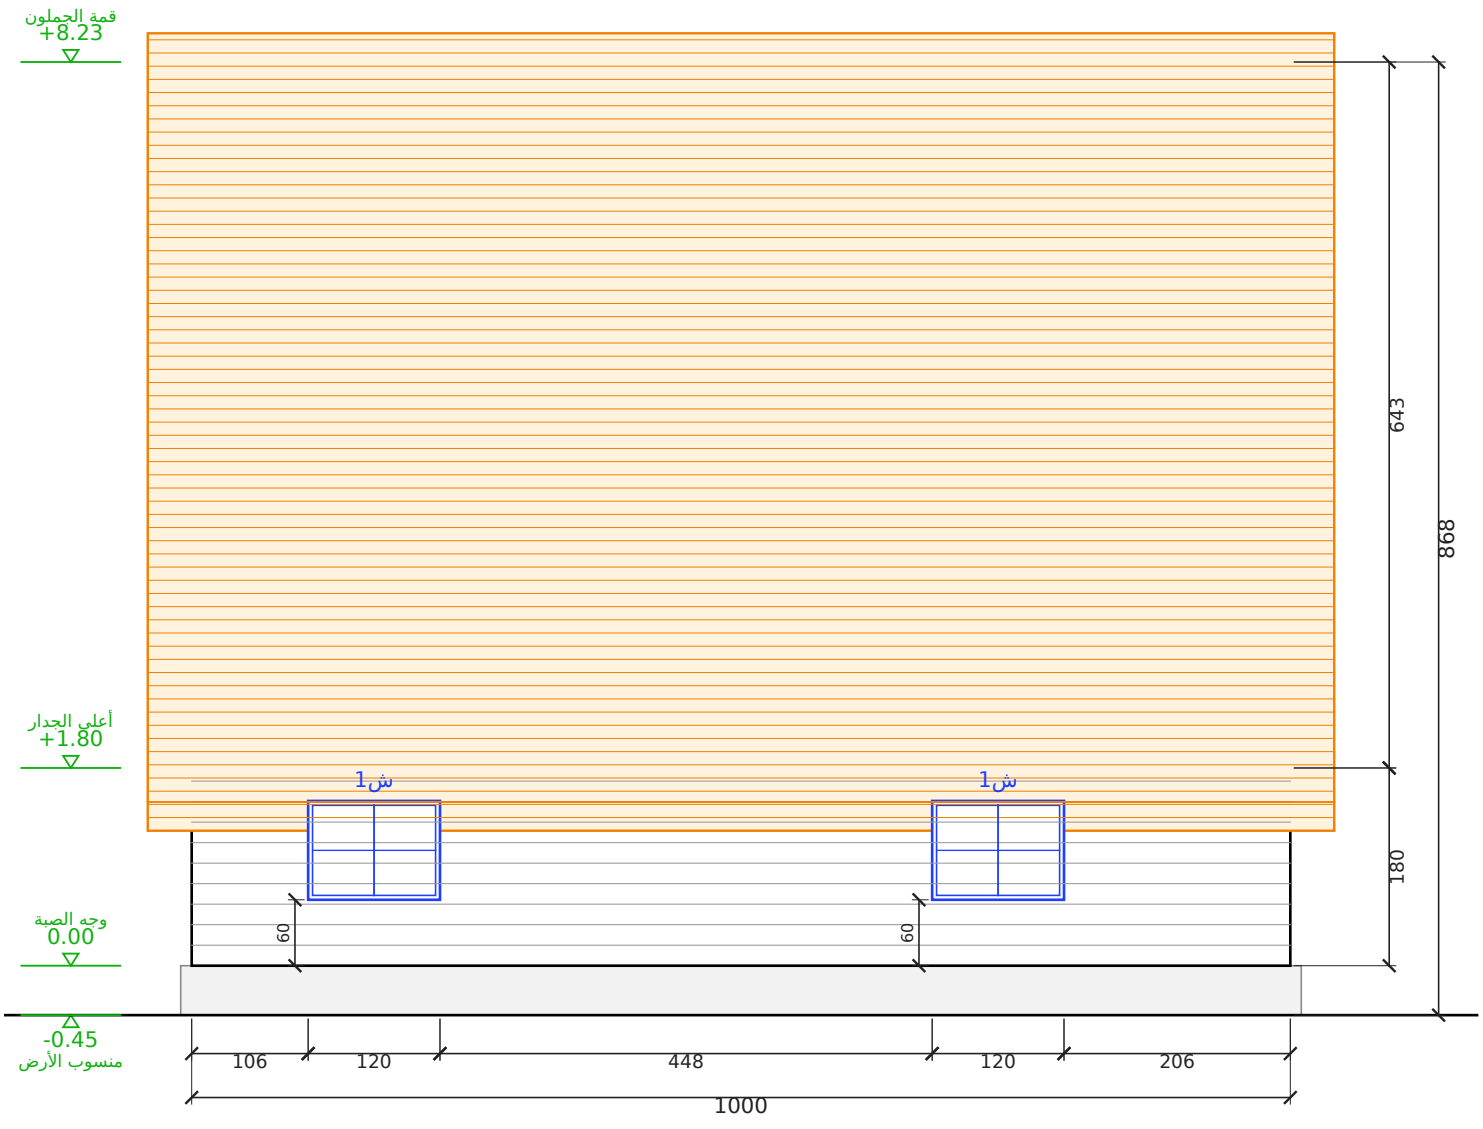


الواجهة الغربية

مقياس 1:50 | الوحدة: سم


المشروع / العميل	عنوان اللوحة	المقياس	التاريخ	رقم اللوحة
كوخ A-frame بواجهة زجاج + ميزانين — صالة وغرفة ومطبخ أمريكي وحمام — 10.00 × 9.00 م **عميل — A-frame 9×10**	**الواجهة الخلفية والواجهة الغربية**	**1:50**	**2026-10-23**	**W-04 (4/13)**

مصنع وتد الأخشاب
Watad Wood Factory


مسقط السقف (جملون)
رفرف 40 سم من كل جهة | مقياس 1:50

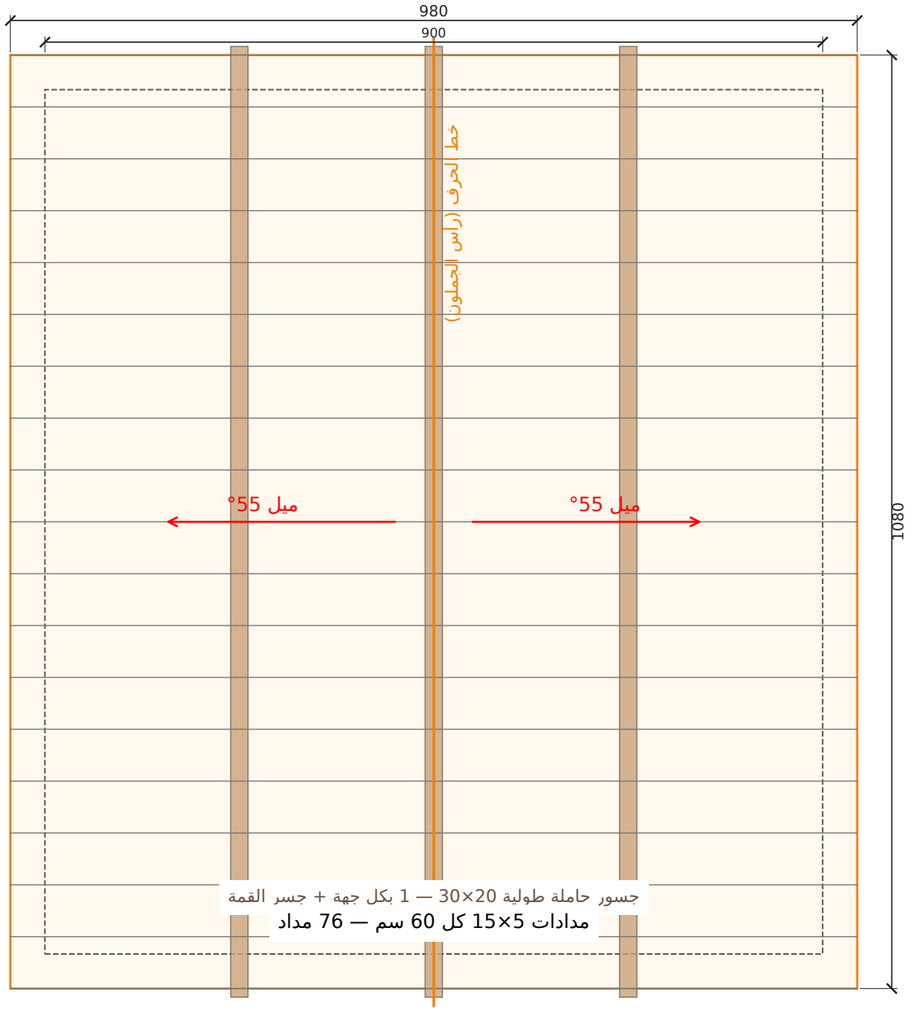

قطاع عرضي أ-أ
مقياس 1:50 | الوحدة: سم

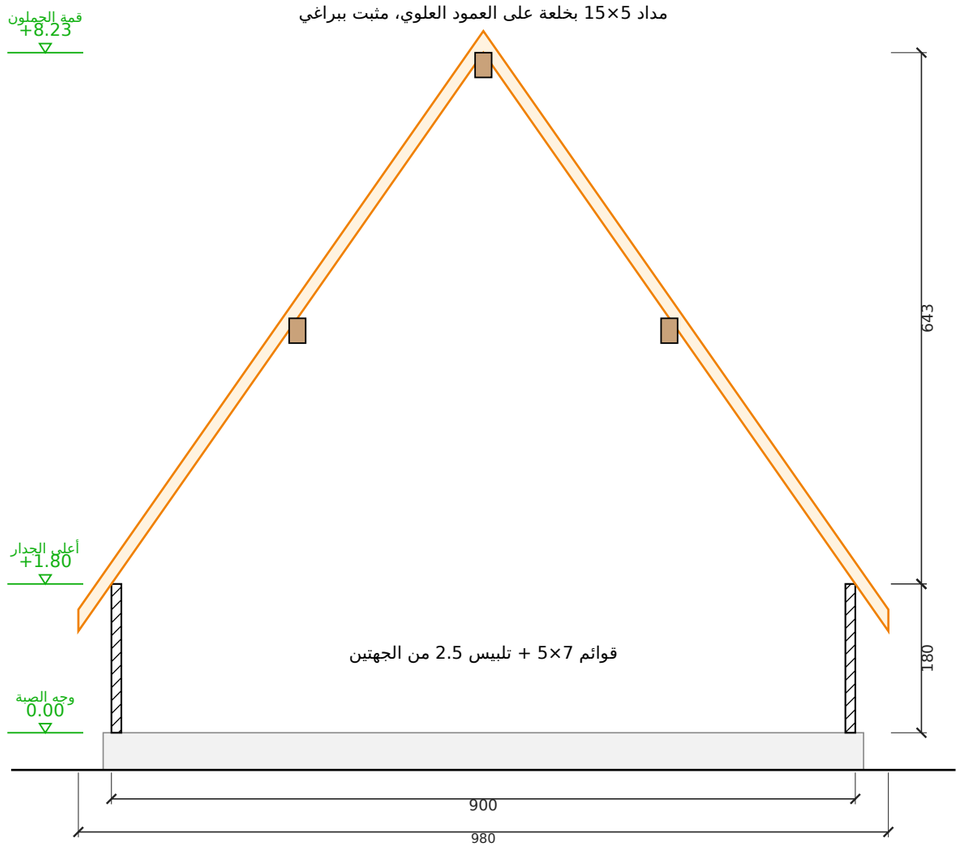

تفصيلة جلوس المداد على العلوي (1:5)

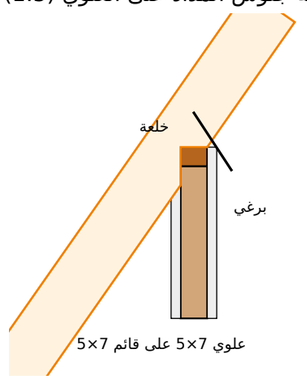

مصنع وتد الأخشاب Watad Wood Factory	المشروع / العميل كوخ A-frame بواجهة زجاج + ميزانين — صالة وغرفة ومطبخ أمريكي وحمام — 9.00 × 10.00 م عميل — A-frame 9×10	عنوان اللوحة مسقط السقف والقطاع	المقياس 1:50	التاريخ 2026-10-23	رقم اللوحة W-05 (5/13)

جدول مقاسات الأبواب والشبابيك
مقاس الفتحة الصافي في الجدار - الوحدة: سم

الرمز	النوع	العرض (سم)	الارتفاع (سم)	ارتفاع الجلسة (سم)	العدد	الموقع
ب1	باب مزدوج	144	220	-	1	الأمامية (زجاج كامل)
ب2	باب	80	210	-	1	غرفة النوم
ب3	باب	70	210	-	1	الحمام
ش4	باب	120	100	-	1	الخلفية
ز1	شباك	190	170	5	2	الأمامية (زجاج كامل) 2
ز1	شباك	160	170	5	2	الأمامية (زجاج كامل) 2
ش1	شباك	120	90	60	3	الشرقية - الغربية 2
ش2	شباك	100	60	100	1	الشرقية
ش3	شباك	60	60	160	1	الخلفية

الإجمالي: أبواب 4 - شبابيك 9

جدول المساحات وبيانات المشروع


بيانات المشروع

البند	البيان
المشروع	كوخ A-frame بواجهة زجاج + ميزانين — صالة وغرفة ومطبخ أمريكي وحمام — 9.00 × 10.00 م
العميل	عميل — A-frame 9×10
الموقع	—
الاستخدام	استراحة / سكن
التاريخ	2026-10-23
نظام البناء	هيكل خشب 5×7 + تلبيس 2.5 سم من الجهتين
السقف	جملون 55° — قرميد معدني


جدول المساحات

م	الفراغ	الأبعاد (م)	المساحة (م2)
1	الصالة (ارتفاع مزدوج)	8.76 × 4.94	43.27
2	غرفة النوم	3.94 × 4.64	18.28
3	المطبخ الأمريكي	4.70 × 2.70	12.69
4	الحمام	2.70 × 1.88	5.08
5	مخزن / غسيل	1.88 × 1.88	3.53
	المساحة الصافية الداخلية		**82.86**
	عتبة المدخل	**2.40 × 1.40**	**3.36**
	المساحة الإجمالية المبنية	**9.00 × 10.00**	**90.00**
	المساحة الكلية (المبنية + التراس)		**93.36**

تأطير جدار جنوب — الطول 888 سم، الارتفاع 180 سم

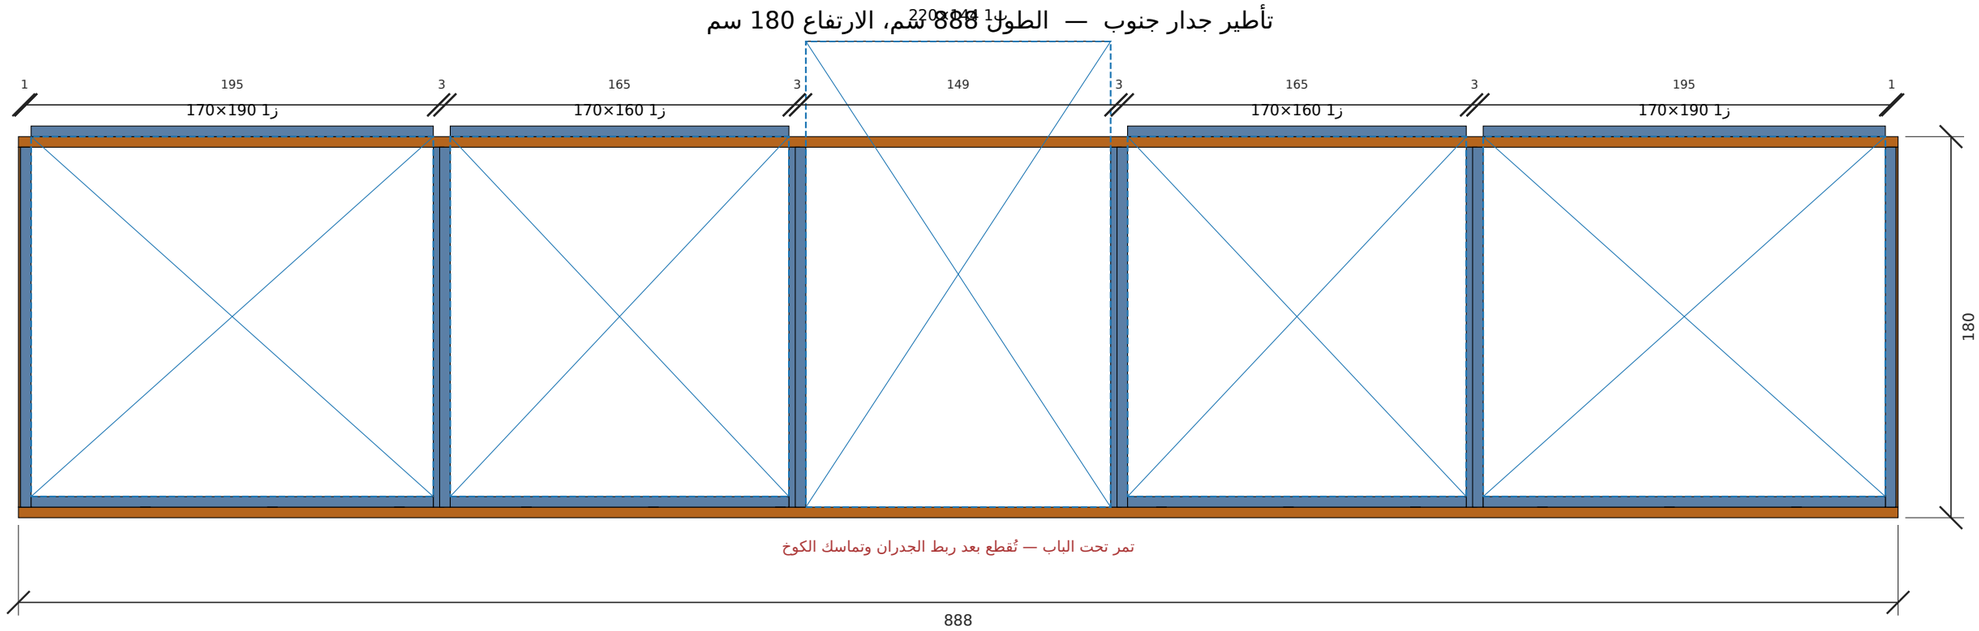


تأطير جدار شرق — الطول 988 سم، الارتفاع 180 سم

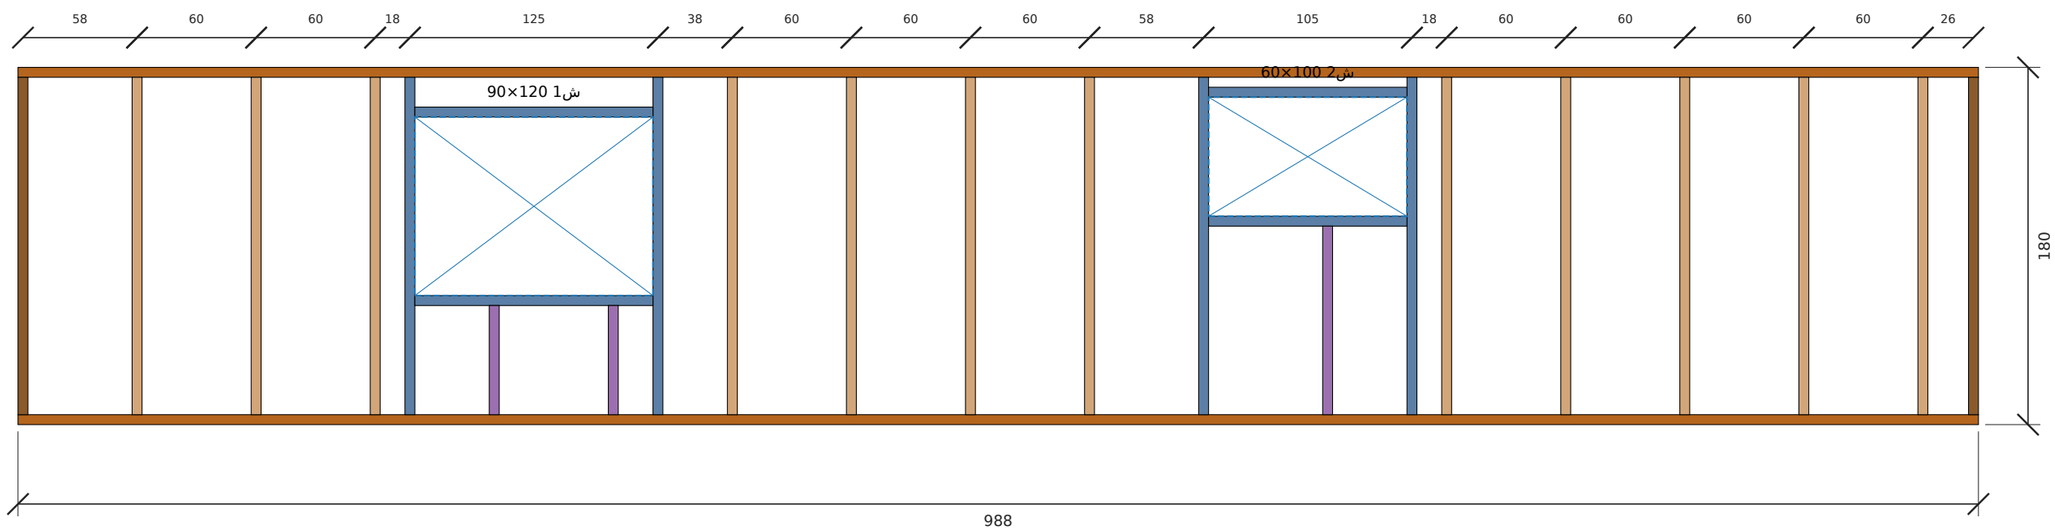


قاعدة سفلية | علوي | عمود | عمود زاوية | جنب فتحة | رأس فتحة | جلسة شباك | عمود قصير

مصنع وتد الأخشاب Watad Wood Factory	المشروع / العميل كوخ A-frame بواجهة زجاج + ميزانين — صالة وغرفة ومطبخ أمريكي وحمام — 9.00 × 10.00 م عميل — A-frame 9×10	عنوان اللوحة لوحات التأطير (للورشة)	المقياس —	التاريخ 2026-10-23	رقم اللوحة W-08 (8/13)

تأطير جدار شمال — الطول 888 سم، الارتفاع 180 سم

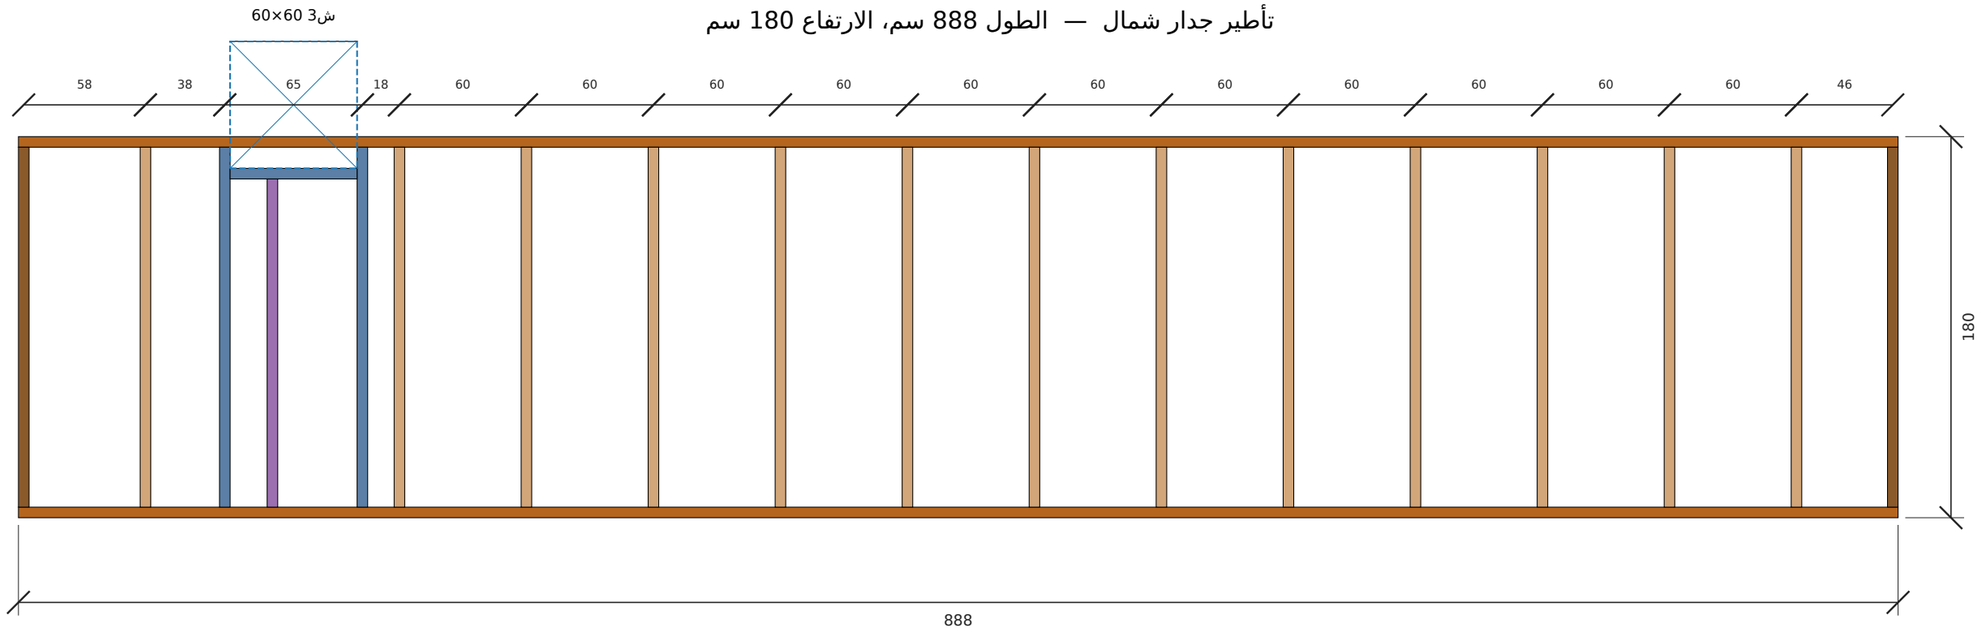


تأطير جدار غرب — الطول 988 سم، الارتفاع 180 سم

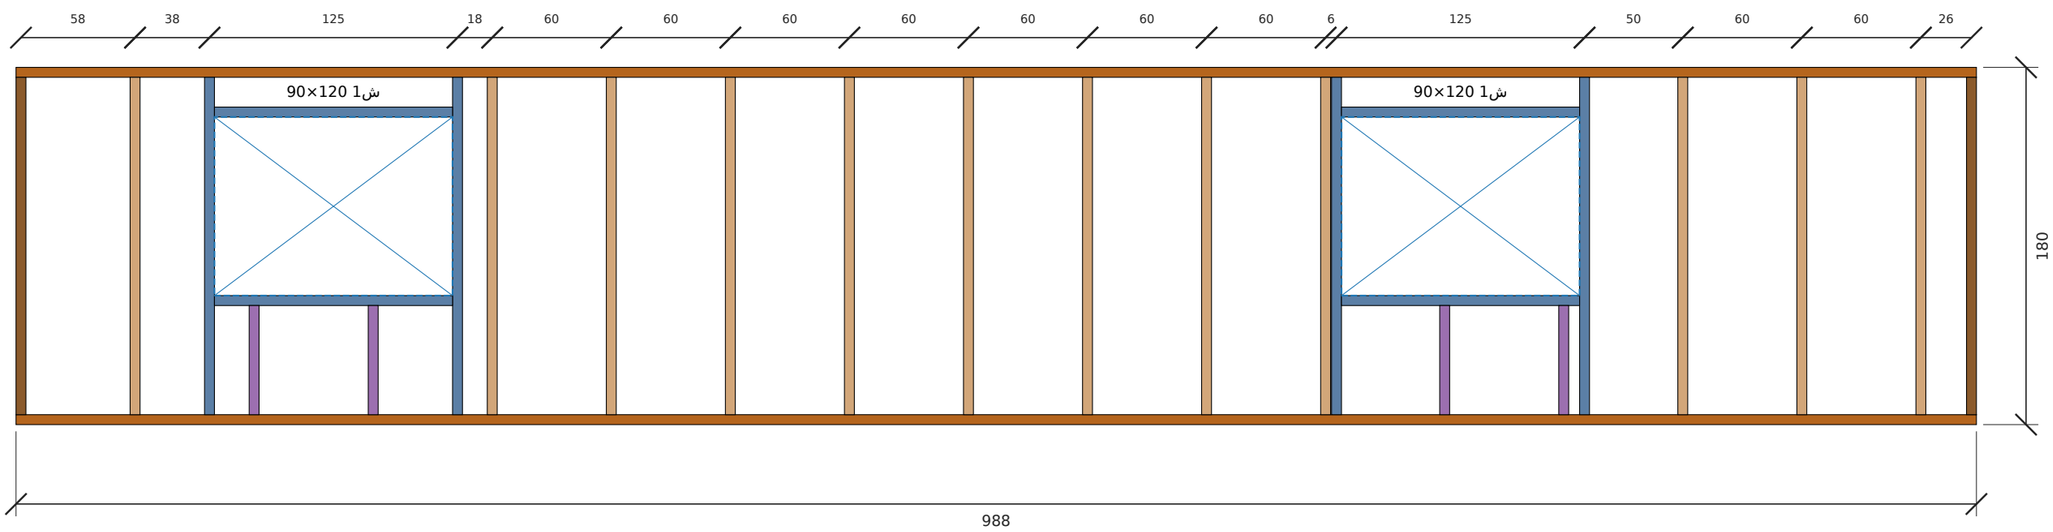


قاعدة سفلية | علوي | عمود | عمود زاوية | جنب فتحة | رأس فتحة | جلسة شباك | عمود قصير

مصنع وتد الأخشاب Watad Wood Factory	المشروع / العميل كوخ A-frame بواجهة زجاج + ميزانين — صالة وغرفة ومطبخ أمريكي وحمام — 9.00 × 10.00 م عميل — A-frame 9×10	عنوان اللوحة لوحات التأطير (للورشة)	المقياس —	التاريخ 2026-10-23	رقم اللوحة W-09 (9/13)

تأطير جدار جدار الغرفة الأمامي — الطول 406 سم، الارتفاع 248 سم (داخلي)

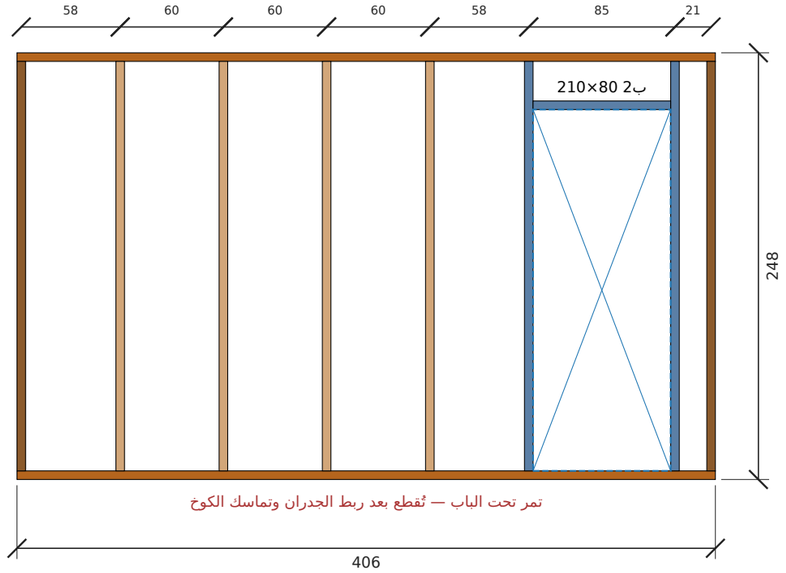


تأطير جدار جدار الغرفة الجانبي — الطول 476 سم، الارتفاع 248 سم (داخلي)

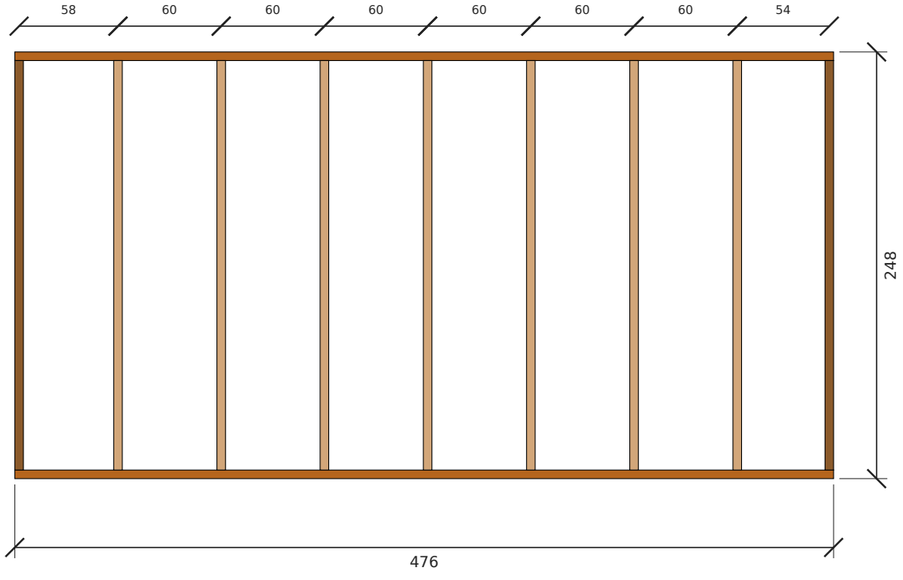


قاعدة سفلية | علوي | عمود | عمود زاوية | جنب فتحة | رأس فتحة | جلسة شباك | عمود قصير

مصنع وتد الأخشاب Watad Wood Factory	المشروع / العميل كوخ A-frame بواجهة زجاج + ميزانين — صالة وغرفة ومطبخ أمريكي وحمام — 9.00 × 10.00 م عميل — A-frame 9×10	عنوان اللوحة لوحات التأطير (للورشة)	المقياس —	التاريخ 2026-10-23	رقم اللوحة W-10 (10/13)

تأطير جدار جدار الحمام — الطول 282 سم، الارتفاع 248 سم (داخلي)

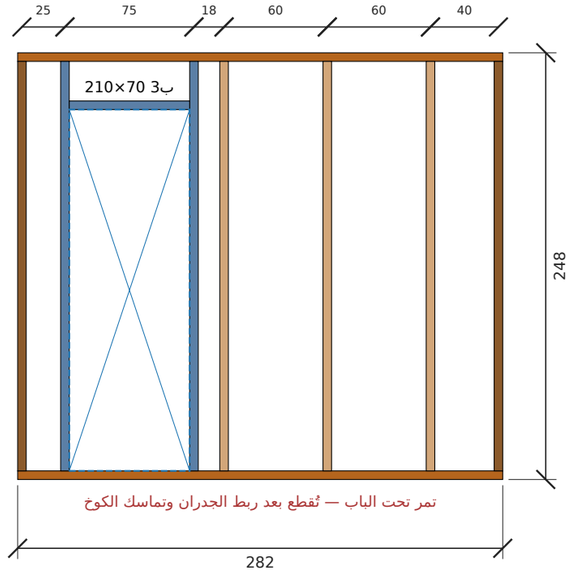

تأطير جدار جدار المخزن — الطول 200 سم، الارتفاع 248 سم (داخلي)

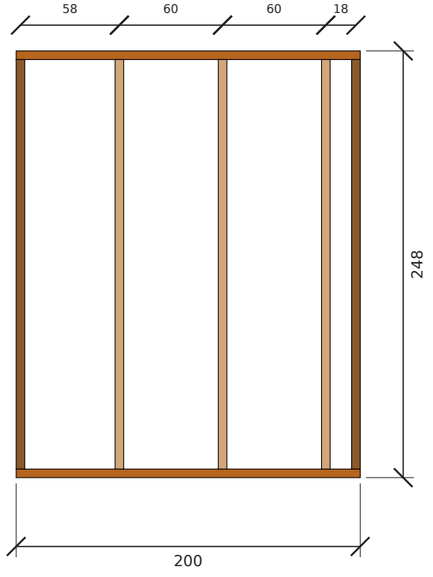

قاعدة سفلية | علوي | عمود | عمود زاوية | جنب فتحة | رأس فتحة | جلسة شباك | عمود قصير

مصنع وتد الأخشاب Watad Wood Factory	المشروع / العميل كوخ A-frame بواجهة زجاج + ميزانين — صالة وغرفة ومطبخ أمريكي وحمام — 9.00 × 10.00 م عميل — A-frame 9×10	عنوان اللوحة لوحات التأطير (للورشة)	المقياس —	التاريخ 2026-10-23	رقم اللوحة W-11 (11/13)

جدول الكميات وخطة تقطيع الطبليات

البند	القيمة
الارتفاع المطلوب / المعتمد	180 / 180 سم
السقف	جملون 55° — أعلى نقطة 823 سم من وجه الصبة
المدادات 5×15	76 مداد (19 خط × قطعتين موصولة فوق الجسر الحامل بتراكب 60 سم) × حتى 514 سم — من طبلية 520
طبليات الطريقة الأولى (مداد + عمود)	76 طبلية × 520 سم
طبليات الطريقة الثانية (3 أعمدة)	0 طبلية × 320 سم
إجمالي الطبليات 5×22.5	76
إجمالي قطع 5×7	151
قائمة تقطيع 5×7	988سم×4 | 888سم×4 | 476سم×2 | 406سم×2 | 282سم×2 | 238سم×29 | 200سم×2 | 190سم×4 | 170سم×65
	160سم×4 | 155سم×1 | 144سم×1 | 120سم×6 | 100سم×2 | 95سم×1 | 80سم×1 | 70سم×1 | 60سم×2
ألواح تلبيس 2.5 سم	247 لوح × 400 سم (مجموع الصفوف 773.6 م، 16 وجه)
أسمنت بورد 12 مم (122×244)	15 لوح (داخل دورات المياه)
العزل	110 لوح فوم صخري 80
الصبة	يجهزها العميل — 20 سم، مفرغة تحت دورات المياه

مراجعة التصميم مقابل قواعد المصنع

النوع	البند	التفاصيل	المقترح
ملاحظة	بحر المدادات	أطول بحر بدون جدار داخلي يحمل المداد: جهة أ: 450 سم، جهة ب: 450 سم. يحتاج رقم المصنع لأقصى بحر مسموح لتحديد المدادات اللي تُقوّى 20×5.	
ملاحظة	الصبة والدرج	ارتفاع الصبة 45 سم ← 3 درجة بقائمة 15.0 سم.	
ملاحظة	مناسيب رؤوس الفتحات	رؤوس الأبواب والشبابيك على مناسيب مختلفة: 150، 160، 175، 210، 220 سم.	
سؤال	يحتاج تأكيد	أقصى بحر للمداد بدون جدار داخلي قبل إضافة تقوية 5×7 (مداد 20×5)؟	
سؤال	يحتاج تأكيد	التغطية الصافية للوح التلبيس بعد التعشيق (مستنتجة مؤقتاً 18.67 سم من 280/15)؟	
سؤال	يحتاج تأكيد	هل يوضع أعمدة قصيرة فوق رأس الشباك/الباب إلى العلوي؟	
سؤال	يحتاج تأكيد	مكان الوصلة في القاعدة والعلوي إذا الجدار أطول من الطبلية؟	