

# المسقط الأفقي مع الفرش

## الأبعاد بالسنتيمتر - الجدران: قوائم 5×7 + تلبيس 2.5 من الجهتين (12 سم)

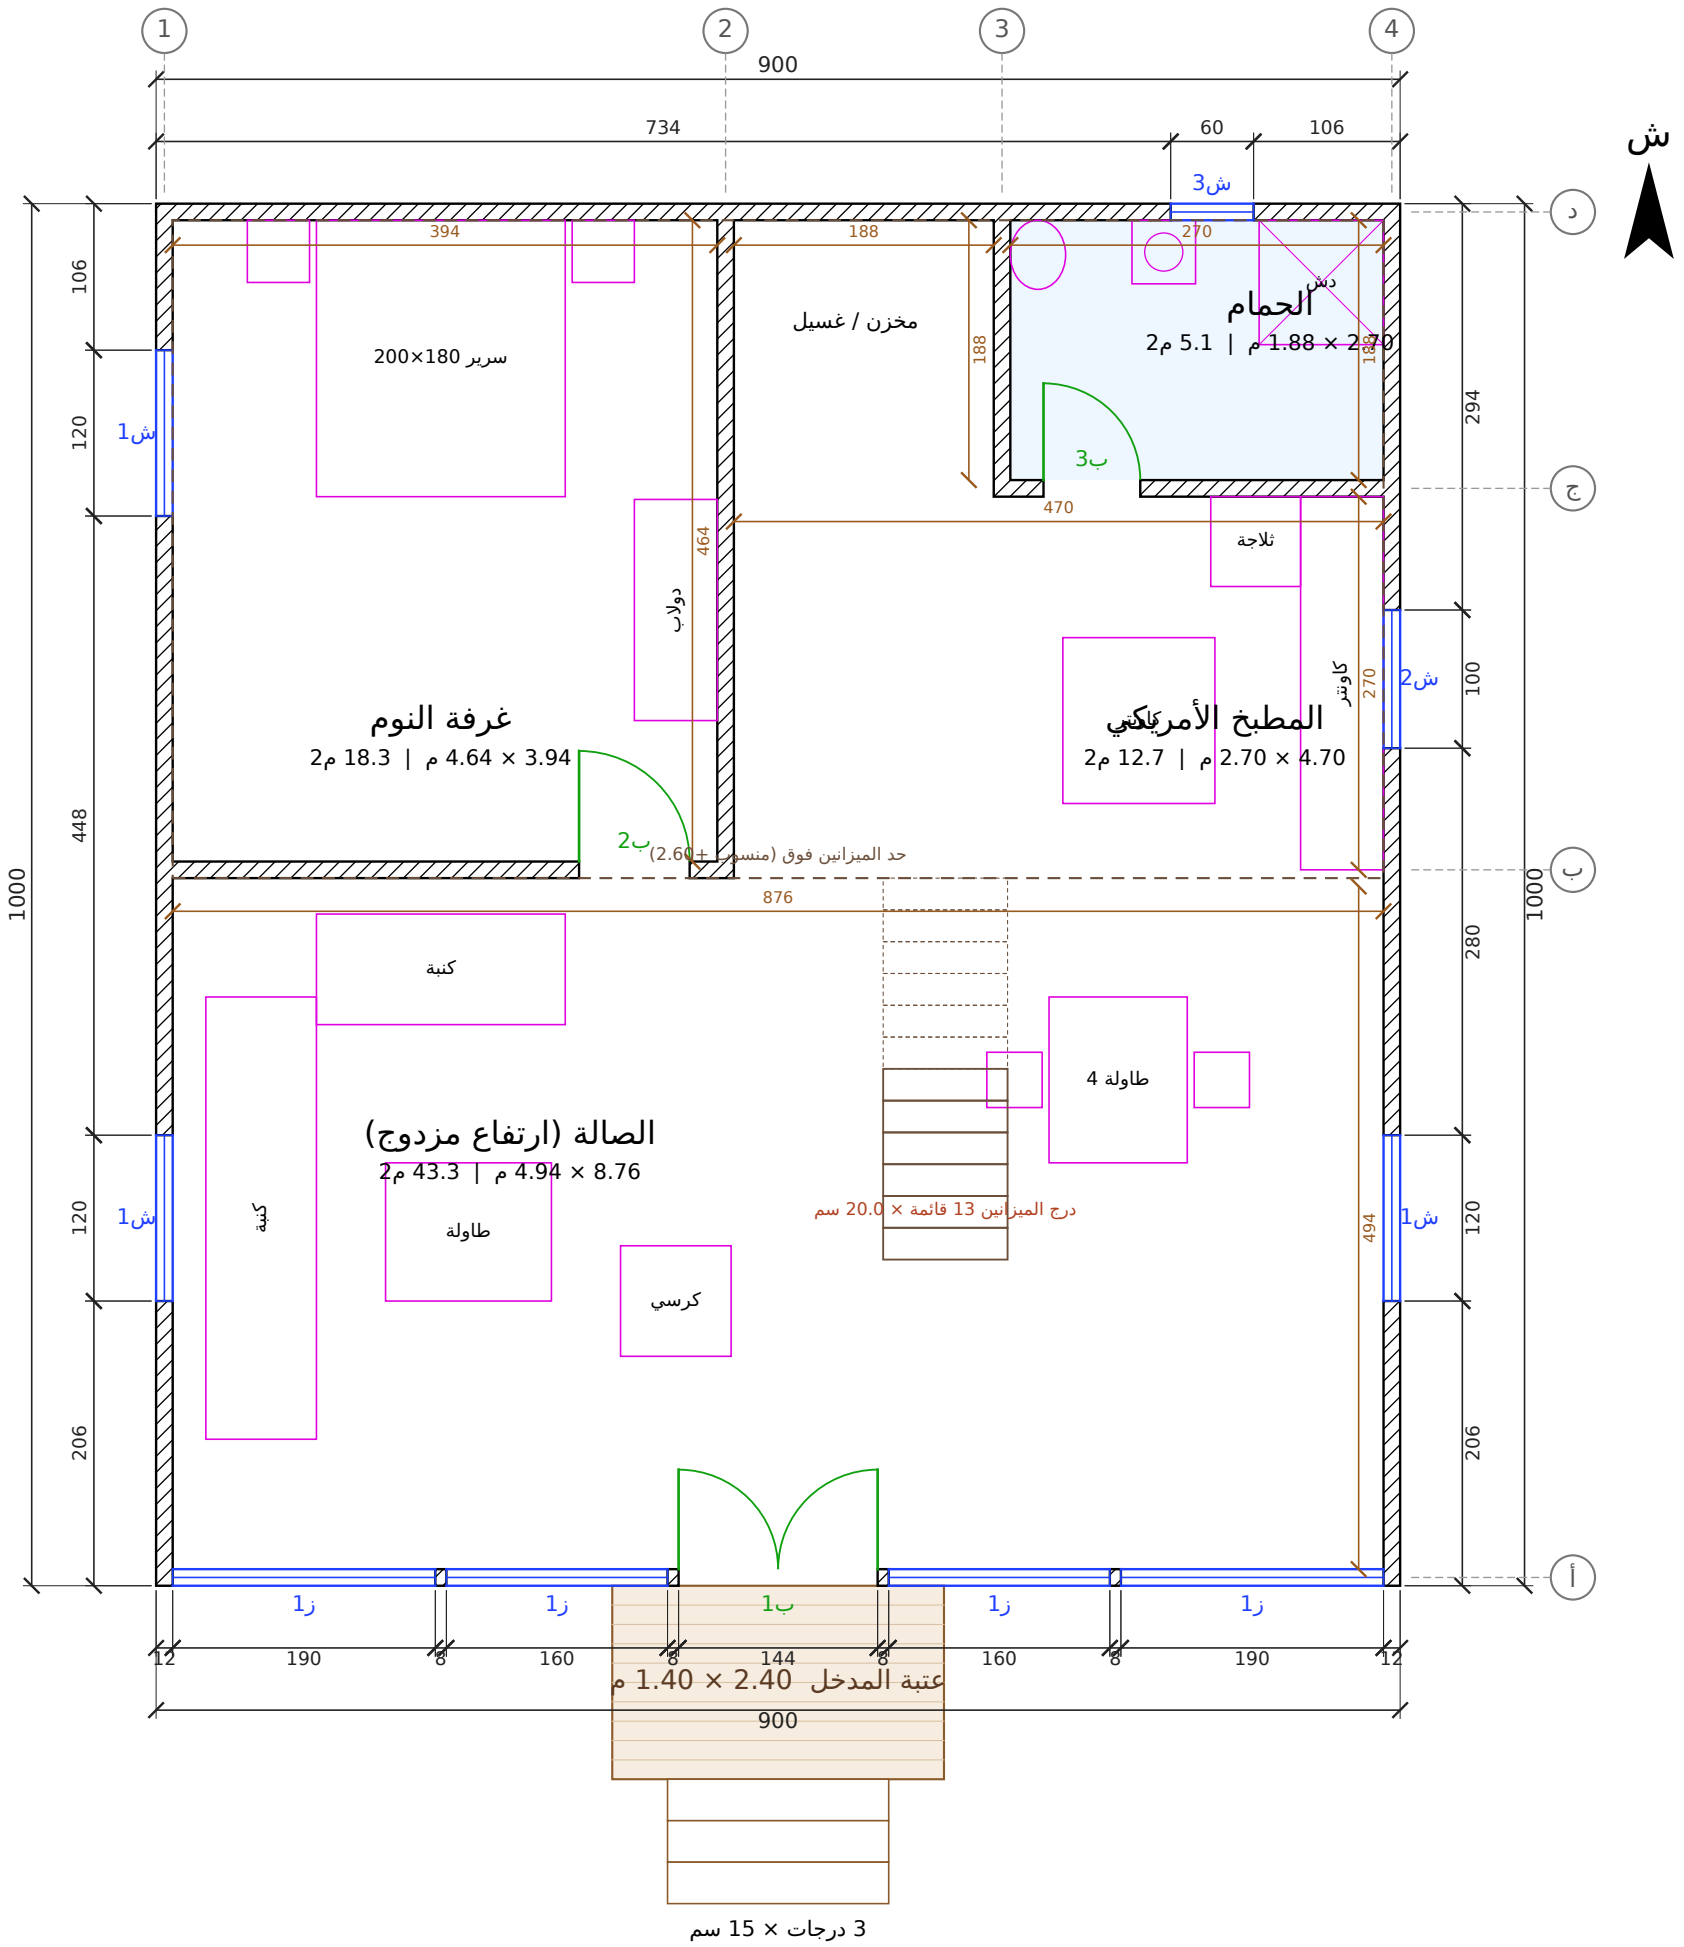



| المشروع / العميل | عنوان اللوحة | المقياس | التاريخ | رقم اللوحة |
|---|---|---|---|---|
| **مصنع وتد الأخشاب** Watad Wood Factory<br>**كوخ A-frame بواجهة زجاج + ميزانين — صالة وغرفة ومطبخ أمريكي وحمام — 9.00 × 10.00 م**<br>**عميل — A-frame 9×10** | **المسقط الأفقي** | **1:50** | **2026-10-23** | **A-01 (1/10)** |

# مسقط الميزانين (نص الدور) — جلسة علوية / نوم إضافي
## منسوب أرضية الميزانين +2.60  |  الأبعاد بالسنتيمتر

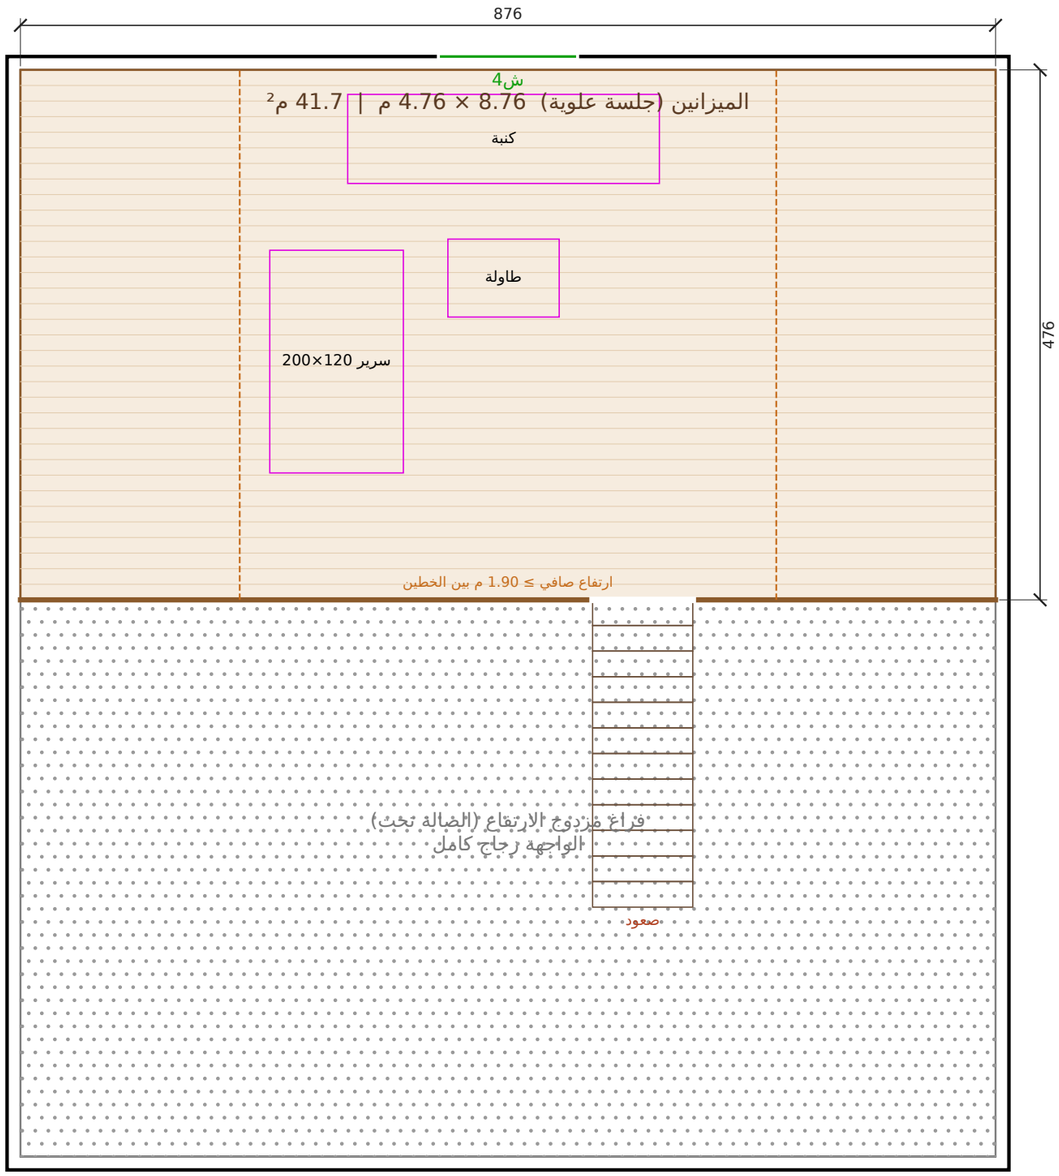



| | | | | | |
|---|---|---|---|---|---|
| **مصنع وتد الأخشاب**<br>Watad Wood Factory | المشروع / العميل<br>**كوخ A-frame بواجهة زجاج + ميزانين — صالة وغرفة ومطبخ أمريكي وحمام — 9.00 × 10.00 م**<br>**عميل — A-frame 9×10** | عنوان اللوحة<br>**مسقط الميزانين** | المقياس<br>**1:50** | التاريخ<br>**2026-10-23** | رقم اللوحة<br>**A-02  (2/10)** |

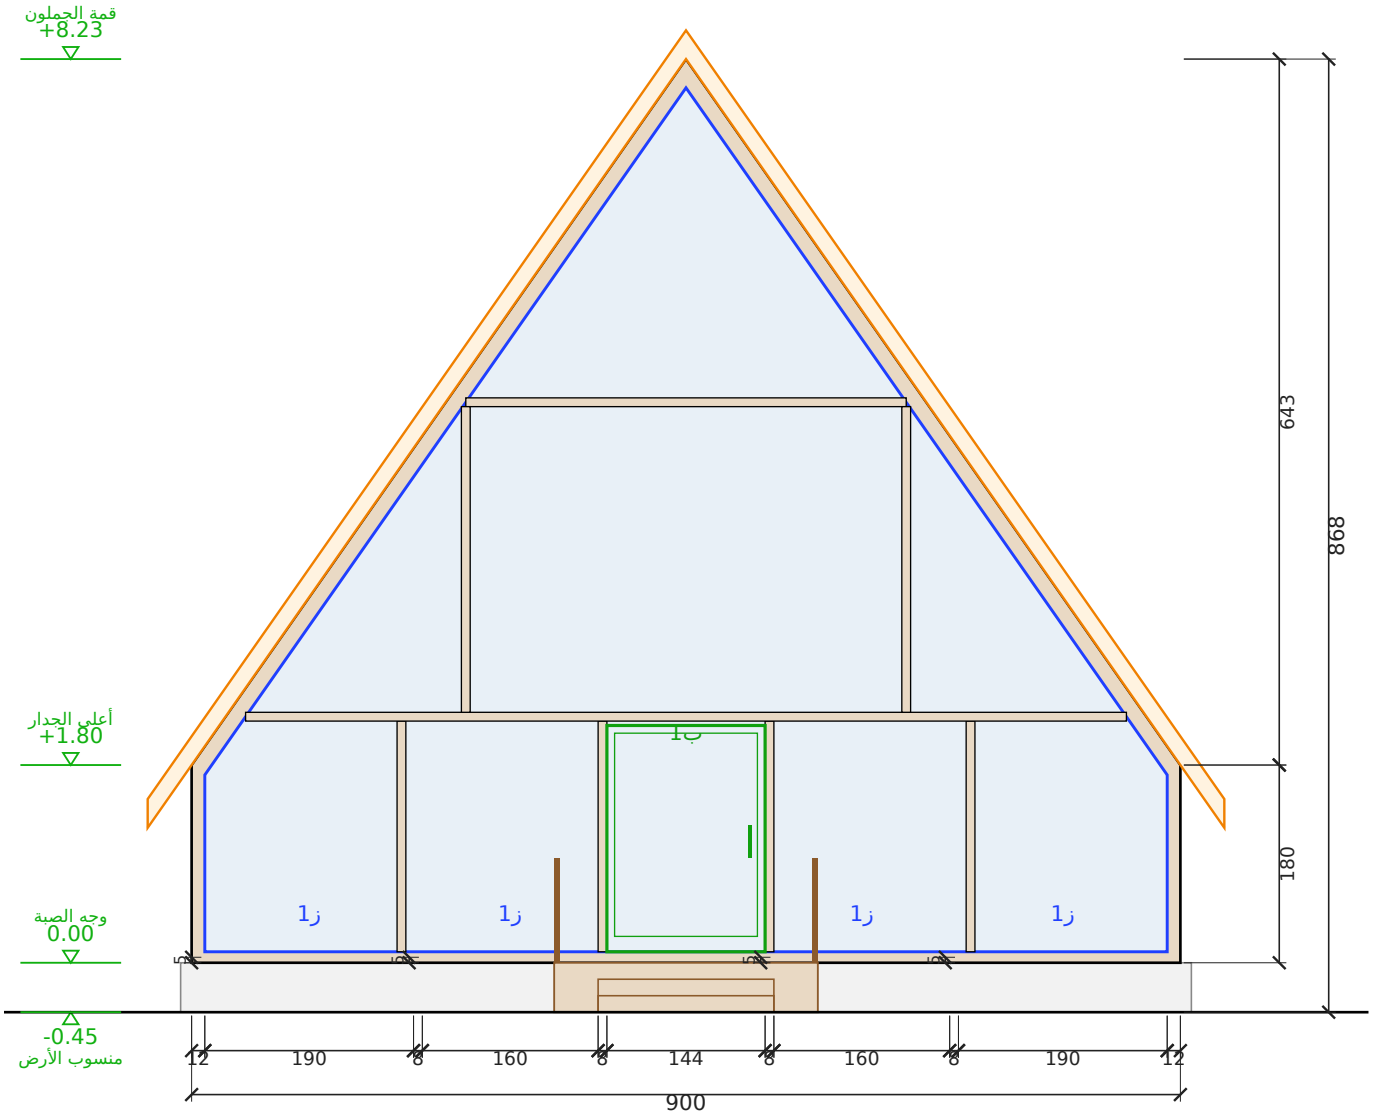


## الواجهة الأمامية (زجاج كامل)

مقياس 1:50 | الوحدة: سم

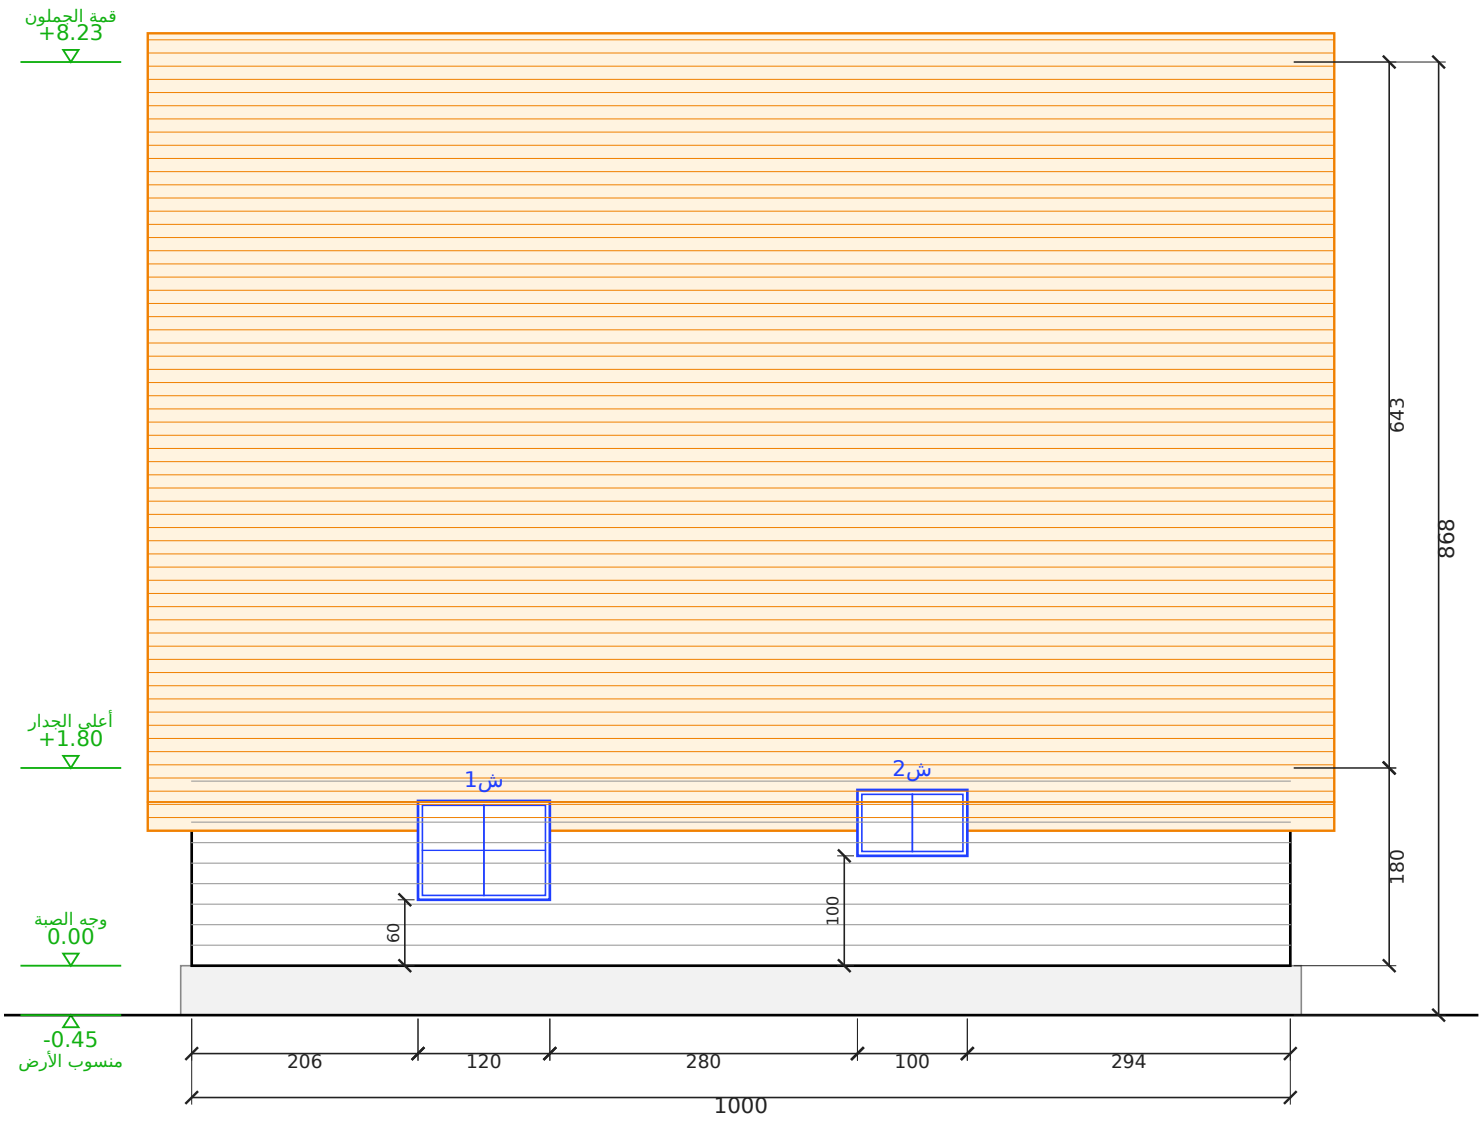



## الواجهة الشرقية

مقياس 1:50 | الوحدة: سم


| المشروع / العميل | عنوان اللوحة | المقياس | التاريخ | رقم اللوحة |
|---|---|---|---|---|
| **كوخ A-frame بواجهة زجاج + ميزانين — صالة وغرفة ومطبخ أمريكي وحمام — 9.00 × 10.00 م**<br>**عميل — A-frame 9×10** | **الواجهة الأمامية (زجاج كامل) والواجهة الشرقية** | **1:50** | **2026-10-23** | **A-03 (3/10)** |

**مصنع وتد الأخشاب**
Watad Wood Factory

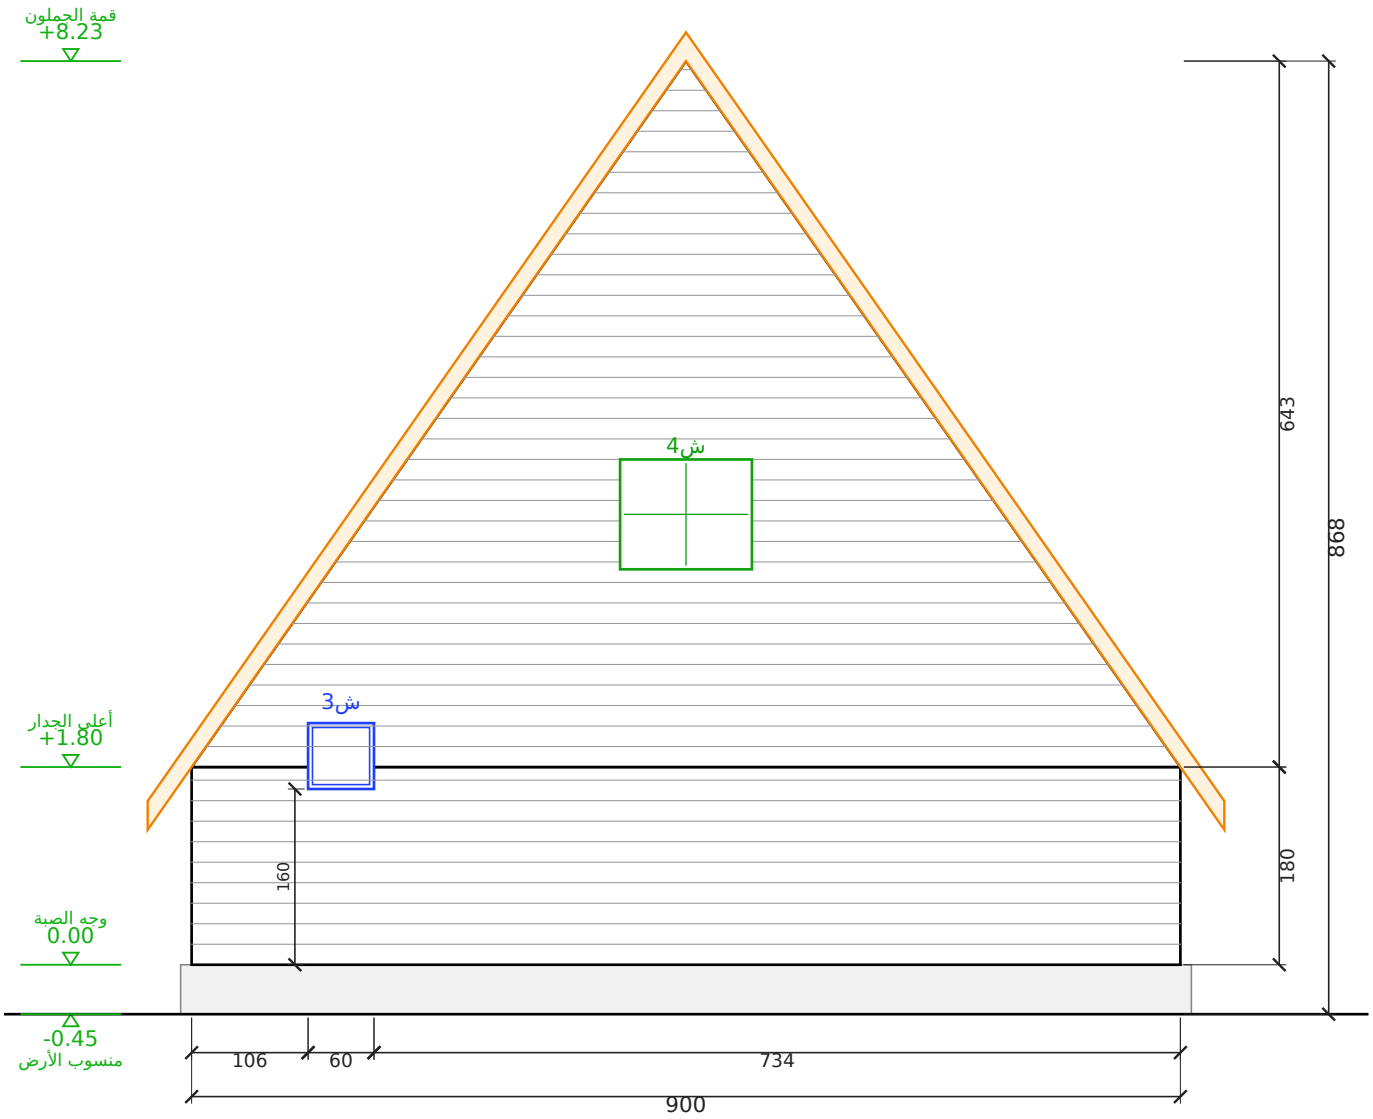


## الواجهة الخلفية

مقياس 1:50 | الوحدة: سم

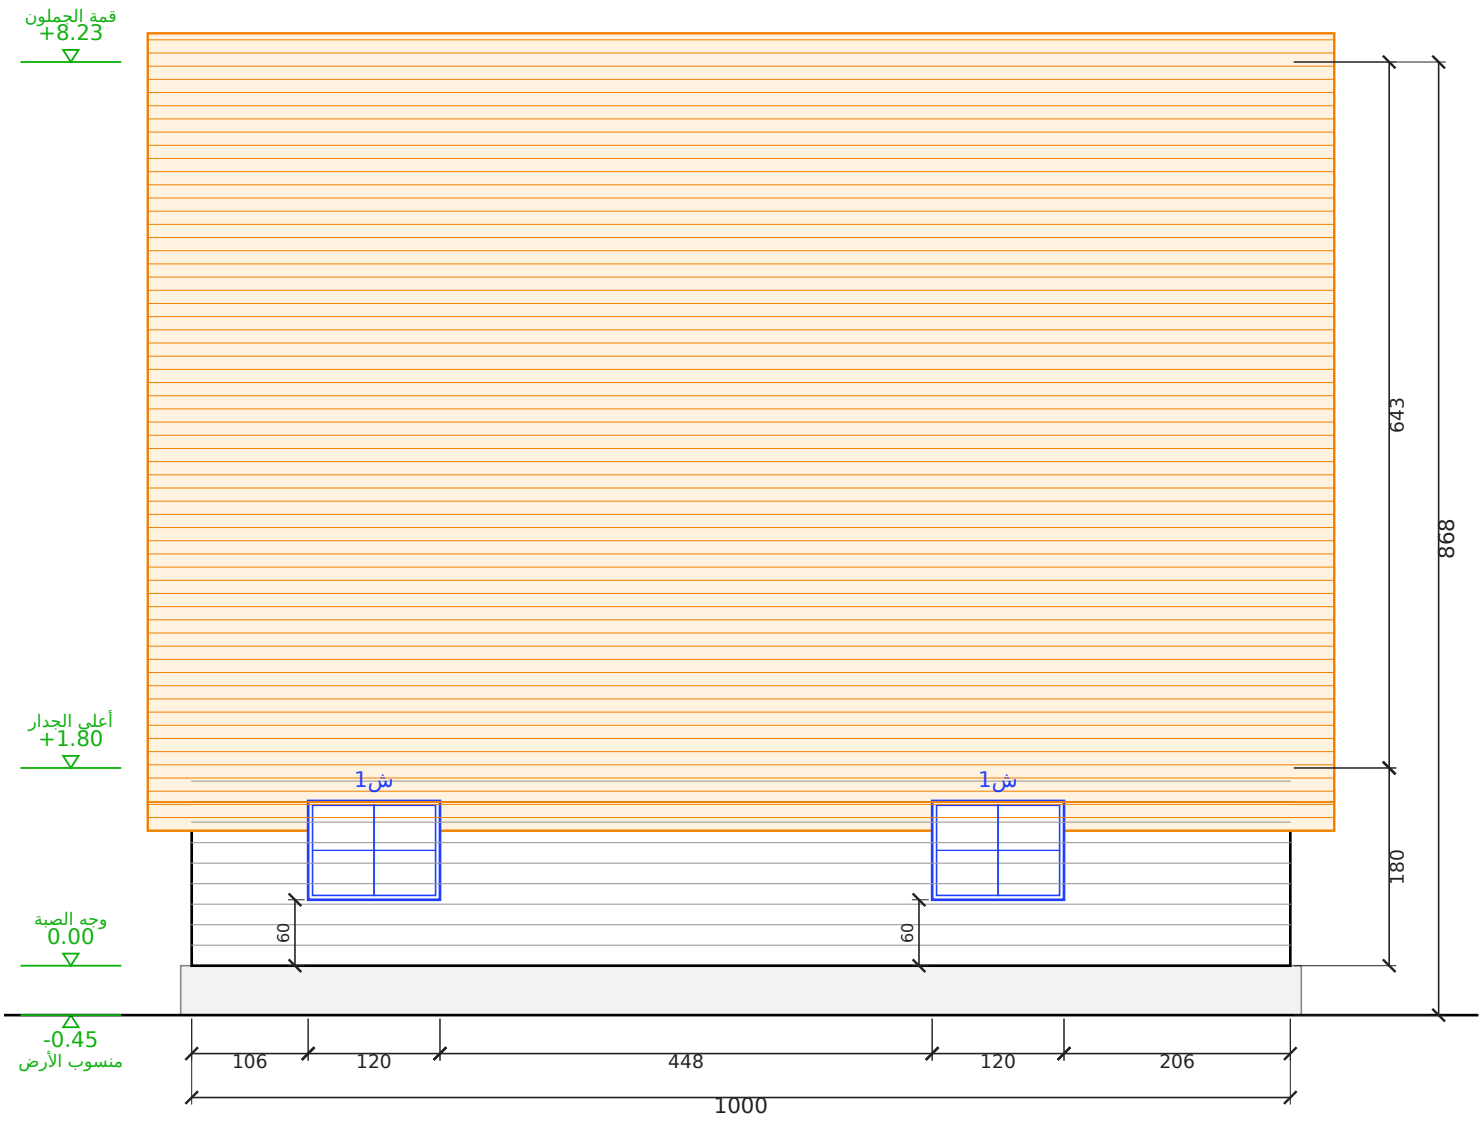



## الواجهة الغربية

مقياس 1:50 | الوحدة: سم


| المشروع / العميل | عنوان اللوحة | المقياس | التاريخ | رقم اللوحة |
|---|---|---|---|---|
| **كوخ A-frame بواجهة زجاج + ميزانين — صالة وغرفة ومطبخ أمريكي وحمام — 10.00 × 9.00**<br>**عميل — A-frame 9×10** | **الواجهة الخلفية والواجهة الغربية** | **1:50** | **2026-10-23** | **A-04 (4/10)** |

**مصنع وتد الأخشاب**
Watad Wood Factory


## مسقط السقف (جملون)
رفرف 40 سم من كل جهة | مقياس 1:50

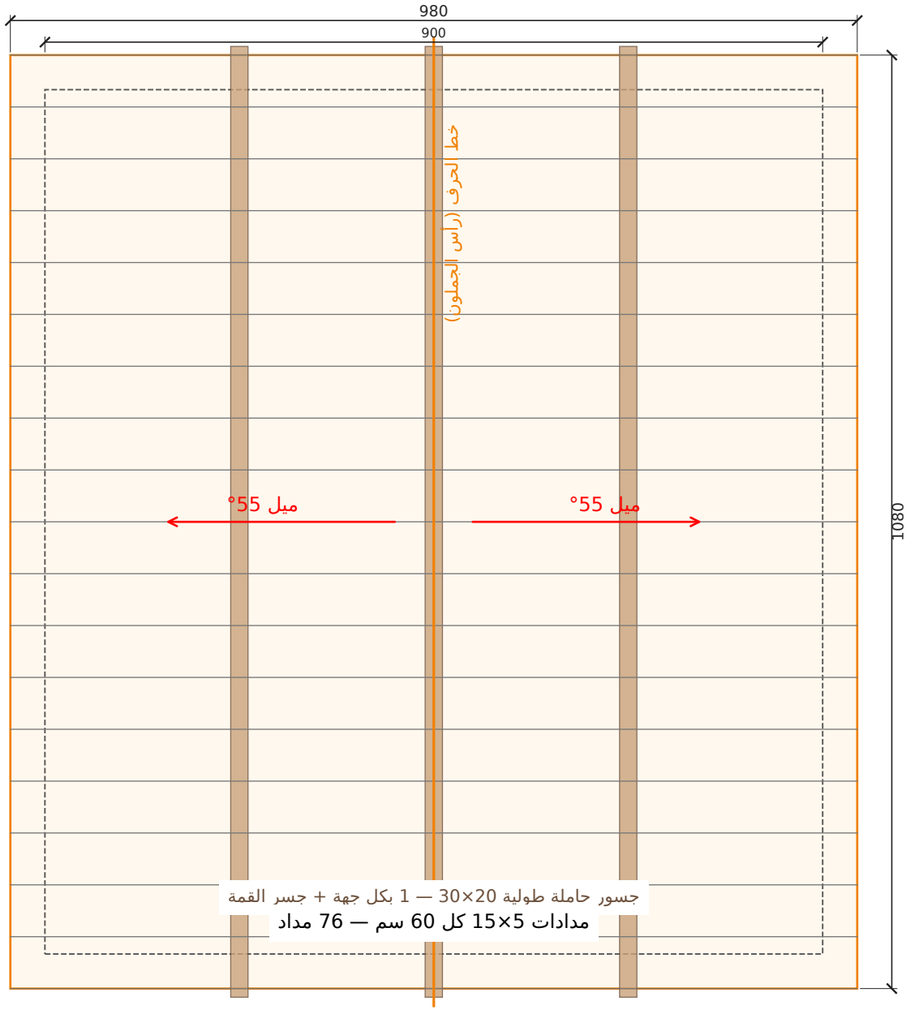


## قطاع عرضي أ-أ
مقياس 1:50 | الوحدة: سم

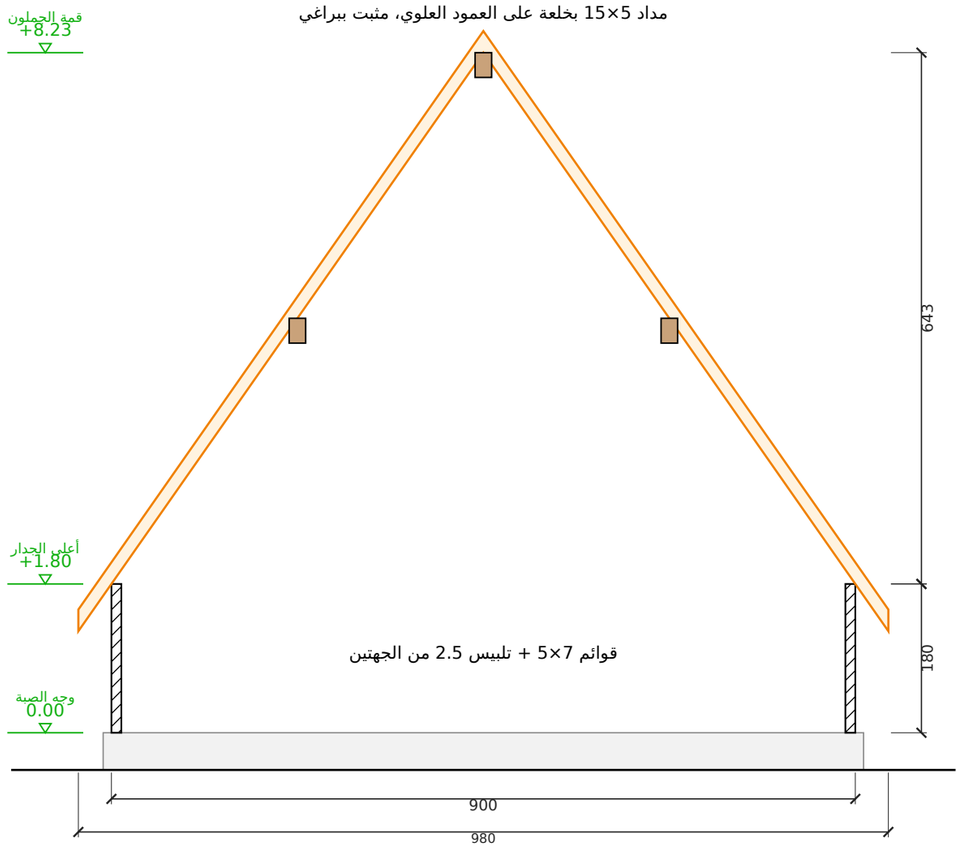


### تفصيلة جلوس المداد على العلوي (1:5)

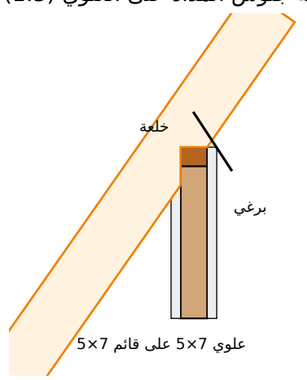


| | | | | | |
|---|---|---|---|---|---|
| المشروع / العميل | عنوان اللوحة | المقياس | التاريخ | رقم اللوحة |
| **مصنع وتد الأخشاب** Watad Wood Factory | **كوخ A-frame بواجهة زجاج + ميزانين — صالة وغرفة ومطبخ أمريكي وحمام — 9.00 × 10.00 م** عميل — A-frame 9×10 | **مسقط السقف والقطاع** | **1:50** | **2026-10-23** | **A-05 (5/10)** |

## جدول مقاسات الأبواب والشبابيك
### مقاس الفتحة الصافي في الجدار - الوحدة: سم

| الرمز | النوع | العرض (سم) | الارتفاع (سم) | ارتفاع الجلسة (سم) | العدد | الموقع |
|---|---|---|---|---|---|---|
| ب1 | باب مزدوج | 144 | 220 | - | 1 | الأمامية (زجاج كامل) |
| ب2 | باب | 80 | 210 | - | 1 | غرفة النوم |
| ب3 | باب | 70 | 210 | - | 1 | الحمام |
| ش4 | باب | 120 | 100 | - | 1 | الخلفية |
| ز1 | شباك | 190 | 170 | 5 | 2 | الأمامية (زجاج كامل) 2 |
| ز1 | شباك | 160 | 170 | 5 | 2 | الأمامية (زجاج كامل) 2 |
| ش1 | شباك | 120 | 90 | 60 | 3 | الشرقية - الغربية 2 |
| ش2 | شباك | 100 | 60 | 100 | 1 | الشرقية |
| ش3 | شباك | 60 | 60 | 160 | 1 | الخلفية |

الإجمالي: أبواب 4 - شبابيك 9

# جدول المساحات وبيانات المشروع

## بيانات المشروع


| البند | البيان |
|---|---|
| المشروع | كوخ A-frame بواجهة زجاج + ميزانين — صالة وغرفة ومطبخ أمريكي وحمام — 9.00 × 10.00 م |
| العميل | عميل — A-frame 9×10 |
| الموقع | — |
| الاستخدام | استراحة / سكن |
| التاريخ | 2026-10-23 |
| نظام البناء | هيكل خشب 5×7 + تلبيس 2.5 سم من الجهتين |
| السقف | جملون 55° — قرميد معدني |

## جدول المساحات


| م | الفراغ | الأبعاد (م) | المساحة (م2) |
|---|---|---|---|
| 1 | الصالة (ارتفاع مزدوج) | 8.76 × 4.94 | 43.27 |
| 2 | غرفة النوم | 3.94 × 4.64 | 18.28 |
| 3 | المطبخ الأمريكي | 4.70 × 2.70 | 12.69 |
| 4 | الحمام | 2.70 × 1.88 | 5.08 |
| 5 | مخزن / غسيل | 1.88 × 1.88 | 3.53 |
| | **المساحة الصافية الداخلية** | | **82.86** |
| | **عتبة المدخل** | **2.40 × 1.40** | **3.36** |
| | **المساحة الإجمالية المبنية** | **9.00 × 10.00** | **90.00** |
| | **المساحة الكلية (المبنية + التراس)** | | **93.36** |

# لقطات المنظور الخارجي

المنظور الأمامي

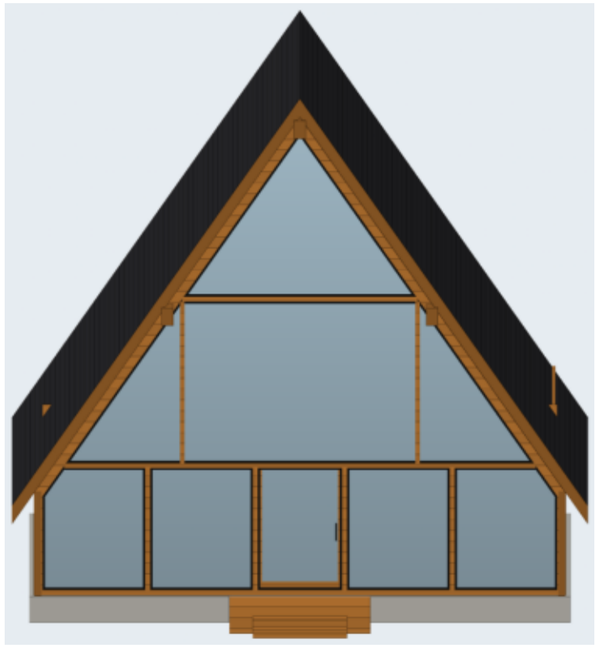


منظور أمامي من اليسار

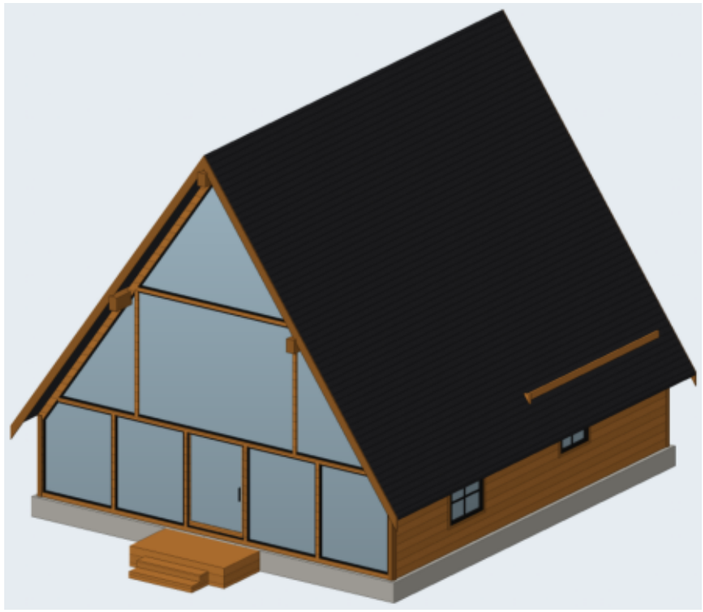


منظور أمامي من اليمين




المنظور الخلفي

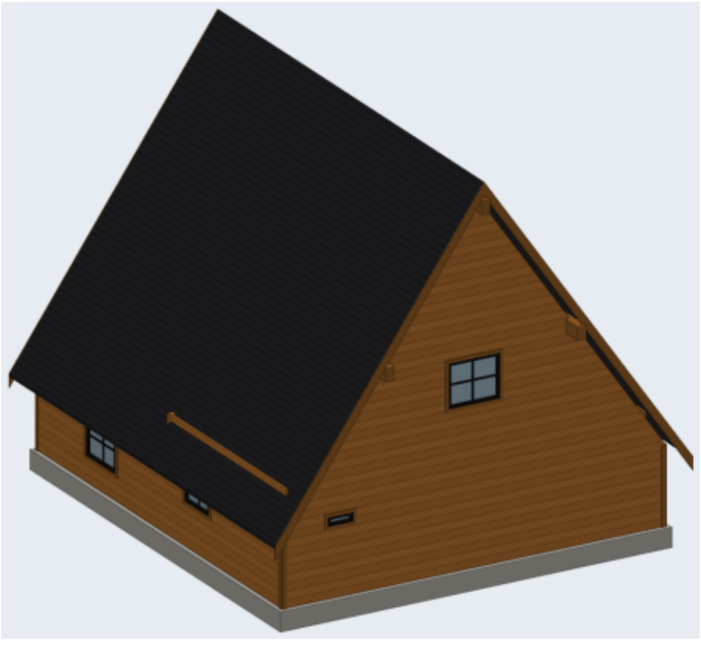

منظور خلفي من اليمين

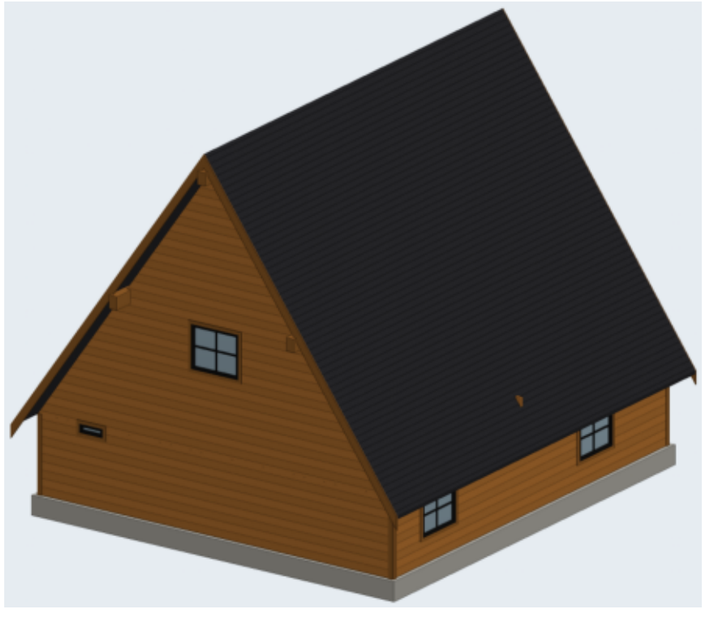


منظر علوي

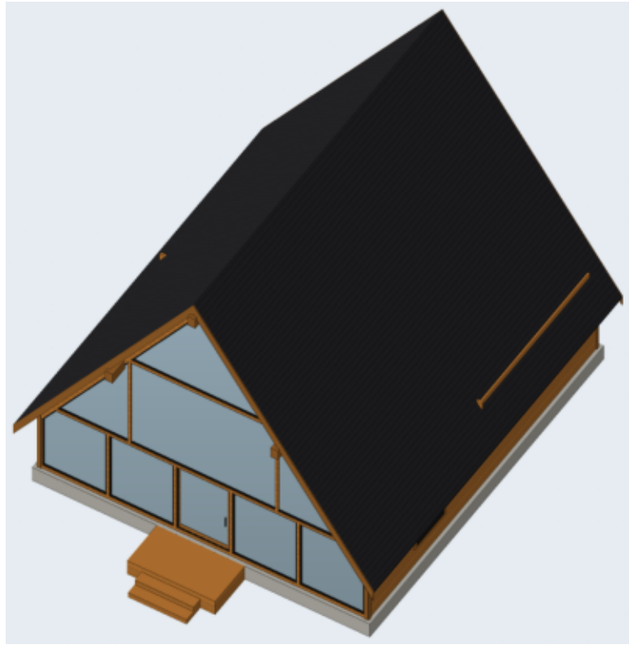

| | | | | |
|---|---|---|---|---|
| **مصنع وتد الأخشاب**<br>Watad Wood Factory | المشروع / العميل<br>**كوخ A-frame بواجهة زجاج + ميزانين — صالة وغرفة ومطبخ أمريكي وحمام — 9.00 × 10.00 م**<br>**عميل — A-frame 9×10** | عنوان اللوحة<br>**لقطات المنظور** | المقياس<br>**—** | التاريخ<br>**2026-10-23** | رقم اللوحة<br>**A-08 (8/10)** |

# المقطع العلوي بالفرش


مقطع أفقي على ارتفاع 1.90 م — توزيع الفرش ومسار الحركة

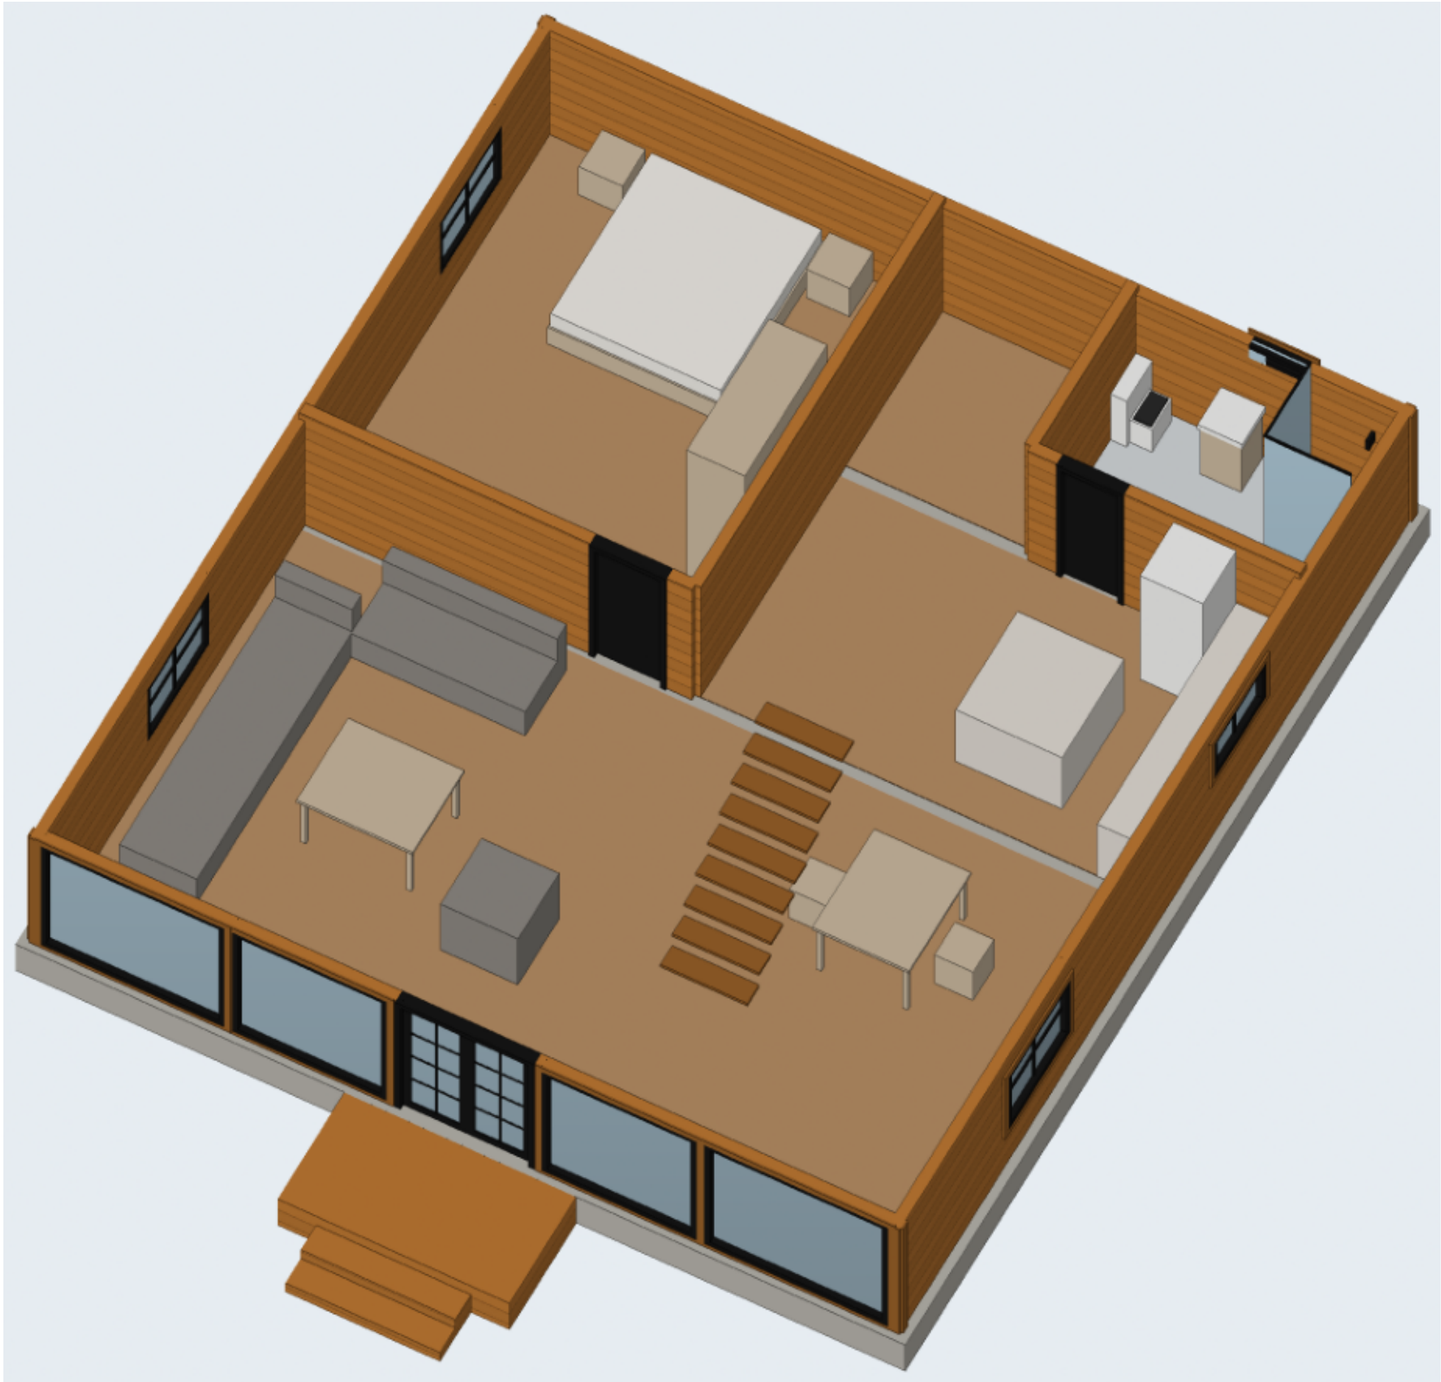

| | | | | | |
|---|---|---|---|---|---|
| مصنع وتد الأخشاب<br>Watad Wood Factory | المشروع / العميل<br>كوخ A-frame بواجهة زجاج + ميزانين — صالة وغرفة ومطبخ أمريكي وحمام — 9.00 × 10.00 م<br>عميل — A-frame 9×10 | عنوان اللوحة<br>المقطع العلوي بالفرش | المقياس<br>— | التاريخ<br>2026-10-23 | رقم اللوحة<br>A-09 (9/10) |

# المنظور ثلاثي الأبعاد والمواد

النمط: جوزي غامق + إطارات سوداء — رندر واقعي بخامات حقيقية

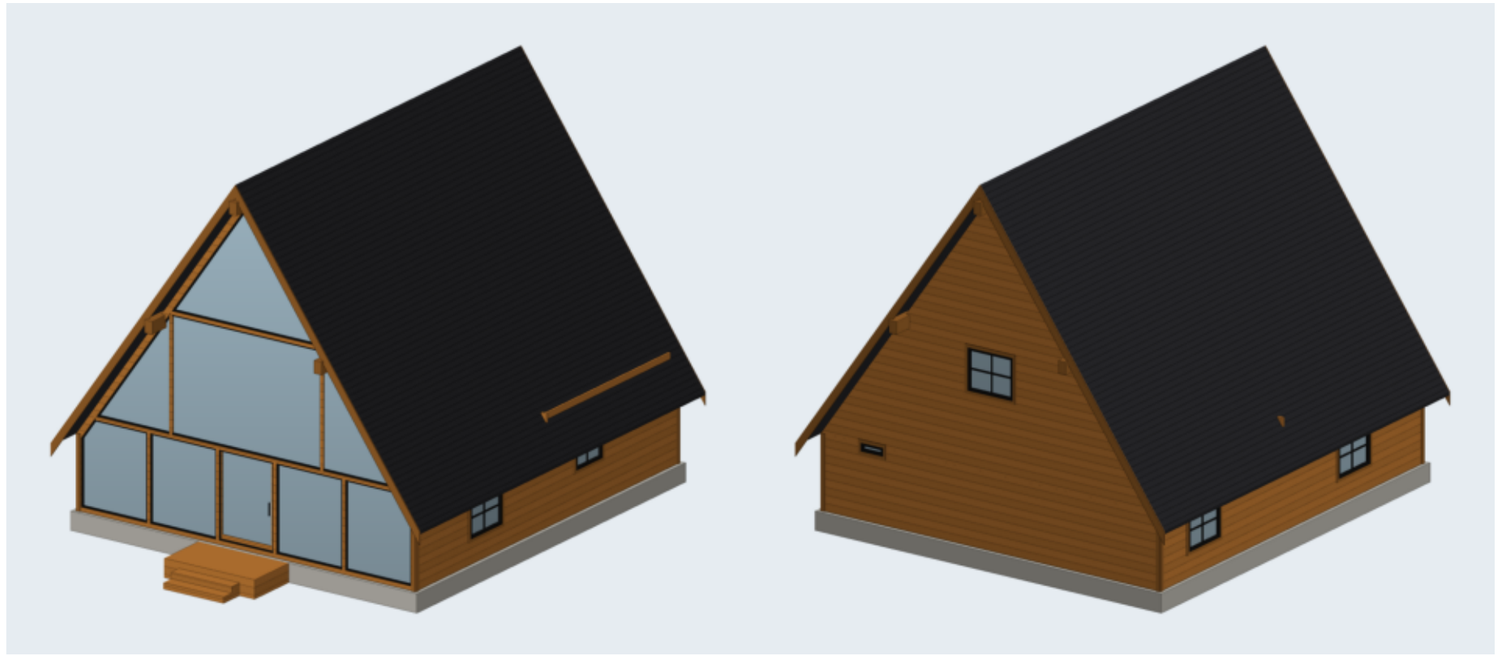

## جدول المواد والألوان

**الخشب / الصبغة**

صبغة عسلي / سيدر

**القرميد**

قرميد رمادي غامق

**الزجاج**

زجاج شفاف

**إطارات الشبابيك والأبواب**

إطار ألمنيوم أسود

**الكنار والزوايا**

نفس الصبغة أغمق درجة


**الصبة**

خرسانة 45 سم


الدربزين: ألواح أفقية متقاربة (عصري)

تقسيم الشبابيك: بدون | الباب الرئيسي: زجاج بتقسيمات (فرنسي)

## أنواع الدربزين المعتمدة (من مشاريع المصنع)

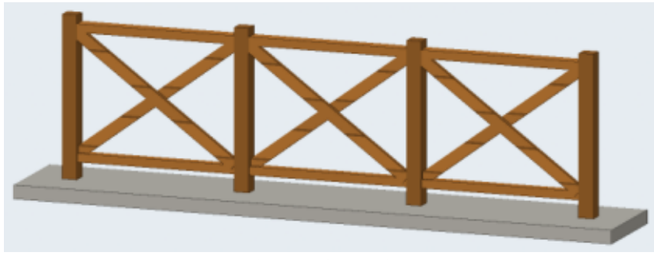

تقاطع X (صورة 5)

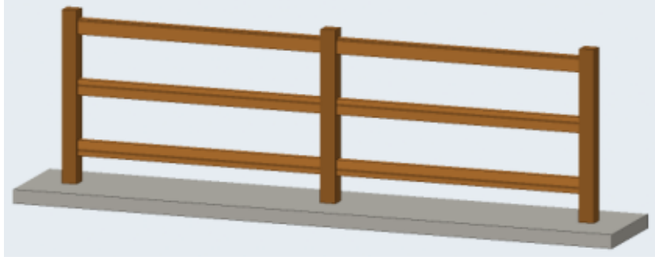

3 مرابيع أفقية (صورة 2)



قوائم رأسية متقاربة (صورة 1)

| المشروع / العميل | عنوان اللوحة | المقياس | التاريخ | رقم اللوحة |
|---|---|---|---|---|
| **كوخ A-frame بواجهة زجاج + ميزانين — صالة وغرفة ومطبخ أمريكي وحمام — 9.00 × 10.00 م عميل — A-frame 9×10** | **المنظور والمواد** | **—** | **2026-10-23** | **A-10 (10/10)** |

**مصنع وتد الأخشاب**
Watad Wood Factory