
المنظور ثلاثي الأبعاد والمواد

النمط: برتقالي محمر + قرميد فحمي + دربزين X — رندر واقعي بخامات حقيقية

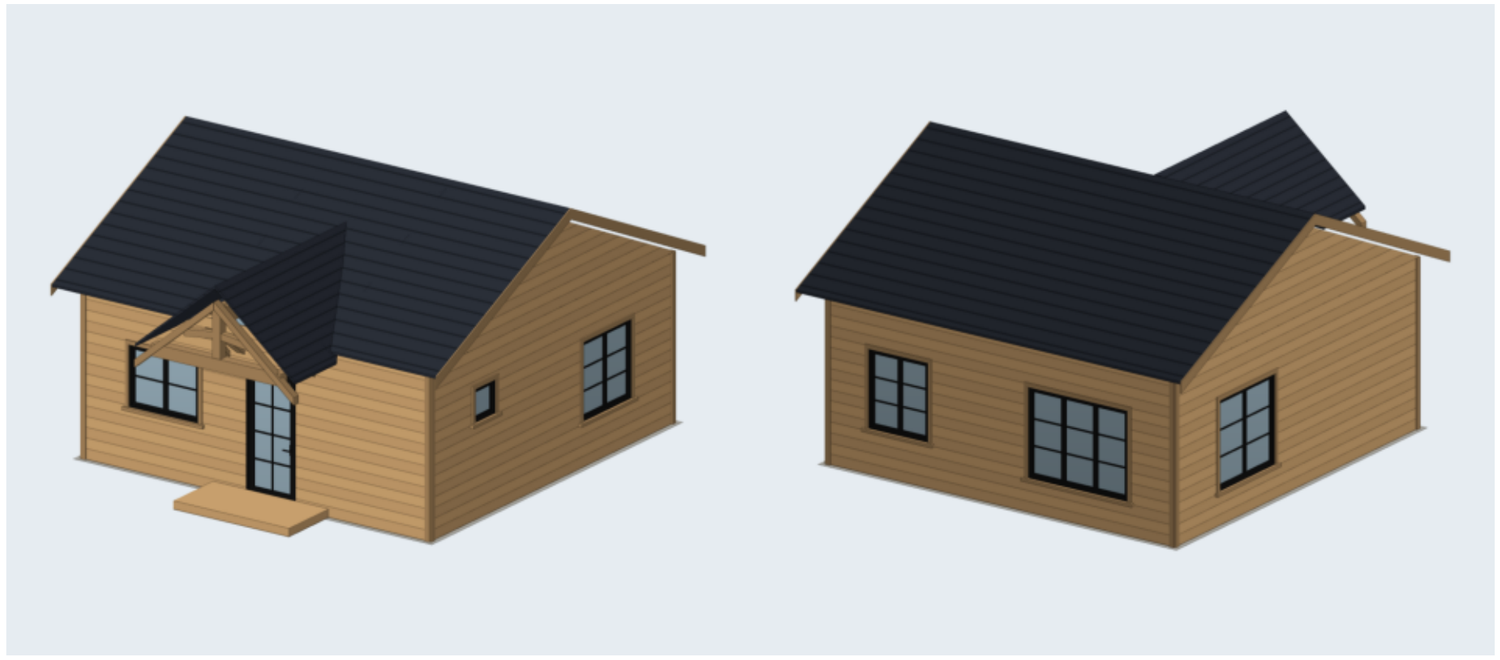

جدول المواد والألوان

الخشب / الصبغة

خشب طبيعي فاتح (بدون صبغة)

القرميد

قرميد فحمي / أسود مزرق

الزجاج

زجاج شفاف

إطارات الشبابيك والأبواب

إطار ألمنيوم أسود

الكنار والزوايا

نفس الصبغة أغمق درجة


الصبة

خرسانة 0 سم


الدربزين: ألواح أفقية متقاربة (عصري)

تقسيم الشبابيك: شبكة | الباب الرئيسي: زجاج بتقسيمات (فرنسي)

أنواع الدربزين المعتمدة (من مشاريع المصنع)

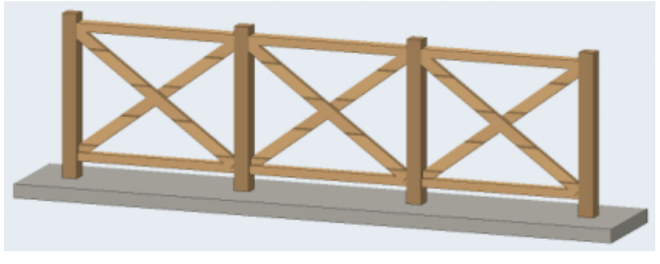

تقاطع X (صورة 5)

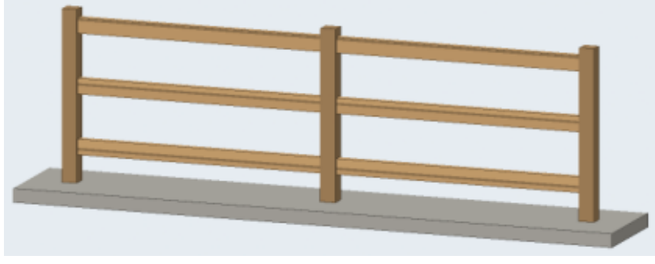

3 مرابيع أفقية (صورة 2)




قوائم رأسية متقاربة (صورة 1)

المشروع / العميل	عنوان اللوحة	المقياس	التاريخ	رقم اللوحة
ملحق سطح – غرفة نوم + صالة + مطبخ مفتوح + حمام – 7.00 × 7.00 م – الطائف **عميل – الطائف (سطح)**	**المنظور والمواد**	**1:50**	**2026-11-08**	**W-01 (1/13)**

مصنع وتد الأخشاب
Watad Wood Factory


المسقط الأفقي مع الفرش

الأبعاد بالسنتيمتر - الجدران: قوائم 7×5 + تلبيس 2.5 من الجهتين (12 سم)

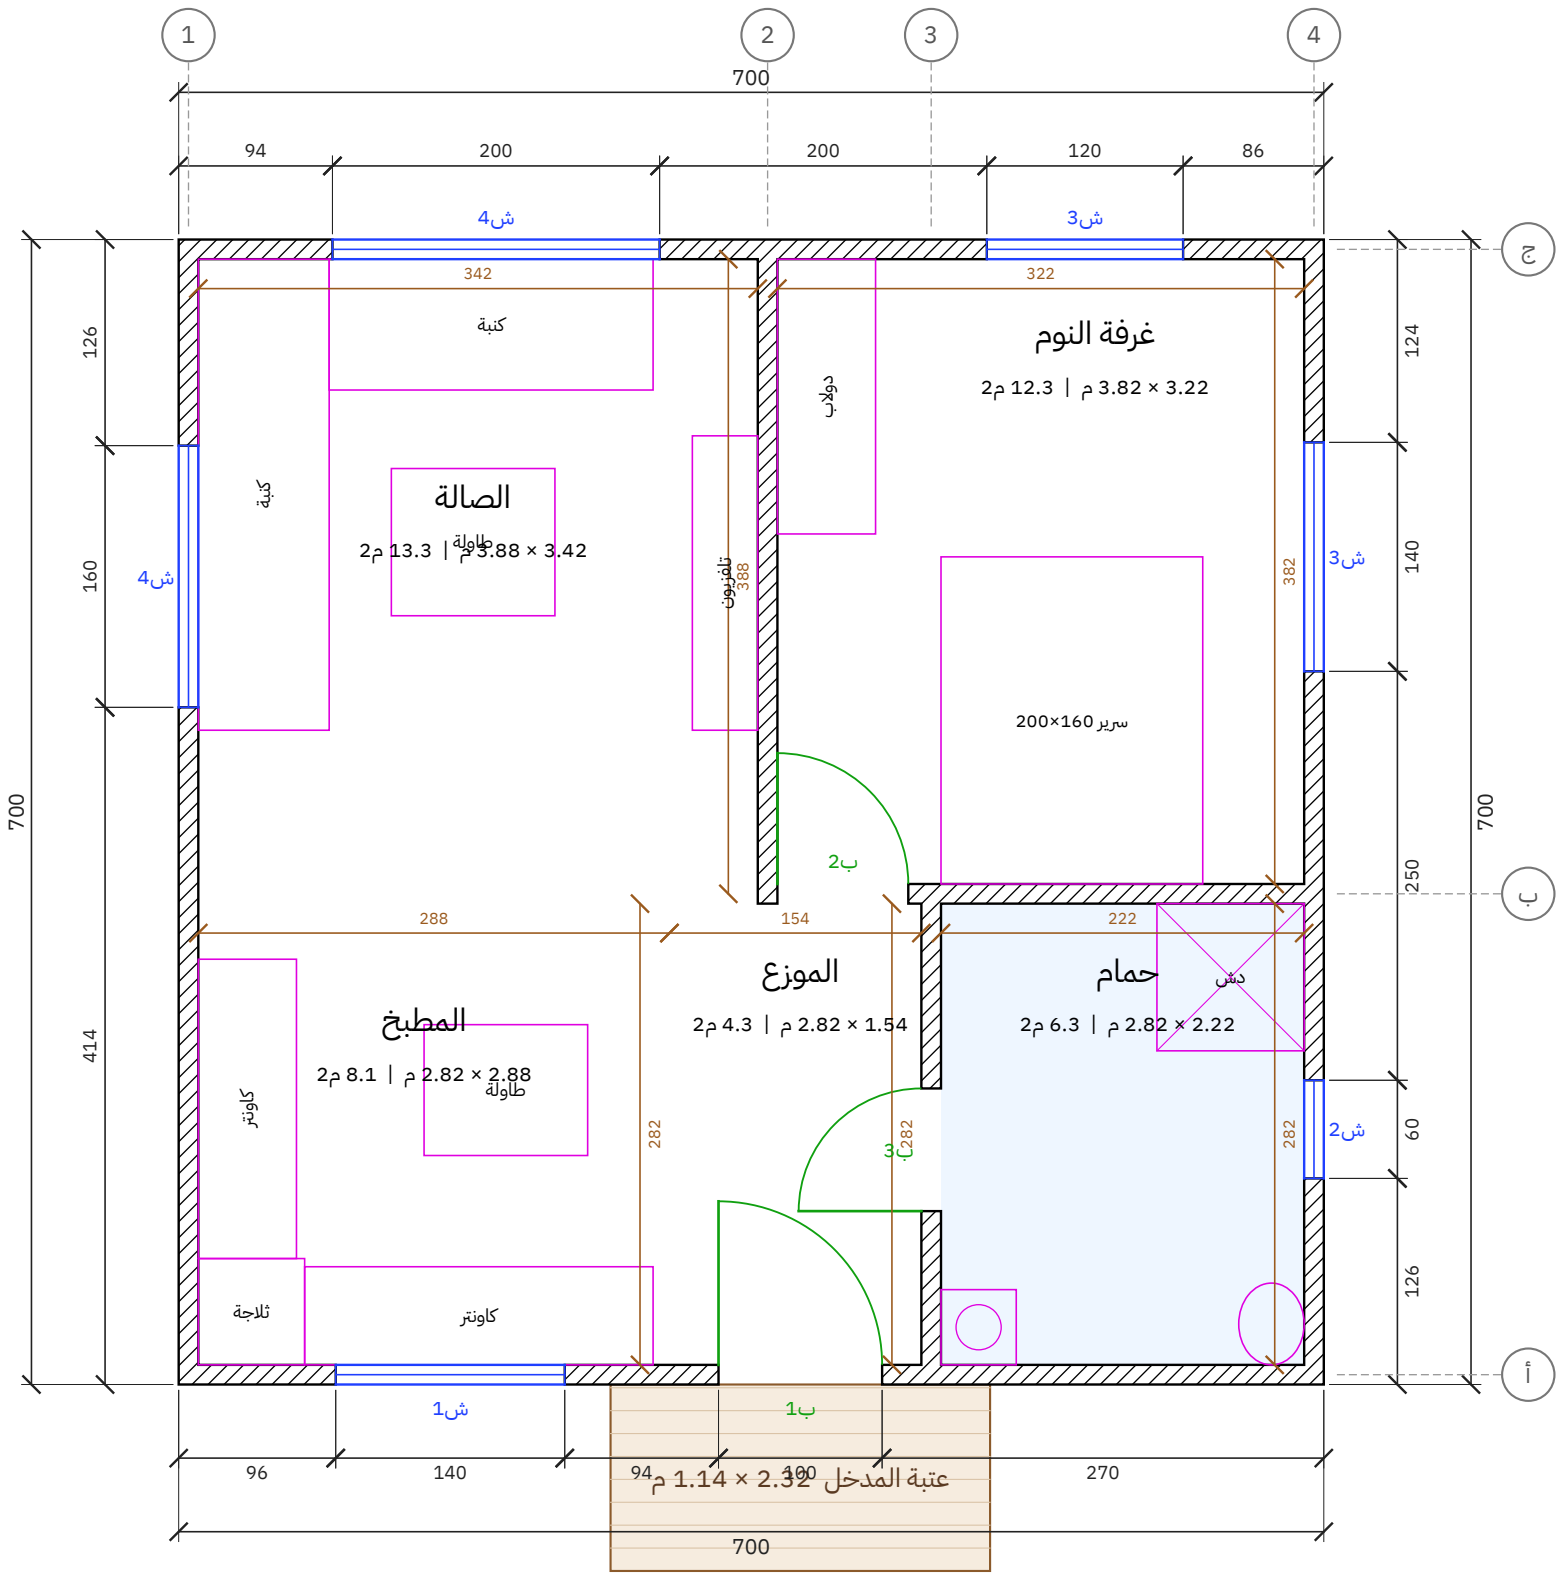


المشروع / العميل	عنوان اللوحة	المقياس	التاريخ	رقم اللوحة
ملحق سطح – غرفة نوم + صالة + مطبخ مفتوح + حمام – 7.00 × 7.00 م – الطائف عميل – الطائف (سطح)	المسقط الأفقي	1:50	2026-11-08	W-02 (2/13)

مصنع وتد الأخشاب
Watad Wood Factory

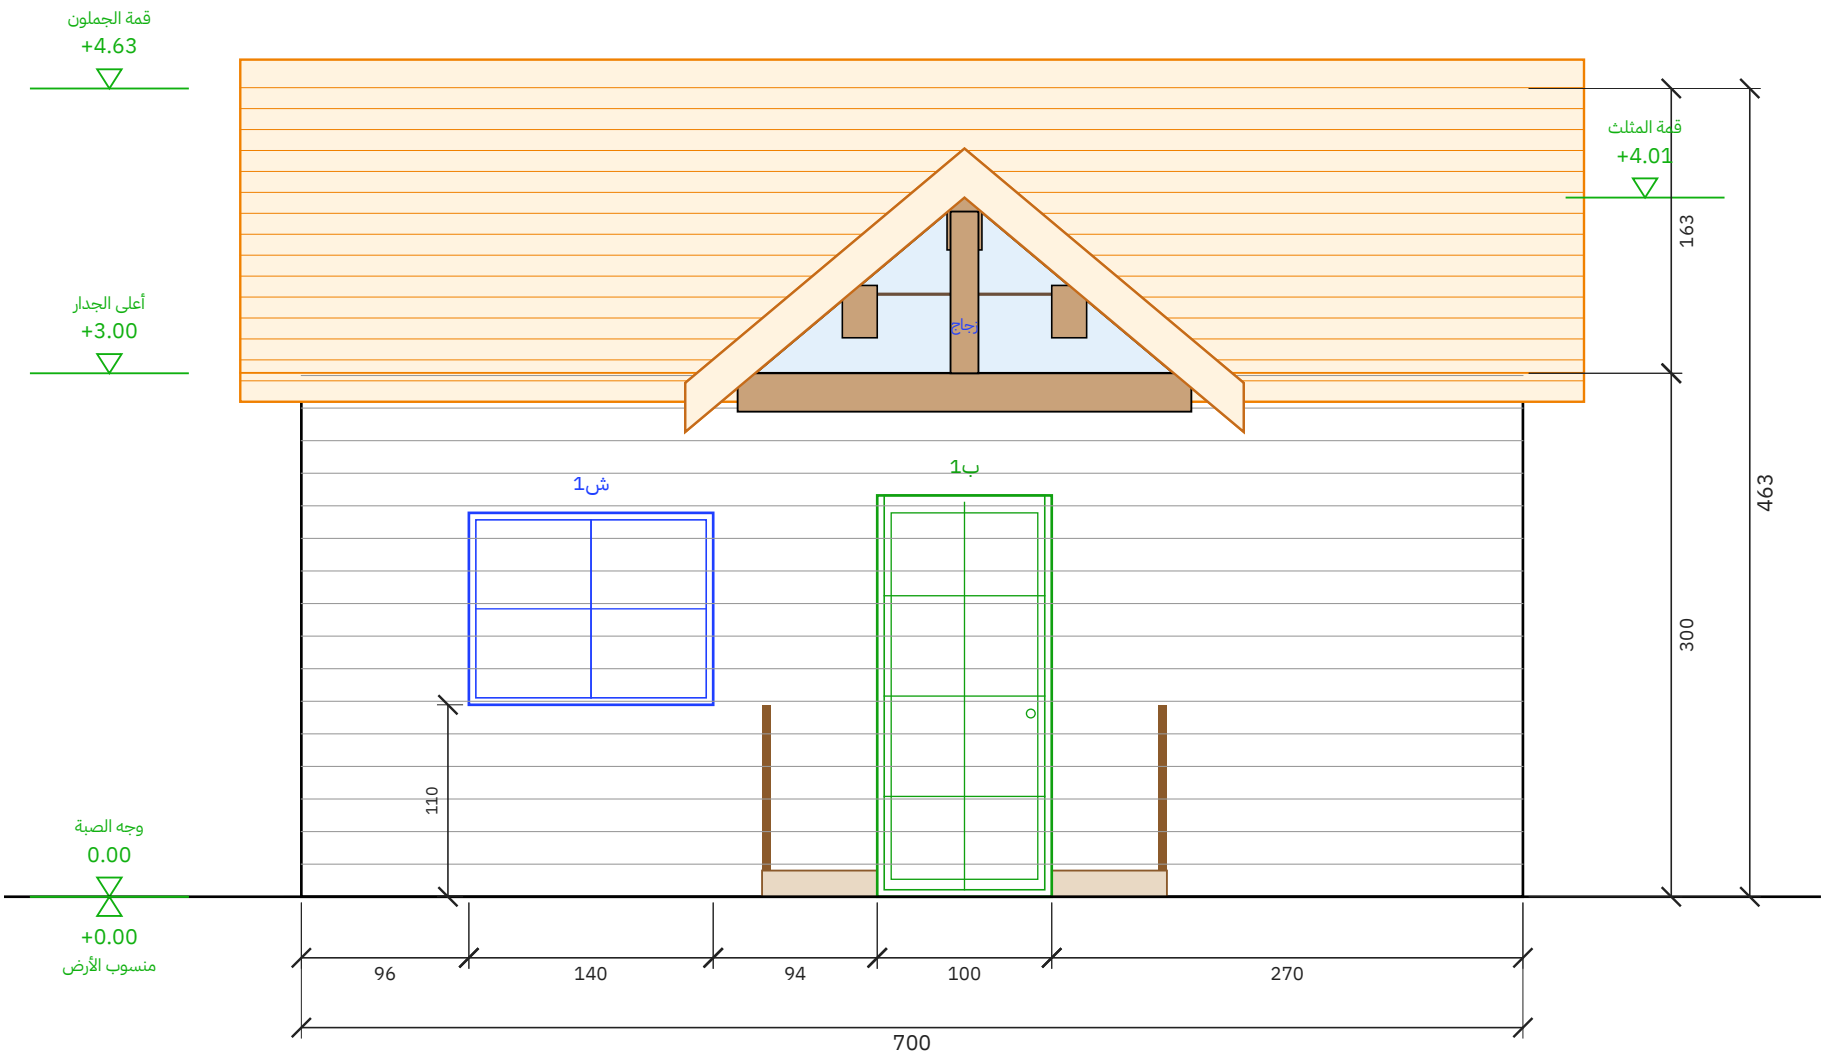

جدار المدخل (جهة درج السطح)

مقياس 1:50 | الوحدة: سم

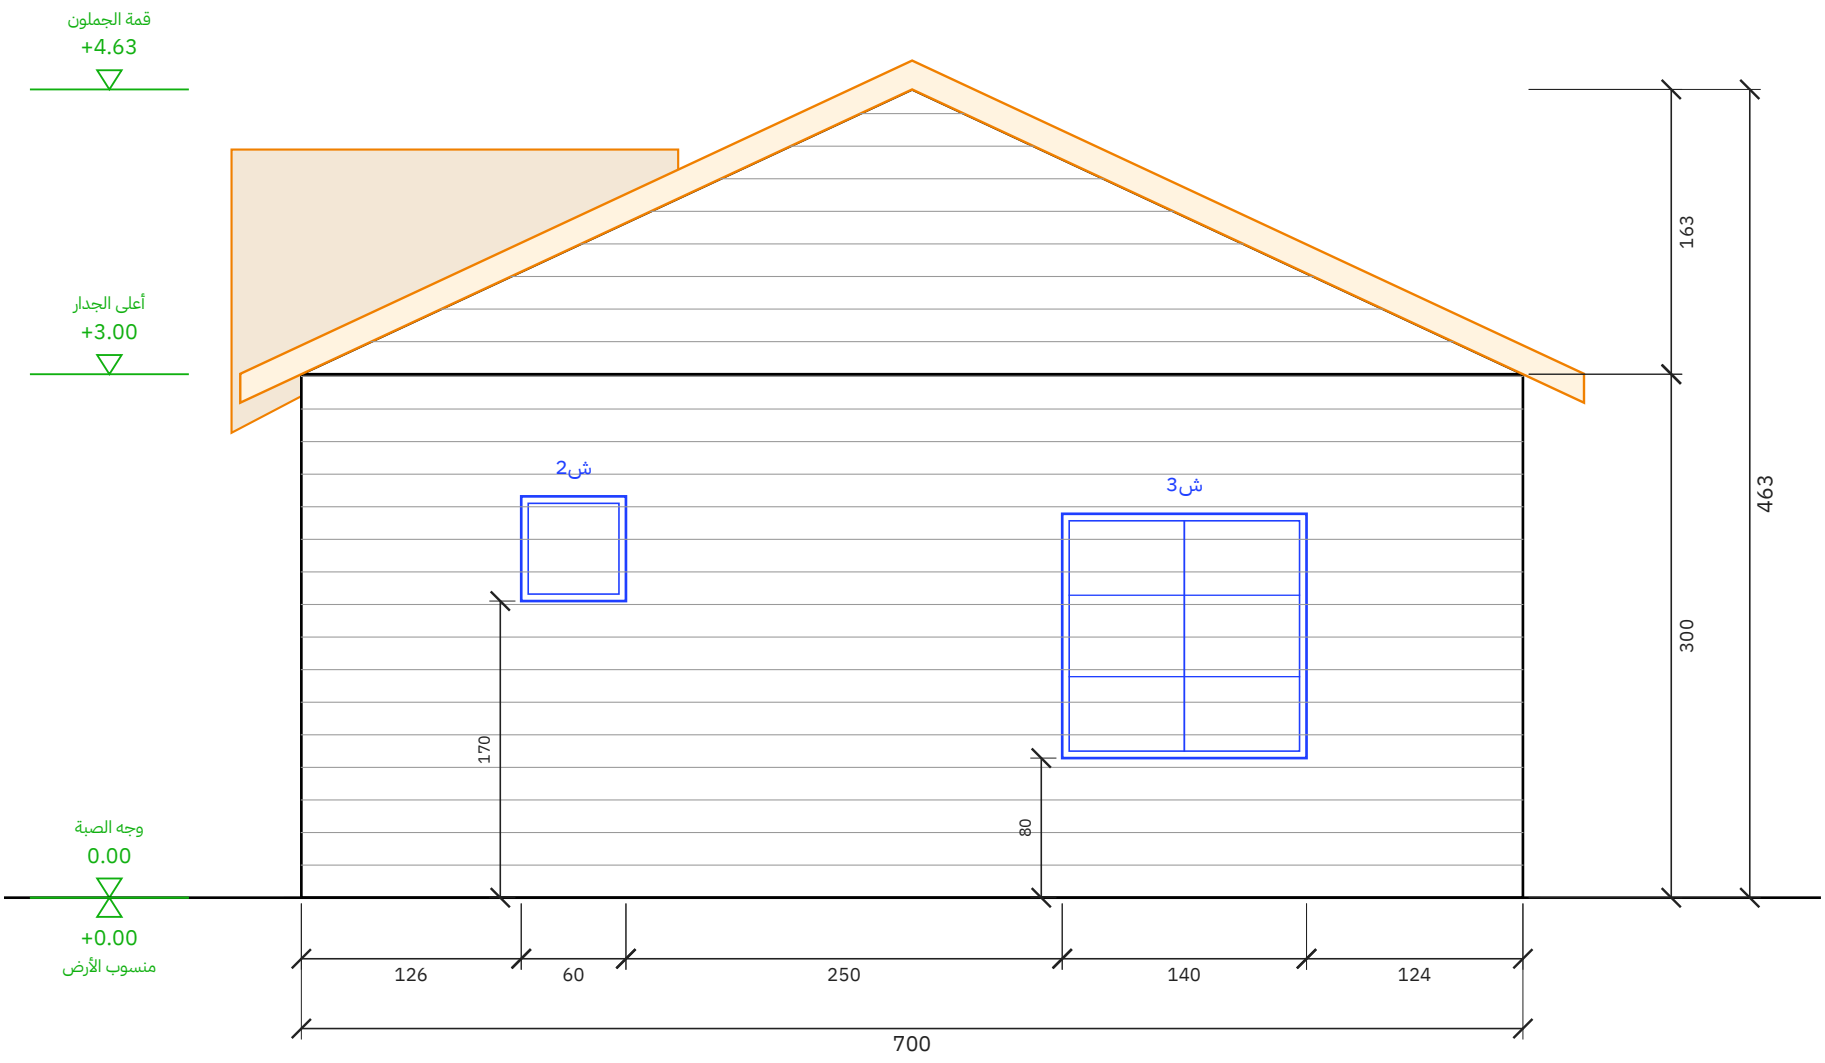


الجدار الأيمن

مقياس 1:50 | الوحدة: سم


المشروع / العميل	عنوان اللوحة	المقياس	التاريخ	رقم اللوحة
ملحق سطح – غرفة نوم + صالة + مطبخ مفتوح + حمام – 7.00 × 7.00 م – الطائف عميل – الطائف (سطح)	جدار المدخل (جهة درج السطح) والجدار الأيمن	1:50	2026-11-08	W-03 (3/13)

مصنع وتد الأخشاب
Watad Wood Factory

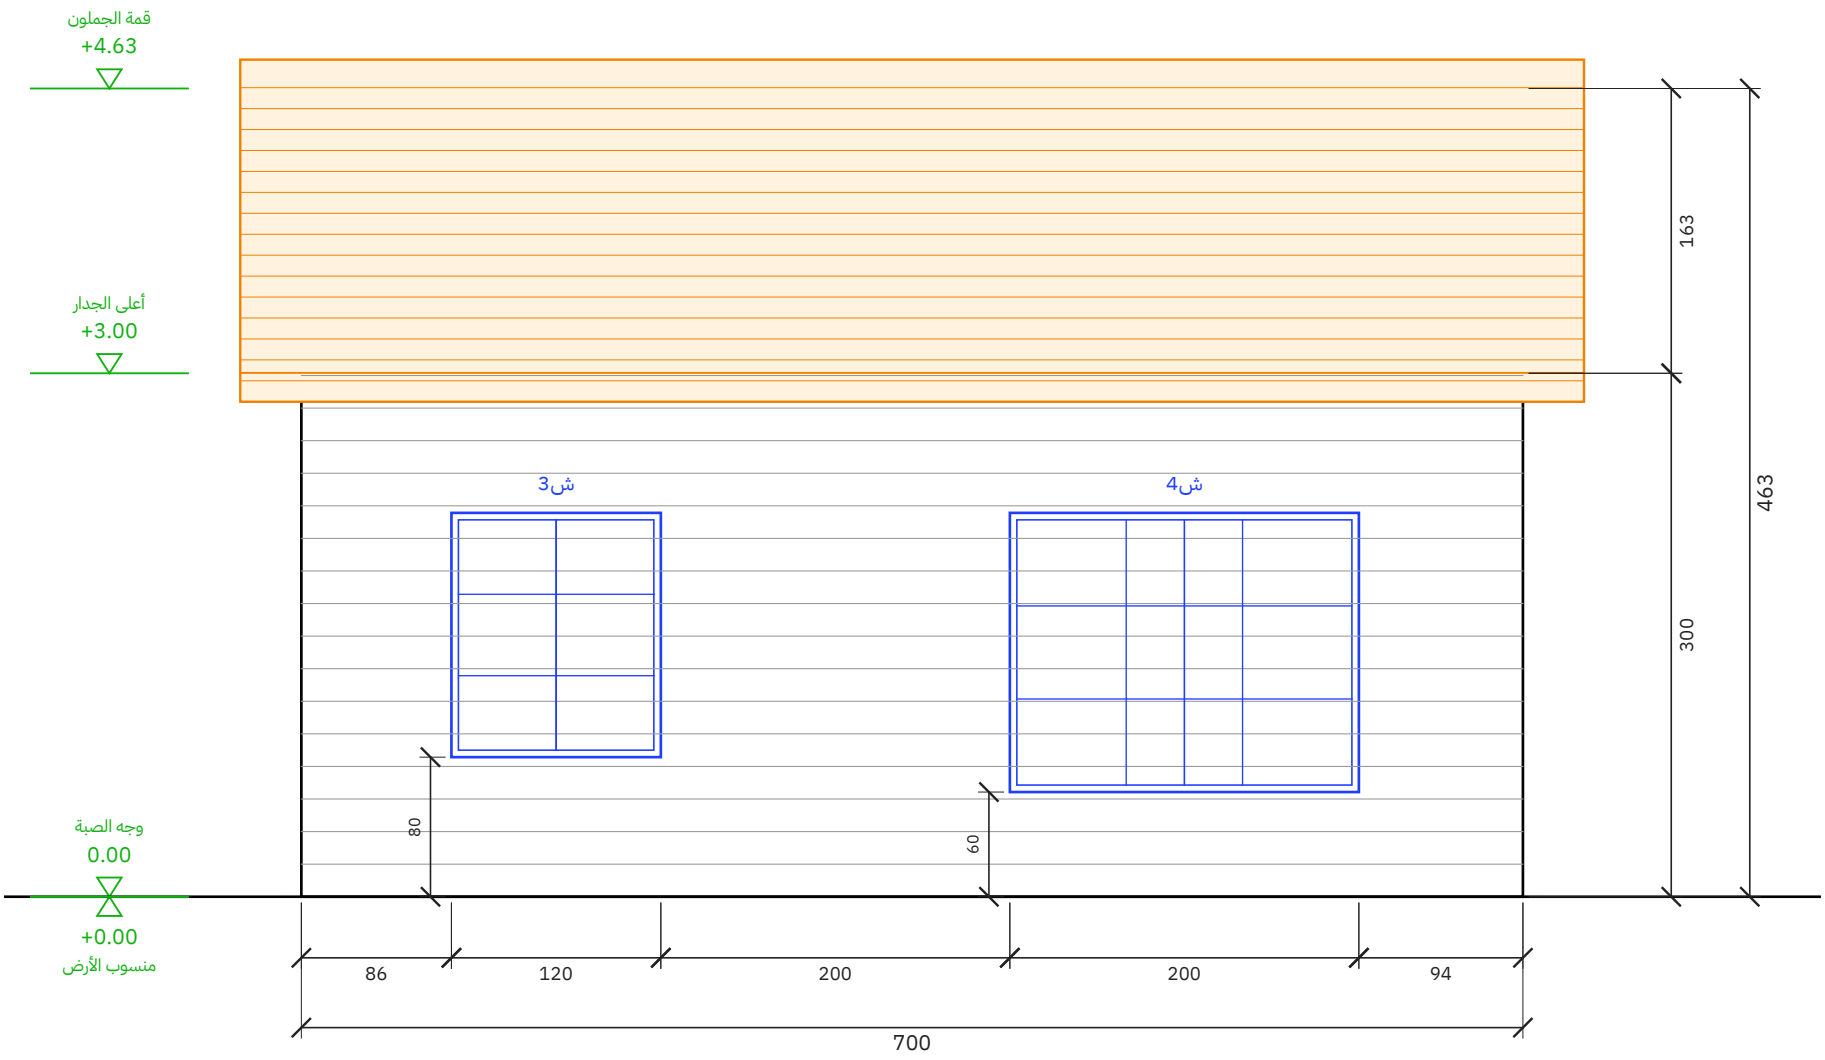

الجدار الخلفي

مقياس 1:50 | الوحدة: سم

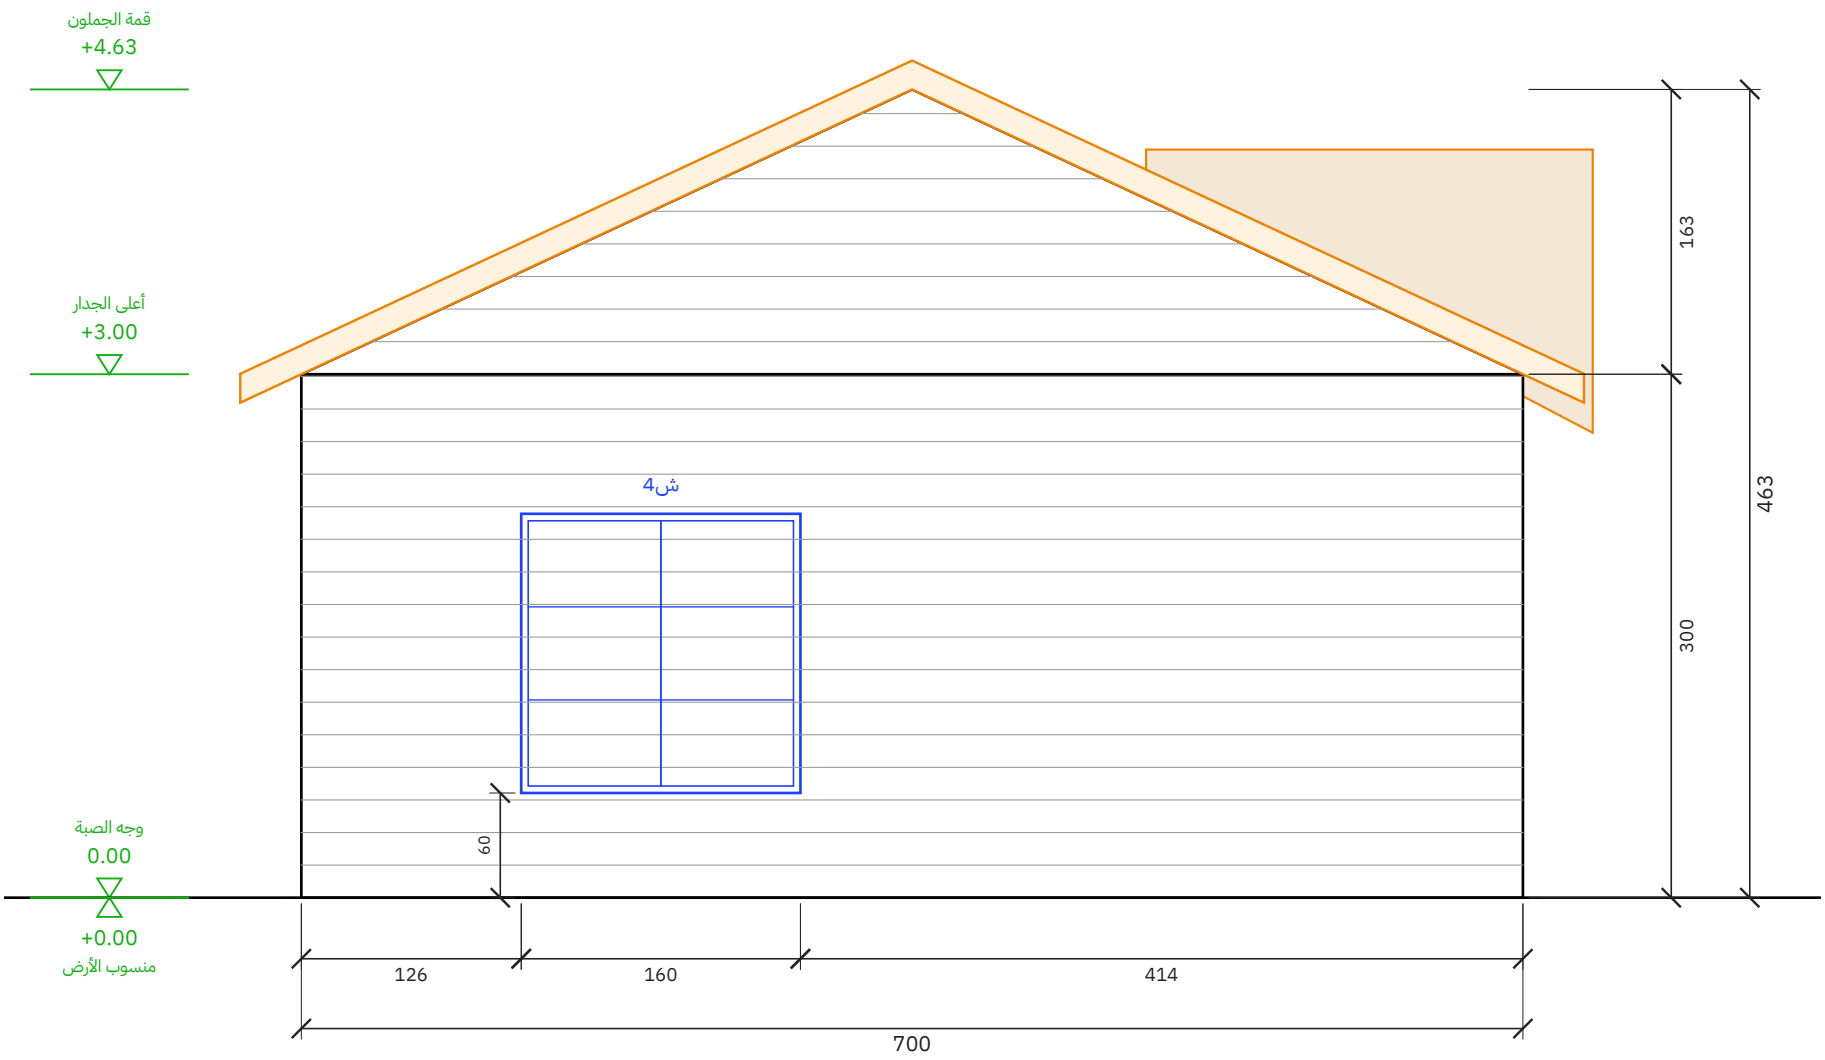

الجدار الأيسر


مقياس 1:50 | الوحدة: سم

المشروع / العميل	عنوان اللوحة	المقياس	التاريخ	رقم اللوحة
ملحق سطح – غرفة نوم + صالة + مطبخ مفتوح + حمام – 7.00 × 7.00 م – الطائف عميل – الطائف (سطح)	الجدار الخلفي والجدار الأيسر	1:50	2026-11-08	W-04 (4/13)

مصنع وتد الأخشاب
Watad Wood Factory

مسقط السقف (جملون)

رفرف 35 سم من كل جهة | مقياس 1:50

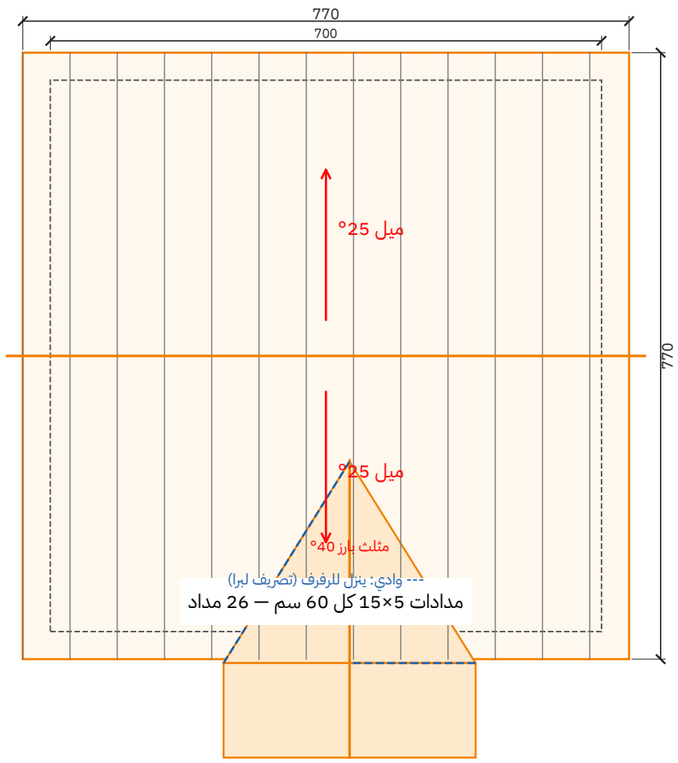


قطاع عرضي أ-أ

مقياس 1:50 | الوحدة: سم



تفصيلة جلوس المداد على العلوي (1:5)

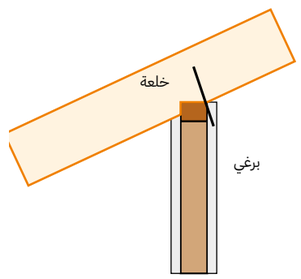

علوي 7×5 على قائم 7×5

المشروع / العميل	عنوان اللوحة	المقياس	التاريخ	رقم اللوحة
ملحق سطح — غرفة نوم + صالة + مطبخ مفتوح + حمام — 7.00 × 7.00 م — الطائف **عميل — الطائف (سطح)**	**مسقط السقف والقطاع**	**1:50**	**2026-11-08**	**W-05 (5/13)**

مصنع وتد الأخشاب
Watad Wood Factory

جدول مقاسات الأبواب والشبابيك

مقاس الفتحة الصافي في الجدار - الوحدة: سم

الرمز	النوع	العرض (سم)	الارتفاع (سم)	ارتفاع الجلسة (سم)	العدد	الموقع
ب1	باب	100	230	-	1	جدار المدخل (جهة درج السطح)
ب2	باب	80	220	-	1	غرفة النوم
ب3	باب	75	210	-	1	الحمام
ش1	شباك	140	110	110	1	جدار المدخل (جهة درج السطح)
ش2	شباك	60	60	170	1	الجدار الأيمن
ش3	شباك	140	140	80	1	الجدار الأيمن
ش3	شباك	120	140	80	1	الجدار الخلفي
ش4	شباك	200	160	60	1	الجدار الخلفي
ش4	شباك	160	160	60	1	الجدار الأيسر

الإجمالي: أبواب 3 - شبابيك 6

جدول المساحات وبيانات المشروع


بيانات المشروع

البند	البيان
المشروع	ملحق سطح — غرفة نوم + صالة + مطبخ مفتوح + حمام — 7.00 × 7.00 م — الطائف
العميل	عميل — الطائف (سطح)
الموقع	الطائف
الاستخدام	ملحق سكني على السطح
التاريخ	2026-11-08
نظام البناء	هيكل خشب 5×7 + تلبيس 2.5 سم من الجهتين
السقف	جملون 25° — قرميد معدني + 1 مثلث بارز


جدول المساحات

م	الفراغ	الأبعاد (م)	المساحة (م2)
1	المطبخ	2.82 × 2.88	8.12
2	الموزع	2.82 × 1.54	4.34
3	حمام	2.82 × 2.22	6.26
4	الصالة	3.42 × 3.88	13.27
5	غرفة النوم	3.22 × 3.82	12.30
	المساحة الصافية الداخلية		**44.29**
	عتبة المدخل	**2.32 × 1.14**	**2.64**
	المساحة الإجمالية المبنية	**7.00 × 7.00**	**49.00**
	المساحة الكلية (المبنية + التراس)		**51.64**

تأطير جدار جنوب — الطول 688 سم، الارتفاع 300 سم

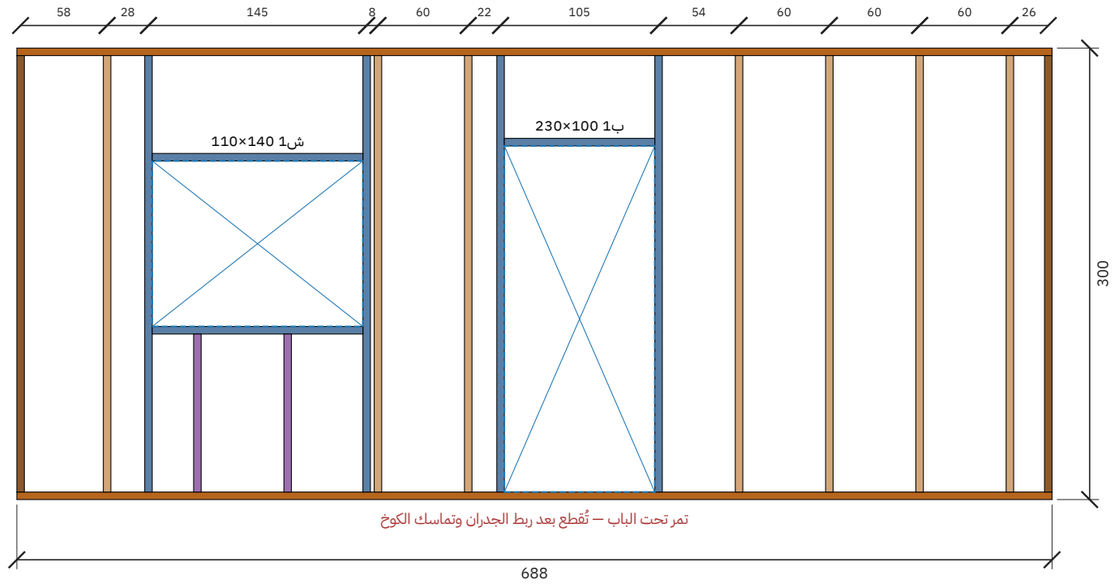

تأطير جدار شرق — الطول 688 سم، الارتفاع 300 سم

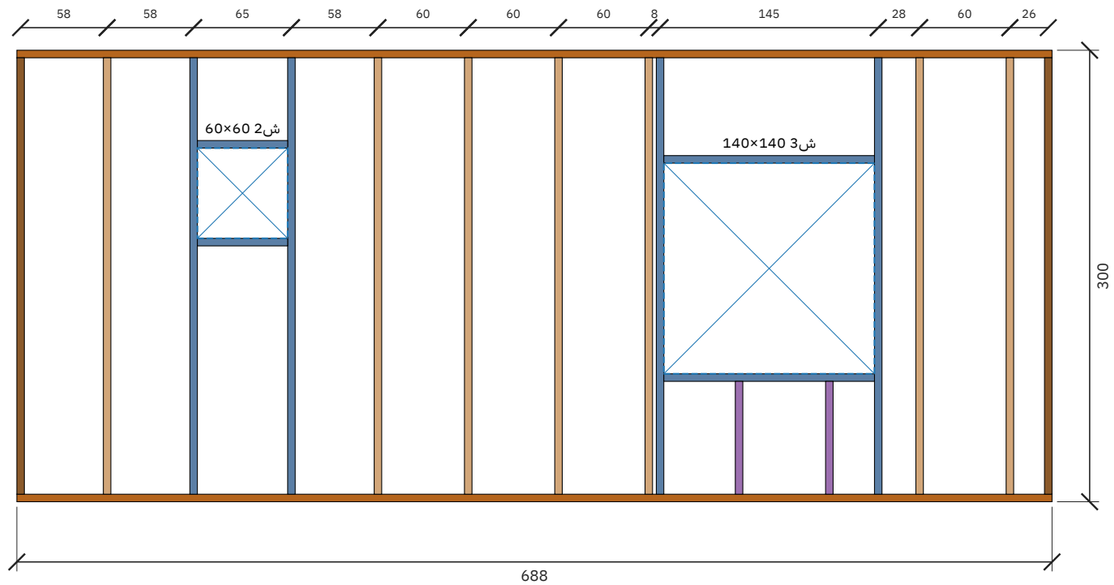


قاعدة سفلية | علوي | عمود | عمود زاوية | جنب فتحة | رأس فتحة | جلسة شباك | عمود قصير


المشروع / العميل	عنوان اللوحة	المقياس	التاريخ	رقم اللوحة
ملحق سطح — غرفة نوم + صالة + مطبخ مفتوح + حمام — 7.00 × 7.00 م — الطائف **عميل — الطائف (سطح)**	**لوحات التأطير (للورشة)**	**—**	**2026-11-08**	**W-08 (8/13)**

مصنع وتد الأخشاب
Watad Wood Factory

تأطير جدار شمال — الطول 688 سم، الارتفاع 300 سم

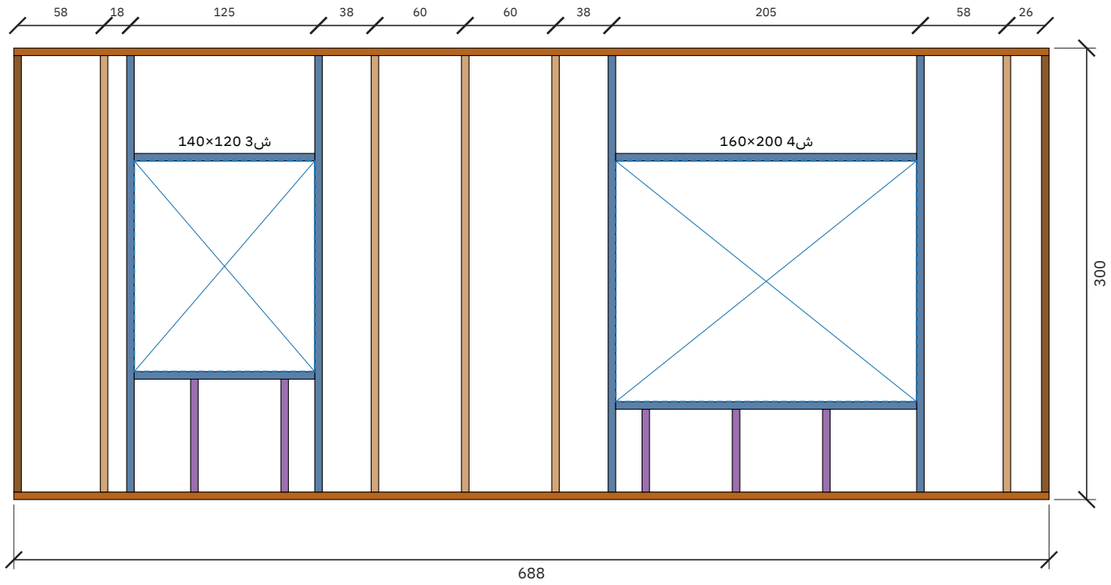

تأطير جدار غرب — الطول 688 سم، الارتفاع 300 سم

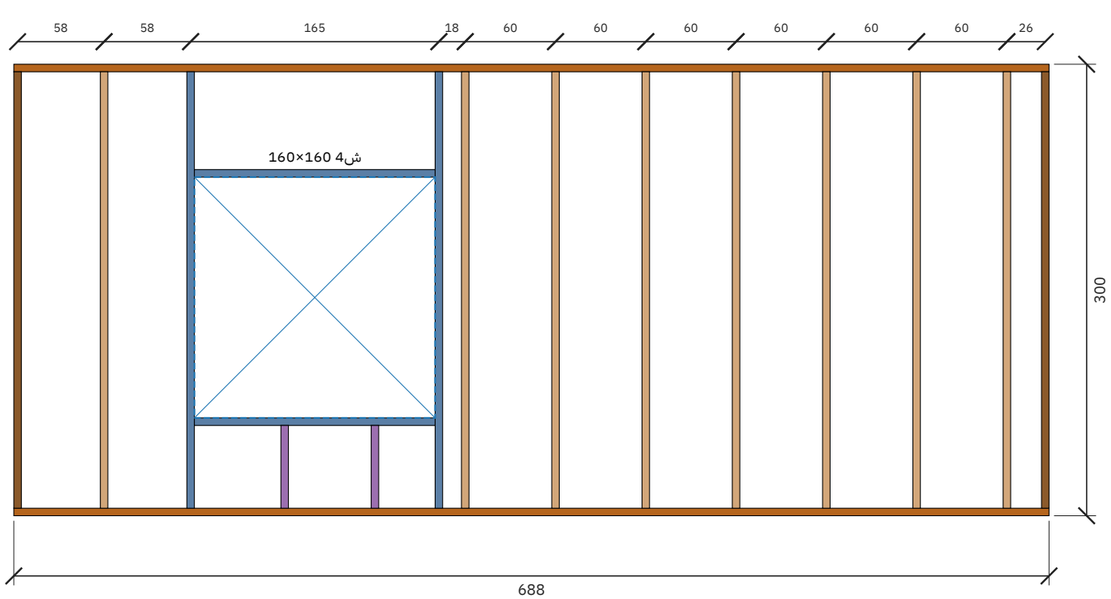


قاعدة سفلية | علوي | عمود | عمود زاوية | جنب فتحة | رأس فتحة | جلسة شباك | عمود قصير


المشروع / العميل	عنوان اللوحة	المقياس	التاريخ	رقم اللوحة
ملحق سطح — غرفة نوم + صالة + مطبخ مفتوح + حمام — 7.00 × 7.00 م — الطائف عميل — الطائف (سطح)	لوحات التأطير (للورشة)	—	2026-11-08	W-09 (9/13)

مصنع وتد الأخشاب
Watad Wood Factory

تأطير جدار جدار غرفة النوم — الصالة — الطول 394 سم، الارتفاع 300 سم (داخلي)

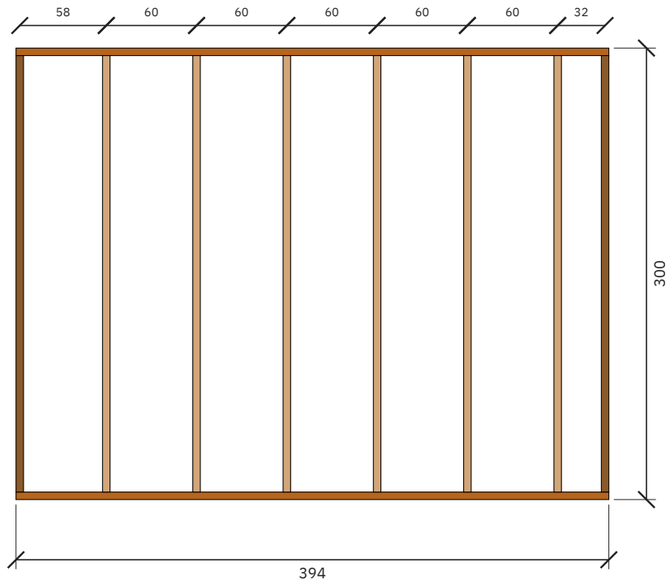


تأطير جدار جدار الحمام وغرفة النوم — الطول 334 سم، الارتفاع 300 سم (داخلي)

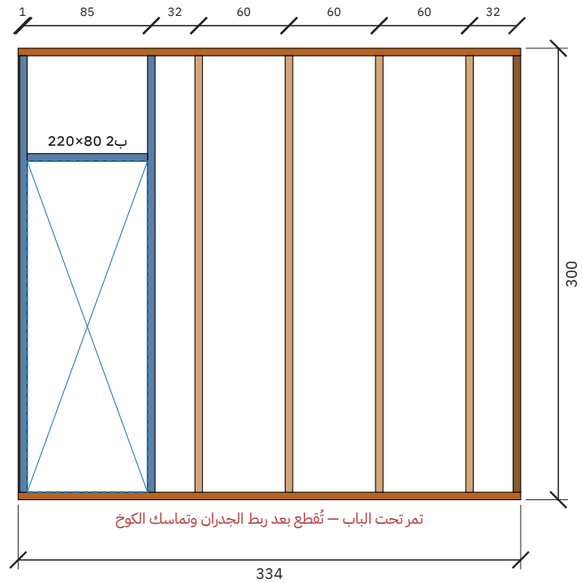

قاعدة سفلية | علوي | عمود | عمود زاوية | جنب فتحة | رأس فتحة | جلسة شباك | عمود قصير

مصنع وتد الأخشاب Watad Wood Factory	المشروع / العميل **ملحق سطح — غرفة نوم + صالة + مطبخ مفتوح + حمام — 7.00 × 7.00 م — الطائف** **عميل — الطائف (سطح)**	عنوان اللوحة **لوحات التأطير (للورشة)**	المقياس **—**	التاريخ **2026-11-08**	رقم اللوحة **W-10 (10/13)**

تأطير جدار جدار الحمام — الموزع — الطول 294 سم، الارتفاع 300 سم (داخلي)

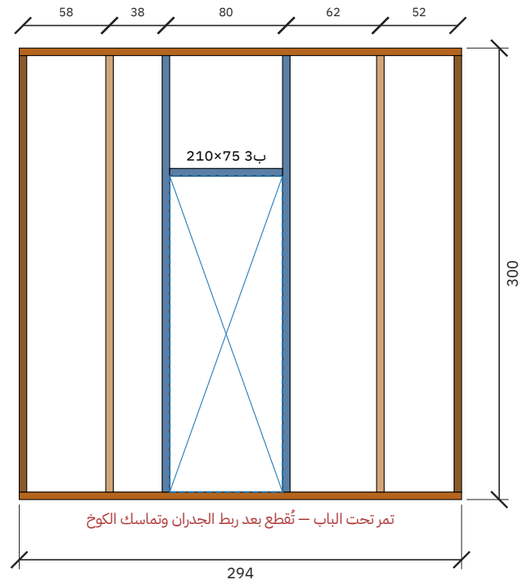

عمود قصير
جلسة شباك
رأس فتحة
جنب فتحة
عمود زاوية
عمود
علوي
قاعدة سفلية

مصنع وتد الأخشاب Watad Wood Factory	المشروع / العميل **ملحق سطح — غرفة نوم + صالة + مطبخ مفتوح + حمام — 7.00 × 7.00 م — الطائف** **عميل — الطائف (سطح)**	عنوان اللوحة **لوحات التأطير (للورشة)**	المقياس **—**	التاريخ **2026-11-08**	رقم اللوحة **W-11 (11/13)**

جدول الكميات وخطة تقطيع الطبليات

البند	القيمة
الارتفاع المطلوب / المعتمد	300 / 300 سم
السقف	جملون 25° — أعلى نقطة 463 سم من وجه الصبة
المدادات 5×15	26 مداد (13 لكل جهة) × حتى 425 سم — من طبلية 480
طبليات الطريقة الأولى (مداد + عمود)	26 طبلية × 480 سم
طبليات الطريقة الثانية (3 أعمدة)	23 طبلية × 320 سم
مدادات المثلث البارز (S) 40°	10 مداد حتى 170 سم (طبلية 320) + 2 مداد وادي 330 سم
إجمالي الطبليات 5×22.5	61
إجمالي قطع 5×7	111
قائمة تقطيع 5×7	688سم×8 | 394سم×2 | 334سم×2 | 294سم×2 | 290سم×71 | 200سم×2 | 160سم×2 | 140سم×4 | 120سم×2
	105سم×2 | 100سم×1 | 80سم×1 | 75سم×5 | 60سم×2 | 55سم×5
ألواح تلبيس 2.5 سم	248 لوح × 400 سم (مجموع الصفوف 915.2 م، 14 وجه)
أسمنت بورد 12 مم (122×244)	20 لوح (داخل دورات المياه)
العزل	134 لوح فوم صخري 80
الصبة	يجهزها العميل — 20 سم، مفرغة تحت دورات المياه

مراجعة التصميم مقابل قواعد المصنع

النوع	البند	التفاصيل	المقترح
خطأ	ب2 غرفة النوم في جدار الحمام وغرفة النوم	الفتحة ملاصقة لطرف الجدار — ما فيه مكان لإطار 7×5.	تُزاح الفتحة 10 سم على الأقل عن الزاوية.
ملاحظة	بحر المدادات	أطول بحر بدون جدار داخلي يحمل المداد: جهة أ: 350 سم، جهة ب: 350 سم. يحتاج رقم المصنع لأقصى بحر مسموح لتحديد المدادات اللي تُقوّى 20×5.	
ملاحظة	الصبة والدرج	ارتفاع الصبة 0 سم ← 1 درجة بقائمة 0.0 سم. بارتفاع 20 سم ما يطلع إلا درجة وحدة؛ للدكة المرتفعة 45 سم = 3 درجات.	
ملاحظة	مناسيب رؤوس الفتحات	رؤوس الأبواب والشبابيك على مناسيب مختلفة: 210، 220، 230 سم.	
سؤال	يحتاج تأكيد	أقصى بحر للمداد بدون جدار داخلي قبل إضافة تقوية 7×5 (مداد 20×5)؟	
سؤال	يحتاج تأكيد	التغطية الصافية للوح التلبيس بعد التعشيق (مستنتجة مؤقتاً 18.67 سم من 280/15)؟	
سؤال	يحتاج تأكيد	هل يوضع أعمدة قصيرة فوق رأس الشباك/الباب إلى العلوي؟	
سؤال	يحتاج تأكيد	مكان الوصلة في القاعدة والعلوي إذا الجدار أطول من الطبلية؟	