



المسقط الأفقي ومسقط السقف
مقياس 1:50 | الوحدة: سم

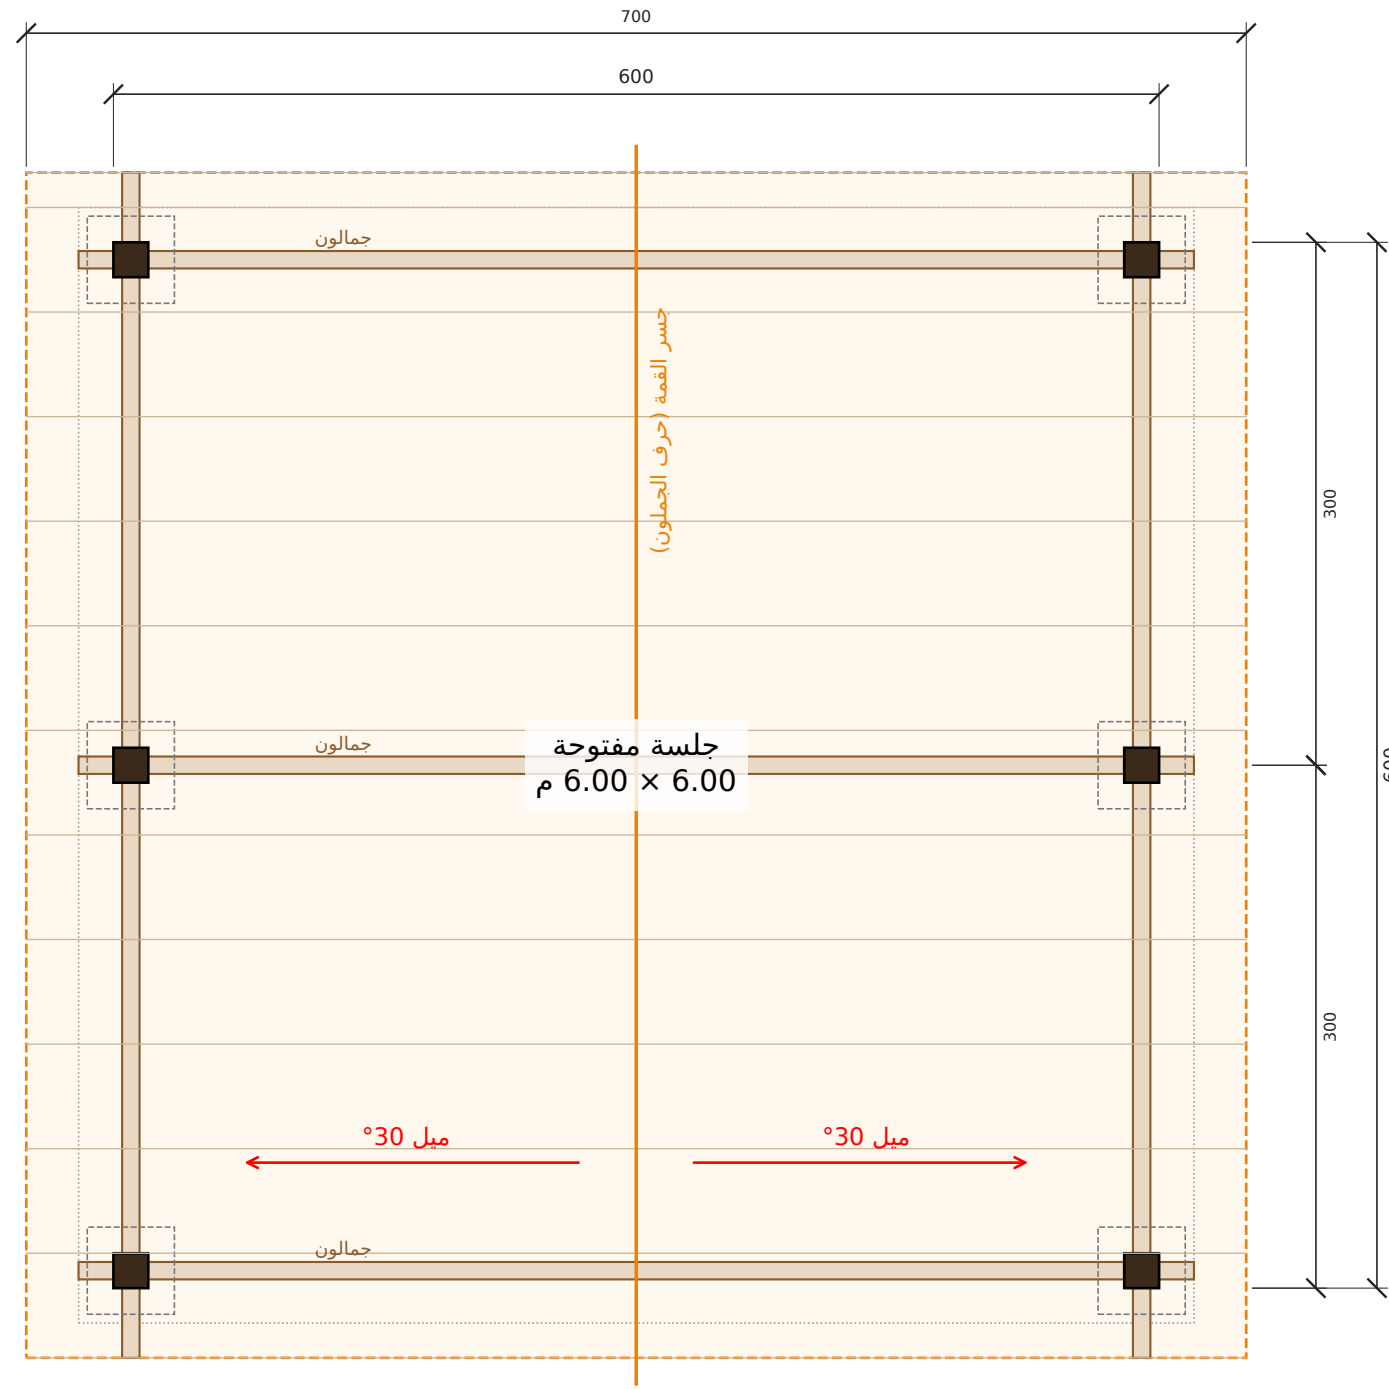

الواجهة الأمامية (الجملون)

■ عمود 20×20 على قاعدة حديد ومسمار تثبيت في قاعدة خرسانة 50×50 (المتقطع) ■ الرفرف المتقطع = حدود السقف

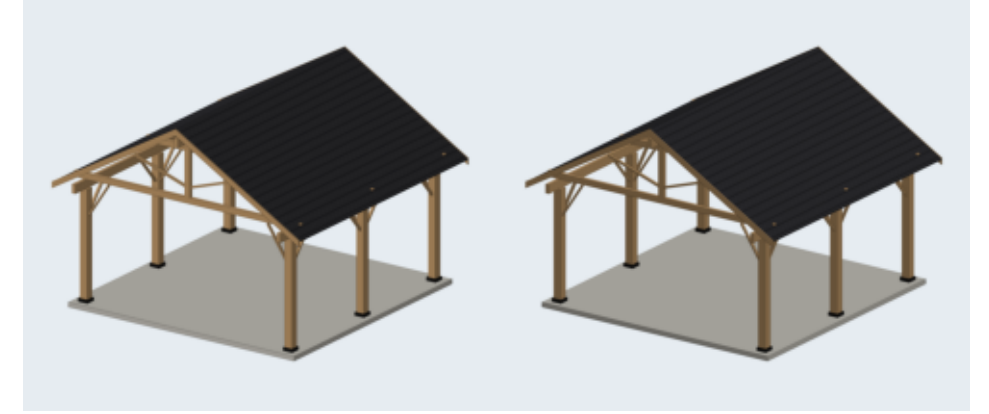

رقم اللوحة

A-01 (1/5)

التاريخ

2026-10-07

المقياس

1:50

عنوان اللوحة

المسقط ومسقط السقف

المشروع / العميل



برجولة خشب 6×6 بجمالونات مكشوفة
عميل — برجولة

مصنع وتد الأخشاب
Watad Wood Factory



الواجهة الأمامية — جمالون مكشوف
مقياس 1:50

الواجهة الجانبية
مقياس 1:50

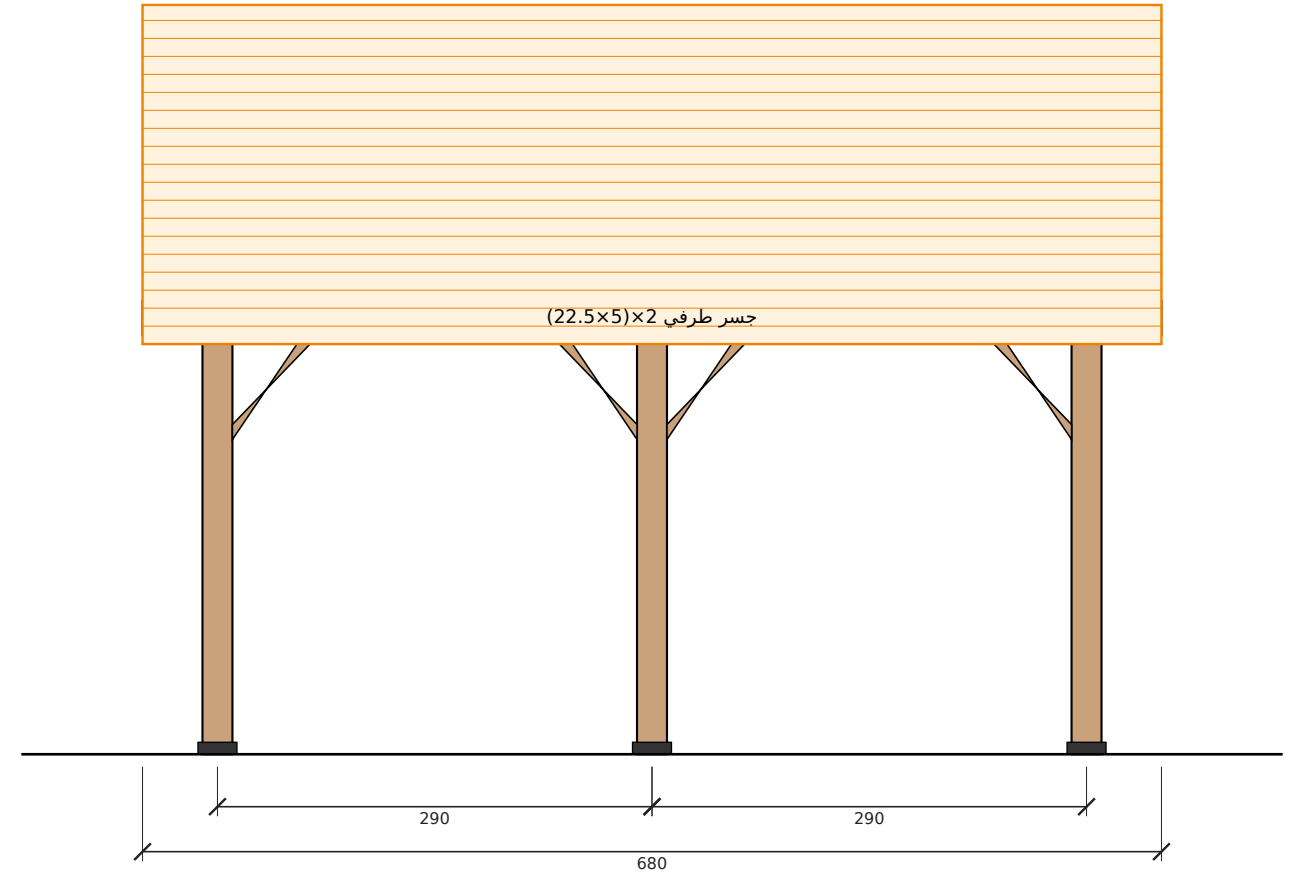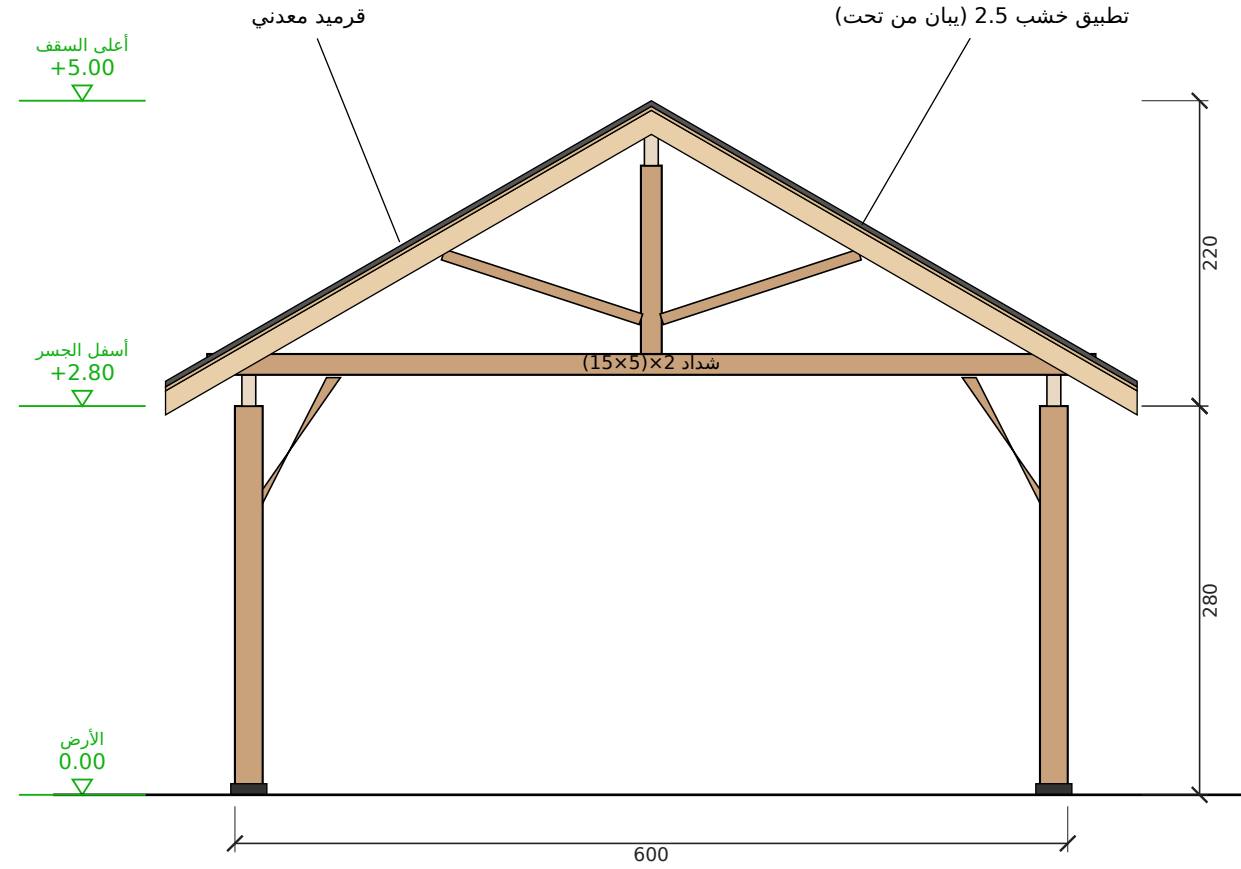

رقم اللوحة

A-02 (2/5)

التاريخ

2026-10-07

المقياس

1:50

عنوان اللوحة

الواجهات


المشروع / العميل

برجولة خشب 6x6 بجمالونات مكشوفة
عميل — برجولة


مصنع وتد الأخشاب
Watad Wood Factory




قطاع الجمالون (كل جمالون)

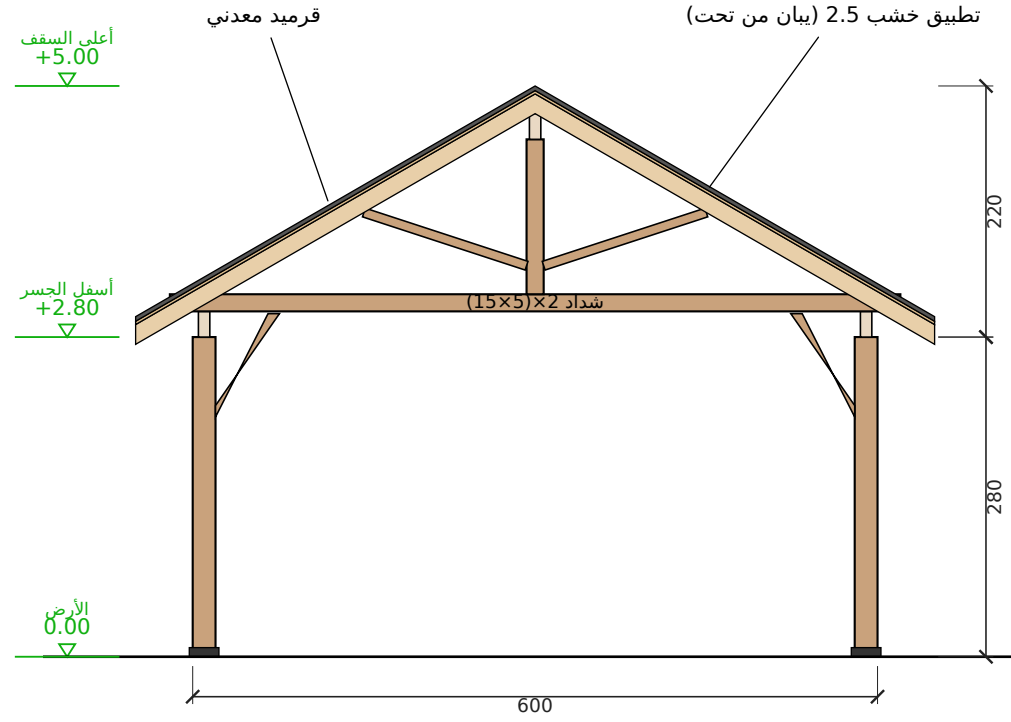

تفصيلة قاعدة العمود مقياس 1:10

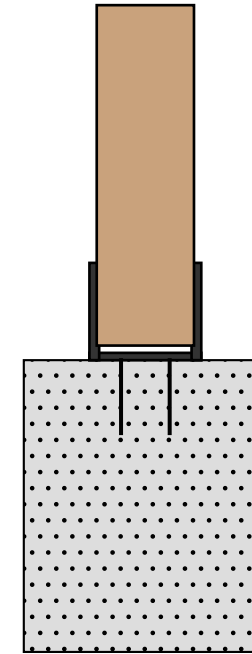

تفصيلة السقف — طبقتين فقط مقياس 1:5

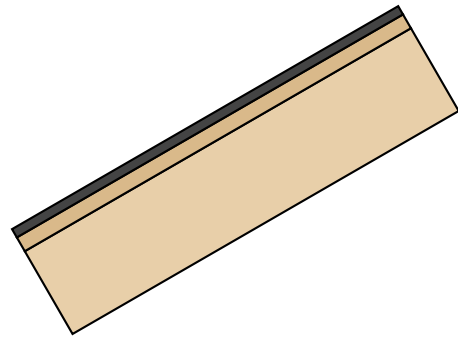

- (2) قرميد معدني مثبت ببراعي على التطبيق
(1) تطبيق خشب لسان ونقر 2.5 سم (السقف الداخلي)
مداد 15x5 كل 60 سم

رقم اللوحة

A-03 (3/5)

التاريخ

2026-10-07

المقياس

1:50 / 1:5

عنوان اللوحة

الجمالون والتفاصيل

المشروع / العميل

برجولة خشب 6x6 بجمالونات مكشوفة
عميل — برجولة

مصنع وتد الأخشاب
Watad Wood Factory



جدول الكميات وبيانات المشروع

الكميات

البند	الوصف	العدد	الطول (سم)	المقطع
أعمدة 20×20 (4 طبقات 20×5 مقصوصة من 22.5×5 مبرغية)	6 عمود × 280 سم	24	290	5×22.5
جسور طرفية (طبقتين 22.5×5) — وصلة فوق العمود الأوسط	2 خط × 680 سم	8	340	5×22.5
جسر القمة (طبقتين 22.5×5)	680 سم	4	340	5×22.5
شداد الجمالون (طبقتين 15×5) — نصين	3 جمالون	12	320	5×15
قائم الجمالون (طبقتين 15×5)	3 جمالون	6	136	5×15
أذرع الجمالون المائلة 15×5	3 × 2	6	157	5×15
مدادات 15×5 كل 60 سم	2 × 13 جهة	26	404	5×15
كوابيل الأعمدة 5×7		14	95	7×5
تطبيق خشب 2.5 سم (الطبقة 1)	55.0 م²	88	400	لوح
قرميد معدني (الطبقة 2) + غطاء الحرف وحواف الجملون	55.0 م²	—	حرف 680	م²
قواعد حديد U مجلفنة + قواعد خرسانة 60×50×50		6	—	طقم

العدد	الطبليات 22.5×5
18	طبليّة 320 سم (15×5)
24	طبليّة 320 سم (22.5×5)
26	طبليّة 480 سم (15×5)
12	طبليّة 480 سم (22.5×5)
80	الإجمالي

بيانات المشروع


البند	البيان
المشروع	برجولة خشب 6×6 بجمالونات مكشوفة
العميل	عميل — برجولة
التاريخ	2026-10-07
المقاس	6.00 × 6.00 م = 36.0 م²
الأعمدة	6 أعمدة 20×20 نازلة للأرض على قواعد حديد
السقف	جملون 30° — طبقتين: تطبيق خشب + قرميد معدني
الجمالونات	3 جمالون مكشوف (شداد + قائم + ذراعين)

التسعير

البند	القيمة
المساحة (م²)	36.00
سعر المتر	يُحدد بعد الاعتماد
الإجمالي	—

• الأرضية (بلاط/خرسانة) على العميل ما لم يُذكر غير ذلك. • الطبليات حسب طرق المصنع — TO_CONFIRM

المنظور ثلاثي الأبعاد

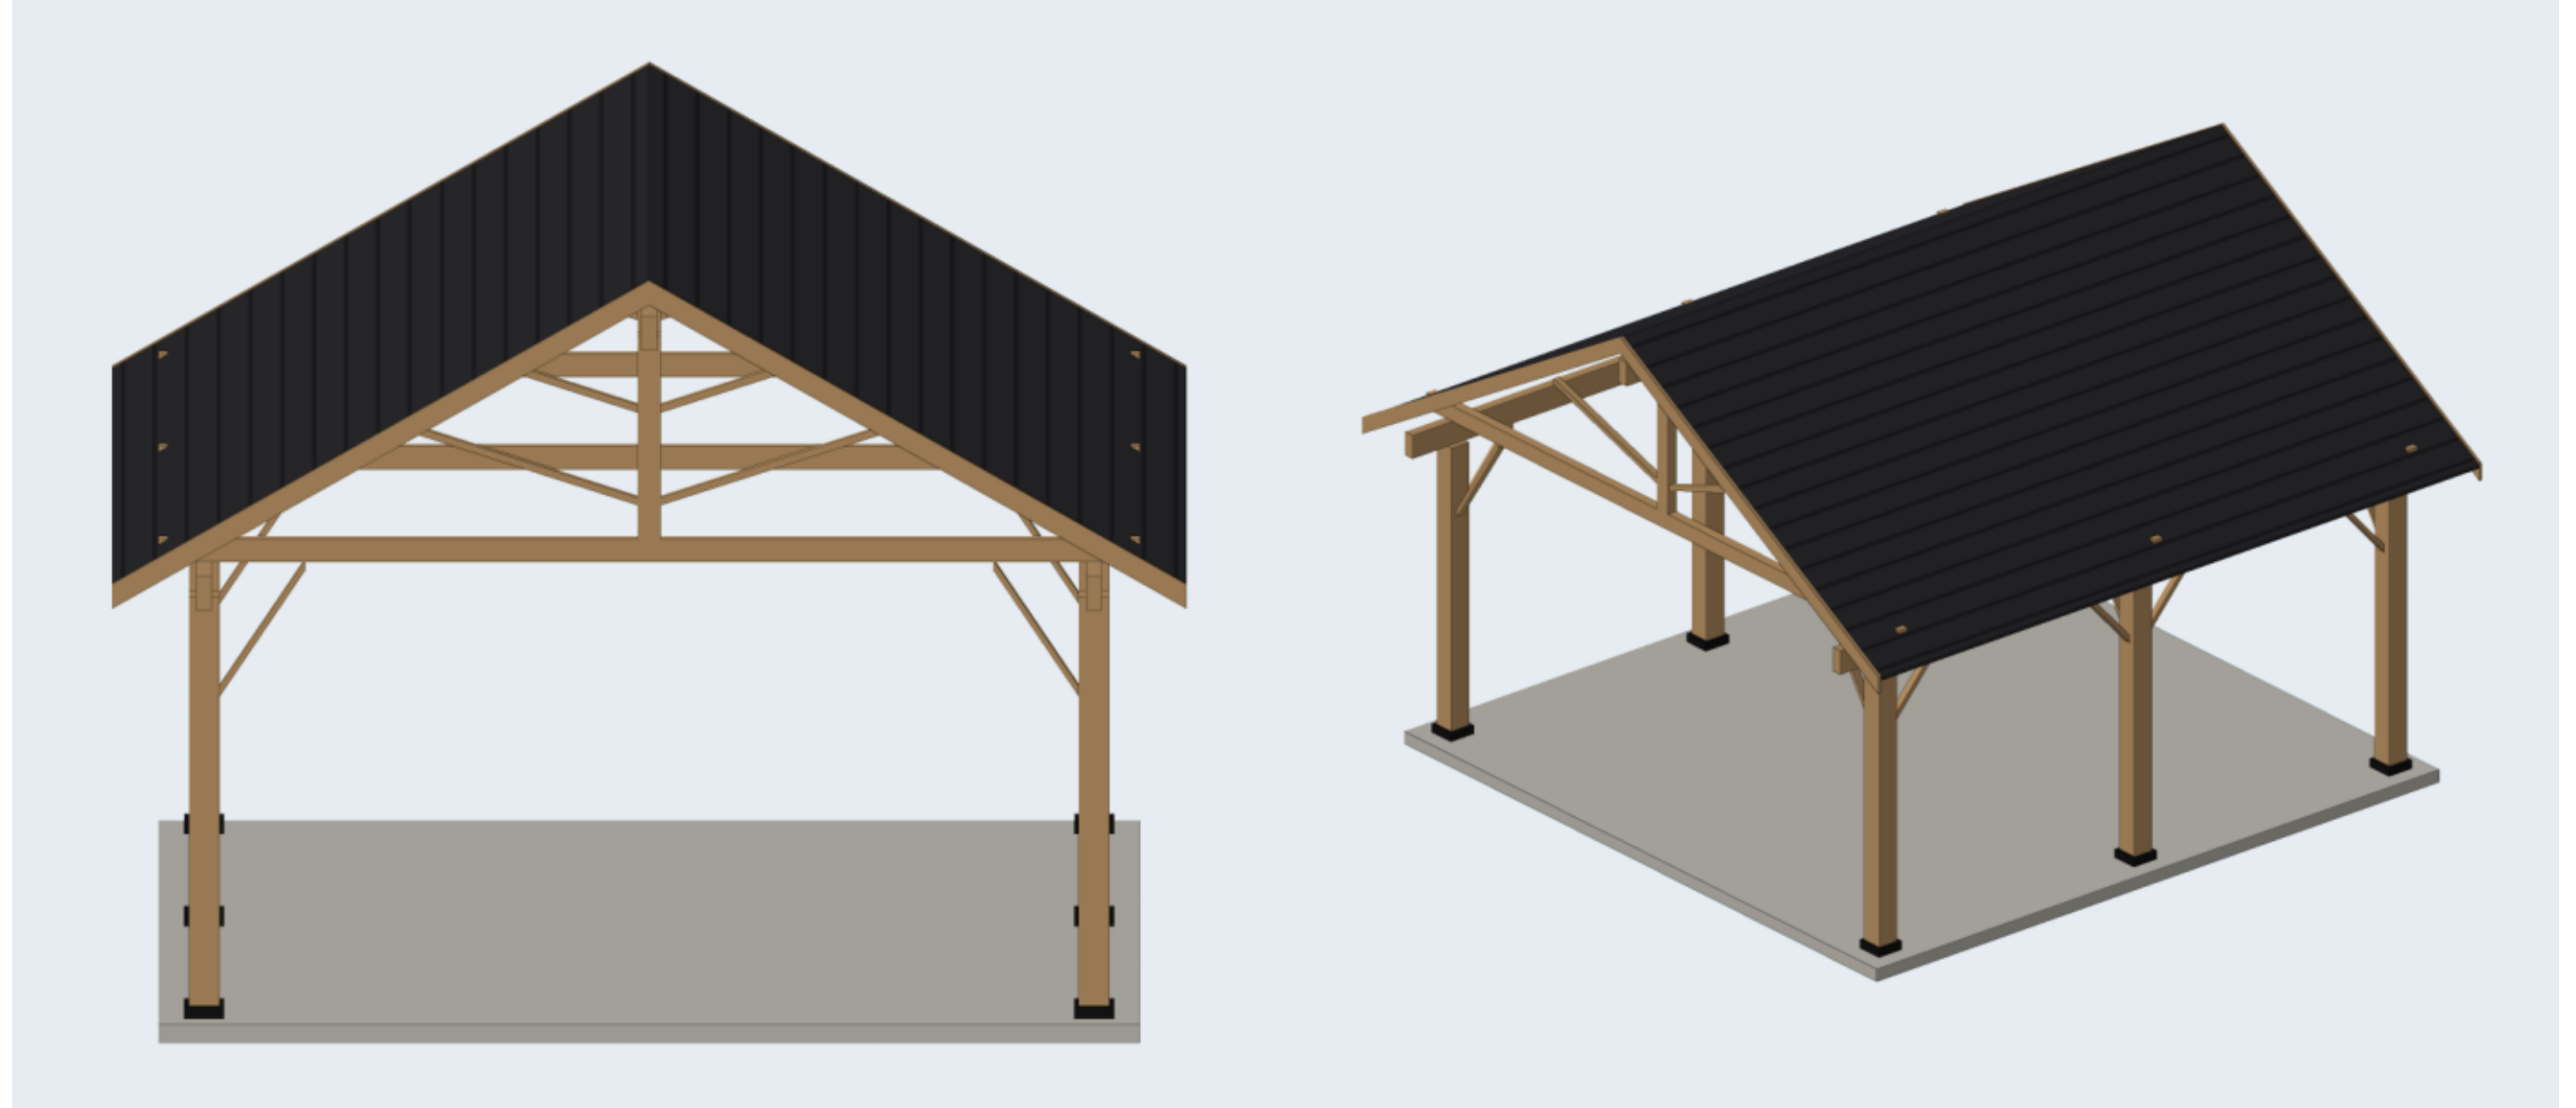

رقم اللوحة

A-05 (5/5)

التاريخ

2026-10-07

المقياس

—

عنوان اللوحة

المنظور

المشروع / العميل

برجولة خشب 6×6 بجمالونات مكشوفة
عميل — برجولة

مصنع وتد الأخشاب
Watad Wood Factory

