
المسقط الأفقي مع الفرش — الدور الأرضي

الأبعاد بالسنتيمتر - الجدران: قوائم 7×5 + تلبيس 2.5 من الجهتين (12 سم) | منسوب الأرضية +0.00

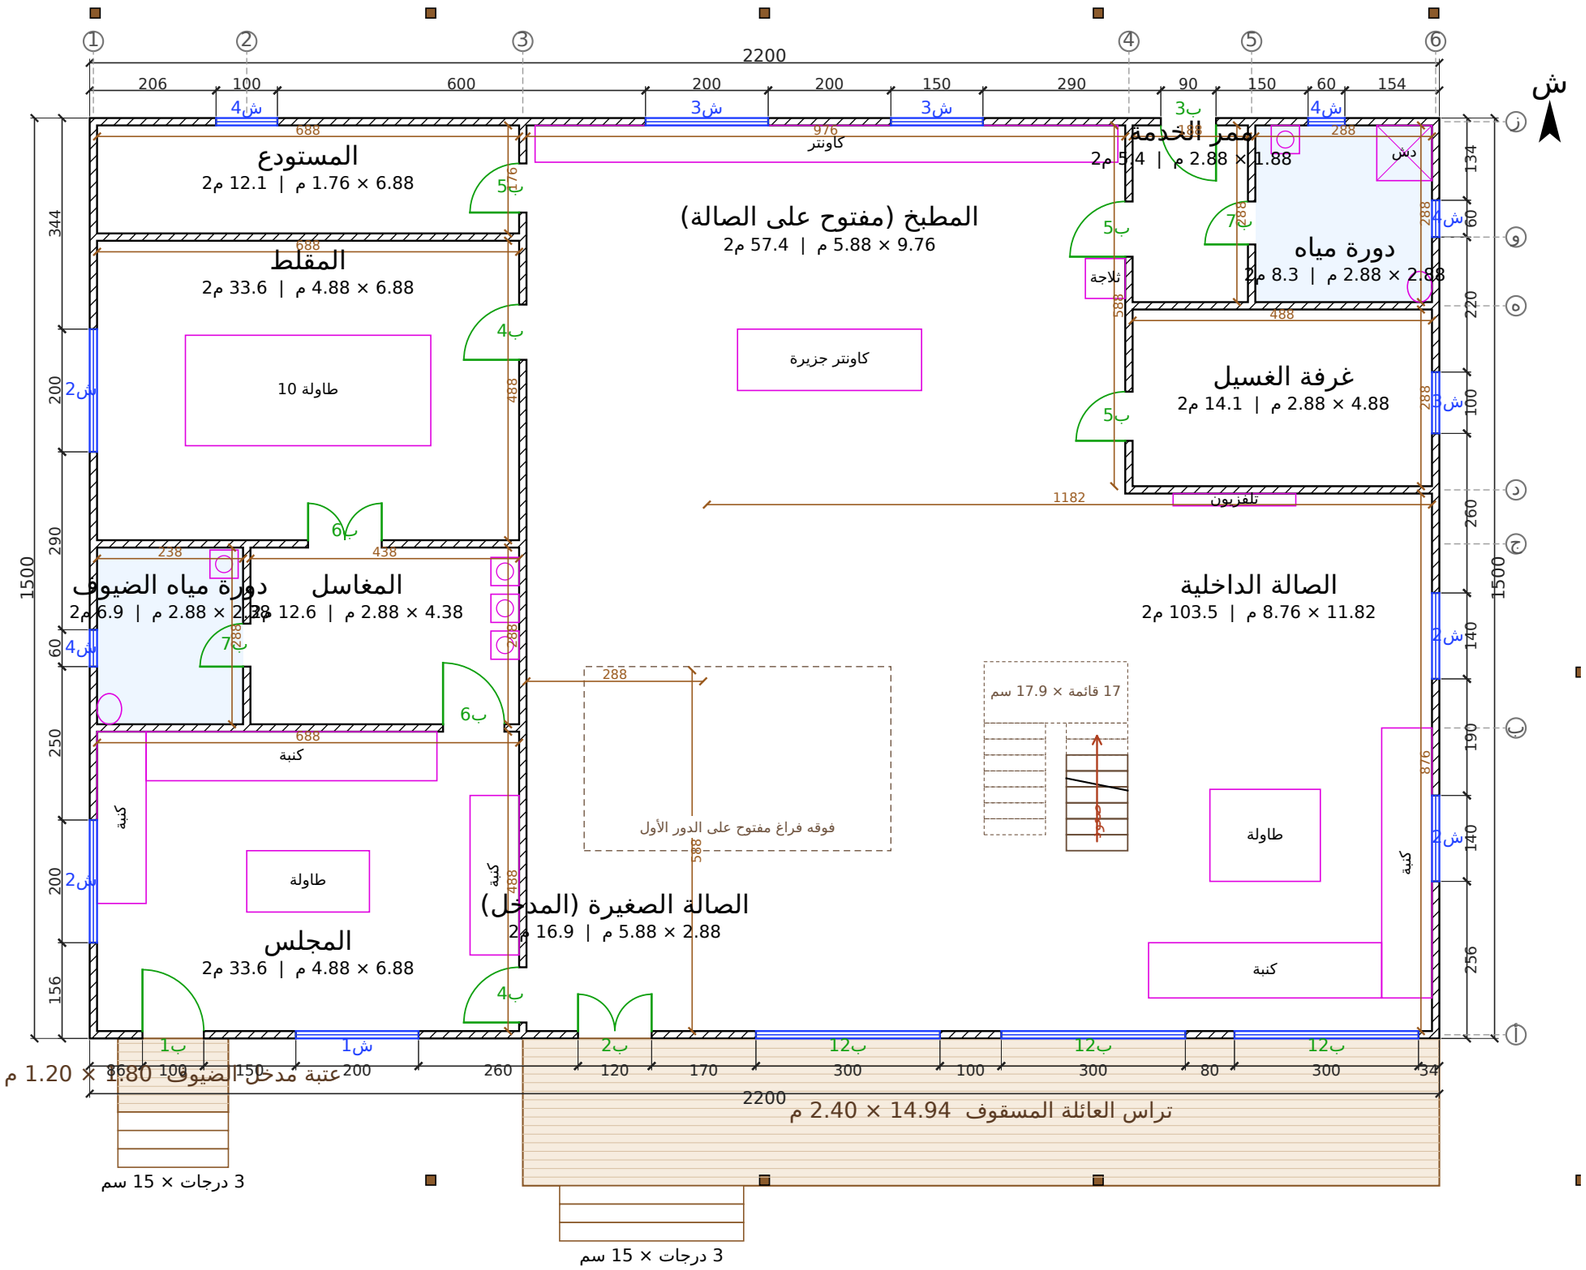


المشروع / العميل	عنوان اللوحة	المقياس	التاريخ	رقم اللوحة
فيلا دورين — مجلس ومقلط + 6 غرف — 15.00 × 22.00 **عميل — فيلا 6 غرف**	**المسقط الأفقي — الدور الأرضي**	**1:50**	**2026-10-21**	**A-01 (1/11)**

مصنع وتد الأخشاب
Watad Wood Factory


المسقط الأفقي مع الفرش — الدور الأول

الأبعاد بالسنتيمتر - الجدران: قوائم 7×5 + تلبيس 2.5 من الجهتين (12 سم) | منسوب الأرضية +3.05

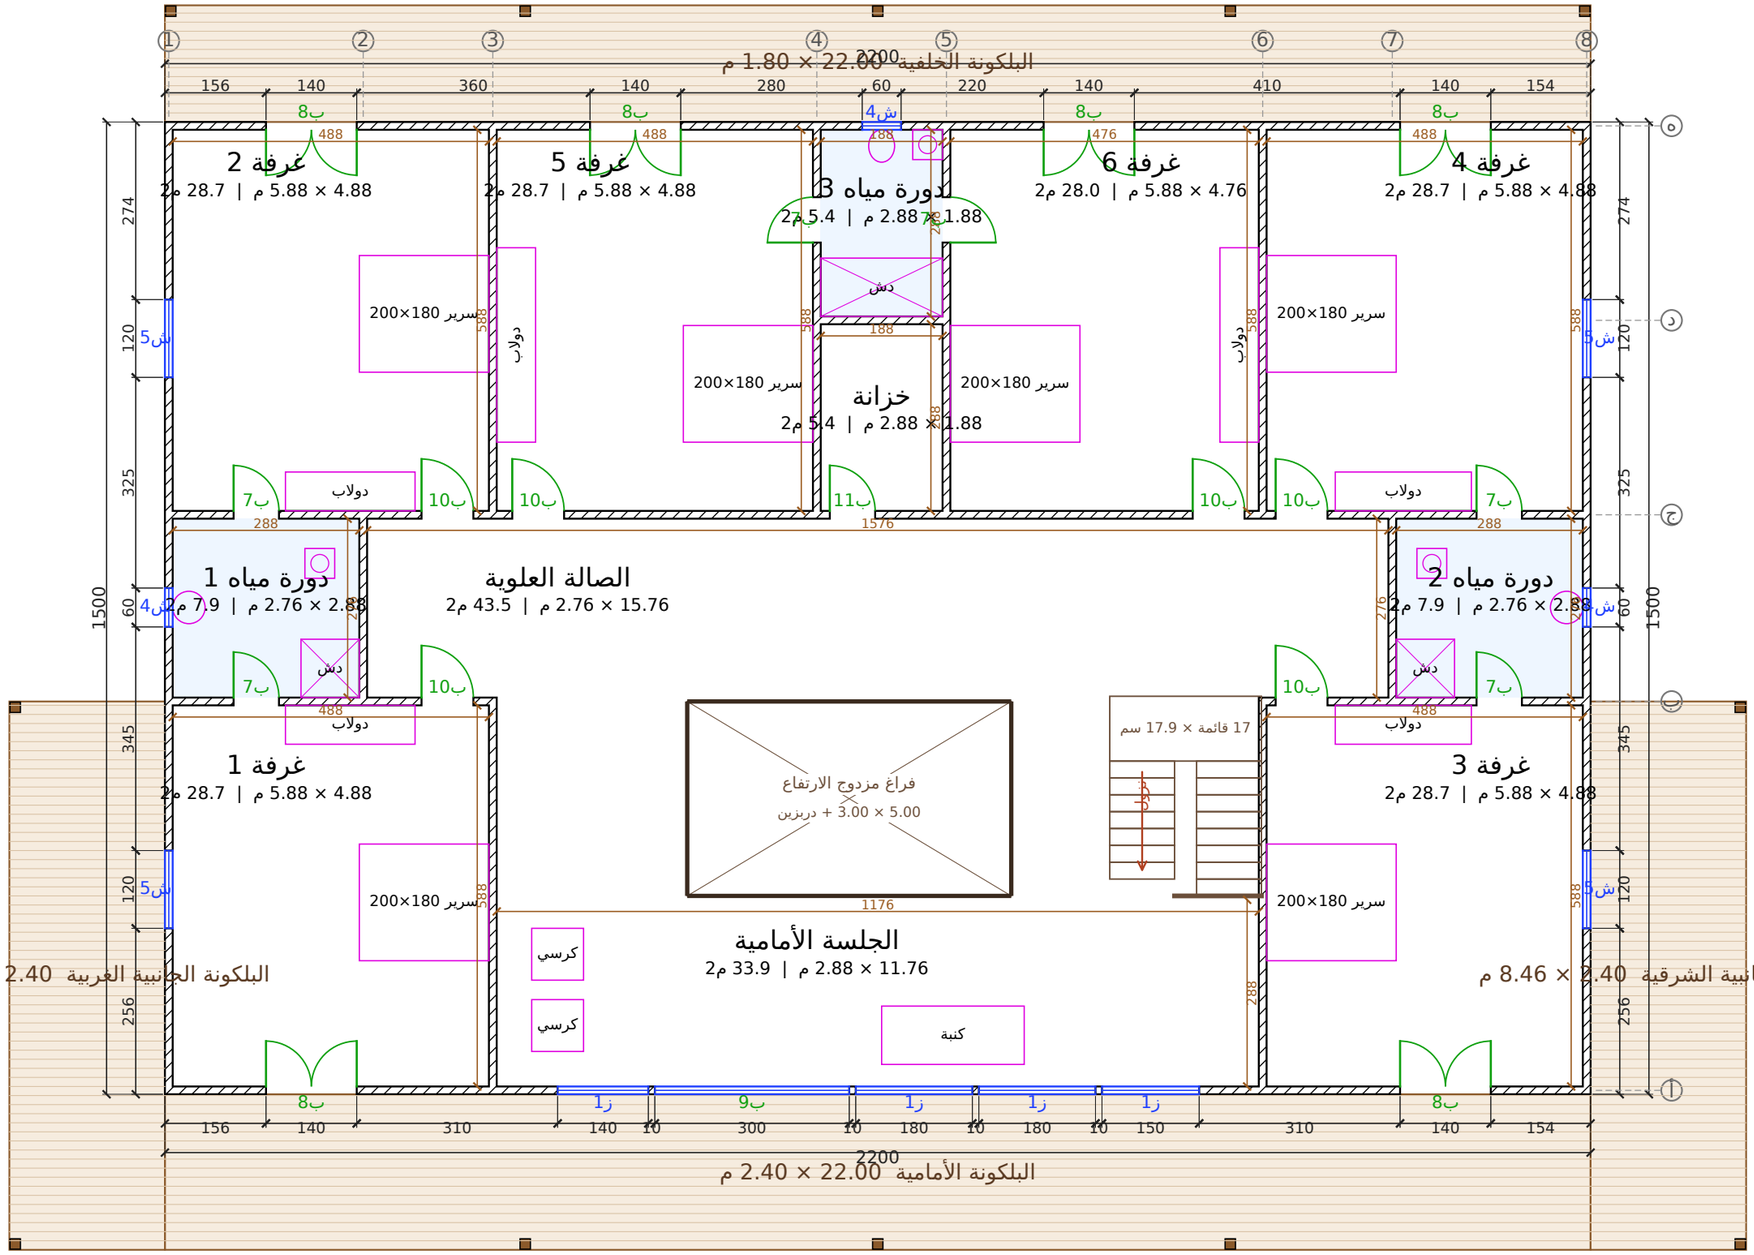


المشروع / العميل	عنوان اللوحة	المقياس	التاريخ	رقم اللوحة
فيلا دورين — مجلس ومقلط + 6 غرف — 15.00 × 22.00 **عميل — فيلا 6 غرف**	**المسقط الأفقي — الدور الأول**	**1:50**	**2026-10-21**	**A-02 (2/11)**

مصنع وتد الأخشاب
Watad Wood Factory

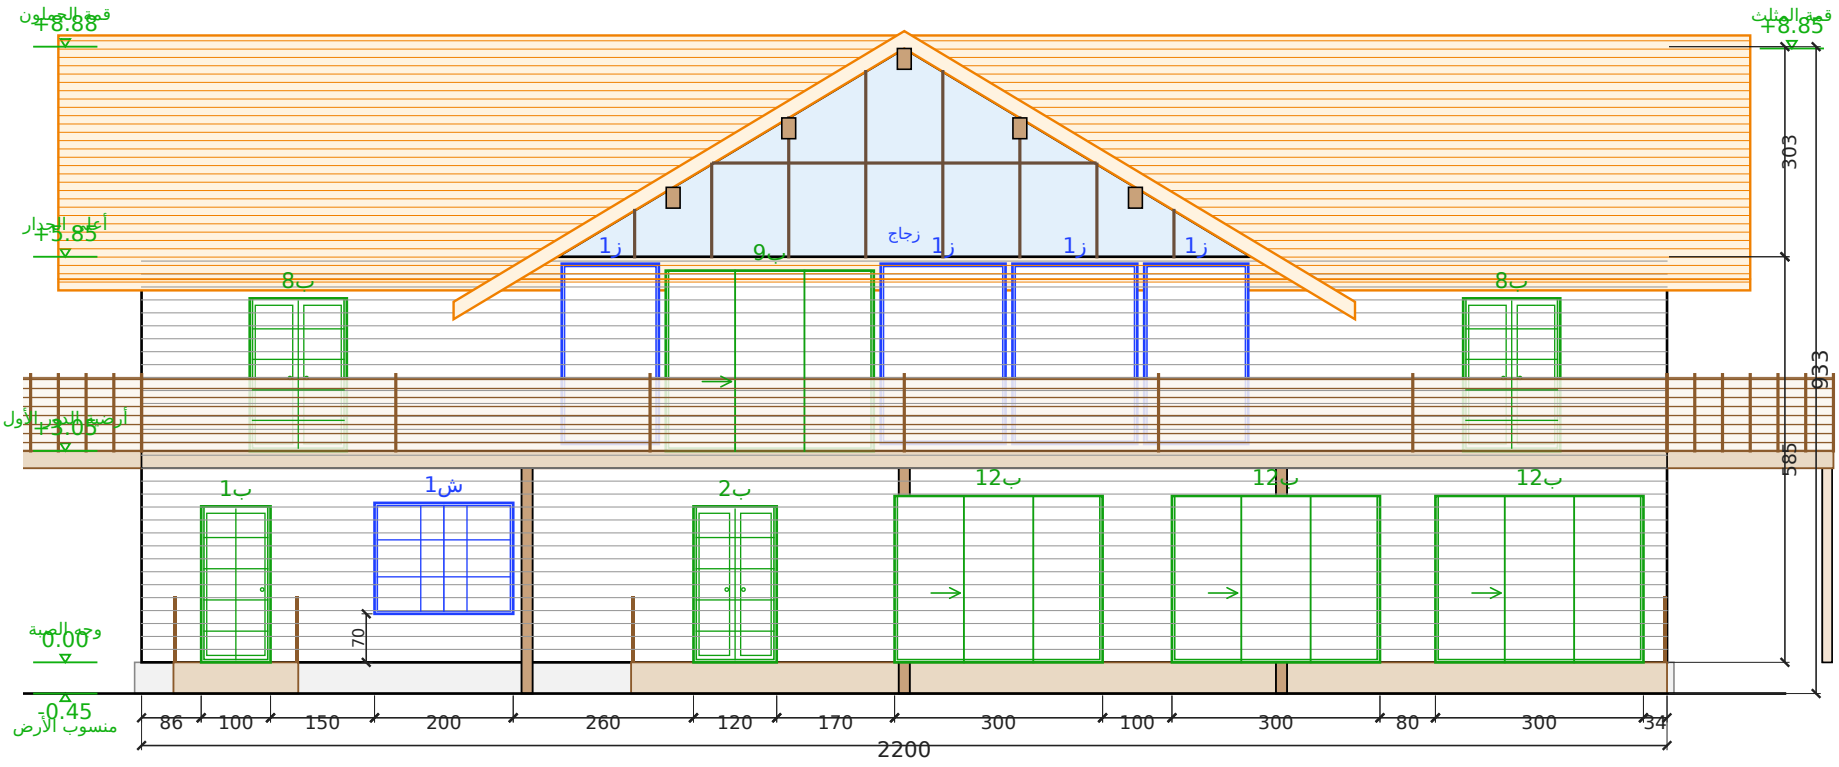

الواجهة الأمامية

مقياس 1:50 | الوحدة: سم

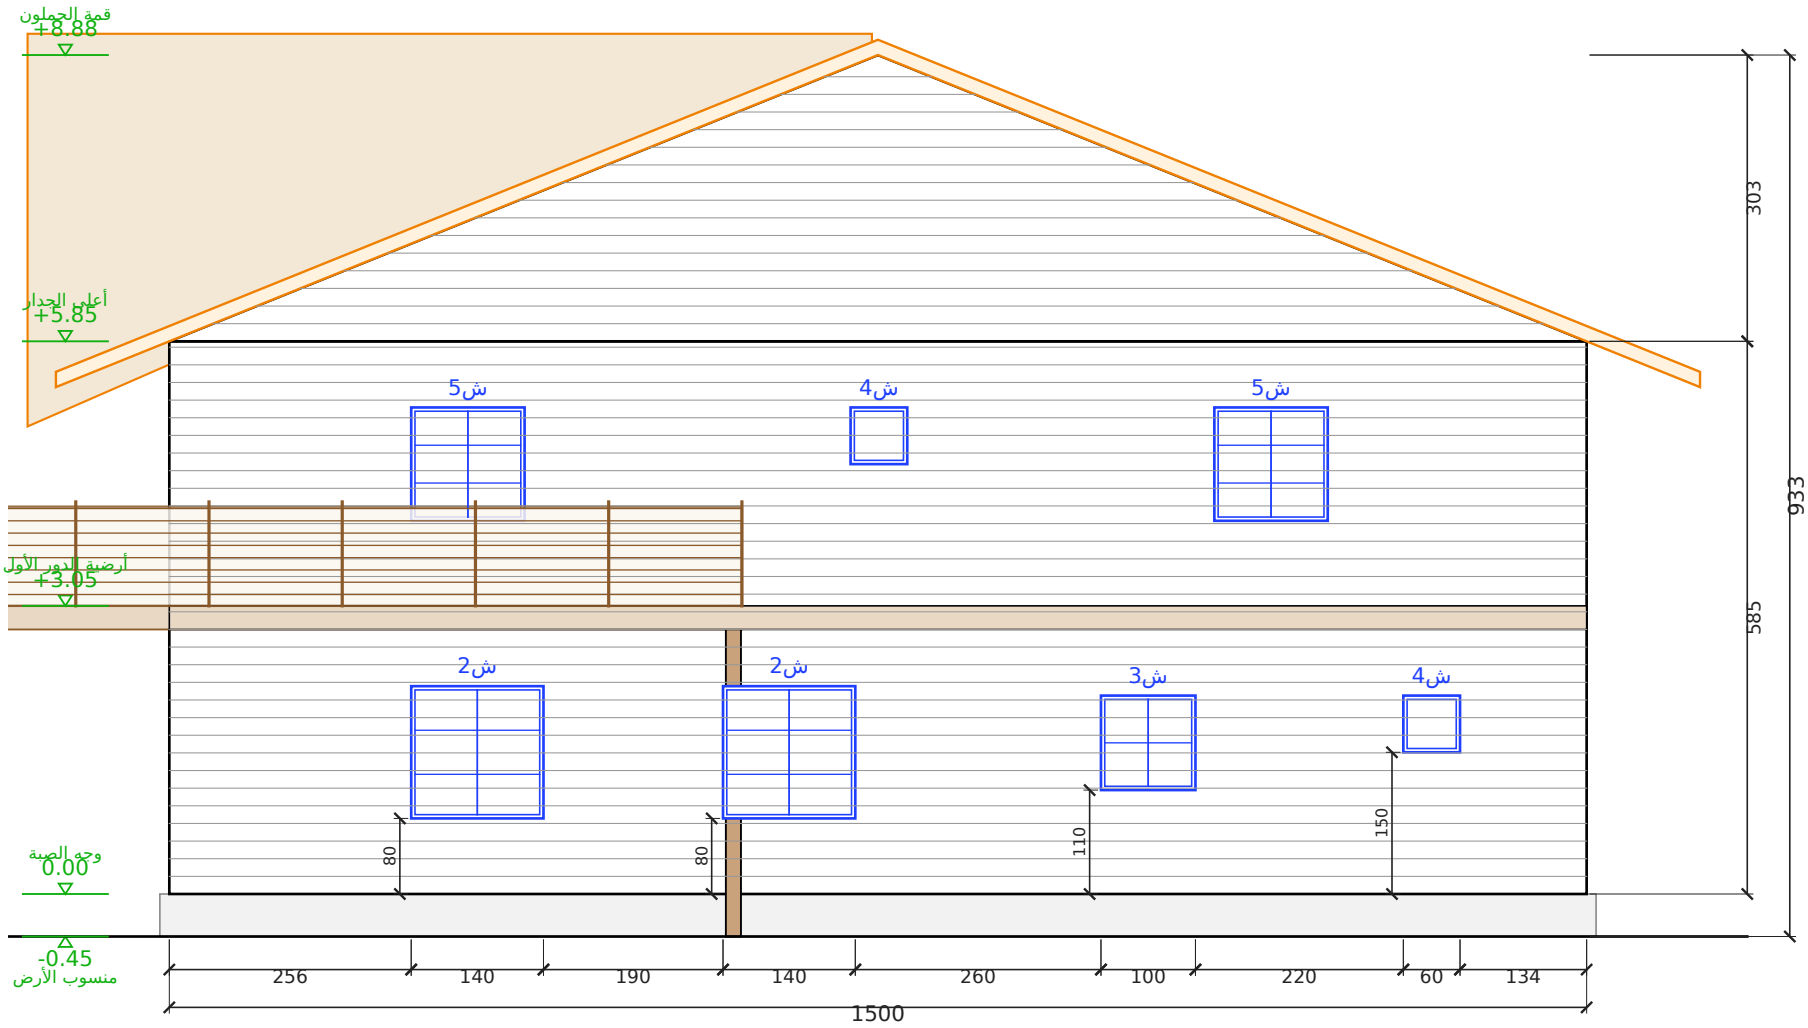


الواجهة الشرقية

مقياس 1:50 | الوحدة: سم


المشروع / العميل	عنوان اللوحة	المقياس	التاريخ	رقم اللوحة
فيلا دورين — مجلس ومقلط + 6 غرف — 15.00 × 22.00 **عميل — فيلا 6 غرف**	**الواجهة الأمامية والواجهة الشرقية**	**1:50**	**2026-10-21**	**A-03 (3/11)**

مصنع وتد الأخشاب
Watad Wood Factory

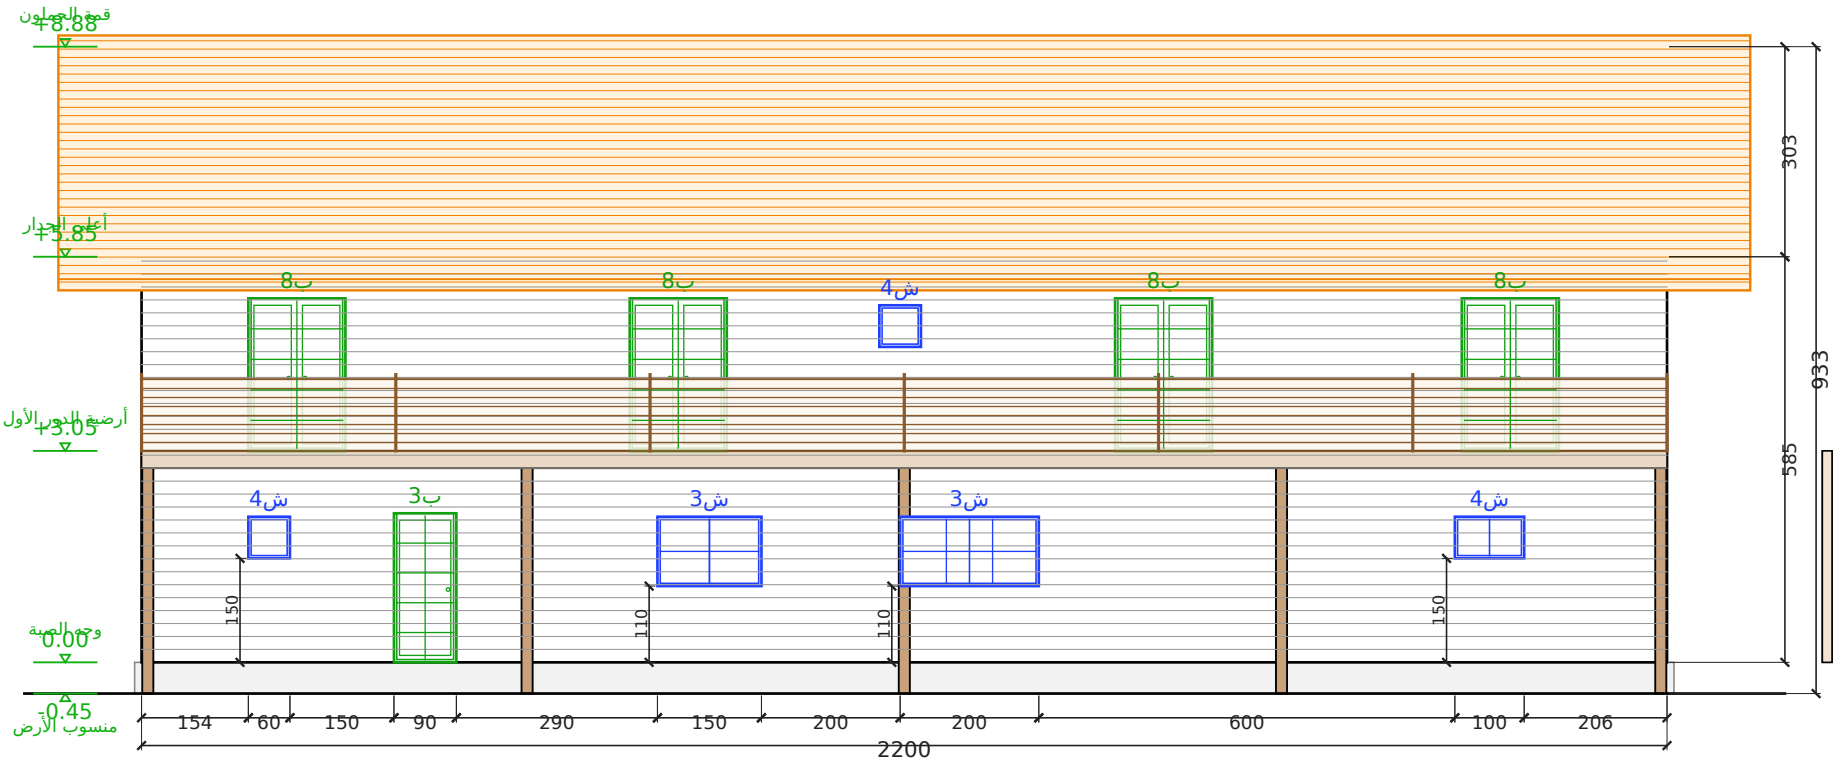

الواجهة الخلفية

مقياس 1:50 | الوحدة: سم

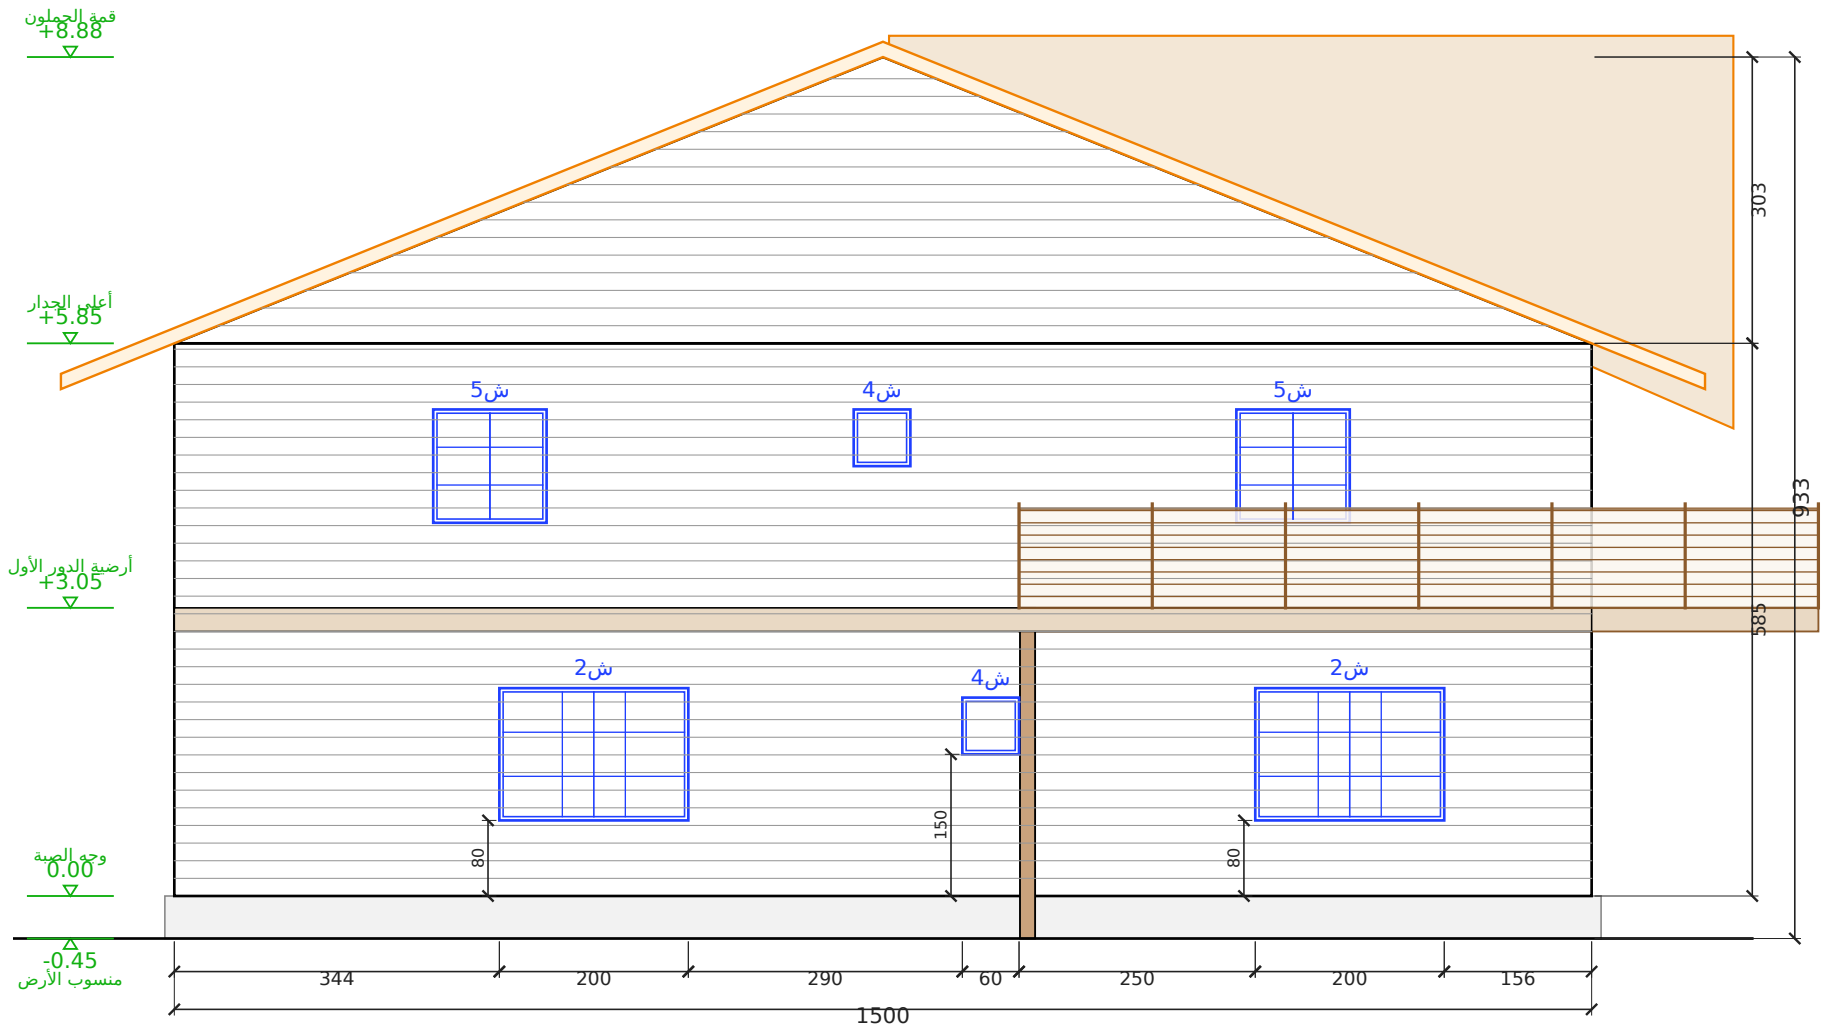


الواجهة الغربية

مقياس 1:50 | الوحدة: سم


المشروع / العميل	عنوان اللوحة	المقياس	التاريخ	رقم اللوحة
فيلا دورين — مجلس ومقلط + 6 غرف — 15.00 × 22.00 **عميل — فيلا 6 غرف**	**الواجهة الخلفية والواجهة الغربية**	**1:50**	**2026-10-21**	**A-04 (4/11)**

مصنع وتد الأخشاب
Watad Wood Factory


مسقط السقف (جملون)
رفرف 120 سم من كل جهة | مقياس 1:50

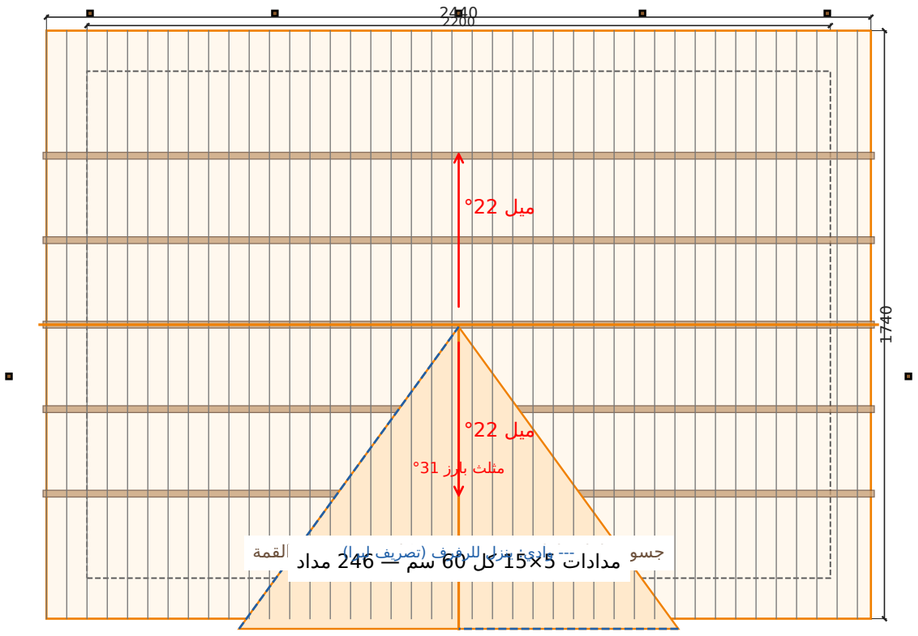

قطاع عرضي أ-أ
مقياس 1:50 | الوحدة: سم

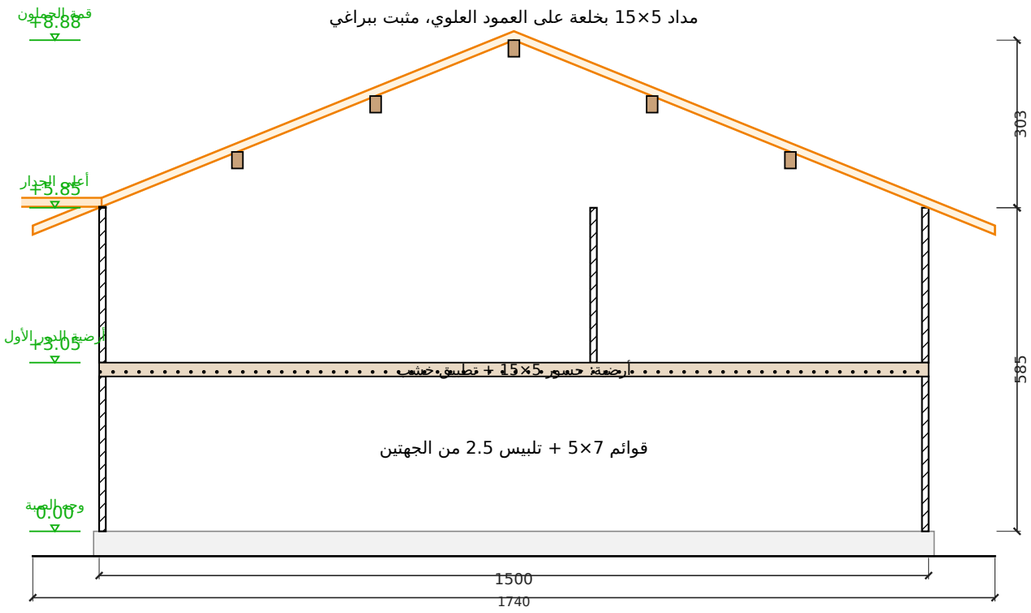

تفصيلة جلوس المداد على العلوي (1:5)

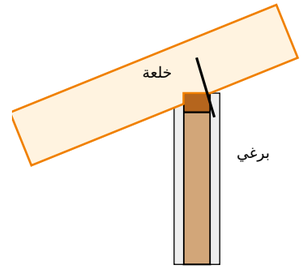

مصنع وتد الأخشاب Watad Wood Factory	المشروع / العميل **فيلا دورين — مجلس ومقلط + 6 غرف — 15.00 × 22.00** **عميل — فيلا 6 غرف**	عنوان اللوحة **مسقط السقف والقطاع**	المقياس **1:50**	التاريخ **2026-10-21**	رقم اللوحة **A-05 (5/11)**

جدول مقاسات الأبواب والشبابيك
مقاس الفتحة الصافي في الجدار - الوحدة: سم

الرمز	النوع	العرض (سم)	الارتفاع (سم)	ارتفاع الجلسة (سم)	العدد	الموقع
ب1	باب	100	225	-	1	الأمامية
ب10	باب	80	210	-	6	غرفة 1 - غرفة 2 - غرفة 5 - غرفة 6 - غرفة 3 - غرفة 4
ب11	باب	70	210	-	1	خزانة
ب12	باب	300	240	-	3	الأمامية 3
ب2	باب مزدوج	120	225	-	1	الأمامية
ب3	باب	90	215	-	1	الخلفية
ب4	باب	90	210	-	2	المجلس — الصالة الصغيرة - المقلط — المطبخ (تقديم)
ب5	باب	80	210	-	2	المستودع - غرفة الغسيل
ب5	باب	90	210	-	1	ممر الخدمة
ب6	باب	100	210	-	1	المجلس — المغاسل
ب6	باب مزدوج	120	210	-	1	المغاسل — المقلط
ب7	باب	70	210	دورة مياه الضيوف - دورة مياه -	8	غرفة 1 — دورة مياه 1 - غرفة 2 — دورة مياه 1 - غرفة 5 — دورة مياه 3 - غرفة 6 — دورة مياه 3 - غرفة 3 — دورة مياه 2 - غرفة
ب8	باب مزدوج	140	220	-	6	الأمامية 2 - الخلفية 4
ب9	باب	300	260	-	1	الأمامية
ز1	شباك	140	260	10	1	الأمامية
ز1	شباك	180	260	10	2	الأمامية 2
ز1	شباك	150	260	10	1	الأمامية
ش1	شباك	200	160	70	1	الأمامية
ش2	شباك	140	140	80	2	الشرقية 2
ش2	شباك	200	140	80	2	الغربية 2
ش3	شباك	100	100	110	1	الشرقية
ش3	شباك	150	100	110	1	الخلفية
ش3	شباك	200	100	110	1	الخلفية
ش4	شباك	60	60	150	6	الشرقية 2 - الخلفية 2 - الغربية 2
ش4	شباك	100	60	150	1	الخلفية
ش5	شباك	120	120	90	4	الشرقية 2 - الغربية 2

الإجمالي: أبواب 35 - شبابيك 23

المشروع / العميل	عنوان اللوحة	المقياس	التاريخ	رقم اللوحة
فيلا دورين — مجلس ومقلط + 6 غرف — 15.00 × 22.00 **عميل — فيلا 6 غرف**	**جدول الأبواب والشبابيك**	**—**	**2026-10-21**	**A-06 (6/11)**

مصنع وتد الأخشاب
Watad Wood Factory

جدول المساحات وبيانات المشروع

بيانات المشروع


البند	البيان
المشروع	فيلا دورين — مجلس ومقلط + 6 غرف — 15.00 × 22.00
العميل	عميل — فيلا 6 غرف
الموقع	—
الاستخدام	سكن خاص
التاريخ	2026-10-21
نظام البناء	هيكل خشب 5×7 + تلبيس 2.5 سم من الجهتين
السقف	جملون 22° — قرميد معدني + 1 مثلث بارز

جدول المساحات


م	الفراغ	الأبعاد (م)	المساحة (م2)
1	أرضي — المجلس	4.88 × 6.88	33.57
2	أرضي — دورة مياه الضيوف	2.38 × 2.88	6.85
3	أرضي — المغاسل	4.38 × 2.88	12.61
4	أرضي — المقلط	4.88 × 6.88	33.57
5	أرضي — المستودع	1.76 × 6.88	12.11
6	أرضي — الصالة الصغيرة (المدخل)	2.88 × 5.88	16.93
7	أرضي — الصالة الداخلية	8.76 × 11.82	103.54
8	أرضي — المطبخ (مفتوح على الصالة)	5.88 × 9.76	57.39
9	أرضي — غرفة الغسيل	2.88 × 4.88	14.05
10	أرضي — ممر الخدمة	2.88 × 1.88	5.41
11	أرضي — دورة مياه	2.88 × 2.88	8.29
12	أول — غرفة 1	5.88 × 4.88	28.69
13	أول — دورة مياه 1	2.76 × 2.88	7.95
14	أول — غرفة 2	5.88 × 4.88	28.69
15	أول — غرفة 3	5.88 × 4.88	28.69
16	أول — دورة مياه 2	2.76 × 2.88	7.95
17	أول — غرفة 4	5.88 × 4.88	28.69
18	أول — غرفة 5	5.88 × 4.88	28.69
19	أول — غرفة 6	5.88 × 4.76	27.99
20	أول — دورة مياه 3	2.88 × 1.88	5.41
21	أول — خزانة	2.88 × 1.88	5.41
22	أول — الجلسة الأمامية	2.88 × 11.76	33.87
23	أول — الصالة العلوية	2.76 × 15.76	43.50
	المساحة الصافية الداخلية		579.91
	عتبة مدخل الضيوف	1.20 × 1.80	2.16
	تراس العائلة المسقوف	2.40 × 14.94	35.86
	البلكونة الأمامية	2.40 × 22.00	52.80
	البلكونة الجانبية الشرقية	8.46 × 2.40	20.30
	البلكونة الجانبية الغربية	**8.46 × 2.40**	**20.30**
	البلكونة الخلفية	**1.80 × 22.00**	**39.60**
	المساحة الإجمالية المبنية	**22.00 × 15.00 × 2 دور**	**660.00**
	المساحة الكلية (المبنية + التراس والبلكونة)		**831.02**

لقطات المنظور الخارجي


المنظور الأمامي

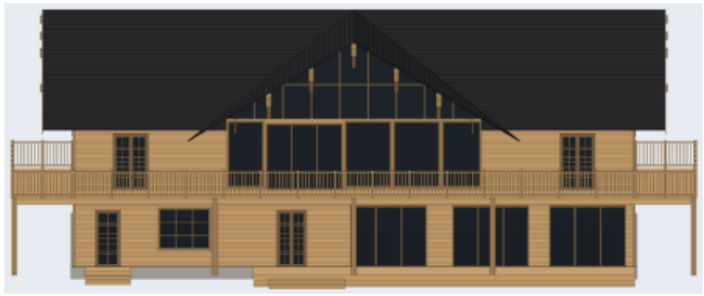


منظور أمامي من اليسار

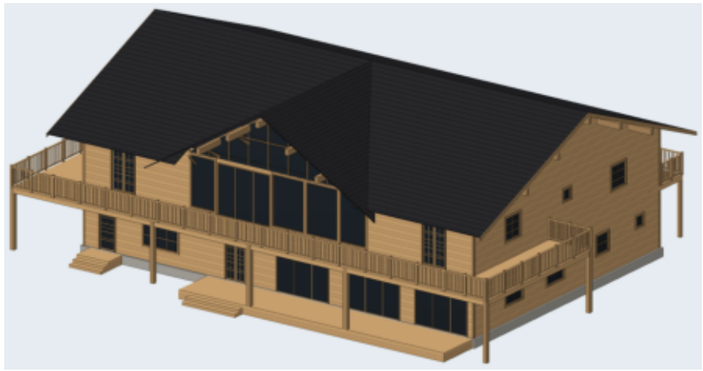

منظور أمامي من اليمين

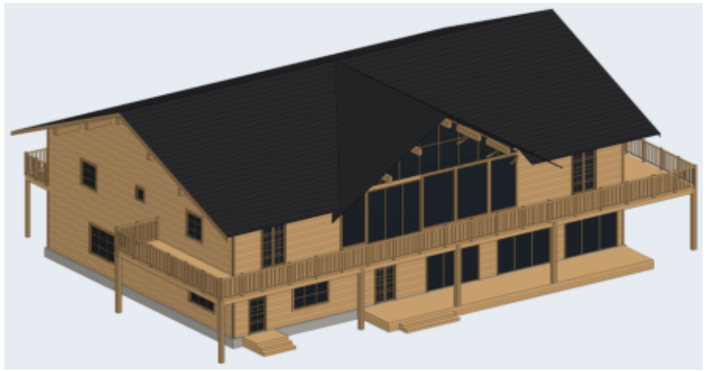


المنظور الخلفي

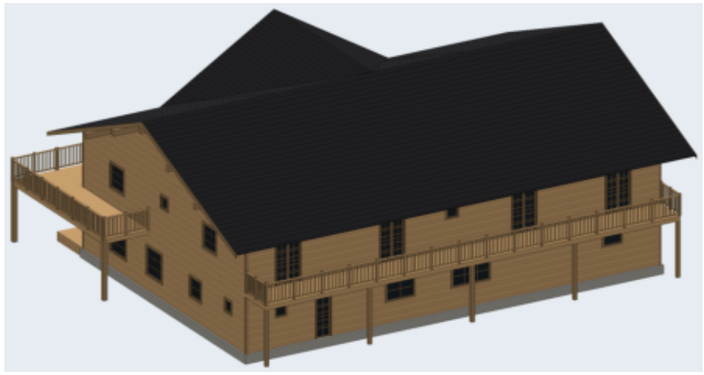

منظور خلفي من اليمين



منظر علوي

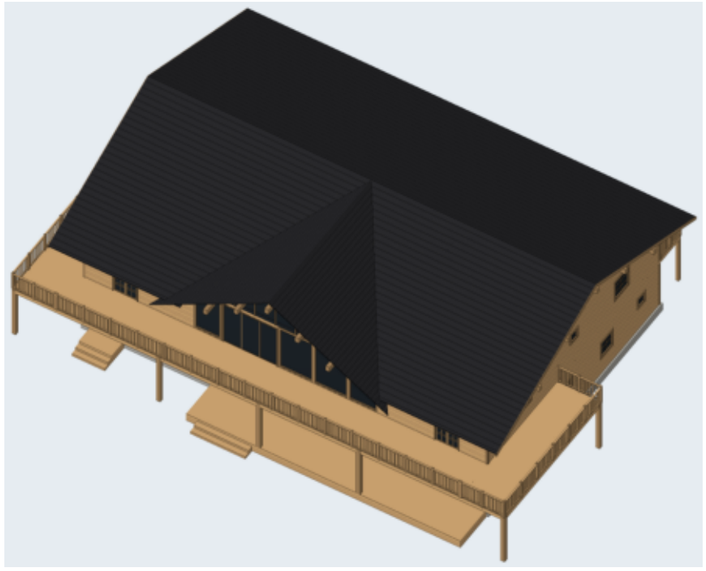


المشروع / العميل	عنوان اللوحة	المقياس	التاريخ	رقم اللوحة
فيلا دورين — مجلس ومقلط + 6 غرف — 15.00 × 22.00 **عميل — فيلا 6 غرف**	**لقطات المنظور**	**—**	**2026-10-21**	**A-08 (8/11)**

مصنع وتد الأخشاب
Watad Wood Factory

المقطع العلوي بالفرش — الدور الأرضي

مقطع أفقي على ارتفاع 1.90 م — توزيع الفرش ومسار الحركة

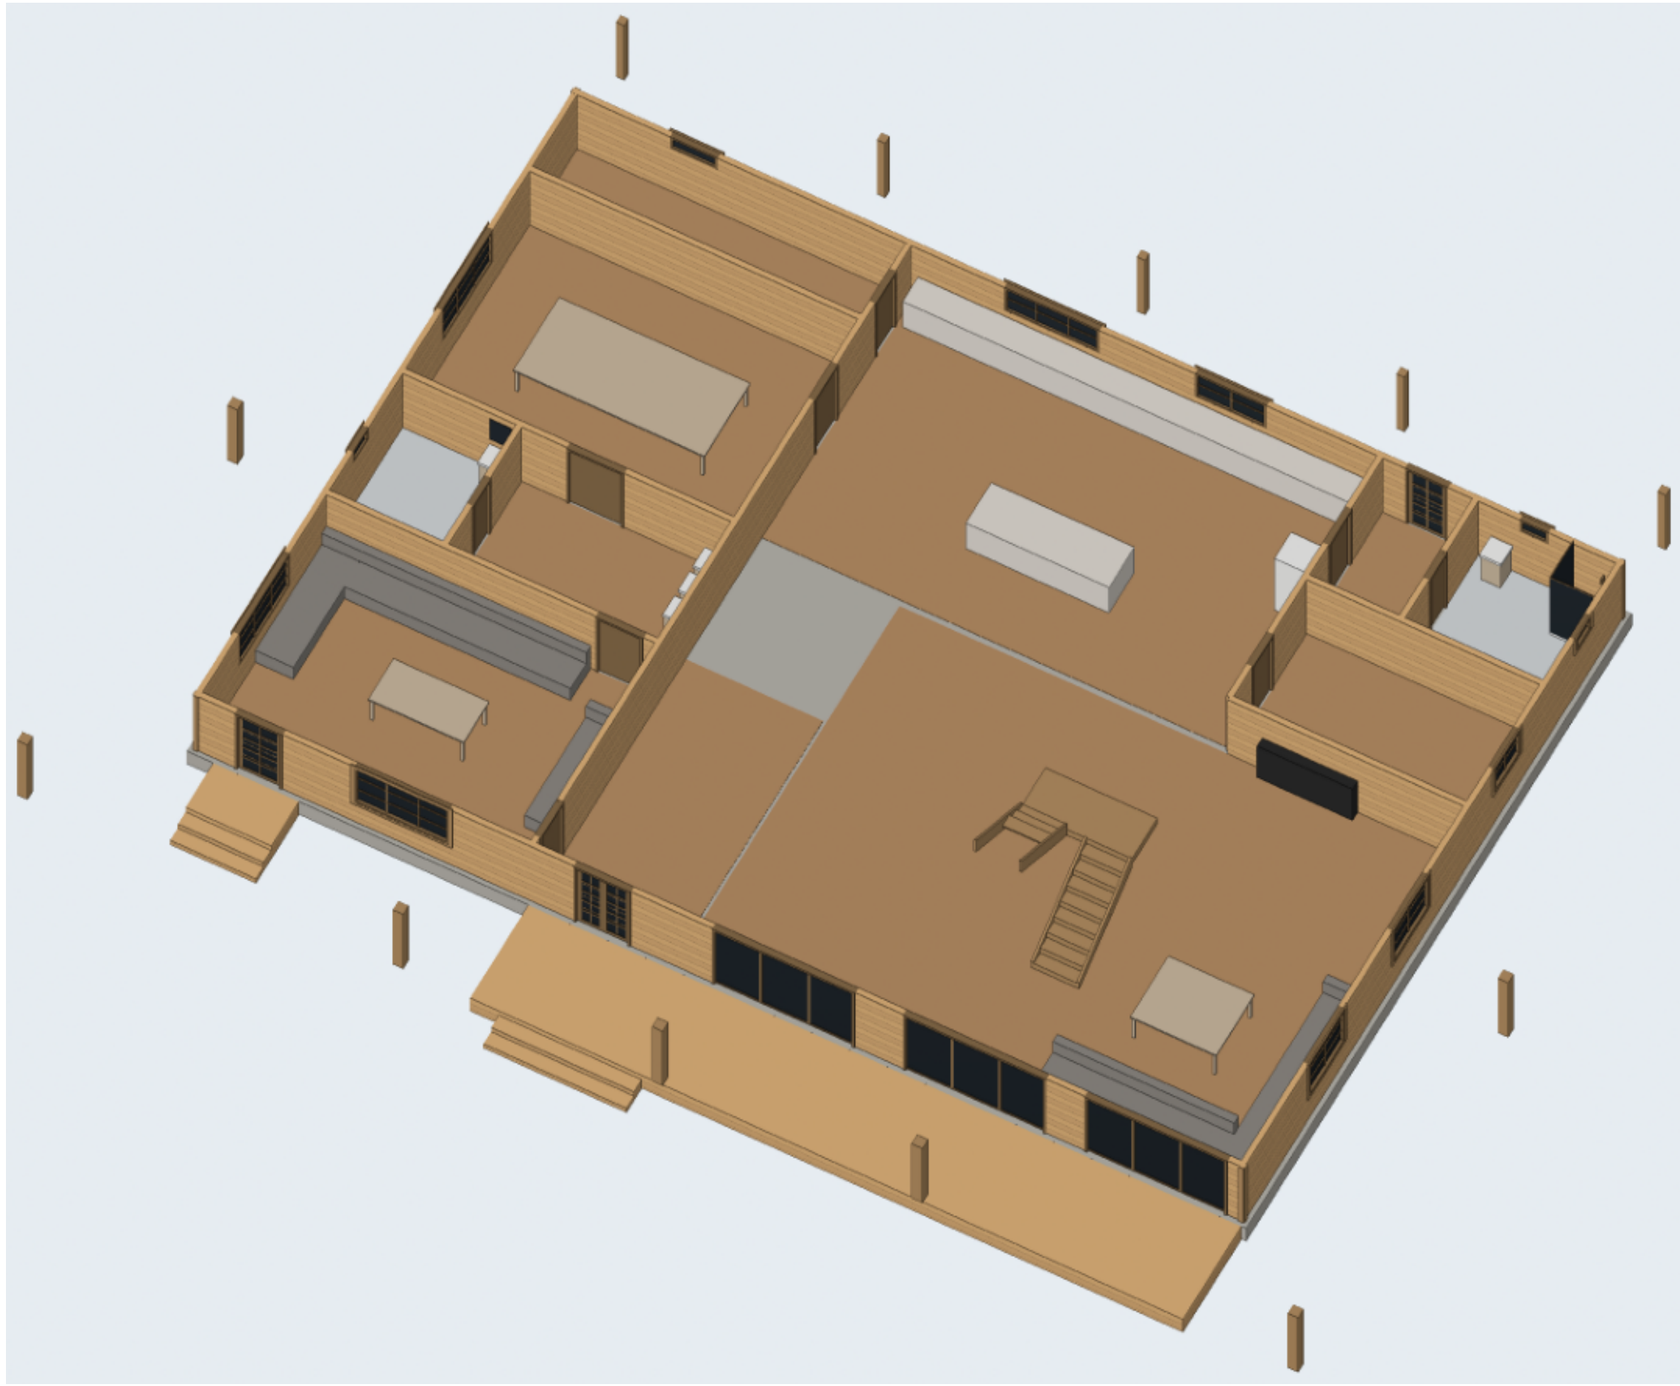


المشروع / العميل	عنوان اللوحة	المقياس	التاريخ	رقم اللوحة
فيلا دورين — مجلس ومقلط + 6 غرف — 15.00 × 22.00 **عميل — فيلا 6 غرف**	**المقطع العلوي بالفرش — الدور الأرضي**	**—**	**2026-10-21**	**A-09 (9/11)**

مصنع وتد الأخشاب
Watad Wood Factory

المقطع العلوي بالفرش — الدور الأول

مقطع أفقي على ارتفاع 1.90 م — توزيع الفرش ومسار الحركة

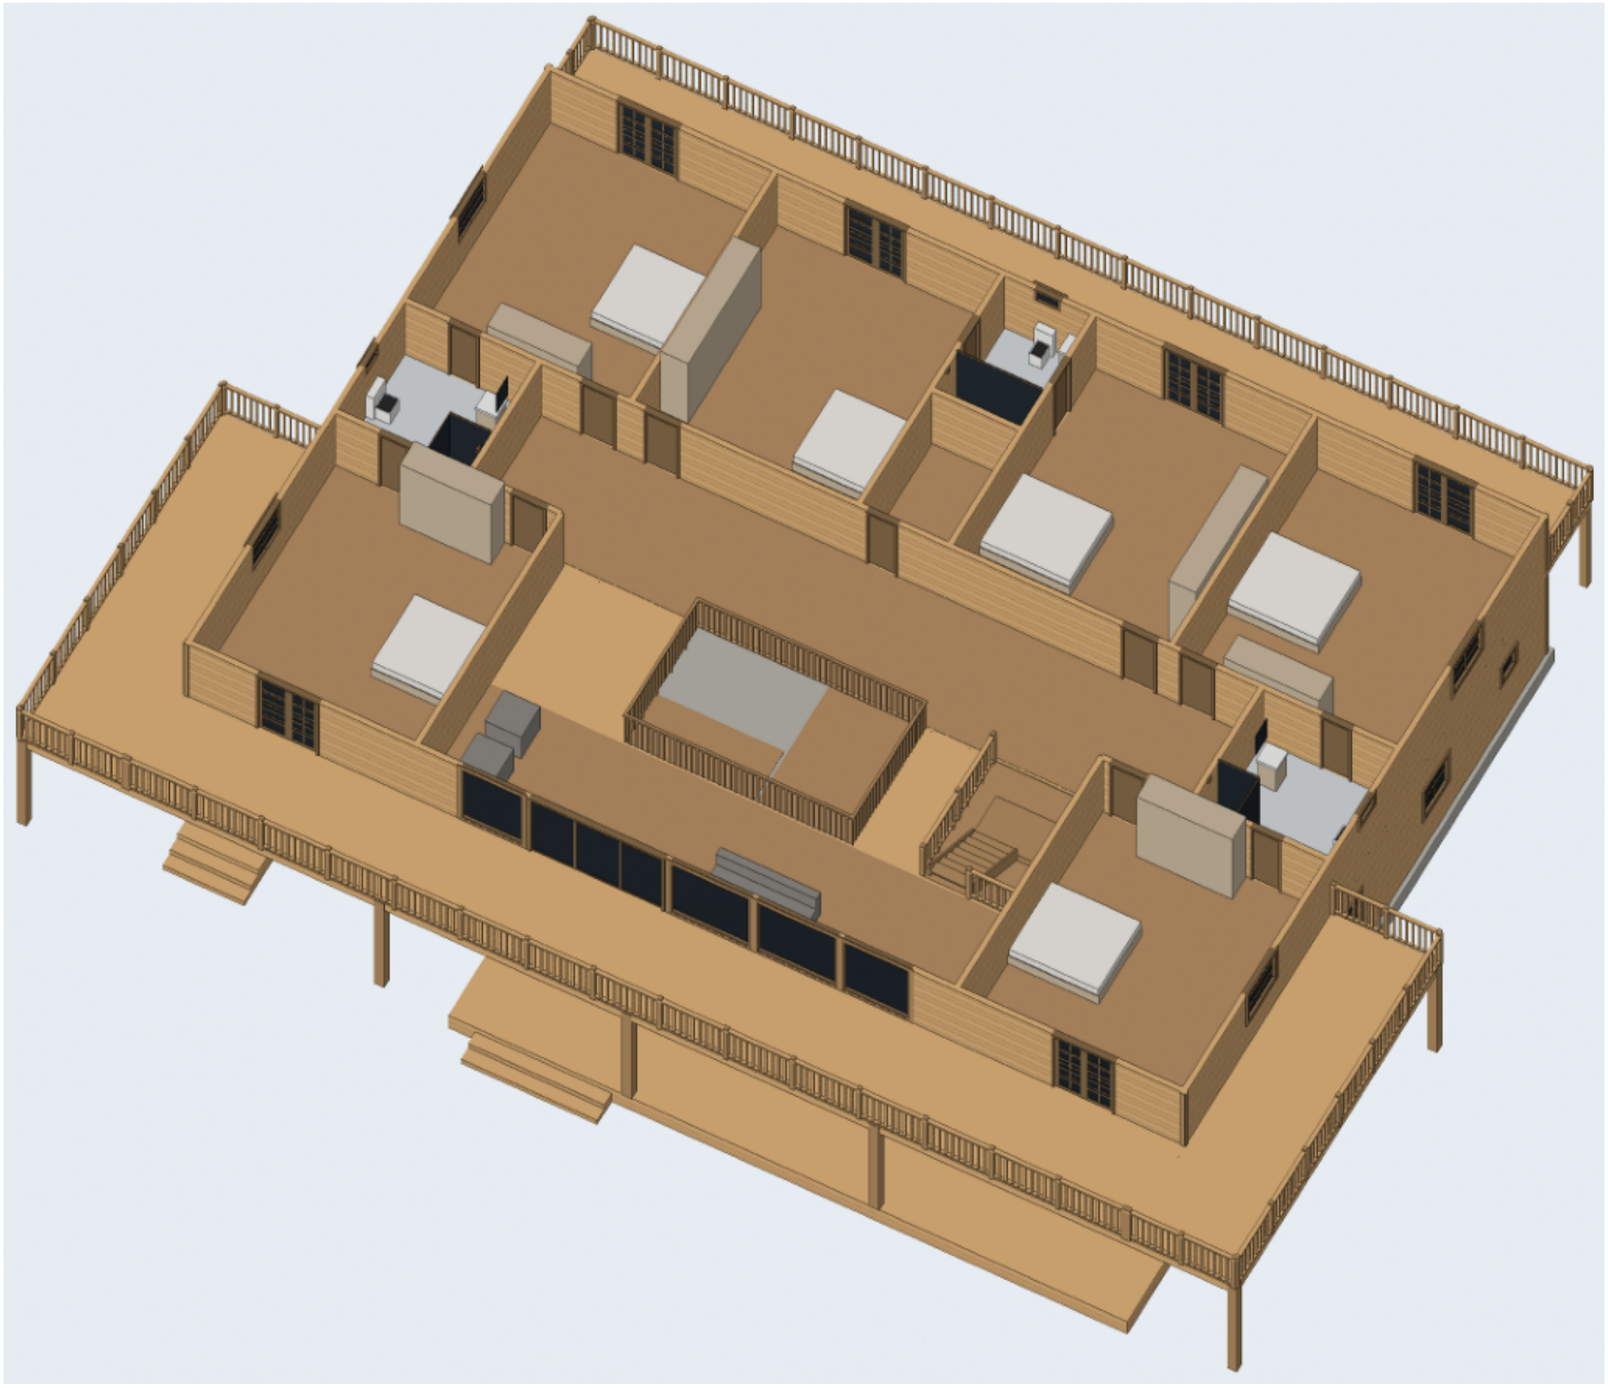


المشروع / العميل	عنوان اللوحة	المقياس	التاريخ	رقم اللوحة
فيلا دورين — مجلس ومقلط + 6 غرف — 15.00 × 22.00 **عميل — فيلا 6 غرف**	**المقطع العلوي بالفرش — الدور الأول**	**—**	**2026-10-21**	**A-10 (10/11)**

مصنع وتد الأخشاب
Watad Wood Factory

المنظور ثلاثي الأبعاد والمواد

النمط: جوزي غامق + إطارات سوداء — رندر واقعي بخامات حقيقية

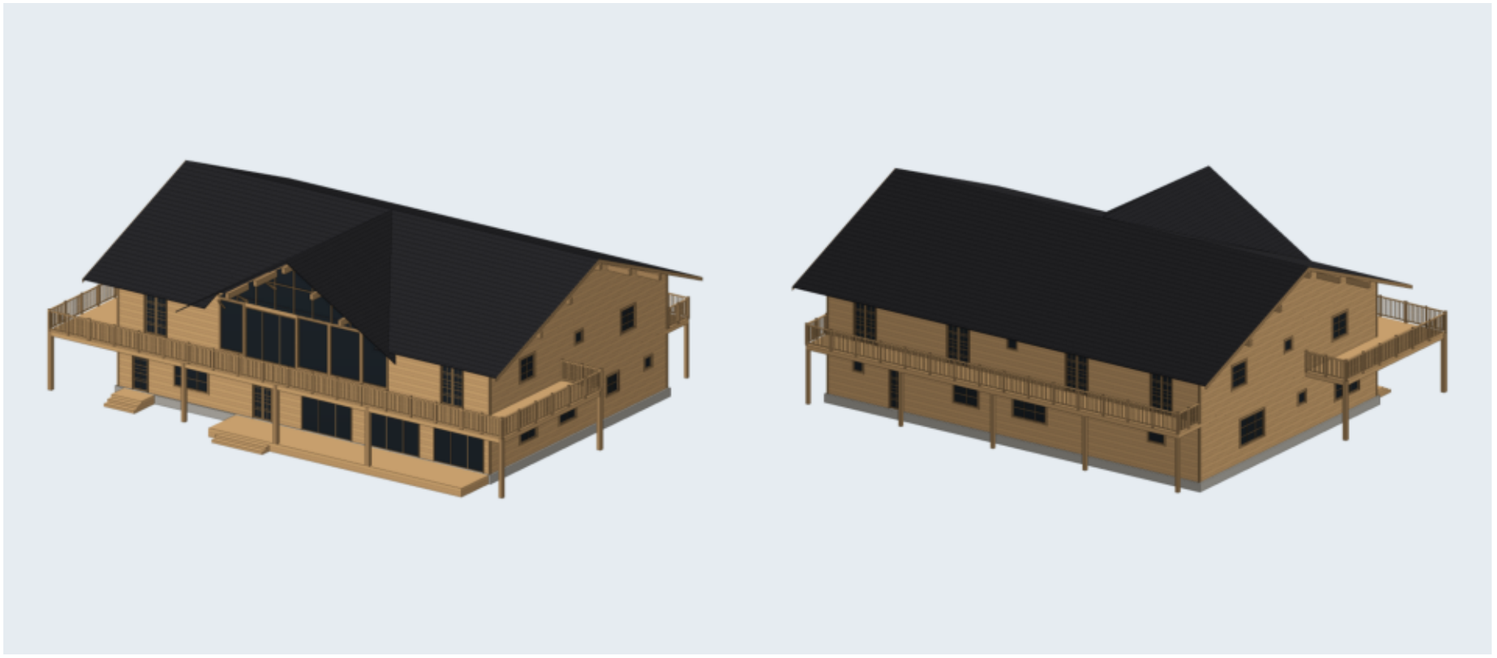

جدول المواد والألوان

الخشب / الصبغة

خشب طبيعي فاتح (بدون صبغة)

القرميد

قرميد رمادي غامق

الزجاج

زجاج عاكس غامق

إطارات الشبابيك والأبواب

إطار خشب بنفس الصبغة أغمق

الكنار والزوايا

نفس الصبغة أغمق درجة


الصبة

خرسانة 45 سم


الدربزين: ألواح أفقية متقاربة (عصري)

تقسيم الشبابيك: بدون | الباب الرئيسي: زجاج بتقسيمات (فرنسي)

أنواع الدربزين المعتمدة (من مشاريع المصنع)

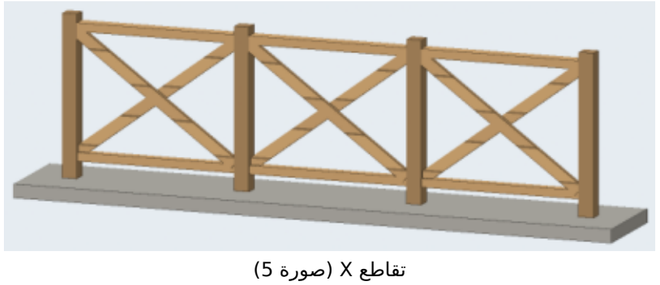

تقاطع X (صورة 5)

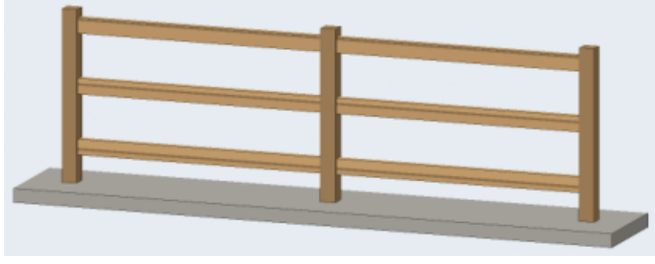

3 مرابيع أفقية (صورة 2)



قوائم رأسية متقاربة (صورة 1)

المشروع / العميل	عنوان اللوحة	المقياس	التاريخ	رقم اللوحة
فيلا دورين — مجلس ومقلط + 6 غرف — 15.00 × 22.00 **عميل — فيلا 6 غرف**	**المنظور والمواد**	**—**	**2026-10-21**	**A-11 (11/11)**

مصنع وتد الأخشاب
Watad Wood Factory