مصنع وتد الأخشاب · ملف التصميم

# فيلا الباحة

11.00 × 8.50 م · دورين · 187 م² · 3 غرف (ماستر) · صالة وطعام ومطبخ

المسقط الأفقي مع الفرش — الدور الأرضي

الأبعاد بالسنتيمتر - الجدران: قوائم 7×5 + تلبيس 2.5 من الجهتين (12 سم) | منسوب الأرضية +0.00

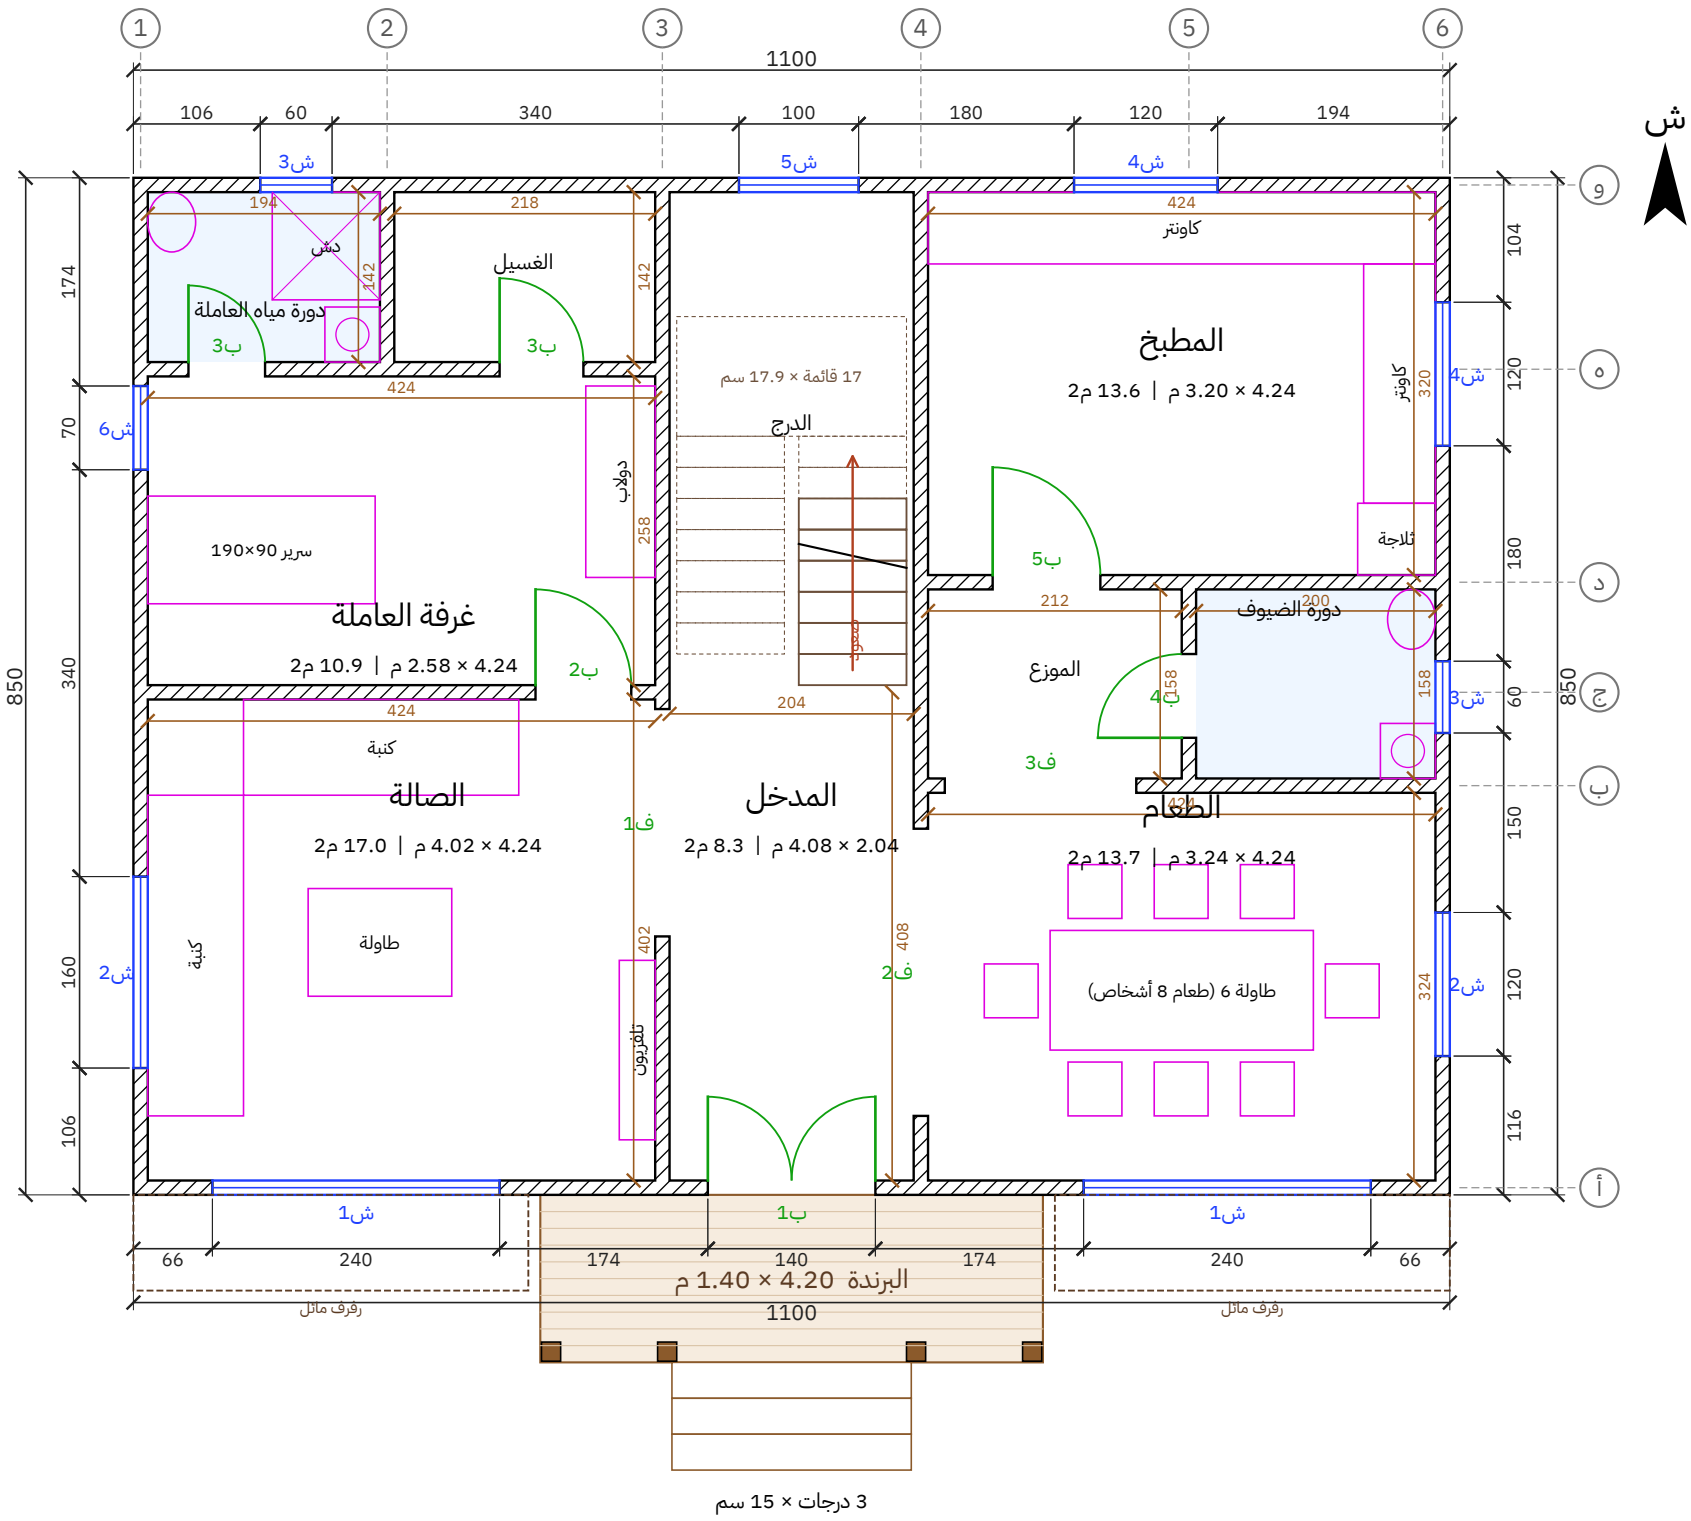


| | | | | | |
|---|---|---|---|---|---|
| مصنع وتد الأخشاب<br>Watad Wood Factory | المشروع / العميل<br>فيلا خشب دورين — واجهة جملون زجاج وبلكونة — 3 غرف (ماستر) — 11.00 × 8.50 م<br>عميل — الباحة | عنوان اللوحة<br>المسقط الأفقي — الدور الأرضي | المقياس<br>1:50 | التاريخ<br>2026-10-23 | رقم اللوحة<br>A-01 (1/11) |

# المسقط الأفقي مع الفرش — الدور الأول

الأبعاد بالسنتيمتر - الجدران: قوائم 7×5 + تلبيس 2.5 من الجهتين (12 سم) | منسوب الأرضية +3.05

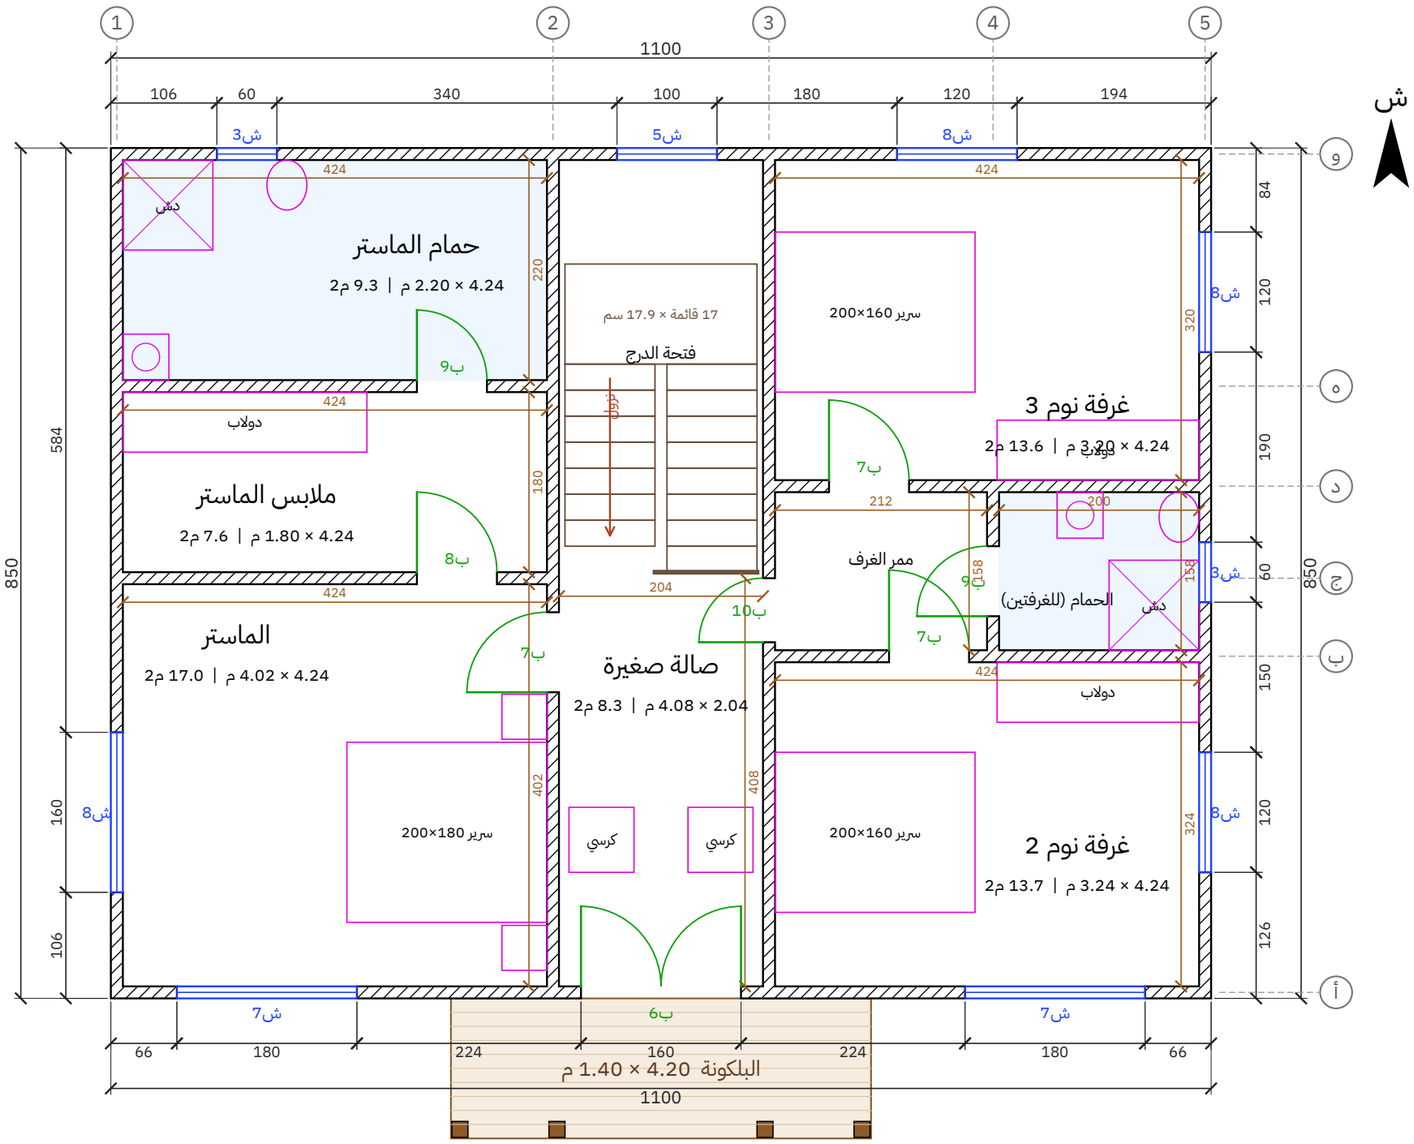


| المشروع / العميل | عنوان اللوحة | المقياس | التاريخ | رقم اللوحة |
|---|---|---|---|---|
| **فيلا خشب دورين — واجهة جملون زجاج وبلكونة — 3 غرف (ماستر) — 11.00 × 8.50 م**<br>**عميل — الباحة** | **المسقط الأفقي — الدور الأول** | **1:50** | **2026-10-23** | **A-02 (2/11)** |

**مصنع وتد الأخشاب**
Watad Wood Factory

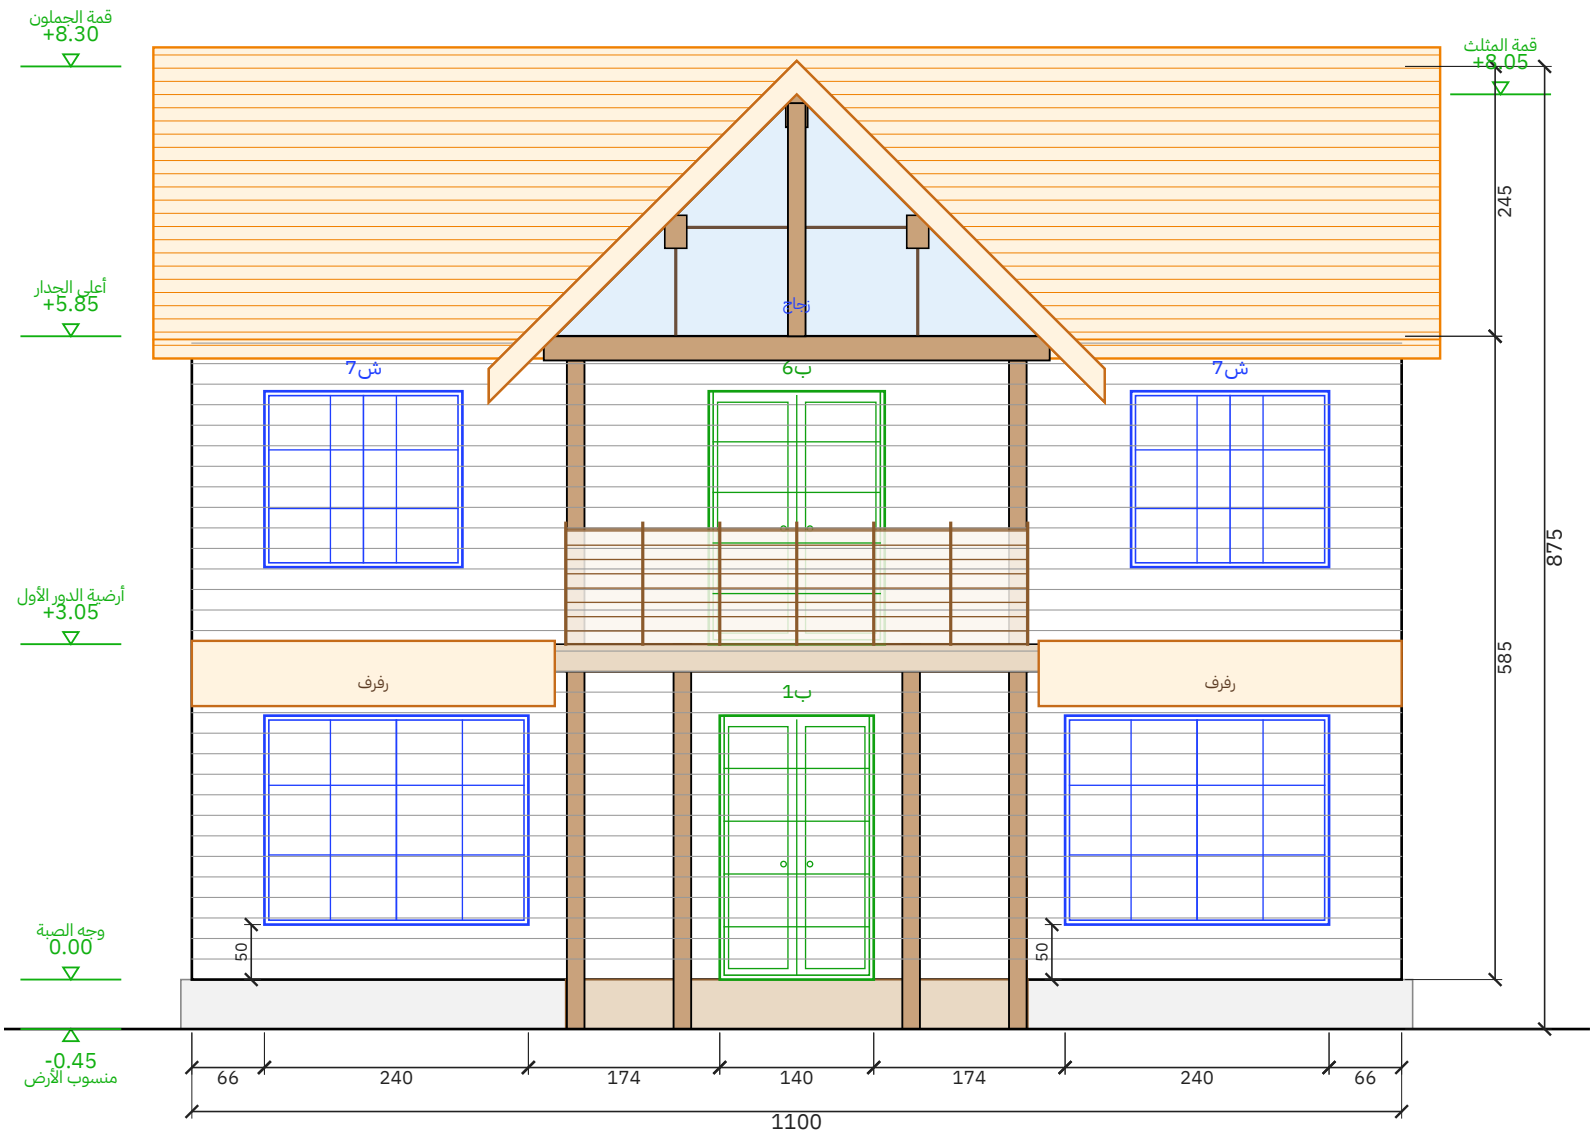


## الواجهة الأمامية

مقياس 1:50 | الوحدة: سم

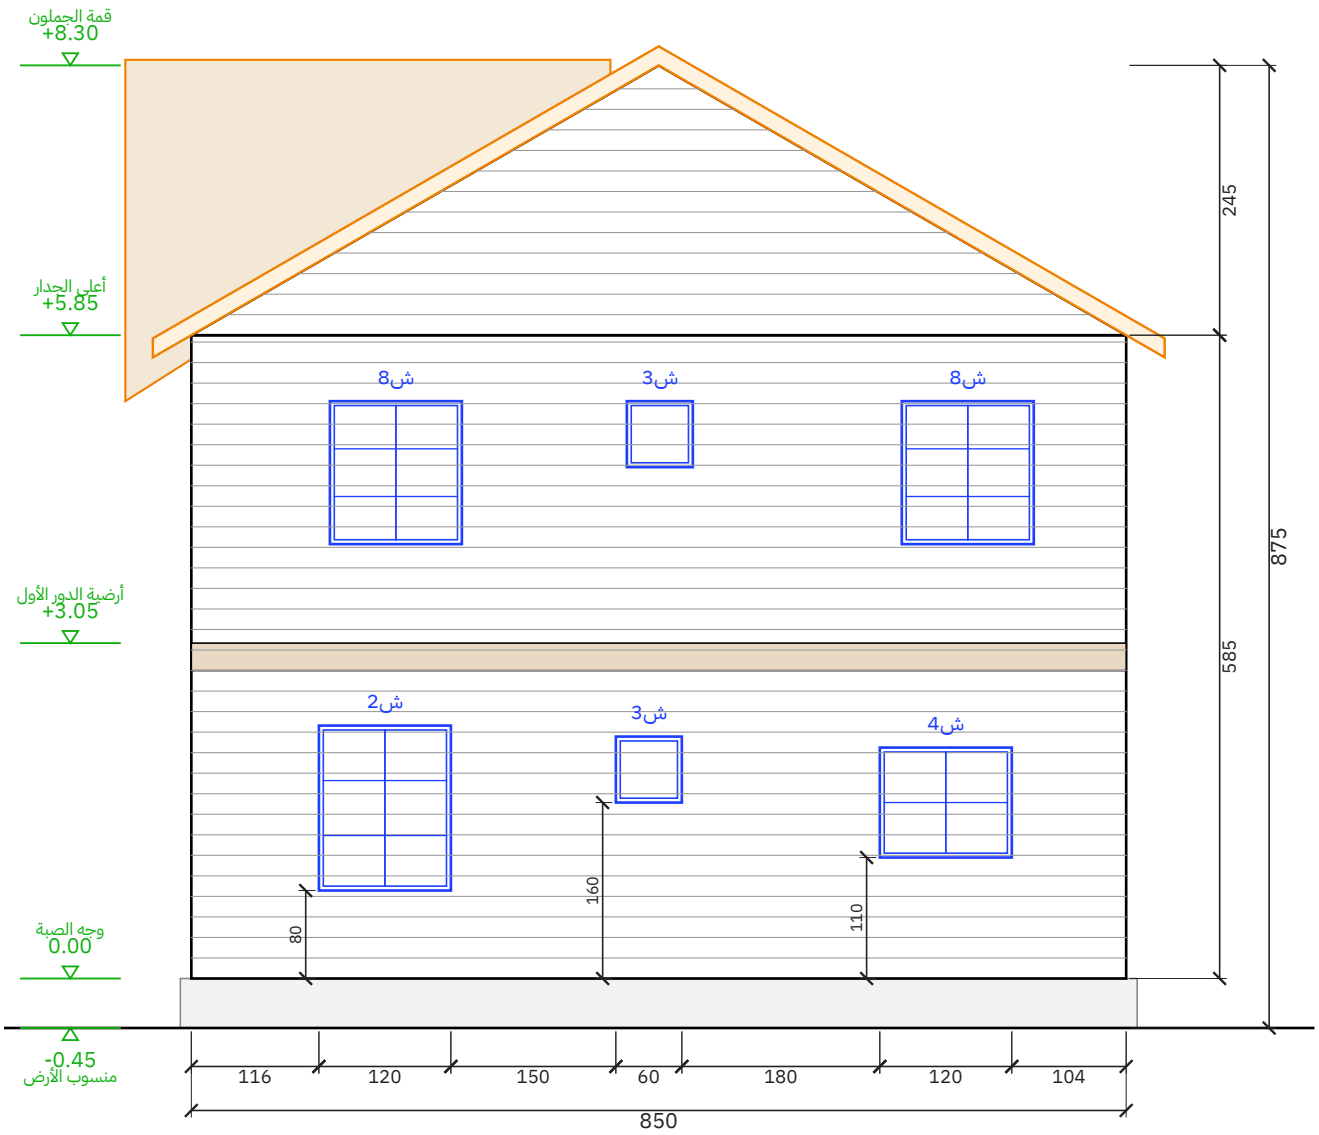


## الواجهة الشرقية

مقياس 1:50 | الوحدة: سم

| | | | | | |
|---|---|---|---|---|---|
| مصنع وتد الأخشاب<br>Watad Wood Factory | المشروع / العميل<br>فيلا خشب دورين – واجهة جملون زجاج وبلكونة – 3 غرف (ماستر) – 11.00 × 8.50 م<br>عميل – الباحة | عنوان اللوحة<br>الواجهة الأمامية والواجهة الشرقية | المقياس<br>1:50 | التاريخ<br>2026-10-23 | رقم اللوحة<br>A-03 (3/11) |

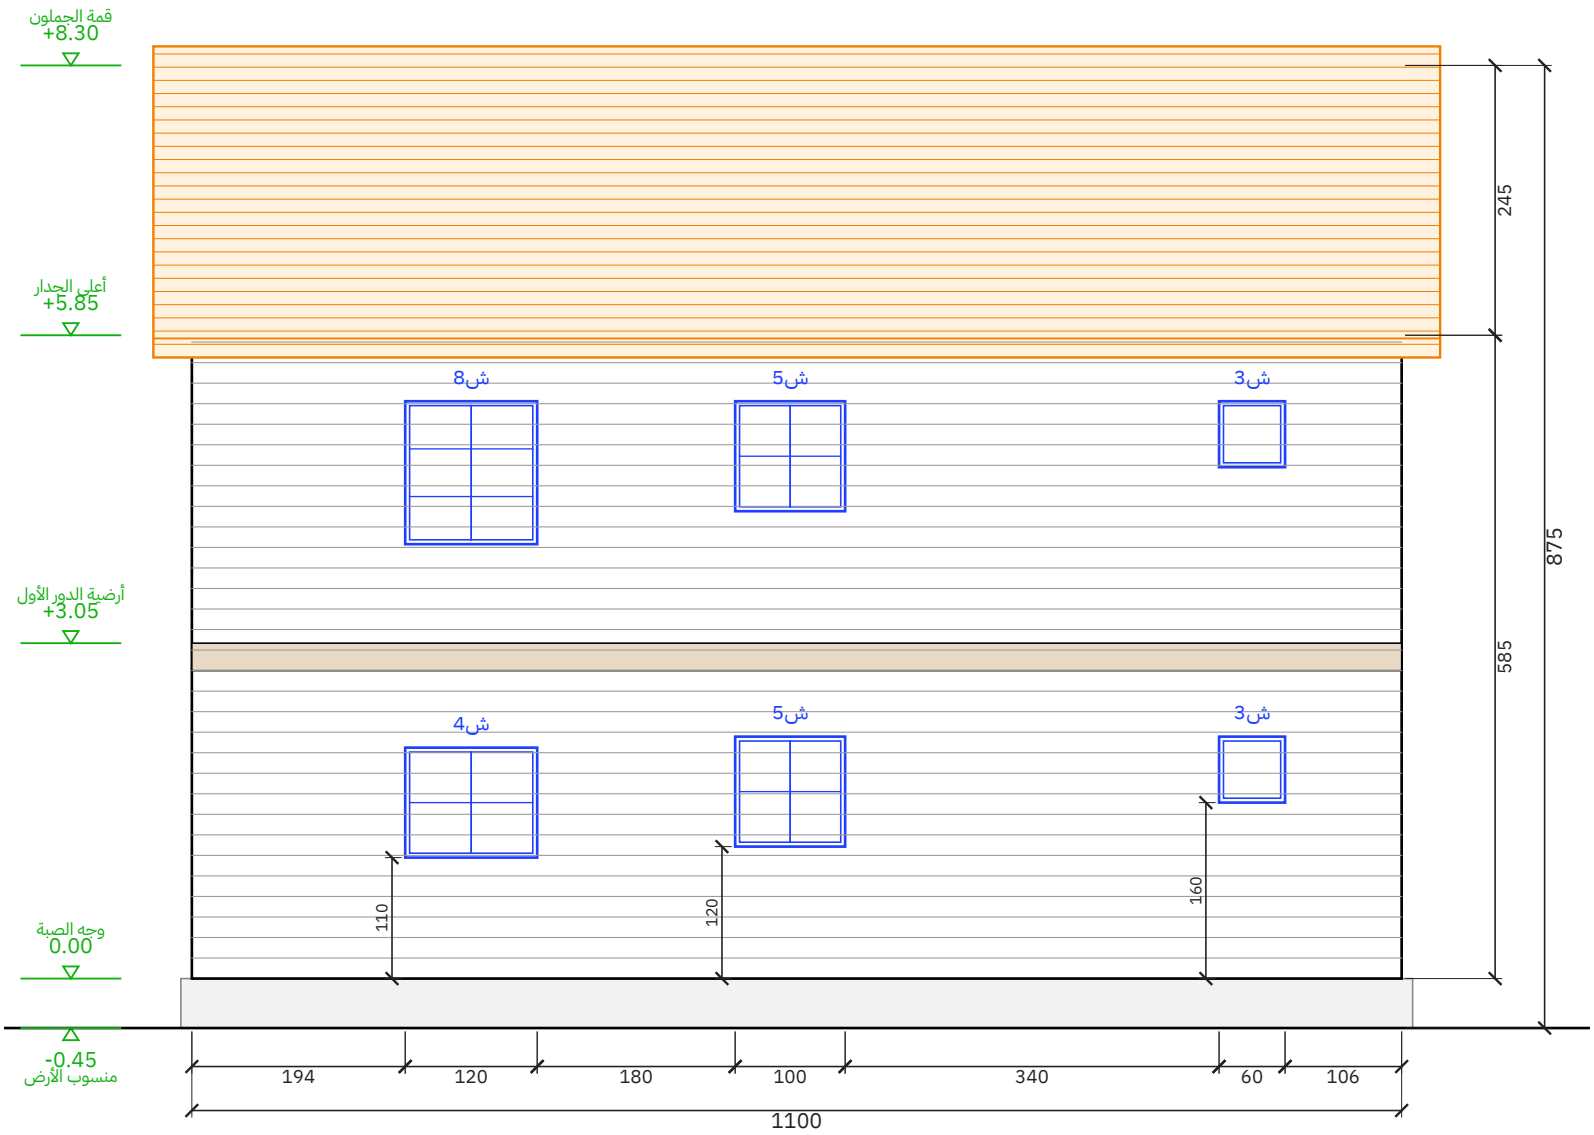


## الواجهة الخلفية

مقياس 1:50 | الوحدة: سم

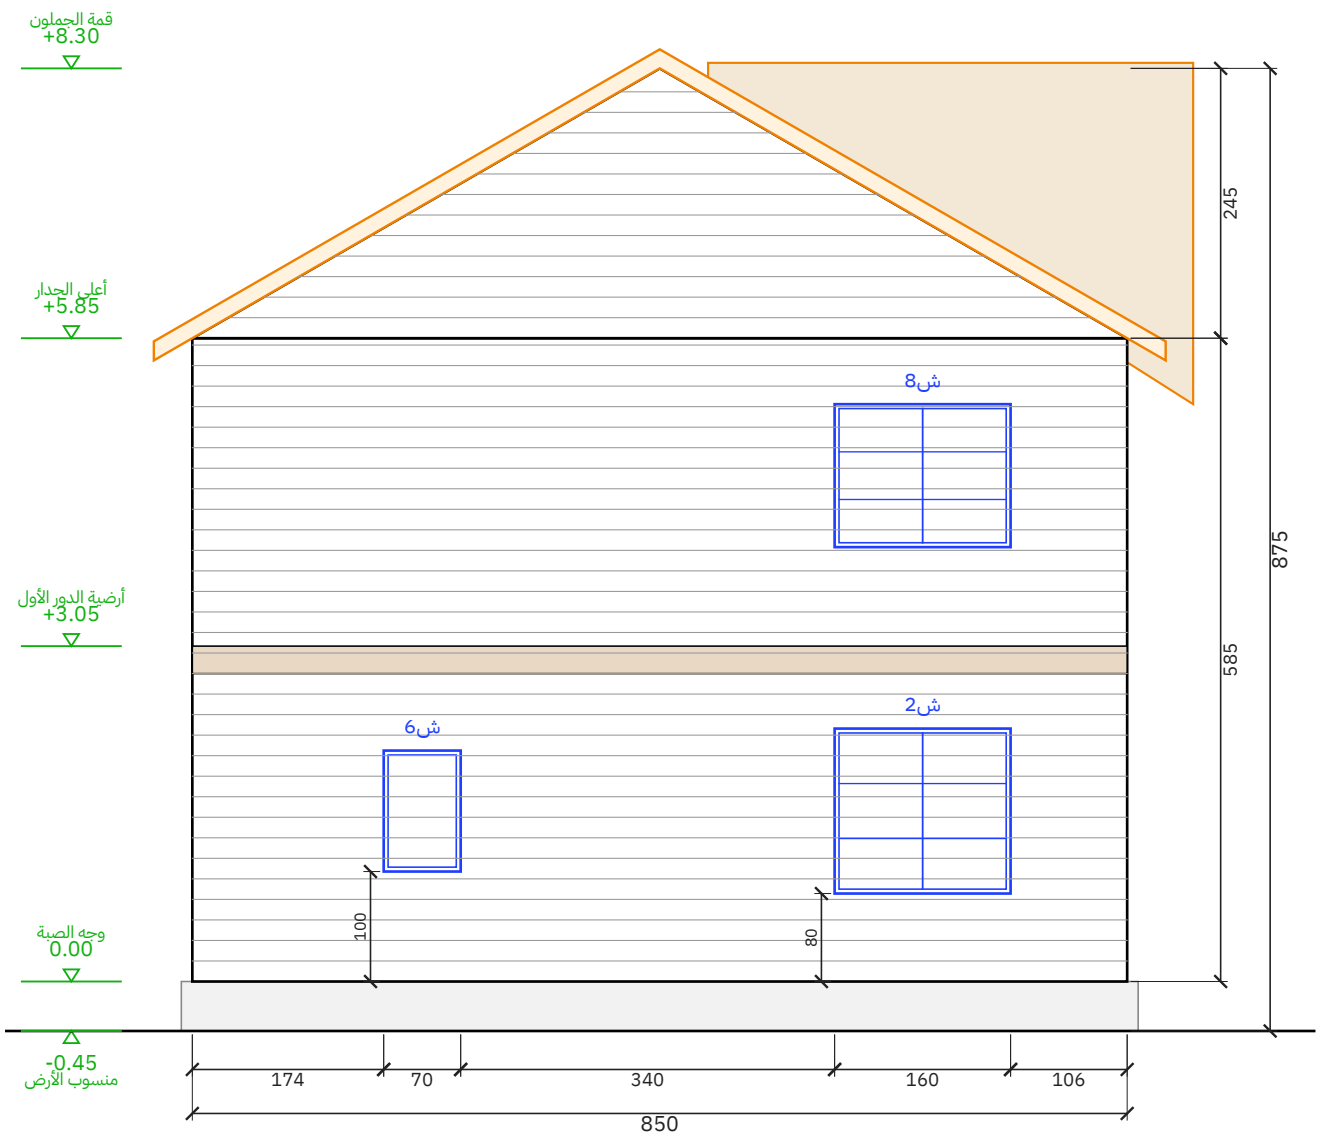


## الواجهة الغربية

مقياس 1:50 | الوحدة: سم

| المشروع / العميل | عنوان اللوحة | المقياس | التاريخ | رقم اللوحة |
|---|---|---|---|---|
| فيلا خشب دورين – واجهة جملون زجاج وبلكونة – 3 غرف (ماستر) – 11.00 × 8.50 م<br>عميل – الباحة | الواجهة الخلفية والواجهة الغربية | 1:50 | 2026-10-23 | A-04 (4/11) |

مصنع وتد الأخشاب
Watad Wood Factory

## قطاع عرضي أ-أ

مقياس 1:50 | الوحدة: سم

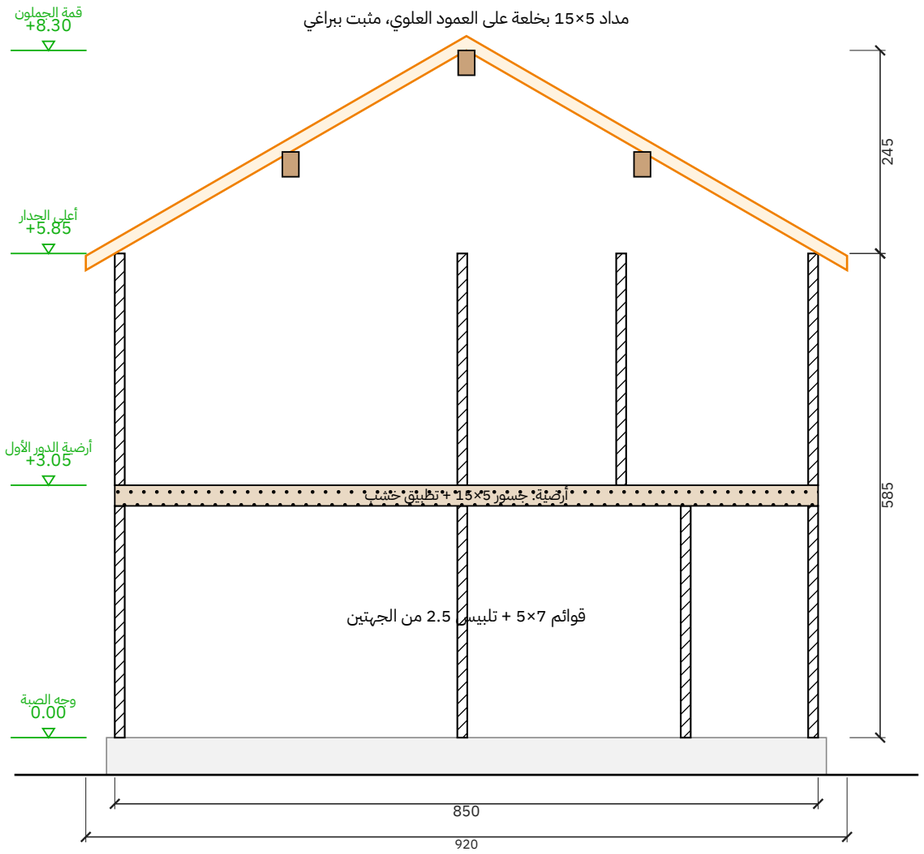


تفصيلة جلوس المداد على العلوي (1:5)

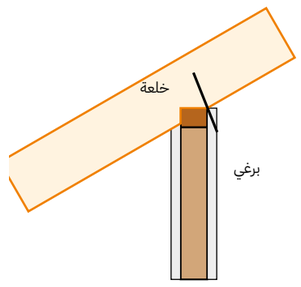


علوي 7×5 على قائم 7×5

## مسقط السقف (جملون)

رفرف 35 سم من كل جهة | مقياس 1:50

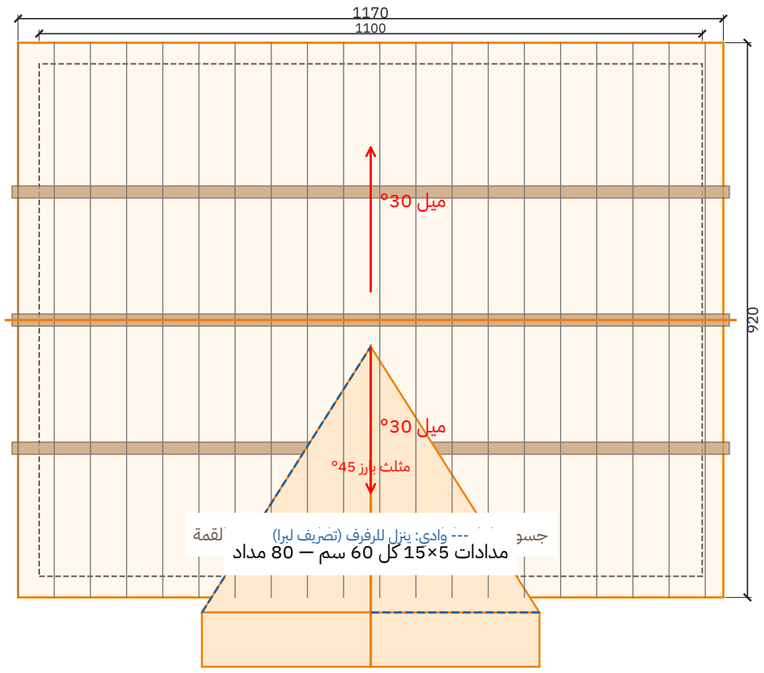


| | | | | |
|---|---|---|---|---|
| المشروع / العميل: فيلا خشب دورين — واجهة جملون زجاج وبلكونة — 3 غرف (ماستر) — 11.00 × 8.50 م — عميل — الباحة | عنوان اللوحة: مسقط السقف والقطاع | المقياس: 1:50 | التاريخ: 2026-10-23 | رقم اللوحة: A-05 (5/11) |

مصنع وتد الأخشاب
Watad Wood Factory

# لقطات المنظور الخارجي

المنظور الأمامي

منظور أمامي من اليسار

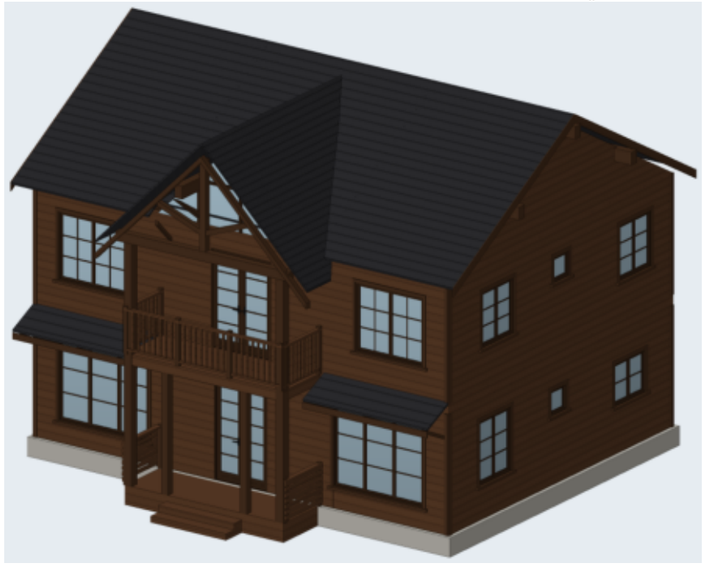

منظور أمامي من اليمين

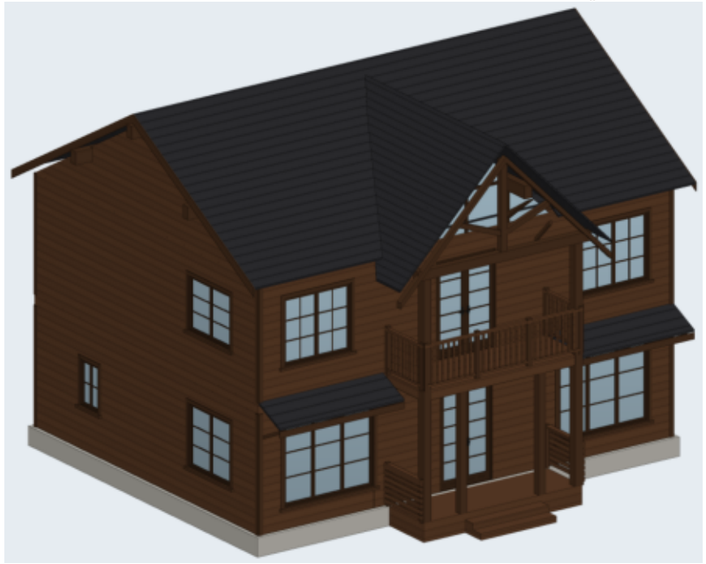

المنظور الخلفي

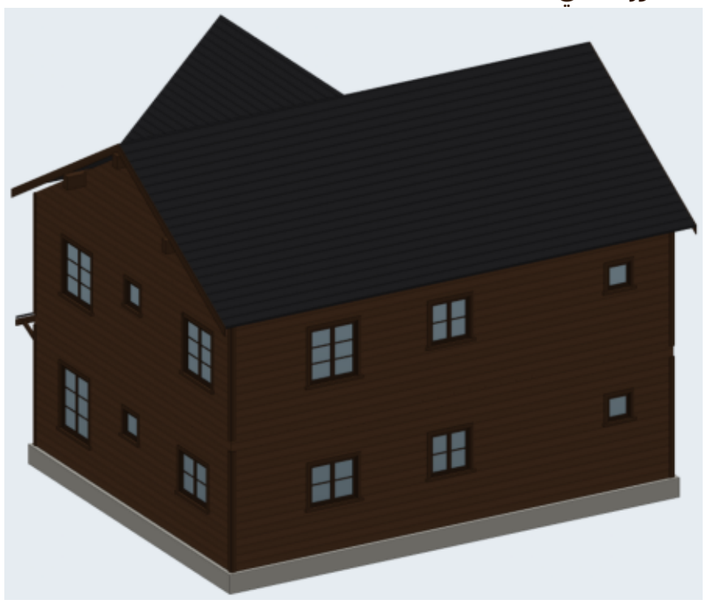

منظور خلفي من اليمين

منظر علوي

| | | | | |
|---|---|---|---|---|
| مصنع وتد الأخشاب<br>Watad Wood Factory | المشروع / العميل<br>فيلا خشب دورين – واجهة جملون زجاج وبلكونة – 3 غرف (ماستر) – 11.00 × 8.50 م<br>عميل – الباحة | عنوان اللوحة<br>لقطات المنظور | المقياس<br>– | التاريخ<br>2026-10-23 | رقم اللوحة<br>A-08 (8/11) |

# المقطع العلوي بالفرش — الدور الأرضي

مقطع أفقي على ارتفاع 1.90 م — توزيع الفرش ومسار الحركة

| | | | | | |
|---|---|---|---|---|---|
| مصنع وتد الأخشاب<br>Watad Wood Factory | المشروع / العميل<br>فيلا خشب دورين — واجهة جملون زجاج وبلكونة — 3 غرف (ماستر) — 11.00 × 8.50 م<br>عميل — الباحة | عنوان اللوحة<br>المقطع العلوي بالفرش — الدور الأرضي | المقياس<br>— | التاريخ<br>2026-10-23 | رقم اللوحة<br>A-09 (9/11) |

# المقطع العلوي بالفرش — الدور الأول

مقطع أفقي على ارتفاع 1.90 م — توزيع الفرش ومسار الحركة

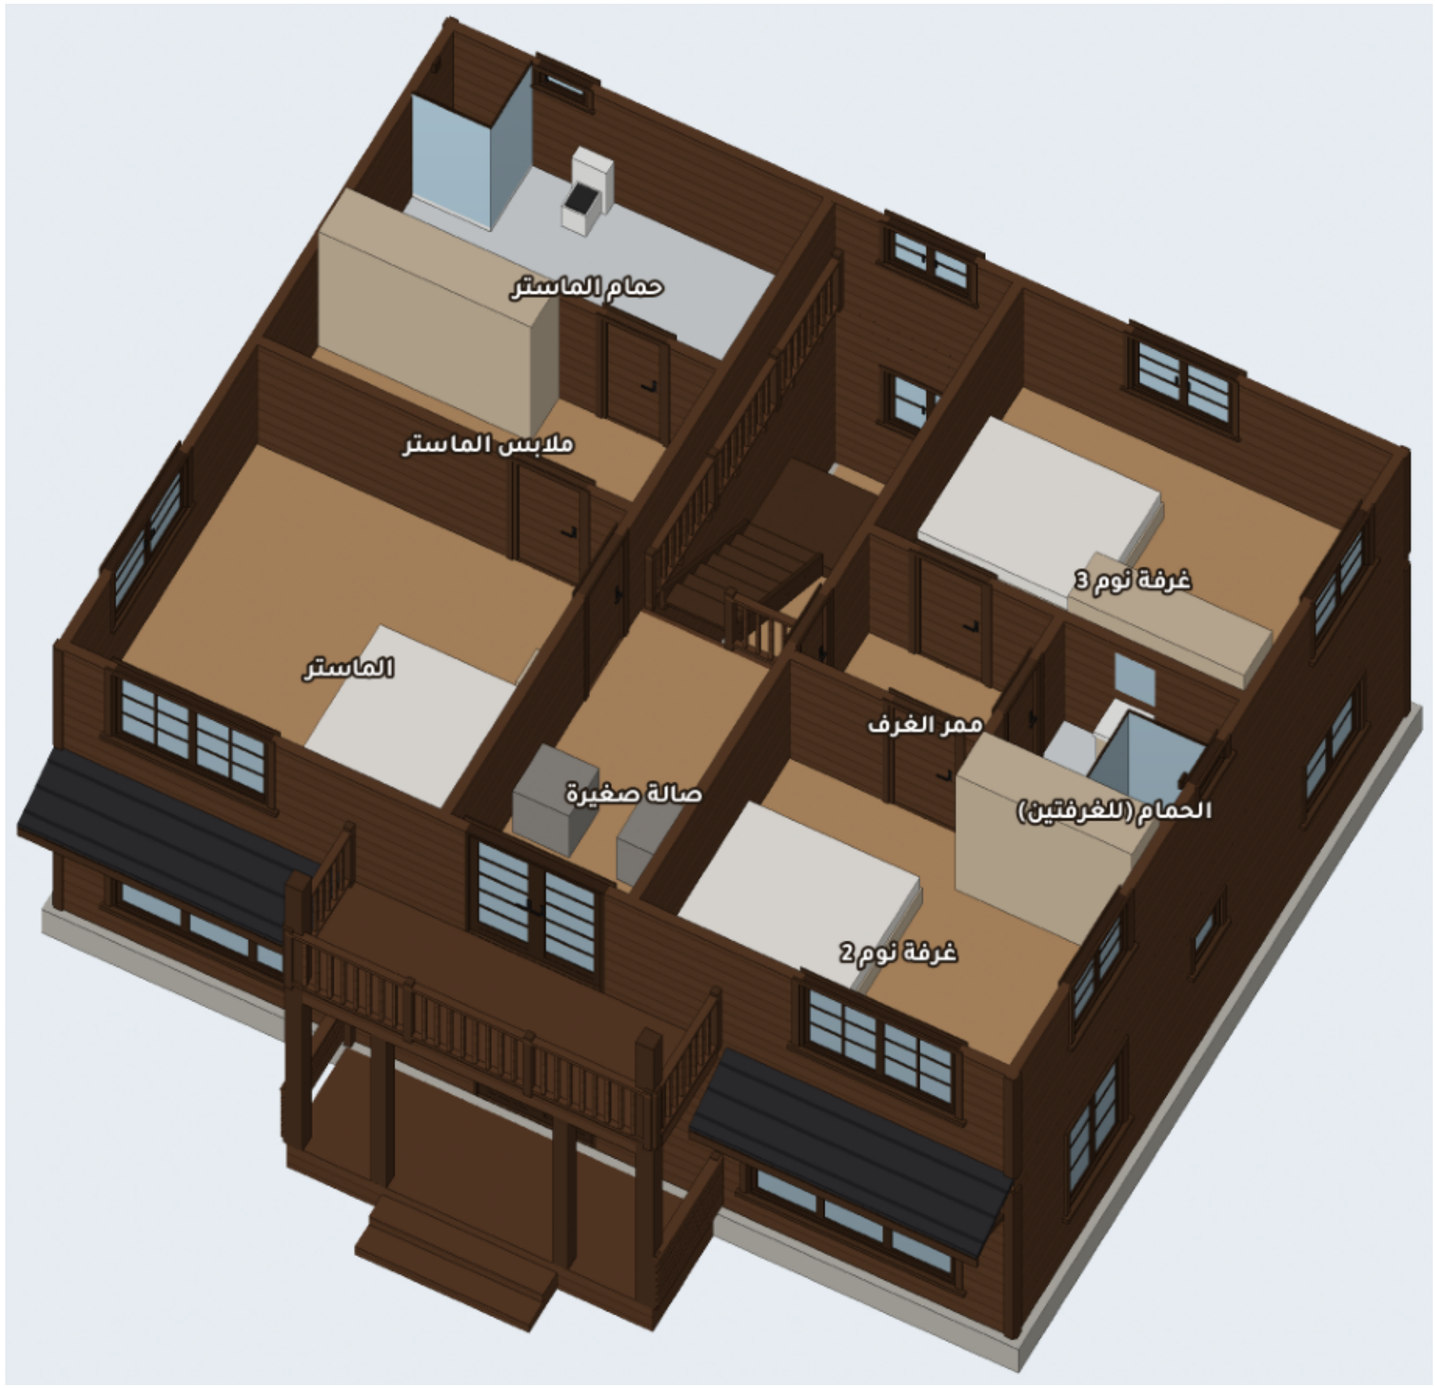


| | | | | |
|---|---|---|---|---|
| مصنع وتد الأخشاب<br>Watad Wood Factory | المشروع / العميل<br>فيلا خشب دورين — واجهة جملون زجاج وبلكونة — 3 غرف (ماستر) — 11.00 × 8.50 م<br>عميل — الباحة | عنوان اللوحة<br>المقطع العلوي بالفرش — الدور الأول | المقياس<br>— | التاريخ<br>2026-10-23 | رقم اللوحة<br>A-10 (10/11) |

مصنع وتد الأخشاب

مصنع وتد الأخشاب

# جدول مقاسات الأبواب والشبابيك

## مقاس الفتحة الصافي في الجدار - الوحدة: سم

| الرمز | النوع | العرض (سم) | الارتفاع (سم) | ارتفاع الجلسة (سم) | العدد | الموقع |
|---|---|---|---|---|---|---|
| ب1 | باب مزدوج | 140 | 240 | - | 1 | الأمامية |
| ب10 | باب | 64 | 210 | - | 1 | ممر الغرف |
| ب2 | باب | 80 | 210 | - | 1 | غرفة العاملة |
| ب3 | باب | 64 | 210 | - | 1 | دورة مياه العاملة |
| ب3 | باب | 70 | 210 | - | 1 | الغسيل |
| ب4 | باب | 70 | 210 | - | 1 | دورة الضيوف |
| ب5 | باب | 90 | 210 | - | 1 | المطبخ |
| ب6 | باب مزدوج | 160 | 230 | - | 1 | الأمامية (البلكونة) |
| ب7 | باب | 80 | 210 | - | 3 | الماستر - غرفة 2 - غرفة 3 |
| ب8 | باب | 80 | 210 | - | 1 | ملابس الماستر |
| ب9 | باب | 70 | 210 | - | 2 | حمام الماستر - الحمام (للغرفتين) |
| ف1 | باب | 190 | 240 | - | 1 | الصالة — المدخل |
| ف2 | باب | 240 | 240 | - | 1 | الطعام — المدخل |
| ف3 | باب | 160 | 220 | - | 1 | الطعام — الموزع |
| ش1 | شباك | 240 | 190 | 50 | 2 | الأمامية 2 |
| ش2 | شباك | 120 | 150 | 80 | 1 | الشرقية |
| ش2 | شباك | 160 | 150 | 80 | 1 | الغربية |
| ش3 | شباك | 60 | 60 | 160 | 4 | الشرقية 2 - الخلفية 2 |
| ش4 | شباك | 120 | 100 | 110 | 2 | الشرقية - الخلفية |
| ش5 | شباك | 100 | 100 | 120 | 2 | الخلفية 2 |
| ش6 | شباك | 70 | 110 | 100 | 1 | الغربية |
| ش7 | شباك | 180 | 160 | 70 | 2 | الأمامية (البلكونة) 2 |
| ش8 | شباك | 120 | 130 | 90 | 3 | الشرقية 2 - الخلفية |
| ش8 | شباك | 160 | 130 | 90 | 1 | الغربية |

الإجمالي: أبواب 17 - شبابيك 19

# المنظور ثلاثي الأبعاد والمواد

النمط: جوزي غامق + إطارات سوداء — رندر واقعي بخامات حقيقية

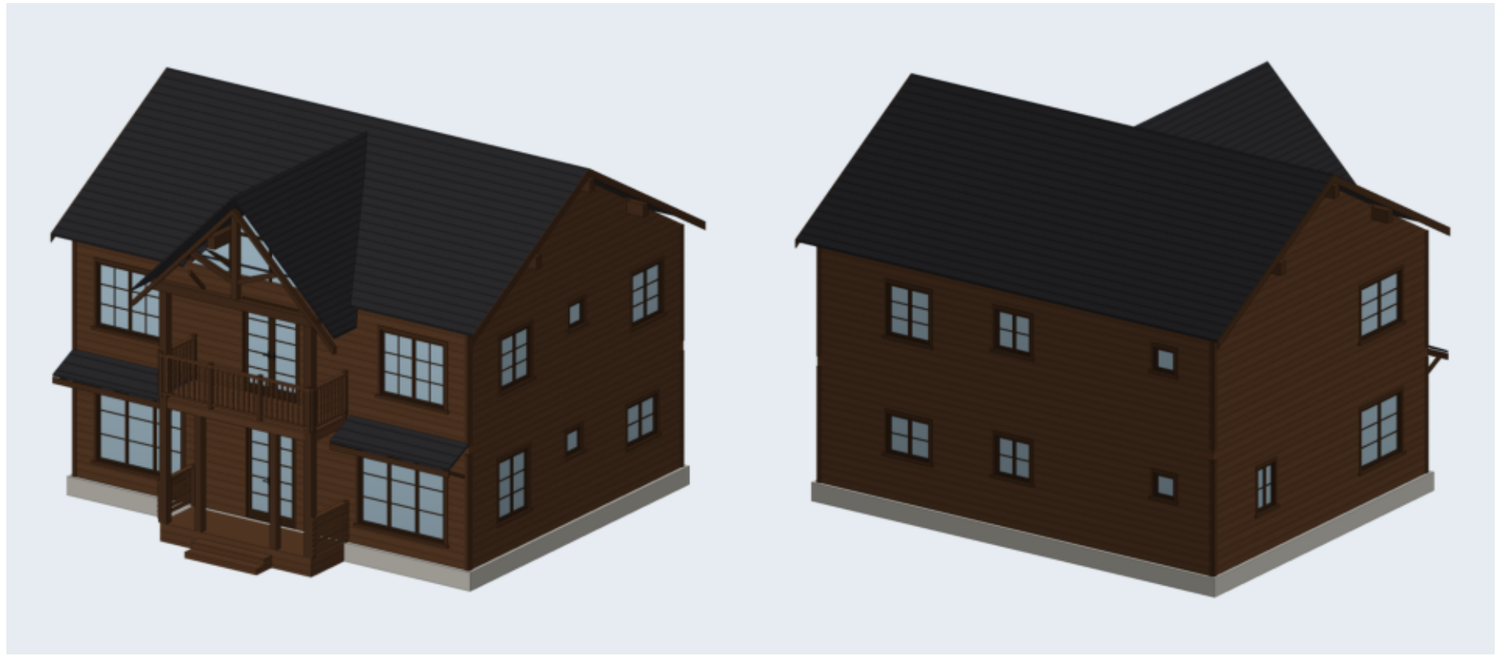

## جدول المواد والألوان

**الخشب / الصبغة**

صبغة جوزي غامق

**القرميد**

قرميد رمادي غامق

**الزجاج**

زجاج شفاف

**إطارات الشبابيك والأبواب**

إطار خشب بنفس الصبغة أغمق

**الكنار والزوايا**

نفس الصبغة أغمق درجة

**الصبة**

خرسانة 45 سم

الدربزين: ألواح أفقية متقاربة (عصري)

تقسيم الشبابيك: شبكة | الباب الرئيسي: زجاج بتقسيمات (فرنسي)

## أنواع الدربزين المعتمدة (من مشاريع المصنع)

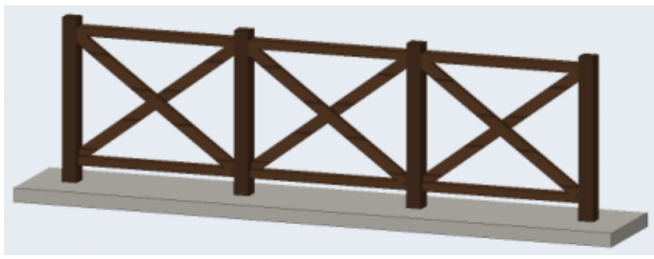

تقاطع X (صورة 5)

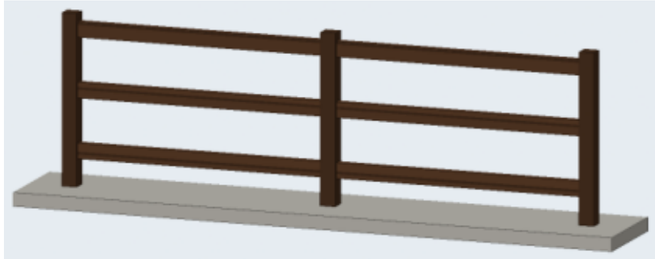

3 مرابيع أفقية (صورة 2)

قوائم رأسية متقاربة (صورة 1)

| المشروع / العميل | عنوان اللوحة | المقياس | التاريخ | رقم اللوحة |
|---|---|---|---|---|
| **مصنع وتد الأخشاب** Watad Wood Factory — **فيلا خشب دورين — واجهة جملون زجاج وبلكونة — 3 غرف (ماستر) — 11.00 × 8.50 م** — **عميل — الباحة** | **المنظور والمواد** | — | **2026-10-23** | **A-11 (11/11)** |

# جدول المساحات وبيانات المشروع والتسعير

## بيانات المشروع

| البند | البيان |
|---|---|
| المشروع | فيلا خشب دورين — واجهة جملون زجاج وبلكونة — 3 غرف (ماستر) — 11.00 × 8.50 م |
| العميل | عميل — الباحة |
| الموقع | الباحة |
| الاستخدام | سكن عائلي |
| التاريخ | 2026-10-23 |
| نظام البناء | هيكل خشب 7×5 + تلبيس 2.5 سم من الجهتين |
| السقف | جملون 30° — قرميد معدني + 1 مثلث بارز |

## التسعير المفصّل

| البند | المبلغ (ريال) |
|---|---|
| الكوخ المبني 187.00 م² × 1,500 | 280,500 |
| البرندة + البلكونة (4.20 × 1.40 × 2) — 11.76 م² × 1,500 | 17,640 |
| **الإجمالي (ريال)** | **298,140** |

**ملاحظات:**

- السعر 1,500 ر.س/م² للدورين حسب المخطط المعتمد — شامل الصبة (بصمة المبنى 11.00 × 8.50 م).
- شامل أدوات التأسيس للسباكة والكهرباء (التمديدات الداخلية).
- التوصيلات الخارجية (عداد الكهرباء والمويه والصرف) على العميل.

## جدول المساحات

| م | الفراغ | الأبعاد (م) | المساحة (م2) |
|---|---|---|---|
| 1 | أرضي — الصالة | 4.24 × 4.02 | 17.04 |
| 2 | أرضي — المدخل | 2.04 × 4.08 | 8.32 |
| 3 | أرضي — الطعام | 4.24 × 3.24 | 13.74 |
| 4 | أرضي — الموزع | 2.12 × 1.58 | 3.35 |
| 5 | أرضي — دورة الضيوف | 2.00 × 1.58 | 3.16 |
| 6 | أرضي — المطبخ | 4.24 × 3.20 | 13.57 |
| 7 | أرضي — الدرج | 1.92 × 4.12 | 7.91 |
| 8 | أرضي — غرفة العاملة | 4.24 × 2.58 | 10.94 |
| 9 | أرضي — دورة مياه العاملة | 1.94 × 1.42 | 2.75 |
| 10 | أرضي — الغسيل | 2.18 × 1.42 | 3.10 |
| 11 | أول — الماستر | 4.24 × 4.02 | 17.04 |
| 12 | أول — صالة صغيرة | 2.04 × 4.08 | 8.32 |
| 13 | أول — ملابس الماستر | 4.24 × 1.80 | 7.63 |
| 14 | أول — حمام الماستر | 4.24 × 2.20 | 9.33 |
| 15 | أول — غرفة نوم 2 | 4.24 × 3.24 | 13.74 |
| 16 | أول — ممر الغرف | 2.12 × 1.58 | 3.35 |
| 17 | أول — الحمام (للغرفتين) | 2.00 × 1.58 | 3.16 |
| 18 | أول — غرفة نوم 3 | 4.24 × 3.20 | 13.57 |
|  | المساحة الصافية الداخلية |  | 160.03 |
|  | **البرندة** | **4.20 × 1.40** | **5.88** |
|  | **البلكونة** | **4.20 × 1.40** | **5.88** |
|  | **المساحة الإجمالية المبنية** | **11.00 × 8.50 × 2 دور** | **187.00** |
|  | **المساحة الكلية (المبنية + التراس والبلكونة)** |  | **198.76** |