
المنظور ثلاثي الأبعاد والمواد

النمط: جوزي غامق + إطارات سوداء — رندر واقعي بخامات حقيقية

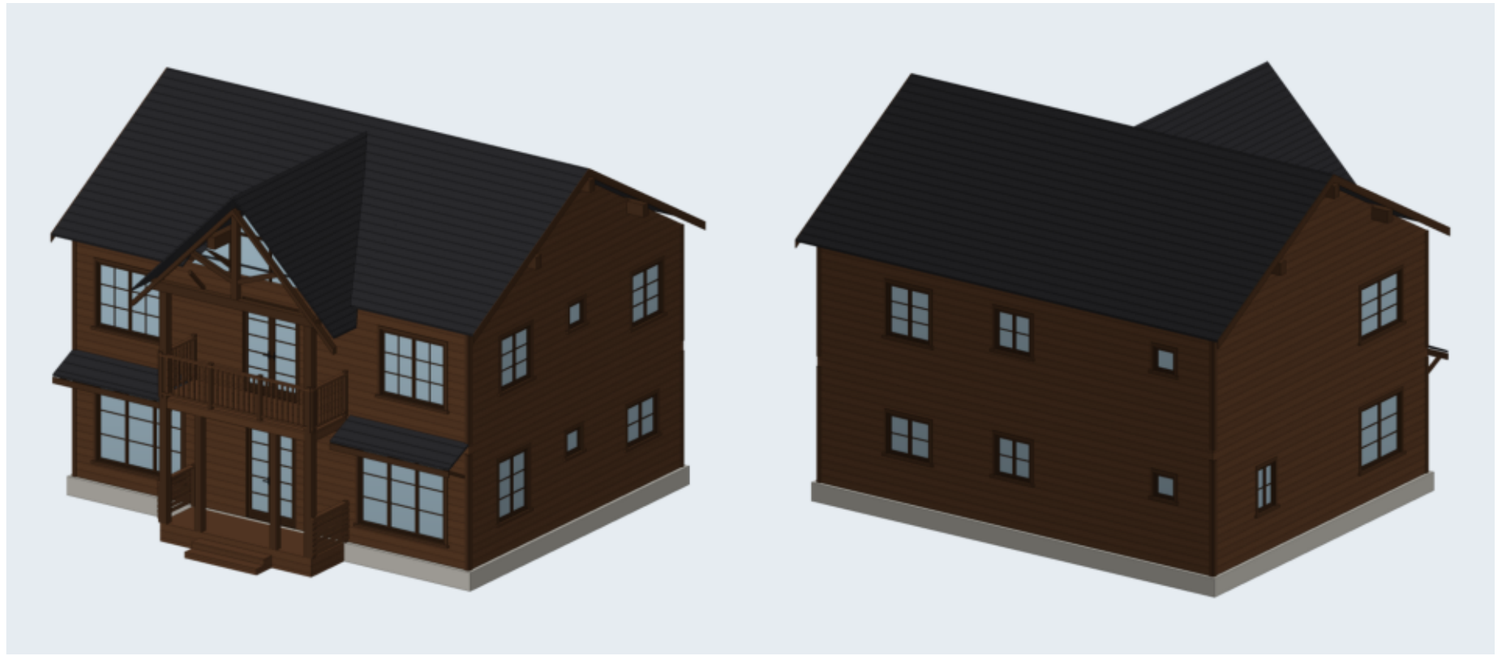

جدول المواد والألوان

الخشب / الصبغة

صبغة جوزي غامق

القرميد

قرميد رمادي غامق

الزجاج

زجاج شفاف

إطارات الشبابيك والأبواب

إطار خشب بنفس الصبغة أغمق

الكنار والزوايا

نفس الصبغة أغمق درجة


الصبة

خرسانة 45 سم


الدربزين: ألواح أفقية متقاربة (عصري)

تقسيم الشبابيك: شبكة | الباب الرئيسي: زجاج بتقسيمات (فرنسي)

أنواع الدربزين المعتمدة (من مشاريع المصنع)

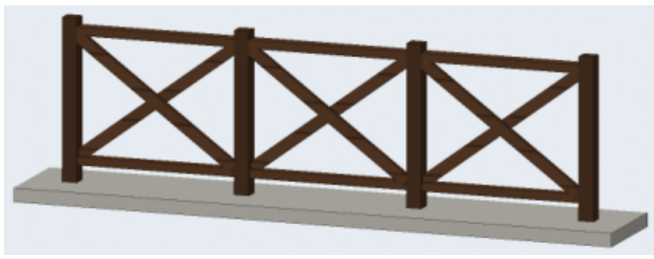

تقاطع X (صورة 5)

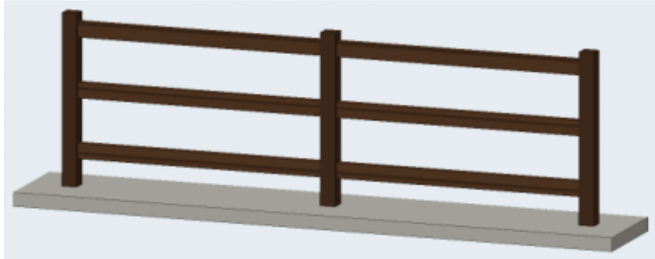

3 مرابيع أفقية (صورة 2)




قوائم رأسية متقاربة (صورة 1)

مصنع وتد الأخشاب Watad Wood Factory	المشروع / العميل **فيلا خشب دورين – واجهة جملون زجاج وبلكونة – 3 غرف (ماستر) – 11.00 × 8.50 م** **عميل – الباحة**	عنوان اللوحة **المنظور والمواد**	المقياس **1:50**	التاريخ **2026-10-23**	رقم اللوحة **W-01 (1/23)**

المسقط الأفقي مع الفرش — الدور الأرضي

الأبعاد بالسنتيمتر - الجدران: قوائم 7×5 + تلبيس 2.5 من الجهتين (12 سم) | منسوب الأرضية +0.00

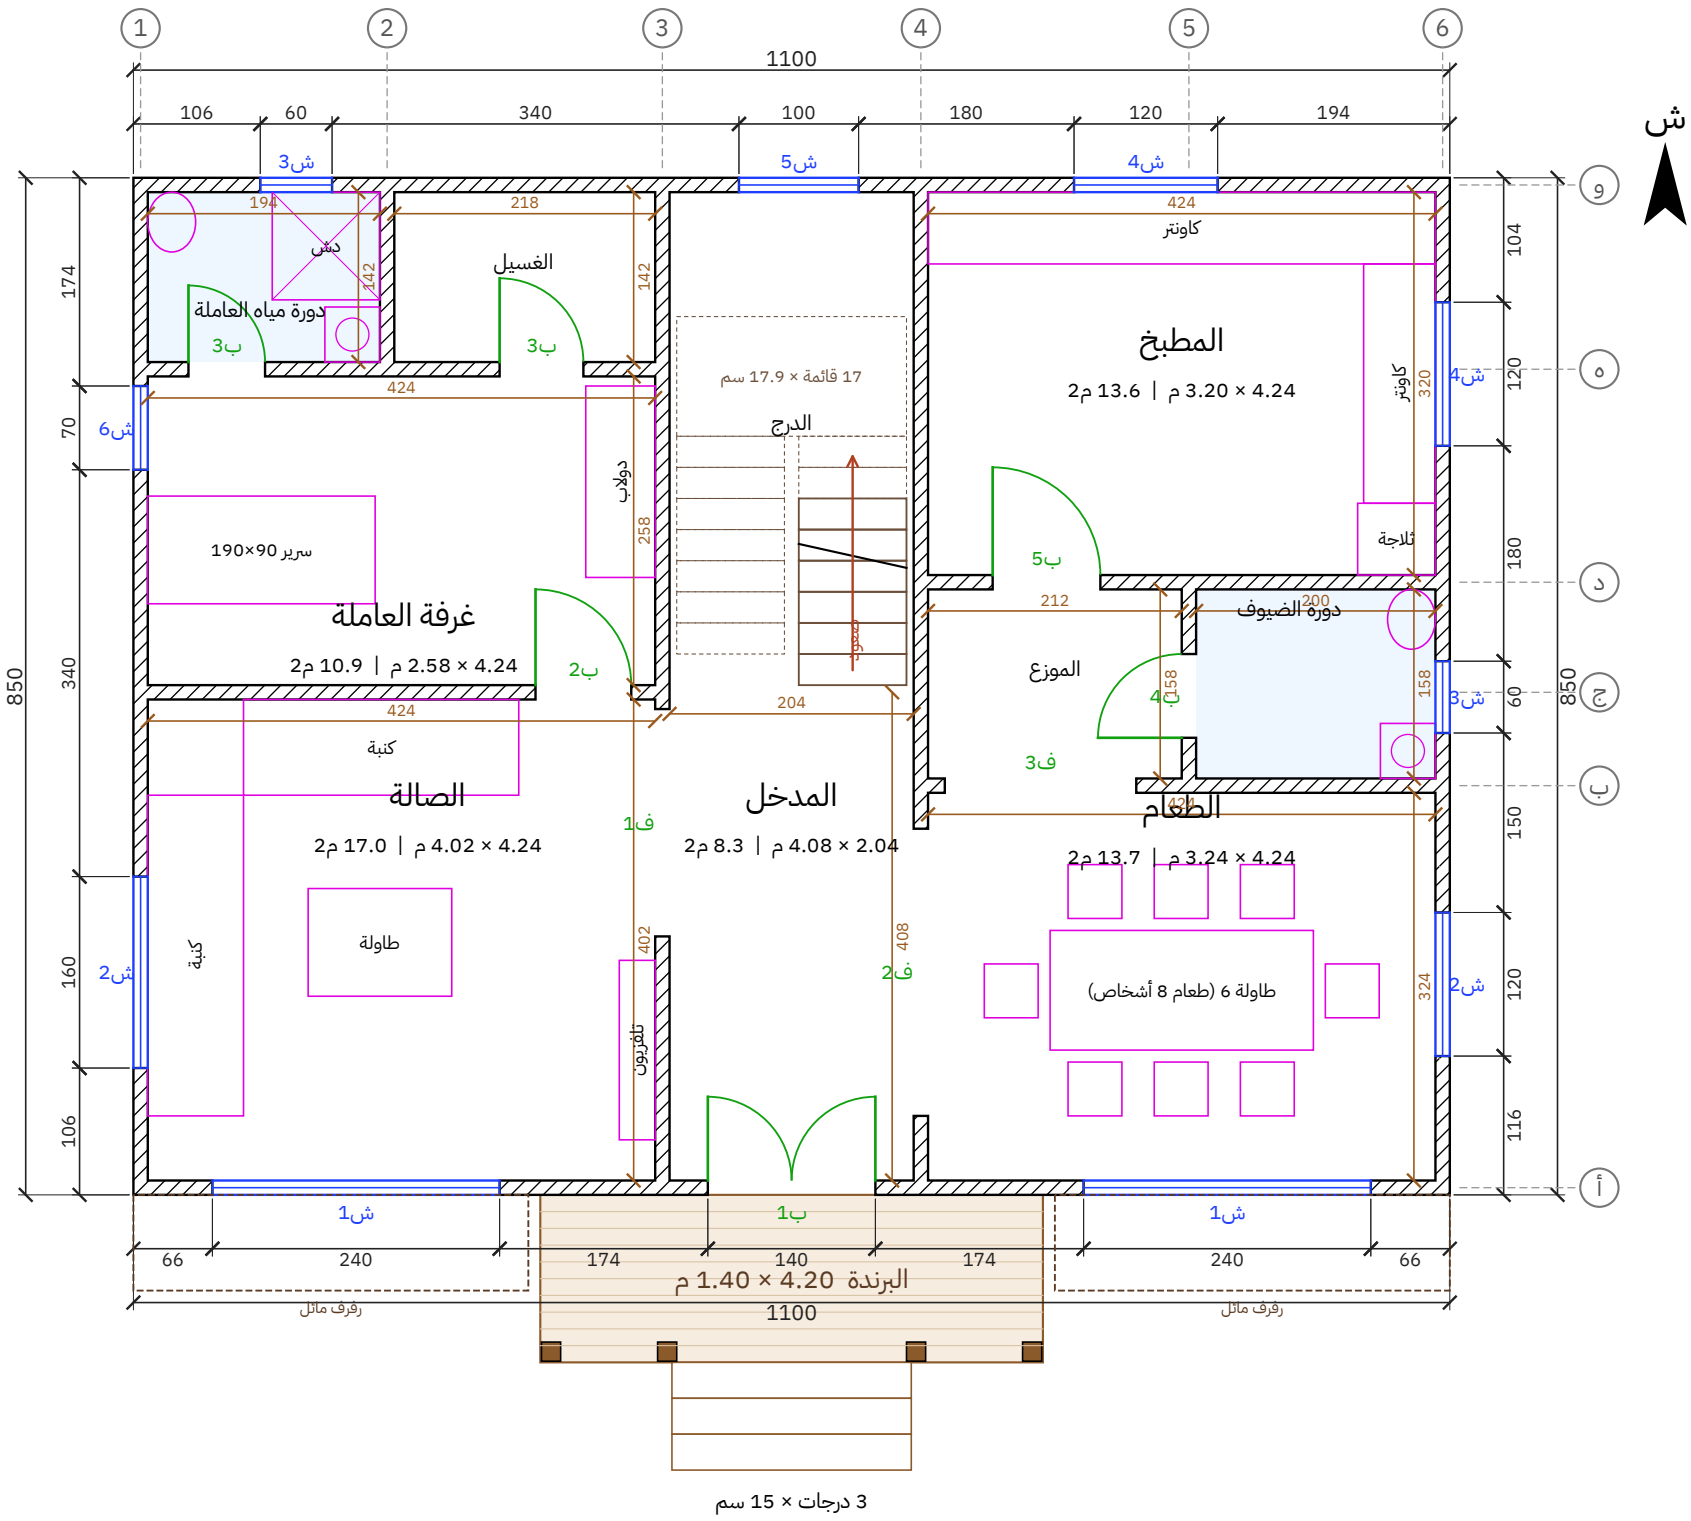


المشروع / العميل	عنوان اللوحة	المقياس	التاريخ	رقم اللوحة
فيلا خشب دورين — واجهة جملون زجاج وبلكونة — 3 غرف (ماستر) — 11.00 × 8.50 م عميل — الباحة	المسقط الأفقي — الدور الأرضي	1:50	2026-10-23	W-02 (2/23)

مصنع وتد الأخشاب
Watad Wood Factory


المسقط الأفقي مع الفرش — الدور الأول

الأبعاد بالسنتيمتر - الجدران: قوائم 7×5 + تلبيس 2.5 من الجهتين (12 سم) | منسوب الأرضية +3.05

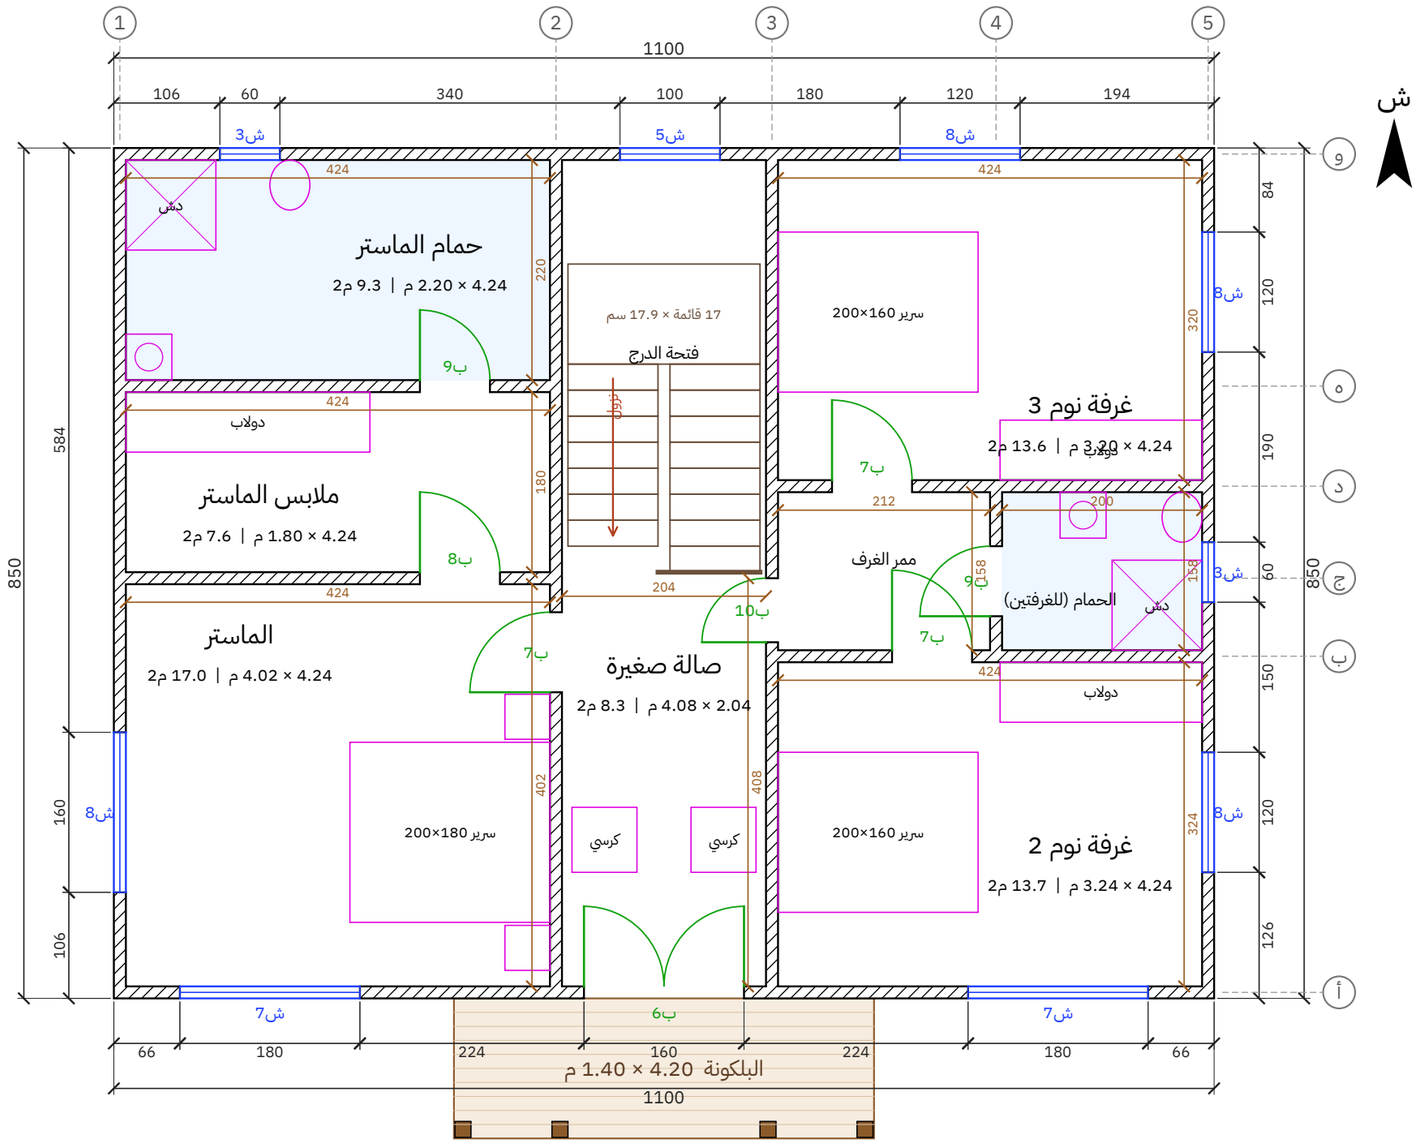


المشروع / العميل	عنوان اللوحة	المقياس	التاريخ	رقم اللوحة
فيلا خشب دورين — واجهة جملون زجاج وبلكونة — 3 غرف (ماستر) — 11.00 × 8.50 م **عميل — الباحة**	**المسقط الأفقي — الدور الأول**	**1:50**	**2026-10-23**	**W-03 (3/23)**

مصنع وتد الأخشاب
Watad Wood Factory

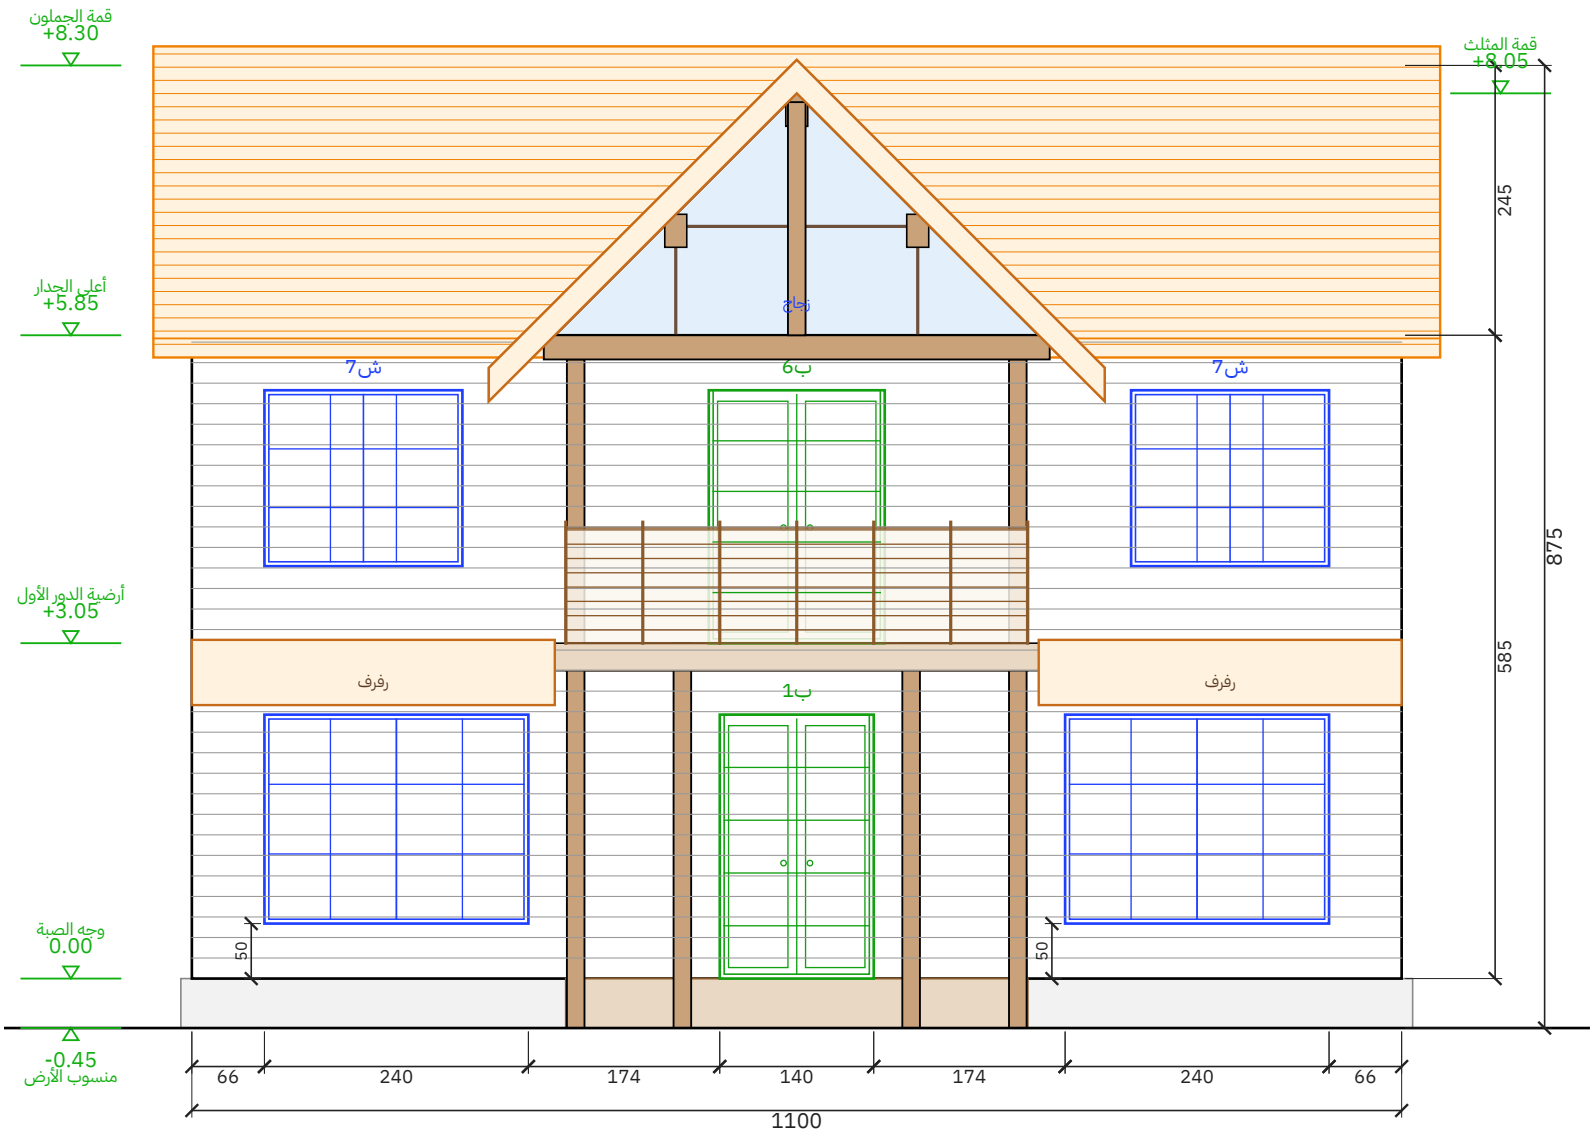

الواجهة الأمامية


مقياس 1:50 | الوحدة: سم

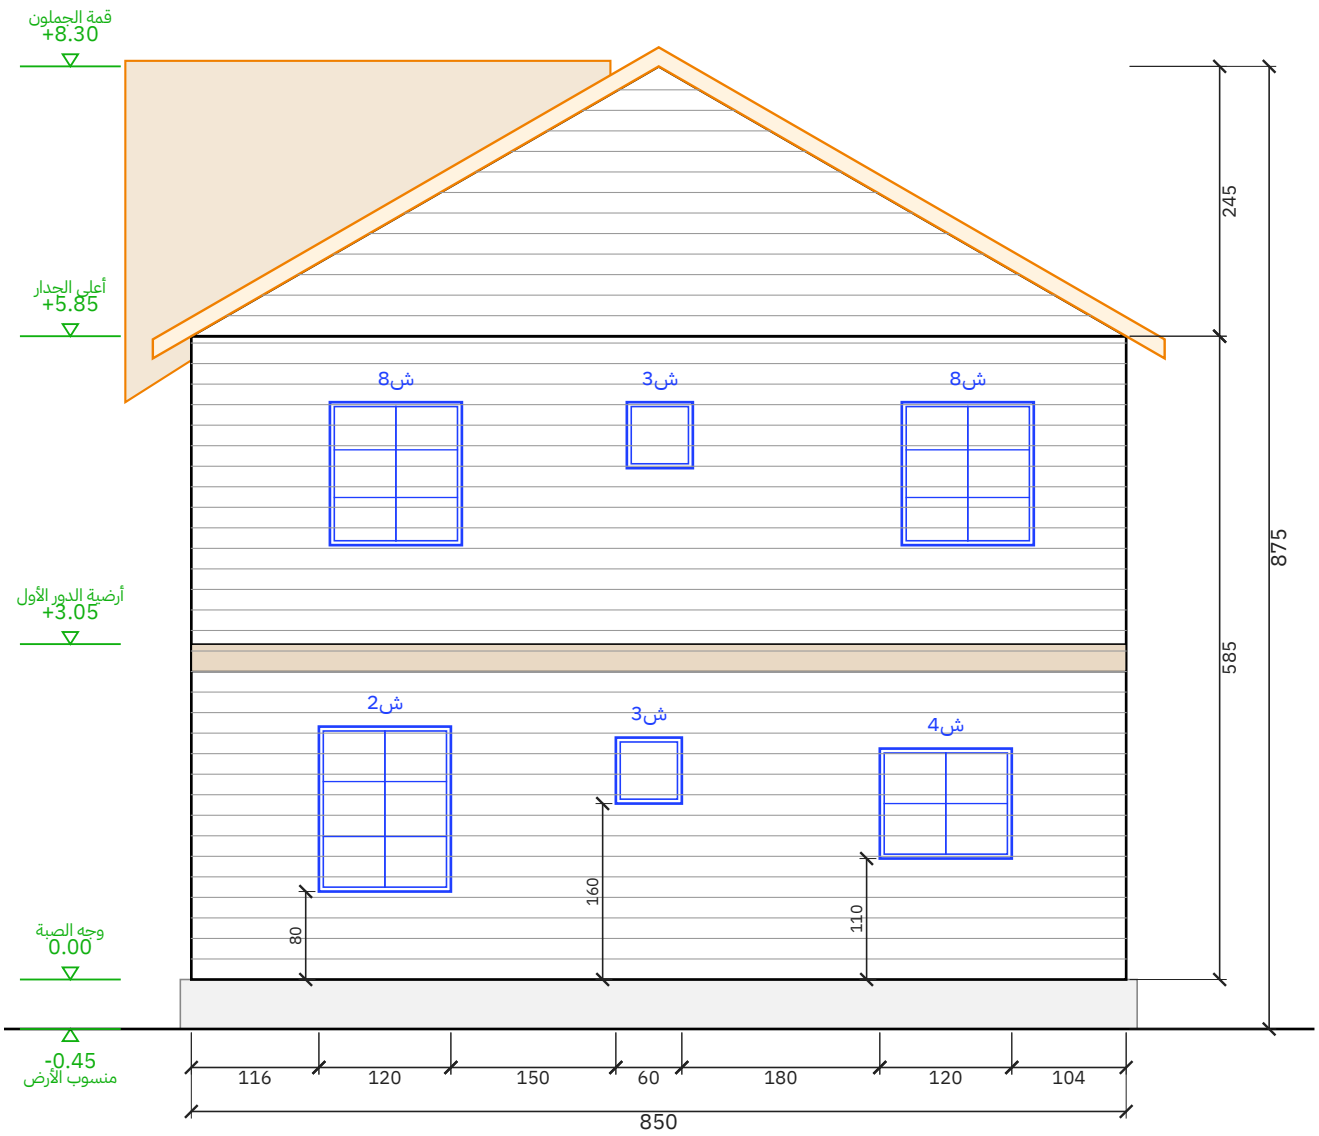

الواجهة الشرقية


مقياس 1:50 | الوحدة: سم

مصنع وتد الأخشاب Watad Wood Factory	المشروع / العميل فيلا خشب دورين – واجهة جملون زجاج وبلكونة – 3 غرف (ماستر) – 11.00 × 8.50 م عميل – الباحة	عنوان اللوحة الواجهة الأمامية والواجهة الشرقية	المقياس 1:50	التاريخ 2026-10-23	رقم اللوحة W-04 (4/23)

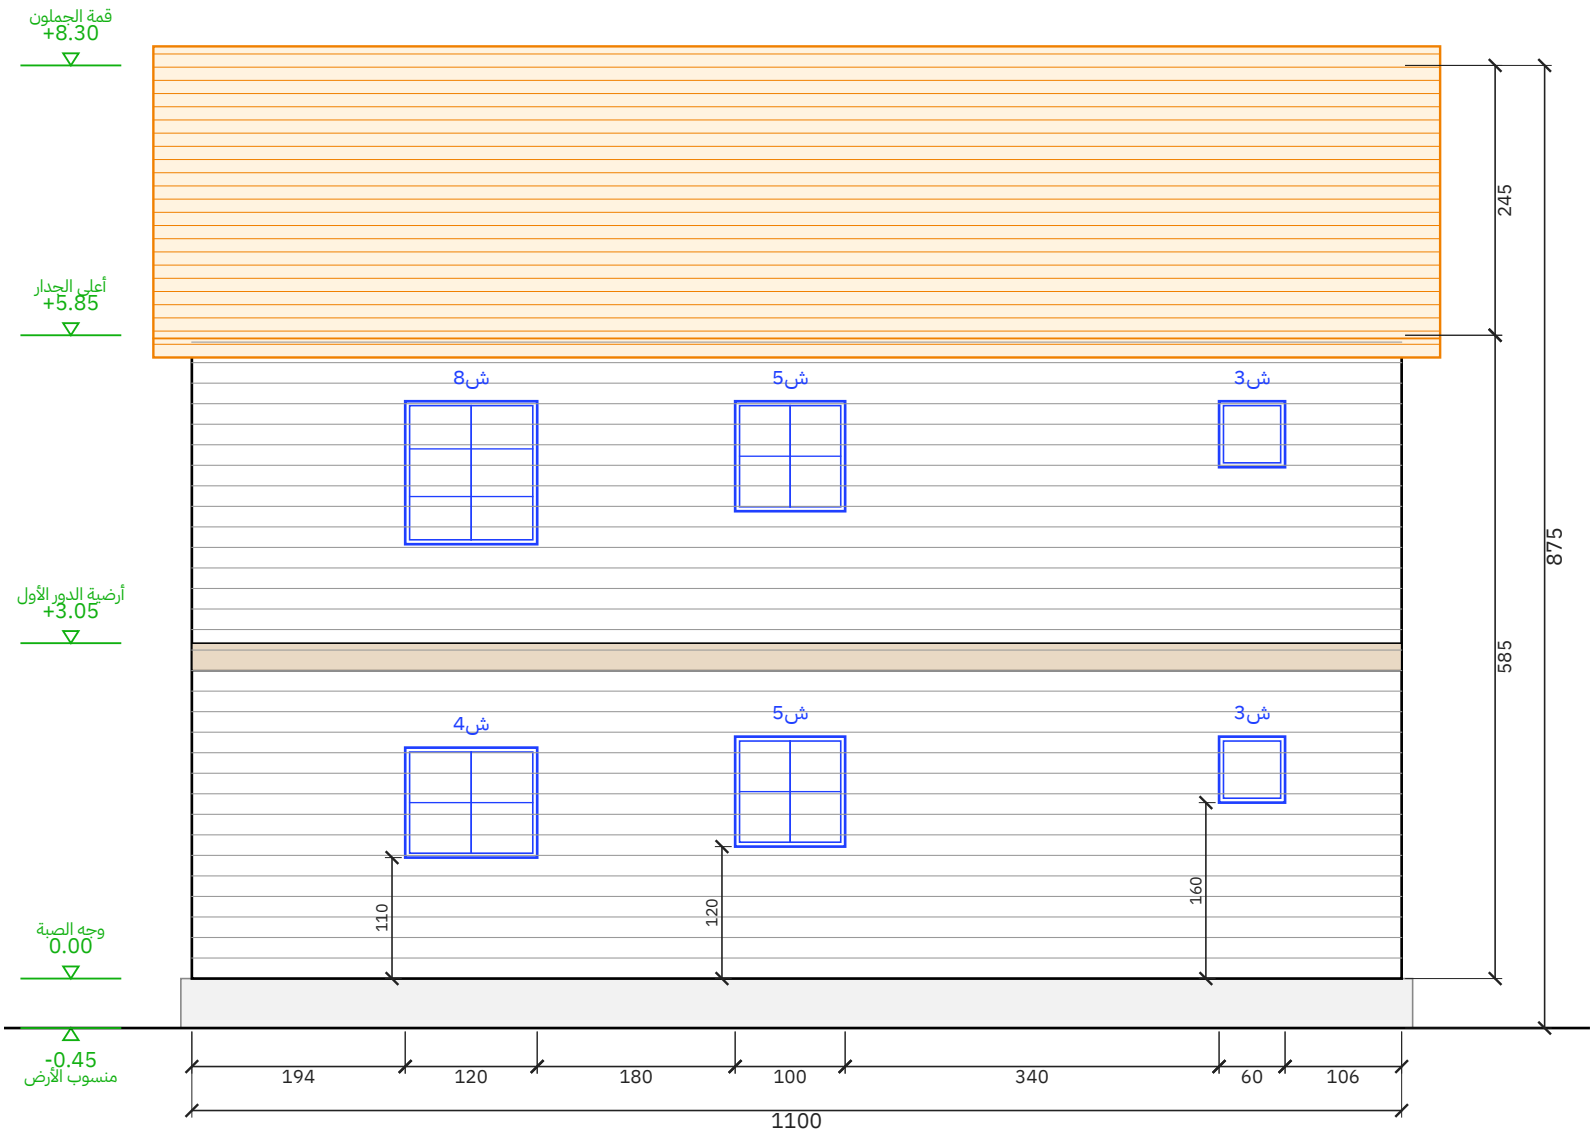

الواجهة الخلفية

مقياس 1:50 | الوحدة: سم

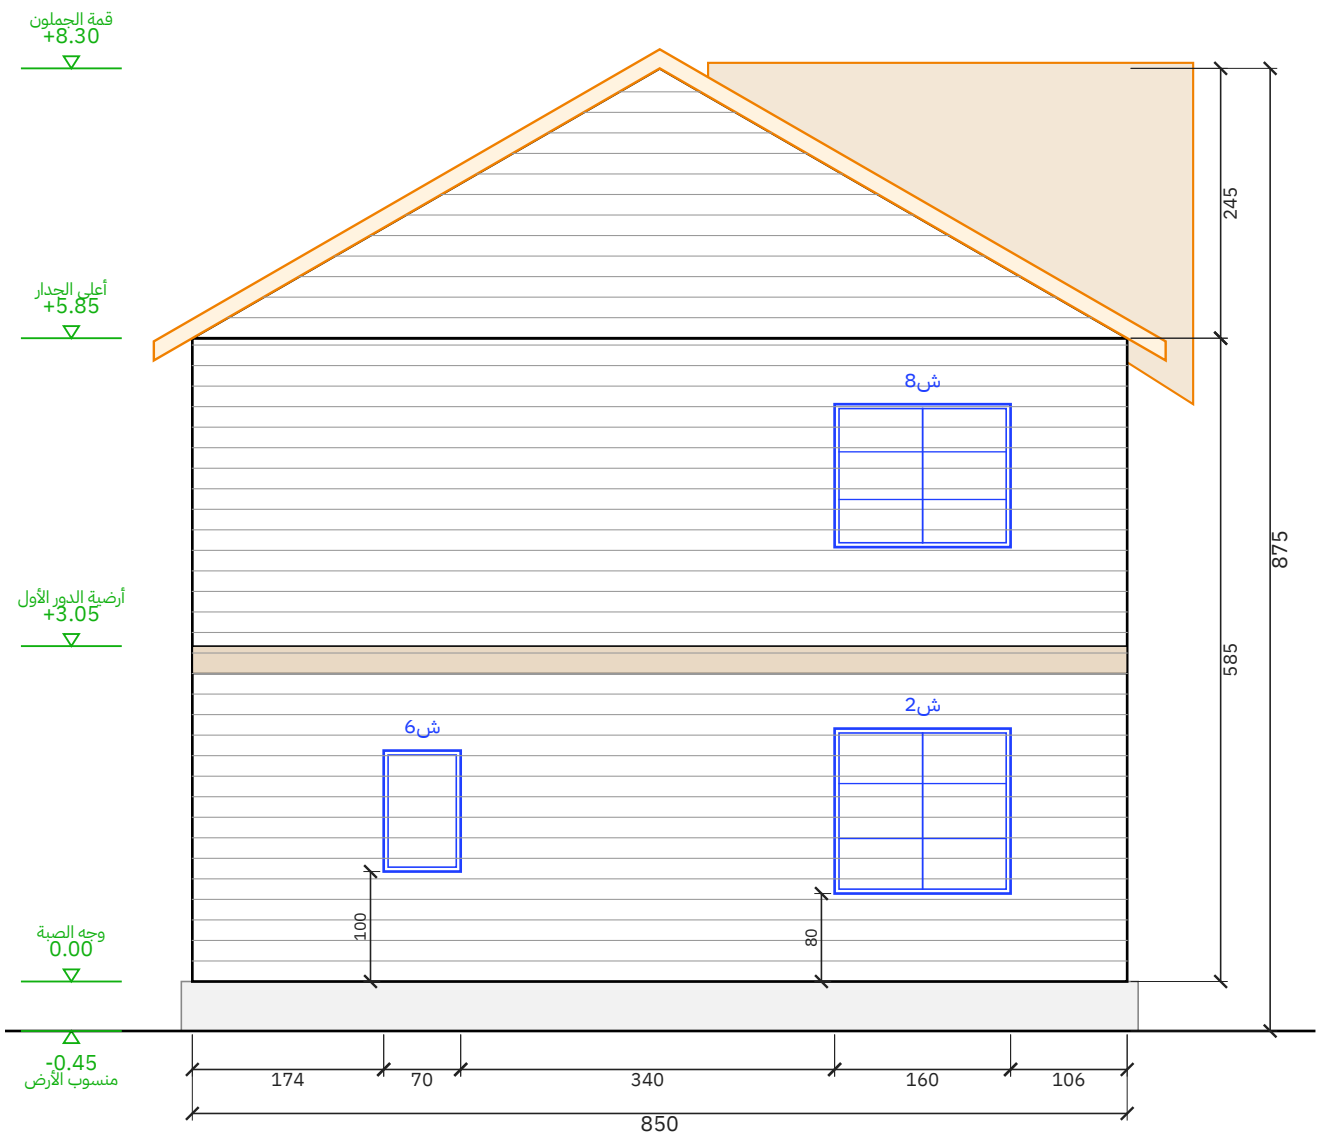

الواجهة الغربية


مقياس 1:50 | الوحدة: سم

المشروع / العميل	عنوان اللوحة	المقياس	التاريخ	رقم اللوحة
فيلا خشب دورين – واجهة جملون زجاج وبلكونة – 3 غرف (ماستر) – 11.00 × 8.50 م عميل – الباحة	الواجهة الخلفية والواجهة الغربية	1:50	2026-10-23	W-05 (5/23)

مصنع وتد الأخشاب
Watad Wood Factory


مسقط السقف (جملون)

رفرف 35 سم من كل جهة | مقياس 1:50

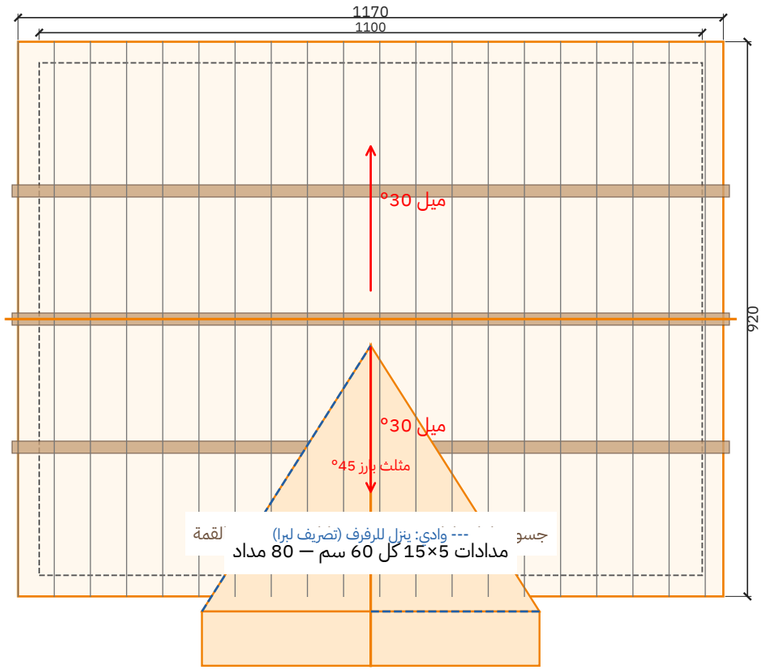


قطاع عرضي أ-أ

مقياس 1:50 | الوحدة: سم

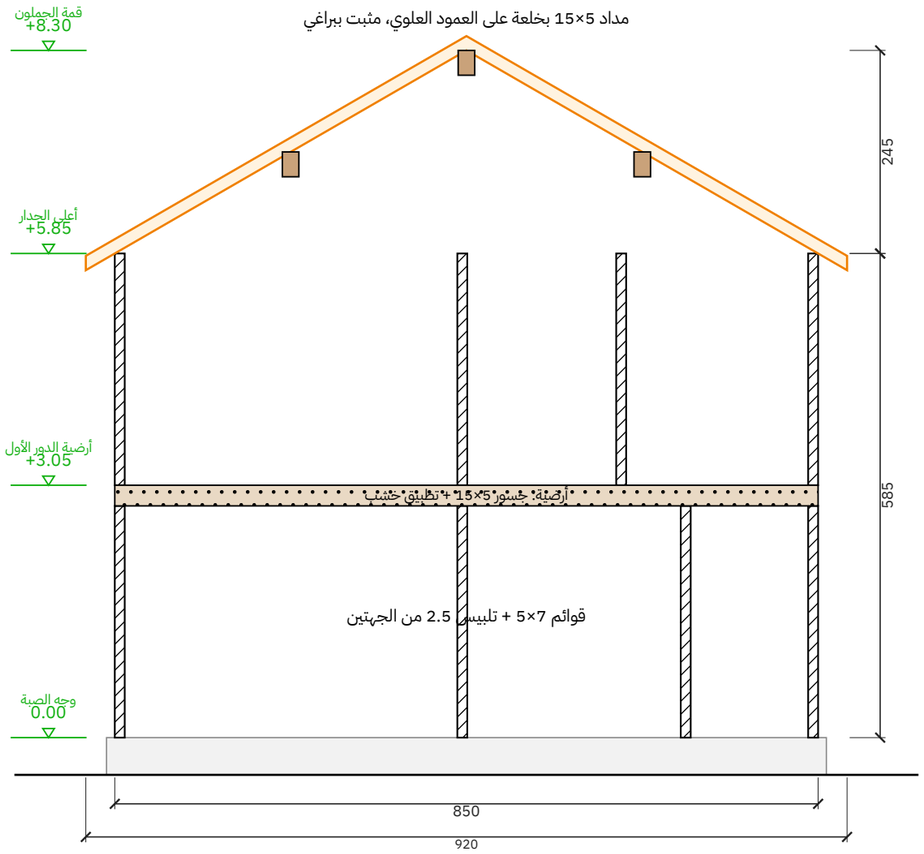

تفصيلة جلوس المداد على العلوي (1:5)

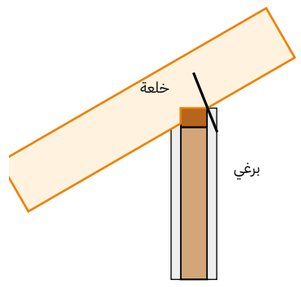

علوي 7×5 على قائم 7×5

المشروع / العميل: فيلا خشب دورين — واجهة جملون زجاج وبلكونة — 3 غرف (ماستر) — 11.00 × 8.50 م — عميل — الباحة	عنوان اللوحة: مسقط السقف والقطاع	المقياس: —	التاريخ: 2026-10-23	رقم اللوحة: W-06 (6/23)

مصنع وتد الأخشاب
Watad Wood Factory

جدول مقاسات الأبواب والشبابيك

مقاس الفتحة الصافي في الجدار - الوحدة: سم

الرمز	النوع	العرض (سم)	الارتفاع (سم)	ارتفاع الجلسة (سم)	العدد	الموقع
ب1	باب مزدوج	140	240	-	1	الأمامية
ب10	باب	64	210	-	1	ممر الغرف
ب2	باب	80	210	-	1	غرفة العاملة
ب3	باب	64	210	-	1	دورة مياه العاملة
ب3	باب	70	210	-	1	الغسيل
ب4	باب	70	210	-	1	دورة الضيوف
ب5	باب	90	210	-	1	المطبخ
ب6	باب مزدوج	160	230	-	1	الأمامية (البلكونة)
ب7	باب	80	210	-	3	الماستر - غرفة 2 - غرفة 3
ب8	باب	80	210	-	1	ملابس الماستر
ب9	باب	70	210	-	2	حمام الماستر - الحمام (للغرفتين)
ف1	باب	190	240	-	1	الصالة — المدخل
ف2	باب	240	240	-	1	الطعام — المدخل
ف3	باب	160	220	-	1	الطعام — الموزع
ش1	شباك	240	190	50	2	الأمامية 2
ش2	شباك	120	150	80	1	الشرقية
ش2	شباك	160	150	80	1	الغربية
ش3	شباك	60	60	160	4	الشرقية 2 - الخلفية 2
ش4	شباك	120	100	110	2	الشرقية - الخلفية
ش5	شباك	100	100	120	2	الخلفية 2
ش6	شباك	70	110	100	1	الغربية
ش7	شباك	180	160	70	2	الأمامية (البلكونة) 2
ش8	شباك	120	130	90	3	الشرقية 2 - الخلفية
ش8	شباك	160	130	90	1	الغربية

الإجمالي: أبواب 17 - شبابيك 19

جدول المساحات وبيانات المشروع والتسعير

بيانات المشروع

البند	البيان
المشروع	فيلا خشب دورين — واجهة جملون زجاج وبلكونة — 3 غرف (ماستر) — 11.00 × 8.50 م
العميل	عميل — الباحة
الموقع	الباحة
الاستخدام	سكن عائلي
التاريخ	2026-10-23
نظام البناء	هيكل خشب 5×7 + تلبيس 2.5 سم من الجهتين
السقف	جملون 30° — قرميد معدني + 1 مثلث بارز

التسعير المفصّل

البند	المبلغ (ريال)
الكوخ المبني 187.00 م² × 1,500	280,500
البرندة + البلكونة (4.20 × 1.40 × 2) — 11.76 م² × 1,500	17,640
الإجمالي (ريال)	**298,140**


ملاحظات:

- السعر 1,500 ر.س/م² للدورين حسب المخطط المعتمد — شامل الصبة (بصمة المبنى 11.00 × 8.50 م).
- شامل أدوات التأسيس للسباكة والكهرباء (التمديدات الداخلية).
- التوصيلات الخارجية (عداد الكهرباء والمويه والصرف) على العميل.


جدول المساحات

م	الفراغ	الأبعاد (م)	المساحة (م2)
1	أرضي — الصالة	4.24 × 4.02	17.04
2	أرضي — المدخل	2.04 × 4.08	8.32
3	أرضي — الطعام	4.24 × 3.24	13.74
4	أرضي — الموزع	2.12 × 1.58	3.35
5	أرضي — دورة الضيوف	2.00 × 1.58	3.16
6	أرضي — المطبخ	4.24 × 3.20	13.57
7	أرضي — الدرج	1.92 × 4.12	7.91
8	أرضي — غرفة العاملة	4.24 × 2.58	10.94
9	أرضي — دورة مياه العاملة	1.94 × 1.42	2.75
10	أرضي — الغسيل	2.18 × 1.42	3.10
11	أول — الماستر	4.24 × 4.02	17.04
12	أول — صالة صغيرة	2.04 × 4.08	8.32
13	أول — ملابس الماستر	4.24 × 1.80	7.63
14	أول — حمام الماستر	4.24 × 2.20	9.33
15	أول — غرفة نوم 2	4.24 × 3.24	13.74
16	أول — ممر الغرف	2.12 × 1.58	3.35
17	أول — الحمام (للغرفتين)	2.00 × 1.58	3.16
18	أول — غرفة نوم 3	4.24 × 3.20	13.57
	المساحة الصافية الداخلية		160.03
	البرندة	**4.20 × 1.40**	**5.88**
	البلكونة	**4.20 × 1.40**	**5.88**
	المساحة الإجمالية المبنية	**11.00 × 8.50 × 2 دور**	**187.00**
	المساحة الكلية (المبنية + التراس والبلكونة)		**198.76**

تأطير جدار أ-جنوب — الطول 1088 سم، الارتفاع 280 سم

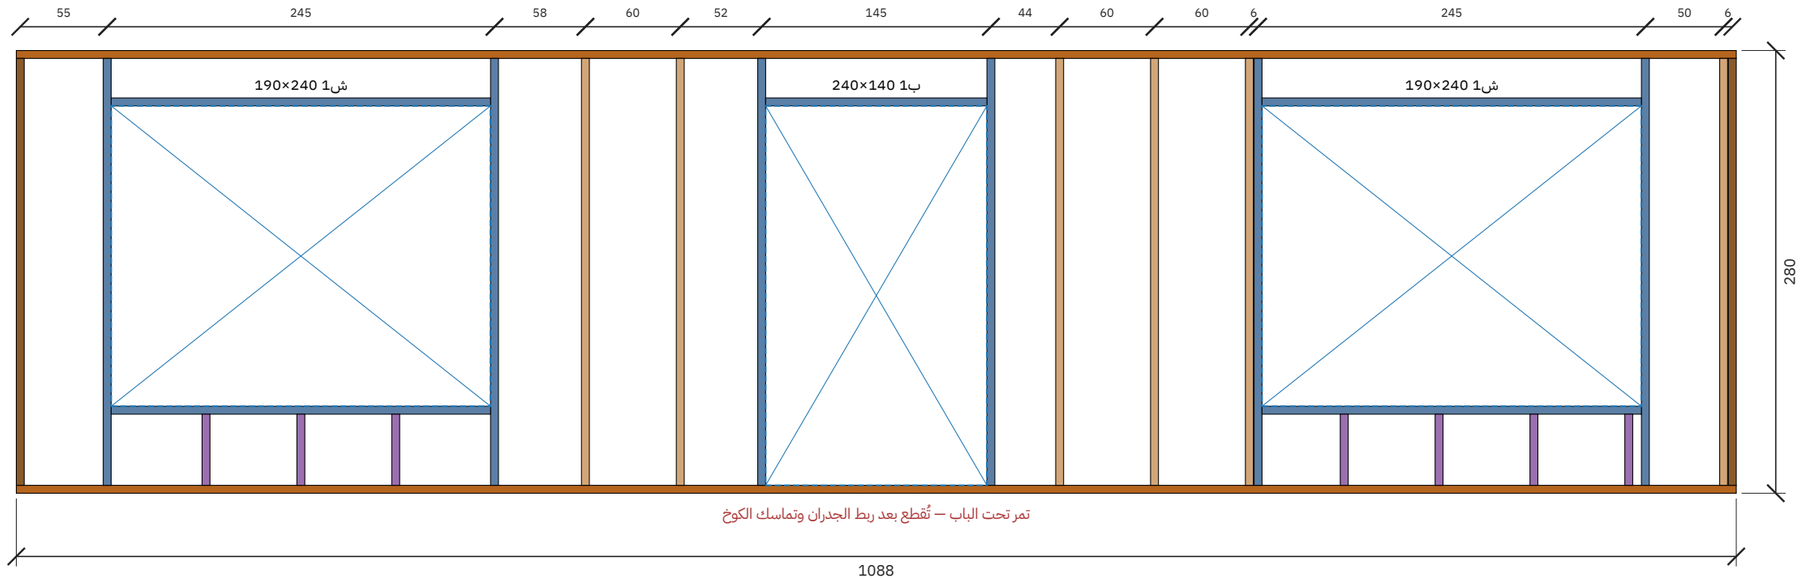

تأطير جدار أ-شرق — الطول 838 سم، الارتفاع 280 سم

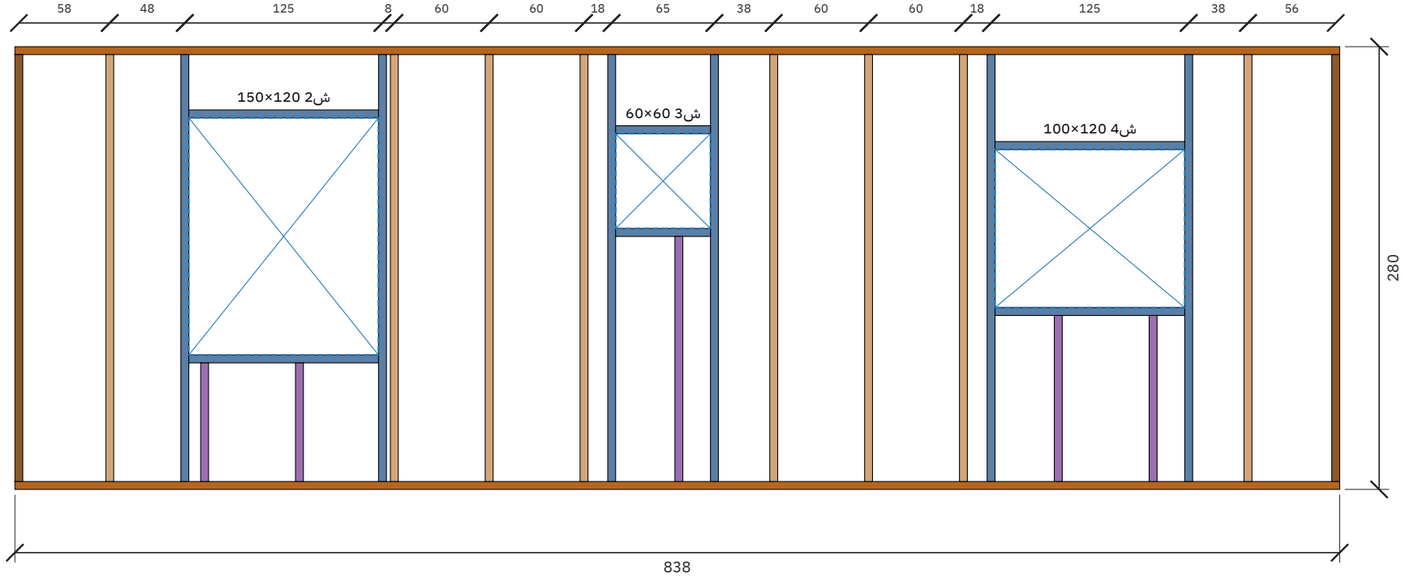


قاعدة سفلية | علوي | عمود | عمود زاوية | جنب فتحة | رأس فتحة | جلسة شباك | عمود قصير


المشروع / العميل	عنوان اللوحة	المقياس	التاريخ	رقم اللوحة
فيلا خشب دورين — واجهة جملون زجاج وبلكونة — 3 غرف (ماستر) — 11.00 × 8.50 م عميل — الباحة	لوحات التأطير (للورشة)	—	2026-10-23	W-09 (9/23)

مصنع وتد الأخشاب
Watad Wood Factory

تأطير جدار أ-شمال — الطول 1088 سم، الارتفاع 280 سم

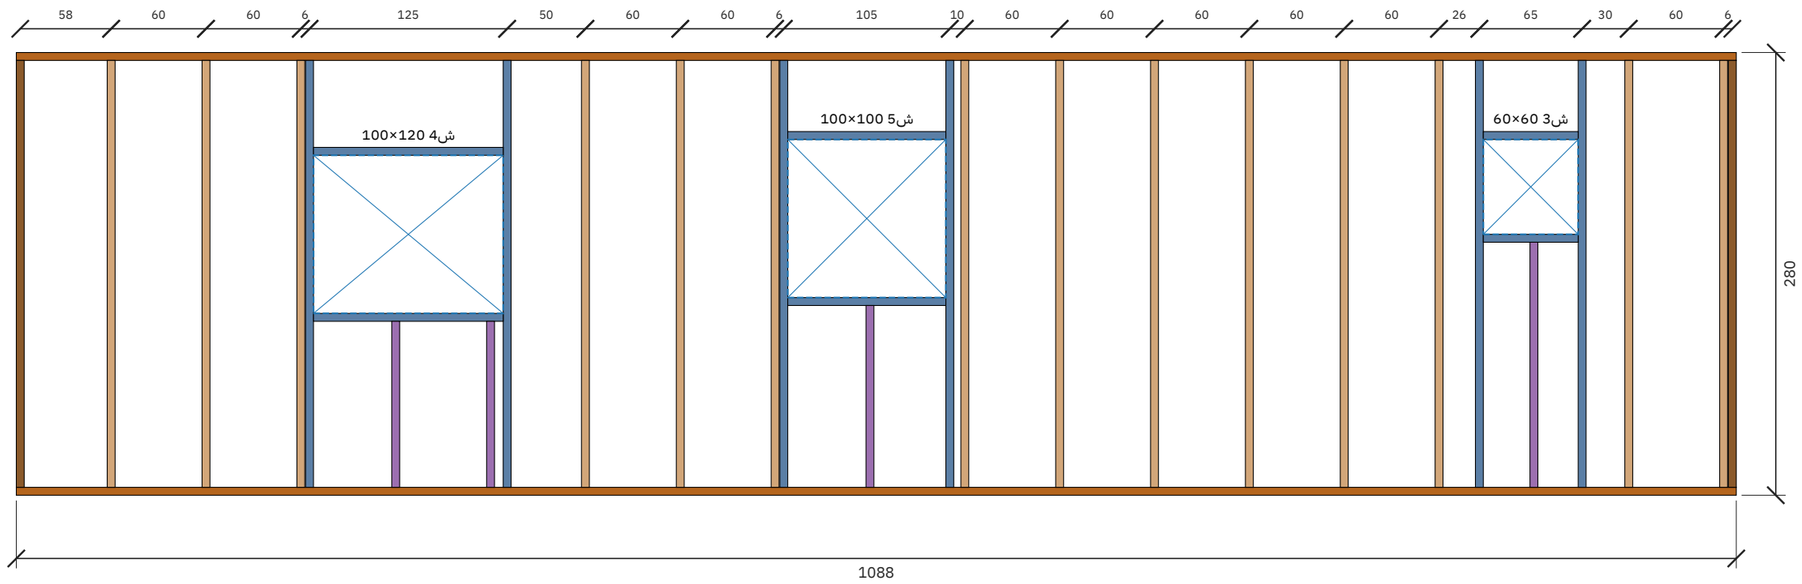


تأطير جدار أ-غرب — الطول 838 سم، الارتفاع 280 سم

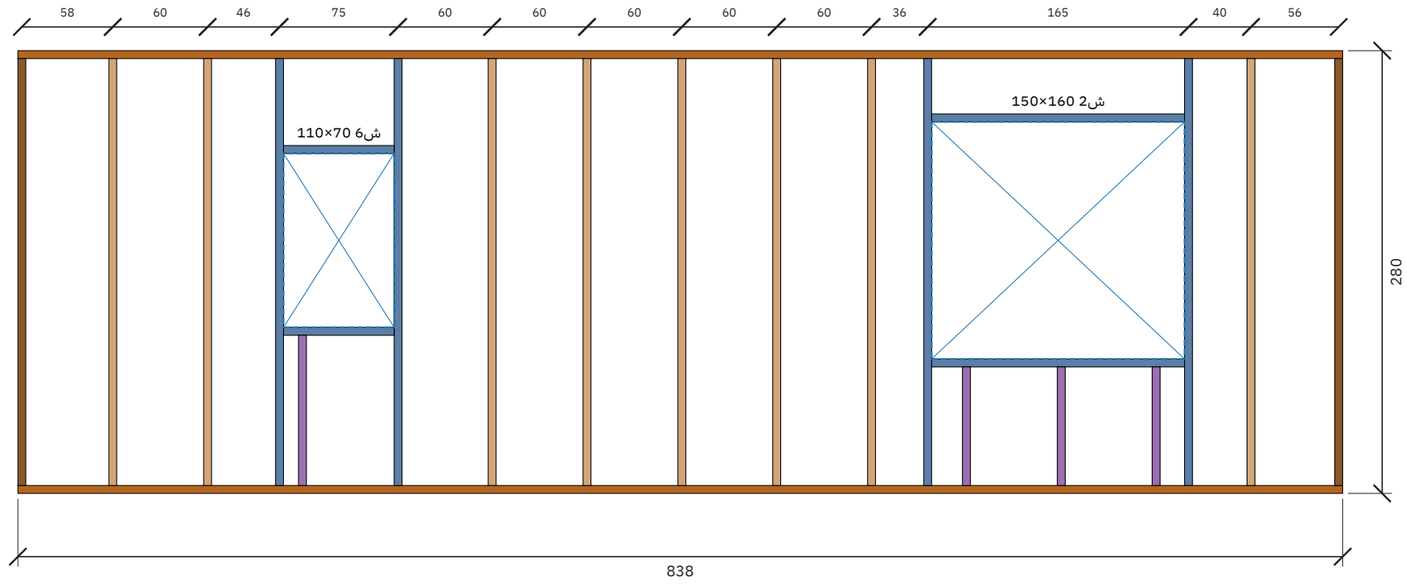


قاعدة سفلية | علوي | عمود | عمود زاوية | جنب فتحة | رأس فتحة | جلسة شباك | عمود قصير

مصنع وتد الأخشاب Watad Wood Factory	المشروع / العميل فيلا خشب دورين — واجهة جملون زجاج وبلكونة — 3 غرف (ماستر) — 11.00 × 8.50 م عميل — الباحة	عنوان اللوحة لوحات التأطير (للورشة)	المقياس —	التاريخ 2026-10-23	رقم اللوحة W-10 (10/23)

تأطير جدار أ-جدار الصالة — الطول 838 سم، الارتفاع 280 سم (داخلي)

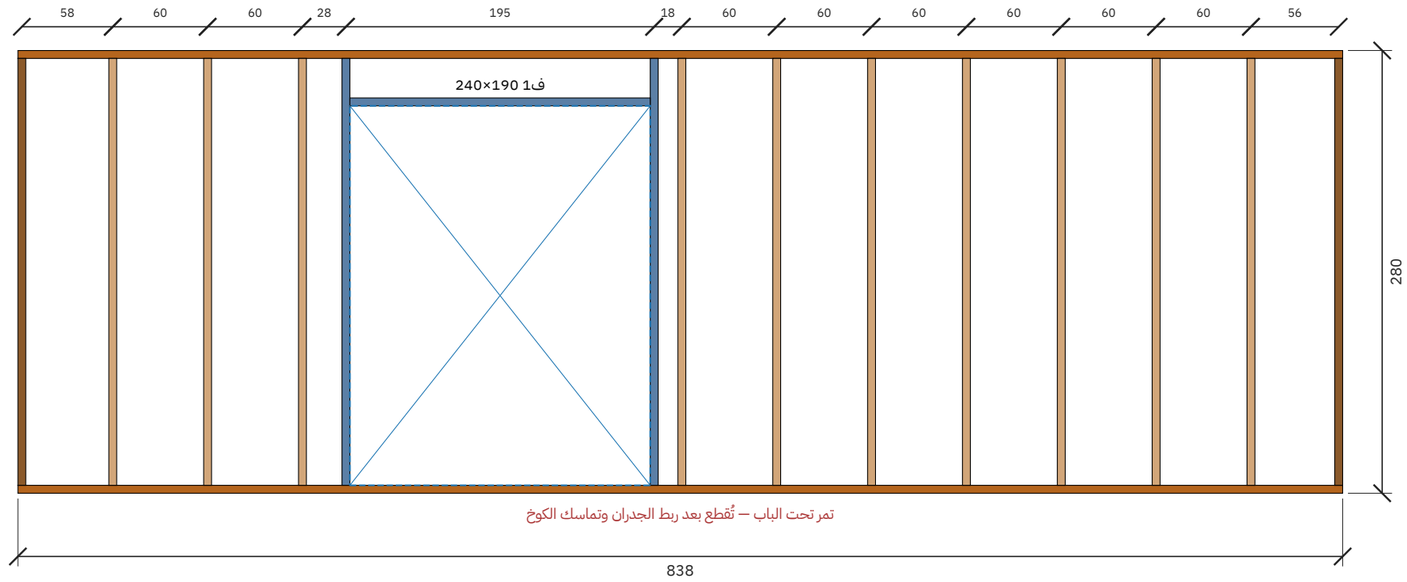


تأطير جدار أ-جدار الطعام — الطول 838 سم، الارتفاع 280 سم (داخلي)

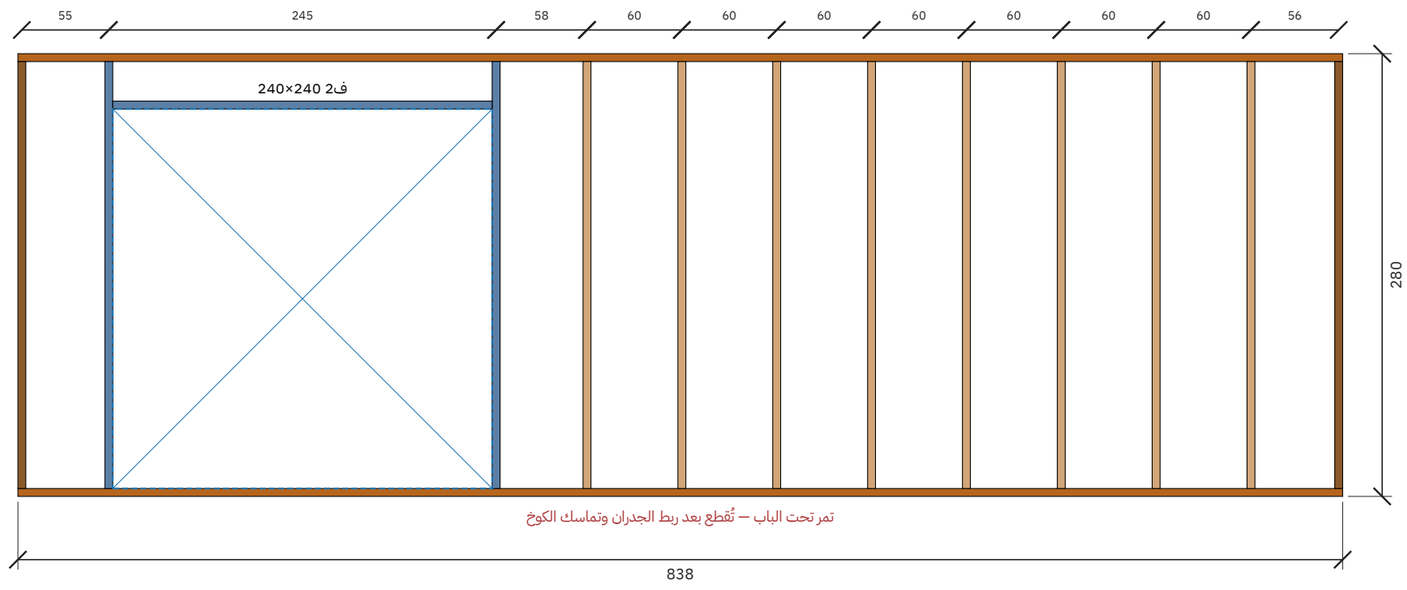


قاعدة سفلية | علوي | عمود | عمود زاوية | جنب فتحة | رأس فتحة | جلسة شباك | عمود قصير

مصنع وتد الأخشاب Watad Wood Factory	المشروع / العميل فيلا خشب دورين — واجهة جملون زجاج وبلكونة — 3 غرف (ماستر) — 11.00 × 8.50 م عميل — الباحة	عنوان اللوحة لوحات التأطير (للورشة)	المقياس —	التاريخ 2026-10-23	رقم اللوحة W-11 (11/23)

تأطير جدار أ-فاصل العاملة — الطول 436 سم، الارتفاع 280 سم (داخلي)

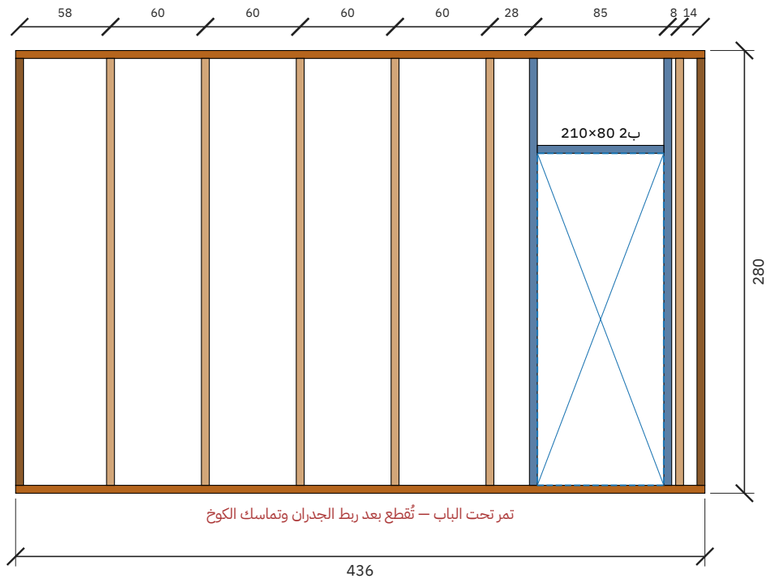


تأطير جدار أ-فاصل دورة العاملة — الطول 436 سم، الارتفاع 280 سم (داخلي)

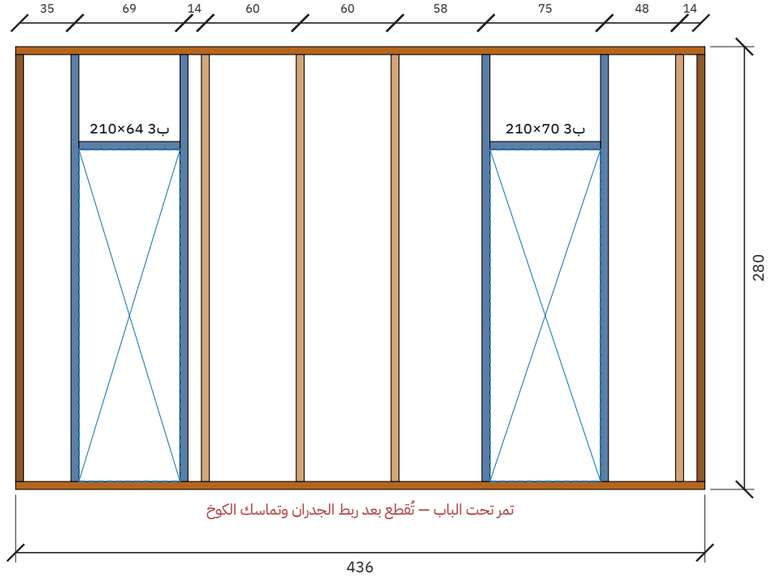


قاعدة سفلية | علوي | عمود | عمود زاوية | جنب فتحة | رأس فتحة | جلسة شباك | عمود قصير

مصنع وتد الأخشاب Watad Wood Factory	المشروع / العميل **فيلا خشب دورين — واجهة جملون زجاج وبلكونة — 3 غرف (ماستر) — 11.00 × 8.50 م** **عميل — الباحة**	عنوان اللوحة **لوحات التأطير (للورشة)**	المقياس **—**	التاريخ **2026-10-23**	رقم اللوحة **W-12 (12/23)**

تأطير جدار أ-جدار الغسيل — الطول 154 سم، الارتفاع 280 سم (داخلي)

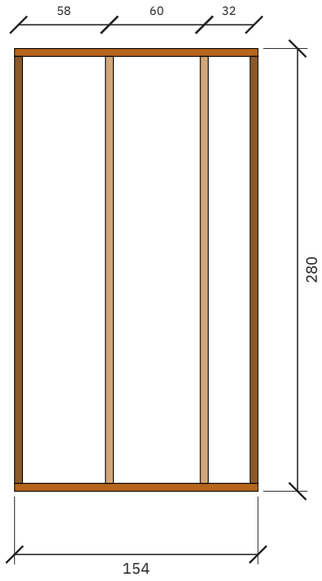


تأطير جدار أ-فاصل الطعام — الطول 436 سم، الارتفاع 280 سم (داخلي)

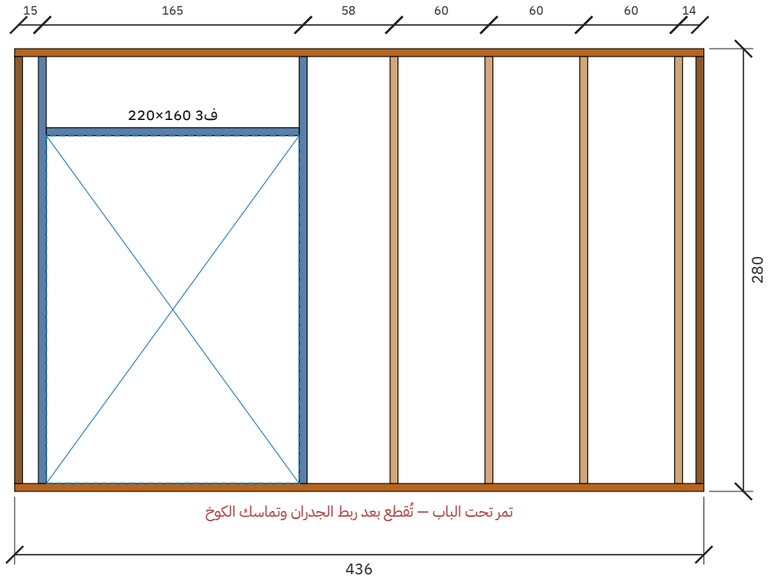


قاعدة سفلية | علوي | عمود | عمود زاوية | جنب فتحة | رأس فتحة | جلسة شباك | عمود قصير

مصنع وتد الأخشاب Watad Wood Factory	المشروع / العميل **فيلا خشب دورين — واجهة جملون زجاج وبلكونة — 3 غرف (ماستر) — 11.00 × 8.50 م** **عميل — الباحة**	عنوان اللوحة **لوحات التأطير (للورشة)**	المقياس **—**	التاريخ **2026-10-23**	رقم اللوحة **W-13 (13/23)**

تأطير جدار أ-جدار دورة الضيوف — الطول 170 سم، الارتفاع 280 سم (داخلي)

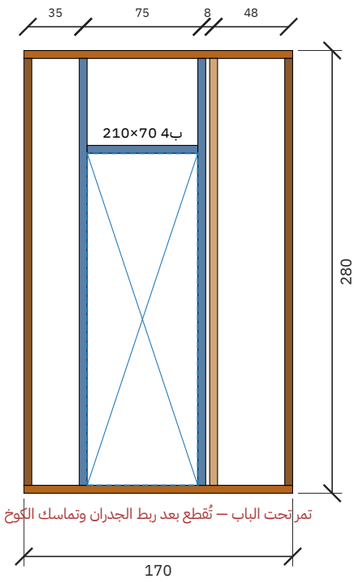


تأطير جدار أ-فاصل المطبخ — الطول 436 سم، الارتفاع 280 سم (داخلي)

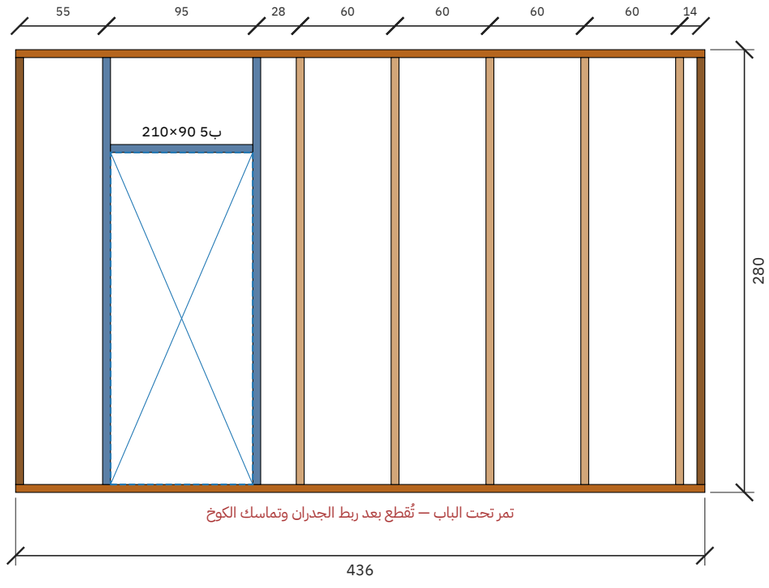


قاعدة سفلية | علوي | عمود | عمود زاوية | جنب فتحة | رأس فتحة | جلسة شباك | عمود قصير

مصنع وتد الأخشاب Watad Wood Factory	المشروع / العميل فيلا خشب دورين — واجهة جملون زجاج وبلكونة — 3 غرف (ماستر) — 11.00 × 8.50 م عميل — الباحة	عنوان اللوحة لوحات التأطير (للورشة)	المقياس —	التاريخ 2026-10-23	رقم اللوحة W-14 (14/23)

تأطير جدار ب-جنوب — الطول 1088 سم، الارتفاع 280 سم

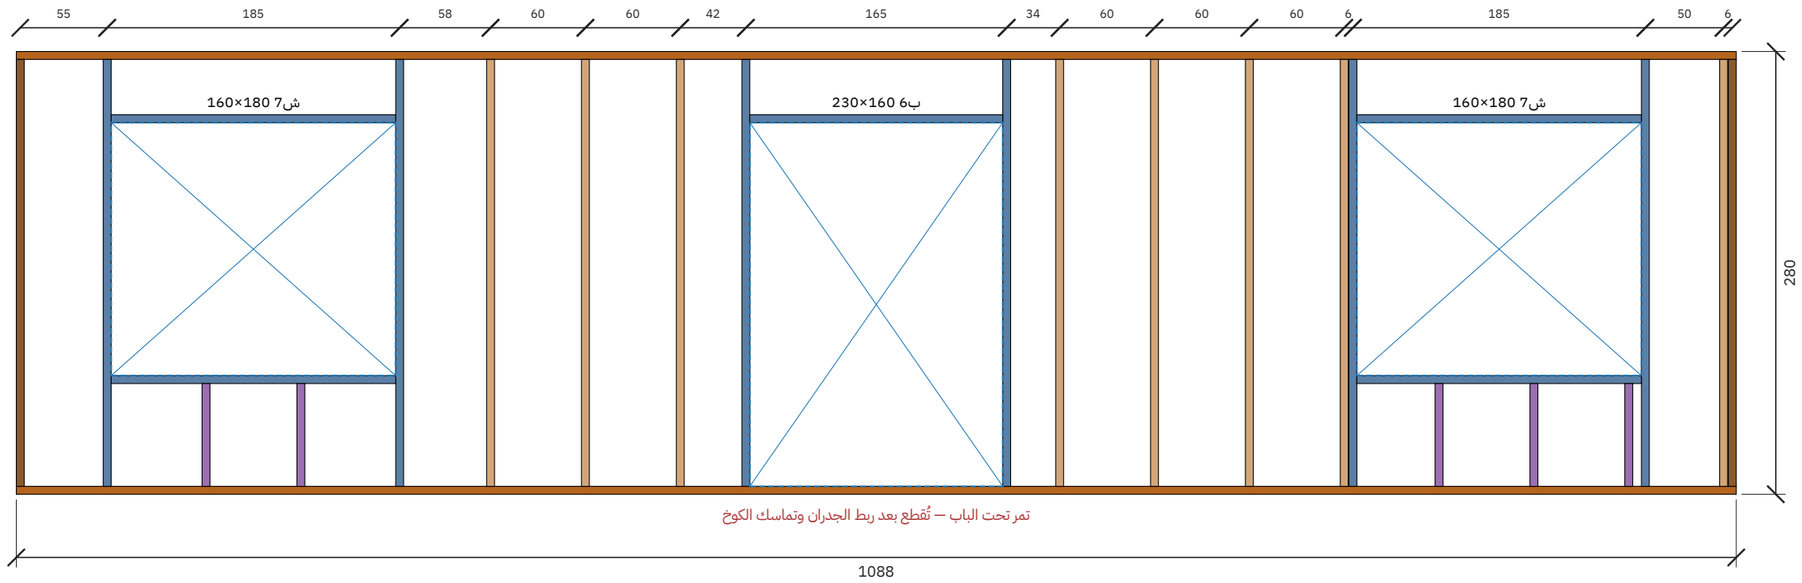

تأطير جدار ب-شرق — الطول 838 سم، الارتفاع 280 سم

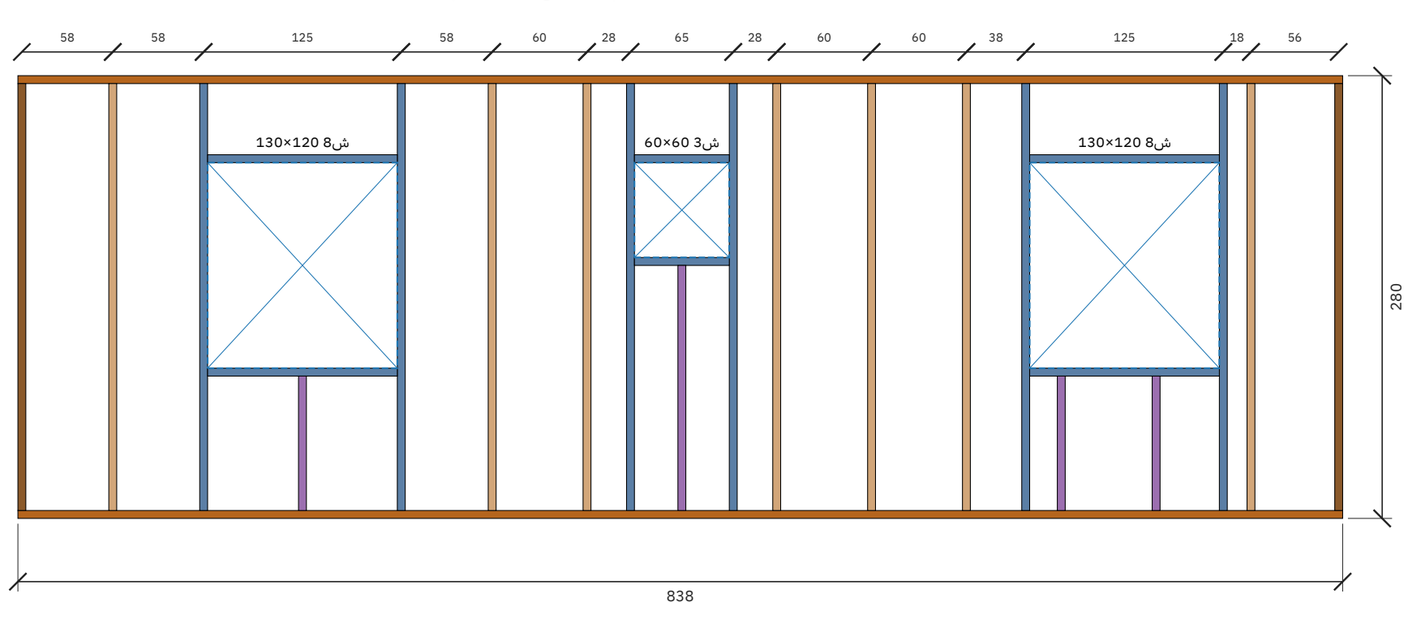


قاعدة سفلية | علوي | عمود | عمود زاوية | جنب فتحة | رأس فتحة | جلسة شباك | عمود قصير


المشروع / العميل	عنوان اللوحة	المقياس	التاريخ	رقم اللوحة
فيلا خشب دورين — واجهة جملون زجاج وبلكونة — 3 غرف (ماستر) — 11.00 × 8.50 م عميل — الباحة	لوحات التأطير (للورشة)	—	2026-10-23	W-15 (15/23)

مصنع وتد الأخشاب
Watad Wood Factory

تأطير جدار ب-شمال — الطول 1088 سم، الارتفاع 280 سم

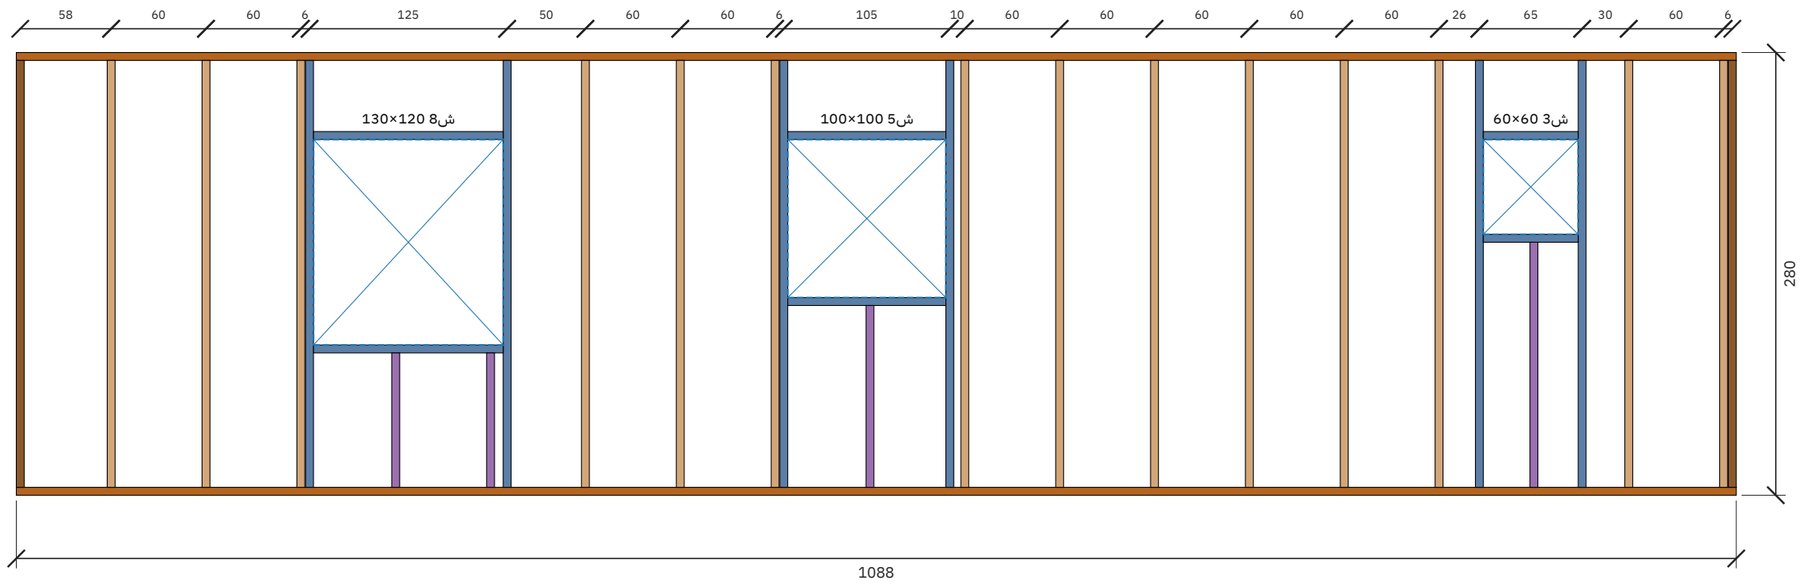


تأطير جدار ب-غرب — الطول 838 سم، الارتفاع 280 سم

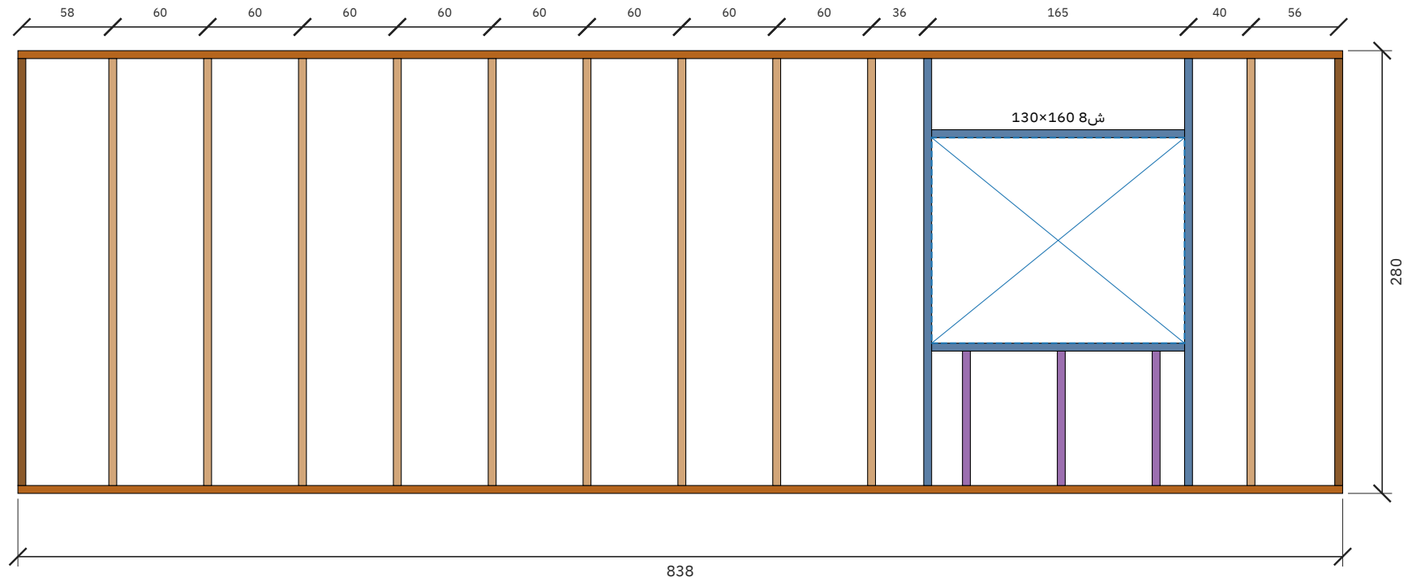


قاعدة سفلية | علوي | عمود | عمود زاوية | جنب فتحة | رأس فتحة | جلسة شباك | عمود قصير

مصنع وتد الأخشاب Watad Wood Factory	المشروع / العميل فيلا خشب دورين — واجهة جملون زجاج وبلكونة — 3 غرف (ماستر) — 11.00 × 8.50 م عميل — الباحة	عنوان اللوحة لوحات التأطير (للورشة)	المقياس —	التاريخ 2026-10-23	رقم اللوحة W-16 (16/23)

تأطير جدار ب-جدار الماستر — الطول 838 سم، الارتفاع 280 سم (داخلي)

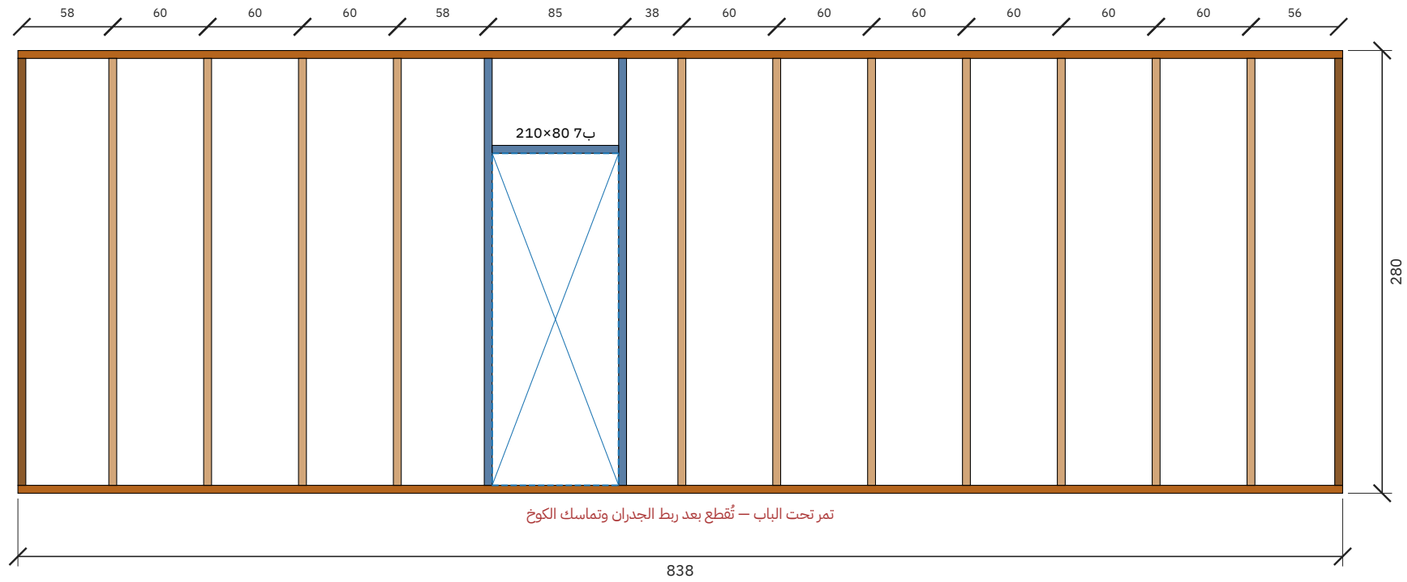

تأطير جدار ب-جدار الغرف — الطول 838 سم، الارتفاع 280 سم (داخلي)

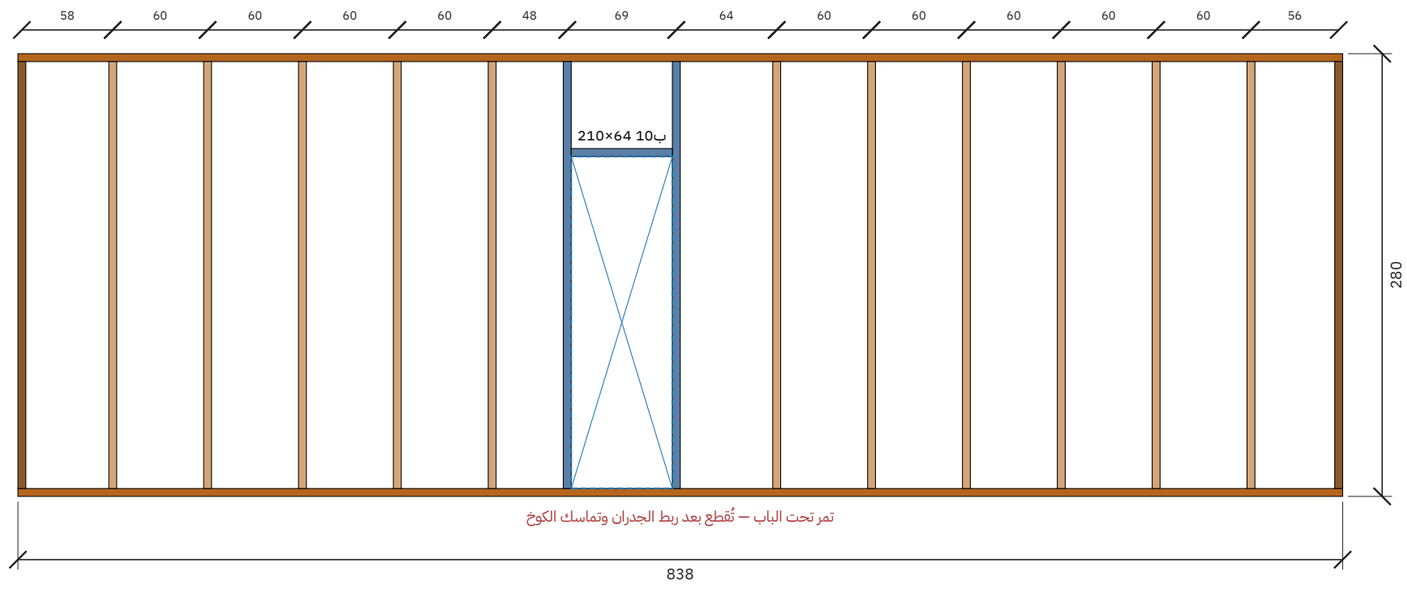


قاعدة سفلية | علوي | عمود | عمود زاوية | جنب فتحة | رأس فتحة | جلسة شباك | عمود قصير


المشروع / العميل	عنوان اللوحة	المقياس	التاريخ	رقم اللوحة
فيلا خشب دورين — واجهة جملون زجاج وبلكونة — 3 غرف (ماستر) — 11.00 × 8.50 م **عميل — الباحة**	**لوحات التأطير (للورشة)**	**—**	**2026-10-23**	**W-17 (17/23)**

مصنع وتد الأخشاب
Watad Wood Factory

تأطير جدار ب-فاصل الملابس — الطول 436 سم، الارتفاع 280 سم (داخلي)

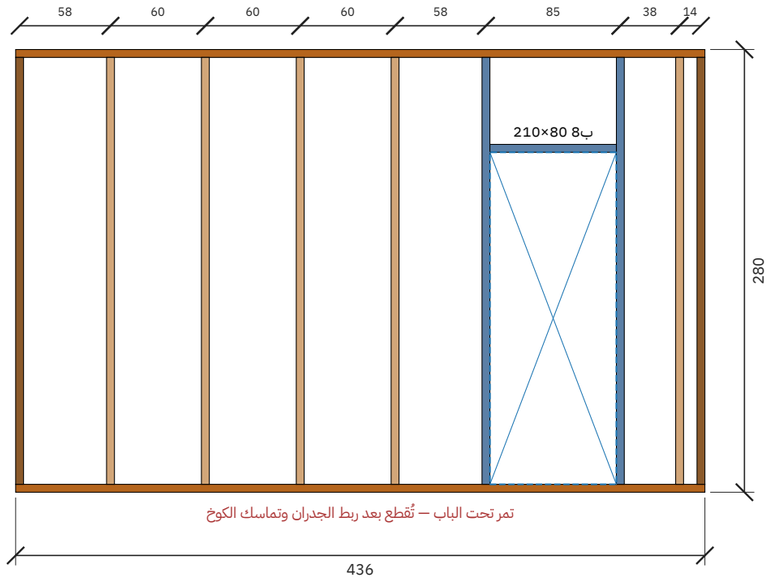

تأطير جدار ب-فاصل حمام الماستر — الطول 436 سم، الارتفاع 280 سم (داخلي)

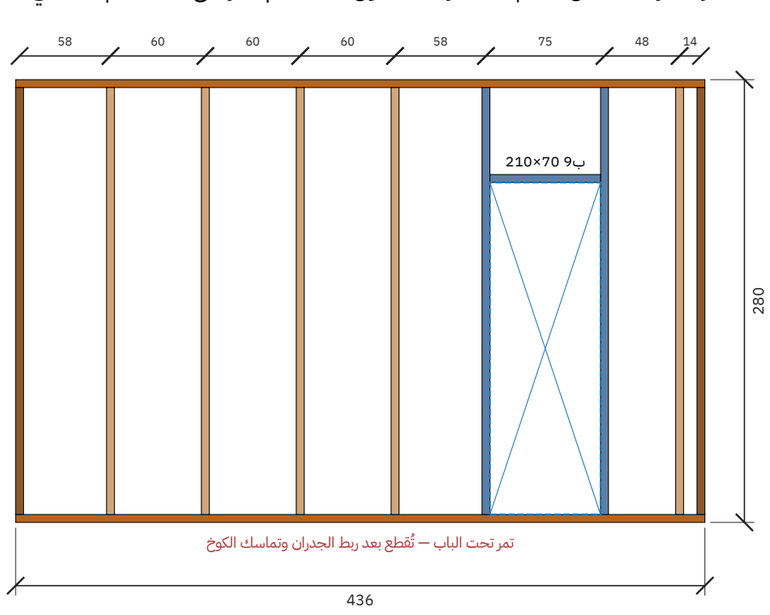


قاعدة سفلية | علوي | عمود | عمود زاوية | جنب فتحة | رأس فتحة | جلسة شباك | عمود قصير


المشروع / العميل	عنوان اللوحة	المقياس	التاريخ	رقم اللوحة
فيلا خشب دورين — واجهة جملون زجاج وبلكونة — 3 غرف (ماستر) — 11.00 × 8.50 م **عميل — الباحة**	**لوحات التأطير (للورشة)**	**—**	**2026-10-23**	**W-18 (18/23)**

مصنع وتد الأخشاب
Watad Wood Factory

تأطير جدار ب-فاصل غرفة 2 — الطول 436 سم، الارتفاع 280 سم (داخلي)

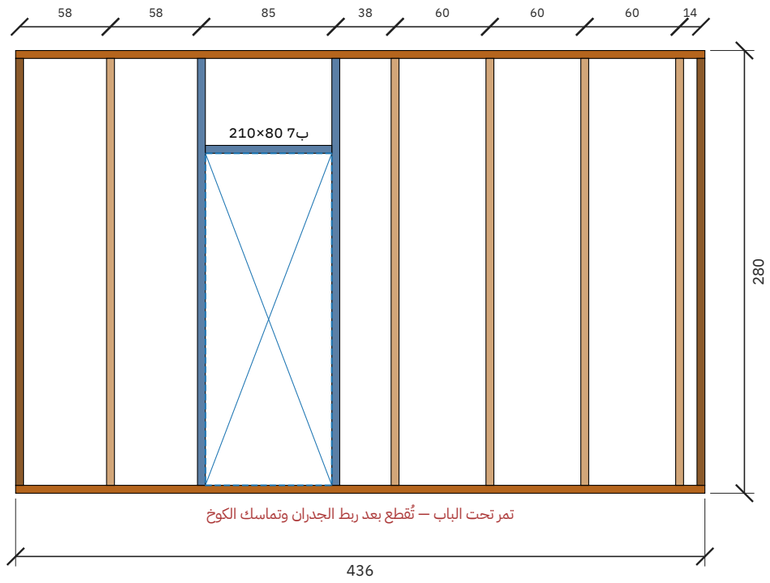

تأطير جدار ب-جدار الحمام — الطول 170 سم، الارتفاع 280 سم (داخلي)

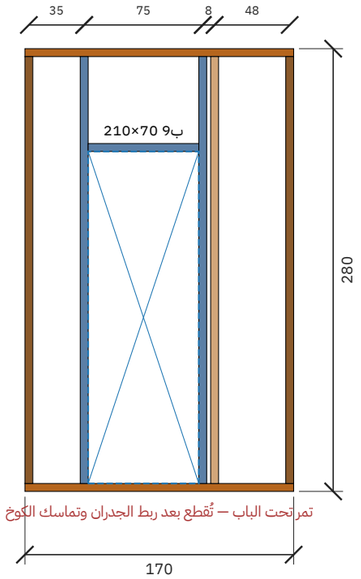


عمود قصير | جلسة شباك | رأس فتحة | جنب فتحة | عمود زاوية | عمود | علوي | قاعدة سفلية

المشروع / العميل **فيلا خشب دورين — واجهة جملون زجاج وبلكونة — 3 غرف (ماستر) — 11.00 × 8.50 م** **عميل — الباحة**	عنوان اللوحة **لوحات التأطير (للورشة)**	المقياس **—**	التاريخ **2026-10-23**	رقم اللوحة **W-19 (19/23)**

مصنع وتد الأخشاب
Watad Wood Factory

تأطير جدار ب-فاصل غرفة 3 — الطول 436 سم، الارتفاع 280 سم (داخلي)

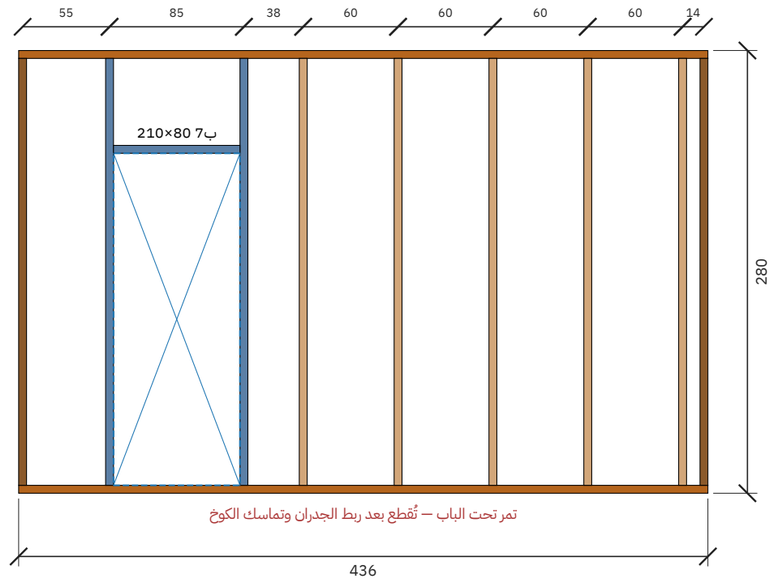

عمود قصير
جلسة شباك
رأس فتحة
جنب فتحة
عمود زاوية
عمود
علوي
قاعدة سفلية

مصنع وتد الأخشاب Watad Wood Factory	المشروع / العميل **فيلا خشب دورين — واجهة جملون زجاج وبلكونة — 3 غرف (ماستر) — 11.00 × 8.50 م** **عميل — الباحة**	عنوان اللوحة **لوحات التأطير (للورشة)**	المقياس **—**	التاريخ **2026-10-23**	رقم اللوحة **W-20 (20/23)**

جدول الكميات وخطة تقطيع الطبليات

البند	القيمة
الارتفاع المطلوب / المعتمد	280 / 280 سم
السقف	جملون 30° — أعلى نقطة 830 سم من وجه الصبة
المدادات 5×15	80 مداد (20 خط × قطعتين موصولة فوق الجسر الحامل بتراكب 60 سم) × حتى 320 سم — من طبلية 480
طبليات الطريقة الأولى (مداد + عمود)	80 طبلية × 480 سم
طبليات الطريقة الثانية (3 أعمدة)	96 طبلية × 320 سم
مدادات أرضية الدور العلوي 5×15 كل 60 سم	70 مداد — 216سم×14، 222سم×14، 226سم×14، 234سم×14، 240سم×14 (طبلية 320 بالطريقة الأولى)
مدادات المثلث البارز (S) 45°	16 مداد حتى 283 سم (طبلية 320) + 2 مداد وادي 593 سم — وصلة
إجمالي الطبليات 5×22.5	264
إجمالي قطع 5×7	413
قائمة تقطيع 5×7	1088سم×8 | 838سم×16 | 436سم×16 | 270سم×276 | 240سم×5 | 190سم×1 | 180سم×4 | 170سم×4 | 160سم×6
	155سم×4 | 154سم×2 | 140سم×1 | 120سم×12 | 115سم×2 | 105سم×4 | 100سم×4 | 95سم×1 | 90سم×1
ألواح تلبيس 2.5 سم	910 لوح × 400 سم (مجموع الصفوف 3185.0 م، 46 وجه)
أسمنت بورد 12 مم (122×244)	72 لوح (داخل دورات المياه)
العزل	485 لوح فوم صخري 80

جدول الكميات وخطة تقطيع الطبليات

البند	القيمة
الصبة	يجهزها العميل — 20 سم، مفرغة تحت دورات المياه

مراجعة التصميم مقابل قواعد المصنع

النوع	البند	التفاصيل	المقترح
ملاحظة	بحر المدادات	أطول بحر بدون جدار داخلي يحمل المداد: جهة أ: 425 سم، جهة ب: 425 سم. يحتاج رقم المصنع لأقصى بحر مسموح لتحديد المدادات اللي تُقوّى 20×5.	
ملاحظة	الصبة والدرج	ارتفاع الصبة 45 سم ← 3 درجة بقائمة 15.0 سم.	
ملاحظة	مناسيب رؤوس الفتحات	رؤوس الأبواب والشبابيك على مناسيب مختلفة: 210، 220، 230، 240 سم.	
تنبيه	مداد الوادي	مداد الوادي 593 سم أطول من الطبلية — يُوصل بوصلة مثبتة فوق جدار/دعامة	وصلة مزدوجة 5×15 مع براغي، ومرتكزة على جدار أو دعامة 5×7.
سؤال	يحتاج تأكيد	أقصى بحر للمداد بدون جدار داخلي قبل إضافة تقوية 5×7 (مداد 20×5)؟	
سؤال	يحتاج تأكيد	التغطية الصافية للوح التلبيس بعد التعشيق (مستنتجة مؤقتاً 18.67 سم من 280/15)؟	
سؤال	يحتاج تأكيد	هل يوضع أعمدة قصيرة فوق رأس الشباك/الباب إلى العلوي؟	
سؤال	يحتاج تأكيد	مكان الوصلة في القاعدة والعلوي إذا الجدار أطول من الطبلية؟	