المنظور ثلاثي الأبعاد والمواد

النمط: جوزي غامق + إطارات سوداء — رندر واقعي بخامات حقيقية



جدول المواد والألوان

الخشب / الصبغة

خشب طبيعي فاتح (بدون صبغة)

القرميد

قرميد رمادي غامق

الزجاج

زجاج عاكس غامق

إطارات الشبابيك والأبواب

إطار خشب بنفس الصبغة أغمق

الكنار والزوايا

نفس الصبغة أغمق درجة


الصبة

خرسانة 45 سم


الدربزين: ألواح أفقية متقاربة (عصري)

تقسيم الشبابيك: بدون | الباب الرئيسي: زجاج بتقسيمات (فرنسي)

أنواع الدربزين المعتمدة (من مشاريع المصنع)

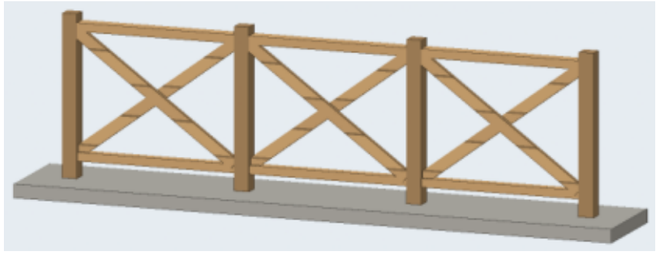

تقاطع X (صورة 5)

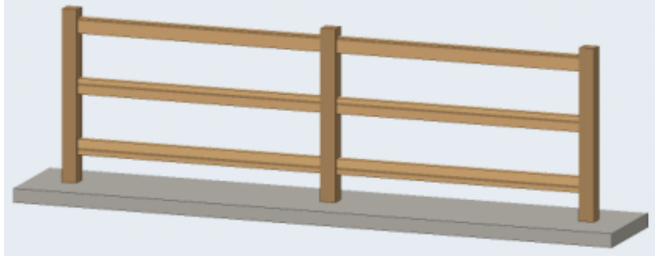

3 مرابيع أفقية (صورة 2)




قوائم رأسية متقاربة (صورة 1)

المشروع / العميل	عنوان اللوحة	المقياس	التاريخ	رقم اللوحة
فيلا خشب دورين — مجلس + غرفتين — 9.00 × 7.00 م (63 م² للدور) **عميل — تبوك**	**المنظور والمواد**	**1:50**	**2026-10-24**	**W-01 (1/21)**

مصنع وتد الأخشاب
Watad Wood Factory

المسقط الأفقي مع الفرش — الدور الأرضي

الأبعاد بالسنتيمتر - الجدران: قوائم 7×5 + تلبيس 2.5 من الجهتين (12 سم) | منسوب الأرضية +0.00

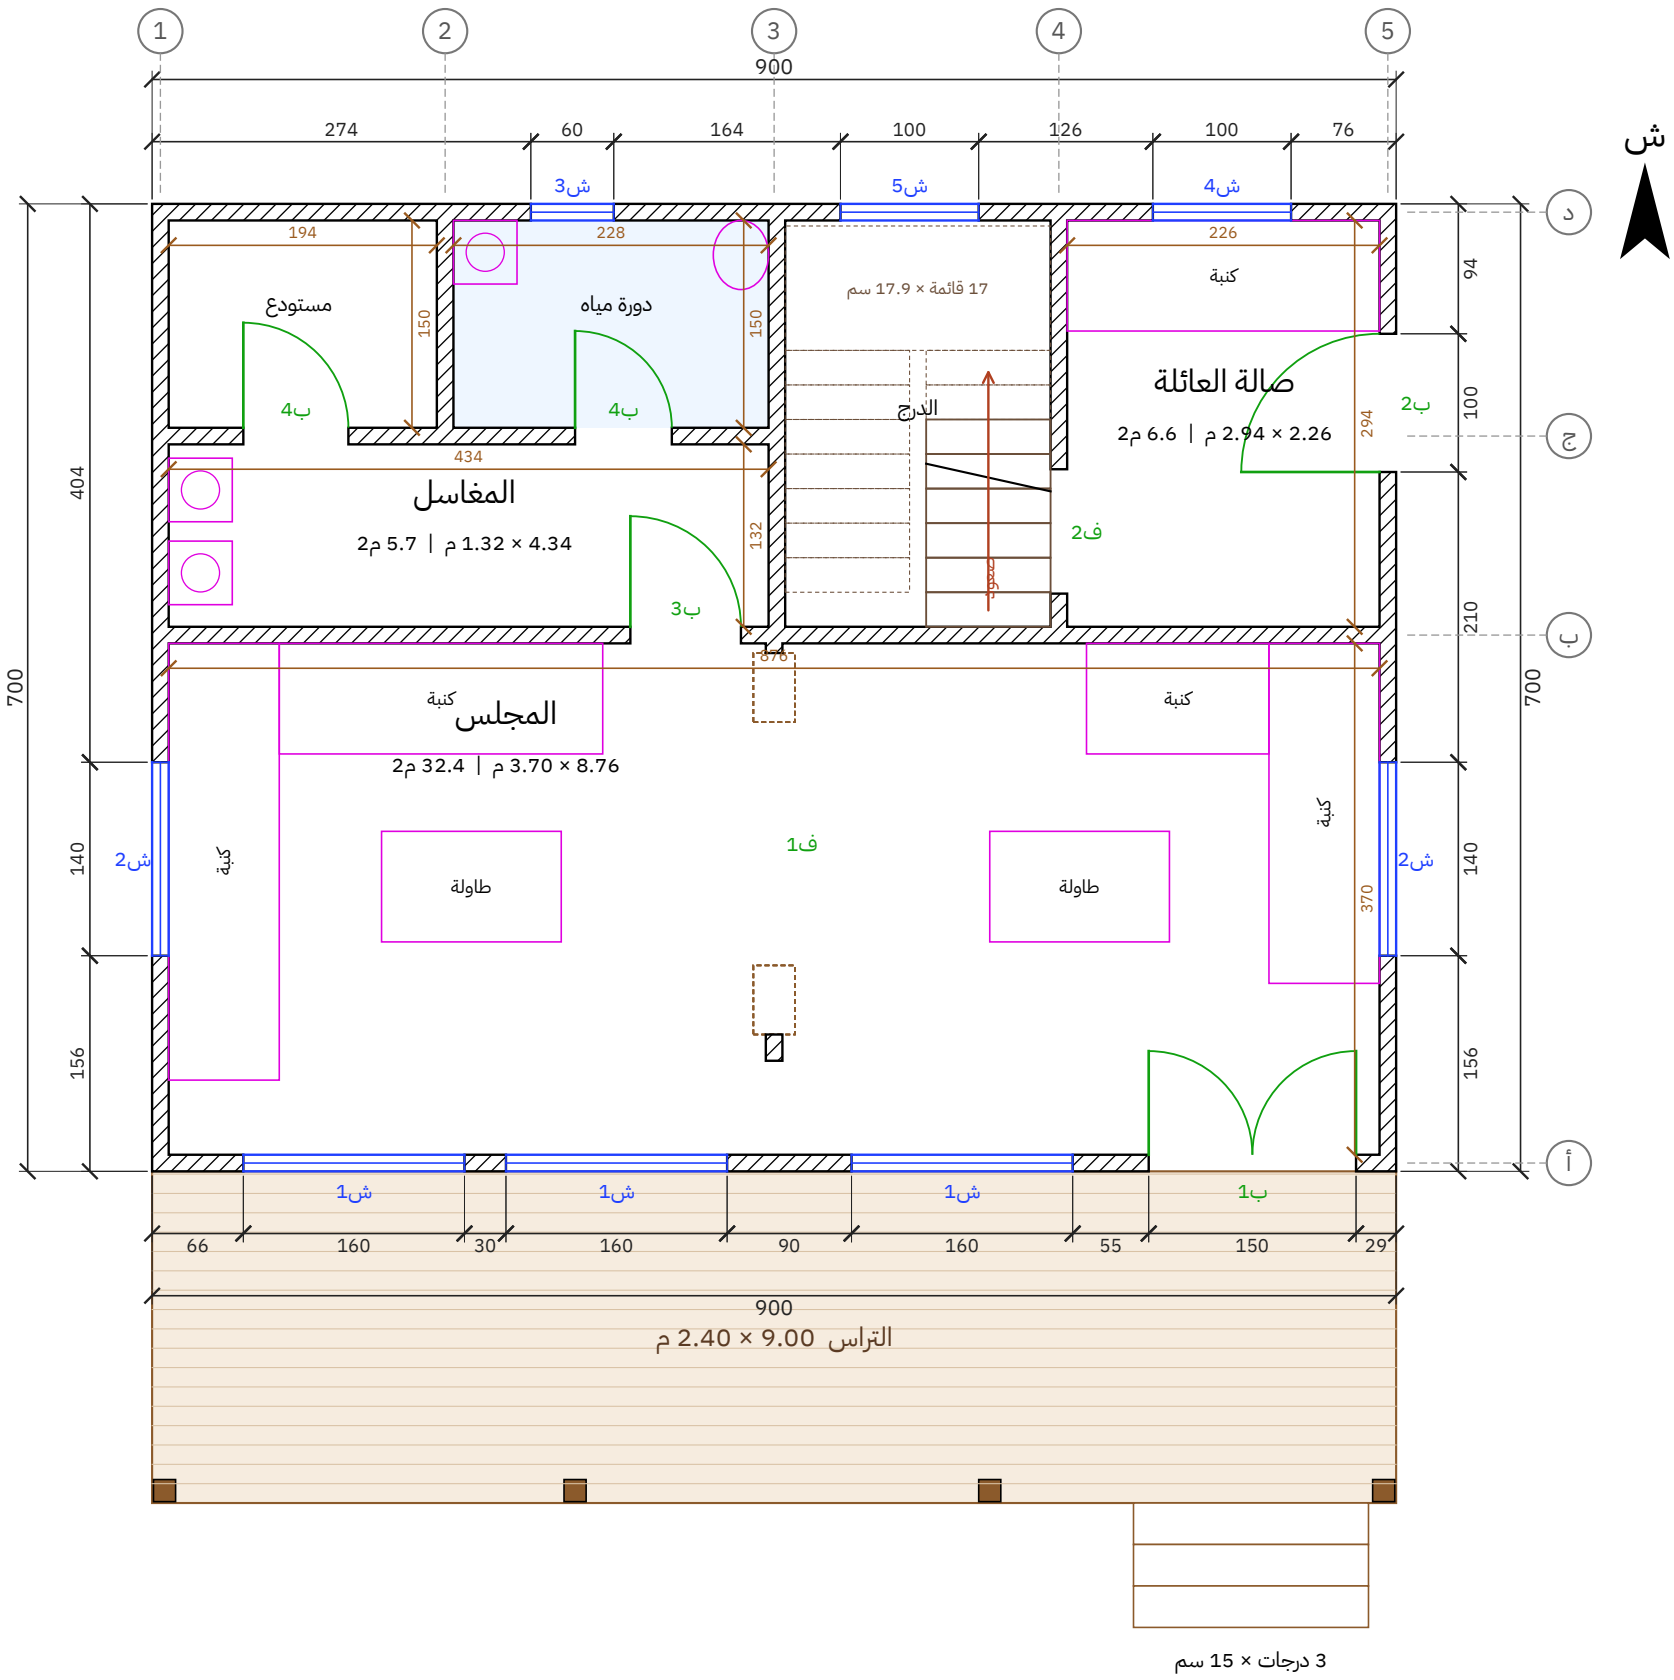


المشروع / العميل	عنوان اللوحة	المقياس	التاريخ	رقم اللوحة
فيلا خشب دورين — مجلس + غرفتين — 9.00 × 7.00 م (63 م² للدور) عميل — تبوك	المسقط الأفقي — الدور الأرضي	1:50	2026-10-24	W-02 (2/21)


مصنع وتد الأخشاب
Watad Wood Factory

المسقط الأفقي مع الفرش — الدور الأول

الأبعاد بالسنتيمتر - الجدران: قوائم 7×5 + تلبيس 2.5 من الجهتين (12 سم) | منسوب الأرضية +3.05

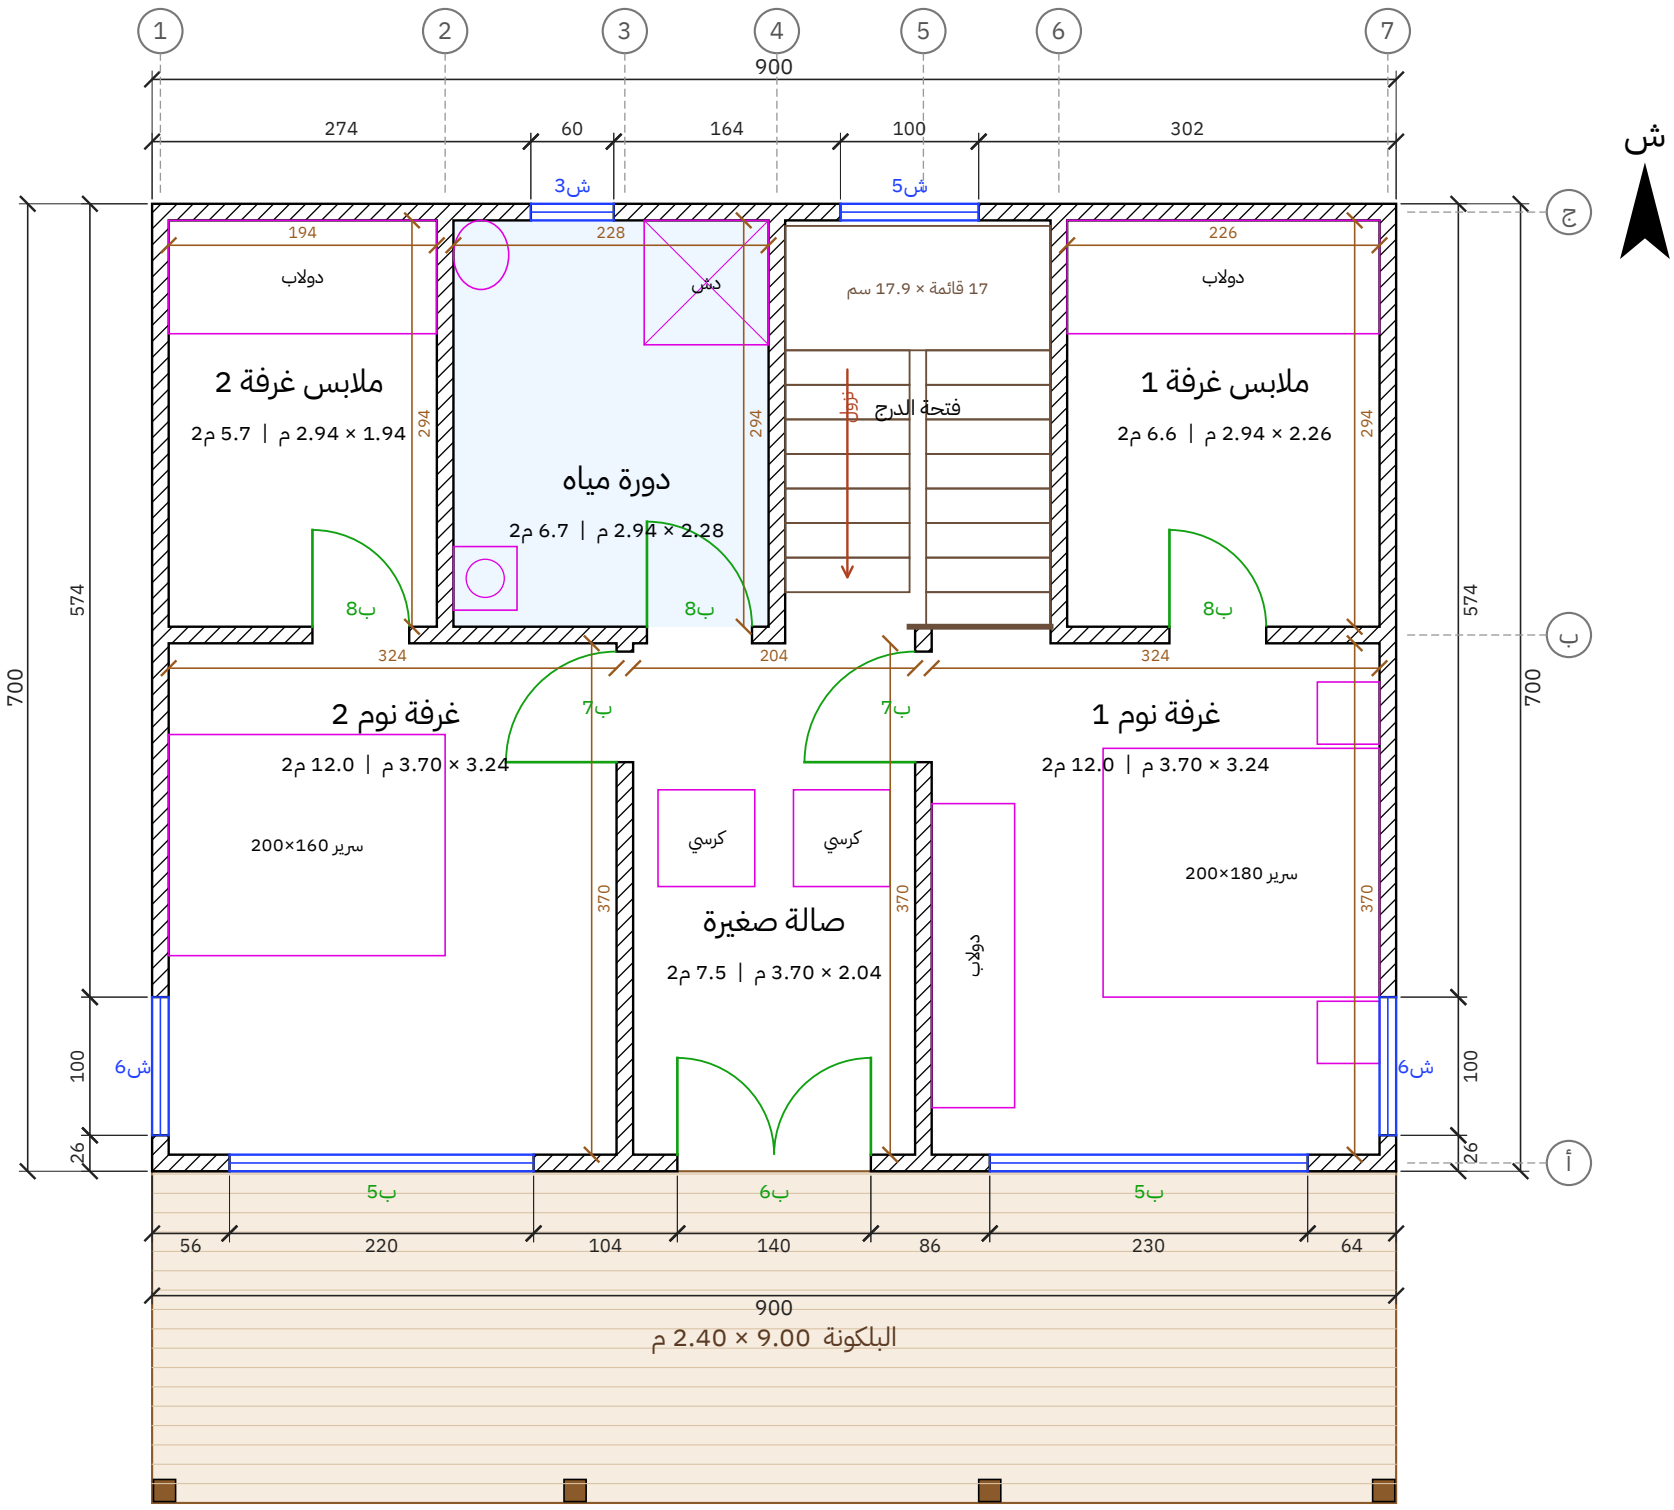


مصنع وتد الأخشاب Watad Wood Factory	المشروع / العميل فيلا خشب دورين — مجلس + غرفتين — 9.00 × 7.00 م (63 م² للدور) عميل — تبوك	عنوان اللوحة المسقط الأفقي — الدور الأول	المقياس 1:50	التاريخ 2026-10-24	رقم اللوحة W-03 (3/21)

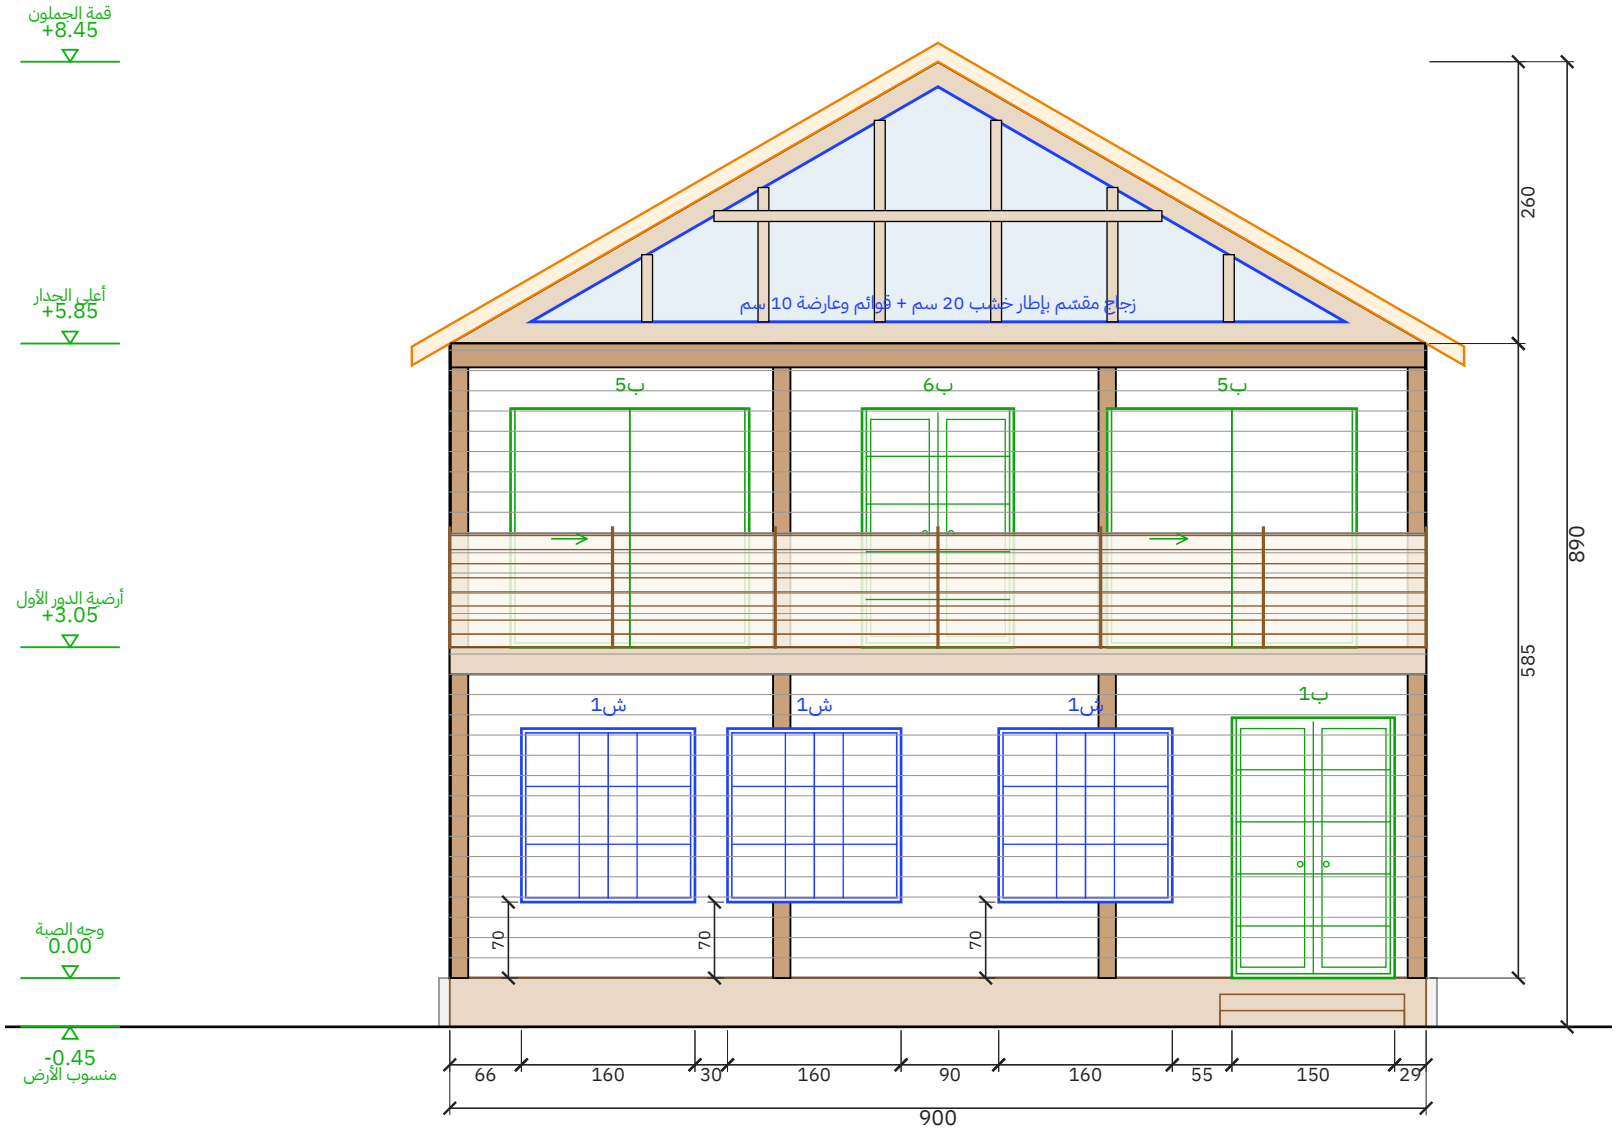

الواجهة الأمامية


مقياس 1:50 | الوحدة: سم

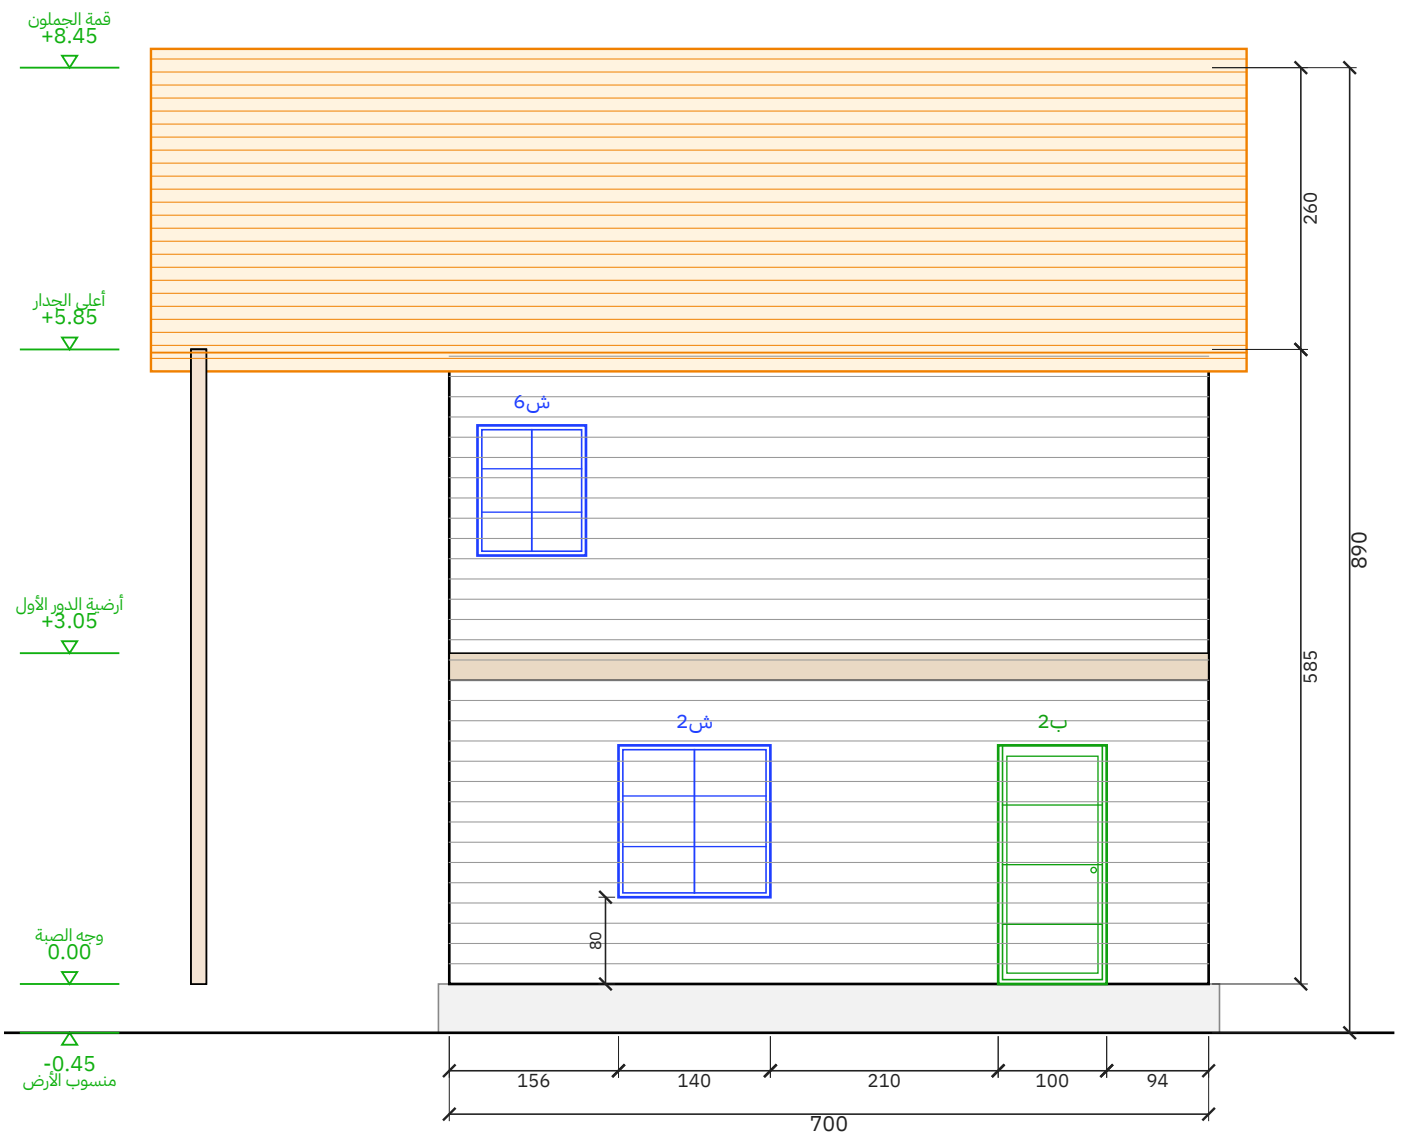

الواجهة الشرقية


مقياس 1:50 | الوحدة: سم

المشروع / العميل	عنوان اللوحة	المقياس	التاريخ	رقم اللوحة
مصنع وتد الأخشاب Watad Wood Factory فيلا خشب دورين – مجلس + غرفتين – 9.00 × 7.00 م (63 م² للدور) عميل – تبوك	الواجهة الأمامية والواجهة الشرقية	1:50	2026-10-24	W-04 (4/21)

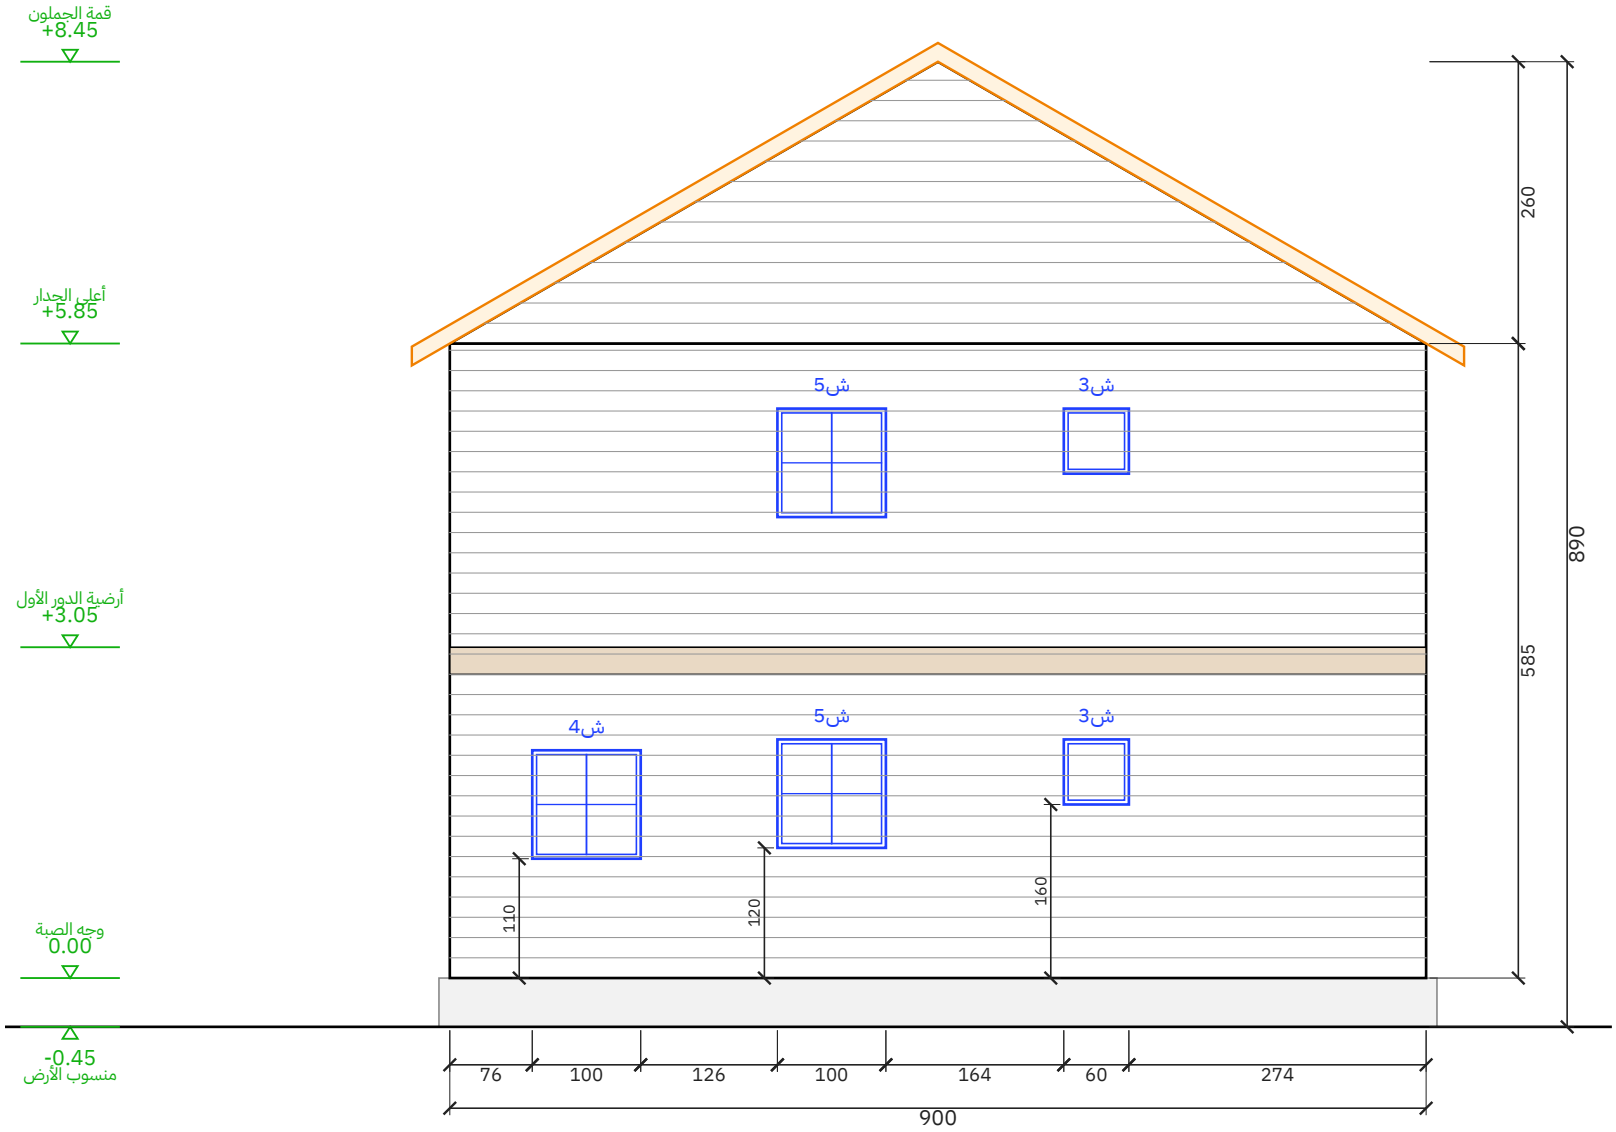

الواجهة الخلفية

مقياس 1:50 | الوحدة: سم

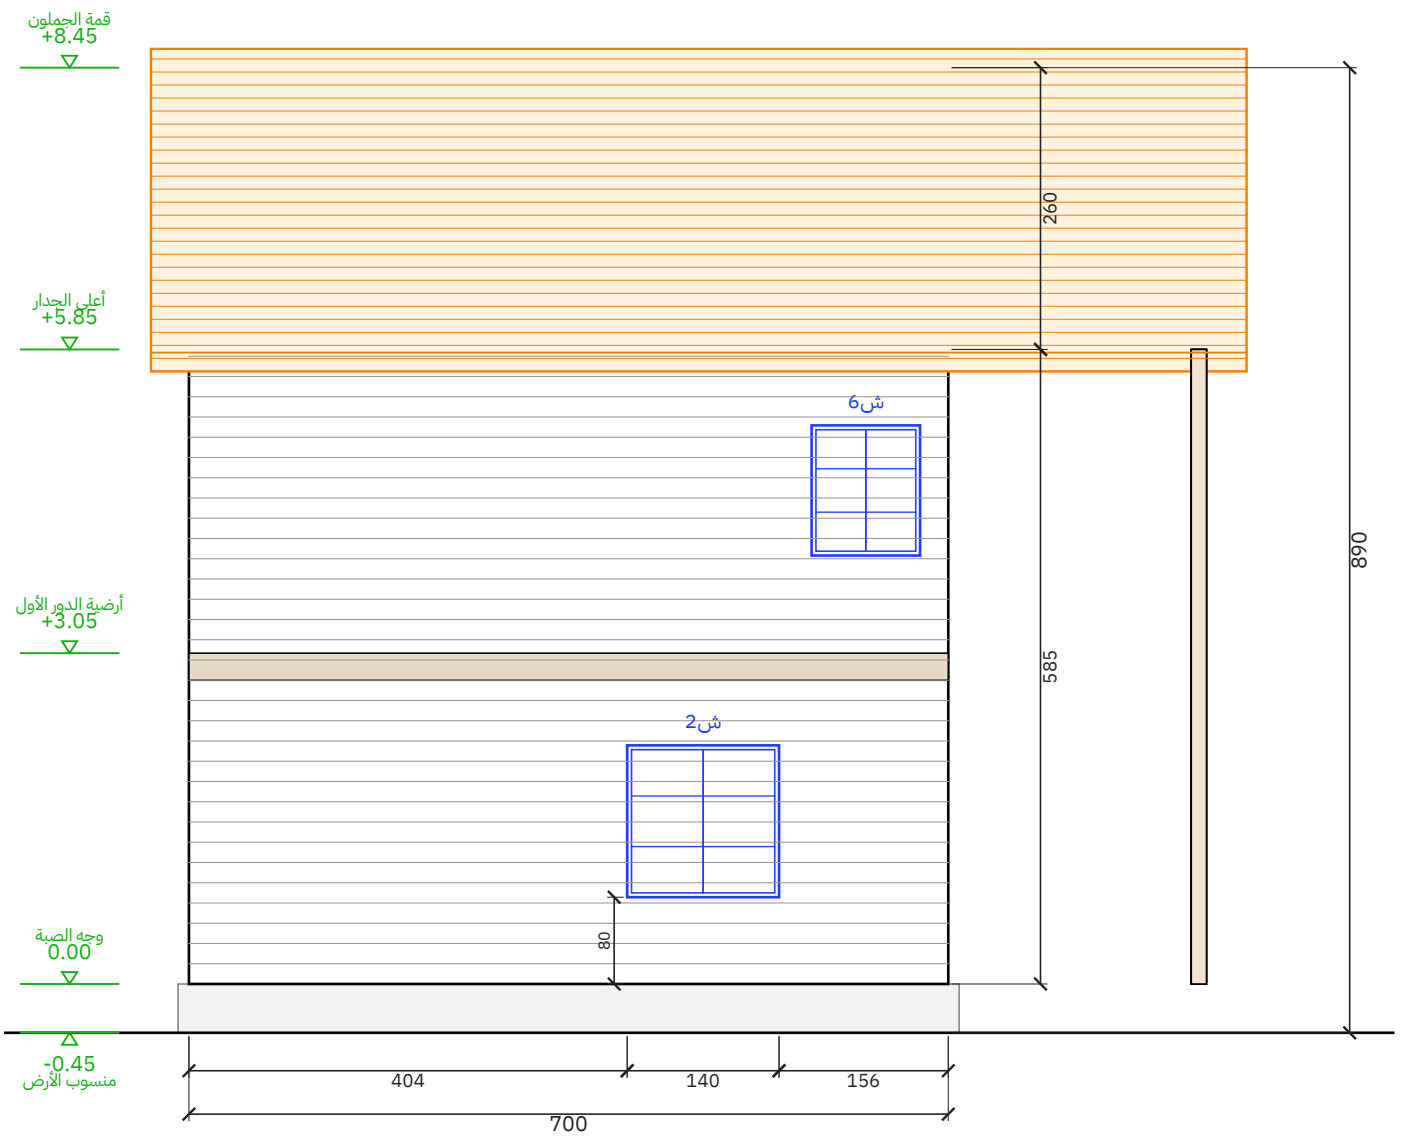

الواجهة الغربية


مقياس 1:50 | الوحدة: سم

المشروع / العميل	عنوان اللوحة	المقياس	التاريخ	رقم اللوحة
فيلا خشب دورين – مجلس + غرفتين – 9.00 × 7.00 م (63 م² للدور) عميل – تبوك	الواجهة الخلفية والواجهة الغربية	1:50	2026-10-24	W-05 (5/21)


مصنع وتد الأخشاب
Watad Wood Factory

قطاع عرضي أ-أ

مقياس 1:50 | الوحدة: سم

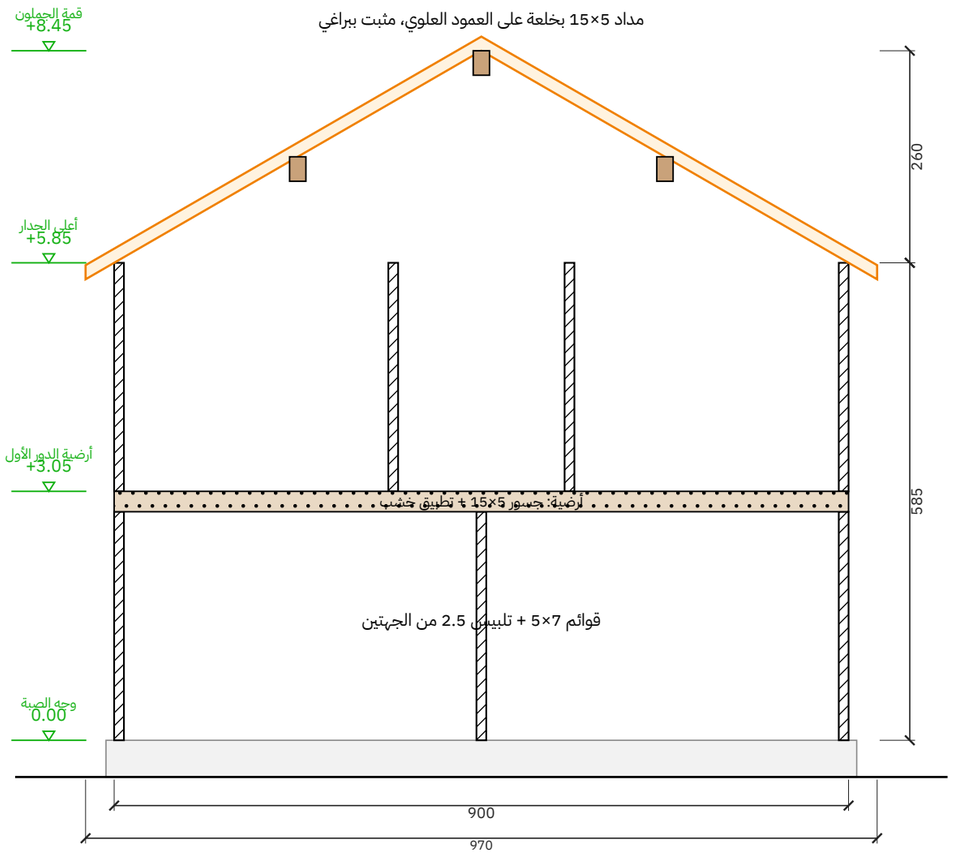


تفصيلة جلوس المداد على العلوي (1:5)

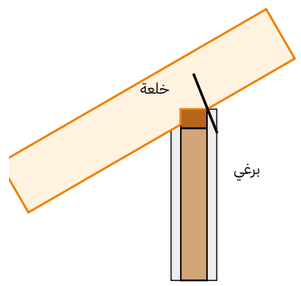

علوي 7×5 على قائم 7×5

مسقط السقف (جملون)

رفرف 35 سم من كل جهة | مقياس 1:50

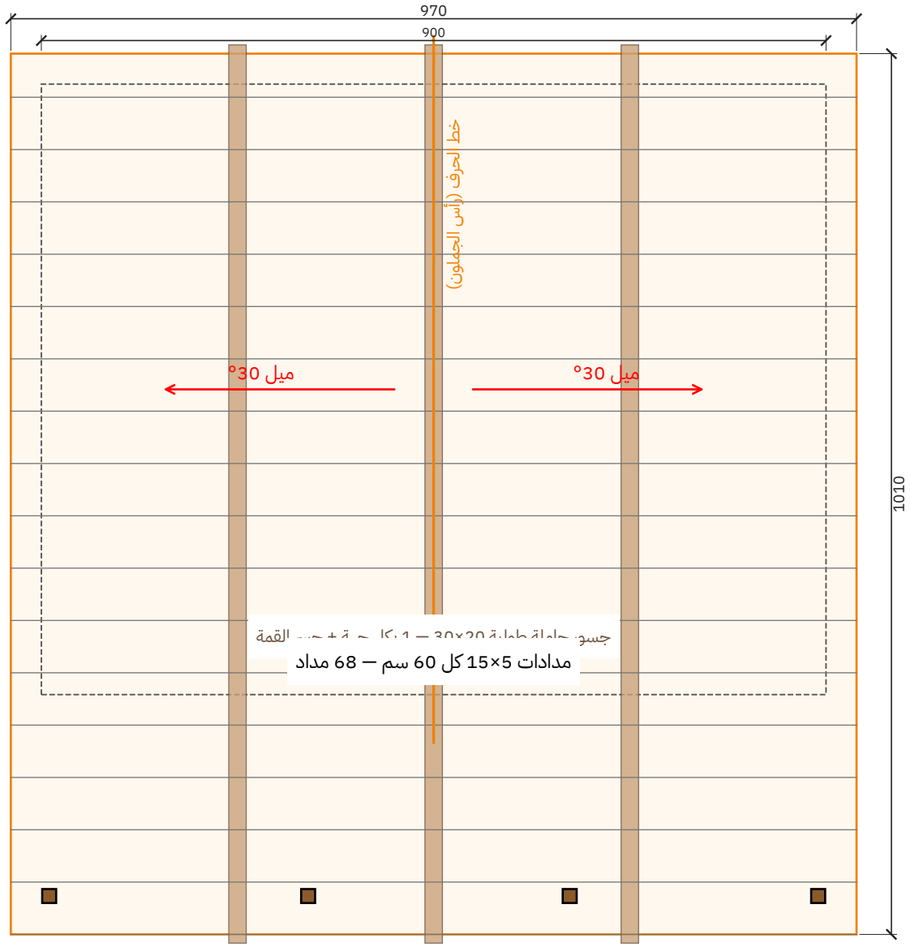

المشروع / العميل: فيلا خشب دورين — مجلس + غرفتين — 9.00 × 7.00 م (63 م² للدور) — عميل — تبوك	عنوان اللوحة: مسقط السقف والقطاع	المقياس: —	التاريخ: 2026-10-24	رقم اللوحة: W-06 (6/21)

مصنع وتد الأخشاب
Watad Wood Factory

جدول مقاسات الأبواب والشبابيك

مقاس الفتحة الصافي في الجدار - الوحدة: سم

الرمز	النوع	العرض (سم)	الارتفاع (سم)	ارتفاع الجلسة (سم)	العدد	الموقع
ب1	باب مزدوج	150	240	-	1	الأمامية
ب2	باب	100	220	-	1	الشرقية
ب3	باب	80	220	-	1	المجلس — المغاسل
ب4	باب	76	210	-	1	المستودع
ب4	باب	70	210	-	1	دورة المياه
ب5	باب مزدوج	220	220	-	1	الأمامية (على البلكونة)
ب5	باب مزدوج	230	220	-	1	الأمامية (على البلكونة)
ب6	باب مزدوج	140	220	-	1	الأمامية (على البلكونة)
ب7	باب	80	210	-	2	غرفة 2 - غرفة 1
ب8	باب	70	210	-	2	ملابس غرفة 2 - ملابس غرفة 1
ب8	باب	76	210	-	1	دورة المياه
ف1	باب	276	250	-	1	بارتشن مفتوح بعمودين مكتبة
ف2	باب	90	220	-	1	صالة العائلة — الدرج
ش1	شباك	160	160	70	3	الأمامية 3
ش2	شباك	140	140	80	2	الشرقية - الغربية
ش3	شباك	60	60	160	2	الخلفية 2
ش4	شباك	100	100	110	1	الخلفية
ش5	شباك	100	100	120	2	الخلفية 2
ش6	شباك	100	120	90	2	الشرقية - الغربية

الإجمالي: أبواب 15 - شبابيك 12

جدول المساحات وبيانات المشروع والتسعير

بيانات المشروع

البند	البيان
المشروع	فيلا خشب دورين — مجلس + غرفتين — 9.00 × 7.00 م (63 م² للدور)
العميل	عميل — تبوك
الموقع	تبوك
الاستخدام	سكن — مجلس ضيوف + غرفتين
التاريخ	2026-10-24
نظام البناء	هيكل خشب 5×7 + تلبيس 2.5 سم من الجهتين
السقف	جملون 30° — قرميد معدني

جدول المساحات

م	الفراغ	الأبعاد (م)	المساحة (م2)
1	أرضي — المجلس	3.70 × 8.76	32.41
2	أرضي — المغاسل	1.32 × 4.34	5.73
3	أرضي — مستودع	1.50 × 1.94	2.91
4	أرضي — دورة مياه	1.50 × 2.28	3.42
5	أرضي — الدرج	2.94 × 1.92	5.64
6	أرضي — صالة العائلة	2.94 × 2.26	6.64
7	أول — غرفة نوم 2	3.70 × 3.24	11.99
8	أول — صالة صغيرة	3.70 × 2.04	7.55
9	أول — غرفة نوم 1	3.70 × 3.24	11.99
10	أول — ملابس غرفة 2	2.94 × 1.94	5.70
11	أول — دورة مياه	2.94 × 2.28	6.70
12	أول — ملابس غرفة 1	2.94 × 2.26	6.64
	المساحة الصافية الداخلية		107.34
	التراس	**9.00 × 2.40**	**21.60**
	البلكونة	**9.00 × 2.40**	**21.60**
	المساحة الإجمالية المبنية	**9.00 × 7.00 × 2 دور**	**126.00**
	المساحة الكلية (المبنية + التراس والبلكونة)		**169.20**


التسعير المفصّل

البند	المبلغ (ريال)
الكوخ المبني 126.00 م² × 1,096	138,096
تراس الأرضي + بلكونة الأول (9.00 × 2.40 × 2) — 43.20 م² × 1,096	47,347
الإجمالي (ريال)	**185,443**


ملاحظات:

- السعر للدورين والتراس والبلكونة حسب المخطط المعتمد — التراس يُسعّر بنفس سعر متر الكوخ.
- الصبة والتمديدات الخارجية على العميل ما لم يُذكر غير ذلك.

تأطير جدار أ-جنوب — الطول 888 سم، الارتفاع 280 سم

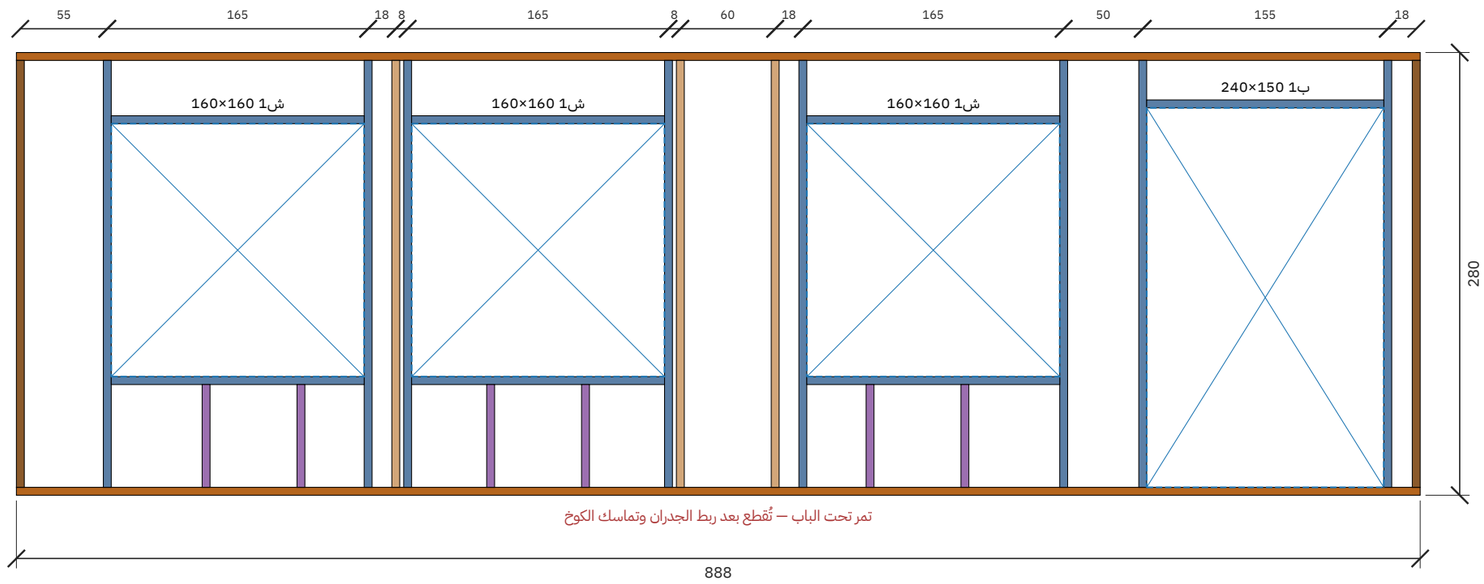

تأطير جدار أ-شرق — الطول 688 سم، الارتفاع 280 سم

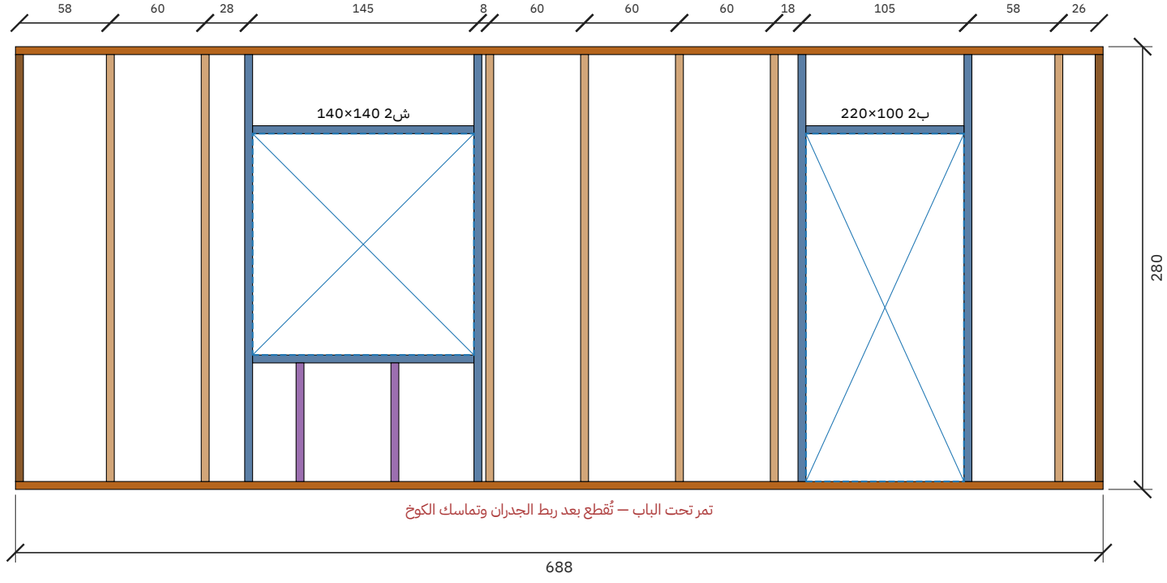


قاعدة سفلية | علوي | عمود | عمود زاوية | جنب فتحة | رأس فتحة | جلسة شباك | عمود قصير


المشروع / العميل	عنوان اللوحة	المقياس	التاريخ	رقم اللوحة
فيلا خشب دورين — مجلس + غرفتين — 9.00 × 7.00 م (63 م² للدور) عميل — تبوك	لوحات التأطير (للورشة)	—	2026-10-24	W-09 (9/21)

مصنع وتد الأخشاب
Watad Wood Factory

تأطير جدار أ-شمال — الطول 888 سم، الارتفاع 280 سم

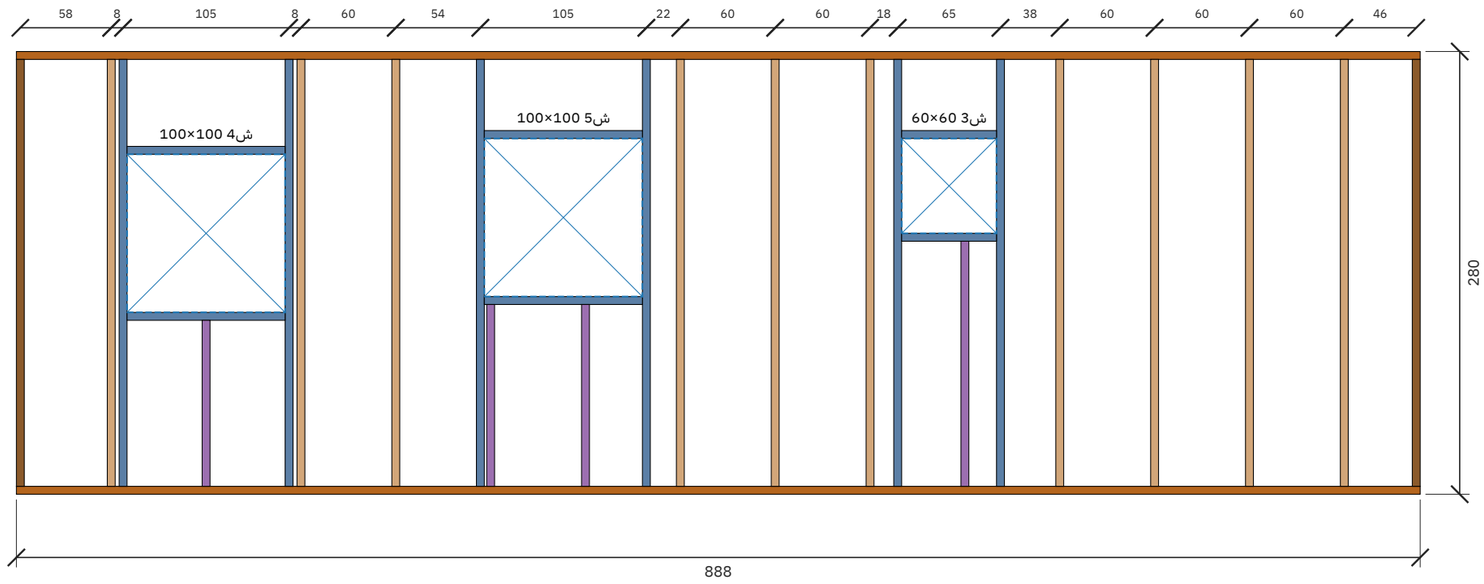

تأطير جدار أ-غرب — الطول 688 سم، الارتفاع 280 سم

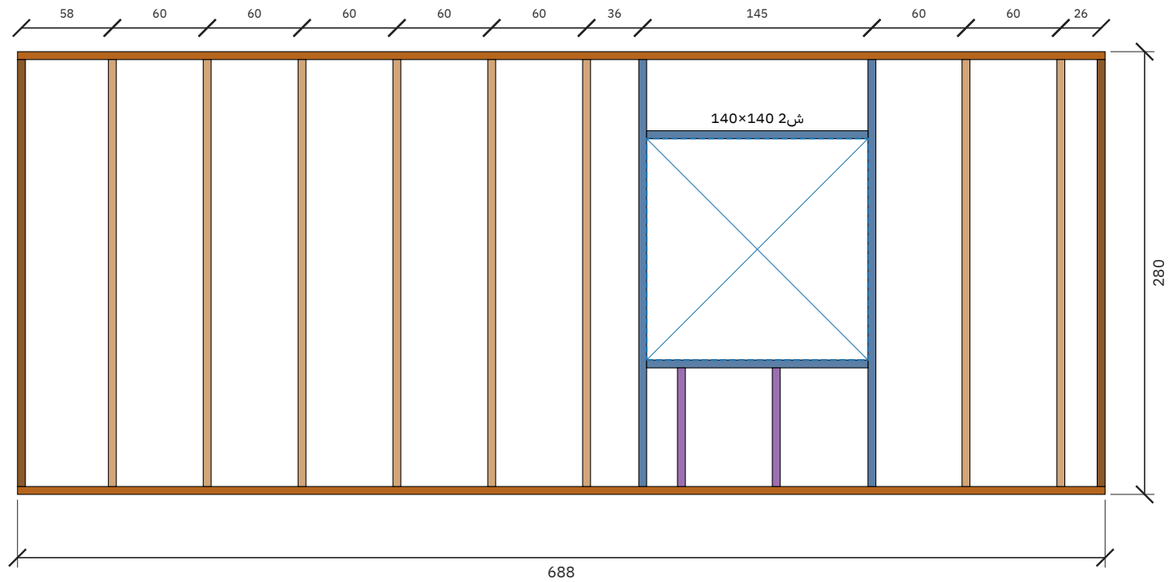


قاعدة سفلية — علوي — عمود — عمود زاوية — جنب فتحة — رأس فتحة — جلسة شباك — عمود قصير


المشروع / العميل	عنوان اللوحة	المقياس	التاريخ	رقم اللوحة
فيلا خشب دورين — مجلس + غرفتين — 9.00 × 7.00 م (63 م² للدور) **عميل — تبوك**	**لوحات التأطير (للورشة)**	**—**	**2026-10-24**	**W-10 (10/21)**

مصنع وتد الأخشاب
Watad Wood Factory

تأطير جدار أ-خلف المجلس — الطول 888 سم، الارتفاع 280 سم (داخلي)

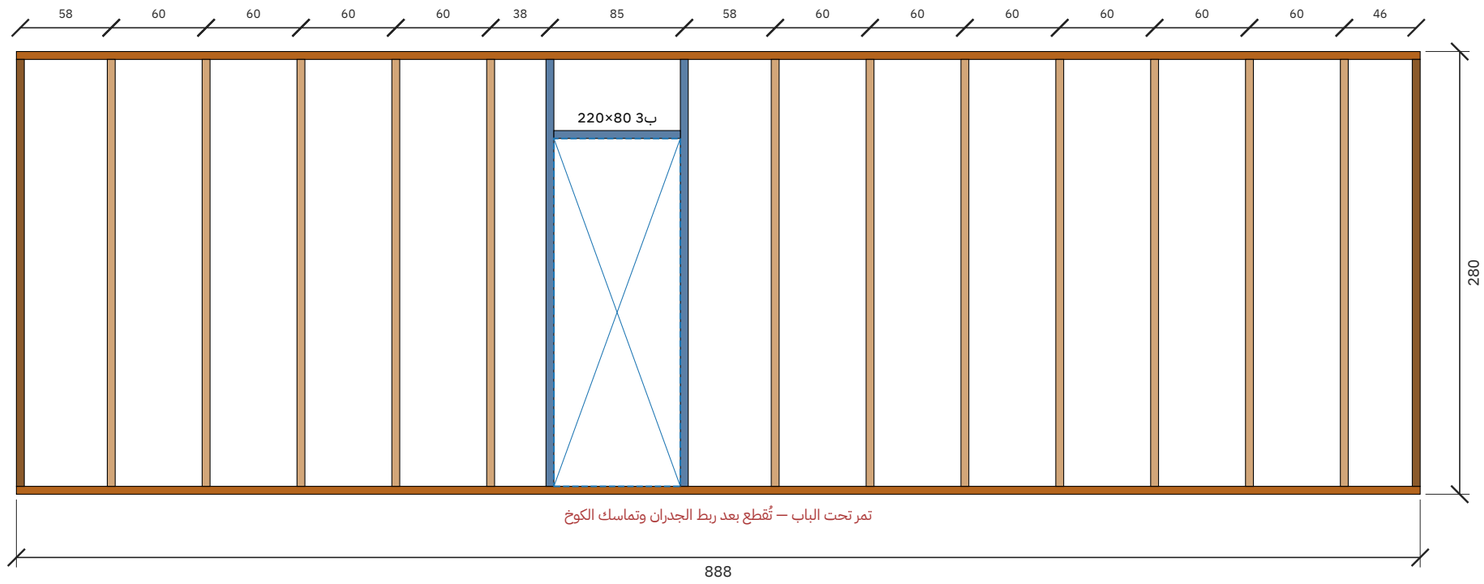


تأطير جدار أ-بارتشن المجلس — الطول 302 سم، الارتفاع 280 سم (داخلي)

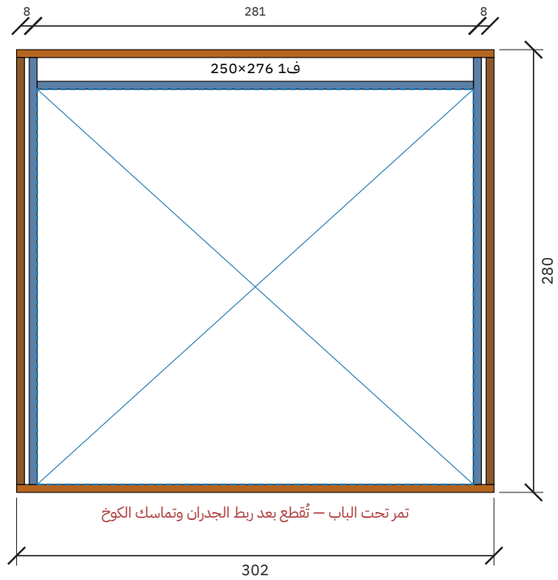


قاعدة سفلية | علوي | عمود | عمود زاوية | جنب فتحة | رأس فتحة | جلسة شباك | عمود قصير

مصنع وتد الأخشاب Watad Wood Factory	المشروع / العميل **فيلا خشب دورين — مجلس + غرفتين — 9.00 × 7.00 م (63 م² للدور)** **عميل — تبوك**	عنوان اللوحة **لوحات التأطير (للورشة)**	المقياس **—**	التاريخ **2026-10-24**	رقم اللوحة **W-11 (11/21)**

تأطير جدار أ-جدار الدرج الغربي — الطول 306 سم، الارتفاع 280 سم (داخلي)

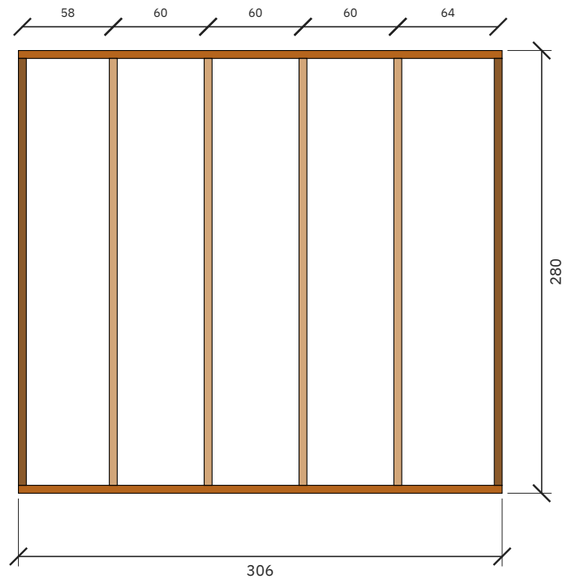

تأطير جدار أ-جدار الدرج الشرقي — الطول 306 سم، الارتفاع 280 سم (داخلي)

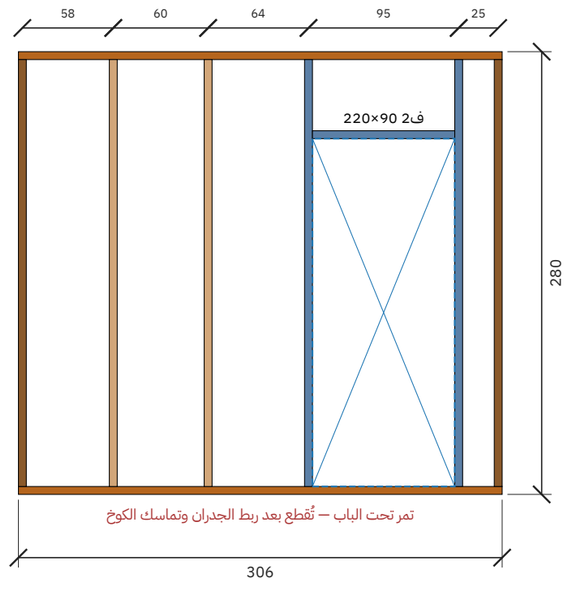


قاعدة سفلية | علوي | عمود | عمود زاوية | جنب فتحة | رأس فتحة | جلسة شباك | عمود قصير


المشروع / العميل	عنوان اللوحة	المقياس	التاريخ	رقم اللوحة
فيلا خشب دورين — مجلس + غرفتين — 9.00 × 7.00 م (63 م² للدور) **عميل — تبوك**	**لوحات التأطير (للورشة)**	**—**	**2026-10-24**	**W-12 (12/21)**

مصنع وتد الأخشاب
Watad Wood Factory

تأطير جدار أ-فاصل المغاسل — الطول 446 سم، الارتفاع 280 سم (داخلي)

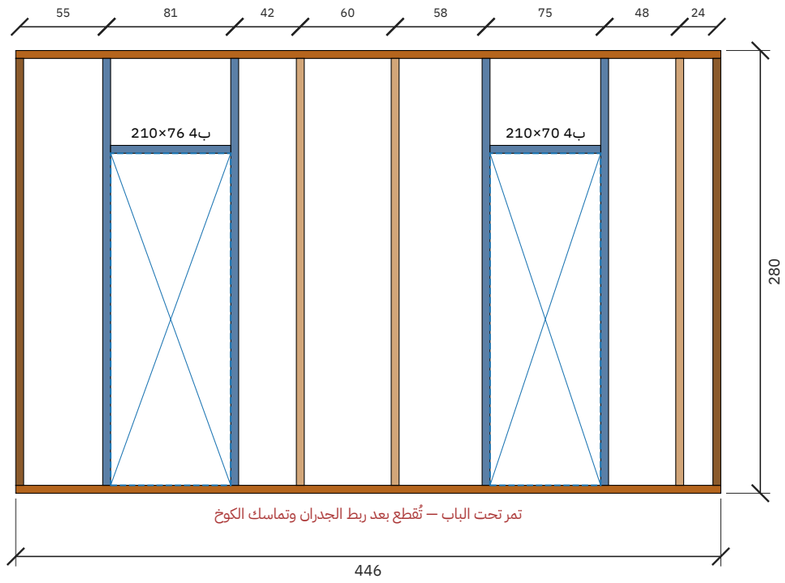

تأطير جدار أ-جدار الدورة — الطول 162 سم، الارتفاع 280 سم (داخلي)

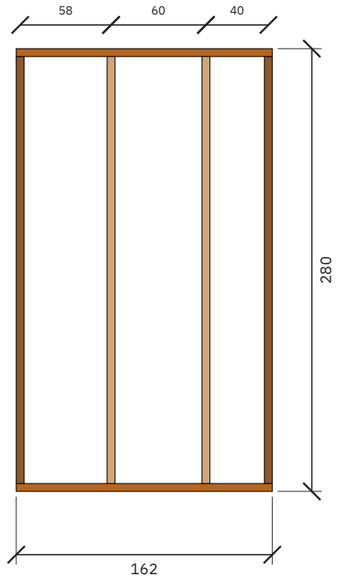


قاعدة سفلية | علوي | عمود | عمود زاوية | جنب فتحة | رأس فتحة | جلسة شباك | عمود قصير


المشروع / العميل	عنوان اللوحة	المقياس	التاريخ	رقم اللوحة
فيلا خشب دورين — مجلس + غرفتين — 9.00 × 7.00 م (63 م² للدور) **عميل — تبوك**	**لوحات التأطير (للورشة)**	**—**	**2026-10-24**	**W-13 (13/21)**

مصنع وتد الأخشاب
Watad Wood Factory

تأطير جدار ب-جنوب — الطول 888 سم، الارتفاع 280 سم

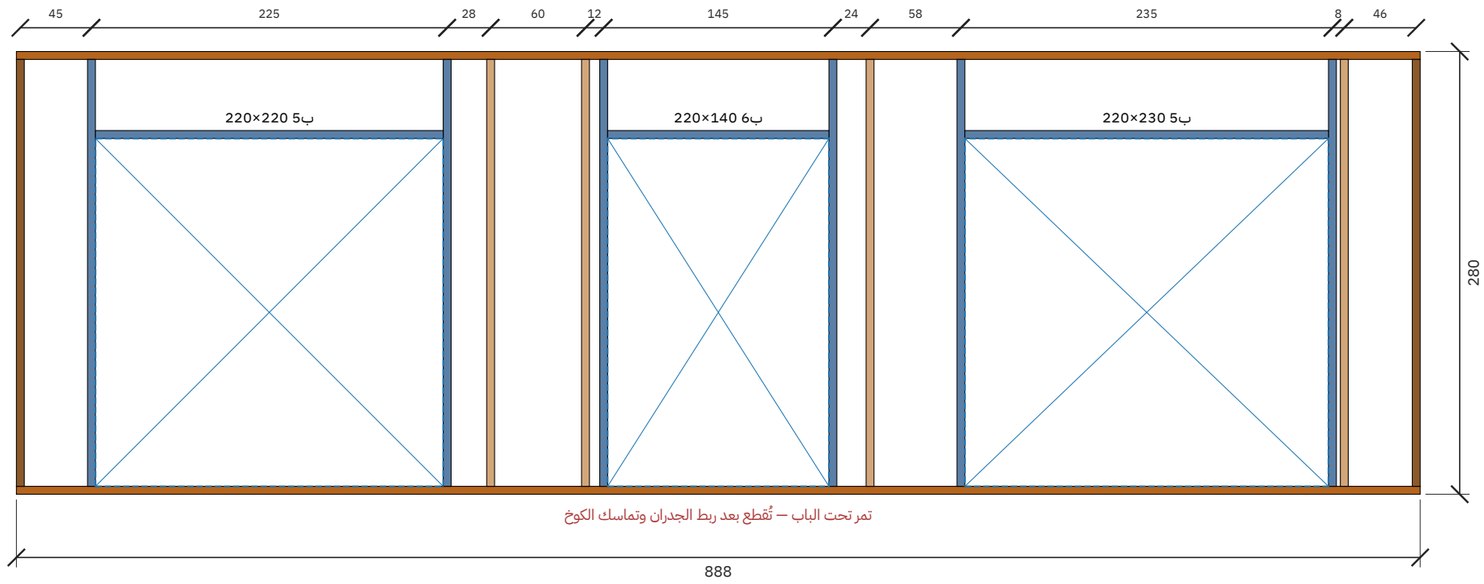

تأطير جدار ب-شرق — الطول 688 سم، الارتفاع 280 سم

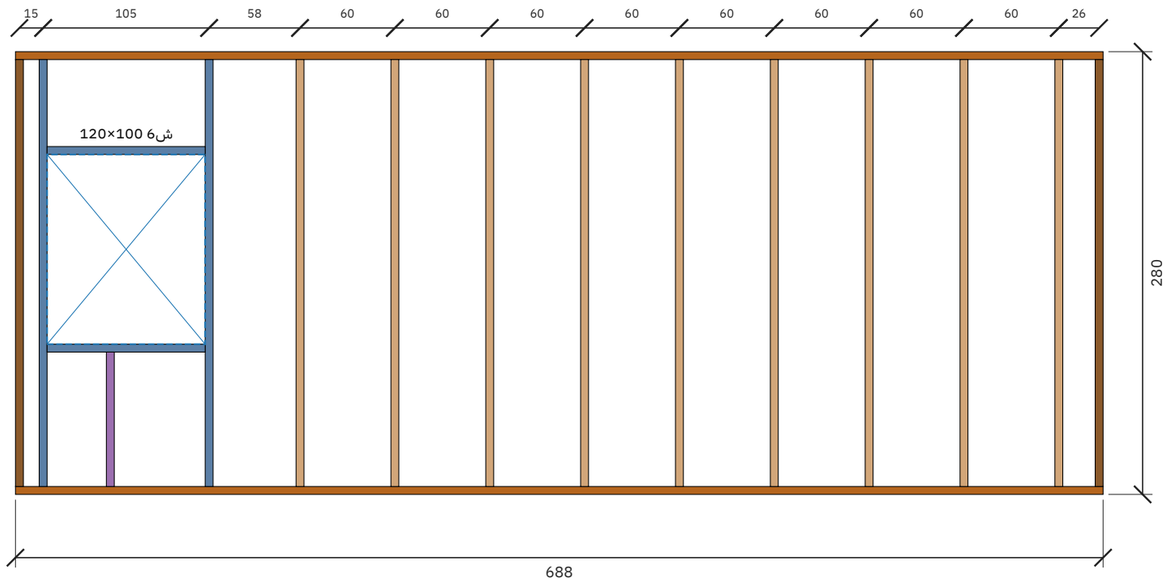


قاعدة سفلية | علوي | عمود | عمود زاوية | جنب فتحة | رأس فتحة | جلسة شباك | عمود قصير


المشروع / العميل	عنوان اللوحة	المقياس	التاريخ	رقم اللوحة
فيلا خشب دورين — مجلس + غرفتين — 9.00 × 7.00 م (63 م² للدور) عميل — تبوك	لوحات التأطير (للورشة)	—	2026-10-24	W-14 (14/21)

مصنع وتد الأخشاب
Watad Wood Factory

تأطير جدار ب-شمال — الطول 888 سم، الارتفاع 280 سم

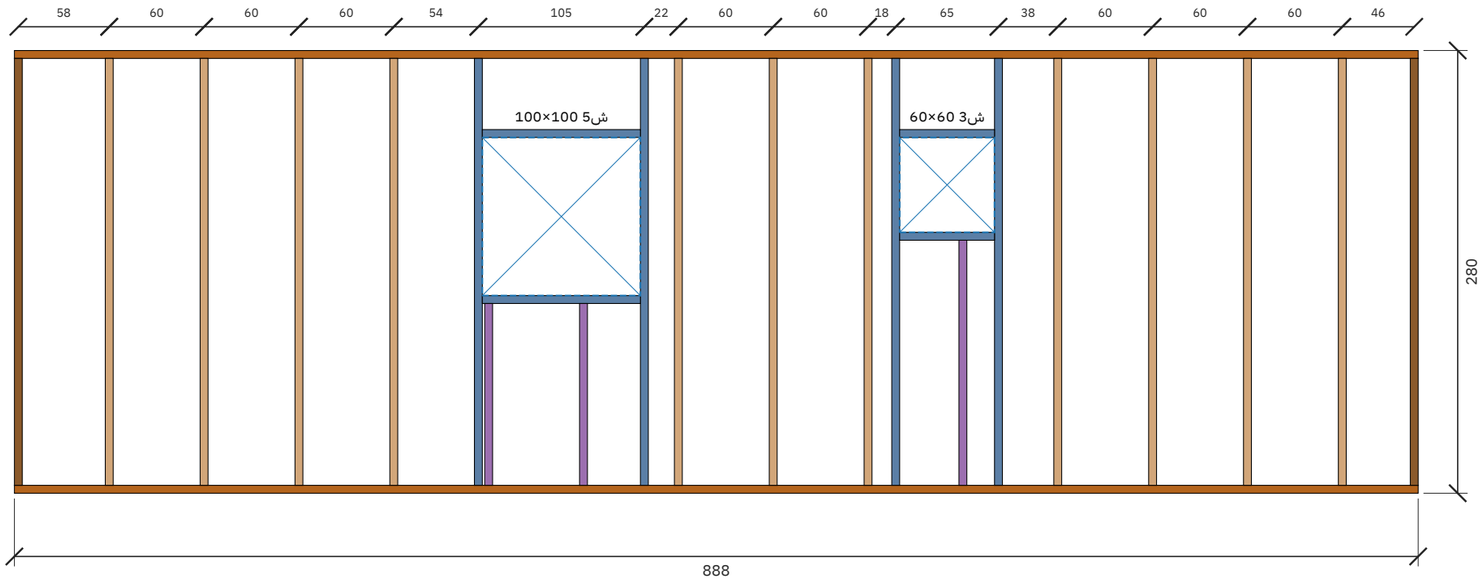


تأطير جدار ب-غرب — الطول 688 سم، الارتفاع 280 سم

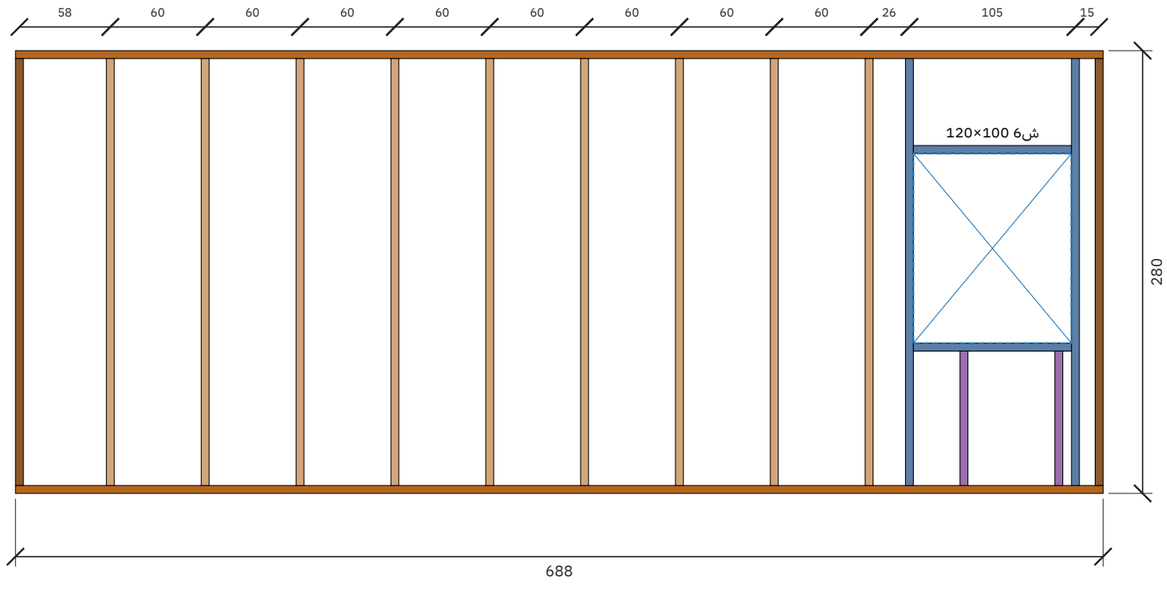


قاعدة سفلية | علوي | عمود | عمود زاوية | جنب فتحة | رأس فتحة | جلسة شباك | عمود قصير

مصنع وتد الأخشاب Watad Wood Factory	المشروع / العميل فيلا خشب دورين — مجلس + غرفتين — 9.00 × 7.00 م (63 م² للدور) عميل — تبوك	عنوان اللوحة لوحات التأطير (للورشة)	المقياس —	التاريخ 2026-10-24	رقم اللوحة W-15 (15/21)

تأطير جدار ب-جدار غرفة 2 — الطول 382 سم، الارتفاع 280 سم (داخلي)

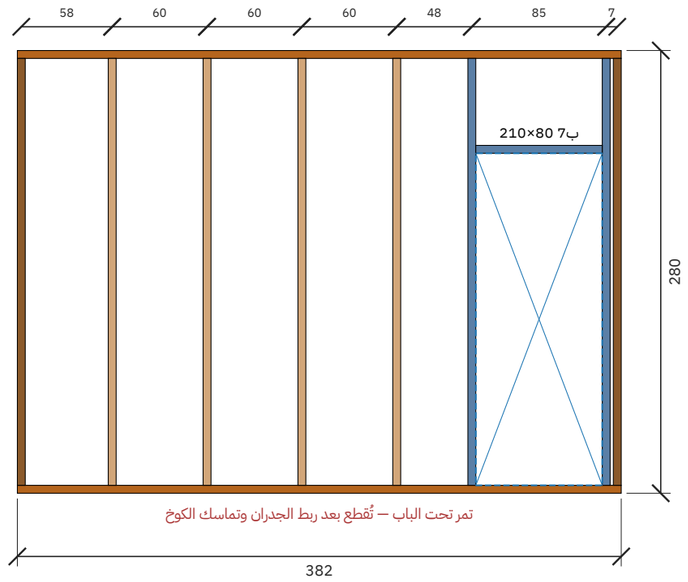


تأطير جدار ب-جدار غرفة 1 — الطول 382 سم، الارتفاع 280 سم (داخلي)

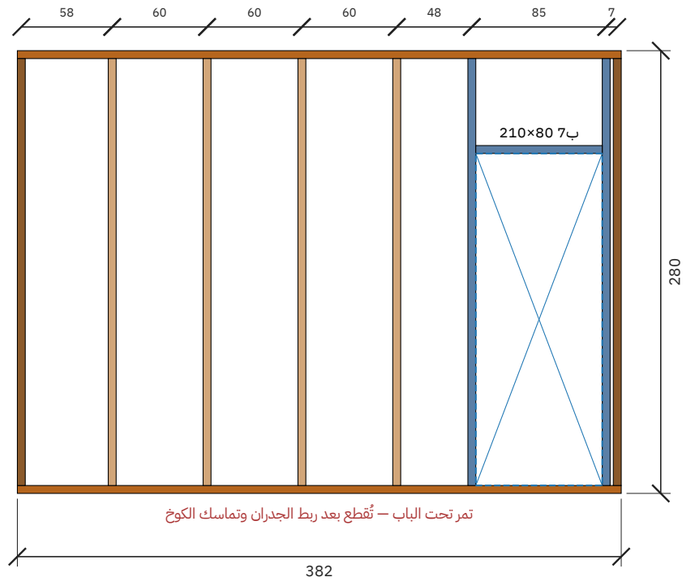


قاعدة سفلية | علوي | عمود | عمود زاوية | جنب فتحة | رأس فتحة | جلسة شباك | عمود قصير

مصنع وتد الأخشاب Watad Wood Factory	المشروع / العميل فيلا خشب دورين — مجلس + غرفتين — 9.00 × 7.00 م (63 م² للدور) عميل — تبوك	عنوان اللوحة لوحات التأطير (للورشة)	المقياس —	التاريخ 2026-10-24	رقم اللوحة W-16 (16/21)

تأطير جدار ب-خلف الغرف غرب — الطول 446 سم، الارتفاع 280 سم (داخلي)

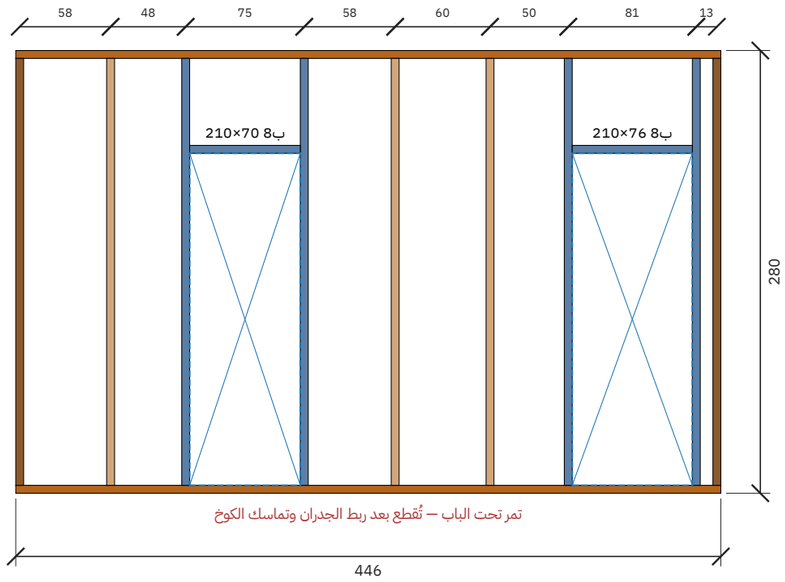


تأطير جدار ب-خلف الغرف شرق — الطول 238 سم، الارتفاع 280 سم (داخلي)

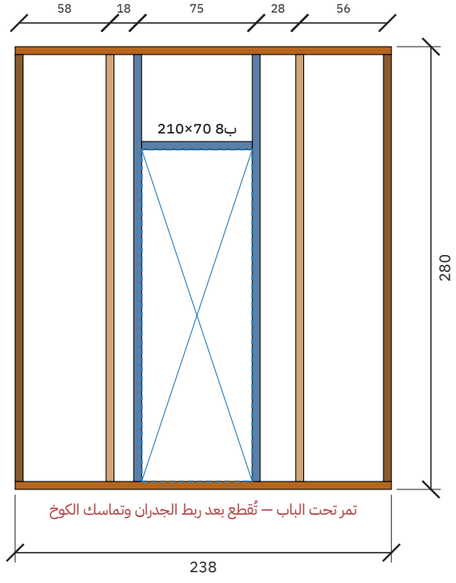


قاعدة سفلية | علوي | عمود | عمود زاوية | جنب فتحة | رأس فتحة | جلسة شباك | عمود قصير

مصنع وتد الأخشاب Watad Wood Factory	المشروع / العميل فيلا خشب دورين — مجلس + غرفتين — 9.00 × 7.00 م (63 م² للدور) عميل — تبوك	عنوان اللوحة لوحات التأطير (للورشة)	المقياس —	التاريخ 2026-10-24	رقم اللوحة W-17 (17/21)

تأطير جدار ب-جدار الدرج الغربي — الطول 306 سم، الارتفاع 280 سم (داخلي)

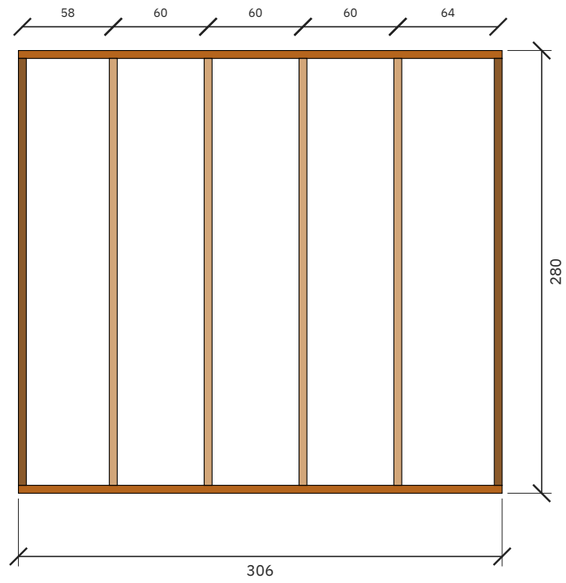


تأطير جدار ب-جدار الدرج الشرقي — الطول 306 سم، الارتفاع 280 سم (داخلي)

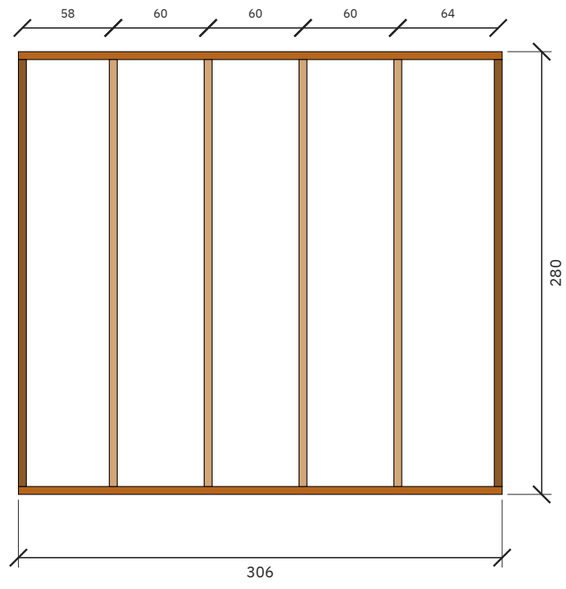

قاعدة سفلية | علوي | عمود | عمود زاوية | جنب فتحة | رأس فتحة | جلسة شباك | عمود قصير

مصنع وتد الأخشاب Watad Wood Factory	المشروع / العميل فيلا خشب دورين — مجلس + غرفتين — 9.00 × 7.00 م (63 م² للدور) عميل — تبوك	عنوان اللوحة لوحات التأطير (للورشة)	المقياس —	التاريخ 2026-10-24	رقم اللوحة W-18 (18/21)

تأطير جدار ب-جدار الدورة — الطول 306 سم، الارتفاع 280 سم (داخلي)

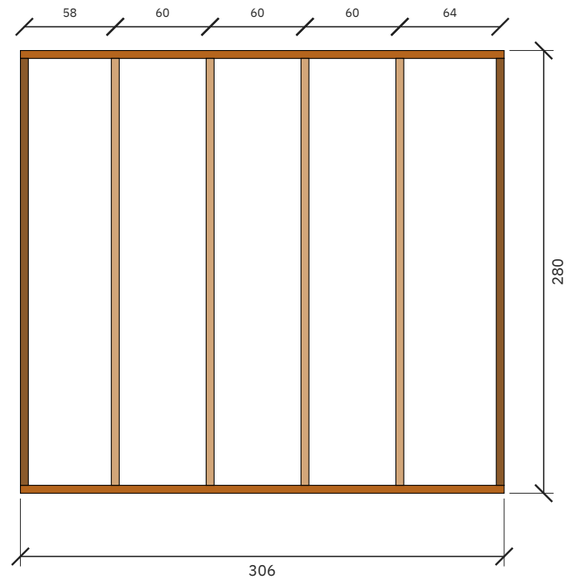

عمود قصير
جلسة شباك
رأس فتحة
جنب فتحة
عمود زاوية
عمود
علوي
قاعدة سفلية

المشروع / العميل	عنوان اللوحة	المقياس	التاريخ	رقم اللوحة
فيلا خشب دورين — مجلس + غرفتين — 9.00 × 7.00 م (63 م² للدور) **عميل — تبوك**	**لوحات التأطير (للورشة)**	**—**	**2026-10-24**	**W-19 (19/21)**

مصنع وتد الأخشاب
Watad Wood Factory

جدول الكميات وخطة تقطيع الطبليات

البند	القيمة
الارتفاع المطلوب / المعتمد	280 / 280 سم
السقف	جملون 30° — أعلى نقطة 845 سم من وجه الصبة
المدادات 5×15	68 مداد (17 خط × قطعتين موصولة فوق الجسر الحامل بتراكب 60 سم) × حتى 335 سم — من طبلية 480
طبليات الطريقة الأولى (مداد + عمود)	68 طبلية × 480 سم
طبليات الطريقة الثانية (3 أعمدة)	66 طبلية × 320 سم
مدادات أرضية الدور العلوي 5×15 كل 60 سم	48 مداد — 214سم×12، 216سم×12، 248سم×24 (طبلية 320 بالطريقة الأولى)
إجمالي الطبليات 5×22.5	182
إجمالي قطع 5×7	306
قائمة تقطيع 5×7	888سم×10 | 688سم×8 | 446سم×4 | 382سم×4 | 306سم×10 | 302سم×2 | 276سم×1 | 270سم×205 | 238سم×2
	230سم×1 | 220سم×1 | 162سم×2 | 160سم×6 | 155سم×2 | 150سم×1 | 140سم×5 | 115سم×4 | 105سم×1
ألواح تلبيس 2.5 سم	641 لوح × 400 سم (مجموع الصفوف 2392.6 م، 42 وجه)
أسمنت بورد 12 مم (122×244)	36 لوح (داخل دورات المياه)
العزل	351 لوح فوم صخري 80
الصبة	يجهزها العميل — 20 سم، مفرغة تحت دورات المياه

مراجعة التصميم مقابل قواعد المصنع

النوع	البند	التفاصيل	المقترح
ملاحظة	بحر المدادات	أطول بحر بدون جدار داخلي يحمل المداد: جهة أ: 342 سم، جهة ب: 342 سم. يحتاج رقم المصنع لأقصى بحر مسموح لتحديد المدادات اللي تُقوّى 20×5.	
ملاحظة	الصبة والدرج	ارتفاع الصبة 45 سم ← 3 درجة بقائمة 15.0 سم.	
ملاحظة	مناسيب رؤوس الفتحات	رؤوس الأبواب والشبابيك على مناسيب مختلفة: 210، 220، 230، 240، 250 سم.	
سؤال	يحتاج تأكيد	أقصى بحر للمداد بدون جدار داخلي قبل إضافة تقوية 5×7 (مداد 20×5)؟	
سؤال	يحتاج تأكيد	التغطية الصافية للوح التلبيس بعد التعشيق (مستنتجة مؤقتاً 18.67 سم من 280/15)؟	
سؤال	يحتاج تأكيد	هل يوضع أعمدة قصيرة فوق رأس الشباك/الباب إلى العلوي؟	
سؤال	يحتاج تأكيد	مكان الوصلة في القاعدة والعلوي إذا الجدار أطول من الطبلية؟	