
جدول مساحات الموقع

البند	المقاس	المساحة (م²)
مساحة الأرض	19.00 × 26.00 م	494.0
مسطح الكوخ (البصمة)	7.00 × 9.00 م	63.0
تراس الكوخ	2.40 × 9.00 م	21.6
جلسة خارجية	4.20 × 7.60 م	31.9
بلاط		77.1
موقف سيارة	4.70 × 11.40 م	53.6
ممر		19.8
المسطحات الخضراء (حديقة)	الباقي	227.0

الموقع العام وتنسيق الحديقة (لاندسكيب)

الأرض 19 × 26 م = 494 م² | الأبعاد بالسنتيمتر

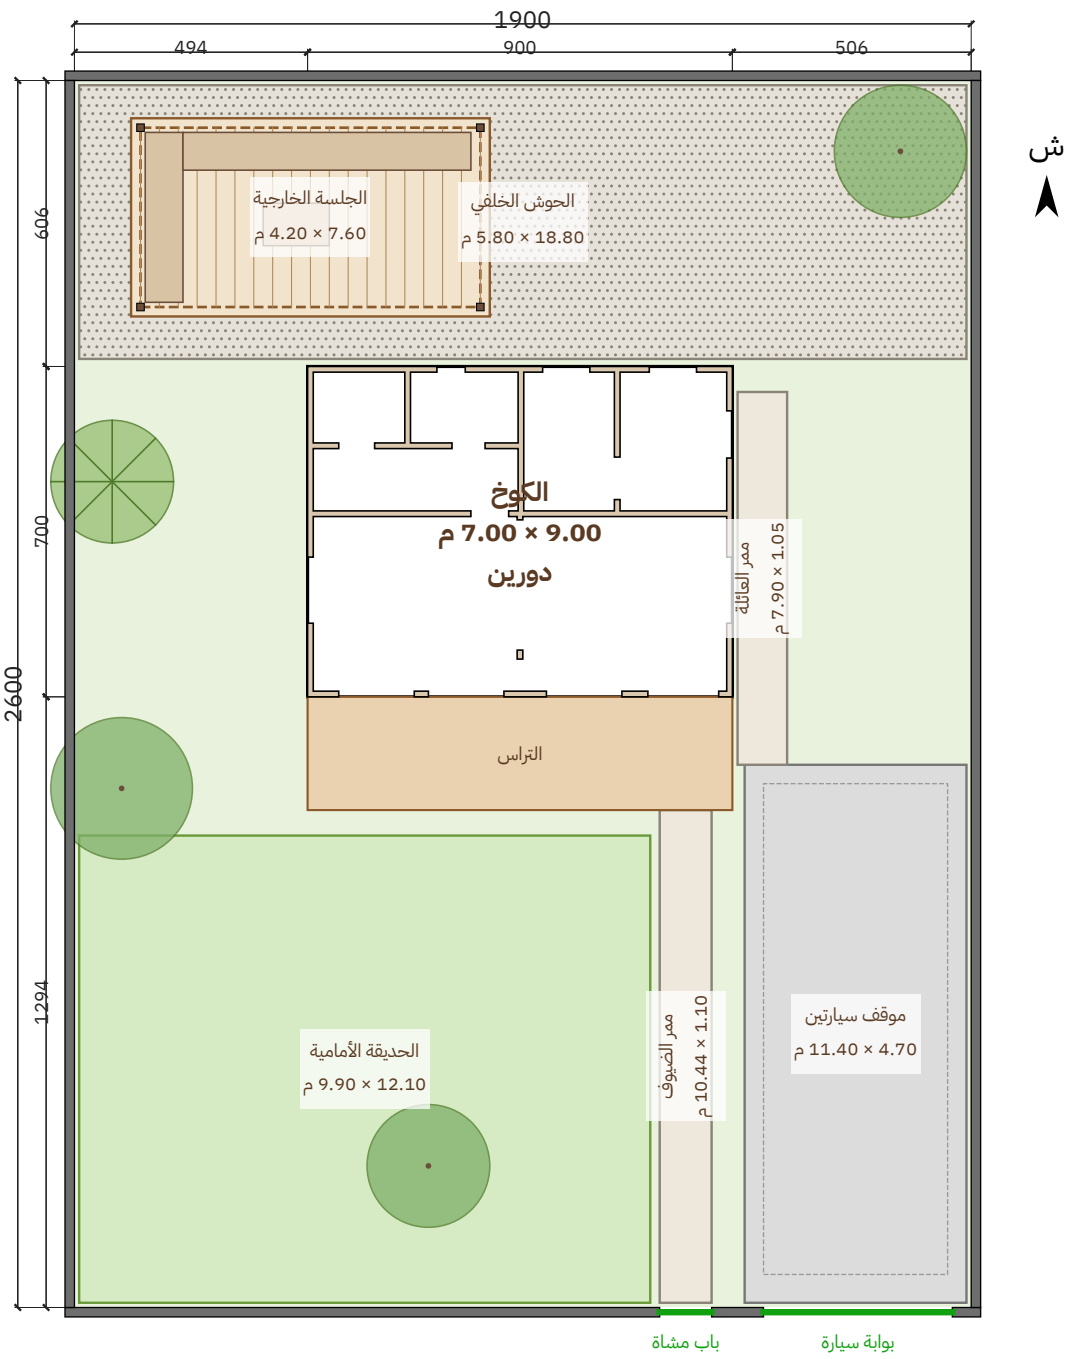


شارع عرض 16 م

المشروع / العميل	عنوان اللوحة	المقياس	التاريخ	رقم اللوحة
فيلا خشب دورين – مجلس + غرفتين – 9.00 × 7.00 م (63 م² للدور) عميل – تبوك	الموقع العام واللاندسكيب	1:200	2026-10-24	A-01 (1/12)

مصنع وتد الأخشاب
Watad Wood Factory

المسقط الأفقي مع الفرش — الدور الأرضي

الأبعاد بالسنتيمتر - الجدران: قوائم 7×5 + تلبيس 2.5 من الجهتين (12 سم) | منسوب الأرضية +0.00

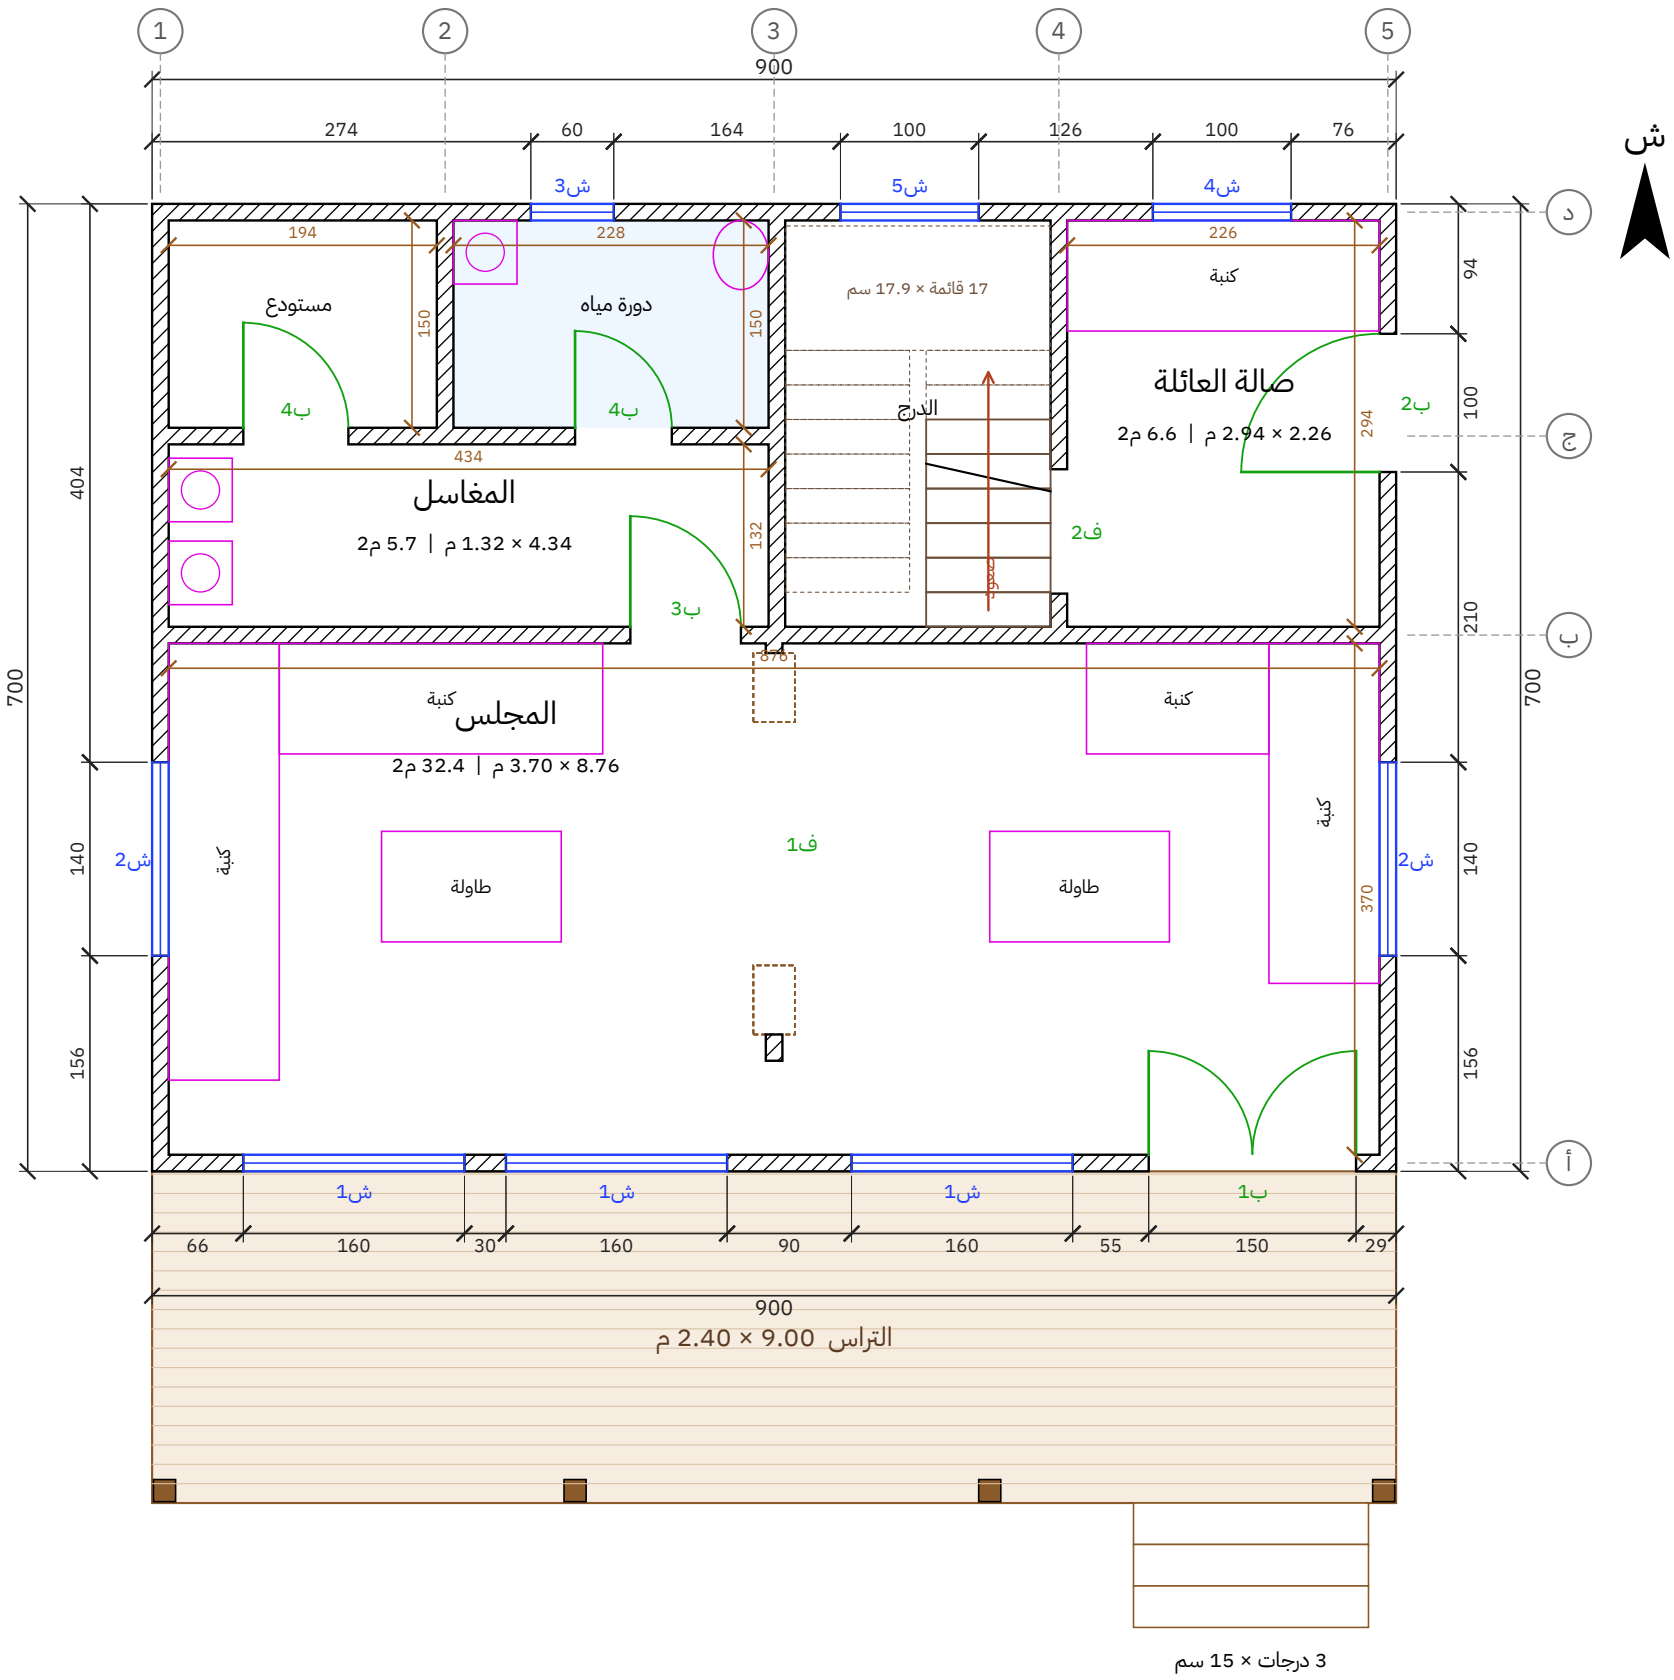


المشروع / العميل	عنوان اللوحة	المقياس	التاريخ	رقم اللوحة
فيلا خشب دورين — مجلس + غرفتين — 9.00 × 7.00 م (63 م² للدور) **عميل — تبوك**	**المسقط الأفقي — الدور الأرضي**	**1:50**	**2026-10-24**	**A-02 (2/12)**


مصنع وتد الأخشاب
Watad Wood Factory

المسقط الأفقي مع الفرش — الدور الأول

الأبعاد بالسنتيمتر - الجدران: قوائم 7×5 + تلبيس 2.5 من الجهتين (12 سم) | منسوب الأرضية +3.05

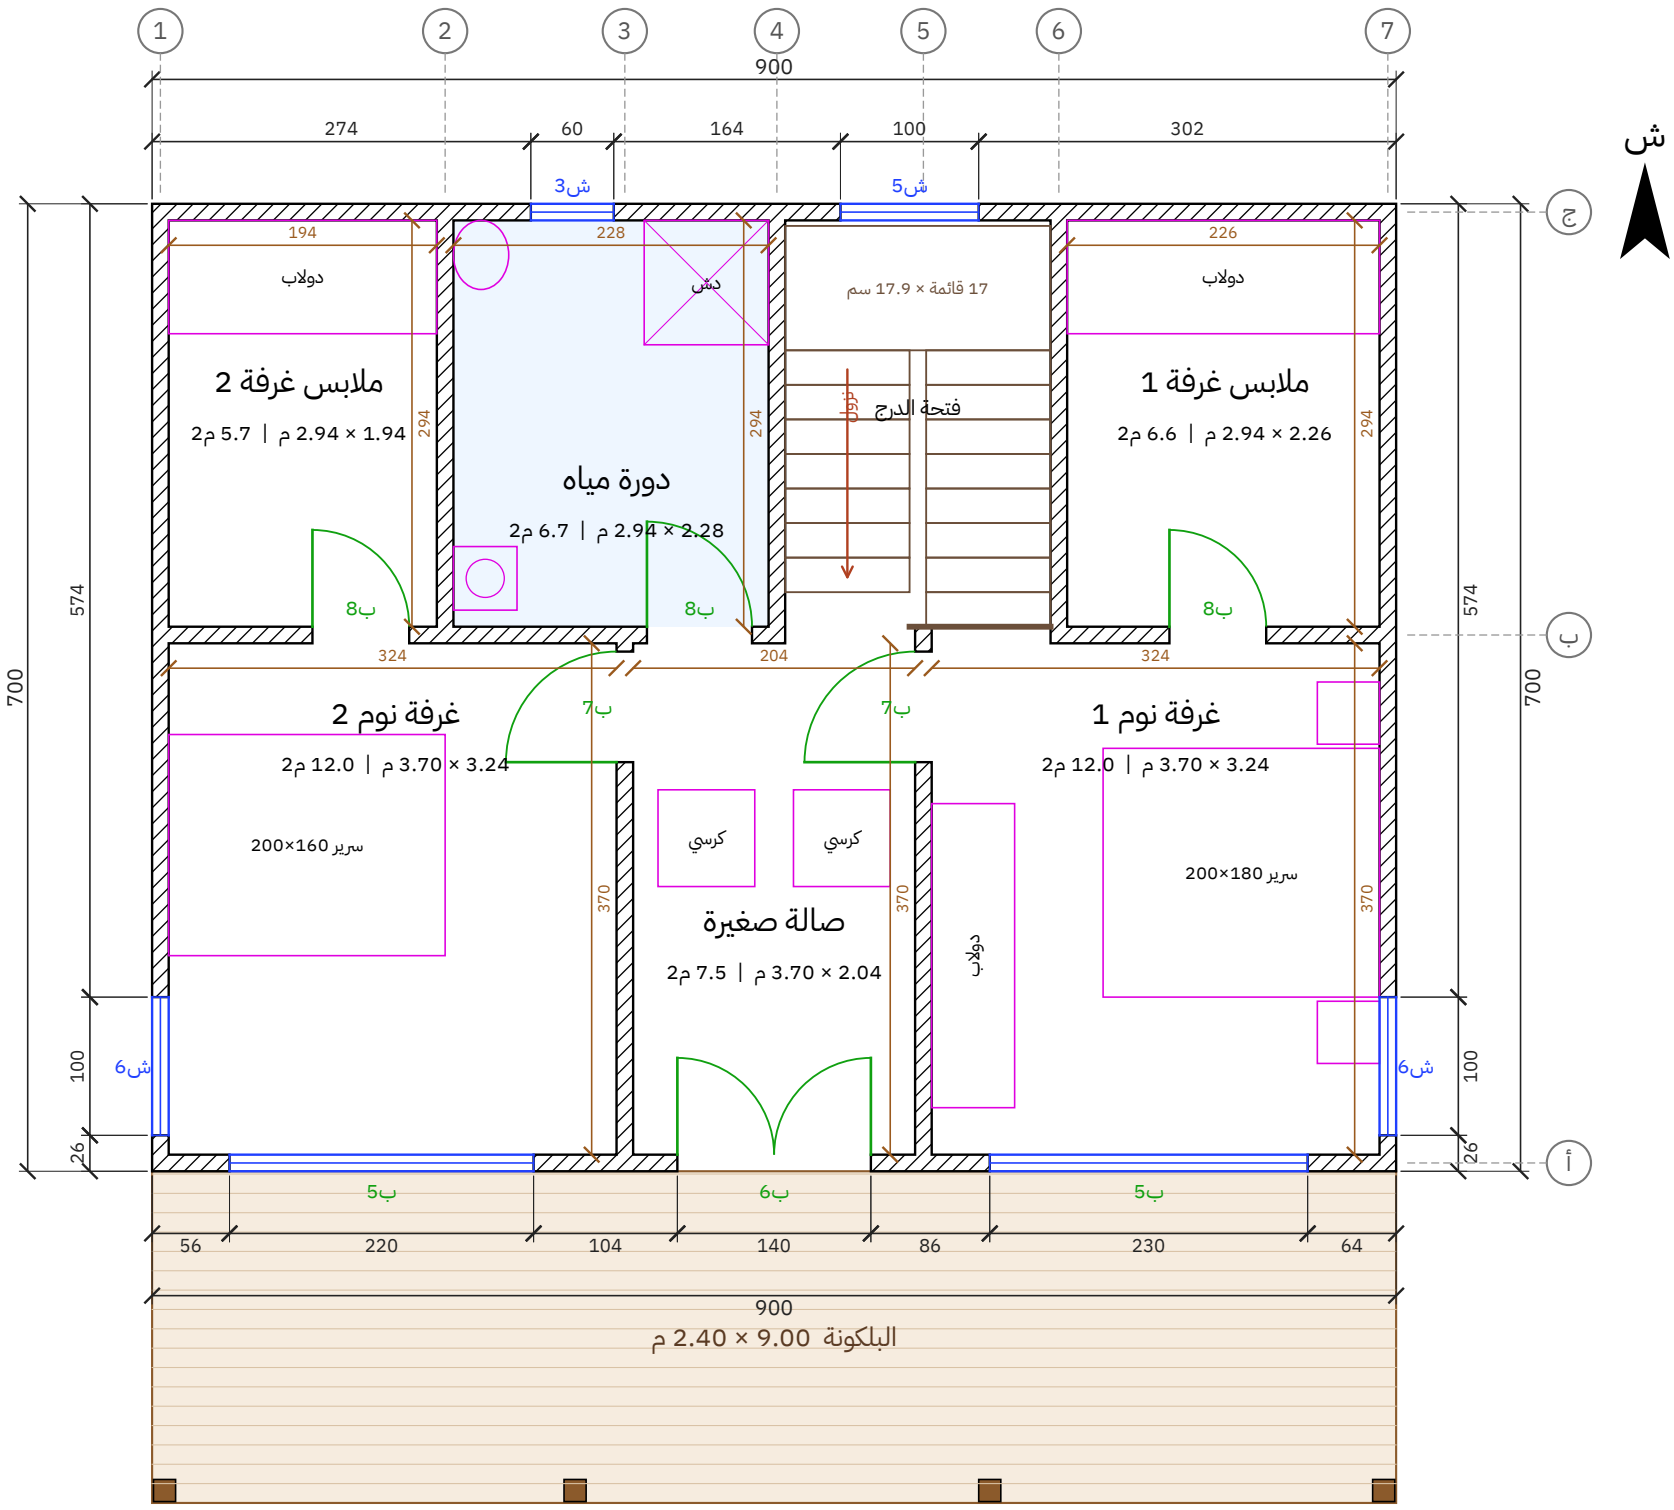


مصنع وتد الأخشاب Watad Wood Factory	المشروع / العميل فيلا خشب دورين — مجلس + غرفتين — 9.00 × 7.00 م (63 م² للدور) عميل — تبوك	عنوان اللوحة المسقط الأفقي — الدور الأول	المقياس 1:50	التاريخ 2026-10-24	رقم اللوحة A-03 (3/12)

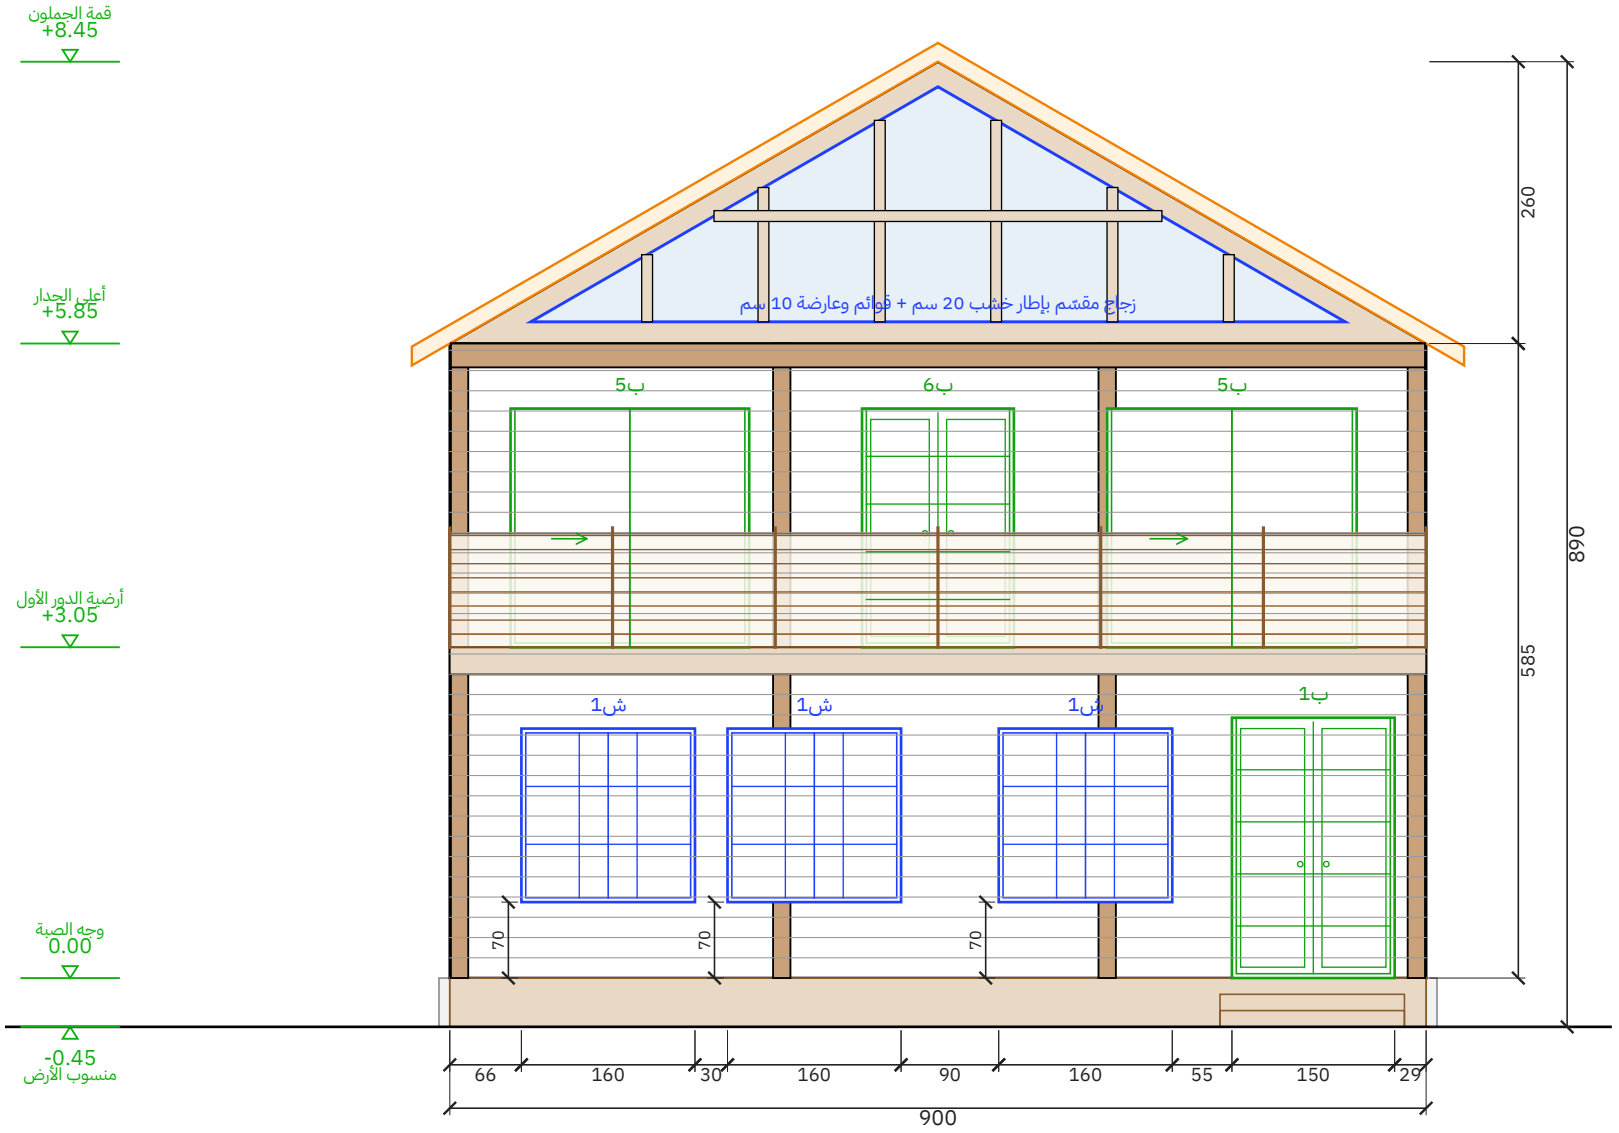

الواجهة الأمامية

مقياس 1:50 | الوحدة: سم

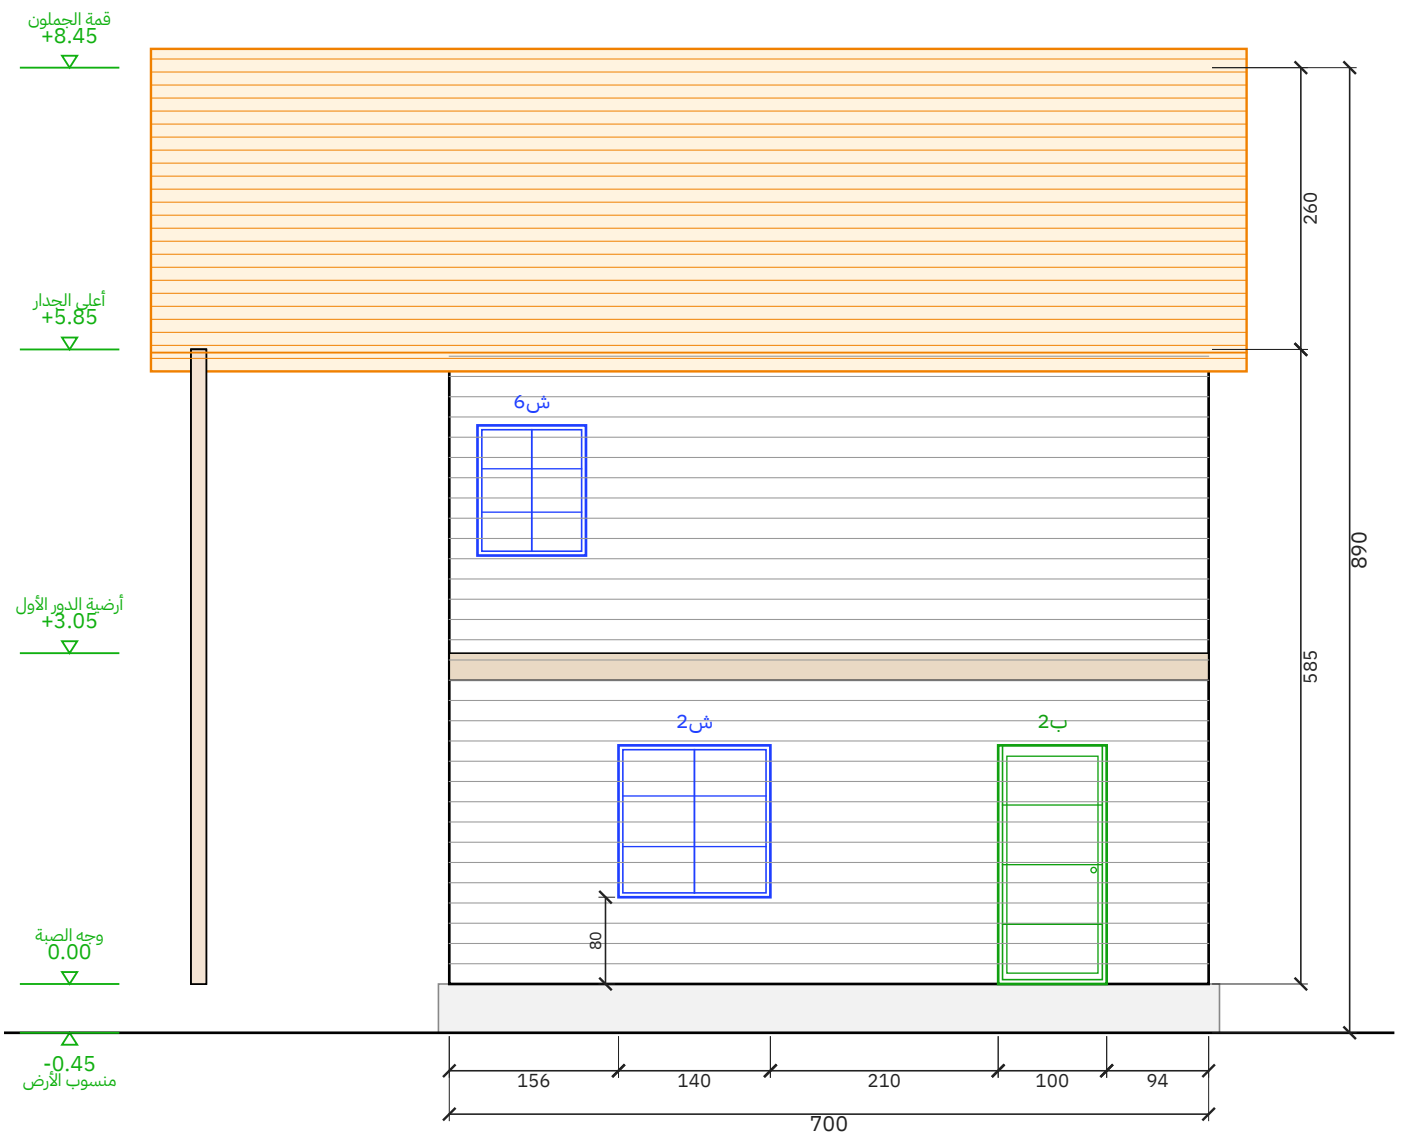


الواجهة الشرقية

مقياس 1:50 | الوحدة: سم


المشروع / العميل	عنوان اللوحة	المقياس	التاريخ	رقم اللوحة
فيلا خشب دورين – مجلس + غرفتين – 9.00 × 7.00 م (63 م² للدور) عميل – تبوك	الواجهة الأمامية والواجهة الشرقية	1:50	2026-10-24	A-04 (4/12)

مصنع وتد الأخشاب
Watad Wood Factory

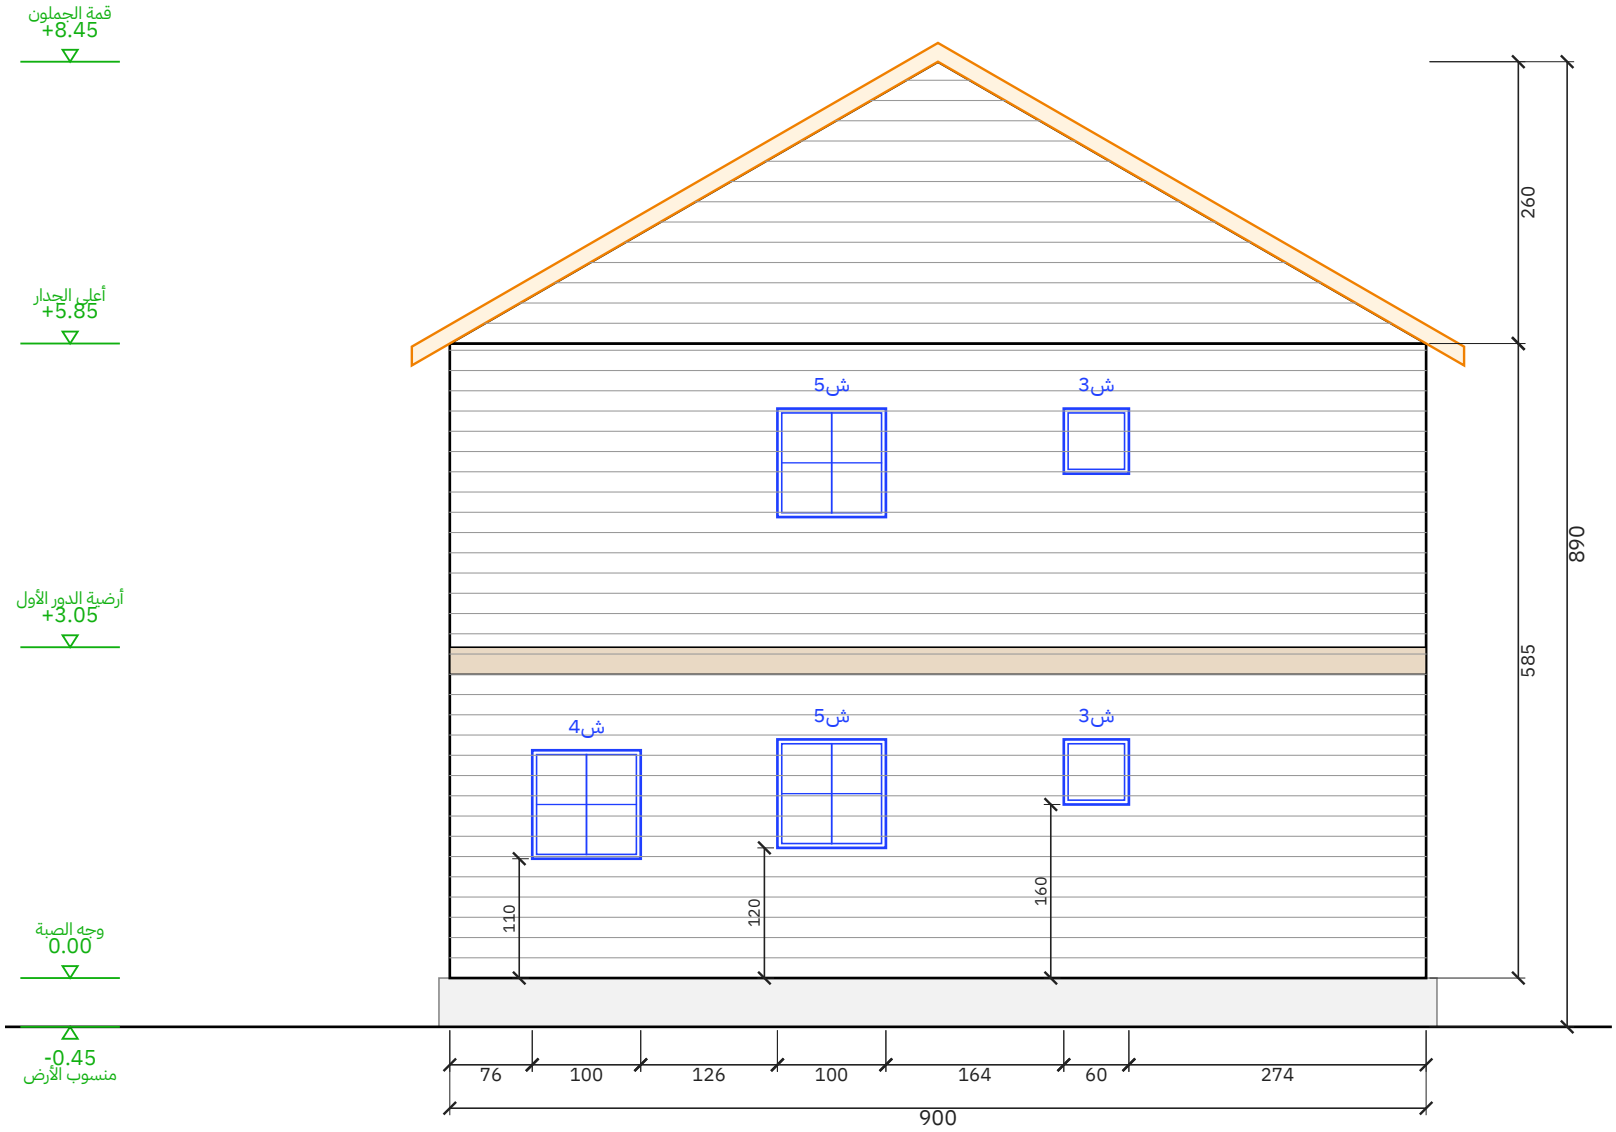

الواجهة الخلفية

مقياس 1:50 | الوحدة: سم

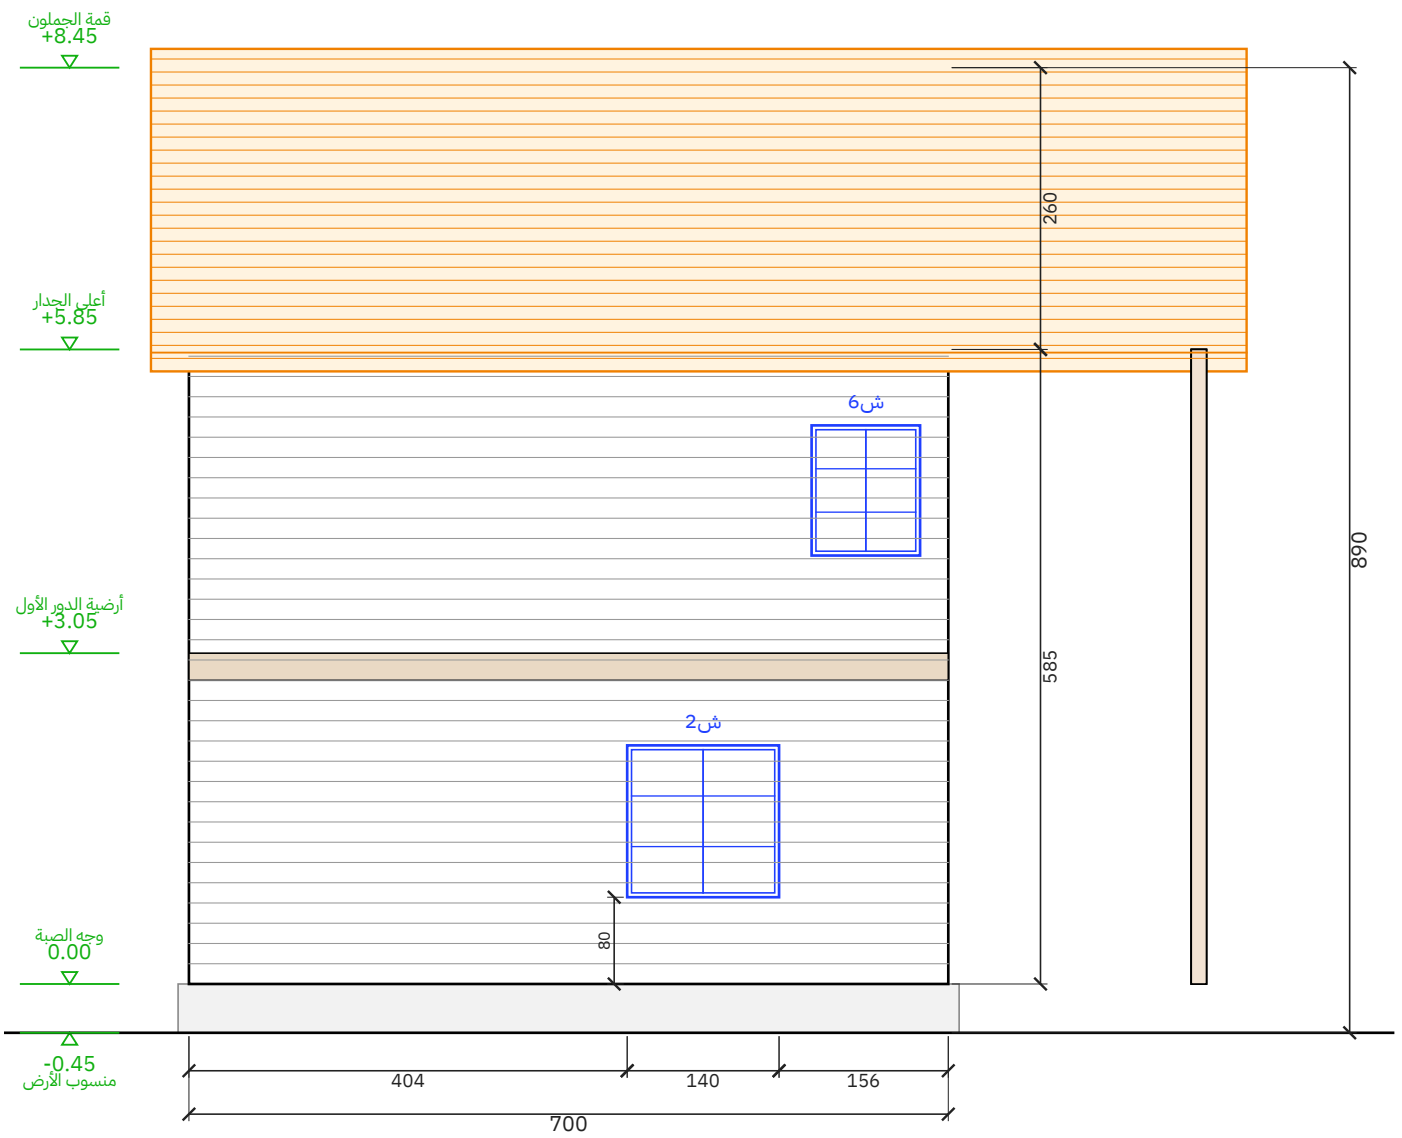

الواجهة الغربية


مقياس 1:50 | الوحدة: سم

المشروع / العميل	عنوان اللوحة	المقياس	التاريخ	رقم اللوحة
فيلا خشب دورين – مجلس + غرفتين – 9.00 × 7.00 م (63 م² للدور) عميل – تبوك	الواجهة الخلفية والواجهة الغربية	1:50	2026-10-24	A-05 (5/12)

مصنع وتد الأخشاب
Watad Wood Factory


مسقط السقف (جملون)

رفرف 35 سم من كل جهة | مقياس 1:50

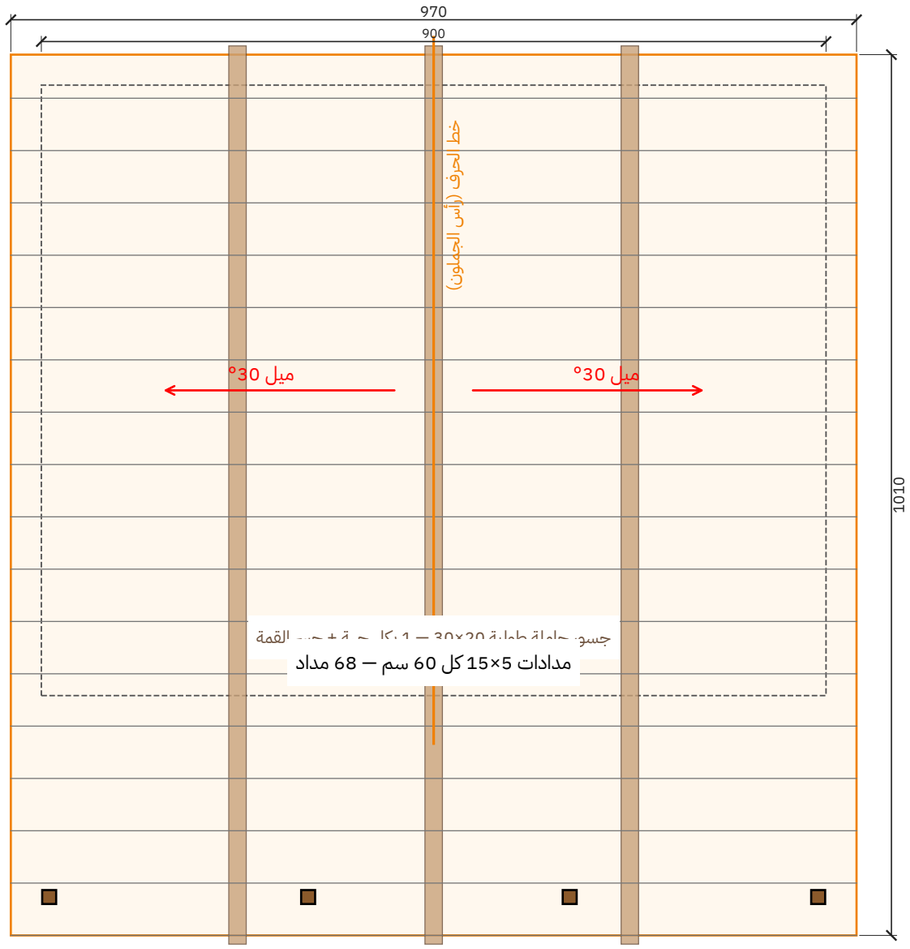


قطاع عرضي أ-أ

مقياس 1:50 | الوحدة: سم

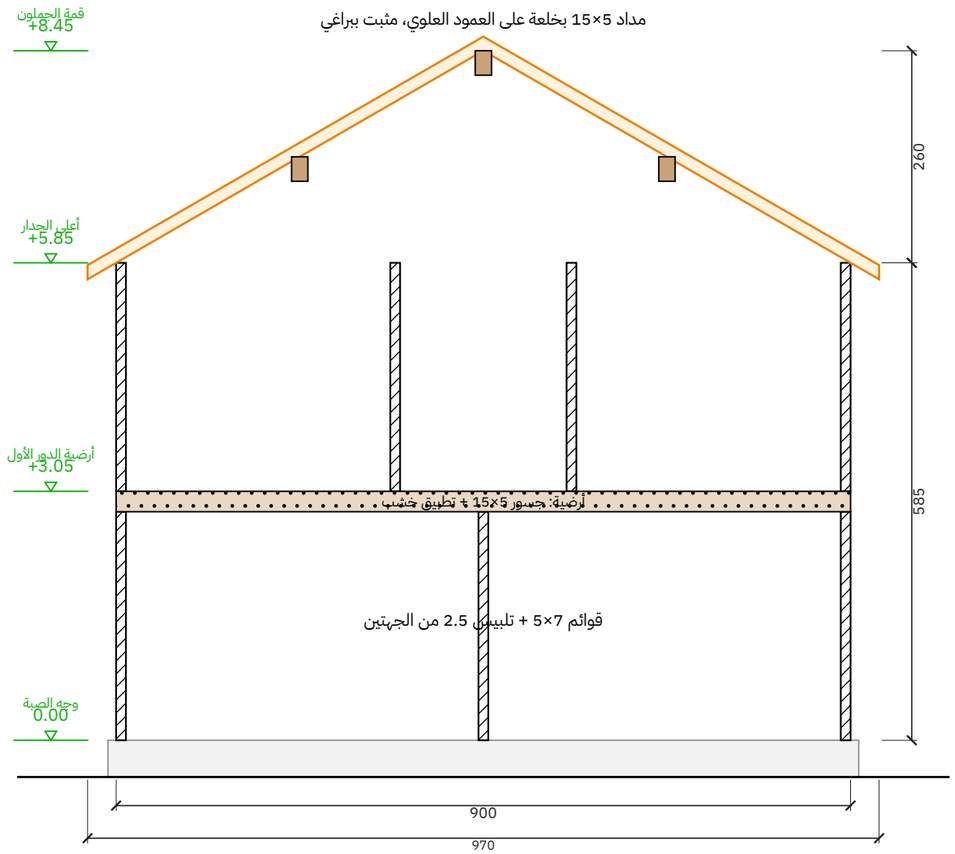

تفصيلة جلوس المداد على العلوي (1:5)

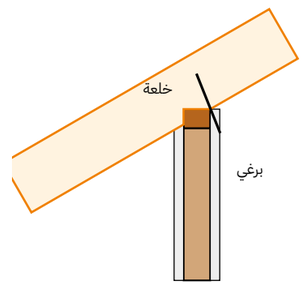

علوي 7×5 على قائم 7×5

المشروع / العميل	عنوان اللوحة	المقياس	التاريخ	رقم اللوحة
فيلا خشب دورين — مجلس + غرفتين — 9.00 × 7.00 م (63 م² للدور) **عميل — تبوك**	**مسقط السقف والقطاع**	**1:50**	**2026-10-24**	**A-06 (6/12)**

مصنع وتد الأخشاب
Watad Wood Factory

جدول مقاسات الأبواب والشبابيك

مقاس الفتحة الصافي في الجدار - الوحدة: سم

الرمز	النوع	العرض (سم)	الارتفاع (سم)	ارتفاع الجلسة (سم)	العدد	الموقع
ب1	باب مزدوج	150	240	-	1	الأمامية
ب2	باب	100	220	-	1	الشرقية
ب3	باب	80	220	-	1	المجلس — المغاسل
ب4	باب	76	210	-	1	المستودع
ب4	باب	70	210	-	1	دورة المياه
ب5	باب مزدوج	220	220	-	1	الأمامية (على البلكونة)
ب5	باب مزدوج	230	220	-	1	الأمامية (على البلكونة)
ب6	باب مزدوج	140	220	-	1	الأمامية (على البلكونة)
ب7	باب	80	210	-	2	غرفة 2 - غرفة 1
ب8	باب	70	210	-	2	ملابس غرفة 2 - ملابس غرفة 1
ب8	باب	76	210	-	1	دورة المياه
ف1	باب	276	250	-	1	بارتشن مفتوح بعمودين مكتبة
ف2	باب	90	220	-	1	صالة العائلة — الدرج
ش1	شباك	160	160	70	3	الأمامية 3
ش2	شباك	140	140	80	2	الشرقية - الغربية
ش3	شباك	60	60	160	2	الخلفية 2
ش4	شباك	100	100	110	1	الخلفية
ش5	شباك	100	100	120	2	الخلفية 2
ش6	شباك	100	120	90	2	الشرقية - الغربية

الإجمالي: أبواب 15 - شبابيك 12

جدول المساحات وبيانات المشروع والتسعير

بيانات المشروع

البند	البيان
المشروع	فيلا خشب دورين — مجلس + غرفتين — 9.00 × 7.00 م (63 م² للدور)
العميل	عميل — تبوك
الموقع	تبوك
الاستخدام	سكن — مجلس ضيوف + غرفتين
التاريخ	2026-10-24
نظام البناء	هيكل خشب 5×7 + تلبيس 2.5 سم من الجهتين
السقف	جملون 30° — قرميد معدني

جدول المساحات

م	الفراغ	الأبعاد (م)	المساحة (م2)
1	أرضي — المجلس	8.76 × 3.70	32.41
2	أرضي — المغاسل	4.34 × 1.32	5.73
3	أرضي — مستودع	1.94 × 1.50	2.91
4	أرضي — دورة مياه	2.28 × 1.50	3.42
5	أرضي — الدرج	1.92 × 2.94	5.64
6	أرضي — صالة العائلة	2.26 × 2.94	6.64
7	أول — غرفة نوم 2	3.24 × 3.70	11.99
8	أول — صالة صغيرة	2.04 × 3.70	7.55
9	أول — غرفة نوم 1	3.24 × 3.70	11.99
10	أول — ملابس غرفة 2	1.94 × 2.94	5.70
11	أول — دورة مياه	2.28 × 2.94	6.70
12	أول — ملابس غرفة 1	2.26 × 2.94	6.64
	المساحة الصافية الداخلية		107.34
	التراس	**9.00 × 2.40**	**21.60**
	البلكونة	**9.00 × 2.40**	**21.60**
	المساحة الإجمالية المبنية	**9.00 × 7.00 × 2 دور**	**126.00**
	المساحة الكلية (المبنية + التراس والبلكونة)		**169.20**

التسعير المفصّل

البند	المبلغ (ريال)
الكوخ المبني 126.00 م² × 1,096	138,096
تراس الأرضي + بلكونة الأول (9.00 × 2.40 × 2) — 43.20 م² × 1,096	47,347
الإجمالي (ريال)	**185,443**

ملاحظات:


- السعر للدورين والتراس والبلكونة حسب المخطط المعتمد — التراس يُسعّر بنفس سعر متر الكوخ.
- الصبة والتمديدات الخارجية على العميل ما لم يُذكر غير ذلك.

لقطات المنظور الخارجي


المنظور الأمامي




منظور أمامي من اليسار

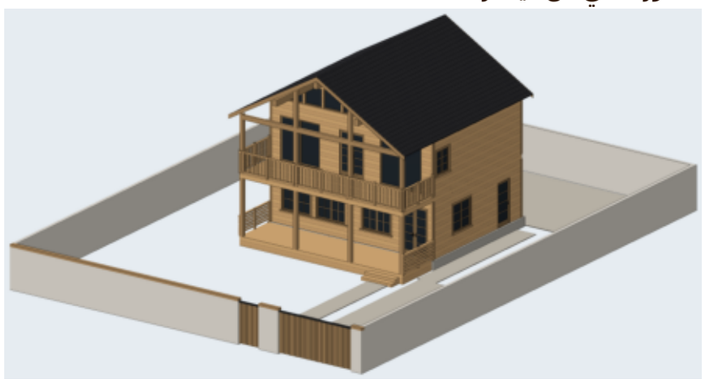


منظور أمامي من اليمين

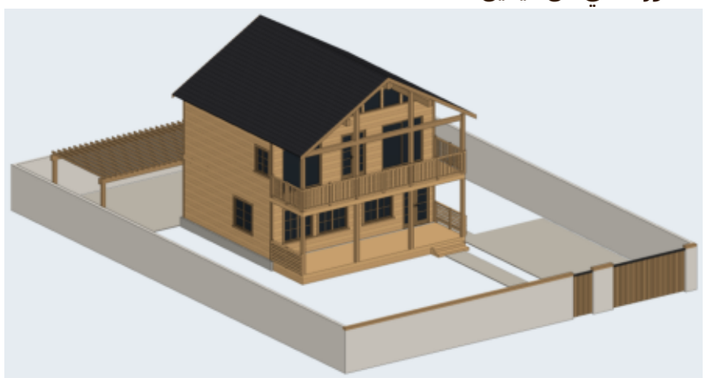


المنظور الخلفي

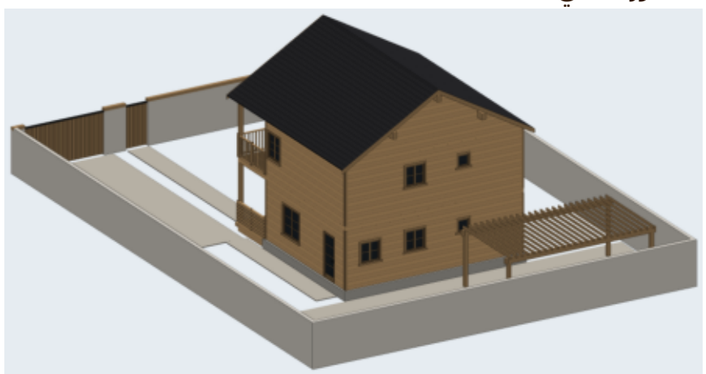

منظور خلفي من اليمين

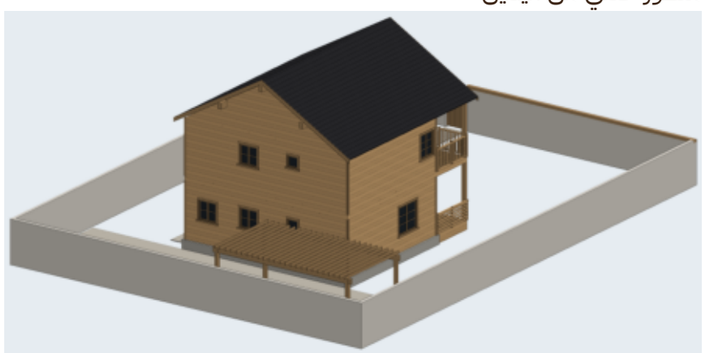


منظر علوي

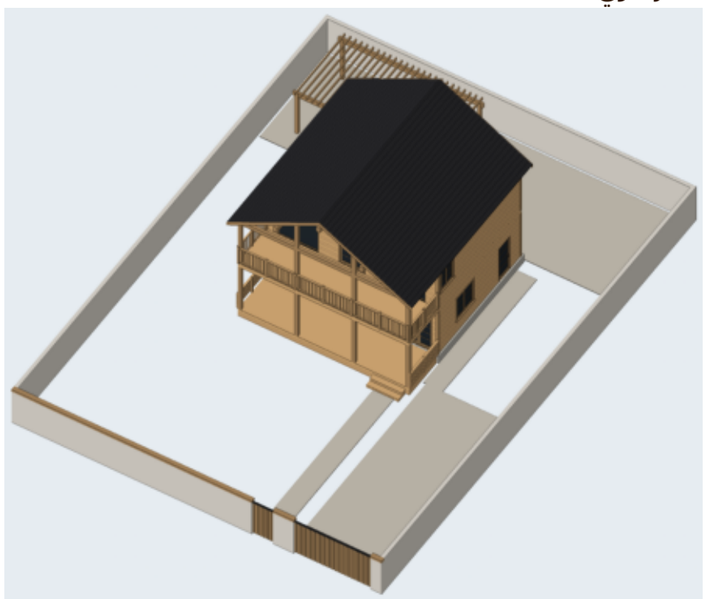

المشروع / العميل	عنوان اللوحة	المقياس	التاريخ	رقم اللوحة
مصنع وتد الأخشاب Watad Wood Factory **فيلا خشب دورين – مجلس + غرفتين – 9.00 × 7.00 م (63 م² للدور)** **عميل – تبوك**	**لقطات المنظور**	–	**2026-10-24**	**A-09 (9/12)**

المقطع العلوي بالفرش — الدور الأرضي


مقطع أفقي على ارتفاع 1.90 م — توزيع الفرش ومسار الحركة

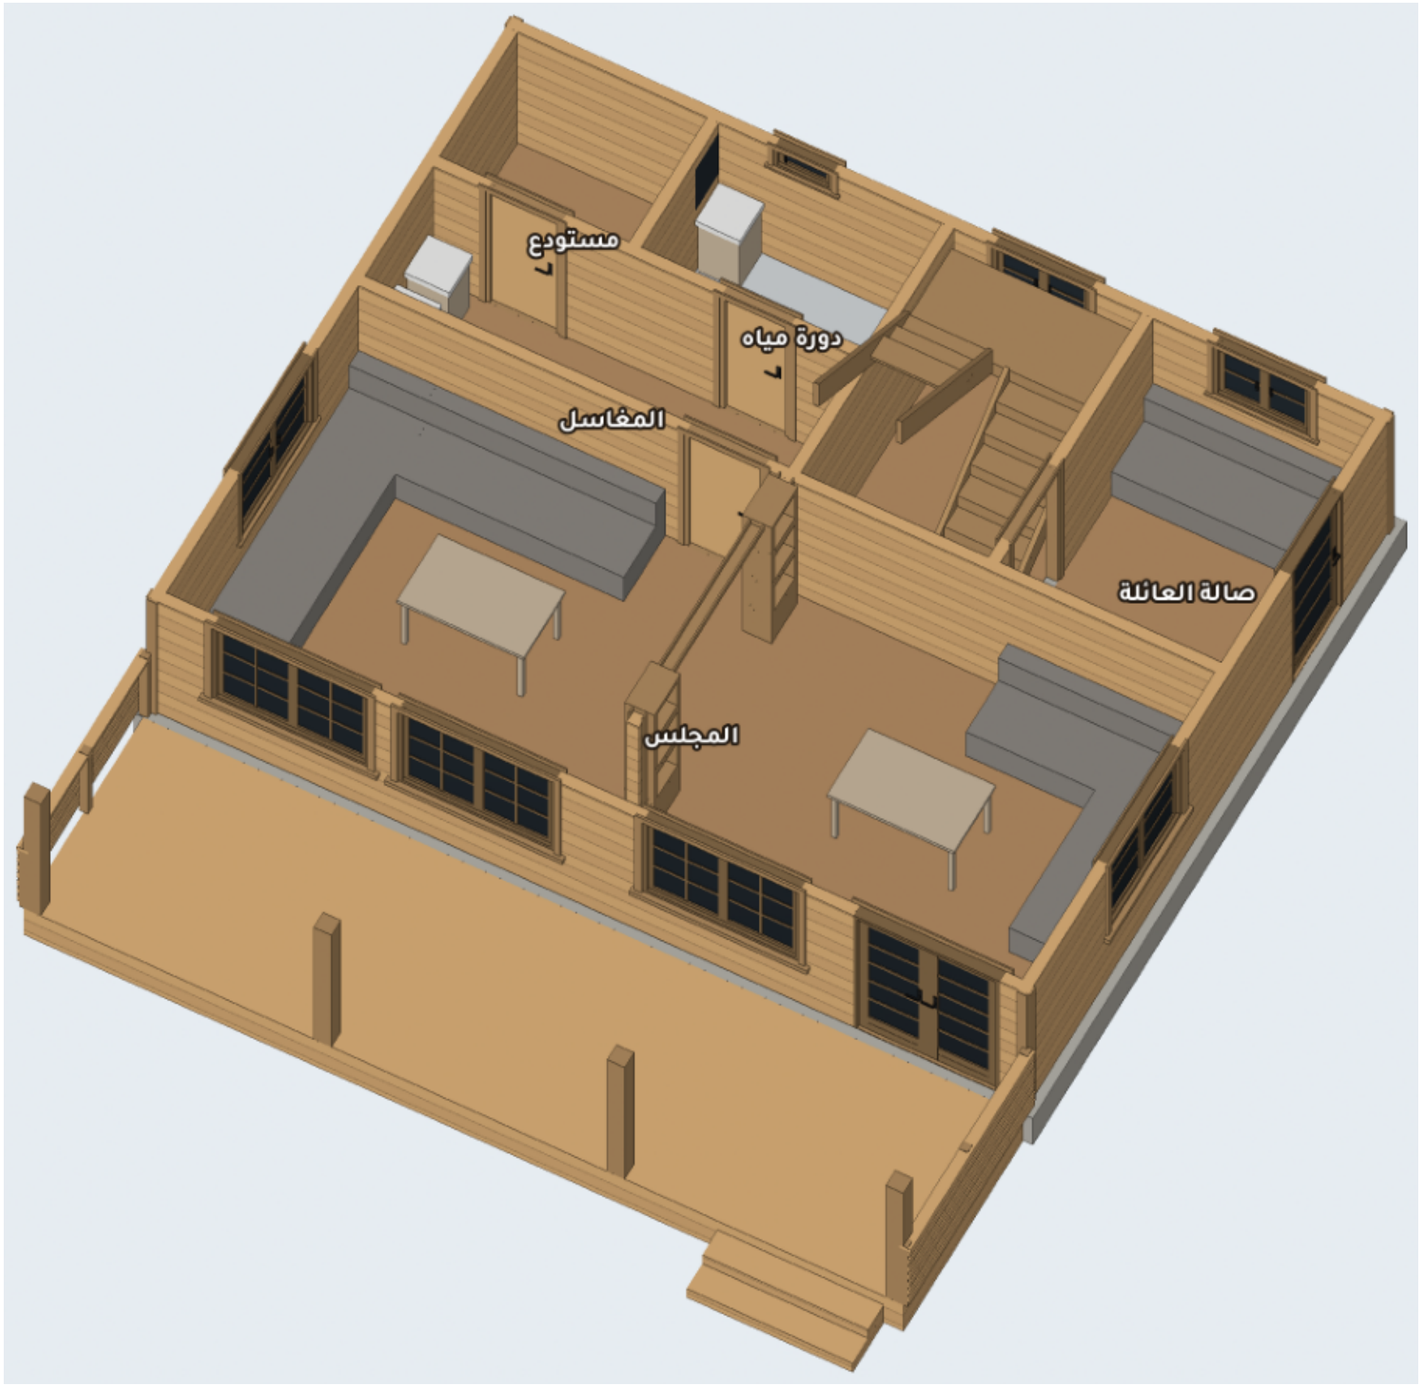

مصنع وتد الأخشاب Watad Wood Factory	المشروع / العميل فيلا خشب دورين — مجلس + غرفتين — 9.00 × 7.00 م (63 م² للدور) عميل — تبوك	عنوان اللوحة المقطع العلوي بالفرش — الدور الأرضي	المقياس —	التاريخ 2026-10-24	رقم اللوحة A-10 (10/12)

المقطع العلوي بالفرش — الدور الأول

مقطع أفقي على ارتفاع 1.90 م — توزيع الفرش ومسار الحركة

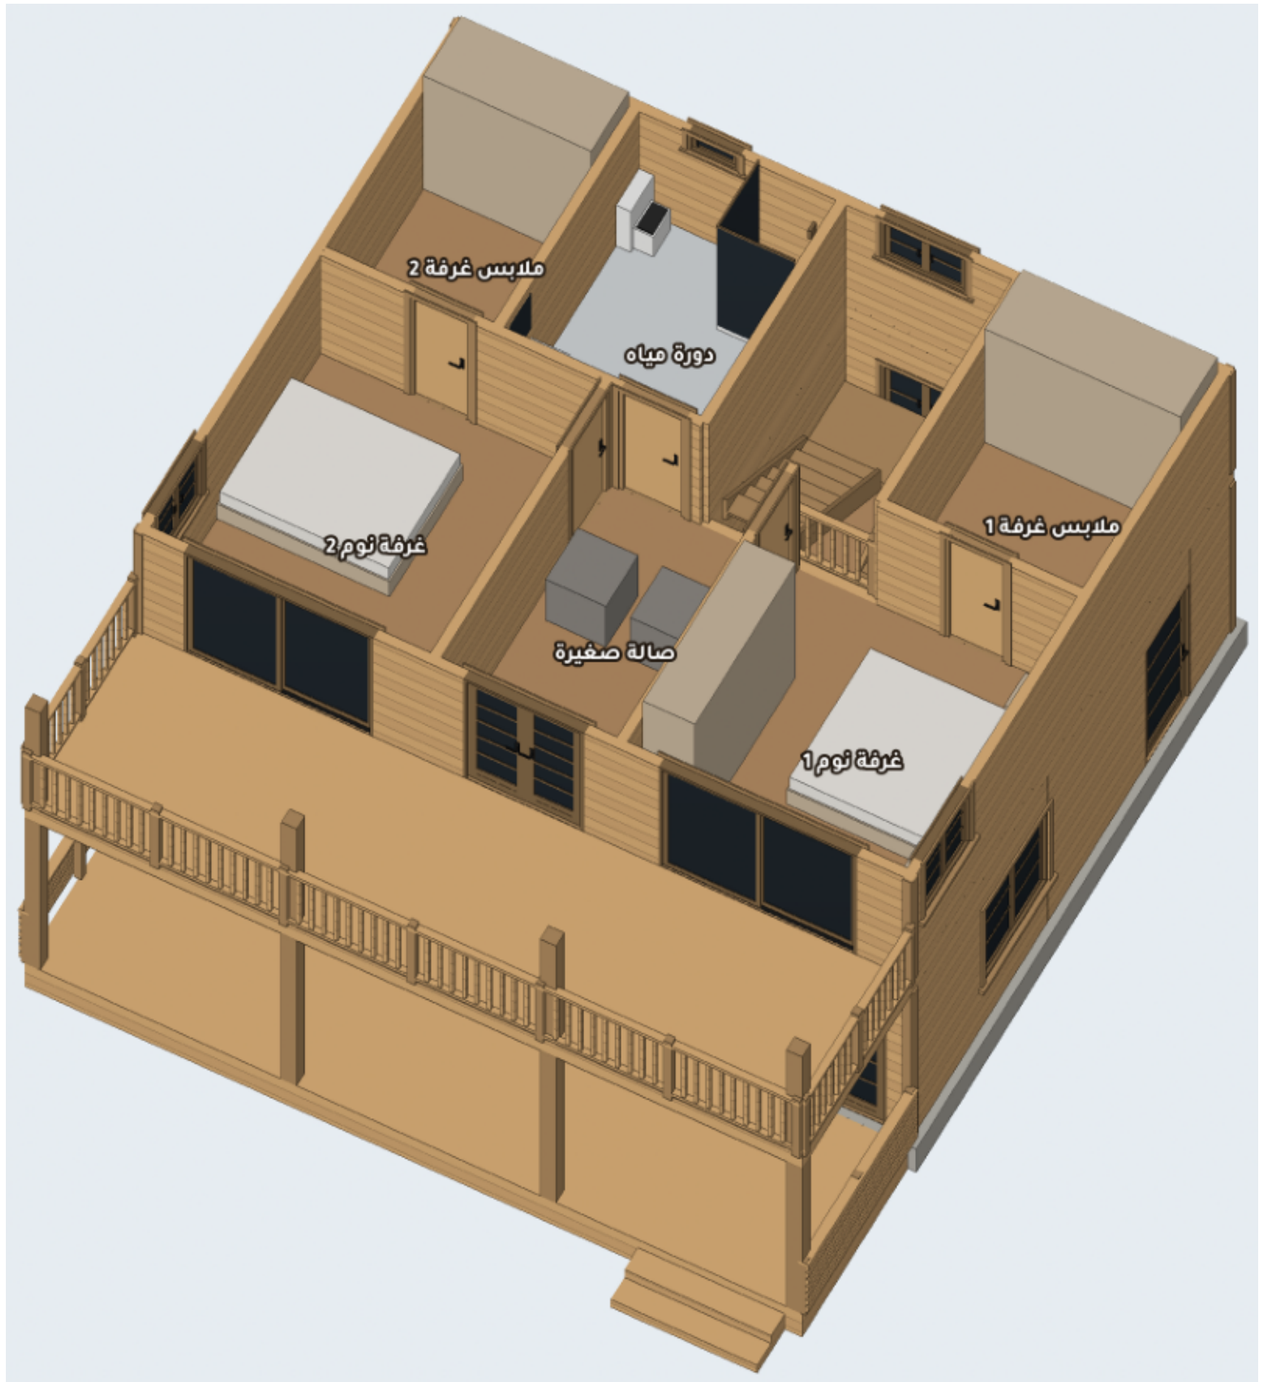

مصنع وتد الأخشاب Watad Wood Factory	المشروع / العميل فيلا خشب دورين — مجلس + غرفتين — 9.00 × 7.00 م (63 م² للدور) عميل — تبوك	عنوان اللوحة المقطع العلوي بالفرش — الدور الأول	المقياس —	التاريخ 2026-10-24	رقم اللوحة A-11 (11/12)

المنظور ثلاثي الأبعاد والمواد

النمط: جوزي غامق + إطارات سوداء — رندر واقعي بخامات حقيقية



جدول المواد والألوان

الخشب / الصبغة

خشب طبيعي فاتح (بدون صبغة)

القرميد

قرميد رمادي غامق

الزجاج

زجاج عاكس غامق

إطارات الشبابيك والأبواب

إطار خشب بنفس الصبغة أغمق

الكنار والزوايا

نفس الصبغة أغمق درجة


الصبة

خرسانة 45 سم


الدربزين: ألواح أفقية متقاربة (عصري)

تقسيم الشبابيك: بدون | الباب الرئيسي: زجاج بتقسيمات (فرنسي)

أنواع الدربزين المعتمدة (من مشاريع المصنع)

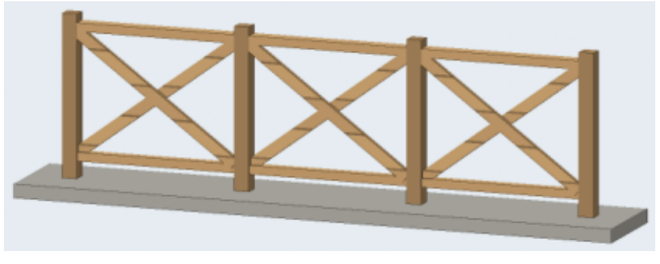

تقاطع X (صورة 5)

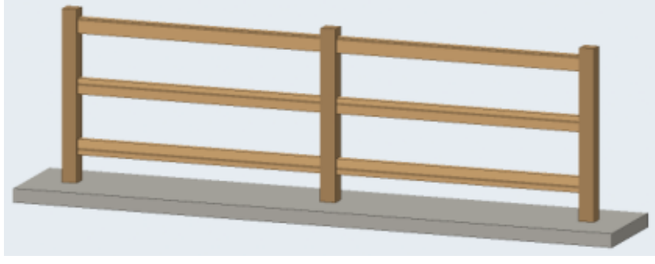

3 مرابيع أفقية (صورة 2)



قوائم رأسية متقاربة (صورة 1)

المشروع / العميل	عنوان اللوحة	المقياس	التاريخ	رقم اللوحة
مصنع وتد الأخشاب Watad Wood Factory **فيلا خشب دورين — مجلس + غرفتين — 9.00 × 7.00 م (63 م² للدور)** **عميل — تبوك**	**المنظور والمواد**	**—**	**2026-10-24**	**A-12 (12/12)**