


## المنظور ثلاثي الأبعاد والمواد

النمط: جوزي غامق + إطارات سوداء — معاينة تقريبية، الإخراج النهائي من 3ds Max

### جدول المواد والألوان

 

#### الخشب / الصبغة

خشب طبيعي فاتح (بدون صبغة)



#### القرميد

قرميد رمادي غامق



#### الزجاج

زجاج عاكس غامق



#### إطارات الشبابيك والأبواب

إطار ألومنيوم أسود



#### الكنار والزوايا

نفس الصبغة أعمق درجة



#### الصبة

خرسانة 45 سم


الدريزين: ألواح أفقية متقاربة (عصري)

تقسيم الشبابيك: بدون | الباب الرئيسي: سحب زجاج


### أنواع الدريزين المعتمدة (من مشاريع المصنع)



قوائم رأسية متقاربة (صورة 1)

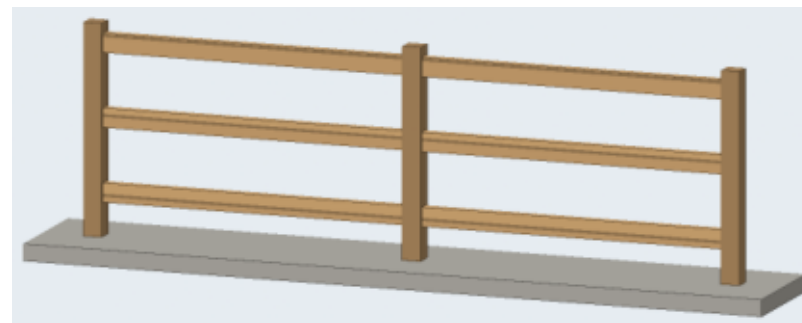

3 مربيع أفقية (صورة 2)

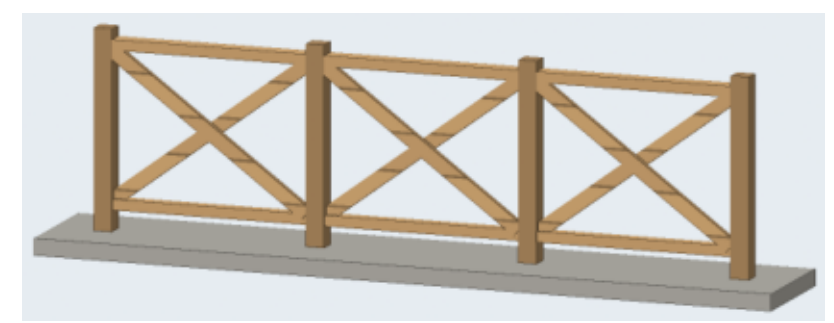

تقاطع X (صورة 5)

رقم اللوحة

W-01 (1/12)

التاريخ

2026-09-29

المقياس

1:50

عنوان اللوحة

المنظور والمواد

المشروع / العميل


كوخ غرفة وتراس 5x7 شامل التراس  
عميل — تصميم حسب الصورة

مصنع وتد الأخشاب

Watad Wood Factory




المسقط الأفقي مع الفرش  
الأبعاد بالسنتيمتر - الجدران: قوائم 5×7 + تليس 2.5 من الجهتين (12 سم)

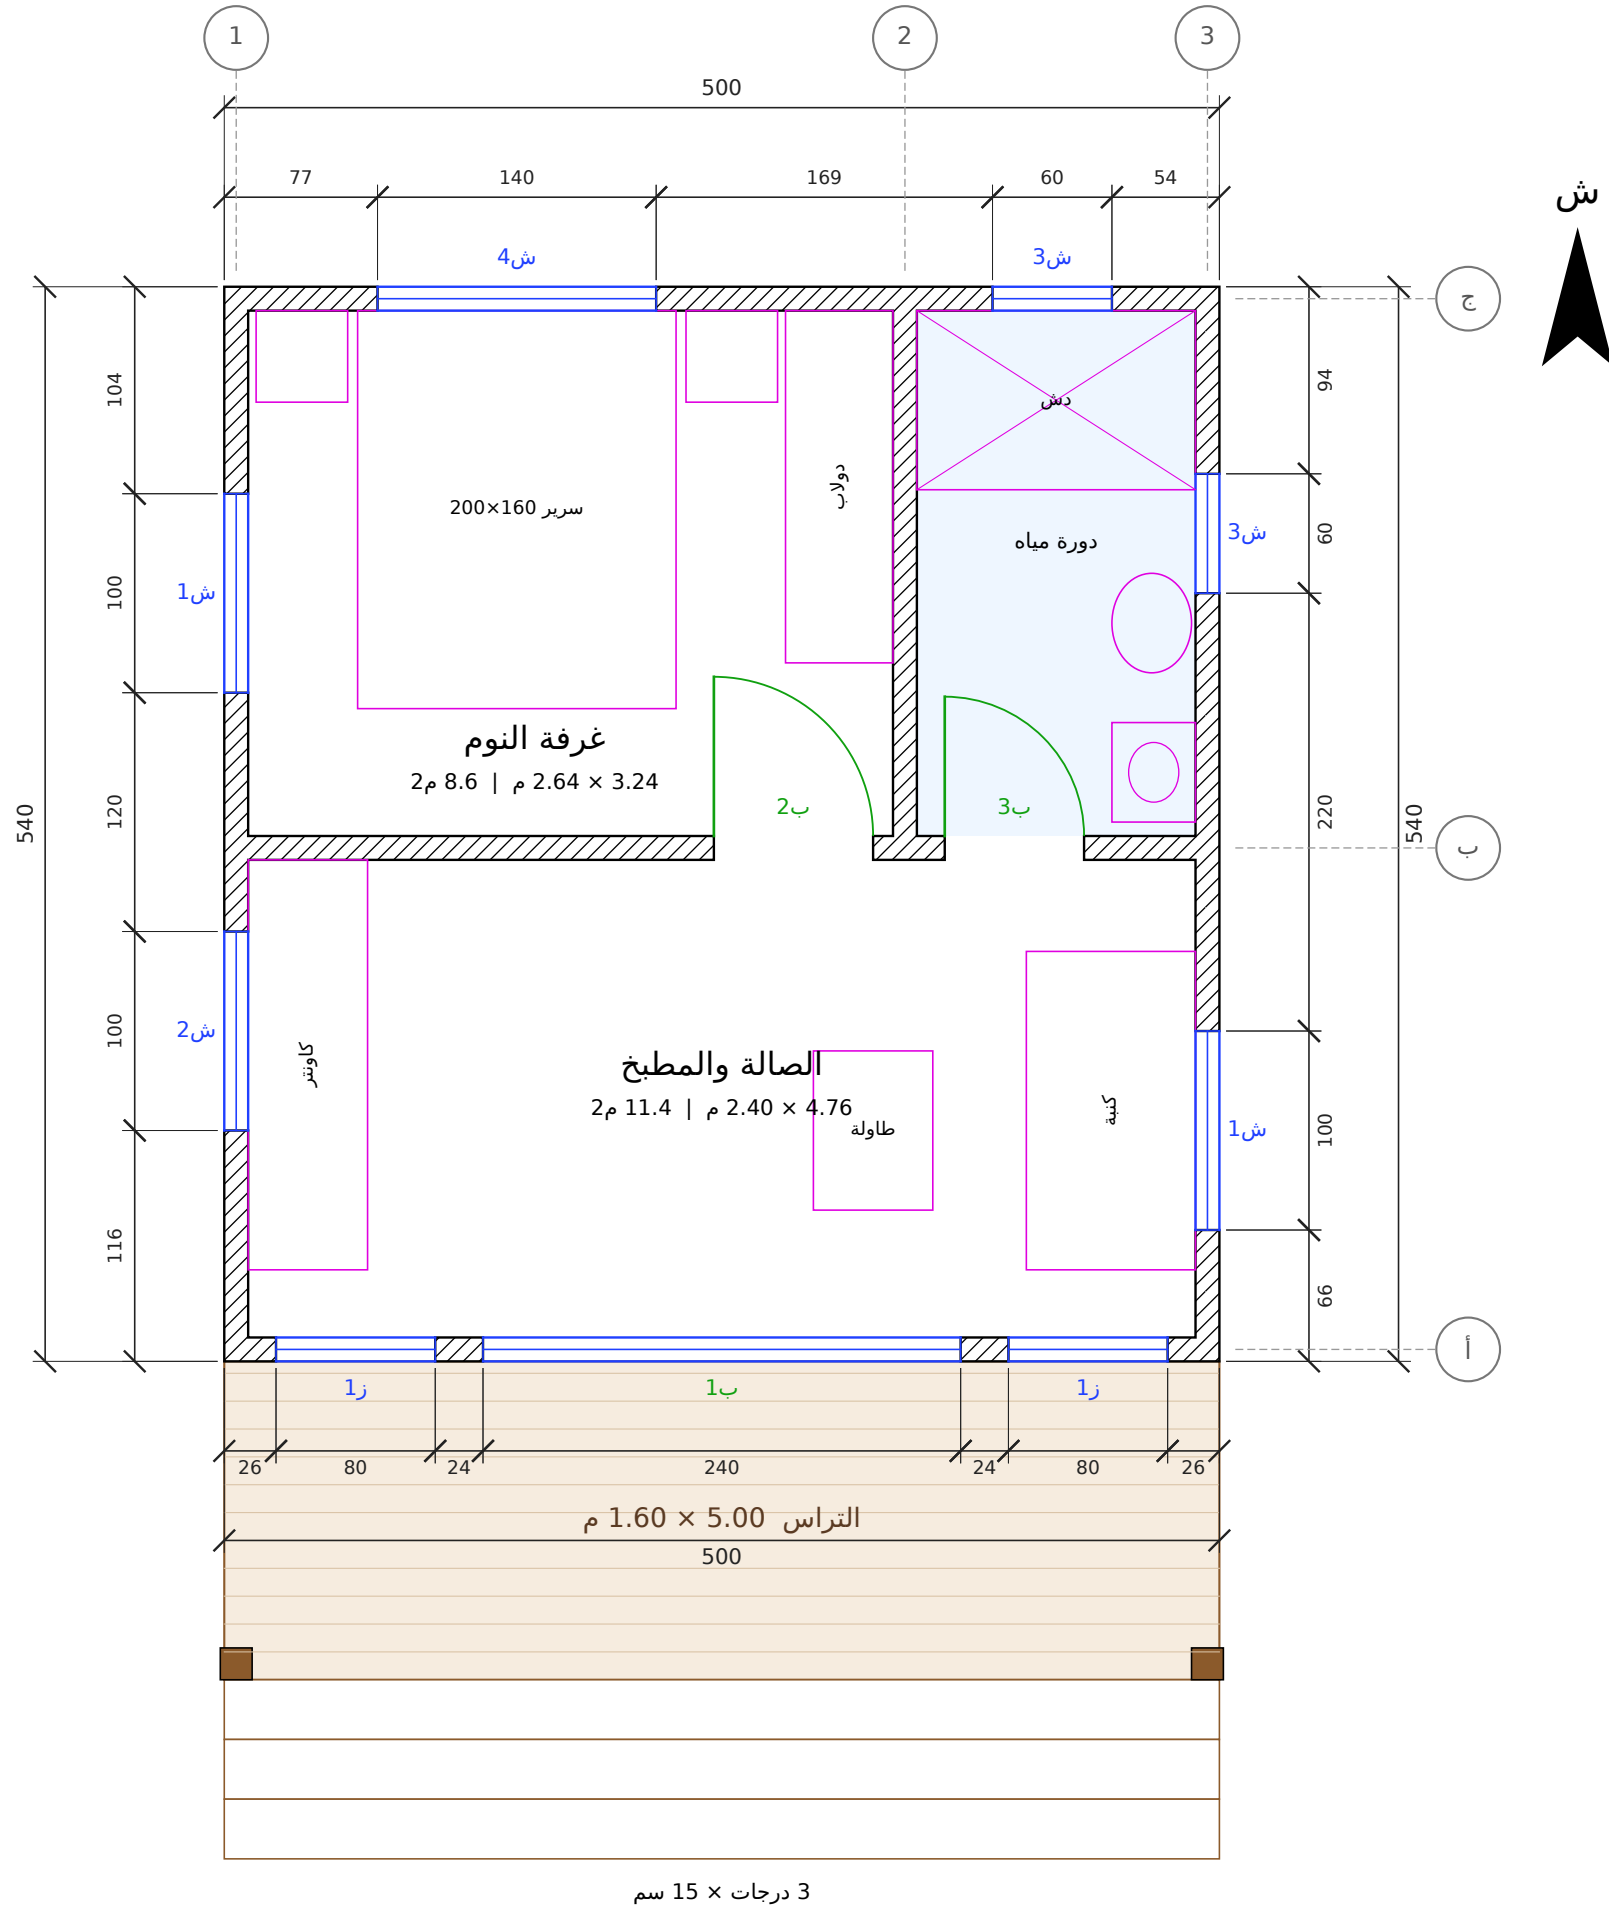


3 درجات × 15 سم

| رقم اللوحة  | التاريخ    | المقياس | عنوان اللوحة  | المشروع / العميل                                          | مصنع وتد الأخشاب<br>Watad Wood Factory |
|-------------|------------|---------|---------------|-----------------------------------------------------------|----------------------------------------|
| W-02 (2/12) | 2026-09-29 | 1:50    | المسقط الأفقي | كوخ غرفة وتراس 7×5 شامل التراس<br>عميل - تصميم حسب الصورة |                                        |

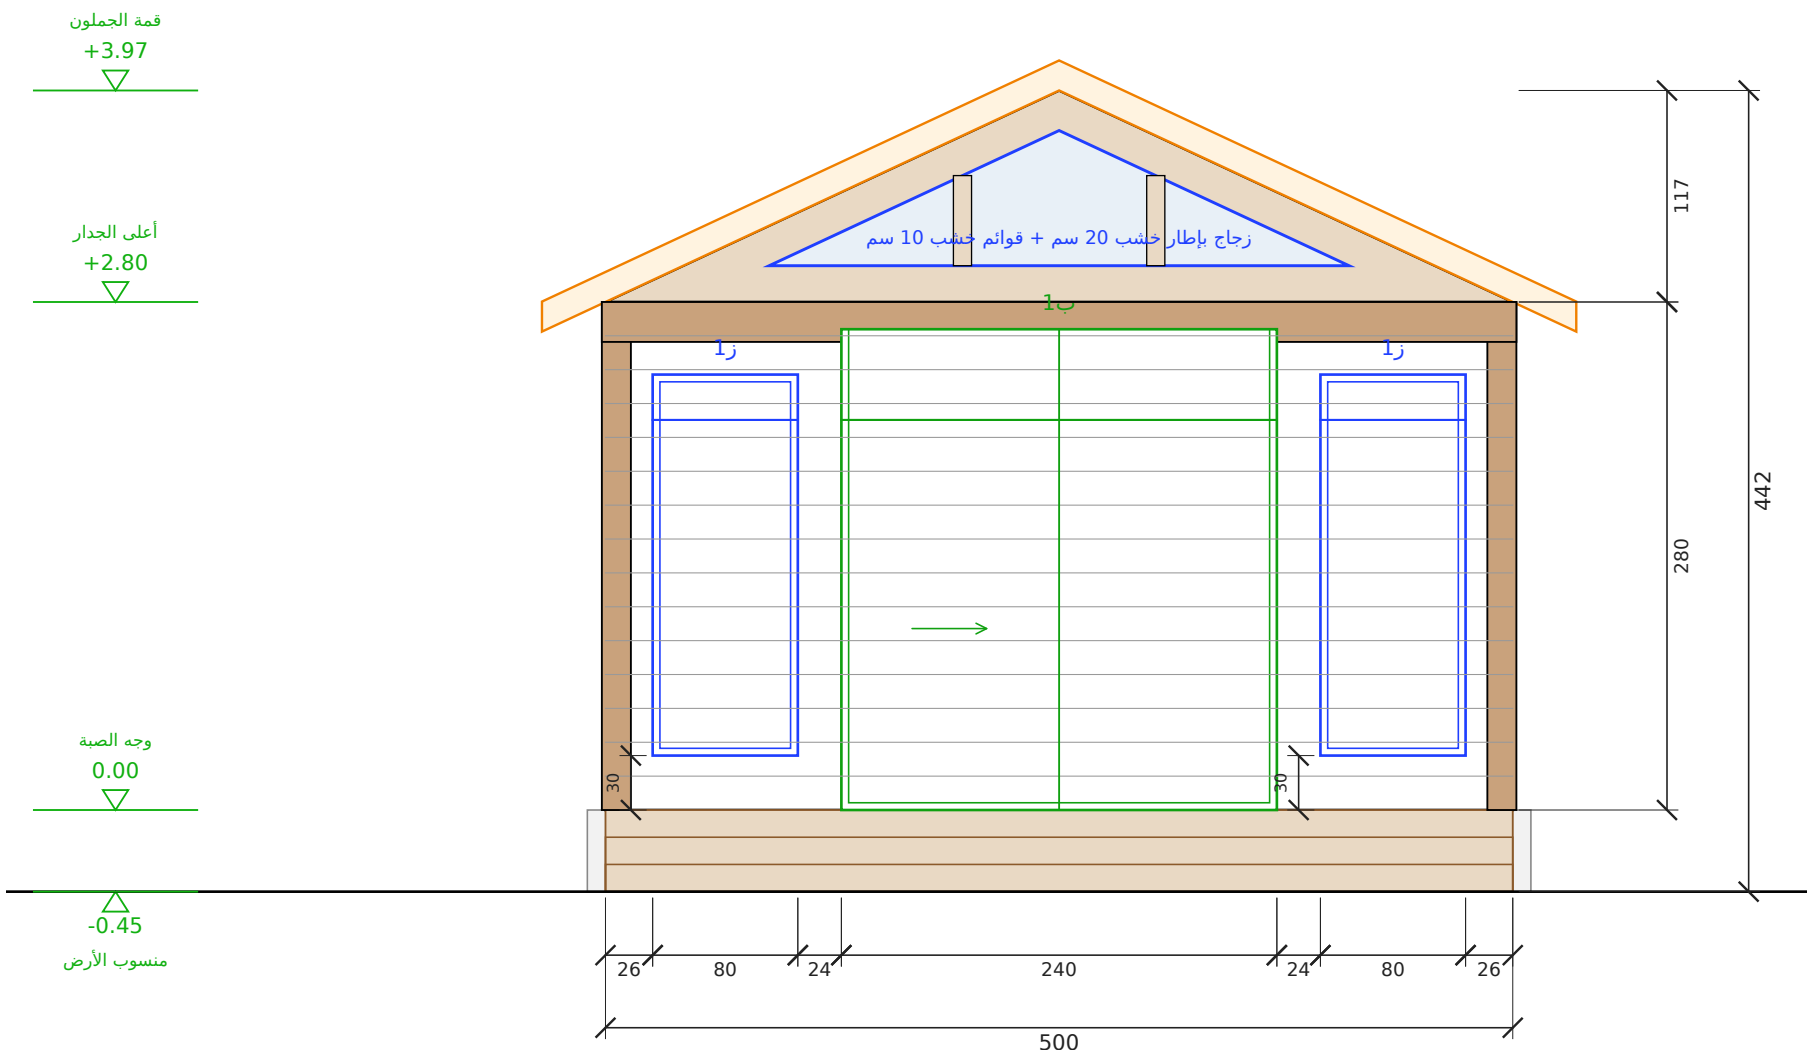

### الواجهة الأمامية (التراس)


مقياس 1:50 | الوحدة: سم

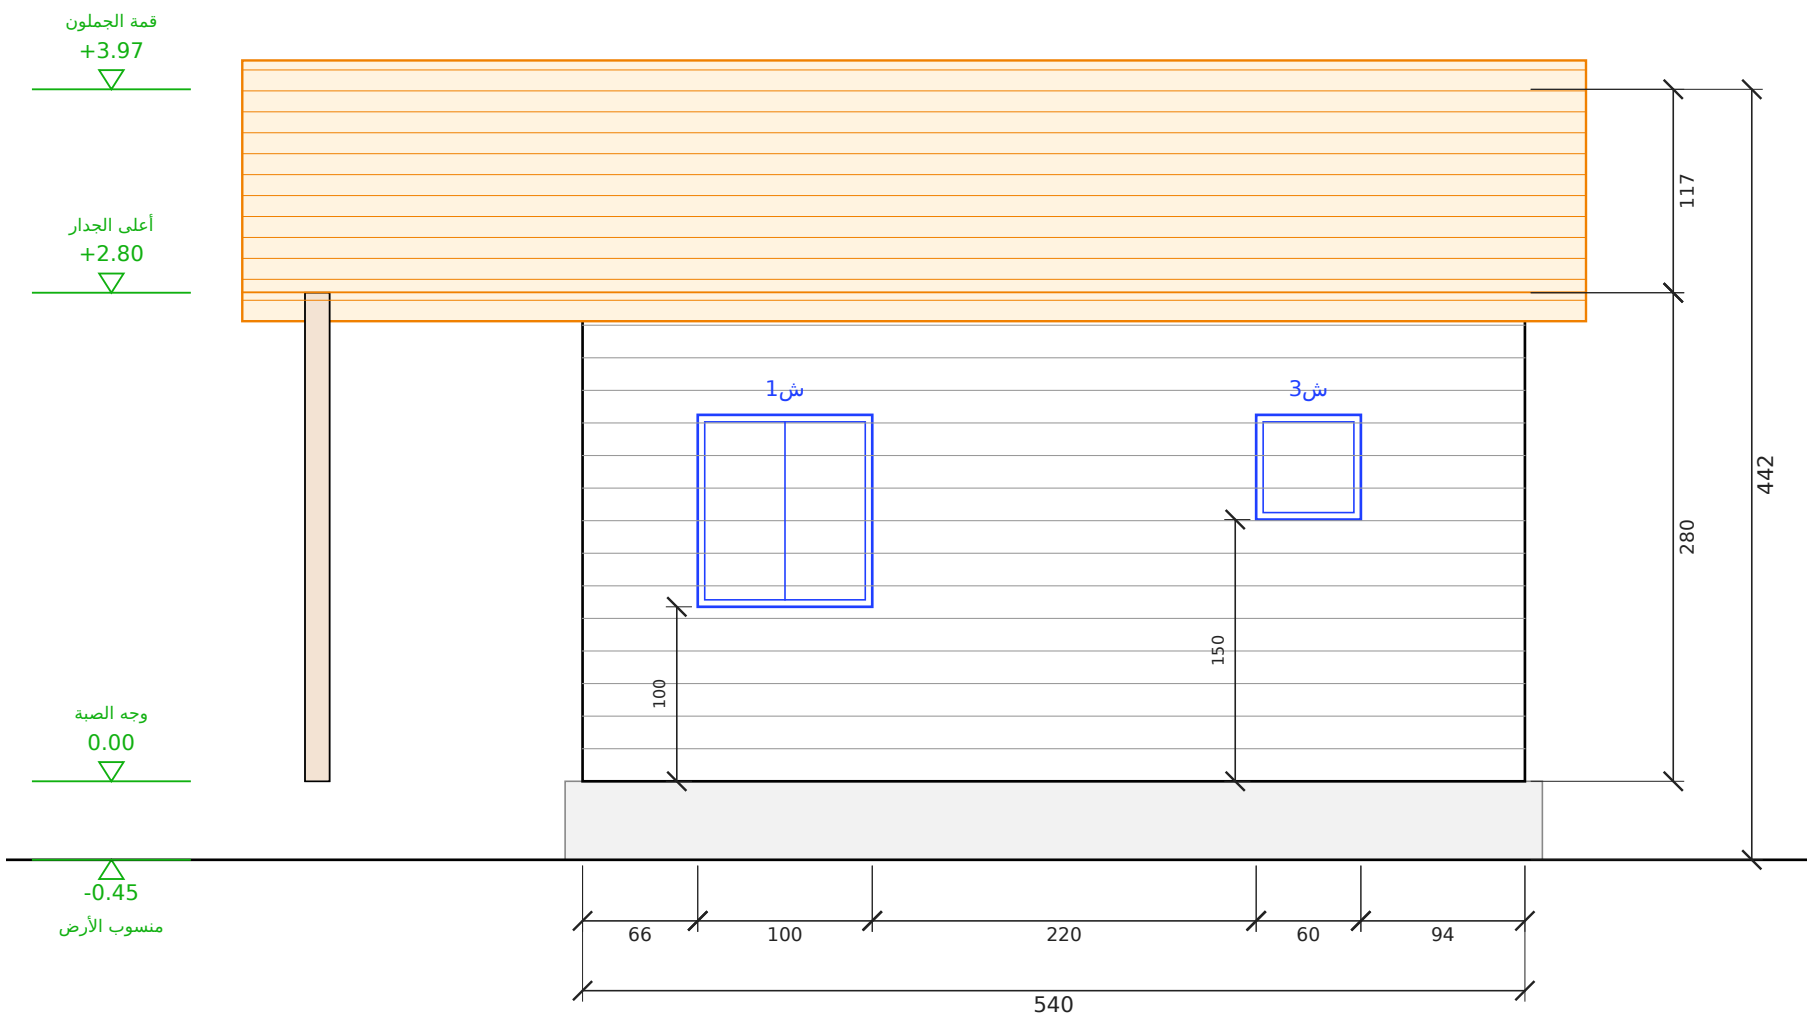

### الواجهة الشرقية


مقياس 1:50 | الوحدة: سم

| رقم اللوحة  | التاريخ    | المقياس | عنوان اللوحة                               | المشروع / العميل                                          | مصنع وتد الأخشاب<br>Watad Wood Factory |
|-------------|------------|---------|--------------------------------------------|-----------------------------------------------------------|----------------------------------------|
| W-03 (3/12) | 2026-09-29 | 1:50    | الواجهة الأمامية (التراس) والواجهة الشرقية | كوخ غرفة وتراس 7x5 شامل التراس<br>عميل - تصميم حسب الصورة |                                        |

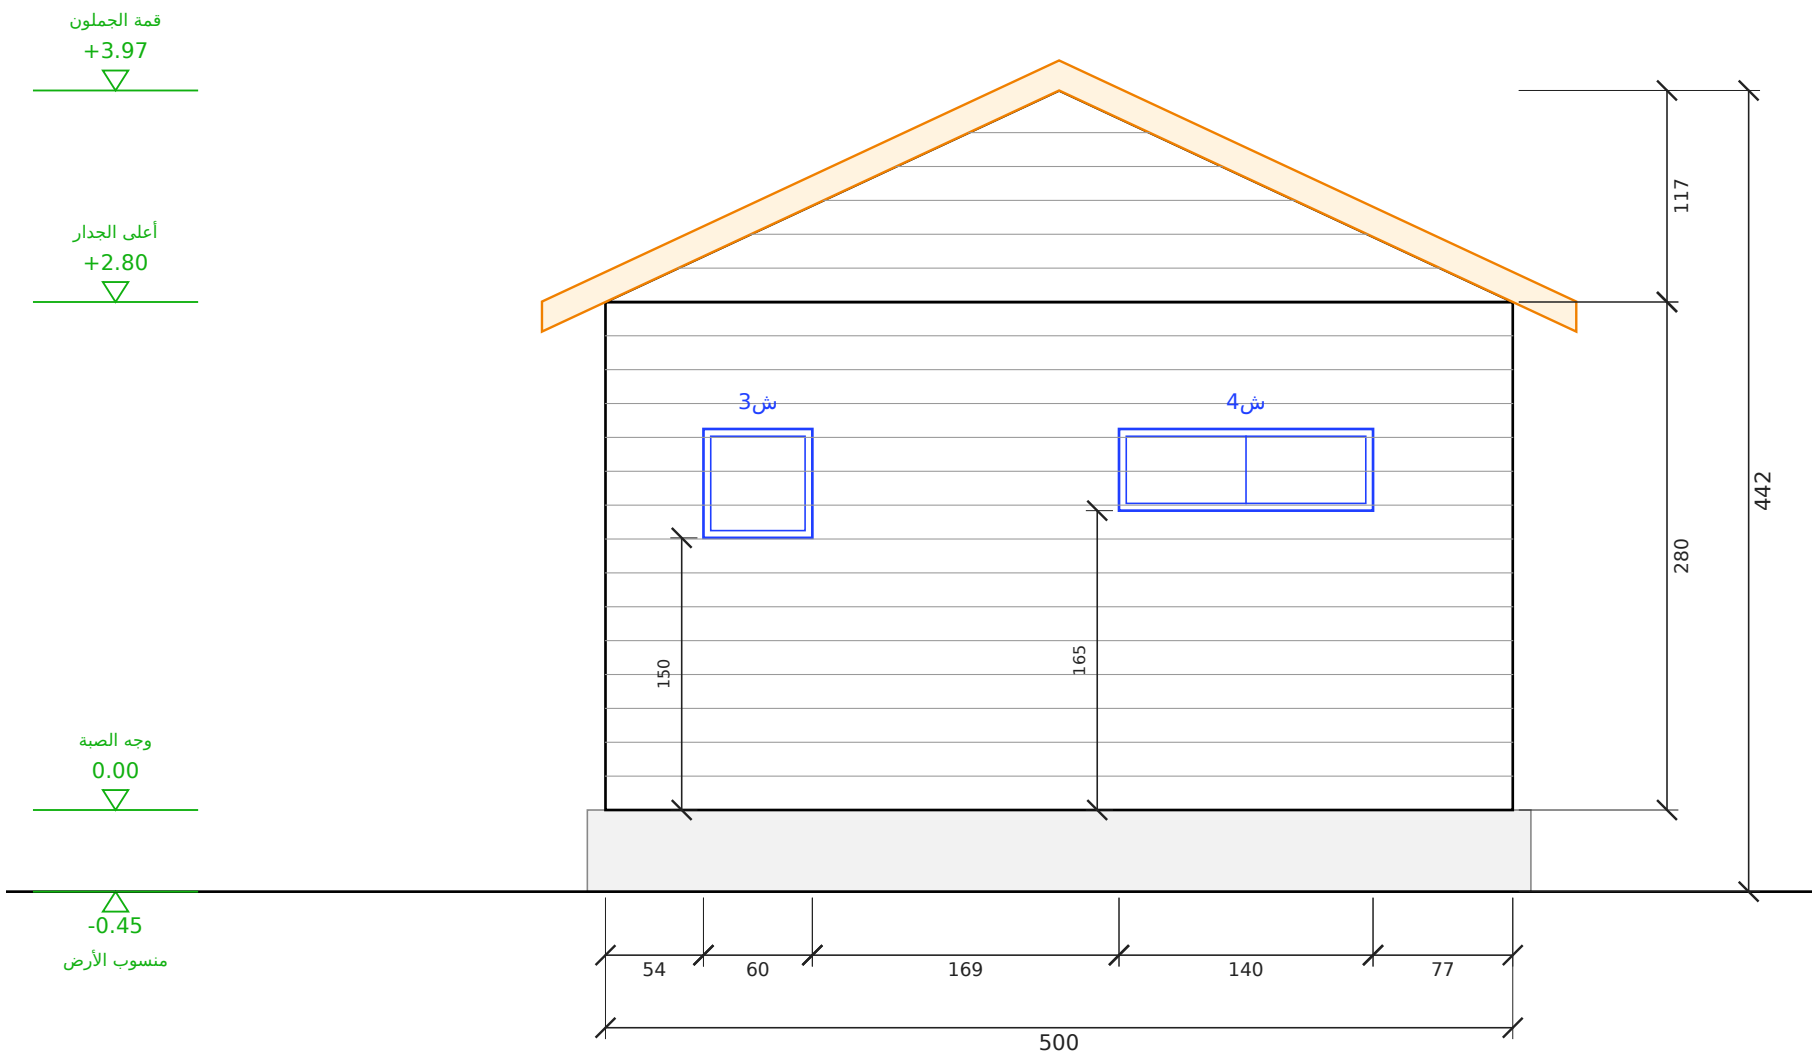

### الواجهة الخلفية

مقياس 1:50 | الوحدة: سم

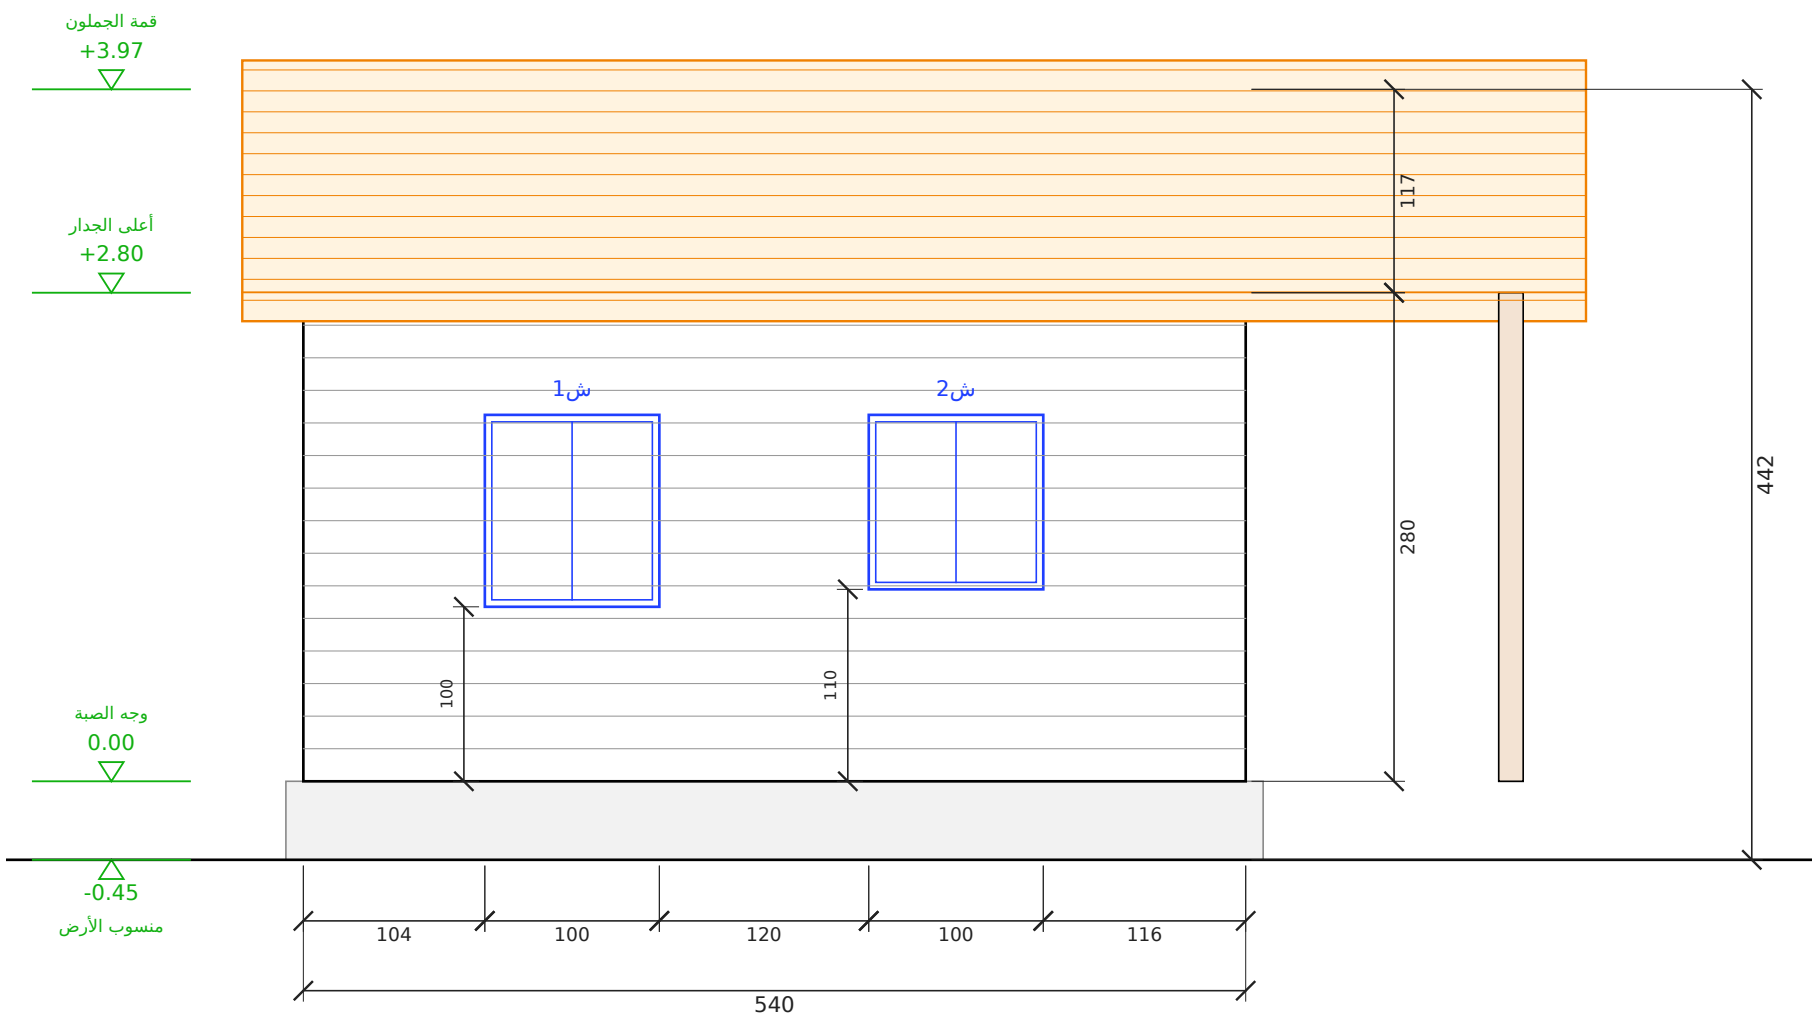


### الواجهة الغربية


مقياس 1:50 | الوحدة: سم

| رقم اللوحة  | التاريخ    | المقياس | عنوان اللوحة                     | المشروع / العميل                                          | مصنع وتد الأخشاب<br>Watad Wood Factory |
|-------------|------------|---------|----------------------------------|-----------------------------------------------------------|----------------------------------------|
| W-04 (4/12) | 2026-09-29 | 1:50    | الواجهة الخلفية والواجهة الغربية | كوخ غرفة وتراس 7x5 شامل التراس<br>عميل - تصميم حسب الصورة |                                        |


مسقط السقف (جملون)  
رفر 35 سم من كل جهة | مقياس 1:50

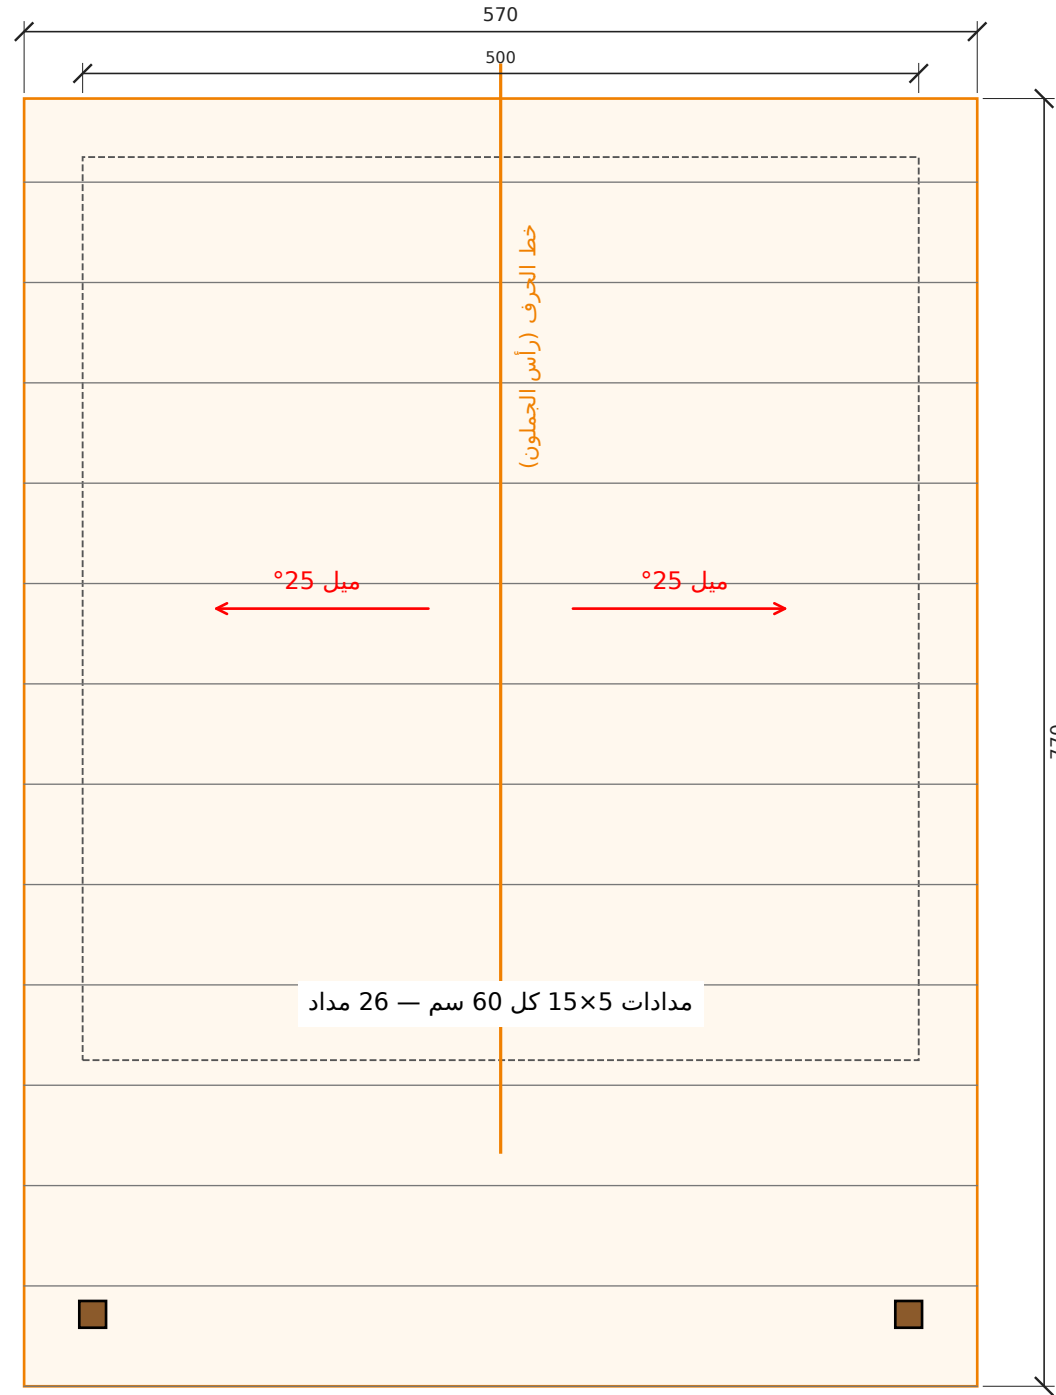

قطاع عرضي أ-أ  
مقياس 1:50 | الوحدة: سم

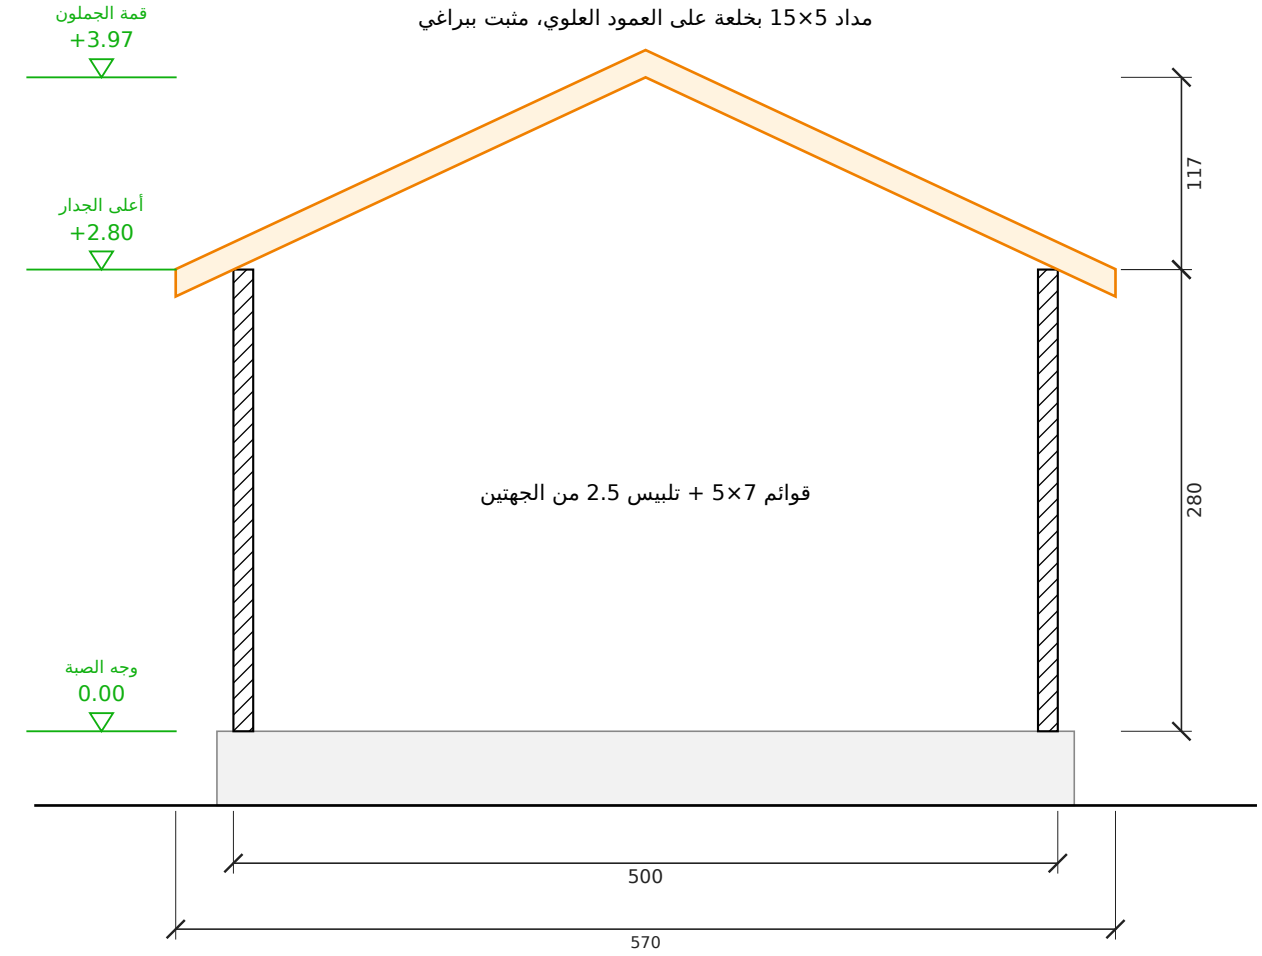

تفصيلة جلوس المداد على العلوي (1:5)

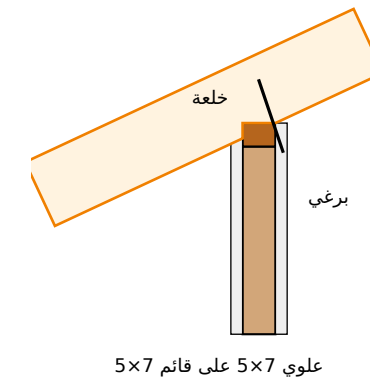

رقم اللوحة

W-05 (5/12)

التاريخ

2026-09-29

المقياس

1:50

عنوان اللوحة

مسقط السقف والقطاع

المشروع / العميل

كوخ غرفة وتراس 7x5 شامل التراس  
عميل - تصميم حسب الصورة

مصنع وتد الأخشاب  
Watad Wood Factory



جدول مقاسات الأبواب والشبابيك  
مقاس الفتحة الصافي في الجدار - الوحدة: سم

| الرمز | النوع     | العرض (سم) | الارتفاع (سم) | ارتفاع الجلسة (سم) | العدد | الموقع              |
|-------|-----------|------------|---------------|--------------------|-------|---------------------|
| ب1    | باب مزدوج | 240        | 265           | -                  | 1     | الأمامية (التراس)   |
| ب2    | باب       | 80         | 210           | -                  | 1     | غرفة النوم          |
| ب3    | باب       | 70         | 210           | -                  | 1     | حمام                |
| ز1    | شباك      | 80         | 210           | 30                 | 2     | الأمامية (التراس) 2 |
| ش1    | شباك      | 100        | 110           | 100                | 2     | الشرقية - الغربية   |
| ش2    | شباك      | 100        | 100           | 110                | 1     | الغربية             |
| ش3    | شباك      | 60         | 60            | 150                | 2     | الشرقية - الخلفية   |
| ش4    | شباك      | 140        | 45            | 165                | 1     | الخلفية             |

الإجمالي: أبواب 3 - شبابيك 8



جدول المساحات وبيانات المشروع والتسعير

جدول المساحات

| م | الفراغ                    | الأبعاد (م) | المساحة (م2) |
|---|---------------------------|-------------|--------------|
| 1 | الصالة والمطبخ            | 4.76 × 2.40 | 11.42        |
| 2 | غرفة النوم                | 3.24 × 2.64 | 8.55         |
| 3 | دورة مياه                 | 1.40 × 2.64 | 3.70         |
|   | المساحة الصافية الداخلية  |             | 23.67        |
|   | التراس المسقوف            | 5.00 × 1.60 | 8.00         |
|   | المساحة الإجمالية المبنية | 5.00 × 5.40 | 27.00        |

بيانات المشروع

| البند       | البيان                                |
|-------------|---------------------------------------|
| المشروع     | كوخ غرفة وتراس 7×5 شامل التراس        |
| العميل      | عميل — تصميم حسب الصورة               |
| الموقع      | —                                     |
| الاستخدام   | استراحة / استجمام                     |
| التاريخ     | 2026-09-29                            |
| نظام البناء | هيكل خشب 5×7 + تليس 2.5 سم من الجهتين |
| السقف       | جملون 25° — قرميد معدني               |


التسعير

| البند                                | القيمة      |
|--------------------------------------|-------------|
| المساحة الكلية — الكوخ + التراس (م2) | 35.00       |
| سعر المتر المربع                     | 1,150 ريال  |
| الإجمالي                             | 40,250 ريال |


ملاحظات:

- السعر لكامل المساحة (الكوخ + التراس المسقوف) حسب المخطط المعتمد.
- الصبة والتמידات الخارجية على العميل ما لم يُذكر غير ذلك.

تأطير جدار جنوب — الطول 488 سم، الارتفاع 280 سم

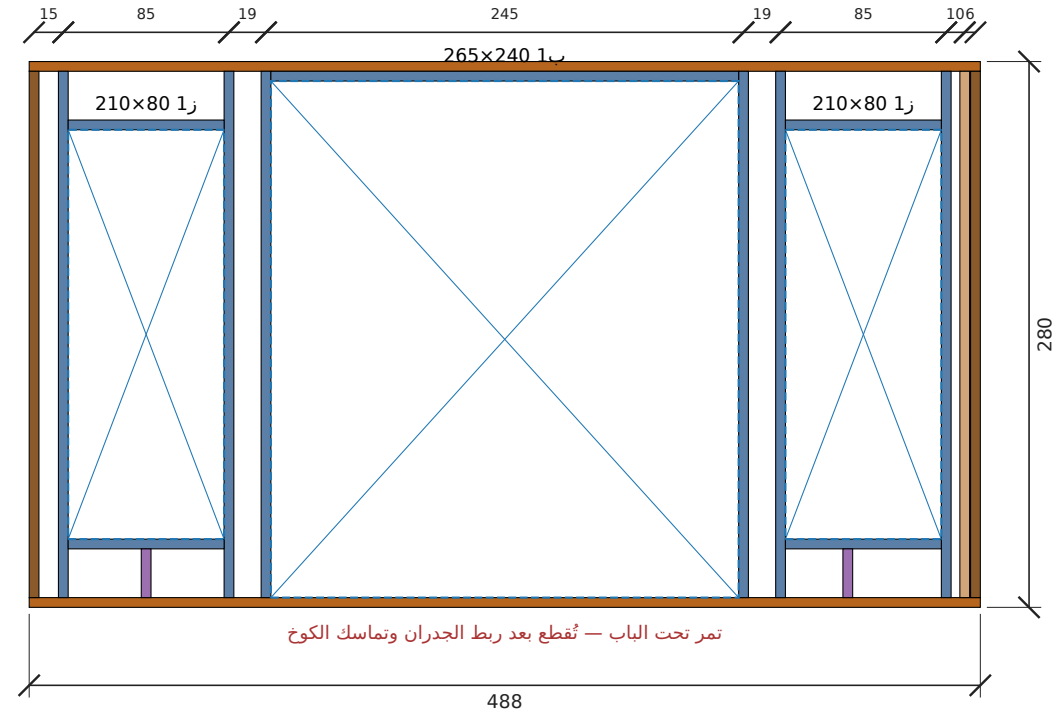

تأطير جدار شرق — الطول 528 سم، الارتفاع 280 سم

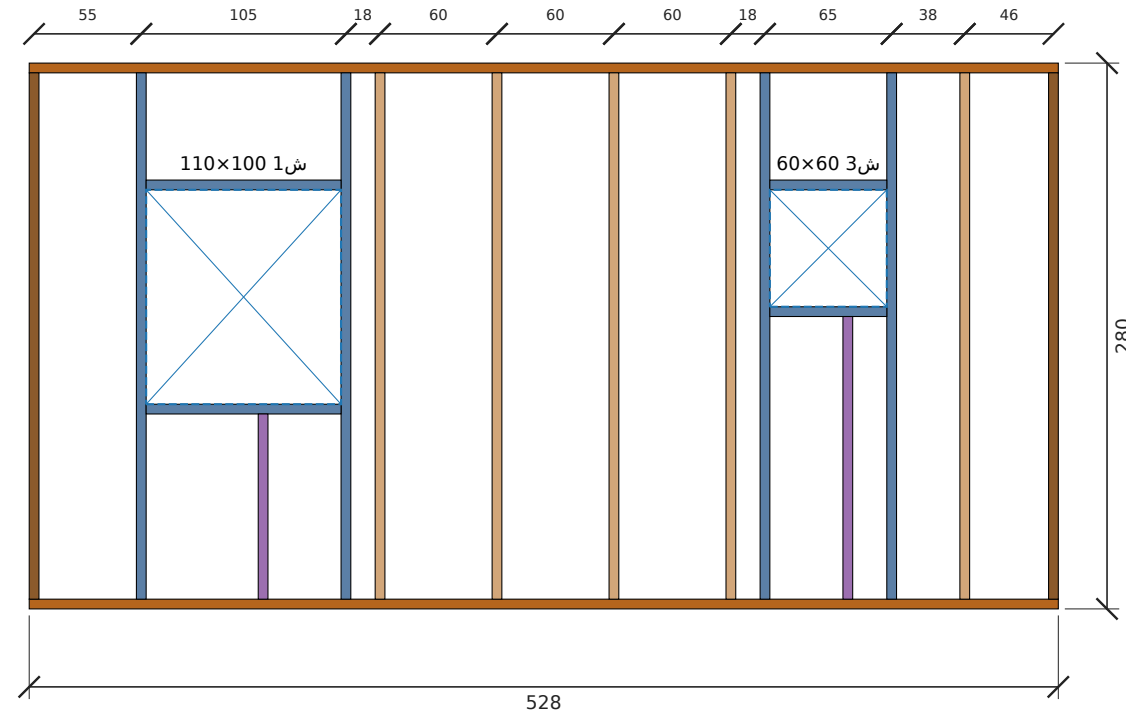

قاعدة سفلية علوي عمود عمود زاوية جنب فتحة رأس فتحة جلسة شباك عمود قصير

رقم اللوحة

W-08 (8/12)

التاريخ

2026-09-29

المقياس

—

عنوان اللوحة

لوحات التأطير (للورشة)

المشروع / العميل


كوخ غرفة وتراس 7x5 شامل التراس  
عميل — تصميم حسب الصورة

مصنع وتد الأخشاب  
Watad Wood Factory






تأطير جدار شمال — الطول 488 سم، الارتفاع 280 سم

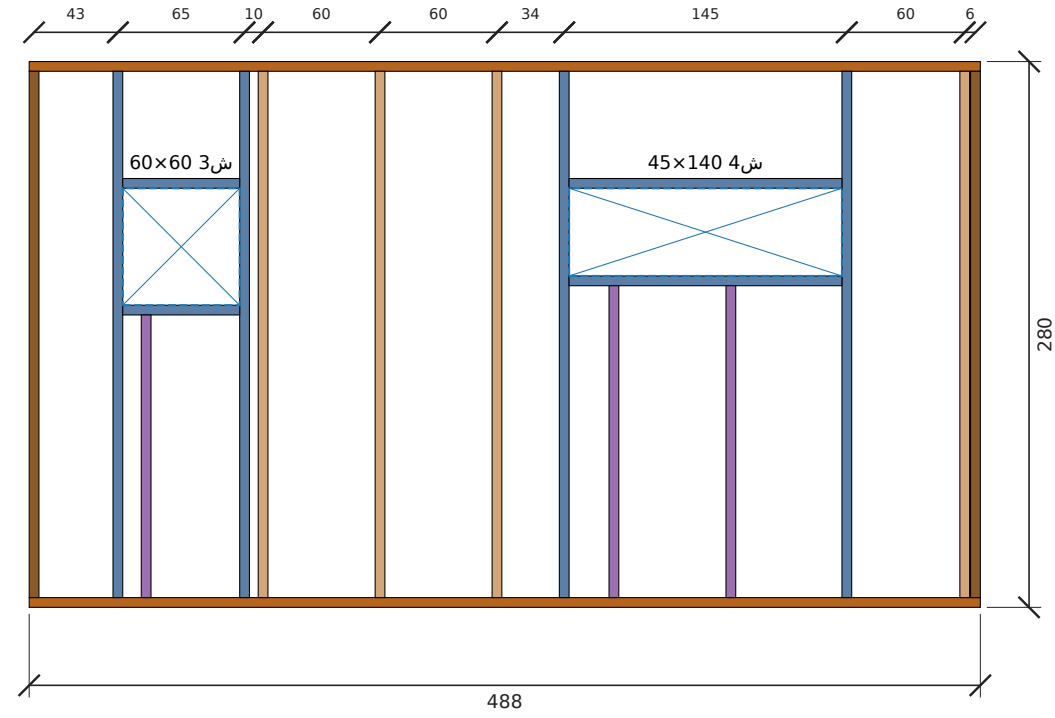

تأطير جدار غرب — الطول 528 سم، الارتفاع 280 سم

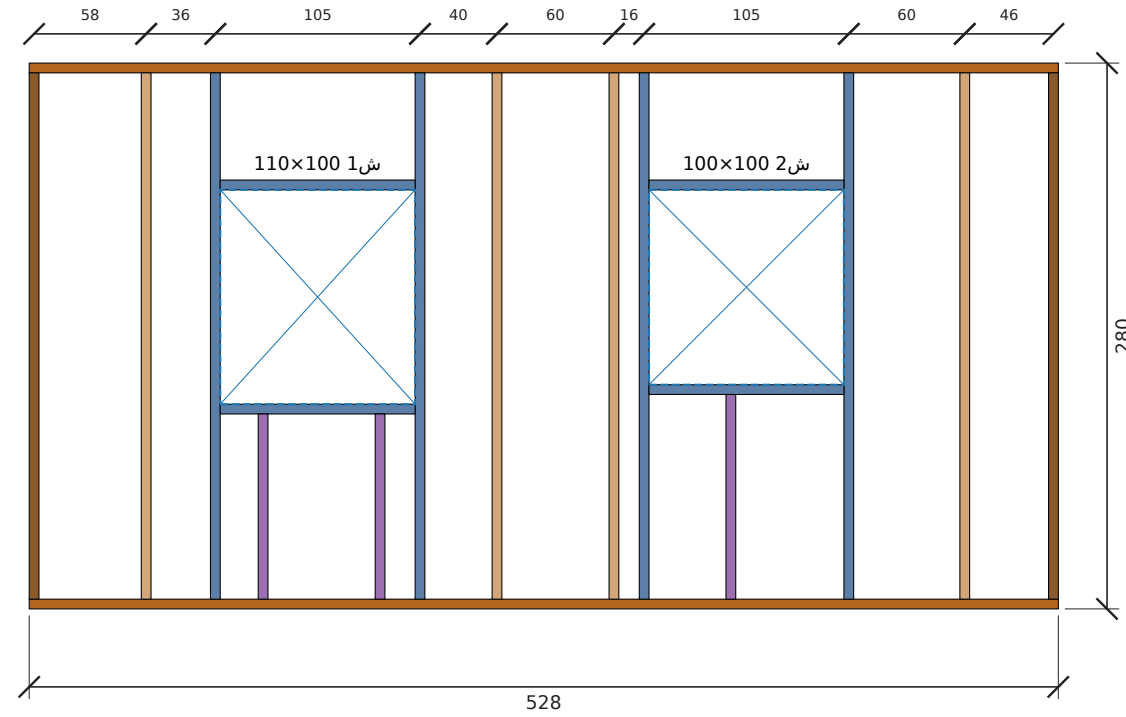

قاعدة سفلية علوي عمود عمود زاوية جنب فتحة رأس فتحة جلسة شباك عمود قصير

رقم اللوحة

W-09 (9/12)

التاريخ

2026-09-29

المقياس

—

عنوان اللوحة

لوحات التأطير (للورشة)


المشروع / العميل

كوخ غرفة وتراس 7×5 شامل التراس  
عميل — تصميم حسب الصورة


مصنع وتد الأخشاب  
Watad Wood Factory



تأطير جدار د1-فاصل الصالة — الطول 488 سم، الارتفاع 280 سم (داخلي)

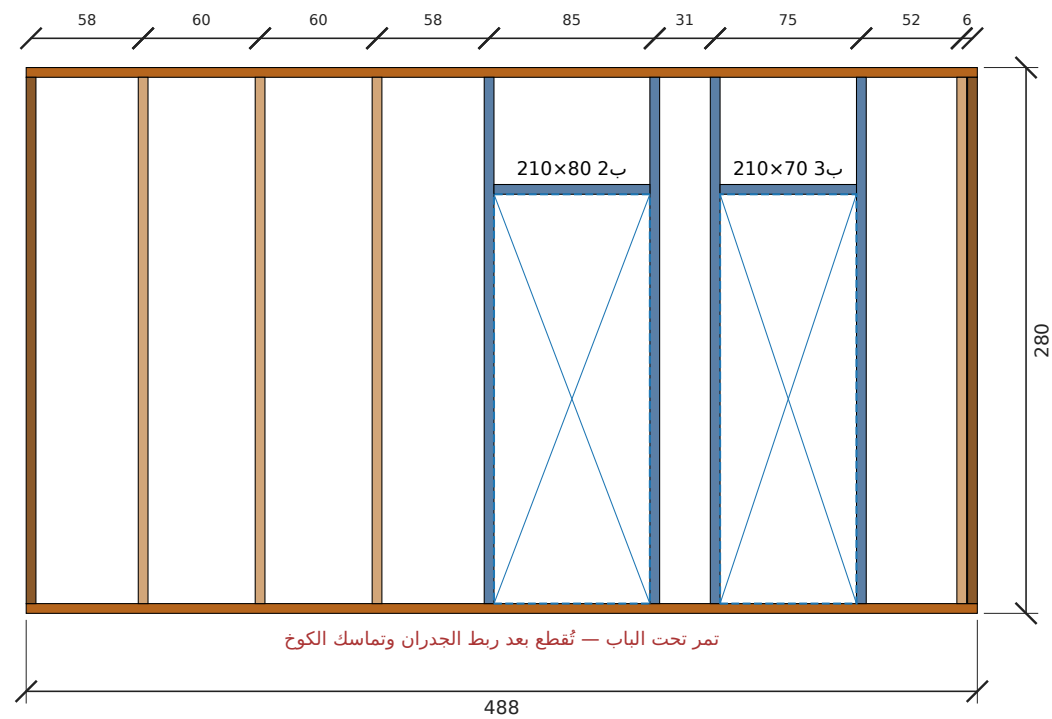

تأطير جدار د2-جدار الحمام — الطول 276 سم، الارتفاع 280 سم (داخلي)

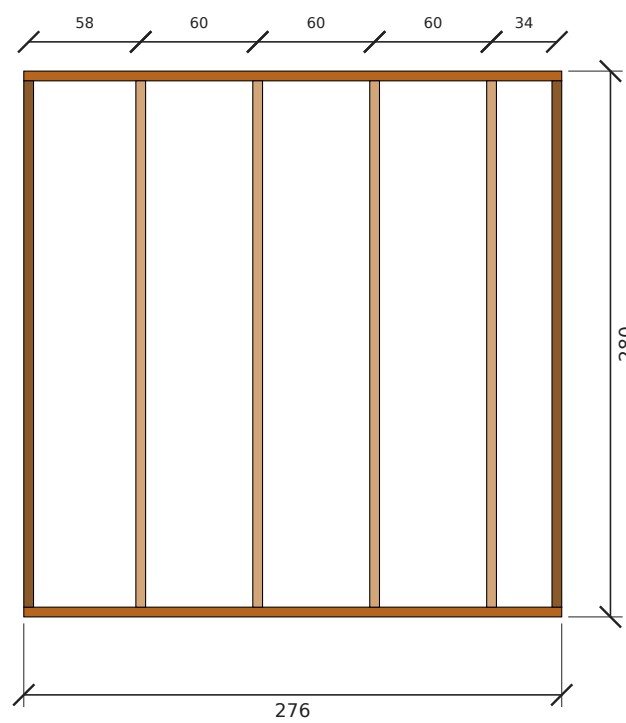

■ قاعدة سفلية 
 ■ علوي 
 ■ عمود 
 ■ عمود زاوية 
 ■ جنب فتحة 
 ■ رأس فتحة 
 ■ جلسة شباك 
 ■ عمود قصير

رقم اللوحة

W-10 (10/12)

التاريخ

2026-09-29

المقياس

—

عنوان اللوحة

لوحات التأطير (للورشة)

المشروع / العميل

كوخ غرفة وتراس 7x5 شامل التراس  
عميل — تصميم حسب الصورة

مصنع وتد الأخشاب  
Watad Wood Factory



جدول الكميات وخطة تقطيع الطبلیات

| البند                               | القيمة                                                                                   |
|-------------------------------------|------------------------------------------------------------------------------------------|
| الارتفاع المطلوب / المعتمد          | 280 / 280 سم                                                                             |
| السقف                               | جملون 25° — قمة 397 سم من وجه الصبة                                                      |
| المدادات 15×5                       | 26 مداد (13 لكل جهة) × 314 سم — من طبلية 320                                             |
| طبلیات الطريقة الأولى (مداد + عمود) | 26 طبلية × 320 سم                                                                        |
| طبلیات الطريقة الثانية (3 أعمدة)    | 21 طبلية × 320 سم                                                                        |
| إجمالي الطبلیات 22.5×5              | 47                                                                                       |
| إجمالي قطع 5×7                      | 97                                                                                       |
| قائمة تقطيع 5×7                     | 528سم×4   488سم×6   276سم×2   270سم×56   240سم×1   160سم×2   145سم×2   140سم×2   105سم×1 |
|                                     | 100سم×6   95سم×3   80سم×5   70سم×1   60سم×4   25سم×2                                     |
| ألواح تلبیس 2.5 سم                  | 148 لوح × 400 سم (مجموع الصفوف 523.2 م، 12 وجه)                                          |
| أسمنت بورد 12 مم (244×122)          | 20 لوح (داخل دورات المياه)                                                               |
| العزل                               | بدون (غير مطلوب)                                                                         |
| الصبة                               | یجهزها العميل — 20 سم، مفرغة تحت دورات المياه                                            |

مراجعة التصميم مقابل قواعد المصنع

| النوع  | البند               | التفاصيل   | المقترح |
|--------|---------------------|---|---------|
| ملاحظة | بحر المدادات        | أطول بحر بدون جدار داخلي يحمل المداد: جهة أ: 250 سم،<br>جهة ب: 250 سم. يحتاج رقم المصنع لأقصى بحر مسموح لتحديد<br>المدادات اللي تُقوّى 5×20. |         |
| ملاحظة | الصبة والدرج        | ارتفاع الصبة 45 سم ← 3 درجة بقائمة 15.0 سم.                                                                                                  |         |
| ملاحظة | مناسيب رؤوس الفتحات | رؤوس الأبواب والشبابيك على مناسيب مختلفة: 210، 240، 265<br>سم.                                                                               |         |
| سؤال   | يحتاج تأكيد         | أقصى بحر للمداد بدون جدار داخلي قبل إضافة تقوية 5×7<br>(مداد 5×20)؟                                                                          |         |
| سؤال   | يحتاج تأكيد         | التغطية الصافية للوح التليس بعد التعشيق (مستنتجة<br>مؤقتاً 18.67 سم من 280/15)؟                                                              |         |
| سؤال   | يحتاج تأكيد         | هل يوضع أعمدة قصيرة فوق رأس الشباك/الباب إلى العلوي؟                                                                                         |         |
| سؤال   | يحتاج تأكيد         | مكان الوصلة في القاعدة والعلوي إذا الجدار أطول من<br>الطيلية؟                                                                                |         |