
المنظور ثلاثي الأبعاد والمواد

النمط: جوزي غامق + إطارات سوداء — رندر واقعي بخامات حقيقية

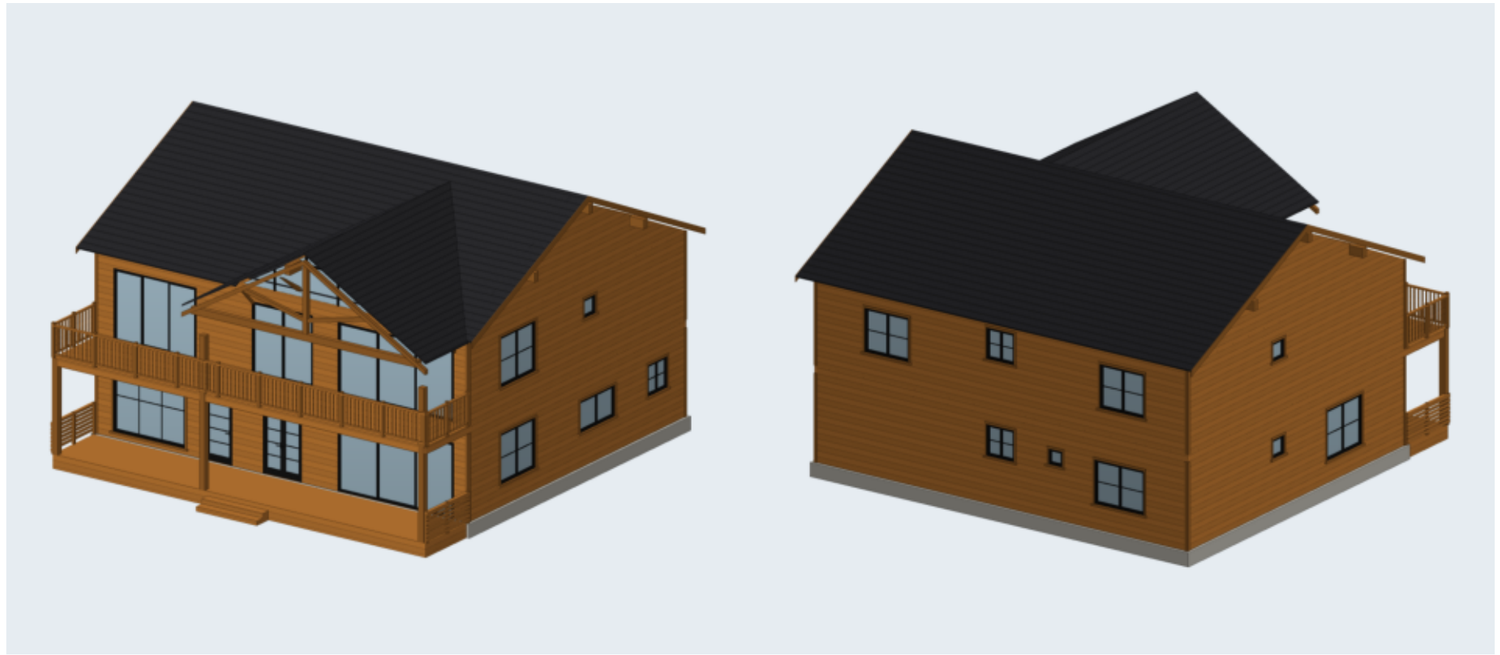

جدول المواد والألوان

الخشب / الصبغة
صبغة عسلي / سيدر

القرميد
قرميد رمادي غامق

الزجاج
زجاج شفاف

إطارات الشبابيك والأبواب
إطار ألمنيوم أسود


الكنار والزوايا
نفس الصبغة أغمق درجة

الصبة
خرسانة 45 سم


الدربزين: ألواح أفقية متقاربة (عصري)

تقسيم الشبابيك: بدون | الباب الرئيسي: زجاج بتقسيمات (فرنسي)

أنواع الدربزين المعتمدة (من مشاريع المصنع)

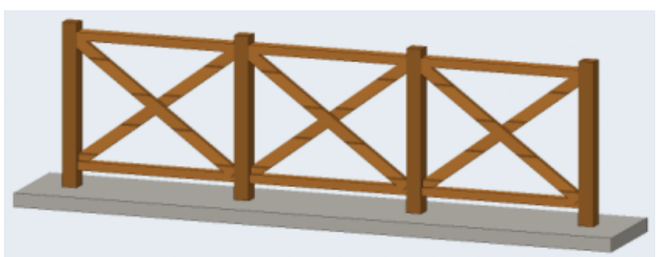

تقاطع X (صورة 5)

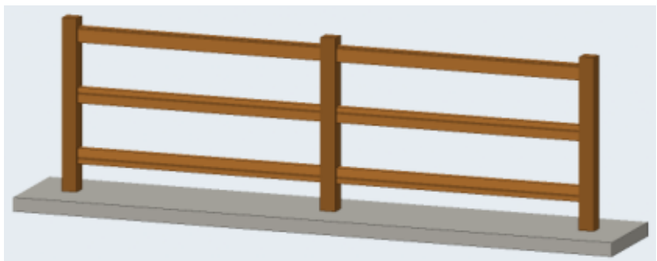

3 مرابيع أفقية (صورة 2)




قوائم رأسية متقاربة (صورة 1)

المشروع / العميل	عنوان اللوحة	المقياس	التاريخ	رقم اللوحة
بيت خشب دورين متكامل – استقبال وصالة وأربع غرف – 13.36 × 11.12 م **عميل – فيلا دورين**	**المنظور والمواد**	**1:50**	**2026-11-01**	**W-01 (1/24)**

مصنع وتد الأخشاب
Watad Wood Factory

المسقط الأفقي مع الفرش — الدور الأرضي


الأبعاد بالسنتيمتر - الجدران: قوائم 7×5 + تلبيس 2.5 من الجهتين (12 سم) | منسوب الأرضية +0.00

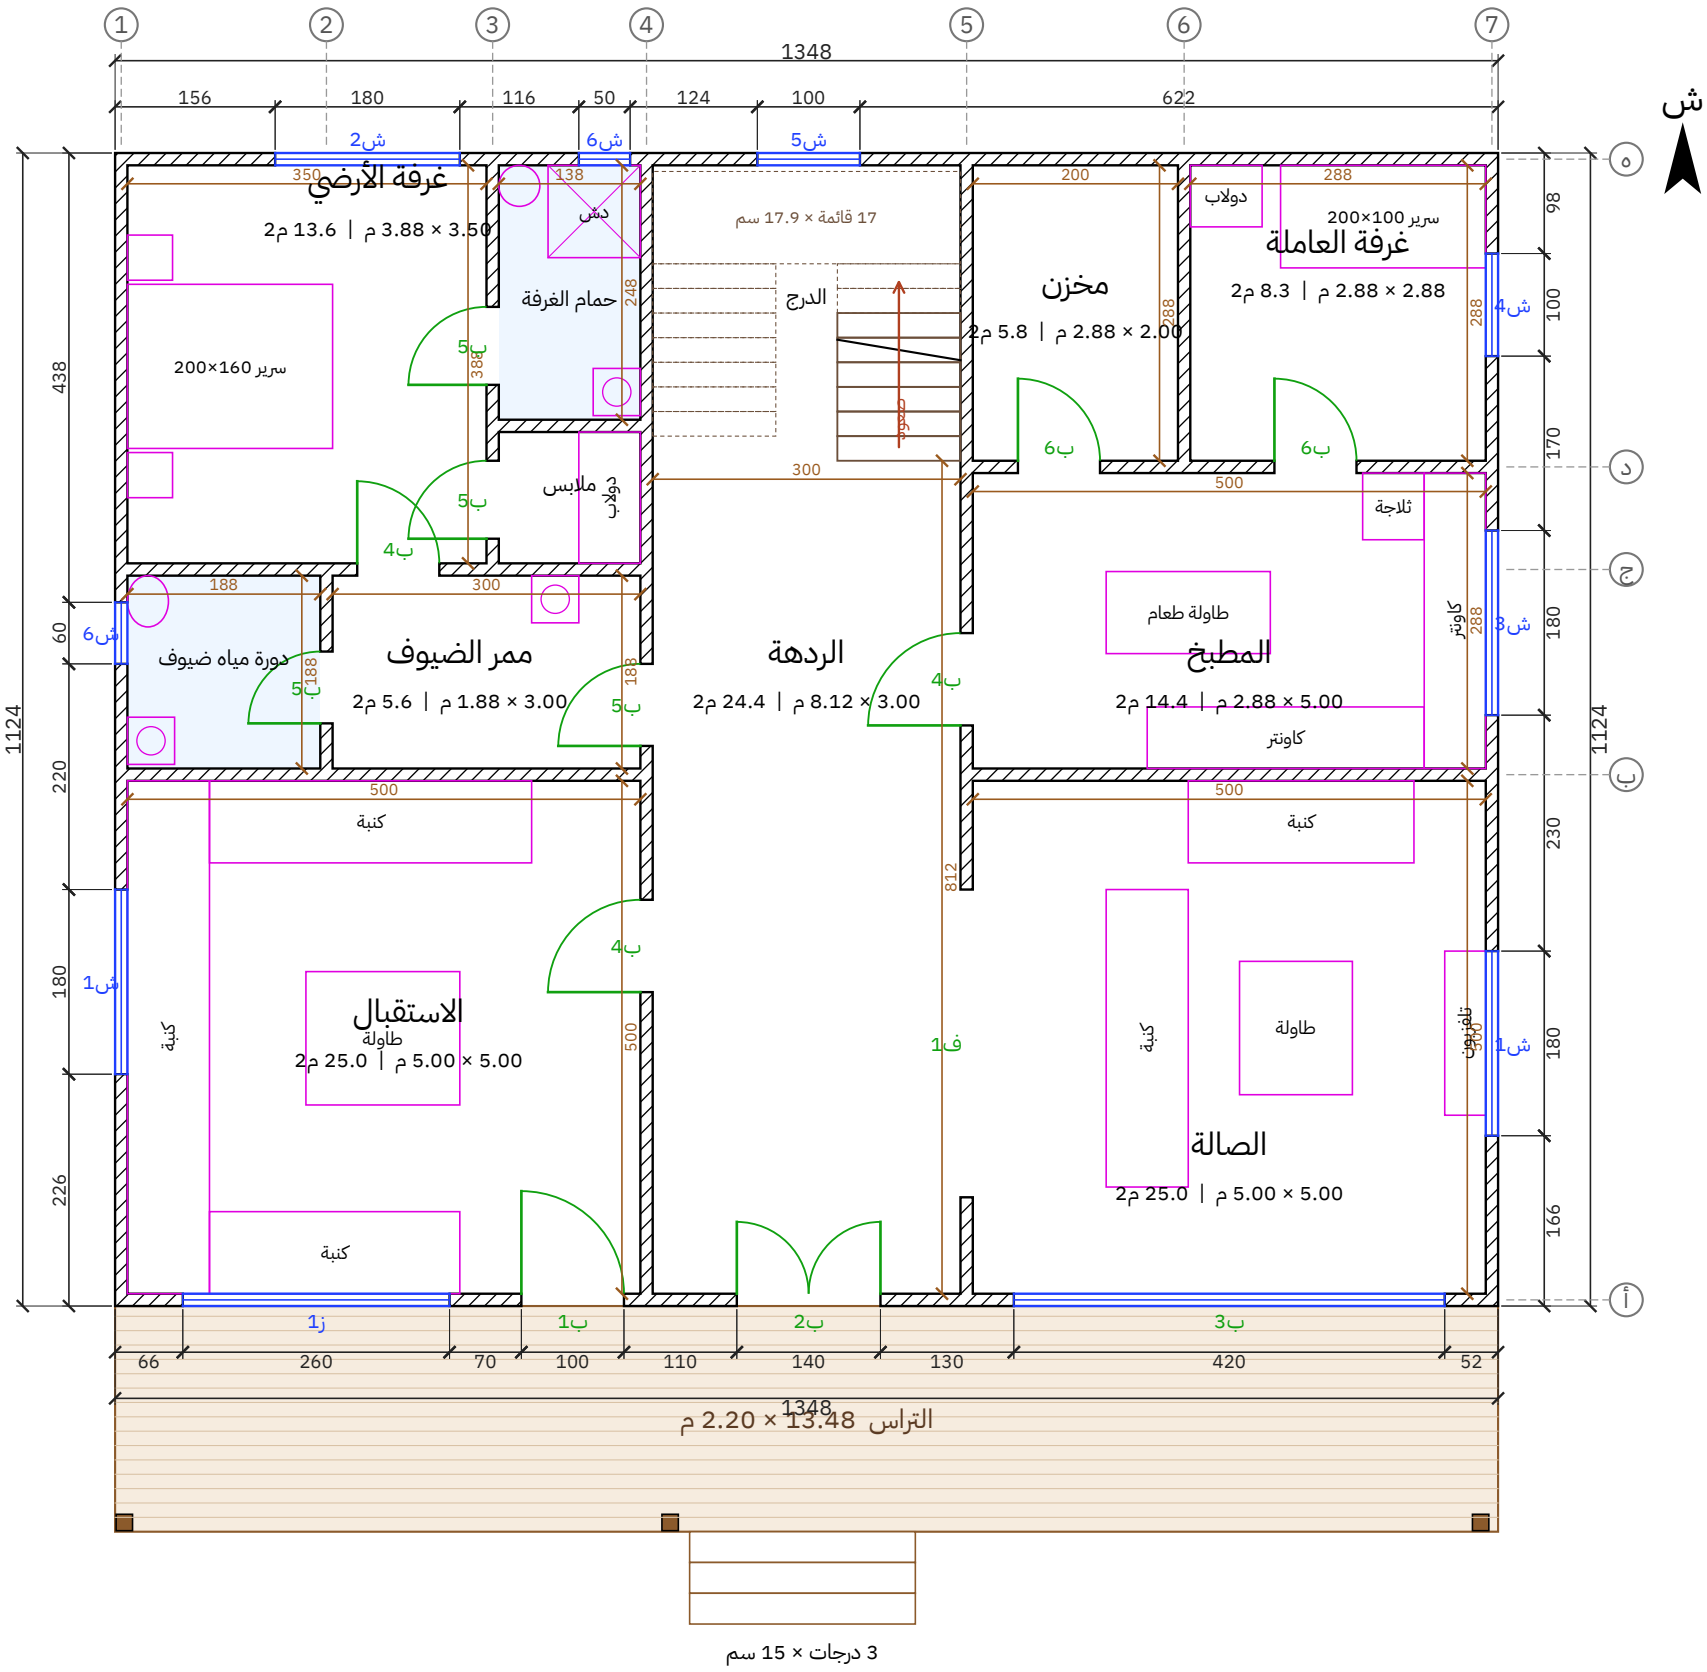

مصنع وتد الأخشاب Watad Wood Factory	المشروع / العميل بيت خشب دورين متكامل — استقبال وصالة وأربع غرف — 13.36 × 11.12 م عميل — فيلا دورين	عنوان اللوحة المسقط الأفقي — الدور الأرضي	المقياس 1:50	التاريخ 2026-11-01	رقم اللوحة W-02 (2/24)

المسقط الأفقي مع الفرش — الدور الأول

الأبعاد بالسنتيمتر - الجدران: قوائم 5×7 + تلبيس 2.5 من الجهتين (12 سم) | منسوب الأرضية +3.05

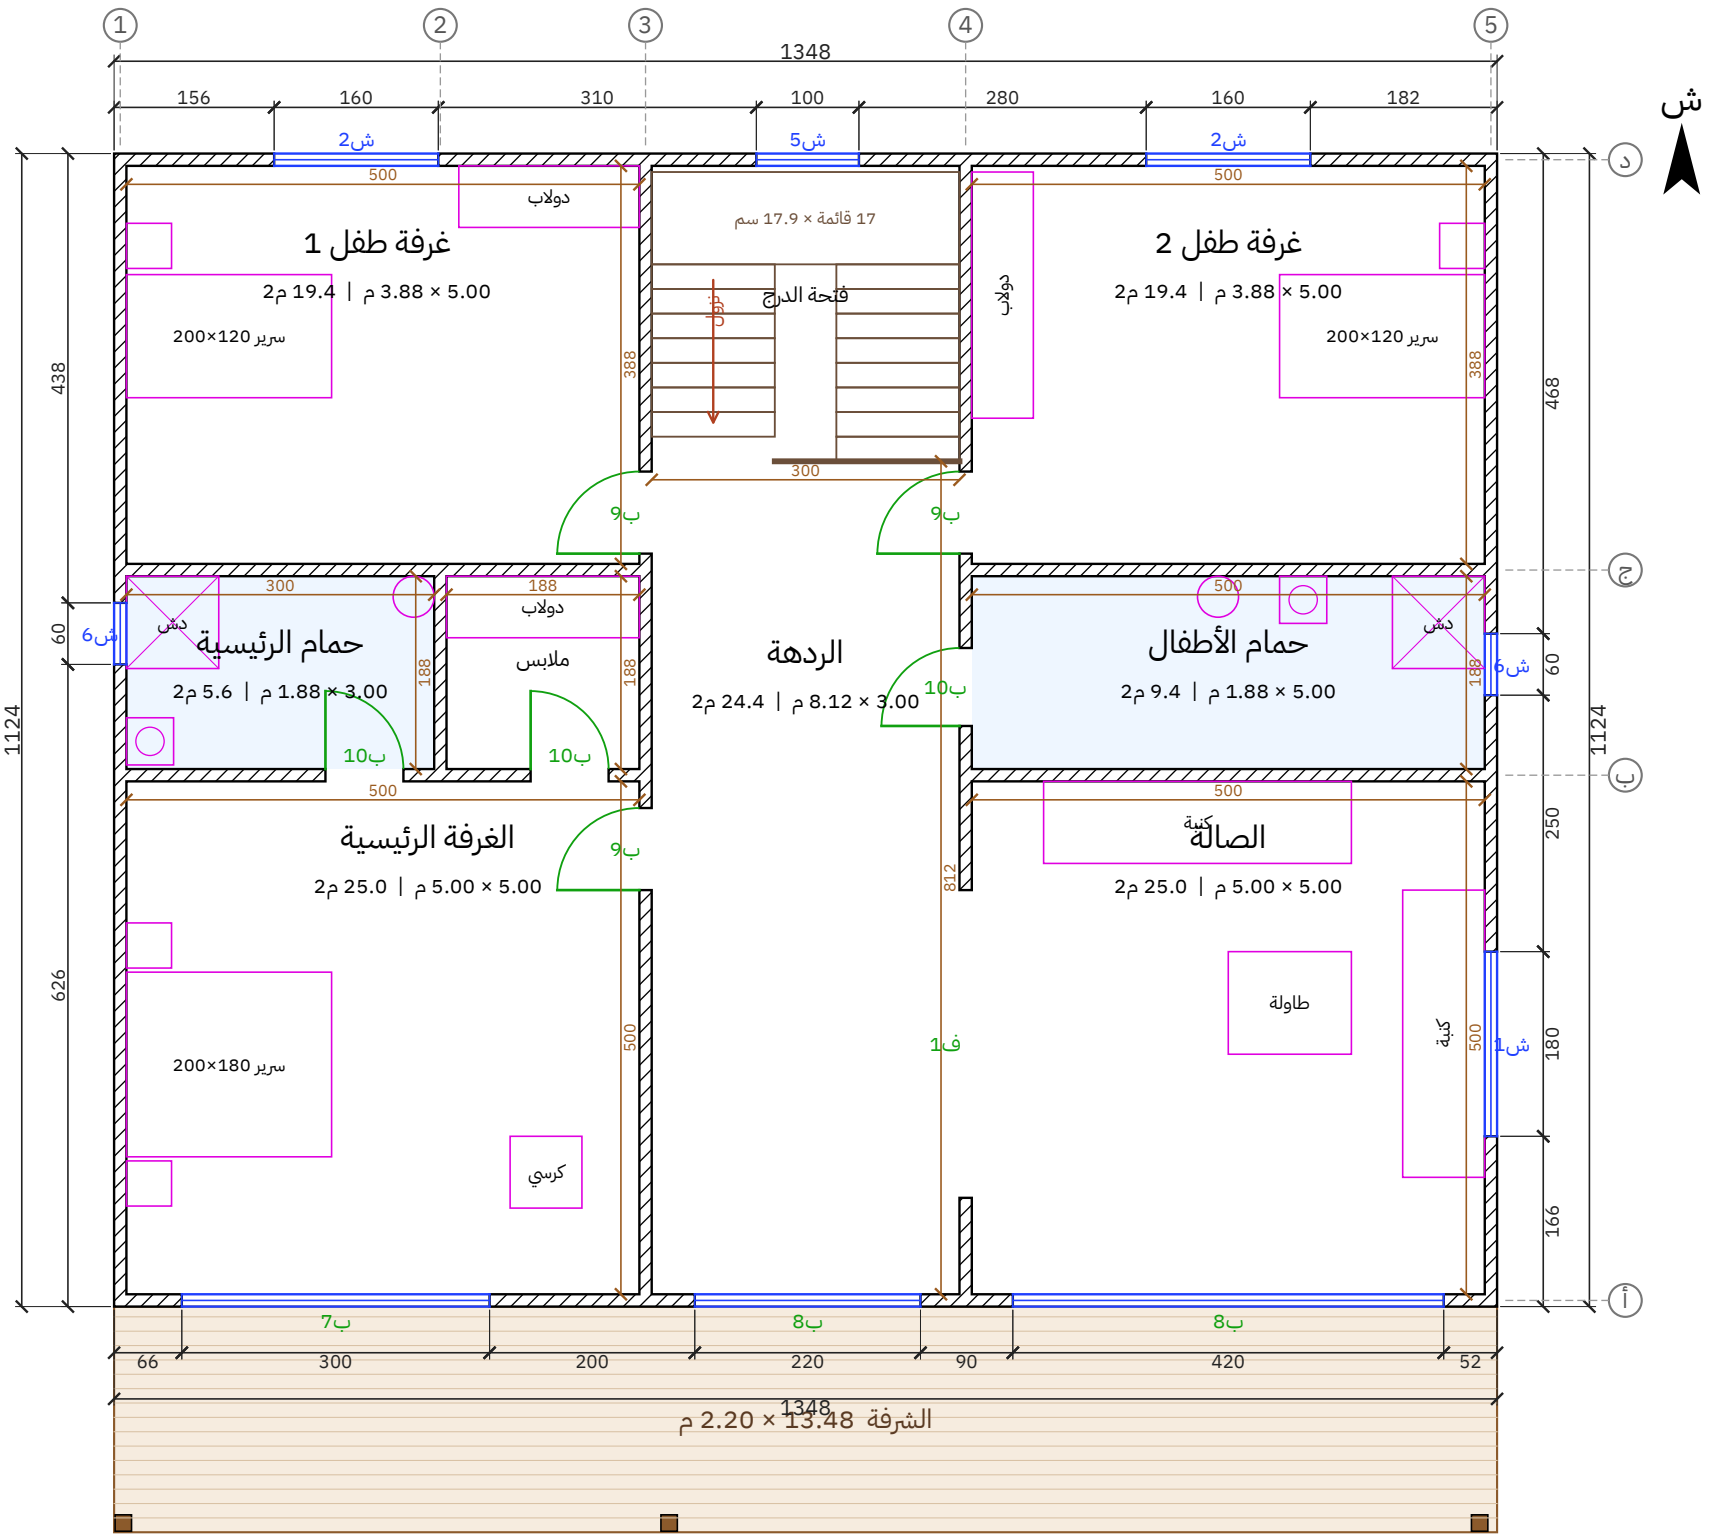


مصنع وتد الأخشاب Watad Wood Factory	المشروع / العميل بيت خشب دورين متكامل — استقبال وصالة وأربع غرف — 13.36 × 11.12 م عميل — فيلا دورين	عنوان اللوحة المسقط الأفقي — الدور الأول	المقياس 1:50	التاريخ 2026-11-01	رقم اللوحة W-03 (3/24)



الواجهة الأمامية


مقياس 1:50 | الوحدة: سم

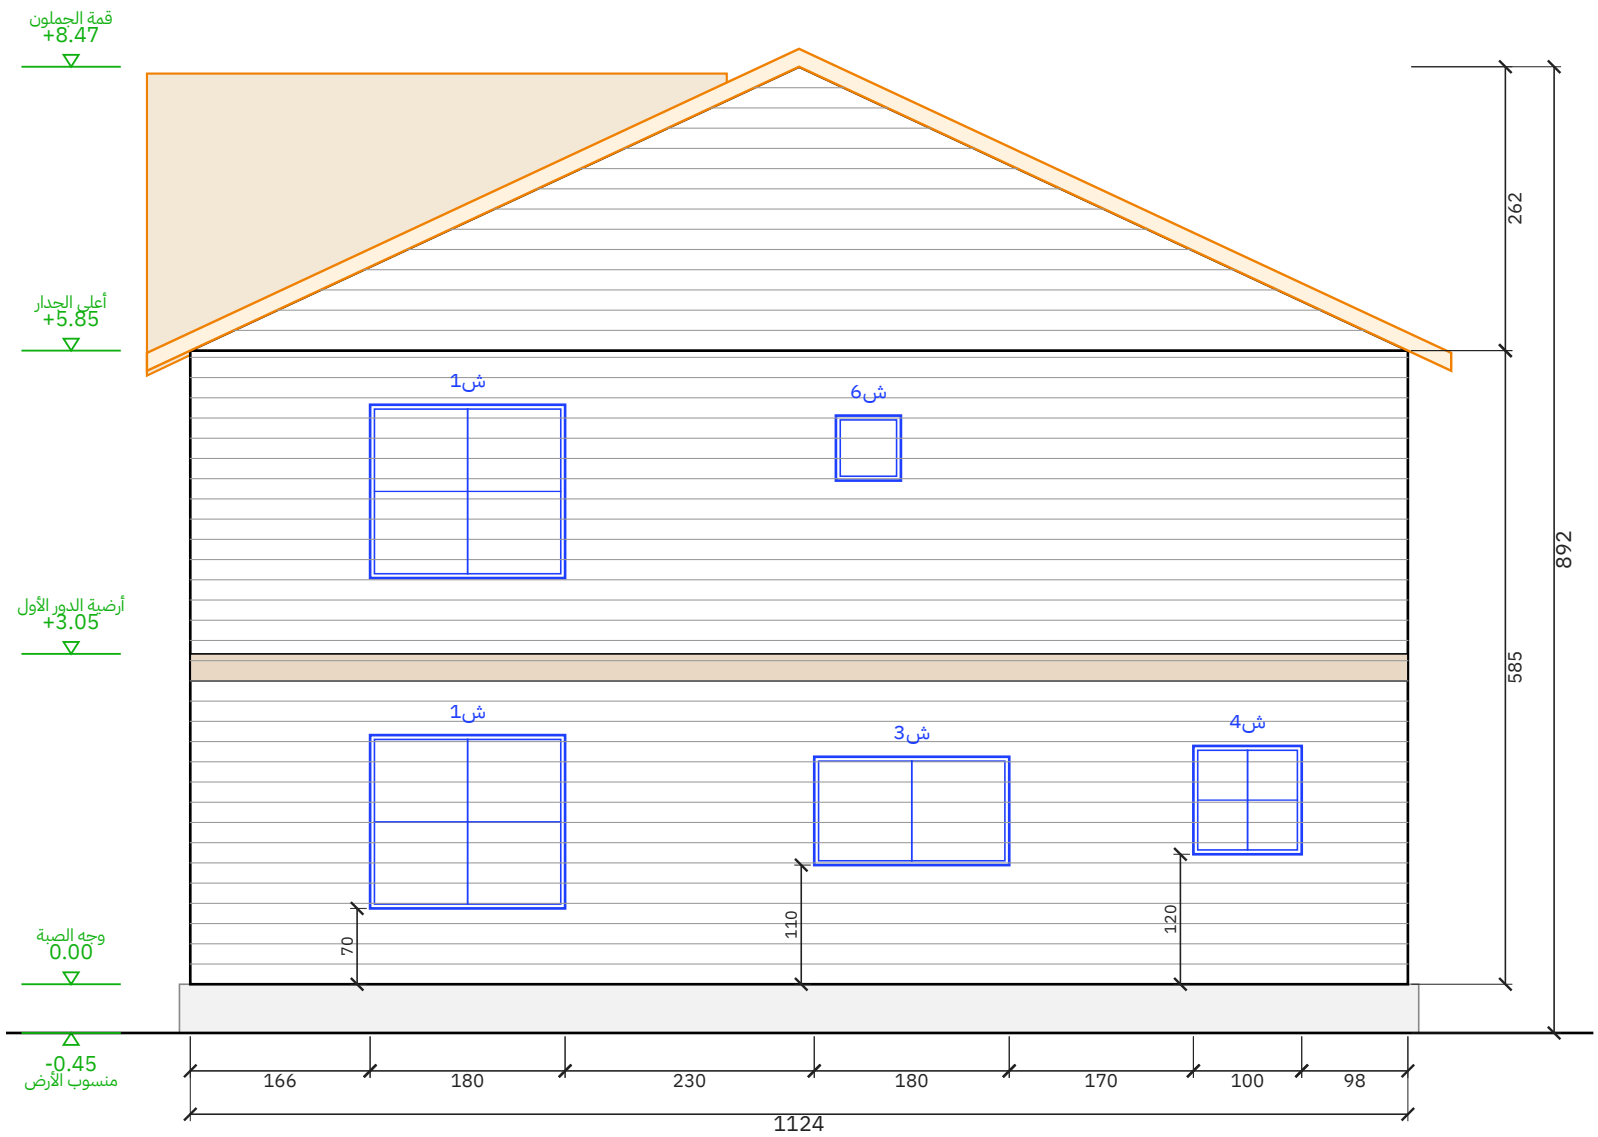

الواجهة الشرقية


مقياس 1:50 | الوحدة: سم

المشروع / العميل	عنوان اللوحة	المقياس	التاريخ	رقم اللوحة	
بيت خشب دورين متكامل – استقبال وصالة وأربع غرف – 13.36 × 11.12 م عميل – فيلا دورين	الواجهة الأمامية والواجهة الشرقية	1:50	2026-11-01	W-04 (4/24)	مصنع وتد الأخشاب Watad Wood Factory

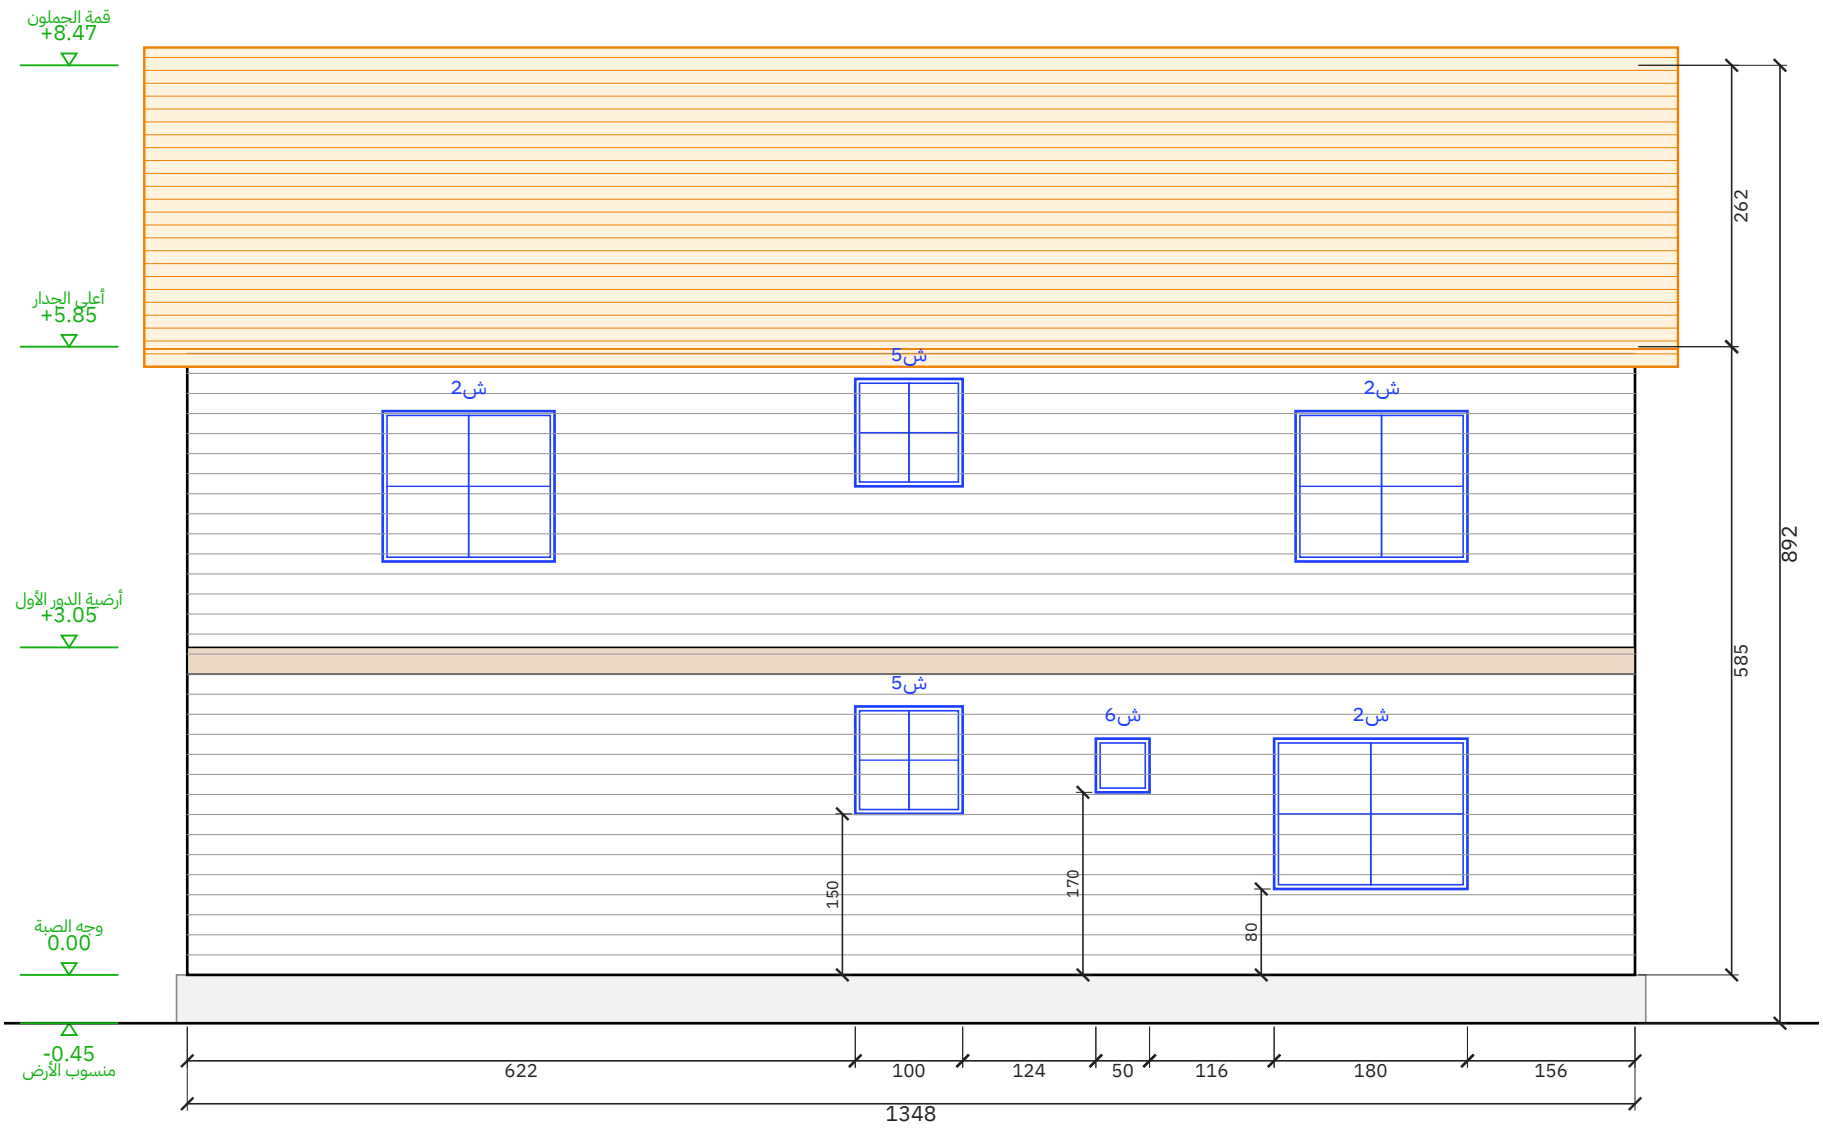

الواجهة الخلفية

مقياس 1:50 | الوحدة: سم

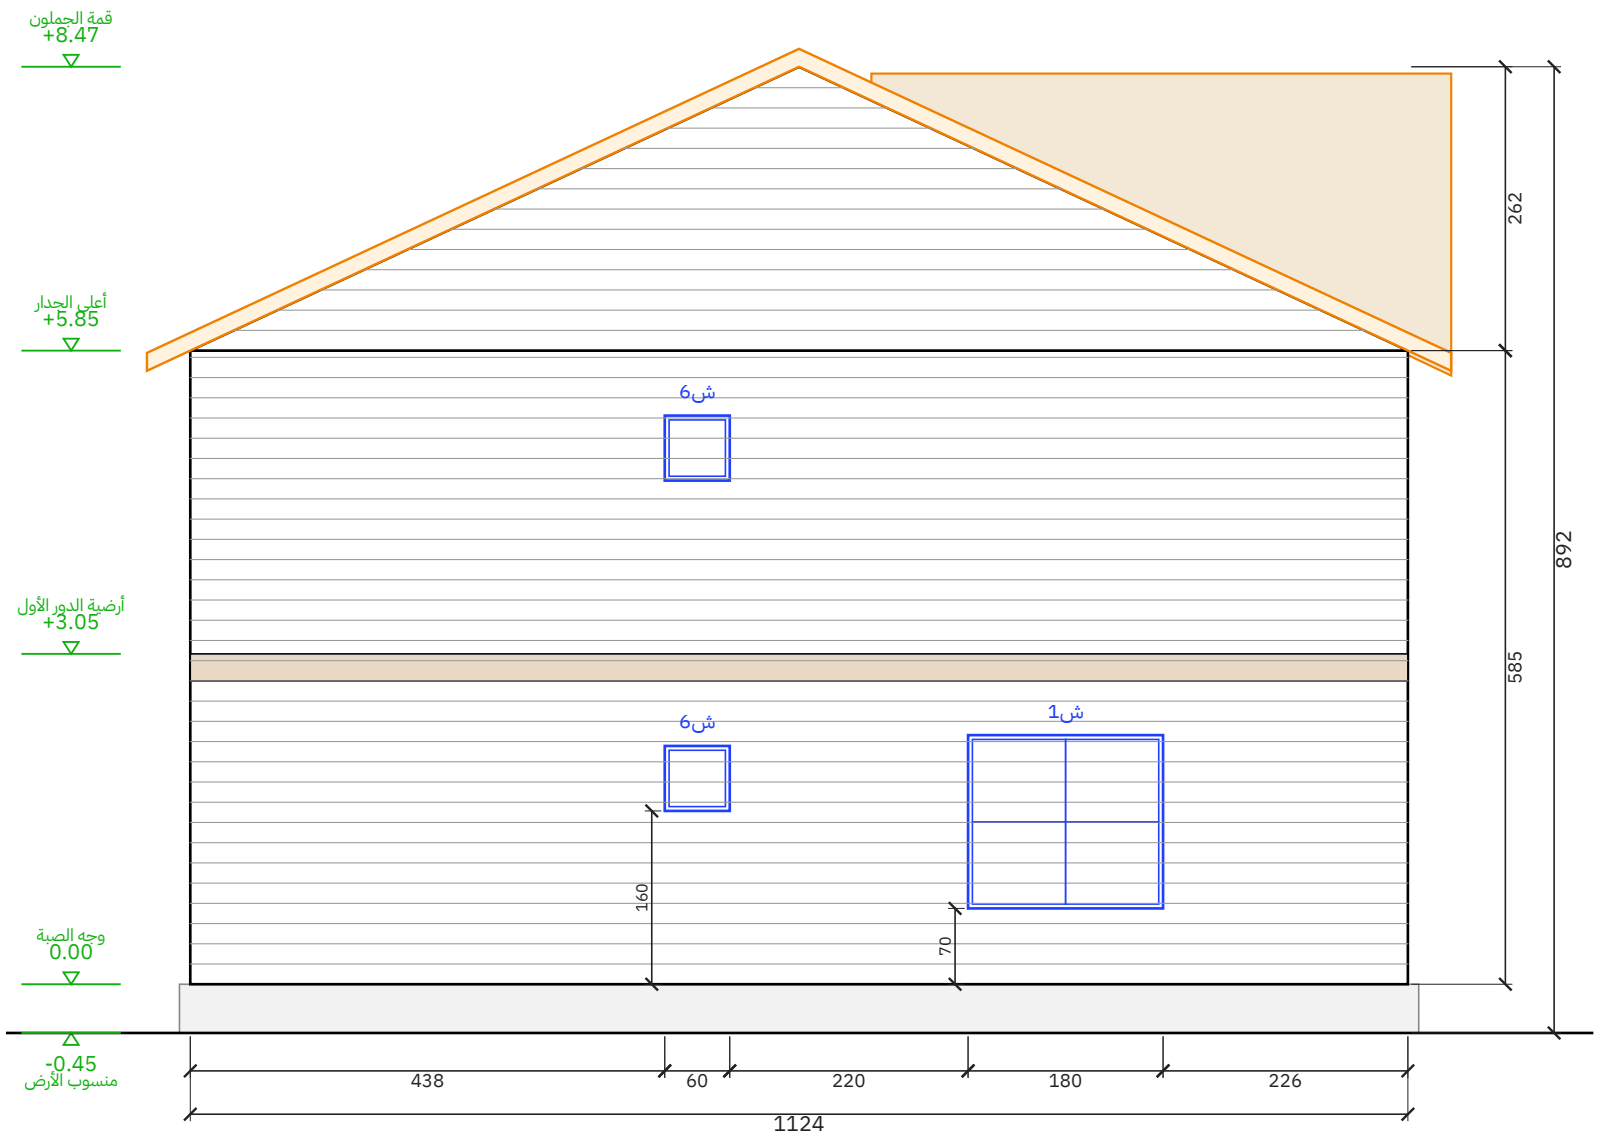


الواجهة الغربية

مقياس 1:50 | الوحدة: سم


المشروع / العميل	عنوان اللوحة	المقياس	التاريخ	رقم اللوحة
مصنع وتد الأخشاب Watad Wood Factory بيت خشب دورين متكامل – استقبال وصالة وأربع غرف – 13.36 × 11.12 م عميل – فيلا دورين	الواجهة الخلفية والواجهة الغربية	1:50	2026-11-01	W-05 (5/24)

قطاع عرضي أ-أ

مقياس 1:50 | الوحدة: سم

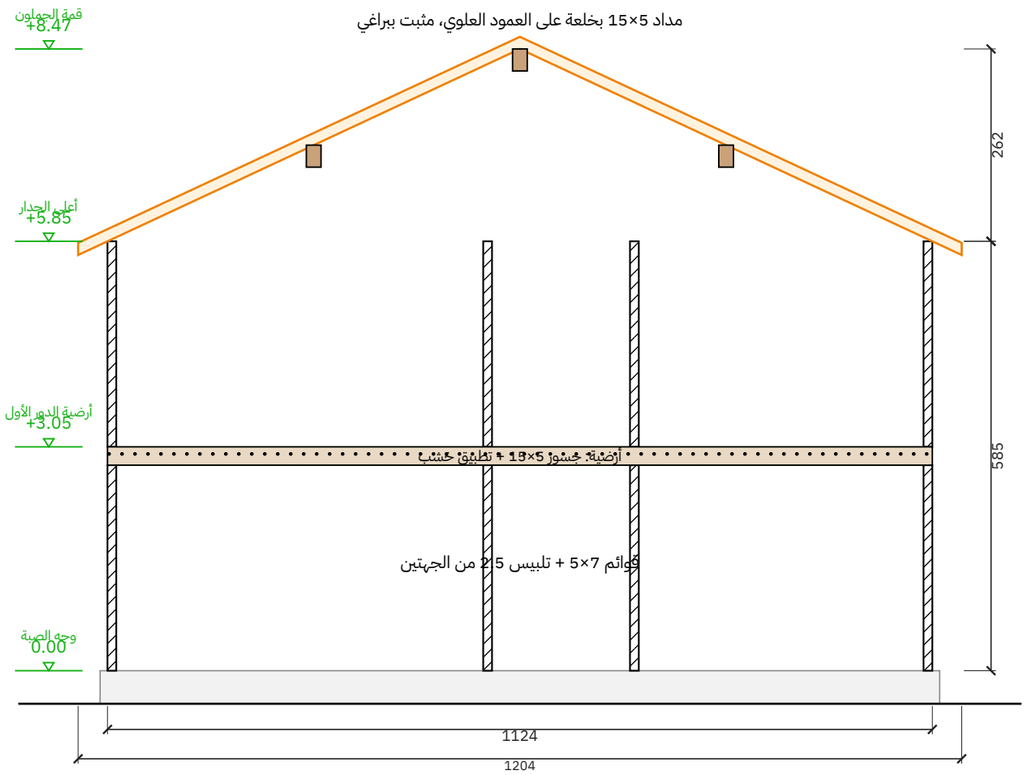


تفصيلة جلوس المداد على العلوي (1:5)

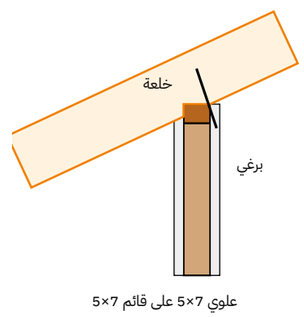

مسقط السقف (جملون)

رفرف 40 سم من كل جهة | مقياس 1:50

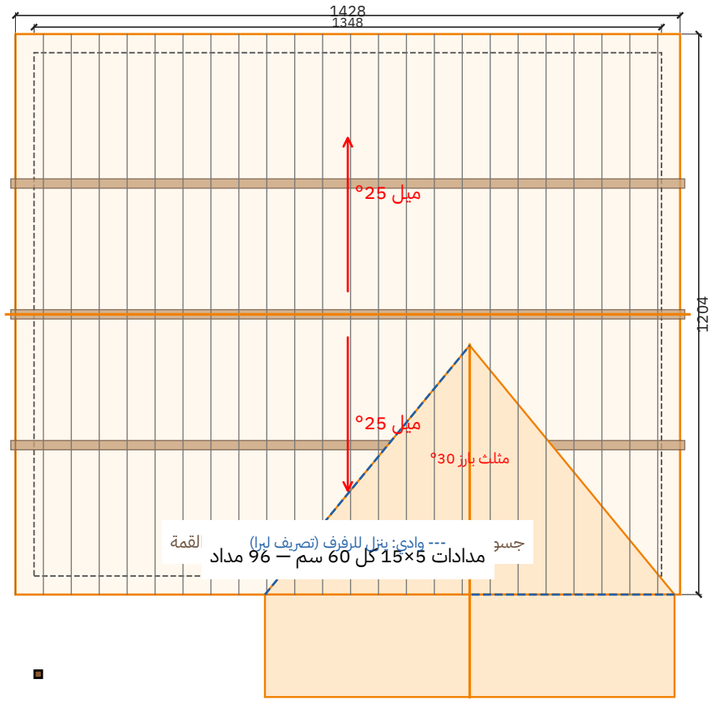

المشروع / العميل	عنوان اللوحة	المقياس	التاريخ	رقم اللوحة
بيت خشب دورين متكامل — استقبال وصالة وأربع غرف — 13.36 × 11.12 م عميل — فيلا دورين	مسقط السقف والقطاع	—	2026-11-01	W-06 (6/24)

مصنع وتد الأخشاب
Watad Wood Factory

جدول مقاسات الأبواب والشبابيك

مقاس الفتحة الصافي في الجدار - الوحدة: سم

الرمز	النوع	العرض (سم)	الارتفاع (سم)	ارتفاع الجلسة (سم)	العدد	الموقع
ب1	باب	100	240	-	1	الأمامية
ب10	باب	76	210	-	3	حمام الأطفال - حمام الرئيسية - غرفة الملابس
ب2	باب مزدوج	140	240	-	1	الأمامية
ب3	باب	420	240	-	1	الأمامية
ب4	باب	90	220	-	2	الاستقبال — الردهة - المطبخ
ب4	باب	80	220	-	1	غرفة الأرضي
ب5	باب	80	220	-	1	ممر الضيوف (المغسلة + دورة المياه + الغرفة)
ب5	باب	70	210	-	1	دورة مياه الضيوف
ب5	باب	76	210	-	2	ملابس الغرفة - حمام الغرفة
ب6	باب	80	210	-	2	المخزن - غرفة العاملة
ب7	باب	300	230	-	1	الأمامية (على الشرفة)
ب8	باب مزدوج	220	230	-	1	الأمامية (على الشرفة)
ب8	باب	420	230	-	1	الأمامية (على الشرفة)
ب9	باب	80	220	-	3	الغرفة الرئيسية - غرفة طفل 1 - غرفة طفل 2
ف1	باب	300	240	-	2	فتحة الصالة 2
ز1	شباك	260	230	20	1	الأمامية
ش1	شباك	180	160	70	3	الشرقية 2 - الغربية
ش2	شباك	180	140	80	1	الخلفية
ش2	شباك	160	140	80	2	الخلفية 2
ش3	شباك	180	100	110	1	الشرقية
ش3	شباك	160	140	80	2	الخلفية 2
ش4	شباك	100	100	120	1	الشرقية
ش5	شباك	100	100	150	2	الخلفية 2
ش6	شباك	50	50	170	1	الخلفية
ش6	شباك	60	60	160	3	الغربية 2 - الشرقية

الإجمالي: أبواب 23 - شبابيك 15

جدول المساحات وبيانات المشروع


بيانات المشروع

البند	البيان
المشروع	بيت خشب دورين متكامل — استقبال وصالة وأربع غرف — 13.36 × 11.12 م
العميل	عميل — فيلا دورين
الموقع	—
الاستخدام	سكن عائلي متكامل
التاريخ	2026-11-01
نظام البناء	هيكل خشب 5×7 + تلبيس 2.5 سم من الجهتين
السقف	جملون 25° — قرميد معدني + 1 مثلث بارز


جدول المساحات

م	الفراغ	الأبعاد (م)	المساحة (م2)
1	أرضي — الاستقبال	5.00 × 5.00	25.00
2	أرضي — الردهة	3.00 × 8.12	24.36
3	أرضي — الصالة	5.00 × 5.00	25.00
4	أرضي — دورة مياه ضيوف	1.88 × 1.88	3.53
5	أرضي — ممر الضيوف	3.00 × 1.88	5.64
6	أرضي — غرفة الأرضي	3.50 × 3.88	13.58
7	أرضي — ملابس	1.38 × 1.28	1.77
8	أرضي — حمام الغرفة	1.38 × 2.48	3.42
9	أرضي — المطبخ	5.00 × 2.88	14.40
10	أرضي — مخزن	2.00 × 2.88	5.76
11	أرضي — غرفة العاملة	2.88 × 2.88	8.29
12	أرضي — الدرج	3.00 × 2.88	8.64
13	أول — الغرفة الرئيسية	5.00 × 5.00	25.00
14	أول — الردهة	3.00 × 8.12	24.36
15	أول — الصالة	5.00 × 5.00	25.00
16	أول — حمام الرئيسية	3.00 × 1.88	5.64
17	أول — ملابس	1.88 × 1.88	3.53
18	أول — غرفة طفل 1	5.00 × 3.88	19.40
19	أول — حمام الأطفال	5.00 × 1.88	9.40
20	أول — غرفة طفل 2	5.00 × 3.88	19.40
	المساحة الصافية الداخلية		271.13
	التراس	**13.48 × 2.20**	**29.66**
	الشرفة	**13.48 × 2.20**	**29.66**
	المساحة الإجمالية المبنية	**13.48 × 11.24 × 2 دور**	**303.03**
	المساحة الكلية (المبنية + التراسات)		**362.34**

تأطير جدار أ-جنوب — الطول 1336 سم، الارتفاع 280 سم

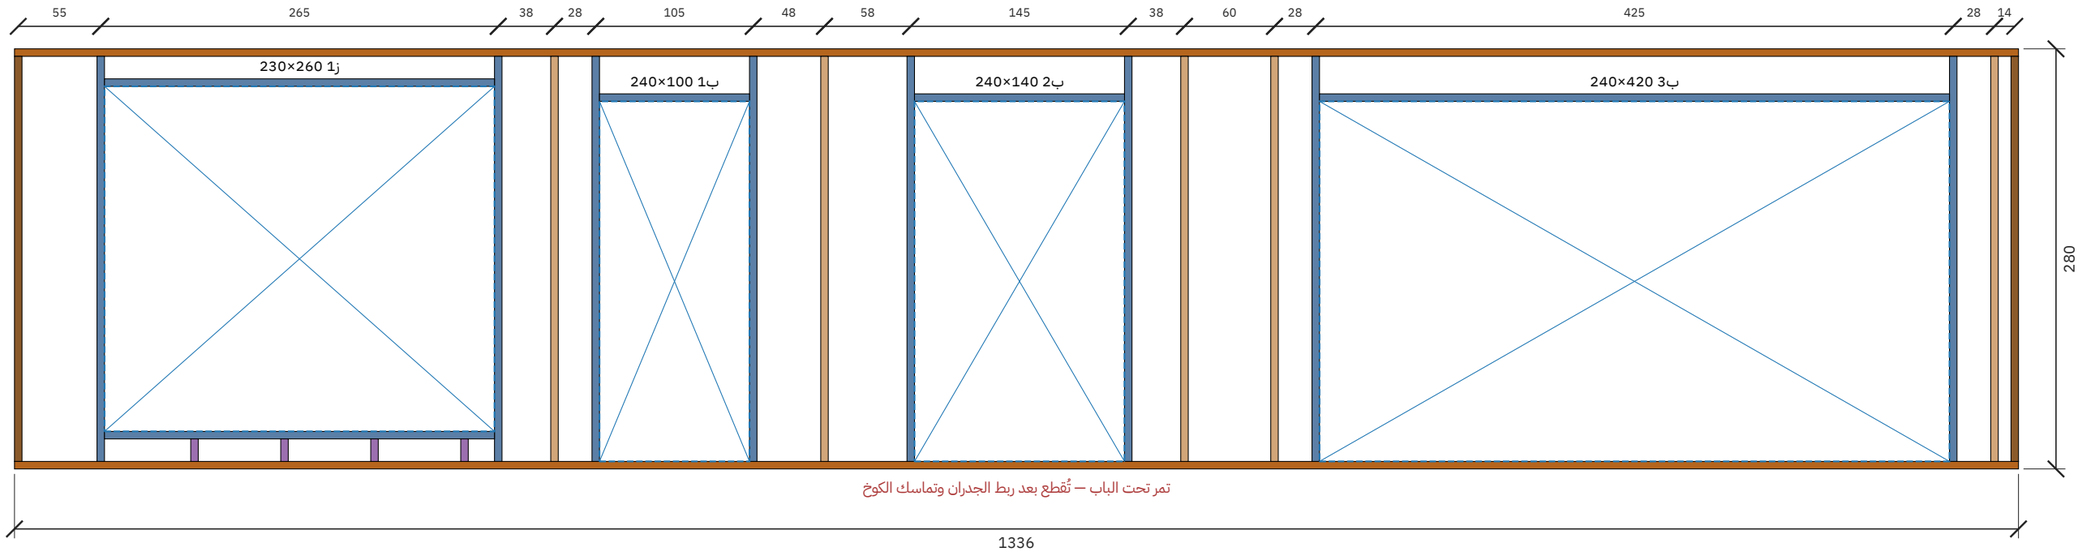

تأطير جدار أ-شرق — الطول 1112 سم، الارتفاع 280 سم

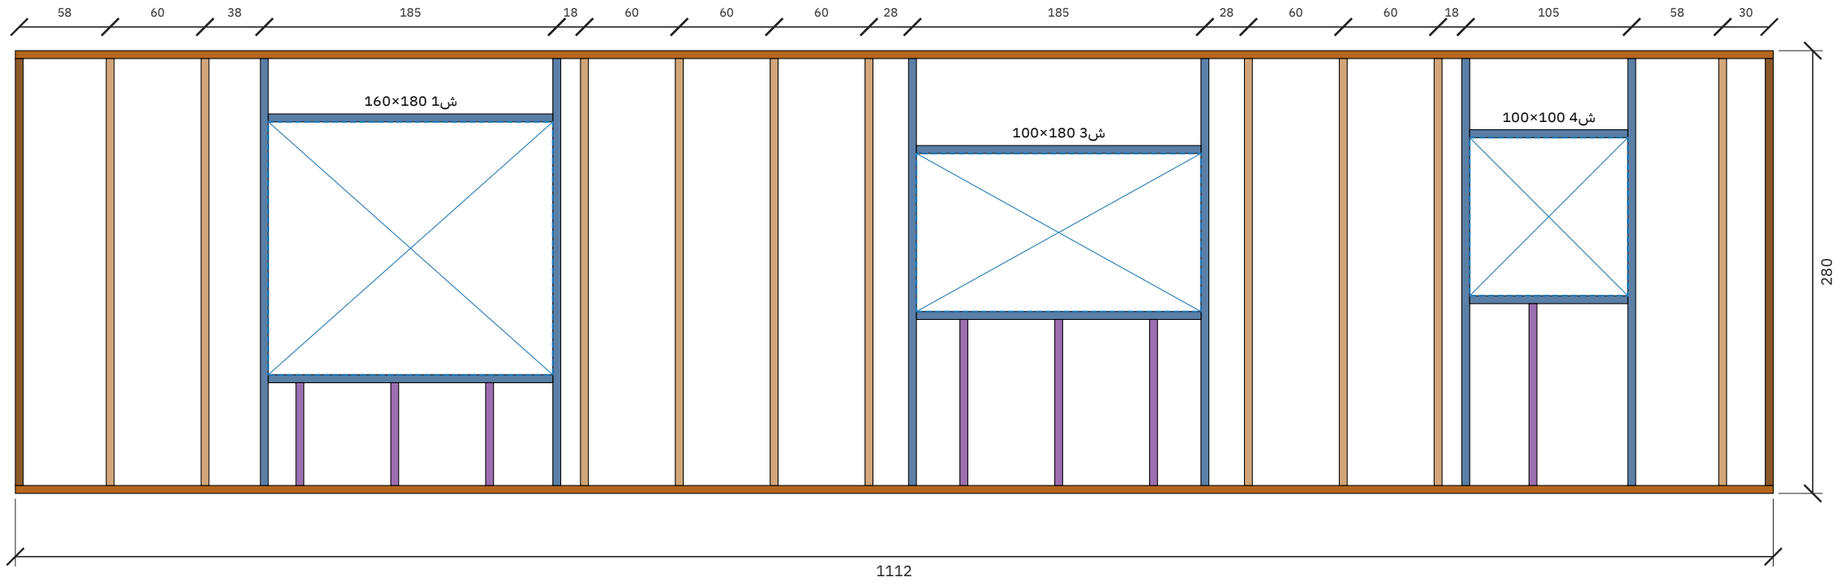


قاعدة سفلية | علوي | عمود | عمود زاوية | جنب فتحة | رأس فتحة | جلسة شباك | عمود قصير


المشروع / العميل	عنوان اللوحة	المقياس	التاريخ	رقم اللوحة
بيت خشب دورين متكامل — استقبال وصالة وأربع غرف — 13.36 × 11.12 م عميل — فيلا دورين	لوحات التأطير (للورشة)	—	2026-11-01	W-09 (9/24)

مصنع وتد الأخشاب
Watad Wood Factory

تأطير جدار أ-شمال — الطول 1336 سم، الارتفاع 280 سم

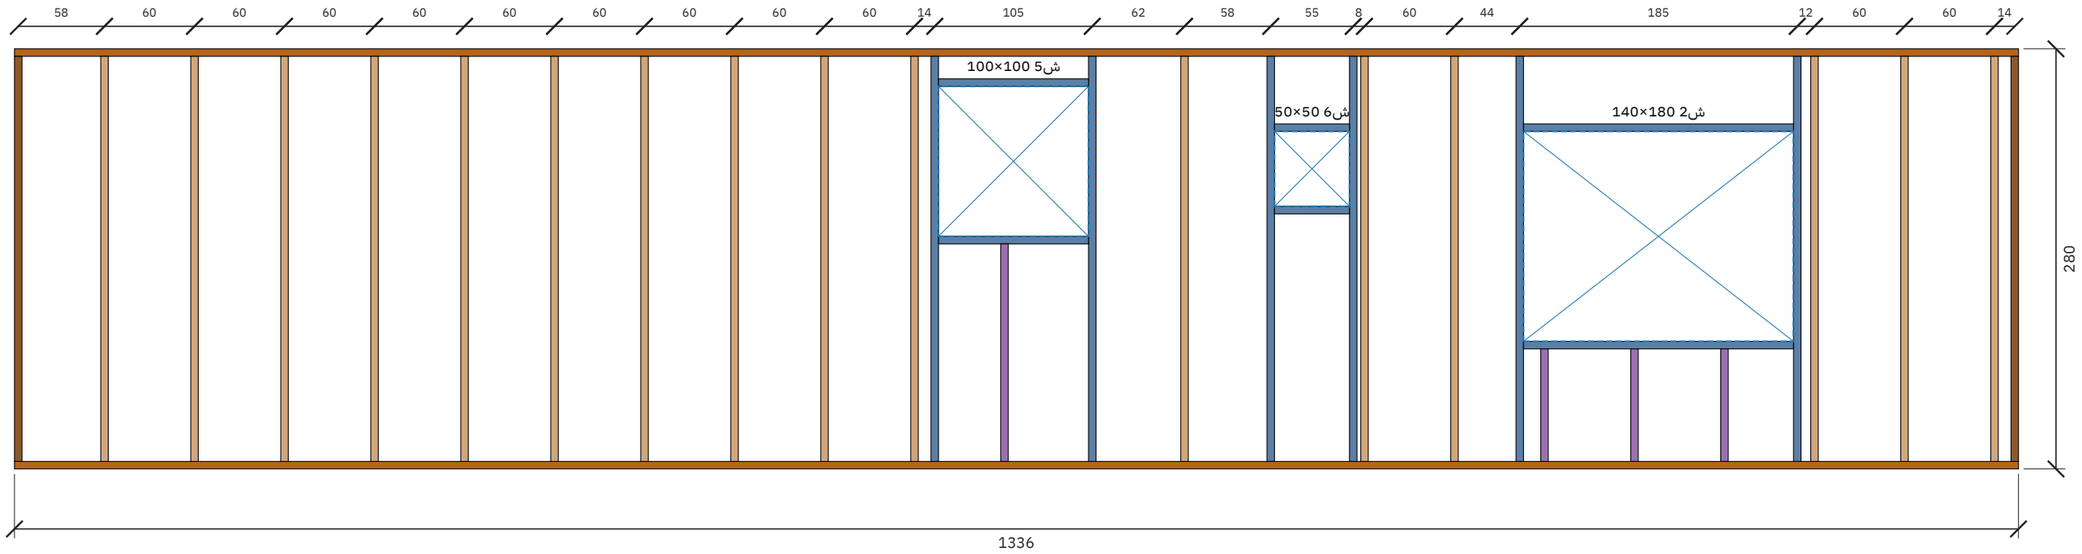

تأطير جدار أ-غرب — الطول 1112 سم، الارتفاع 280 سم

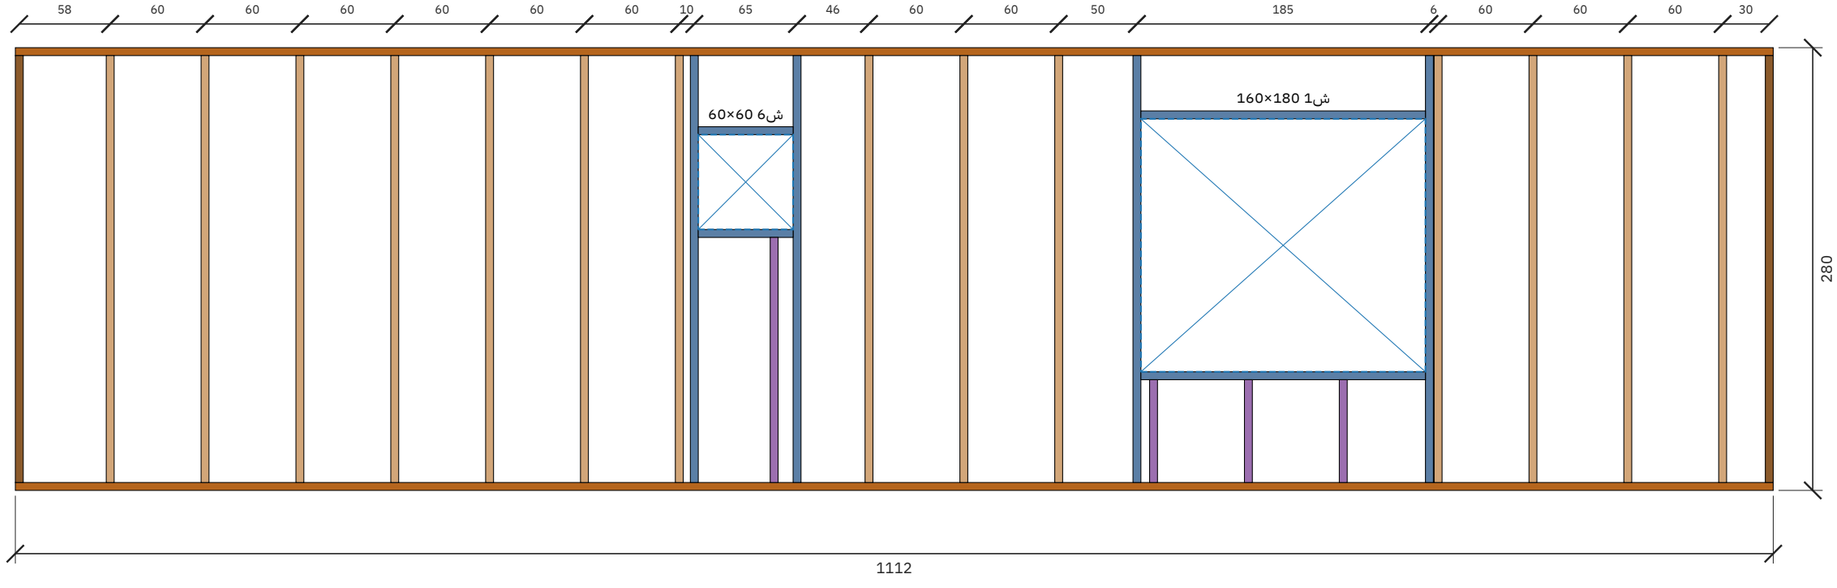


قاعدة سفلية | علوي | عمود | عمود زاوية | جنب فتحة | رأس فتحة | جلسة شباك | عمود قصير


المشروع / العميل	عنوان اللوحة	المقياس	التاريخ	رقم اللوحة
بيت خشب دورين متكامل — استقبال وصالة وأربع غرف — 13.36 × 11.12 م **عميل — فيلا دورين**	**لوحات التأطير (للورشة)**	**—**	**2026-11-01**	**W-10 (10/24)**

مصنع وتد الأخشاب
Watad Wood Factory

تأطير جدار أ-جدار الردهة الغربي — الطول 1112 سم، الارتفاع 280 سم (داخلي)

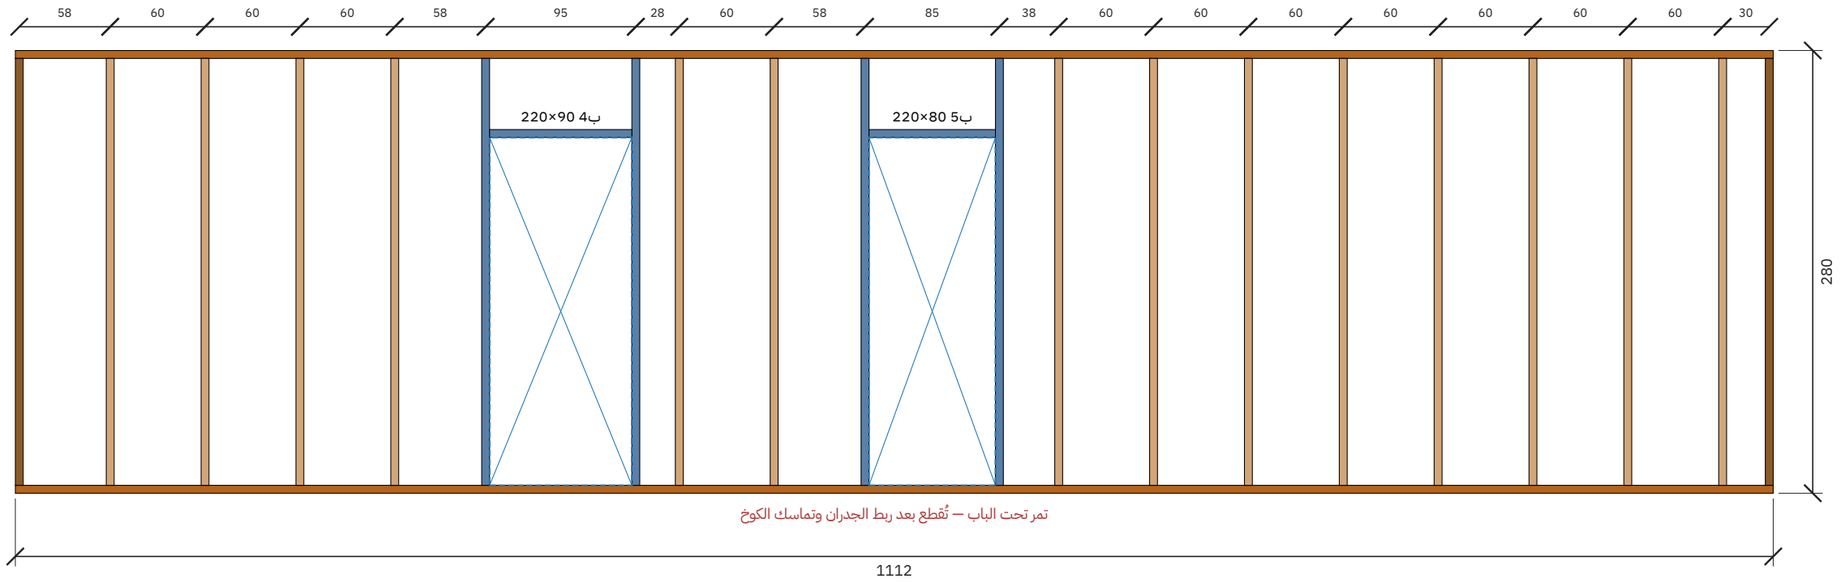

تأطير جدار أ-جدار الردهة الشرقي — الطول 1112 سم، الارتفاع 280 سم (داخلي)

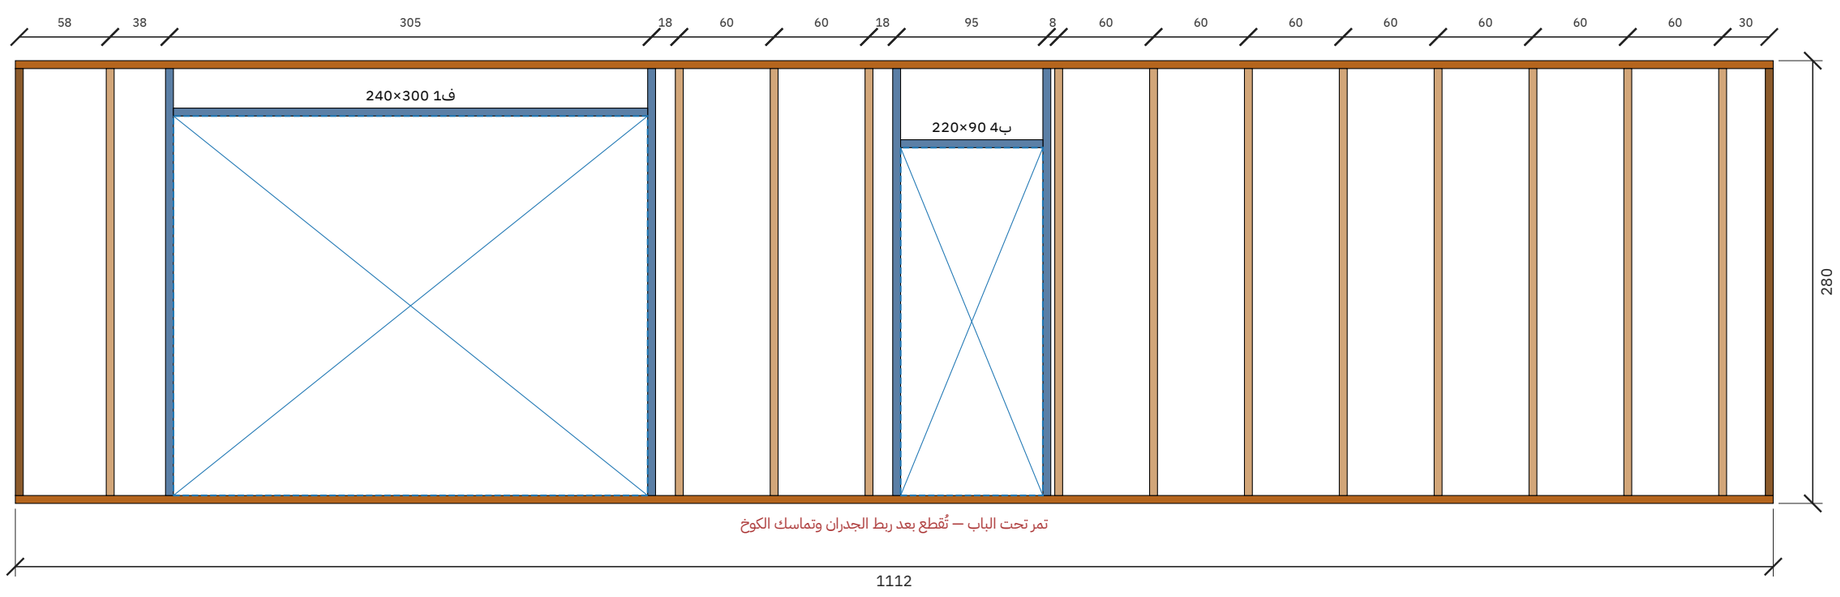


قاعدة سفلية | علوي | عمود | عمود زاوية | جنب فتحة | رأس فتحة | جلسة شباك | عمود قصير


المشروع / العميل	عنوان اللوحة	المقياس	التاريخ	رقم اللوحة
بيت خشب دورين متكامل — استقبال وصالة وأربع غرف — 13.36 × 11.12 م **عميل — فيلا دورين**	**لوحات التأطير (للورشة)**	—	**2026-11-01**	**W-11 (11/24)**

مصنع وتد الأخشاب
Watad Wood Factory

تأطير جدار أ-خلف الاستقبال — الطول 512 سم، الارتفاع 280 سم (داخلي)

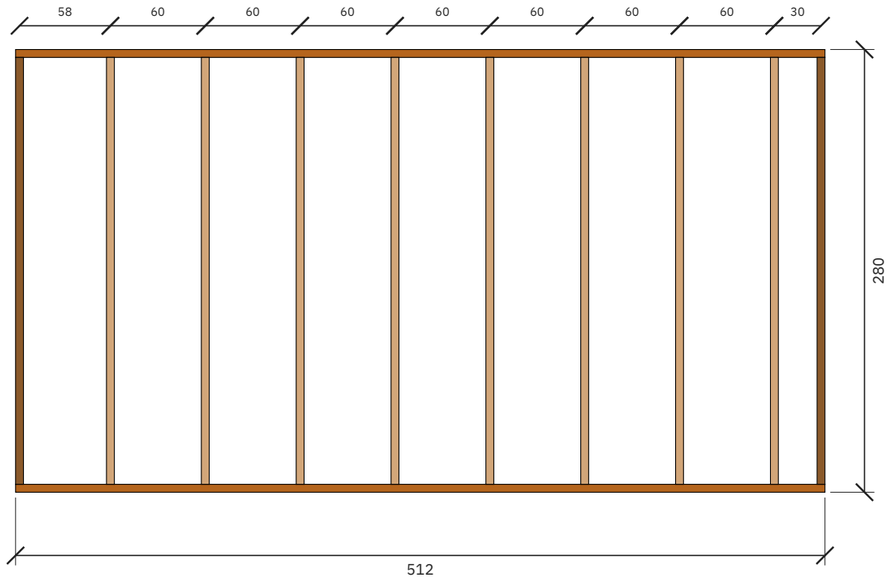

تأطير جدار أ-خلف الصالة — الطول 512 سم، الارتفاع 280 سم (داخلي)

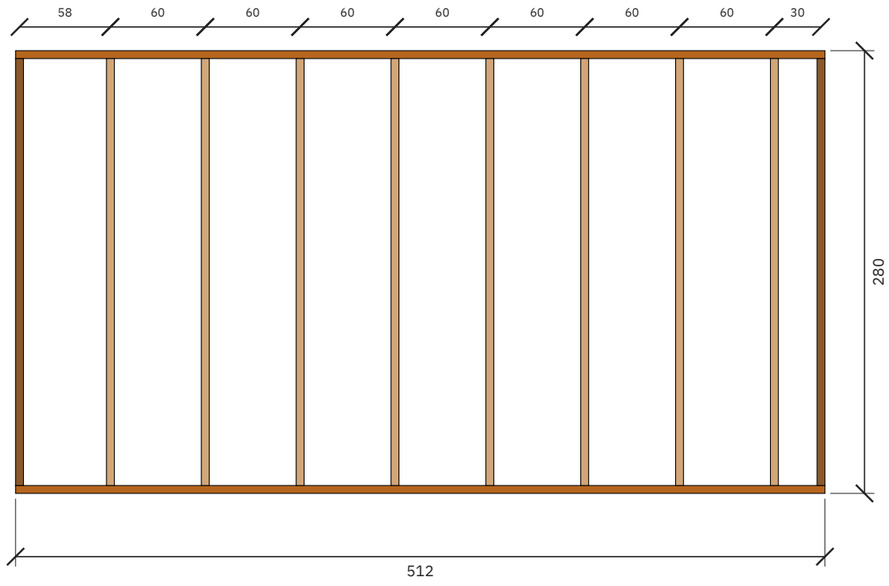


قاعدة سفلية | علوي | عمود | عمود زاوية | جنب فتحة | رأس فتحة | جلسة شباك | عمود قصير


المشروع / العميل	عنوان اللوحة	المقياس	التاريخ	رقم اللوحة
بيت خشب دورين متكامل – استقبال وصالة وأربع غرف – 13.36 × 11.12 م **عميل – فيلا دورين**	**لوحات التأطير (للورشة)**	**–**	**2026-11-01**	**W-12 (12/24)**

مصنع وتد الأخشاب
Watad Wood Factory

تأطير جدار أ-فاصل الغرفة — الطول 512 سم، الارتفاع 280 سم (داخلي)

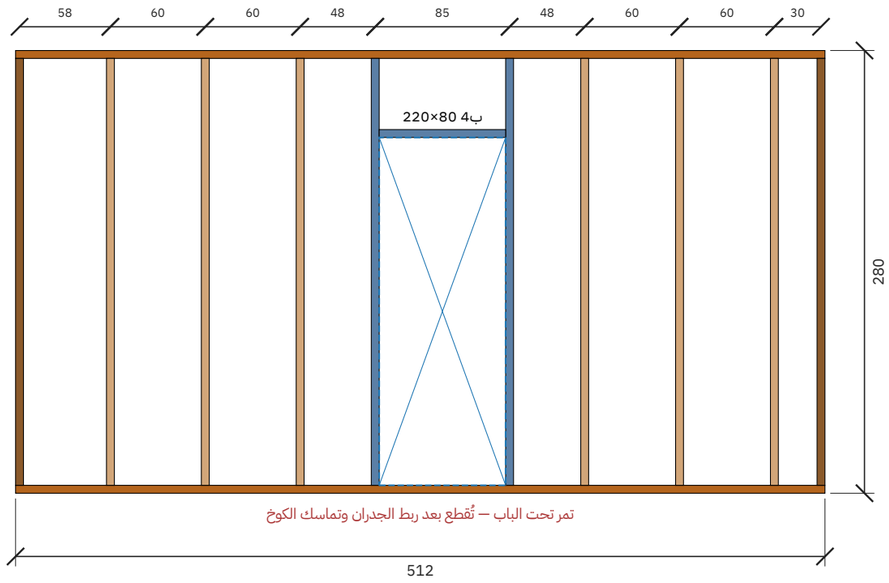

تأطير جدار أ-دورة الضيوف/الممر — الطول 200 سم، الارتفاع 280 سم (داخلي)

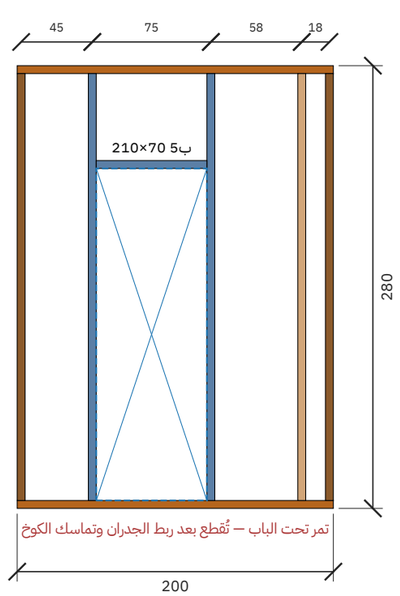


قاعدة سفلية | علوي | عمود | عمود زاوية | جنب فتحة | رأس فتحة | جلسة شباك | عمود قصير


المشروع / العميل	عنوان اللوحة	المقياس	التاريخ	رقم اللوحة
بيت خشب دورين متكامل — استقبال وصالة وأربع غرف — 13.36 × 11.12 م **عميل — فيلا دورين**	**لوحات التأطير (للورشة)**	**—**	**2026-11-01**	**W-13 (13/24)**

مصنع وتد الأخشاب
Watad Wood Factory

تأطير جدار أ-الغرفة/الحمام — الطول 400 سم، الارتفاع 280 سم (داخلي)

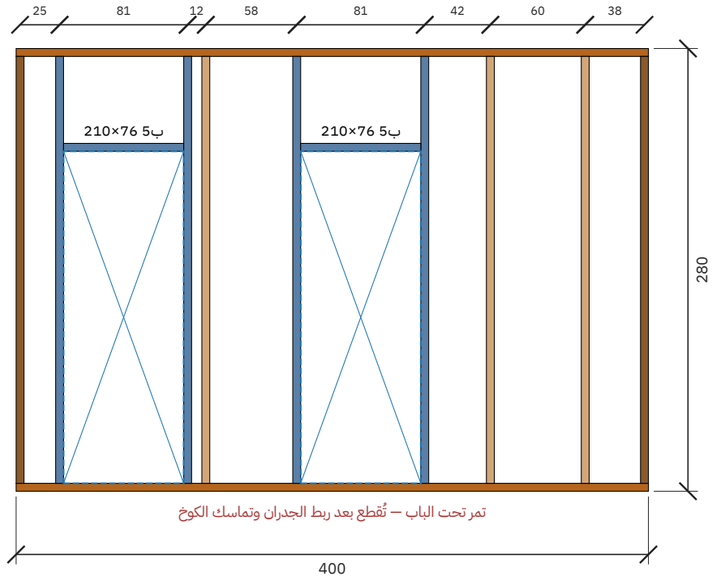


تأطير جدار أ-ملابس/حمام — الطول 150 سم، الارتفاع 280 سم (داخلي)

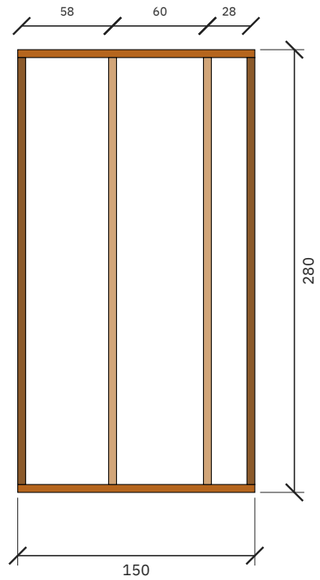


قاعدة سفلية | علوي | عمود | عمود زاوية | جنب فتحة | رأس فتحة | جلسة شباك | عمود قصير

مصنع وتد الأخشاب Watad Wood Factory	المشروع / العميل بيت خشب دورين متكامل — استقبال وصالة وأربع غرف — 13.36 × 11.12 م عميل — فيلا دورين	عنوان اللوحة لوحات التأطير (للورشة)	المقياس —	التاريخ 2026-11-01	رقم اللوحة W-14 (14/24)

تأطير جدار أ-خلف المطبخ — الطول 512 سم، الارتفاع 280 سم (داخلي)

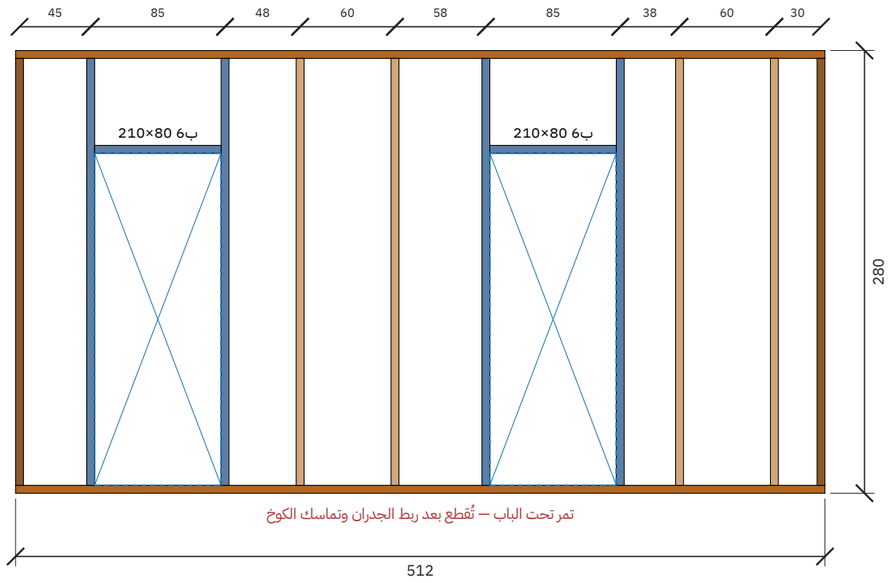

تأطير جدار أ-المخزن/العاملة — الطول 300 سم، الارتفاع 280 سم (داخلي)

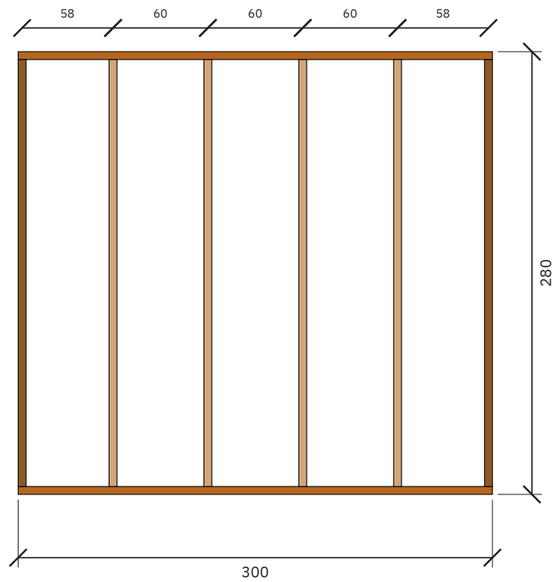


قاعدة سفلية | علوي | عمود | عمود زاوية | جنب فتحة | رأس فتحة | جلسة شباك | عمود قصير


المشروع / العميل	عنوان اللوحة	المقياس	التاريخ	رقم اللوحة
بيت خشب دورين متكامل — استقبال وصالة وأربع غرف — 13.36 × 11.12 م عميل — فيلا دورين	لوحات التأطير (للورشة)	—	2026-11-01	W-15 (15/24)

مصنع وتد الأخشاب
Watad Wood Factory

تأطير جدار ب-جنوب — الطول 1336 سم، الارتفاع 280 سم

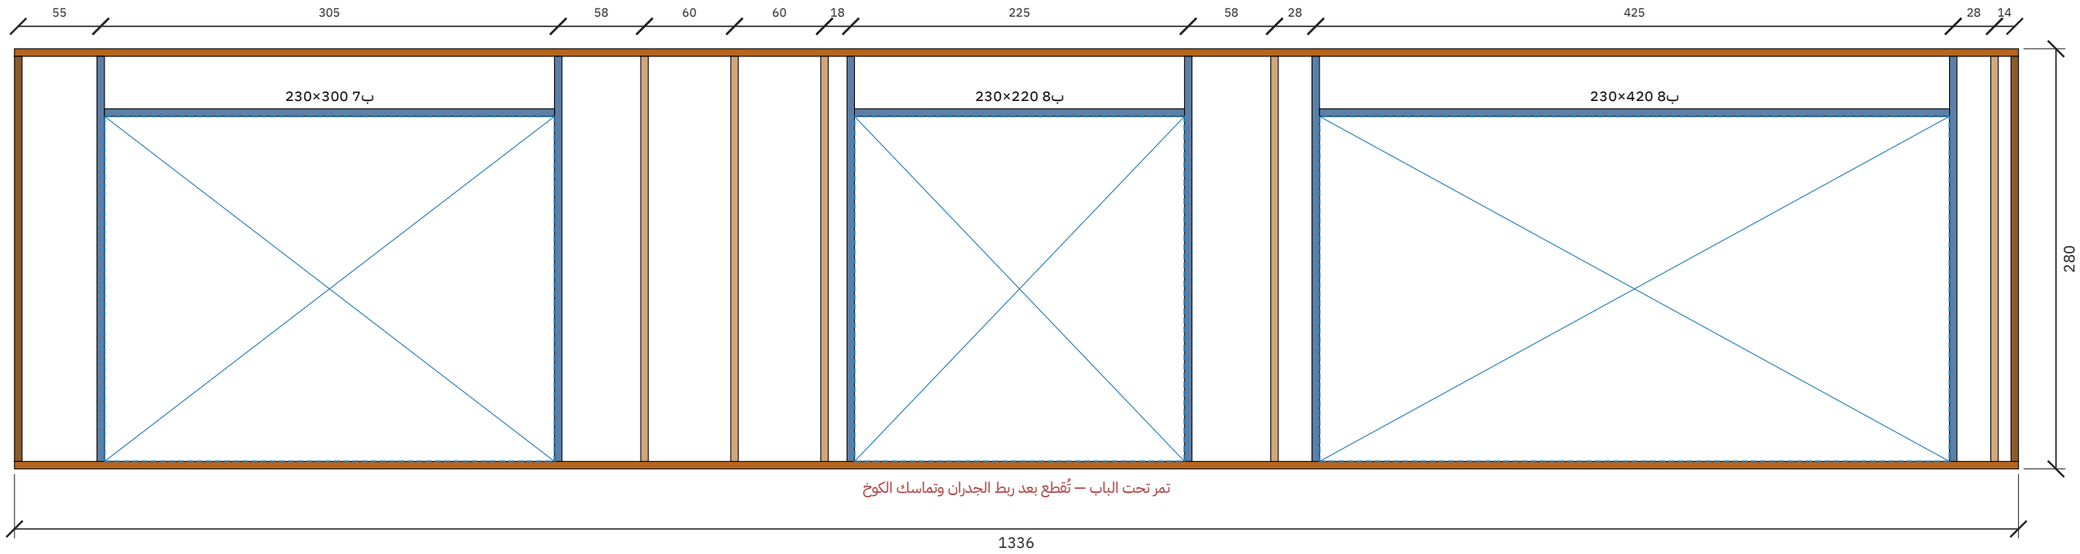

تأطير جدار ب-شرق — الطول 1112 سم، الارتفاع 280 سم

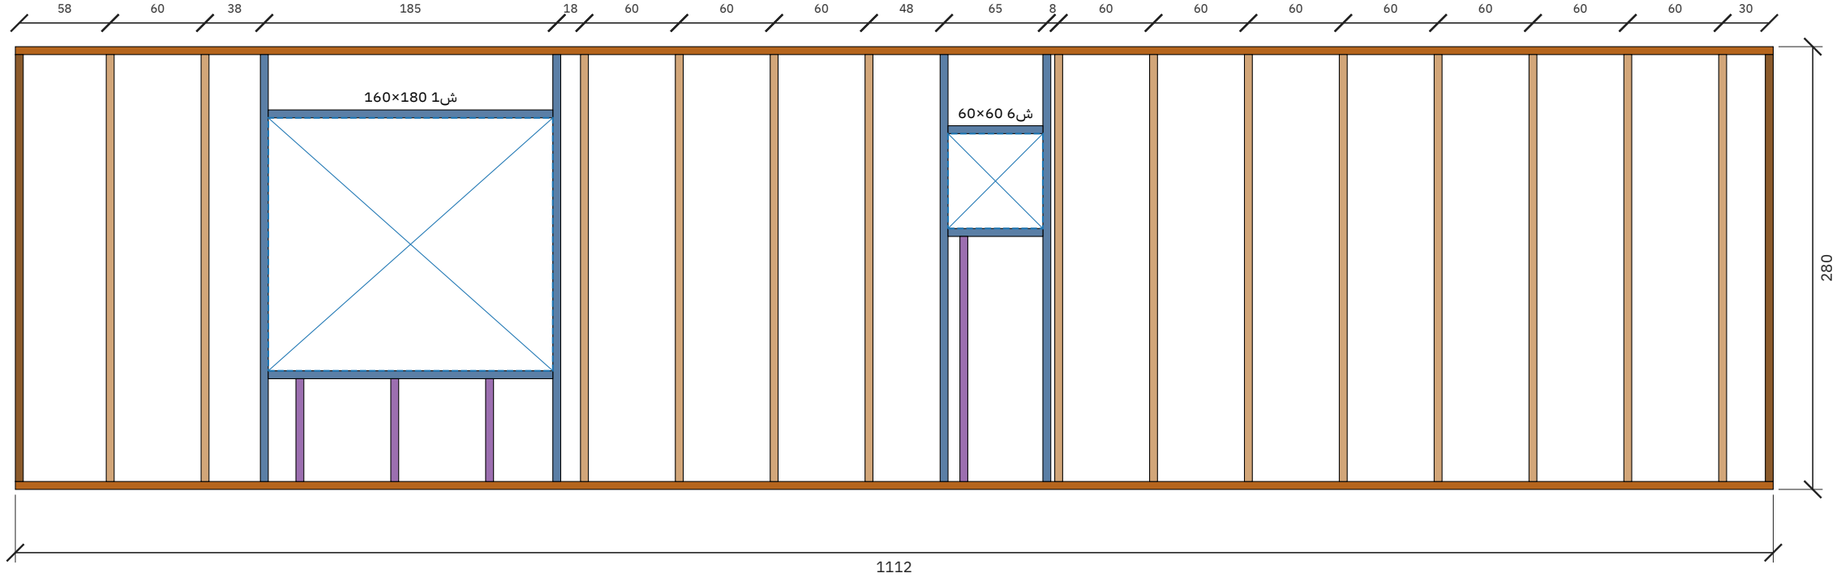


قاعدة سفلية — علوي — عمود — عمود زاوية — جنب فتحة — رأس فتحة — جلسة شباك — عمود قصير


المشروع / العميل	عنوان اللوحة	المقياس	التاريخ	رقم اللوحة
بيت خشب دورين متكامل — استقبال وصالة وأربع غرف — 13.36 × 11.12 م عميل — فيلا دورين	لوحات التأطير (للورشة)	—	2026-11-01	W-16 (16/24)

مصنع وتد الأخشاب
Watad Wood Factory

تأطير جدار ب-شمال — الطول 1336 سم، الارتفاع 280 سم

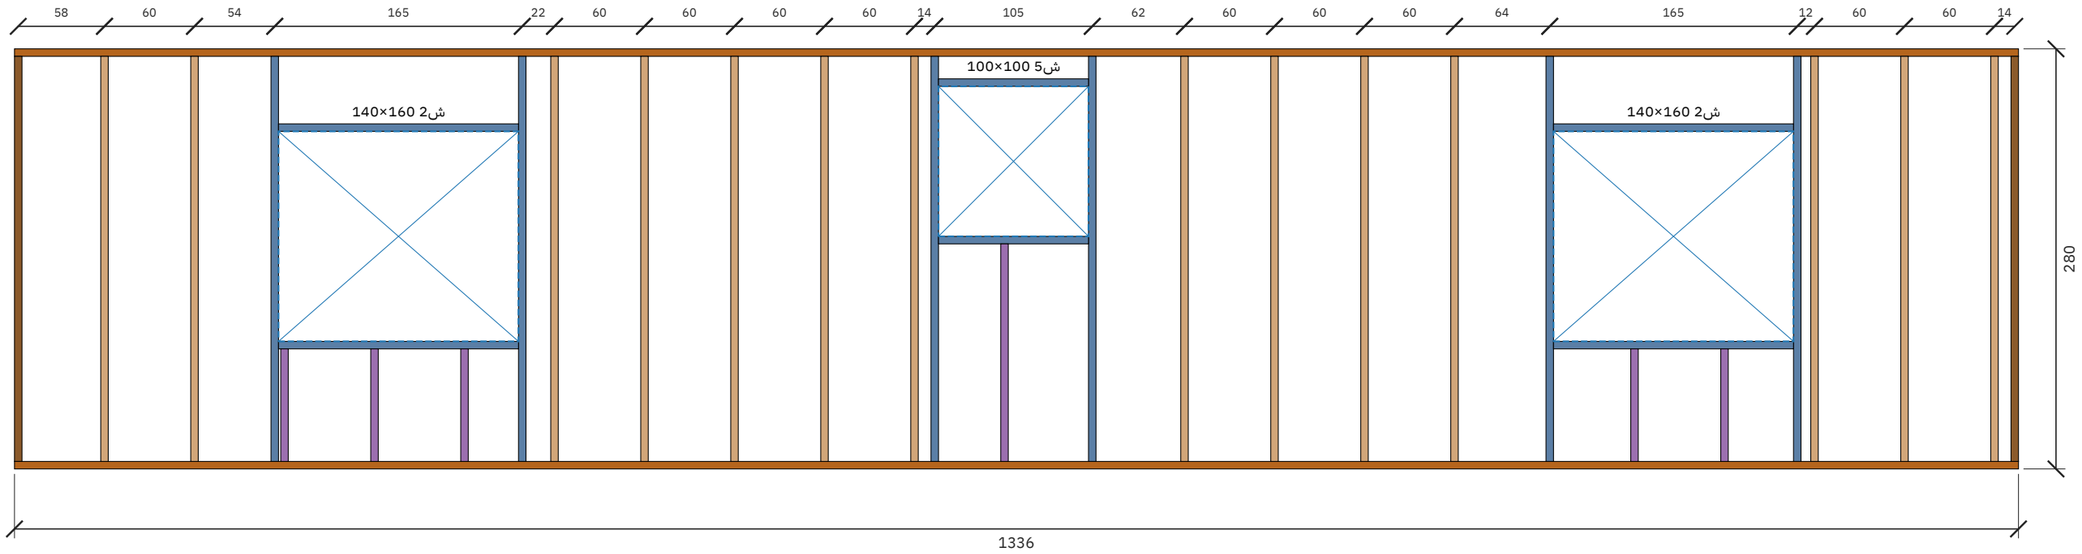

تأطير جدار ب-غرب — الطول 1112 سم، الارتفاع 280 سم

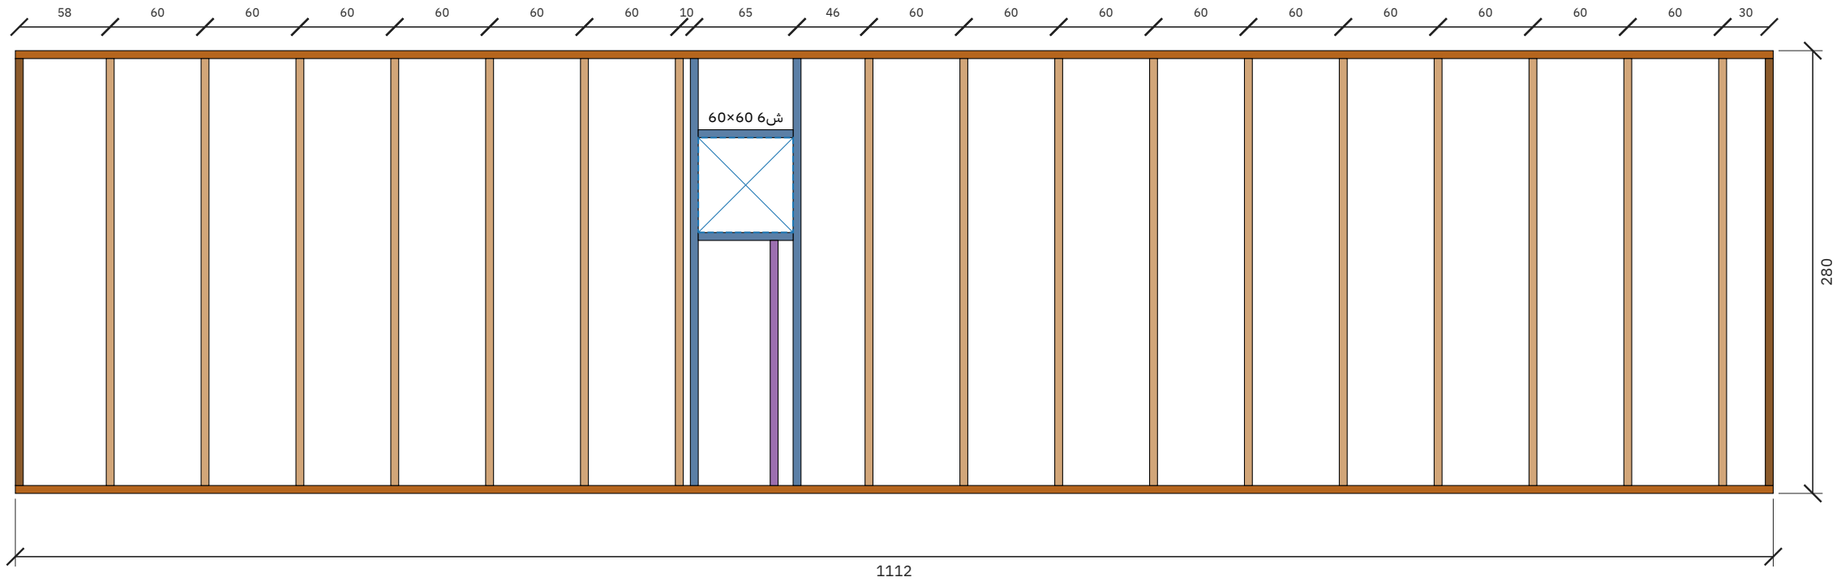


قاعدة سفلية | علوي | عمود | عمود زاوية | جنب فتحة | رأس فتحة | جلسة شباك | عمود قصير


المشروع / العميل	عنوان اللوحة	المقياس	التاريخ	رقم اللوحة
بيت خشب دورين متكامل – استقبال وصالة وأربع غرف – 13.36 × 11.12 م **عميل – فيلا دورين**	**لوحات التأطير (للورشة)**	**–**	**2026-11-01**	**W-17 (17/24)**

مصنع وتد الأخشاب
Watad Wood Factory

تأطير جدار ب-جدار الردهة الغربي — الطول 1112 سم، الارتفاع 280 سم (داخلي)

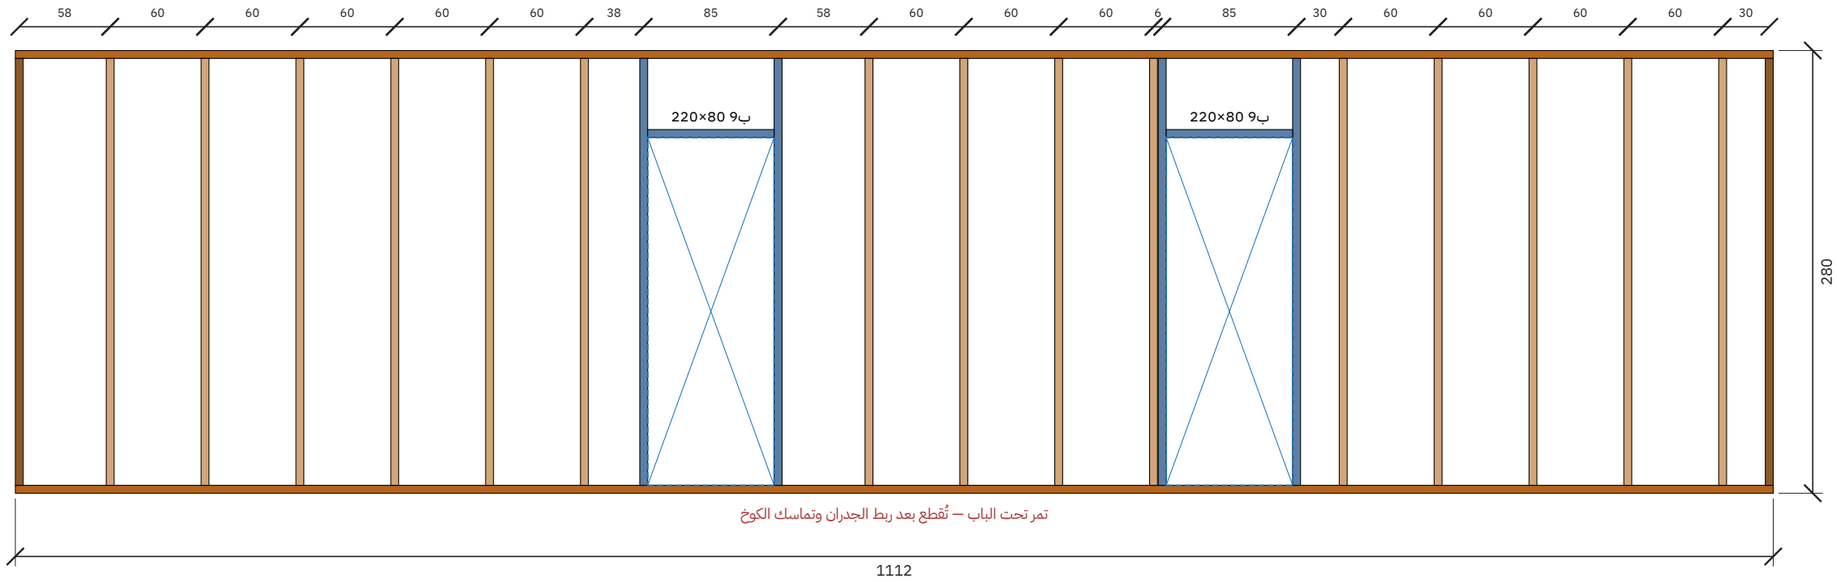

تأطير جدار ب-جدار الردهة الشرقي — الطول 1112 سم، الارتفاع 280 سم (داخلي)

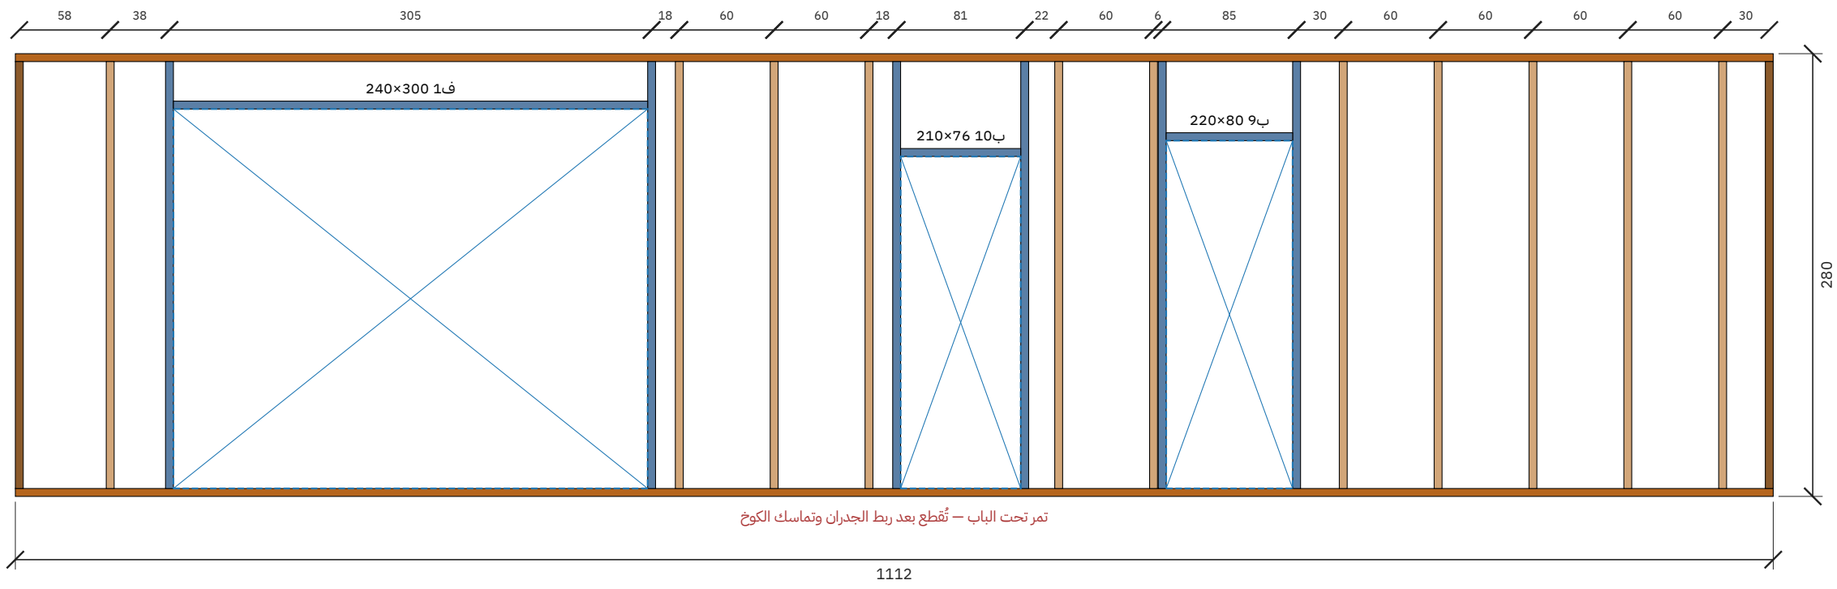


قاعدة سفلية | علوي | عمود | عمود زاوية | جنب فتحة | رأس فتحة | جلسة شباك | عمود قصير


المشروع / العميل	عنوان اللوحة	المقياس	التاريخ	رقم اللوحة
بيت خشب دورين متكامل — استقبال وصالة وأربع غرف — 13.36 × 11.12 م عميل — فيلا دورين	لوحات التأطير (للورشة)	—	2026-11-01	W-18 (18/24)

مصنع وتد الأخشاب
Watad Wood Factory

تأطير جدار ب-خلف الرئيسية — الطول 512 سم، الارتفاع 280 سم (داخلي)

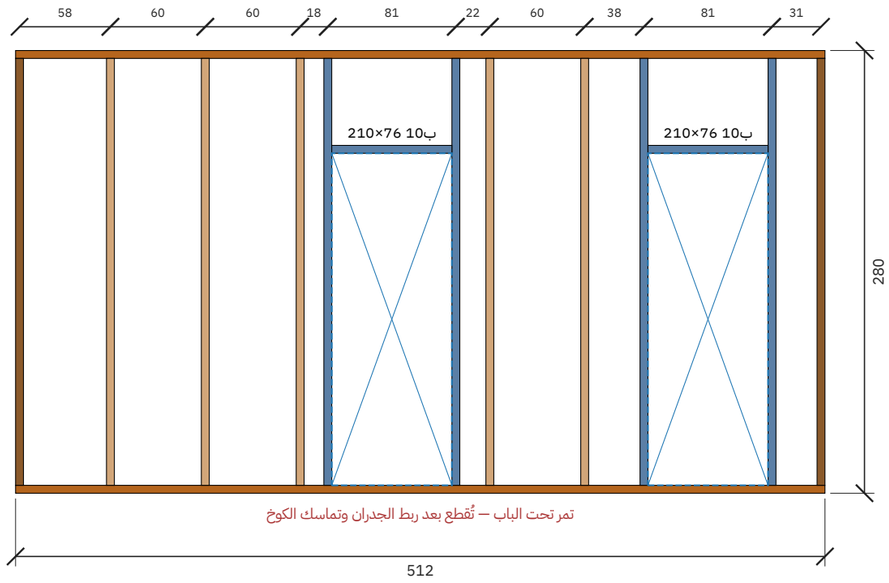

تأطير جدار ب-حمام/ملابس — الطول 200 سم، الارتفاع 280 سم (داخلي)

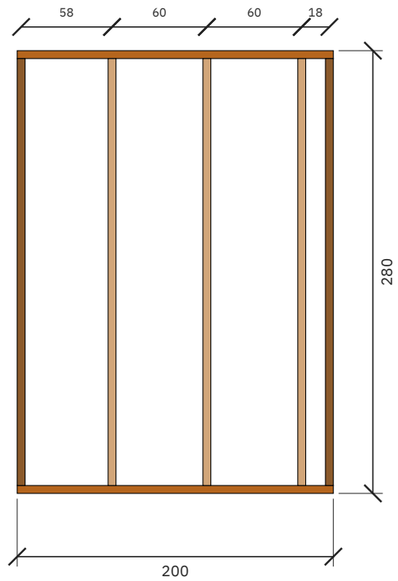


عمود قصير | جلسة شباك | رأس فتحة | جنب فتحة | عمود زاوية | عمود | علوي | قاعدة سفلية


المشروع / العميل	عنوان اللوحة	المقياس	التاريخ	رقم اللوحة
بيت خشب دورين متكامل — استقبال وصالة وأربع غرف — 13.36 × 11.12 م **عميل — فيلا دورين**	**لوحات التأطير (للورشة)**	**—**	**2026-11-01**	**W-19 (19/24)**

مصنع وتد الأخشاب
Watad Wood Factory

تأطير جدار ب-خلف الحمام الرئيسي — الطول 512 سم، الارتفاع 280 سم (داخلي)

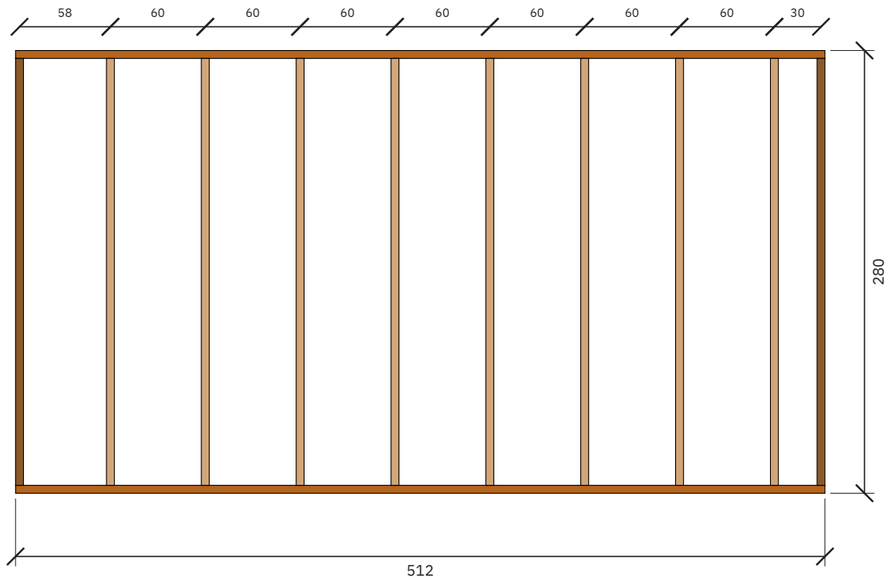

تأطير جدار ب-خلف الصالة — الطول 512 سم، الارتفاع 280 سم (داخلي)

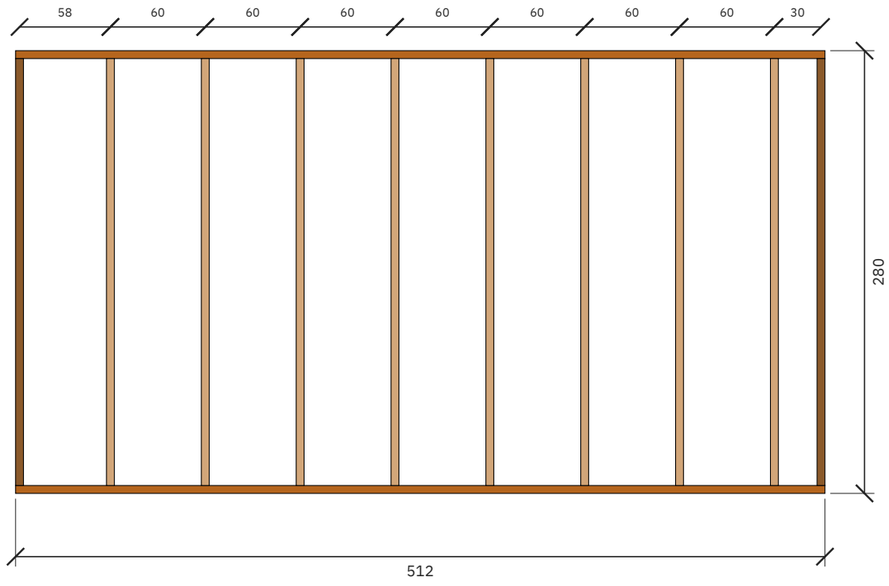


قاعدة سفلية | علوي | عمود | عمود زاوية | جنب فتحة | رأس فتحة | جلسة شباك | عمود قصير

المشروع / العميل	عنوان اللوحة	المقياس	التاريخ	رقم اللوحة
بيت خشب دورين متكامل – استقبال وصالة وأربع غرف – 13.36 × 11.12 م **عميل – فيلا دورين**	**لوحات التأطير (للورشة)**	**–**	**2026-11-01**	**W-20 (20/24)**

مصنع وتد الأخشاب
Watad Wood Factory

تأطير جدار ب-خلف حمام الأطفال — الطول 512 سم، الارتفاع 280 سم (داخلي)

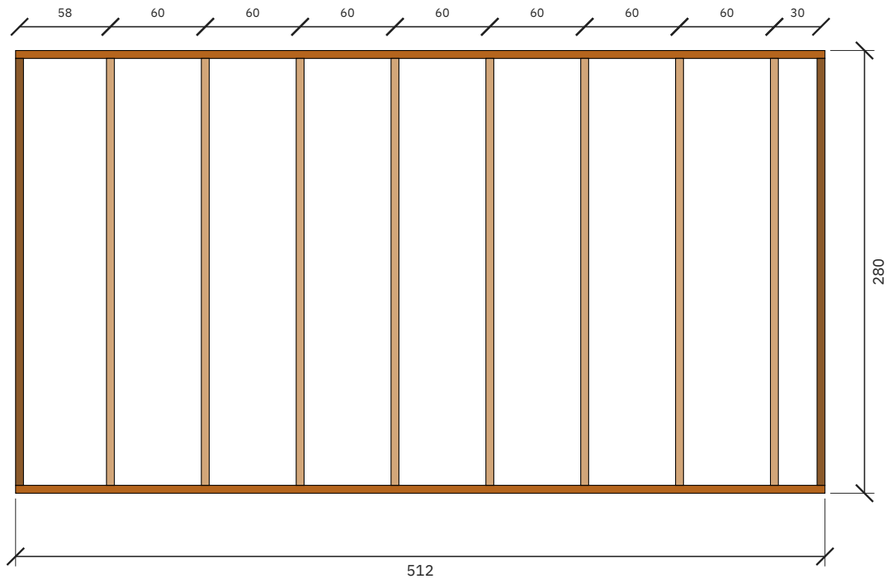

عمود قصير
جلسة شباك
رأس فتحة
جنب فتحة
عمود زاوية
عمود
علوي
قاعدة سفلية

مصنع وتد الأخشاب Watad Wood Factory	المشروع / العميل بيت خشب دورين متكامل — استقبال وصالة وأربع غرف — 13.36 × 11.12 م عميل — فيلا دورين	عنوان اللوحة لوحات التأطير (للورشة)	المقياس —	التاريخ 2026-11-01	رقم اللوحة W-21 (21/24)

جدول الكميات وخطة تقطيع الطبليات

البند	القيمة
الارتفاع المطلوب / المعتمد	280 / 280 سم
السقف	جملون 25° — أعلى نقطة 847 سم من وجه الصبة
المدادات 5×15	96 مداد (24 خط × قطعتين موصولة فوق الجسر الحامل بتراكب 60 سم) × حتى 387 سم — من طبلية 480
طبليات الطريقة الأولى (مداد + عمود)	96 طبلية × 480 سم
طبليات الطريقة الثانية (3 أعمدة)	122 طبلية × 320 سم
مدادات أرضية الدور العلوي 5×15 كل 60 سم	114 مداد — 160سم×19، 172سم×19، 210سم×19، 222سم×19، 310سم×19، 322سم×19 (طبلية 480 بالطريقة الأولى)
مدادات المثلث البارز (S) 30°	18 مداد حتى 312 سم (طبلية 320) + 2 مداد وادي 738 سم — وصلة
إجمالي الطبليات 5×22.5	352
إجمالي قطع 5×7	474
قائمة تقطيع 5×7	1336سم×8 | 1112سم×16 | 512سم×16 | 420سم×2 | 400سم×2 | 300سم×5 | 270سم×341 | 260سم×2 | 220سم×1
	200سم×4 | 180سم×10 | 160سم×4 | 155سم×3 | 150سم×2 | 145سم×2 | 140سم×1 | 115سم×1 | 105سم×3
ألواح تلبيس 2.5 سم	1160 لوح × 400 سم (مجموع الصفوف 4110.4 م، 50 وجه)
أسمنت بورد 12 مم (122×244)	84 لوح (داخل دورات المياه)
العزل	616 لوح فوم صخري 80

جدول الكميات وخطة تقطيع الطبليات

البند	القيمة
الصبة	يجهزها العميل — 20 سم، مفرغة تحت دورات المياه

مراجعة التصميم مقابل قواعد المصنع

النوع	البند	التفاصيل	المقترح
ملاحظة	حمام الأطفال غير مكدّس	دورة المياه العلوية ليست فوق دورة مياه أرضية — تحتاج خط صرف خارجي مستقل على الجدار.	يُفضّل تكديس الحمامات فوق بعض (قاعدة المصنع).
ملاحظة	بحر المدادات	أطول بحر بدون جدار داخلي يحمل المداد: جهة أ: 562 سم، جهة ب: 562 سم. يحتاج رقم المصنع لأقصى بحر مسموح لتحديد المدادات اللي تُقوّى 20×5.	
ملاحظة	الصبة والدرج	ارتفاع الصبة 45 سم ← 3 درجة بقائمة 15.0 سم.	
ملاحظة	مناسيب رؤوس الفتحات	رؤوس الأبواب والشبابيك على مناسيب مختلفة: 210، 220، 230، 240، 250 سم.	
تنبيه	مداد الوادي	مداد الوادي 738 سم أطول من الطبلية — يُوصل بوصلة مثبتة فوق جدار/دعامة	وصلة مزدوجة 5×15 مع براغي، ومرتكزة على جدار أو دعامة 5×7.
سؤال	يحتاج تأكيد	أقصى بحر للمداد بدون جدار داخلي قبل إضافة تقوية 5×7 (مداد 20×5)؟	
سؤال	يحتاج تأكيد	التغطية الصافية للوح التلبيس بعد التعشيق (مستنتجة مؤقتاً 18.67 سم من 280/15)؟	
سؤال	يحتاج تأكيد	هل يوضع أعمدة قصيرة فوق رأس الشباك/الباب إلى العلوي؟	
سؤال	يحتاج تأكيد	مكان الوصلة في القاعدة والعلوي إذا الجدار أطول من الطبلية؟	