
المسقط الأفقي مع الفرش — الدور الأرضي


الأبعاد بالسنتيمتر - الجدران: قوائم 7×5 + تلبيس 2.5 من الجهتين (12 سم) | منسوب الأرضية +0.00

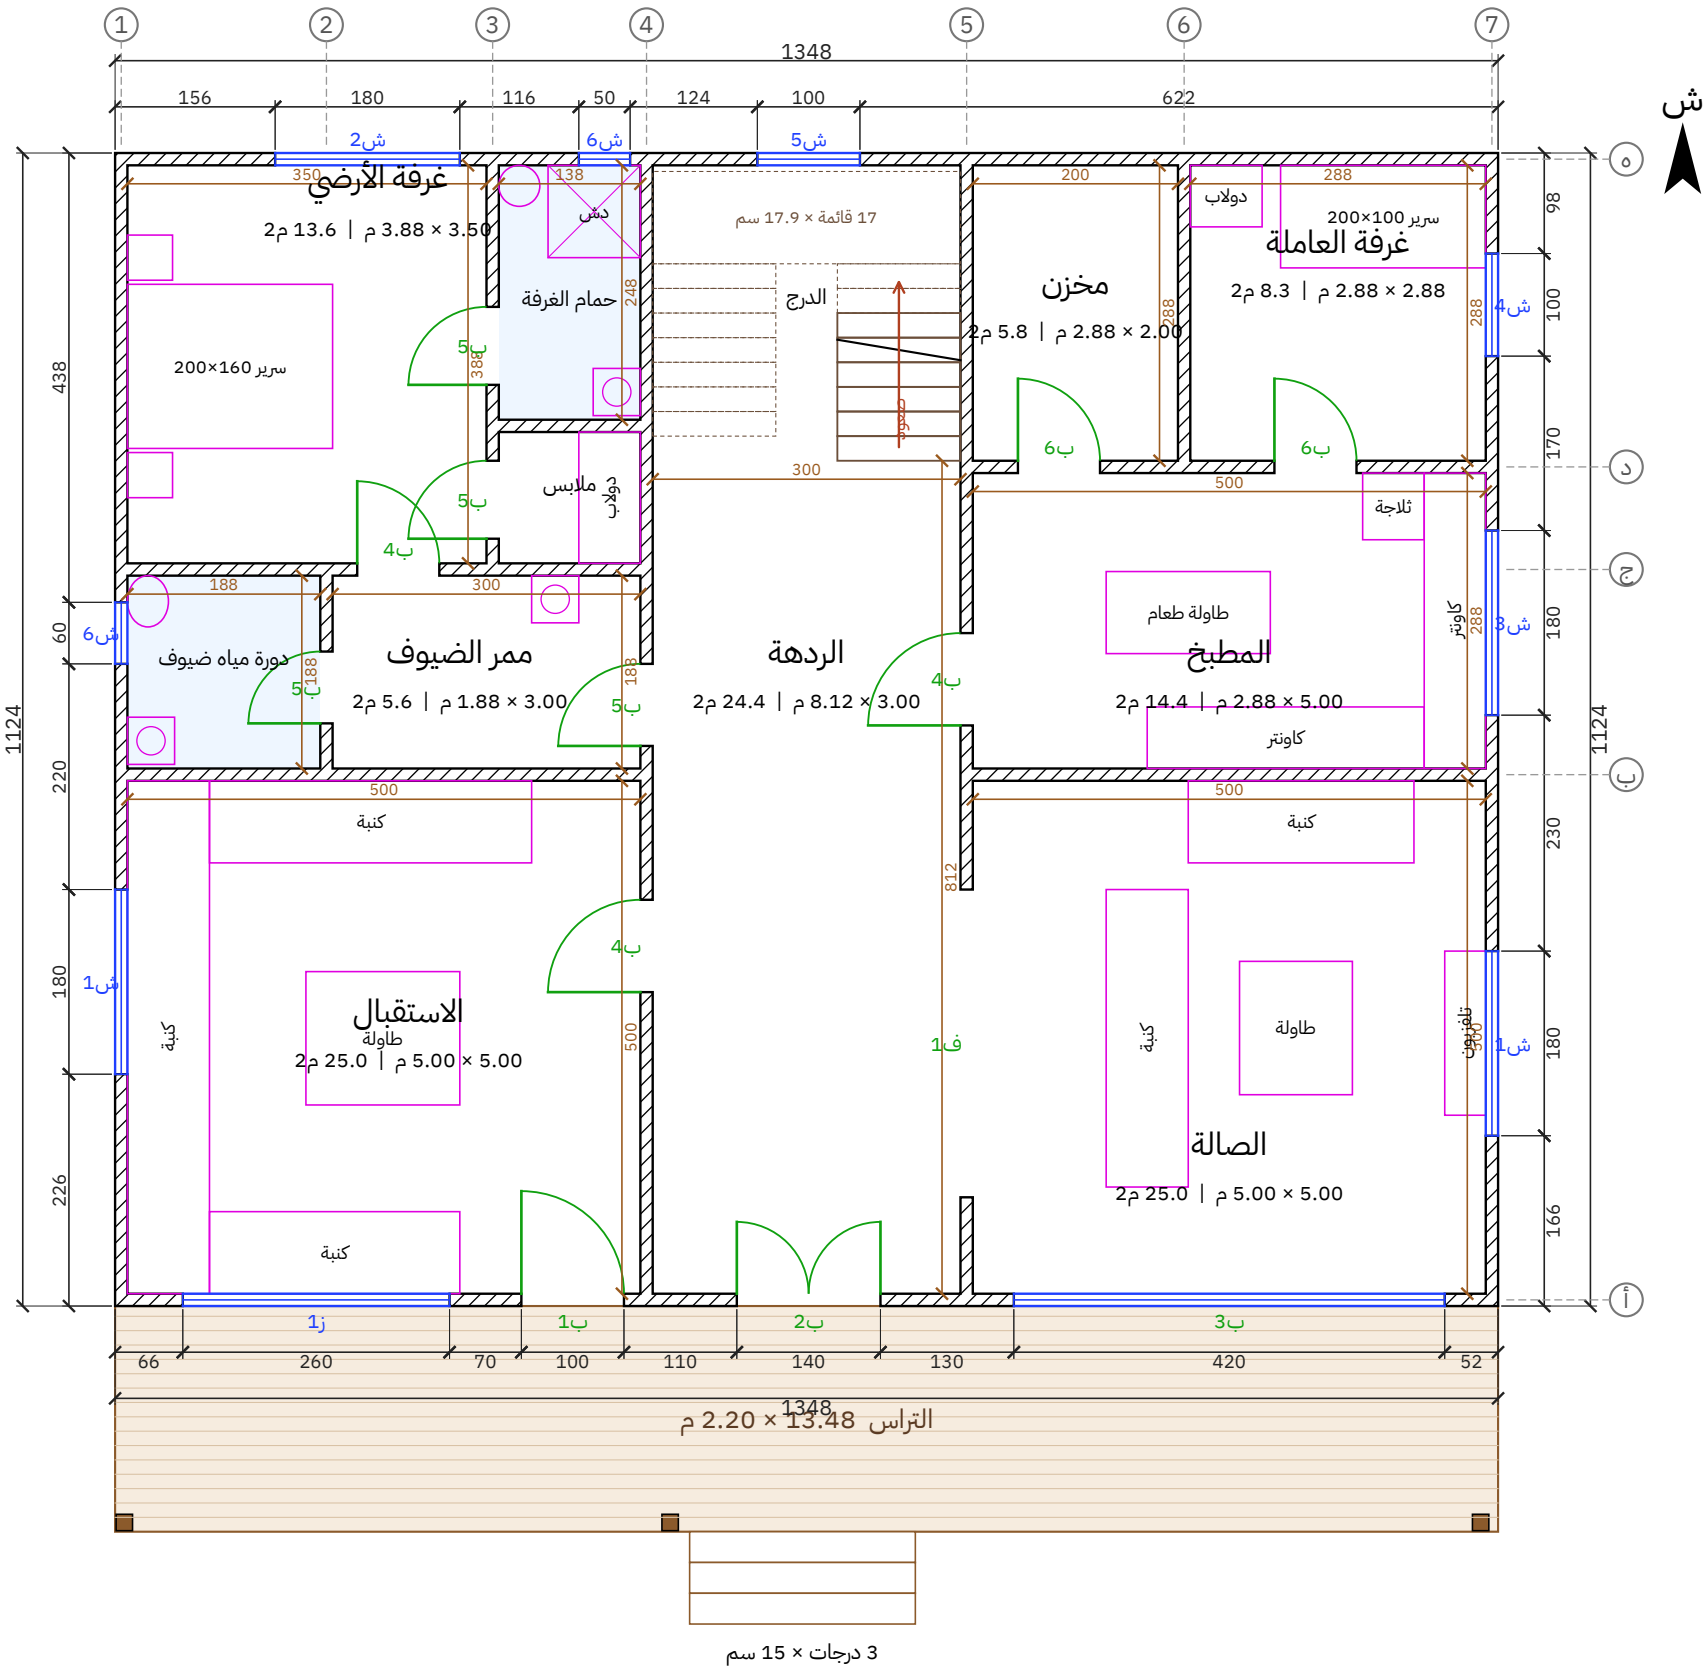

المشروع / العميل	عنوان اللوحة	المقياس	التاريخ	رقم اللوحة
مصنع وتد الأخشاب — Watad Wood Factory بيت خشب دورين متكامل — استقبال وصالة وأربع غرف — 13.36 × 11.12 م عميل — فيلا دورين	المسقط الأفقي — الدور الأرضي	1:50	2026-11-01	A-01 (1/11)

المسقط الأفقي مع الفرش — الدور الأول

الأبعاد بالسنتيمتر - الجدران: قوائم 5×7 + تلبيس 2.5 من الجهتين (12 سم) | منسوب الأرضية +3.05

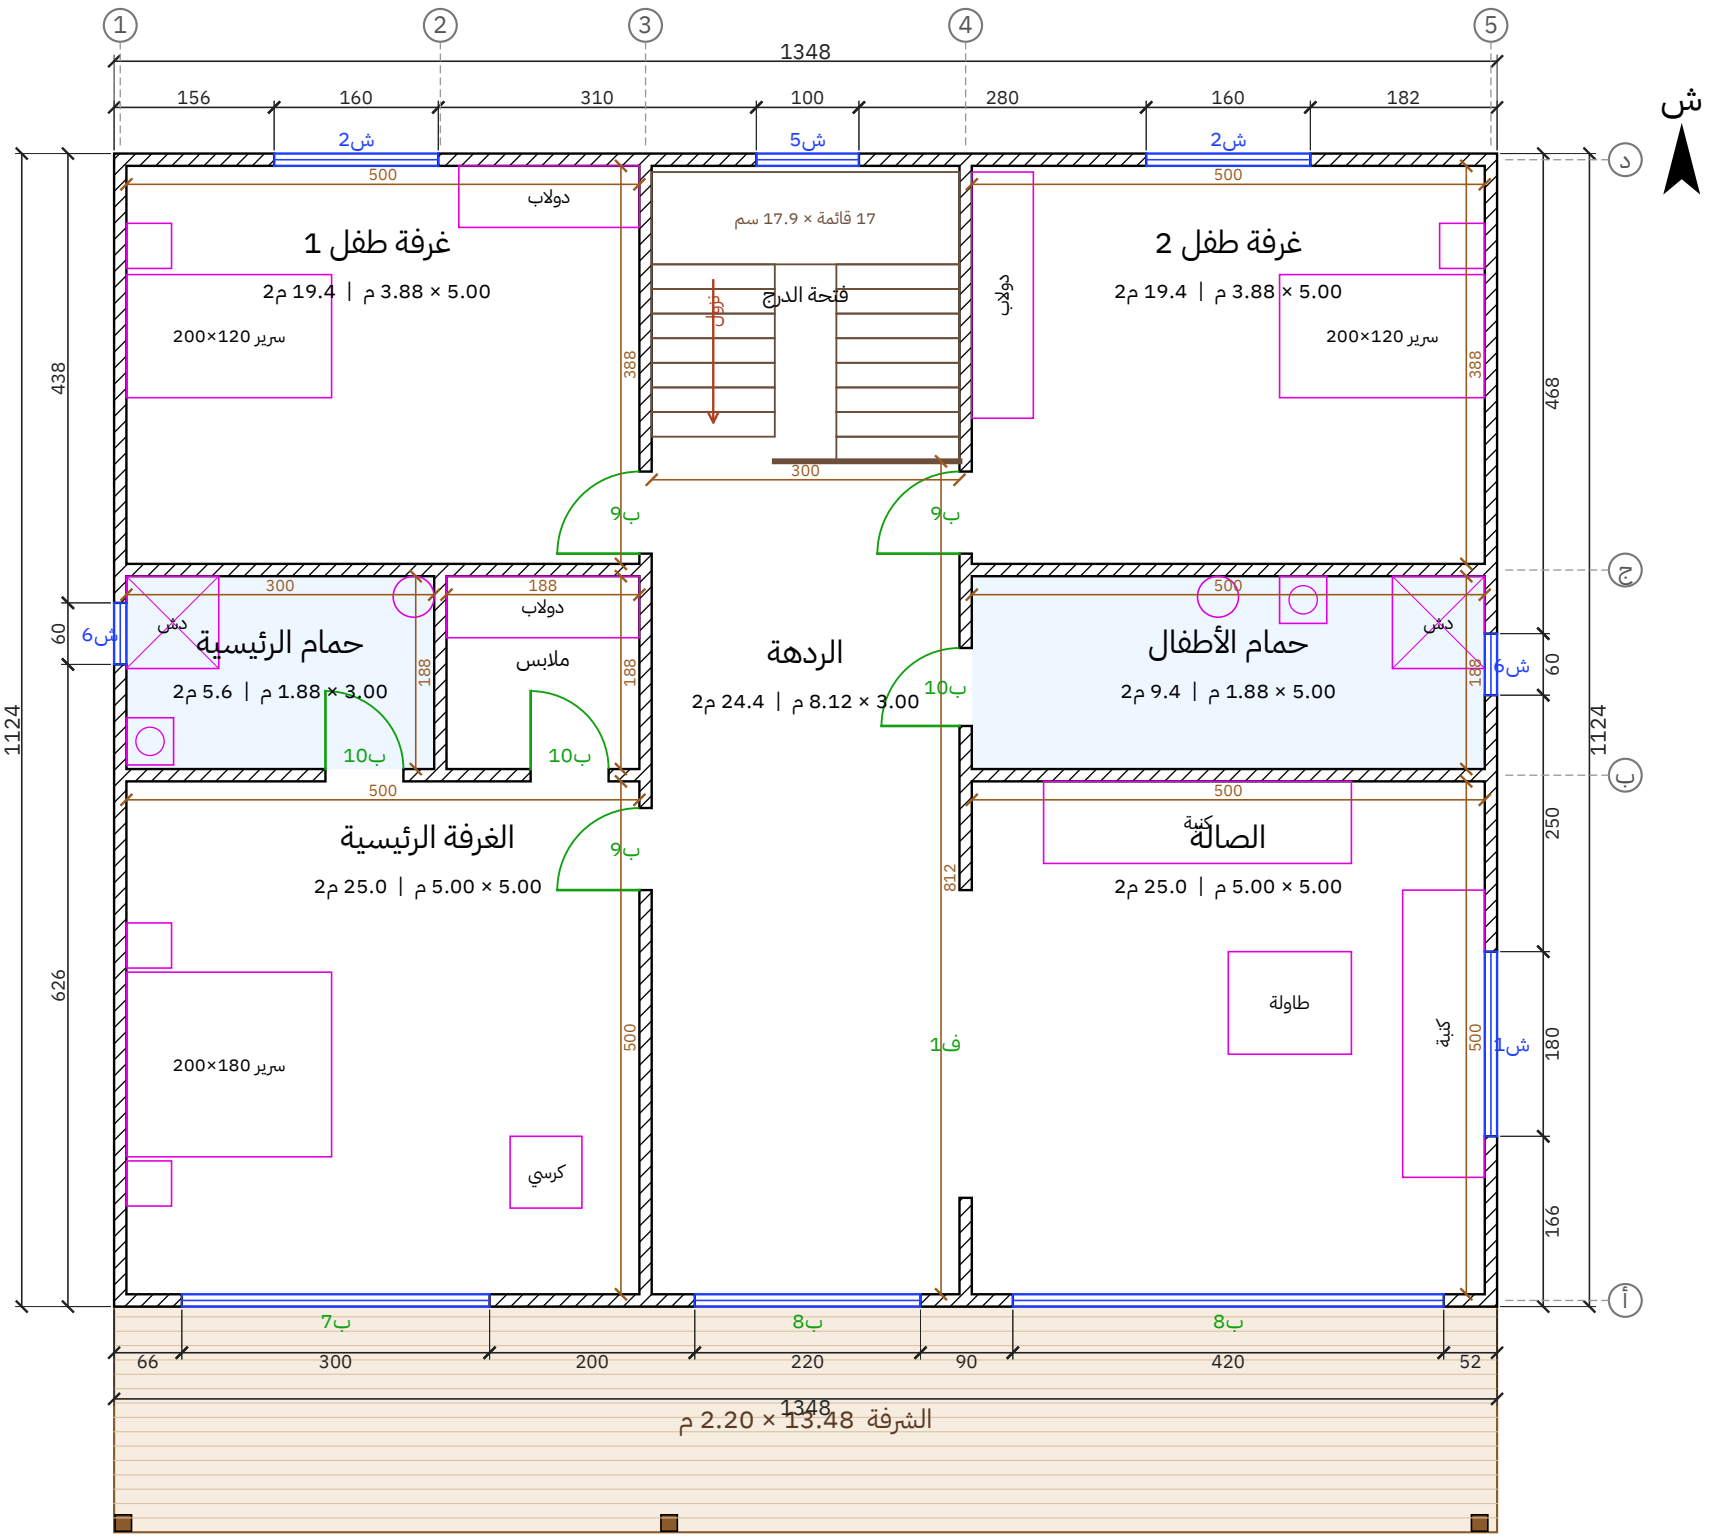


مصنع وتد الأخشاب Watad Wood Factory	المشروع / العميل بيت خشب دورين متكامل — استقبال وصالة وأربع غرف — 13.36 × 11.12 م عميل — فيلا دورين	عنوان اللوحة المسقط الأفقي — الدور الأول	المقياس 1:50	التاريخ 2026-11-01	رقم اللوحة A-02 (2/11)



الواجهة الأمامية

مقياس 1:50 | الوحدة: سم

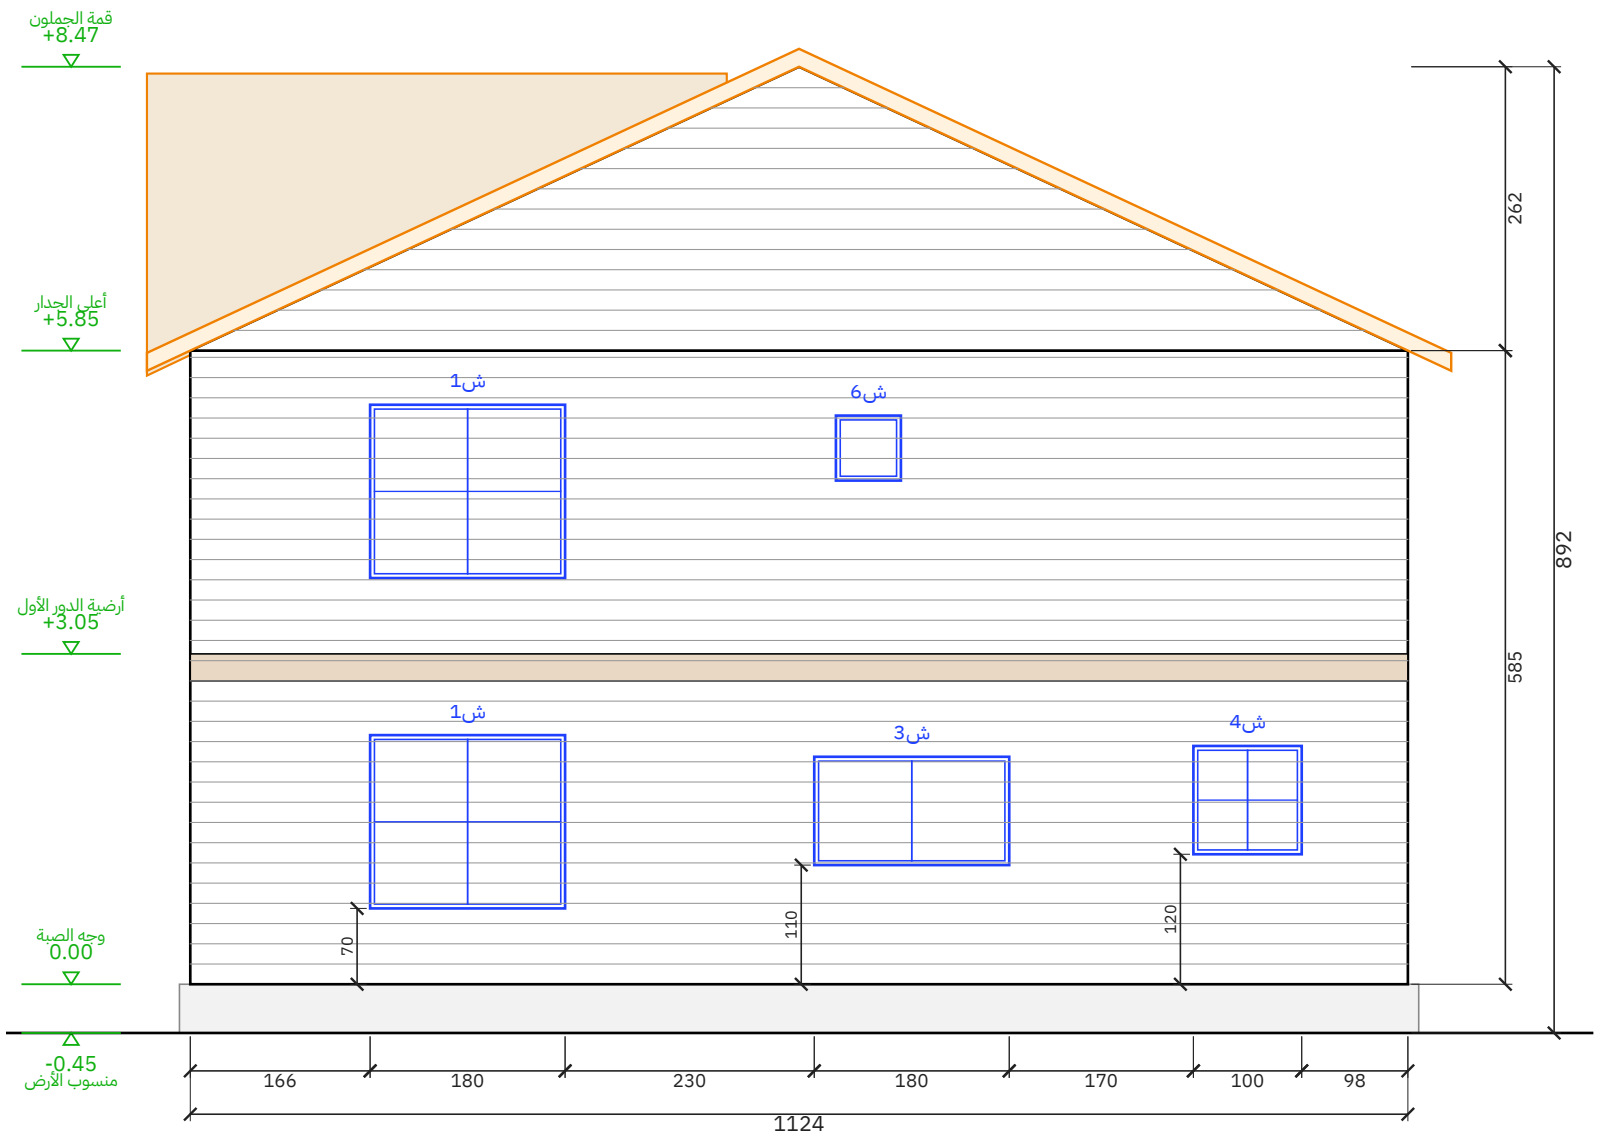


الواجهة الشرقية

مقياس 1:50 | الوحدة: سم


المشروع / العميل	عنوان اللوحة	المقياس	التاريخ	رقم اللوحة
بيت خشب دورين متكامل – استقبال وصالة وأربع غرف – 13.36 × 11.12 م عميل – فيلا دورين	الواجهة الأمامية والواجهة الشرقية	1:50	2026-11-01	A-03 (3/11)

مصنع وتد الأخشاب
Watad Wood Factory

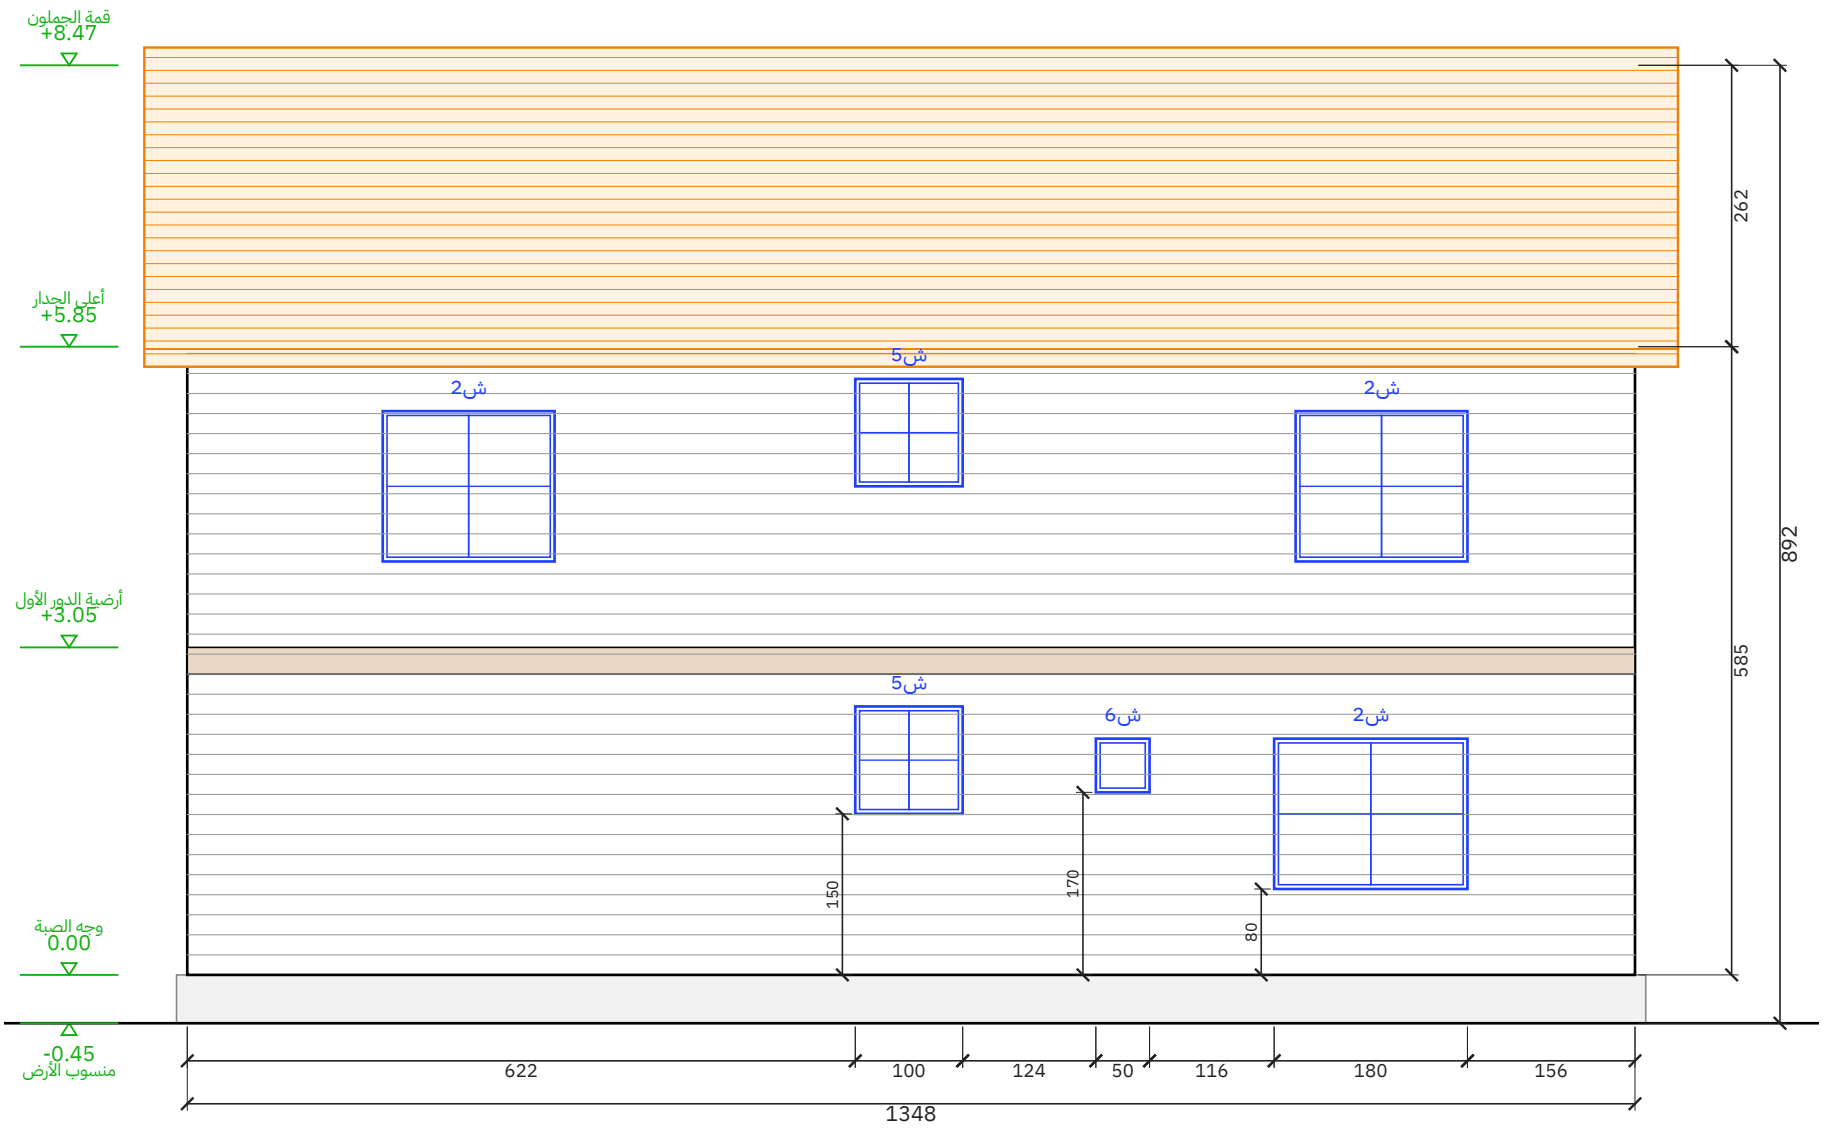

الواجهة الخلفية

مقياس 1:50 | الوحدة: سم

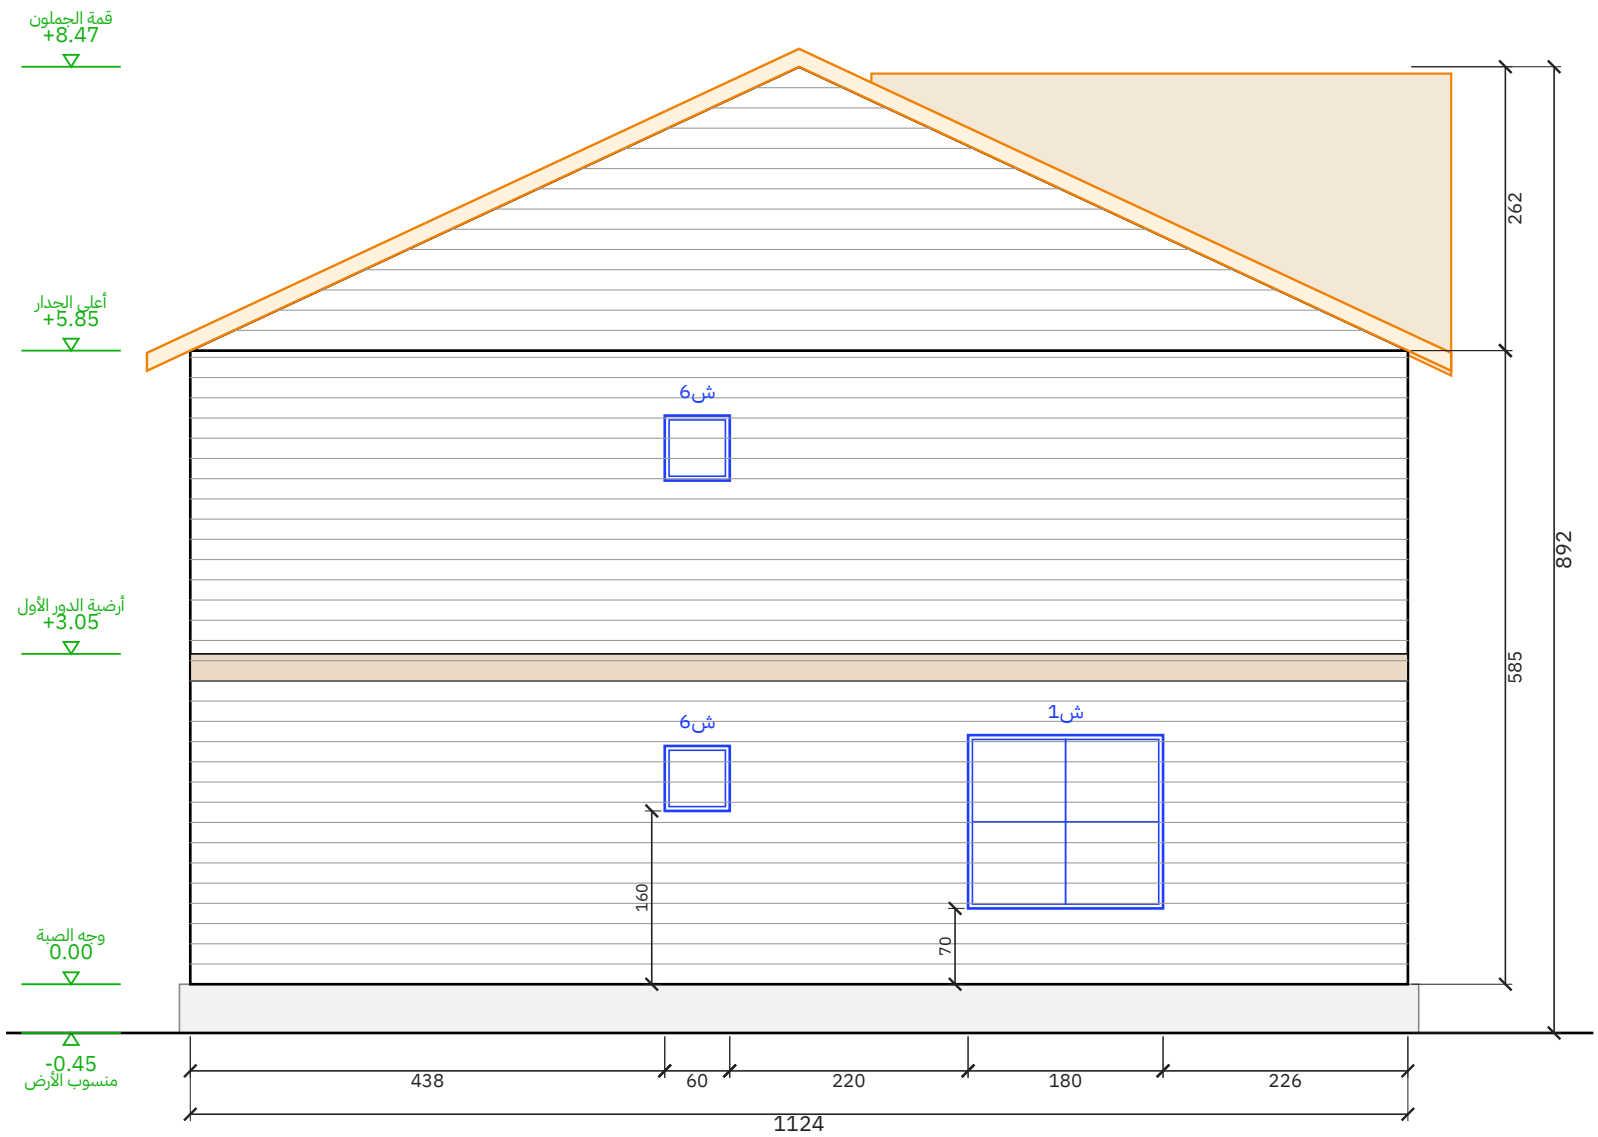


الواجهة الغربية

مقياس 1:50 | الوحدة: سم

المشروع / العميل	عنوان اللوحة	المقياس	التاريخ	رقم اللوحة
مصنع وتد الأخشاب Watad Wood Factory بيت خشب دورين متكامل – استقبال وصالة وأربع غرف – 13.36 × 11.12 م عميل – فيلا دورين	الواجهة الخلفية والواجهة الغربية	1:50	2026-11-01	A-04 (4/11)


مسقط السقف (جملون)

رفرف 40 سم من كل جهة | مقياس 1:50

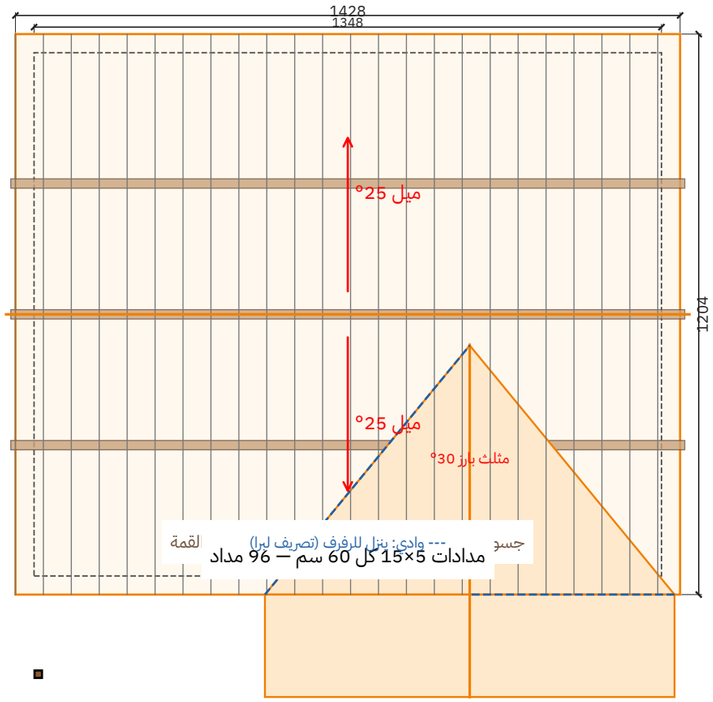


قطاع عرضي أ-أ

مقياس 1:50 | الوحدة: سم

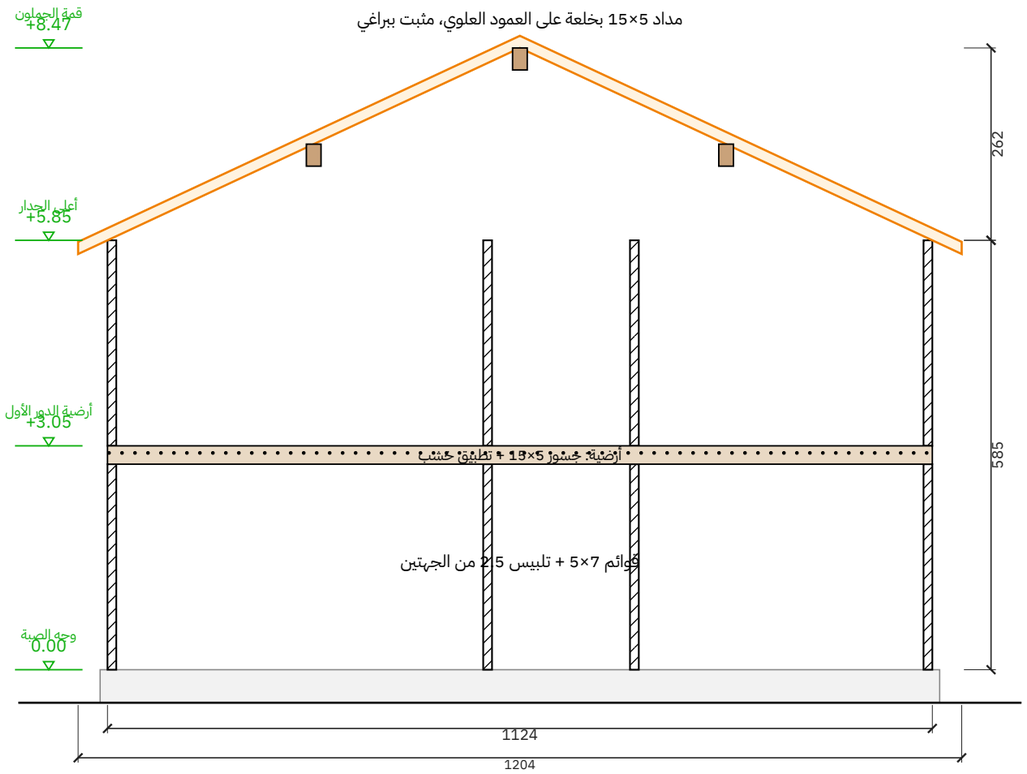

تفصيلة جلوس المداد على العلوي (1:5)

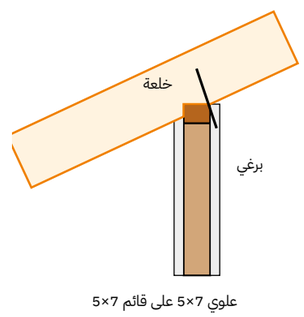

المشروع / العميل **بيت خشب دورين متكامل — استقبال وصالة وأربع غرف — 13.36 × 11.12 م** **عميل — فيلا دورين**	عنوان اللوحة **مسقط السقف والقطاع**	المقياس **1:50**	التاريخ **2026-11-01**	رقم اللوحة **A-05 (5/11)**

مصنع وتد الأخشاب
Watad Wood Factory

جدول مقاسات الأبواب والشبابيك

مقاس الفتحة الصافي في الجدار - الوحدة: سم

الرمز	النوع	العرض (سم)	الارتفاع (سم)	ارتفاع الجلسة (سم)	العدد	الموقع
ب1	باب	100	240	-	1	الأمامية
ب10	باب	76	210	-	3	حمام الأطفال - حمام الرئيسية - غرفة الملابس
ب2	باب مزدوج	140	240	-	1	الأمامية
ب3	باب	420	240	-	1	الأمامية
ب4	باب	90	220	-	2	الاستقبال — الردهة - المطبخ
ب4	باب	80	220	-	1	غرفة الأرضي
ب5	باب	80	220	-	1	ممر الضيوف (المغسلة + دورة المياه + الغرفة)
ب5	باب	70	210	-	1	دورة مياه الضيوف
ب5	باب	76	210	-	2	ملابس الغرفة - حمام الغرفة
ب6	باب	80	210	-	2	المخزن - غرفة العاملة
ب7	باب	300	230	-	1	الأمامية (على الشرفة)
ب8	باب مزدوج	220	230	-	1	الأمامية (على الشرفة)
ب8	باب	420	230	-	1	الأمامية (على الشرفة)
ب9	باب	80	220	-	3	الغرفة الرئيسية - غرفة طفل 1 - غرفة طفل 2
ف1	باب	300	240	-	2	فتحة الصالة 2
ز1	شباك	260	230	20	1	الأمامية
ش1	شباك	180	160	70	3	الشرقية 2 - الغربية
ش2	شباك	180	140	80	1	الخلفية
ش2	شباك	160	140	80	2	الخلفية 2
ش3	شباك	180	100	110	1	الشرقية
ش3	شباك	160	140	80	2	الخلفية 2
ش4	شباك	100	100	120	1	الشرقية
ش5	شباك	100	100	150	2	الخلفية 2
ش6	شباك	50	50	170	1	الخلفية
ش6	شباك	60	60	160	3	الغربية 2 - الشرقية

الإجمالي: أبواب 23 - شبابيك 15

جدول المساحات وبيانات المشروع

بيانات المشروع

البند	البيان
المشروع	بيت خشب دورين متكامل — استقبال وصالة وأربع غرف — 13.36 × 11.12 م
العميل	عميل — فيلا دورين
الموقع	—
الاستخدام	سكن عائلي متكامل
التاريخ	2026-11-01
نظام البناء	هيكل خشب 5×7 + تلبيس 2.5 سم من الجهتين
السقف	جملون 25° — قرميد معدني + 1 مثلث بارز

جدول المساحات


م	الفراغ	الأبعاد (م)	المساحة (م2)
1	أرضي — الاستقبال	5.00 × 5.00	25.00
2	أرضي — الردهة	3.00 × 8.12	24.36
3	أرضي — الصالة	5.00 × 5.00	25.00
4	أرضي — دورة مياه ضيوف	1.88 × 1.88	3.53
5	أرضي — ممر الضيوف	3.00 × 1.88	5.64
6	أرضي — غرفة الأرضي	3.50 × 3.88	13.58
7	أرضي — ملابس	1.38 × 1.28	1.77
8	أرضي — حمام الغرفة	1.38 × 2.48	3.42
9	أرضي — المطبخ	5.00 × 2.88	14.40
10	أرضي — مخزن	2.00 × 2.88	5.76
11	أرضي — غرفة العاملة	2.88 × 2.88	8.29
12	أرضي — الدرج	3.00 × 2.88	8.64
13	أول — الغرفة الرئيسية	5.00 × 5.00	25.00
14	أول — الردهة	3.00 × 8.12	24.36
15	أول — الصالة	5.00 × 5.00	25.00
16	أول — حمام الرئيسية	3.00 × 1.88	5.64
17	أول — ملابس	1.88 × 1.88	3.53
18	أول — غرفة طفل 1	5.00 × 3.88	19.40
19	أول — حمام الأطفال	5.00 × 1.88	9.40
20	أول — غرفة طفل 2	5.00 × 3.88	19.40
	المساحة الصافية الداخلية		271.13
	التراس	**13.48 × 2.20**	**29.66**
	الشرفة	**13.48 × 2.20**	**29.66**
	المساحة الإجمالية المبنية	**13.48 × 11.24 × 2 دور**	**303.03**
	المساحة الكلية (المبنية + التراسات)		**362.34**

لقطات المنظور الخارجي

المنظور الأمامي




منظور أمامي من اليسار

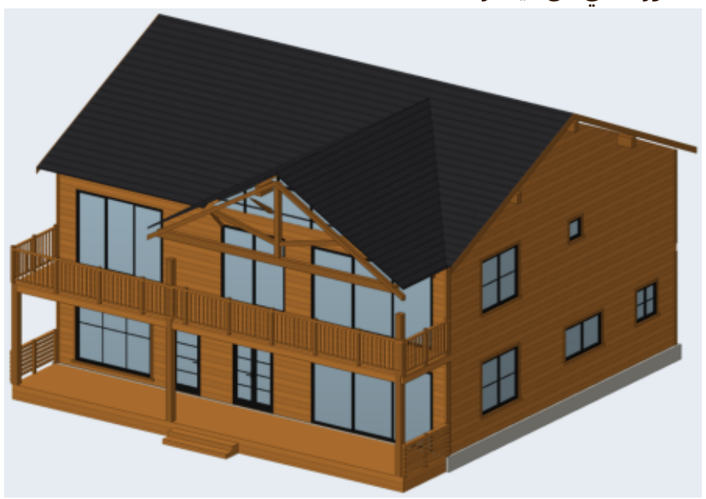

منظور أمامي من اليمين




المنظور الخلفي

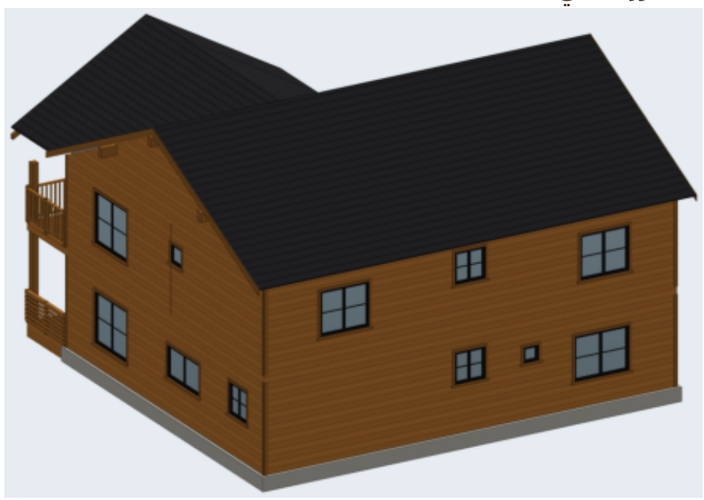

منظور خلفي من اليمين



منظر علوي

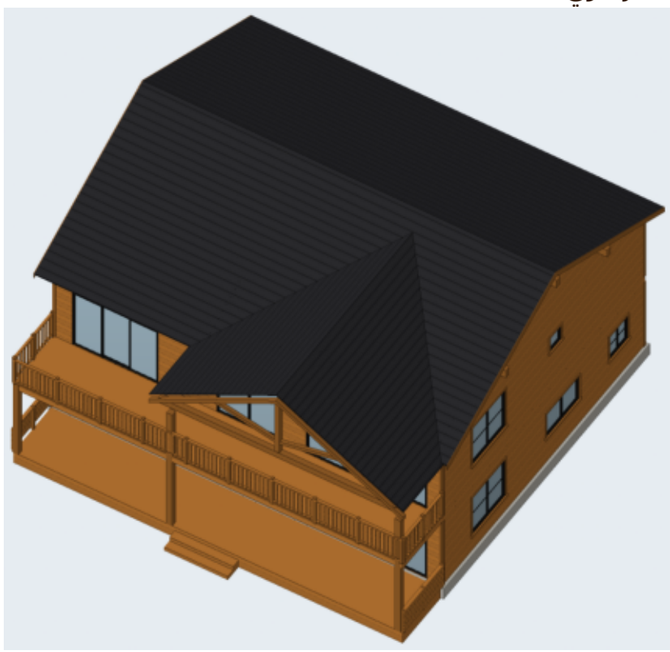


المشروع / العميل	عنوان اللوحة	المقياس	التاريخ	رقم اللوحة
بيت خشب دورين متكامل – استقبال وصالة وأربع غرف – 13.36 × 11.12 م **عميل – فيلا دورين**	**لقطات المنظور**	**–**	**2026-11-01**	**A-08 (8/11)**

مصنع وتد الأخشاب
Watad Wood Factory

المقطع العلوي بالفرش — الدور الأرضي

مقطع أفقي على ارتفاع 1.90 م — توزيع الفرش ومسار الحركة

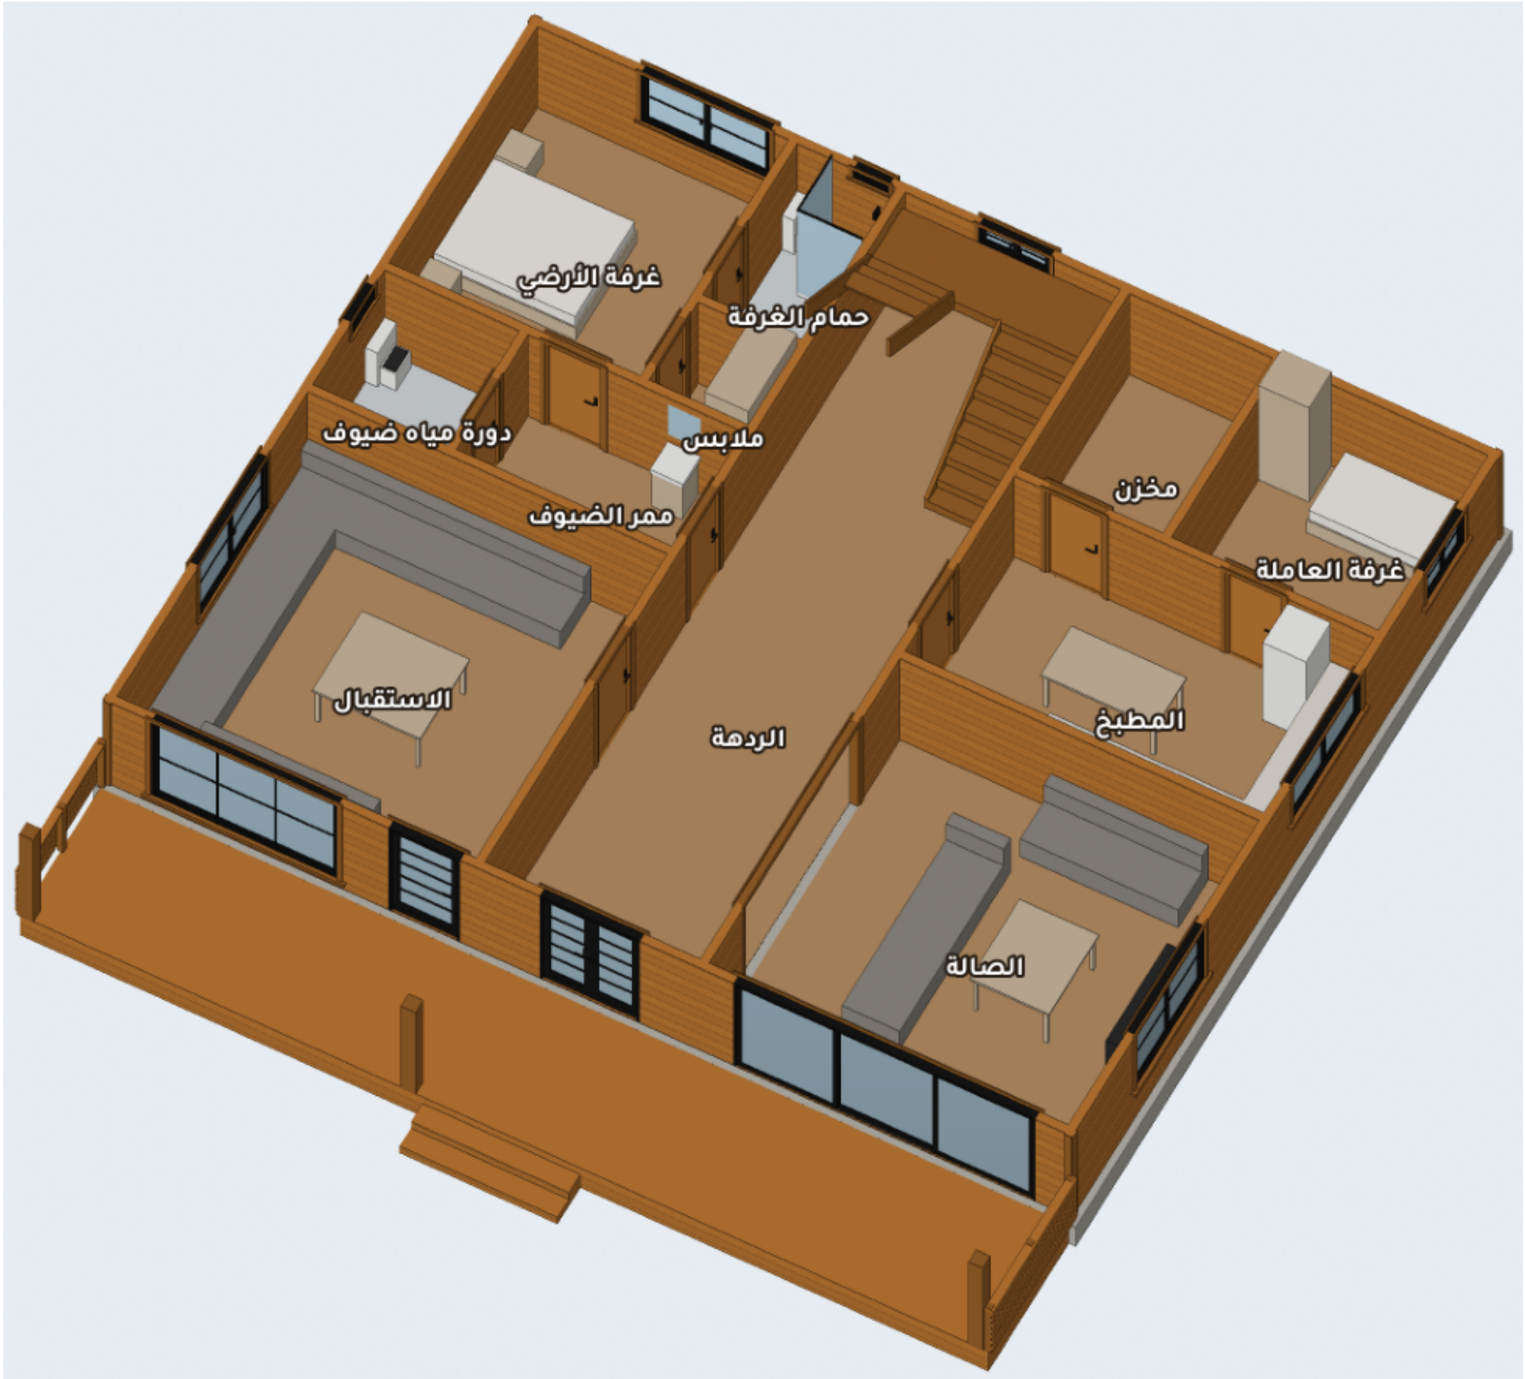


المشروع / العميل	عنوان اللوحة	المقياس	التاريخ	رقم اللوحة
بيت خشب دورين متكامل — استقبال وصالة وأربع غرف — 13.36 × 11.12 م عميل — فيلا دورين	المقطع العلوي بالفرش — الدور الأرضي	—	2026-11-01	A-09 (9/11)

مصنع وتد الأخشاب
Watad Wood Factory

المقطع العلوي بالفرش — الدور الأول

مقطع أفقي على ارتفاع 1.90 م — توزيع الفرش ومسار الحركة

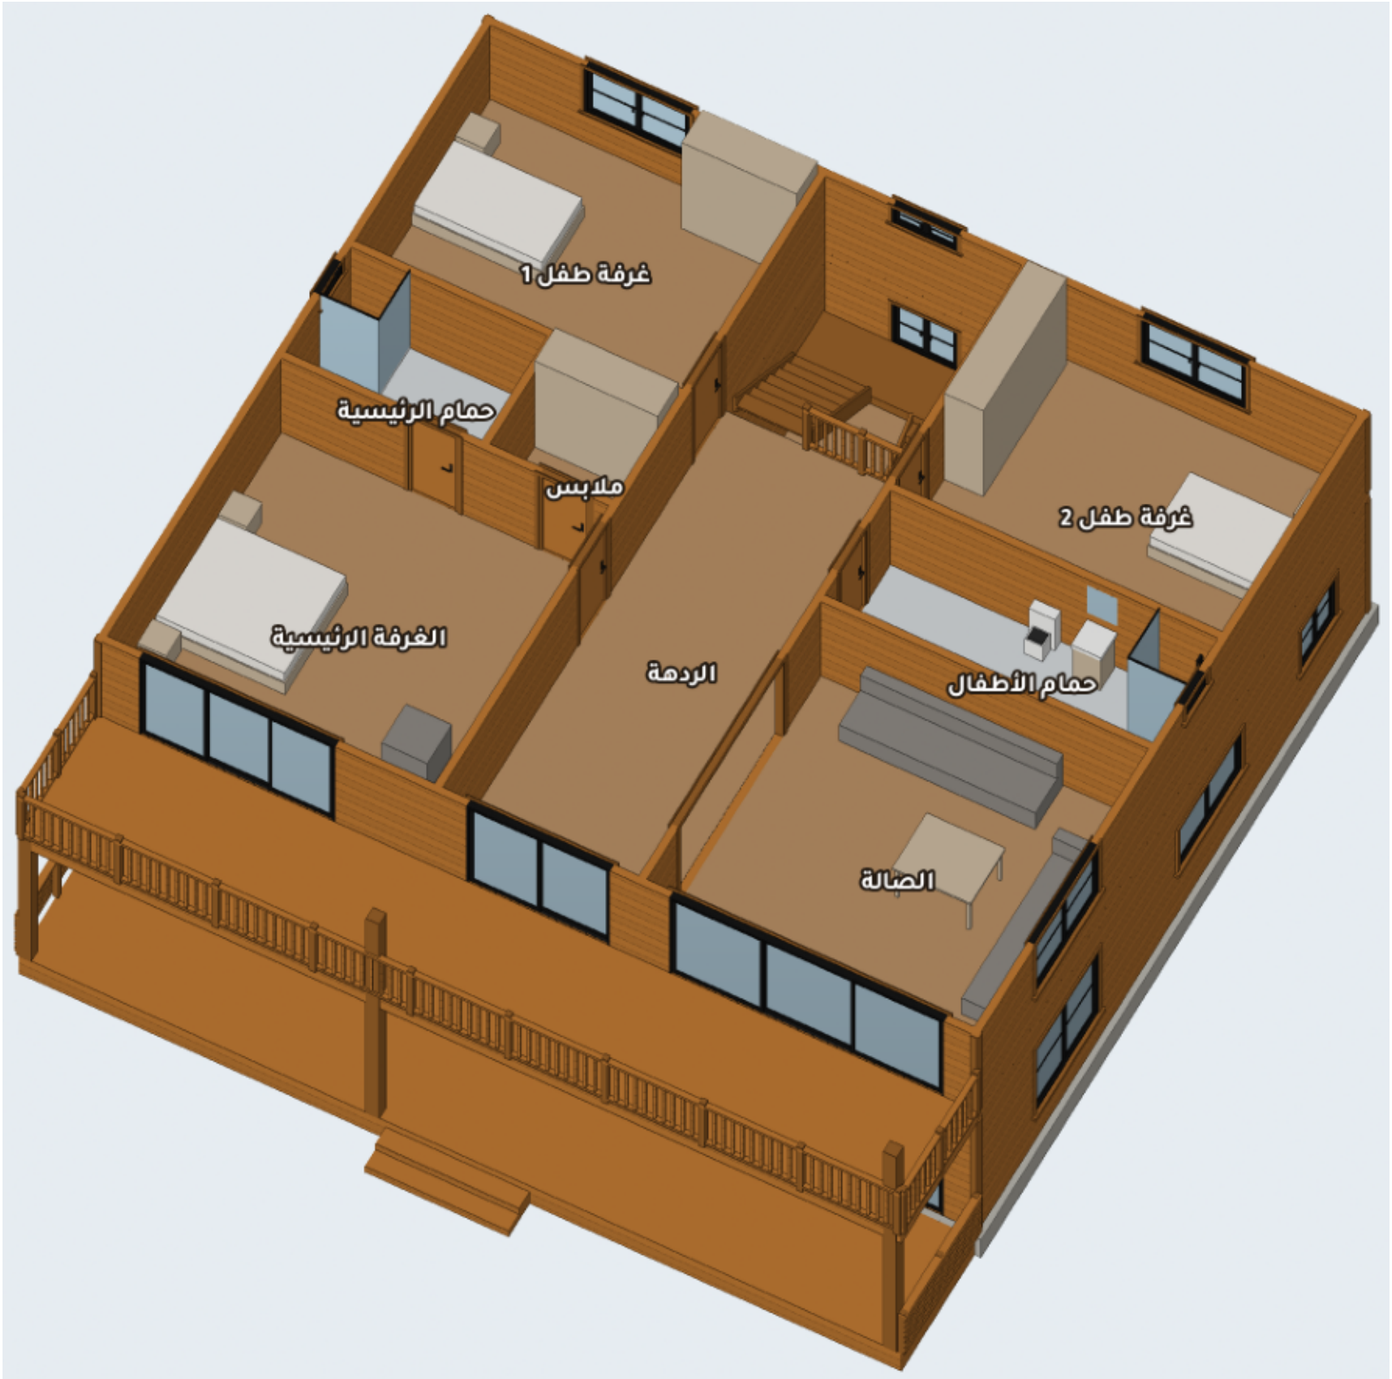


المشروع / العميل	عنوان اللوحة	المقياس	التاريخ	رقم اللوحة
بيت خشب دورين متكامل — استقبال وصالة وأربع غرف — 13.36 × 11.12 م عميل — فيلا دورين	المقطع العلوي بالفرش — الدور الأول	—	2026-11-01	A-10 (10/11)

مصنع وتد الأخشاب
Watad Wood Factory

المنظور ثلاثي الأبعاد والمواد

النمط: جوزي غامق + إطارات سوداء — رندر واقعي بخامات حقيقية

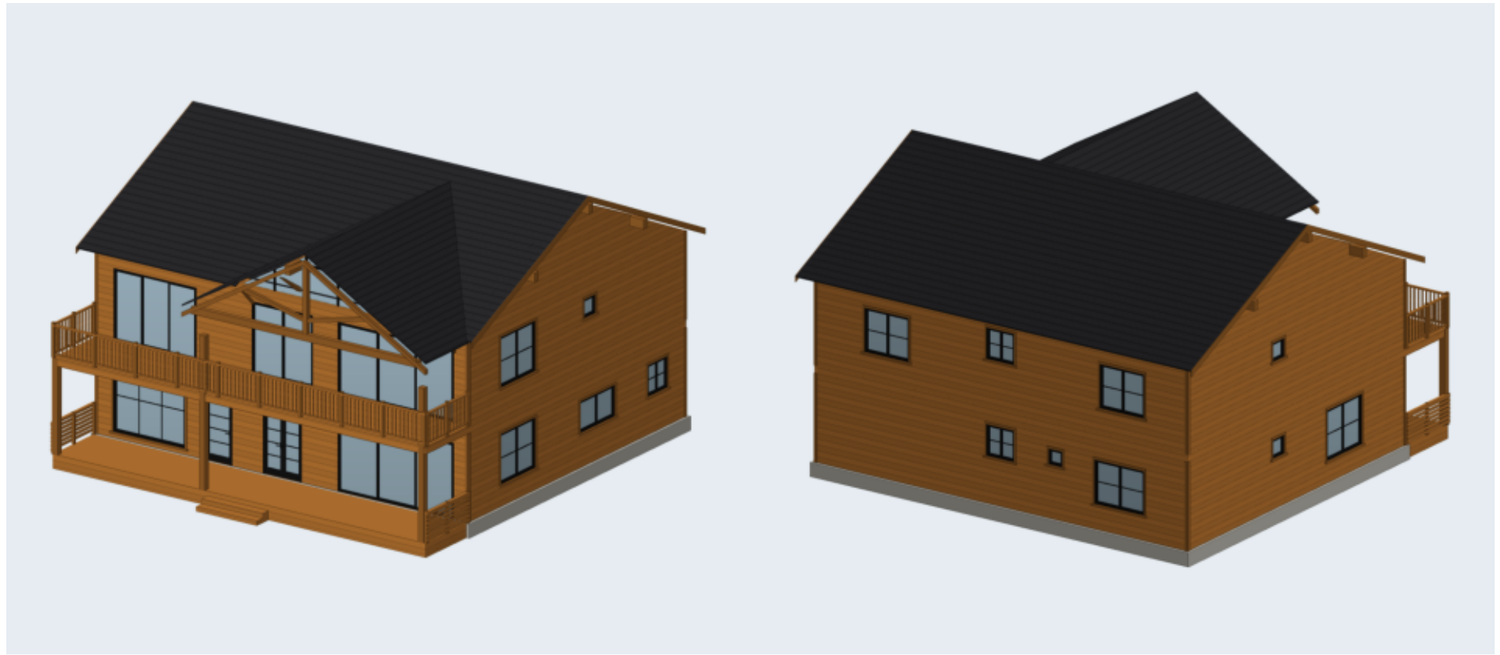

جدول المواد والألوان

الخشب / الصبغة
صبغة عسلي / سيدر

القرميد
قرميد رمادي غامق

الزجاج
زجاج شفاف

إطارات الشبابيك والأبواب
إطار ألمنيوم أسود


الكنار والزوايا
نفس الصبغة أغمق درجة

الصبة
خرسانة 45 سم


الدربزين: ألواح أفقية متقاربة (عصري)

تقسيم الشبابيك: بدون | الباب الرئيسي: زجاج بتقسيمات (فرنسي)

أنواع الدربزين المعتمدة (من مشاريع المصنع)

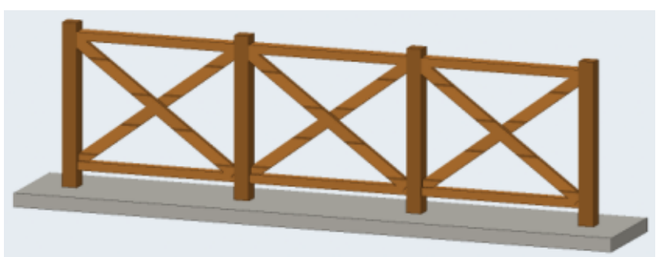

تقاطع X (صورة 5)

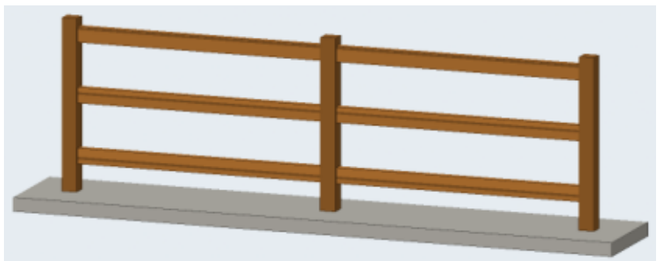

3 مرابيع أفقية (صورة 2)



قوائم رأسية متقاربة (صورة 1)

المشروع / العميل	عنوان اللوحة	المقياس	التاريخ	رقم اللوحة
مصنع وتد الأخشاب Watad Wood Factory **بيت خشب دورين متكامل – استقبال وصالة وأربع غرف – 13.36 × 11.12 م** **عميل – فيلا دورين**	**المنظور والمواد**	**–**	**2026-11-01**	**A-11 (11/11)**