
المنظور ثلاثي الأبعاد والمواد

النمط: جوزي غامق + إطارات سوداء — رندر واقعي بخامات حقيقية

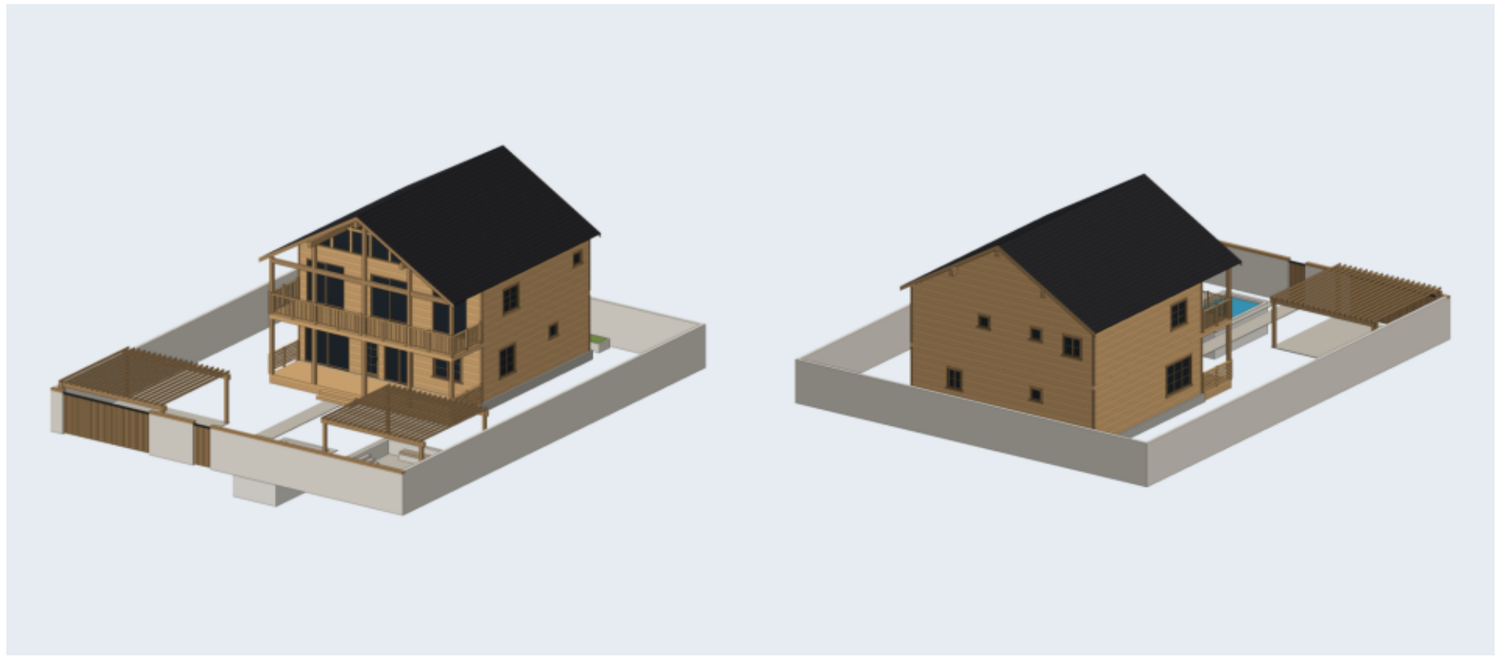

جدول المواد والألوان

الخشب / الصبغة

خشب طبيعي فاتح (بدون صبغة)

القرميد

قرميد رمادي غامق

الزجاج

زجاج عاكس غامق

إطارات الشبابيك والأبواب

إطار خشب بنفس الصبغة أغمق

الكنار والزوايا

نفس الصبغة أغمق درجة


الصبة

خرسانة 45 سم


الدربزين: ألواح أفقية متقاربة (عصري)

تقسيم الشبابيك: بدون | الباب الرئيسي: سحاب زجاج

أنواع الدربزين المعتمدة (من مشاريع المصنع)

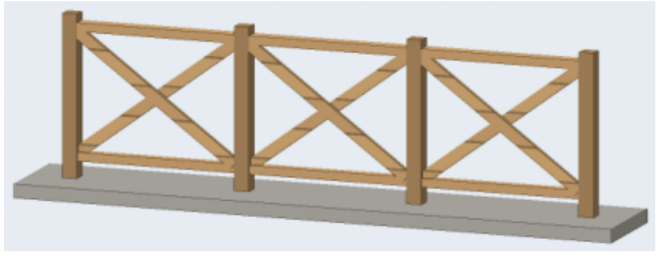

تقاطع X (صورة 5)

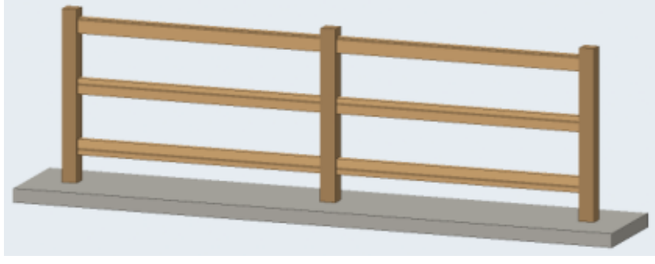

3 مرابيع أفقية (صورة 2)




قوائم رأسية متقاربة (صورة 1)

مصنع وتد الأخشاب Watad Wood Factory	المشروع / العميل كوخ الهدا — دورين — 3 غرف نوم + مجلس + بلكونة — 10.60 × 9.00 م عميل — الهدا	عنوان اللوحة المنظور والمواد	المقياس 1:50	التاريخ 2026-11-08	رقم اللوحة W-01 (1/24)

المسقط الأفقي مع الفرش — الدور الأرضي


الأبعاد بالسنتيمتر - الجدران: قوائم 5×7 + تلبيس 2.5 من الجهتين (12 سم) | منسوب الأرضية +0.00

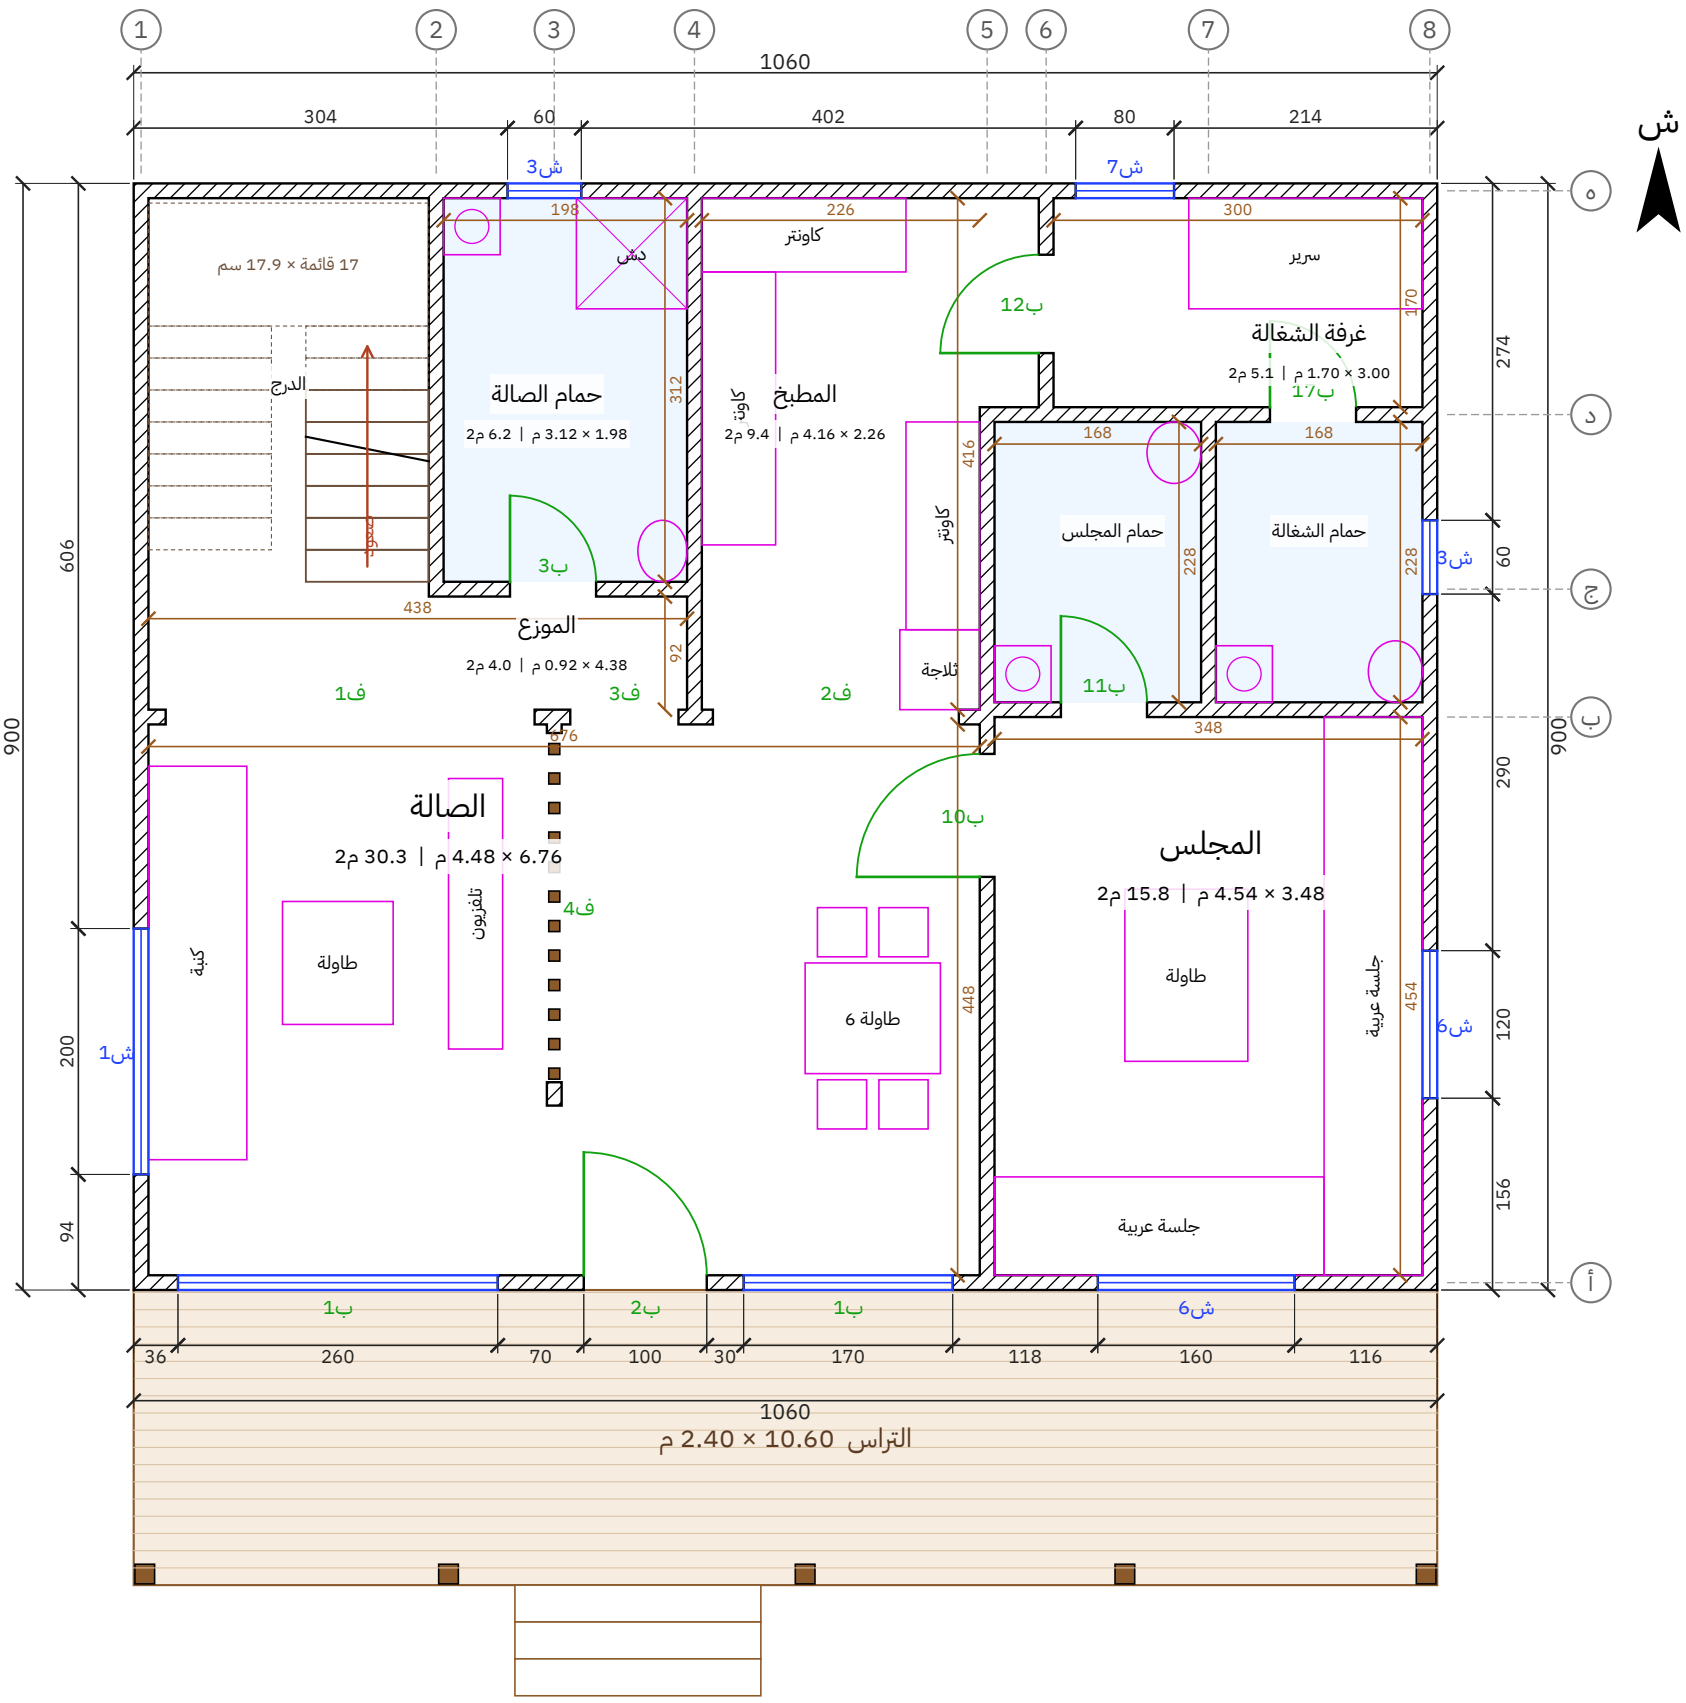

المشروع / العميل	عنوان اللوحة	المقياس	التاريخ	رقم اللوحة	
كوخ الهدا — دورين — 3 غرف نوم + مجلس + بلكونة — 10.60 × 9.00 م عميل — الهدا	المسقط الأفقي — الدور الأرضي	1:50	2026-11-08	W-02 (2/24)	مصنع وتد الأخشاب Watad Wood Factory

المسقط الأفقي مع الفرش — الدور الأول

الأبعاد بالسنتيمتر - الجدران: قوائم 7×5 + تلبيس 2.5 من الجهتين (12 سم) | منسوب الأرضية +3.05

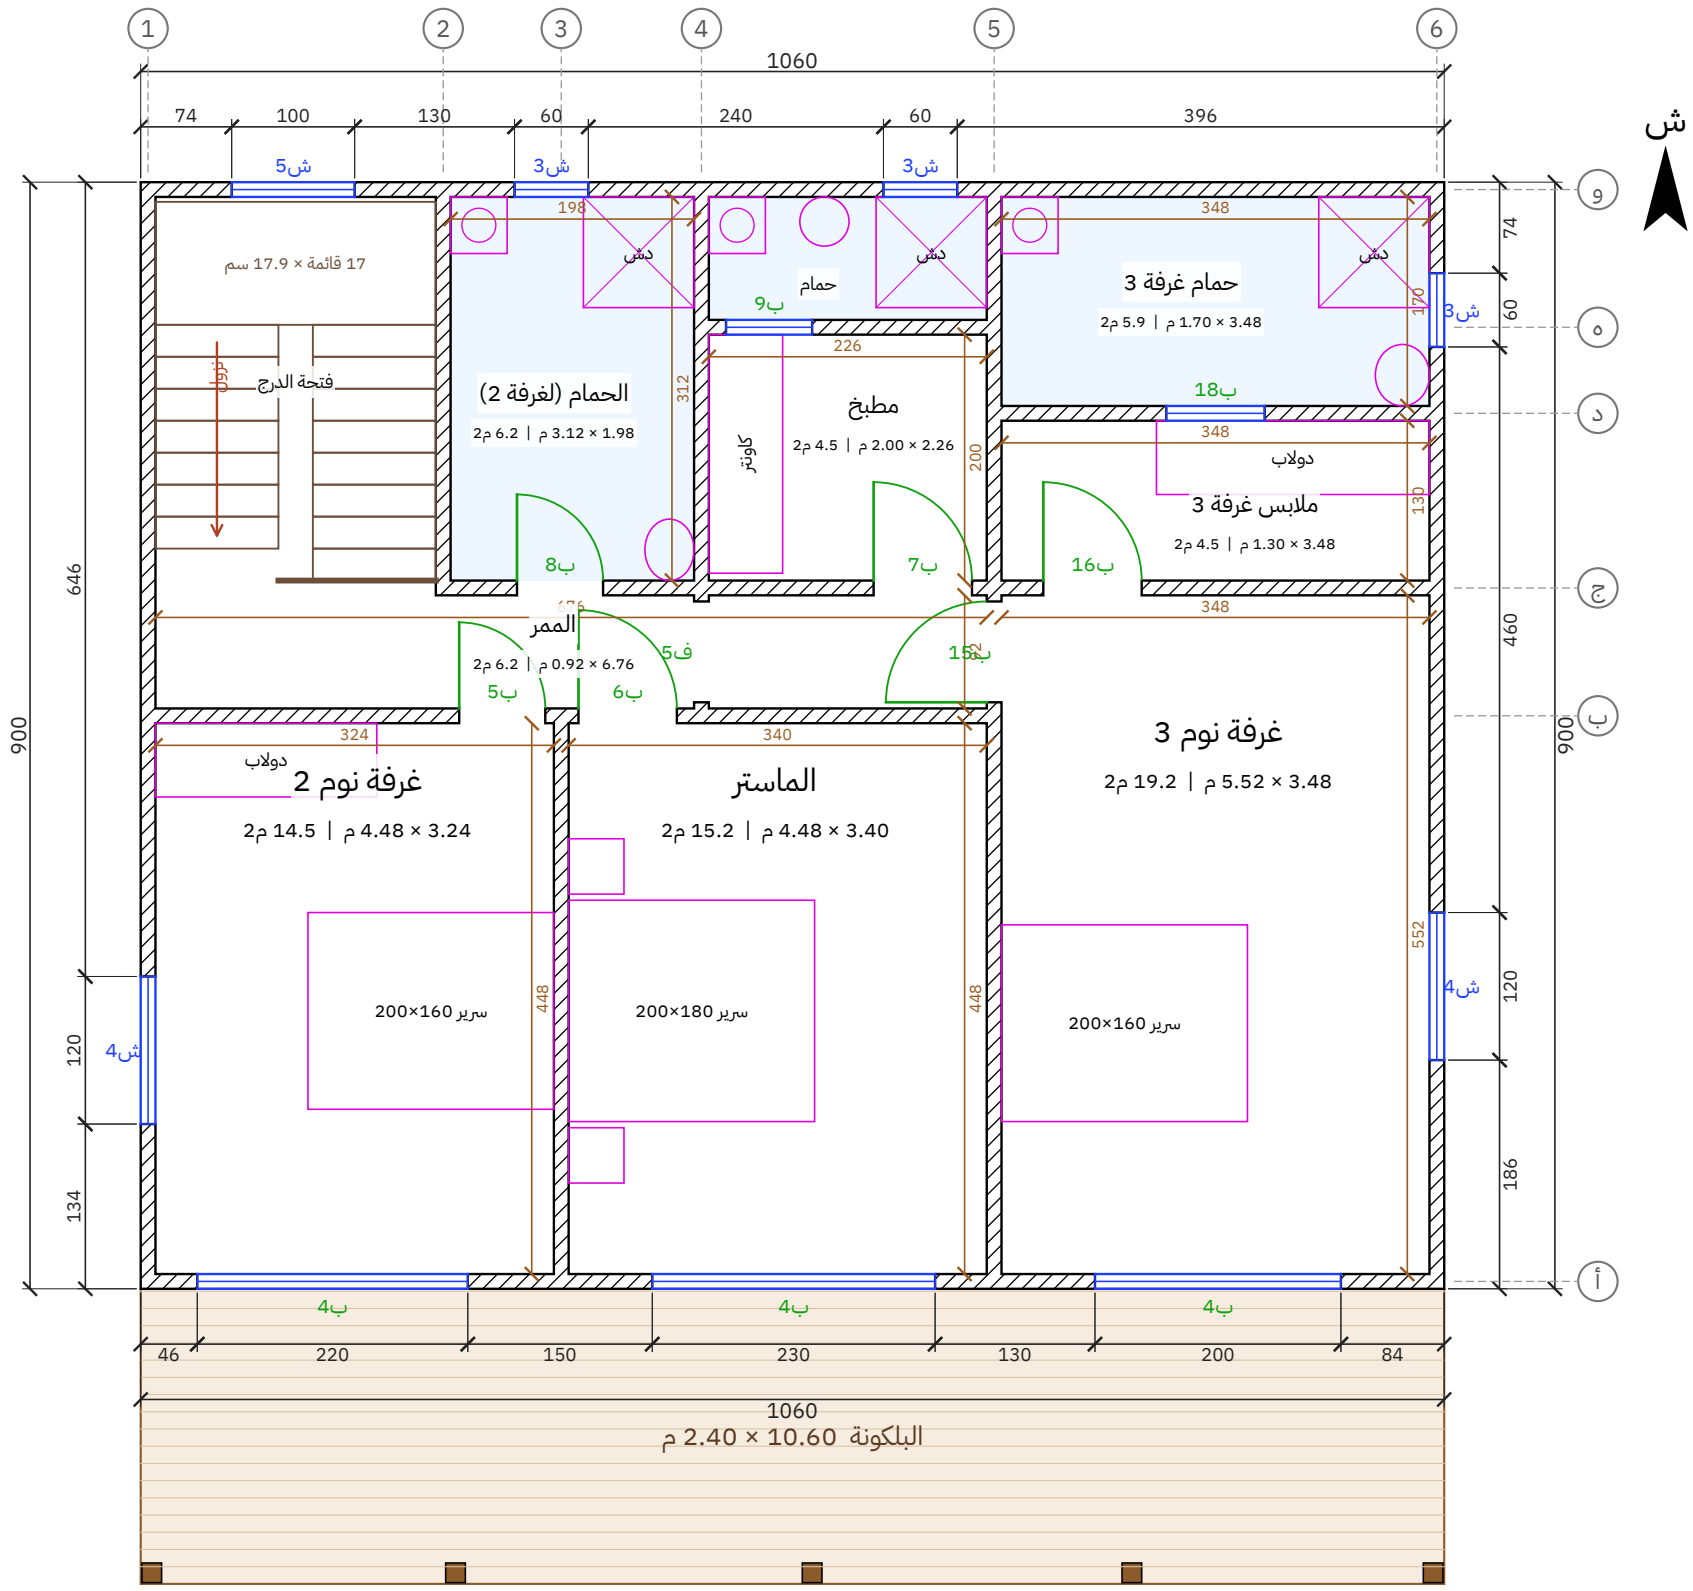

المشروع / العميل	عنوان اللوحة	المقياس	التاريخ	رقم اللوحة
كوخ الهدا — دورين — 3 غرف نوم + مجلس + بلكونة — 10.60 × 9.00 م عميل — الهدا	المسقط الأفقي — الدور الأول	1:50	2026-11-08	W-03 (3/24)

مصنع وتد الأخشاب
Watad Wood Factory


جدول مساحات الموقع

البند	المقاس	المساحة (م²)
مساحة الأرض	20.00 × 24.67 م	493.4
مسطح الكوخ (البصمة)	10.60 × 9.00 م	95.4
تراس الكوخ	10.60 × 2.40 م	25.4
مسبح	2.50 × 4.40 م	11.0
جلسة شتوية مدفونة (أشتوية)	5.20 × 4.80 م	25.0
بلاط		14.3
موقف سيارة	6.00 × 5.50 م	33.0
ممر	1.00 × 11.17 م	11.2
أحواض زراعة	10.20 × 0.90 م	9.2
المسطحات الخضراء (حديقة)	الباقي	269.0

- أرض مفترضة 20.00 × 24.67 م (المقاس الفعلي يوصل من العميل) بسور 2.20 م تكسية حجر + بوابة سيارة 5.00 م + باب مشاة على محور المدخل.
- موقف سيارتين 6.00 × 5.50 م بمظلة خشب، ممر مستقيم لدرج التراس، مسبح غطس، أشتوية مدفونة بمشب تحت برجولة، ونخيل وأشجار على السور.


الموقع العام وتنسيق الحديقة (لاندسكيب)

الأرض 20 × 25 م = 493 م² | الأبعاد بالسنتيمتر

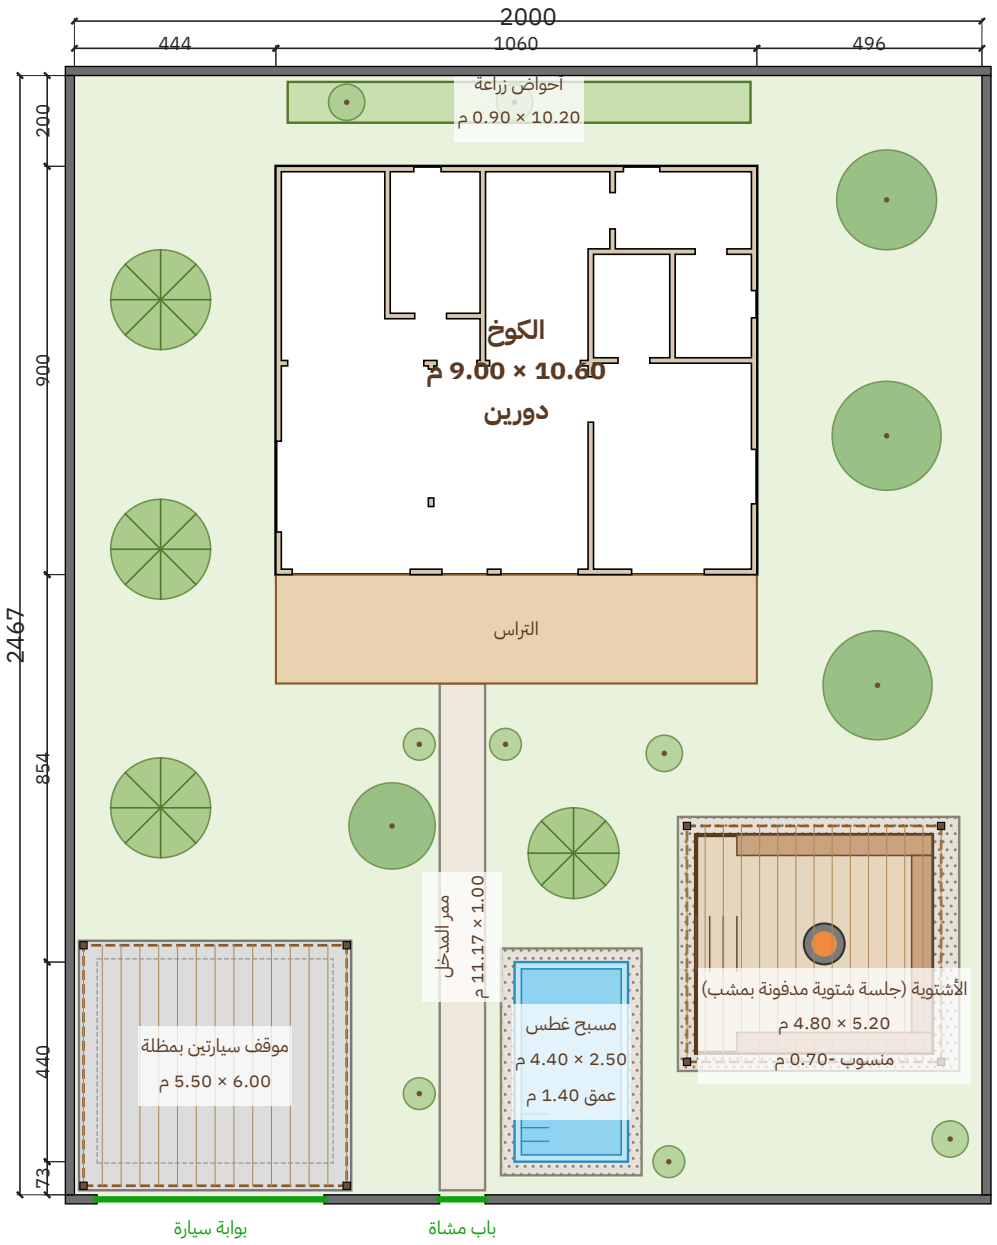


المشروع / العميل	عنوان اللوحة	المقياس	التاريخ	رقم اللوحة
كوخ الهدا – دورين – 3 غرف نوم + مجلس + بلكونة – 10.60 × 9.00 م عميل – الهدا	الموقع العام واللاندسكيب	1:200	2026-11-08	A-01 (1/12)

مصنع وتد الأخشاب
Watad Wood Factory

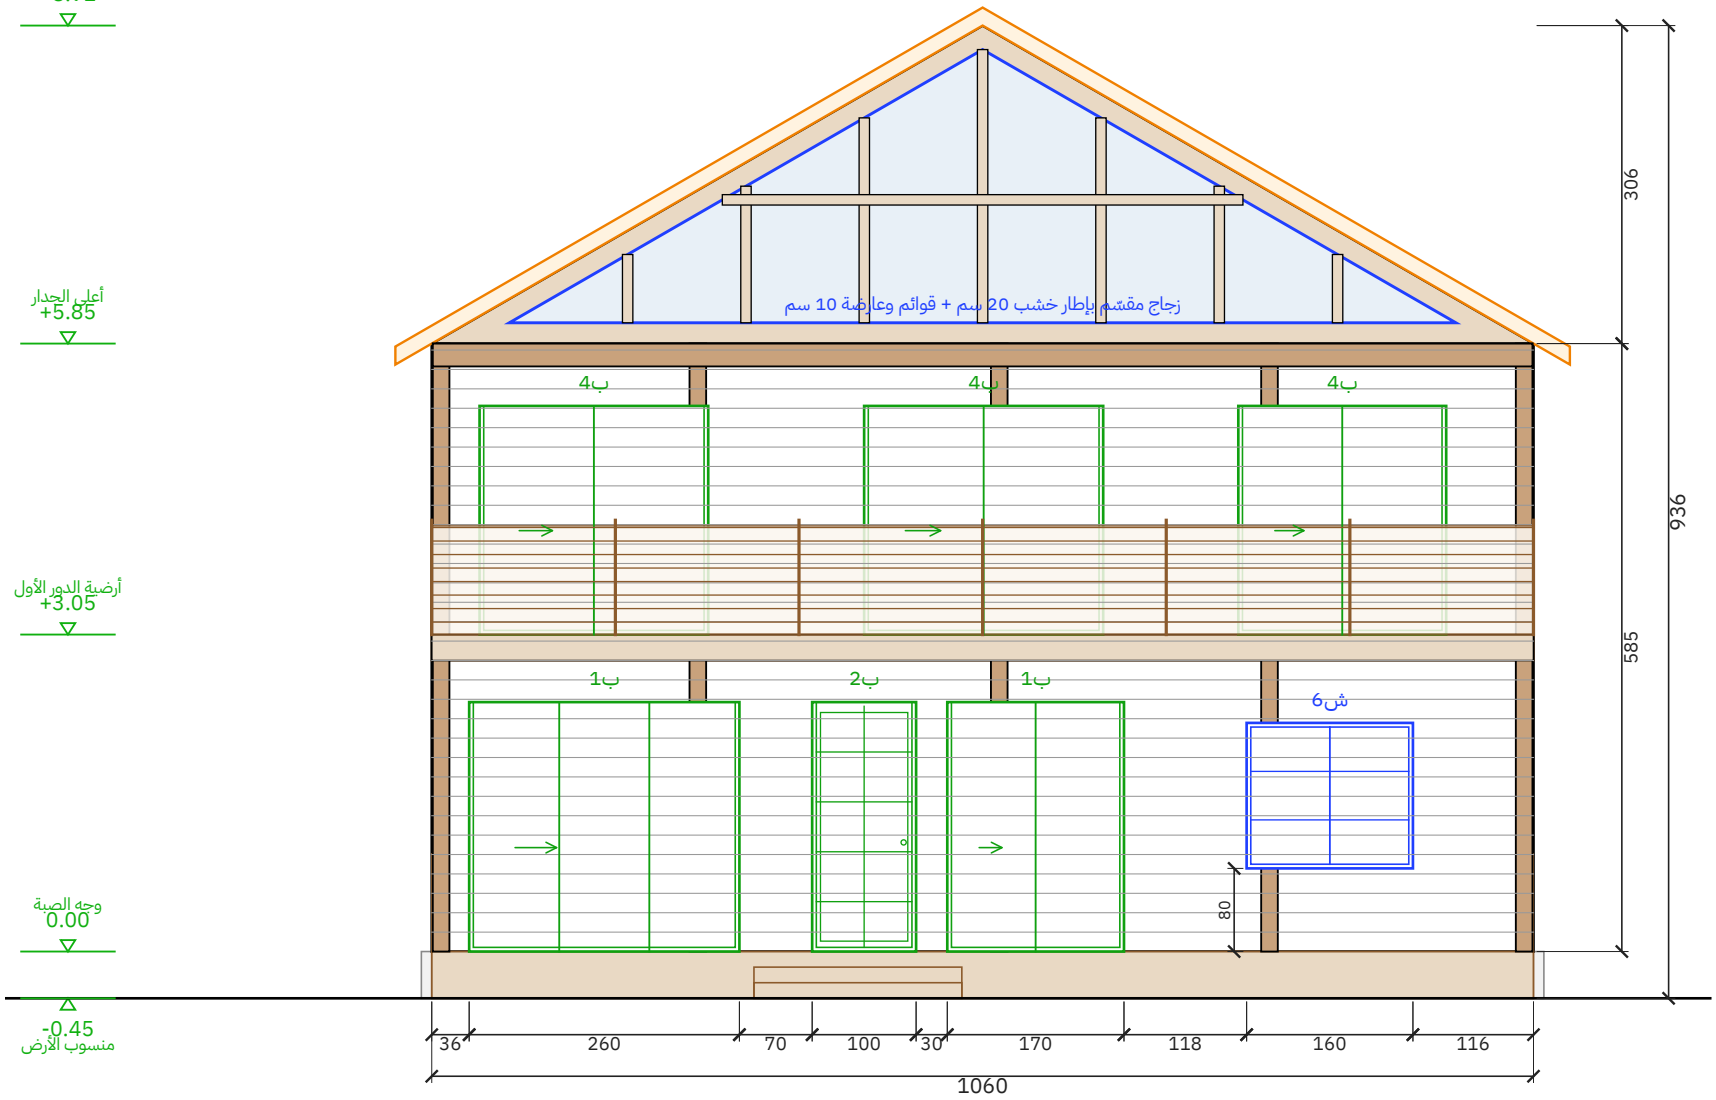

الواجهة الأمامية

مقياس 1:50 | الوحدة: سم

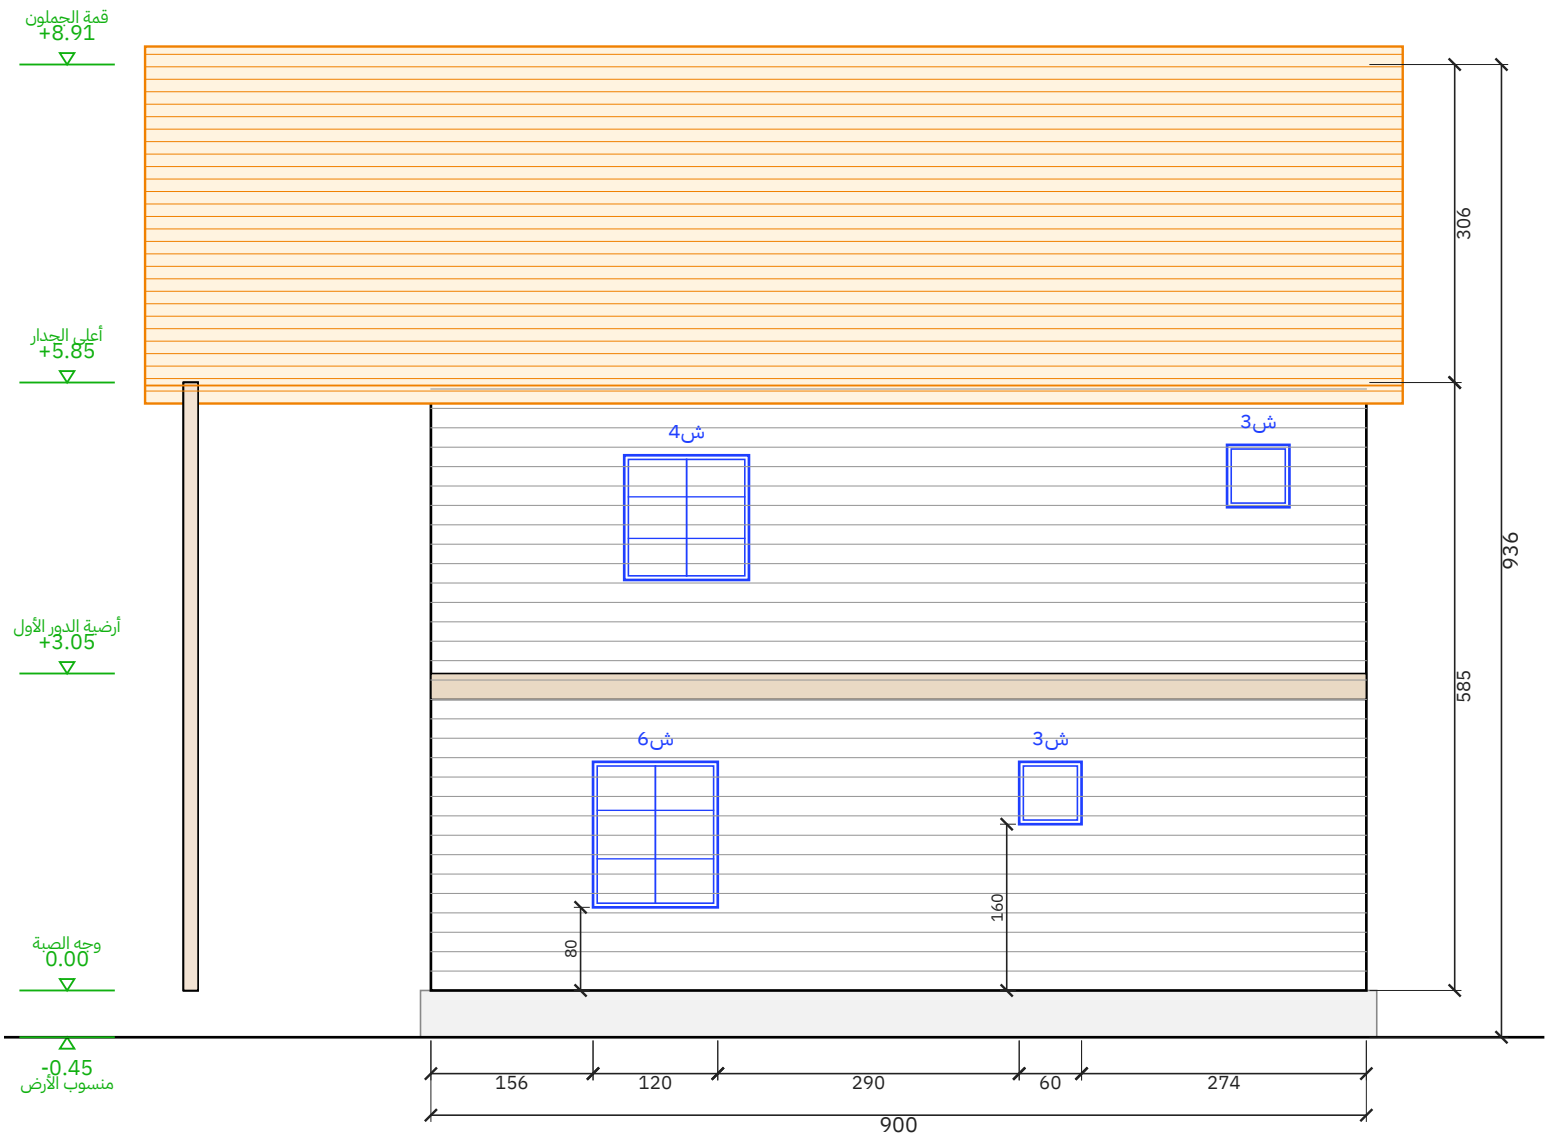


الواجهة الشرقية

مقياس 1:50 | الوحدة: سم


المشروع / العميل	عنوان اللوحة	المقياس	التاريخ	رقم اللوحة
كوخ الهدا – دورين – 3 غرف نوم + مجلس + بلكونة – 10.60 × 9.00 م عميل – الهدا	الواجهة الأمامية والواجهة الشرقية	1:50	2026-11-08	W-04 (4/24)

مصنع وتد الأخشاب
Watad Wood Factory

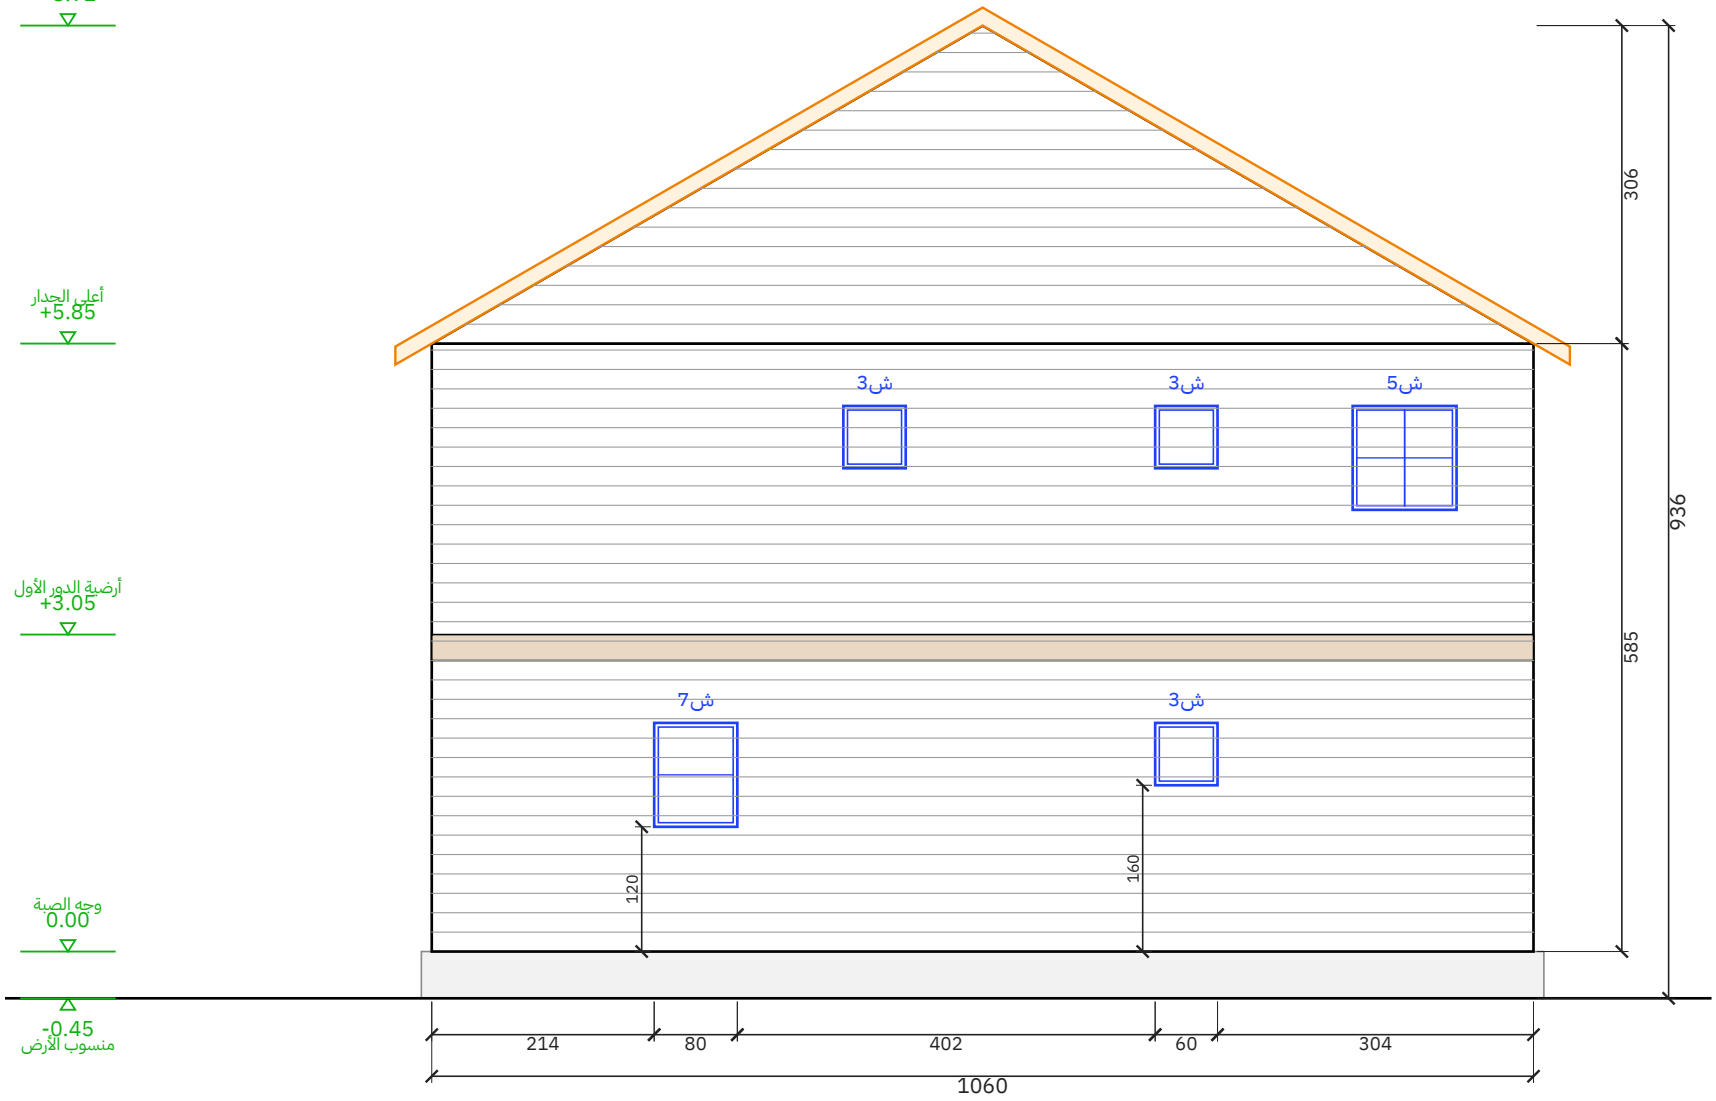

الواجهة الخلفية

مقياس 1:50 | الوحدة: سم

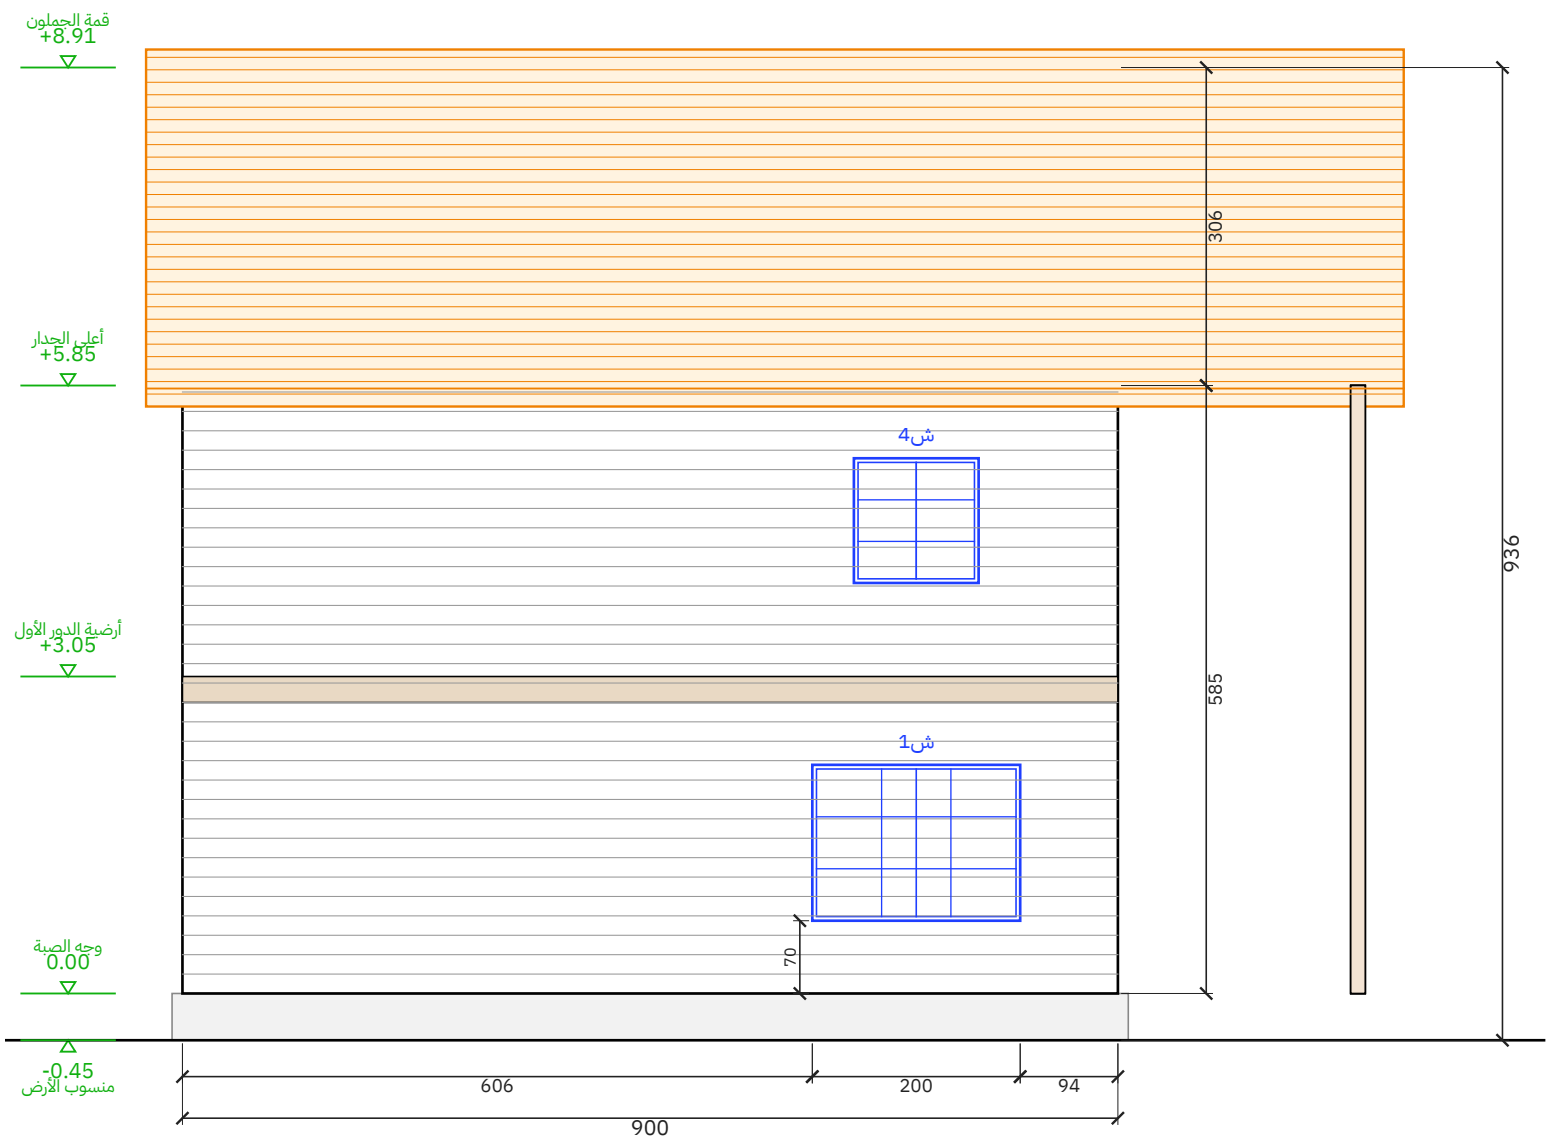

الواجهة الغربية


مقياس 1:50 | الوحدة: سم

المشروع / العميل	عنوان اللوحة	المقياس	التاريخ	رقم اللوحة
كوخ الهدا – دورين – 3 غرف نوم + مجلس + بلكونة – 10.60 × 9.00 م **عميل – الهدا**	**الواجهة الخلفية والواجهة الغربية**	**1:50**	**2026-11-08**	**W-05 (5/24)**

مصنع وتد الأخشاب
Watad Wood Factory


مسقط السقف (جملون)

رفرف 35 سم من كل جهة | مقياس 1:50

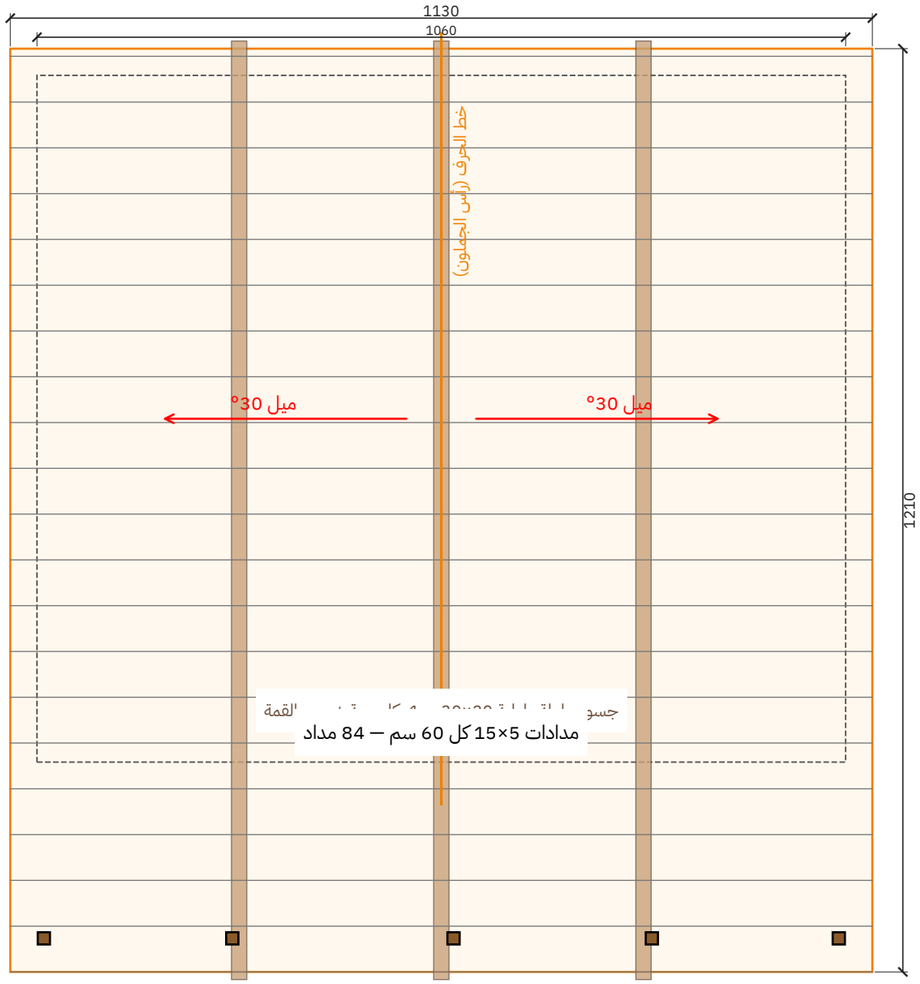


قطاع عرضي أ-أ

مقياس 1:50 | الوحدة: سم

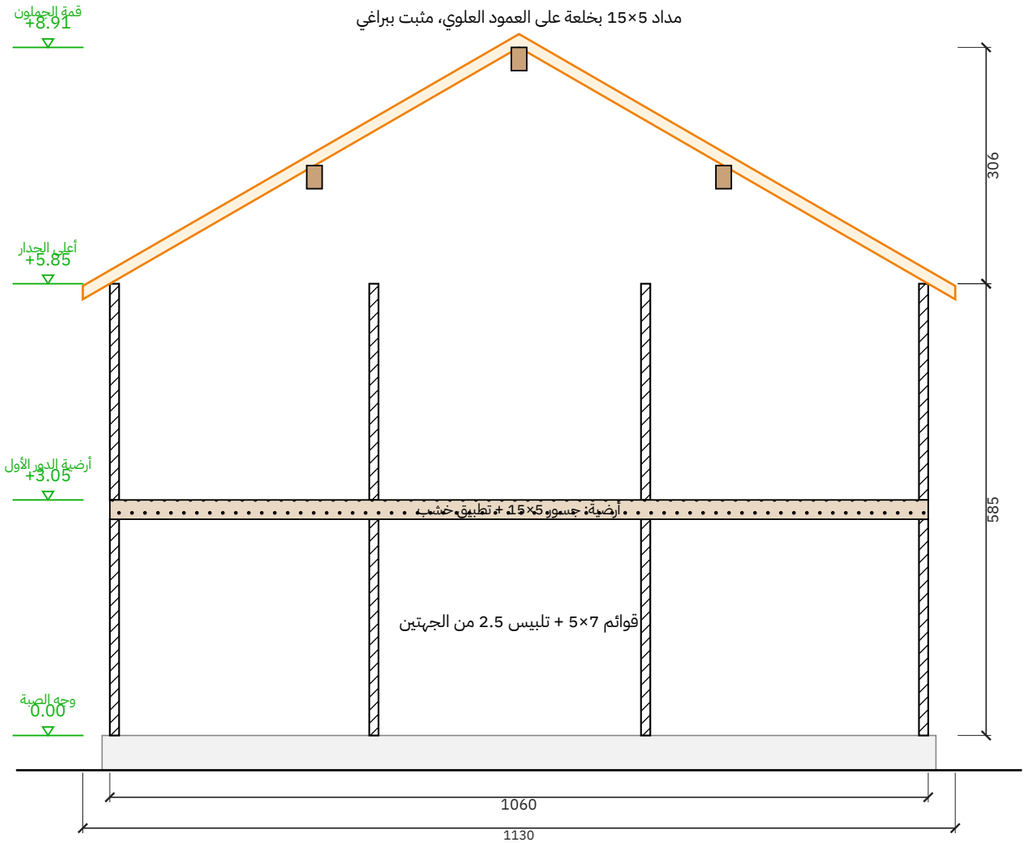

تفصيلة جلوس المداد على العلوي (1:5)

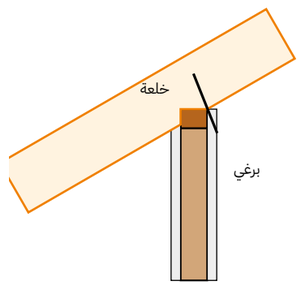

علوي 7×5 على قائم 7×5

المشروع / العميل **كوخ الهدا — دورين — 3 غرف نوم + مجلس + بلكونة — 10.60 × 9.00 م** **عميل — الهدا**	عنوان اللوحة **مسقط السقف والقطاع**	المقياس **—**	التاريخ **2026-11-08**	رقم اللوحة **W-06 (6/24)**

مصنع وتد الأخشاب
Watad Wood Factory

جدول مقاسات الأبواب والشبابيك

مقاس الفتحة الصافي في الجدار - الوحدة: سم

الرمز	النوع	العرض (سم)	الارتفاع (سم)	ارتفاع الجلسة (سم)	العدد	الموقع
ب1	باب مزدوج	260	240	-	1	الأمامية
ب1	باب مزدوج	170	240	-	1	الأمامية
ب10	باب	100	220	-	1	المجلس (من الصالة)
ب11	باب	70	210	-	1	دورة مياه المجلس
ب12	باب	80	210	-	1	غرفة الشغالة (من المطبخ)
ب15	باب	82	220	-	1	غرفة نوم 3
ب16	باب	80	210	-	1	غرفة الملابس (غرفة 3)
ب17	باب	70	210	-	1	حمام الشغالة
ب18	باب	80	210	-	1	حمام غرفة 3
ب2	باب	100	240	-	1	الأمامية
ب3	باب	70	210	-	1	حمام الصالة
ب4	باب مزدوج	220	220	-	1	الأمامية (على البلكونة)
ب4	باب مزدوج	230	220	-	1	الأمامية (على البلكونة)
ب4	باب مزدوج	200	220	-	1	الأمامية (على البلكونة)
ب5	باب	70	210	-	1	غرفة نوم 2
ب6	باب	80	210	-	1	الماستر
ب7	باب	80	210	-	1	المطبخ
ب8	باب	70	210	-	1	الحمام
ب9	باب	70	210	-	1	الحمام
ف1	باب	300	220	-	1	فتحة الجلسة — الموزع والدرج
ف2	باب	200	220	-	1	فتحة المطبخ
ف3	باب	88	220	-	1	فتحة المدخل — الموزع
ف4	باب	284	250	-	1	بارتشن أعمدة خشب
ف5	باب	82	220	-	1	الممر — غرفة 3
ش1	شباك	200	150	70	1	الغربية
ش3	شباك	60	60	160	5	الشرقية 2 - الخلفية 3
ش4	شباك	120	120	90	2	الشرقية - الغربية
ش5	شباك	100	100	120	1	الخلفية
ش6	شباك	160	140	80	1	الأمامية
ش6	شباك	120	140	80	1	الشرقية
ش7	شباك	80	100	120	1	الخلفية

الإجمالي: أبواب 24 - شبابيك 12

جدول المساحات وبيانات المشروع والتسعير

بيانات المشروع

البند	البيان
المشروع	كوخ الهدا — دورين — 3 غرف نوم + مجلس + بلكونة — 10.60 × 9.00 م
العميل	عميل — الهدا
الموقع	الهدا — الطائف
الاستخدام	كوخ سكني/استثماري
التاريخ	2026-11-08
نظام البناء	هيكل خشب 5×7 + تلبيس 2.5 سم من الجهتين
السقف	جملون 30° — قرميد معدني

جدول المساحات

م	الفراغ	الأبعاد (م)	المساحة (م2)
1	أرضي — الصالة	6.76 × 4.48	30.28
2	أرضي — الموزع	4.38 × 0.92	4.03
3	أرضي — الدرج	2.28 × 3.00	6.84
4	أرضي — حمام الصالة	1.98 × 3.12	6.18
5	أرضي — المطبخ	2.26 × 4.16	9.40
6	أرضي — المجلس	3.48 × 4.54	15.80
7	أرضي — حمام المجلس	1.68 × 2.28	3.83
8	أرضي — حمام الشغالة	1.68 × 2.28	3.83
9	أرضي — غرفة الشغالة	3.00 × 1.70	5.10
10	أول — غرفة نوم 2	3.24 × 4.48	14.52
11	أول — الماستر	3.40 × 4.48	15.23
12	أول — الممر	6.76 × 0.92	6.22
13	أول — الحمام (لغرفة 2)	1.98 × 3.12	6.18
14	أول — مطبخ	2.26 × 2.00	4.52
15	أول — حمام	2.26 × 1.00	2.26
16	أول — غرفة نوم 3	3.48 × 5.52	19.21
17	أول — ملابس غرفة 3	3.48 × 1.30	4.52
18	أول — حمام غرفة 3	3.48 × 1.70	5.92
	المساحة الصافية الداخلية		163.87
	التراس	**10.60 × 2.40**	**25.44**
	البلكونة	**10.60 × 2.40**	**25.44**
	المساحة الإجمالية المبنية	**10.60 × 9.00 × 2 دور**	**190.80**
	المساحة الكلية (المبنية + التراس والبلكونة)		**241.68**


التسعير المفصّل

البند	المبلغ (ريال)
الكوخ المبني 190.80 م² × 1,096	209,117
تراس الأرضي + البلكونة بالأول (10.60 × 2.40 × 2) — 50.88 م² × 1,096	55,764
الإجمالي (ريال)	**264,881**


ملاحظات:

- السعر للكوخ (الدورين) والتراس والبلكونات حسب المخطط المعتمد — التراس والبلكونة تُسعّر بنفس سعر متر الكوخ.
- أعمال الموقع (السور والبوابات والمسبح والجلسة الشتوية والبلاط والزراعة) عن طريق المقاول وتُسعّر منفصلة.
- الصبة والتمديدات الخارجية على العميل ما لم يُذكر غير ذلك.

تأطير جدار أ-جنوب — الطول 1048 سم، الارتفاع 280 سم

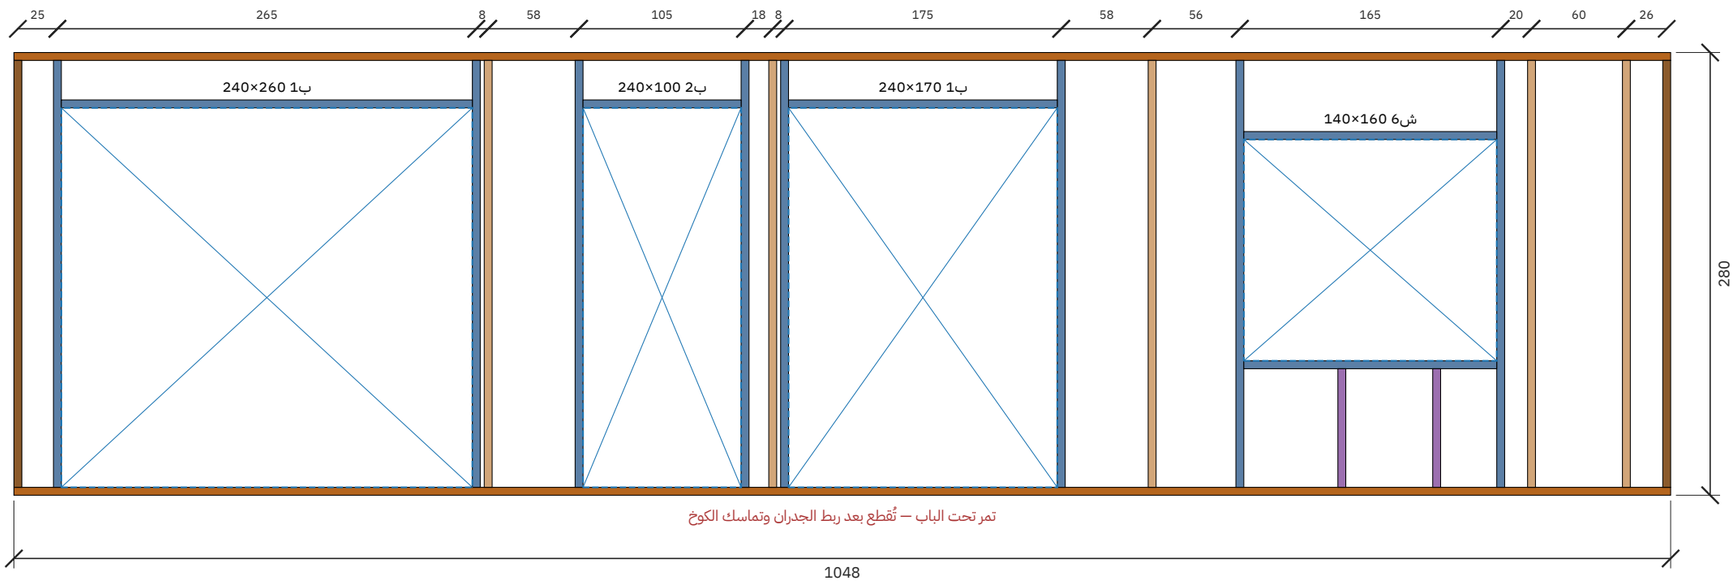


تأطير جدار أ-شرق — الطول 888 سم، الارتفاع 280 سم

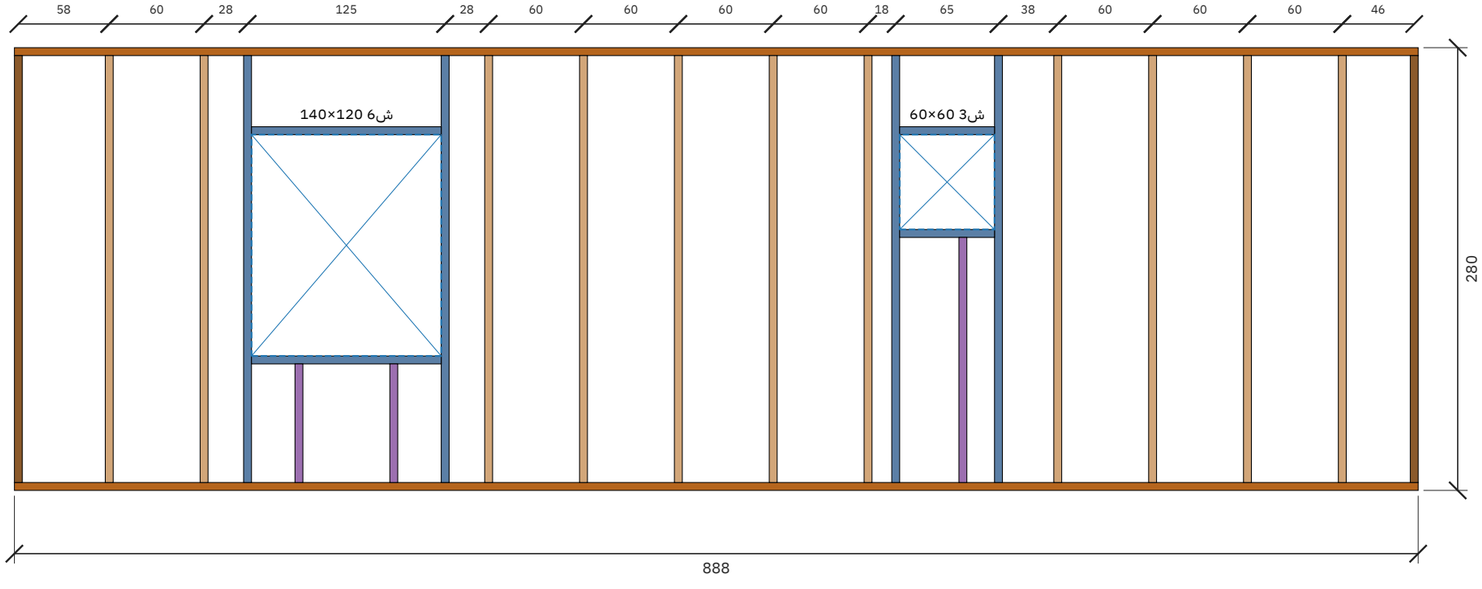


قاعدة سفلية | علوي | عمود | عمود زاوية | جنب فتحة | رأس فتحة | جلسة شباك | عمود قصير

مصنع وتد الأخشاب Watad Wood Factory	المشروع / العميل كوخ الهدا — دورين — 3 غرف نوم + مجلس + بلكونة — 10.60 × 9.00 م عميل — الهدا	عنوان اللوحة لوحات التأطير (للورشة)	المقياس —	التاريخ 2026-11-08	رقم اللوحة W-09 (9/24)

تأطير جدار أ-فاصل المجلس — الطول 706 سم، الارتفاع 280 سم (داخلي)

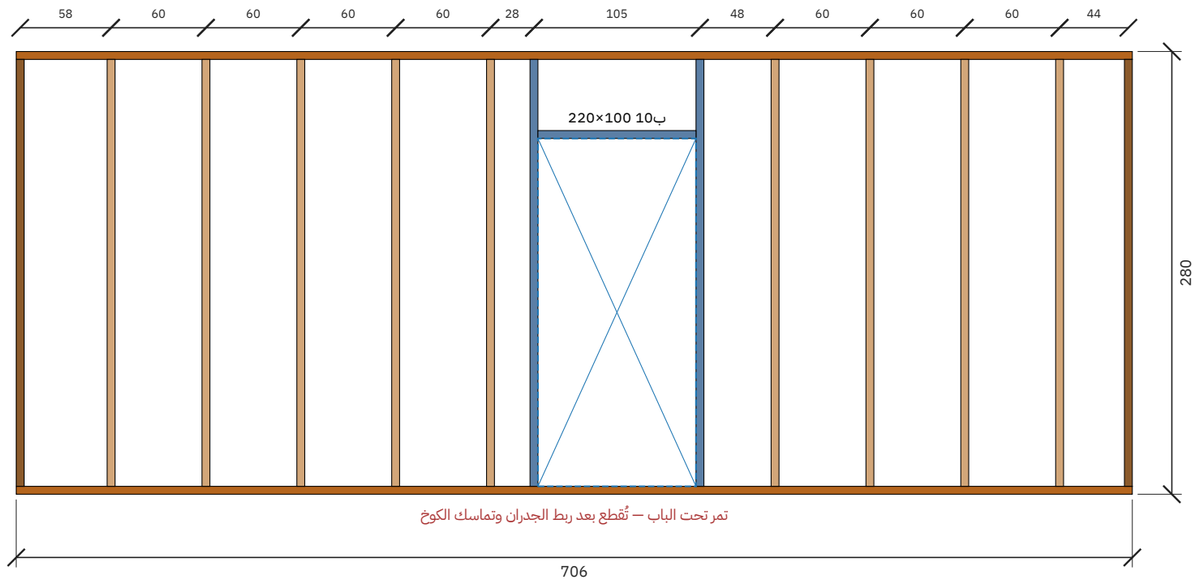


تأطير جدار أ-فاصل دورة المياه — الطول 360 سم، الارتفاع 280 سم (داخلي)

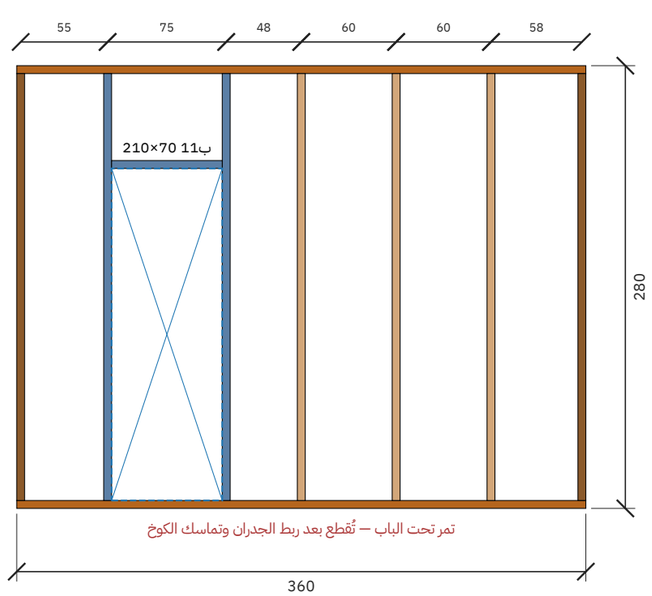


قاعدة سفلية | علوي | عمود | عمود زاوية | جنب فتحة | رأس فتحة | جلسة شباك | عمود قصير

مصنع وتد الأخشاب Watad Wood Factory	المشروع / العميل كوخ الهدا — دورين — 3 غرف نوم + مجلس + بلكونة — 10.60 × 9.00 م عميل — الهدا	عنوان اللوحة لوحات التأطير (للورشة)	المقياس —	التاريخ 2026-11-08	رقم اللوحة W-10 (10/24)

تأطير جدار أ-فاصل غرفة الشغالة — الطول 360 سم، الارتفاع 280 سم (داخلي)

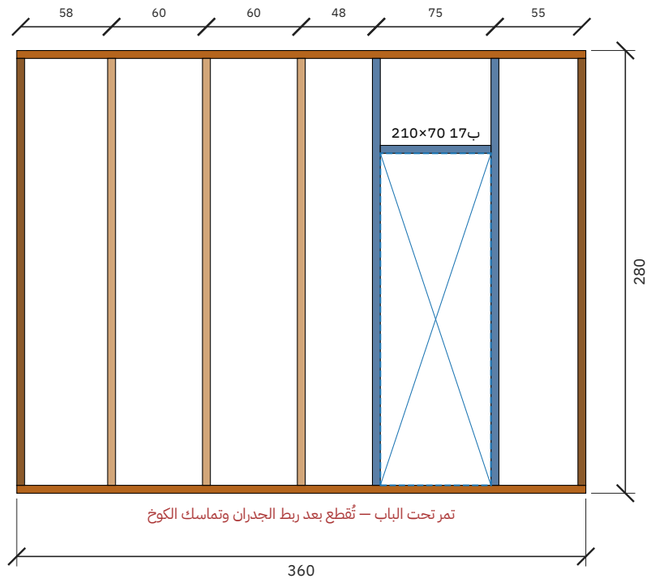


تأطير جدار أ-جدار غرفة الشغالة — المطبخ — الطول 182 سم، الارتفاع 280 سم (داخلي)

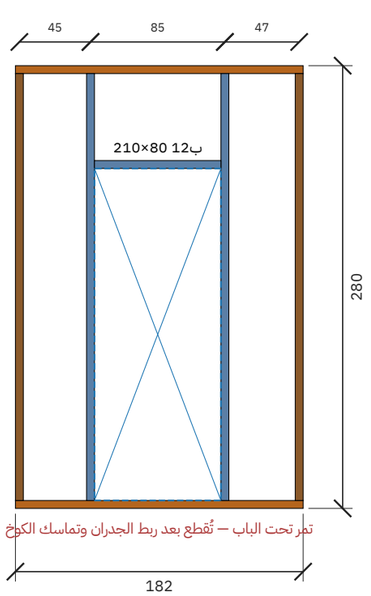


قاعدة سفلية | علوي | عمود | عمود زاوية | جنب فتحة | رأس فتحة | جلسة شباك | عمود قصير

مصنع وتد الأخشاب Watad Wood Factory	المشروع / العميل كوخ الهدا — دورين — 3 غرف نوم + مجلس + بلكونة — 10.60 × 9.00 م عميل — الهدا	عنوان اللوحة لوحات التأطير (للورشة)	المقياس —	التاريخ 2026-11-08	رقم اللوحة W-11 (11/24)

تأطير جدار أ-فاصل دورتي المياه — الطول 240 سم، الارتفاع 280 سم (داخلي)

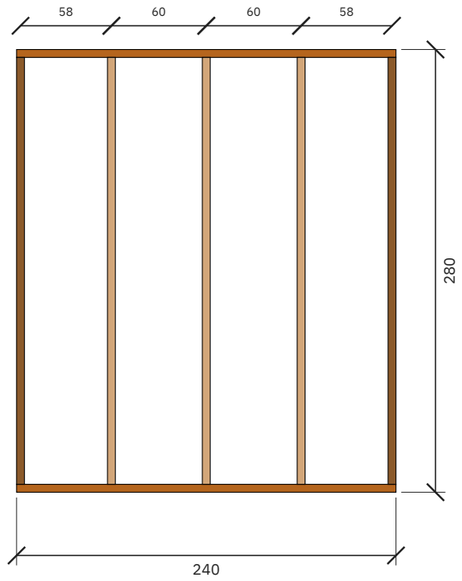

تأطير جدار أ-شمال — الطول 1048 سم، الارتفاع 280 سم

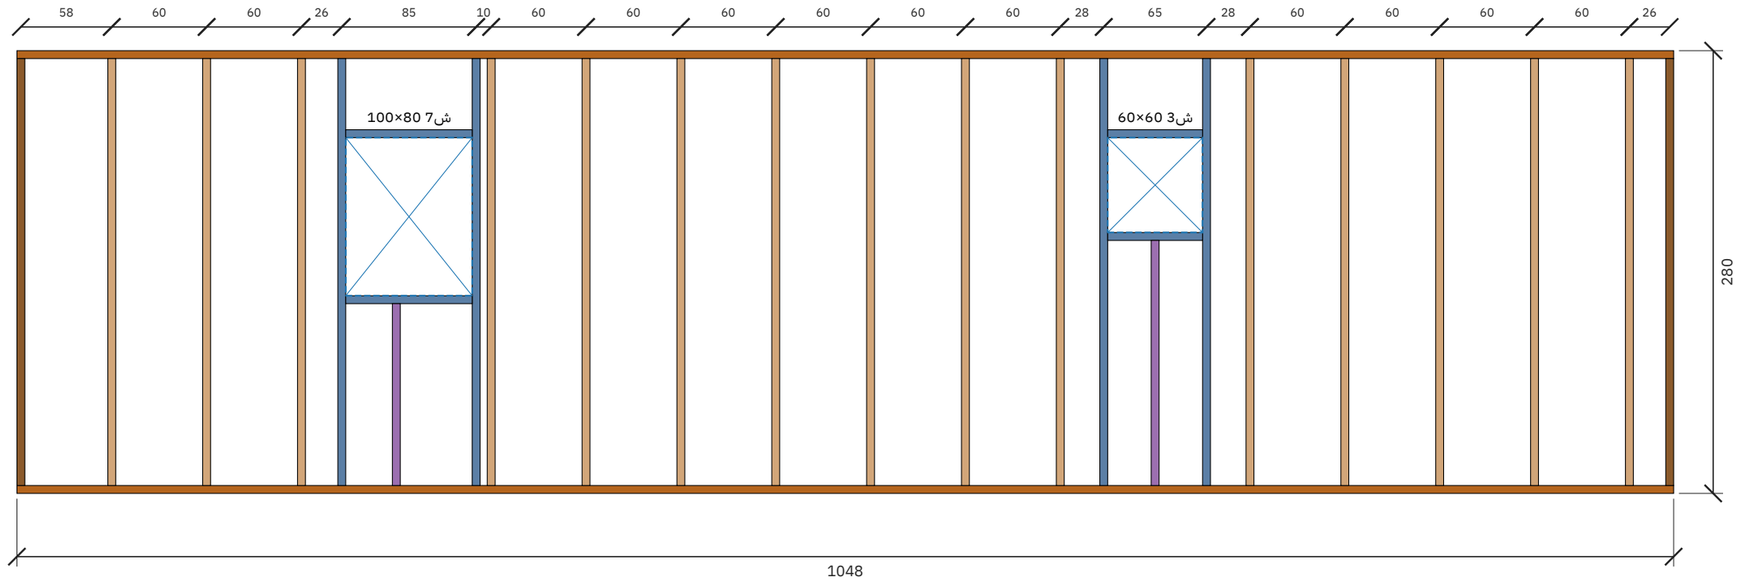


قاعدة سفلية | علوي | عمود | عمود زاوية | جنب فتحة | رأس فتحة | جلسة شباك | عمود قصير


المشروع / العميل	عنوان اللوحة	المقياس	التاريخ	رقم اللوحة
كوخ الهدا — دورين — 3 غرف نوم + مجلس + بلكونة — 10.60 × 9.00 م **عميل — الهدا**	**لوحات التأطير (للورشة)**	—	**2026-11-08**	**W-12 (12/24)**

مصنع وتد الأخشاب
Watad Wood Factory

تأطير جدار أ-غرب — الطول 888 سم، الارتفاع 280 سم

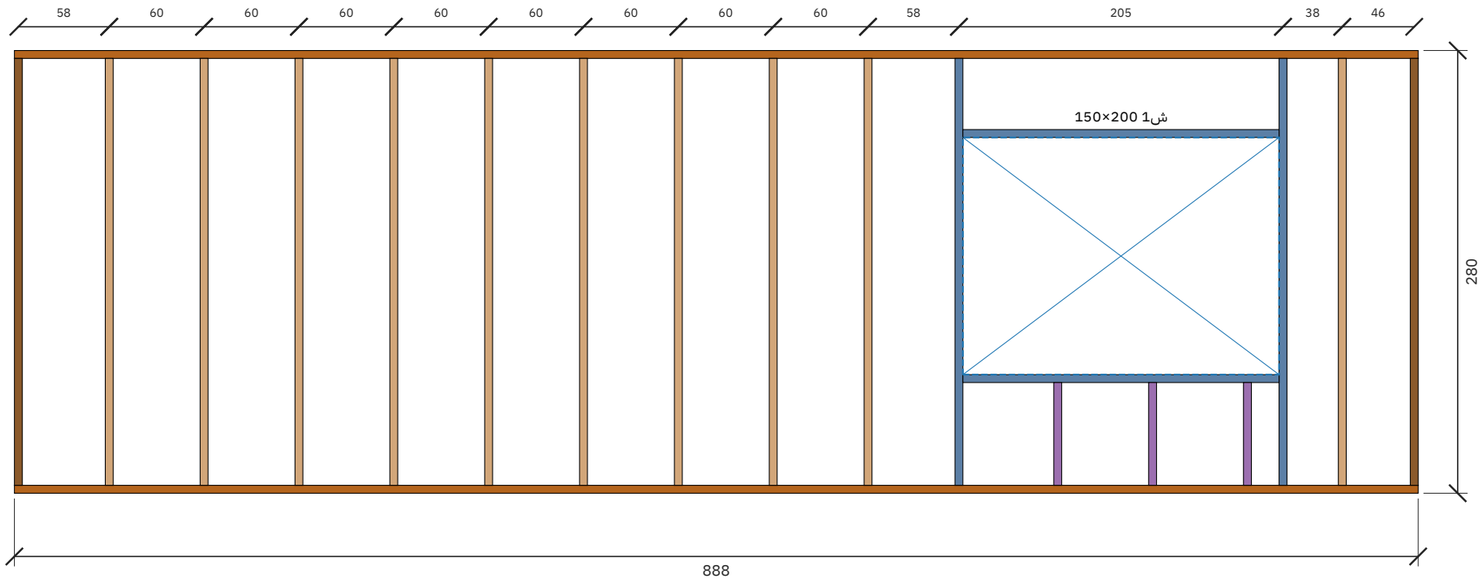


تأطير جدار أ-فاصل الصالة — الطول 688 سم، الارتفاع 280 سم (داخلي)

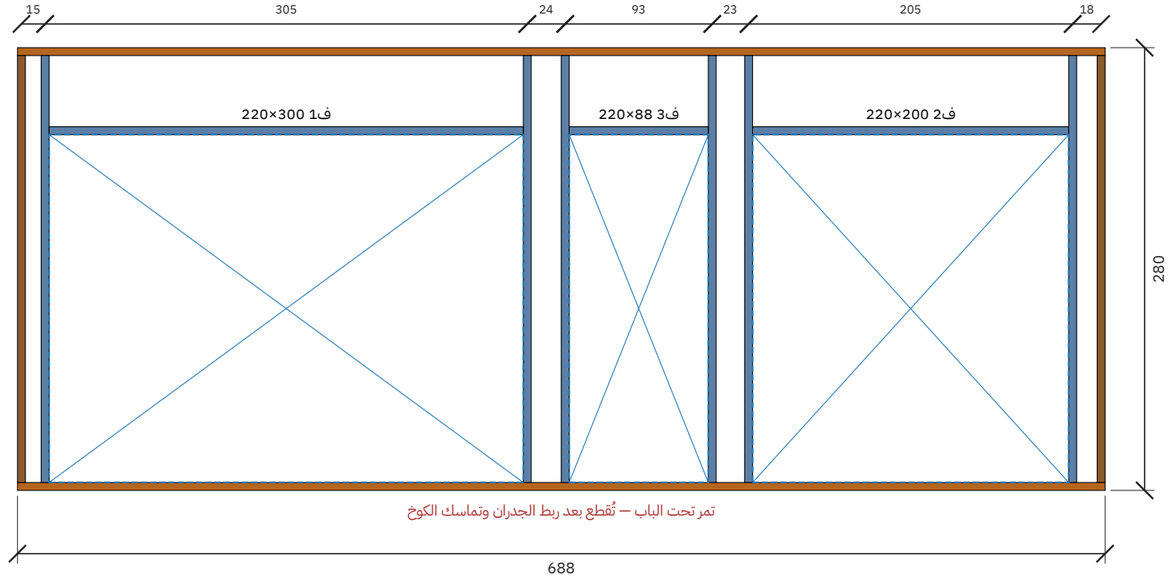


قاعدة سفلية · علوي · عمود · عمود زاوية · جنب فتحة · رأس فتحة · جلسة شباك · عمود قصير

مصنع وتد الأخشاب Watad Wood Factory	المشروع / العميل كوخ الهدا — دورين — 3 غرف نوم + مجلس + بلكونة — 10.60 × 9.00 م عميل — الهدا	عنوان اللوحة لوحات التأطير (للورشة)	المقياس —	التاريخ 2026-11-08	رقم اللوحة W-13 (13/24)

تأطير جدار أ-بارتشن الصالة — الطول 310 سم، الارتفاع 280 سم (داخلي)

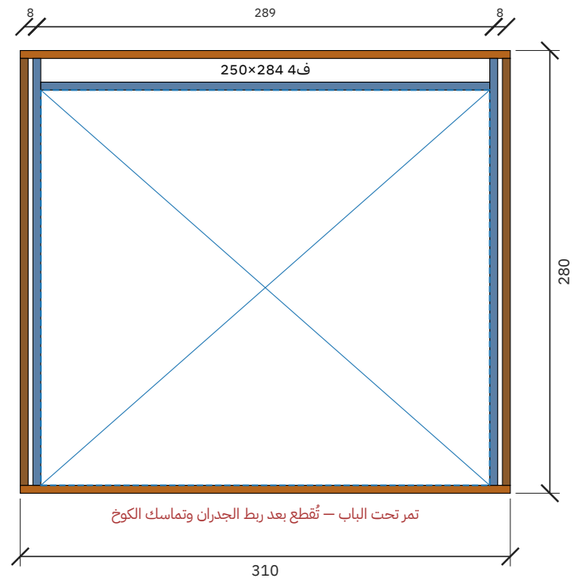


تأطير جدار أ-فاصل الحمام — الطول 210 سم، الارتفاع 280 سم (داخلي)

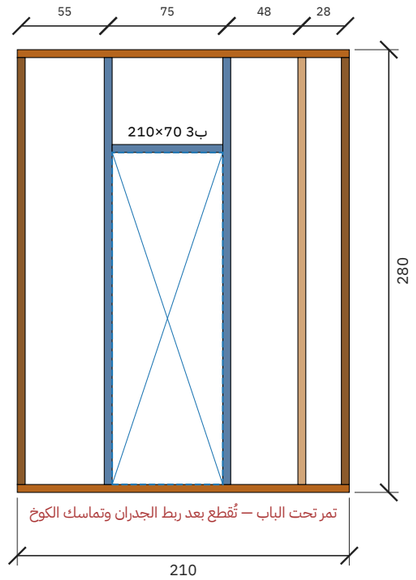


قاعدة سفلية | علوي | عمود | عمود زاوية | جنب فتحة | رأس فتحة | جلسة شباك | عمود قصير

مصنع وتد الأخشاب Watad Wood Factory	المشروع / العميل **كوخ الهدا — دورين — 3 غرف نوم + مجلس + بلكونة — 10.60 × 9.00 م** **عميل — الهدا**	عنوان اللوحة **لوحات التأطير (للورشة)**	المقياس **—**	التاريخ **2026-11-08**	رقم اللوحة **W-14 (14/24)**

تأطير جدار أ-جدار الدرج — الطول 324 سم، الارتفاع 280 سم (داخلي)

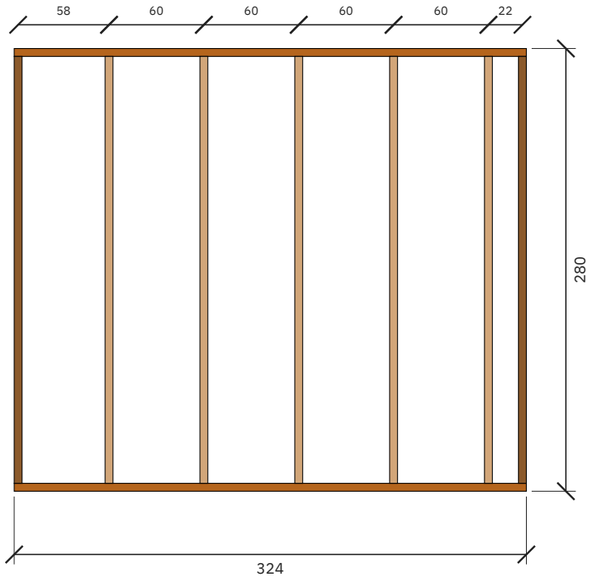


تأطير جدار أ-جدار المطبخ — الطول 428 سم، الارتفاع 280 سم (داخلي)

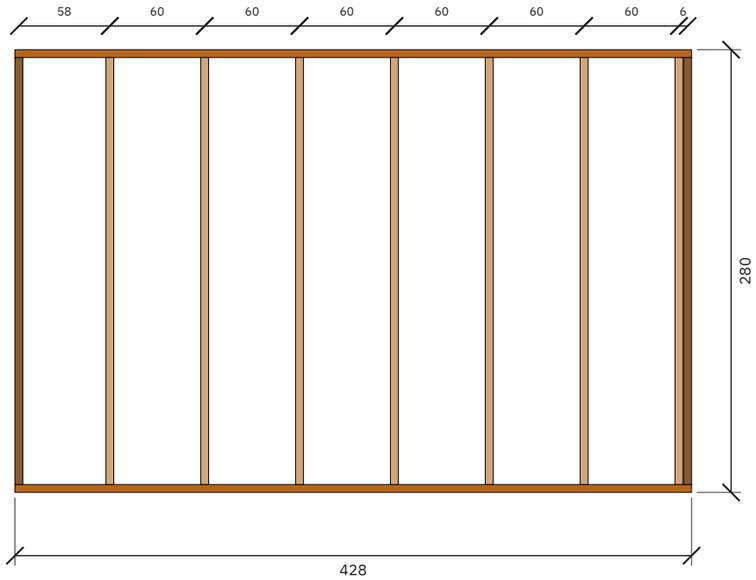


قاعدة سفلية | علوي | عمود | عمود زاوية | جنب فتحة | رأس فتحة | جلسة شباك | عمود قصير

مصنع وتد الأخشاب Watad Wood Factory	المشروع / العميل كوخ الهدا — دورين — 3 غرف نوم + مجلس + بلكونة — 10.60 × 9.00 م عميل — الهدا	عنوان اللوحة لوحات التأطير (للورشة)	المقياس —	التاريخ 2026-11-08	رقم اللوحة W-15 (15/24)

تأطير جدار ب-جنوب — الطول 1048 سم، الارتفاع 280 سم

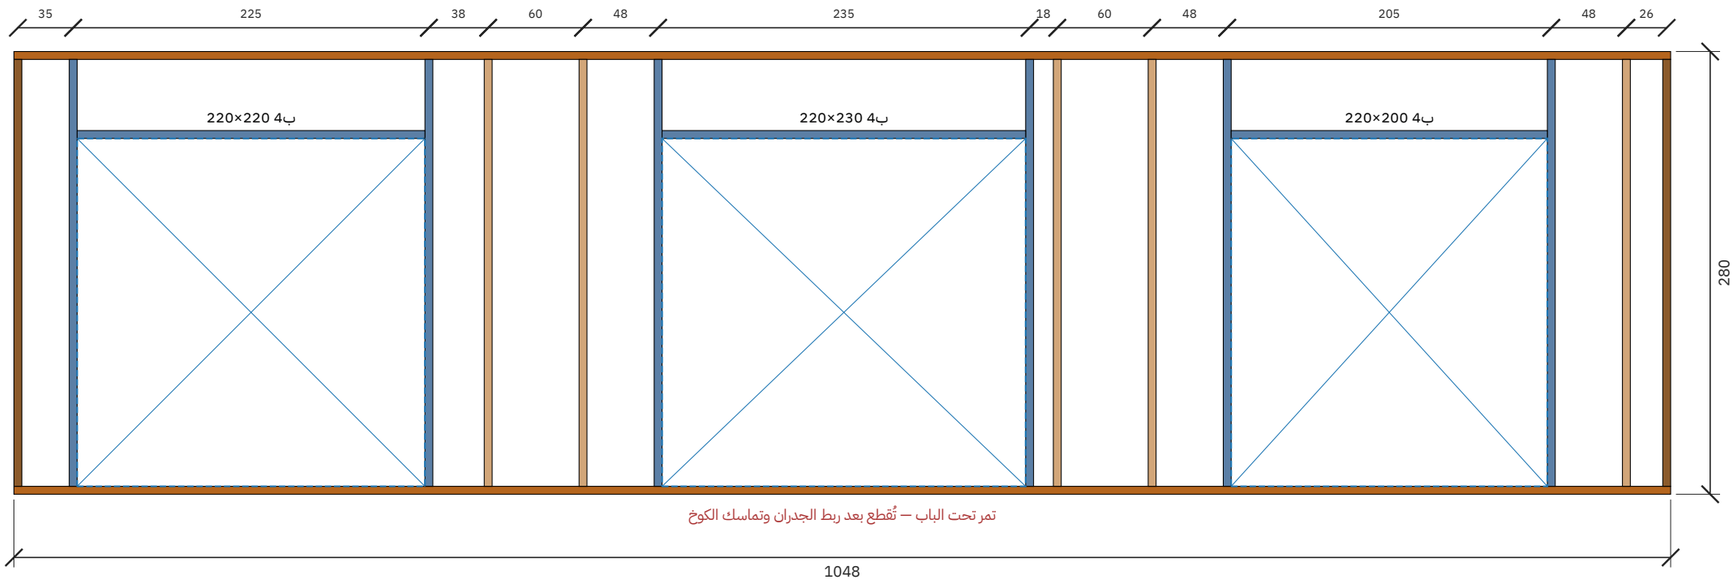

تأطير جدار ب-شرق — الطول 888 سم، الارتفاع 280 سم

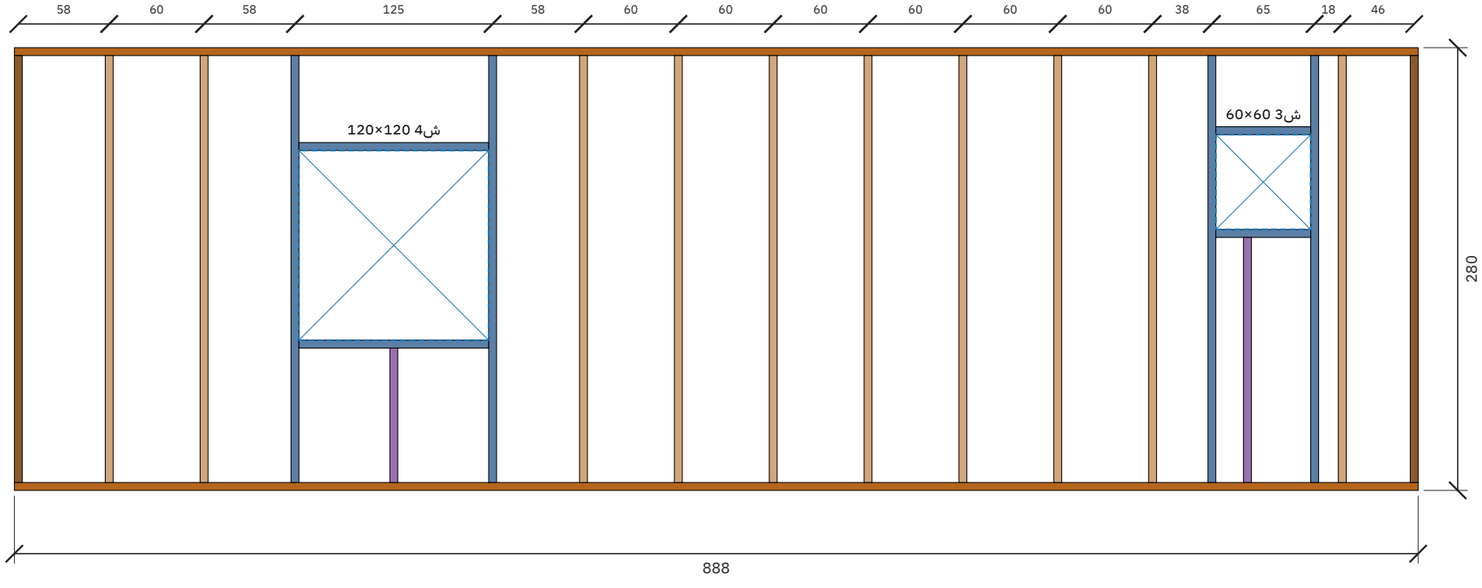


قاعدة سفلية | علوي | عمود | عمود زاوية | جنب فتحة | رأس فتحة | جلسة شباك | عمود قصير


المشروع / العميل	عنوان اللوحة	المقياس	التاريخ	رقم اللوحة
كوخ الهدا — دورين — 3 غرف نوم + مجلس + بلكونة — 10.60 × 9.00 م **عميل — الهدا**	**لوحات التأطير (للورشة)**	**—**	**2026-11-08**	**W-16 (16/24)**

مصنع وتد الأخشاب
Watad Wood Factory

تأطير جدار ب-شمال — الطول 1048 سم، الارتفاع 280 سم

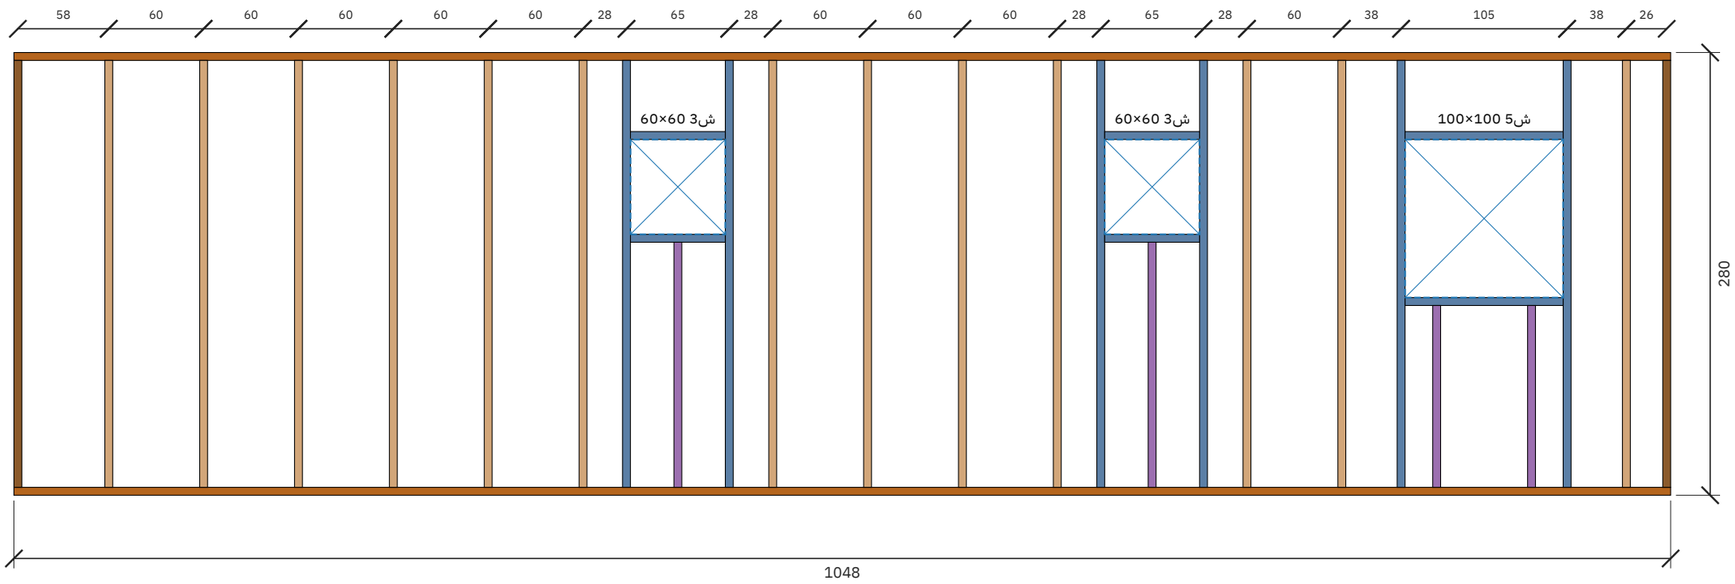


تأطير جدار ب-غرب — الطول 888 سم، الارتفاع 280 سم

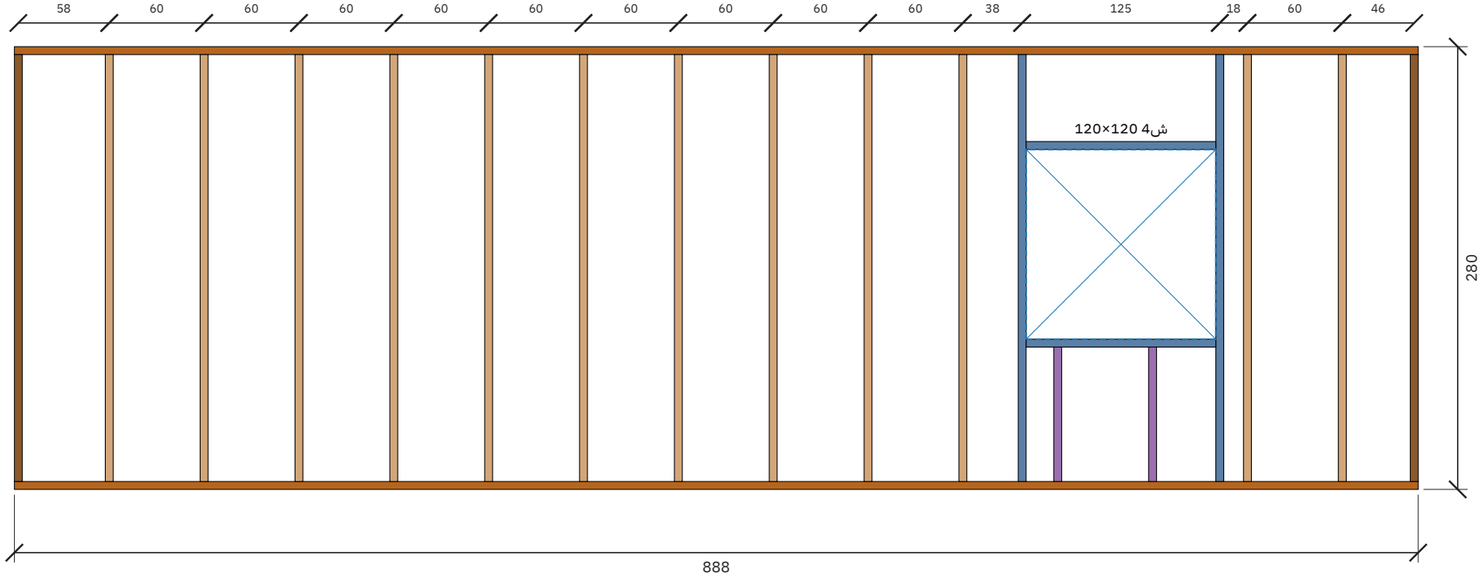


قاعدة سفلية | علوي | عمود | عمود زاوية | جنب فتحة | رأس فتحة | جلسة شباك | عمود قصير

مصنع وتد الأخشاب Watad Wood Factory	المشروع / العميل كوخ الهدا — دورين — 3 غرف نوم + مجلس + بلكونة — 10.60 × 9.00 م عميل — الهدا	عنوان اللوحة لوحات التأطير (للورشة)	المقياس —	التاريخ 2026-11-08	رقم اللوحة W-17 (17/24)

تأطير جدار ب-فاصل أمامي — الطول 688 سم، الارتفاع 280 سم (داخلي)

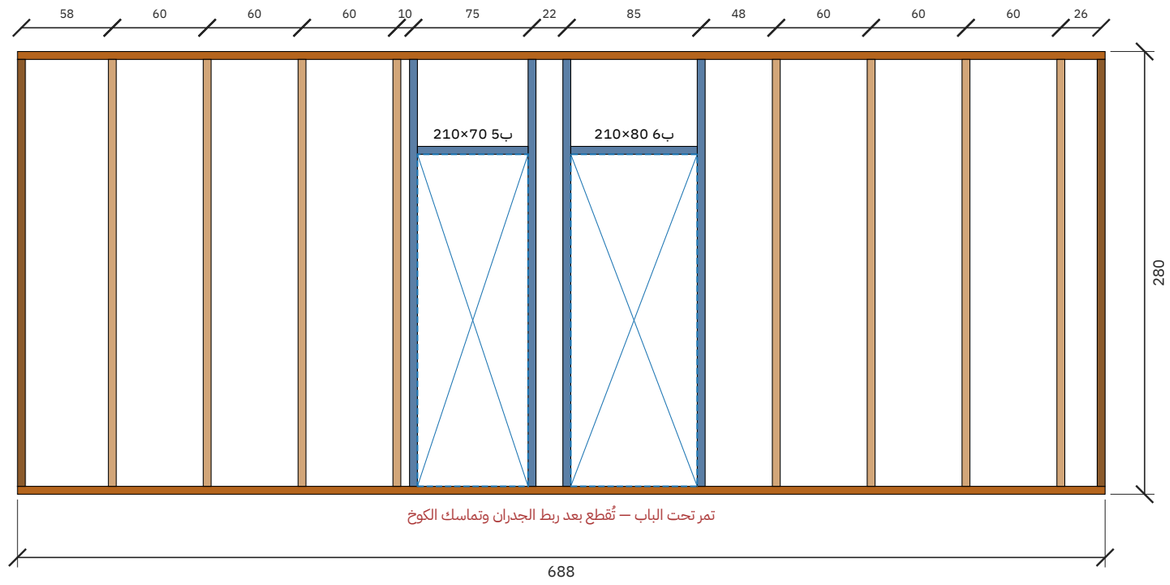


تأطير جدار ب-فاصل الغرف — الطول 460 سم، الارتفاع 280 سم (داخلي)

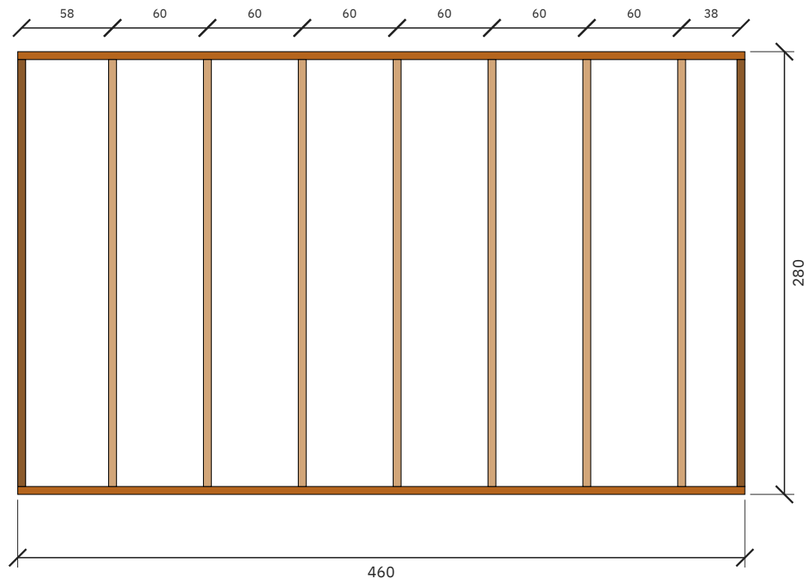


قاعدة سفلية | علوي | عمود | عمود زاوية | جنب فتحة | رأس فتحة | جلسة شباك | عمود قصير

مصنع وتد الأخشاب Watad Wood Factory	المشروع / العميل كوخ الهدا — دورين — 3 غرف نوم + مجلس + بلكونة — 10.60 × 9.00 م عميل — الهدا	عنوان اللوحة لوحات التأطير (للورشة)	المقياس —	التاريخ 2026-11-08	رقم اللوحة W-18 (18/24)

تأطير جدار ب-فاصل الحمام — الطول 210 سم، الارتفاع 280 سم (داخلي)

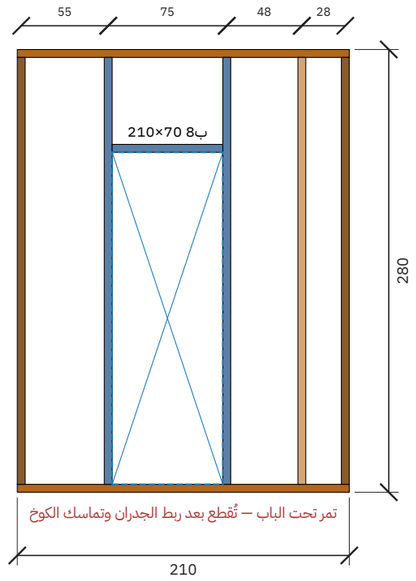


تأطير جدار ب-جدار الدرج — الطول 324 سم، الارتفاع 280 سم (داخلي)

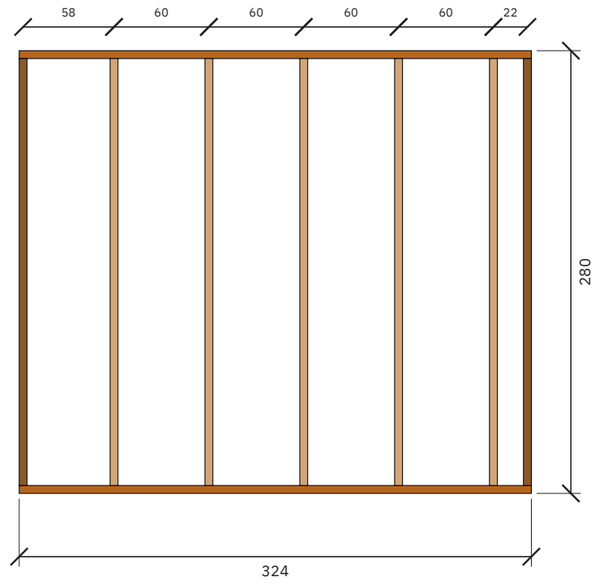


قاعدة سفلية | علوي | عمود | عمود زاوية | جنب فتحة | رأس فتحة | جلسة شباك | عمود قصير

مصنع وتد الأخشاب Watad Wood Factory	المشروع / العميل كوخ الهدا — دورين — 3 غرف نوم + مجلس + بلكونة — 10.60 × 9.00 م عميل — الهدا	عنوان اللوحة لوحات التأطير (للورشة)	المقياس —	التاريخ 2026-11-08	رقم اللوحة W-19 (19/24)

تأطير جدار ب-جدار الملابس — الطول 428 سم، الارتفاع 280 سم (داخلي)

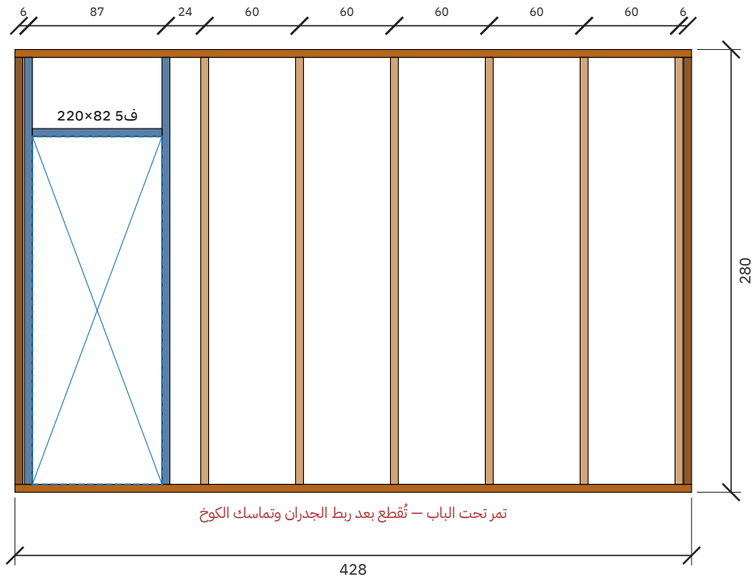


تأطير جدار ب-فاصل المطبخ — الطول 238 سم، الارتفاع 280 سم (داخلي)

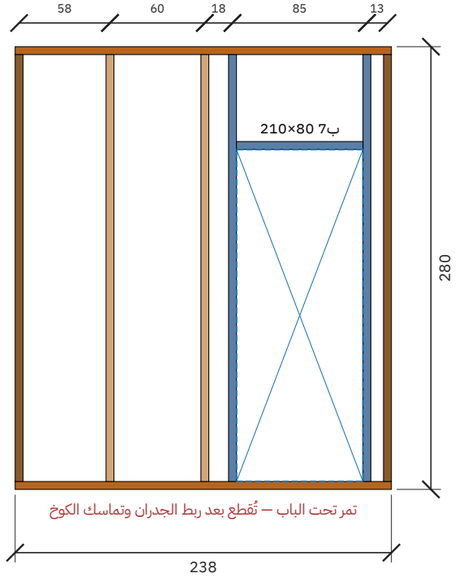


قاعدة سفلية · علوي · عمود · عمود زاوية · جنب فتحة · رأس فتحة · جلسة شباك · عمود قصير

مصنع وتد الأخشاب Watad Wood Factory	المشروع / العميل **كوخ الهدا — دورين — 3 غرف نوم + مجلس + بلكونة — 10.60 × 9.00 م** **عميل — الهدا**	عنوان اللوحة **لوحات التأطير (للورشة)**	المقياس **—**	التاريخ **2026-11-08**	رقم اللوحة **W-20 (20/24)**

تأطير جدار ب-فاصل الحمام (المطبخ) — الطول 238 سم، الارتفاع 280 سم (داخلي)

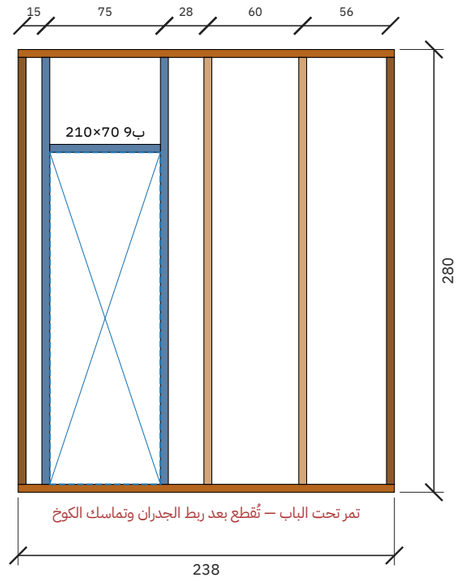

تأطير جدار ب-فاصل غرفة 3 — الطول 888 سم، الارتفاع 280 سم (داخلي)

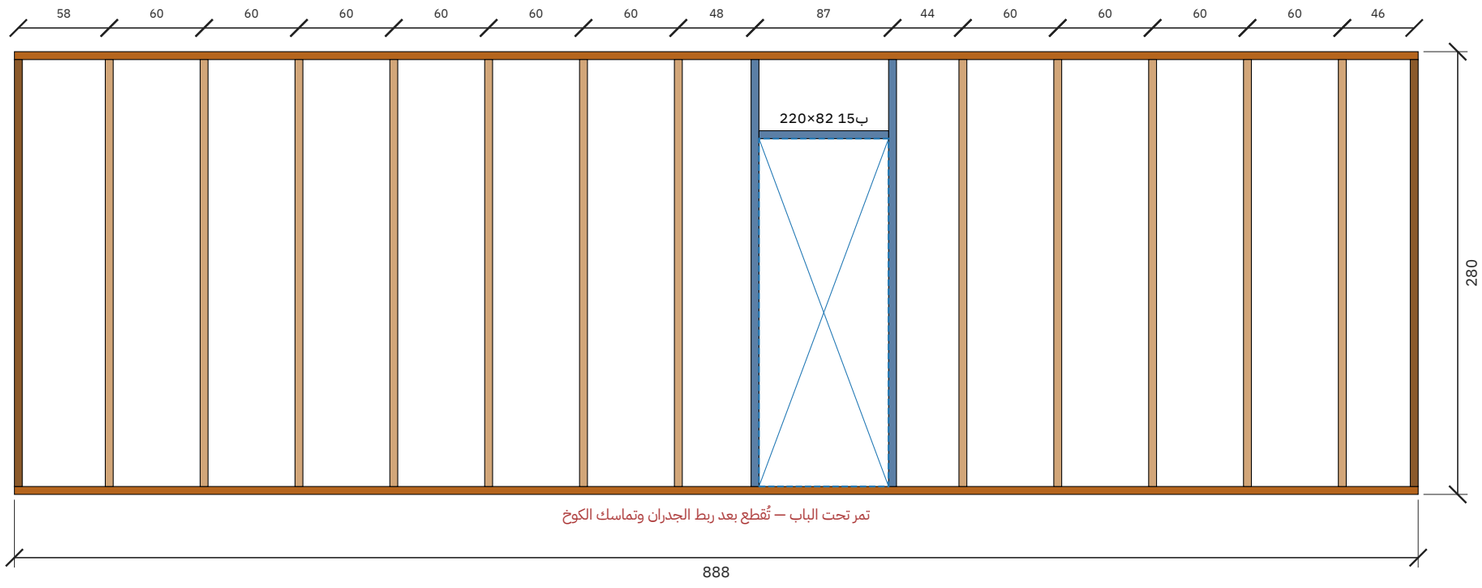


قاعدة سفلية | علوي | عمود | عمود زاوية | جنب فتحة | رأس فتحة | جلسة شباك | عمود قصير


المشروع / العميل	عنوان اللوحة	المقياس	التاريخ	رقم اللوحة
كوخ الهدا — دورين — 3 غرف نوم + مجلس + بلكونة — 10.60 × 9.00 م عميل — الهدا	لوحات التأطير (للورشة)	—	2026-11-08	W-21 (21/24)

مصنع وتد الأخشاب
Watad Wood Factory

تأطير جدار ب-فاصل حمام غرفة 3 — الطول 360 سم، الارتفاع 280 سم (داخلي)

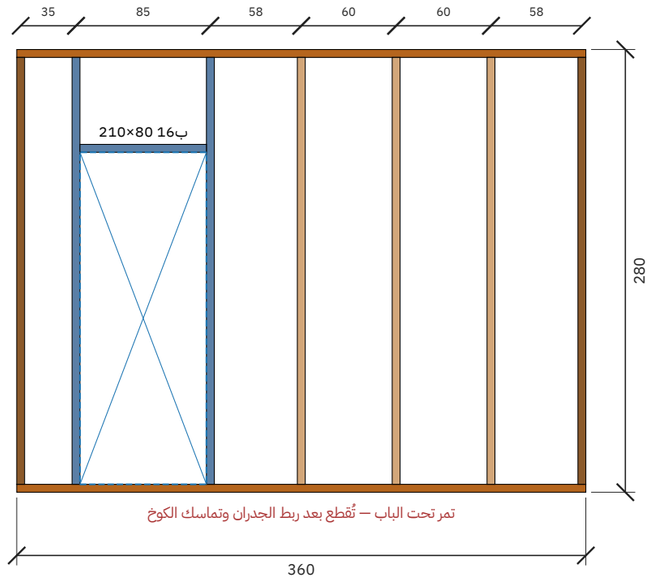

تأطير جدار ب-فاصل الملابس — حمام غرفة 3 — الطول 360 سم، الارتفاع 280 سم (داخلي)

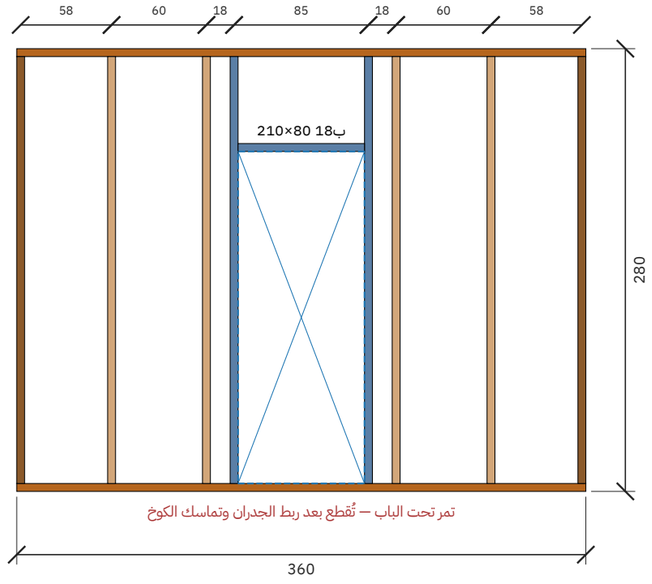

قاعدة سفلية | علوي | عمود | عمود زاوية | جنب فتحة | رأس فتحة | جلسة شباك | عمود قصير

المشروع / العميل	عنوان اللوحة	المقياس	التاريخ	رقم اللوحة
كوخ الهدا — دورين — 3 غرف نوم + مجلس + بلكونة — 10.60 × 9.00 م عميل — الهدا	لوحات التأطير (للورشة)	—	2026-11-08	W-22 (22/24)

مصنع وتد الأخشاب
Watad Wood Factory

جدول الكميات وخطة تقطيع الطبليات

البند	القيمة
الارتفاع المطلوب / المعتمد	280 / 280 سم
السقف	جملون 30° — أعلى نقطة 891 سم من وجه الصبة
المدادات 5×15	84 مداد (21 خط × قطعتين موصولة فوق الجسر الحامل بتراكب 60 سم) × حتى 381 سم — من طبلية 480
طبليات الطريقة الأولى (مداد + عمود)	84 طبلية × 480 سم
طبليات الطريقة الثانية (3 أعمدة)	99 طبلية × 320 سم
مدادات أرضية الدور العلوي 5×15 كل 60 سم	105 مداد — 58سم×15، 106سم×15، 124سم×15، 142سم×15، 190سم×15، 248سم×15، 250سم×15 (طبلية 320 بالطريقة الأولى)
إجمالي الطبليات 5×22.5	288
إجمالي قطع 5×7	412
قائمة تقطيع 5×7	1048سم×8 | 888سم×10 | 706سم×2 | 688سم×4 | 460سم×2 | 428سم×4 | 360سم×8 | 324سم×4 | 310سم×2
	300سم×1 | 284سم×1 | 270سم×290 | 260سم×1 | 240سم×2 | 238سم×4 | 230سم×1 | 220سم×1 | 210سم×4
ألواح تلبيس 2.5 سم	846 لوح × 400 سم (مجموع الصفوف 3003.2 م، 56 وجه)
أسمنت بورد 12 مم (122×244)	104 لوح (داخل دورات المياه)
العزل	497 لوح فوم صخري 80
الصبة	يجهزها العميل — 20 سم، مفرغة تحت دورات المياه

مراجعة التصميم مقابل قواعد المصنع

النوع	البند	التفاصيل	المقترح
خطأ	حمام المجلس بدون جدار خارجي	السباكة في المصنع تمشي من الخارج والصبة مفرغة تحت دورات المياه — هذا الحمام محصور داخل المبنى.	يُنقل الحمام ليلمس جدار خارجي، أو يُعتمد مسار سباكة تحت الصبة بقرار من المصنع.
تنبيه	تهوية حمام المجلس	لا يوجد شباك — يحتاج شفاط هواء.	إضافة شفاط أو شباك صغير.
ملاحظة	حمام غير مكدّس	دورة المياه العلوية ليست فوق دورة مياه أرضية — تحتاج خط صرف خارجي مستقل على الجدار.	يُفضّل تكديس الحمامات فوق بعض (قاعدة المصنع).
ملاحظة	حمام غرفة 3 غير مكدّس	دورة المياه العلوية ليست فوق دورة مياه أرضية — تحتاج خط صرف خارجي مستقل على الجدار.	يُفضّل تكديس الحمامات فوق بعض (قاعدة المصنع).
ملاحظة	بحر المدادات	أطول بحر بدون جدار داخلي يحمل المداد: جهة أ: 456 سم، جهة ب: 366 سم. يحتاج رقم المصنع لأقصى بحر مسموح لتحديد المدادات اللي تُقوّى 20×5.	
ملاحظة	الصبة والدرج	ارتفاع الصبة 45 سم ← 3 درجة بقائمة 15.0 سم.	
ملاحظة	مناسيب رؤوس الفتحات	رؤوس الأبواب والشبابيك على مناسيب مختلفة: 210، 220، 240، 250 سم.	
سؤال	يحتاج تأكيد	أقصى بحر للمداد بدون جدار داخلي قبل إضافة تقوية 7×5 (مداد 20×5)؟	
سؤال	يحتاج تأكيد	التغطية الصافية للوح التلبيس بعد التعشيق (مستنتجة مؤقتاً 18.67 سم من 280/15)؟	
سؤال	يحتاج تأكيد	هل يوضع أعمدة قصيرة فوق رأس الشباك/الباب إلى العلوي؟	
سؤال	يحتاج تأكيد	مكان الوصلة في القاعدة والعلوي إذا الجدار أطول من الطبلية؟	