


المنظور ثلاثي الأبعاد والمواد

النمط: جوزي غامق + إطارات سوداء — معاينة تقريبية، الإخراج النهائي من 3ds Max

جدول المواد والألوان

 

الخشب / الصبغة

خشب طبيعي فاتح (بدون صبغة)



القرميد

قرميد رمادي غامق



الزجاج

زجاج عاكس غامق



إطارات الشبابيك والأبواب

إطار ألومنيوم أسود



الكنار والزوايا

نفس الصبغة أعمق درجة



الصبة

خرسانة 45 سم


الدريزين: ألواح أفقية متقاربة (عصري)

تقسيم الشبابيك: بدون | الباب الرئيسي: سحب زجاج


أنواع الدريزين المعتمدة (من مشاريع المصنع)



قوائم رأسية متقاربة (صورة 1)

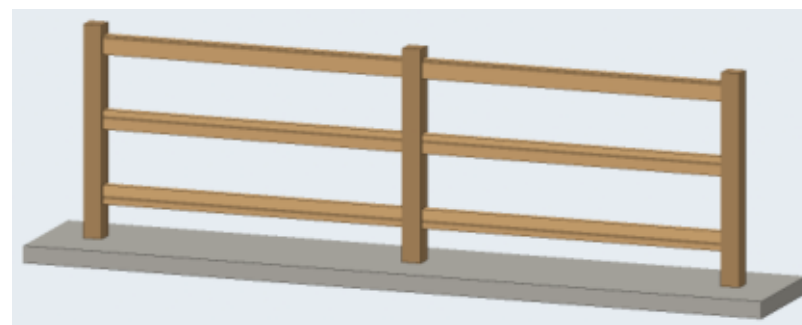

3 مربيع أفقية (صورة 2)

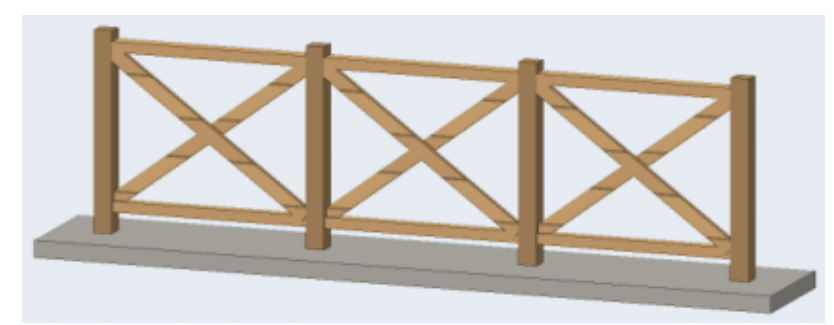

تقاطع X (صورة 5)

رقم اللوحة

W-01 (1/12)

التاريخ

2026-09-29

المقياس

1:50

عنوان اللوحة

المنظور والمواد

المشروع / العميل


كوخ غرفة وتراس 5x7 شامل التراس
عميل — تصميم حسب الصورة

مصنع وتد الأخشاب

Watad Wood Factory




المسقط الأفقي مع الفرش
الأبعاد بالسنتيمتر - الجدران: قوائم 5×7 + تليس 2.5 من الجهتين (12 سم)

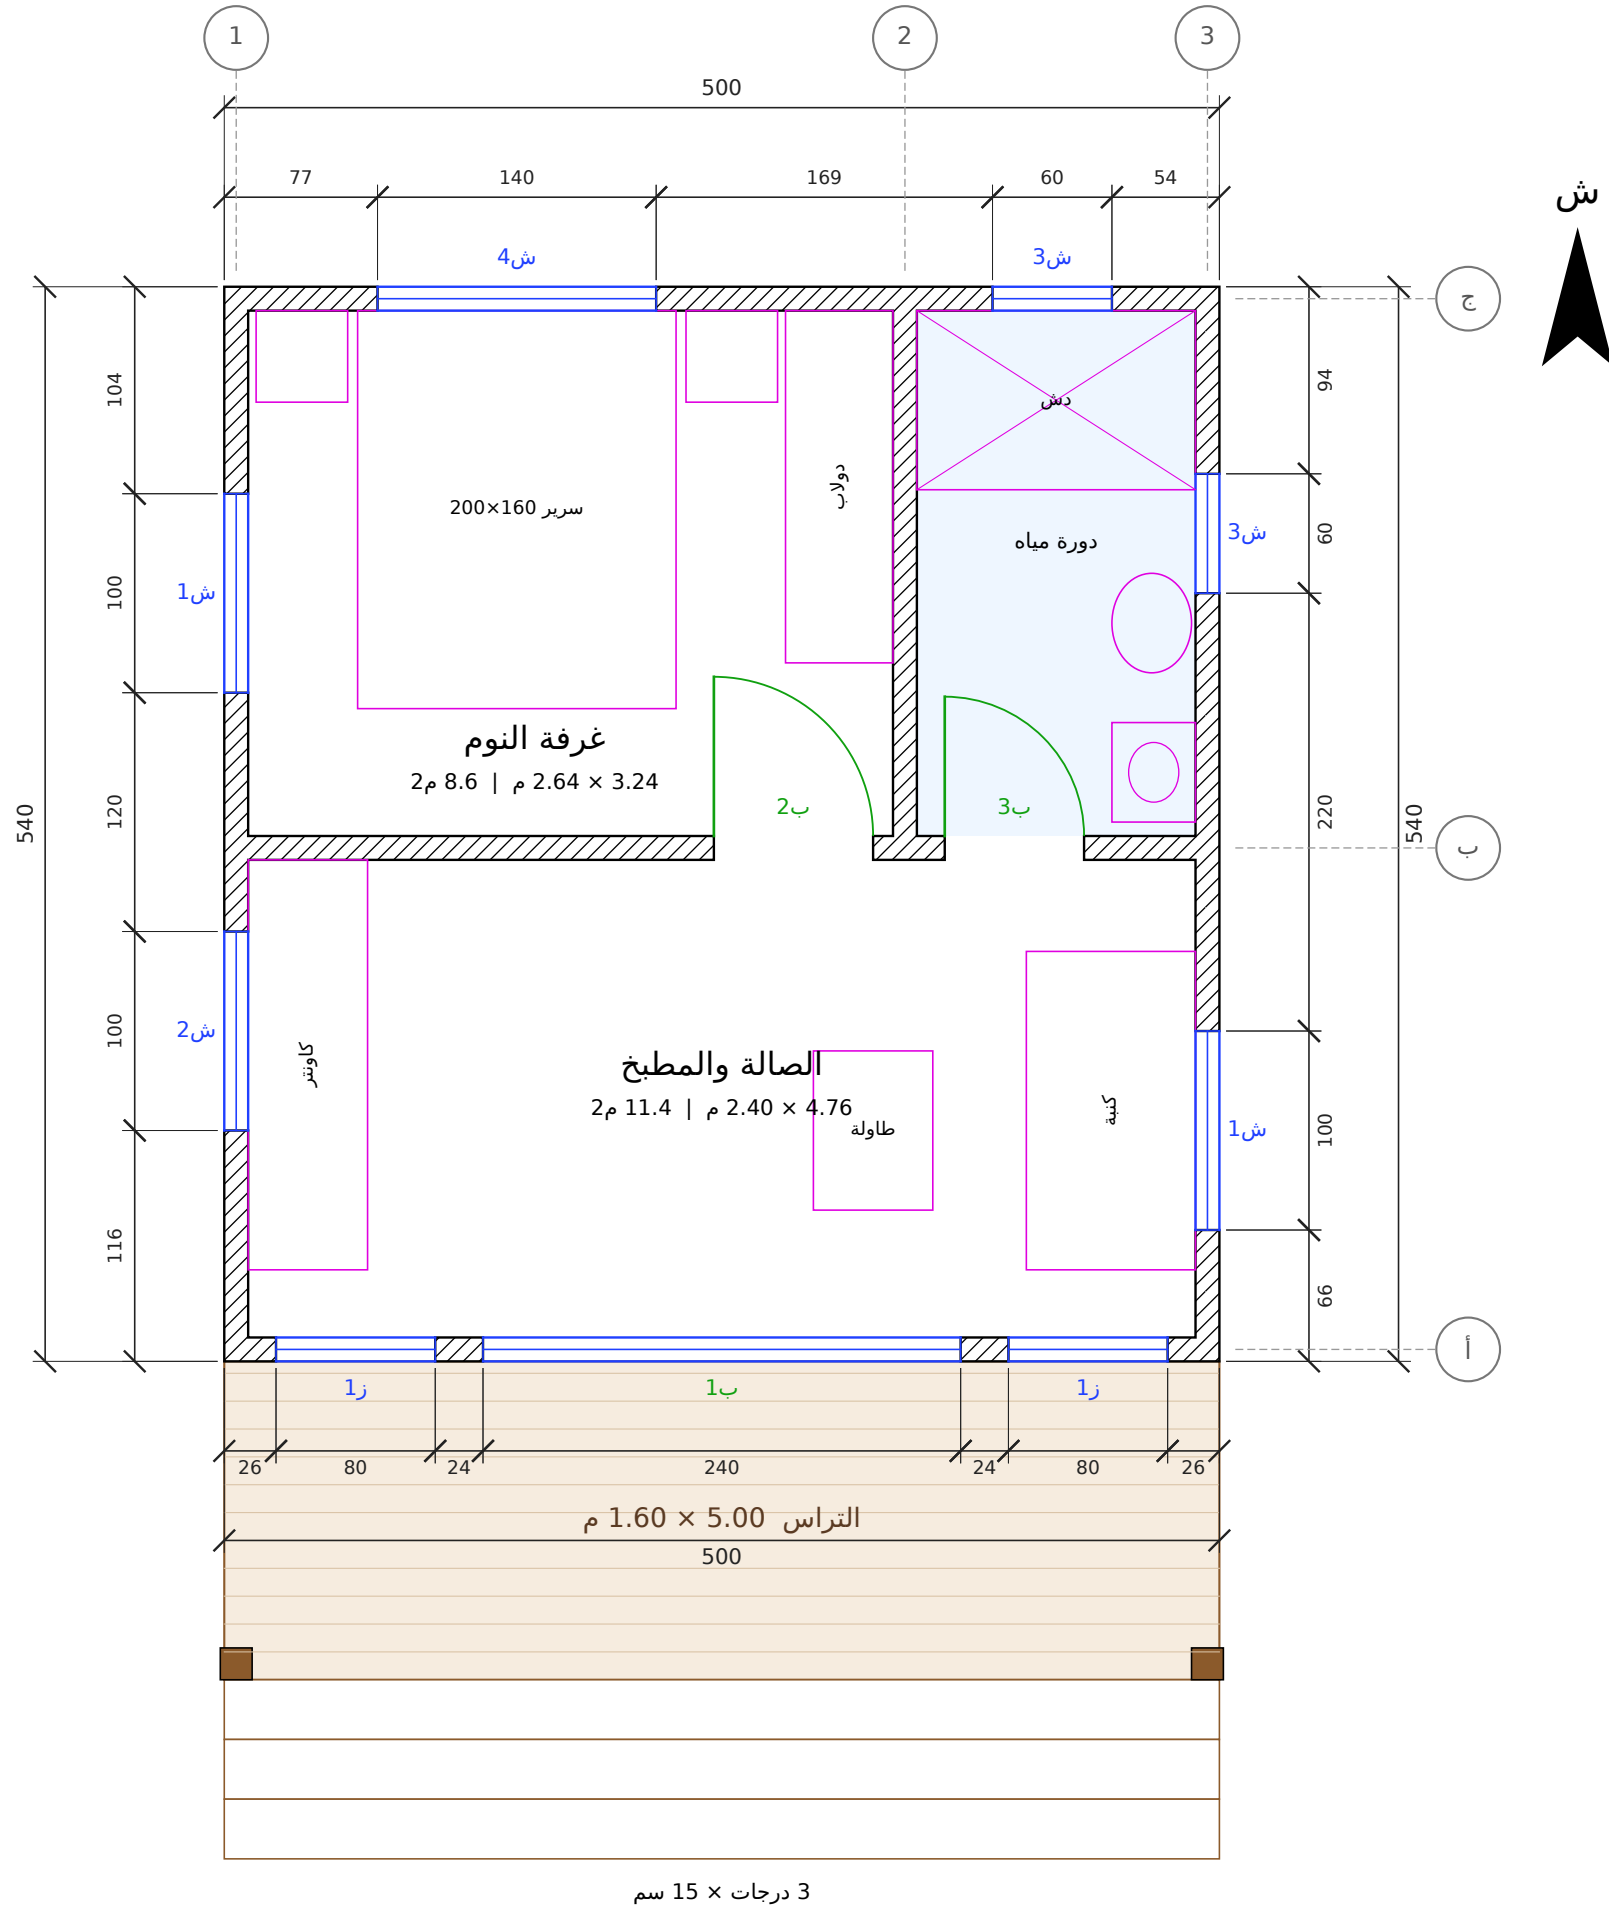


3 درجات × 15 سم

رقم اللوحة	التاريخ	المقياس	عنوان اللوحة	المشروع / العميل	مصنع وتد الأخشاب Watad Wood Factory
W-02 (2/12)	2026-09-29	1:50	المسقط الأفقي	كوخ غرفة وتراس 7×5 شامل التراس عميل - تصميم حسب الصورة	

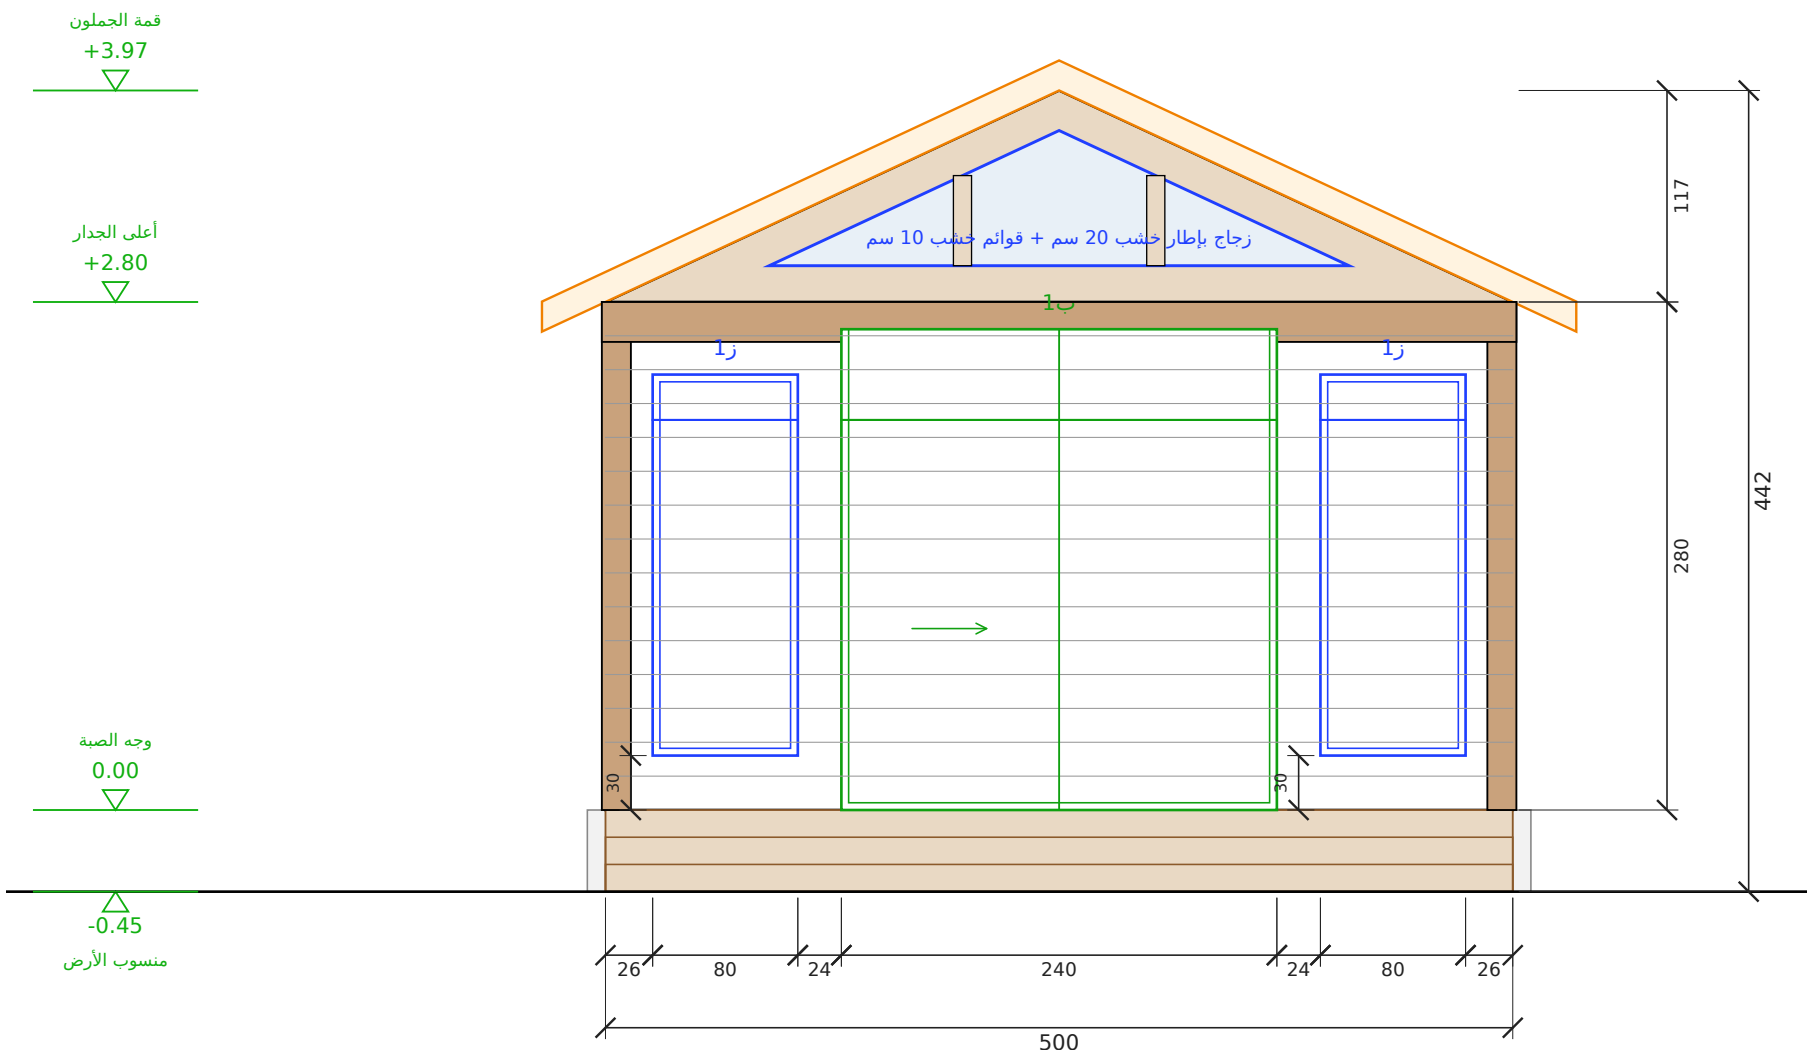

الواجهة الأمامية (التراس)


مقياس 1:50 | الوحدة: سم

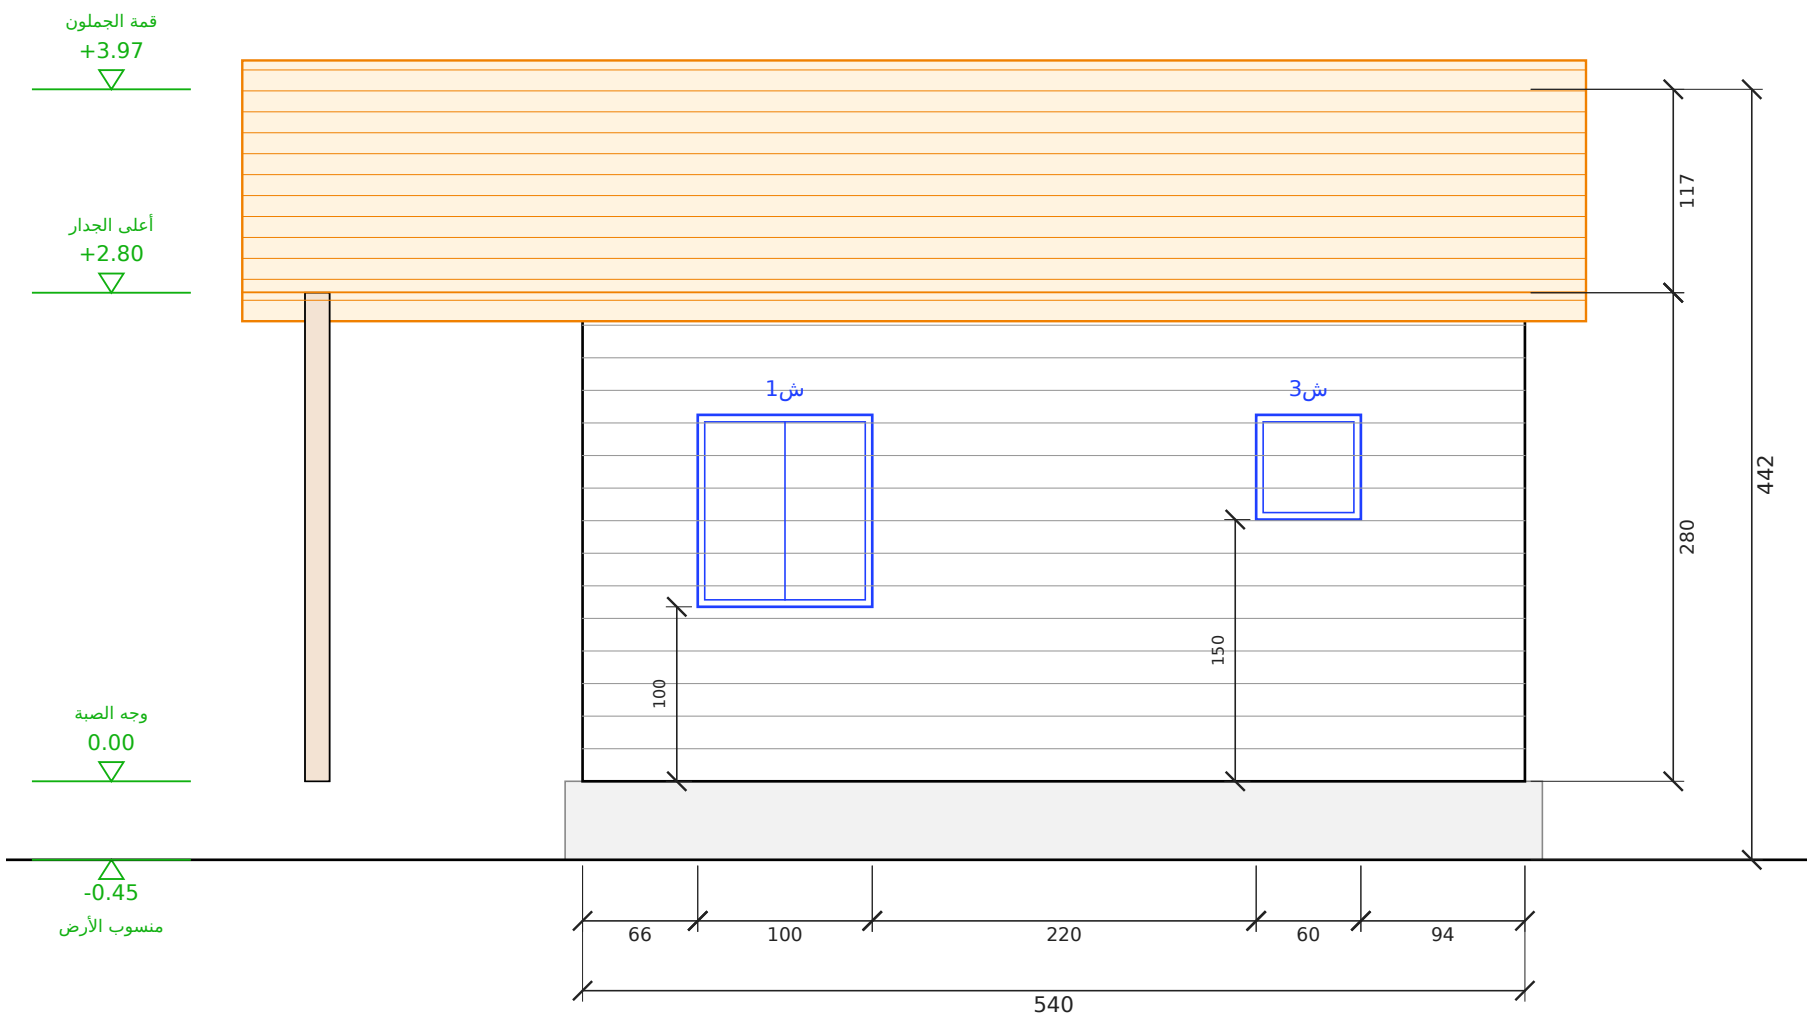

الواجهة الشرقية


مقياس 1:50 | الوحدة: سم

رقم اللوحة	التاريخ	المقياس	عنوان اللوحة	المشروع / العميل	مصنع وتد الأخشاب Watad Wood Factory
W-03 (3/12)	2026-09-29	1:50	الواجهة الأمامية (التراس) والواجهة الشرقية	كوخ غرفة وتراس 7x5 شامل التراس عميل - تصميم حسب الصورة	

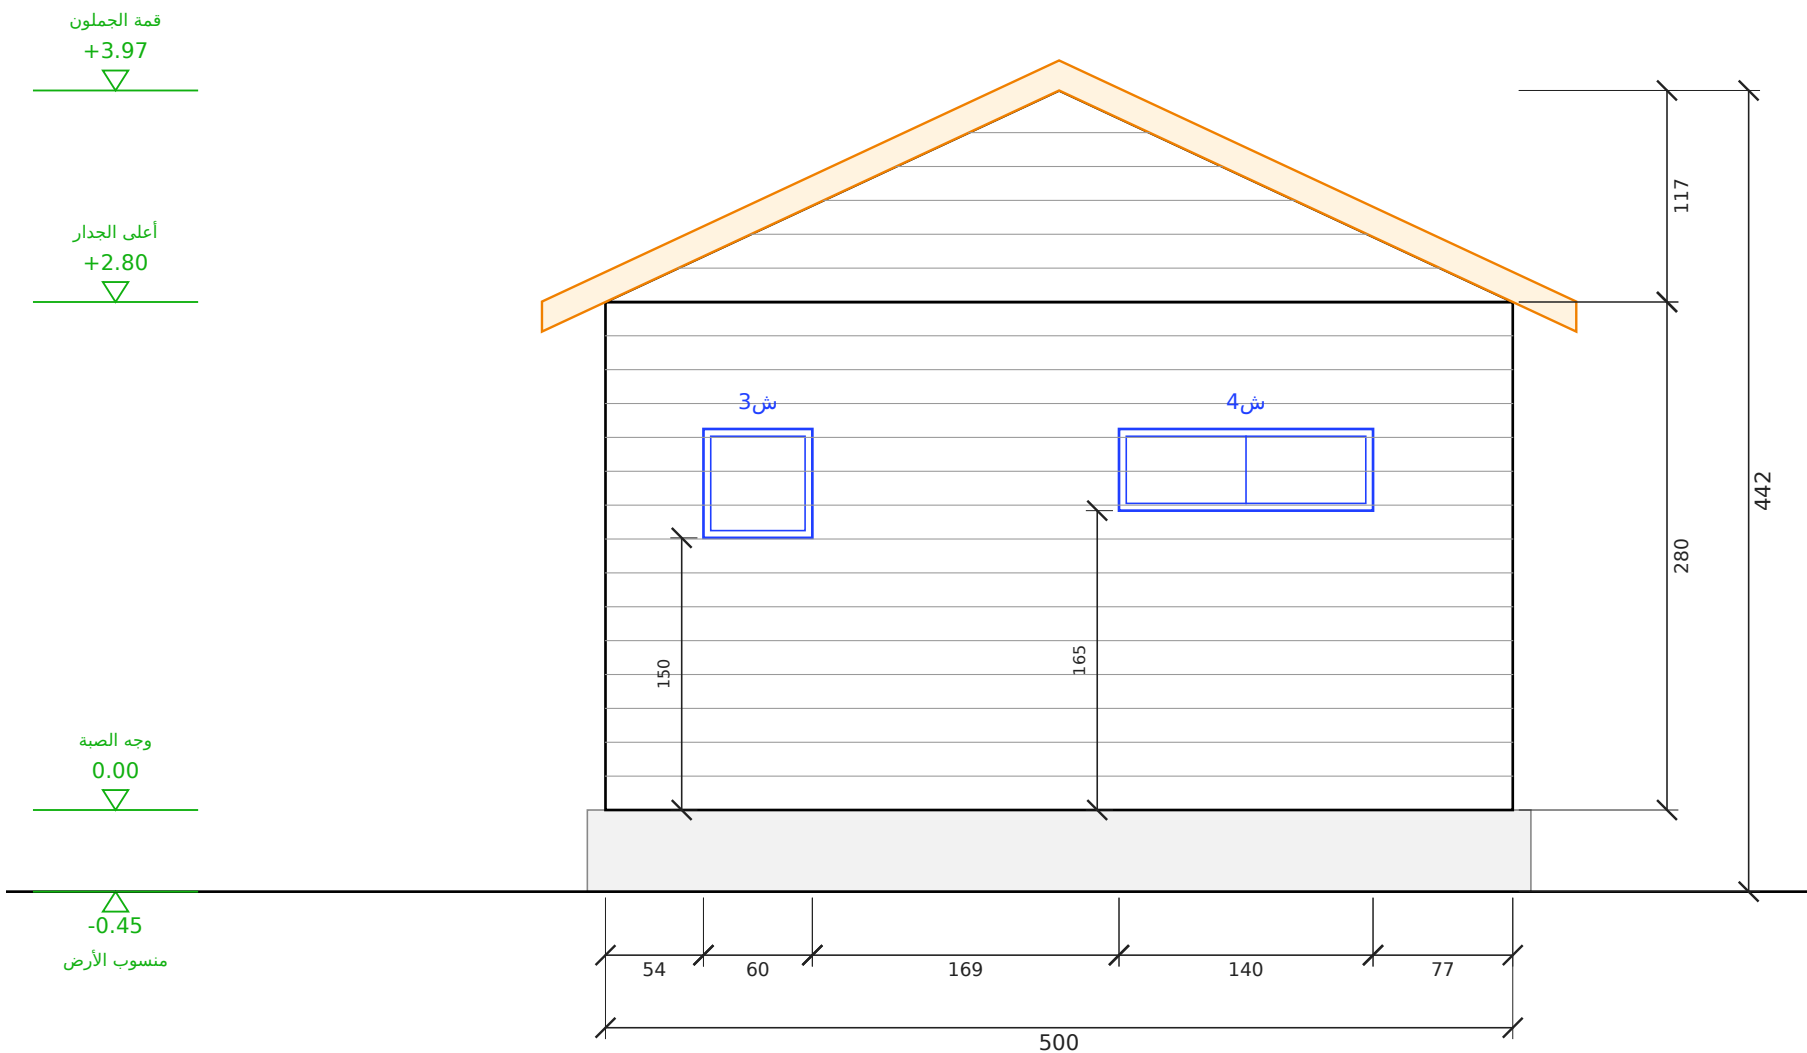

الواجهة الخلفية

مقياس 1:50 | الوحدة: سم

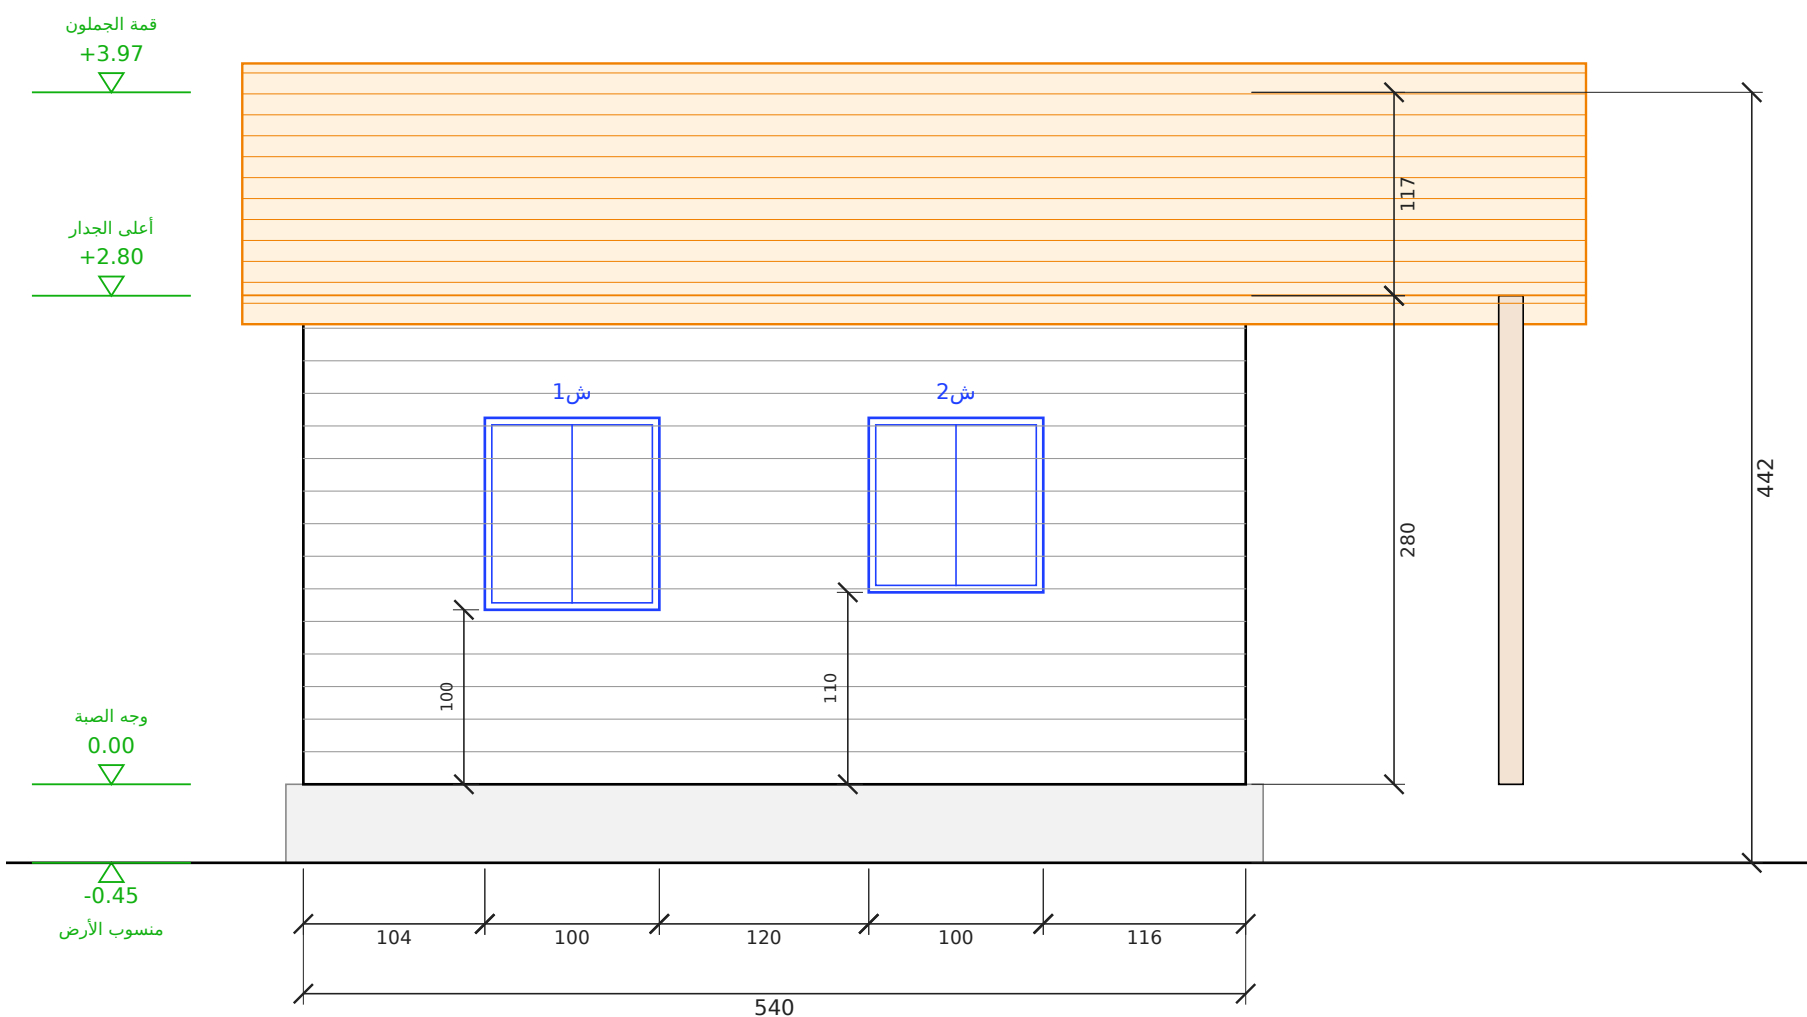


الواجهة الغربية


مقياس 1:50 | الوحدة: سم

رقم اللوحة	التاريخ	المقياس	عنوان اللوحة	المشروع / العميل	مصنع وتد الأخشاب Watad Wood Factory
W-04 (4/12)	2026-09-29	1:50	الواجهة الخلفية والواجهة الغربية	كوخ غرفة وتراس 7x5 شامل التراس عميل - تصميم حسب الصورة	


مسقط السقف (جملون)
رفر 35 سم من كل جهة | مقياس 1:50

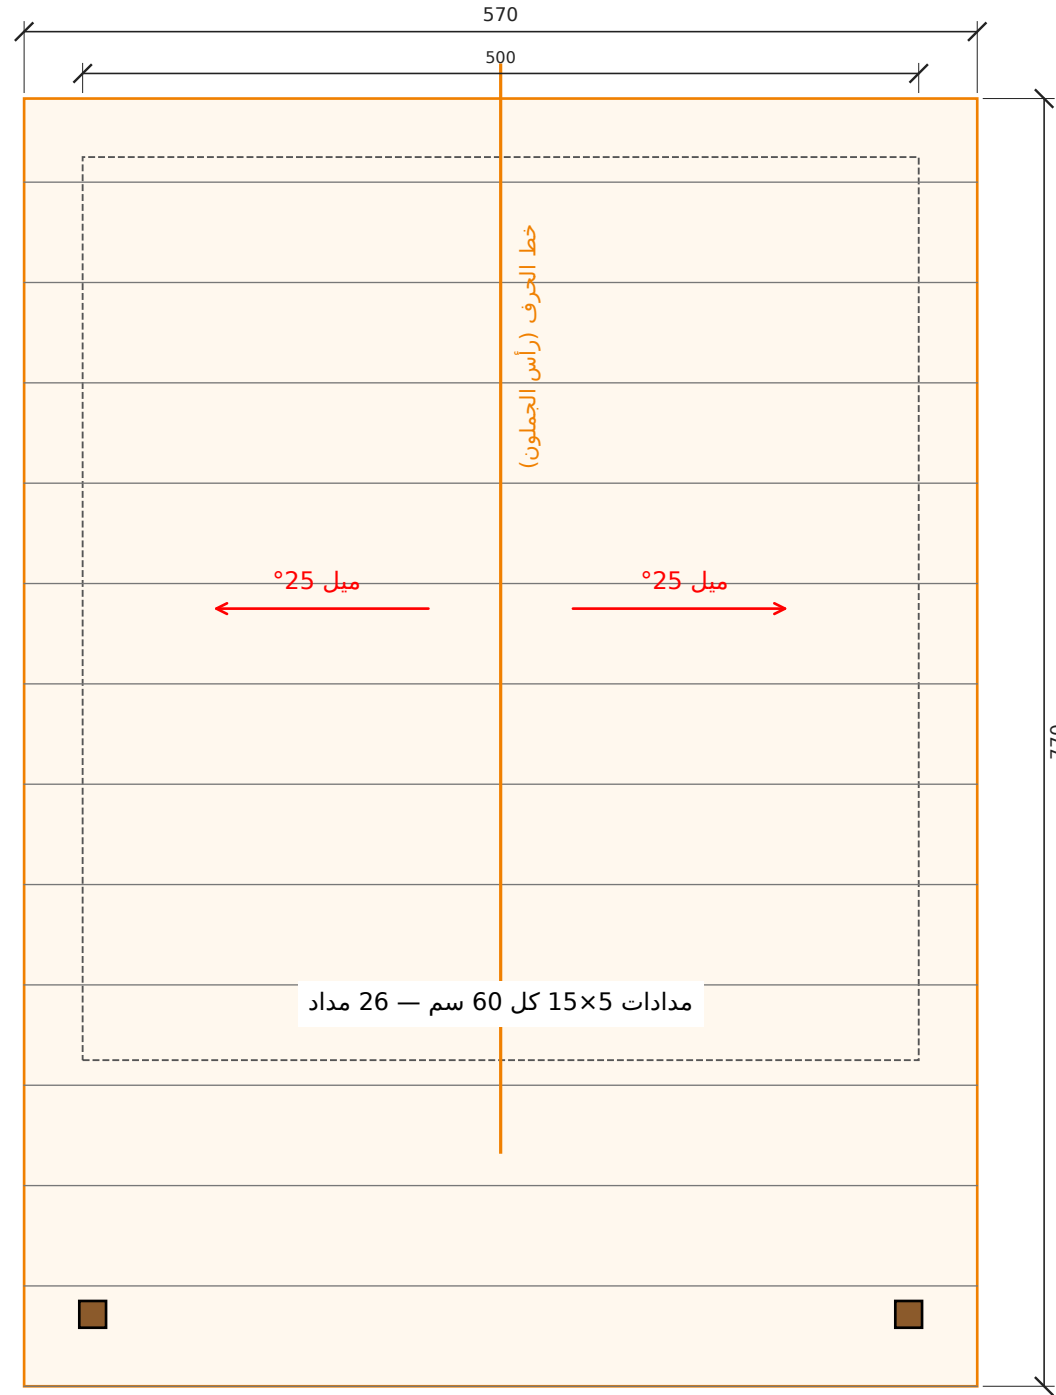

قطاع عرضي أ-أ
مقياس 1:50 | الوحدة: سم

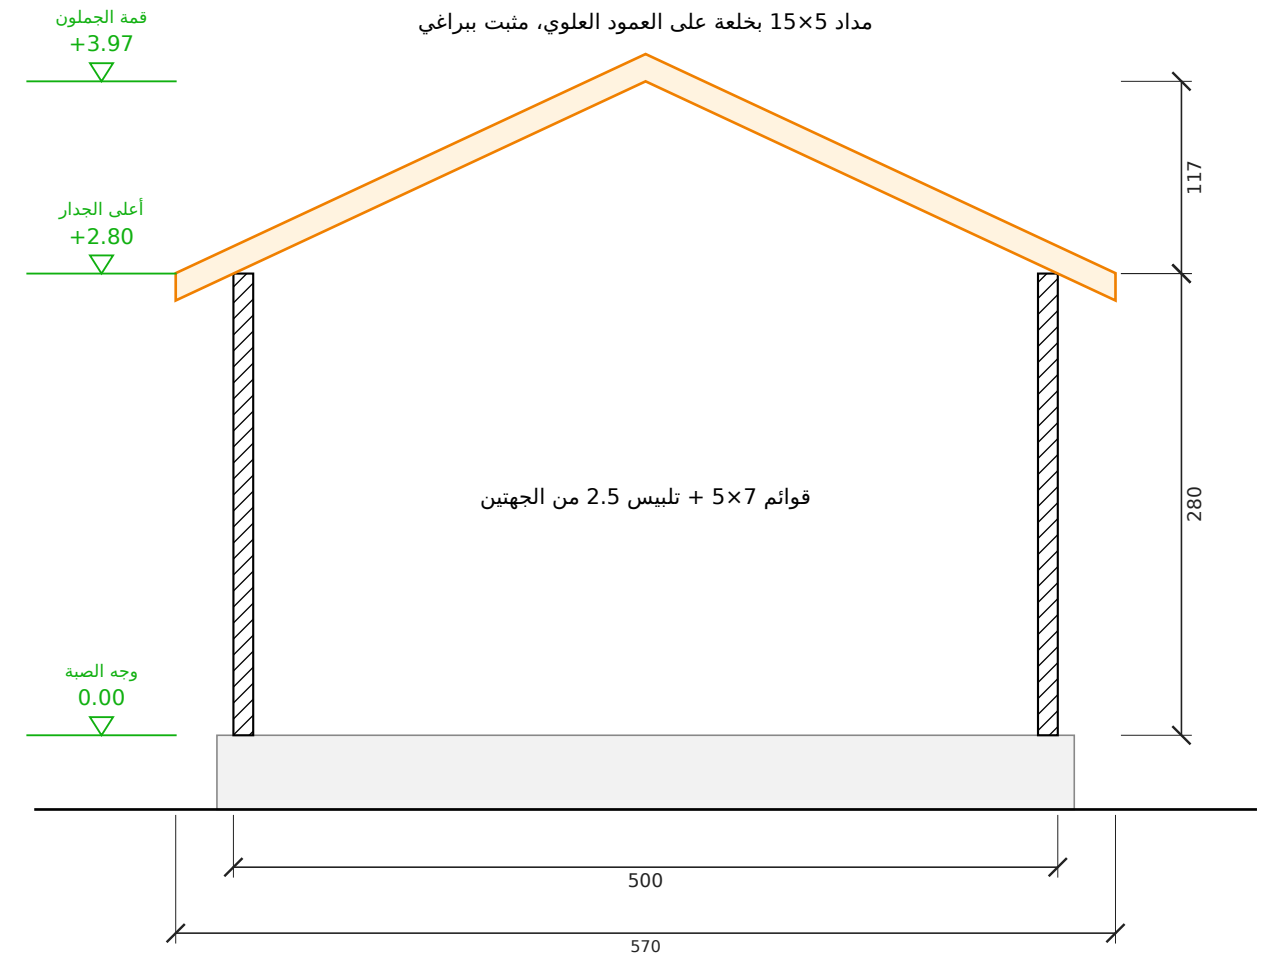

تفصيلة جلوس المداد على العلوي (1:5)

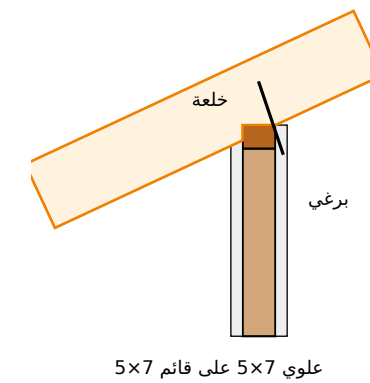

رقم اللوحة

W-05 (5/12)

التاريخ

2026-09-29

المقياس

1:50

عنوان اللوحة

مسقط السقف والقطاع

المشروع / العميل

كوخ غرفة وتراس 7x5 شامل التراس
عميل — تصميم حسب الصورة

مصنع وتد الأخشاب
Watad Wood Factory



جدول مقاسات الأبواب والشبابيك
مقاس الفتحة الصافي في الجدار - الوحدة: سم

الرمز	النوع	العرض (سم)	الارتفاع (سم)	ارتفاع الجلسة (سم)	العدد	الموقع
ب1	باب مزدوج	240	265	-	1	الأمامية (التراس)
ب2	باب	80	210	-	1	غرفة النوم
ب3	باب	70	210	-	1	حمام
ز1	شباك	80	210	30	2	الأمامية (التراس) 2
ش1	شباك	100	110	100	2	الشرقية - الغربية
ش2	شباك	100	100	110	1	الغربية
ش3	شباك	60	60	150	2	الشرقية - الخلفية
ش4	شباك	140	45	165	1	الخلفية

الإجمالي: أبواب 3 - شبابيك 8

جدول المساحات وبيانات المشروع والتسعير

جدول المساحات

م	الفراغ	الأبعاد (م)	المساحة (م2)
1	الصالة والمطبخ	4.76 × 2.40	11.42
2	غرفة النوم	3.24 × 2.64	8.55
3	دورة مياه	1.40 × 2.64	3.70
	المساحة الصافية الداخلية		23.67
	التراس المسقوف	5.00 × 1.60	8.00
	المساحة الإجمالية المبنية	5.00 × 5.40	27.00

بيانات المشروع

البند	البيان
المشروع	كوخ غرفة وتراس 7×5 شامل التراس
العميل	عميل — تصميم حسب الصورة
الموقع	—
الاستخدام	استراحة / استجمام
التاريخ	2026-09-29
نظام البناء	هيكل خشب 5×7 + تليس 2.5 سم من الجهتين
السقف	جملون 25° — قرميد معدني

التسعير


عرض اليوم الوطني

البند	القيمة
المساحة الكلية — الكوخ + التراس (م2)	35.00
سعر المتر المربع — عرض اليوم الوطني	1,096 ريال
الإجمالي	38,360 ريال


ملاحظات:

- السعر لكامل المساحة (الكوخ + التراس المسقوف) حسب المخطط المعتمد.
- الصبة والتوريدات الخارجية على العميل ما لم يُذكر غير ذلك.

تأطير جدار جنوب — الطول 488 سم، الارتفاع 280 سم

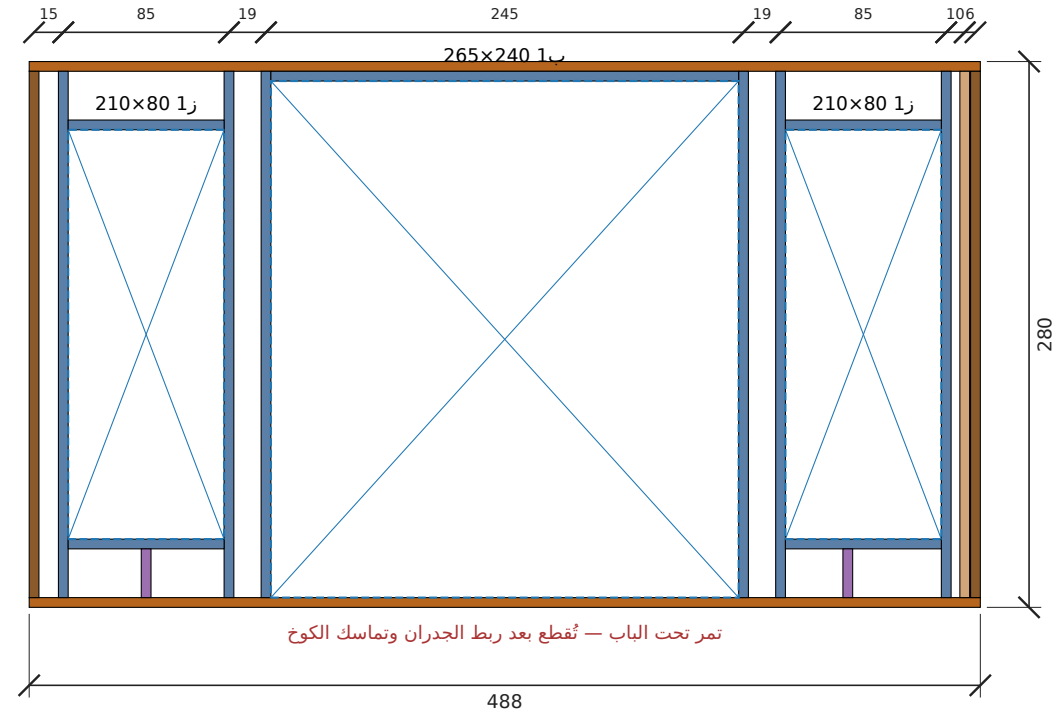

تأطير جدار شرق — الطول 528 سم، الارتفاع 280 سم

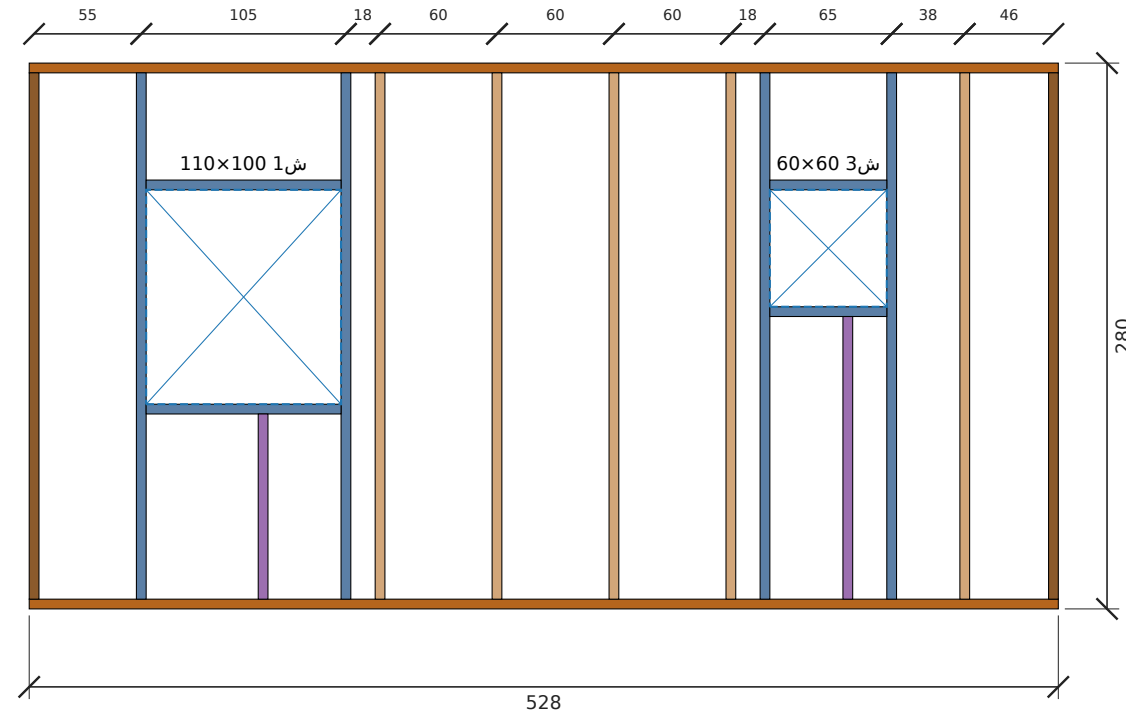

قاعدة سفلية علوي عمود عمود زاوية جنب فتحة رأس فتحة جلسة شباك عمود قصير

رقم اللوحة

W-08 (8/12)

التاريخ

2026-09-29

المقياس

—

عنوان اللوحة

لوحات التأطير (للورشة)


المشروع / العميل

كوخ غرفة وتراس 7x5 شامل التراس
عميل — تصميم حسب الصورة


مصنع وتد الأخشاب
Watad Wood Factory



تأطير جدار شمال — الطول 488 سم، الارتفاع 280 سم

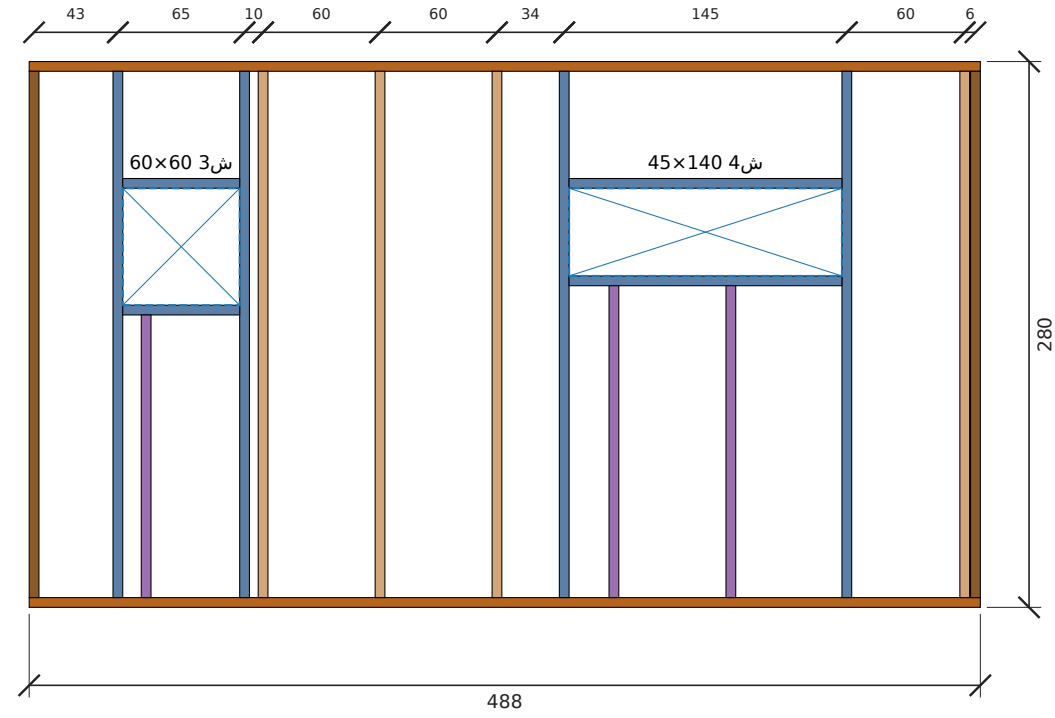

تأطير جدار غرب — الطول 528 سم، الارتفاع 280 سم

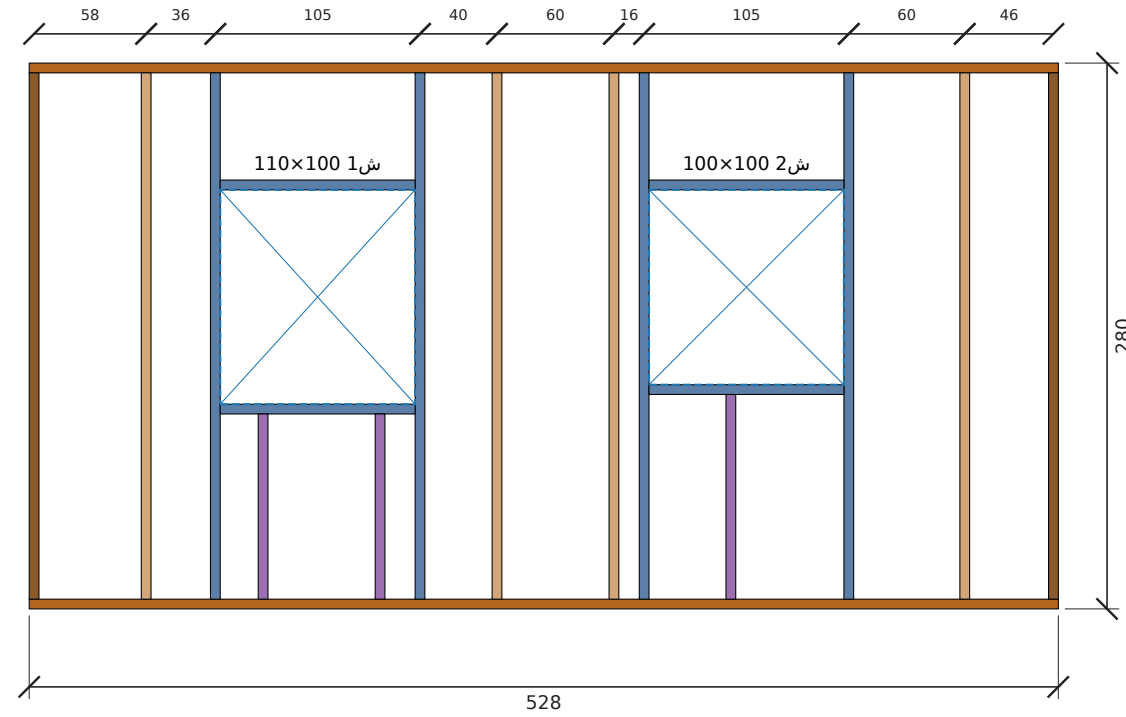

■ قاعدة سفلية
 ■ علوي
 ■ عمود
 ■ عمود زاوية
 ■ جنب فتحة
 ■ رأس فتحة
 ■ جلسة شباك
 ■ عمود قصير

رقم اللوحة

W-09 (9/12)

التاريخ

2026-09-29

المقياس

—

عنوان اللوحة

لوحات التأطير (للورشة)


المشروع / العميل

كوخ غرفة وتراس 7×5 شامل التراس
عميل — تصميم حسب الصورة


مصنع وتد الأخشاب
Watad Wood Factory



تأطير جدار د1-فاصل الصالة — الطول 488 سم، الارتفاع 280 سم (داخلي)

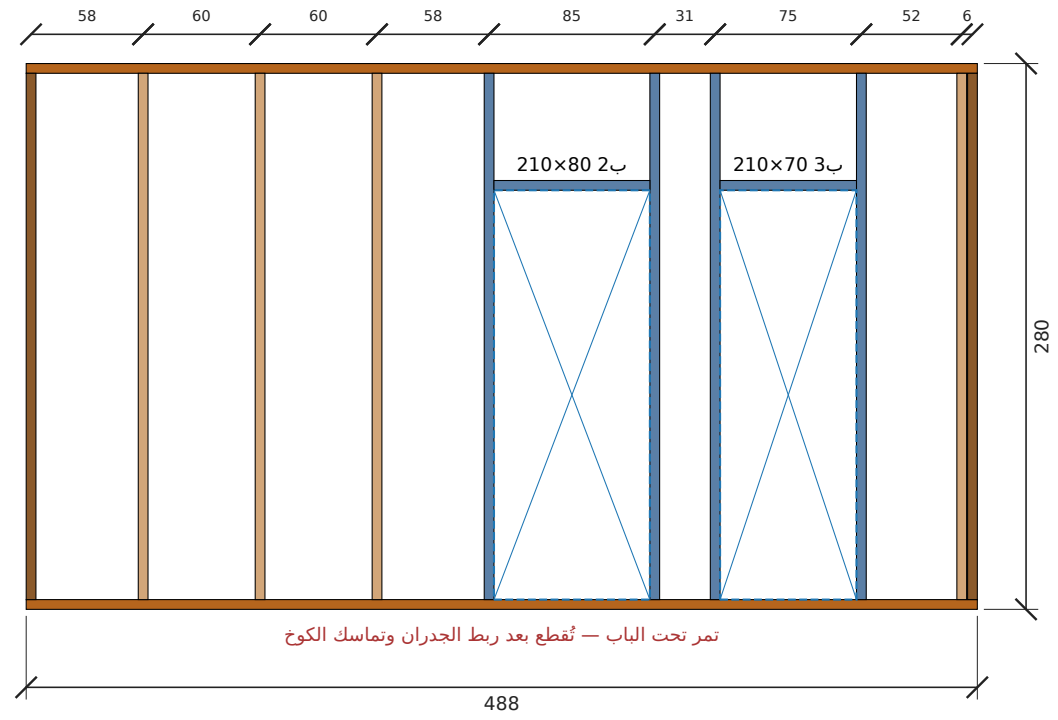

تأطير جدار د2-جدار الحمام — الطول 276 سم، الارتفاع 280 سم (داخلي)

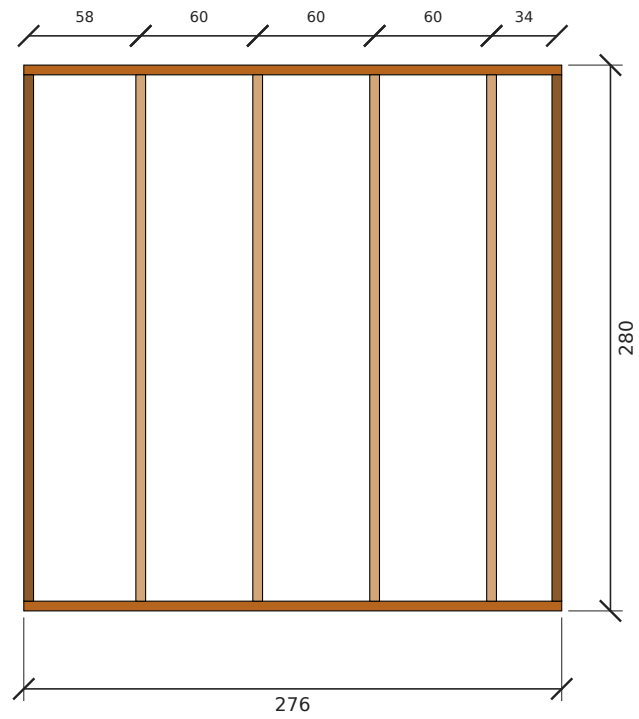

قاعدة سفلية علوي عمود عمود زاوية جنب فتحة رأس فتحة جلسة شباك عمود قصير

رقم اللوحة

W-10 (10/12)

التاريخ

2026-09-29

المقياس

—

عنوان اللوحة

لوحات التأطير (للورشة)

المشروع / العميل

كوخ غرفة وتراس 7×5 شامل التراس
عميل — تصميم حسب الصورة

مصنع وتد الأخشاب
Watad Wood Factory



جدول الكميات وخطة تقطيع الطبلیات

البند	القيمة
الارتفاع المطلوب / المعتمد	280 / 280 سم
السقف	جملون 25° — قمة 397 سم من وجه الصبة
المدادات 15×5	26 مداد (13 لكل جهة) × 314 سم — من طبلية 320
طبلیات الطريقة الأولى (مداد + عمود)	26 طبلية × 320 سم
طبلیات الطريقة الثانية (3 أعمدة)	21 طبلية × 320 سم
إجمالي الطبلیات 22.5×5	47
إجمالي قطع 5×7	97
قائمة تقطيع 5×7	528سم×4 488سم×6 276سم×2 270سم×56 240سم×1 160سم×2 145سم×2 140سم×2 105سم×1
	100سم×6 95سم×3 80سم×5 70سم×1 60سم×4 25سم×2
ألواح تلييس 2.5 سم	148 لوح × 400 سم (مجموع الصفوف 523.2 م، 12 وجه)
أسمنت بورد 12 مم (244×122)	20 لوح (داخل دورات المياه)
العزل	بدون (غير مطلوب)
الصبة	يجهزها العميل — 20 سم، مفرغة تحت دورات المياه

مراجعة التصميم مقابل قواعد المصنع

النوع	البند	التفاصيل	المقترح
ملاحظة	بحر المدادات	أطول بحر بدون جدار داخلي يحمل المداد: جهة أ: 250 سم، جهة ب: 250 سم. يحتاج رقم المصنع لأقصى بحر مسموح لتحديد المدادات اللي تُقوّى 5×20.	
ملاحظة	الصبة والدرج	ارتفاع الصبة 45 سم ← 3 درجة بقائمة 15.0 سم.	
ملاحظة	مناسيب رؤوس الفتحات	رؤوس الأبواب والشبابيك على مناسيب مختلفة: 210، 240، 265 سم.	
سؤال	يحتاج تأكيد	أقصى بحر للمداد بدون جدار داخلي قبل إضافة تقوية 5×7 (مداد 5×20)؟	
سؤال	يحتاج تأكيد	التغطية الصافية للوح التليس بعد التعشيق (مستنتجة مؤقتاً 18.67 سم من 280/15)؟	
سؤال	يحتاج تأكيد	هل يوضع أعمدة قصيرة فوق رأس الشباك/الباب إلى العلوي؟	
سؤال	يحتاج تأكيد	مكان الوصلة في القاعدة والعلوي إذا الجدار أطول من الطيلية؟	