
المسقط الأفقي مع الفرش — الدور الأرضي

الأبعاد بالسنتيمتر - الجدران: قوائم 7×5 + تلبيس 2.5 من الجهتين (12 سم) | منسوب الأرضية +0.00

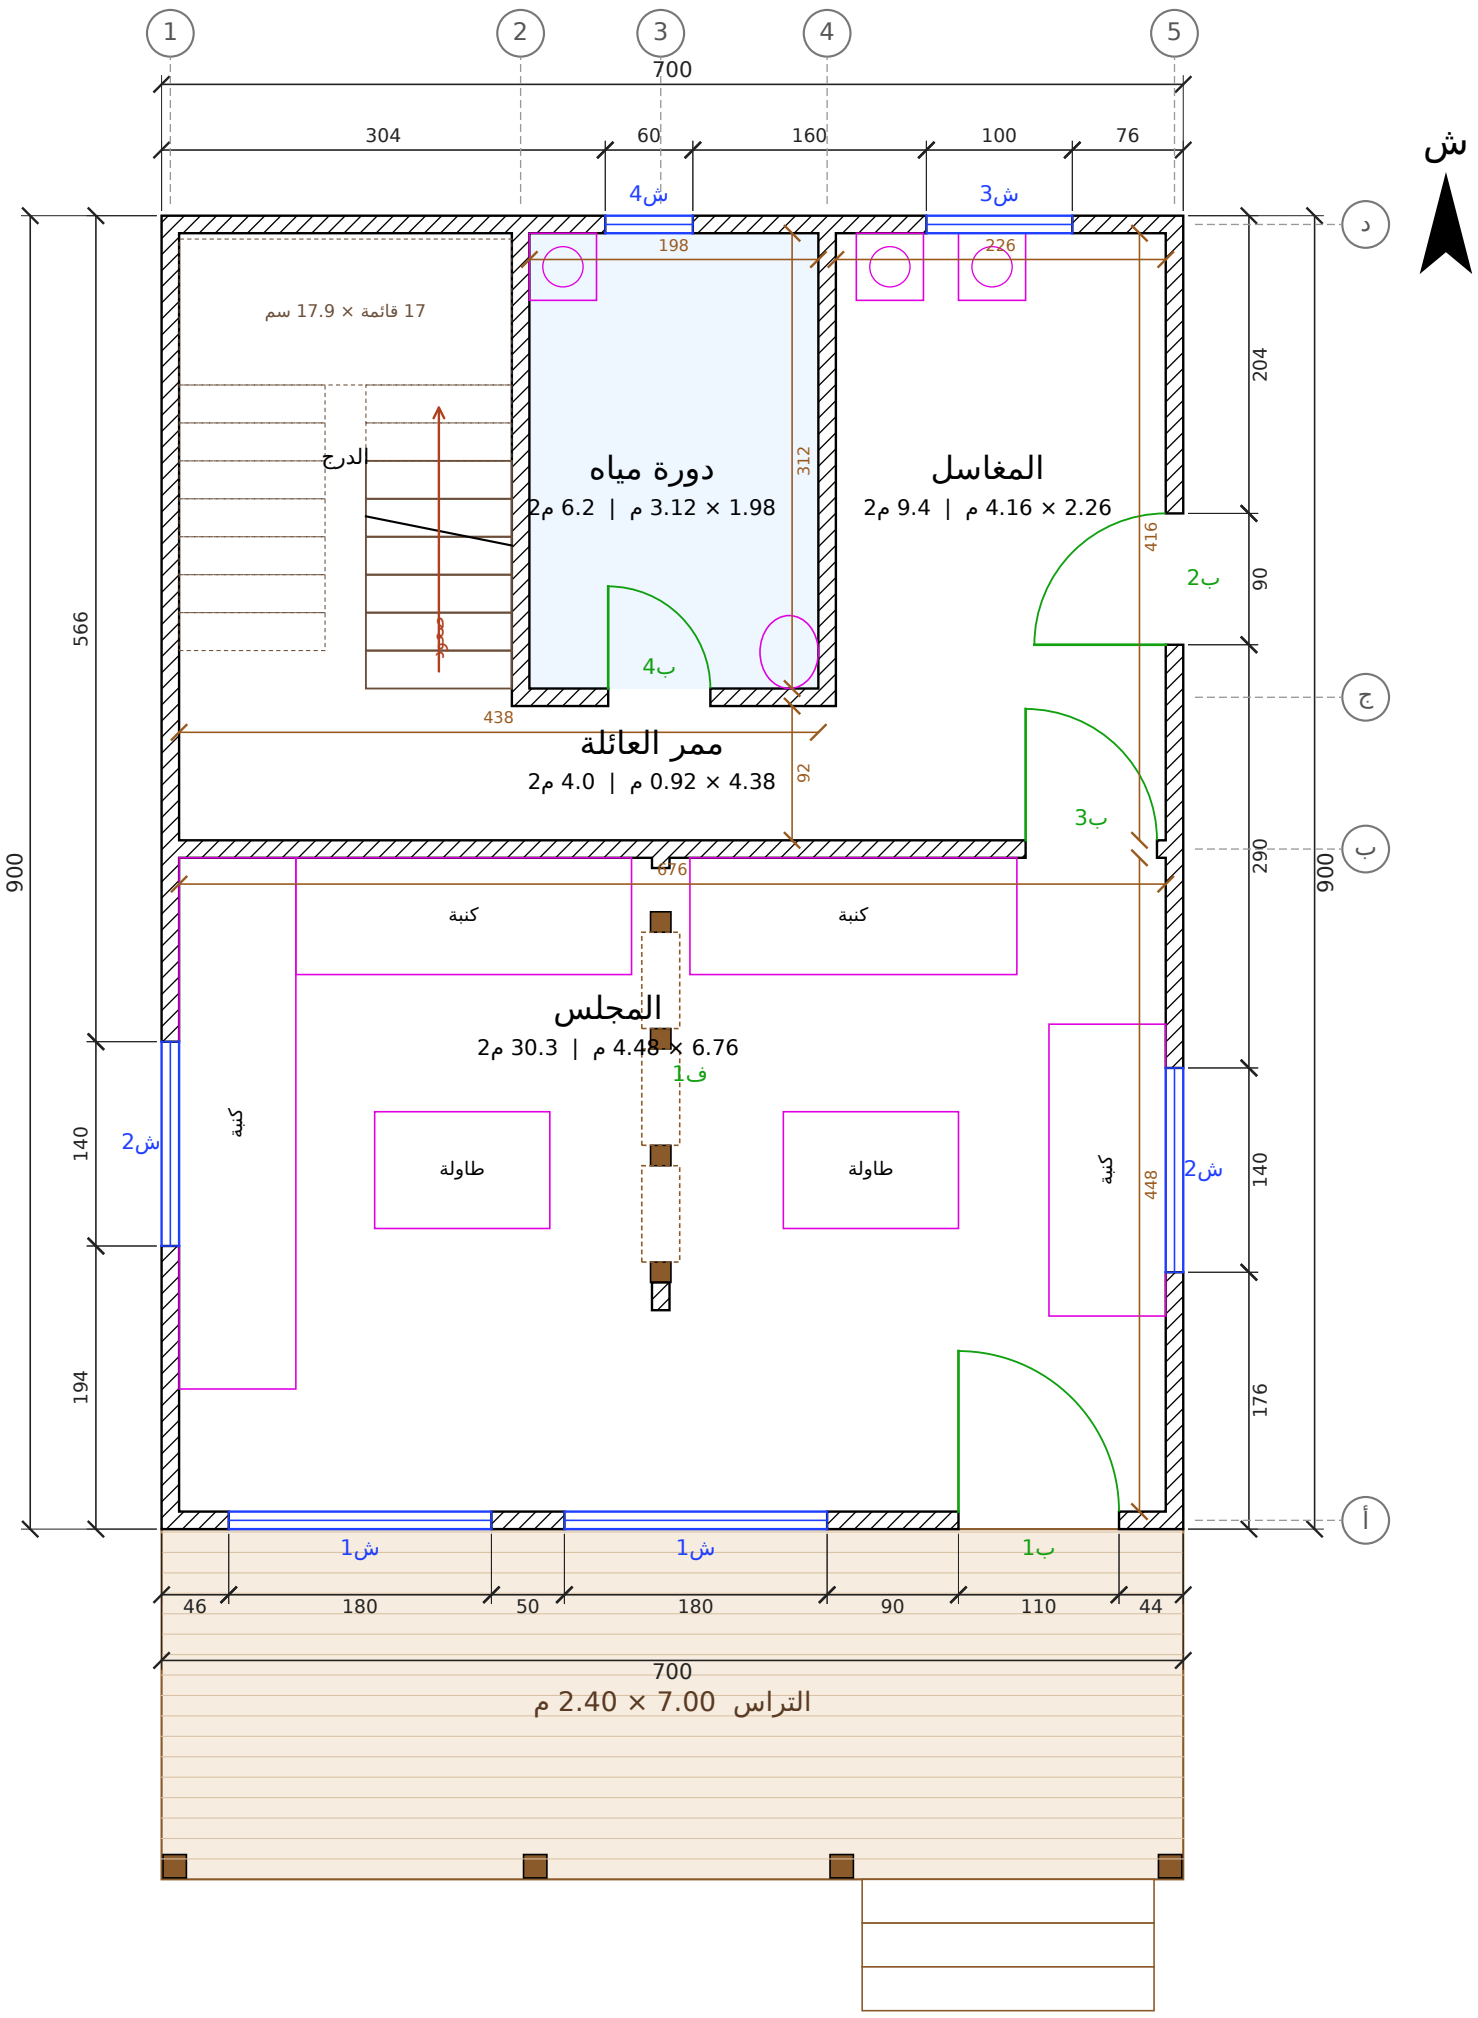


المشروع / العميل	عنوان اللوحة	المقياس	التاريخ	رقم اللوحة
فيلا خشب دورين — مجلس + غرفتين — 7.00 × 9.00 م (63 م² للدور) **عميل — تبوك**	**المسقط الأفقي — الدور الأرضي**	**1:50**	**2026-10-23**	**A-01 (1/11)**

مصنع وتد الأخشاب
Watad Wood Factory


المسقط الأفقي مع الفرش — الدور الأول

الأبعاد بالسنتيمتر - الجدران: قوائم 5×7 + تلبيس 2.5 من الجهتين (12 سم) | منسوب الأرضية +3.05

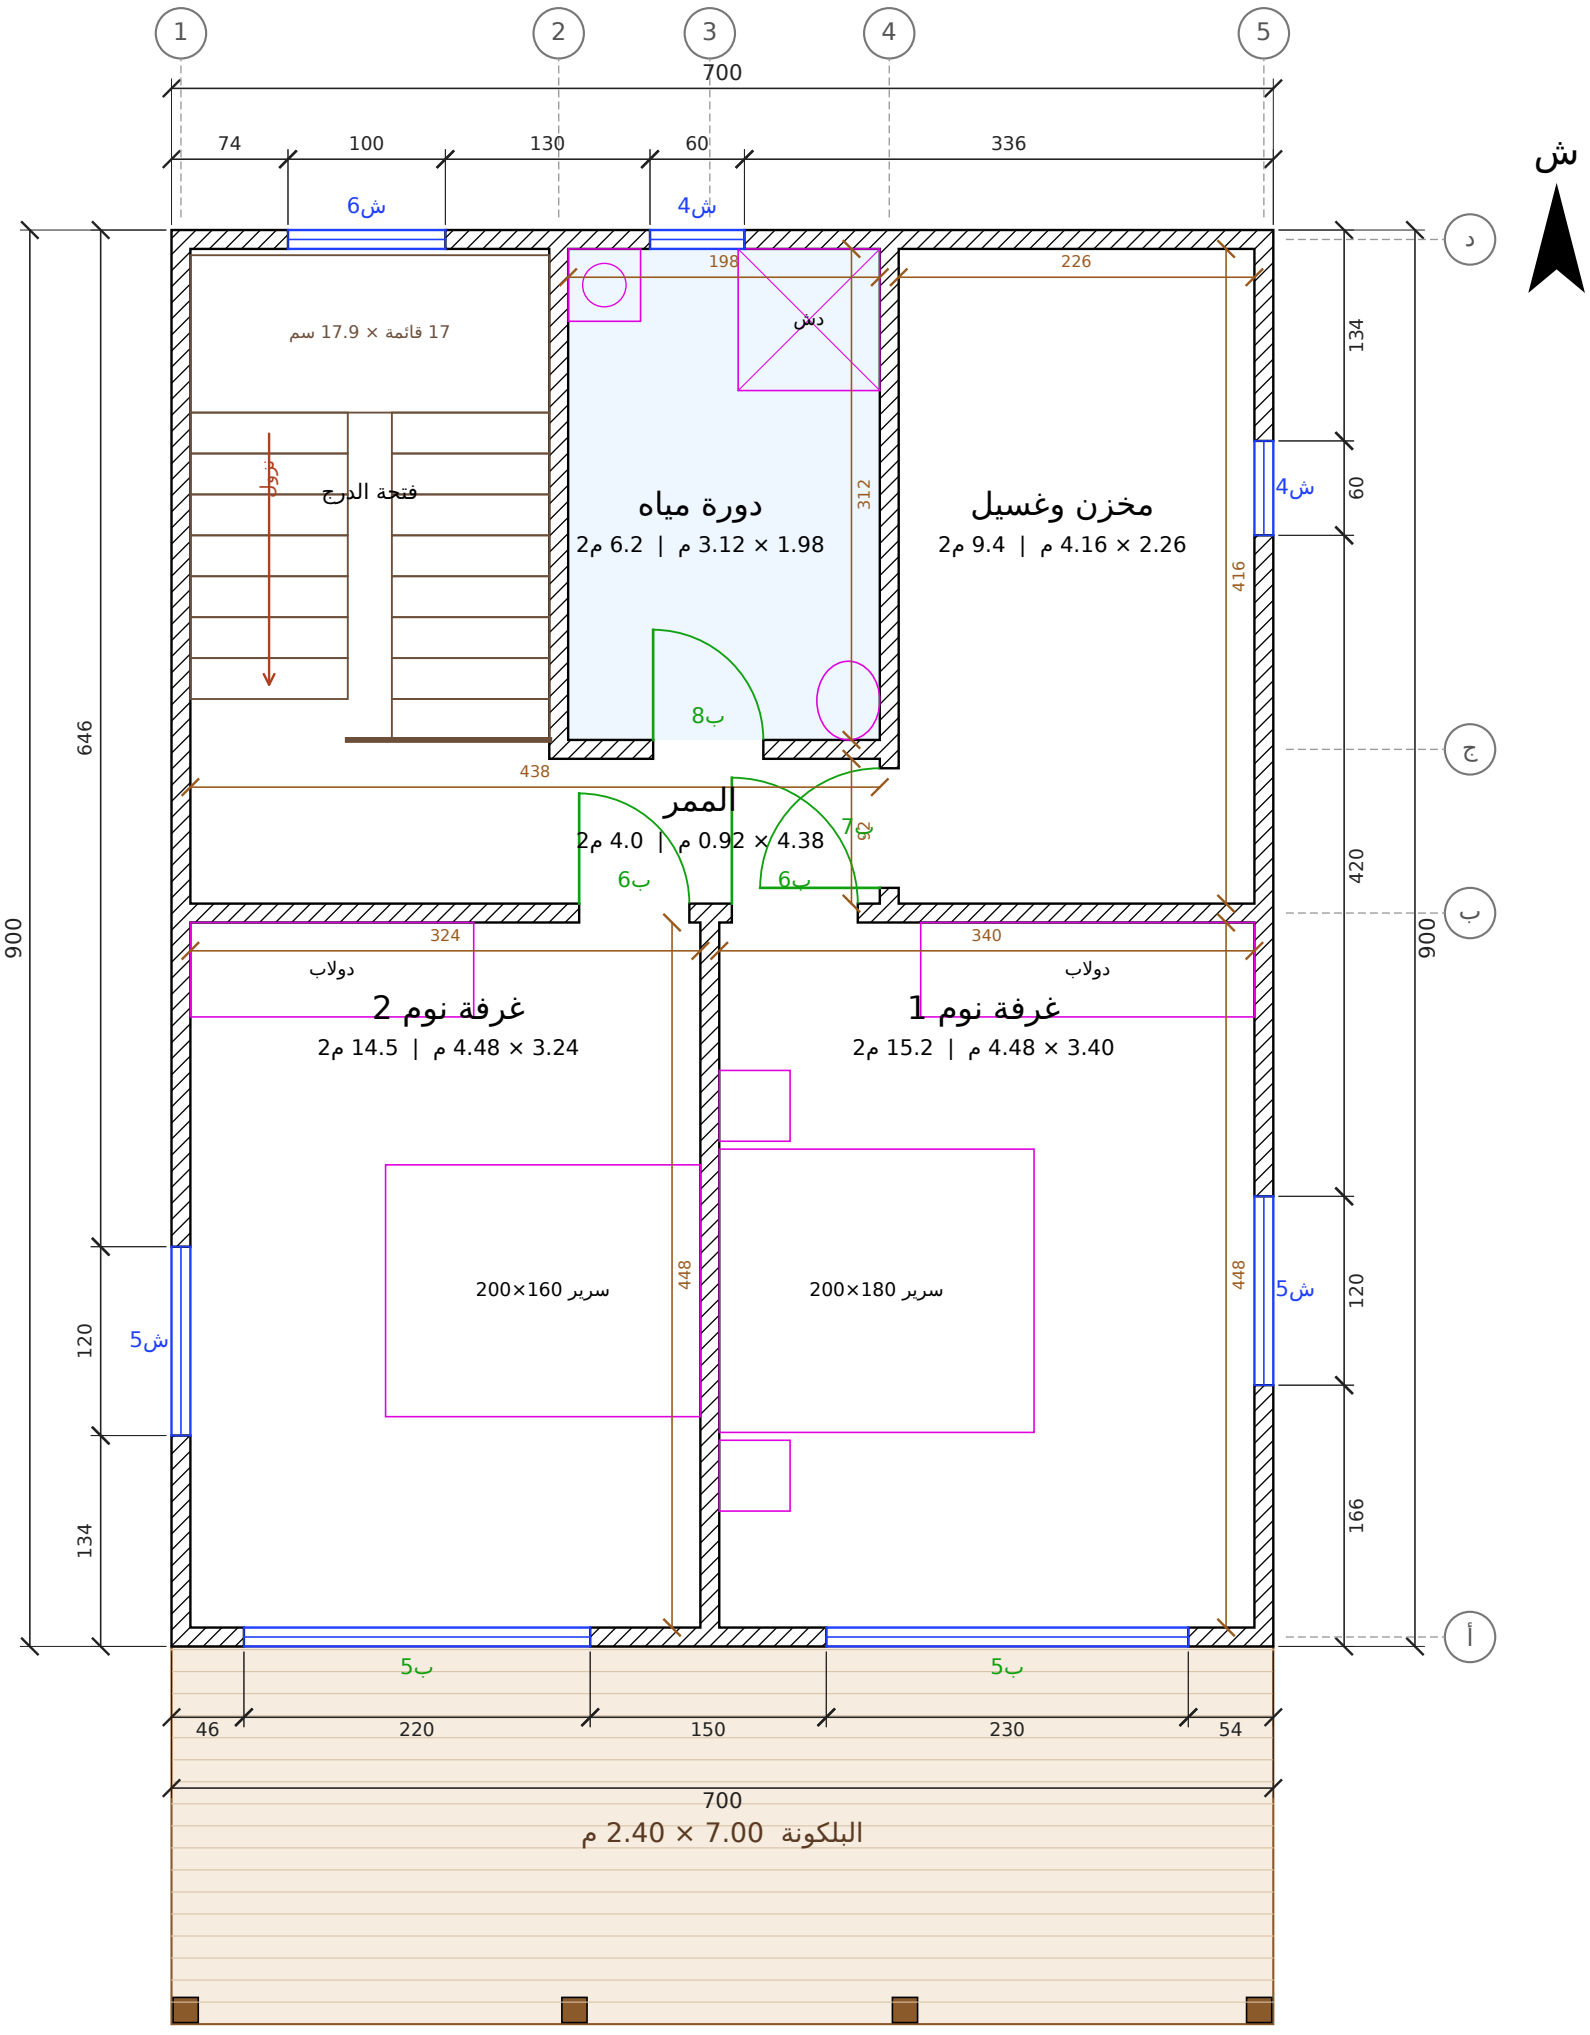


المشروع / العميل	عنوان اللوحة	المقياس	التاريخ	رقم اللوحة
فيلا خشب دورين — مجلس + غرفتين — 7.00 × 9.00 م (63 م² للدور) **عميل — تبوك**	**المسقط الأفقي — الدور الأول**	**1:50**	**2026-10-23**	**A-02 (2/11)**

مصنع وتد الأخشاب
Watad Wood Factory

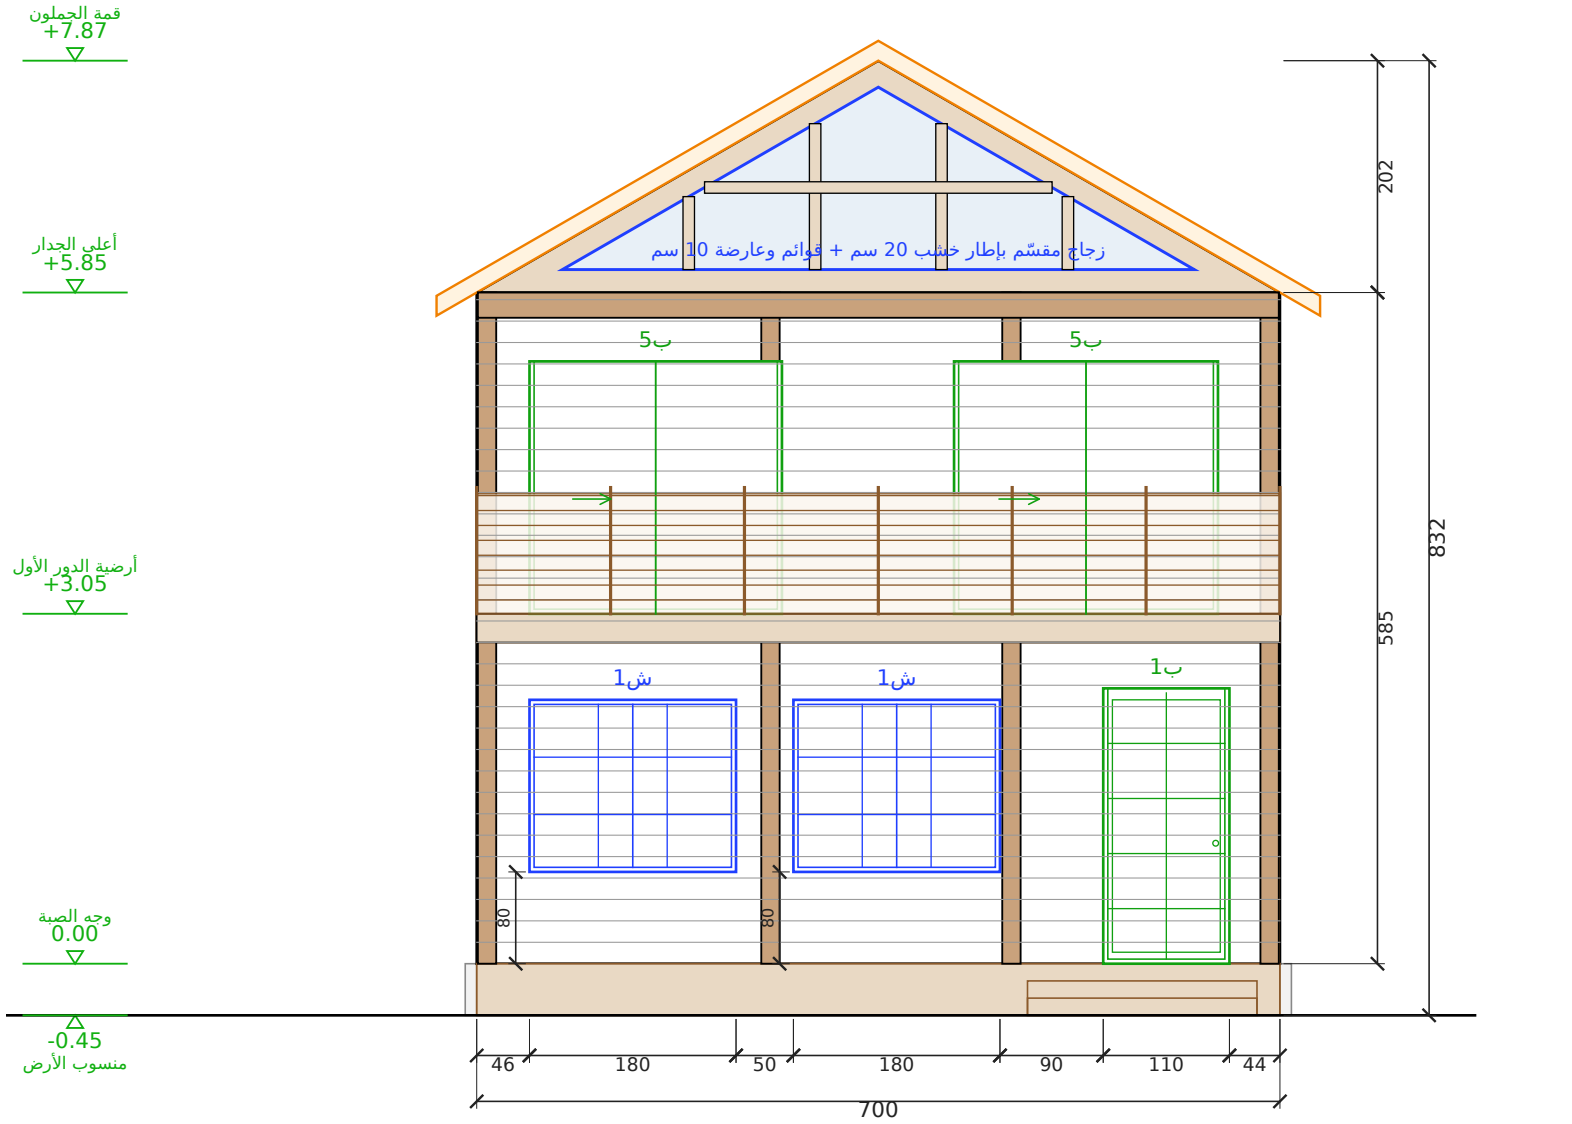

الواجهة الأمامية


مقياس 1:50 | الوحدة: سم

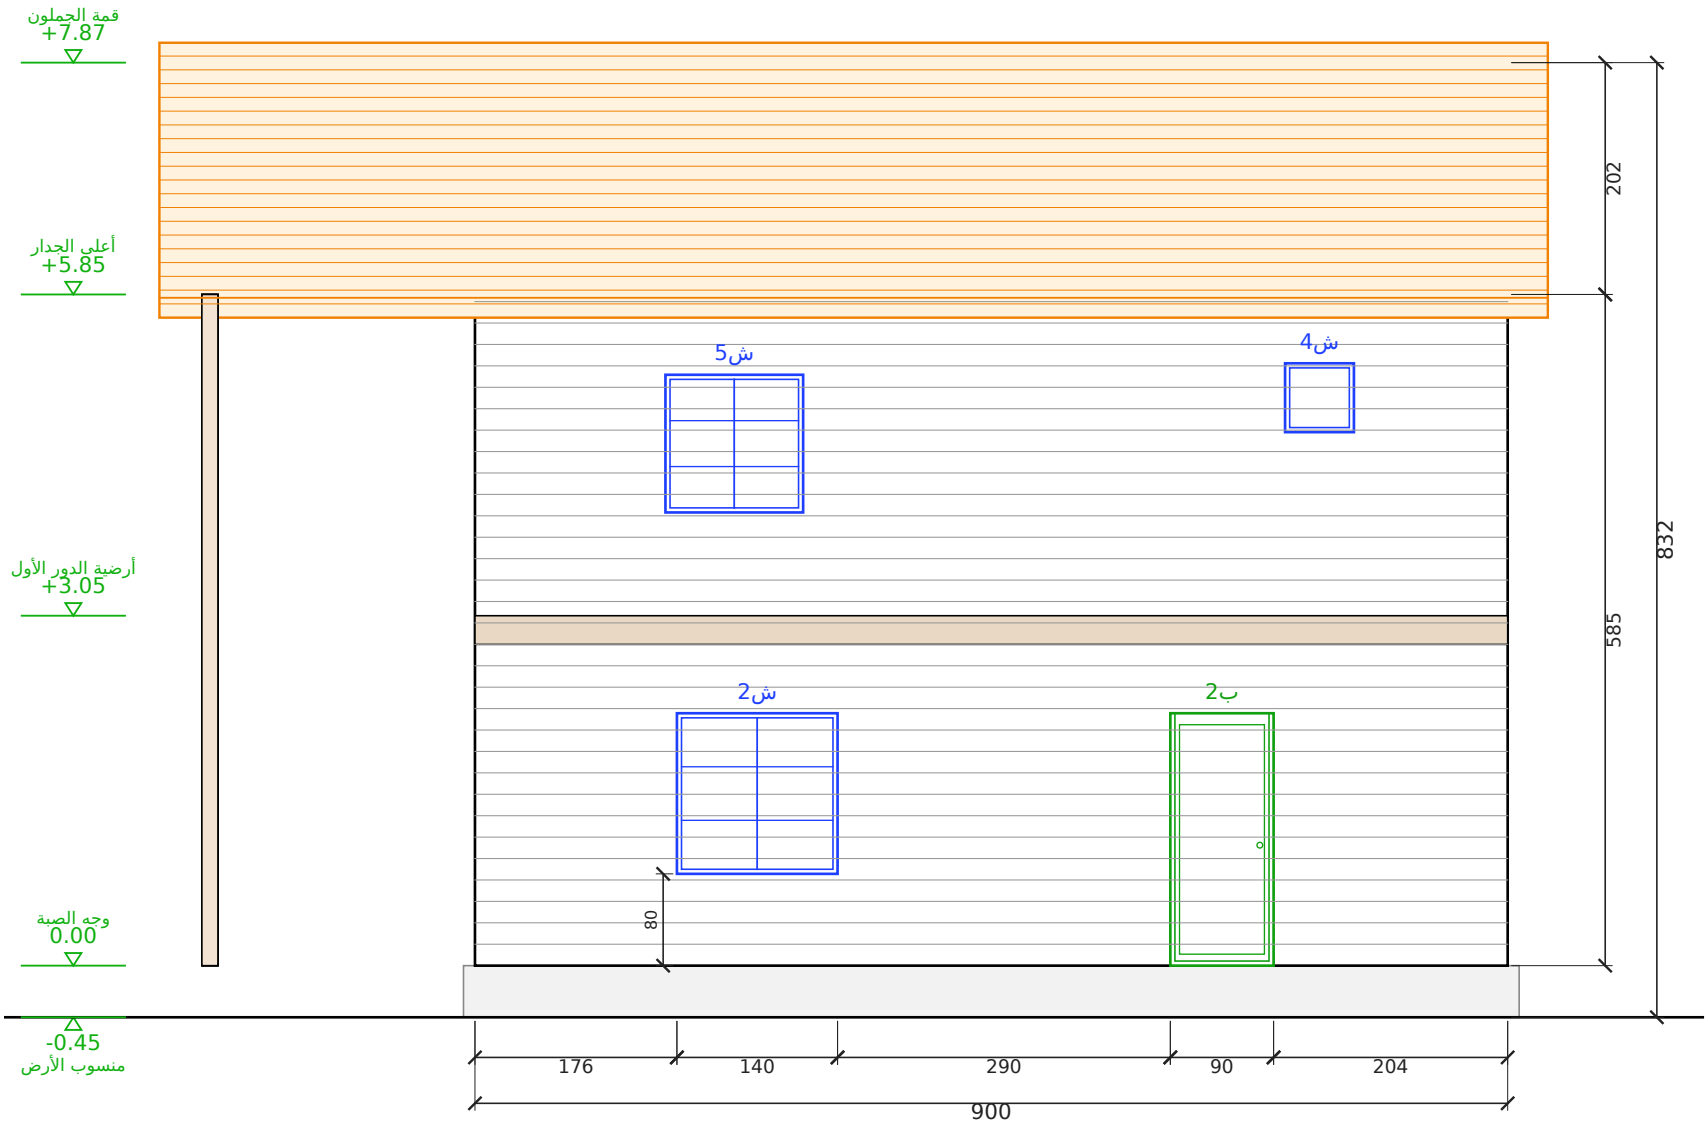

الواجهة الشرقية


مقياس 1:50 | الوحدة: سم

مصنع وتد الأخشاب Watad Wood Factory	المشروع / العميل فيلا خشب دورين — مجلس + غرفتين — 7.00 × 9.00 م (63 م² للدور) عميل — تبوك	عنوان اللوحة الواجهة الأمامية والواجهة الشرقية	المقياس 1:50	التاريخ 2026-10-23	رقم اللوحة A-03 (3/11)

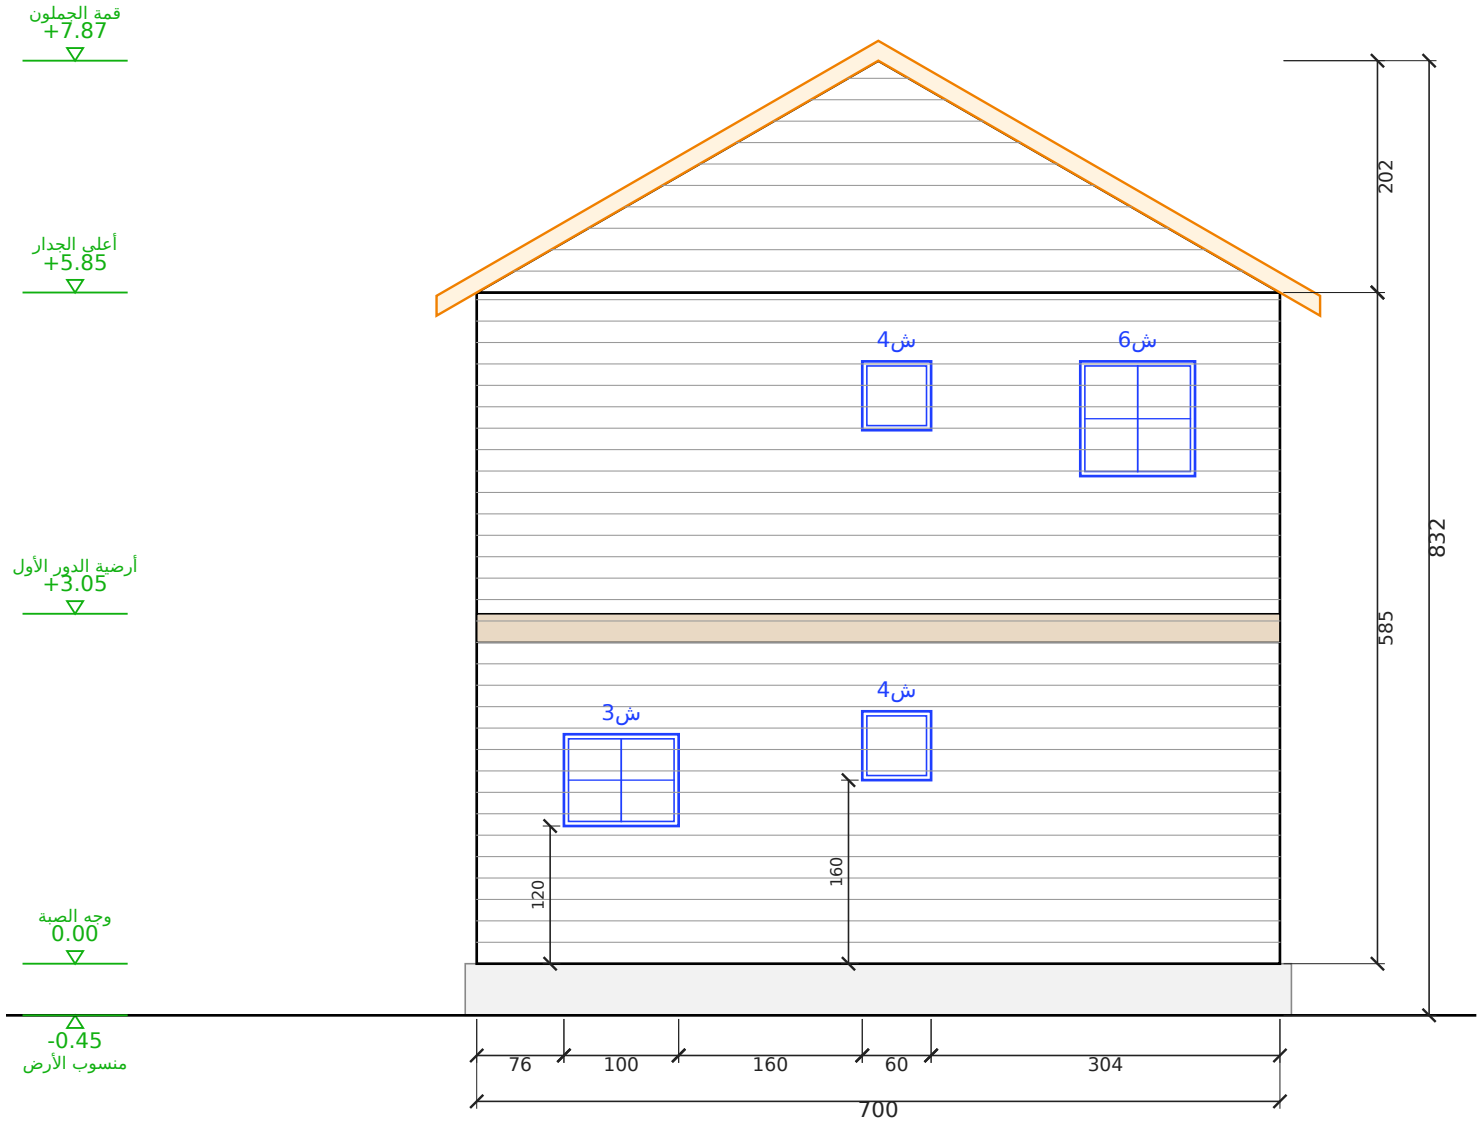

الواجهة الخلفية

مقياس 1:50 | الوحدة: سم

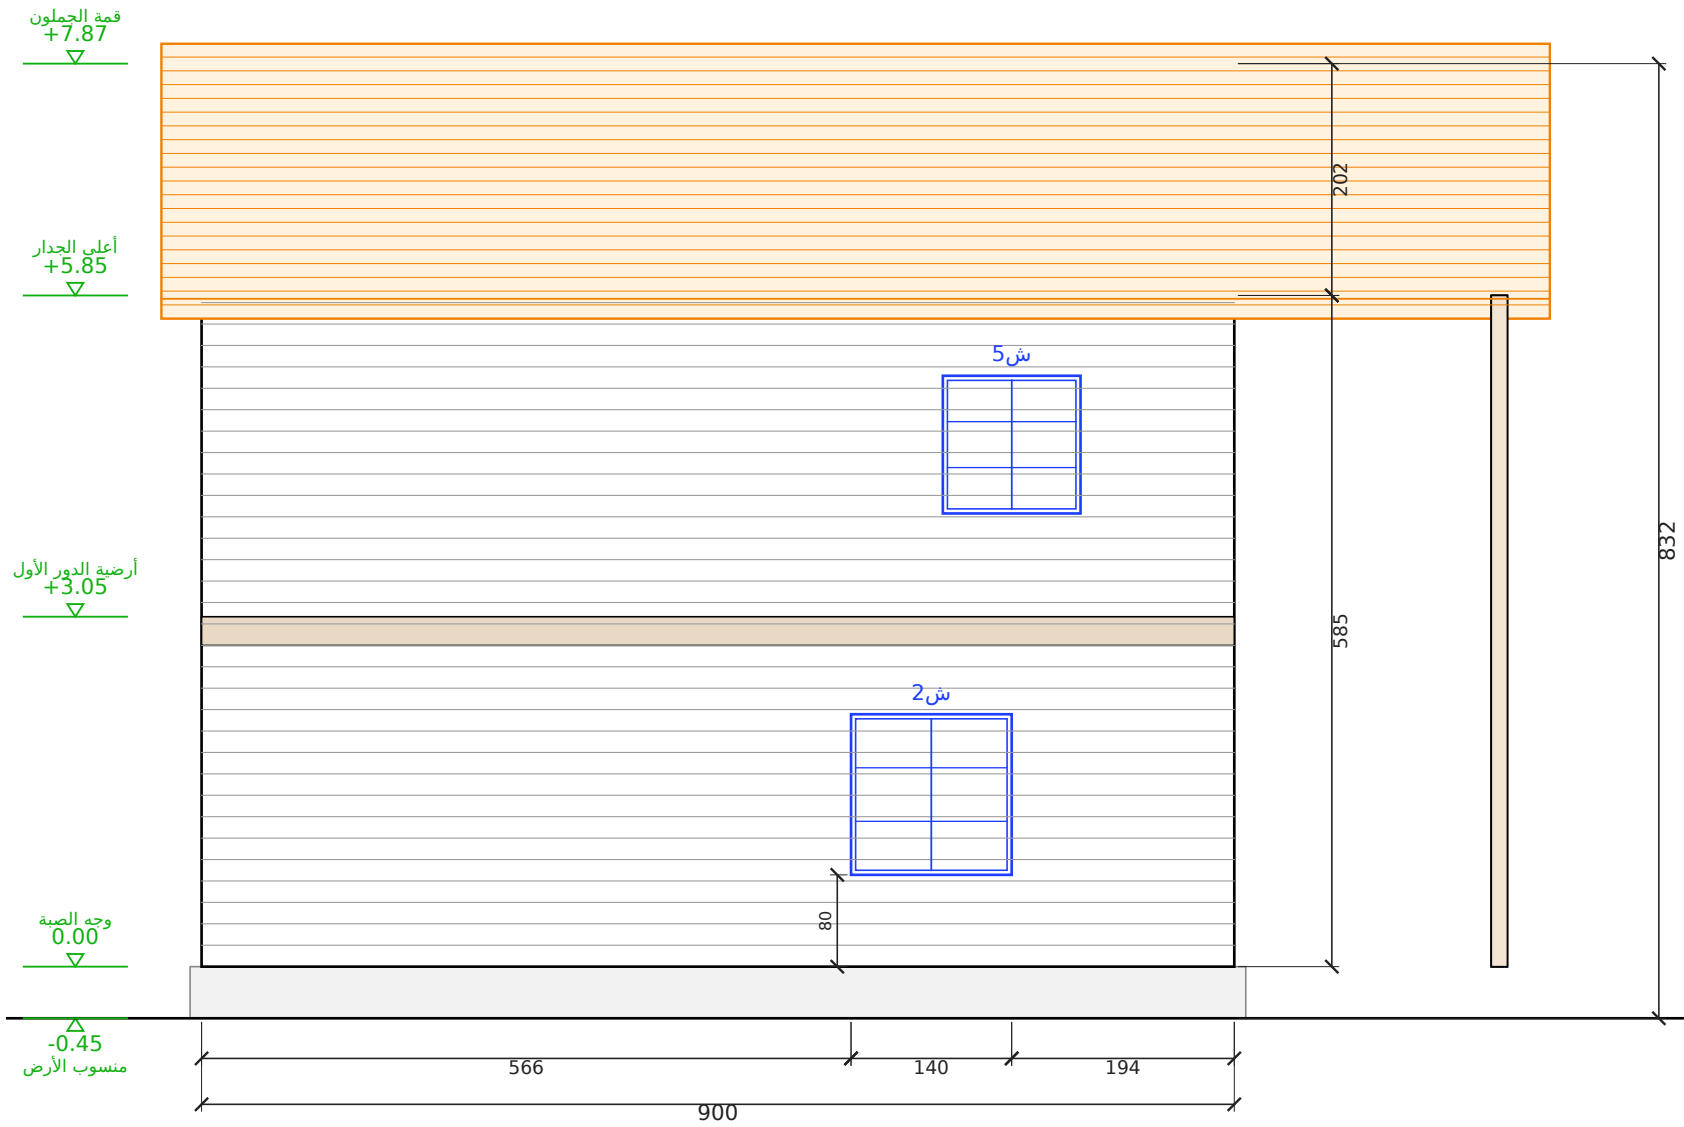


الواجهة الغربية


مقياس 1:50 | الوحدة: سم

المشروع / العميل	عنوان اللوحة	المقياس	التاريخ	رقم اللوحة
مصنع وتد الأخشاب Watad Wood Factory **فيلا خشب دورين — مجلس + غرفتين — 7.00 × 9.00 م (63 م² للدور)** **عميل — تبوك**	**الواجهة الخلفية والواجهة الغربية**	**1:50**	**2026-10-23**	**A-04 (4/11)**


مسقط السقف (جملون)
رفرف 35 سم من كل جهة | مقياس 1:50

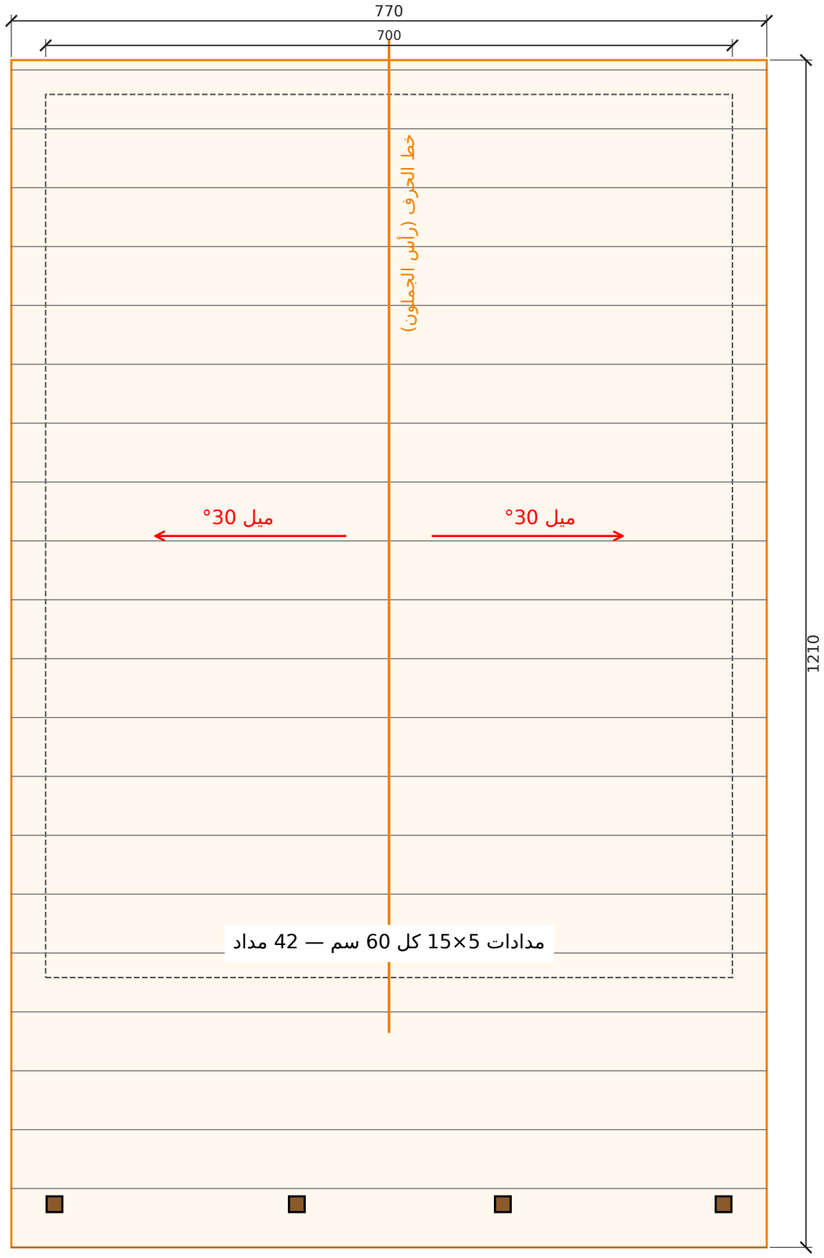

قطاع عرضي أ-أ
مقياس 1:50 | الوحدة: سم

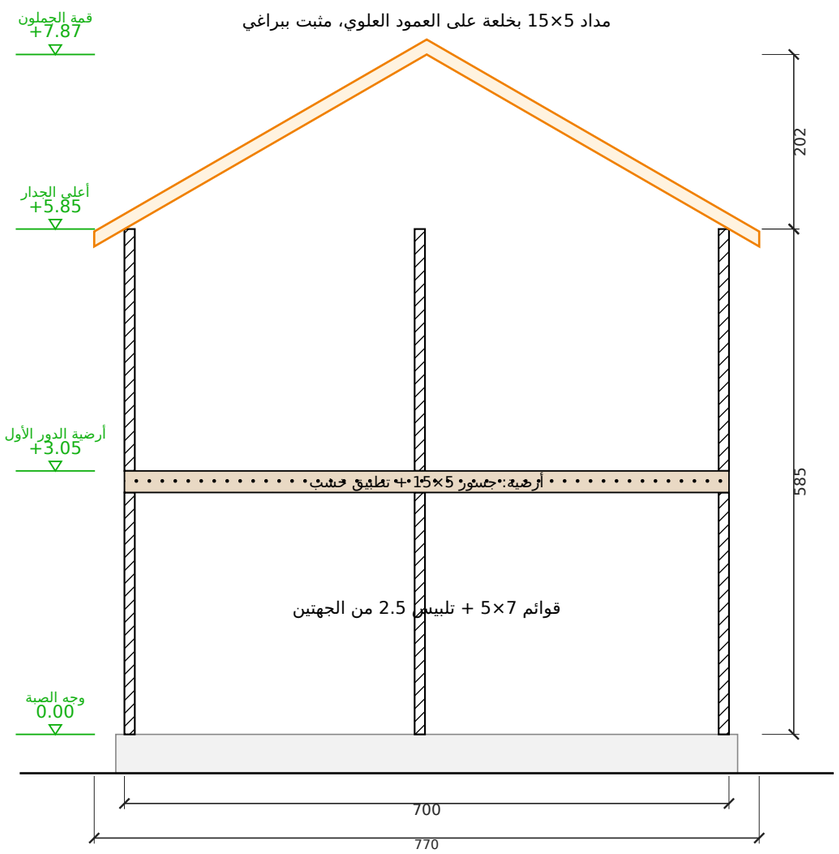

تفصيلة جلوس المداد على العلوي (1:5)

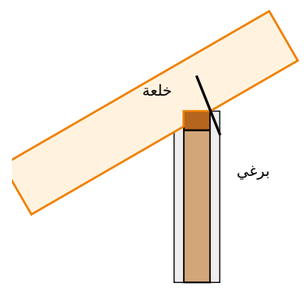

علوي 7×5 على قائم 7×5

المشروع / العميل	عنوان اللوحة	المقياس	التاريخ	رقم اللوحة
فيلا خشب دورين — مجلس + غرفتين — 7.00 × 9.00 م (63 م² للدور) **عميل — تبوك**	**مسقط السقف والقطاع**	**1:50**	**2026-10-23**	**A-05 (5/11)**

مصنع وتد الأخشاب
Watad Wood Factory

جدول مقاسات الأبواب والشبابيك
مقاس الفتحة الصافي في الجدار - الوحدة: سم

الرمز	النوع	العرض (سم)	الارتفاع (سم)	ارتفاع الجلسة (سم)	العدد	الموقع
ب1	باب	110	240	-	1	الأمامية
ب2	باب	90	220	-	1	الشرقية
ب3	باب	90	220	-	1	المجلس — المغاسل
ب4	باب	70	210	-	1	دورة المياه
ب5	باب مزدوج	220	220	-	1	الأمامية (على البلكونة)
ب5	باب مزدوج	230	220	-	1	الأمامية (على البلكونة)
ب6	باب	70	210	-	1	غرفة 2
ب6	باب	80	210	-	1	غرفة 1
ب7	باب	76	210	-	1	المخزن والغسيل
ب8	باب	70	210	-	1	دورة المياه
ف1	باب	284	250	-	1	بارتشن أعمدة وصناديق
ش1	شباك	180	150	80	2	الأمامية 2
ش2	شباك	140	140	80	2	الشرقية - الغربية
ش3	شباك	100	80	120	1	الخلفية
ش4	شباك	60	60	160	3	الخلفية 2 - الشرقية
ش5	شباك	120	120	90	2	الشرقية - الغربية
ش6	شباك	100	100	120	1	الخلفية

الإجمالي: أبواب 11 - شبابيك 11

جدول المساحات وبيانات المشروع والتسعير

بيانات المشروع

البند	البيان
المشروع	فيلا خشب دورين — مجلس + غرفتين — 7.00 × 9.00 م (63 م² للدور)
العميل	عميل — تبوك
الموقع	تبوك
الاستخدام	سكن — مجلس ضيوف + غرفتين
التاريخ	2026-10-23
نظام البناء	هيكل خشب 7×5 + تلبيس 2.5 سم من الجهتين
السقف	جملون 30° — قرميد معدني

جدول المساحات

م	الفراغ	الأبعاد (م)	المساحة (م2)
1	أرضي — المجلس	6.76 × 4.48	30.28
2	أرضي — ممر العائلة	4.38 × 0.92	4.03
3	أرضي — الدرج	2.28 × 3.00	6.84
4	أرضي — دورة مياه	1.98 × 3.12	6.18
5	أرضي — المغاسل	2.26 × 4.16	9.40
6	أول — غرفة نوم 2	3.24 × 4.48	14.52
7	أول — غرفة نوم 1	3.40 × 4.48	15.23
8	أول — الممر	4.38 × 0.92	4.03
9	أول — دورة مياه	1.98 × 3.12	6.18
10	أول — مخزن وغسيل	2.26 × 4.16	9.40
	المساحة الصافية الداخلية		106.09
	التراس	**7.00 × 2.40**	**16.80**
	البلكونة	**7.00 × 2.40**	**16.80**
	المساحة الإجمالية المبنية	**7.00 × 9.00 × 2 دور**	**126.00**
	المساحة الكلية (المبنية + التراس والبلكونة)		**159.60**

التسعير المفصّل

البند	المبلغ (ريال)
الكوخ المبني 126.00 م² × 1,096	138,096
تراس الأرضي + بلكونة الأول (7.00 × 2.40 × 2) — 33.60 م² × 1,096	36,826
الإجمالي (ريال)	**174,922**

ملاحظات:

- السعر للدورين والتراس والبلكونة حسب المخطط المعتمد — التراس يُسعّر بنفس سعر متر الكوخ.
- الصبة والتمديدات الخارجية على العميل ما لم يُذكر غير ذلك.

لقطات المنظور الخارجي


المنظور الأمامي



منظور أمامي من اليسار




منظور أمامي من اليمين

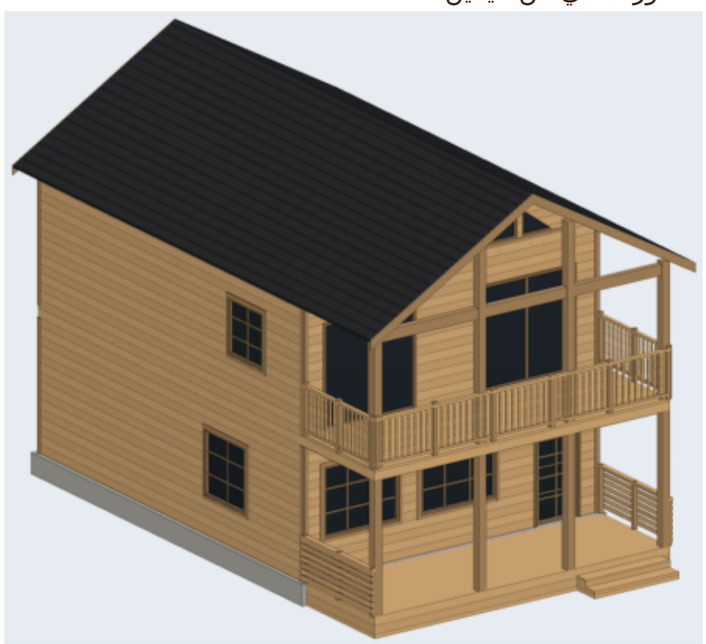


المنظور الخلفي



منظور خلفي من اليمين

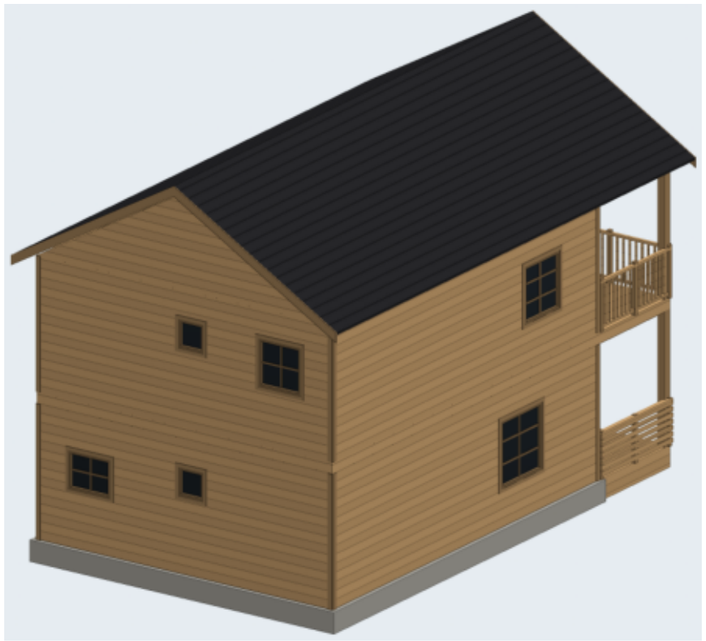


منظر علوي

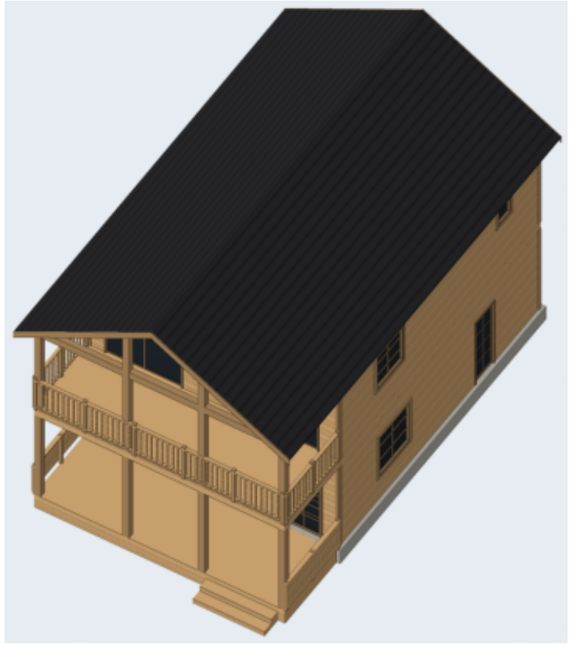

مصنع وتد الأخشاب Watad Wood Factory	المشروع / العميل **فيلا خشب دورين — مجلس + غرفتين — 7.00 × 9.00 م (63 م² للدور)** **عميل — تبوك**	عنوان اللوحة **لقطات المنظور**	المقياس **—**	التاريخ **2026-10-23**	رقم اللوحة **A-08 (8/11)**

المقطع العلوي بالفرش — الدور الأرضي


مقطع أفقي على ارتفاع 1.90 م — توزيع الفرش ومسار الحركة

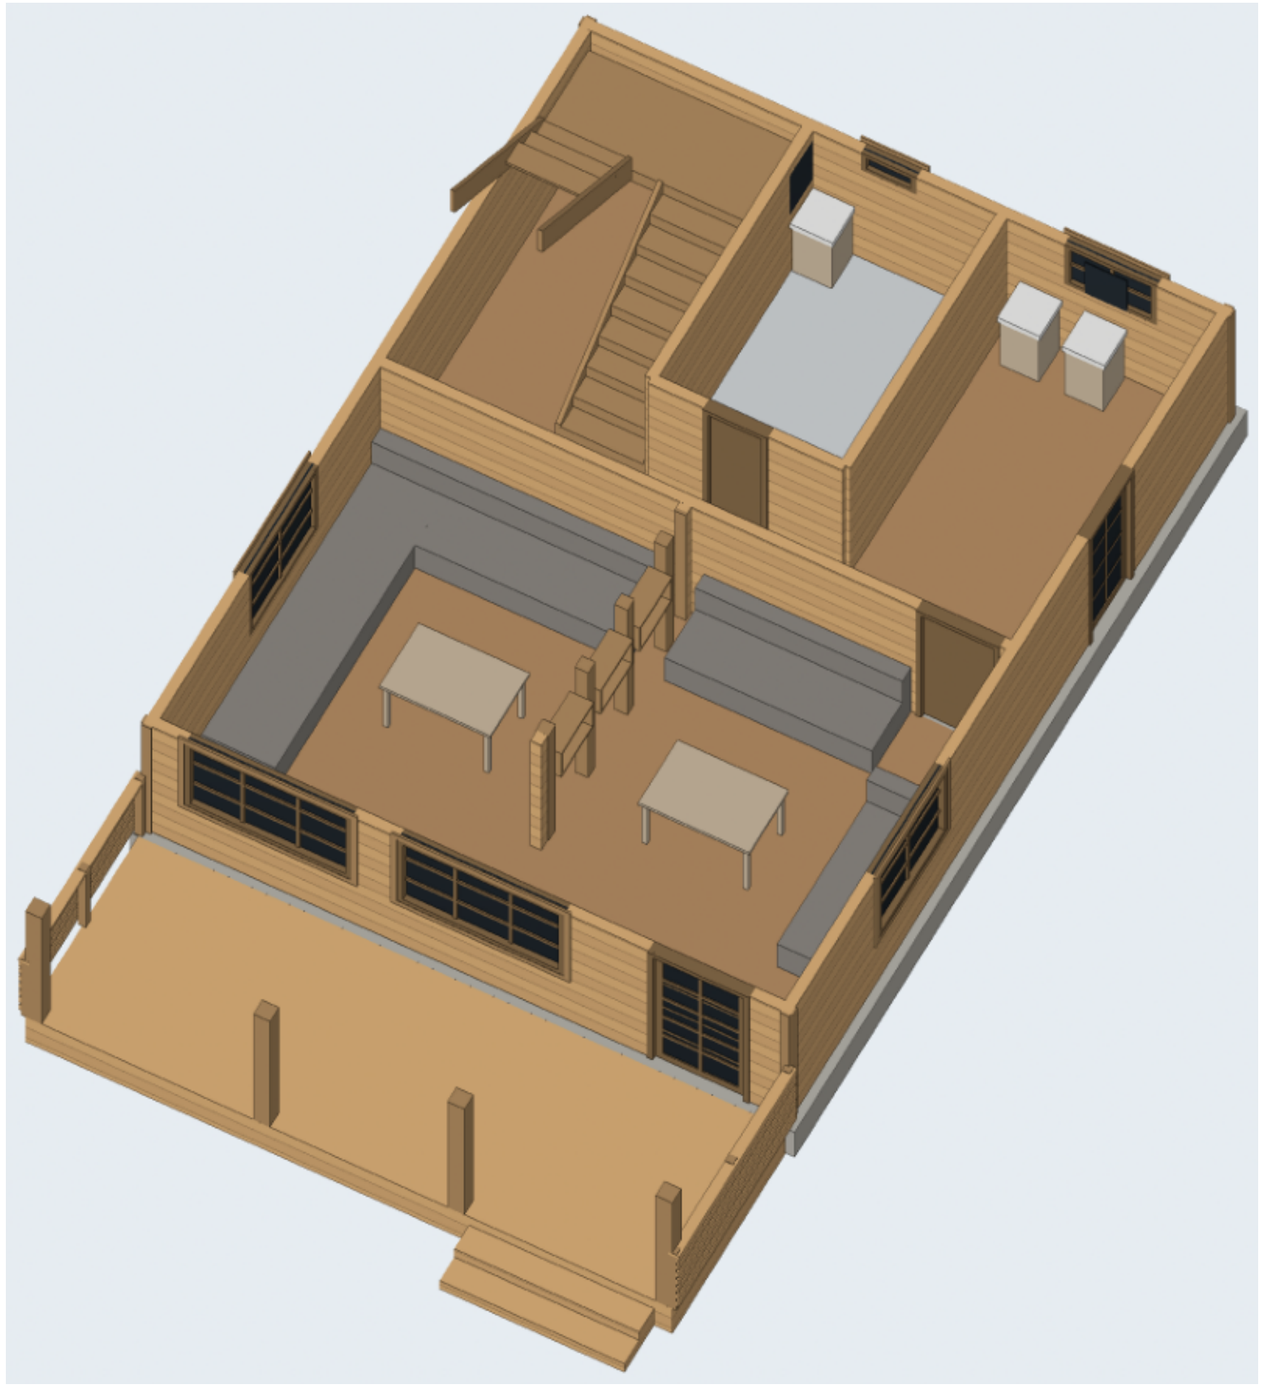

المشروع / العميل	عنوان اللوحة	المقياس	التاريخ	رقم اللوحة
مصنع وتد الأخشاب Watad Wood Factory **فيلا خشب دورين — مجلس + غرفتين — 7.00 × 9.00 م (63 م² للدور)** **عميل — تبوك**	**المقطع العلوي بالفرش — الدور الأرضي**	**—**	**2026-10-23**	**A-09 (9/11)**

المقطع العلوي بالفرش — الدور الأول

مقطع أفقي على ارتفاع 1.90 م — توزيع الفرش ومسار الحركة

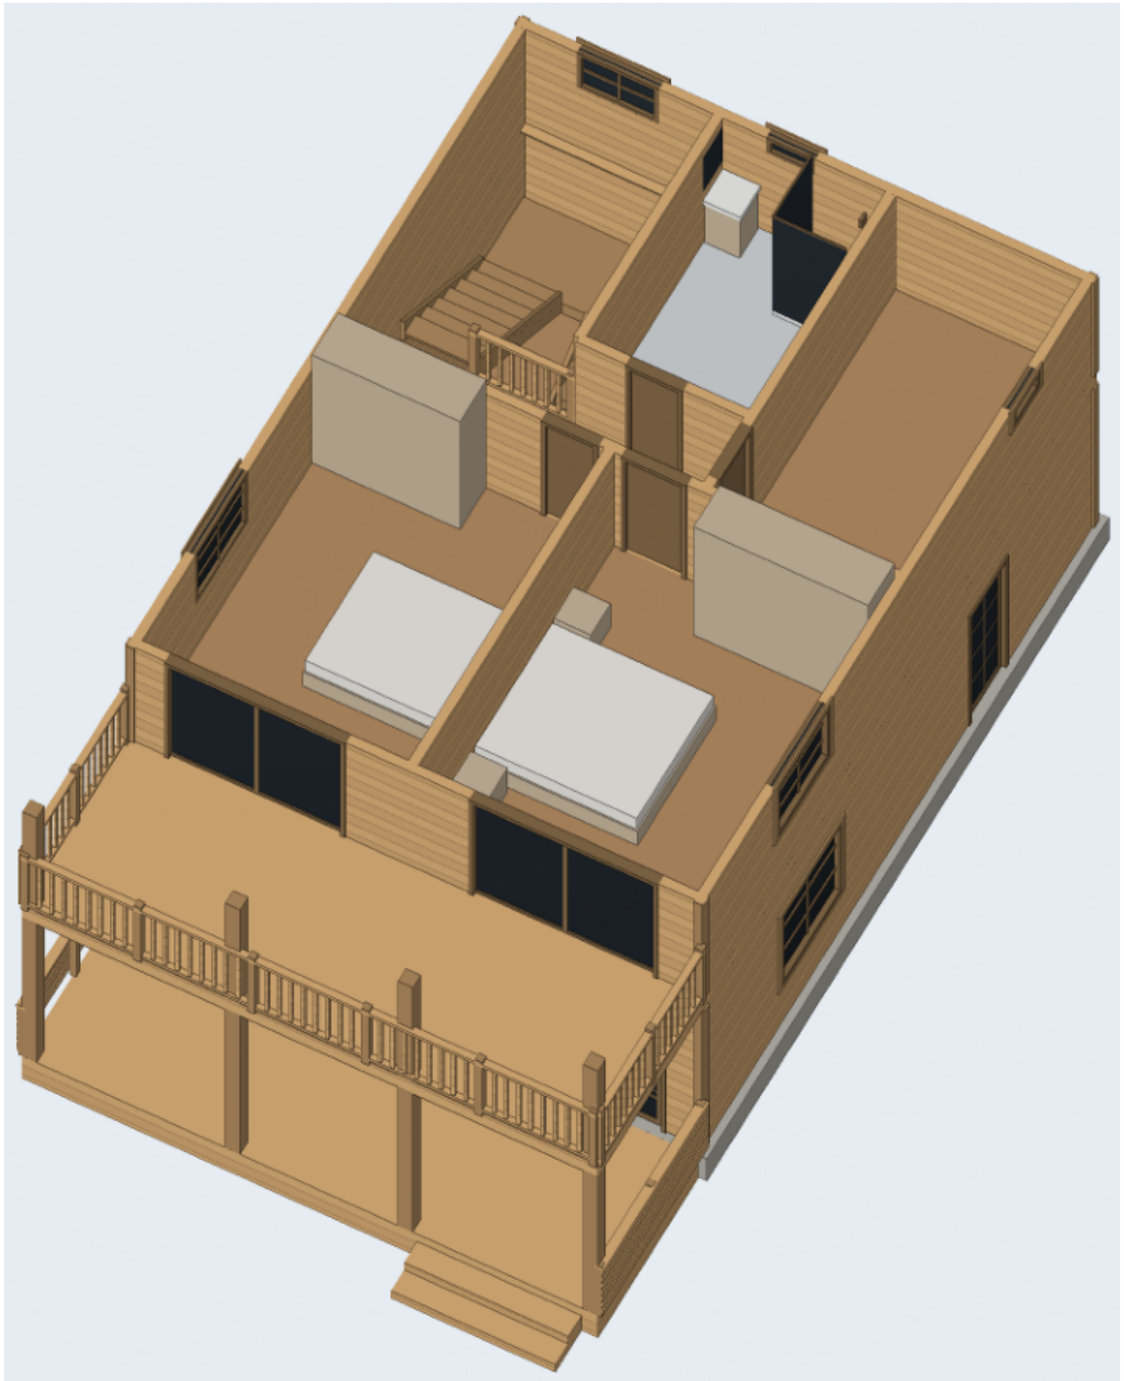

المشروع / العميل	عنوان اللوحة	المقياس	التاريخ	رقم اللوحة
فيلا خشب دورين — مجلس + غرفتين — 7.00 × 9.00 م (63 م² للدور) **عميل — تبوك**	**المقطع العلوي بالفرش — الدور الأول**	**—**	**2026-10-23**	**A-10 (10/11)**

مصنع وتد الأخشاب
Watad Wood Factory

المنظور ثلاثي الأبعاد والمواد

النمط: جوزي غامق + إطارات سوداء — رندر واقعي بخامات حقيقية



جدول المواد والألوان

الخشب / الصبغة

خشب طبيعي فاتح (بدون صبغة)

القرميد

قرميد رمادي غامق

الزجاج

زجاج عاكس غامق

إطارات الشبابيك والأبواب

إطار خشب بنفس الصبغة أغمق

الكنار والزوايا

نفس الصبغة أغمق درجة


الصبة

خرسانة 45 سم


الدربزين: ألواح أفقية متقاربة (عصري)

تقسيم الشبابيك: بدون | الباب الرئيسي: زجاج بتقسيمات (فرنسي)

أنواع الدربزين المعتمدة (من مشاريع المصنع)

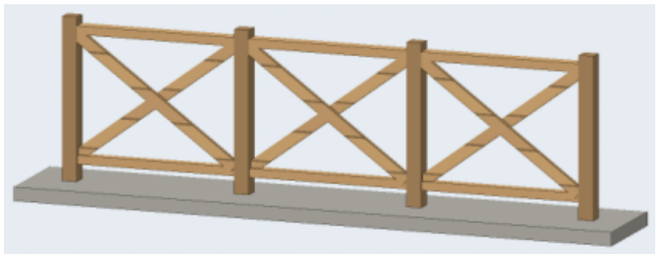

تقاطع X (صورة 5)

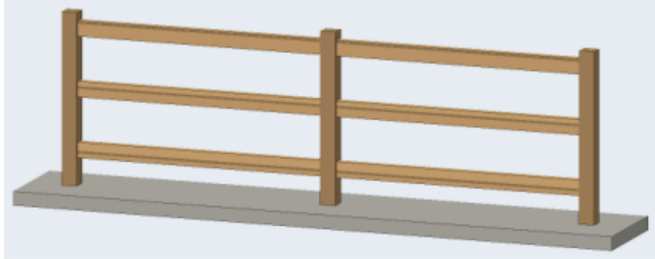

3 مرابيع أفقية (صورة 2)



قوائم رأسية متقاربة (صورة 1)

المشروع / العميل	عنوان اللوحة	المقياس	التاريخ	رقم اللوحة
مصنع وتد الأخشاب Watad Wood Factory **فيلا خشب دورين — مجلس + غرفتين — 7.00 × 9.00 م (63 م² للدور)** **عميل — تبوك**	**المنظور والمواد**	**—**	**2026-10-23**	**A-11 (11/11)**

الرندر الواقعي — الخارج نهاراً · أمامي من اليسار



مصنع وتد الأخشاب

الرندر الواقعي — الخارج نهاراً · أمامي من اليمين



مصنع وتد الأخشاب

الرندر الواقعي — الخارج نهاراً · الواجهة الأمامية



مصنع وتد الأخشاب

الرندر الواقعي — الخارج نهاراً · خلفي من اليسار



مصنع وتد الأخشاب

الرندر الواقعي — وقت الغروب وبالليل · أمامي من اليسار — وقت الغروب



مصنع وتد الأخشاب

الرندر الواقعي — وقت الغروب وبالليل · أمامي من اليمين — وقت الغروب



مصنع وتد الأخشاب

الرندر الواقعي — وقت الغروب وبالليل · المجلس — البارتشن وصناديق الفازات — بالليل والإنارة شغالة



مصنع وتد الأخشاب

الرندر الواقعي — الداخل · المجلس — البارتشن وصناديق الفازات



مصنع وتد الأخشاب

الرندر الواقعي — الداخل · المجلس — من الجلسة الغربية



مصنع وتد الأخشاب



مصنع وتد الأخشاب