
المنظور ثلاثي الأبعاد والمواد

النمط: جوزي غامق + إطارات سوداء — رندر واقعي بخامات حقيقية

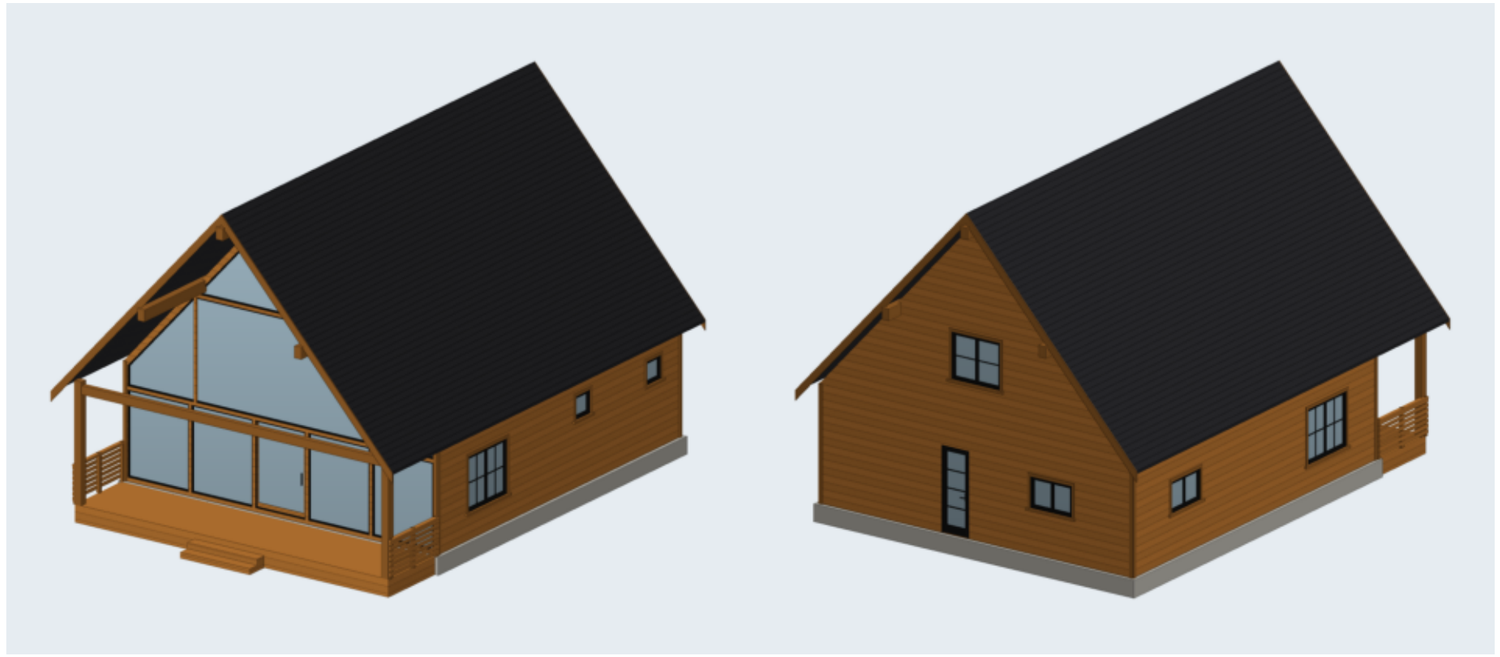

جدول المواد والألوان

الخشب / الصبغة

صبغة عسلي / سيدر

القرميد

قرميد رمادي غامق

الزجاج

زجاج شفاف

إطارات الشبابيك والأبواب

إطار ألمنيوم أسود

الكنار والزوايا

نفس الصبغة أغمق درجة


الصبة

خرسانة 45 سم


الدربزين: ألواح أفقية متقاربة (عصري)

تقسيم الشبابيك: بدون | الباب الرئيسي: زجاج بتقسيمات (فرنسي)

أنواع الدربزين المعتمدة (من مشاريع المصنع)

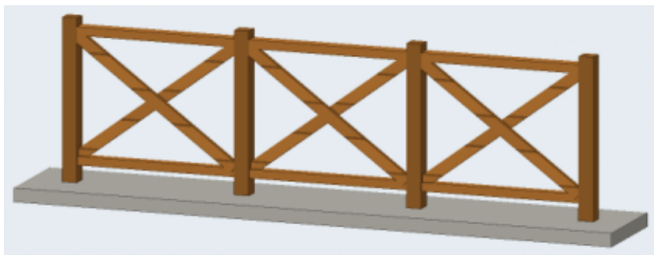

تقاطع X (صورة 5)

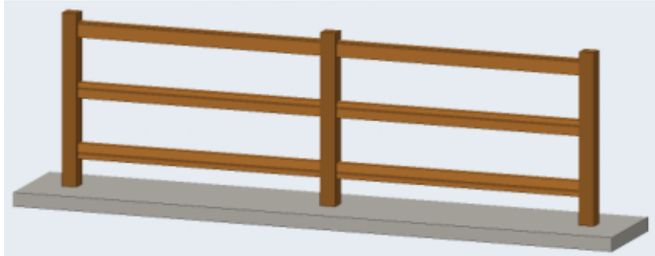

3 مرابيع أفقية (صورة 2)




قوائم رأسية متقاربة (صورة 1)

المشروع / العميل	عنوان اللوحة	المقياس	التاريخ	رقم اللوحة
مصنع وتد الأخشاب Watad Wood Factory — **كوخ A-frame دورين — صالة ومطبخ أمريكي وحمامين + غرفتين وحمام — 9.00 × 10.00 م** — **عميل — A-frame دورين**	**المنظور والمواد**	**1:50**	**2026-10-24**	**W-01 (1/13)**


المسقط الأفقي مع الفرش

الأبعاد بالسنتيمتر - الجدران: قوائم 7×5 + تلبيس 2.5 من الجهتين (12 سم)

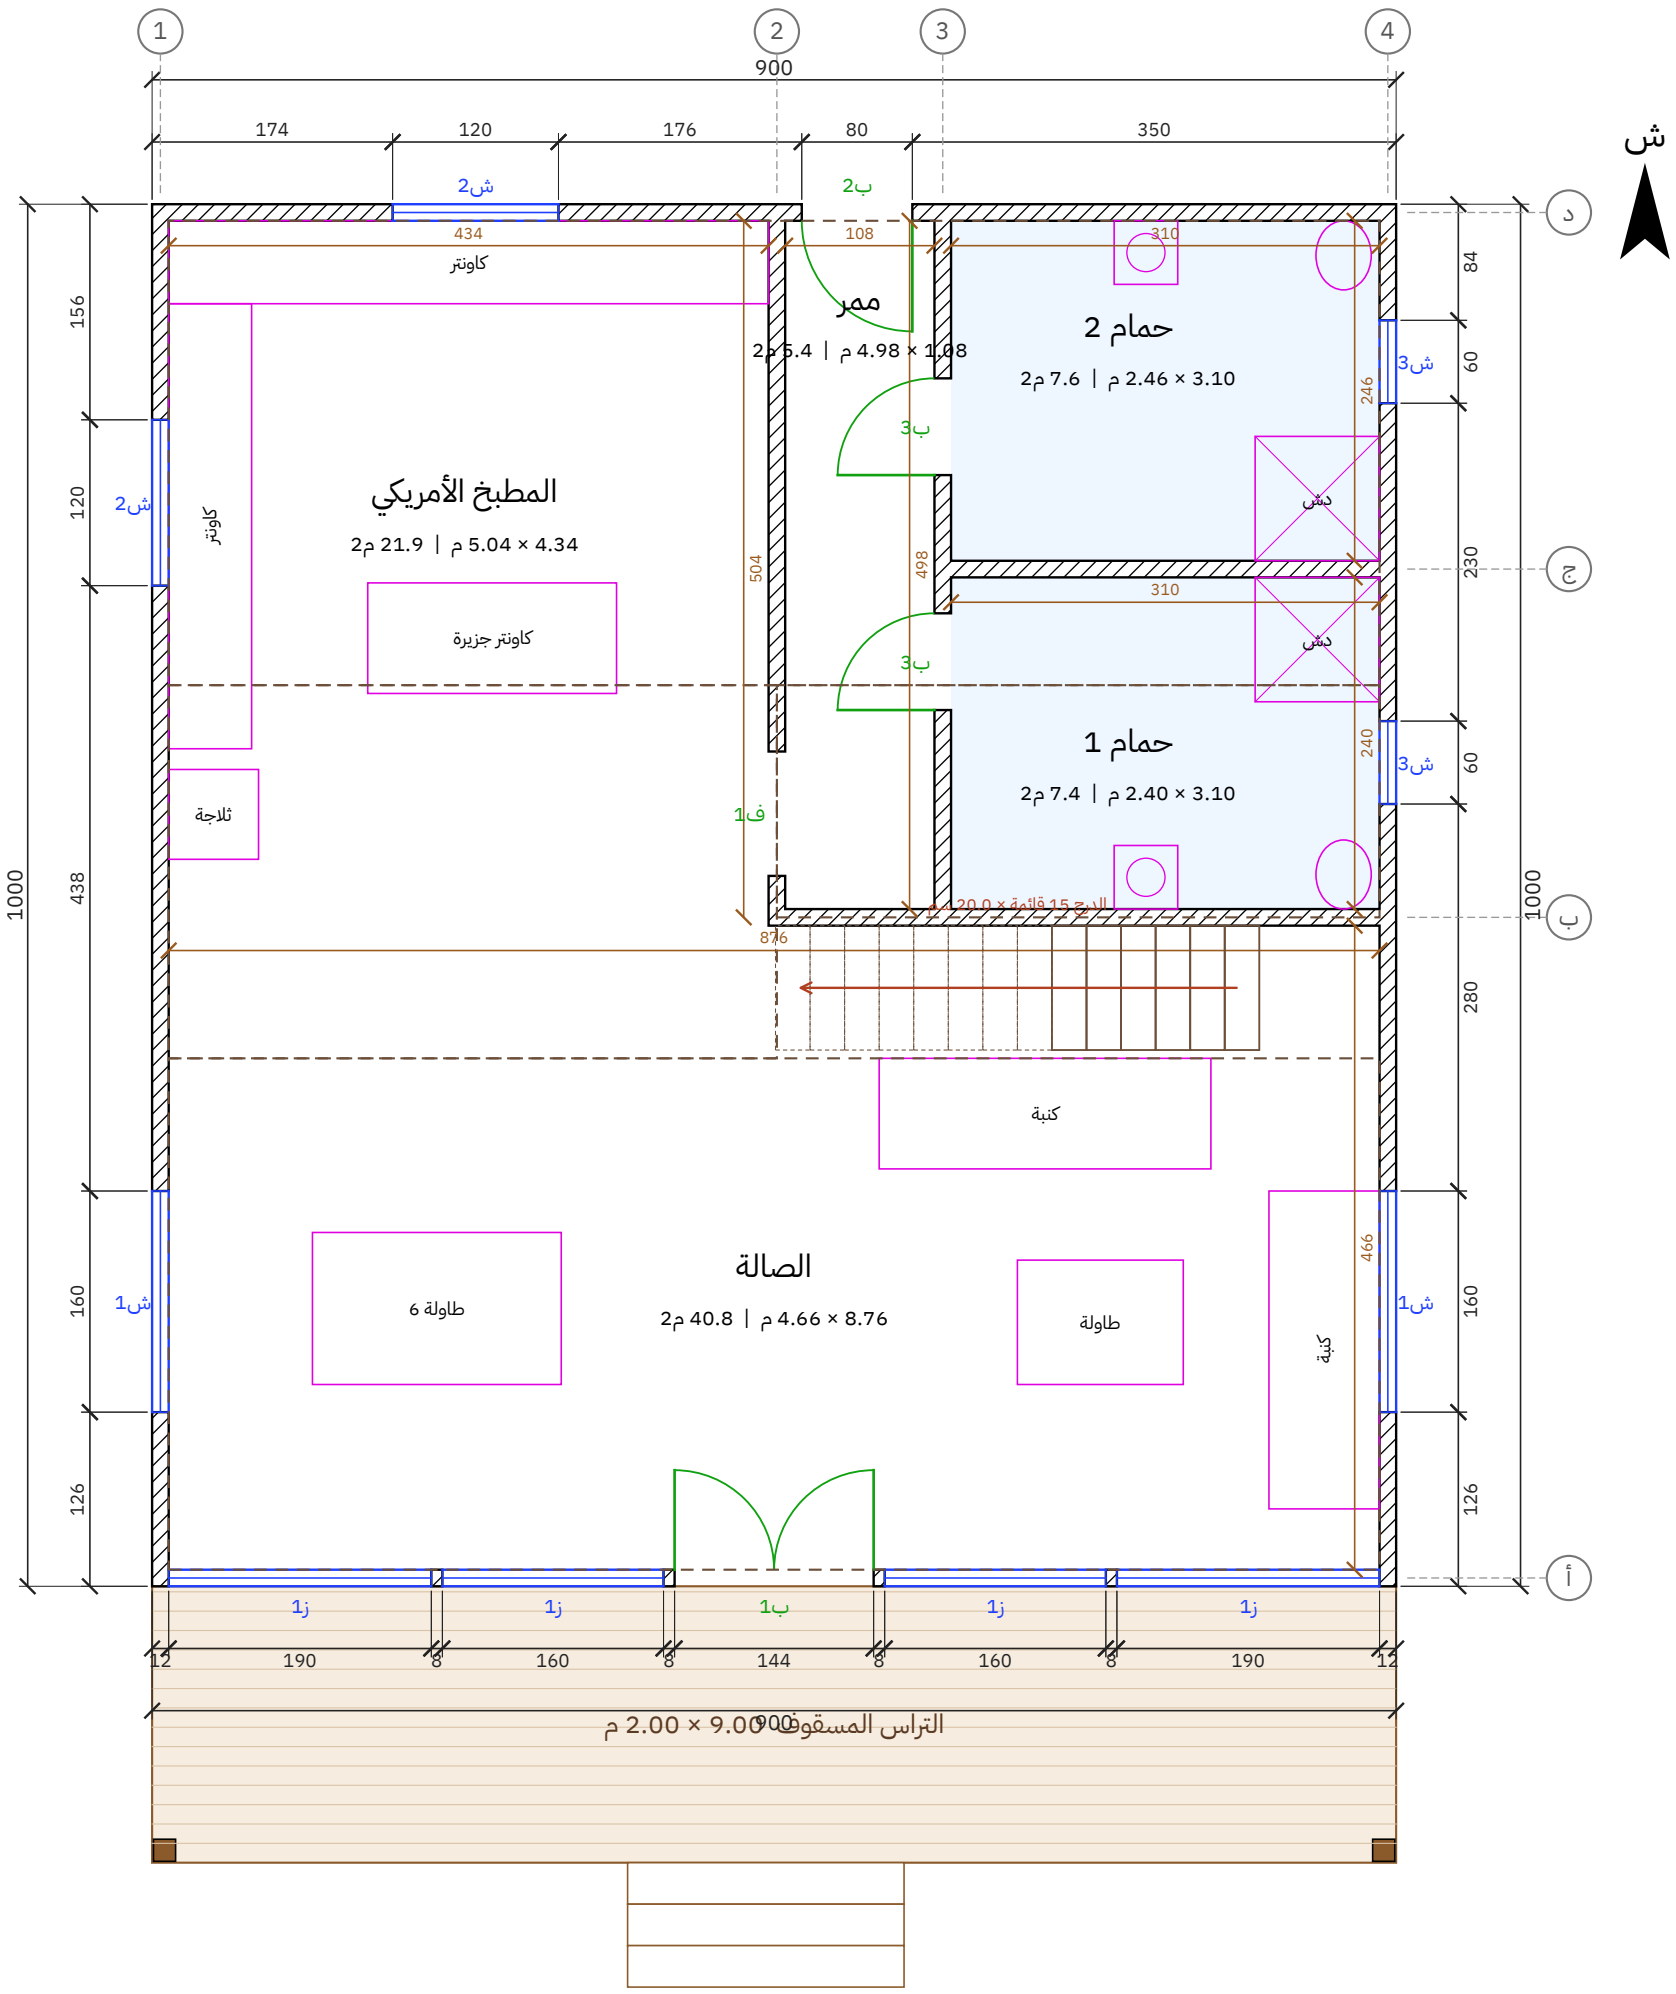


المشروع / العميل	عنوان اللوحة	المقياس	التاريخ	رقم اللوحة
كوخ A-frame دورين — صالة ومطبخ أمريكي وحمامين + غرفتين وحمام — 9.00 × 10.00 م عميل — A-frame دورين	المسقط الأفقي	1:50	2026-10-24	W-02 (2/13)

مصنع وتد الأخشاب
Watad Wood Factory

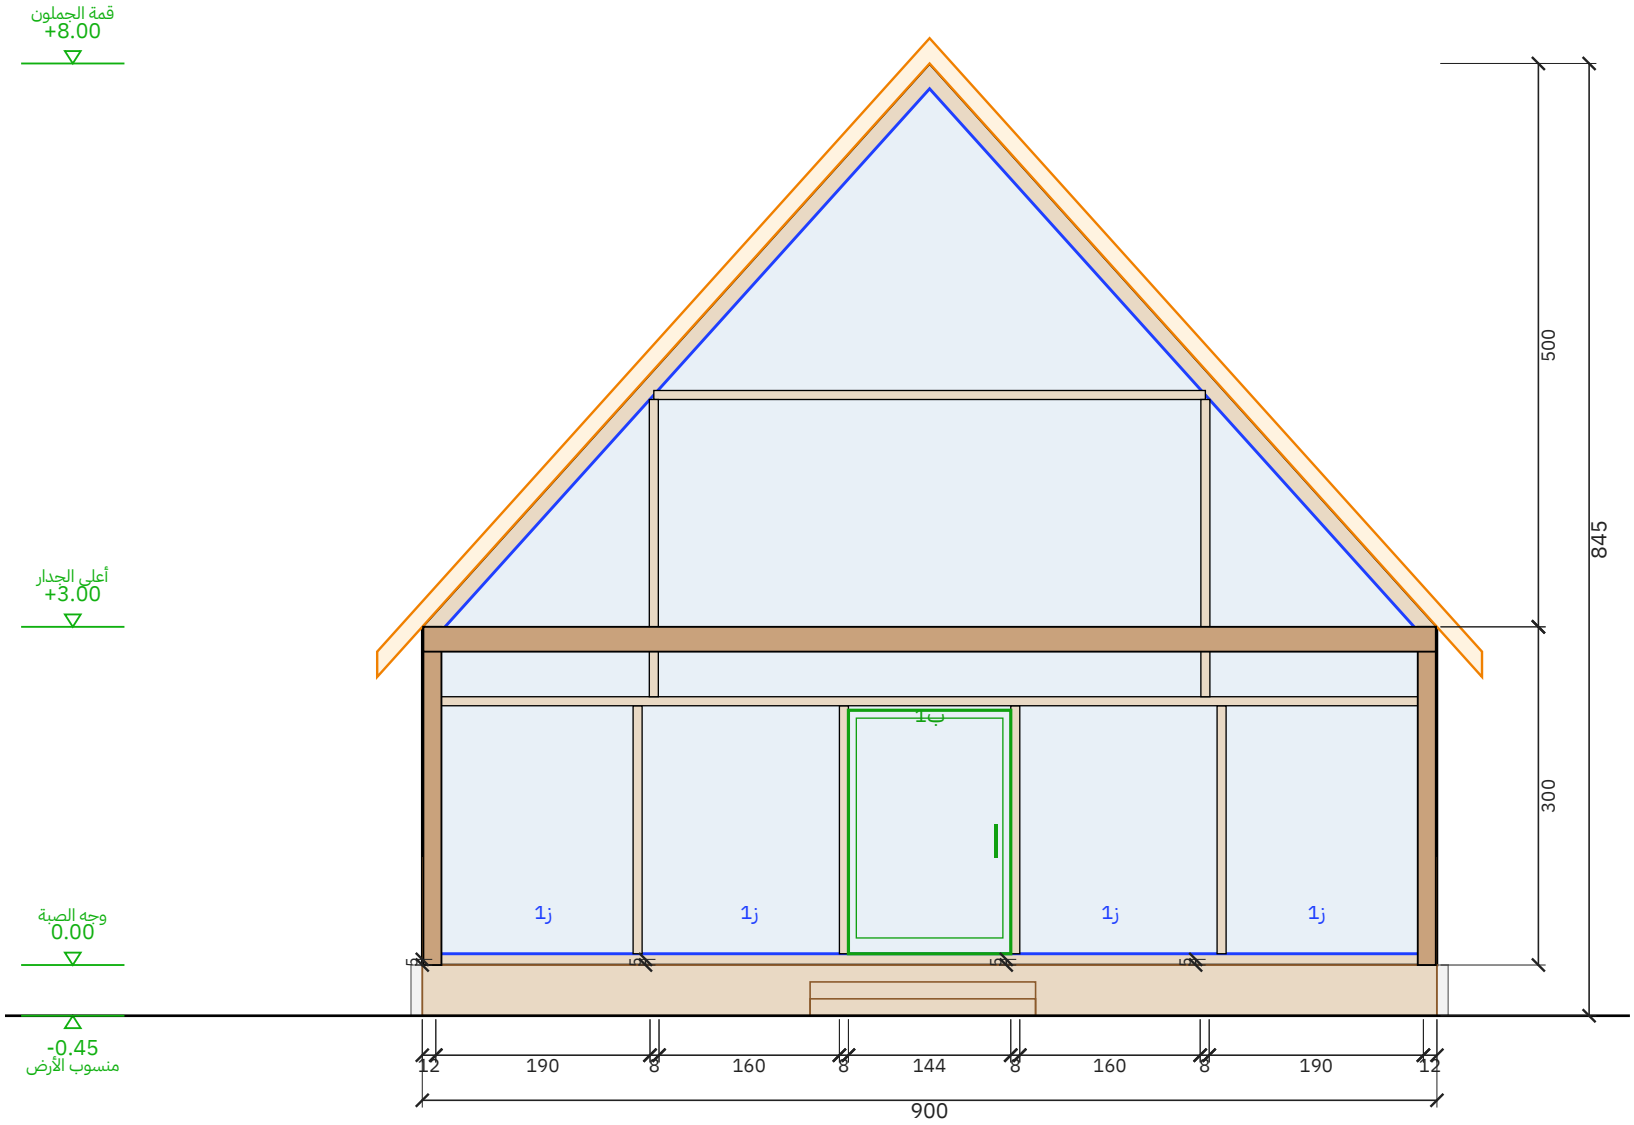

الواجهة الأمامية (زجاج كامل)

مقياس 1:50 | الوحدة: سم

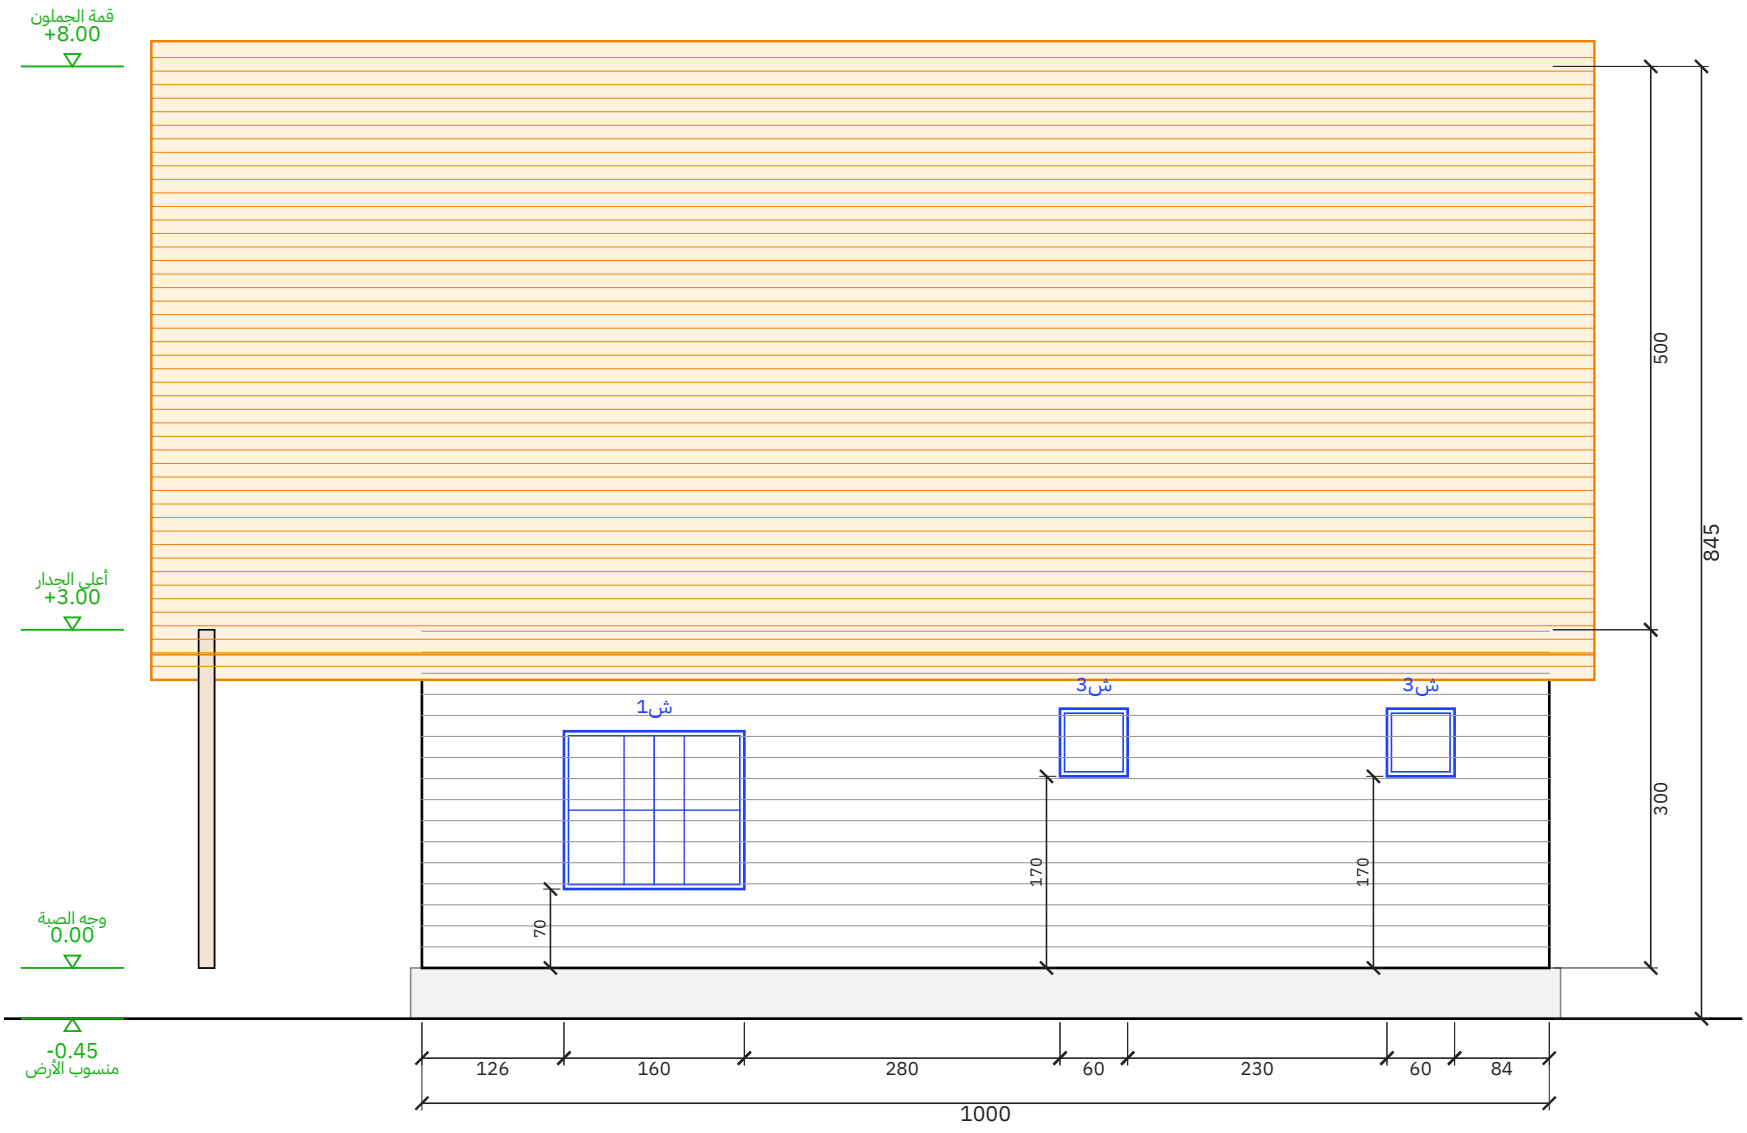


الواجهة الشرقية

مقياس 1:50 | الوحدة: سم


المشروع / العميل	عنوان اللوحة	المقياس	التاريخ	رقم اللوحة
كوخ A-frame دورين — صالة ومطبخ أمريكي وحمامين + غرفتين وحمام — 9.00 × 10.00 م عميل — A-frame دورين	الواجهة الأمامية (زجاج كامل) والواجهة الشرقية	1:50	2026-10-24	W-03 (3/13)

مصنع وتد الأخشاب
Watad Wood Factory

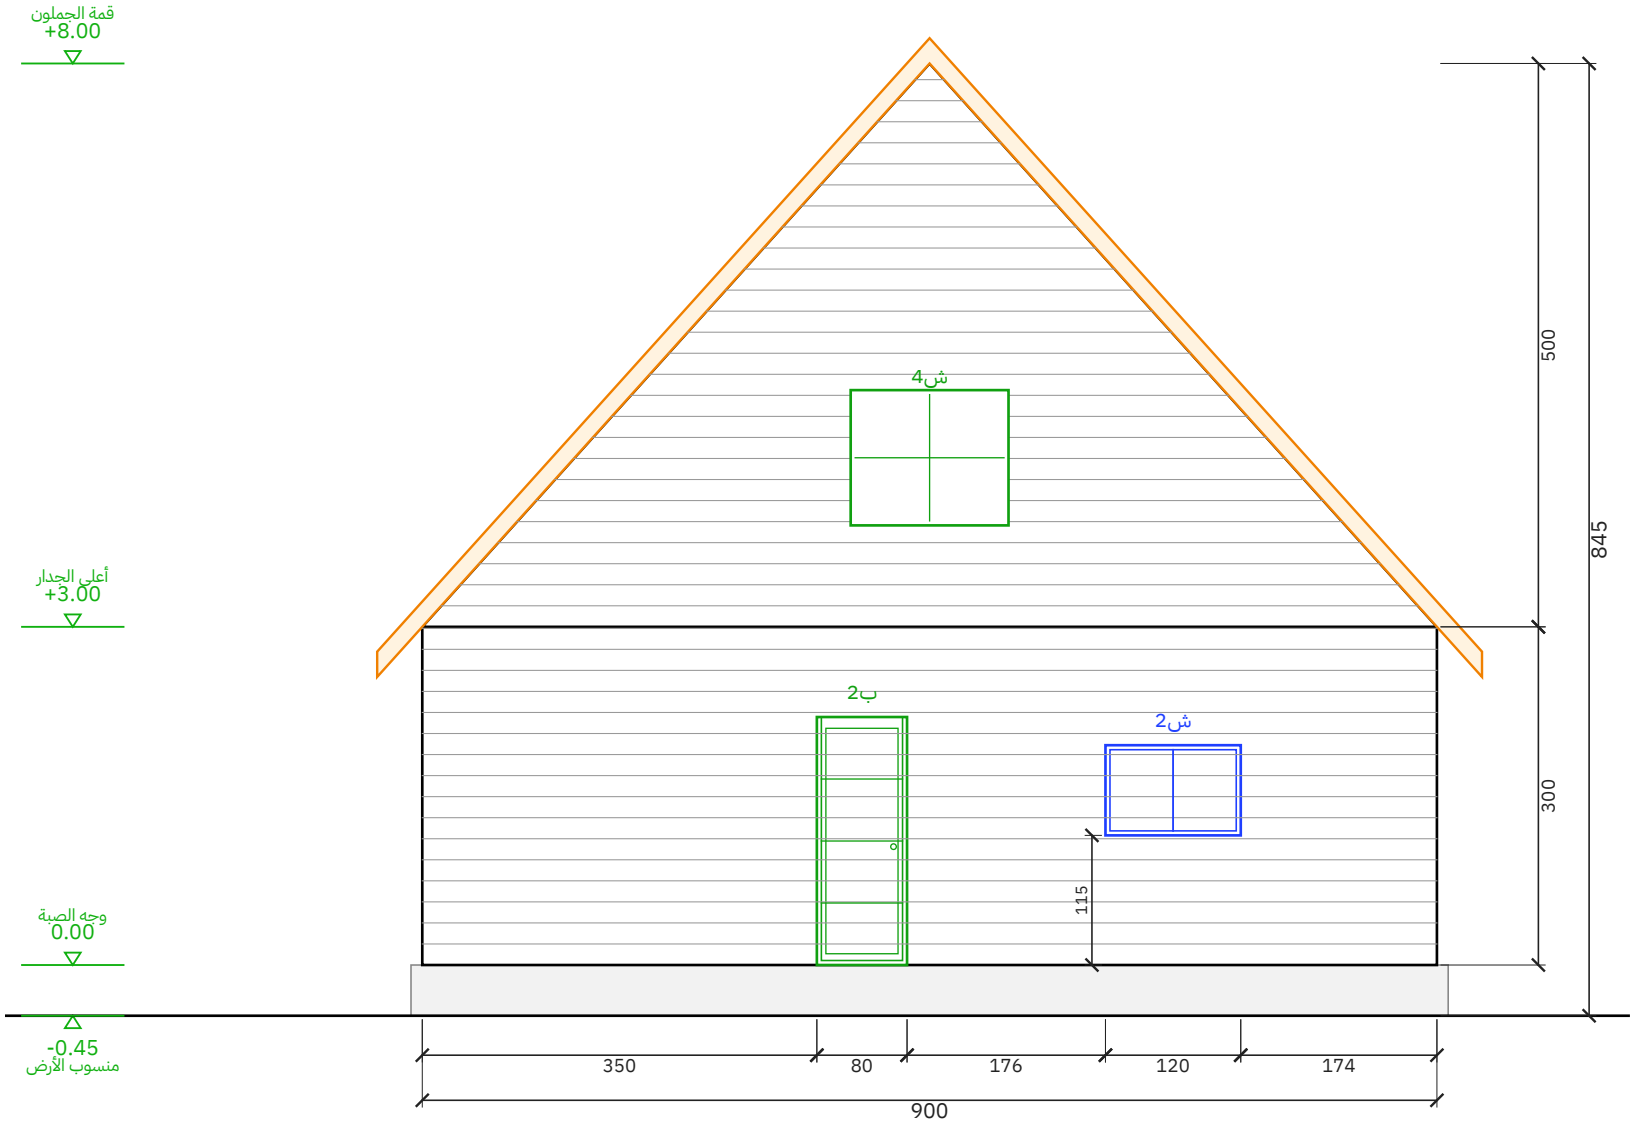

الواجهة الخلفية

مقياس 1:50 | الوحدة: سم

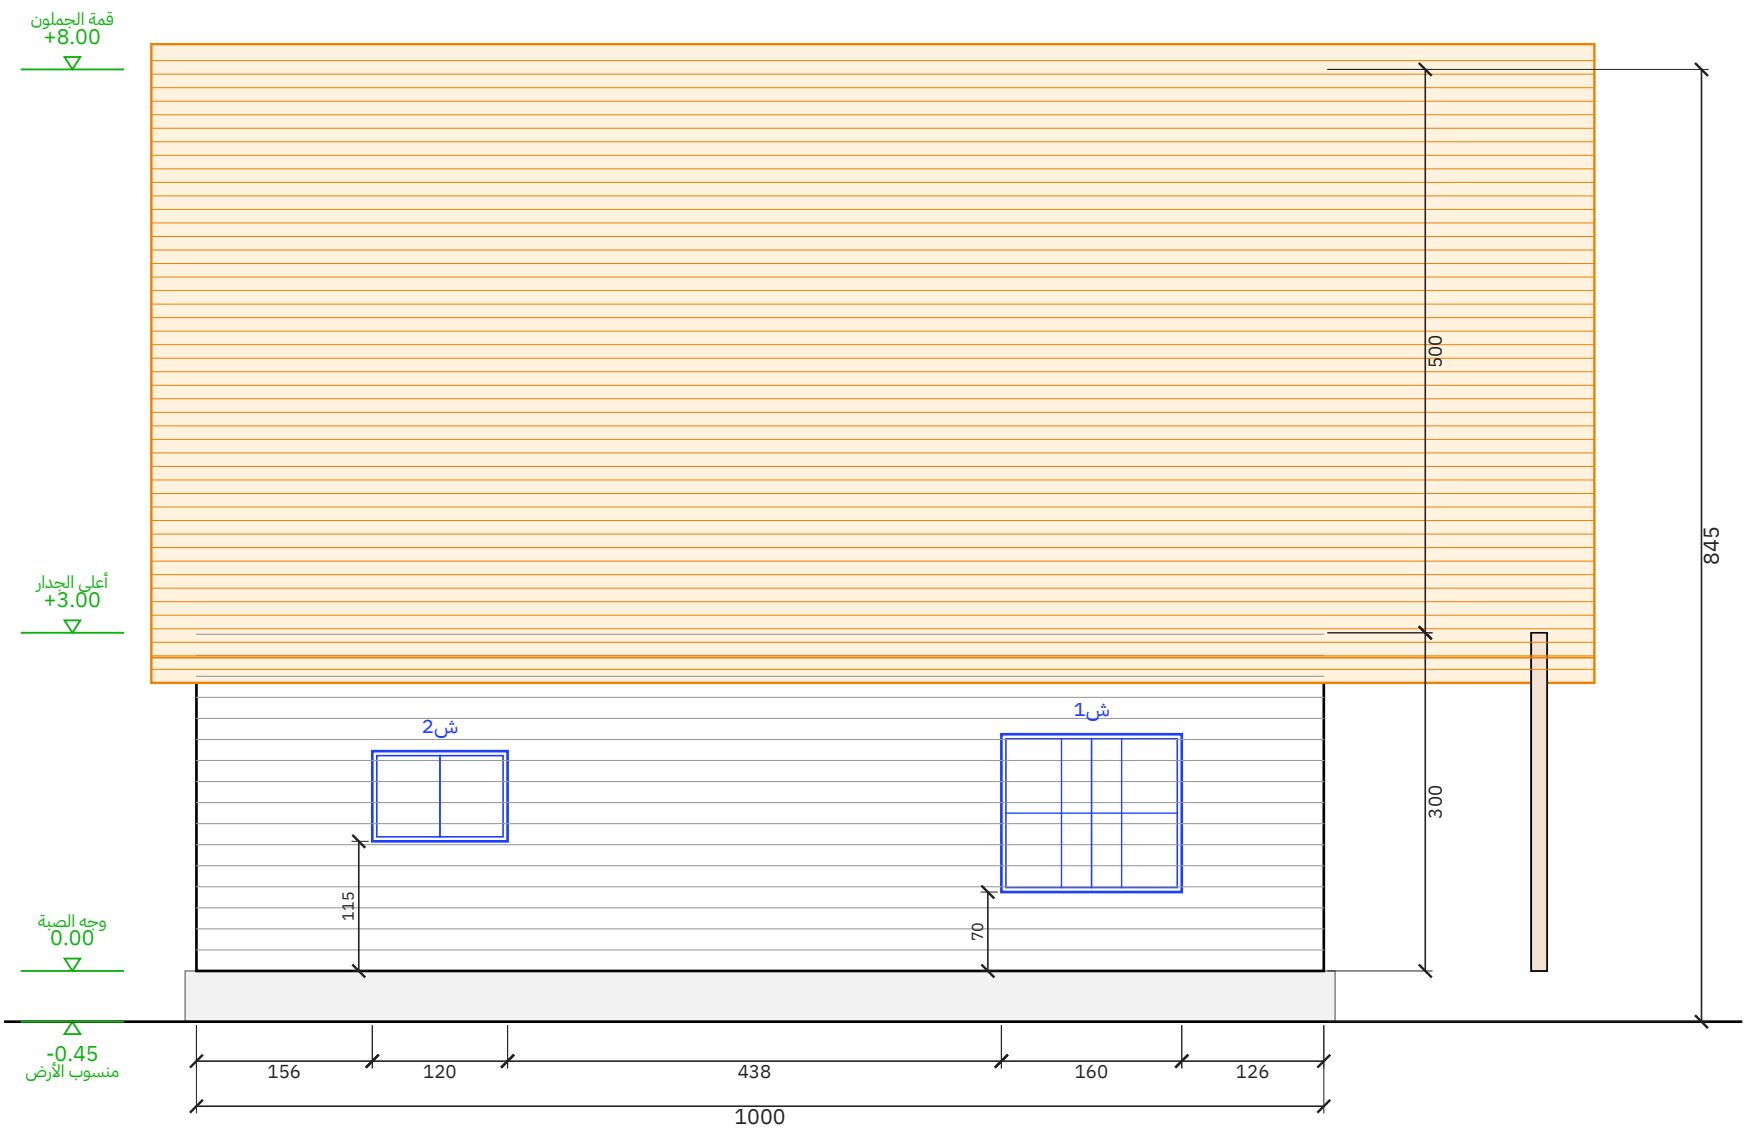

الواجهة الغربية


مقياس 1:50 | الوحدة: سم

المشروع / العميل	عنوان اللوحة	المقياس	التاريخ	رقم اللوحة
نوع A-frame دورين — صالة ومطبخ أمريكي وحمامين + غرفتين وحمام — 9.00 × 10.00 م عميل — A-frame دورين	الواجهة الخلفية والواجهة الغربية	1:50	2026-10-24	W-04 (4/13)

مصنع وتد الأخشاب
Watad Wood Factory


مسقط السقف (جملون)

رفرف 40 سم من كل جهة | مقياس 1:50

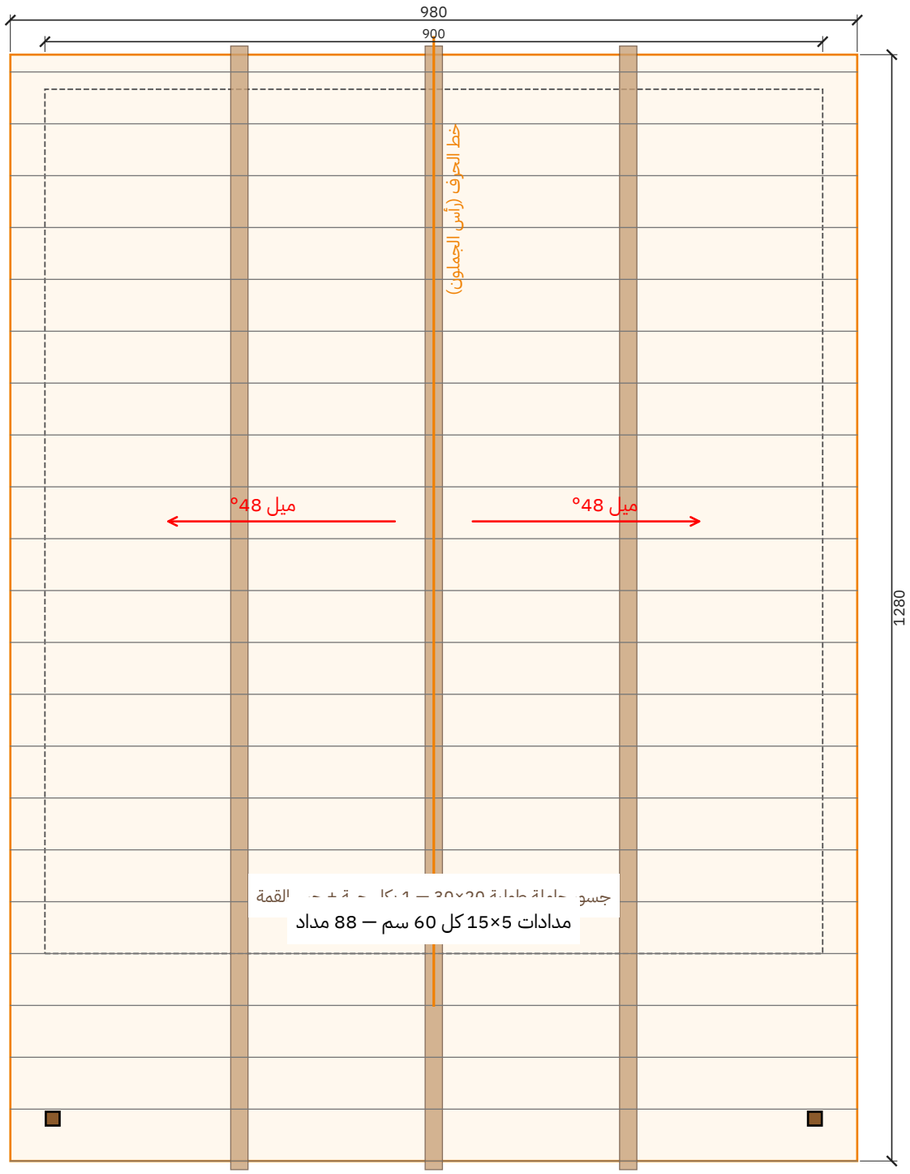


قطاع عرضي أ-أ

مقياس 1:50 | الوحدة: سم

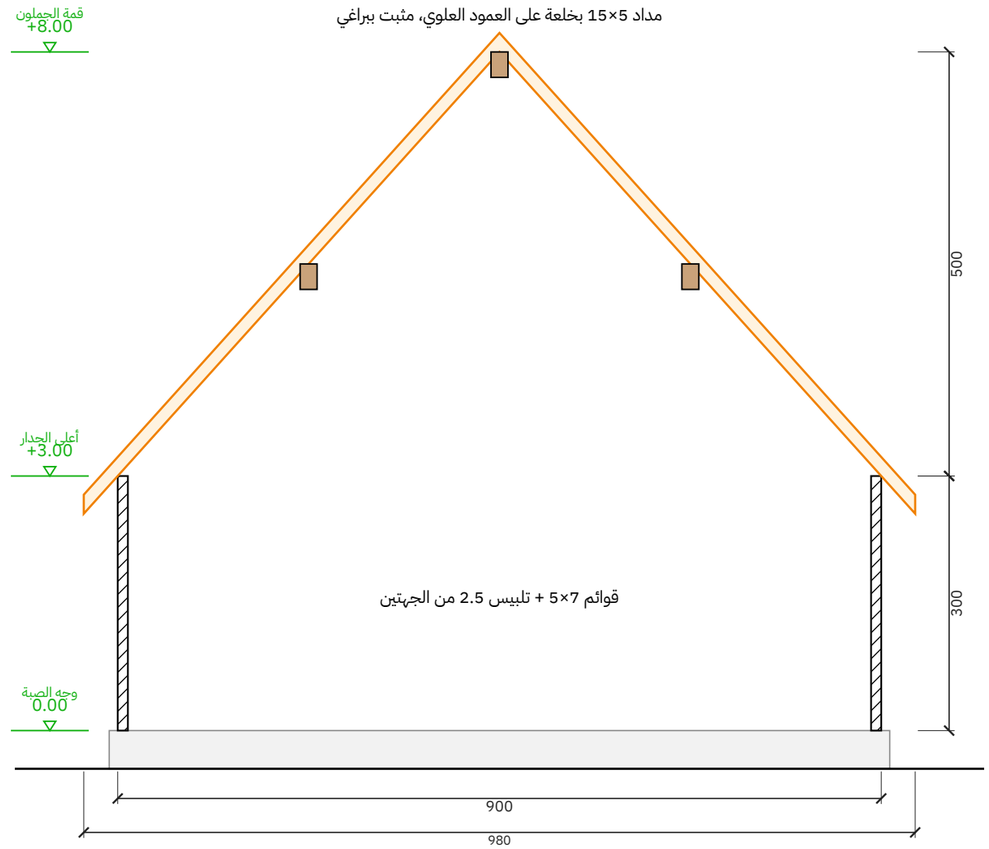

تفصيلة جلوس المداد على العلوي (1:5)

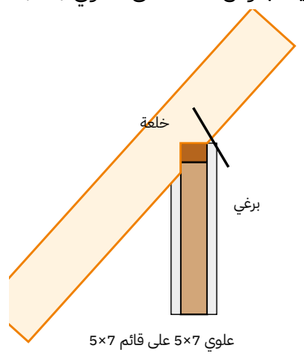

المشروع / العميل كوخ A-frame دورين — صالة ومطبخ أمريكي وحمامين + غرفتين وحمام — 9.00 × 10.00 م عميل — A-frame دورين	عنوان اللوحة مسقط السقف والقطاع	المقياس 1:50	التاريخ 2026-10-24	رقم اللوحة W-05 (5/13)

مصنع وتد الأخشاب
Watad Wood Factory

جدول مقاسات الأبواب والشبابيك

مقاس الفتحة الصافي في الجدار - الوحدة: سم

الرمز	النوع	العرض (سم)	الارتفاع (سم)	ارتفاع الجلسة (سم)	العدد	الموقع
ب1	باب مزدوج	144	230	-	1	الأمامية (زجاج كامل)
ب2	باب	80	220	-	1	الخلفية
ب3	باب	70	210	-	2	حمام 1 - حمام 2
ش4	باب	140	120	-	1	الخلفية
ف1	باب	90	220	-	1	فتحة الممر
ز1	شباك	190	220	5	2	الأمامية (زجاج كامل) 2
ز1	شباك	160	220	5	2	الأمامية (زجاج كامل) 2
ش1	شباك	160	140	70	2	الشرقية - الغربية
ش2	شباك	120	80	115	2	الخلفية - الغربية
ش3	شباك	60	60	170	2	الشرقية 2

الإجمالي: أبواب 6 - شبابيك 10

جدول المساحات وبيانات المشروع


بيانات المشروع

البند	البيان
المشروع	كوخ A-frame دورين — صالة ومطبخ أمريكي وحمامين + غرفتين وحمام — 9.00 × 10.00 م
العميل	عميل — A-frame دورين
الموقع	—
الاستخدام	سكن / استراحة
التاريخ	2026-10-24
نظام البناء	هيكل خشب 5×7 + تلبيس 2.5 سم من الجهتين
السقف	جملون 48° — قرميد معدني


جدول المساحات

م	الفراغ	الأبعاد (م)	المساحة (م2)
1	الصالة	4.66 × 8.76	40.82
2	المطبخ الأمريكي	4.34 × 5.04	21.87
3	ممر	1.08 × 4.98	5.38
4	حمام 1	2.40 × 3.10	7.44
5	حمام 2	2.46 × 3.10	7.63
	المساحة الصافية الداخلية		**83.14**
	التراس المسقوف	**2.00 × 9.00**	**18.00**
	المساحة الإجمالية المبنية	**10.00 × 9.00**	**90.00**
	المساحة الكلية (المبنية + التراس)		**108.00**

تأطير جدار جنوب — الطول 888 سم، الارتفاع 300 سم

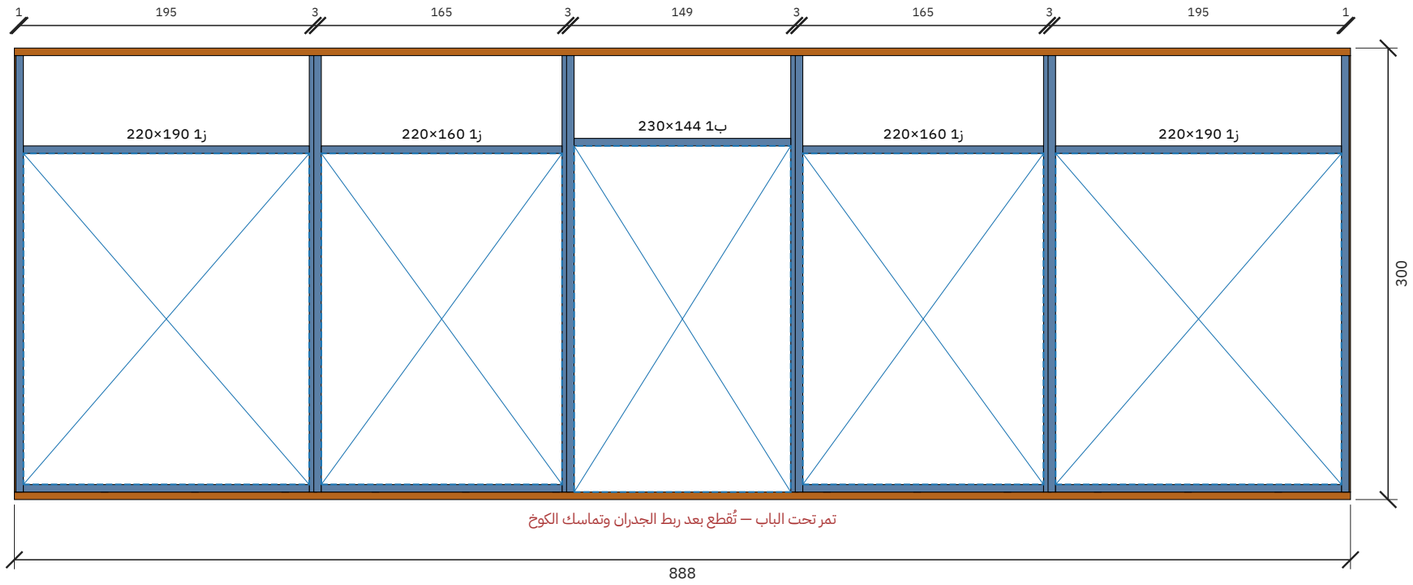

تأطير جدار شرق — الطول 988 سم، الارتفاع 300 سم

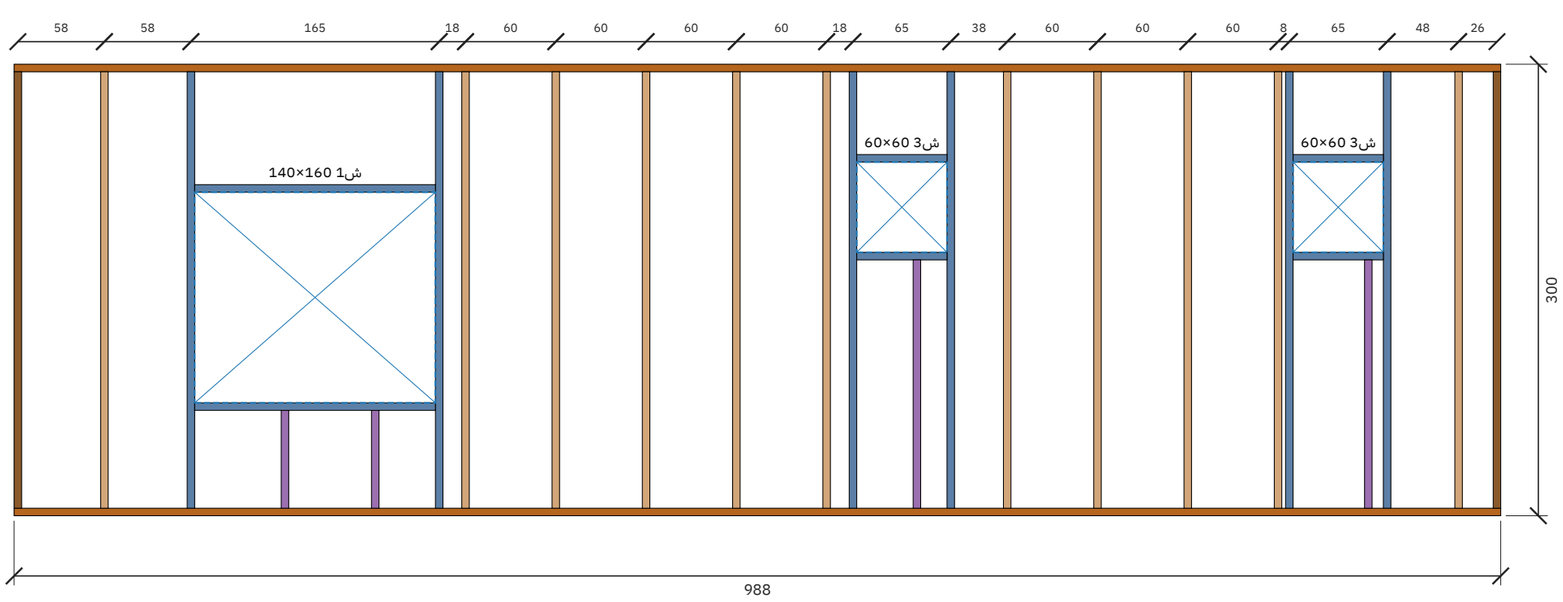


قاعدة سفلية | علوي | عمود | عمود زاوية | جنب فتحة | رأس فتحة | جلسة شباك | عمود قصير


المشروع / العميل	عنوان اللوحة	المقياس	التاريخ	رقم اللوحة
كوخ A-frame دورين – صالة ومطبخ أمريكي وحمامين + غرفتين وحمام – 9.00 × 10.00 م عميل – A-frame دورين	لوحات التأطير (للورشة)	–	2026-10-24	W-08 (8/13)

مصنع وتد الأخشاب
Watad Wood Factory

تأطير جدار شمال — الطول 888 سم، الارتفاع 300 سم

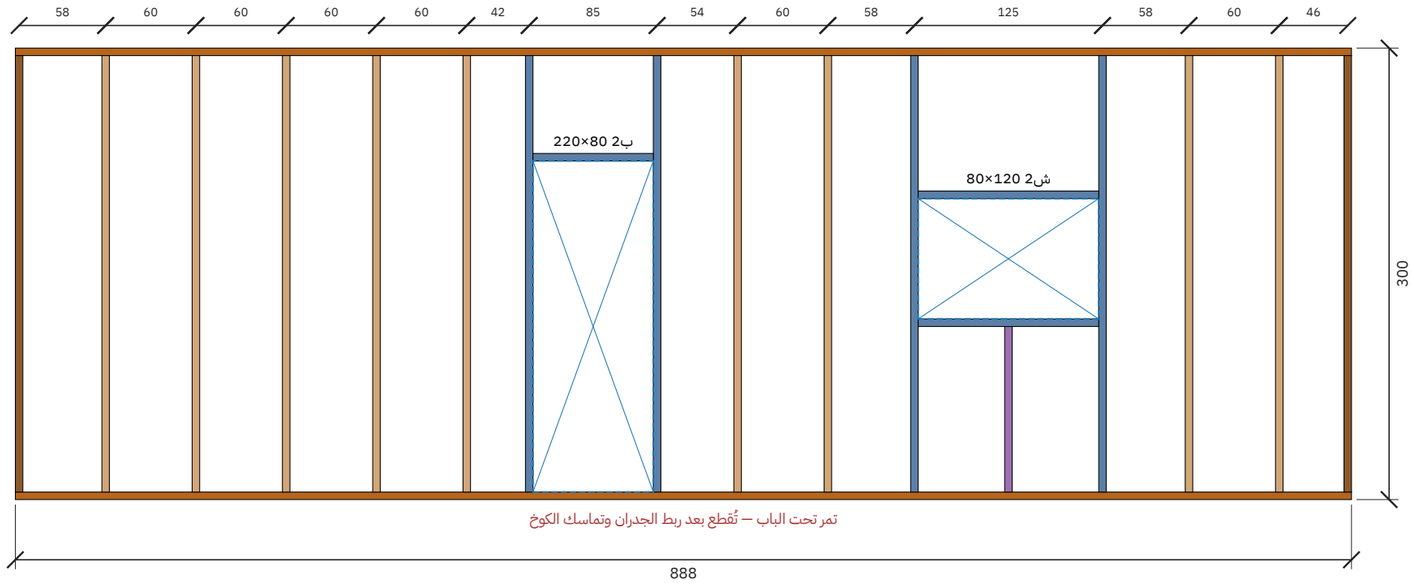

تأطير جدار غرب — الطول 988 سم، الارتفاع 300 سم

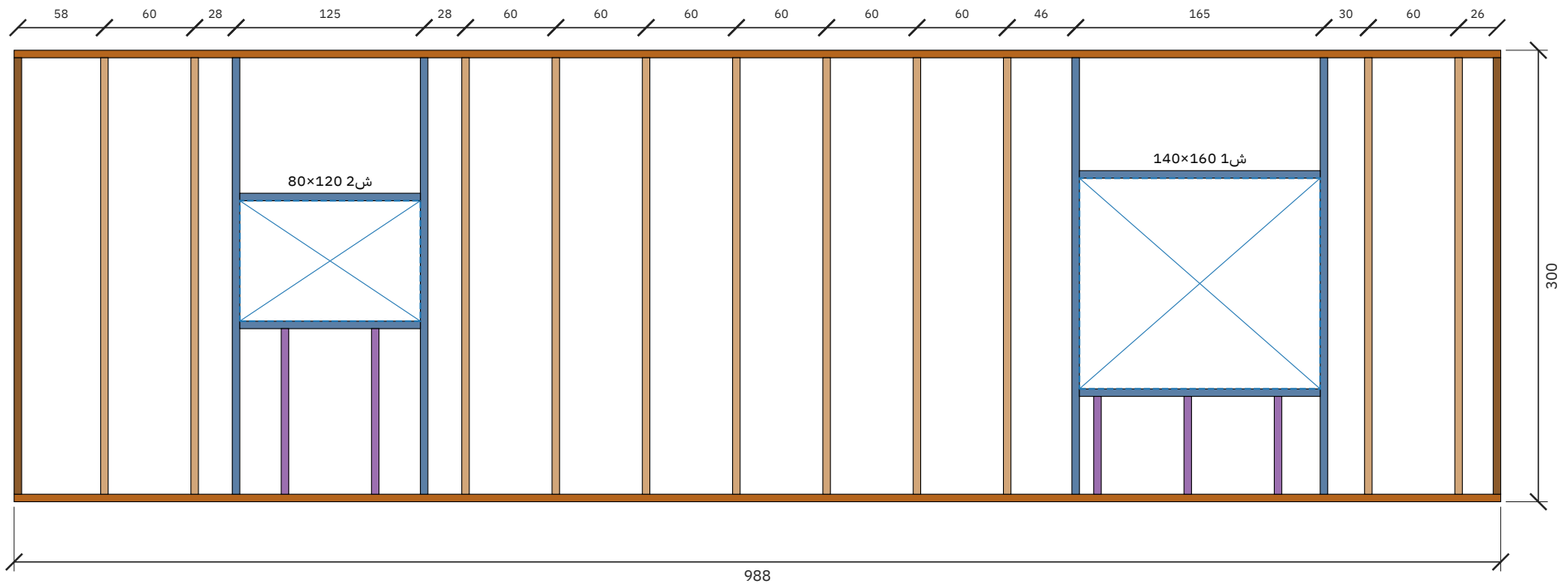


قاعدة سفلية | علوي | عمود | عمود زاوية | جنب فتحة | رأس فتحة | جلسة شباك | عمود قصير


المشروع / العميل	عنوان اللوحة	المقياس	التاريخ	رقم اللوحة
كوخ A-frame دورين – صالة ومطبخ أمريكي وحمامين + غرفتين وحمام – 9.00 × 10.00 م عميل – A-frame دورين	لوحات التأطير (للورشة)	–	2026-10-24	W-09 (9/13)

مصنع وتد الأخشاب
Watad Wood Factory

تأطير جدار جدار خلف الدرج — الطول 442 سم، الارتفاع 300 سم (داخلي)

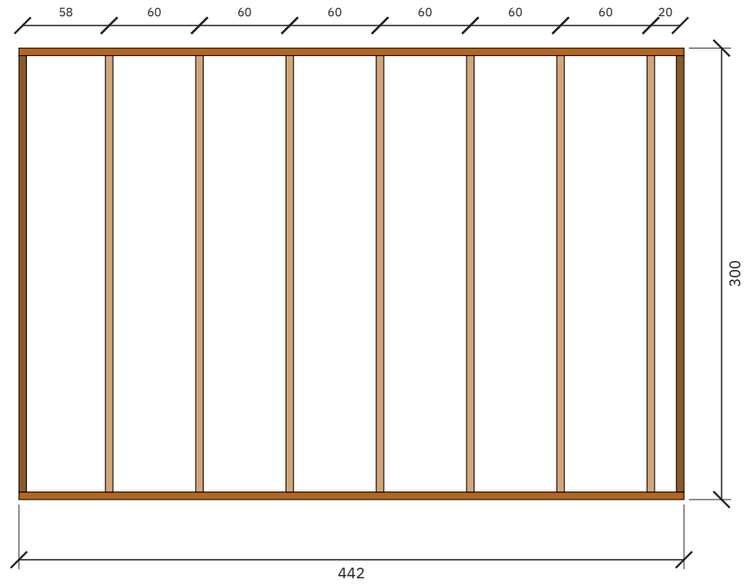


تأطير جدار جدار المطبخ — الممر — الطول 510 سم، الارتفاع 300 سم (داخلي)

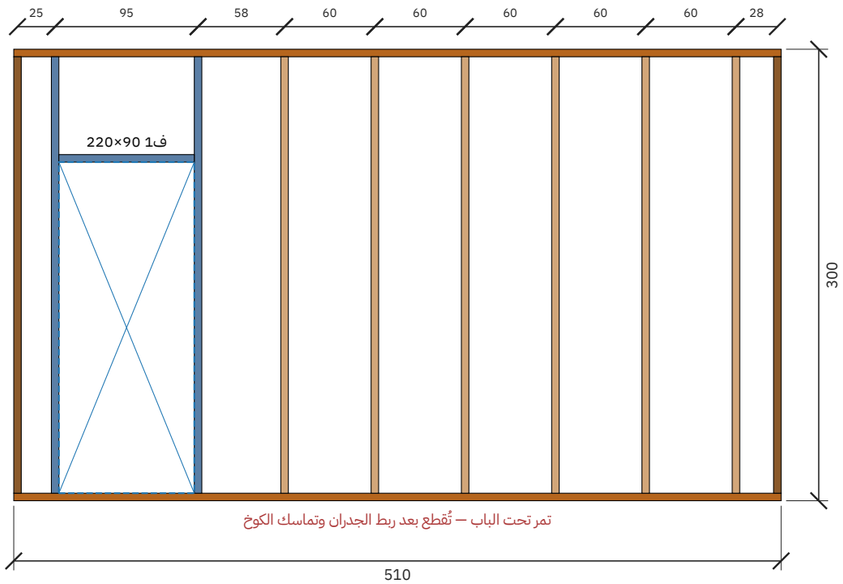


قاعدة سفلية | علوي | عمود | عمود زاوية | جنب فتحة | رأس فتحة | جلسة شباك | عمود قصير

مصنع وتد الأخشاب Watad Wood Factory	المشروع / العميل **كوخ A-frame دورين — صالة ومطبخ أمريكي وحمامين + غرفتين وحمام — 9.00 × 10.00 م** **عميل — A-frame دورين**	عنوان اللوحة **لوحات التأطير (للورشة)**	المقياس **—**	التاريخ **2026-10-24**	رقم اللوحة **W-10 (10/13)**

تأطير جدار جدار الحمامات — الطول 510 سم، الارتفاع 300 سم (داخلي)

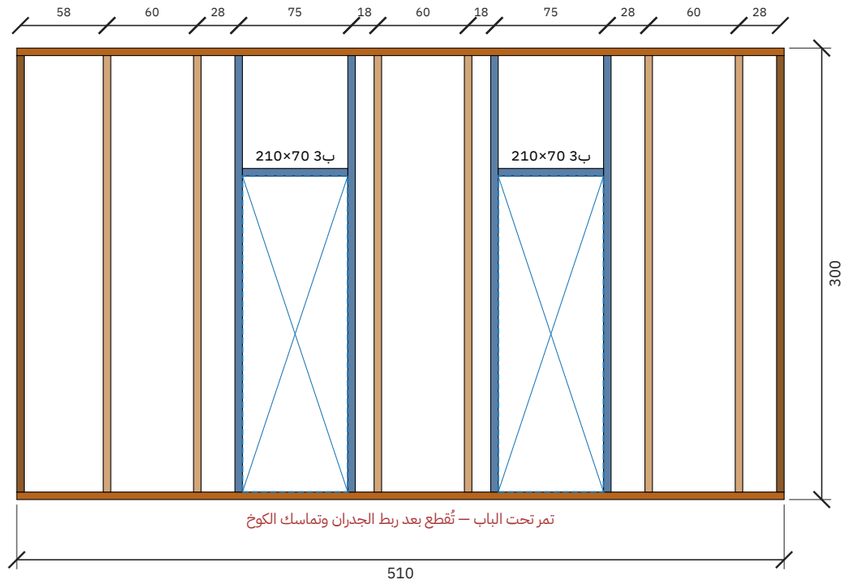

تأطير جدار فاصل الحمامين — الطول 322 سم، الارتفاع 300 سم (داخلي)

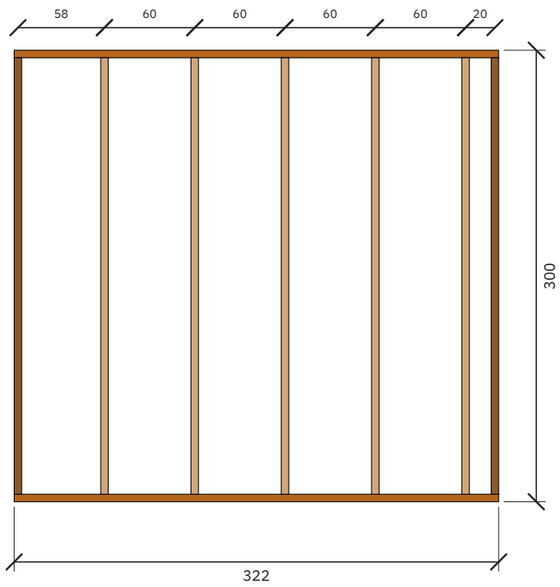

قاعدة سفلية | علوي | عمود | عمود زاوية | جنب فتحة | رأس فتحة | جلسة شباك | عمود قصير

مصنع وتد الأخشاب Watad Wood Factory	المشروع / العميل **كوخ A-frame دورين — صالة ومطبخ أمريكي وحمامين + غرفتين وحمام — 9.00 × 10.00 م** **عميل — A-frame دورين**	عنوان اللوحة **لوحات التأطير (للورشة)**	المقياس **—**	التاريخ **2026-10-24**	رقم اللوحة **W-11 (11/13)**

جدول الكميات وخطة تقطيع الطبليات

البند	القيمة
الارتفاع المطلوب / المعتمد	300 / 300 سم
السقف	جملون 48° — أعلى نقطة 800 سم من وجه الصبة
المدادات 5×15	88 مداد (22 خط × قطعتين موصولة فوق الجسر الحامل بتراكب 60 سم) × حتى 441 سم — من طبلية 480
طبليات الطريقة الأولى (مداد + عمود)	88 طبلية × 480 سم
طبليات الطريقة الثانية (3 أعمدة)	17 طبلية × 320 سم
إجمالي الطبليات 5×22.5	105
إجمالي قطع 5×7	164
قائمة تقطيع 5×7	988سم×4 | 888سم×4 | 510سم×4 | 442سم×2 | 322سم×2 | 290سم×101 | 190سم×4 | 165سم×2 | 160سم×8
	144سم×1 | 120سم×4 | 110سم×3 | 90سم×1 | 80سم×1 | 70سم×2 | 65سم×5 | 60سم×4 | 5سم×12
ألواح تلبيس 2.5 سم	330 لوح × 400 سم (مجموع الصفوف 1145.8 م، 16 وجه)
أسمنت بورد 12 مم (122×244)	44 لوح (داخل دورات المياه)
العزل	186 لوح فوم صخري 80
الصبة	يجهزها العميل — 20 سم، مفرغة تحت دورات المياه

مراجعة التصميم مقابل قواعد المصنع

النوع	البند	التفاصيل	المقترح
ملاحظة	بحر المدادات	أطول بحر بدون جدار داخلي يحمل المداد: جهة أ: 450 سم، جهة ب: 450 سم. يحتاج رقم المصنع لأقصى بحر مسموح لتحديد المدادات اللي تُقوّى 20×5.	
ملاحظة	الصبة والدرج	ارتفاع الصبة 45 سم ← 3 درجة بقائمة 15.0 سم.	
ملاحظة	مناسيب رؤوس الفتحات	رؤوس الأبواب والشبابيك على مناسيب مختلفة: 195، 210، 220، 225، 230 سم.	
سؤال	يحتاج تأكيد	أقصى بحر للمداد بدون جدار داخلي قبل إضافة تقوية 7×5 (مداد 20×5)؟	
سؤال	يحتاج تأكيد	التغطية الصافية للوح التلبيس بعد التعشيق (مستنتجة مؤقتاً 18.67 سم من 280/15)؟	
سؤال	يحتاج تأكيد	هل يوضع أعمدة قصيرة فوق رأس الشباك/الباب إلى العلوي؟	
سؤال	يحتاج تأكيد	مكان الوصلة في القاعدة والعلوي إذا الجدار أطول من الطبلية؟	