
المسقط الأفقي مع الفرش

الأبعاد بالسنتيمتر - الجدران: قوائم 7×5 + تلبيس 2.5 من الجهتين (12 سم)

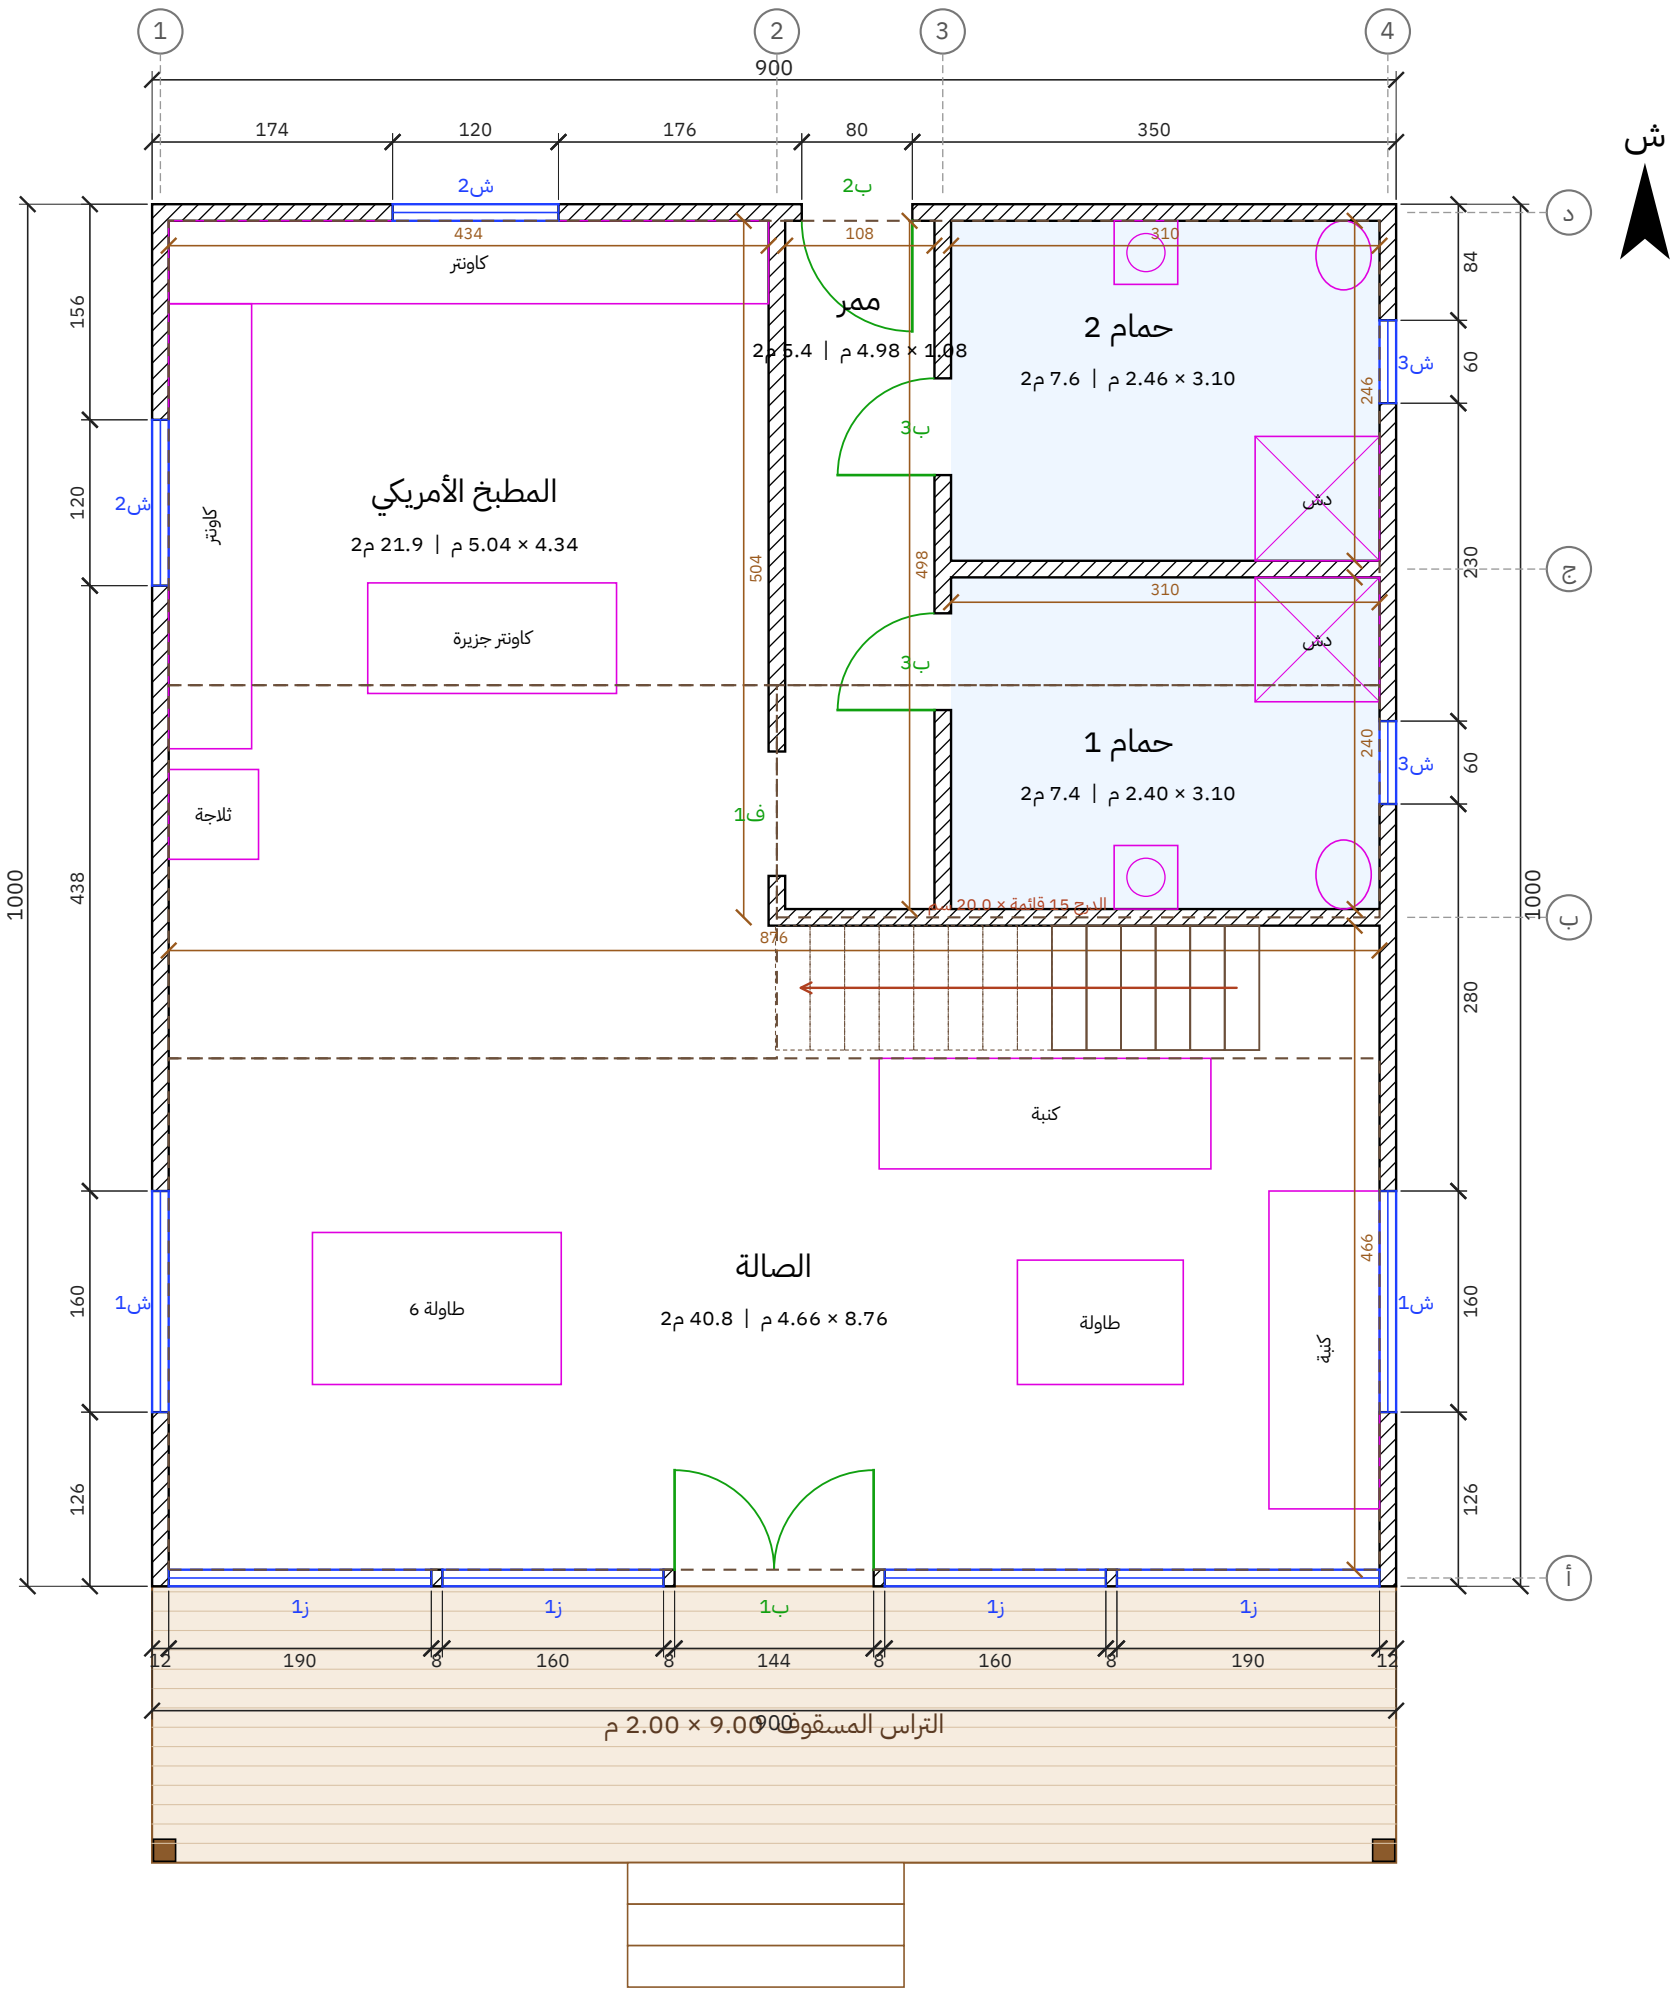


المشروع / العميل	عنوان اللوحة	المقياس	التاريخ	رقم اللوحة
كوخ A-frame دورين — صالة ومطبخ أمريكي وحمامين + غرفتين وحمام — 9.00 × 10.00 م عميل — A-frame دورين	المسقط الأفقي	1:50	2026-10-24	A-01 (1/10)


مصنع وتد الأخشاب
Watad Wood Factory

المسقط الأفقي مع الفرش — الدور الأول (داخل المثلث)

منسوب الأرضية +3.00 | الأبعاد بالسنتيمتر | الوقفة الكاملة ≥ 2.10 م بين الخطين المتقطعين

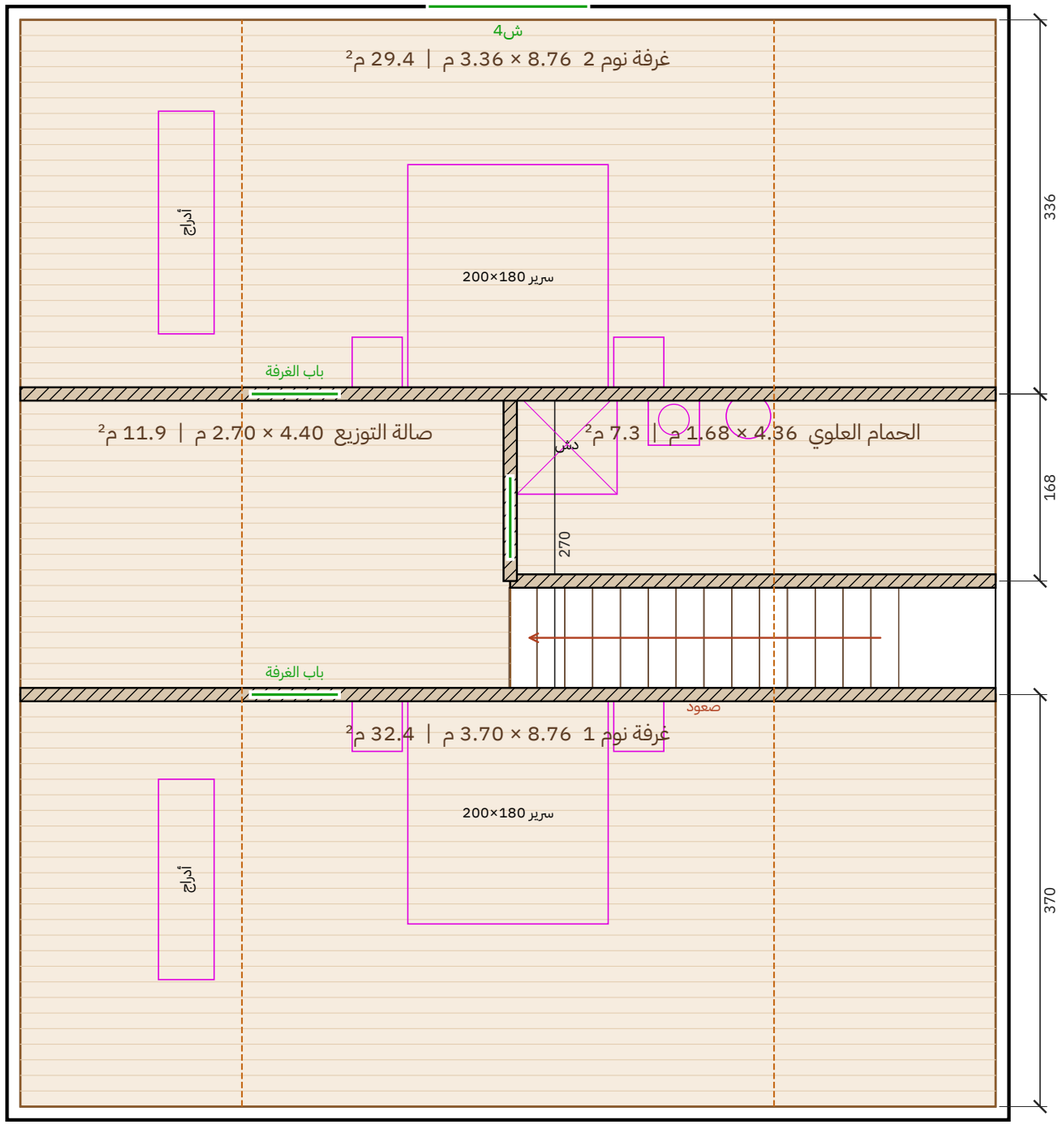


مصنع وتد الأخشاب Watad Wood Factory	المشروع / العميل **كوخ A-frame دورين — صالة ومطبخ أمريكي وحمامين + غرفتين وحمام — 9.00 × 10.00 م** **عميل — A-frame دورين**	عنوان اللوحة **المسقط الأفقي مع الفرش — الدور الأول (داخل المثلث)**	المقياس **1:50**	التاريخ **2026-10-24**	رقم اللوحة **A-02 (2/10)**

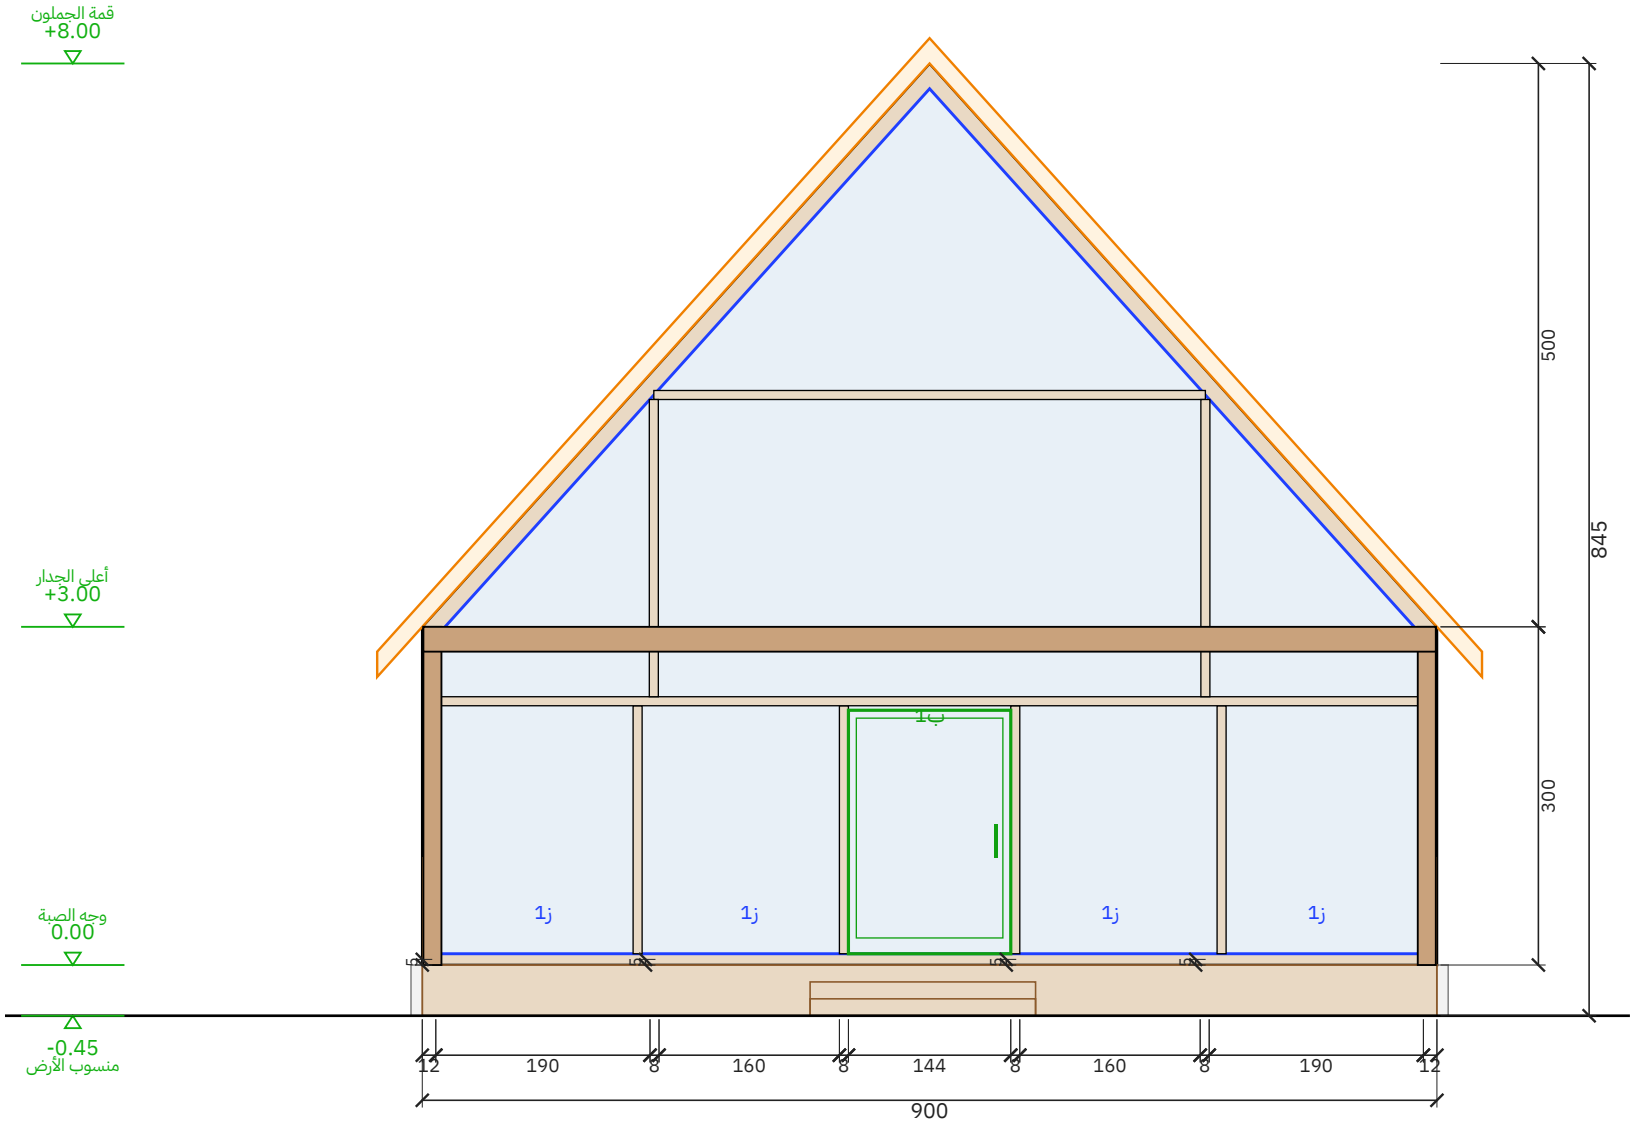

الواجهة الأمامية (زجاج كامل)

مقياس 1:50 | الوحدة: سم

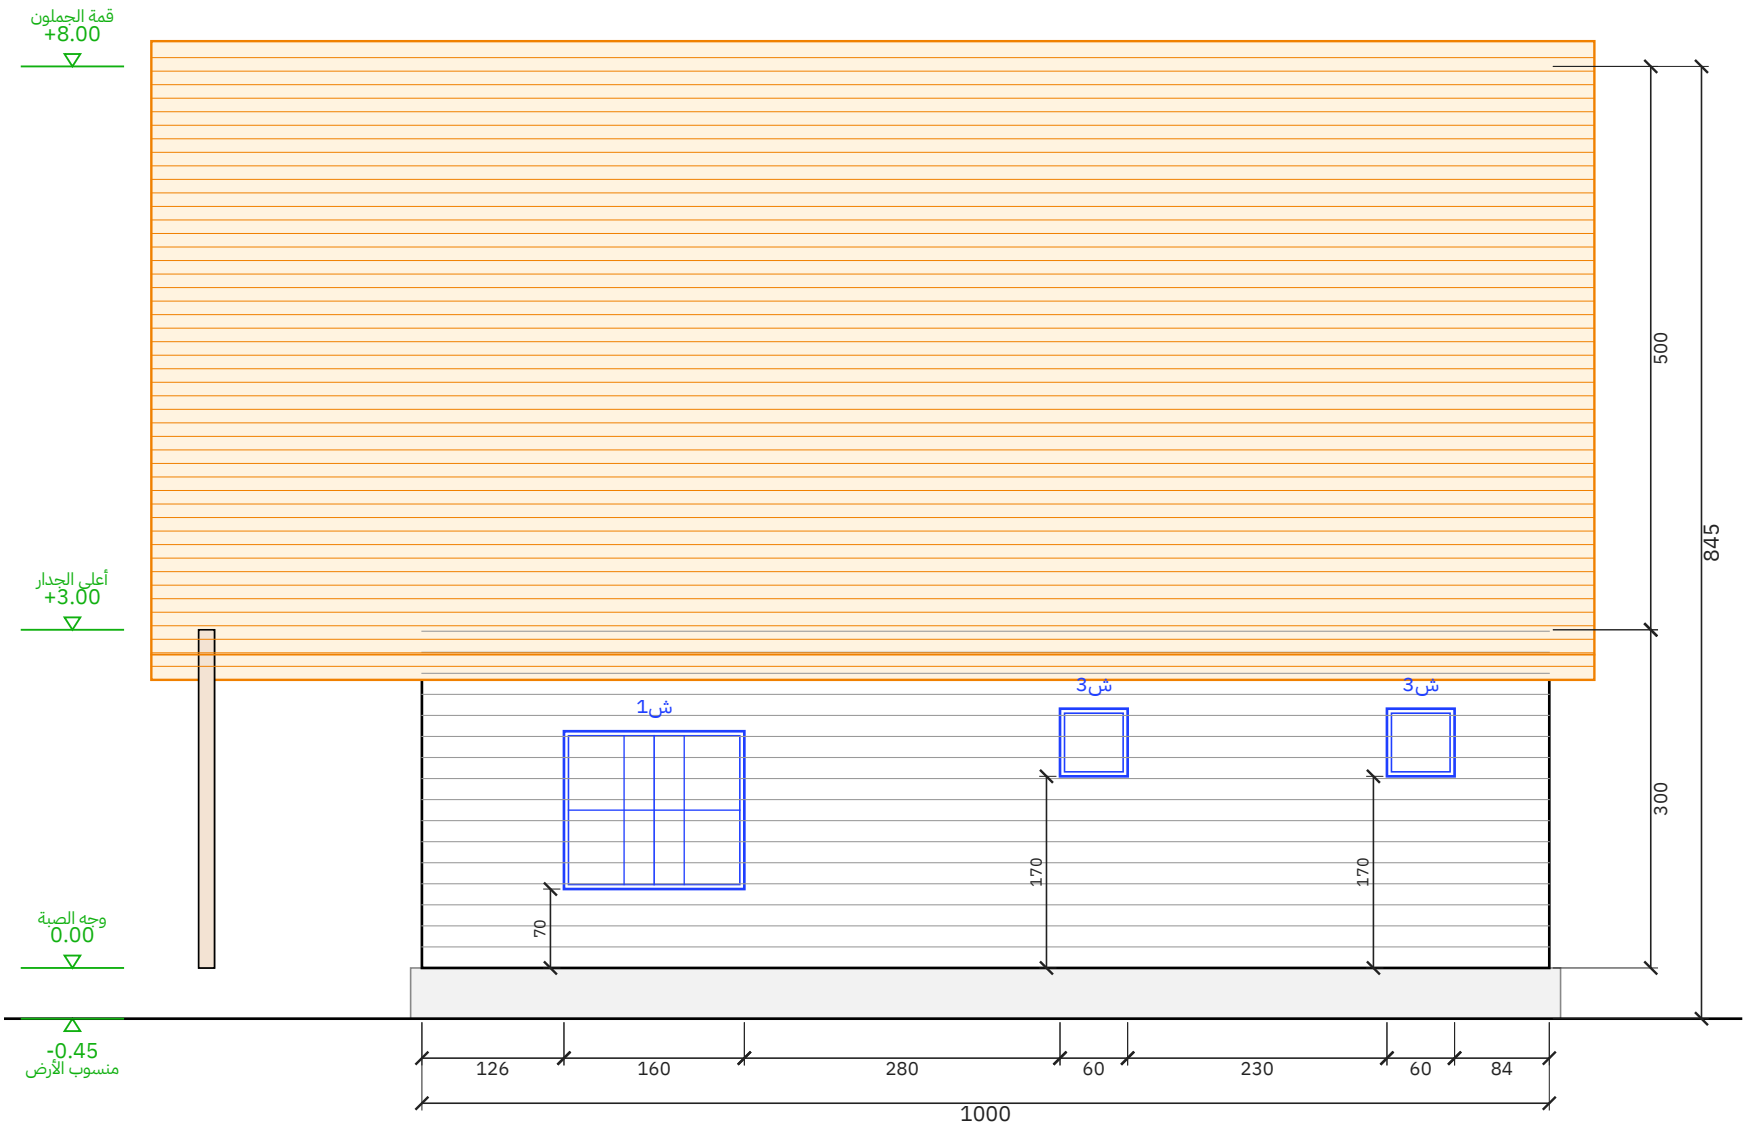


الواجهة الشرقية

مقياس 1:50 | الوحدة: سم


المشروع / العميل	عنوان اللوحة	المقياس	التاريخ	رقم اللوحة
نوع A-frame دورين — صالة ومطبخ أمريكي وحمامين + غرفتين وحمام — 9.00 × 10.00 م عميل — A-frame دورين	الواجهة الأمامية (زجاج كامل) والواجهة الشرقية	1:50	2026-10-24	A-03 (3/10)

مصنع وتد الأخشاب
Watad Wood Factory

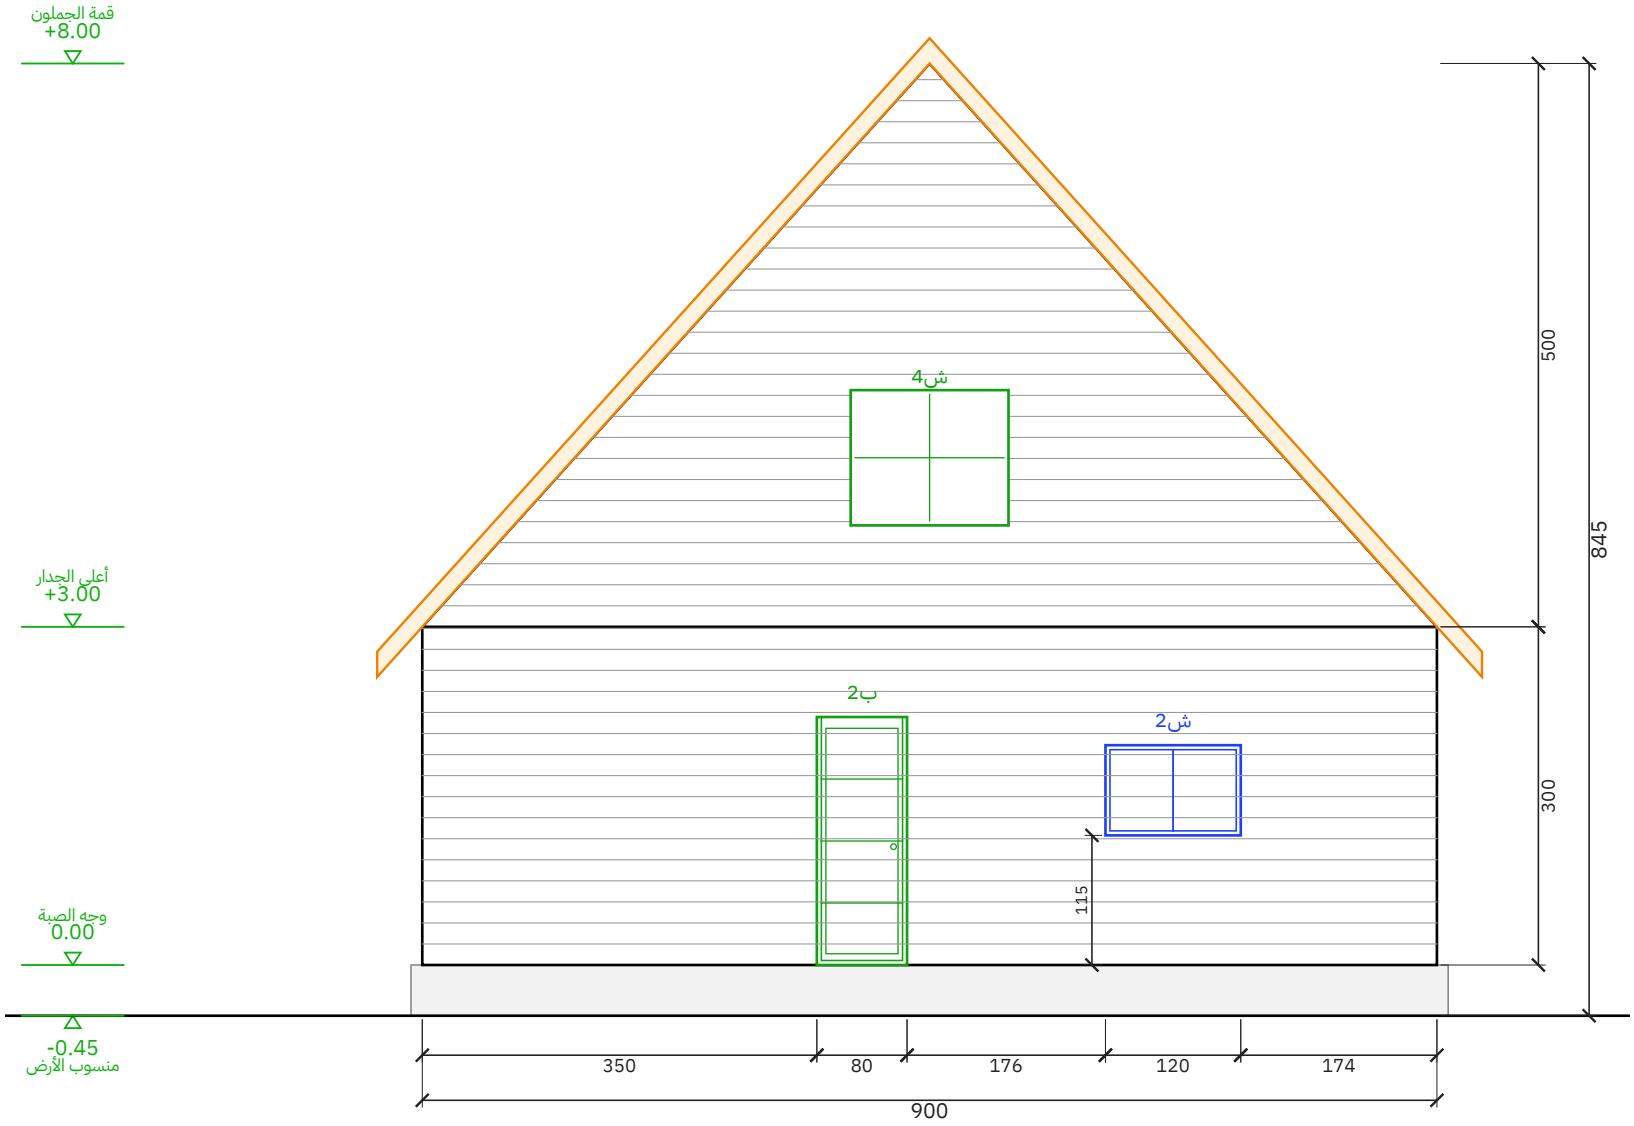

الواجهة الخلفية

مقياس 1:50 | الوحدة: سم

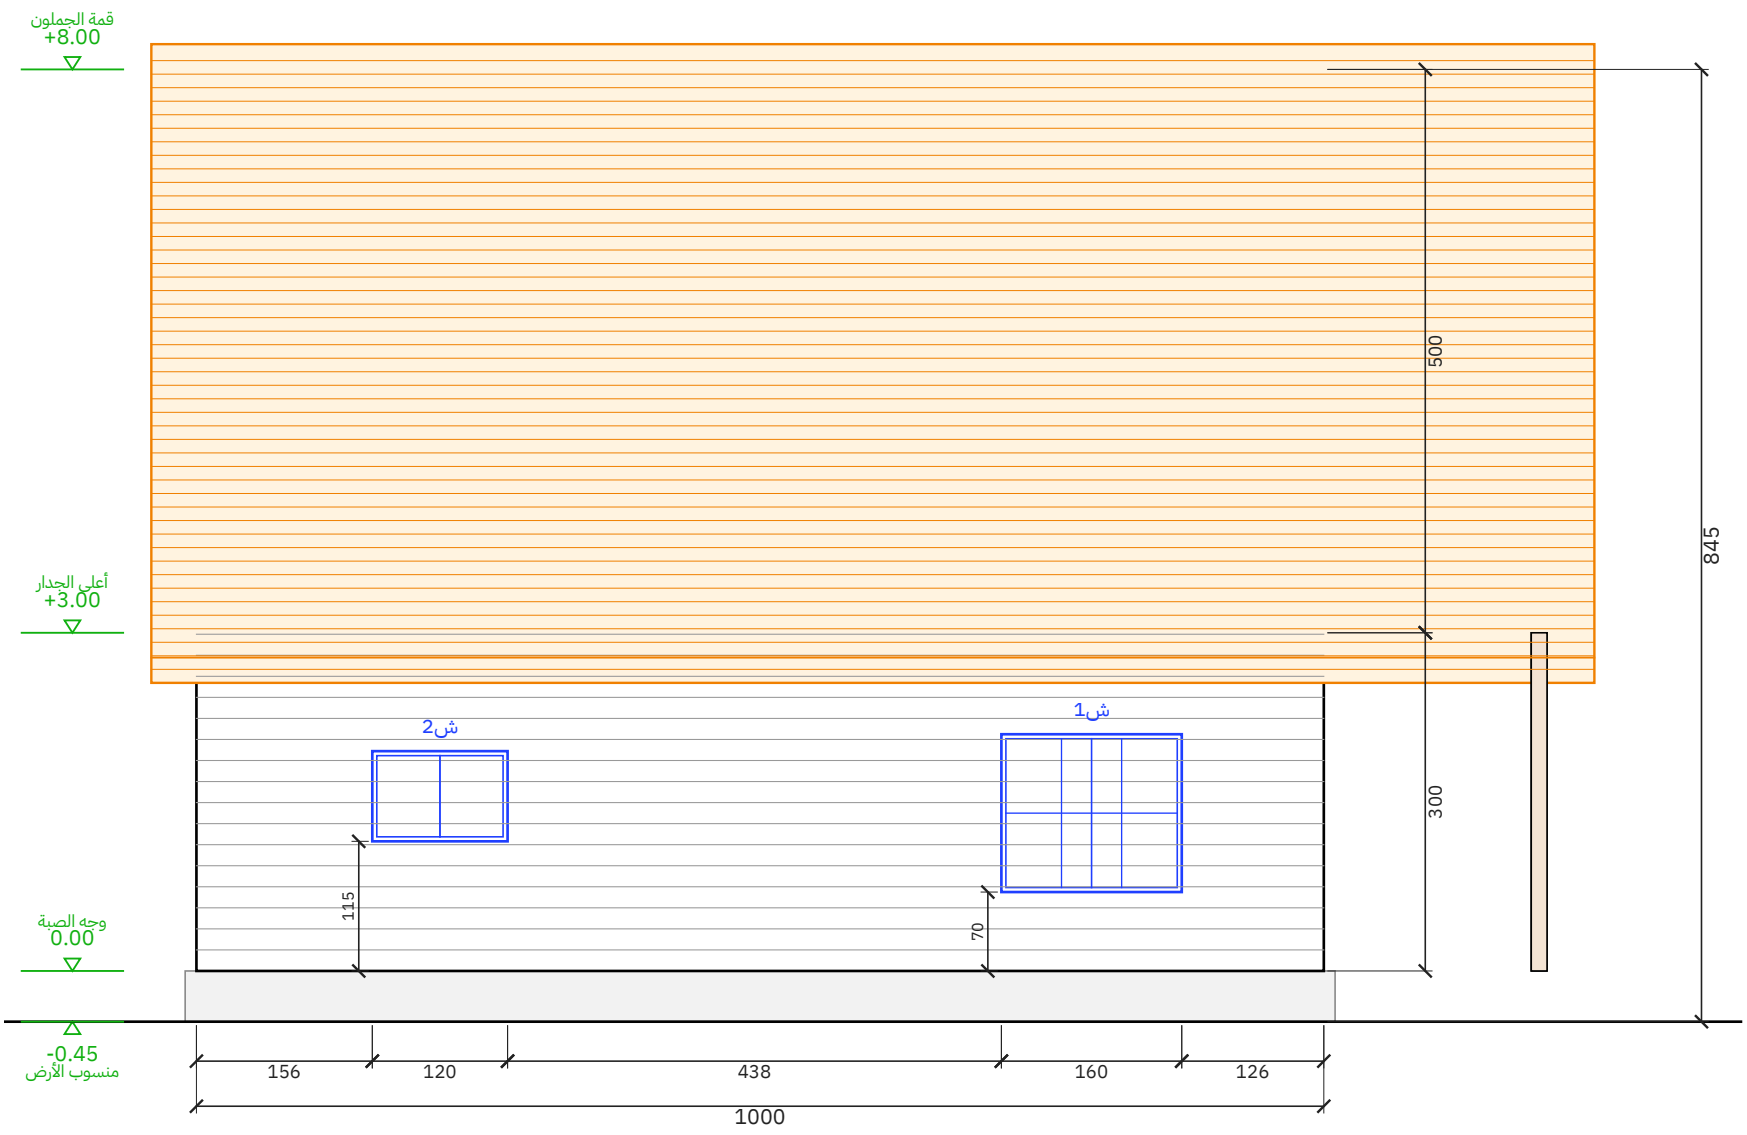

الواجهة الغربية


مقياس 1:50 | الوحدة: سم

المشروع / العميل	عنوان اللوحة	المقياس	التاريخ	رقم اللوحة
نوع A-frame دورين — صالة ومطبخ أمريكي وحمامين + غرفتين وحمام — 9.00 × 10.00 م عميل — A-frame دورين	الواجهة الخلفية والواجهة الغربية	1:50	2026-10-24	A-04 (4/10)

مصنع وتد الأخشاب
Watad Wood Factory


مسقط السقف (جملون)

رفرف 40 سم من كل جهة | مقياس 1:50

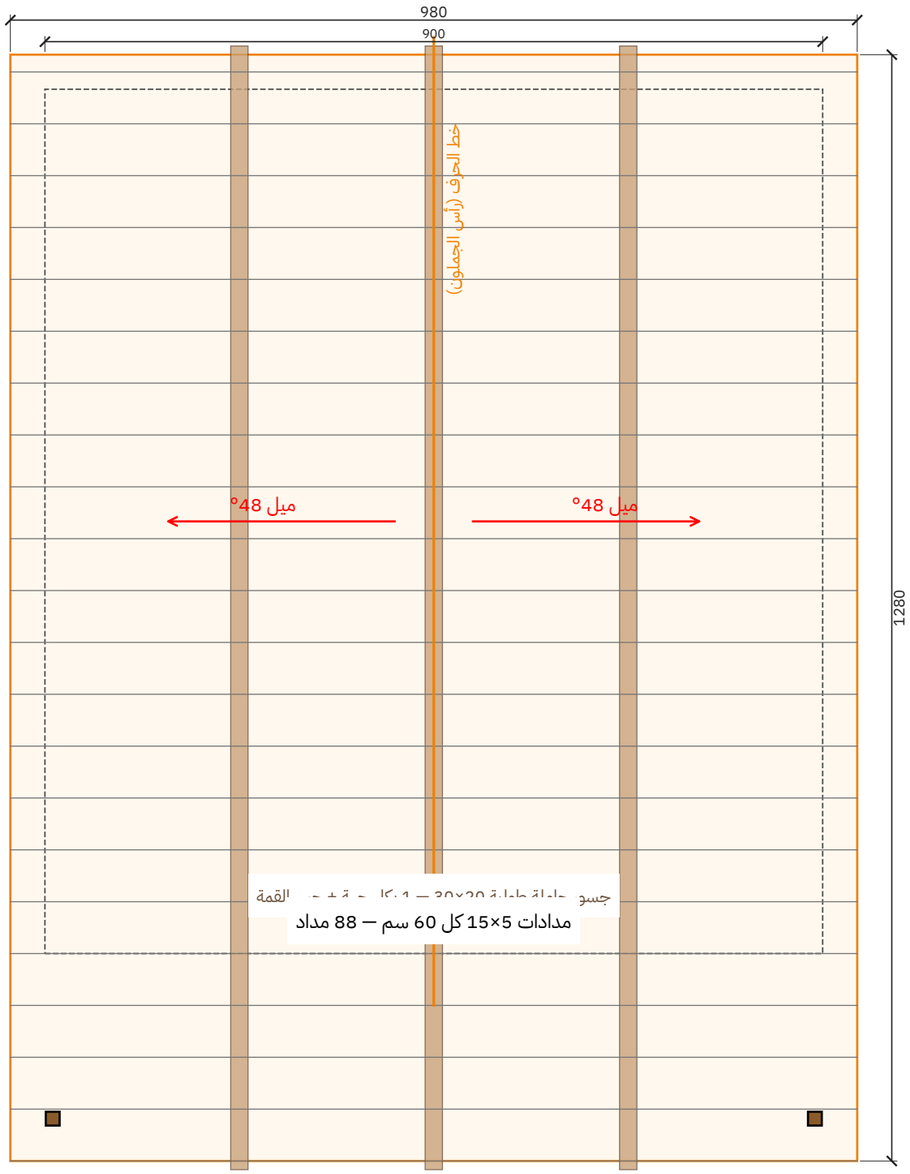


قطاع عرضي أ-أ

مقياس 1:50 | الوحدة: سم

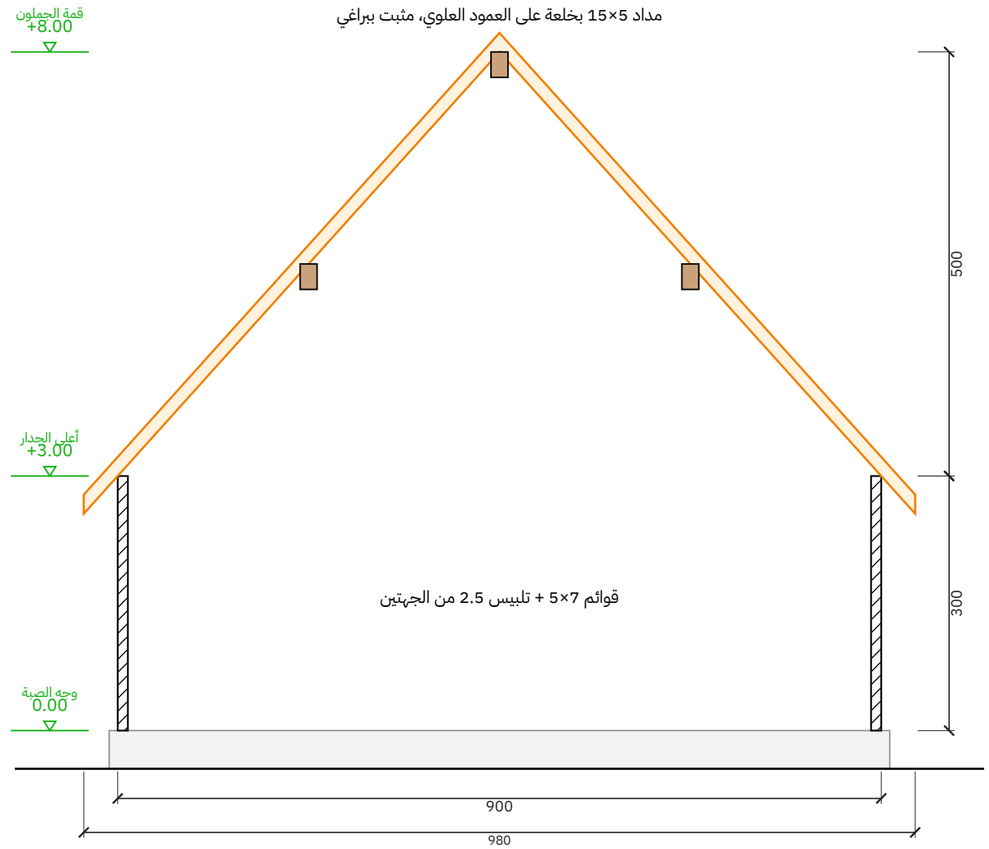

تفصيلة جلوس المداد على العلوي (1:5)

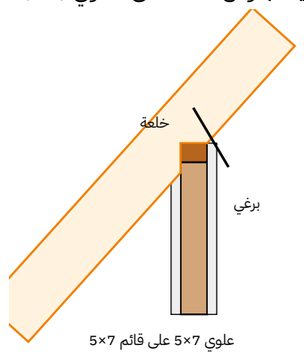

المشروع / العميل **كوخ A-frame دورين — صالة ومطبخ أمريكي وحمامين + غرفتين وحمام — 9.00 × 10.00 م** **عميل — A-frame دورين**	عنوان اللوحة **مسقط السقف والقطاع**	المقياس **1:50**	التاريخ **2026-10-24**	رقم اللوحة **A-05 (5/10)**

مصنع وتد الأخشاب
Watad Wood Factory

جدول مقاسات الأبواب والشبابيك

مقاس الفتحة الصافي في الجدار - الوحدة: سم

الرمز	النوع	العرض (سم)	الارتفاع (سم)	ارتفاع الجلسة (سم)	العدد	الموقع
ب1	باب مزدوج	144	230	-	1	الأمامية (زجاج كامل)
ب2	باب	80	220	-	1	الخلفية
ب3	باب	70	210	-	2	حمام 1 - حمام 2
ش4	باب	140	120	-	1	الخلفية
ف1	باب	90	220	-	1	فتحة الممر
ز1	شباك	190	220	5	2	الأمامية (زجاج كامل) 2
ز1	شباك	160	220	5	2	الأمامية (زجاج كامل) 2
ش1	شباك	160	140	70	2	الشرقية - الغربية
ش2	شباك	120	80	115	2	الخلفية - الغربية
ش3	شباك	60	60	170	2	الشرقية 2

الإجمالي: أبواب 6 - شبابيك 10

مصنع وتد الأخشاب Watad Wood Factory	المشروع / العميل كوخ A-frame دورين — صالة ومطبخ أمريكي وحمامين + غرفتين وحمام — 9.00 × 10.00 م عميل — A-frame دورين	عنوان اللوحة جدول الأبواب والشبابيك	المقياس —	التاريخ 2026-10-24	رقم اللوحة A-06 (6/10)

جدول المساحات وبيانات المشروع

بيانات المشروع

البند	البيان
المشروع	كوخ A-frame دورين — صالة ومطبخ أمريكي وحمامين + غرفتين وحمام — 9.00 × 10.00 م
العميل	عميل — A-frame دورين
الموقع	—
الاستخدام	سكن / استراحة
التاريخ	2026-10-24
نظام البناء	هيكل خشب 5×7 + تلبيس 2.5 سم من الجهتين
السقف	جملون 48° — قرميد معدني

جدول المساحات

م	الفراغ	الأبعاد (م)	المساحة (م2)
1	الصالة	4.66 × 8.76	40.82
2	المطبخ الأمريكي	4.34 × 5.04	21.87
3	ممر	1.08 × 4.98	5.38
4	حمام 1	2.40 × 3.10	7.44
5	حمام 2	2.46 × 3.10	7.63
	المساحة الصافية الداخلية		**83.14**
	التراس المسقوف	**2.00 × 9.00**	**18.00**
	المساحة الإجمالية المبنية	**10.00 × 9.00**	**90.00**
	المساحة الكلية (المبنية + التراس)		**108.00**

لقطات المنظور الخارجي

المنظور الأمامي




منظور أمامي من اليسار



منظور أمامي من اليمين




المنظور الخلفي

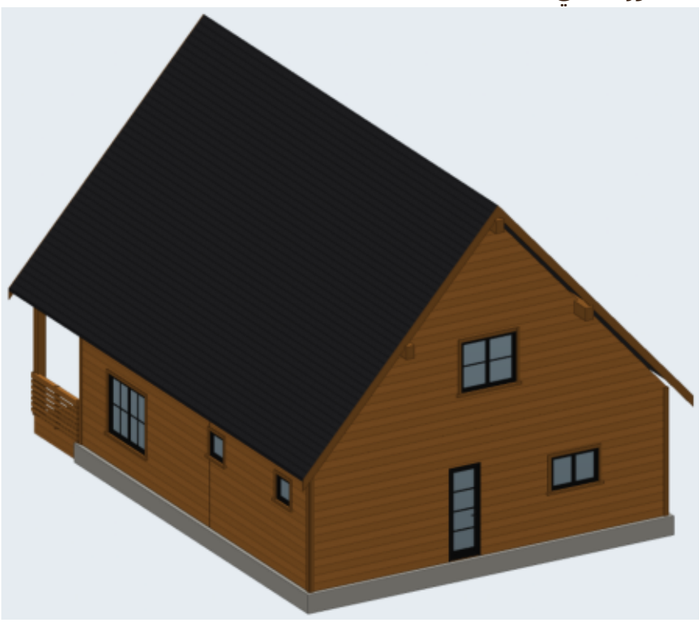

منظور خلفي من اليمين



منظر علوي

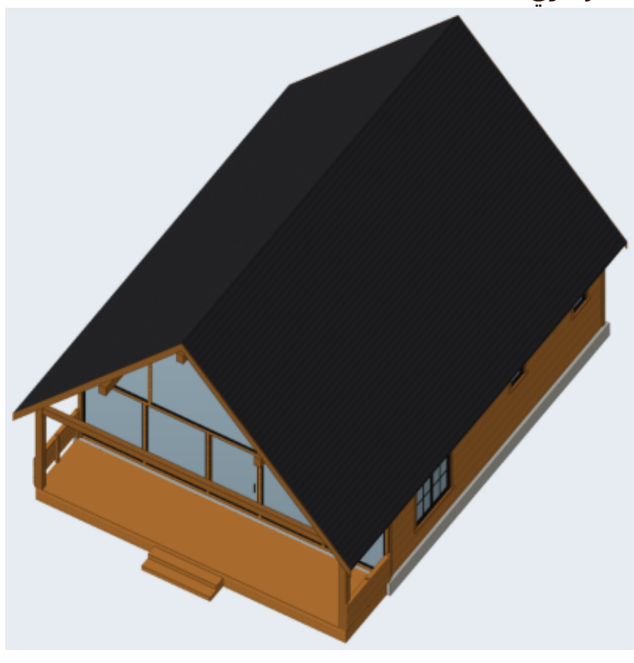


المشروع / العميل	عنوان اللوحة	المقياس	التاريخ	رقم اللوحة
كوخ A-frame دورين — صالة ومطبخ أمريكي وحمامين + غرفتين وحمام — 9.00 × 10.00 م **عميل — A-frame دورين**	**لقطات المنظور**	**—**	**2026-10-24**	**A-08 (8/10)**

مصنع وتد الأخشاب
Watad Wood Factory

المقطع العلوي بالفرش

مقطع أفقي على ارتفاع 1.90 م — توزيع الفرش ومسار الحركة

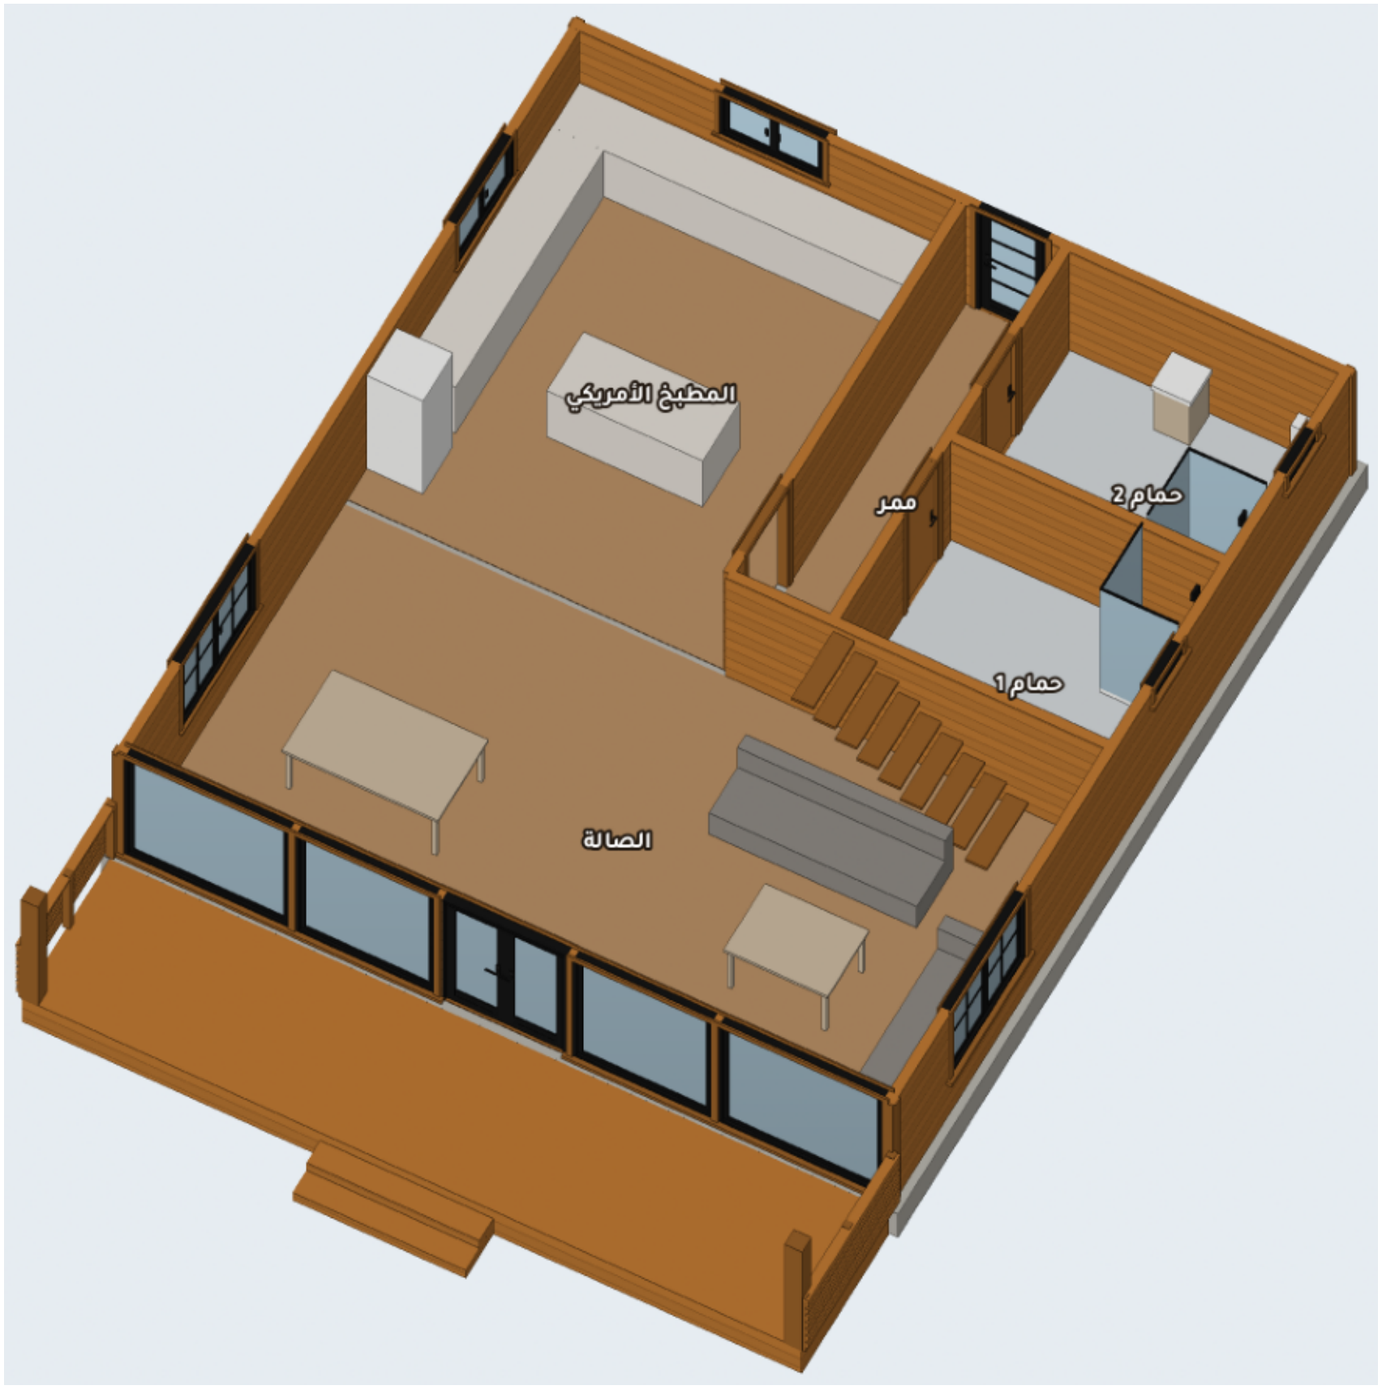


المشروع / العميل	عنوان اللوحة	المقياس	التاريخ	رقم اللوحة
كوخ A-frame دورين — صالة ومطبخ أمريكي وحمامين + غرفتين وحمام — 9.00 × 10.00 م **عميل — A-frame دورين**	**المقطع العلوي بالفرش**	**—**	**2026-10-24**	**A-09 (9/10)**

مصنع وتد الأخشاب
Watad Wood Factory

المنظور ثلاثي الأبعاد والمواد

النمط: جوزي غامق + إطارات سوداء — رندر واقعي بخامات حقيقية

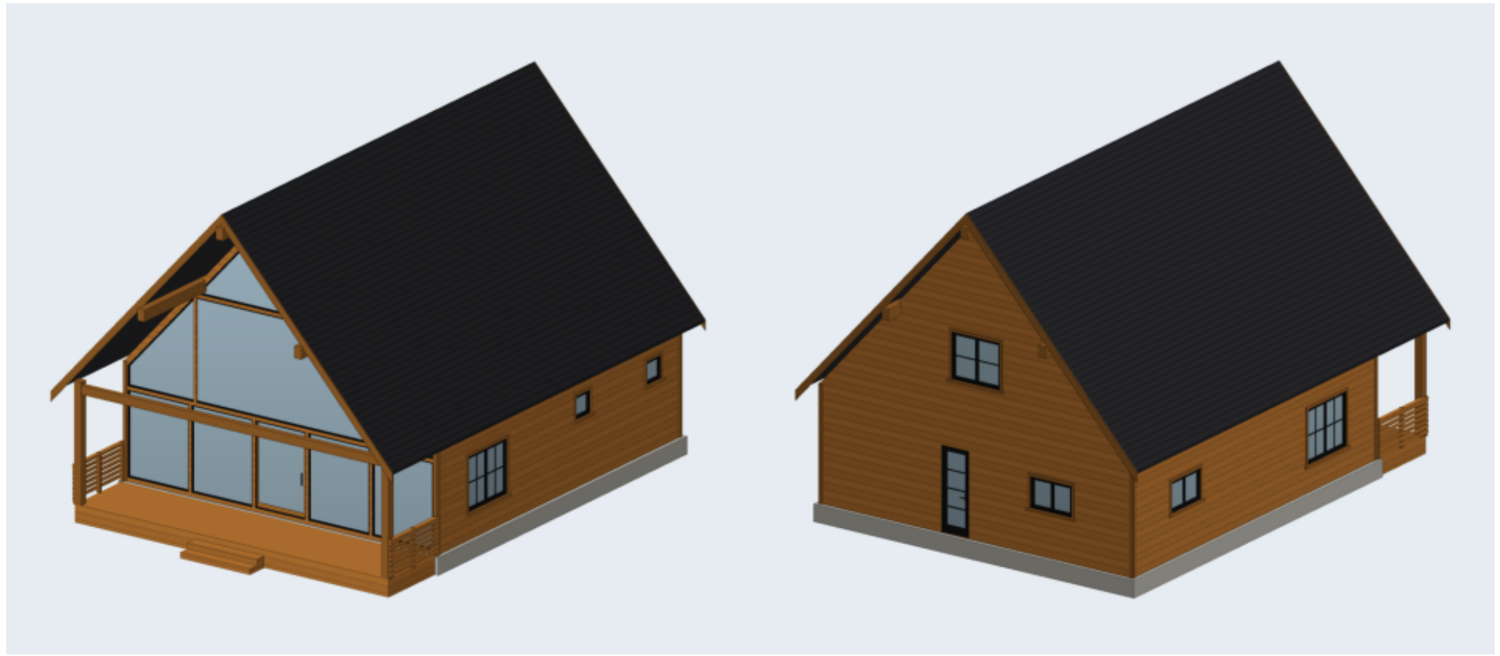

جدول المواد والألوان

الخشب / الصبغة

صبغة عسلي / سيدر

القرميد

قرميد رمادي غامق

الزجاج

زجاج شفاف

إطارات الشبابيك والأبواب

إطار ألمنيوم أسود

الكنار والزوايا

نفس الصبغة أغمق درجة


الصبة

خرسانة 45 سم


الدربزين: ألواح أفقية متقاربة (عصري)

تقسيم الشبابيك: بدون | الباب الرئيسي: زجاج بتقسيمات (فرنسي)

أنواع الدربزين المعتمدة (من مشاريع المصنع)

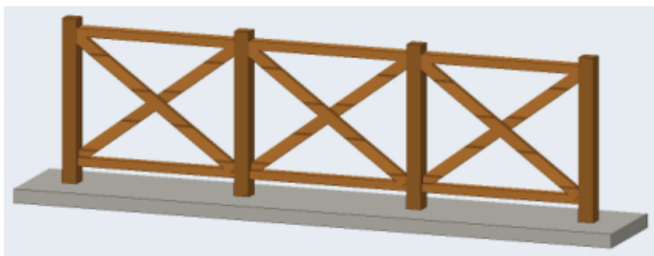

تقاطع X (صورة 5)

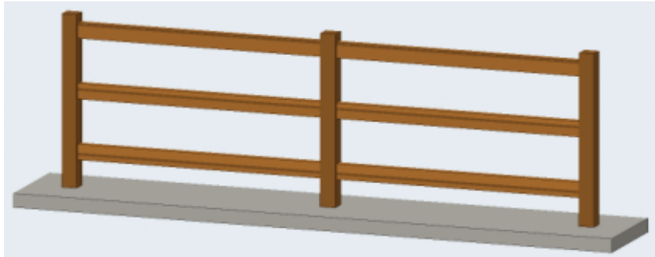

3 مرابيع أفقية (صورة 2)



قوائم رأسية متقاربة (صورة 1)

المشروع / العميل	عنوان اللوحة	المقياس	التاريخ	رقم اللوحة
مصنع وتد الأخشاب Watad Wood Factory — **كوخ A-frame دورين — صالة ومطبخ أمريكي وحمامين + غرفتين وحمام — 9.00 × 10.00 م** — **عميل — A-frame دورين**	**المنظور والمواد**	**—**	**2026-10-24**	**A-10 (10/10)**