

المسقط الأفقي مع الفرش

الأبعاد بالسنتيمتر - الجدران: قوائم 7×5 + تلبيس 2.5 من الجهتين (12 سم)

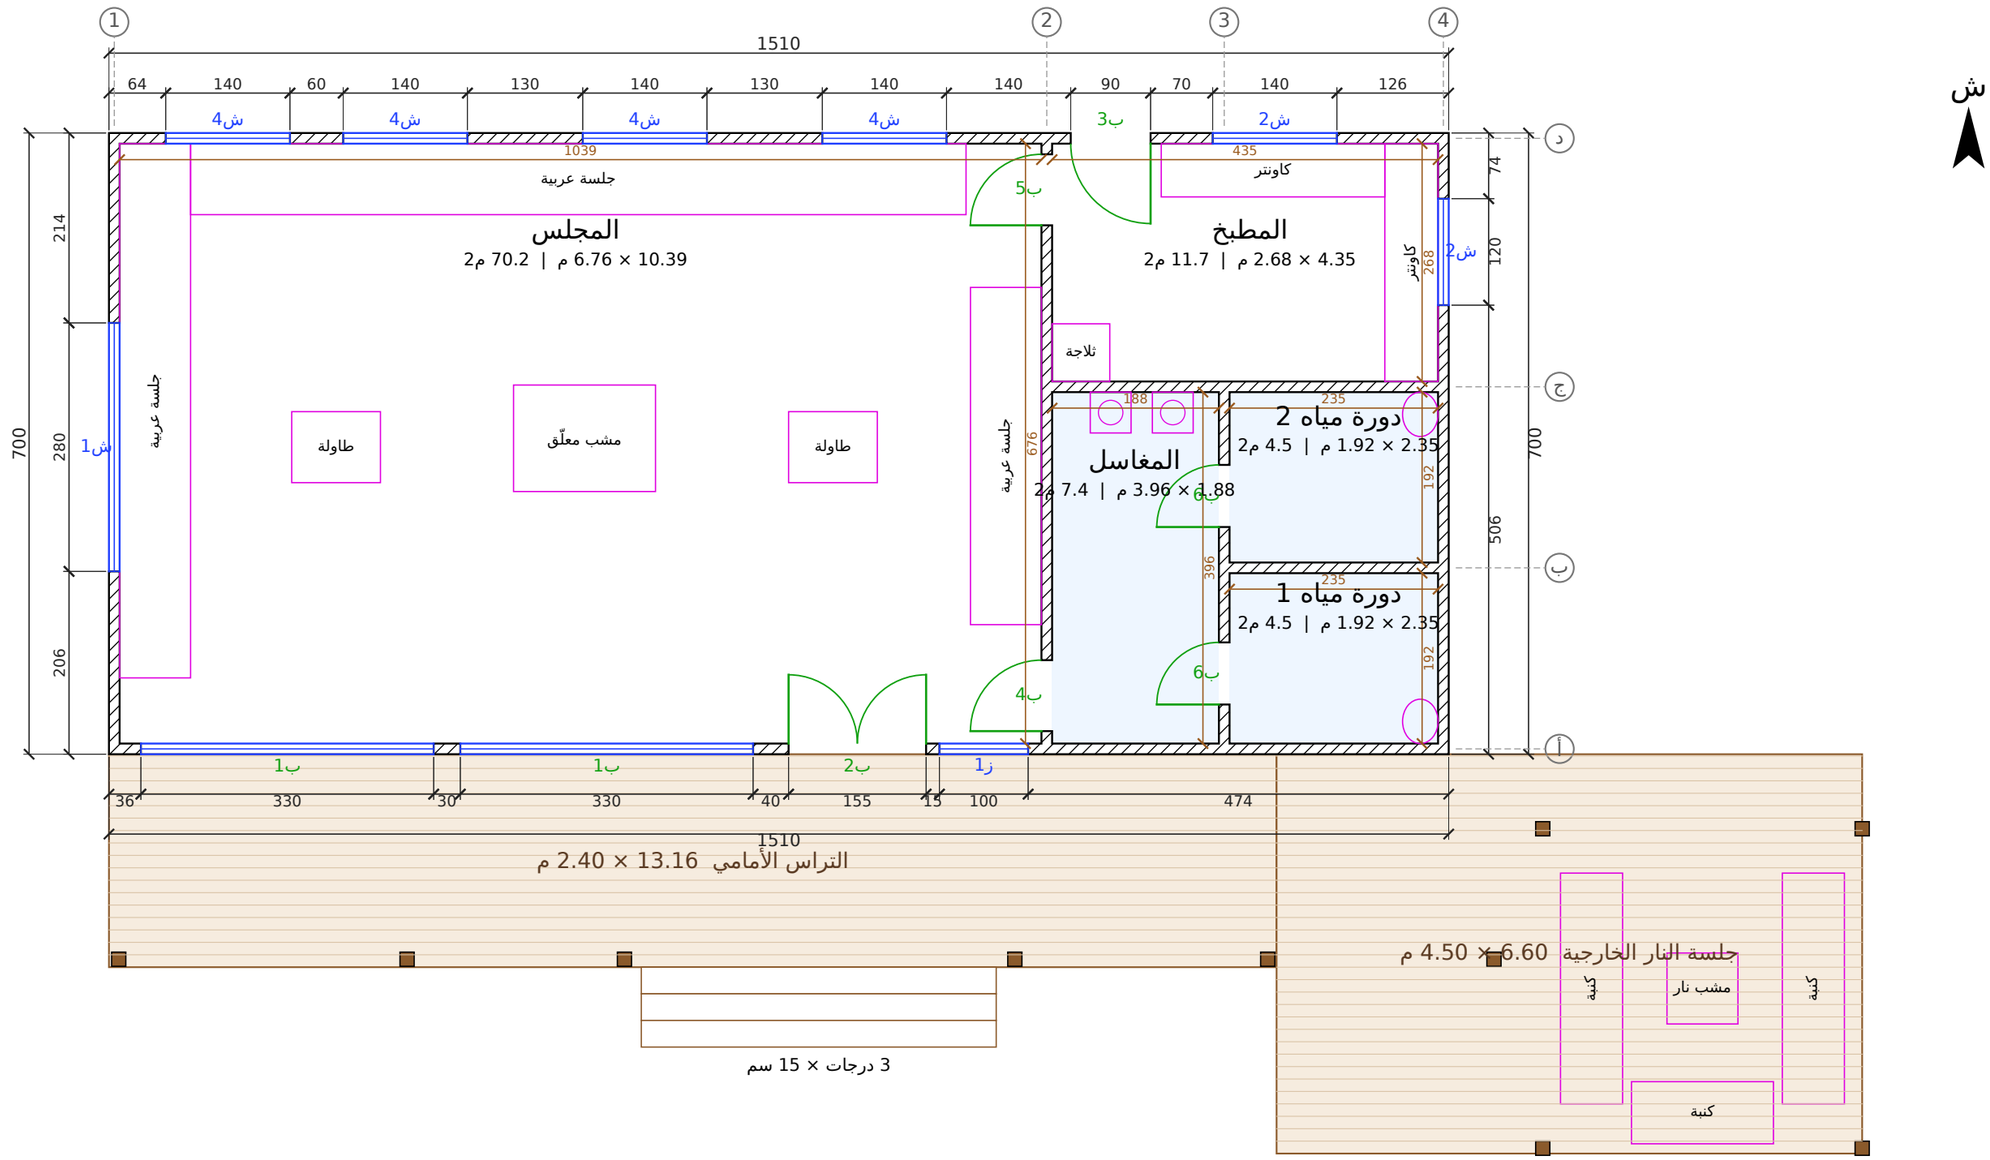


المشروع / العميل	عنوان اللوحة	المقياس	التاريخ	رقم اللوحة
مجلس كوخ خشب (بدل الخيمة) — 15.10 × 7.00 = 105.7 م² **عميل — مجلس خيمة إلى كوخ**	**المسقط الأفقي**	**1:50**	**2026-10-22**	**A-01 (1/11)**

مصنع وتد الأخشاب
Watad Wood Factory

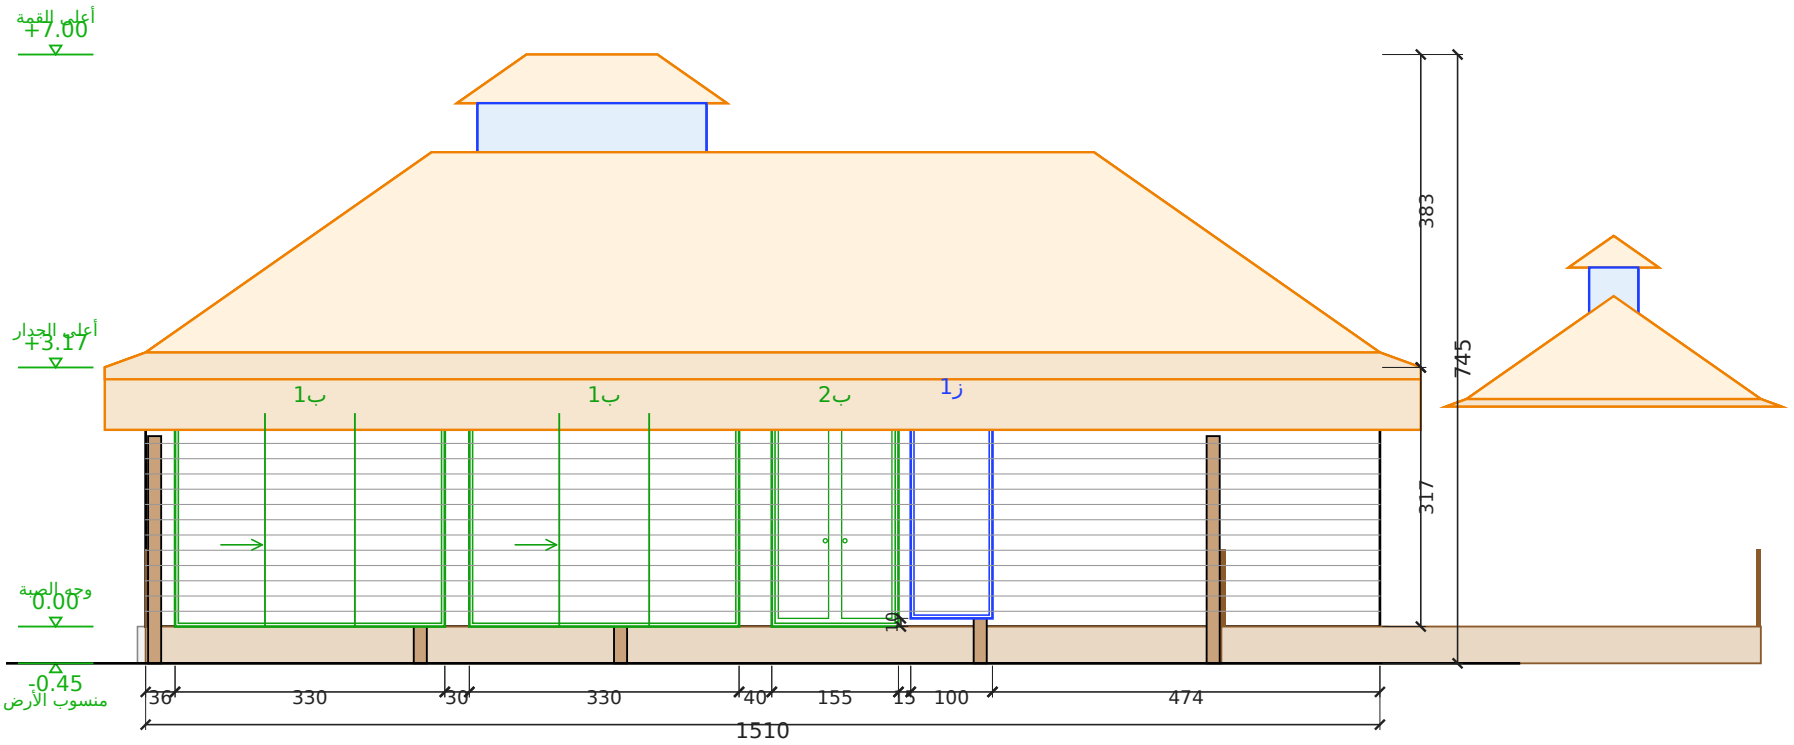

الواجهة الأمامية

مقياس 1:50 | الوحدة: سم

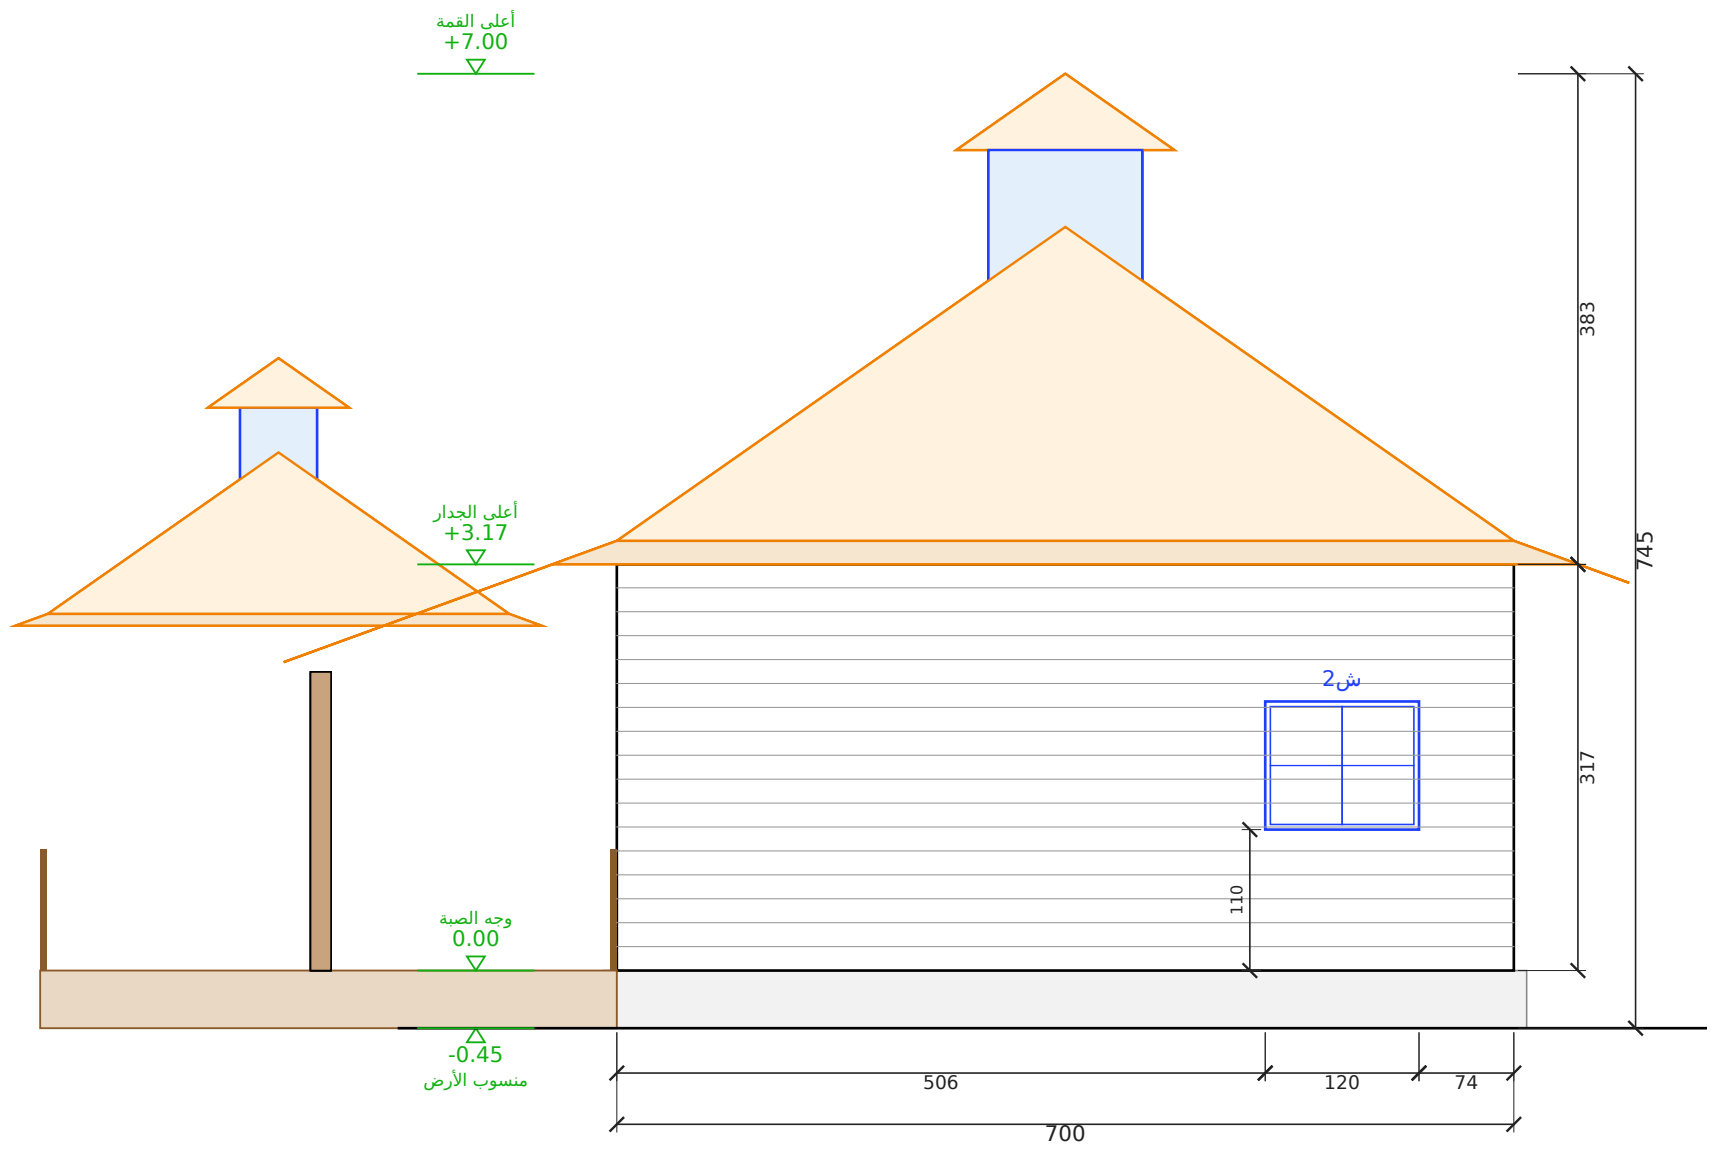


الواجهة الشرقية

مقياس 1:50 | الوحدة: سم


المشروع / العميل	عنوان اللوحة	المقياس	التاريخ	رقم اللوحة
مجلس كوخ خشب (بدل الخيمة) — 15.10 × 7.00 = 105.7 م² عميل — مجلس خيمة إلى كوخ	الواجهة الأمامية والواجهة الشرقية	1:50	2026-10-22	A-02 (2/11)

مصنع وتد الأخشاب
Watad Wood Factory

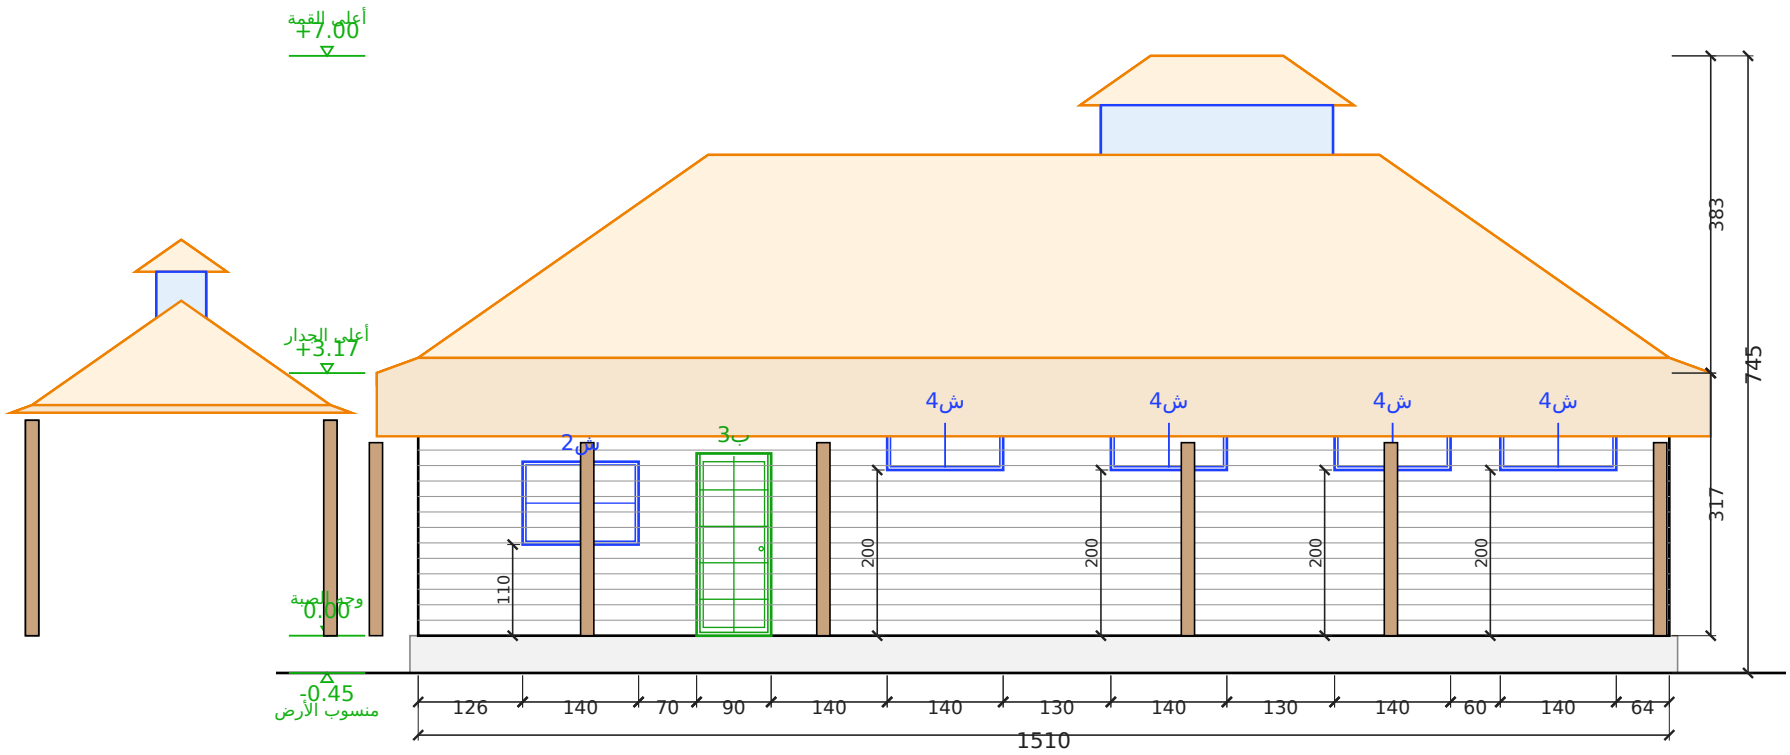

الواجهة الخلفية

مقياس 1:50 | الوحدة: سم

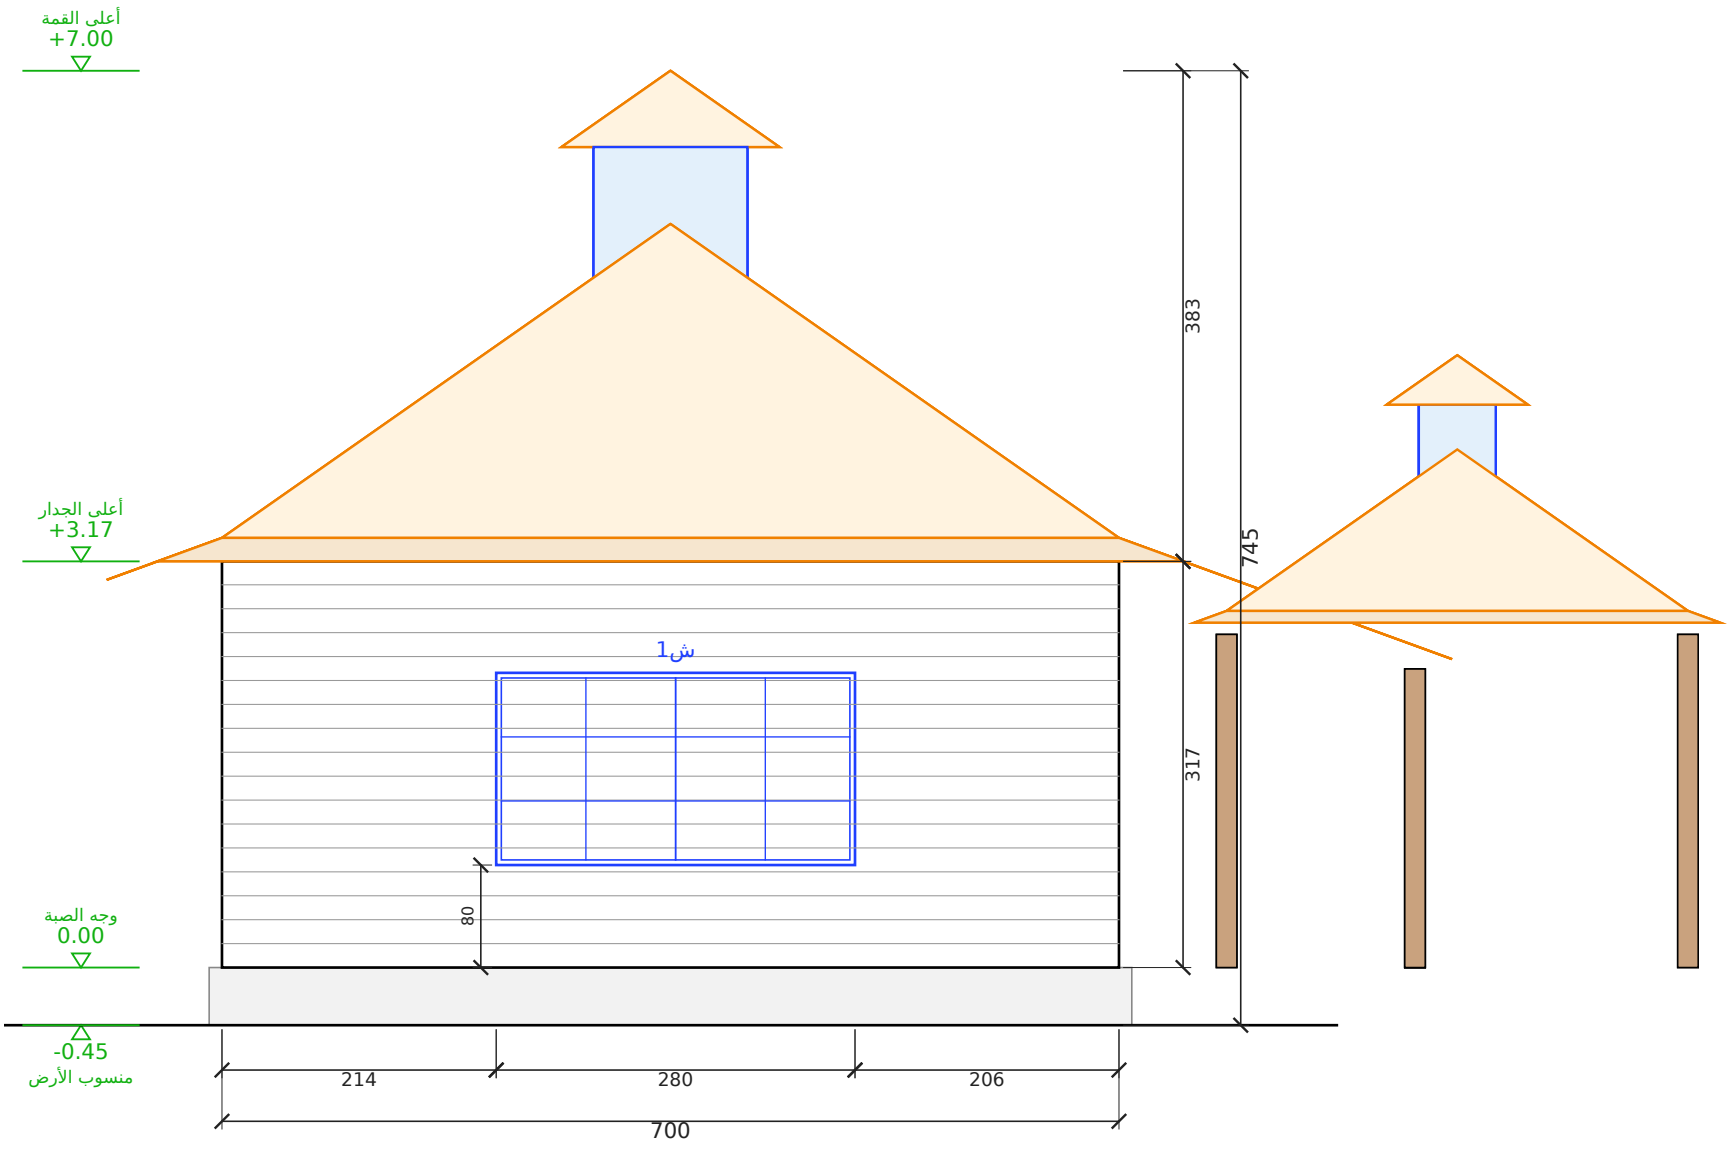


الواجهة الغربية

مقياس 1:50 | الوحدة: سم

المشروع / العميل	عنوان اللوحة	المقياس	التاريخ	رقم اللوحة
مجلس كوخ خشب (بدل الخيمة) — 15.10 × 7.00 = 105.7 م² عميل — مجلس خيمة إلى كوخ	الواجهة الخلفية والواجهة الغربية	1:50	2026-10-22	A-03 (3/11)


مصنع وتد الأخشاب
Watad Wood Factory

مسقط السقف — سقف الخيمة المنساب
كل الأسطح تصرّف للخارج — بدون وديان | مقياس 1:50

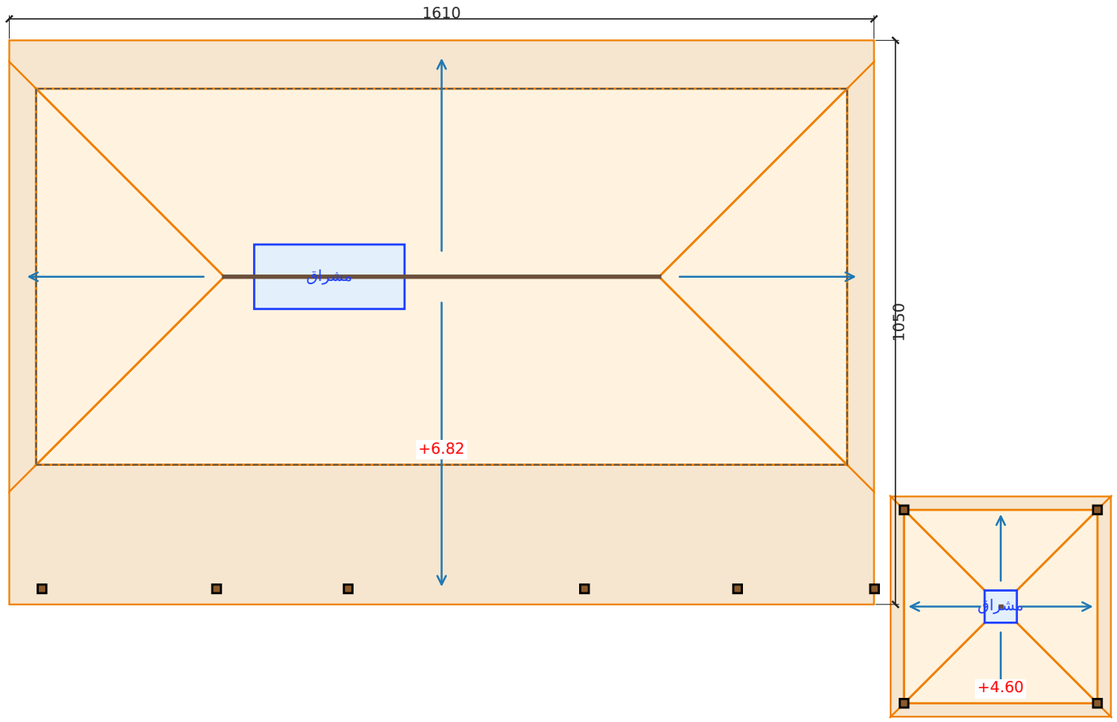

المداد العلوي 4.27 م (ميل 35°) + مداد الرفرف 3.09 م (ميل 20°) — الركني 5.52 م بوصلة

قطاع عرضي يمر بالمشراق
الكسرة عند الجدار: 35° فوق ثم 20° منساب | مقياس 1:50

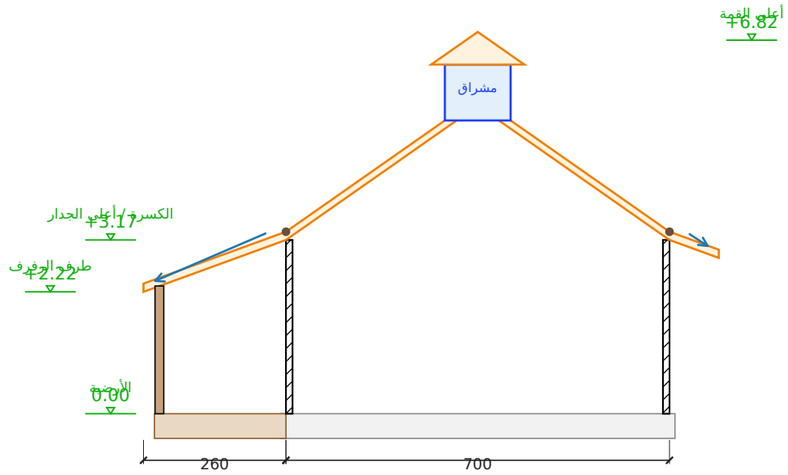

المشروع / العميل	عنوان اللوحة	المقياس	التاريخ	رقم اللوحة
مجلس كوخ خشب (بدل الخيمة) — 15.10 × 7.00 = 105.7 م² **عميل — مجلس خيمة إلى كوخ**	**مسقط السقف والقطاع**	**1:50**	**2026-10-22**	**A-04 (4/11)**

مصنع وتد الأخشاب
Watad Wood Factory

جدول مقاسات الأبواب والشبابيك
مقاس الفتحة الصافي في الجدار - الوحدة: سم

الرمز	النوع	العرض (سم)	الارتفاع (سم)	ارتفاع الجلسة (سم)	العدد	الموقع
ب1	باب	330	260	-	2	الأمامية 2
ب2	باب مزدوج	155	260	-	1	الأمامية
ب3	باب	90	220	-	1	الخلفية
ب4	باب	80	220	-	1	دورات المياه
ب5	باب	80	220	-	1	المطبخ (تقديم)
ب6	باب	70	210	-	2	كبينة 1 - كبينة 2
ز1	شباك	100	260	10	1	الأمامية
ش1	شباك	280	150	80	1	الغربية
ش2	شباك	120	100	110	1	الشرقية
ش2	شباك	140	100	110	1	الخلفية
ش4	شباك	140	60	200	4	الخلفية 4

الإجمالي: أبواب 8 - شبابيك 8

جدول المساحات وبيانات المشروع والتسعير

بيانات المشروع

البند	البيان
المشروع	مجلس كوخ خشب (بدل الخيمة) — 15.10 × 7.00 = 105.7 م²
العميل	عميل — مجلس خيمة إلى كوخ
الموقع	—
الاستخدام	مجلس / استراحة
التاريخ	2026-10-22
نظام البناء	هيكل خشب 5×7 + تلبيس 2.5 سم من الجهتين
السقف	جملون 35° — قرميد معدني

التسعير

البند	القيمة
المساحة المبنية (م2)	105.70
سعر المتر المربع	1,096 ريال
الإجمالي	**115,847 ريال**

ملاحظات:

- السعر على مساحة الكوخ 105.7 م² (نفس مساحة المخطط الأصلي).
- التراس الأمامي المسقوف وخيمة جلسة النار والمشراق الزجاج حسب الاتفاق.

جدول المساحات

م	الفراغ	الأبعاد (م)	المساحة (م2)
1	المجلس	10.39 × 6.76	70.24
2	المغاسل	1.88 × 3.96	7.44
3	دورة مياه 1	2.35 × 1.92	4.51
4	دورة مياه 2	2.35 × 1.92	4.51
5	المطبخ	4.35 × 2.68	11.66
	المساحة الصافية الداخلية		98.36
	التراس الأمامي (مجاناً)	**13.16 × 2.40**	**31.58**
	جلسة النار الخارجية (مجاناً)	**6.60 × 4.50**	**29.70**
	المساحة الإجمالية المبنية	**15.10 × 7.00**	**105.70**
	المساحة الكلية (المبنية + التراس والبلكونة)		**166.98**

الصور الواقعية — الخارج

أمامي من اليسار



رندر واقعي بخامات حقيقية وإضاءة طبيعية — الألوان النهائية حسب عينات المورد

أمامي من اليمين



الواجهة الأمامية



خلفي من اليسار



المشروع / العميل	عنوان اللوحة	المقياس	التاريخ	رقم اللوحة
مجلس كوخ خشب (بدل الخيمة) — 15.10 × 7.00 = 105.7 م² **عميل — مجلس خيمة إلى كوخ**	**الصور الواقعية — الخارج**	**—**	**2026-10-22**	**A-07 (7/11)**

مصنع وتد الأخشاب
Watad Wood Factory

الصور الواقعية — وقت الغروب

أمامي من اليسار — وقت الغروب



أمامي من اليمين — وقت الغروب



المجلس — من المدخل — بالليل والإنارة شغالة



المجلس — جدار الخشب واللوحات — بالليل والإنارة شغالة



المشروع / العميل	عنوان اللوحة	المقياس	التاريخ	رقم اللوحة
مجلس كوخ خشب (بدل الخيمة) — 15.10 × 7.00 = 105.7 م² **عميل — مجلس خيمة إلى كوخ**	**الصور الواقعية — الغروب**	**—**	**2026-10-22**	**A-08 (8/11)**

مصنع وتد الأخشاب
Watad Wood Factory

الصور الواقعية — الداخل

المجلس — من المدخل



المجلس — جدار الخشب واللوحات



المجلس — المشب والمشراق




الأثاث للتوضيح فقط — مواقع القطع ومقاساتها حسب المسقط

مصنع وتد الأخشاب Watad Wood Factory	المشروع / العميل **مجلس كوخ خشب (بدل الخيمة) — 15.10 × 7.00 = 105.7 م²** **عميل — مجلس خيمة إلى كوخ**	عنوان اللوحة **الصور الواقعية — الداخل**	المقياس **—**	التاريخ **2026-10-22**	رقم اللوحة **A-09 (9/11)**

المقطع العلوي بالفرش

مقطع أفقي على ارتفاع 1.90 م — توزيع الفرش ومسار الحركة

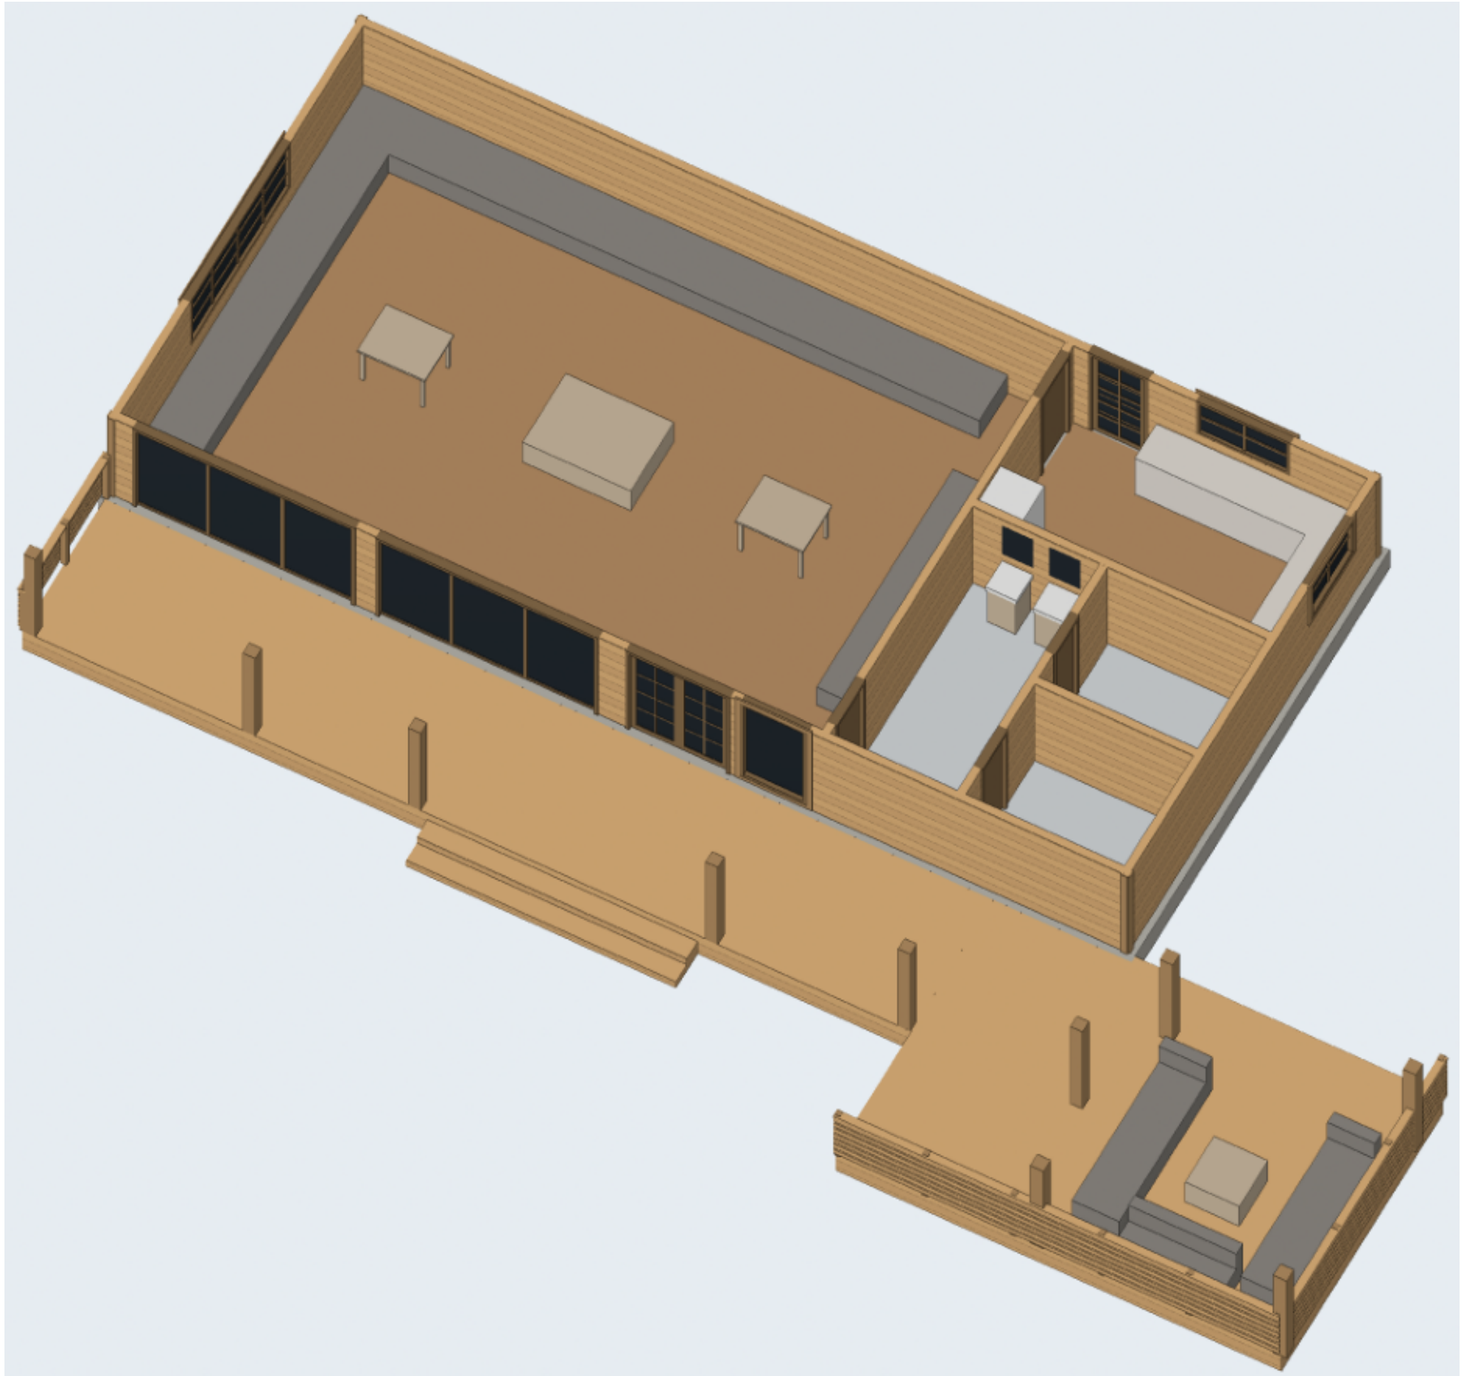

المشروع / العميل	عنوان اللوحة	المقياس	التاريخ	رقم اللوحة
مجلس كوخ خشب (بدل الخيمة) — 15.10 × 7.00 = 105.7 م² **عميل — مجلس خيمة إلى كوخ**	**المقطع العلوي بالفرش**	**—**	**2026-10-22**	**A-10 (10/11)**

مصنع وتد الأخشاب
Watad Wood Factory

المنظور ثلاثي الأبعاد والمواد

النمط: جوزي غامق + إطارات سوداء — رندر واقعي بخامات حقيقية





جدول المواد والألوان

الخشب / الصبغة

خشب طبيعي فاتح (بدون صبغة)

القرميد

صاج معدني رملي فاتح (لون قماش بيت الشعر)

الزجاج

زجاج عاكس غامق

إطارات الشبابيك والأبواب

إطار خشب بنفس الصبغة أغمق

الكنار والزوايا

نفس الصبغة أغمق درجة


الصبة

خرسانة 45 سم


الدربزين: ألواح أفقية متقاربة (عصري)

تقسيم الشبابيك: بدون | الباب الرئيسي: سحاب زجاج

أنواع الدربزين المعتمدة (من مشاريع المصنع)

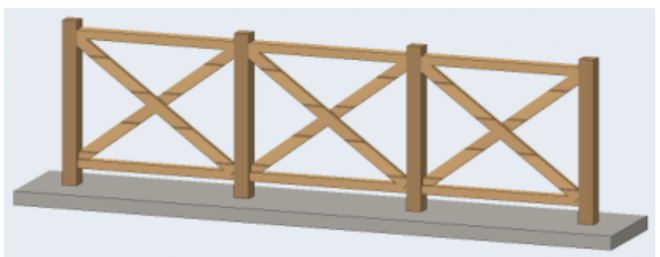

تقاطع X (صورة 5)

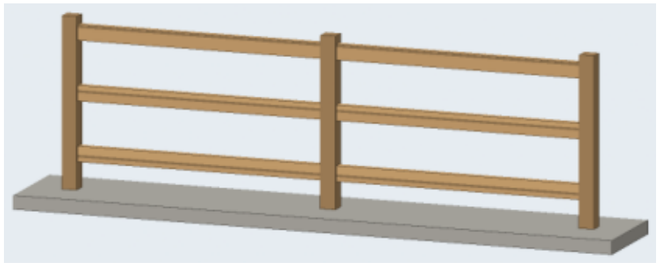

3 مرابيع أفقية (صورة 2)



قوائم رأسية متقاربة (صورة 1)

المشروع / العميل	عنوان اللوحة	المقياس	التاريخ	رقم اللوحة
مجلس كوخ خشب (بدل الخيمة) — 15.10 × 7.00 = 105.7 م² **عميل — مجلس خيمة إلى كوخ**	**المنظور والمواد**	**—**	**2026-10-22**	**A-11 (11/11)**

مصنع وتد الأخشاب
Watad Wood Factory