
المنظور ثلاثي الأبعاد والمواد

النمط: خشب طبيعي + قرميد فحمي — رندر واقعي بخامات حقيقية

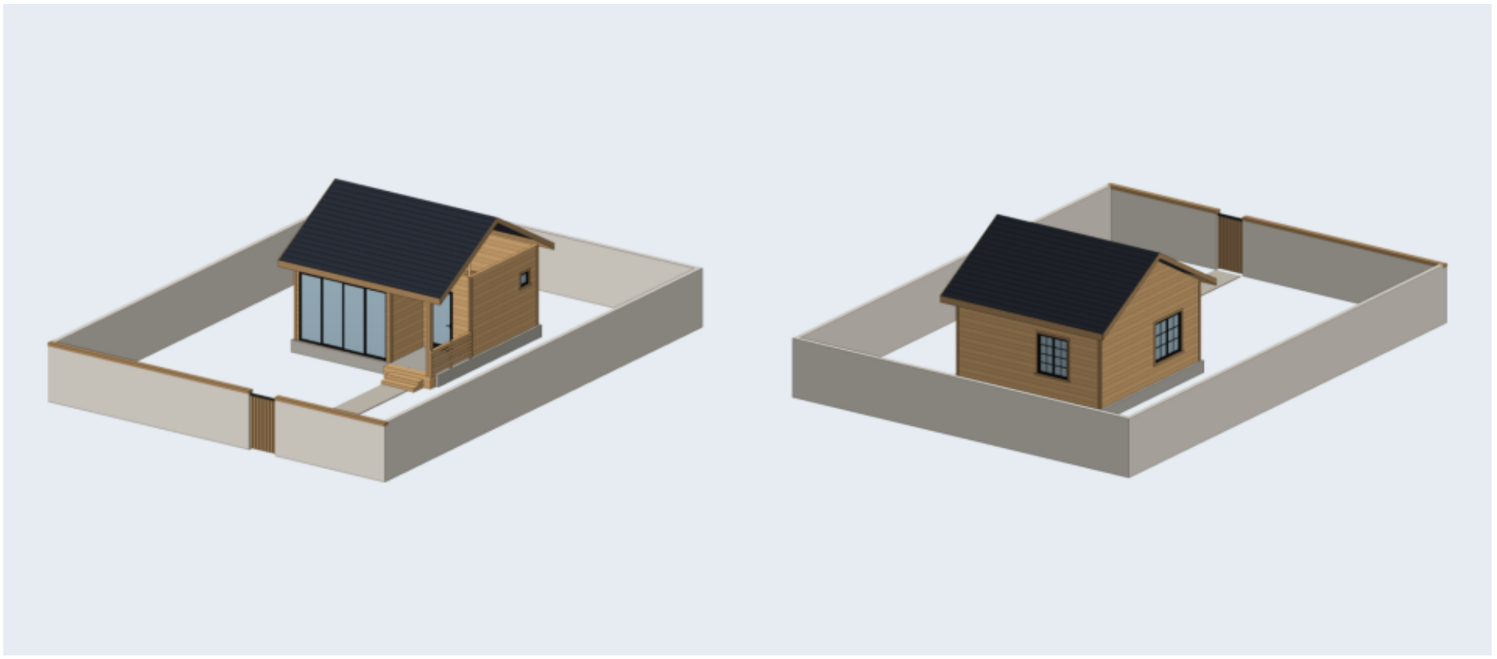

جدول المواد والألوان

الخشب / الصبغة

خشب طبيعي فاتح (بدون صبغة)

القرميد

قرميد فحمي / أسود مزرق

الزجاج

زجاج شفاف

إطارات الشبابيك والأبواب

إطار ألمنيوم أسود

الكنار والزوايا

نفس الصبغة أغمق درجة


الصبة

خرسانة 45 سم


الدربزين: ألواح أفقية متقاربة (عصري)

تقسيم الشبابيك: شبكة | الباب الرئيسي: زجاج بتقسيمات (فرنسي)

أنواع الدربزين المعتمدة (من مشاريع المصنع)

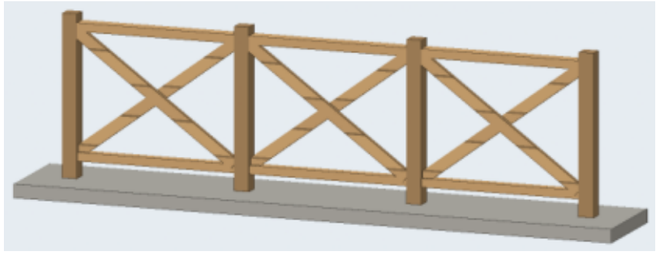

تقاطع X (صورة 5)

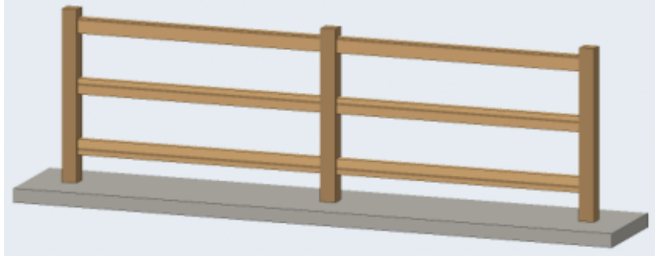

3 مرابيع أفقية (صورة 2)




قوائم رأسية متقاربة (صورة 1)

المشروع / العميل	عنوان اللوحة	المقياس	التاريخ	رقم اللوحة
مجلس خشب منفصل 4.00 × 6.00 م بواجهة زجاج ومدخل ودورة مياه **عميل – مجلس منفصل**	**المنظور والمواد**	**1:50**	**2026-11-03**	**W-01 (1/14)**

مصنع وتد الأخشاب
Watad Wood Factory


المسقط الأفقي مع الفرش

الأبعاد بالسنتيمتر - الجدران: قوائم 7×5 + تلبيس 2.5 من الجهتين (12 سم)

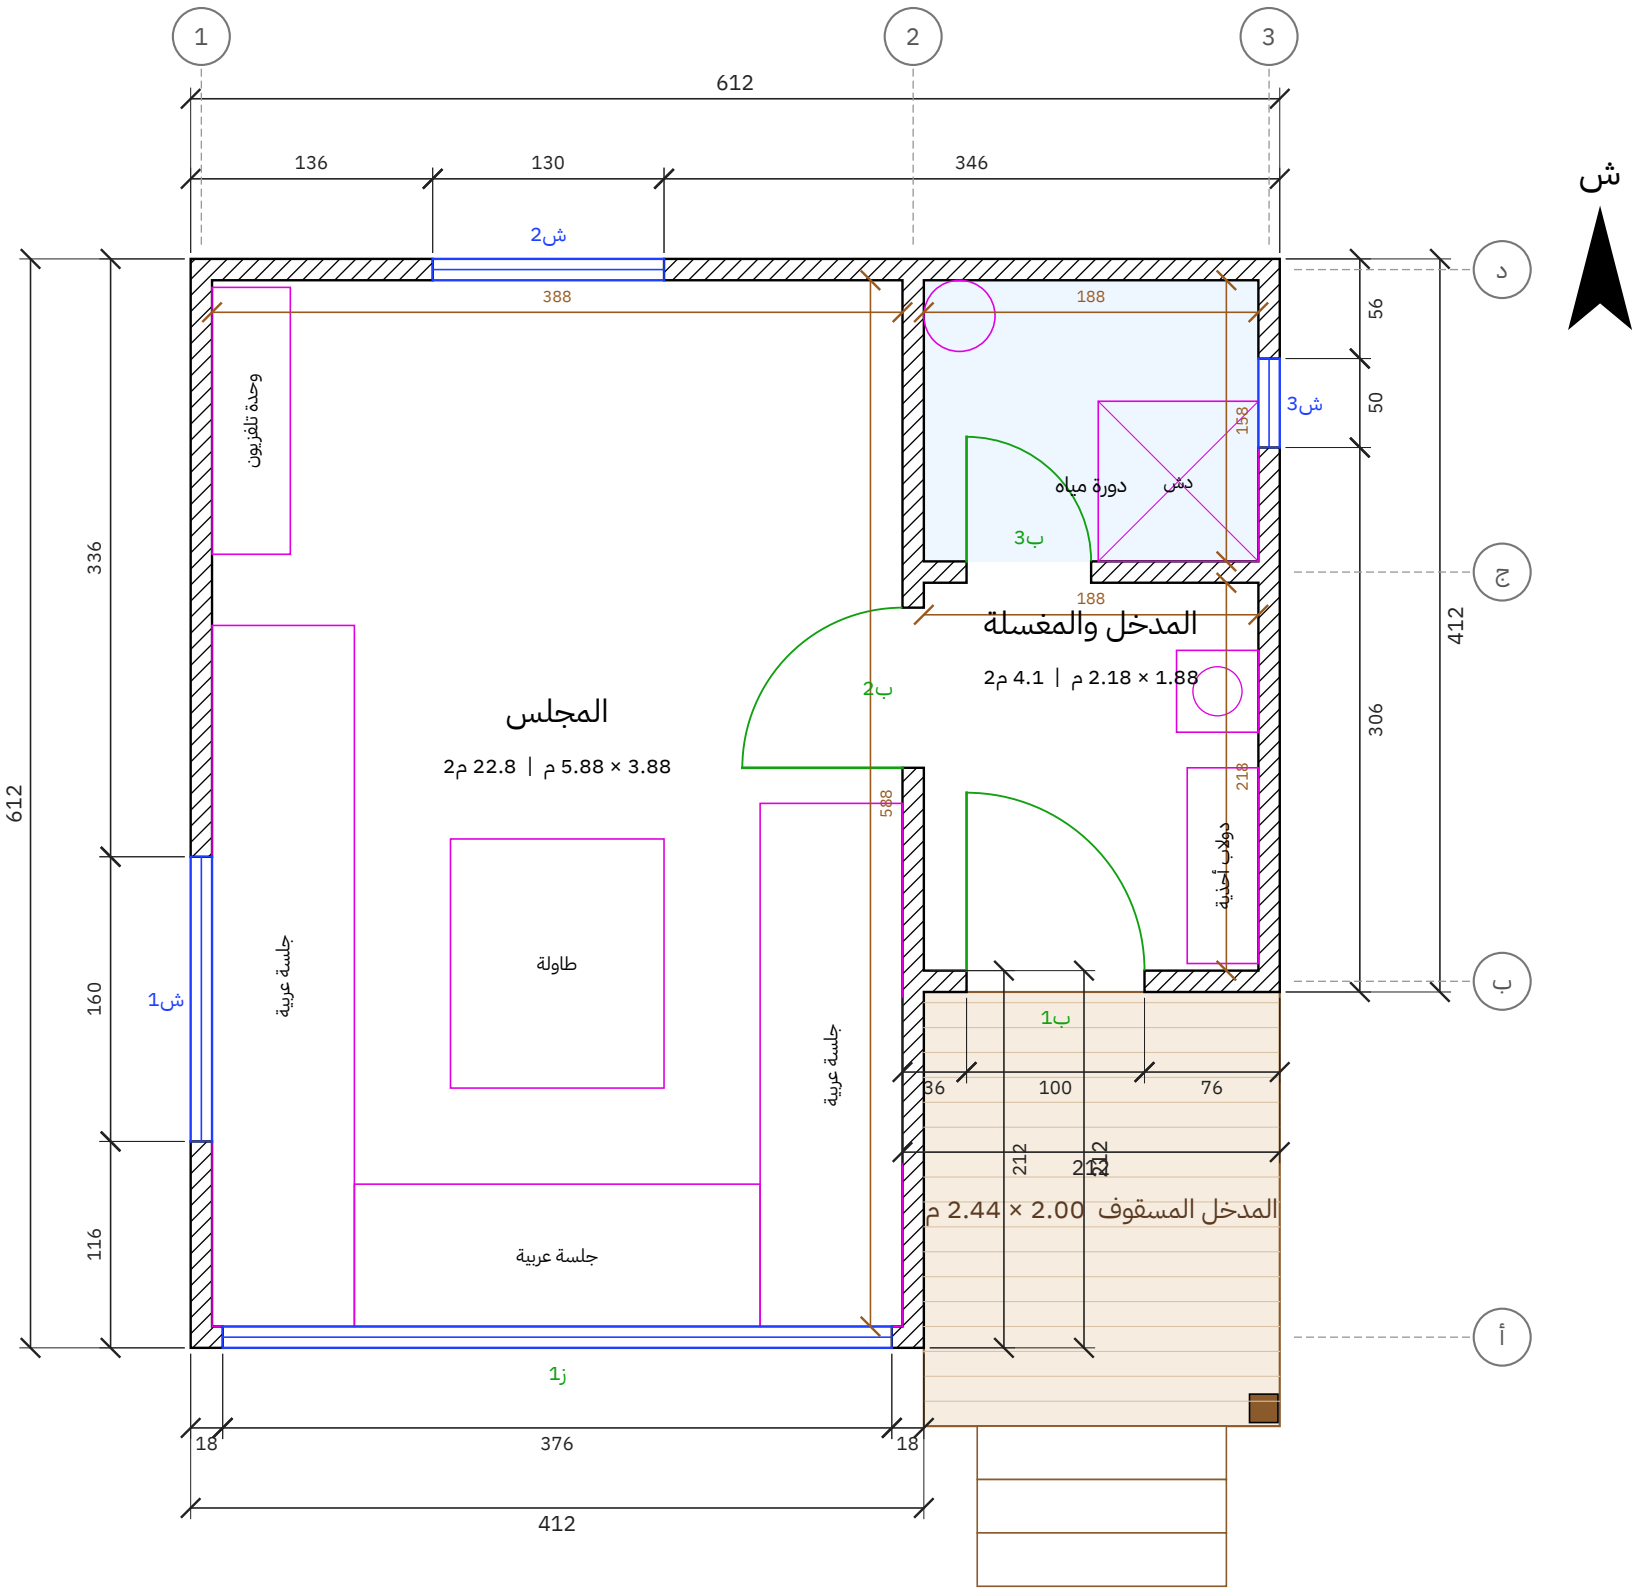


3 درجات × 15 سم

مصنع وتد الأخشاب Watad Wood Factory	المشروع / العميل مجلس خشب منفصل 4.00 × 6.00 م بواجهة زجاج ومدخل ودورة مياه عميل – مجلس منفصل	عنوان اللوحة المسقط الأفقي	المقياس 1:50	التاريخ 2026-11-03	رقم اللوحة W-02 (2/14)

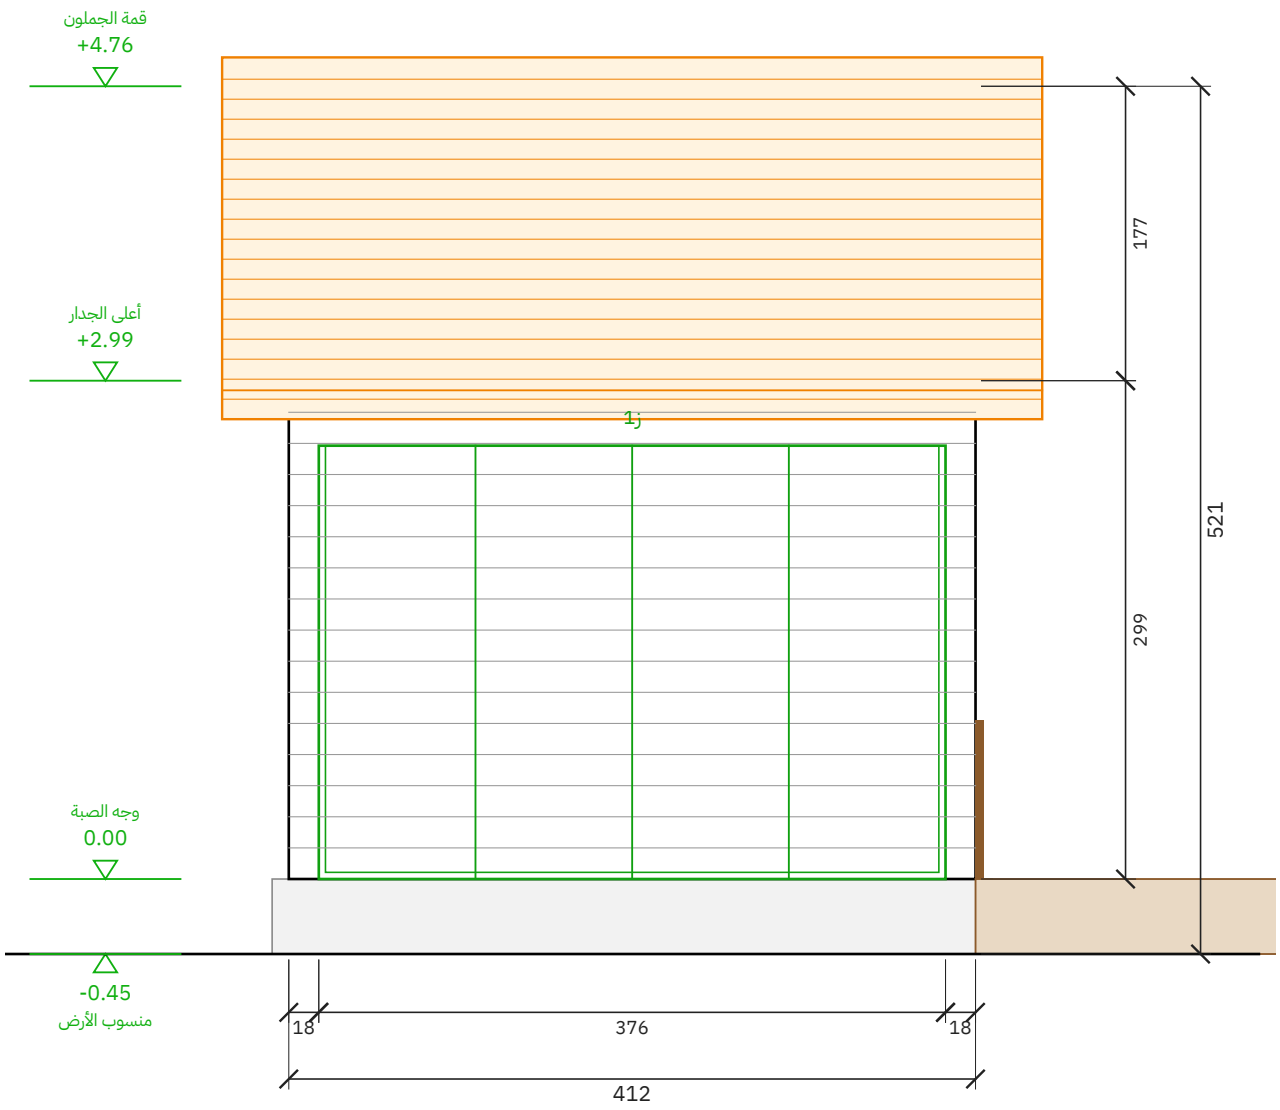

الواجهة الأمامية


مقياس 1:50 | الوحدة: سم

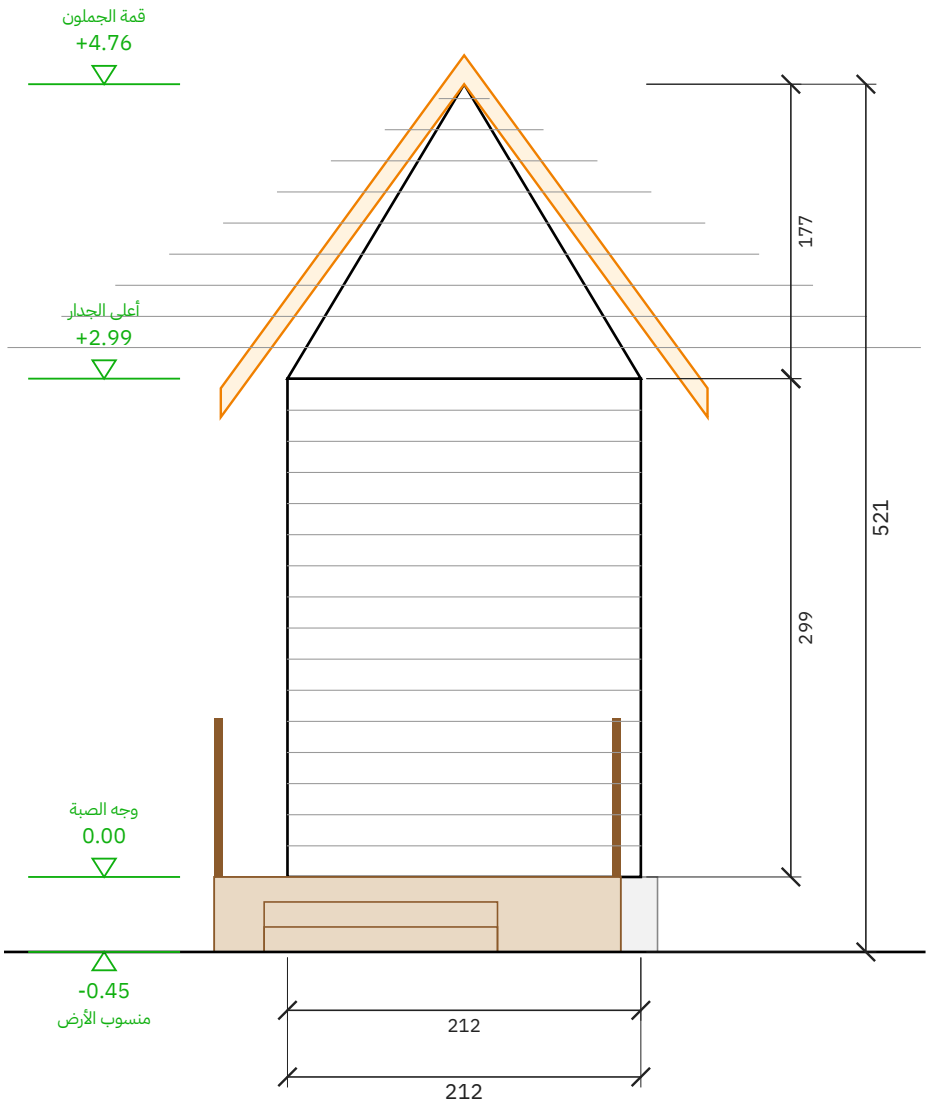

الواجهة الأمامية – المدخل


مقياس 1:50 | الوحدة: سم

المشروع / العميل	عنوان اللوحة	المقياس	التاريخ	رقم اللوحة
مصنع وتد الأخشاب Watad Wood Factory مجلس خشب منفصل 4.00 × 6.00 م بواجهة زجاج ومدخل ودورة مياه عميل – مجلس منفصل	الواجهة الأمامية والواجهة الأمامية – المدخل	1:50	2026-11-03	W-03 (3/14)

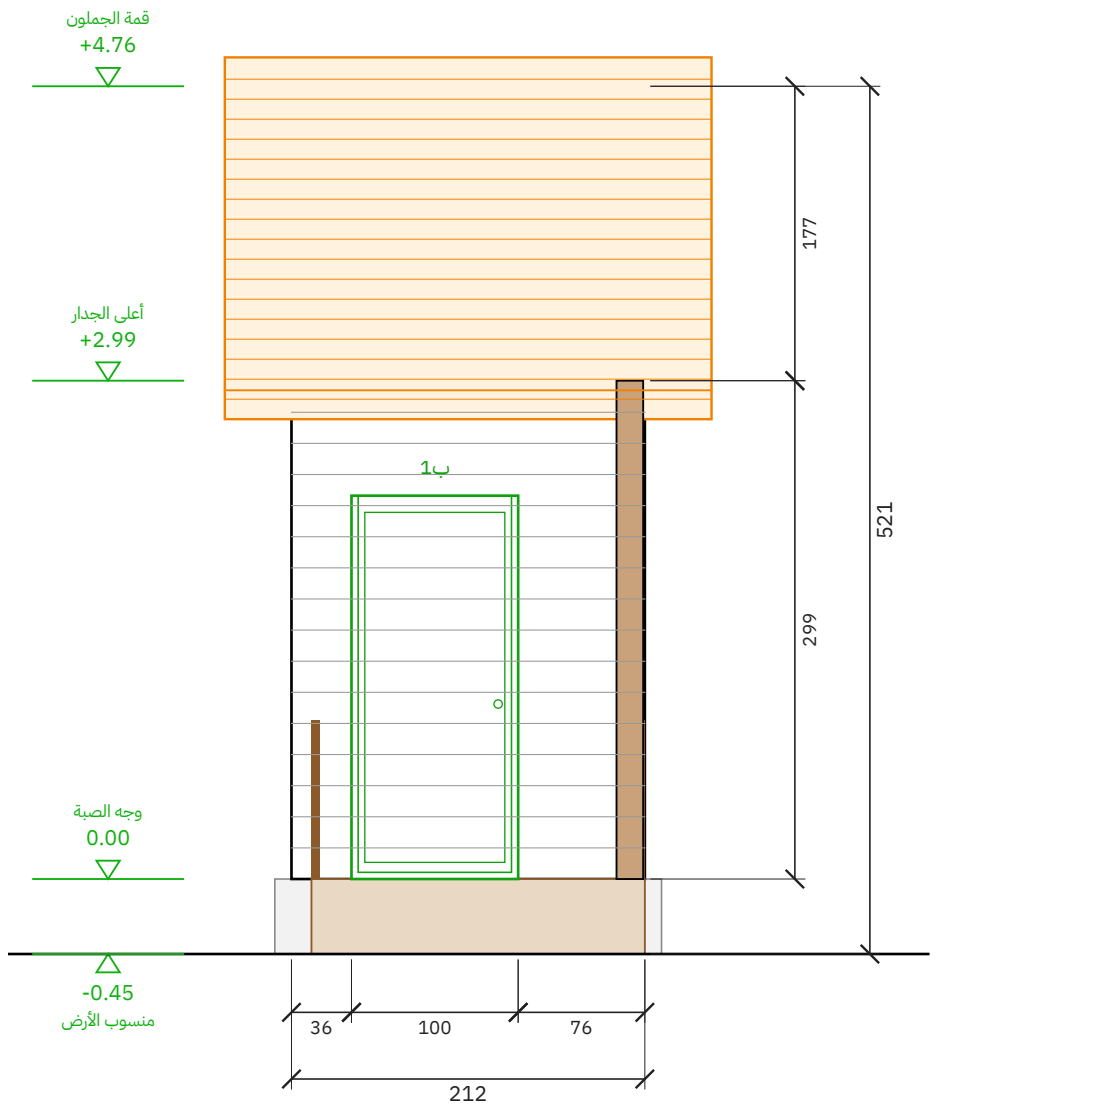

الواجهة الأمامية – المدخل

مقياس 1:50 | الوحدة: سم

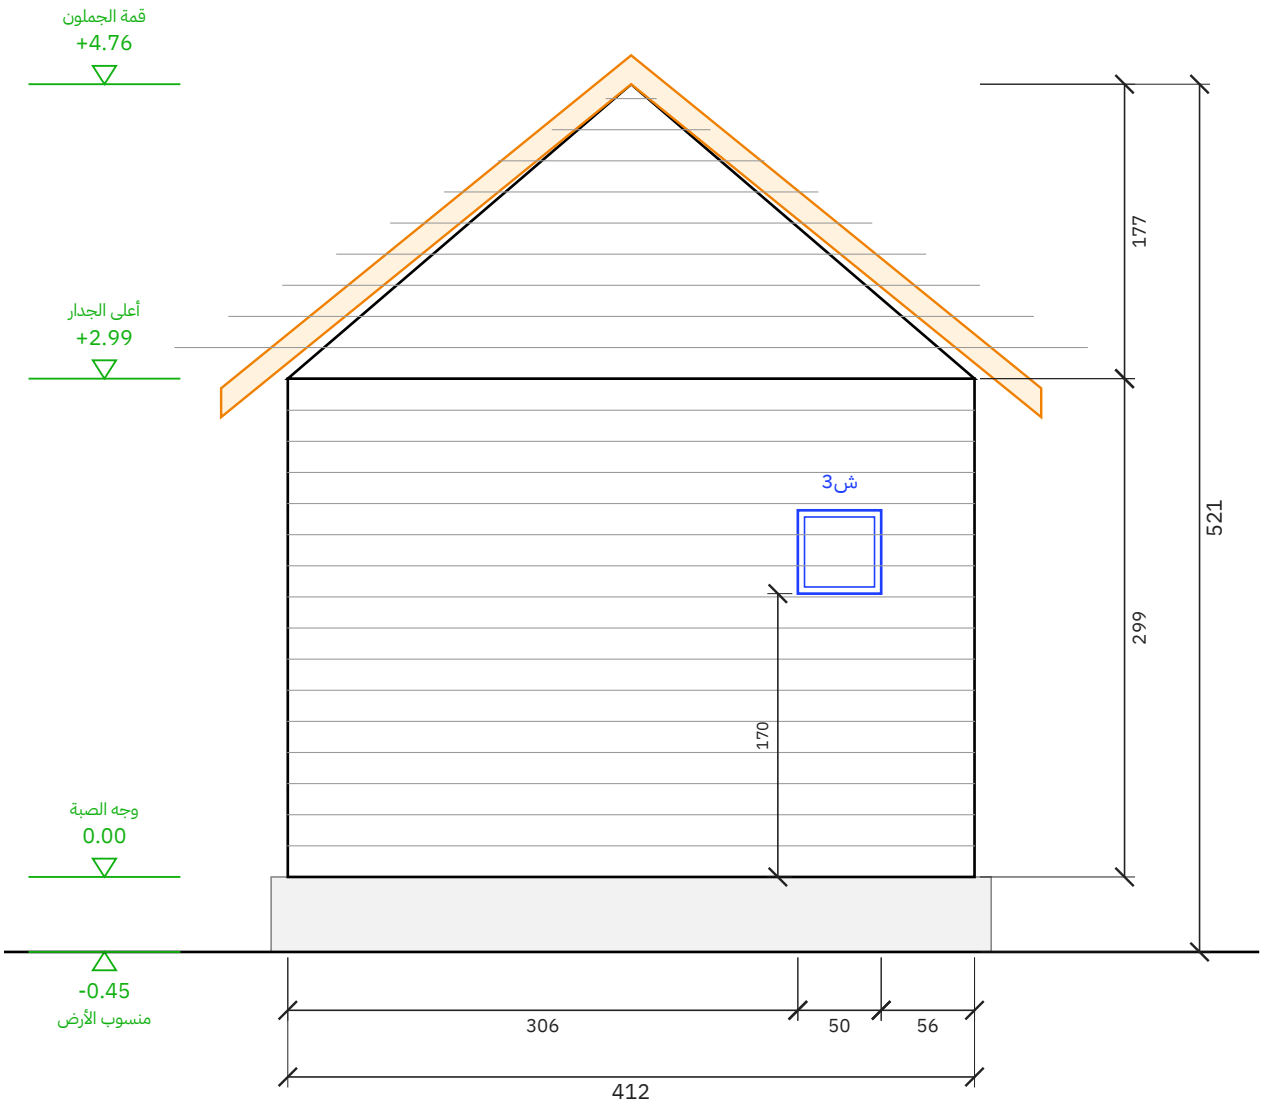


الواجهة الشرقية

مقياس 1:50 | الوحدة: سم


المشروع / العميل	عنوان اللوحة	المقياس	التاريخ	رقم اللوحة
مجلس خشب منفصل 4.00 × 6.00 م بواجهة زجاج ومدخل ودورة مياه عميل – مجلس منفصل	الواجهة الأمامية – المدخل والواجهة الشرقية	1:50	2026-11-03	W-04 (4/14)

مصنع وتد الأخشاب
Watad Wood Factory

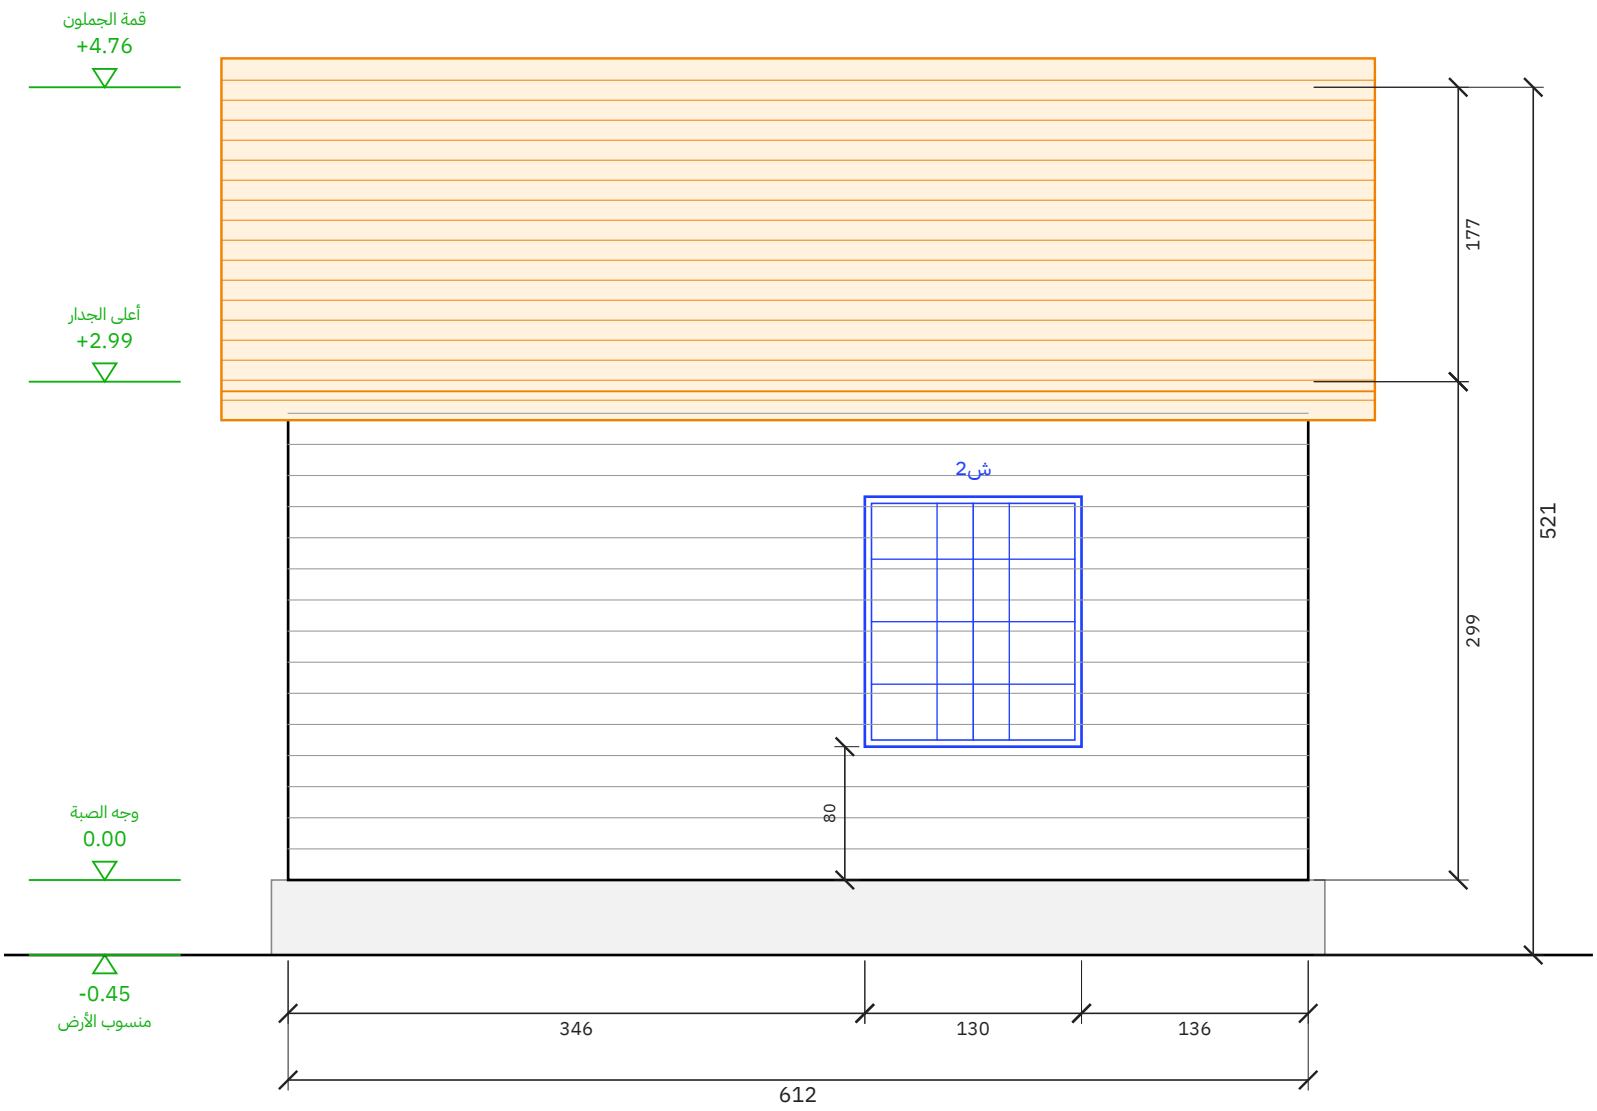

الواجهة الخلفية

مقياس 1:50 | الوحدة: سم

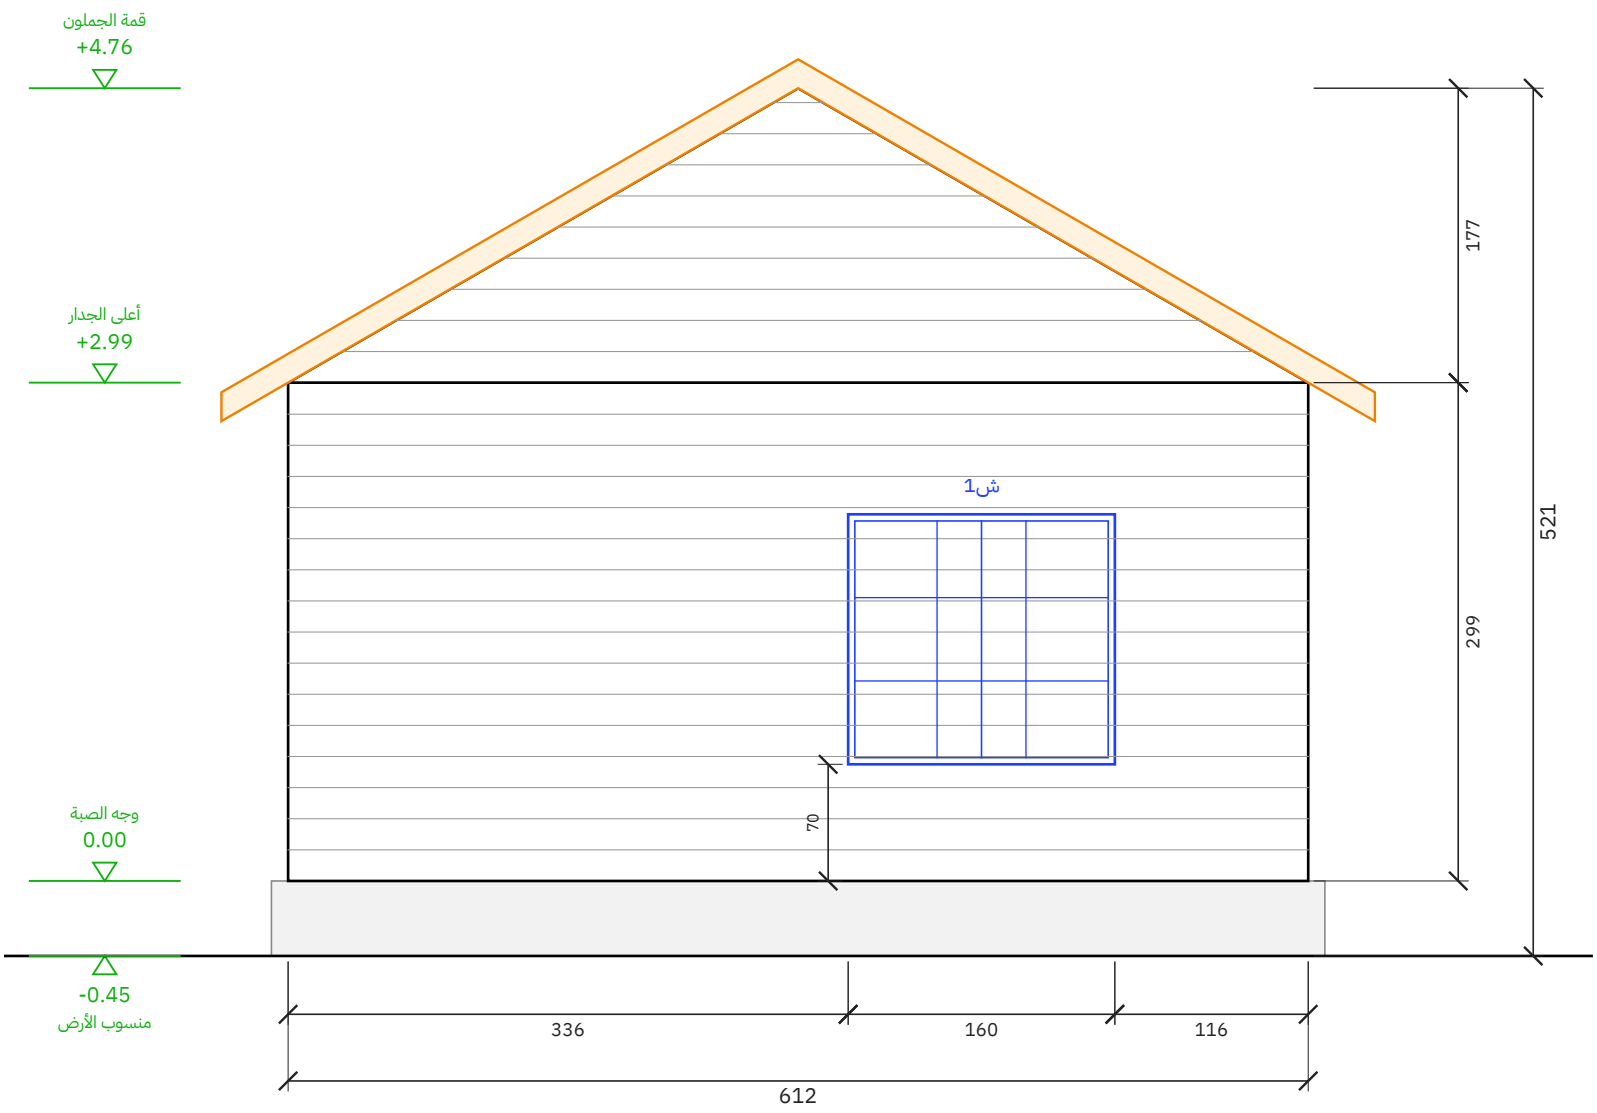

الواجهة الغربية


مقياس 1:50 | الوحدة: سم

المشروع / العميل	عنوان اللوحة	المقياس	التاريخ	رقم اللوحة
مجلس خشب منفصل 4.00 × 6.00 م بواجهة زجاج ومدخل ودورة مياه عميل – مجلس منفصل	الواجهة الخلفية والواجهة الغربية	1:50	2026-11-03	W-05 (5/14)

مصنع وتد الأخشاب
Watad Wood Factory


مسقط السقف (جملون)

رفرف 40 سم من كل جهة | مقياس 1:50

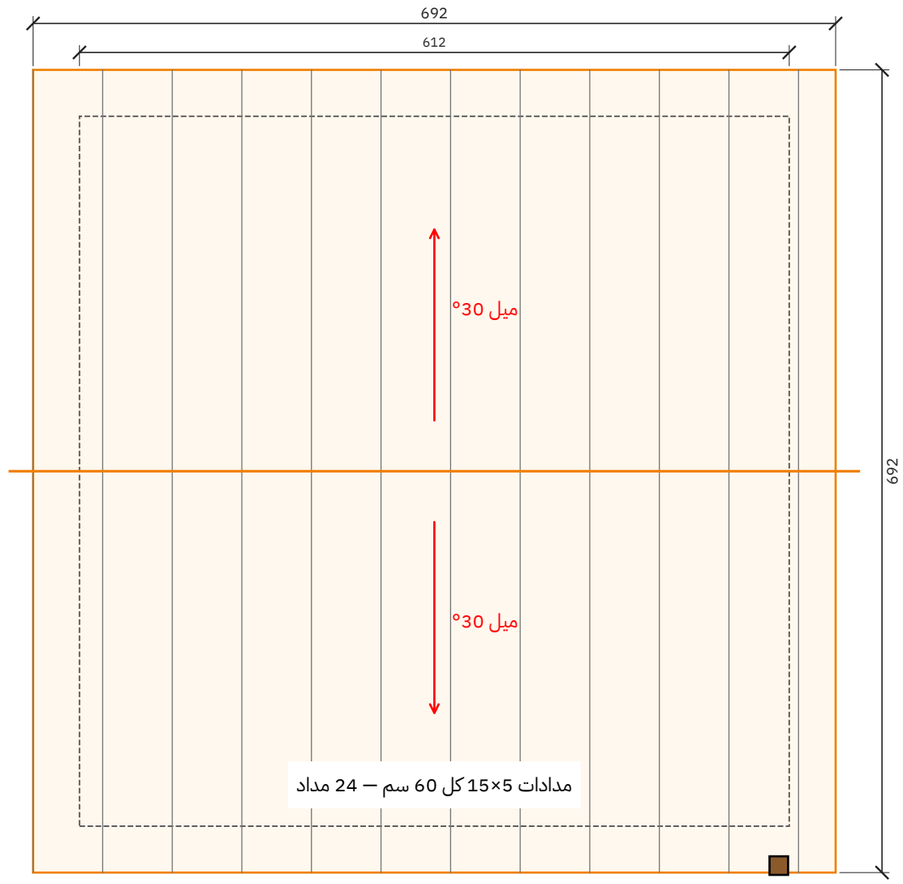


قطاع عرضي أ-أ

مقياس 1:50 | الوحدة: سم

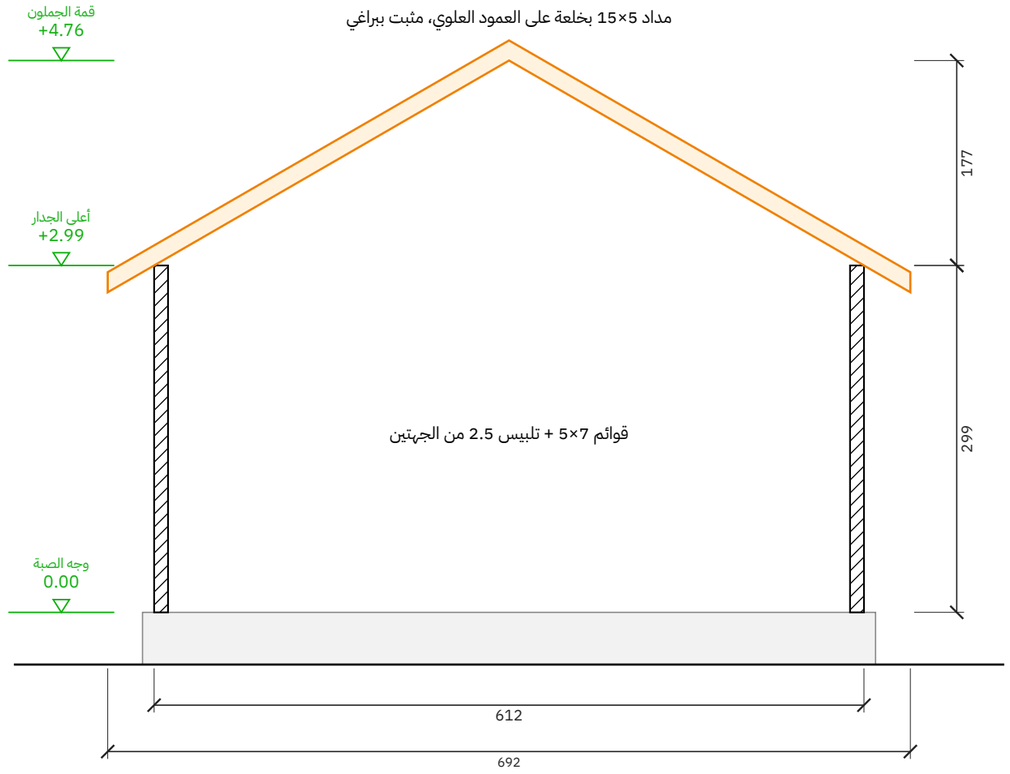

تفصيلة جلوس المداد على العلوي (1:5)

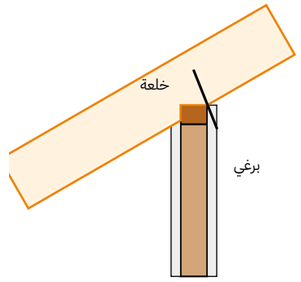

المشروع / العميل **مجلس خشب منفصل 4.00 × 6.00 م بواجهة زجاج ومدخل ودورة مياه** **عميل — مجلس منفصل**	عنوان اللوحة **مسقط السقف والقطاع**	المقياس **—**	التاريخ **2026-11-03**	رقم اللوحة **W-06 (6/14)**

مصنع وتد الأخشاب
Watad Wood Factory

جدول مقاسات الأبواب والشبابيك

مقاس الفتحة الصافي في الجدار - الوحدة: سم

الرمز	النوع	العرض (سم)	الارتفاع (سم)	ارتفاع الجلسة (سم)	العدد	الموقع
ب1	باب	100	230	-	1	الأمامية — المدخل
ب2	باب	90	220	-	1	المدخل — المجلس
ب3	باب	70	210	-	1	دورة المياه
ز1	باب	376	260	-	1	الأمامية
ش1	شباك	160	150	70	1	الغربية
ش2	شباك	130	150	80	1	الخلفية
ش3	شباك	50	50	170	1	الشرقية

الإجمالي: أبواب 4 - شبابيك 3

جدول المساحات وبيانات المشروع


بيانات المشروع

البند	البيان
المشروع	مجلس خشب منفصل 4.00 × 6.00 م بواجهة زجاج ومدخل ودورة مياه
العميل	عميل — مجلس منفصل
الموقع	—
الاستخدام	مجلس ضيافة
التاريخ	2026-11-03
نظام البناء	هيكل خشب 5×7 + تلبيس 2.5 سم من الجهتين
السقف	جملون 30° — قرميد معدني


جدول المساحات

م	الفراغ	الأبعاد (م)	المساحة (م2)
1	المجلس	3.88 × 5.88	22.81
2	المدخل والمغسلة	1.88 × 2.18	4.10
3	دورة مياه	1.88 × 1.58	2.97
	المساحة الصافية الداخلية		**29.88**
	المدخل المسقوف	**2.00 × 2.44**	**4.88**
	المساحة الإجمالية المبنية	**6.12 × 6.12**	**37.45**
	المساحة الكلية (المبنية + التراس)		**42.33**

تأطير جدار جنوب — الطول 400 سم، الارتفاع 299 سم

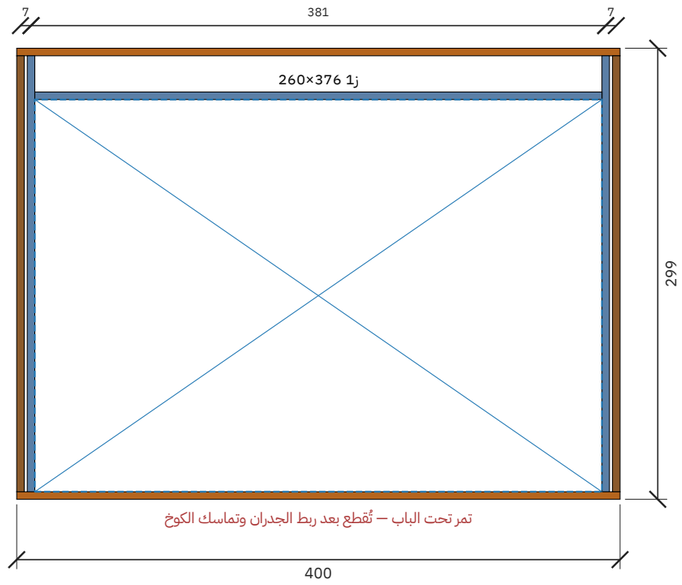


تأطير جدار جدار المدخل المسقوف — الطول 200 سم، الارتفاع 299 سم

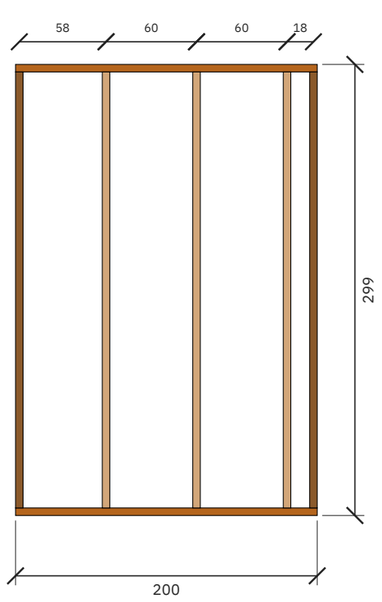


قاعدة سفلية | علوي | عمود | عمود زاوية | جنب فتحة | رأس فتحة | جلسة شباك | عمود قصير

مصنع وتد الأخشاب Watad Wood Factory	المشروع / العميل **مجلس خشب منفصل 4.00 × 6.00 م بواجهة زجاج ومدخل ودورة مياه** **عميل — مجلس منفصل**	عنوان اللوحة **لوحات التأطير (للورشة)**	المقياس **—**	التاريخ **2026-11-03**	رقم اللوحة **W-09 (9/14)**

تأطير جدار جدار المدخل — الطول 200 سم، الارتفاع 299 سم

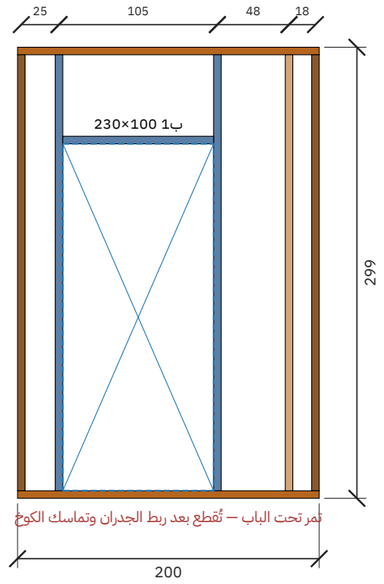


تأطير جدار شرق — الطول 400 سم، الارتفاع 299 سم

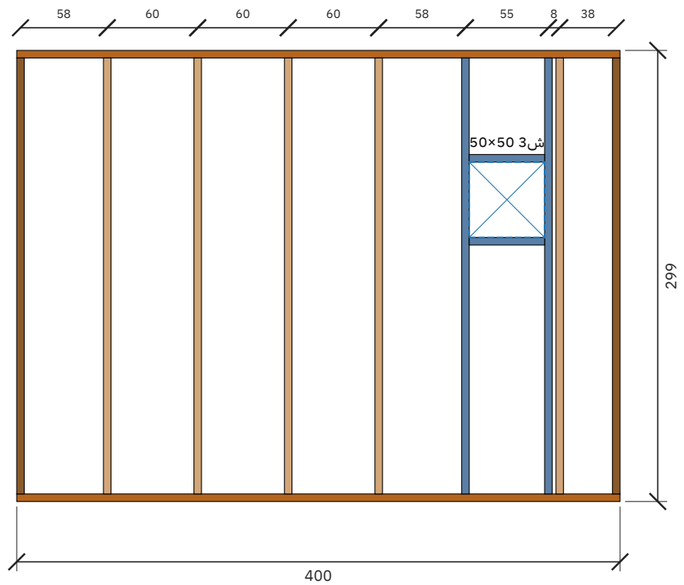


قاعدة سفلية | علوي | عمود | عمود زاوية | جنب فتحة | رأس فتحة | جلسة شباك | عمود قصير

مصنع وتد الأخشاب Watad Wood Factory	المشروع / العميل **مجلس خشب منفصل 4.00 × 6.00 م بواجهة زجاج ومدخل ودورة مياه** **عميل — مجلس منفصل**	عنوان اللوحة **لوحات التأطير (للورشة)**	المقياس —	التاريخ **2026-11-03**	رقم اللوحة **W-10 (10/14)**

تأطير جدار شمال — الطول 600 سم، الارتفاع 299 سم

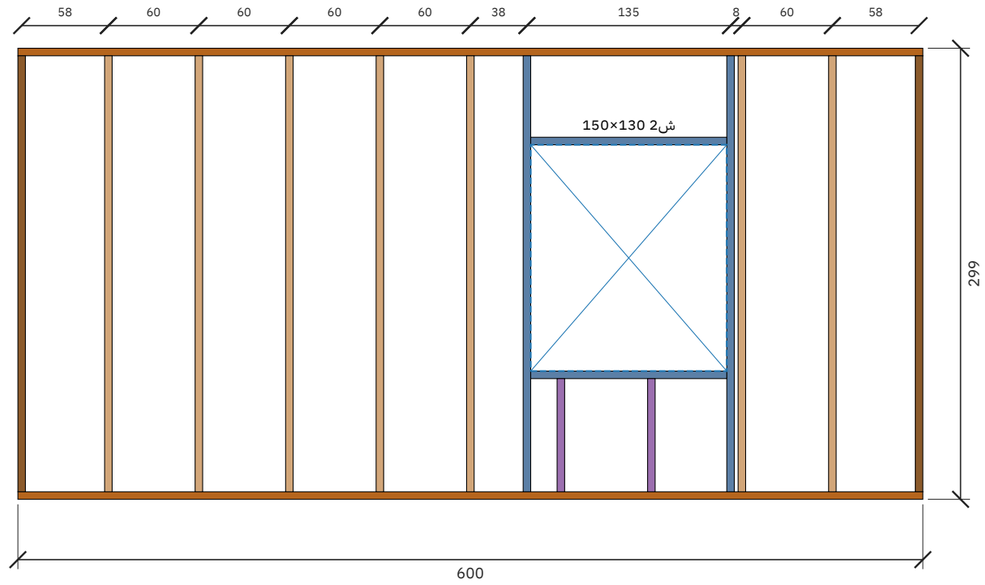


تأطير جدار غرب — الطول 600 سم، الارتفاع 299 سم

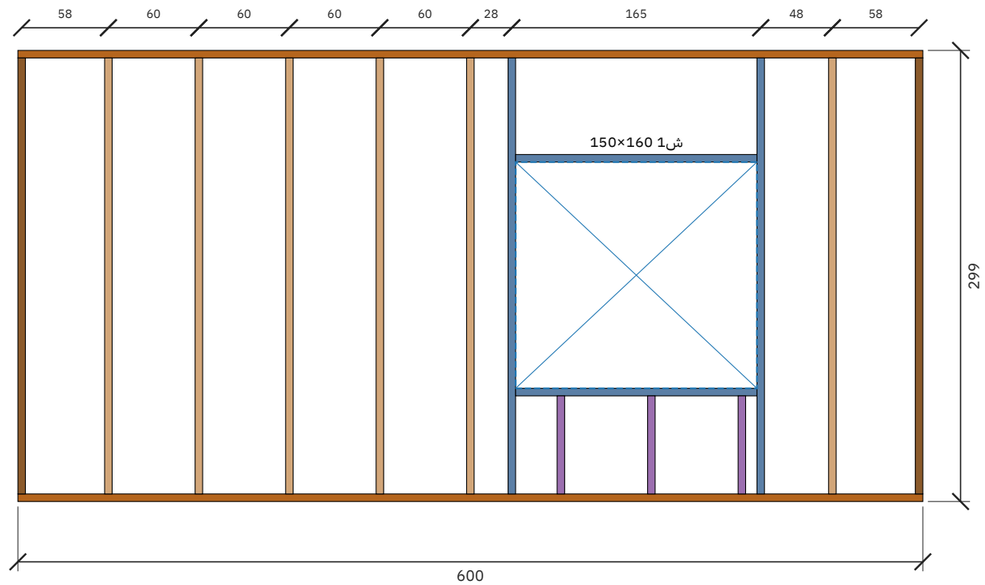


قاعدة سفلية | علوي | عمود | عمود زاوية | جنب فتحة | رأس فتحة | جلسة شباك | عمود قصير

مصنع وتد الأخشاب Watad Wood Factory	المشروع / العميل **مجلس خشب منفصل 4.00 × 6.00 م بواجهة زجاج ومدخل ودورة مياه** **عميل – مجلس منفصل**	عنوان اللوحة **لوحات التأطير (للورشة)**	المقياس **–**	التاريخ **2026-11-03**	رقم اللوحة **W-11 (11/14)**

تأطير جدار جدار المجلس الشرقي — الطول 400 سم، الارتفاع 299 سم (داخلي)

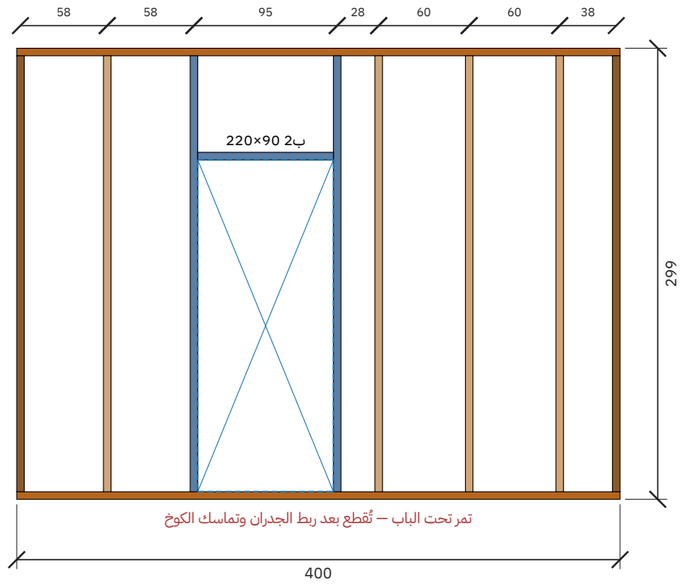

تأطير جدار جدار دورة المياه — الطول 200 سم، الارتفاع 299 سم (داخلي)

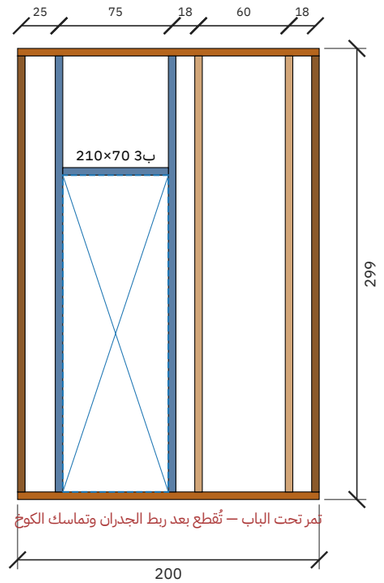

قاعدة سفلية | علوي | عمود | عمود زاوية | جنب فتحة | رأس فتحة | جلسة شباك | عمود قصير

مصنع وتد الأخشاب Watad Wood Factory	المشروع / العميل **مجلس خشب منفصل 4.00 × 6.00 م بواجهة زجاج ومدخل ودورة مياه** **عميل — مجلس منفصل**	عنوان اللوحة **لوحات التأطير (للورشة)**	المقياس **—**	التاريخ **2026-11-03**	رقم اللوحة **W-12 (12/14)**

جدول الكميات وخطة تقطيع الطبليات

البند	القيمة
الارتفاع المطلوب / المعتمد	290 / 299 سم
السقف	جملون 30° — أعلى نقطة 476 سم من وجه الصبة
المدادات 5×15	24 مداد (12 لكل جهة) × حتى 400 سم — من طبلية 480
طبليات الطريقة الأولى (مداد + عمود)	24 طبلية × 480 سم
طبليات الطريقة الثانية (3 أعمدة)	19 طبلية × 320 سم
إجمالي الطبليات 5×22.5	43
إجمالي قطع 5×7	89
قائمة تقطيع 5×7	600سم×4 | 400سم×6 | 376سم×1 | 289سم×58 | 200سم×6 | 160سم×2 | 130سم×2 | 100سم×1 | 90سم×1
	75سم×2 | 70سم×1 | 65سم×3 | 50سم×2
ألواح تلبيس 2.5 سم	177 لوح × 400 سم (مجموع الصفوف 677.6 م، 16 وجه)
أسمنت بورد 12 مم (122×244)	16 لوح (داخل دورات المياه)
العزل	97 لوح فوم صخري 80
الصبة	يجهزها العميل — 20 سم، مفرغة تحت دورات المياه

مراجعة التصميم مقابل قواعد المصنع

النوع	البند	التفاصيل	المقترح
ملاحظة	تعديل الارتفاع	الارتفاع المطلوب 290 سم ← المعتمد 299 سم.	بتغطية صافية 18.67 سم للوح، الارتفاع 299 سم = 16 صف كامل بدون تقطيع آخر لوح (يوفر وقت العامل ويعطي شكل أنظف).
ملاحظة	بحر المدادات	أطول بحر بدون جدار داخلي يحمل المداد: جهة أ: 306 سم، جهة ب: 306 سم. يحتاج رقم المصنع لأقصى بحر مسموح لتحديد المدادات اللي تُقوّى 20×5.	
ملاحظة	الصبة والدرج	ارتفاع الصبة 45 سم ← 3 درجة بقائمة 15.0 سم.	
ملاحظة	مناسيب رؤوس الفتحات	رؤوس الأبواب والشبابيك على مناسيب مختلفة: 210، 220، 230، 260 سم.	
سؤال	يحتاج تأكيد	أقصى بحر للمداد بدون جدار داخلي قبل إضافة تقوية 7×5 (مداد 20×5)؟	
سؤال	يحتاج تأكيد	التغطية الصافية للوح التلبيس بعد التعشيق (مستنتجة مؤقتاً 18.67 سم من 280/15)؟	
سؤال	يحتاج تأكيد	هل يوضع أعمدة قصيرة فوق رأس الشباك/الباب إلى العلوي؟	
سؤال	يحتاج تأكيد	مكان الوصلة في القاعدة والعلوي إذا الجدار أطول من الطبلية؟	