
المسقط الأفقي مع الفرش

الأبعاد بالسنتيمتر - الجدران: قوائم 7×5 + تلبيس 2.5 من الجهتين (12 سم)

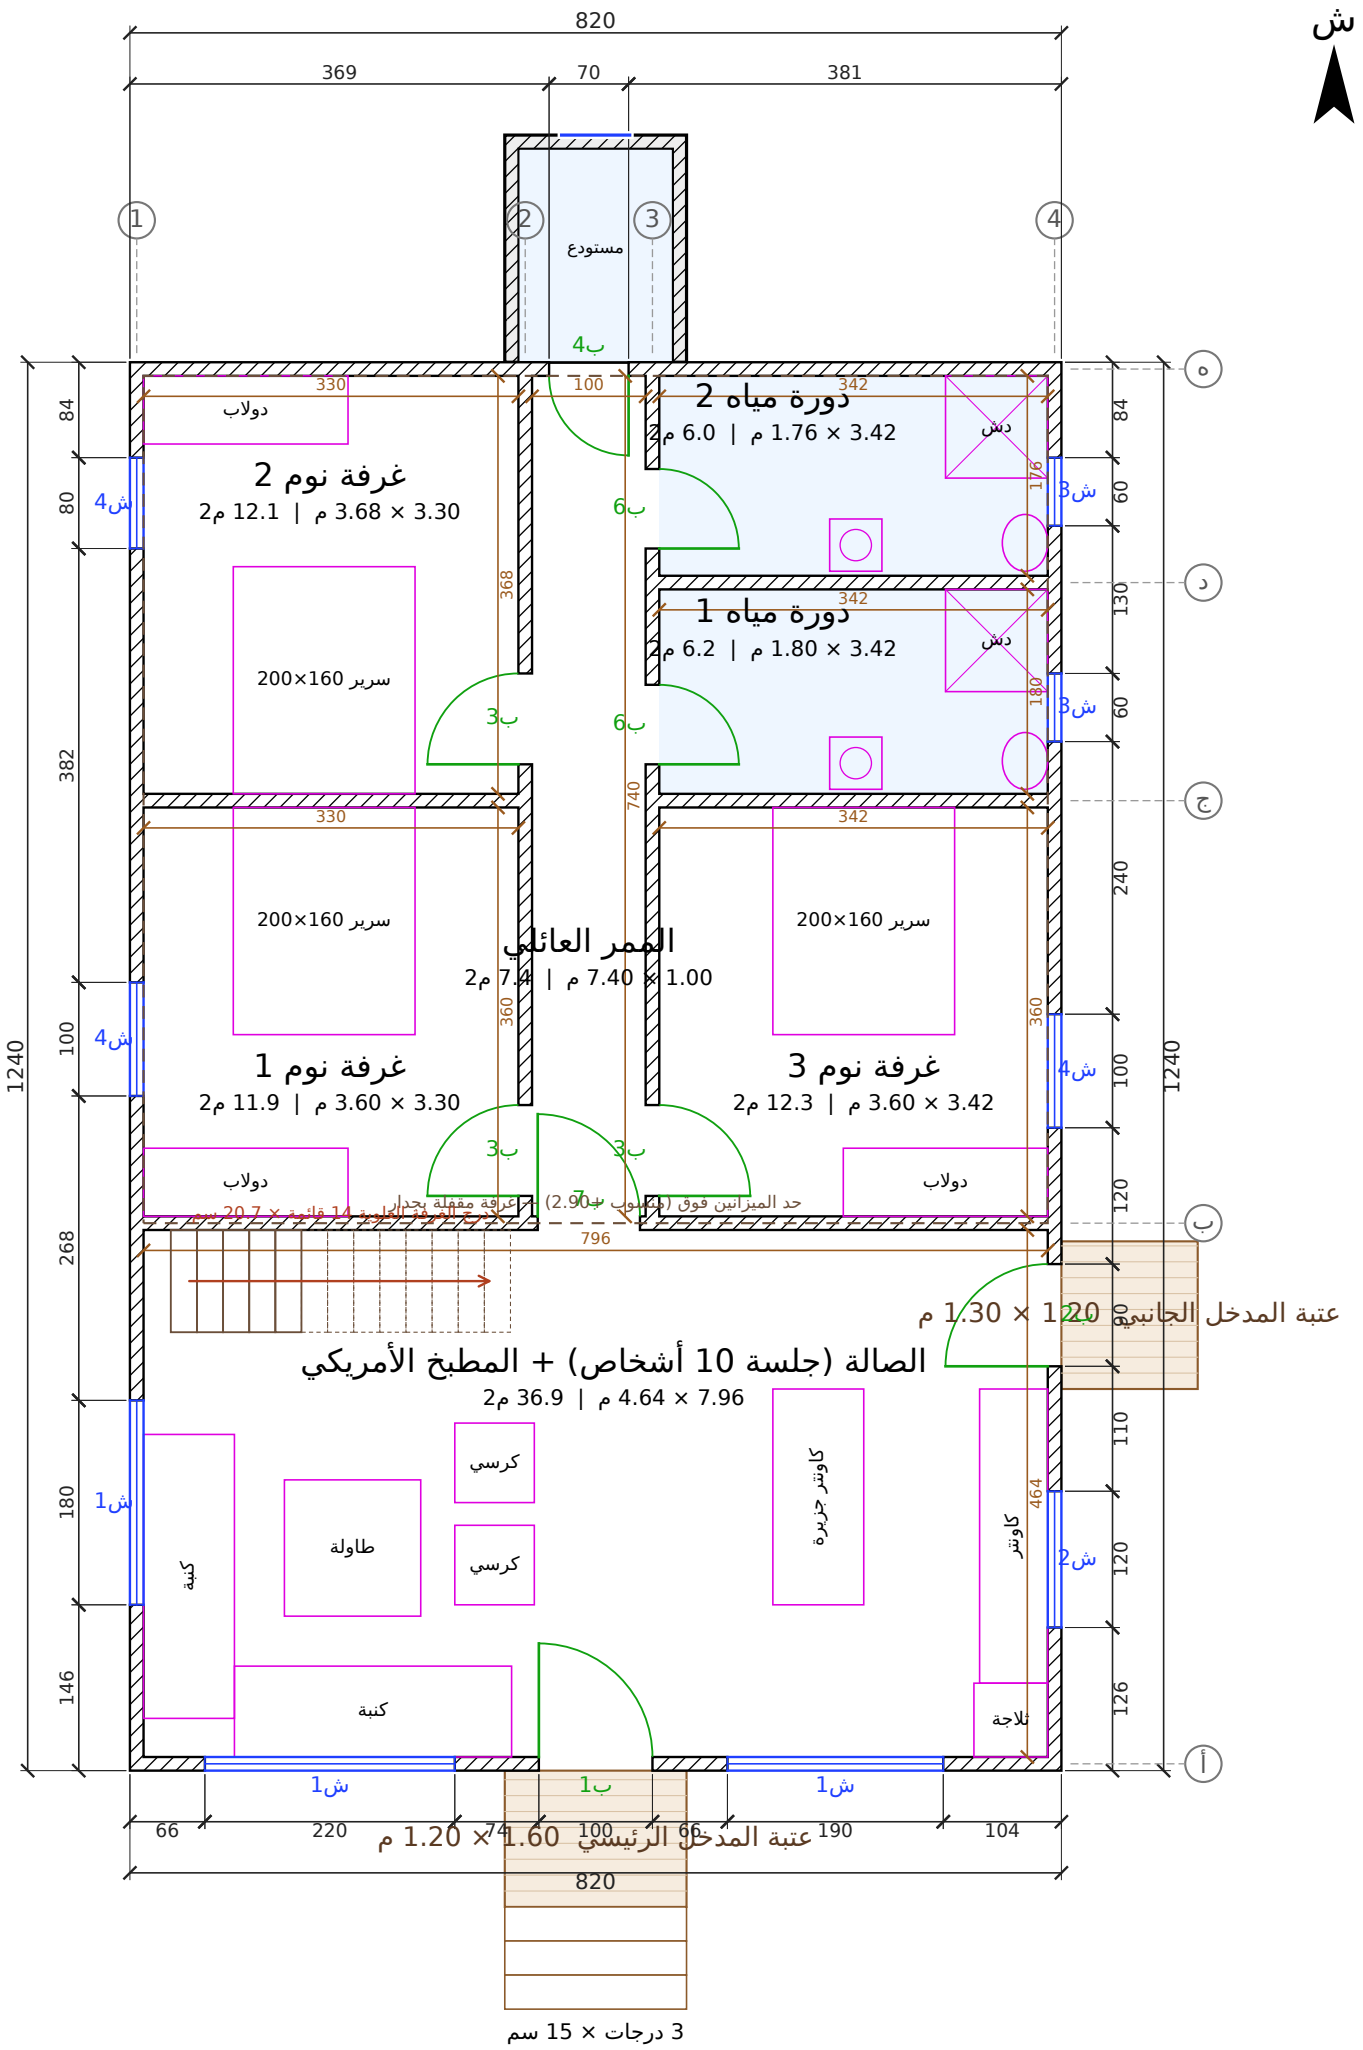


المشروع / العميل	عنوان اللوحة	المقياس	التاريخ	رقم اللوحة
كوخ مزرعة — 3 غرف + غرفة علوية — 12.40 × 8.20 **عميل — مزرعة الرياض**	**المسقط الأفقي**	**1:50**	**2026-10-20**	**A-01 (1/10)**

مصنع وتد الأخشاب
Watad Wood Factory


مسقط الميزانين (نص الدور) — غرفة النوم

منسوب أرضية الميزانين +2.90 | الأبعاد بالسنتيمتر

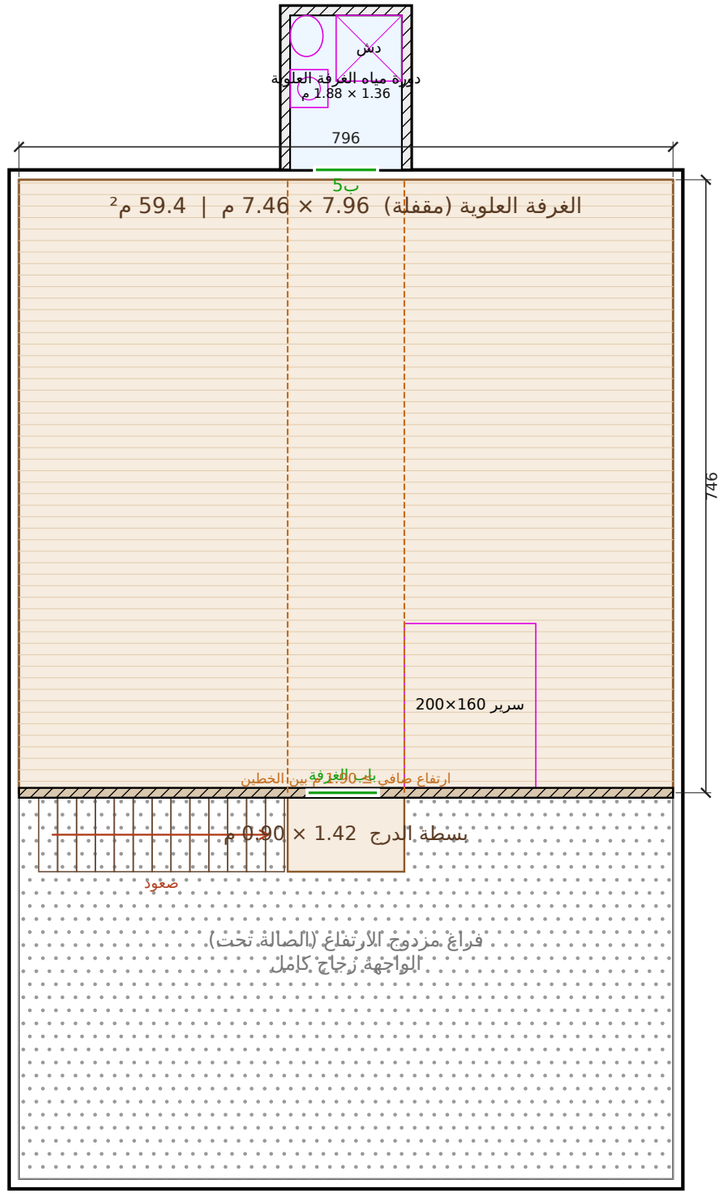


المشروع / العميل	عنوان اللوحة	المقياس	التاريخ	رقم اللوحة
كوخ مزرعة — 3 غرف + غرفة علوية — 12.40 × 8.20 **عميل — مزرعة الرياض**	**مسقط الميزانين**	**1:50**	**2026-10-20**	**A-02 (2/10)**

مصنع وتد الأخشاب
Watad Wood Factory

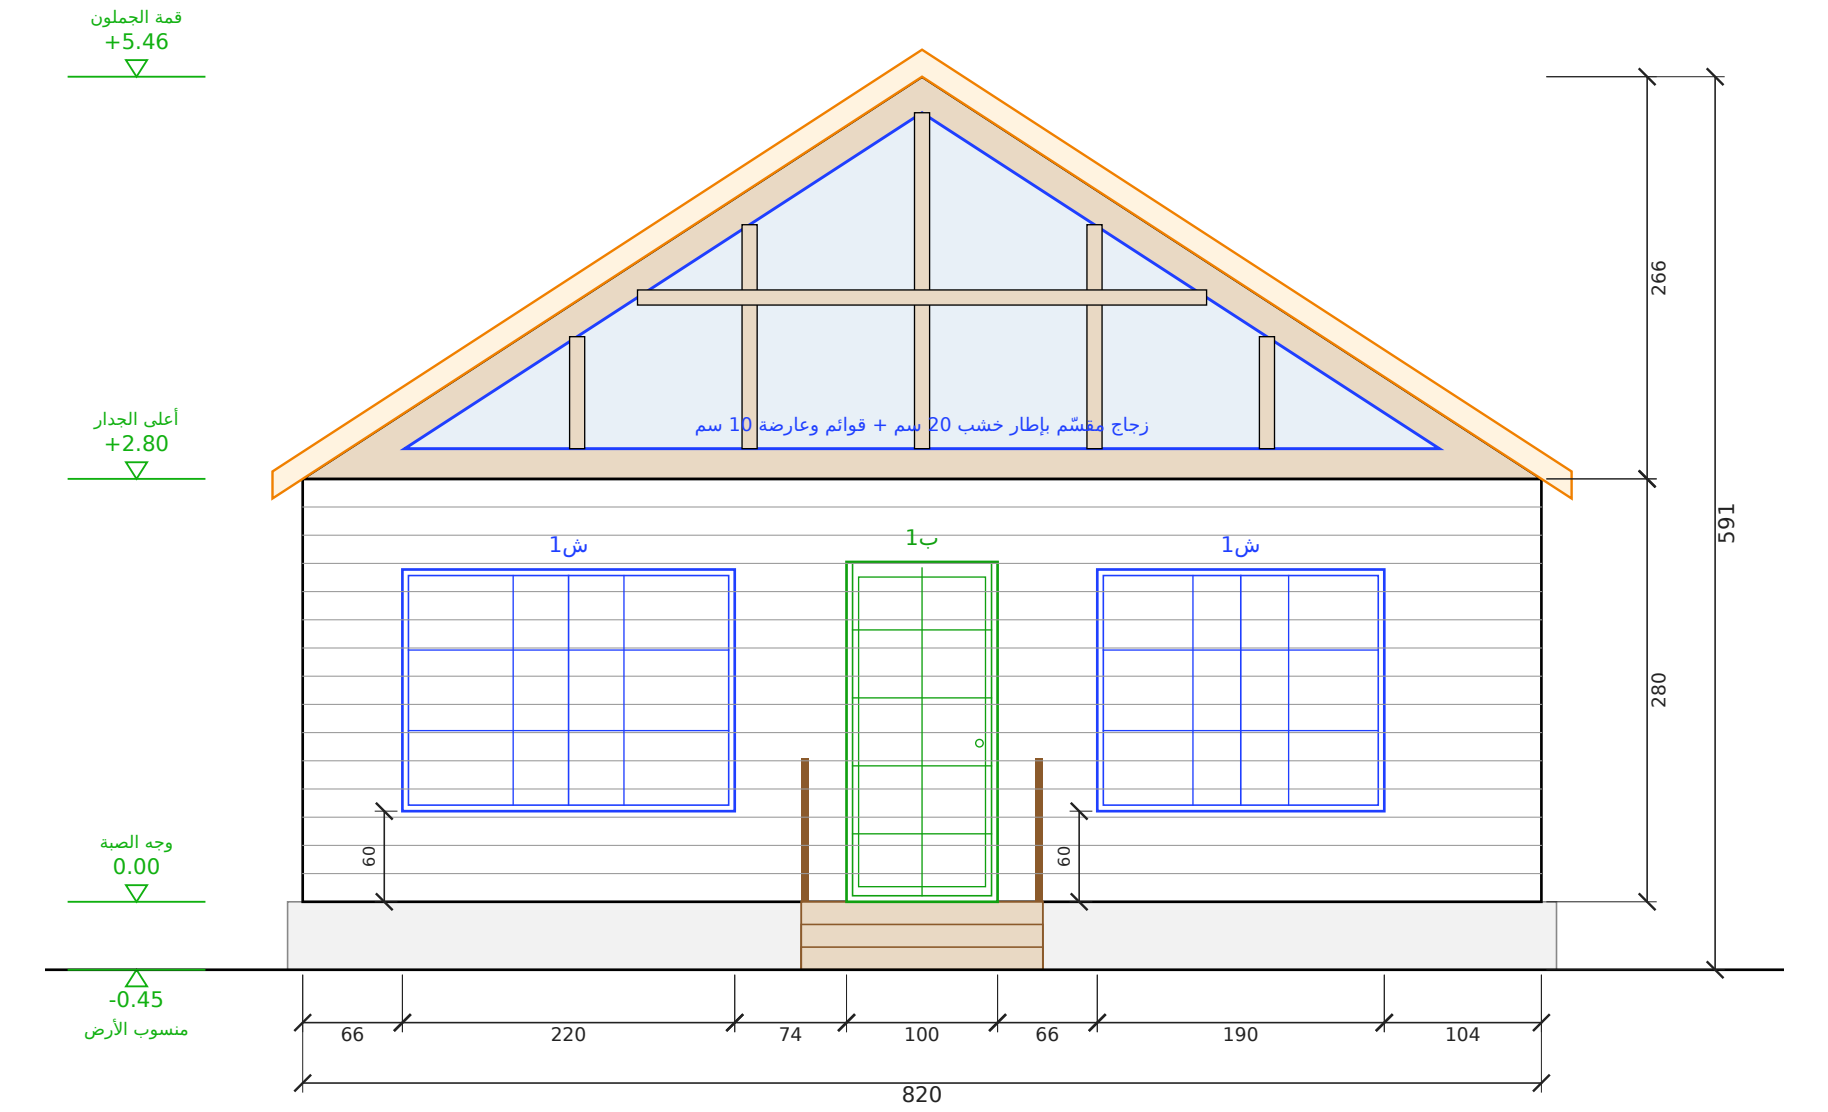

الواجهة الأمامية

مقياس 1:50 | الوحدة: سم

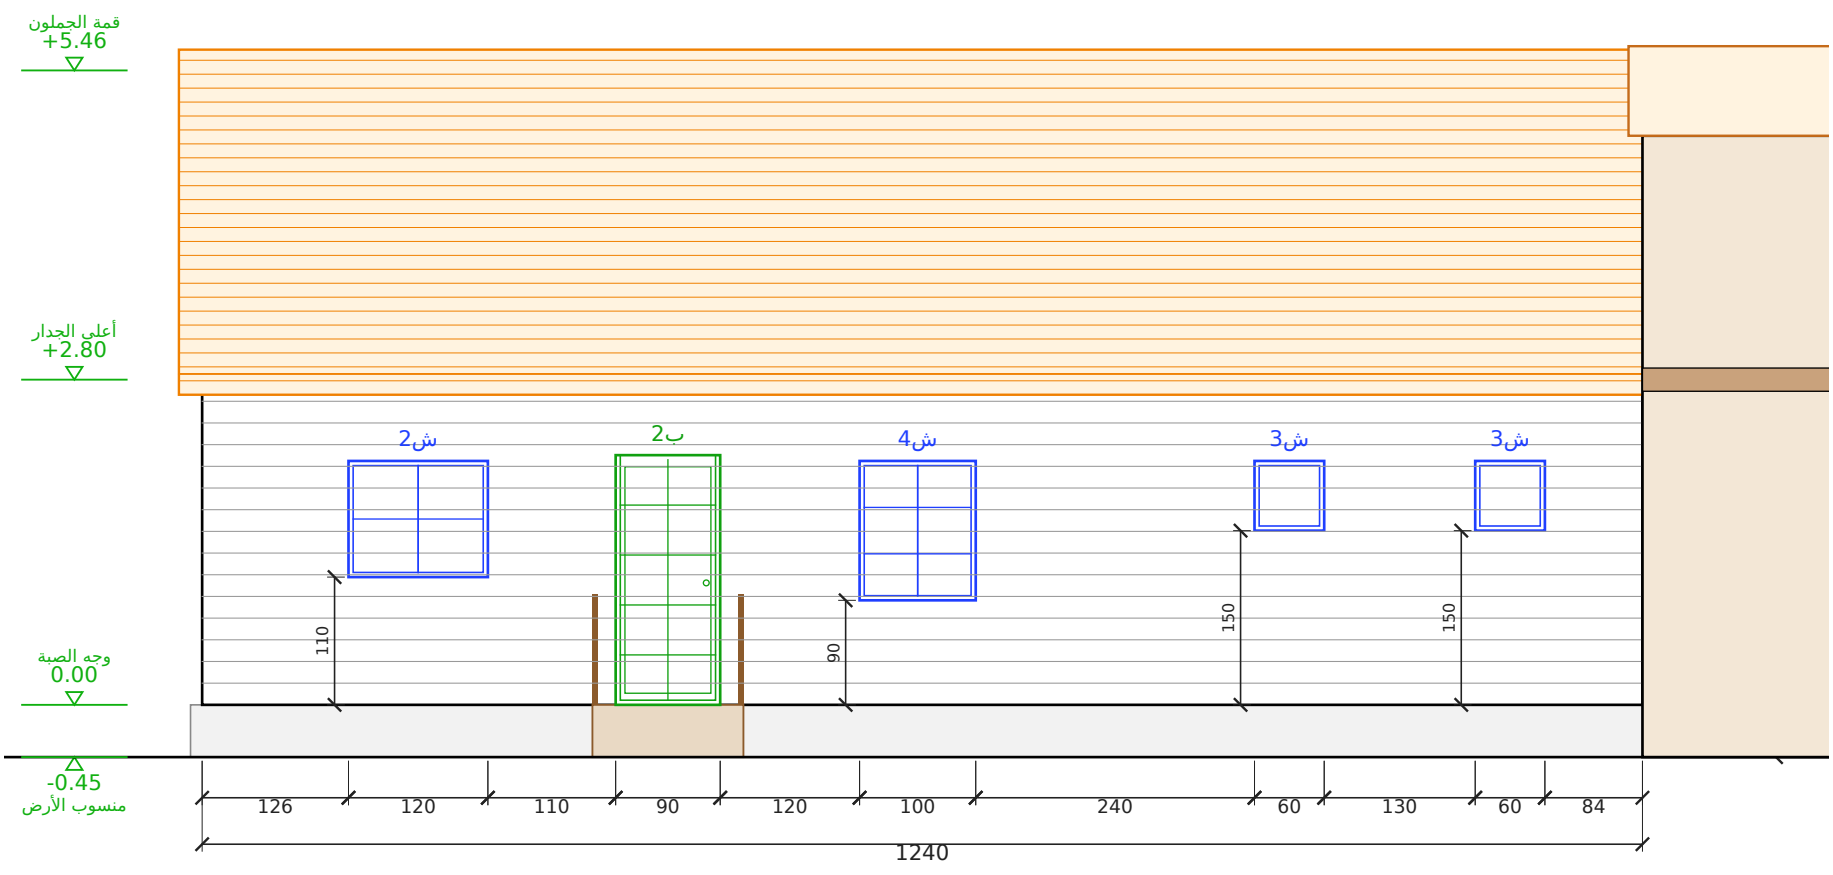


الواجهة الشرقية

مقياس 1:50 | الوحدة: سم


المشروع / العميل	عنوان اللوحة	المقياس	التاريخ	رقم اللوحة
كوخ مزرعة — 3 غرف + غرفة علوية — 12.40 × 8.20 **عميل — مزرعة الرياض**	**الواجهة الأمامية والواجهة الشرقية**	**1:50**	**2026-10-20**	**A-03 (3/10)**

مصنع وتد الأخشاب
Watad Wood Factory

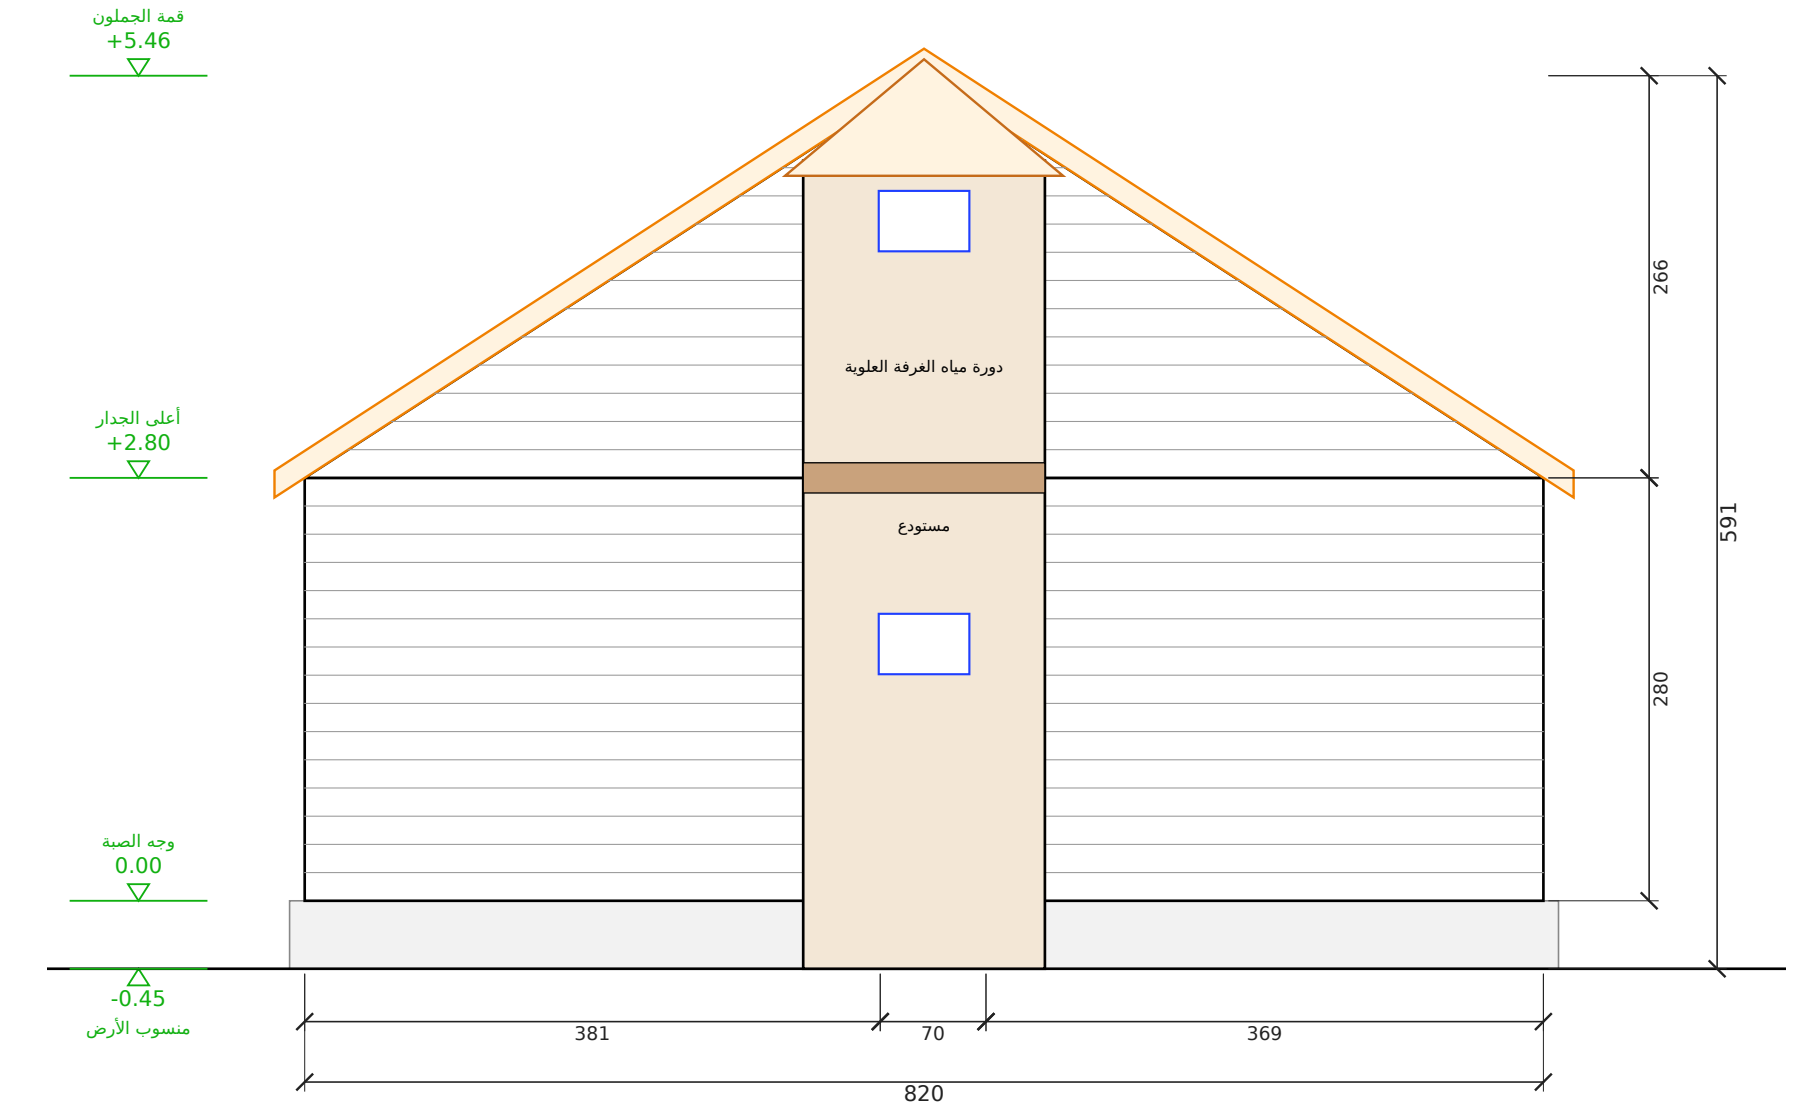

الواجهة الخلفية

مقياس 1:50 | الوحدة: سم

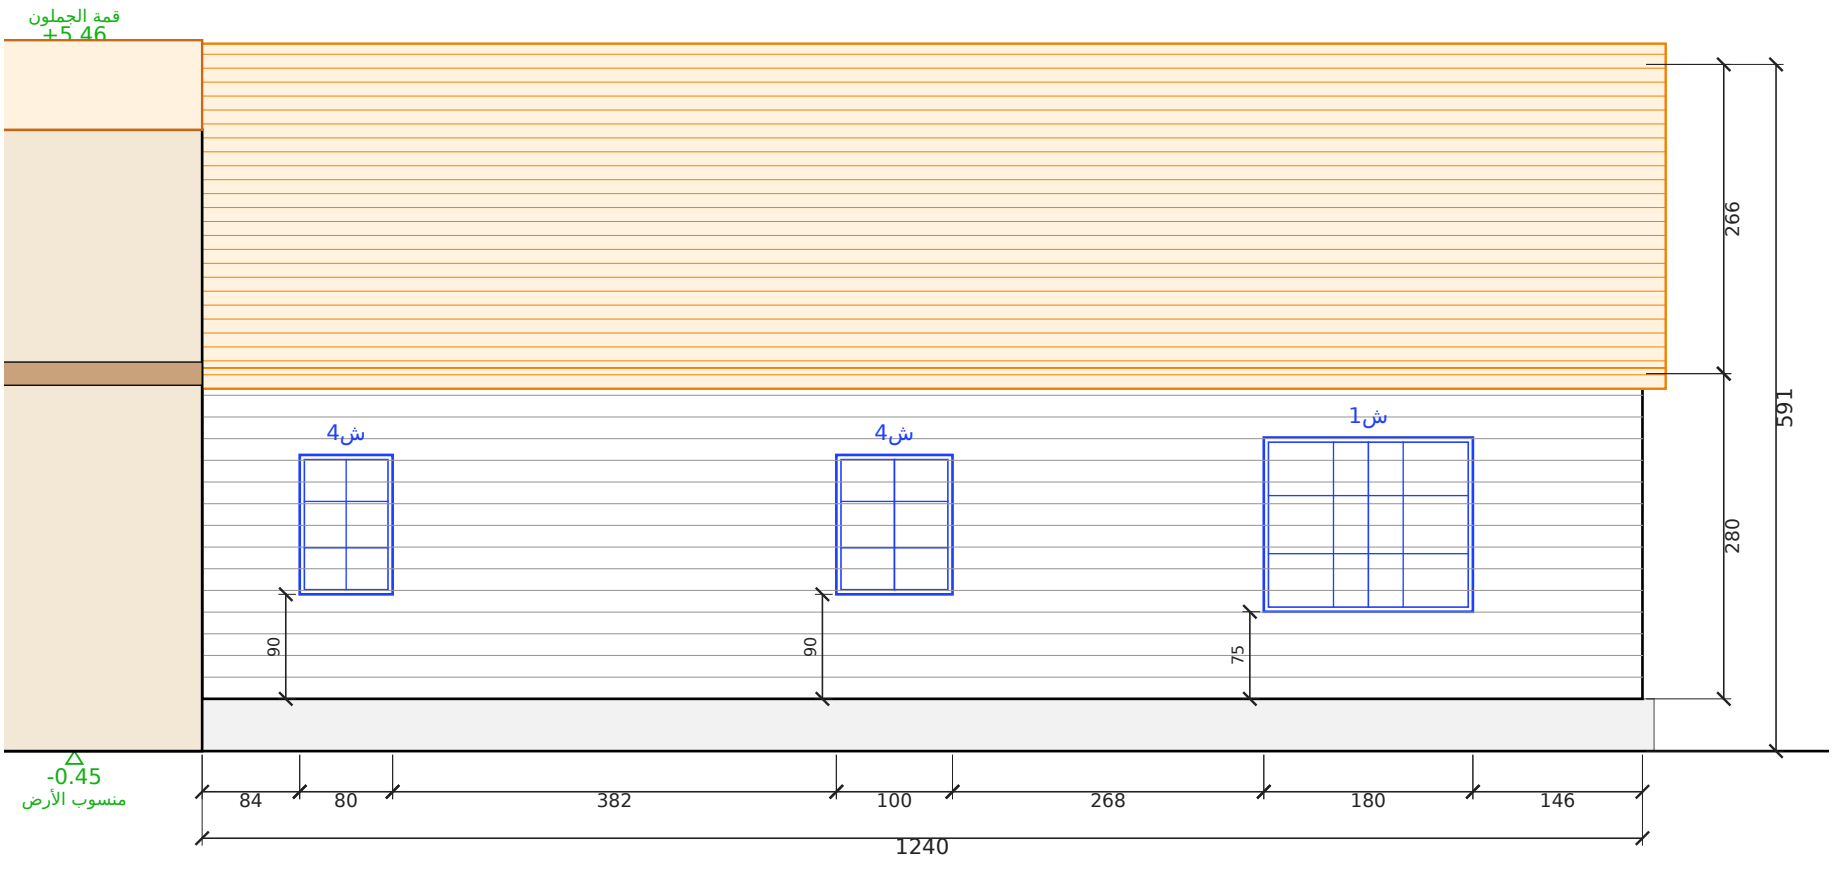


الواجهة الغربية

مقياس 1:50 | الوحدة: سم


المشروع / العميل	عنوان اللوحة	المقياس	التاريخ	رقم اللوحة
كوخ مزرعة — 3 غرف + غرفة علوية — 12.40 × 8.20 **عميل — مزرعة الرياض**	**الواجهة الخلفية والواجهة الغربية**	**1:50**	**2026-10-20**	**A-04 (4/10)**

مصنع وتد الأخشاب
Watad Wood Factory


مسقط السقف (جملون)
رفرف 20 سم من كل جهة | مقياس 1:50

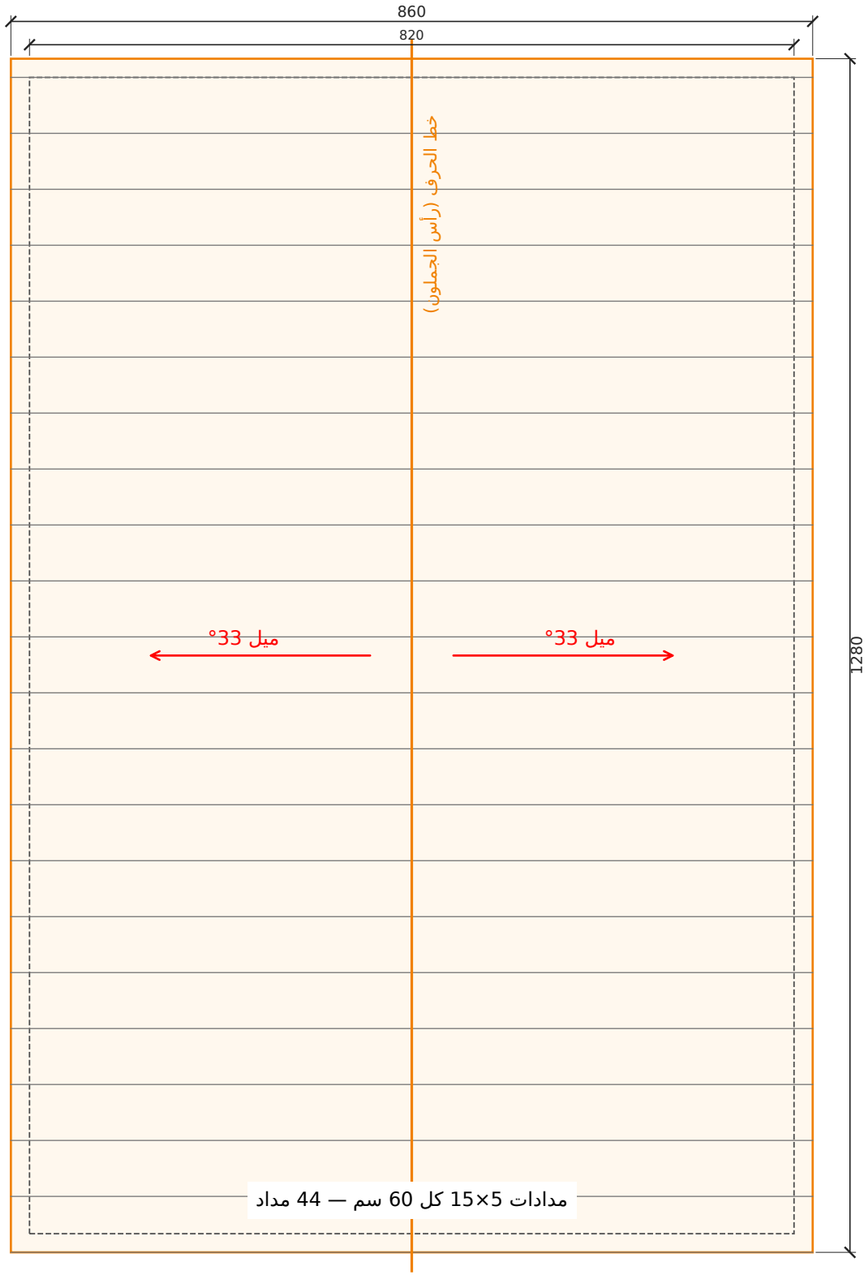

قطاع عرضي أ-أ
مقياس 1:50 | الوحدة: سم

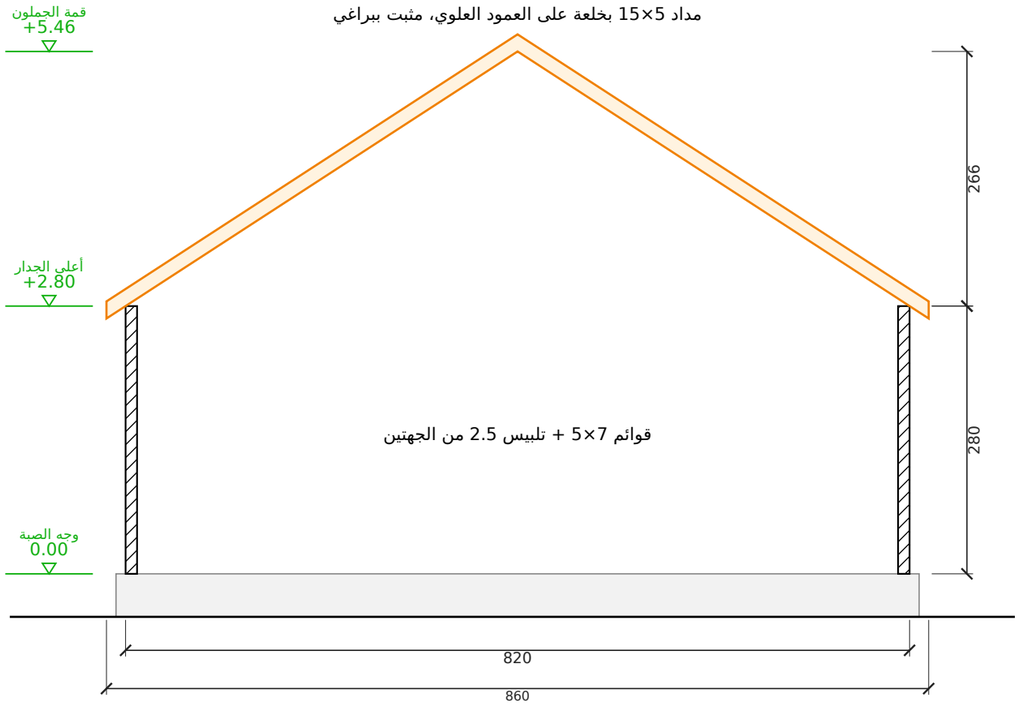

تفصيلة جلوس المداد على العلوي (1:5)

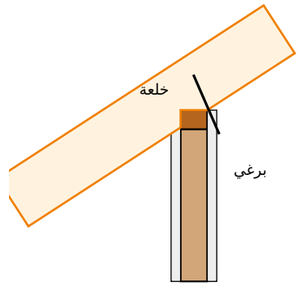

علوي 7×5 على قائم 7×5

المشروع / العميل	عنوان اللوحة	المقياس	التاريخ	رقم اللوحة
كوخ مزرعة — 3 غرف + غرفة علوية — 12.40 × 8.20 **عميل — مزرعة الرياض**	**مسقط السقف والقطاع**	**1:50**	**2026-10-20**	**A-05 (5/10)**

مصنع وتد الأخشاب
Watad Wood Factory

جدول مقاسات الأبواب والشبابيك
مقاس الفتحة الصافي في الجدار - الوحدة: سم

الرمز	النوع	العرض (سم)	الارتفاع (سم)	ارتفاع الجلسة (سم)	العدد	الموقع
ب1	باب	100	225	-	1	الأمامية
ب2	باب	90	215	-	1	الشرقية
ب3	باب	80	210	-	3	غرفة 1 - غرفة 2 - غرفة 3
ب4	باب	70	205	-	1	الخلفية
ب5	باب	70	200	-	1	الخلفية
ب6	باب	70	210	-	2	دورة مياه 1 - دورة مياه 2
ب7	باب	90	210	-	1	باب الممر العائلي
ش1	شباك	220	160	60	1	الأمامية
ش1	شباك	190	160	60	1	الأمامية
ش1	شباك	180	150	75	1	الغربية
ش2	شباك	120	100	110	1	الشرقية
ش3	شباك	60	60	150	2	الشرقية 2
ش4	شباك	100	120	90	2	الشرقية - الغربية
ش4	شباك	80	120	90	1	الغربية

الإجمالي: أبواب 10 - شبابيك 9

جدول المساحات وبيانات المشروع

بيانات المشروع

البند	البيان
المشروع	كوخ مزرعة — 3 غرف + غرفة علوية — 8.20 × 12.40
العميل	عميل — مزرعة الرياض
الموقع	الرياض (مزرعة)
الاستخدام	سكن
التاريخ	2026-10-20
نظام البناء	هيكل خشب 5×7 + تلبيس 2.5 سم من الجهتين
السقف	جملون 33° — قرميد معدني

جدول المساحات

م	الفراغ	الأبعاد (م)	المساحة (م2)
1	الصالة (جلسة 10 أشخاص) + المطبخ الأمريكي	7.96 × 4.64	36.93
2	غرفة نوم 1	3.30 × 3.60	11.88
3	غرفة نوم 2	3.30 × 3.68	12.14
4	الممر العائلي	1.00 × 7.40	7.40
5	غرفة نوم 3	3.42 × 3.60	12.31
6	دورة مياه 1	3.42 × 1.80	6.16
7	دورة مياه 2	3.42 × 1.76	6.02
	المساحة الصافية الداخلية		**92.85**
	التراس المسقوف + تراس الدور الأول	**1.60 × 1.20 × 3**	**4.76**
	المساحة الإجمالية المبنية	**8.20 × 12.40**	**101.68**

لقطات المنظور الخارجي

المنظور الأمامي




منظور أمامي من اليسار




منظور أمامي من اليمين




المنظور الخلفي

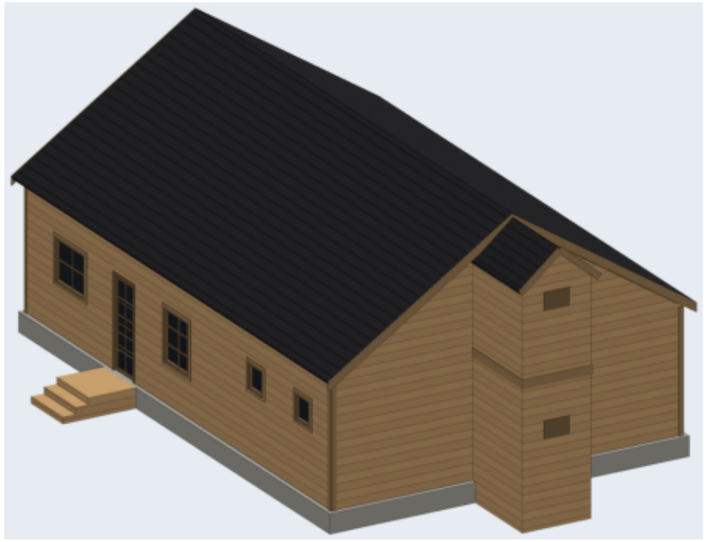

منظور خلفي من اليمين

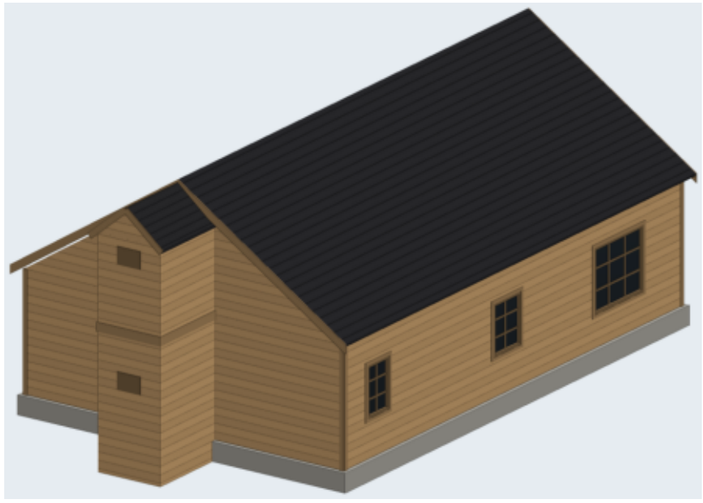

منظر علوي

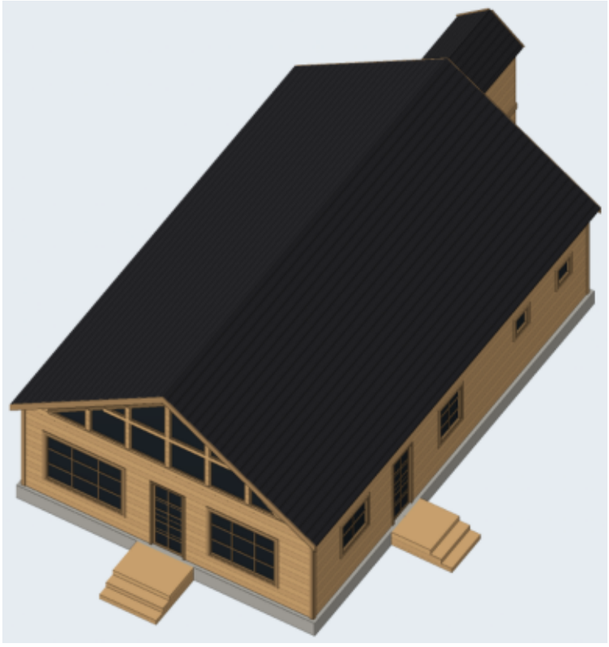


المشروع / العميل	عنوان اللوحة	المقياس	التاريخ	رقم اللوحة
كوخ مزرعة — 3 غرف + غرفة علوية — 12.40 × 8.20 **عميل — مزرعة الرياض**	**لقطات المنظور**	**—**	**2026-10-20**	**A-08 (8/10)**

مصنع وتد الأخشاب
Watad Wood Factory

المقطع العلوي بالفرش

مقطع أفقي على ارتفاع 1.90 م — توزيع الفرش ومسار الحركة

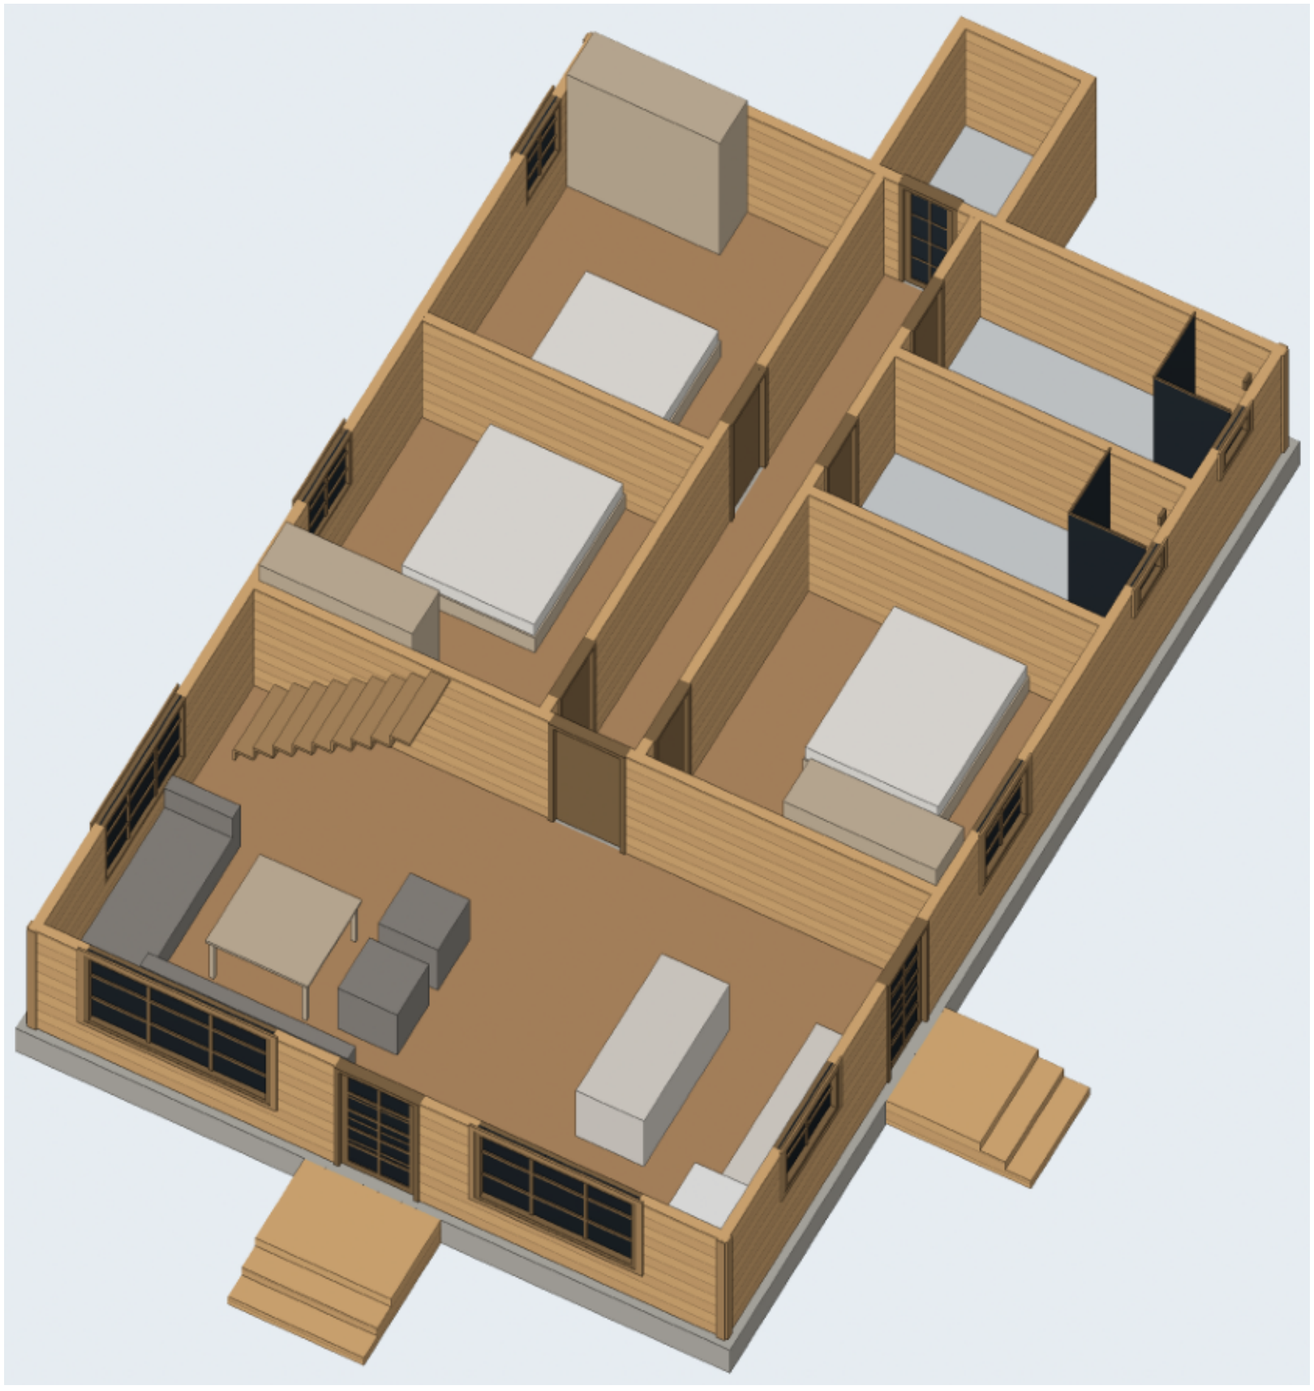

المشروع / العميل	عنوان اللوحة	المقياس	التاريخ	رقم اللوحة
كوخ مزرعة — 3 غرف + غرفة علوية — 8.20 × 12.40 **عميل — مزرعة الرياض**	**المقطع العلوي بالفرش**	**—**	**2026-10-20**	**A-09 (9/10)**

مصنع وتد الأخشاب
Watad Wood Factory

المنظور ثلاثي الأبعاد والمواد

النمط: جوزي غامق + إطارات سوداء — رندر واقعي بخامات حقيقية



جدول المواد والألوان

الخشب / الصبغة

خشب طبيعي فاتح (بدون صبغة)

القرميد

قرميد رمادي غامق

الزجاج

زجاج عاكس غامق

إطارات الشبابيك والأبواب

إطار خشب بنفس الصبغة أغمق

الكنار والزوايا

نفس الصبغة أغمق درجة


الصبة

خرسانة 45 سم


الدربزين: ألواح أفقية متقاربة (عصري)

تقسيم الشبابيك: بدون | الباب الرئيسي: زجاج بتقسيمات (فرنسي)

أنواع الدربزين المعتمدة (من مشاريع المصنع)

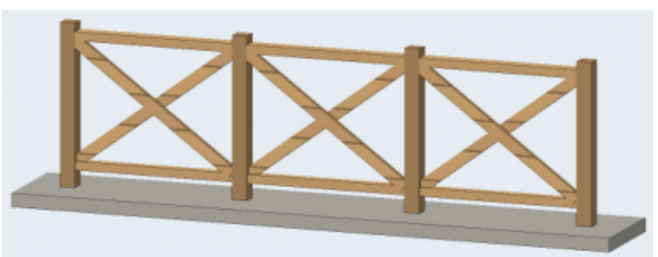

تقاطع X (صورة 5)

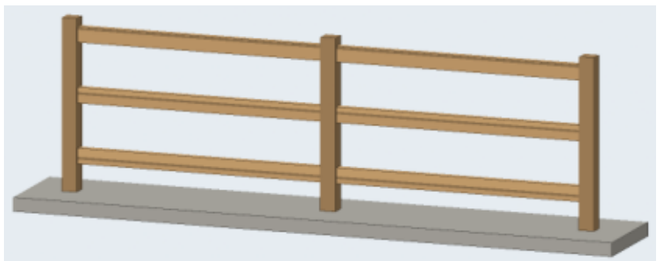

3 مرابيع أفقية (صورة 2)



قوائم رأسية متقاربة (صورة 1)

المشروع / العميل	عنوان اللوحة	المقياس	التاريخ	رقم اللوحة
كوخ مزرعة — 3 غرف + غرفة علوية — 8.20 × 12.40 **عميل — مزرعة الرياض**	**المنظور والمواد**	**—**	**2026-10-20**	**A-10 (10/10)**

مصنع وتد الأخشاب
Watad Wood Factory