

المسقط الأفقي مع الفرش

الأبعاد بالسنتيمتر - الجدران: قوائم 7×5 + تلبيس 2.5 من الجهتين (12 سم)

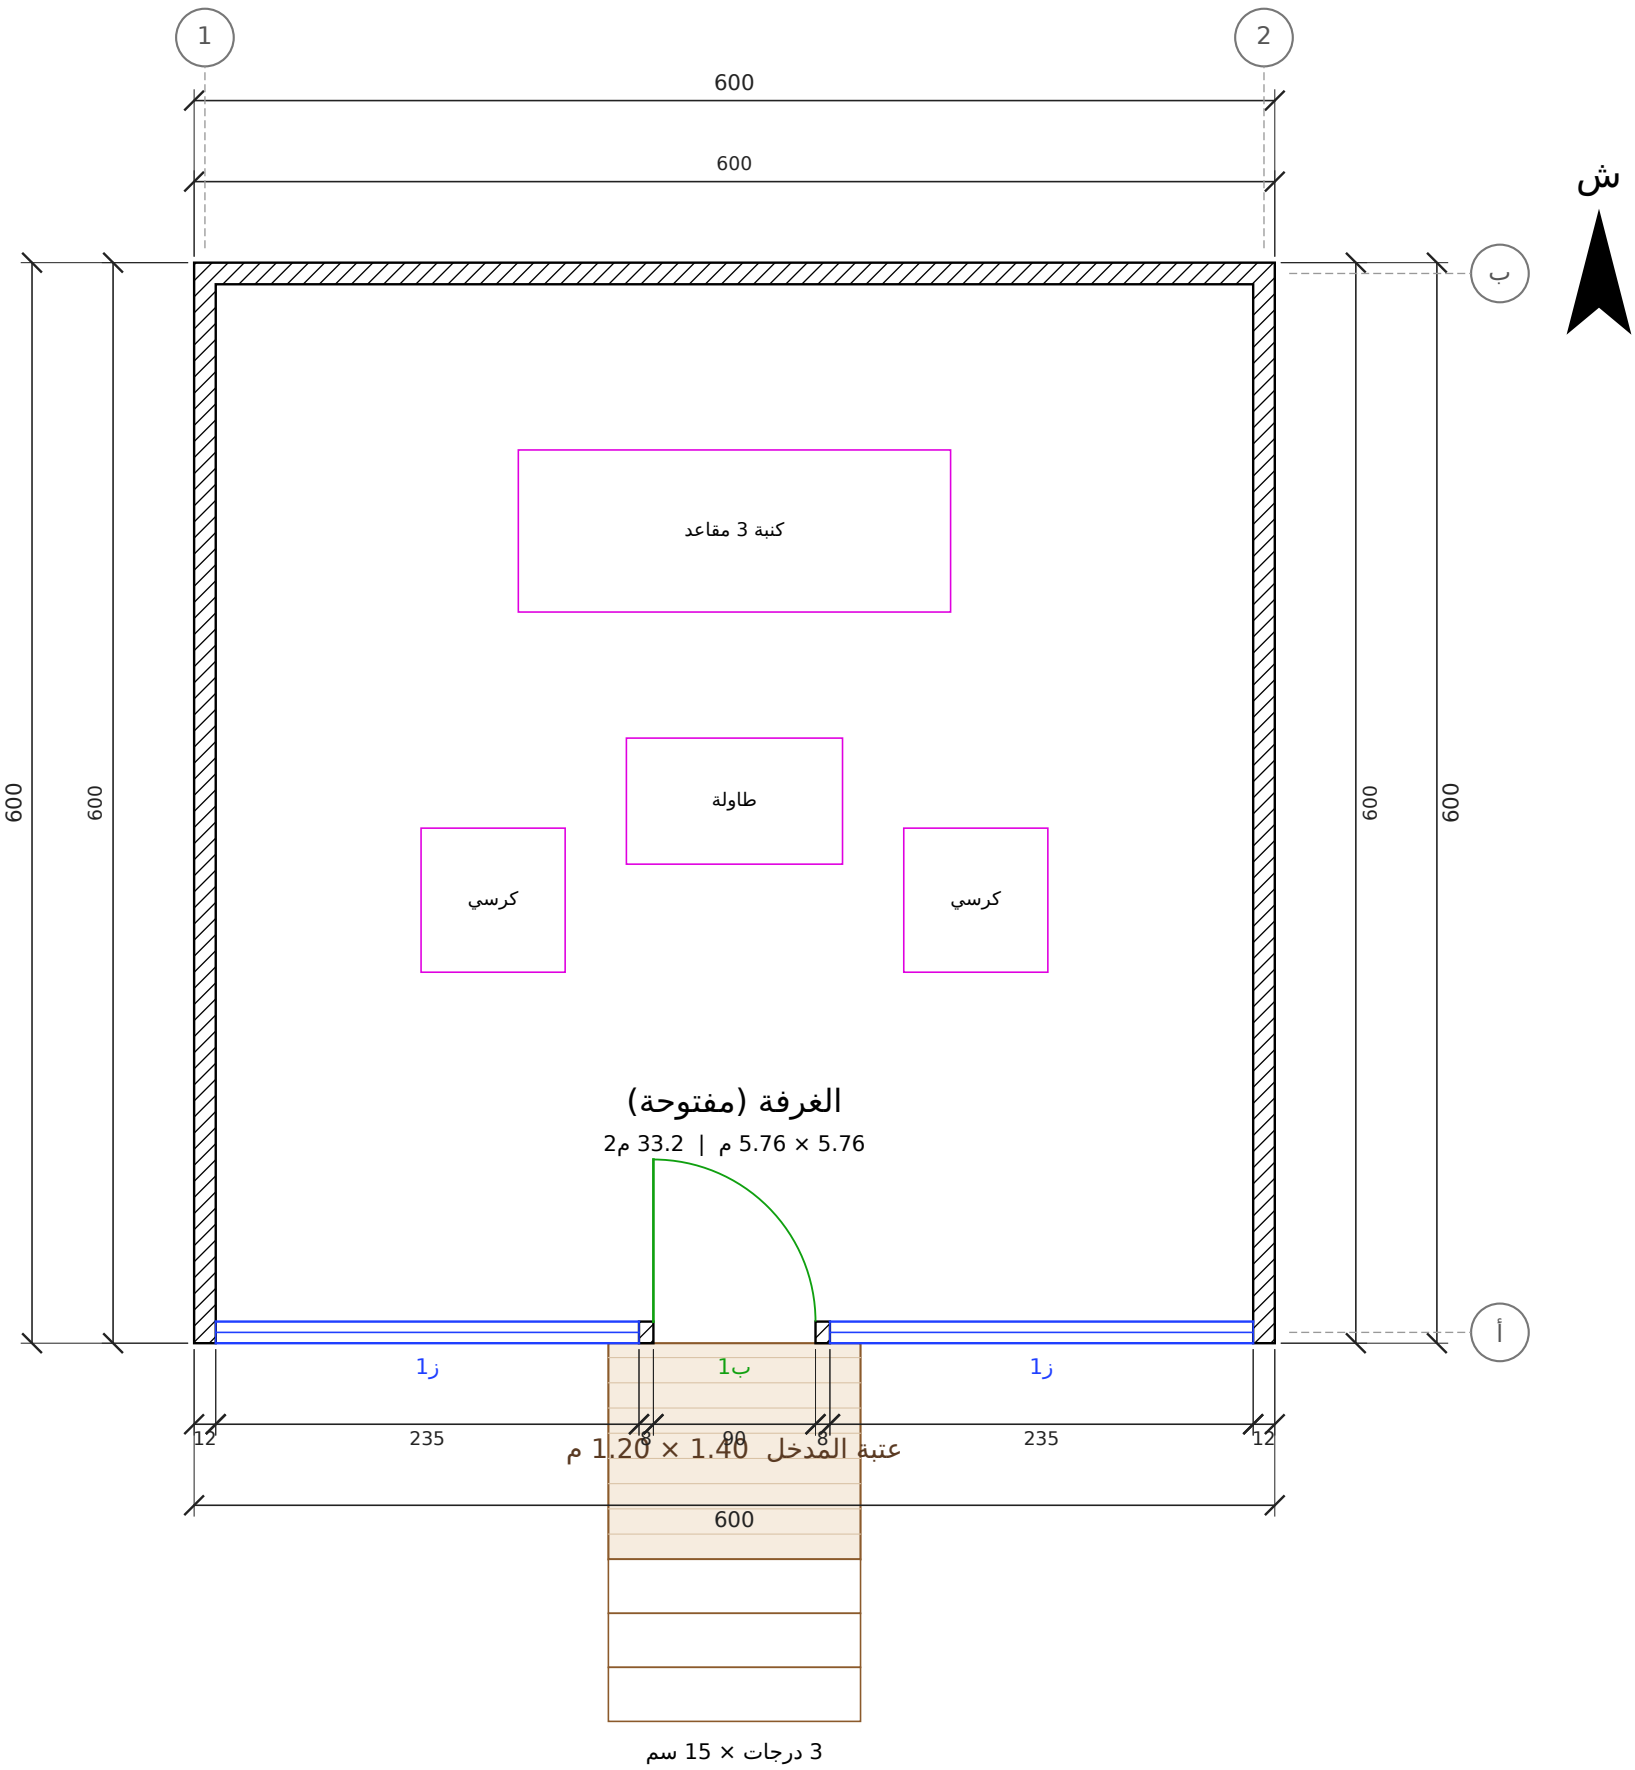


المشروع / العميل	عنوان اللوحة	المقياس	التاريخ	رقم اللوحة
مصنع وتد الأخشاب Watad Wood Factory **كوخ A-frame بواجهة زجاج كاملة — غرفة وحدة 6 × 6 = 36 م²** **عميل — A-frame 6×6**	**المسقط الأفقي**	**1:50**	**2026-10-20**	**A-01 (1/9)**

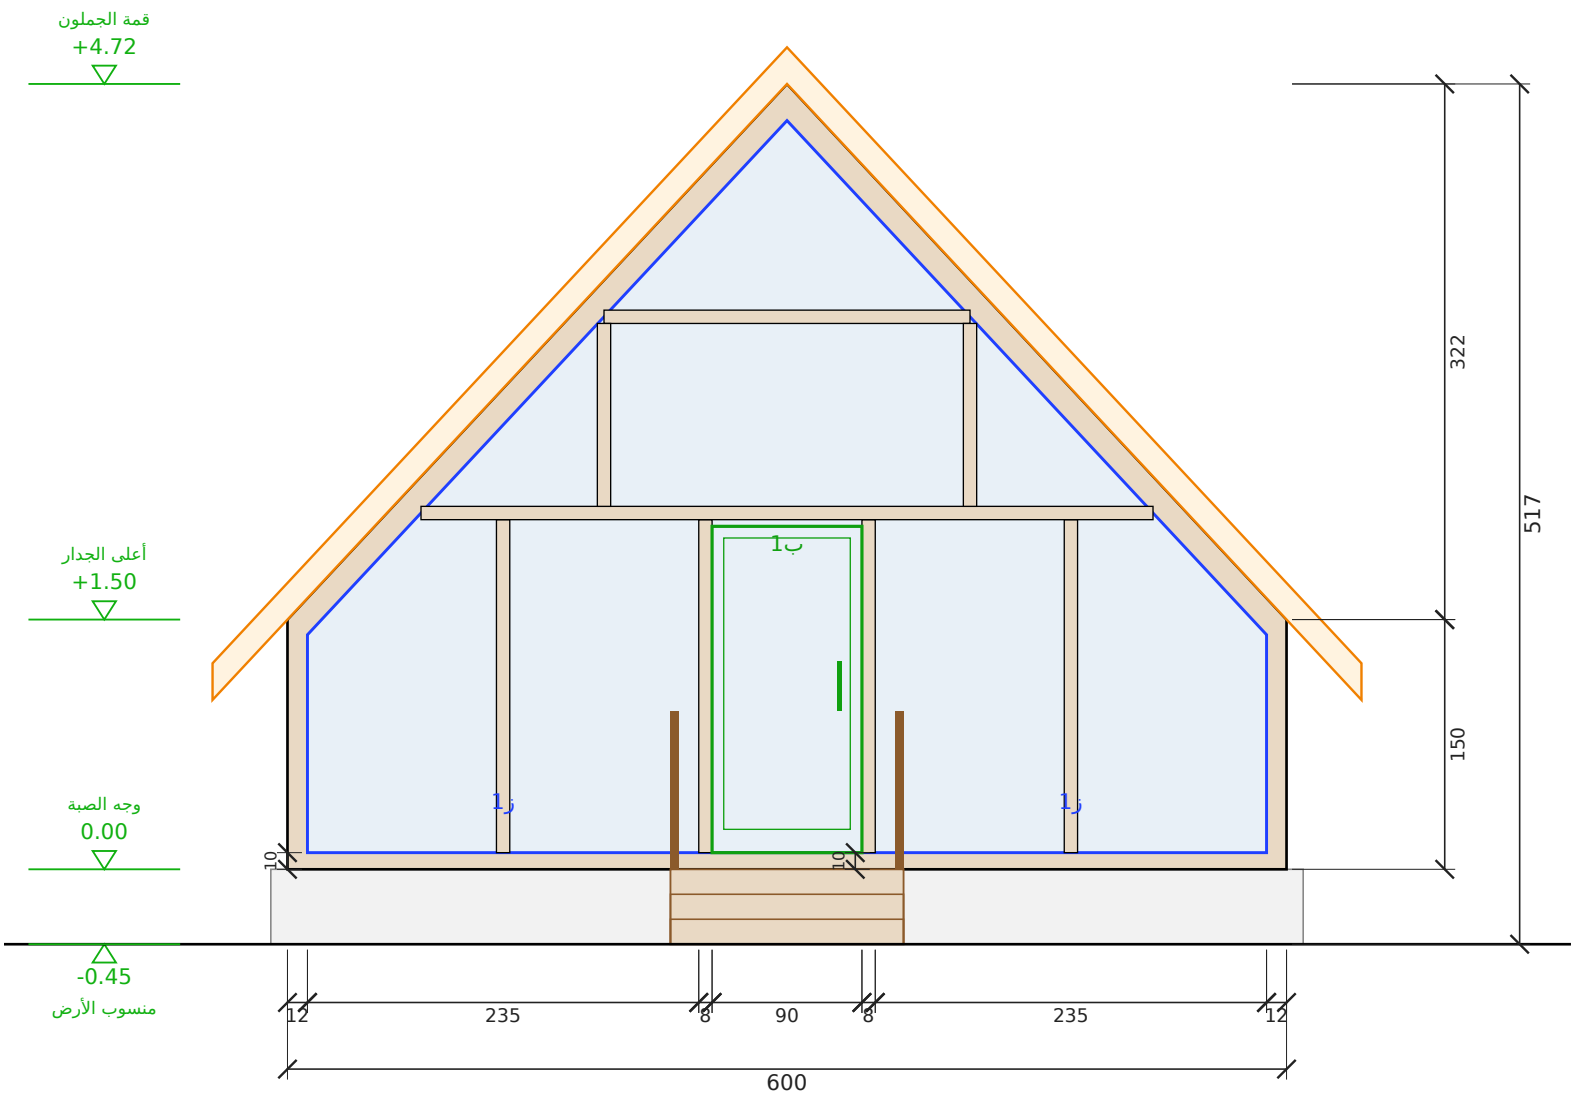

الواجهة الأمامية (زجاج كامل)

مقياس 1:50 | الوحدة: سم

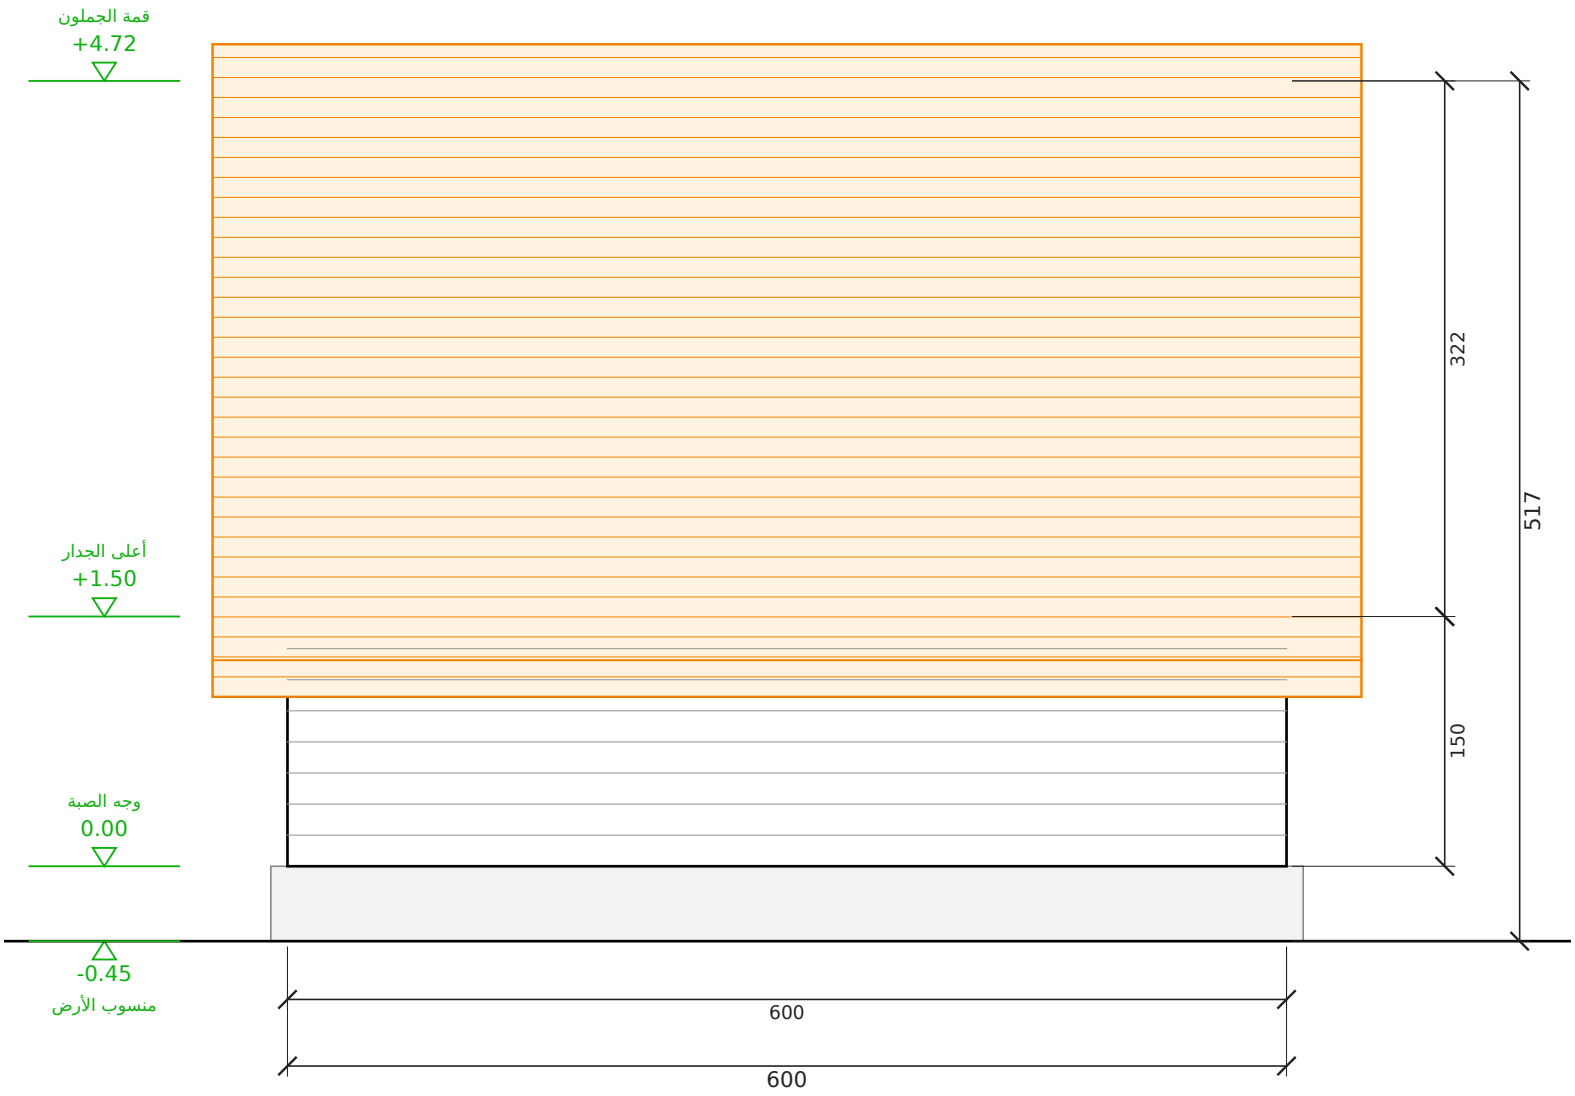


الواجهة الشرقية

مقياس 1:50 | الوحدة: سم


المشروع / العميل	عنوان اللوحة	المقياس	التاريخ	رقم اللوحة
كوخ A-frame بواجهة زجاج كاملة — غرفة وحدة 6 × 6 = 36 م² عميل — A-frame 6×6	الواجهة الأمامية (زجاج كامل) والواجهة الشرقية	1:50	2026-10-20	A-02 (2/9)

مصنع وتد الأخشاب
Watad Wood Factory

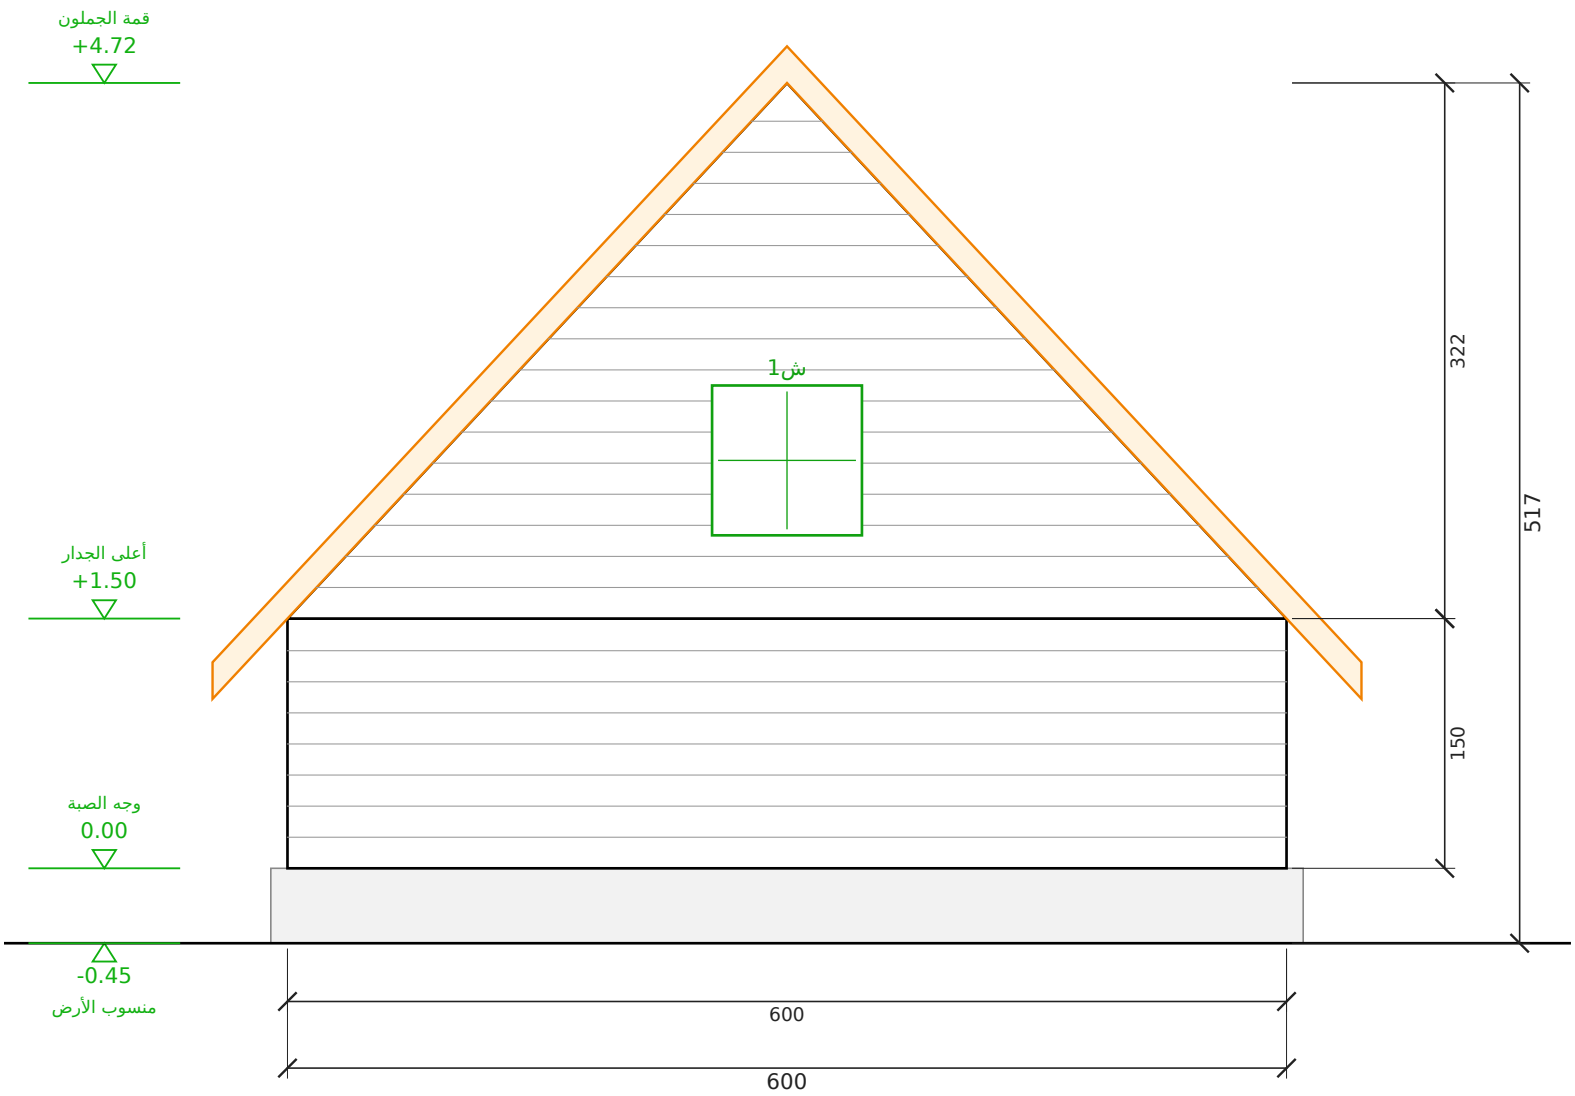

الواجهة الخلفية

مقياس 1:50 | الوحدة: سم

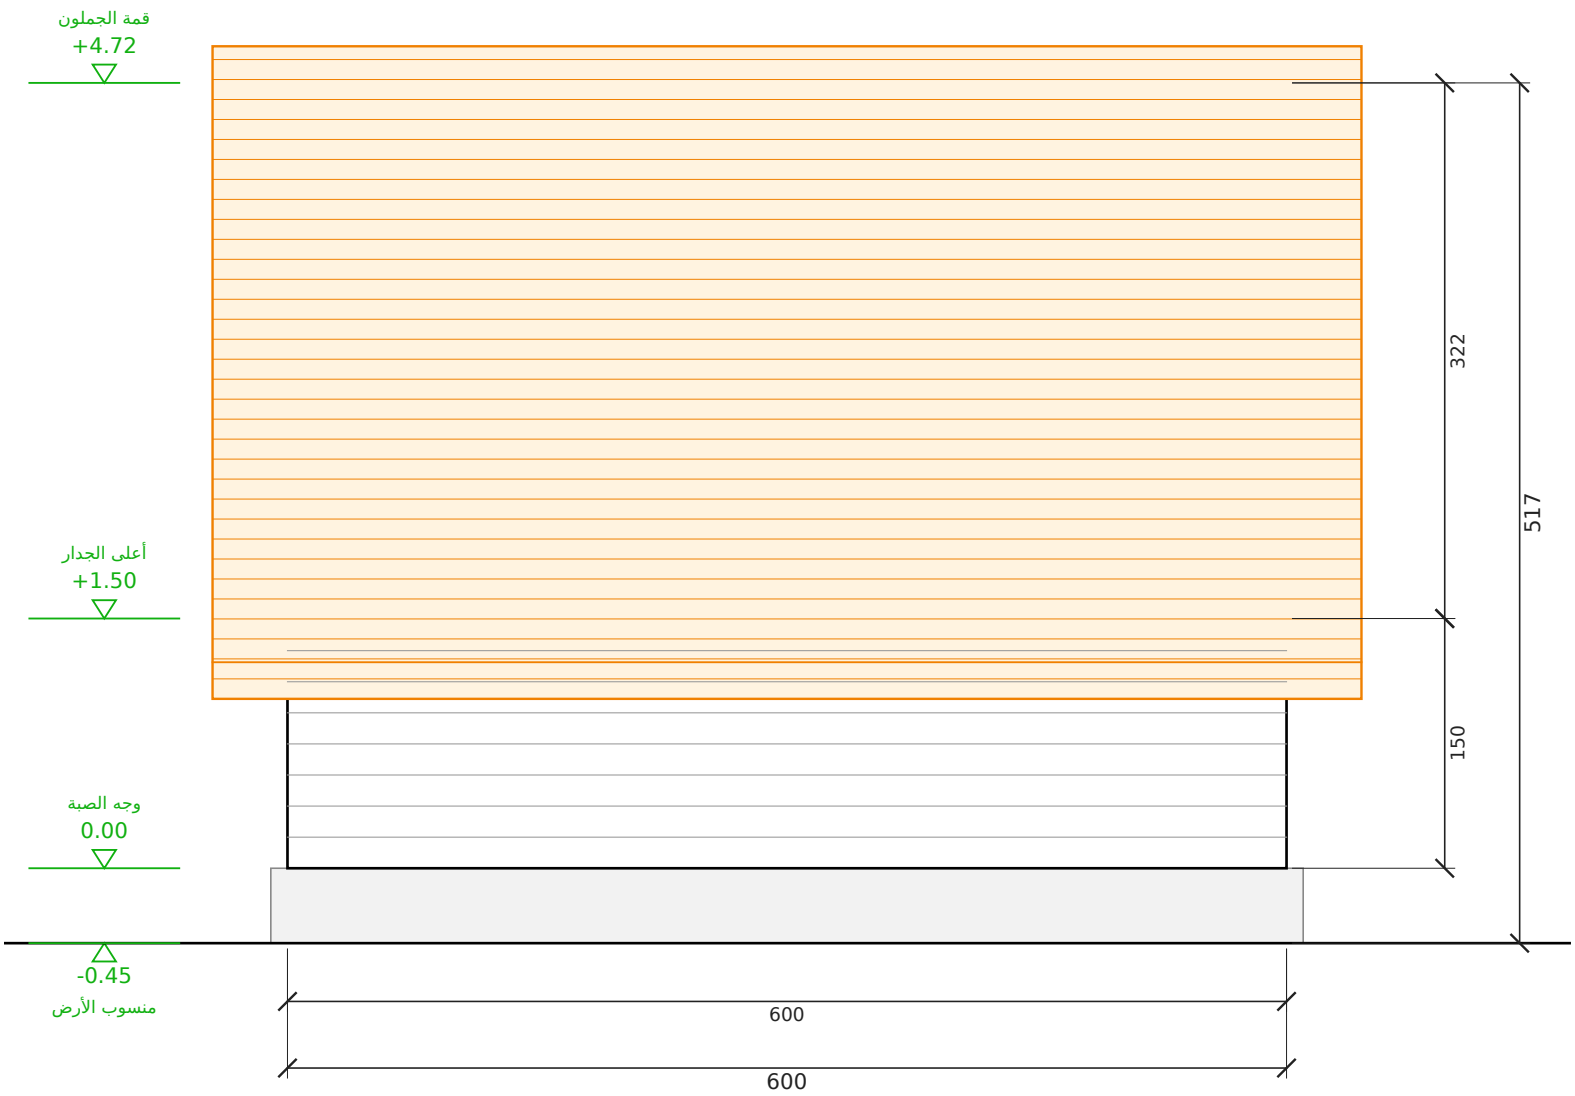


الواجهة الغربية


مقياس 1:50 | الوحدة: سم

المشروع / العميل	عنوان اللوحة	المقياس	التاريخ	رقم اللوحة
مصنع وتد الأخشاب Watad Wood Factory **كوخ A-frame بواجهة زجاج كاملة — غرفة وحدة 6 × 6 = 36 م²** **عميل — A-frame 6×6**	**الواجهة الخلفية والواجهة الغربية**	**1:50**	**2026-10-20**	**A-03 (3/9)**


مسقط السقف (جملون)
رفرف 45 سم من كل جهة | مقياس 1:50

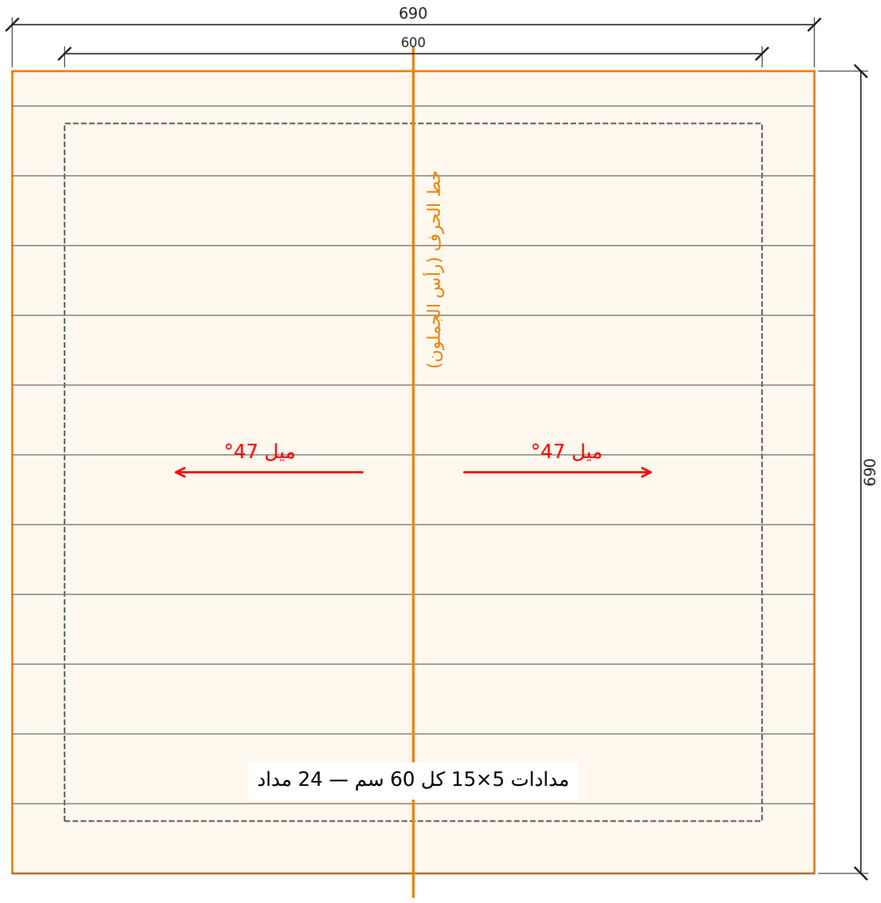

قطاع عرضي أ-أ
مقياس 1:50 | الوحدة: سم

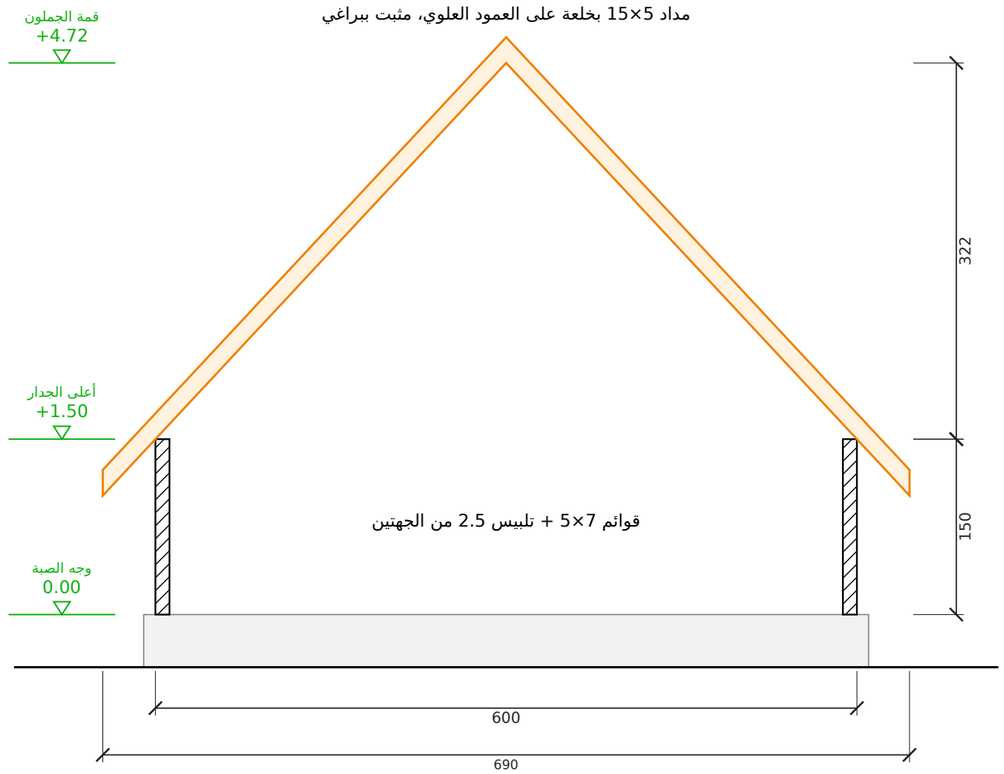

تفصيلة جلوس المداد على العلوي (1:5)

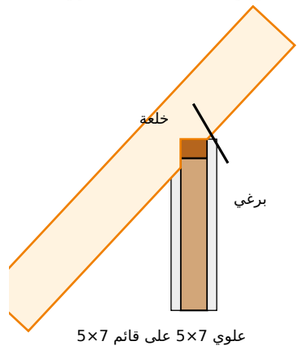

المشروع / العميل **كوخ A-frame بواجهة زجاج كاملة — غرفة وحدة 6 × 6 = 36 م²** **عميل — A-frame 6×6**	عنوان اللوحة **مسقط السقف والقطاع**	المقياس **1:50**	التاريخ **2026-10-20**	رقم اللوحة **A-04 (4/9)**

مصنع وتد الأخشاب
Watad Wood Factory

جدول مقاسات الأبواب والشبابيك
مقاس الفتحة الصافي في الجدار - الوحدة: سم

الرمز	النوع	العرض (سم)	الارتفاع (سم)	ارتفاع الجلسة (سم)	العدد	الموقع
ب1	باب	90	210	-	1	الأمامية (زجاج كامل)
ش1	باب	90	90	-	1	الخلفية
ز1	شباك	235	140	10	2	الأمامية (زجاج كامل) 2

الإجمالي: أبواب 2 - شبابيك 2

جدول المساحات وبيانات المشروع

بيانات المشروع


البند	البيان
المشروع	كوخ A-frame بواجهة زجاج كاملة — غرفة وحدة 6 × 6 = 36 م²
العميل	عميل — A-frame 6×6
الموقع	—
الاستخدام	استراحة / جلسة
التاريخ	2026-10-20
نظام البناء	هيكل خشب 5×7 + تلبيس 2.5 سم من الجهتين
السقف	جملون 47° — قرميد معدني

جدول المساحات

م	الفراغ	الأبعاد (م)	المساحة (م2)
1	الغرفة (مفتوحة)	5.76 × 5.76	33.18
	المساحة الصافية الداخلية		**33.18**
	عتبة المدخل	**1.40 × 1.20**	**1.68**
	المساحة الإجمالية المبنية	**6.00 × 6.00**	**36.00**

لقطات المنظور الخارجي

المنظور الأمامي

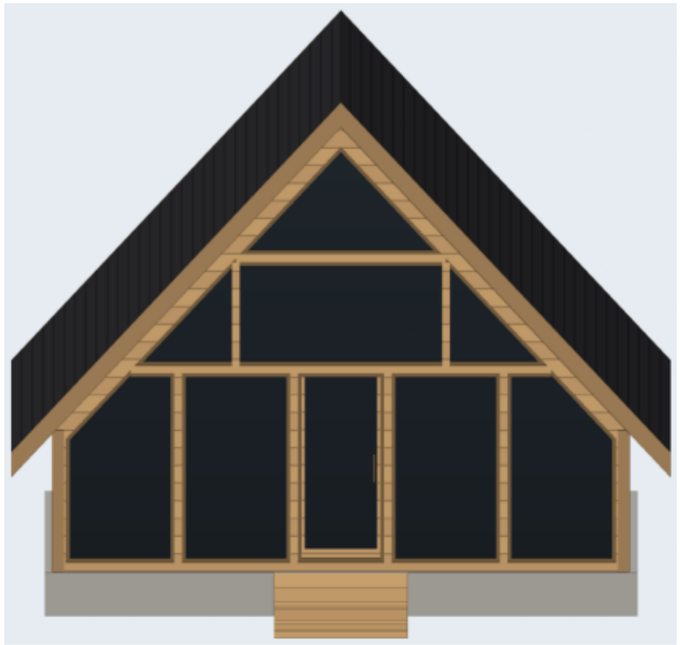

منظور أمامي من اليسار




منظور أمامي من اليمين




المنظور الخلفي



منظور خلفي من اليمين

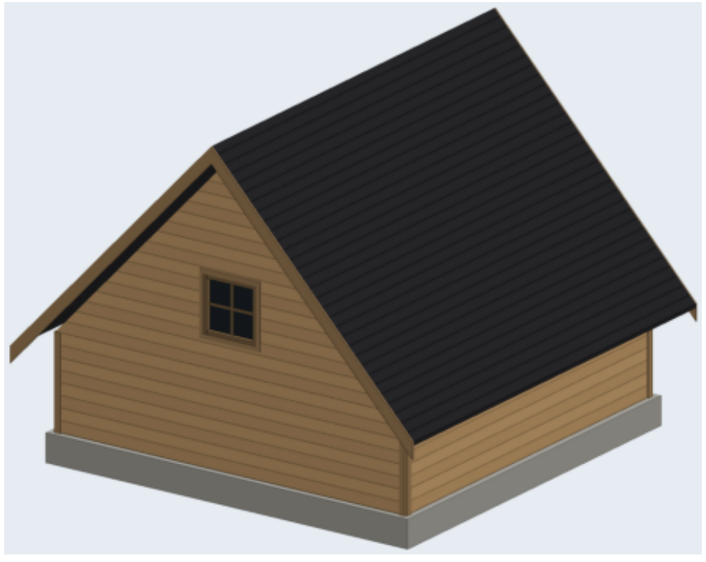

منظر علوي

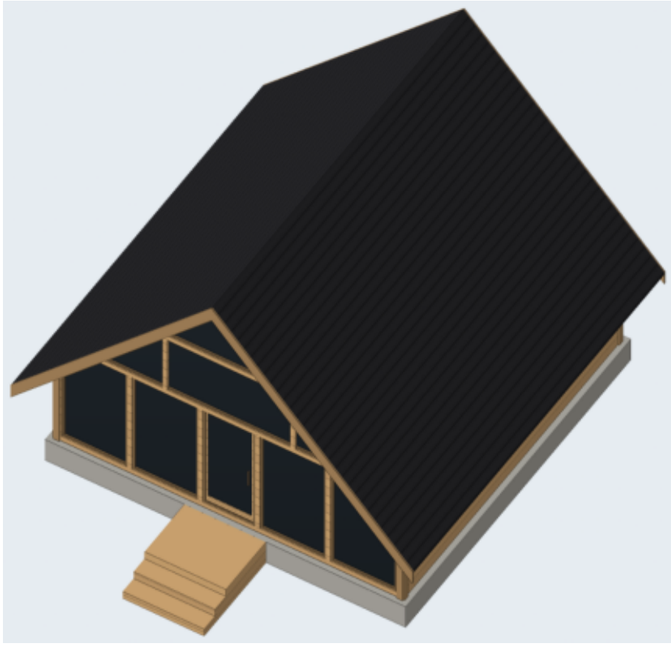


المشروع / العميل	عنوان اللوحة	المقياس	التاريخ	رقم اللوحة
كوخ A-frame بواجهة زجاج كاملة — غرفة وحدة 6 × 6 = 36 م² **عميل — A-frame 6×6**	**لقطات المنظور**	**—**	**2026-10-20**	**A-07 (7/9)**

مصنع وتد الأخشاب
Watad Wood Factory

المقطع العلوي بالفرش

مقطع أفقي على ارتفاع 1.90 م — توزيع الفرش ومسار الحركة

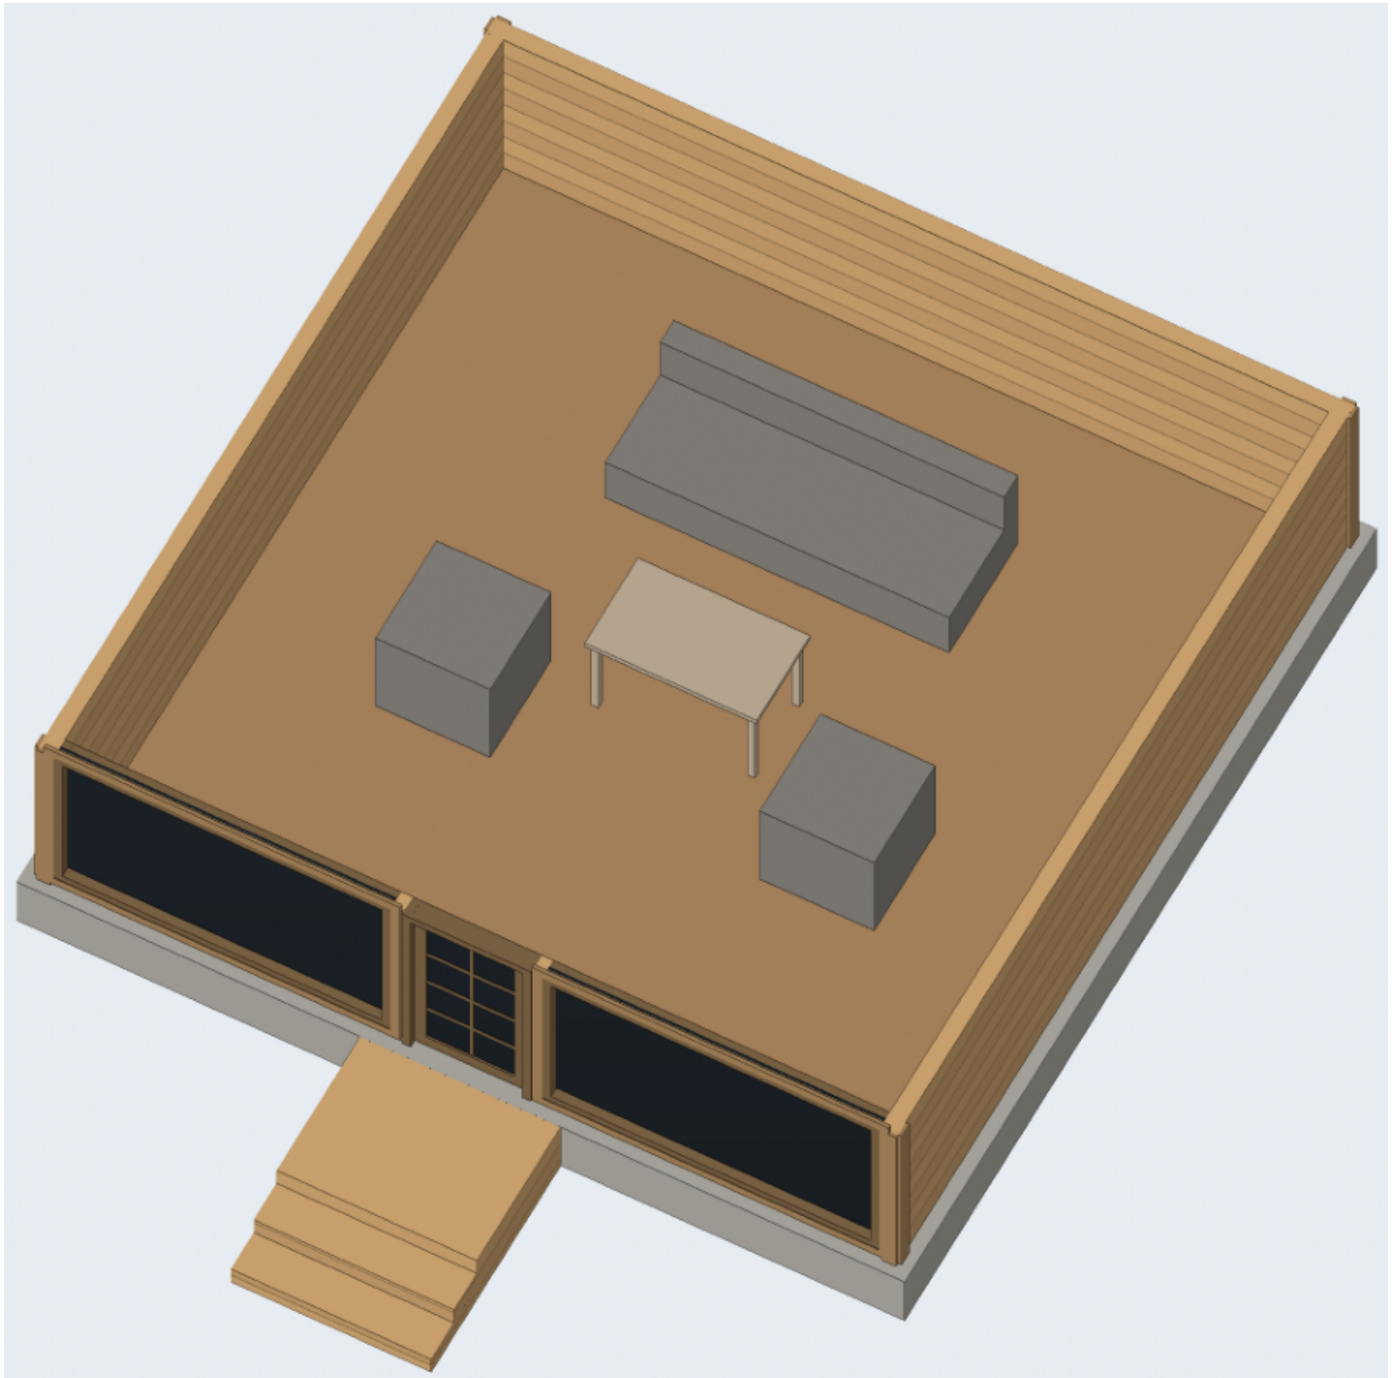

المشروع / العميل	عنوان اللوحة	المقياس	التاريخ	رقم اللوحة
كوخ A-frame بواجهة زجاج كاملة — غرفة وحدة 6 × 6 = 36 م² عميل — A-frame 6×6	المقطع العلوي بالفرش	—	2026-10-20	A-08 (8/9)

مصنع وتد الأخشاب
Watad Wood Factory

المنظور ثلاثي الأبعاد والمواد

النمط: جوزي غامق + إطارات سوداء — رندر واقعي بخامات حقيقية



جدول المواد والألوان

الخشب / الصبغة

خشب طبيعي فاتح (بدون صبغة)

القرميد

قرميد رمادي غامق

الزجاج

زجاج عاكس غامق

إطارات الشبابيك والأبواب

إطار خشب بنفس الصبغة أغمق

الكنار والزوايا

نفس الصبغة أغمق درجة


الصبة

خرسانة 45 سم


الدربزين: ألواح أفقية متقاربة (عصري)

تقسيم الشبابيك: بدون | الباب الرئيسي: زجاج بتقسيمات (فرنسي)

أنواع الدربزين المعتمدة (من مشاريع المصنع)

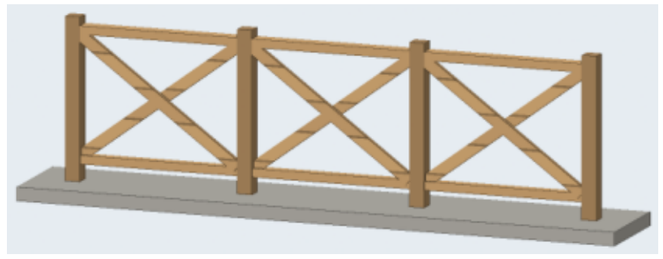

تقاطع X (صورة 5)

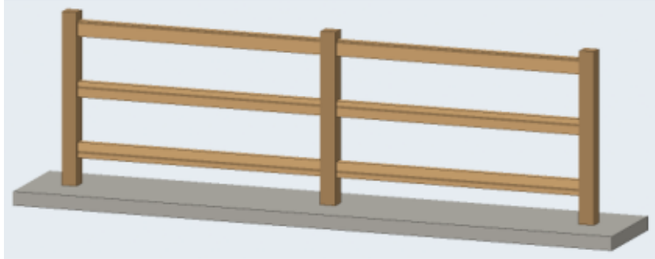

3 مرابيع أفقية (صورة 2)



قوائم رأسية متقاربة (صورة 1)

المشروع / العميل	عنوان اللوحة	المقياس	التاريخ	رقم اللوحة
مصنع وتد الأخشاب Watad Wood Factory **كوخ A-frame بواجهة زجاج كاملة — غرفة وحدة 6 × 6 = 36 م²** **عميل — A-frame 6×6**	**المنظور والمواد**	**—**	**2026-10-20**	**A-09 (9/9)**