
المسقط الأفقي مع الفرش

الأبعاد بالسنتيمتر - الجدران: قوائم 5×7 + تلبيس 2.5 من الجهتين (12 سم)

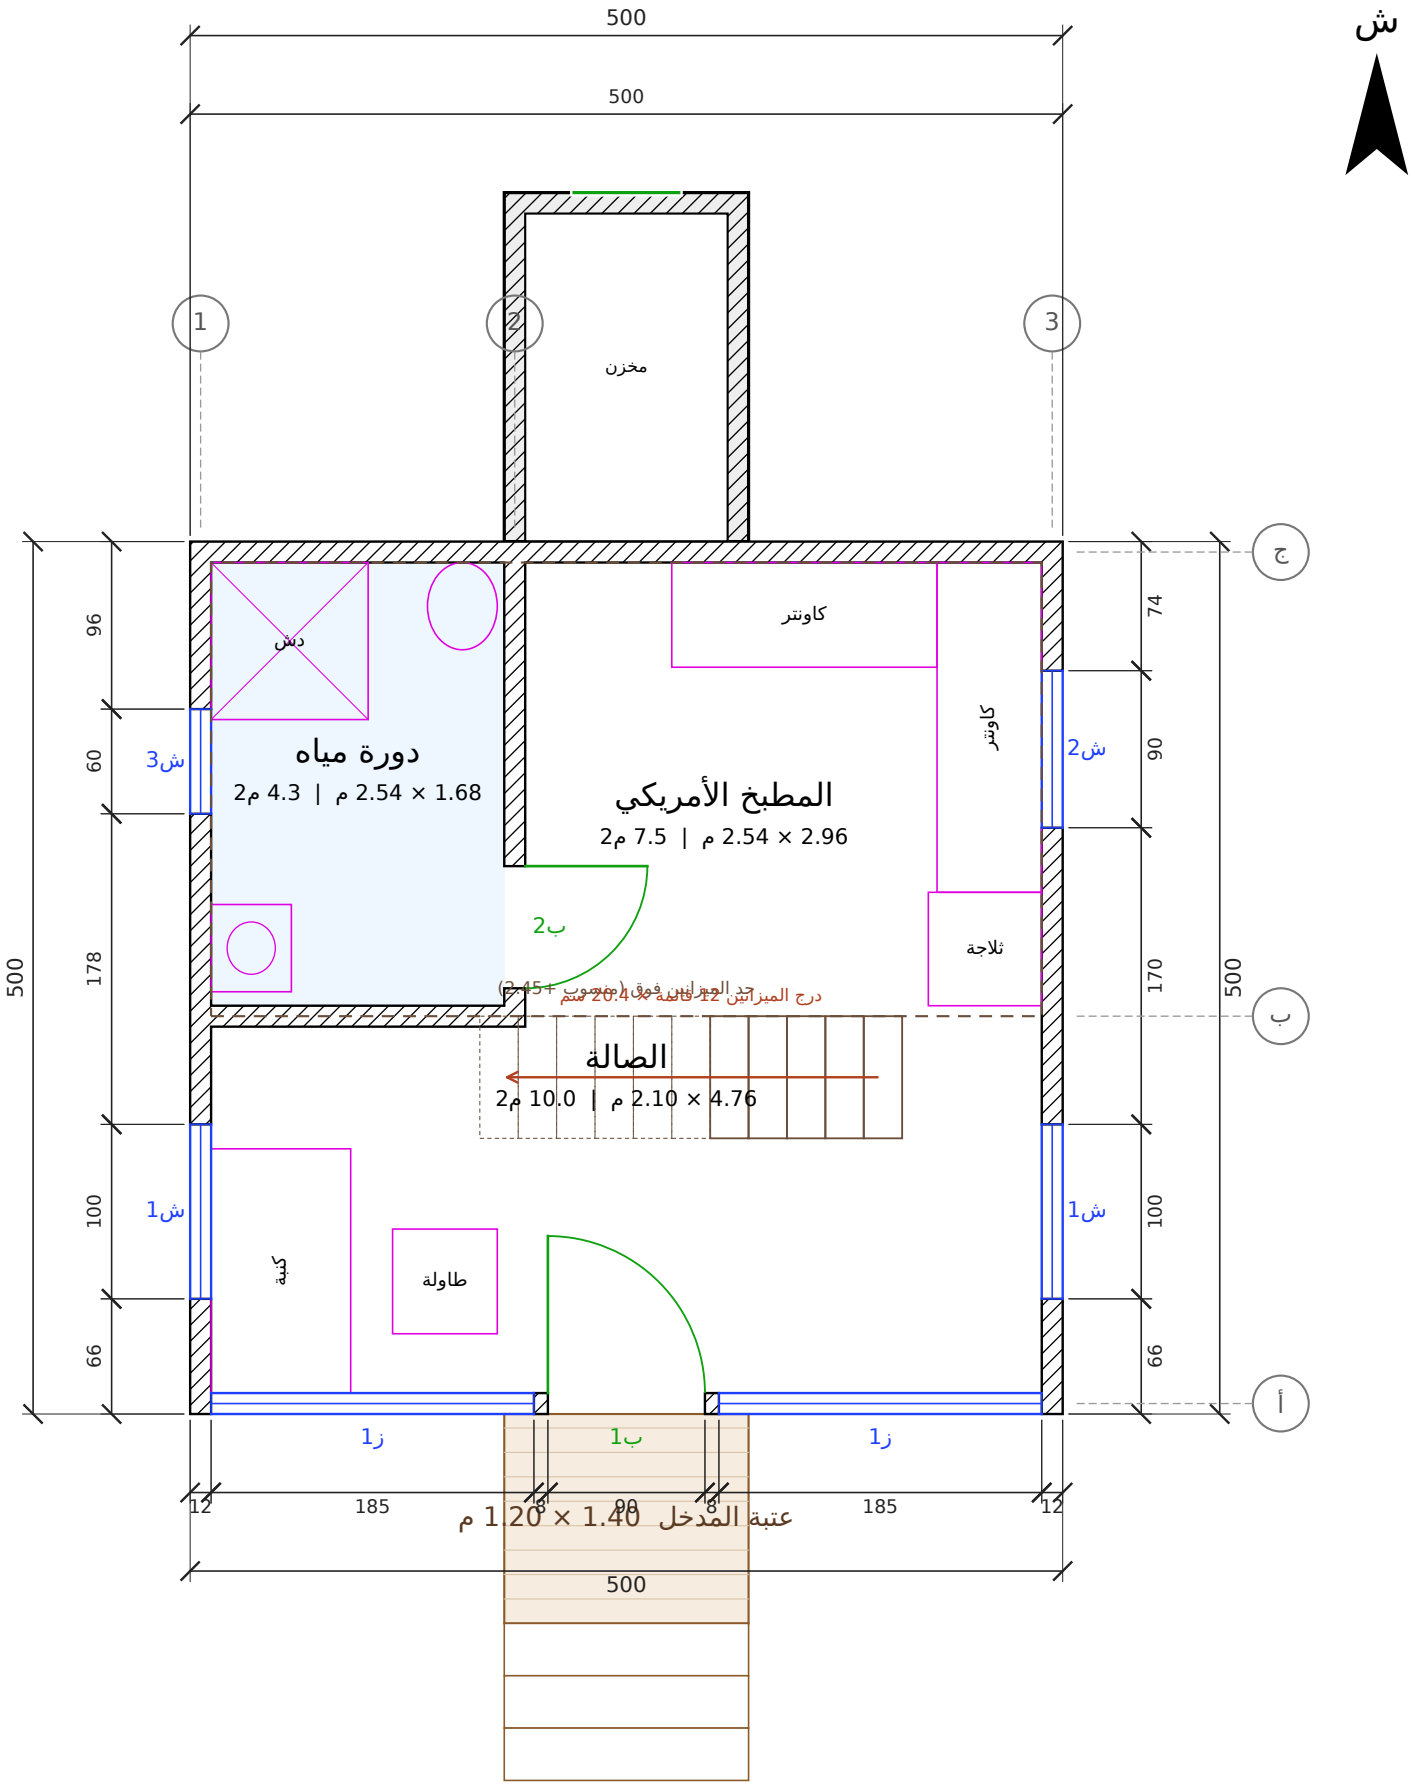


3 درجات × 15 سم

مصنع وتد الأخشاب Watad Wood Factory	المشروع / العميل **كوخ A-frame بواجهة زجاج + ميزانين — 25 م²** **عميل — الهدا**	عنوان اللوحة **المسقط الأفقي**	المقياس **1:50**	التاريخ **2026-10-18**	رقم اللوحة **A-01 (1/10)**


مسقط الميزانين (نص الدور) — غرفة النوم

منسوب أرضية الميزانين +2.45 | الأبعاد بالسنتيمتر

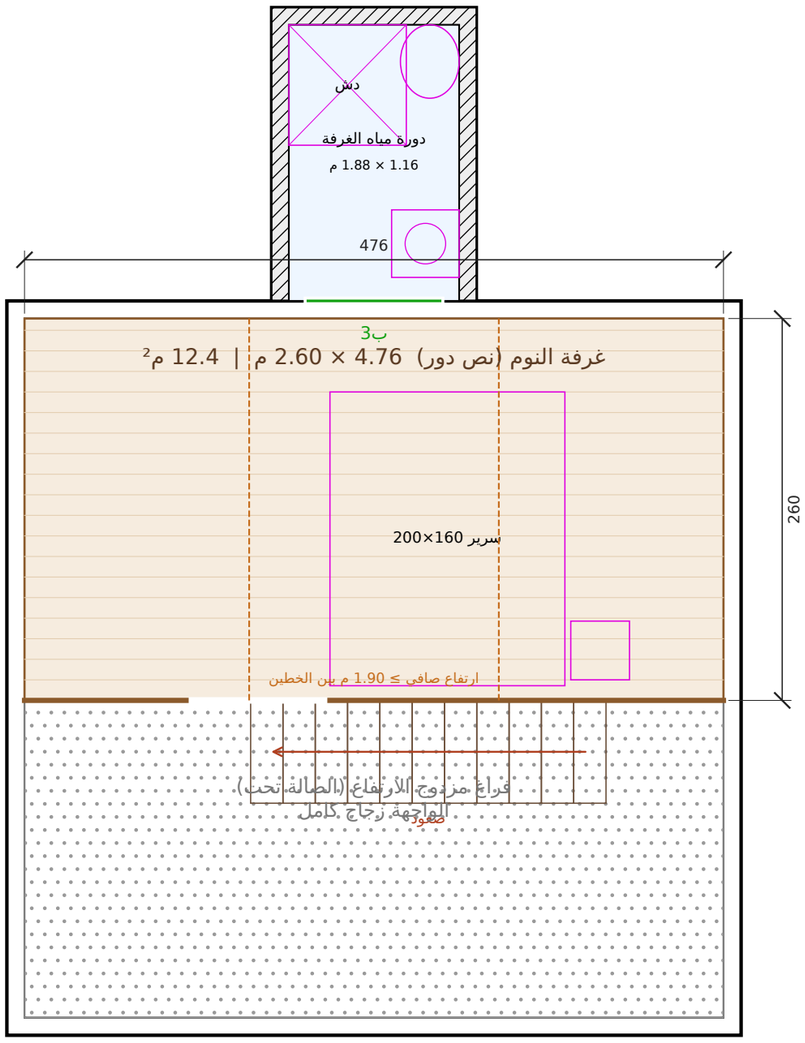


المشروع / العميل	عنوان اللوحة	المقياس	التاريخ	رقم اللوحة
كوخ A-frame بواجهة زجاج + ميزانين — 25 م² **عميل — الهدا**	**مسقط الميزانين**	**1:50**	**2026-10-18**	**A-02 (2/10)**

مصنع وتد الأخشاب
Watad Wood Factory

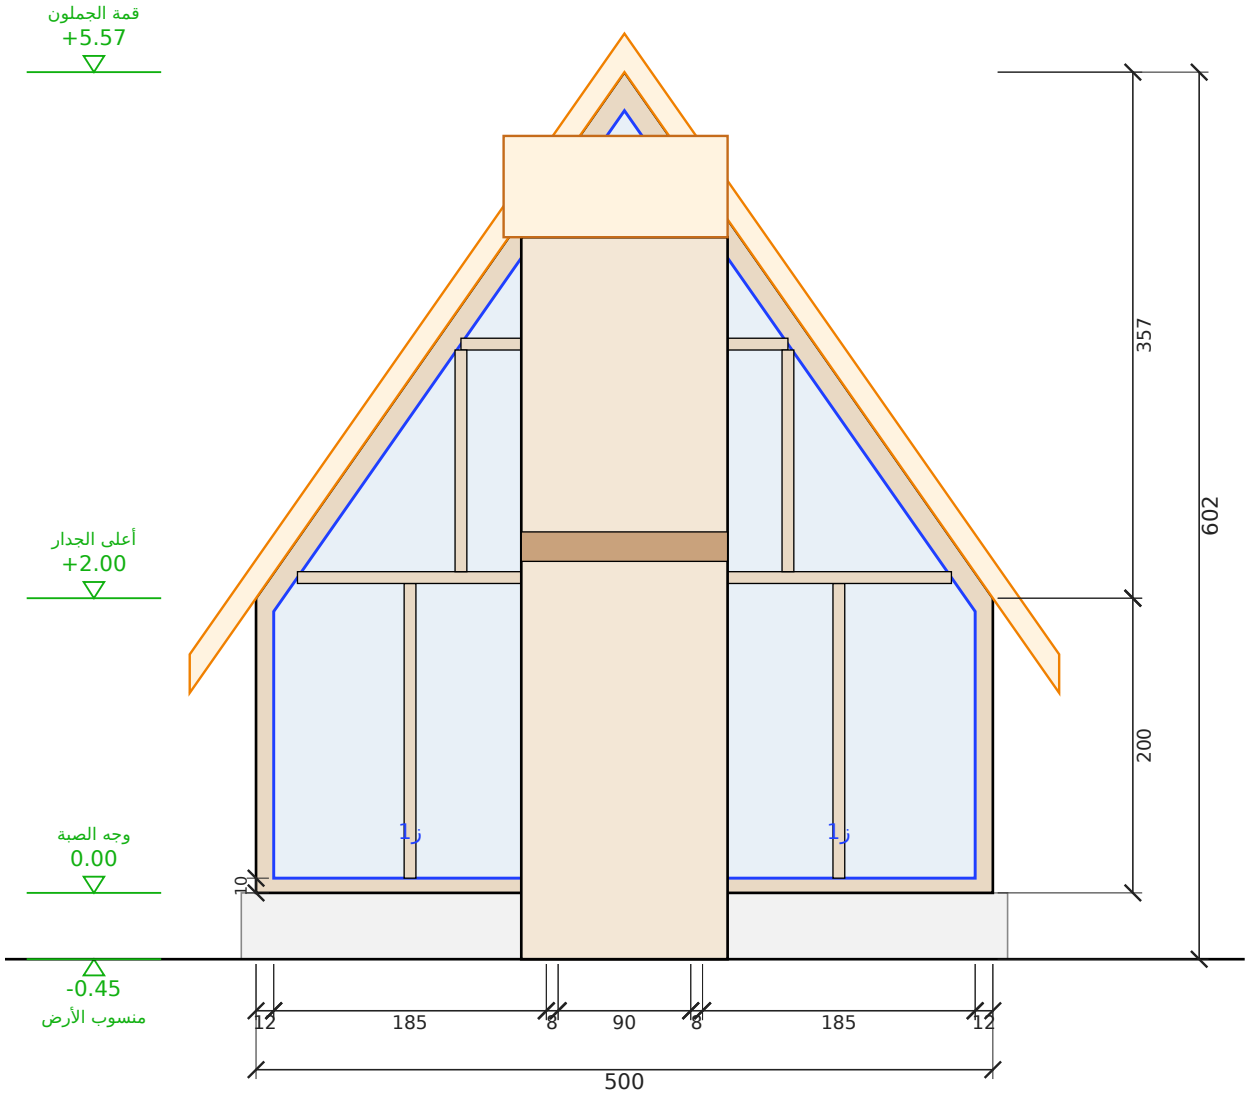

الواجهة الأمامية

مقياس 1:50 | الوحدة: سم

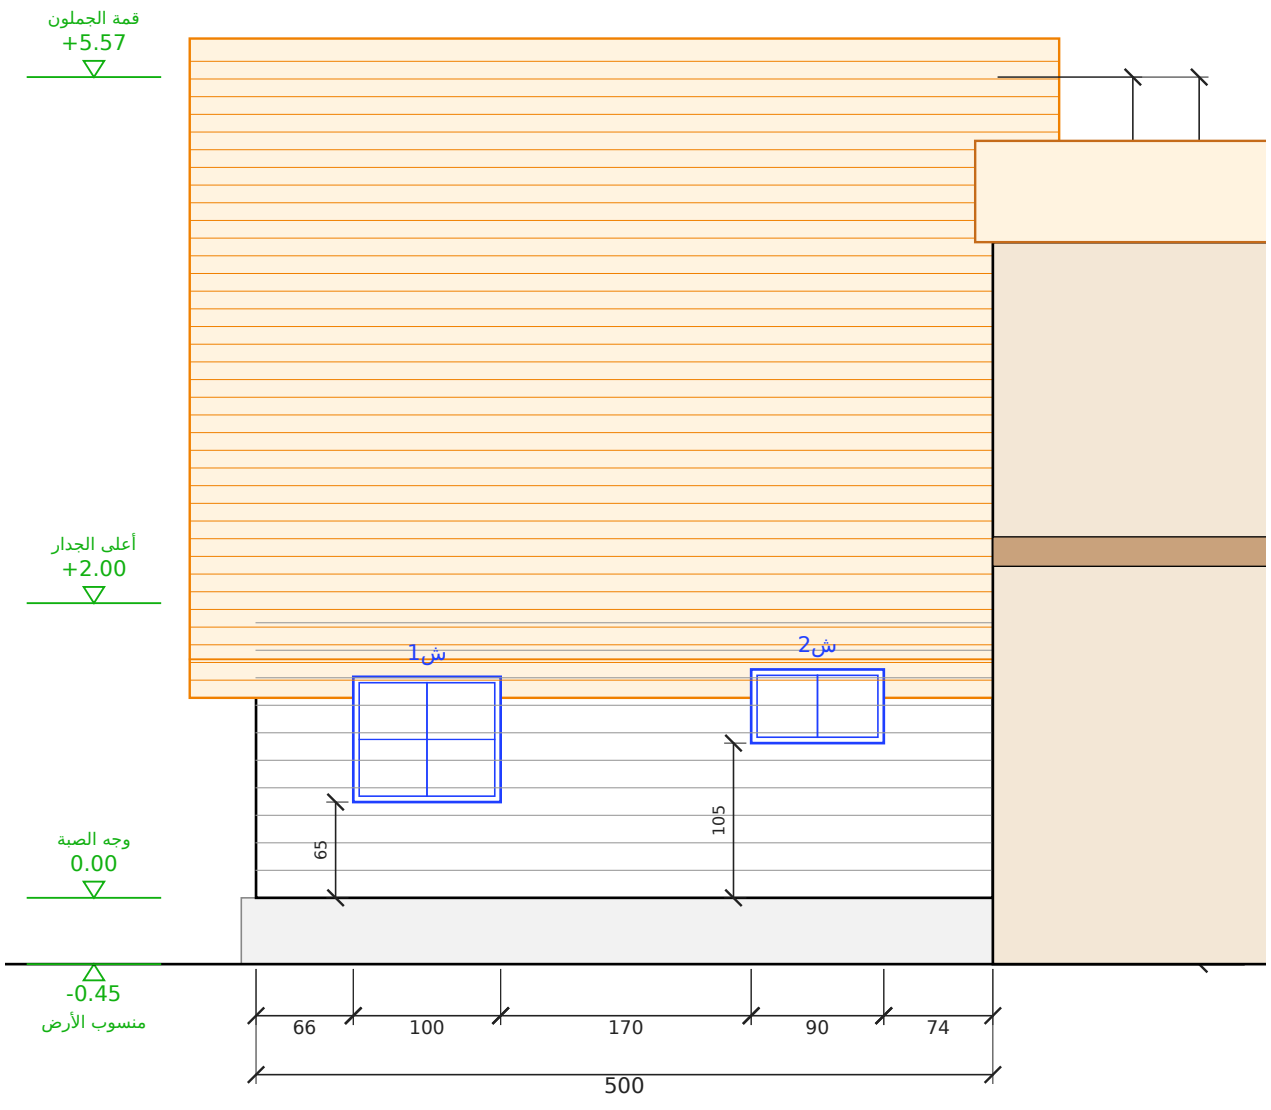


الواجهة الشرقية

مقياس 1:50 | الوحدة: سم


المشروع / العميل	عنوان اللوحة	المقياس	التاريخ	رقم اللوحة
كوخ A-frame بواجهة زجاج + ميزانين — 25 م² **عميل — الهدا**	**الواجهة الأمامية والواجهة الشرقية**	**1:50**	**2026-10-18**	**A-03 (3/10)**

مصنع وتد الأخشاب
Watad Wood Factory

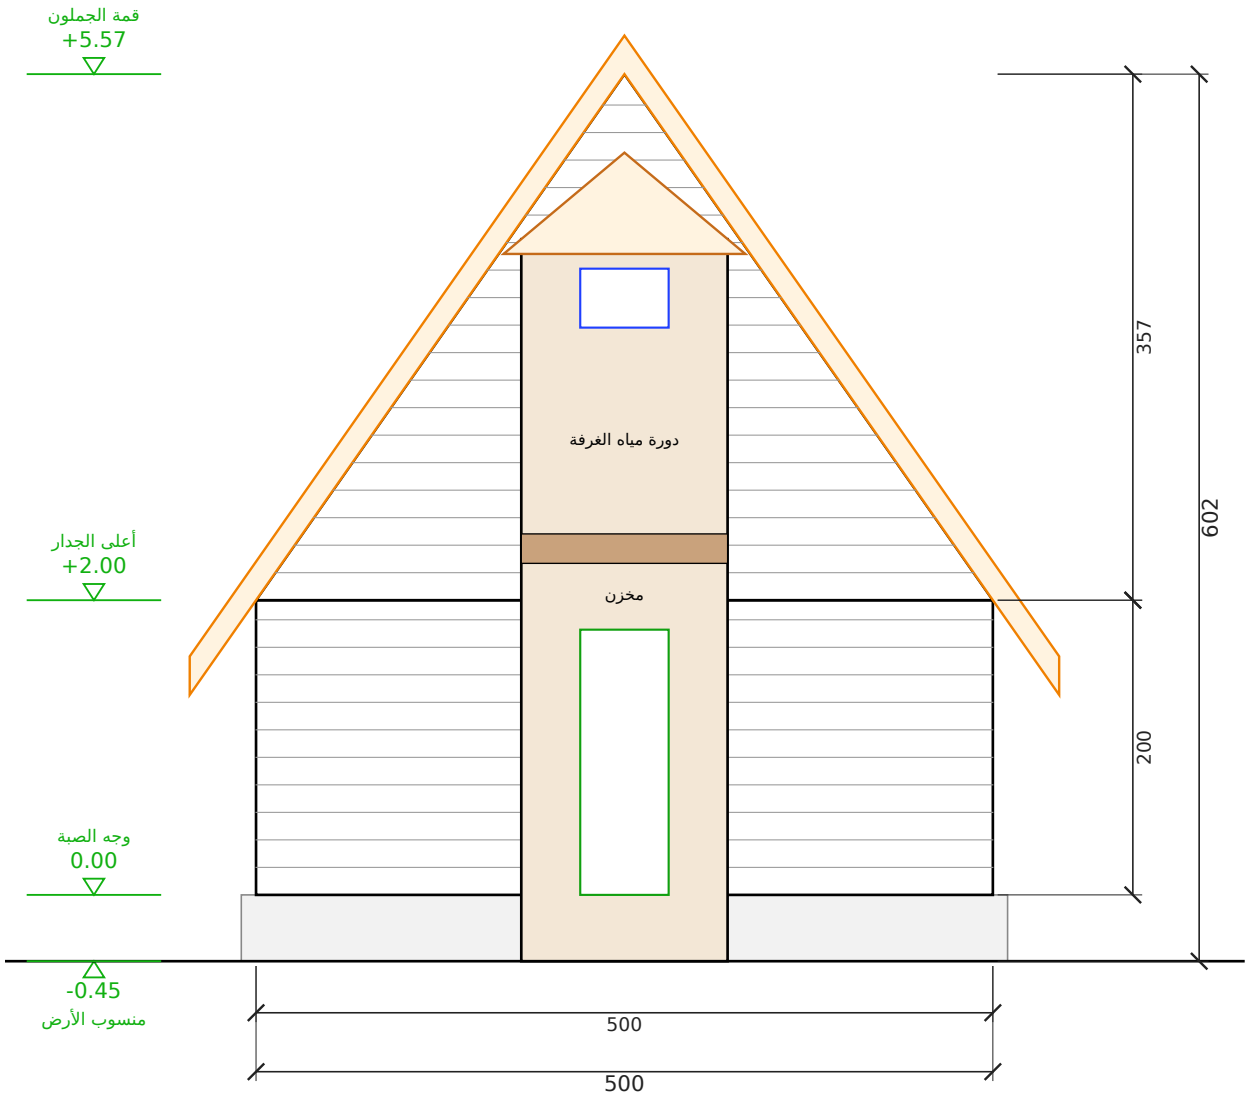

الواجهة الخلفية

مقياس 1:50 | الوحدة: سم

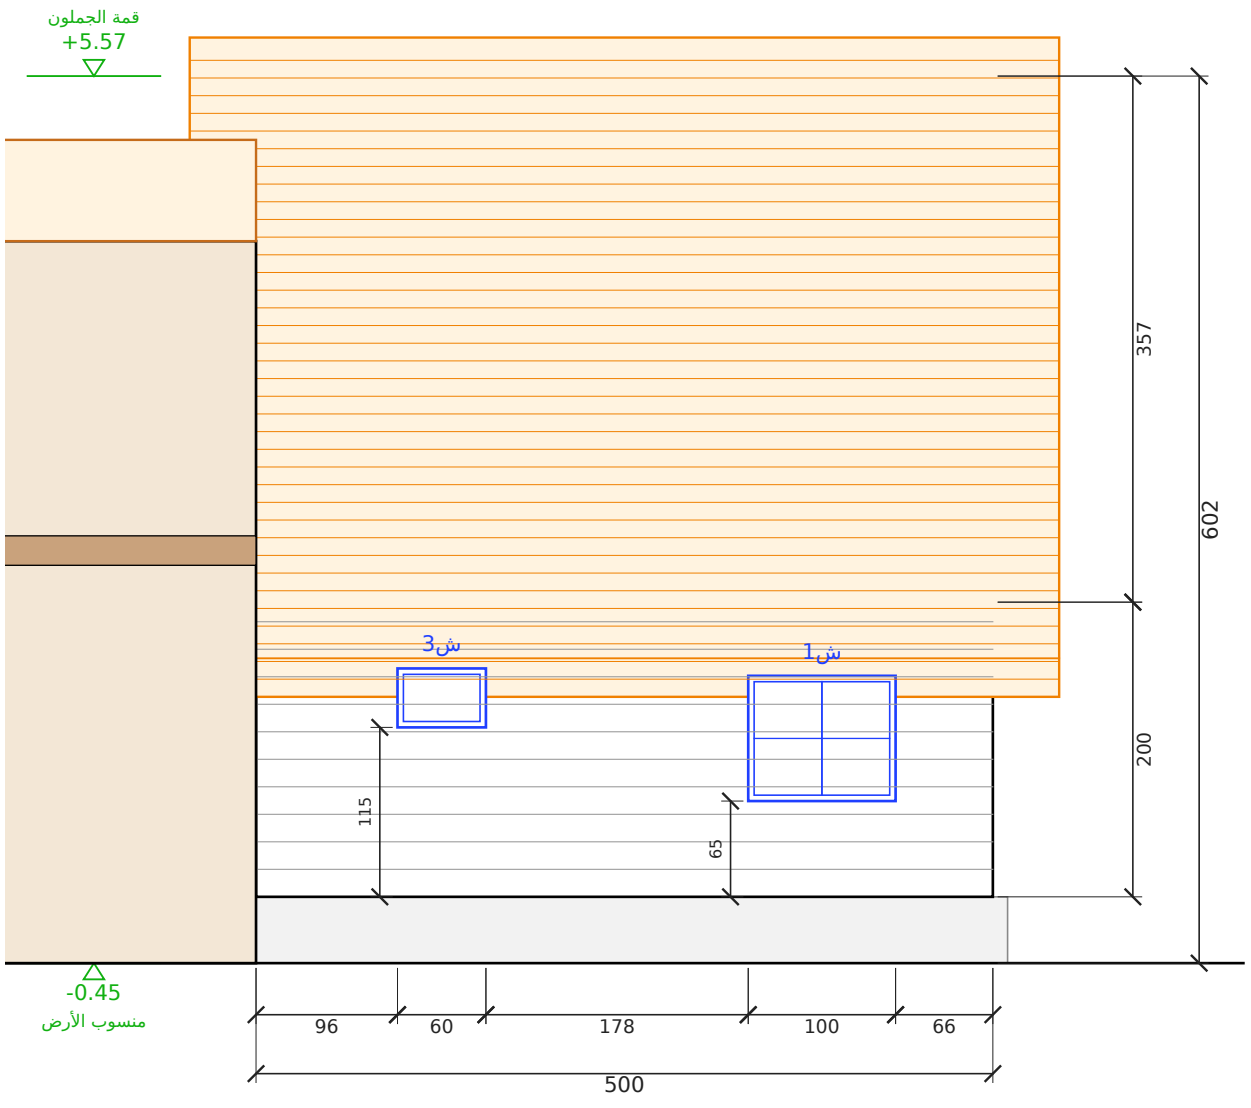


الواجهة الغربية

مقياس 1:50 | الوحدة: سم


المشروع / العميل	عنوان اللوحة	المقياس	التاريخ	رقم اللوحة
كوخ A-frame بواجهة زجاج + ميزانين — 25 م² **عميل — الهدا**	**الواجهة الخلفية والواجهة الغربية**	**1:50**	**2026-10-18**	**A-04 (4/10)**

مصنع وتد الأخشاب
Watad Wood Factory


مسقط السقف (جملون)
رفرف 45 سم من كل جهة | مقياس 1:50

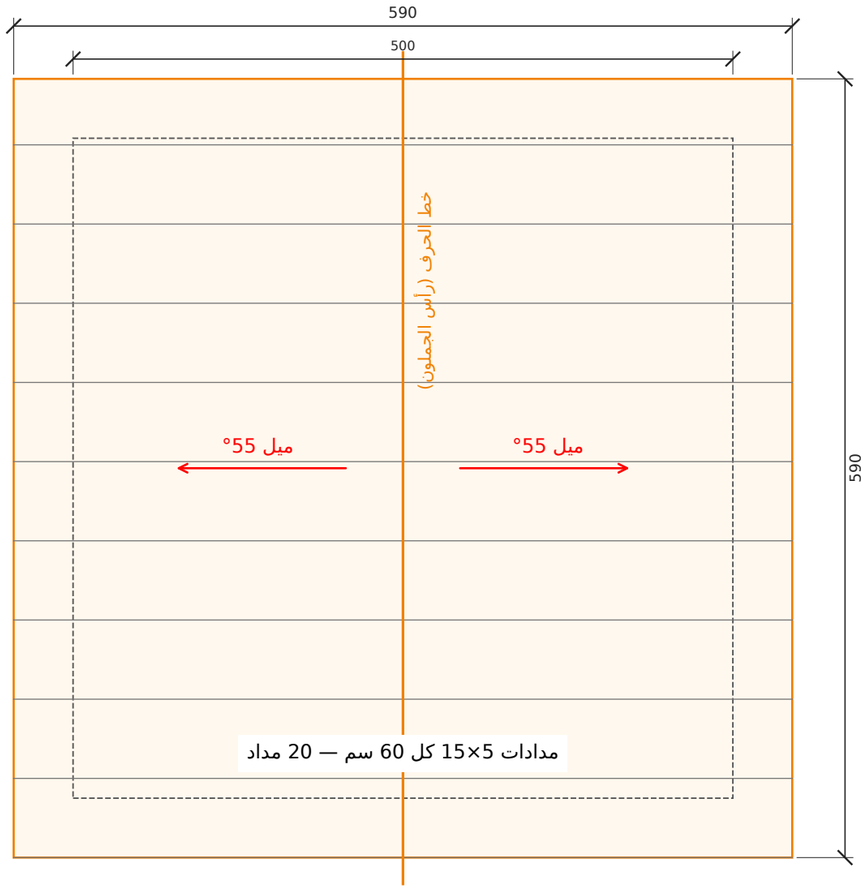

قطاع عرضي أ-أ
مقياس 1:50 | الوحدة: سم

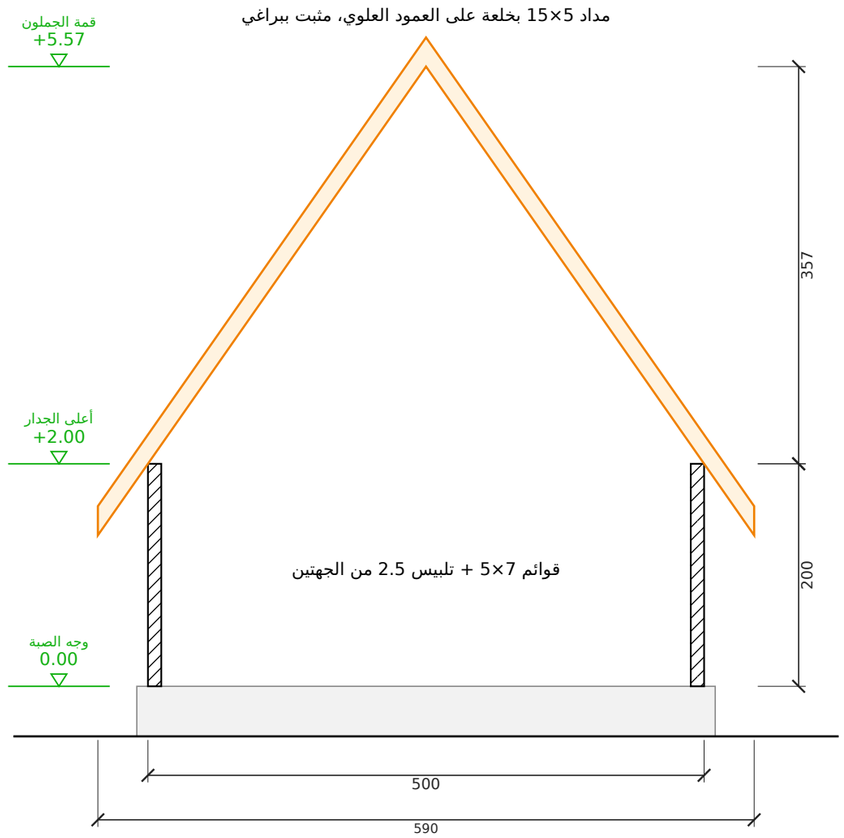

تفصيلة جلوس المداد على العلوي (1:5)

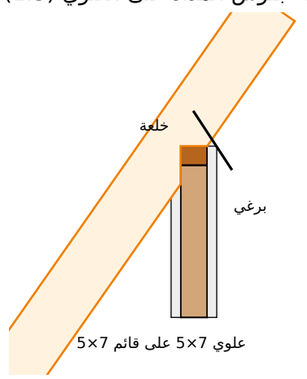

المشروع / العميل	عنوان اللوحة	المقياس	التاريخ	رقم اللوحة
كوخ A-frame بواجهة زجاج + ميزانين — 25 م² عميل — الهدا	مسقط السقف والقطاع	1:50	2026-10-18	A-05 (5/10)

مصنع وتد الأخشاب
Watad Wood Factory

جدول مقاسات الأبواب والشبابيك
مقاس الفتحة الصافي في الجدار - الوحدة: سم

الرمز	النوع	العرض (سم)	الارتفاع (سم)	ارتفاع الجلسة (سم)	العدد	الموقع
ب1	باب	90	210	-	1	الأمامية
ب2	باب	70	205	-	1	دورة المياه
ب3	باب	90	200	-	1	الخلفية
ز1	شباك	185	200	10	2	الأمامية 2
ش1	شباك	100	85	65	2	الشرقية - الغربية
ش2	شباك	90	50	105	1	الشرقية
ش3	شباك	60	40	115	1	الغربية

الإجمالي: أبواب 3 - شبابيك 6

المشروع / العميل	عنوان اللوحة	المقياس	التاريخ	رقم اللوحة
كوخ A-frame بواجهة زجاج + ميزانين — 25 م² **عميل — الهدا**	**جدول الأبواب والشبابيك**	**—**	**2026-10-18**	**A-06 (6/10)**

مصنع وتد الأخشاب
Watad Wood Factory

جدول المساحات وبيانات المشروع

بيانات المشروع

البند	البيان
المشروع	كوخ A-frame بواجهة زجاج + ميزانين — 25 م²
العميل	عميل — الهدا
الموقع	الهدا
الاستخدام	استراحة / سكن
التاريخ	2026-10-18
نظام البناء	هيكل خشب 5×7 + تلبيس 2.5 سم من الجهتين
السقف	جملون 55° — قرميد معدني

جدول المساحات

م	الفراغ	الأبعاد (م)	المساحة (م2)
1	الصالة	4.76 × 2.10	10.00
2	المطبخ الأمريكي	2.96 × 2.54	7.52
3	دورة مياه	1.68 × 2.54	4.27
	المساحة الصافية الداخلية		**21.78**
	عتبة المدخل	**1.40 × 1.20**	**1.68**
	المساحة الإجمالية المبنية	**5.00 × 5.00**	**25.00**

لقطات المنظور الخارجي

المنظور الأمامي




منظور أمامي من اليسار



منظور أمامي من اليمين



المنظور الخلفي

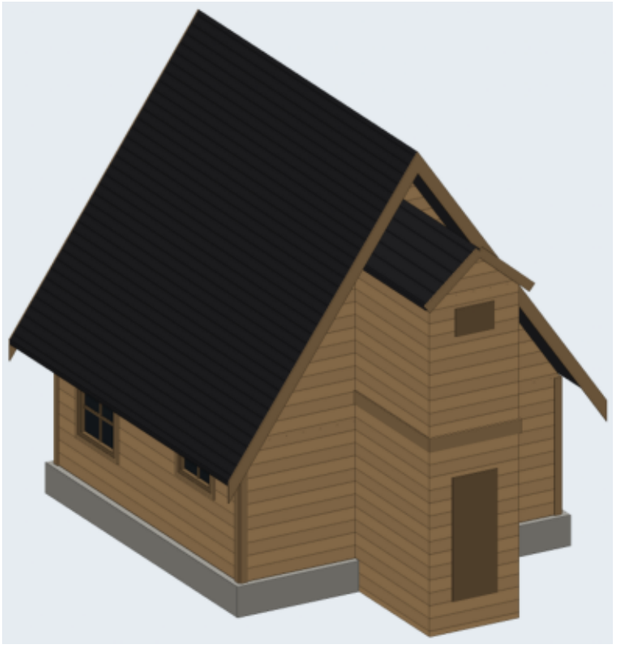

منظور خلفي من اليمين



منظر علوي




المشروع / العميل **كوخ A-frame بواجهة زجاج + ميزانين — 25 م²** **عميل — الهدا**	عنوان اللوحة **لقطات المنظور**	المقياس **—**	التاريخ **2026-10-18**	رقم اللوحة **A-08 (8/10)**

مصنع وتد الأخشاب
Watad Wood Factory

المقطع العلوي بالفرش

مقطع أفقي على ارتفاع 1.90 م — توزيع الفرش ومسار الحركة

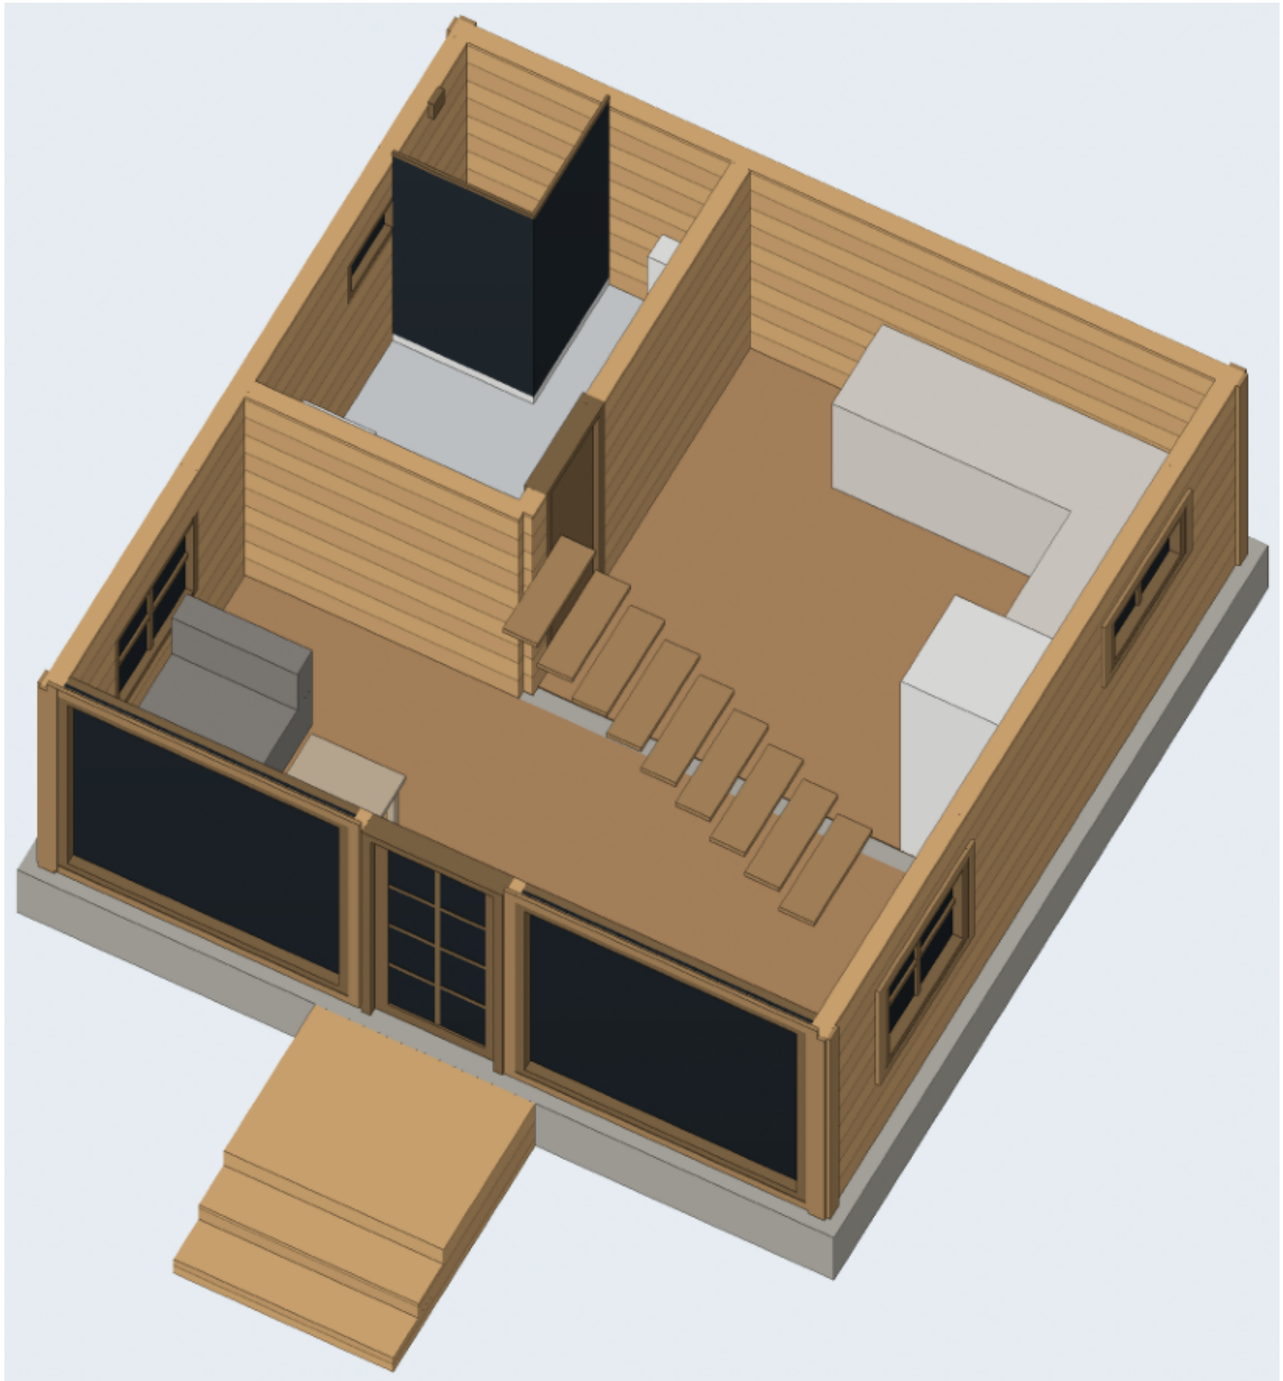


المشروع / العميل	عنوان اللوحة	المقياس	التاريخ	رقم اللوحة
كوخ A-frame بواجهة زجاج + ميزانين — 25 م² عميل — الهدا	المقطع العلوي بالفرش	—	2026-10-18	A-09 (9/10)

مصنع وتد الأخشاب
Watad Wood Factory

المنظور ثلاثي الأبعاد والمواد

النمط: جوزي غامق + إطارات سوداء — رندر واقعي بخامات حقيقية

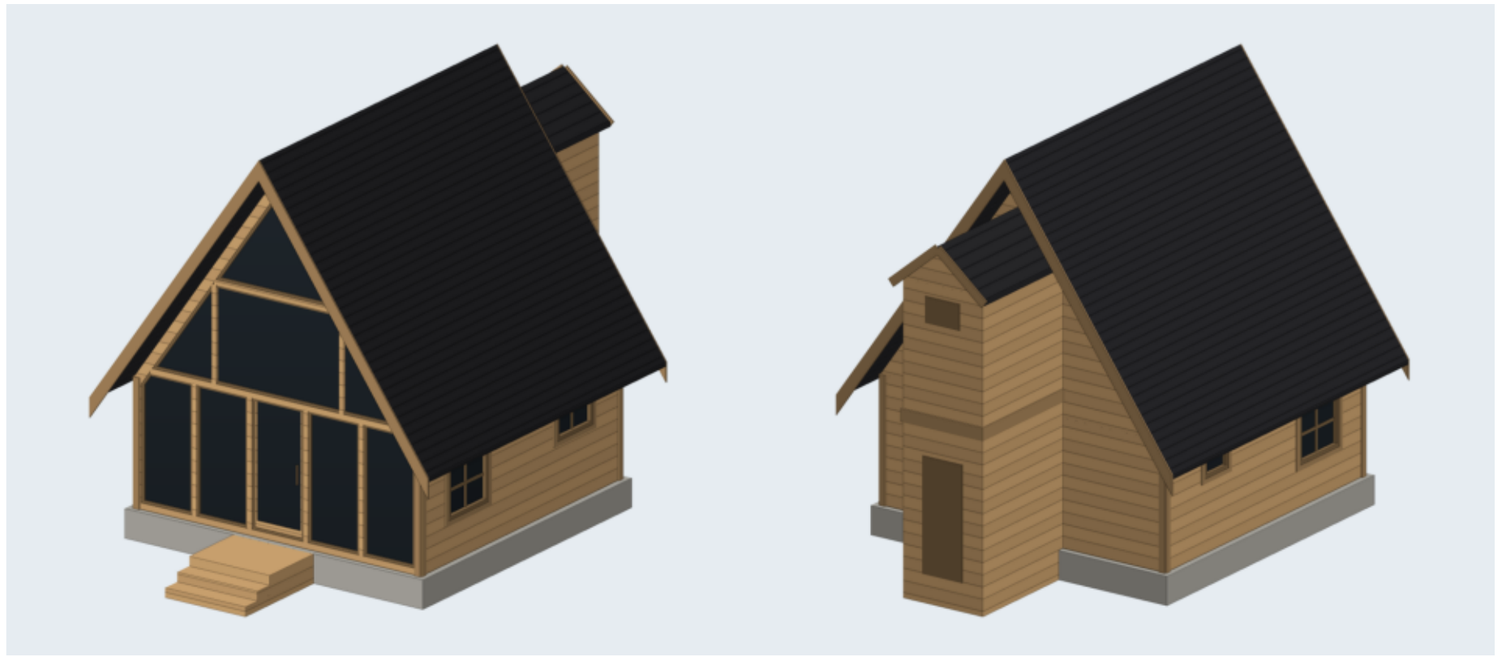

جدول المواد والألوان

الخشب / الصبغة

خشب طبيعي فاتح (بدون صبغة)

القرميد

قرميد رمادي غامق

الزجاج

زجاج عاكس غامق

إطارات الشبابيك والأبواب

إطار خشب بنفس الصبغة أغمق

الكنار والزوايا

نفس الصبغة أغمق درجة


الصبة

خرسانة 45 سم


الدربزين: ألواح أفقية متقاربة (عصري)

تقسيم الشبابيك: بدون | الباب الرئيسي: زجاج بتقسيمات (فرنسي)

أنواع الدربزين المعتمدة (من مشاريع المصنع)

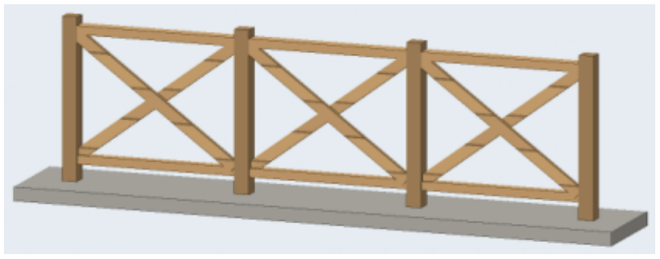

تقاطع X (صورة 5)

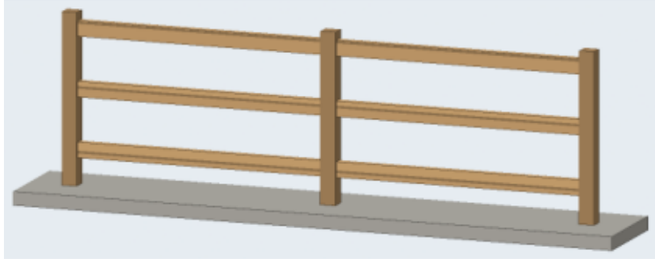

3 مرابيع أفقية (صورة 2)



قوائم رأسية متقاربة (صورة 1)

المشروع / العميل	عنوان اللوحة	المقياس	التاريخ	رقم اللوحة
كوخ A-frame بواجهة زجاج + ميزانين — 25 م² **عميل — الهدا**	**المنظور والمواد**	**—**	**2026-10-18**	**A-10 (10/10)**

مصنع وتد الأخشاب
Watad Wood Factory