المنظور ثلاثي الأبعاد والمواد

النمط: جوزي غامق + إطارات سوداء — رندر واقعي بخامات حقيقية



جدول المواد والألوان

الخشب / الصبغة

صبغة عسلي / سيدر

القرميد

قرميد رمادي غامق

الزجاج

زجاج شفاف

إطارات الشبابيك والأبواب

إطار ألمنيوم أسود

الكنار والزوايا

نفس الصبغة أغمق درجة


الصبة

خرسانة 45 سم


الدربزين: ألواح أفقية متقاربة (عصري)

تقسيم الشبابيك: بدون | الباب الرئيسي: زجاج بتقسيمات (فرنسي)

أنواع الدربزين المعتمدة (من مشاريع المصنع)

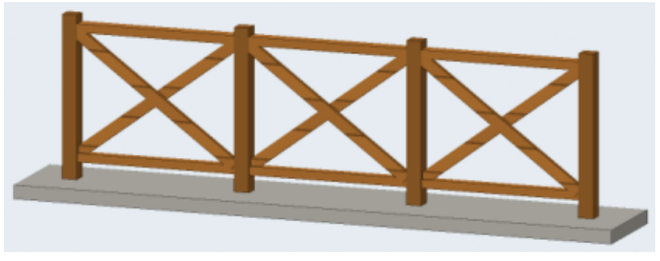

تقاطع X (صورة 5)

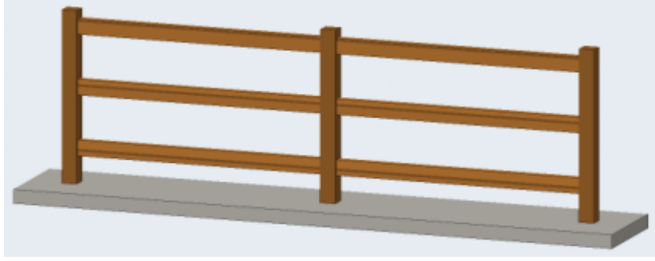

3 مرابيع أفقية (صورة 2)




قوائم رأسية متقاربة (صورة 1)

المشروع / العميل	عنوان اللوحة	المقياس	التاريخ	رقم اللوحة
كوخ واجهة زجاج — صالة ومطبخ أمريكي وحمام — 6.00 × 5.00 م (30 م²) **عميل — كوخ 6×5**	**المنظور والمواد**	**1:50**	**2026-10-26**	**W-01 (1/12)**

مصنع وتد الأخشاب
Watad Wood Factory


المسقط الأفقي مع الفرش

الأبعاد بالسنتيمتر - الجدران: قوائم 5×7 + تلبيس 2.5 من الجهتين (12 سم)

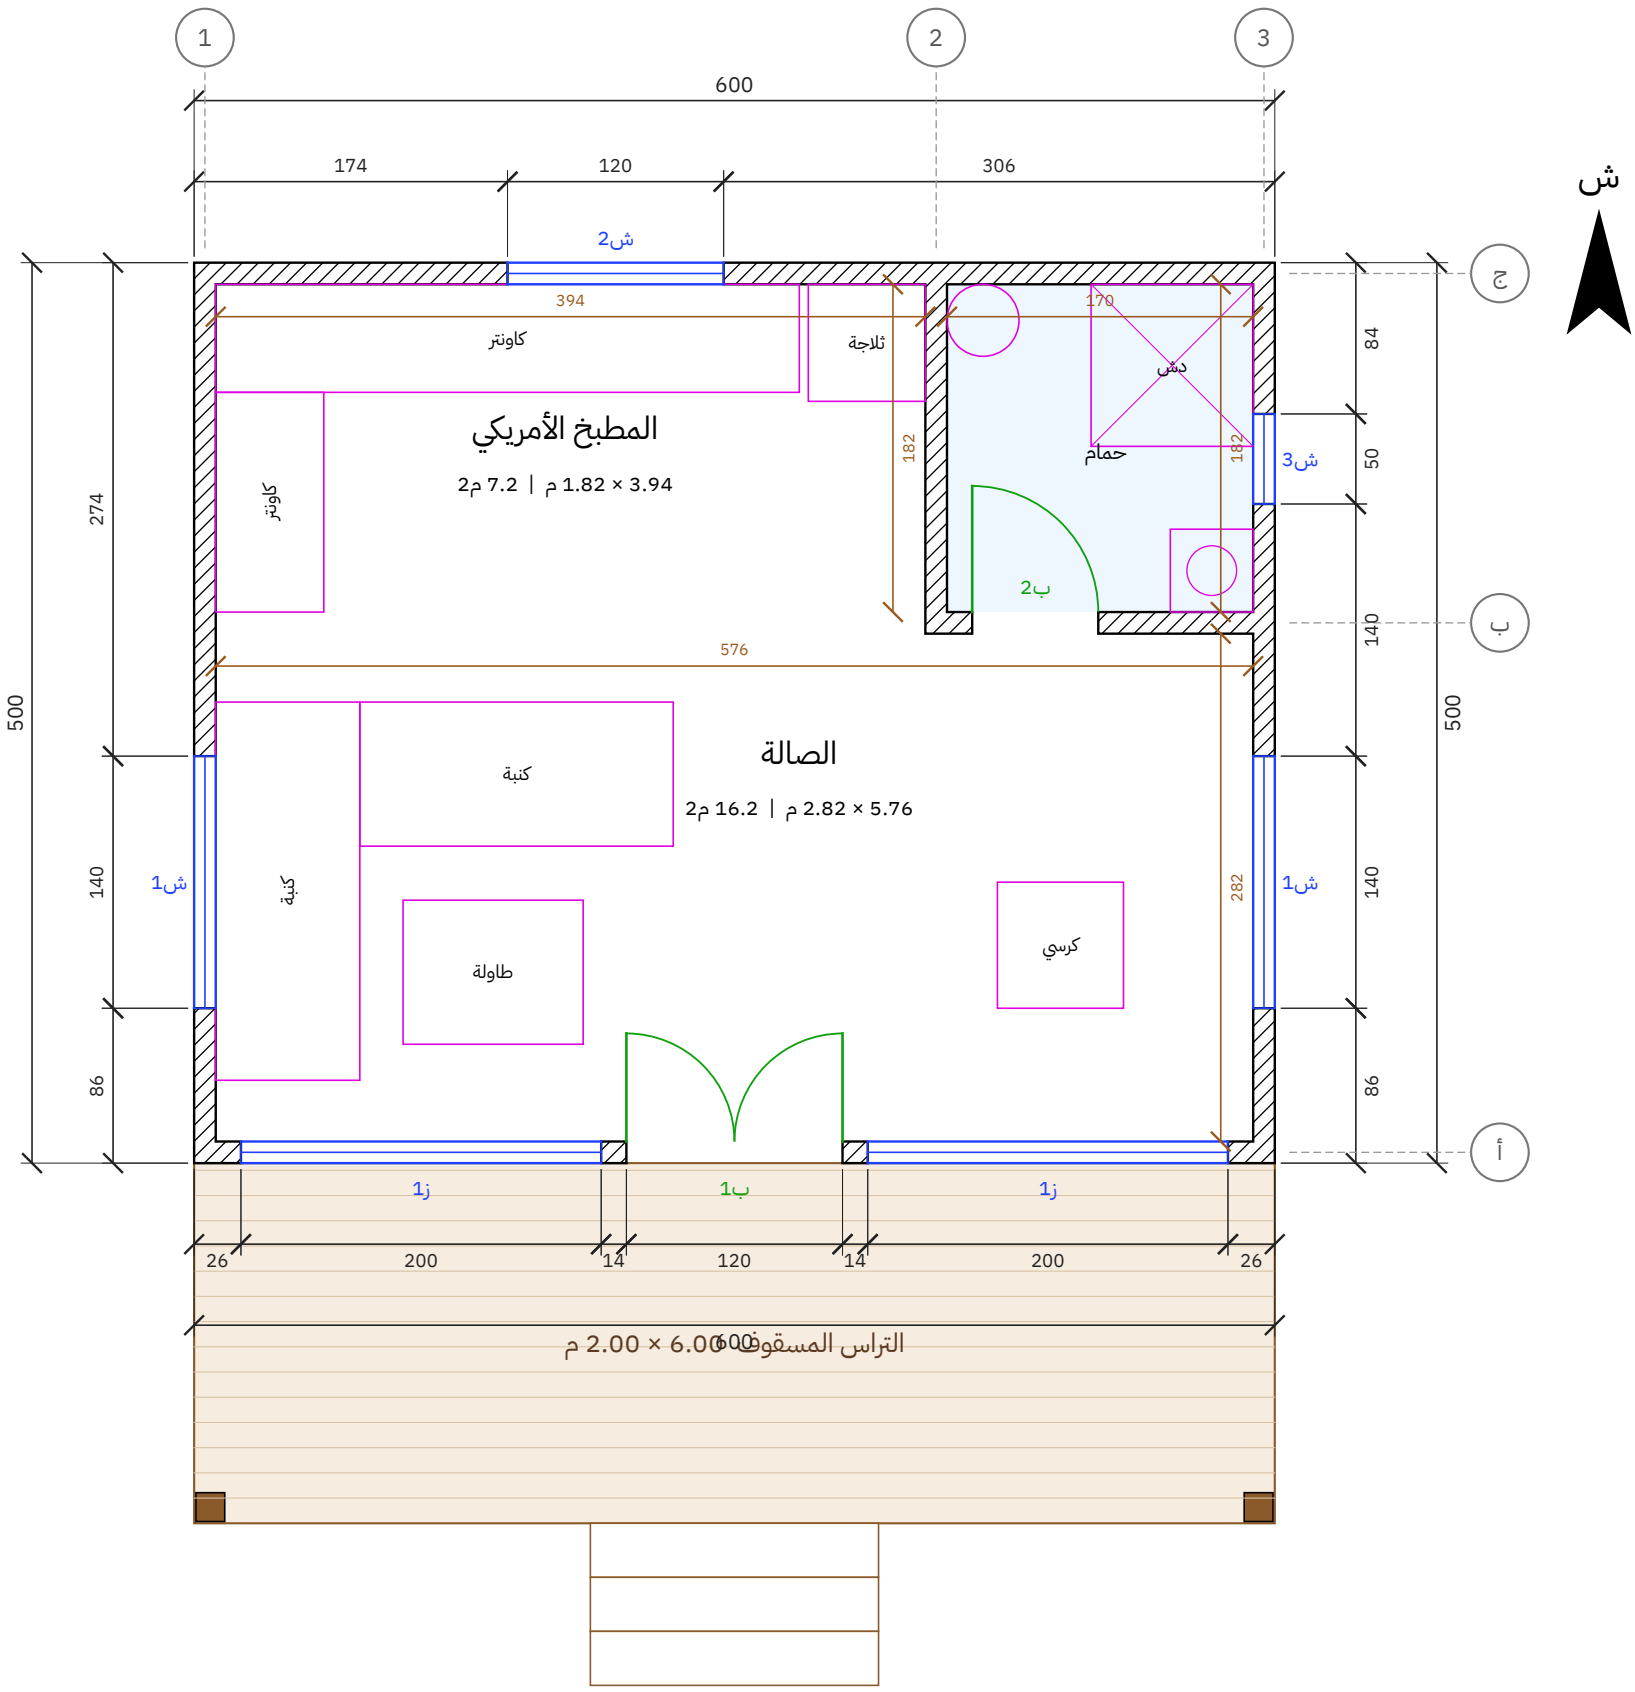


3 درجات × 15 سم

مصنع وتد الأخشاب Watad Wood Factory	المشروع / العميل كوخ واجهة زجاج – صالة ومطبخ أمريكي وحمام – 6.00 × 5.00 م (30 م²) عميل – كوخ 6×5	عنوان اللوحة المسقط الأفقي	المقياس 1:50	التاريخ 2026-10-26	رقم اللوحة W-02 (2/12)

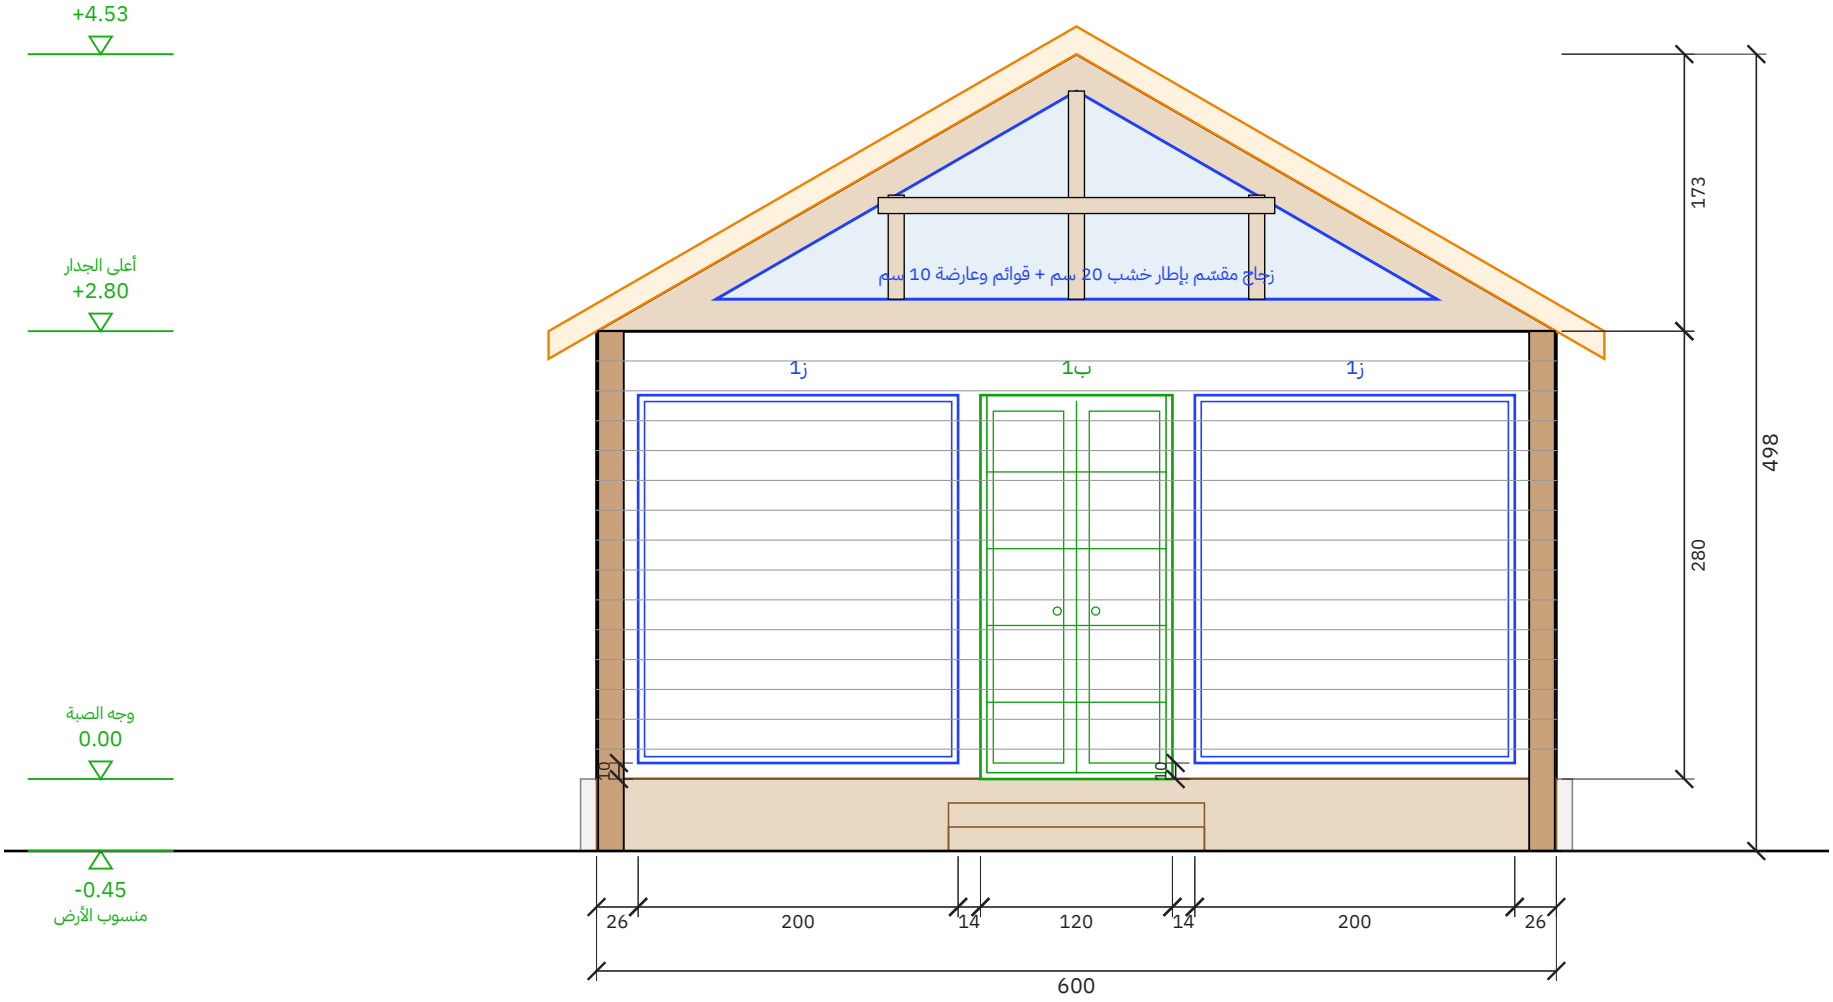

الواجهة الأمامية (زجاج)

مقياس 1:50 | الوحدة: سم

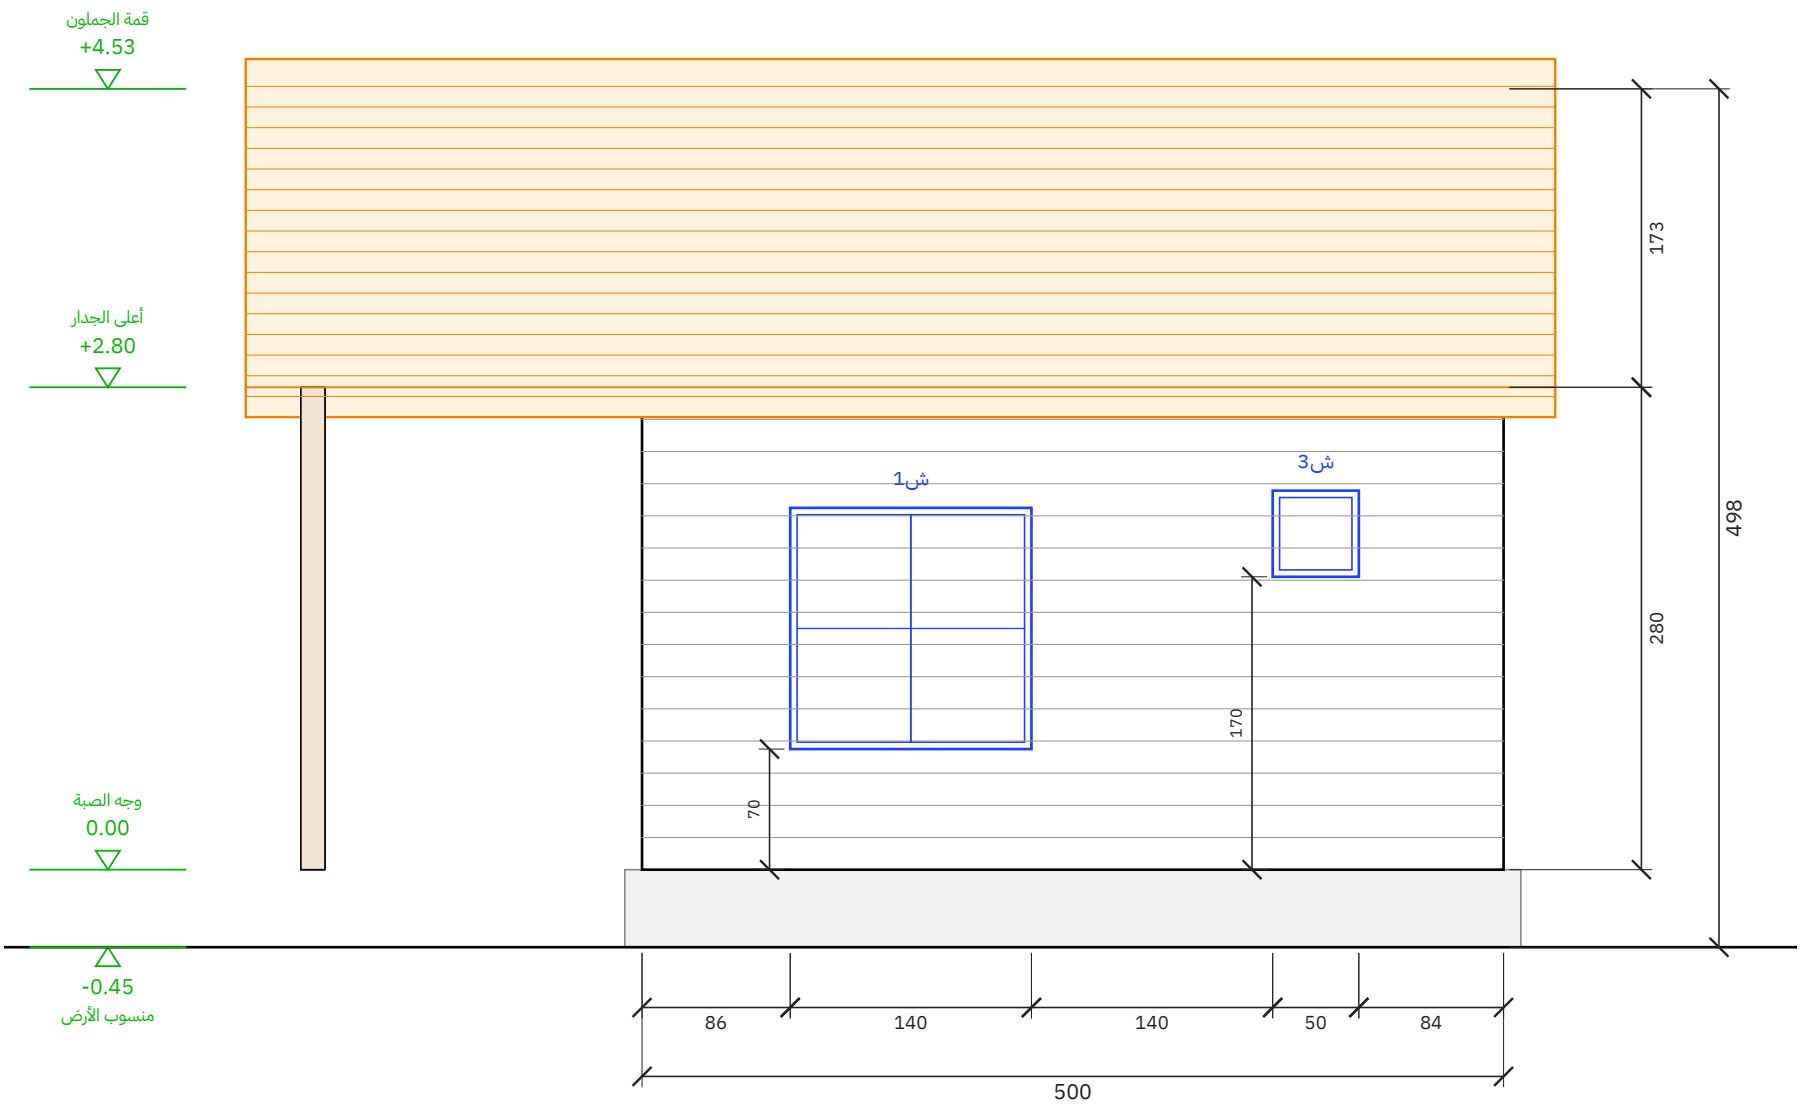


الواجهة الشرقية

مقياس 1:50 | الوحدة: سم


المشروع / العميل	عنوان اللوحة	المقياس	التاريخ	رقم اللوحة
كوخ واجهة زجاج – صالة ومطبخ أمريكي وحمام – 6.00 × 5.00 م (30 م²) عميل – كوخ 6×5	الواجهة الأمامية (زجاج) والواجهة الشرقية	1:50	2026-10-26	W-03 (3/12)

مصنع وتد الأخشاب
Watad Wood Factory

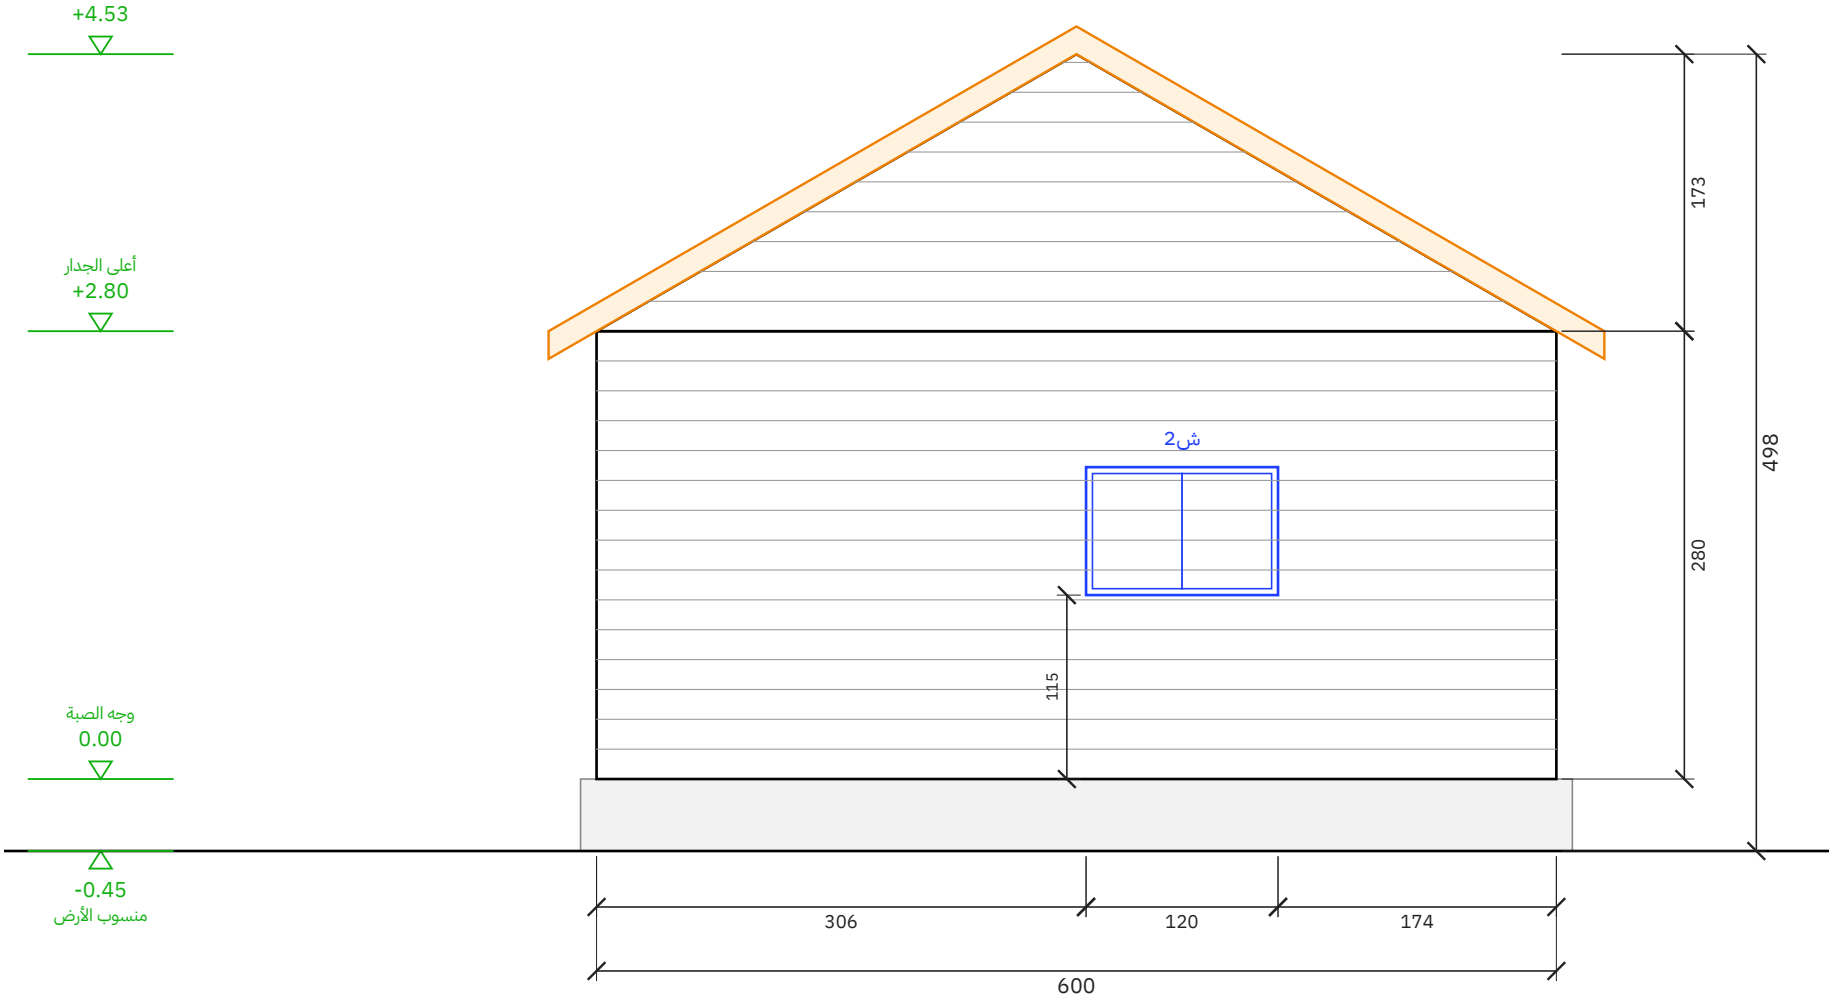

الواجهة الخلفية

مقياس 1:50 | الوحدة: سم

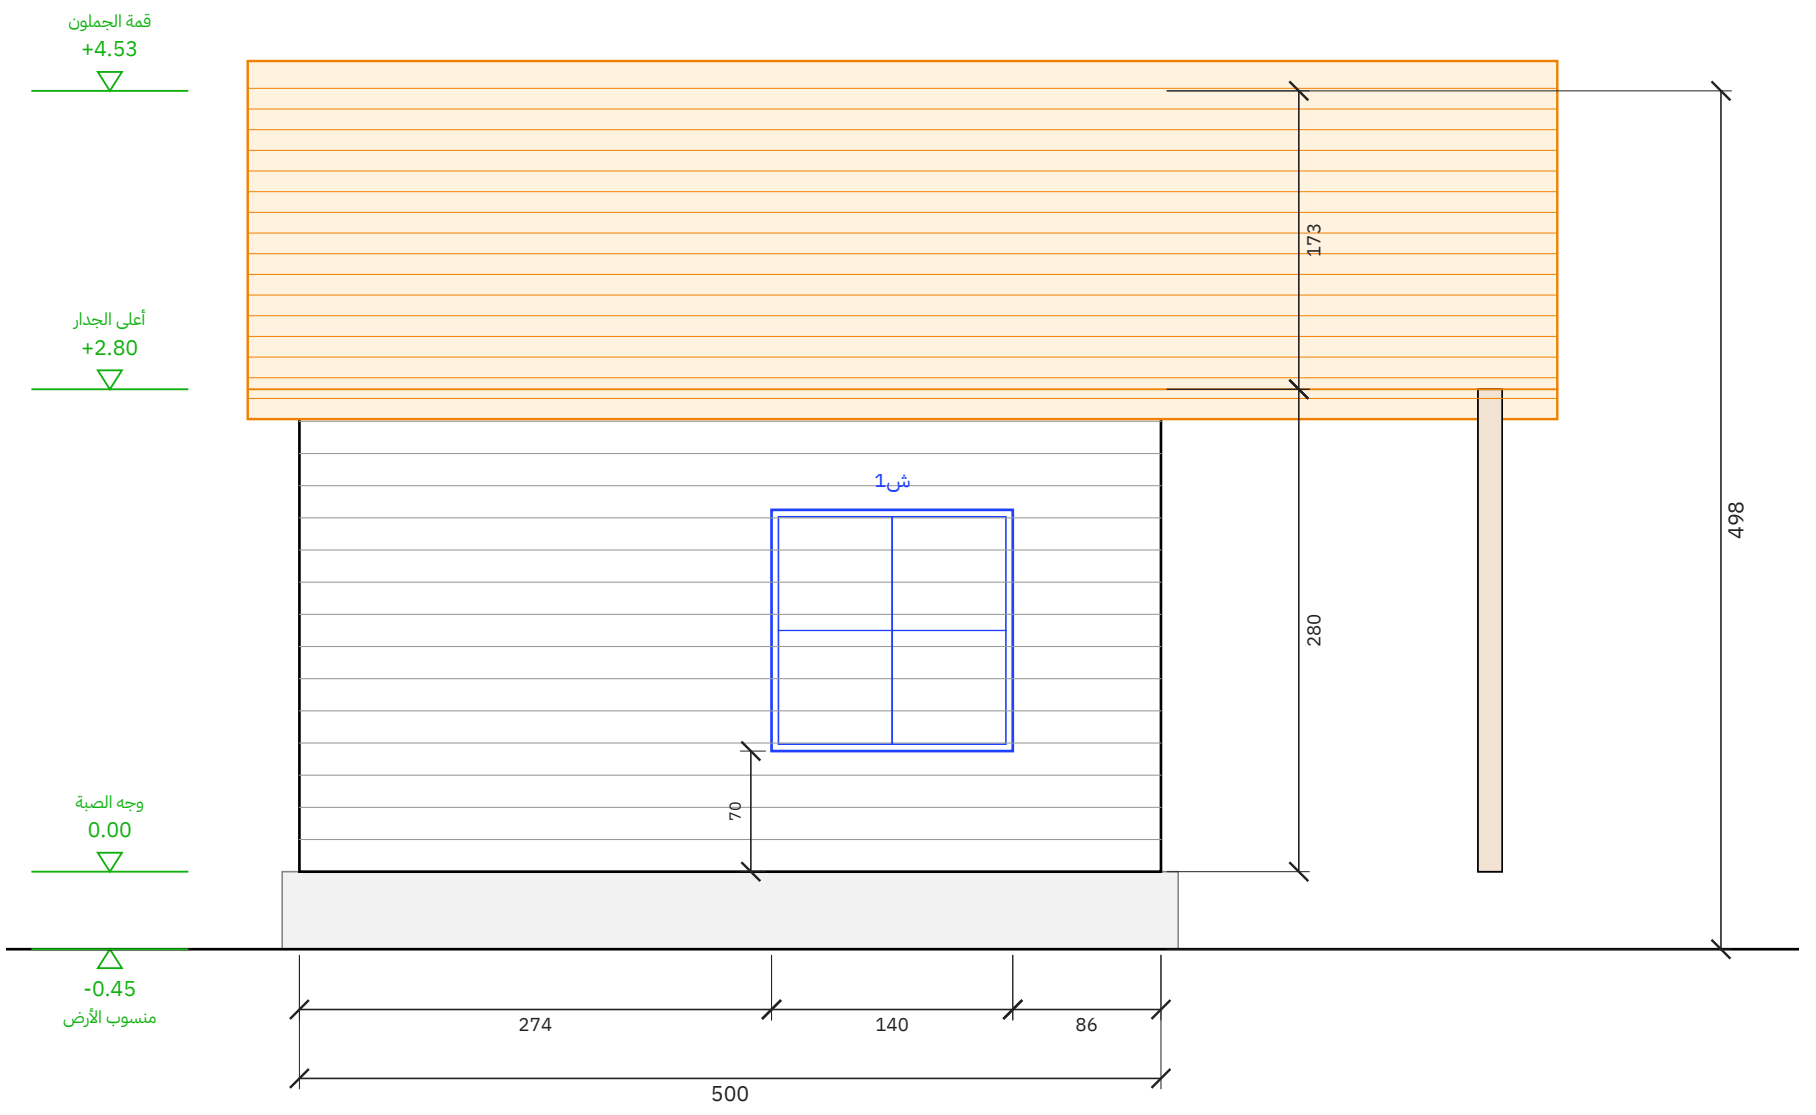

الواجهة الغربية


مقياس 1:50 | الوحدة: سم

المشروع / العميل	عنوان اللوحة	المقياس	التاريخ	رقم اللوحة
كوخ واجهة زجاج – صالة ومطبخ أمريكي وحمام – 6.00 × 5.00 م (30 م²) عميل – كوخ 6×5	الواجهة الخلفية والواجهة الغربية	1:50	2026-10-26	W-04 (4/12)

مصنع وتد الأخشاب
Watad Wood Factory


مسقط السقف (جملون)

رفرف 30 سم من كل جهة | مقياس 1:50

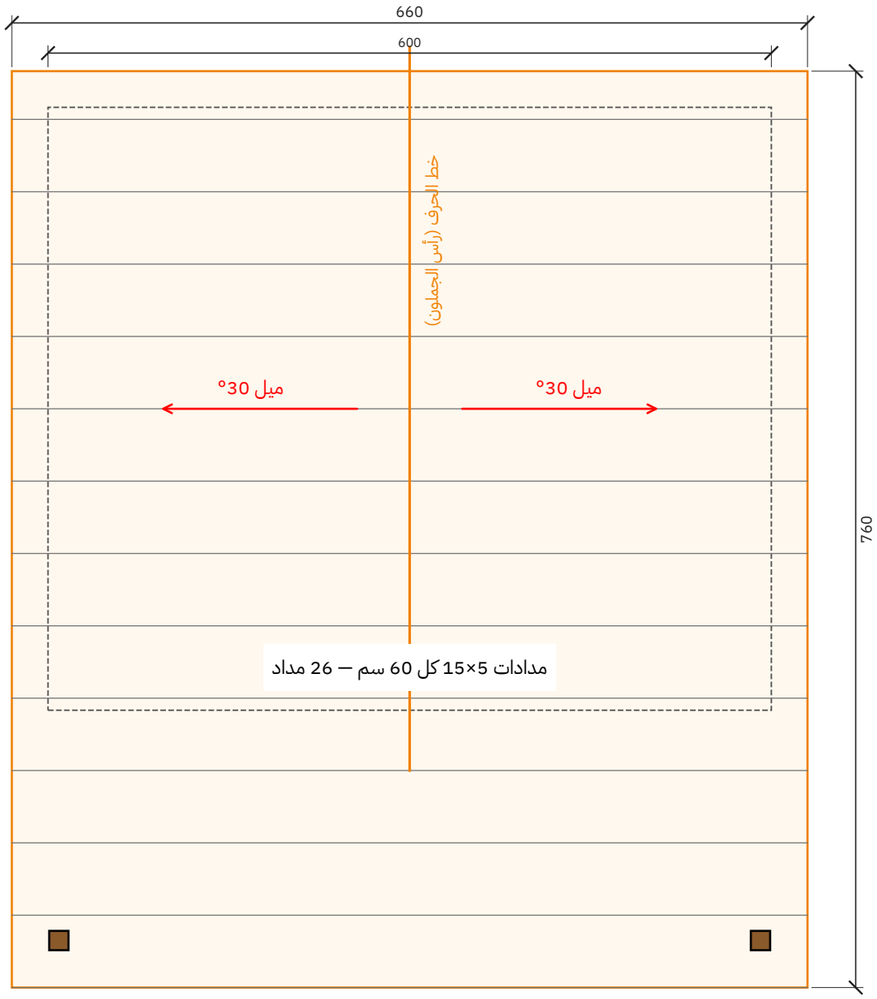


قطاع عرضي أ-أ

مقياس 1:50 | الوحدة: سم

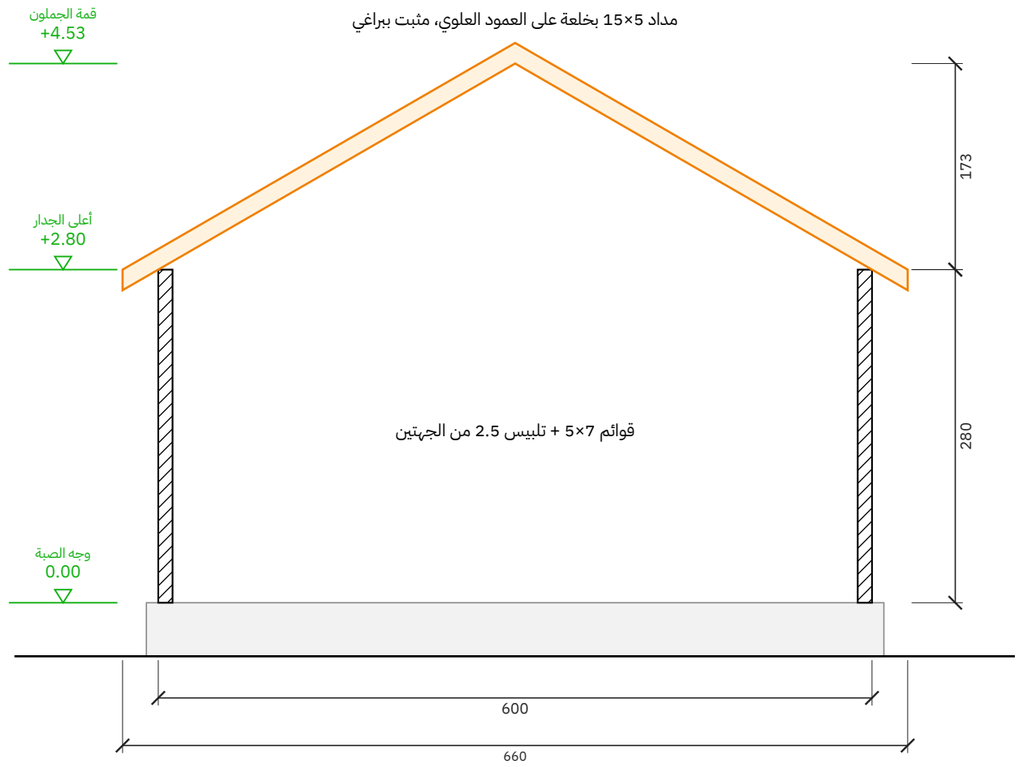

تفصيلة جلوس المداد على العلوي (1:5)

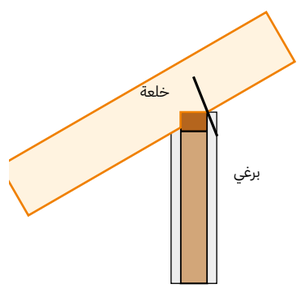

علوي 7×5 على قائم 7×5

المشروع / العميل	عنوان اللوحة	المقياس	التاريخ	رقم اللوحة
كوخ واجهة زجاج — صالة ومطبخ أمريكي وحمام — 6.00 × 5.00 م (30 م²) **عميل — كوخ 6×5**	**مسقط السقف والقطاع**	**1:50**	**2026-10-26**	**W-05 (5/12)**

مصنع وتد الأخشاب
Watad Wood Factory

جدول مقاسات الأبواب والشبابيك

مقاس الفتحة الصافي في الجدار - الوحدة: سم

الرمز	النوع	العرض (سم)	الارتفاع (سم)	ارتفاع الجلسة (سم)	العدد	الموقع
ب1	باب مزدوج	120	240	-	1	الأمامية (زجاج)
ب2	باب	70	210	-	1	الحمام
ز1	شباك	200	230	10	2	الأمامية (زجاج) 2
ش1	شباك	140	140	70	2	الشرقية - الغربية
ش2	شباك	120	80	115	1	الخلفية
ش3	شباك	50	50	170	1	الشرقية

الإجمالي: أبواب 2 - شبابيك 6

جدول المساحات وبيانات المشروع والتسعير

بيانات المشروع

البند	البيان
المشروع	كوخ واجهة زجاج — صالة ومطبخ أمريكي وحمام — 6.00 × 5.00 م (30 م²)
العميل	عميل — كوخ 6×5
الموقع	—
الاستخدام	استراحة
التاريخ	2026-10-26
نظام البناء	هيكل خشب 7×5 + تلبيس 2.5 سم من الجهتين
السقف	جملون 30° — قرميد معدني

جدول المساحات

م	الفراغ	الأبعاد (م)	المساحة (م2)
1	الصالة	5.76 × 2.82	16.24
2	المطبخ الأمريكي	3.94 × 1.82	7.17
3	حمام	1.70 × 1.82	3.09
	المساحة الصافية الداخلية		**26.51**
	التراس المسقوف	**6.00 × 2.00**	**12.00**
	المساحة الإجمالية المبنية	**6.00 × 5.00**	**30.00**
	المساحة الكلية (المبنية + التراس)		**42.00**


التسعير المفصّل

البند	المبلغ (ريال)
الكوخ المبني 30.00 م² × 1,400	42,000
التراس المسقوف (6.00 × 2.00) — 12 م² × 1,400	16,800
الإجمالي (ريال)	**58,800**


ملاحظات:

- السعر 1,400 ريال/م² على مساحة الكوخ — التراس المسقوف بنفس سعر المتر.
- الصبة والتمديدات الخارجية على العميل ما لم يُذكر غير ذلك.

تأطير جدار جنوب — الطول 588 سم، الارتفاع 280 سم

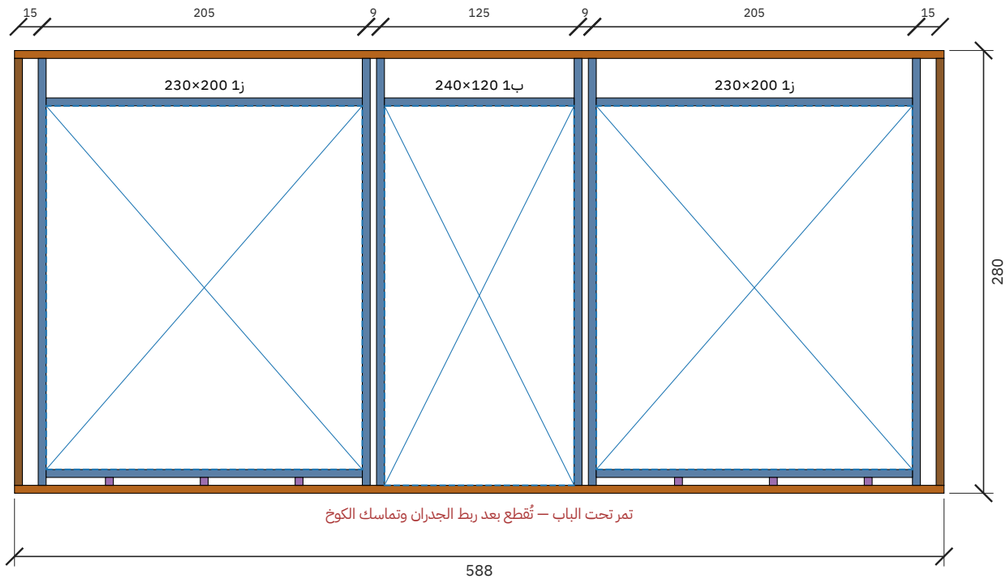


تأطير جدار شرق — الطول 488 سم، الارتفاع 280 سم

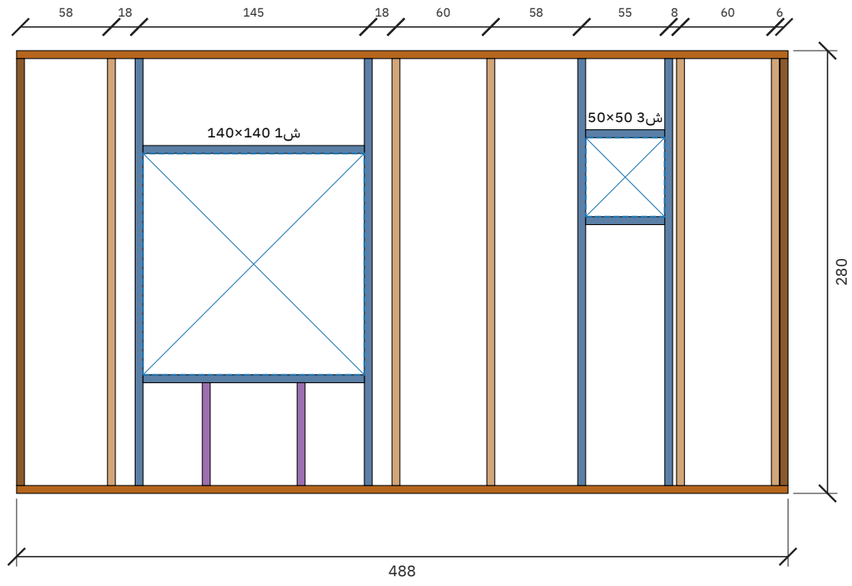


عمود قصير | جلسة شباك | رأس فتحة | جنب فتحة | عمود زاوية | عمود | علوي | قاعدة سفلية

مصنع وتد الأخشاب Watad Wood Factory	المشروع / العميل كوخ واجهة زجاج — صالة ومطبخ أمريكي وحمام — 6.00 × 5.00 م (30 م²) عميل — كوخ 6×5	عنوان اللوحة لوحات التأطير (للورشة)	المقياس —	التاريخ 2026-10-26	رقم اللوحة W-08 (8/12)

تأطير جدار شمال — الطول 588 سم، الارتفاع 280 سم

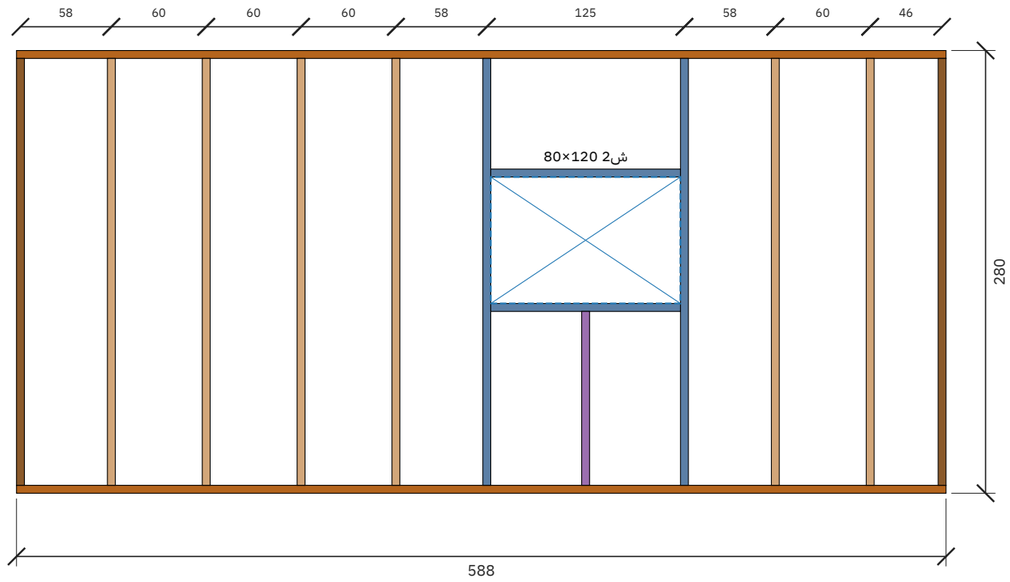


تأطير جدار غرب — الطول 488 سم، الارتفاع 280 سم

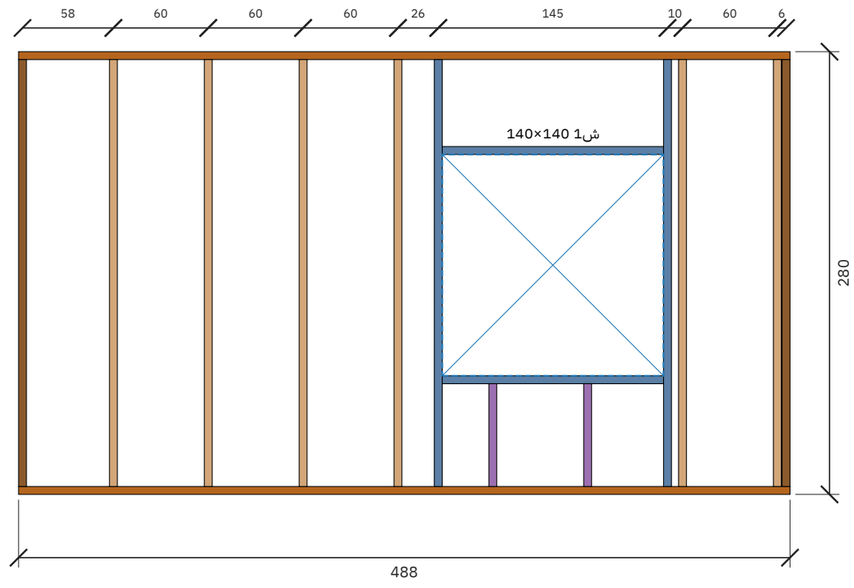


قاعدة سفلية | علوي | عمود | عمود زاوية | جنب فتحة | رأس فتحة | جلسة شباك | عمود قصير

مصنع وتد الأخشاب Watad Wood Factory	المشروع / العميل كوخ واجهة زجاج — صالة ومطبخ أمريكي وحمام — 6.00 × 5.00 م (30 م²) عميل — كوخ 6×5	عنوان اللوحة لوحات التأطير (للورشة)	المقياس —	التاريخ 2026-10-26	رقم اللوحة W-09 (9/12)

تأطير جدار جدار الحمام — الطول 182 سم، الارتفاع 280 سم (داخلي)

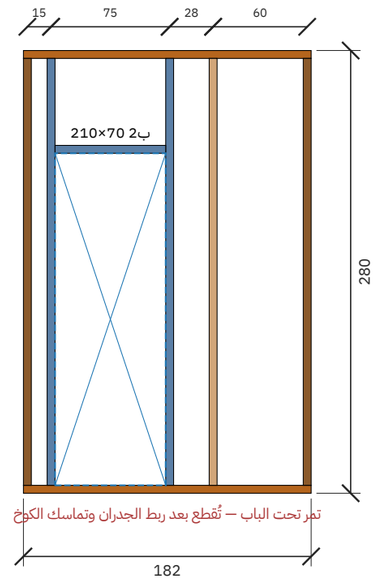

تأطير جدار جدار الحمام الغربي — الطول 194 سم، الارتفاع 280 سم (داخلي)

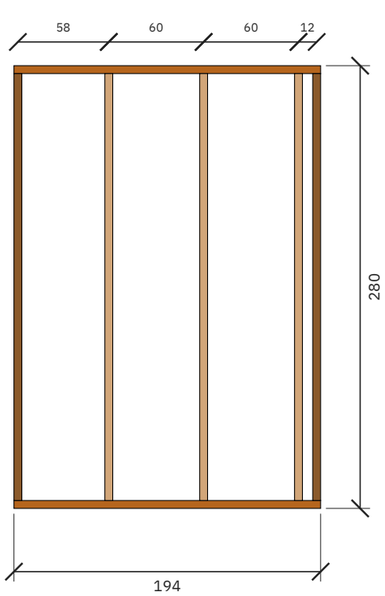

عمود قصير | جلسة شباك | رأس فتحة | جنب فتحة | عمود زاوية | عمود | علوي | قاعدة سفلية

المشروع / العميل	عنوان اللوحة	المقياس	التاريخ	رقم اللوحة
كوخ واجهة زجاج — صالة ومطبخ أمريكي وحمام — 6.00 × 5.00 م (30 م²) عميل — كوخ 6×5	لوحات التأطير (للورشة)	—	2026-10-26	W-10 (10/12)

مصنع وتد الأخشاب
Watad Wood Factory

جدول الكميات وخطة تقطيع الطبليات

البند	القيمة
الارتفاع المطلوب / المعتمد	280 / 280 سم
السقف	جملون 30° — أعلى نقطة 453 سم من وجه الصبة
المدادات 5×15	26 مداد (13 لكل جهة) × حتى 381 سم — من طبلية 480
طبليات الطريقة الأولى (مداد + عمود)	26 طبلية × 480 سم
طبليات الطريقة الثانية (3 أعمدة)	13 طبلية × 320 سم
إجمالي الطبليات 5×22.5	39
إجمالي قطع 5×7	86
قائمة تقطيع 5×7	588سم×4 | 488سم×4 | 270سم×49 | 200سم×4 | 194سم×2 | 182سم×2 | 140سم×4 | 120سم×3 | 110سم×1
	70سم×1 | 65سم×4 | 50سم×2 | 5سم×6
ألواح تلبيس 2.5 سم	122 لوح × 400 سم (مجموع الصفوف 440.0 م، 12 وجه)
أسمنت بورد 12 مم (122×244)	16 لوح (داخل دورات المياه)
العزل	73 لوح فوم صخري 80
الصبة	يجهزها العميل — 20 سم، مفرغة تحت دورات المياه

مراجعة التصميم مقابل قواعد المصنع

النوع	البند	التفاصيل	المقترح
ملاحظة	بحر المدادات	أطول بحر بدون جدار داخلي يحمل المداد: جهة أ: 300 سم، جهة ب: 300 سم. يحتاج رقم المصنع لأقصى بحر مسموح لتحديد المدادات اللي تُقوّى 20×5.	
ملاحظة	الصبة والدرج	ارتفاع الصبة 45 سم ← 3 درجة بقائمة 15.0 سم.	
ملاحظة	مناسيب رؤوس الفتحات	رؤوس الأبواب والشبابيك على مناسيب مختلفة: 195، 210، 220، 240 سم.	
سؤال	يحتاج تأكيد	أقصى بحر للمداد بدون جدار داخلي قبل إضافة تقوية 5×7 (مداد 20×5)؟	
سؤال	يحتاج تأكيد	التغطية الصافية للوح التلبيس بعد التعشيق (مستنتجة مؤقتاً 18.67 سم من 280/15)؟	
سؤال	يحتاج تأكيد	هل يوضع أعمدة قصيرة فوق رأس الشباك/الباب إلى العلوي؟	
سؤال	يحتاج تأكيد	مكان الوصلة في القاعدة والعلوي إذا الجدار أطول من الطبلية؟	