

المسقط الأفقي مع الفرش

الأبعاد بالسنتيمتر - الجدران: قوائم 7×5 + تلبيس 2.5 من الجهتين (12 سم)

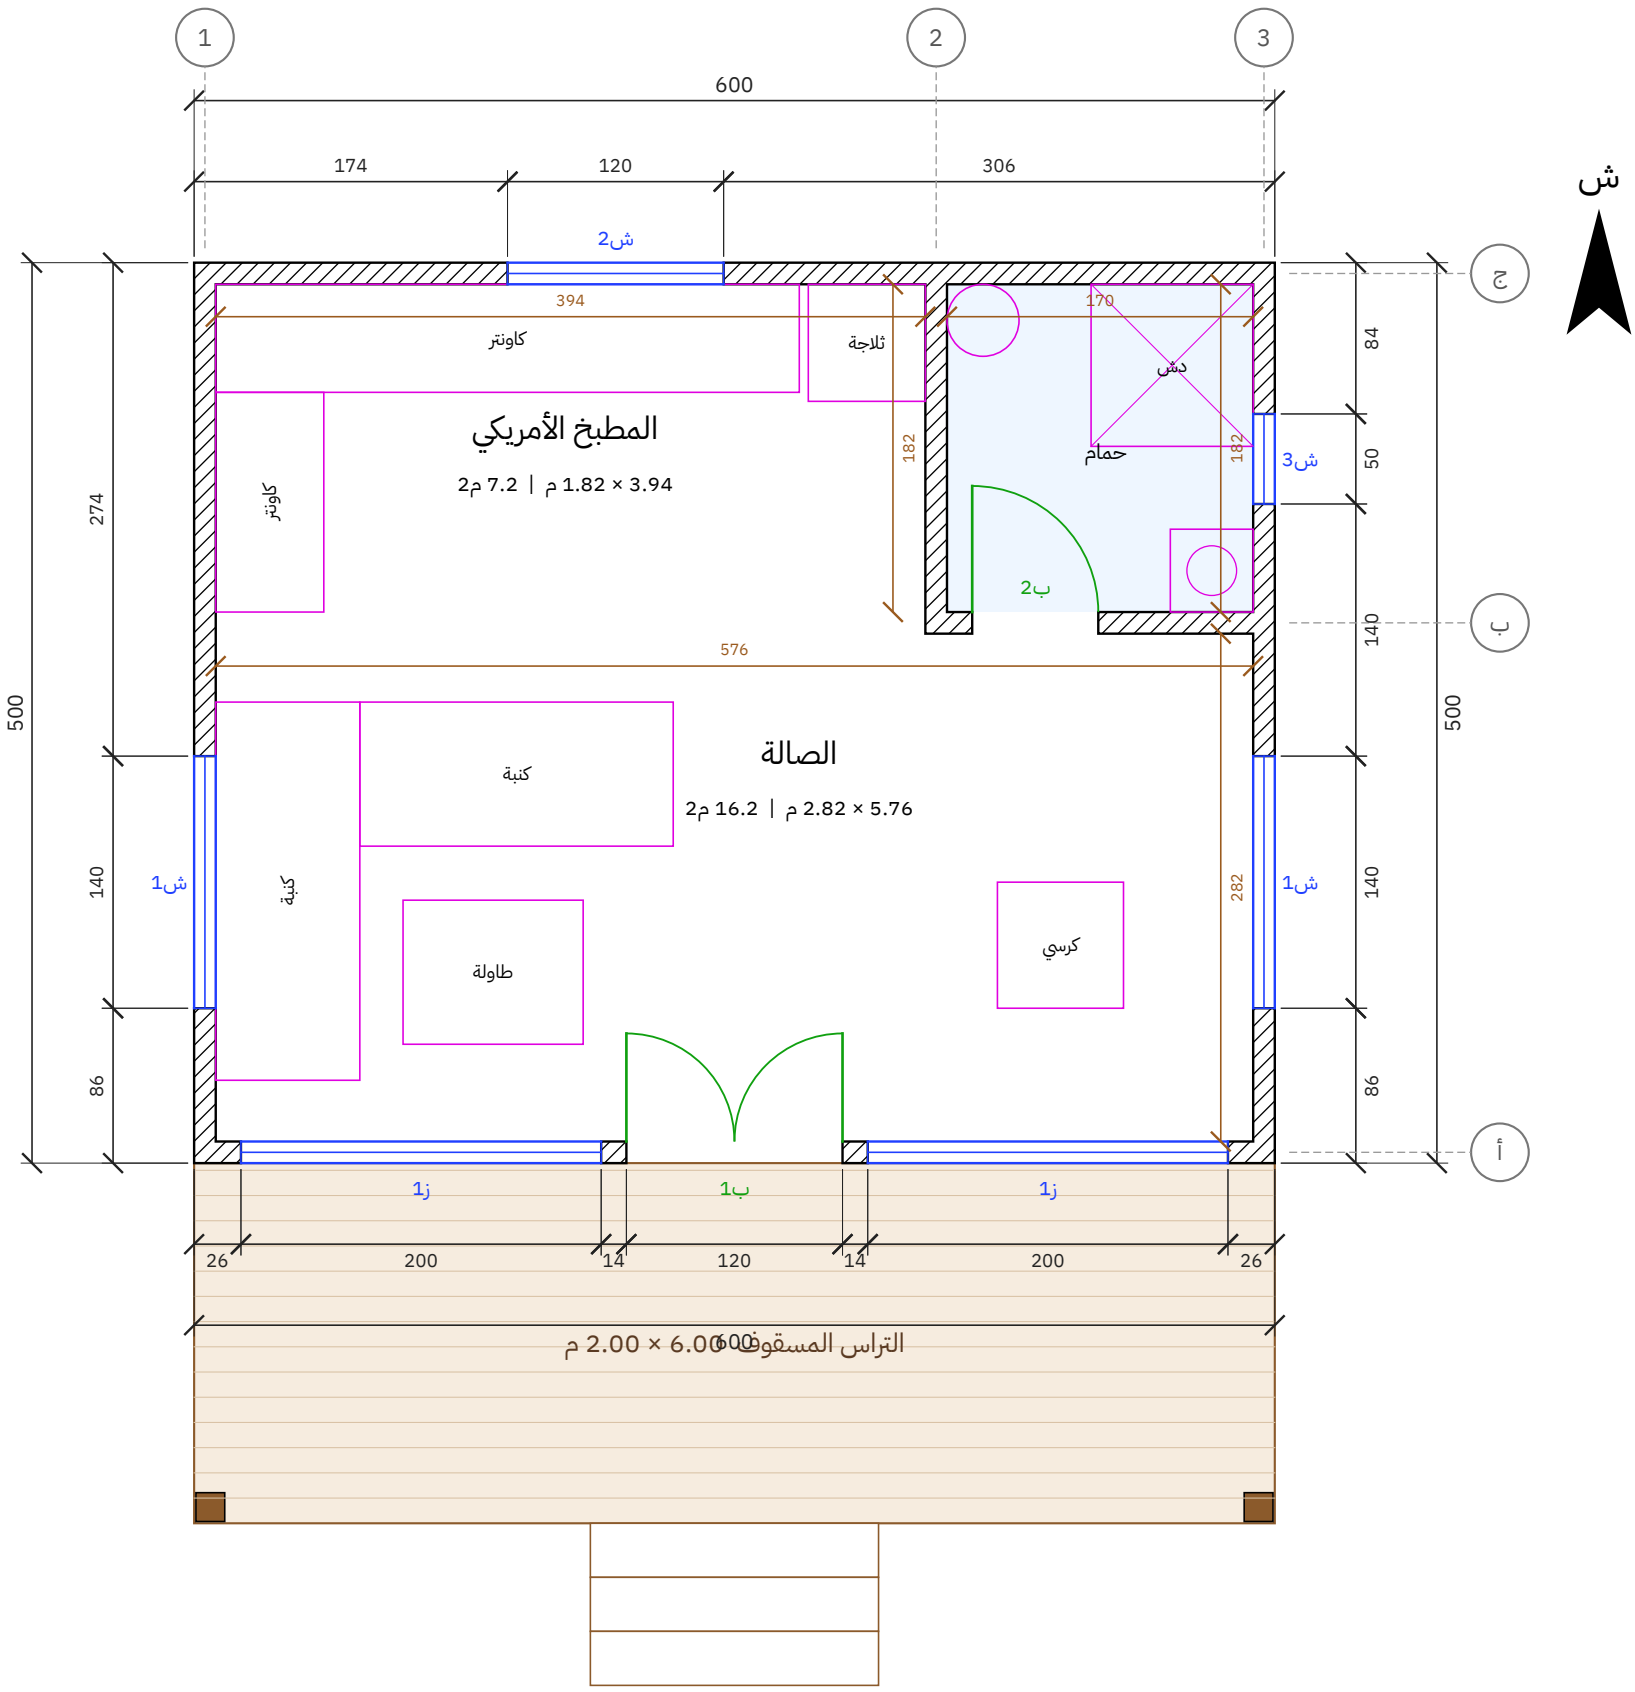


3 درجات × 15 سم

مصنع وتد الأخشاب Watad Wood Factory	المشروع / العميل كوخ واجهة زجاج – صالة ومطبخ أمريكي وحمام – 6.00 × 5.00 م (30 م²) عميل – كوخ 6×5	عنوان اللوحة المسقط الأفقي	المقياس 1:50	التاريخ 2026-10-26	رقم اللوحة A-01 (1/9)

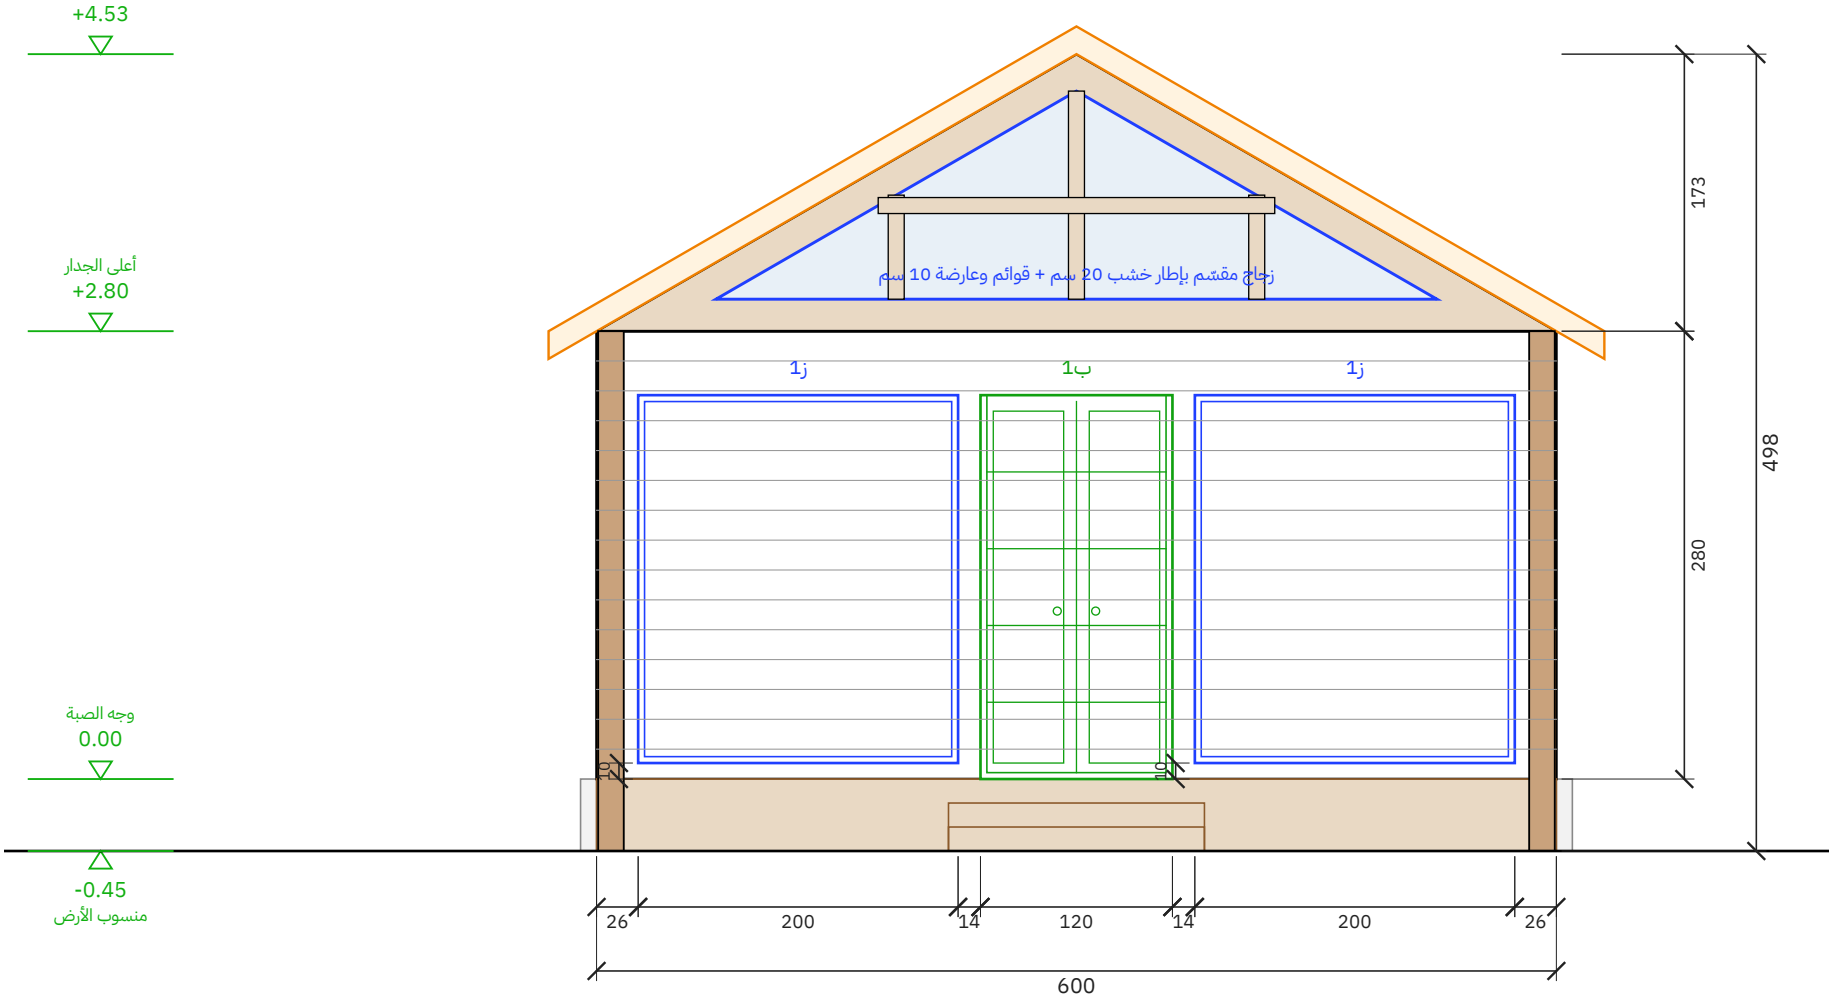

الواجهة الأمامية (زجاج)

مقياس 1:50 | الوحدة: سم

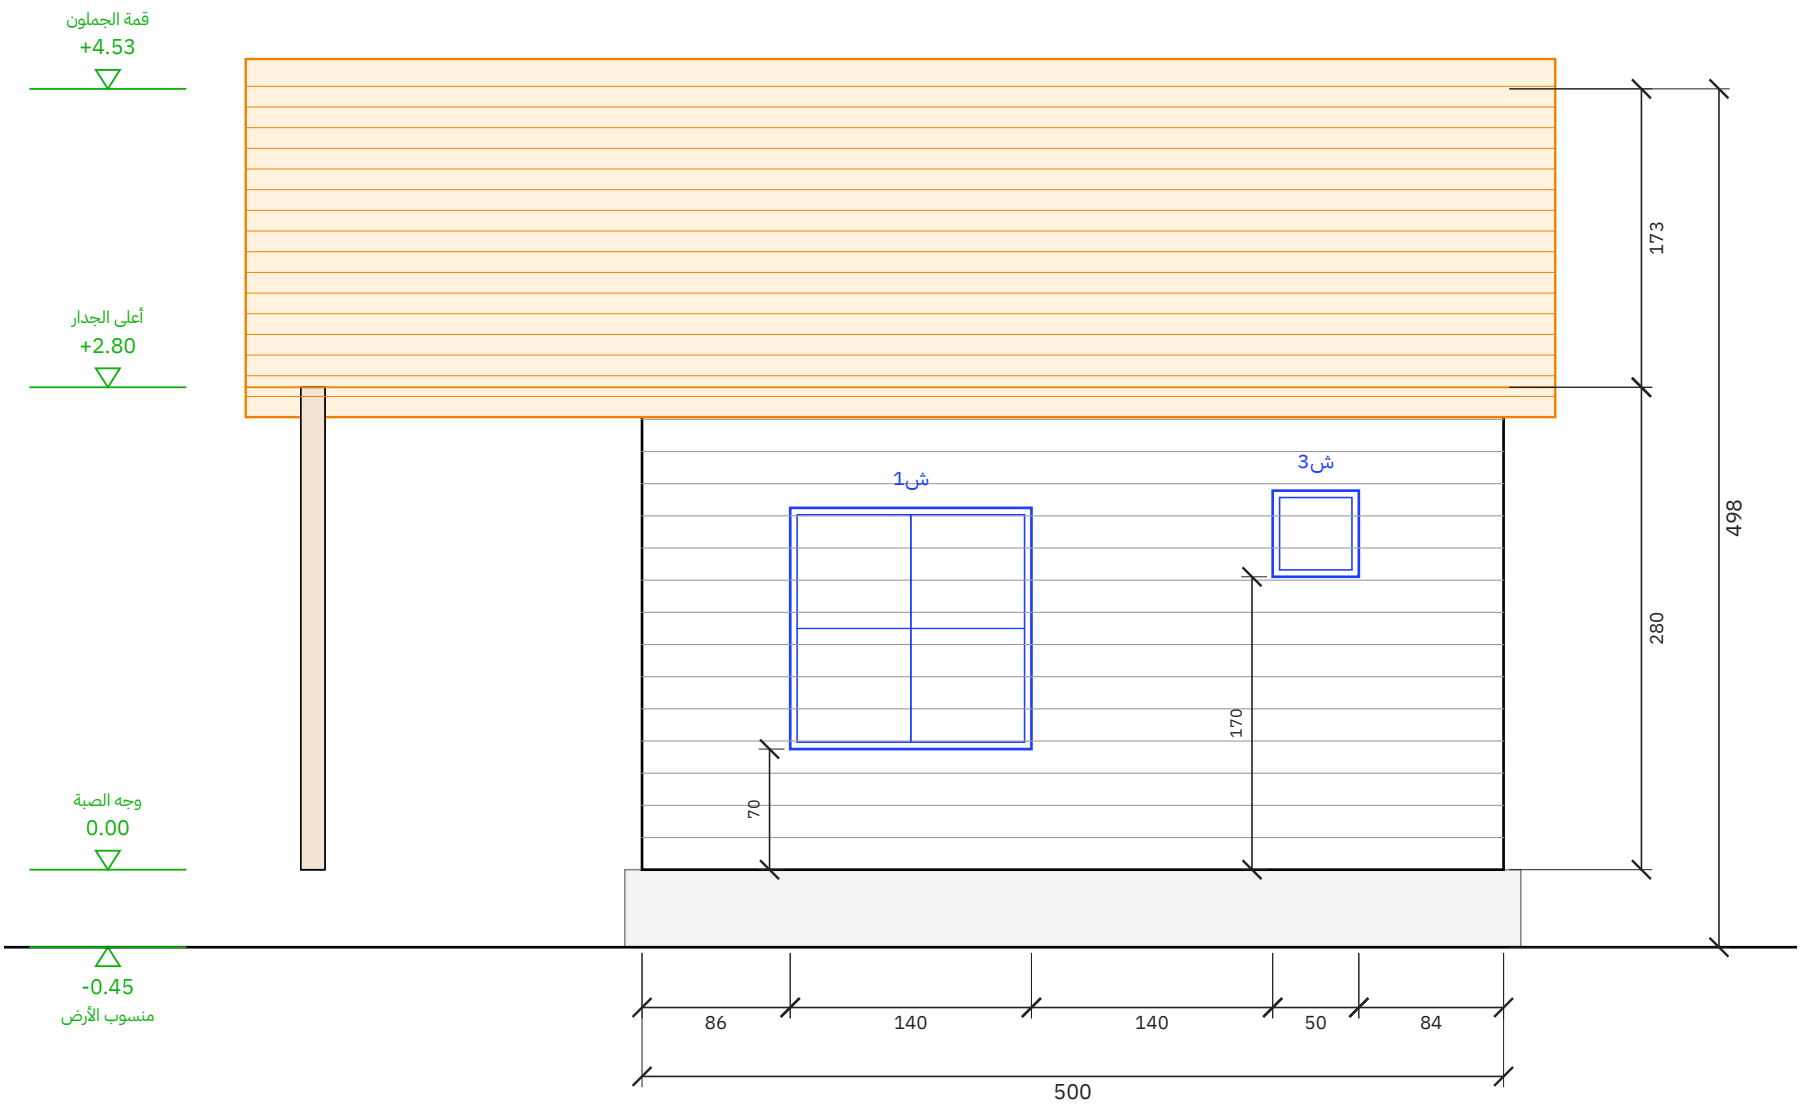


الواجهة الشرقية

مقياس 1:50 | الوحدة: سم


المشروع / العميل	عنوان اللوحة	المقياس	التاريخ	رقم اللوحة
كوخ واجهة زجاج – صالة ومطبخ أمريكي وحمام – 6.00 × 5.00 م (30 م²) عميل – كوخ 6×5	الواجهة الأمامية (زجاج) والواجهة الشرقية	1:50	2026-10-26	A-02 (2/9)

مصنع وتد الأخشاب
Watad Wood Factory

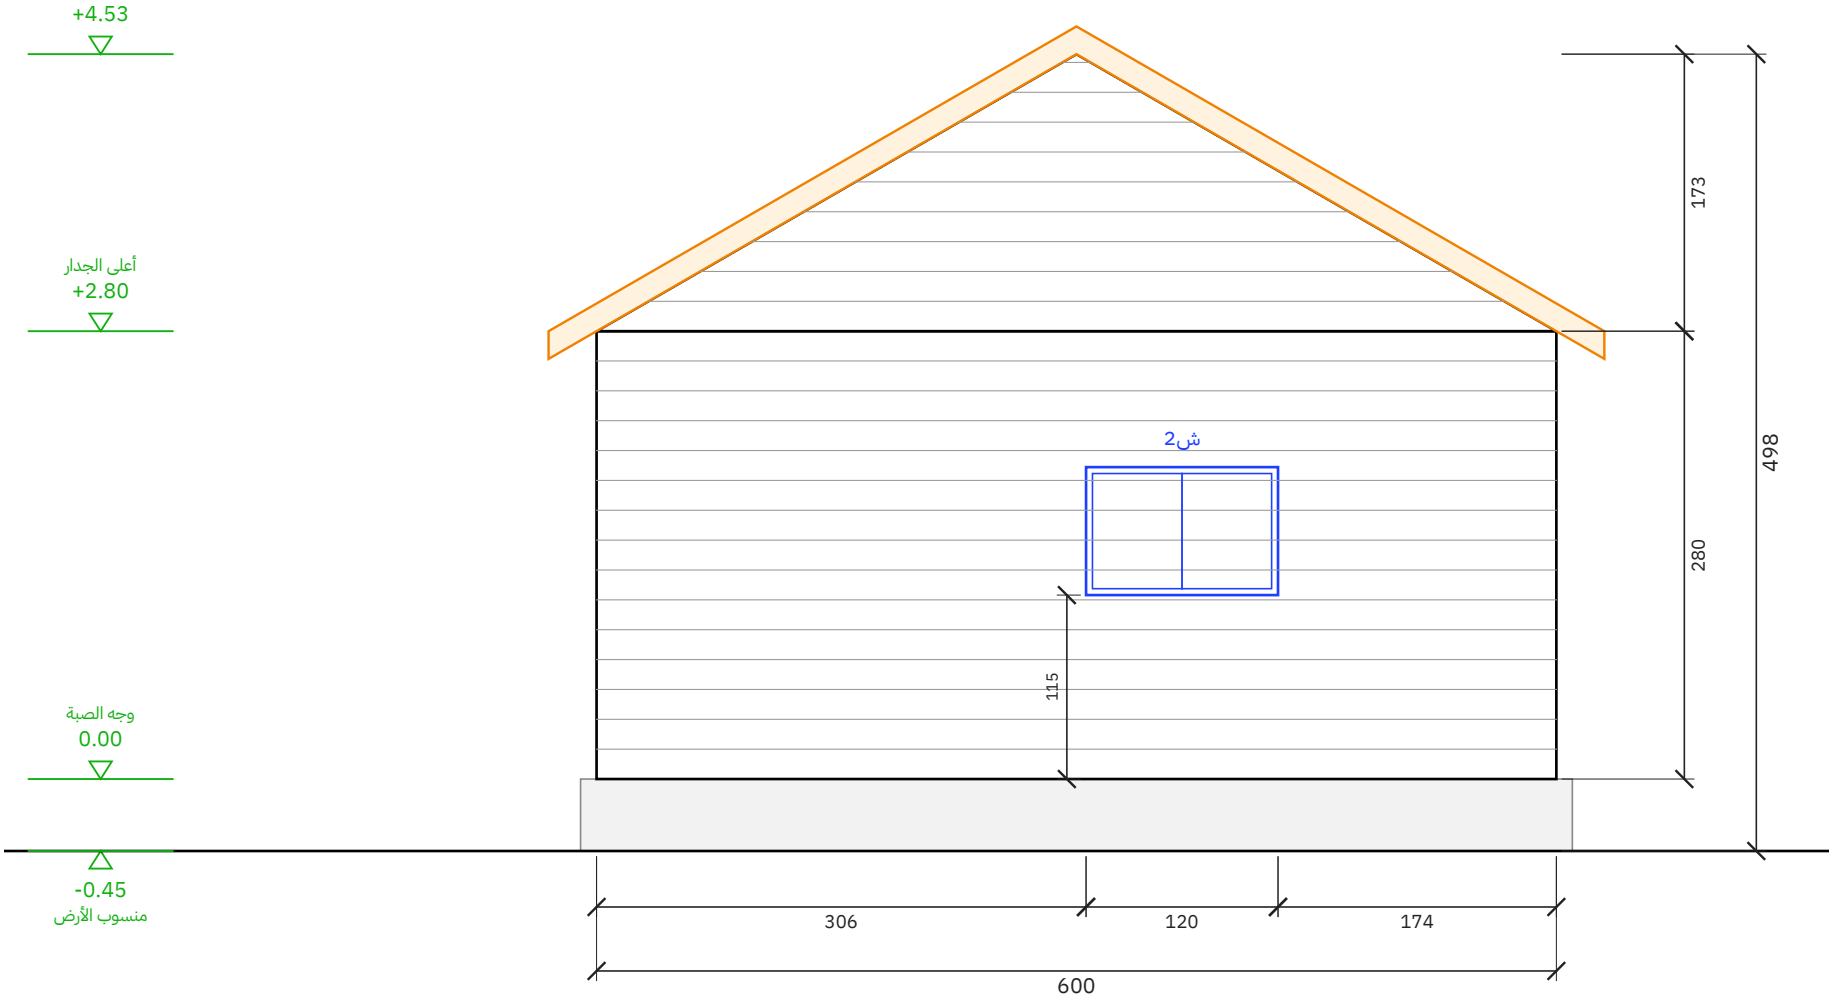

الواجهة الخلفية

مقياس 1:50 | الوحدة: سم

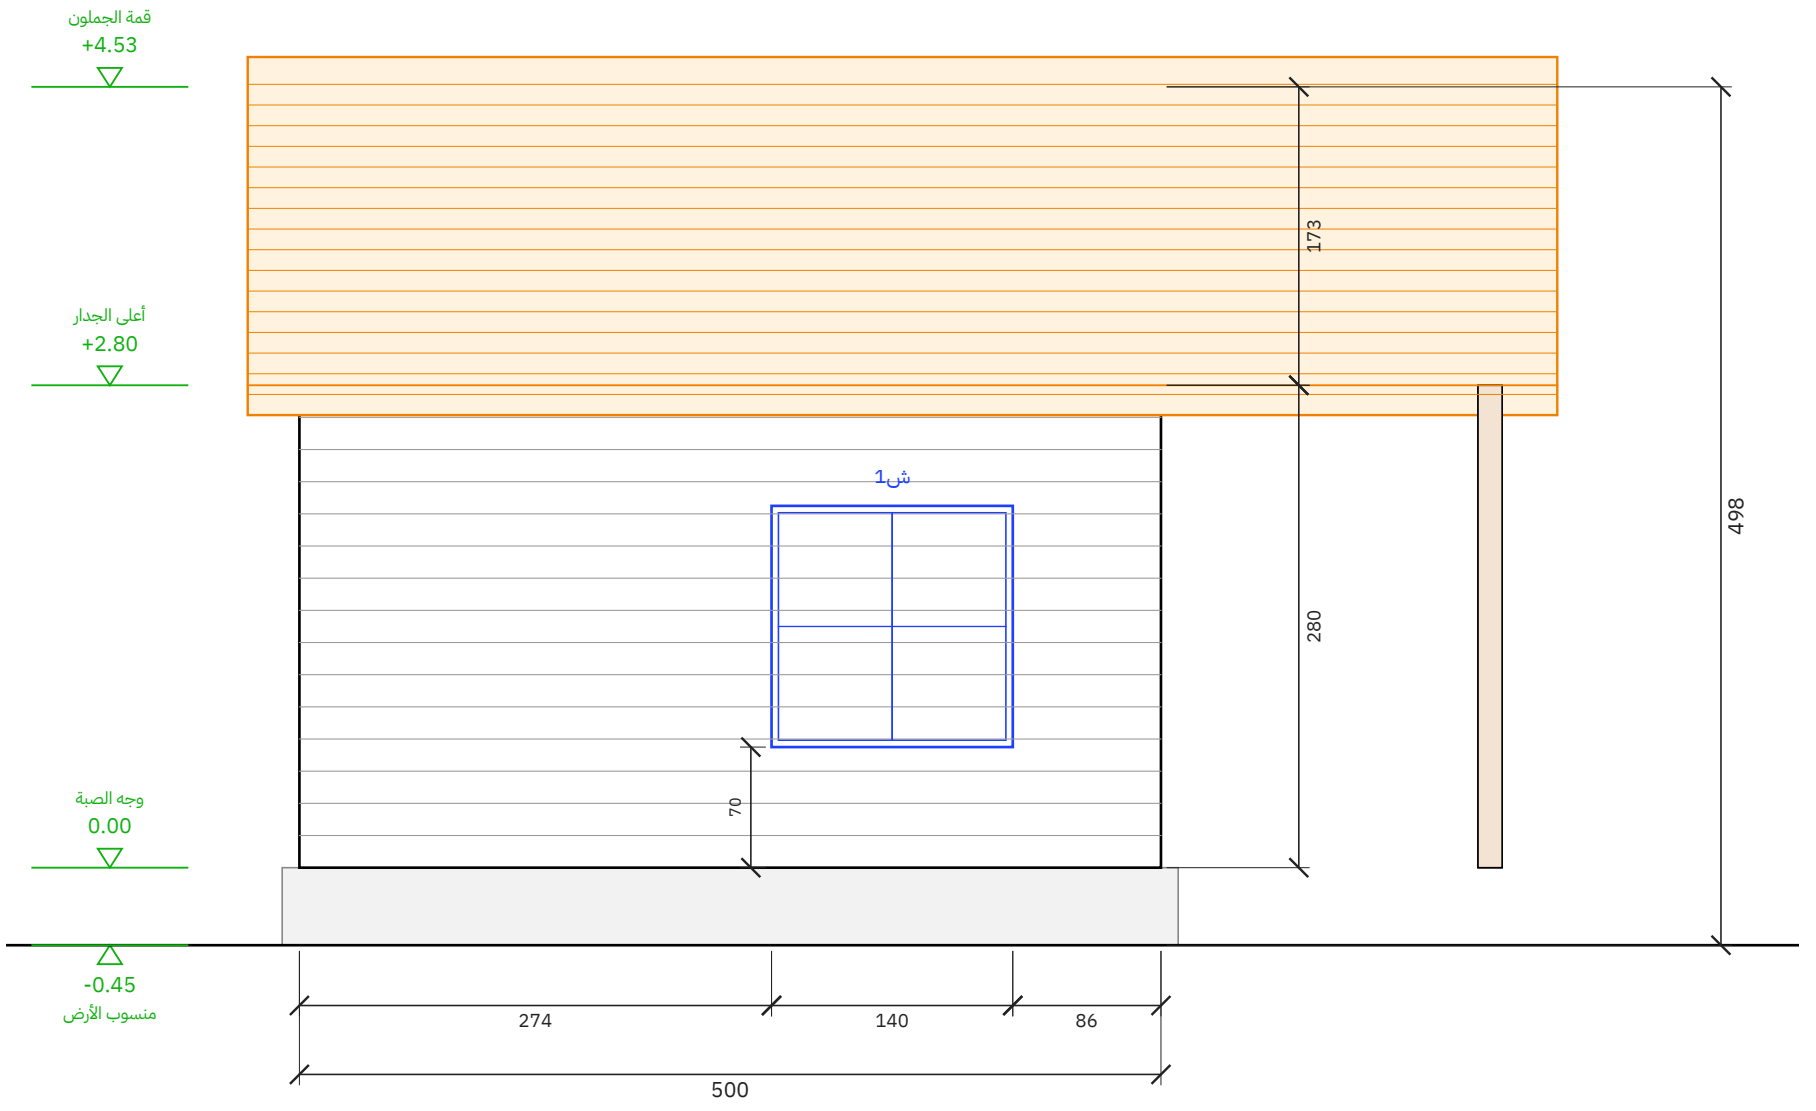

الواجهة الغربية


مقياس 1:50 | الوحدة: سم

المشروع / العميل	عنوان اللوحة	المقياس	التاريخ	رقم اللوحة
كوخ واجهة زجاج – صالة ومطبخ أمريكي وحمام – 6.00 × 5.00 م (30 م²) عميل – كوخ 6×5	الواجهة الخلفية والواجهة الغربية	1:50	2026-10-26	A-03 (3/9)

مصنع وتد الأخشاب
Watad Wood Factory


مسقط السقف (جملون)

رفرف 30 سم من كل جهة | مقياس 1:50

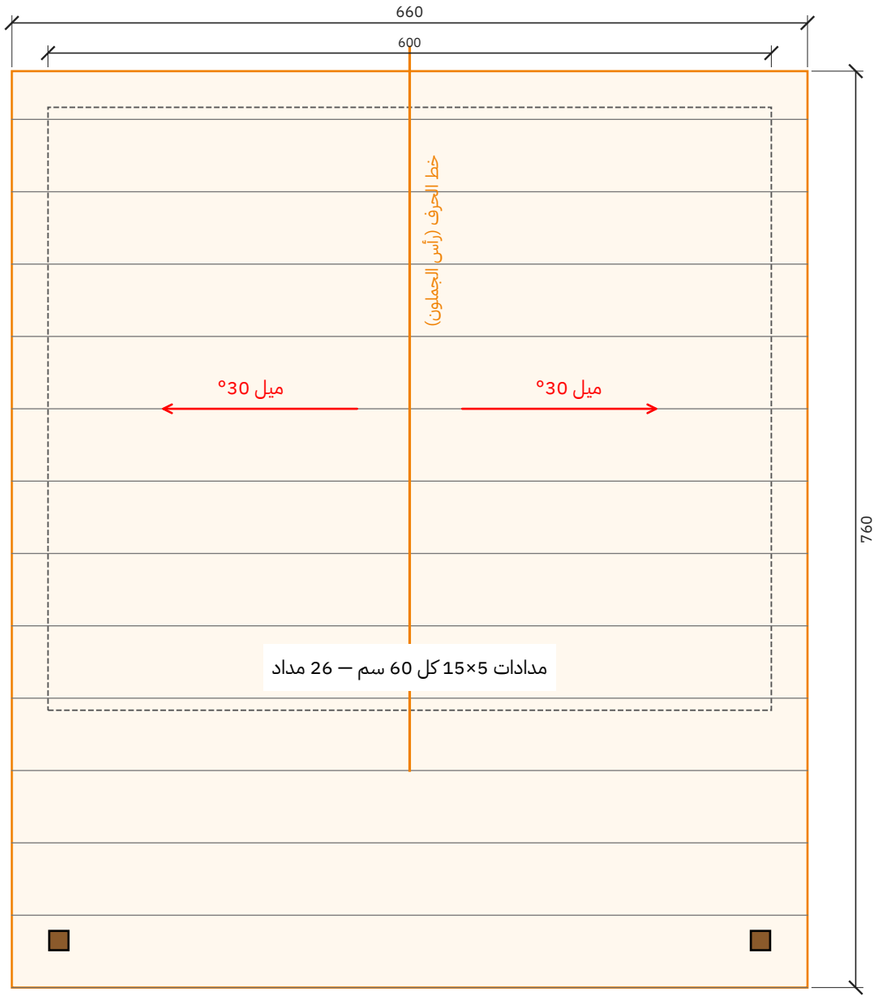


قطاع عرضي أ-أ

مقياس 1:50 | الوحدة: سم

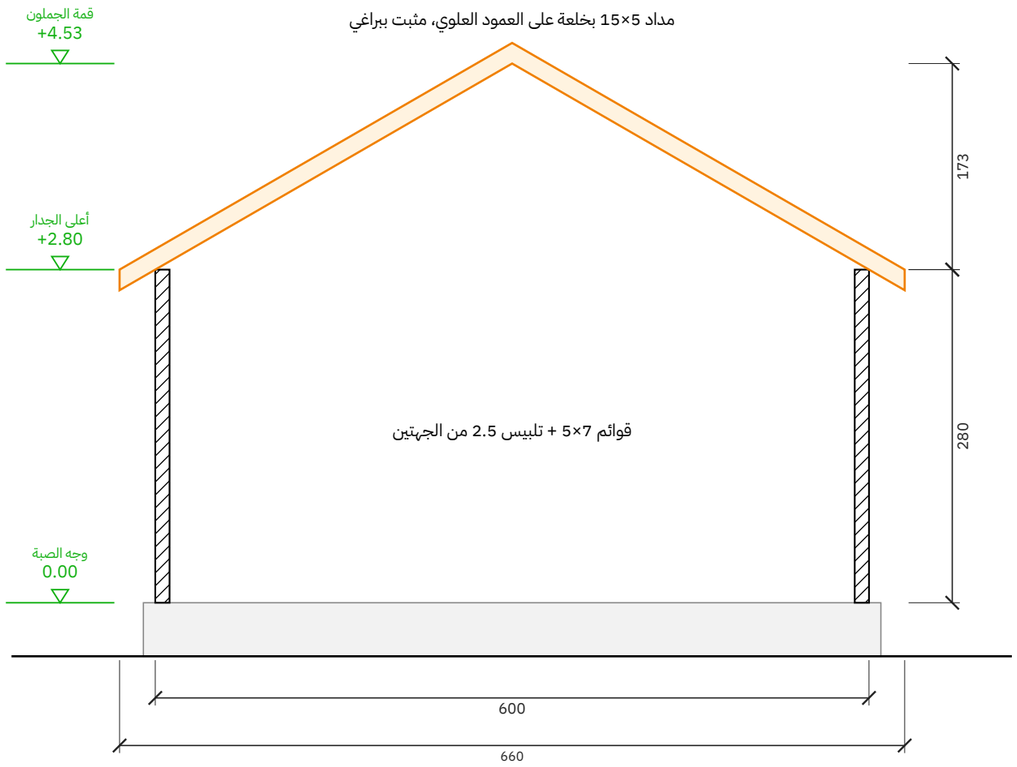

تفصيلة جلوس المداد على العلوي (1:5)

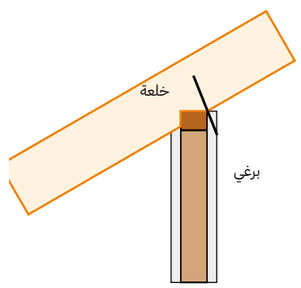

علوي 7×5 على قائم 7×5

المشروع / العميل	عنوان اللوحة	المقياس	التاريخ	رقم اللوحة
كوخ واجهة زجاج — صالة ومطبخ أمريكي وحمام — 6.00 × 5.00 م (30 م²) **عميل — كوخ 6×5**	**مسقط السقف والقطاع**	**1:50**	**2026-10-26**	**A-04 (4/9)**

مصنع وتد الأخشاب
Watad Wood Factory

جدول مقاسات الأبواب والشبابيك

مقاس الفتحة الصافي في الجدار - الوحدة: سم

الرمز	النوع	العرض (سم)	الارتفاع (سم)	ارتفاع الجلسة (سم)	العدد	الموقع
ب1	باب مزدوج	120	240	-	1	الأمامية (زجاج)
ب2	باب	70	210	-	1	الحمام
ز1	شباك	200	230	10	2	الأمامية (زجاج) 2
ش1	شباك	140	140	70	2	الشرقية - الغربية
ش2	شباك	120	80	115	1	الخلفية
ش3	شباك	50	50	170	1	الشرقية

الإجمالي: أبواب 2 - شبابيك 6

جدول المساحات وبيانات المشروع والتسعير

بيانات المشروع

البند	البيان
المشروع	كوخ واجهة زجاج — صالة ومطبخ أمريكي وحمام — 6.00 × 5.00 م (30 م²)
العميل	عميل — كوخ 6×5
الموقع	—
الاستخدام	استراحة
التاريخ	2026-10-26
نظام البناء	هيكل خشب 7×5 + تلبيس 2.5 سم من الجهتين
السقف	جملون 30° — قرميد معدني

جدول المساحات

م	الفراغ	الأبعاد (م)	المساحة (م2)
1	الصالة	5.76 × 2.82	16.24
2	المطبخ الأمريكي	3.94 × 1.82	7.17
3	حمام	1.70 × 1.82	3.09
	المساحة الصافية الداخلية		**26.51**
	التراس المسقوف	**6.00 × 2.00**	**12.00**
	المساحة الإجمالية المبنية	**6.00 × 5.00**	**30.00**
	المساحة الكلية (المبنية + التراس)		**42.00**

التسعير المفصّل

البند	المبلغ (ريال)
الكوخ المبني 30.00 م² × 1,400	42,000
التراس المسقوف (6.00 × 2.00) — 12 م² × 1,400	16,800
الإجمالي (ريال)	**58,800**

ملاحظات:

- السعر 1,400 ريال/م² على مساحة الكوخ — التراس المسقوف بنفس سعر المتر.
- الصبة والتمديدات الخارجية على العميل ما لم يُذكر غير ذلك.

لقطات المنظور الخارجي

المنظور الأمامي



منظور أمامي من اليسار



منظور أمامي من اليمين




المنظور الخلفي



منظور خلفي من اليمين



منظر علوي

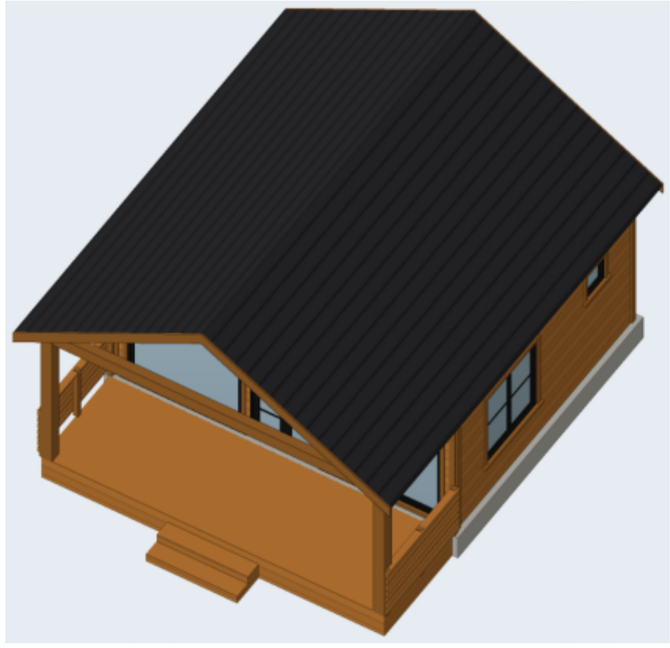


المشروع / العميل كوخ واجهة زجاج – صالة ومطبخ أمريكي وحمام – 6.00 × 5.00 م (30 م²) عميل – كوخ 6×5	عنوان اللوحة لقطات المنظور	المقياس –	التاريخ 2026-10-26	رقم اللوحة A-07 (7/9)

مصنع وتد الأخشاب
Watad Wood Factory

المقطع العلوي بالفرش

مقطع أفقي على ارتفاع 1.90 م — توزيع الفرش ومسار الحركة

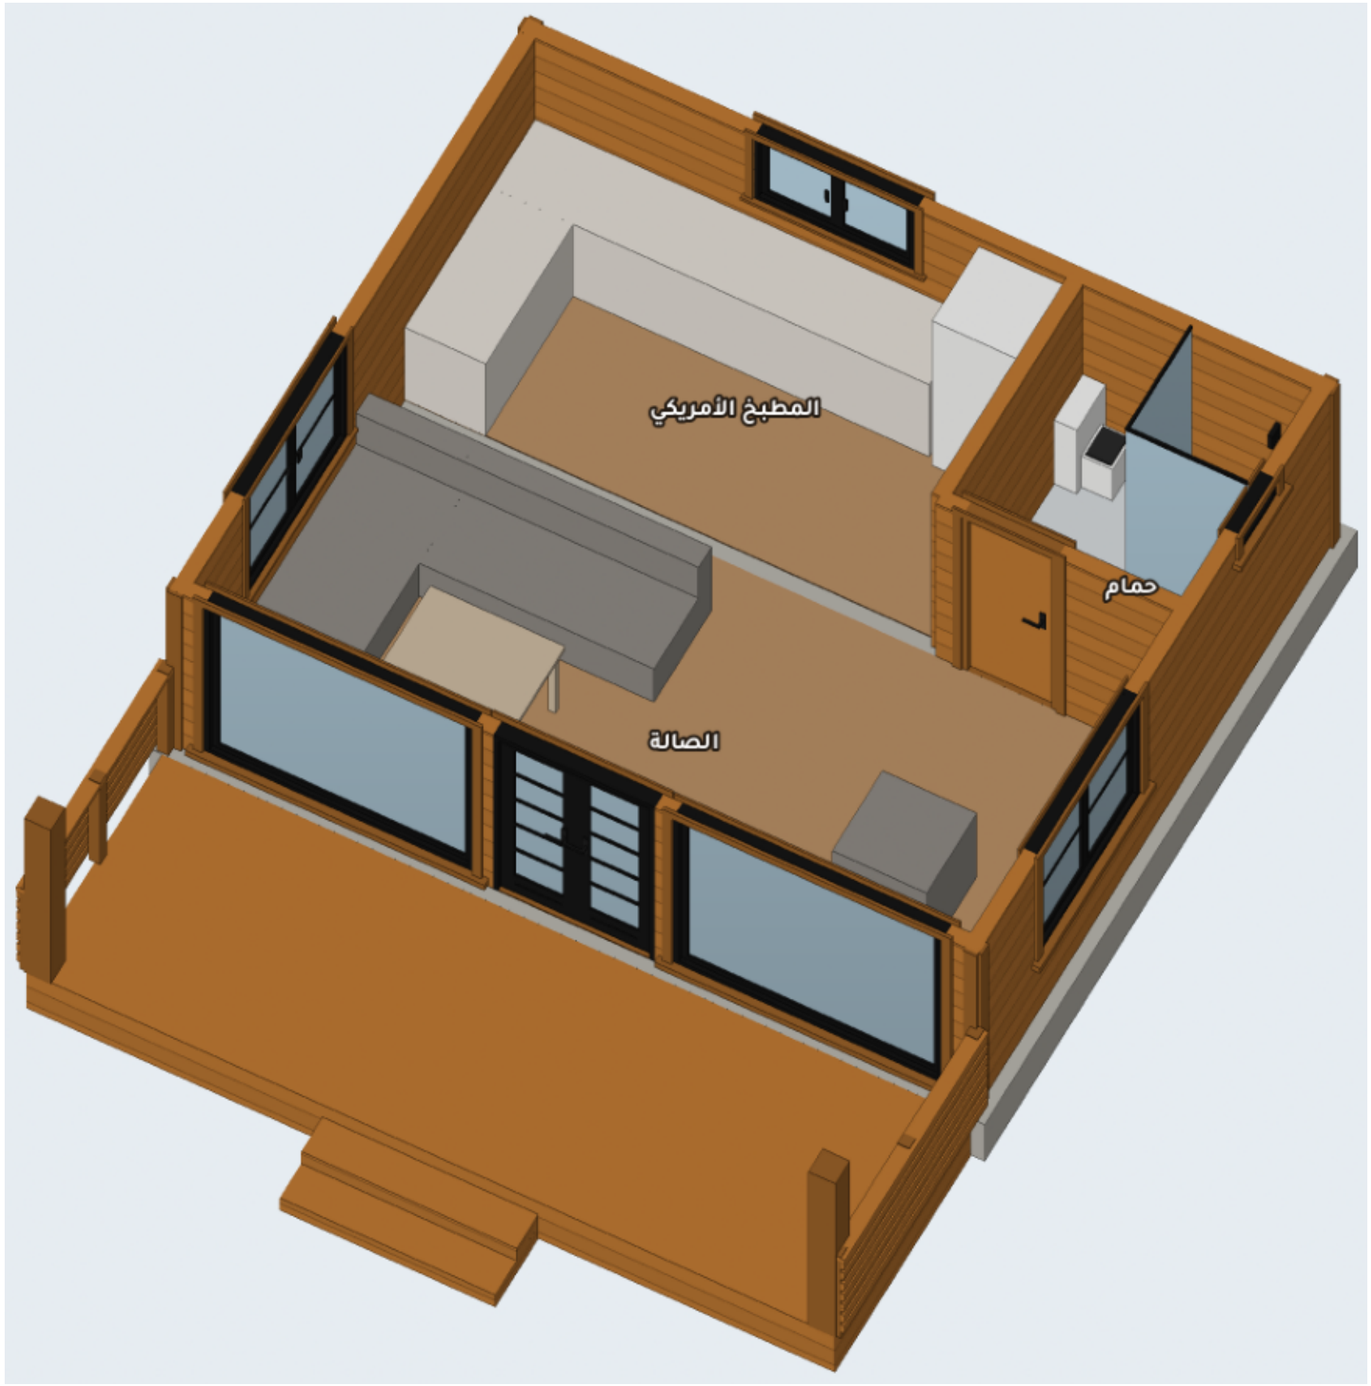

المشروع / العميل	عنوان اللوحة	المقياس	التاريخ	رقم اللوحة
كوخ واجهة زجاج — صالة ومطبخ أمريكي وحمام — 6.00 × 5.00 م (30 م²) عميل — كوخ 6×5	المقطع العلوي بالفرش	—	2026-10-26	A-08 (8/9)

مصنع وتد الأخشاب
Watad Wood Factory

المنظور ثلاثي الأبعاد والمواد

النمط: جوزي غامق + إطارات سوداء — رندر واقعي بخامات حقيقية



جدول المواد والألوان

الخشب / الصبغة

صبغة عسلي / سيدر

القرميد

قرميد رمادي غامق

الزجاج

زجاج شفاف

إطارات الشبابيك والأبواب

إطار ألمنيوم أسود

الكنار والزوايا

نفس الصبغة أغمق درجة


الصبة

خرسانة 45 سم


الدربزين: ألواح أفقية متقاربة (عصري)

تقسيم الشبابيك: بدون | الباب الرئيسي: زجاج بتقسيمات (فرنسي)

أنواع الدربزين المعتمدة (من مشاريع المصنع)

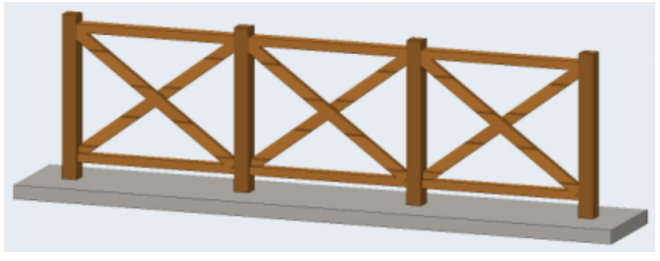

تقاطع X (صورة 5)

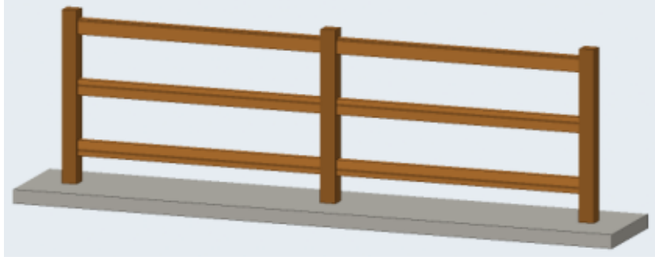

3 مرابيع أفقية (صورة 2)



قوائم رأسية متقاربة (صورة 1)

المشروع / العميل	عنوان اللوحة	المقياس	التاريخ	رقم اللوحة
كوخ واجهة زجاج — صالة ومطبخ أمريكي وحمام — 6.00 × 5.00 م (30 م²) **عميل — كوخ 6×5**	**المنظور والمواد**	**—**	**2026-10-26**	**A-09 (9/9)**

مصنع وتد الأخشاب
Watad Wood Factory