

المسقط الأفقي مع الفرش

الأبعاد بالسنتيمتر - الجدران: قوائم 7×5 + تلبيس 2.5 من الجهتين (12 سم)

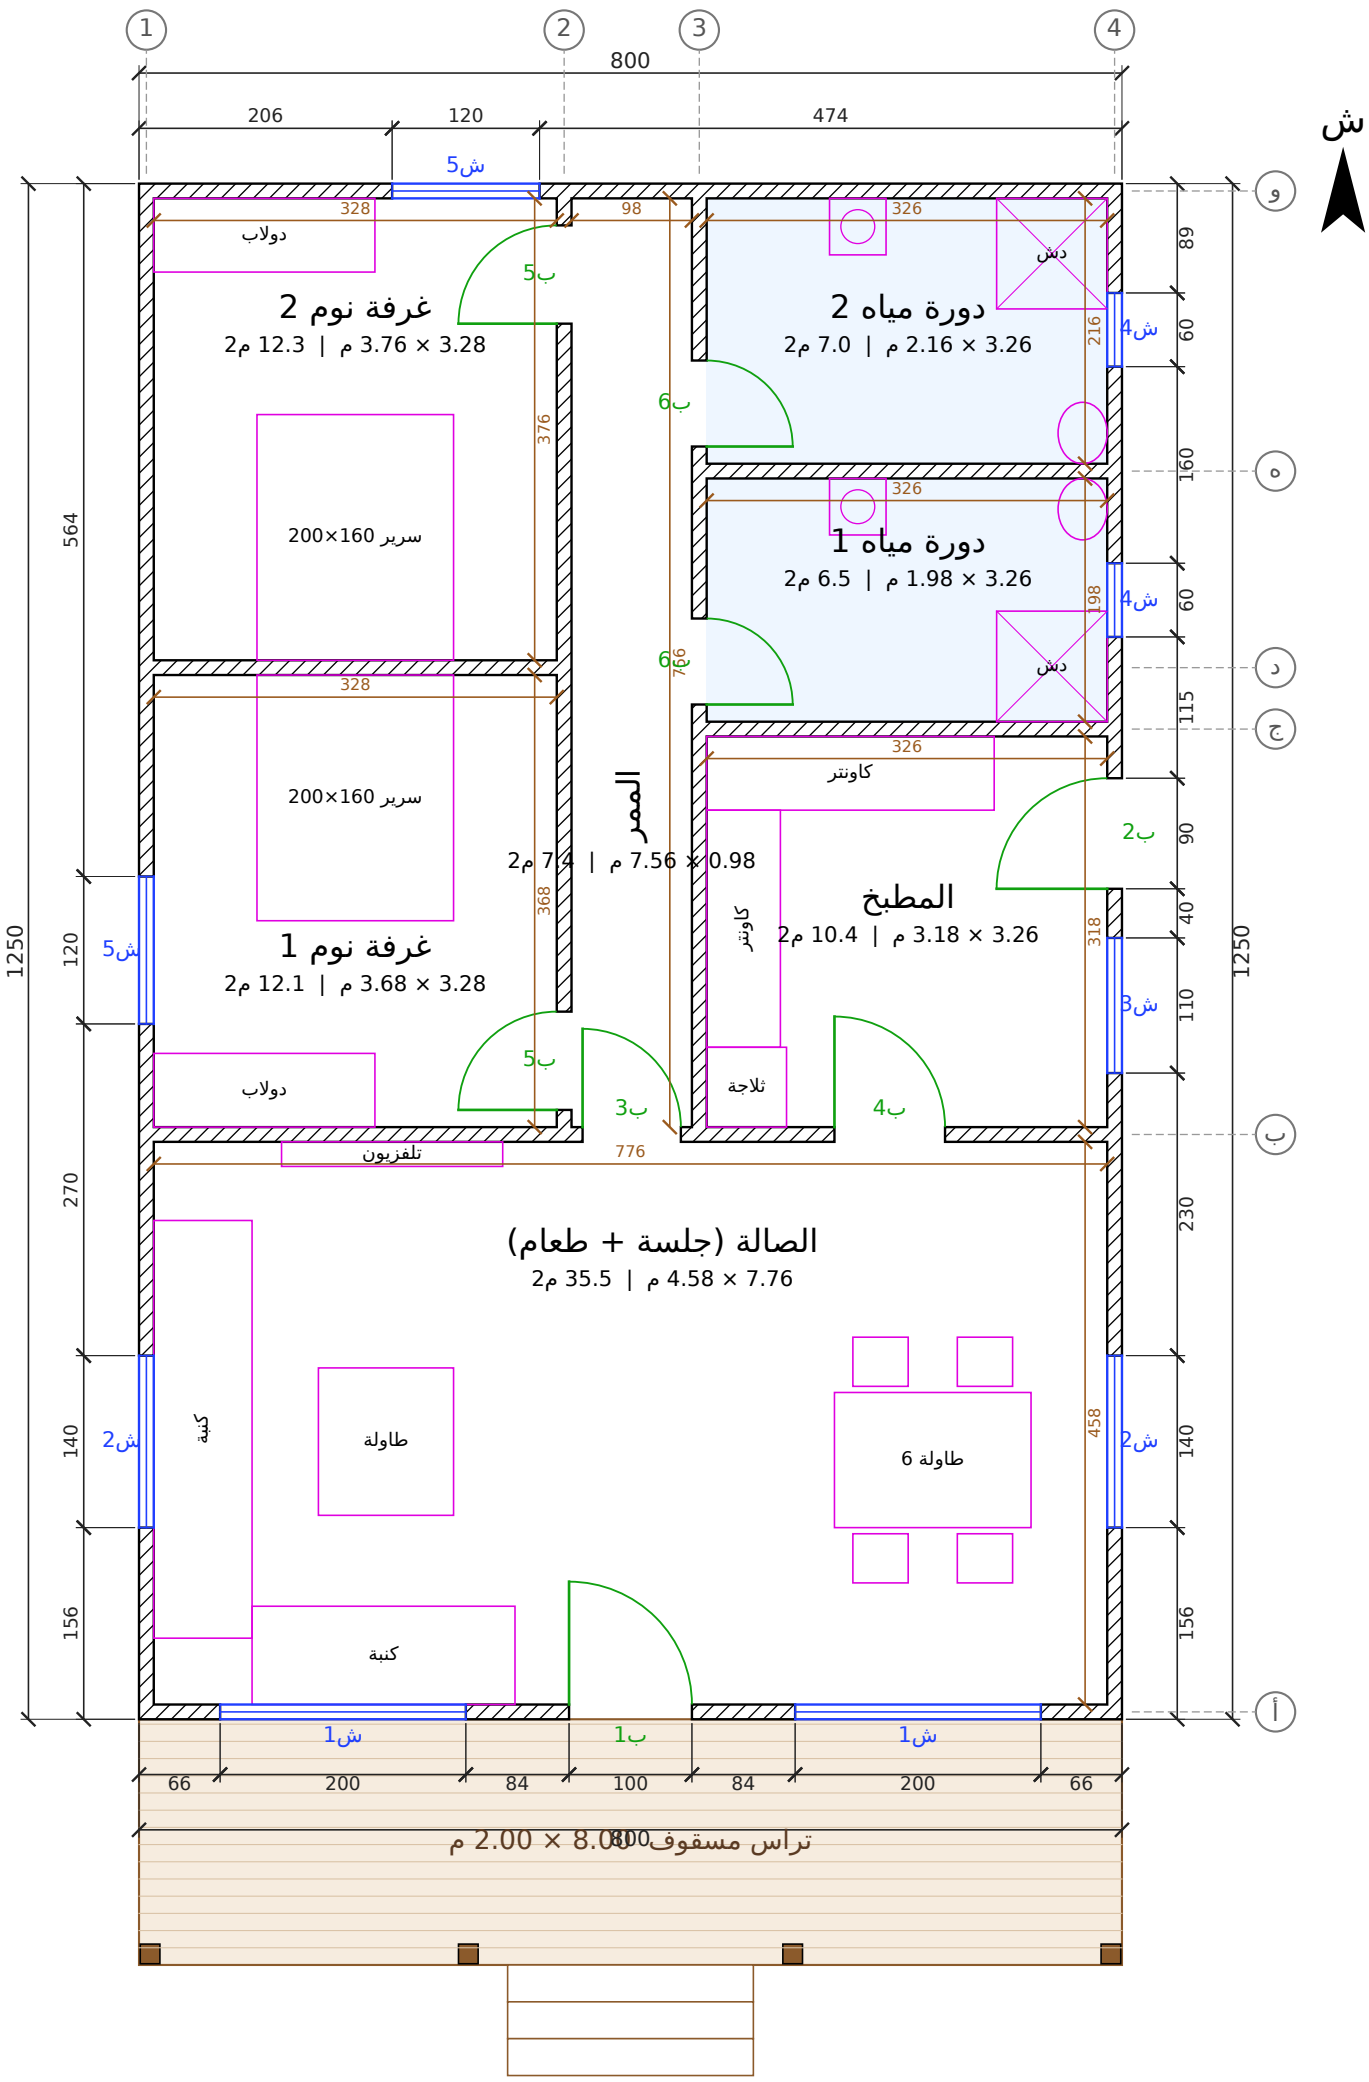


المشروع / العميل	عنوان اللوحة	المقياس	التاريخ	رقم اللوحة
مصنع وتد الأخشاب Watad Wood Factory **استراحة — غرفتين + صالة كبيرة — 8.00 × 12.50 = 100 م²** **عميل — استراحة 100 م²**	**المسقط الأفقي**	**1:50**	**2026-10-21**	**A-01 (1/9)**

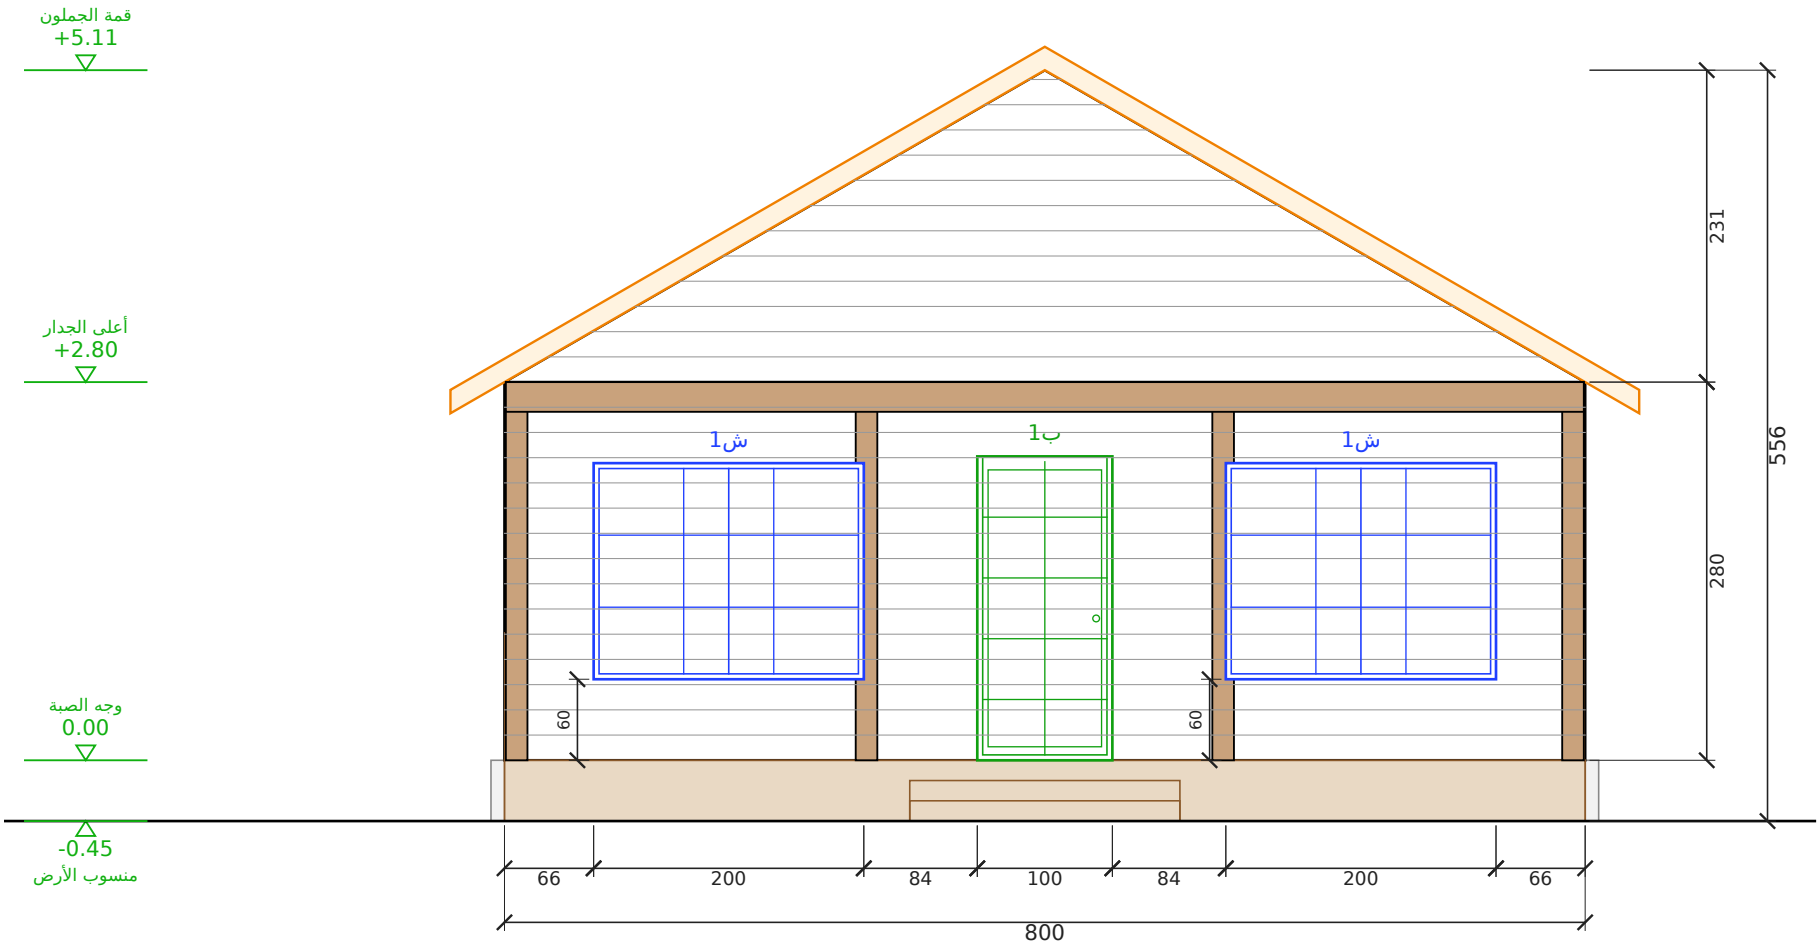

الواجهة الأمامية

مقياس 1:50 | الوحدة: سم

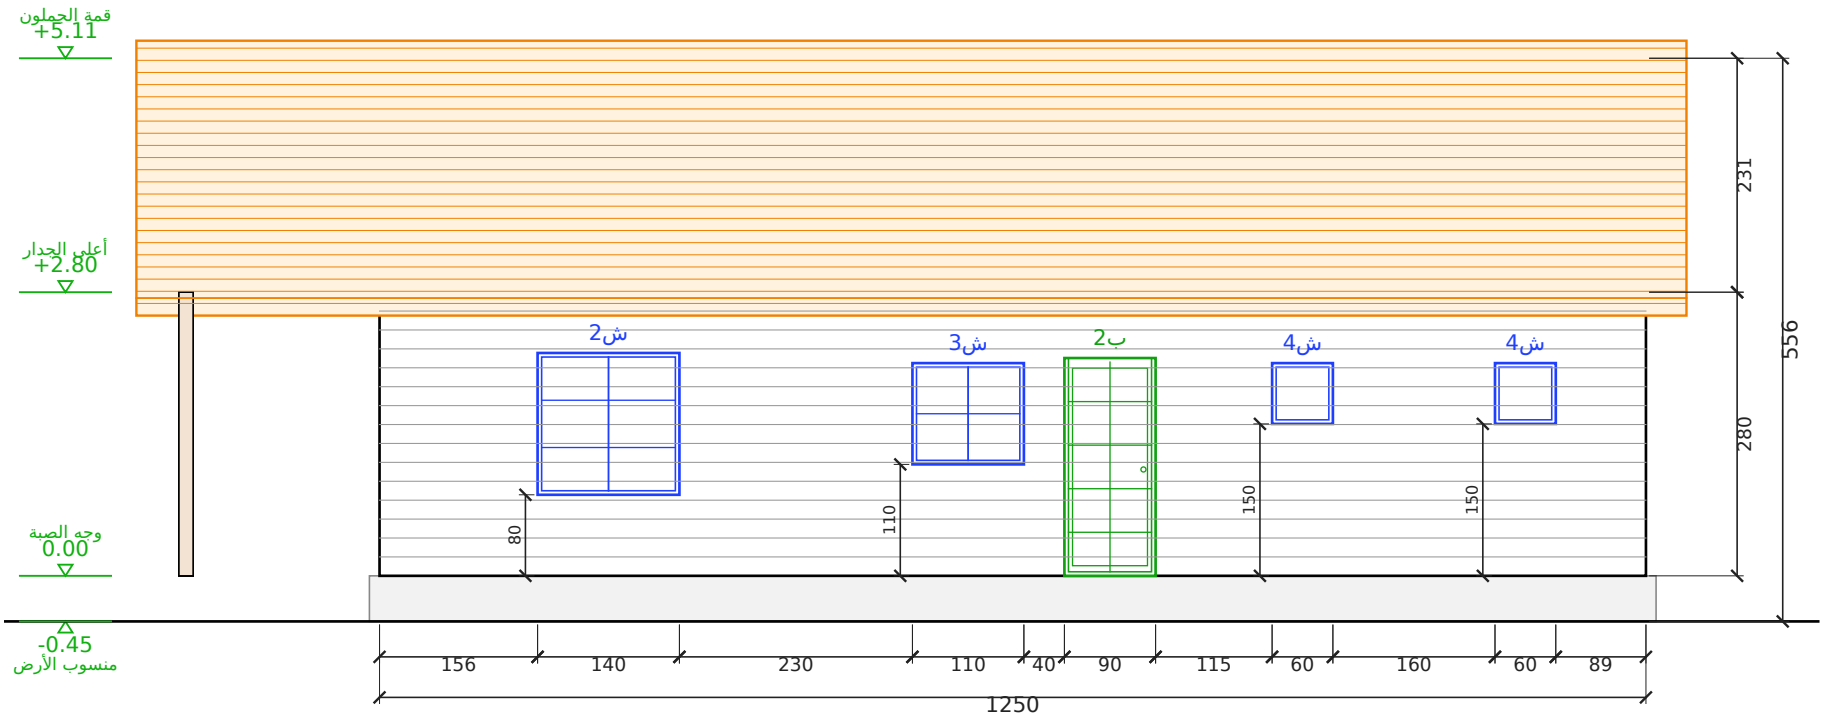


الواجهة الشرقية

مقياس 1:50 | الوحدة: سم


المشروع / العميل	عنوان اللوحة	المقياس	التاريخ	رقم اللوحة
استراحة — غرفتين + صالة كبيرة — 8.00 × 12.50 = 100 م² **عميل — استراحة 100 م²**	**الواجهة الأمامية والواجهة الشرقية**	**1:50**	**2026-10-21**	**A-02 (2/9)**

مصنع وتد الأخشاب
Watad Wood Factory

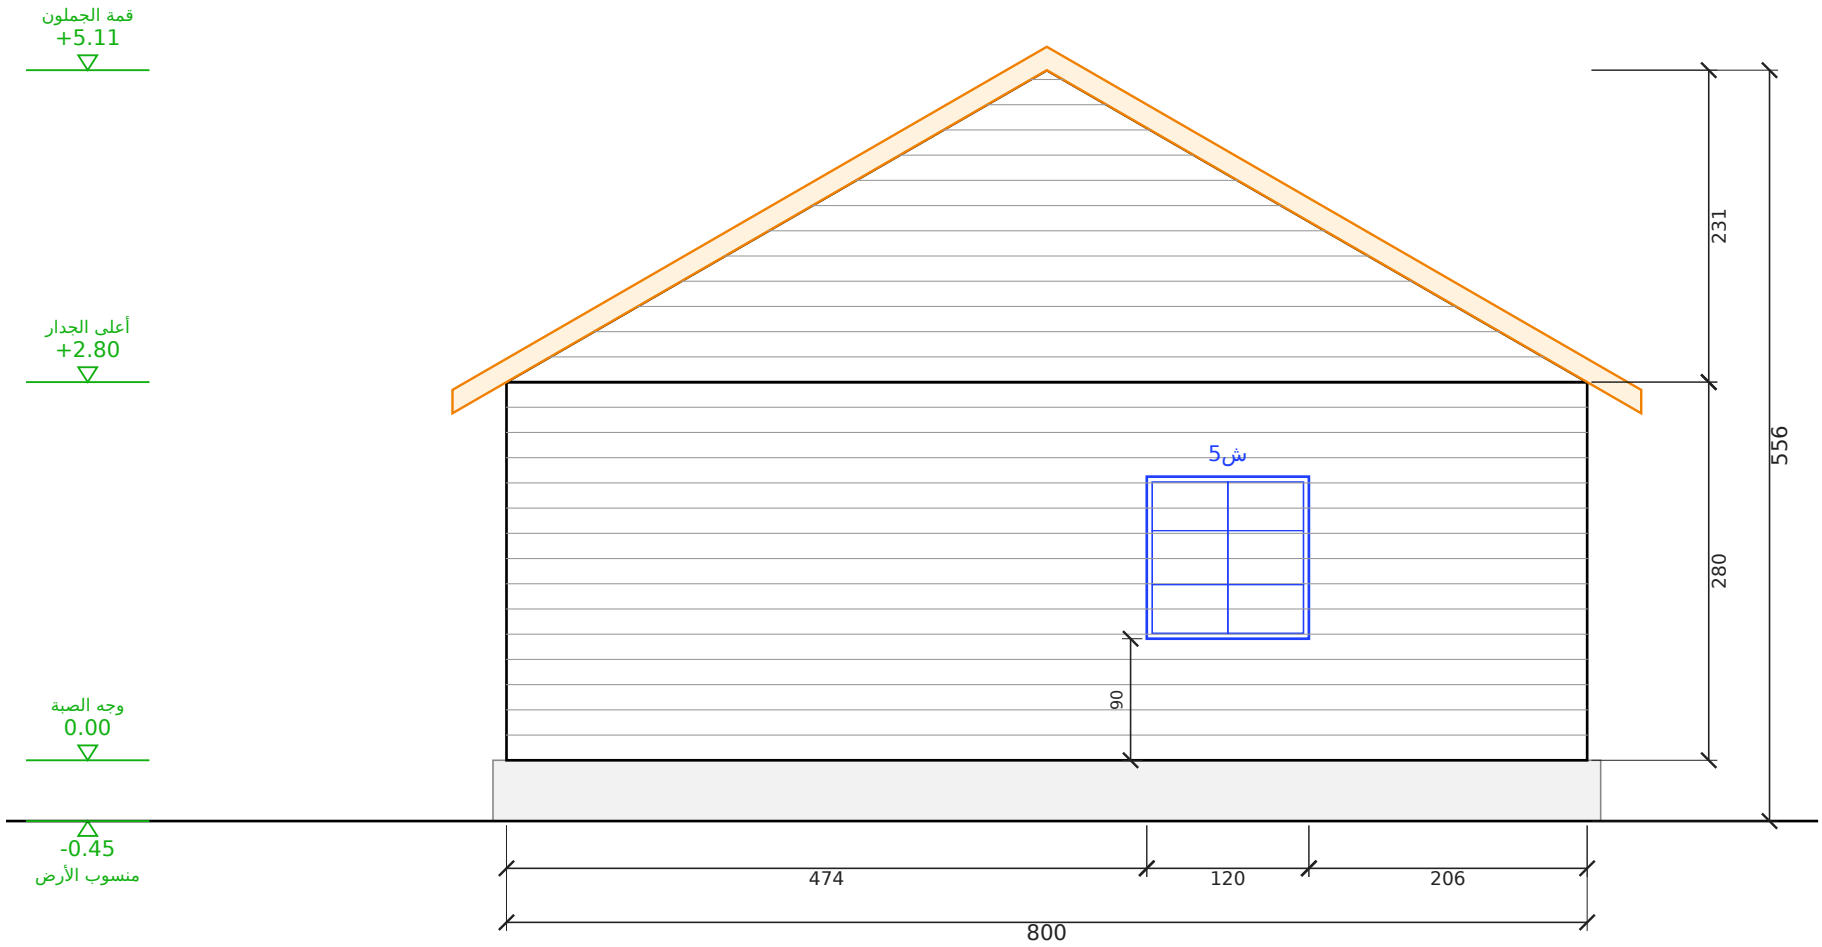

الواجهة الخلفية

مقياس 1:50 | الوحدة: سم

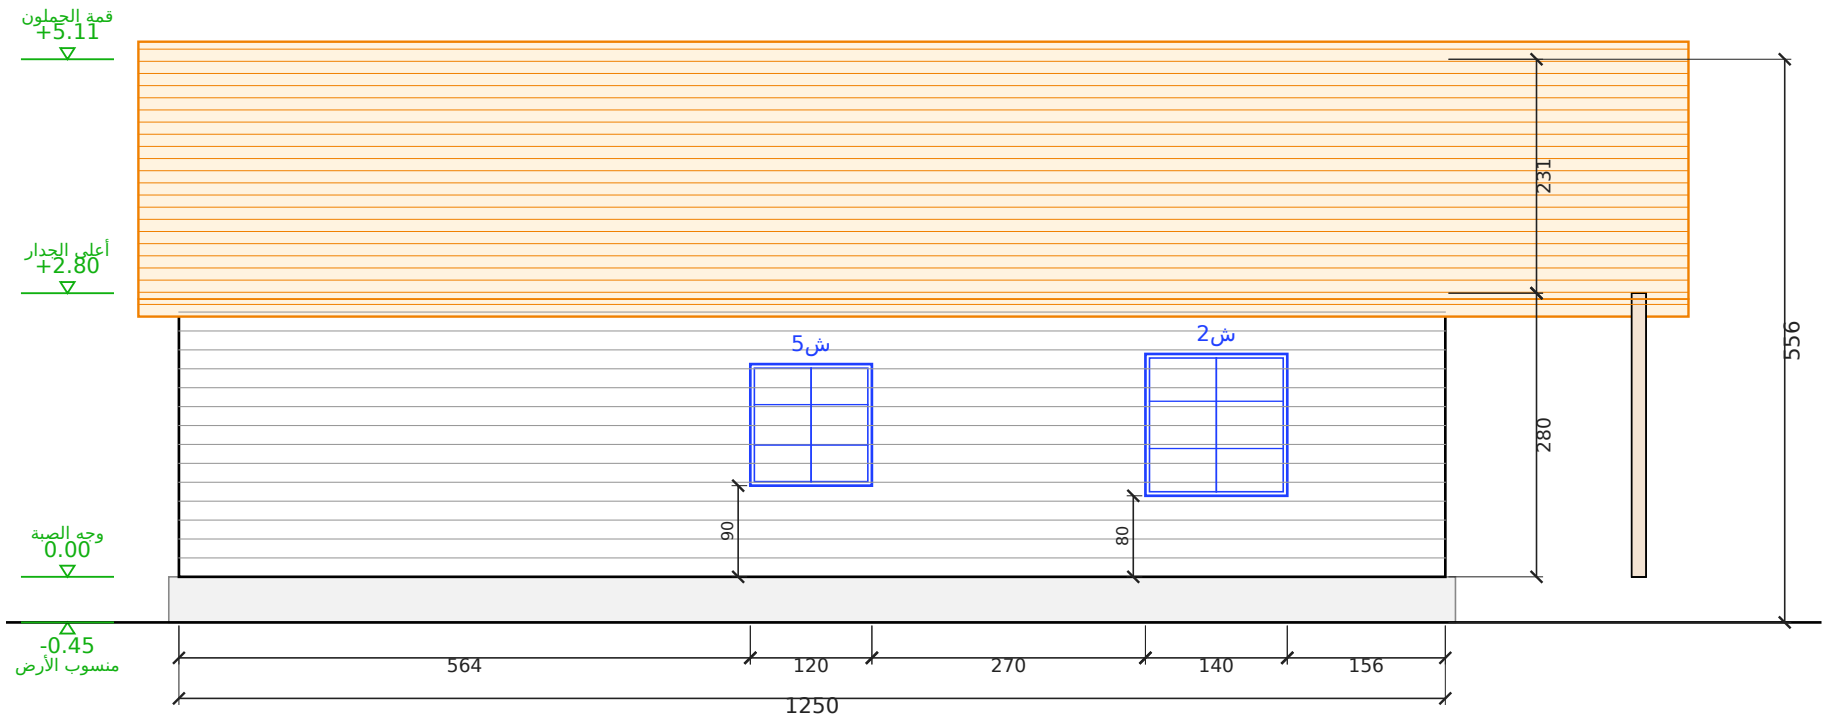


الواجهة الغربية

مقياس 1:50 | الوحدة: سم


المشروع / العميل	عنوان اللوحة	المقياس	التاريخ	رقم اللوحة
استراحة — غرفتين + صالة كبيرة — 8.00 × 12.50 = 100 م² **عميل — استراحة 100 م²**	**الواجهة الخلفية والواجهة الغربية**	**1:50**	**2026-10-21**	**A-03 (3/9)**

مصنع وتد الأخشاب
Watad Wood Factory


مسقط السقف (جملون)
رفرف 40 سم من كل جهة | مقياس 1:50

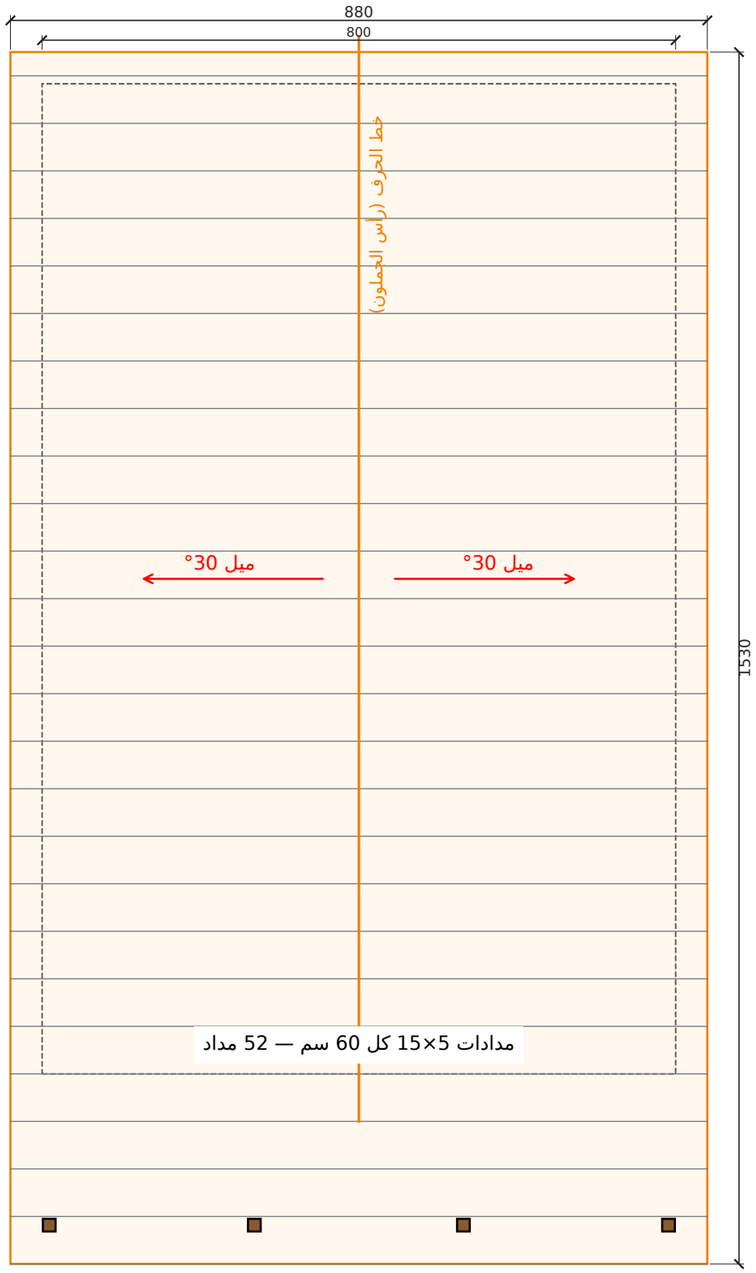

قطاع عرضي أ-أ
مقياس 1:50 | الوحدة: سم

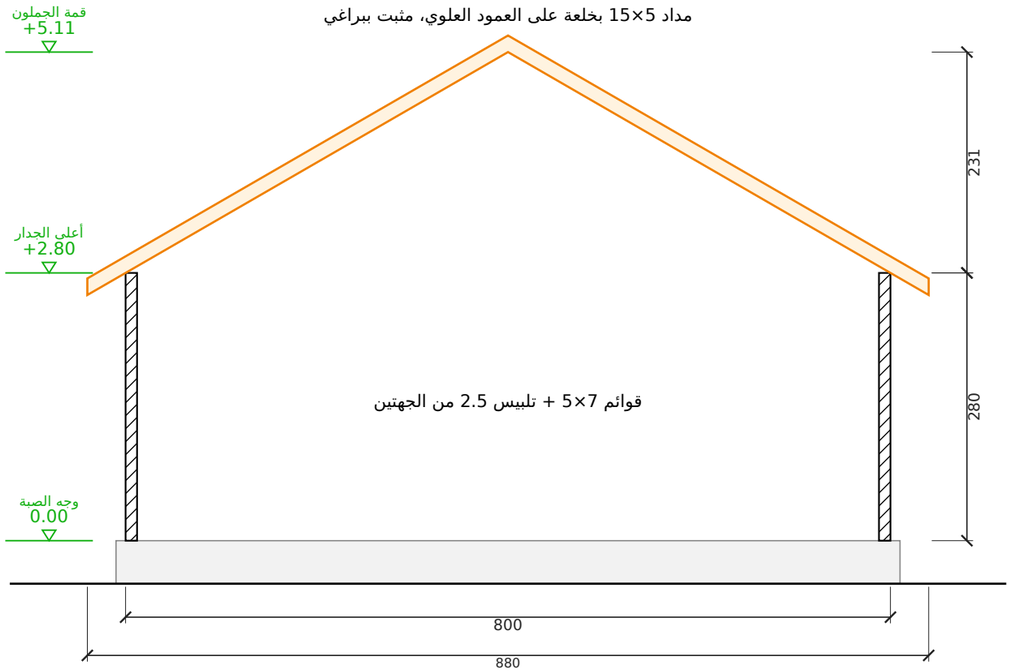

تفصيلة جلوس المداد على العلوي (1:5)

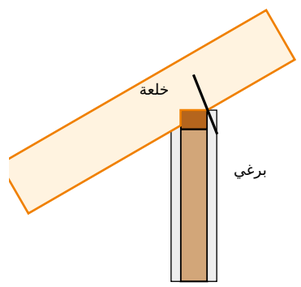

علوي 7×5 على قائم 7×5

المشروع / العميل	عنوان اللوحة	المقياس	التاريخ	رقم اللوحة
استراحة — غرفتين + صالة كبيرة — 8.00 × 12.50 = 100 م² **عميل — استراحة 100 م²**	**مسقط السقف والقطاع**	**1:50**	**2026-10-21**	**A-04 (4/9)**

مصنع وتد الأخشاب
Watad Wood Factory

جدول مقاسات الأبواب والشبابيك
مقاس الفتحة الصافي في الجدار - الوحدة: سم

الرمز	النوع	العرض (سم)	الارتفاع (سم)	ارتفاع الجلسة (سم)	العدد	الموقع
ب1	باب	100	225	-	1	الأمامية
ب2	باب	90	215	-	1	الشرقية
ب3	باب	80	210	-	1	باب الممر العائلي
ب4	باب	90	210	-	1	المطبخ
ب5	باب	80	210	-	2	غرفة نوم 1 - غرفة نوم 2
ب6	باب	70	210	-	2	دورة مياه 1 - دورة مياه 2
ش1	شباك	200	160	60	2	الأمامية 2
ش2	شباك	140	140	80	2	الشرقية - الغربية
ش3	شباك	110	100	110	1	الشرقية
ش4	شباك	60	60	150	2	الشرقية 2
ش5	شباك	120	120	90	2	الخلفية - الغربية

الإجمالي: أبواب 8 - شبابيك 9

جدول المساحات وبيانات المشروع

بيانات المشروع

البند	البيان
المشروع	استراحة — غرفتين + صالة كبيرة — 8.00 × 12.50 = 100 م²
العميل	عميل — استراحة 100 م²
الموقع	—
الاستخدام	استراحة
التاريخ	2026-10-21
نظام البناء	هيكل خشب 5×7 + تلبيس 2.5 سم من الجهتين
السقف	جملون 30° — قرميد معدني

جدول المساحات

م	الفراغ	الأبعاد (م)	المساحة (م2)
1	الصالة (جلسة + طعام)	7.76 × 4.58	35.54
2	غرفة نوم 1	3.28 × 3.68	12.07
3	غرفة نوم 2	3.28 × 3.76	12.33
4	الممر	0.98 × 7.56	7.41
5	المطبخ	3.26 × 3.18	10.37
6	دورة مياه 1	3.26 × 1.98	6.45
7	دورة مياه 2	3.26 × 2.16	7.04
	المساحة الصافية الداخلية		**91.22**
	التراس المسقوف	**8.00 × 2.00**	**16.00**
	المساحة الإجمالية المبنية	**8.00 × 12.50**	**100.00**

لقطات المنظور الخارجي


المنظور الأمامي




منظور أمامي من اليسار




منظور أمامي من اليمين

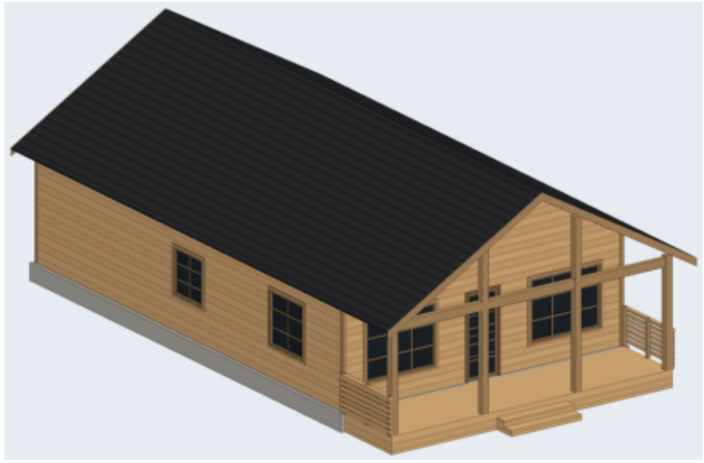


المنظور الخلفي

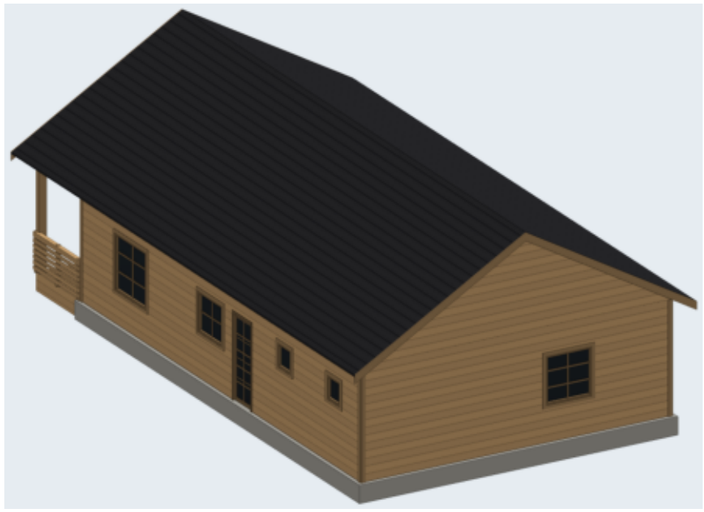

منظور خلفي من اليمين

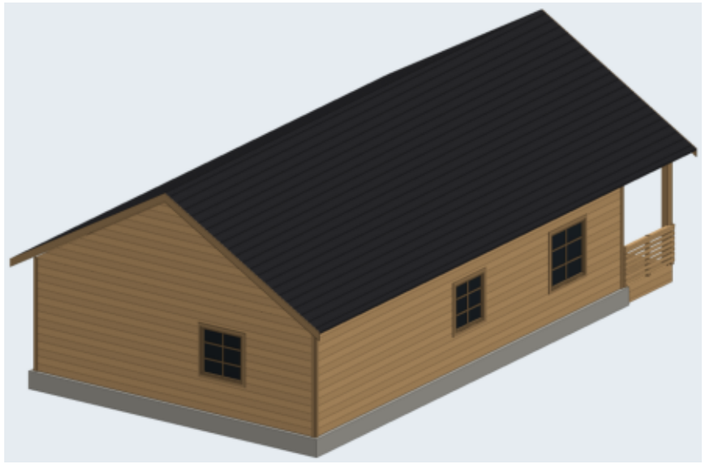


منظر علوي

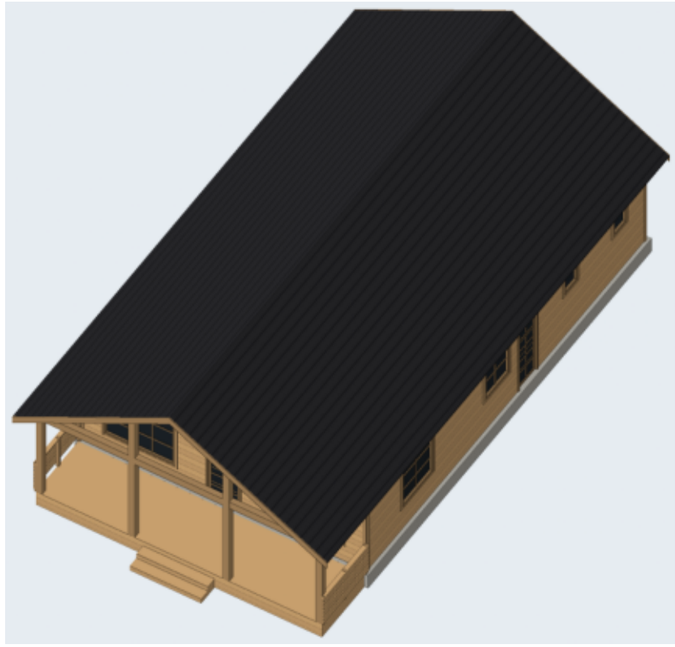

مصنع وتد الأخشاب Watad Wood Factory	المشروع / العميل **استراحة — غرفتين + صالة كبيرة — 8.00 × 12.50 = 100 م²** **عميل — استراحة 100 م²**	عنوان اللوحة **لقطات المنظور**	المقياس **—**	التاريخ **2026-10-21**	رقم اللوحة **A-07 (7/9)**

المقطع العلوي بالفرش

مقطع أفقي على ارتفاع 1.90 م — توزيع الفرش ومسار الحركة

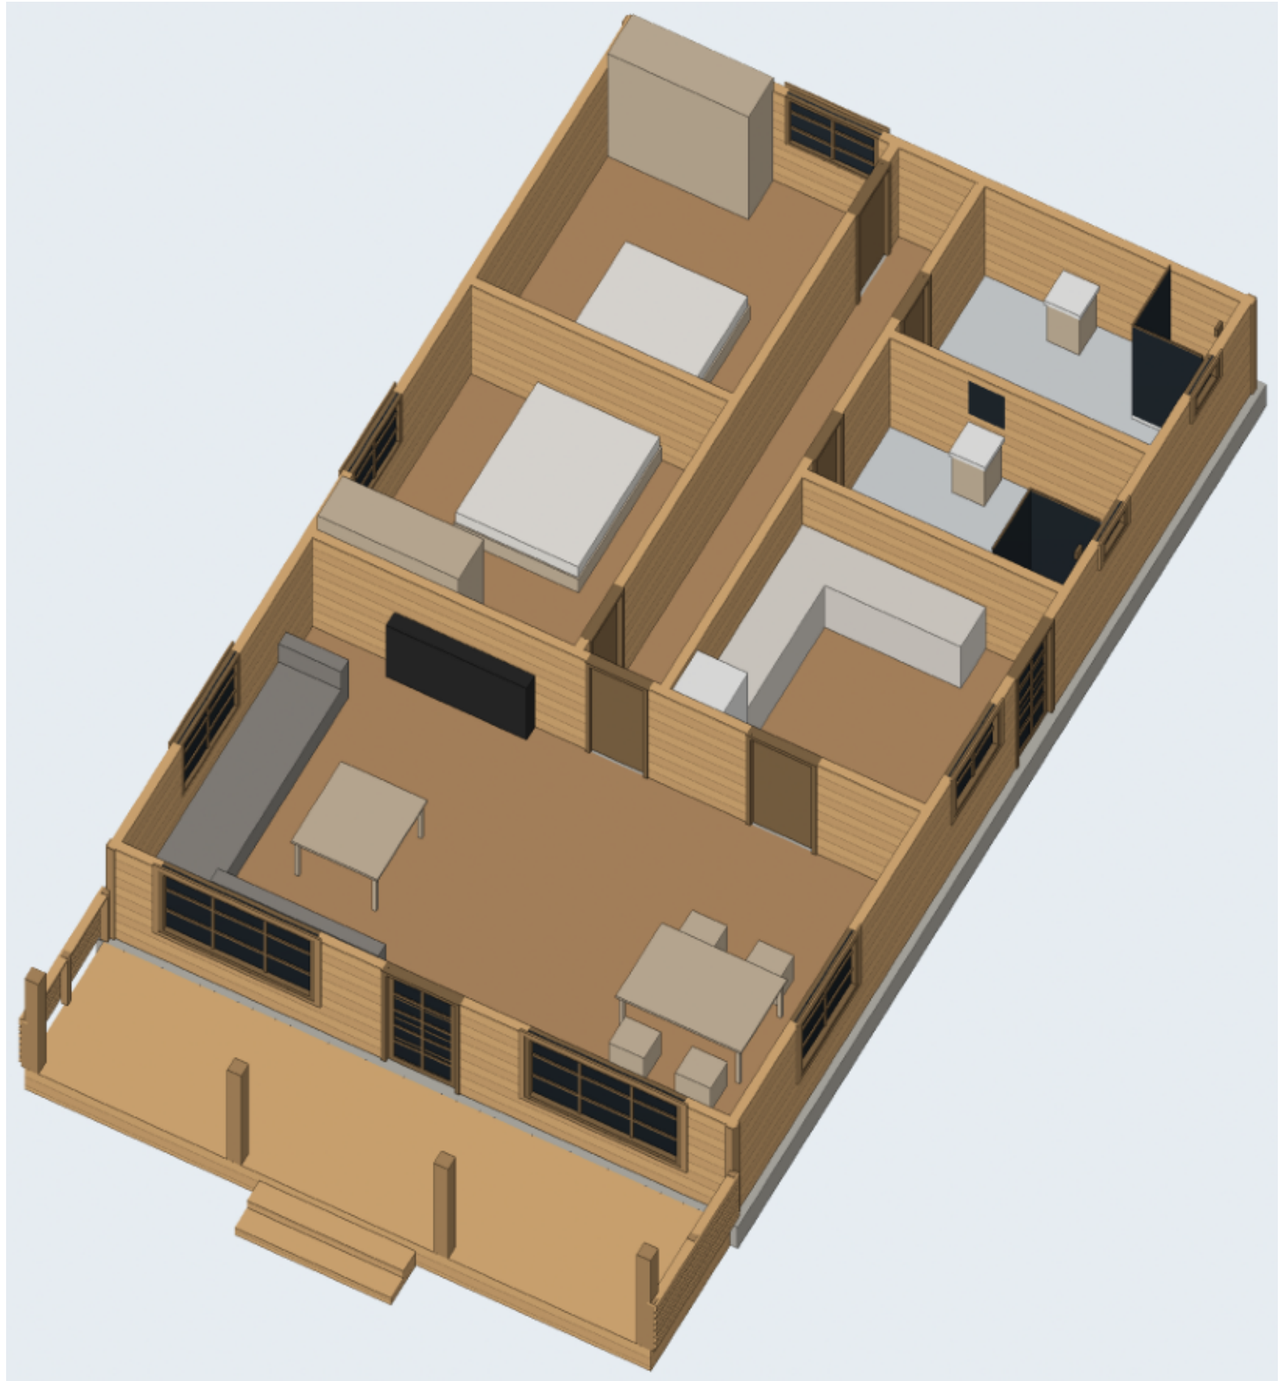

المشروع / العميل	عنوان اللوحة	المقياس	التاريخ	رقم اللوحة
استراحة — غرفتين + صالة كبيرة — 8.00 × 12.50 = 100 م² **عميل — استراحة 100 م²**	**المقطع العلوي بالفرش**	**—**	**2026-10-21**	**A-08 (8/9)**

مصنع وتد الأخشاب
Watad Wood Factory

المنظور ثلاثي الأبعاد والمواد

النمط: جوزي غامق + إطارات سوداء — رندر واقعي بخامات حقيقية



جدول المواد والألوان

الخشب / الصبغة

خشب طبيعي فاتح (بدون صبغة)

القرميد

قرميد رمادي غامق

الزجاج

زجاج عاكس غامق

إطارات الشبابيك والأبواب

إطار خشب بنفس الصبغة أغمق

الكنار والزوايا

نفس الصبغة أغمق درجة


الصبة

خرسانة 45 سم


الدربزين: ألواح أفقية متقاربة (عصري)

تقسيم الشبابيك: بدون | الباب الرئيسي: زجاج بتقسيمات (فرنسي)

أنواع الدربزين المعتمدة (من مشاريع المصنع)

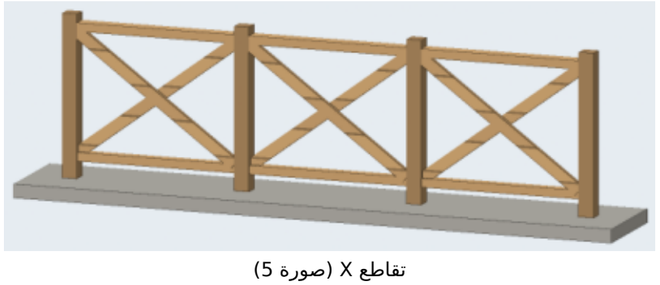

تقاطع X (صورة 5)

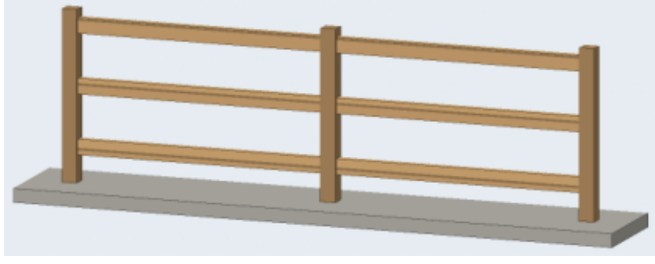

3 مرابيع أفقية (صورة 2)



قوائم رأسية متقاربة (صورة 1)

المشروع / العميل	عنوان اللوحة	المقياس	التاريخ	رقم اللوحة
استراحة — غرفتين + صالة كبيرة — 8.00 × 12.50 = 100 م² **عميل — استراحة 100 م²**	**المنظور والمواد**	—	**2026-10-21**	**A-09 (9/9)**

مصنع وتد الأخشاب
Watad Wood Factory