
المنظور ثلاثي الأبعاد والمواد

النمط: برتقالي محمر + قرميد فحمي + دربزين X — رندر واقعي بخامات حقيقية

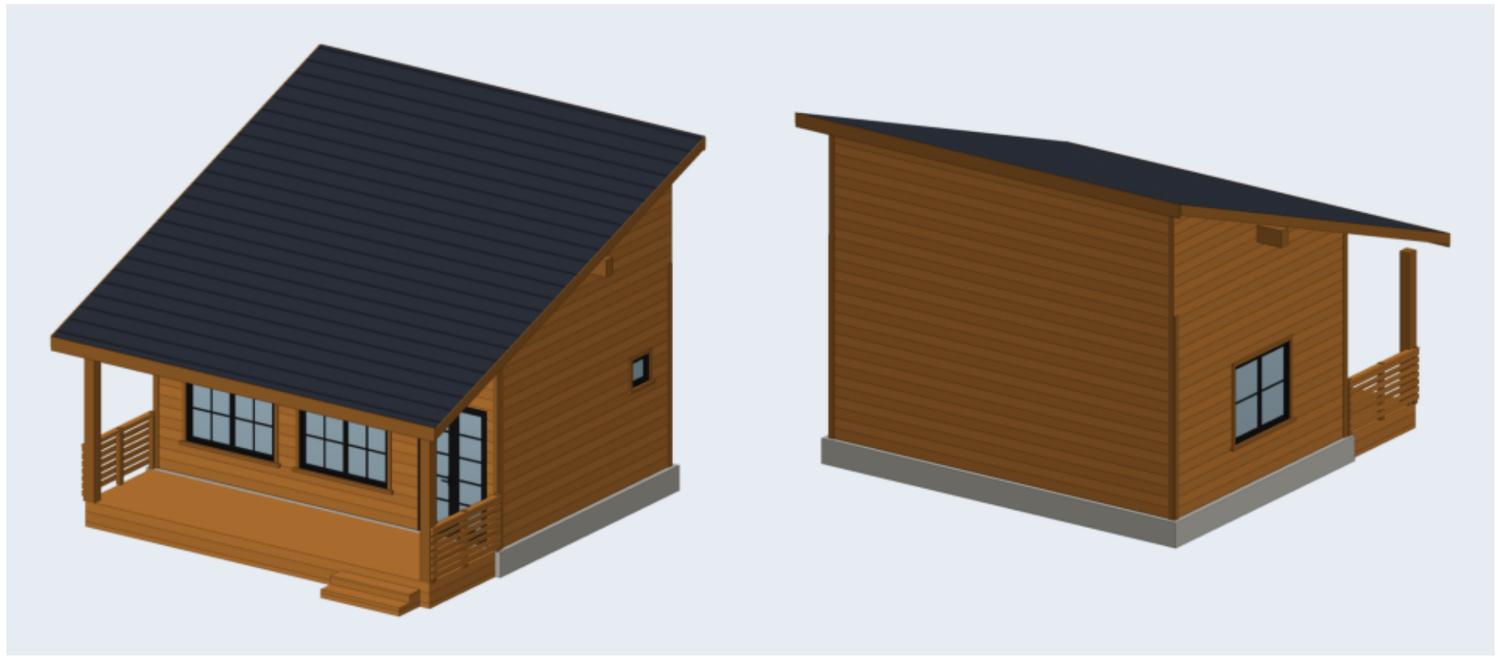

جدول المواد والألوان

الخشب / الصبغة

صبغة عسلي / سيدر

القرميد

قرميد فحمي / أسود مزرق

الزجاج

زجاج شفاف

إطارات الشبابيك والأبواب

إطار ألمنيوم أسود

الكنار والزوايا

نفس الصبغة أغمق درجة


الصبة

خرسانة 45 سم


الدربزين: ألواح أفقية متقاربة (عصري)

تقسيم الشبابيك: شبكة | الباب الرئيسي: زجاج بتقسيمات (فرنسي)

أنواع الدربزين المعتمدة (من مشاريع المصنع)

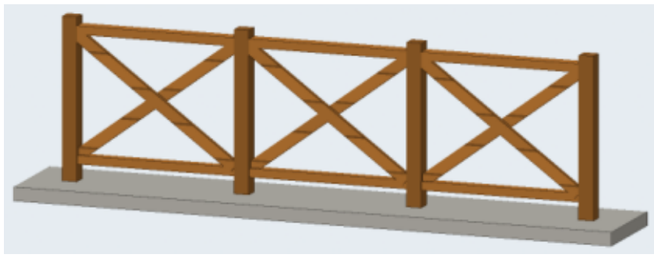

تقاطع X (صورة 5)

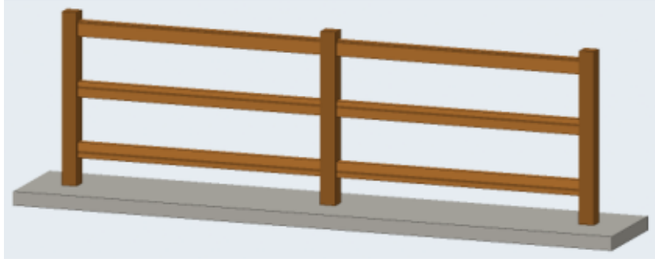

3 مرابيع أفقية (صورة 2)




قوائم رأسية متقاربة (صورة 1)

مصنع وتد الأخشاب Watad Wood Factory	المشروع / العميل: **مجلس خشب 7.00 × 5.00 م — سقف مائل ممتد على جلسة خارجية — عميل — مجلس 7×5**	عنوان اللوحة: **المنظور والمواد**	المقياس: **1:50**	التاريخ: **2026-10-29**	رقم اللوحة: **W-01 (1/12)**


المسقط الأفقي مع الفرش

الأبعاد بالسنتيمتر - الجدران: قوائم 7×5 + تلبيس 2.5 من الجهتين (12 سم)

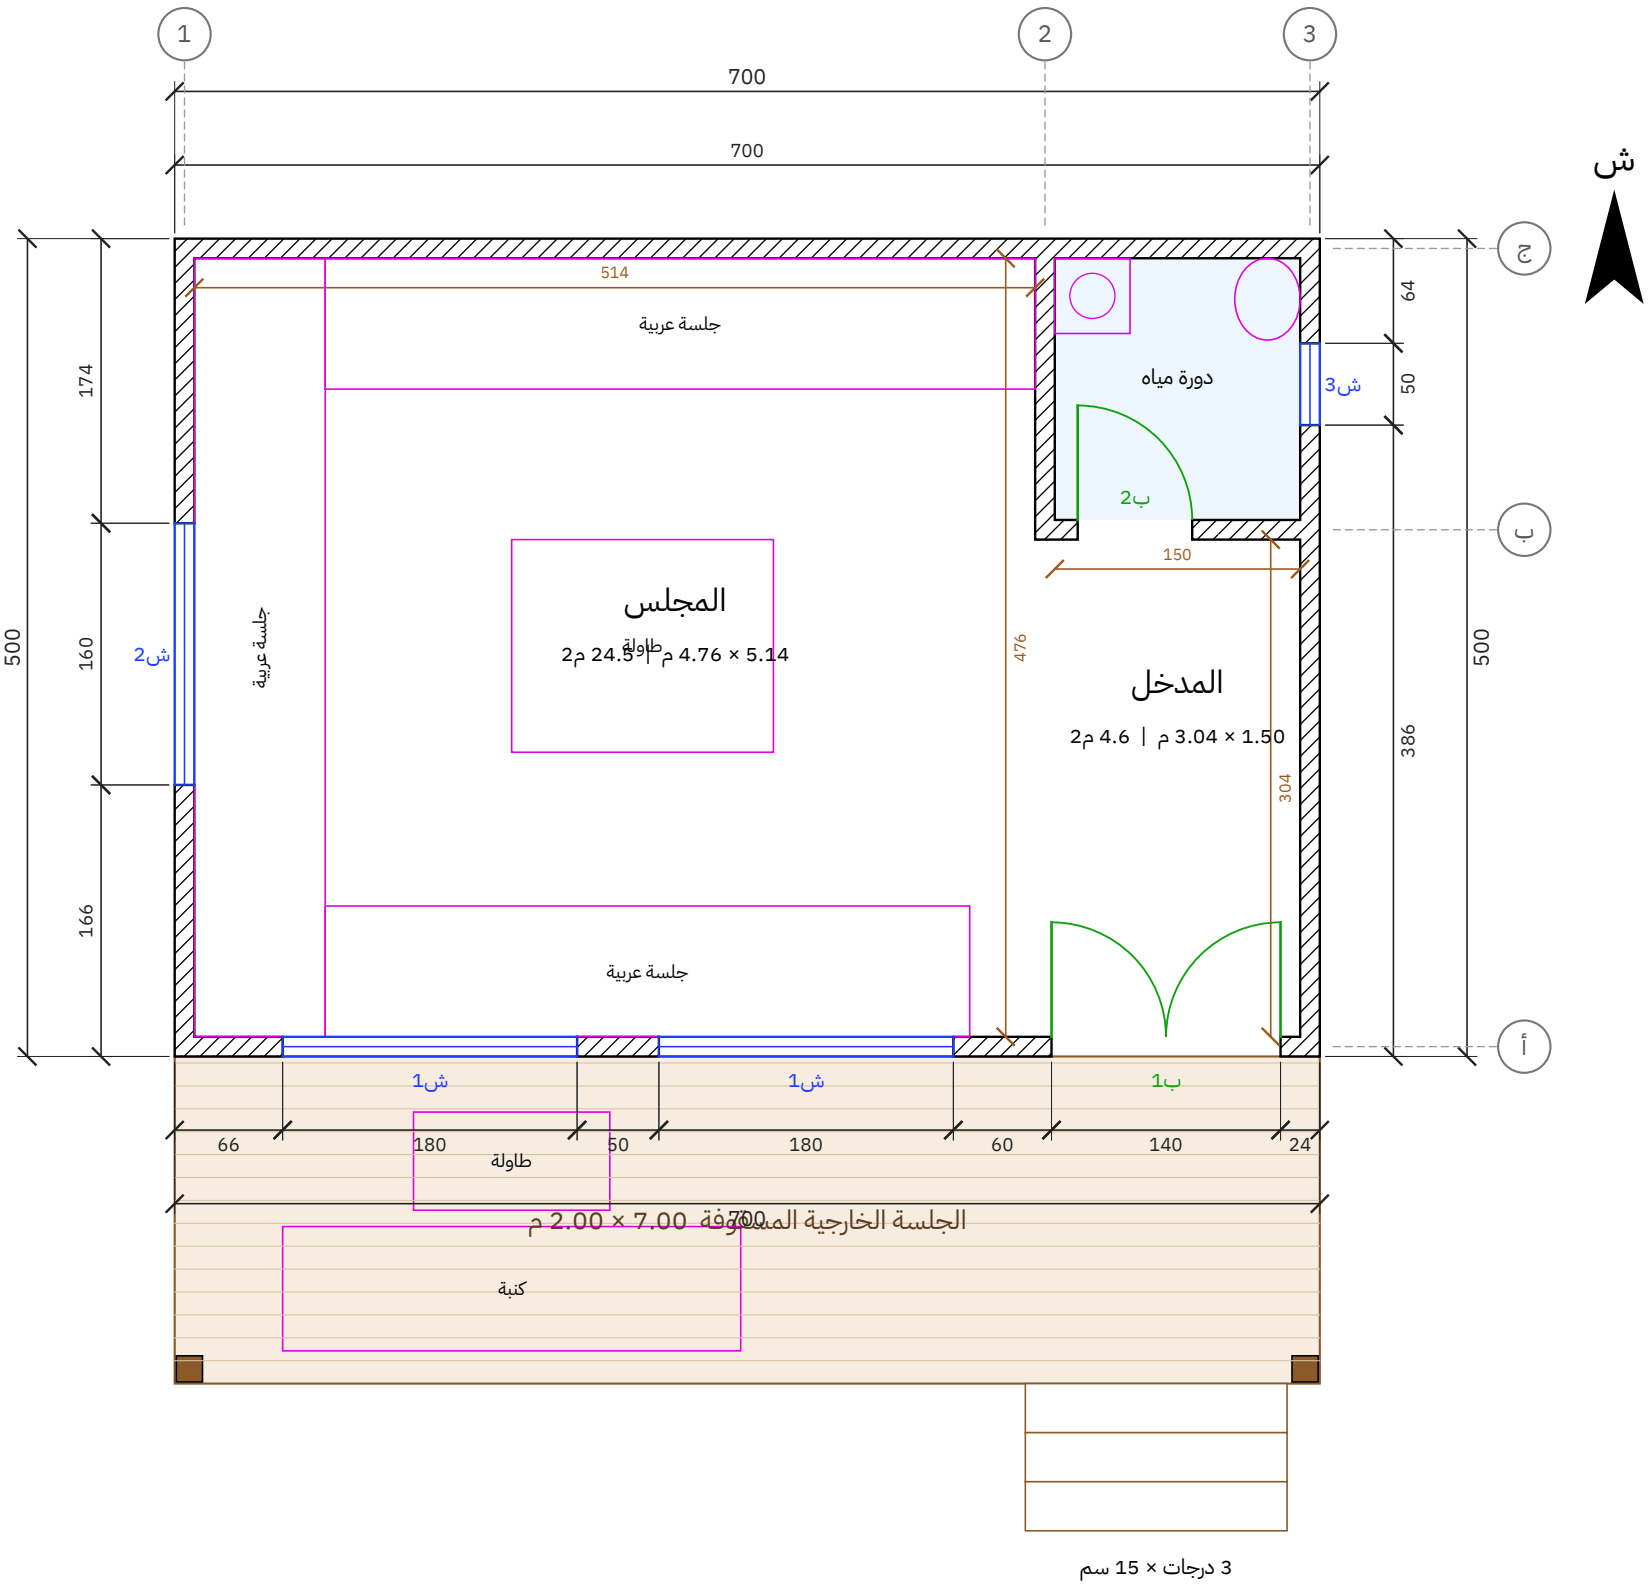


المشروع / العميل	عنوان اللوحة	المقياس	التاريخ	رقم اللوحة
مجلس خشب 7.00 × 5.00 م – سقف مائل ممتد على جلسة خارجية **عميل – مجلس 7×5**	**المسقط الأفقي**	**1:50**	**2026-10-29**	**W-02 (2/12)**

مصنع وتد الأخشاب
Watad Wood Factory

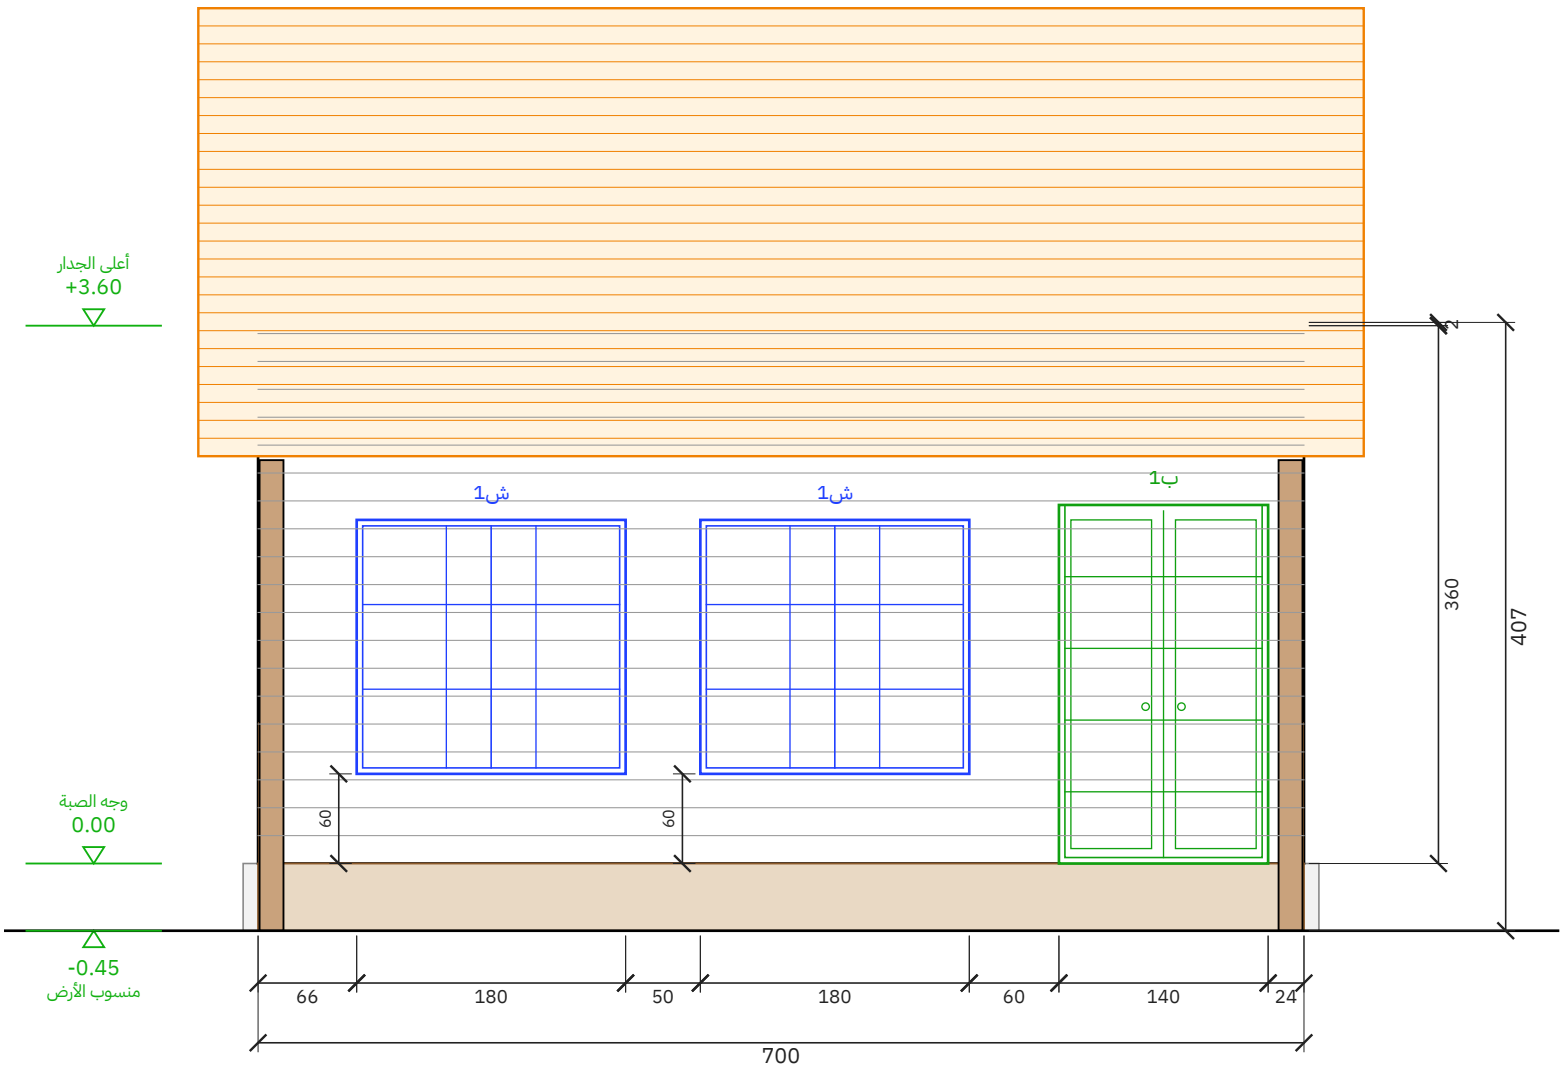

الواجهة الأمامية (على الحوش)

مقياس 1:50 | الوحدة: سم

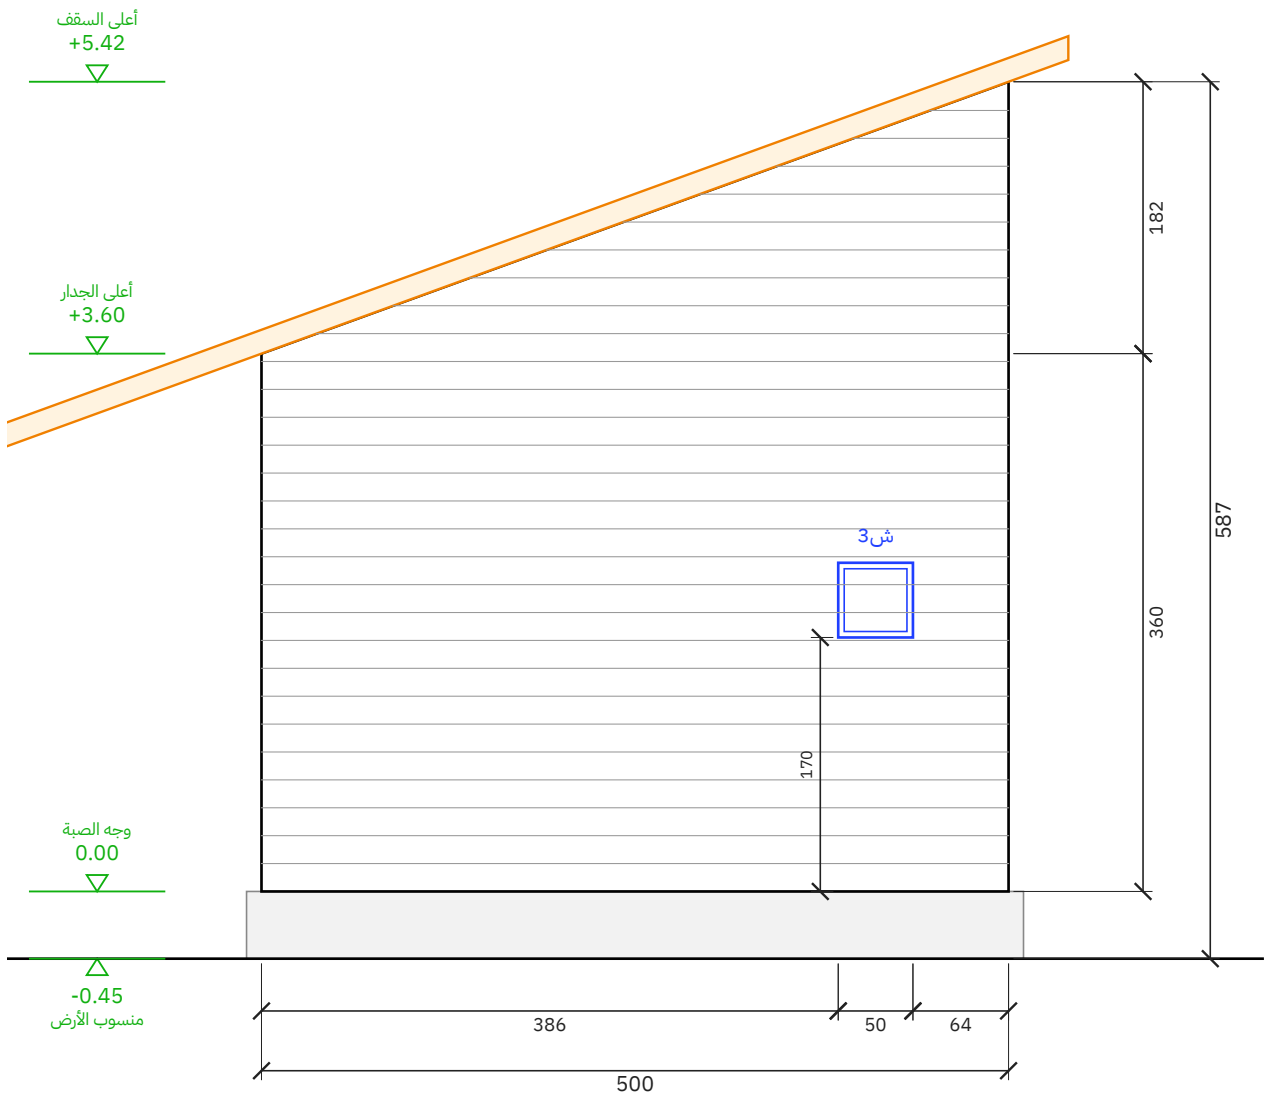


الواجهة الشرقية

مقياس 1:50 | الوحدة: سم


المشروع / العميل	عنوان اللوحة	المقياس	التاريخ	رقم اللوحة
مجلس خشب 7.00 × 5.00 م — سقف مائل ممتد على جلسة خارجية عميل — مجلس 7×5	الواجهة الأمامية (على الحوش) والواجهة الشرقية	1:50	2026-10-29	W-03 (3/12)

مصنع وتد الأخشاب
Watad Wood Factory

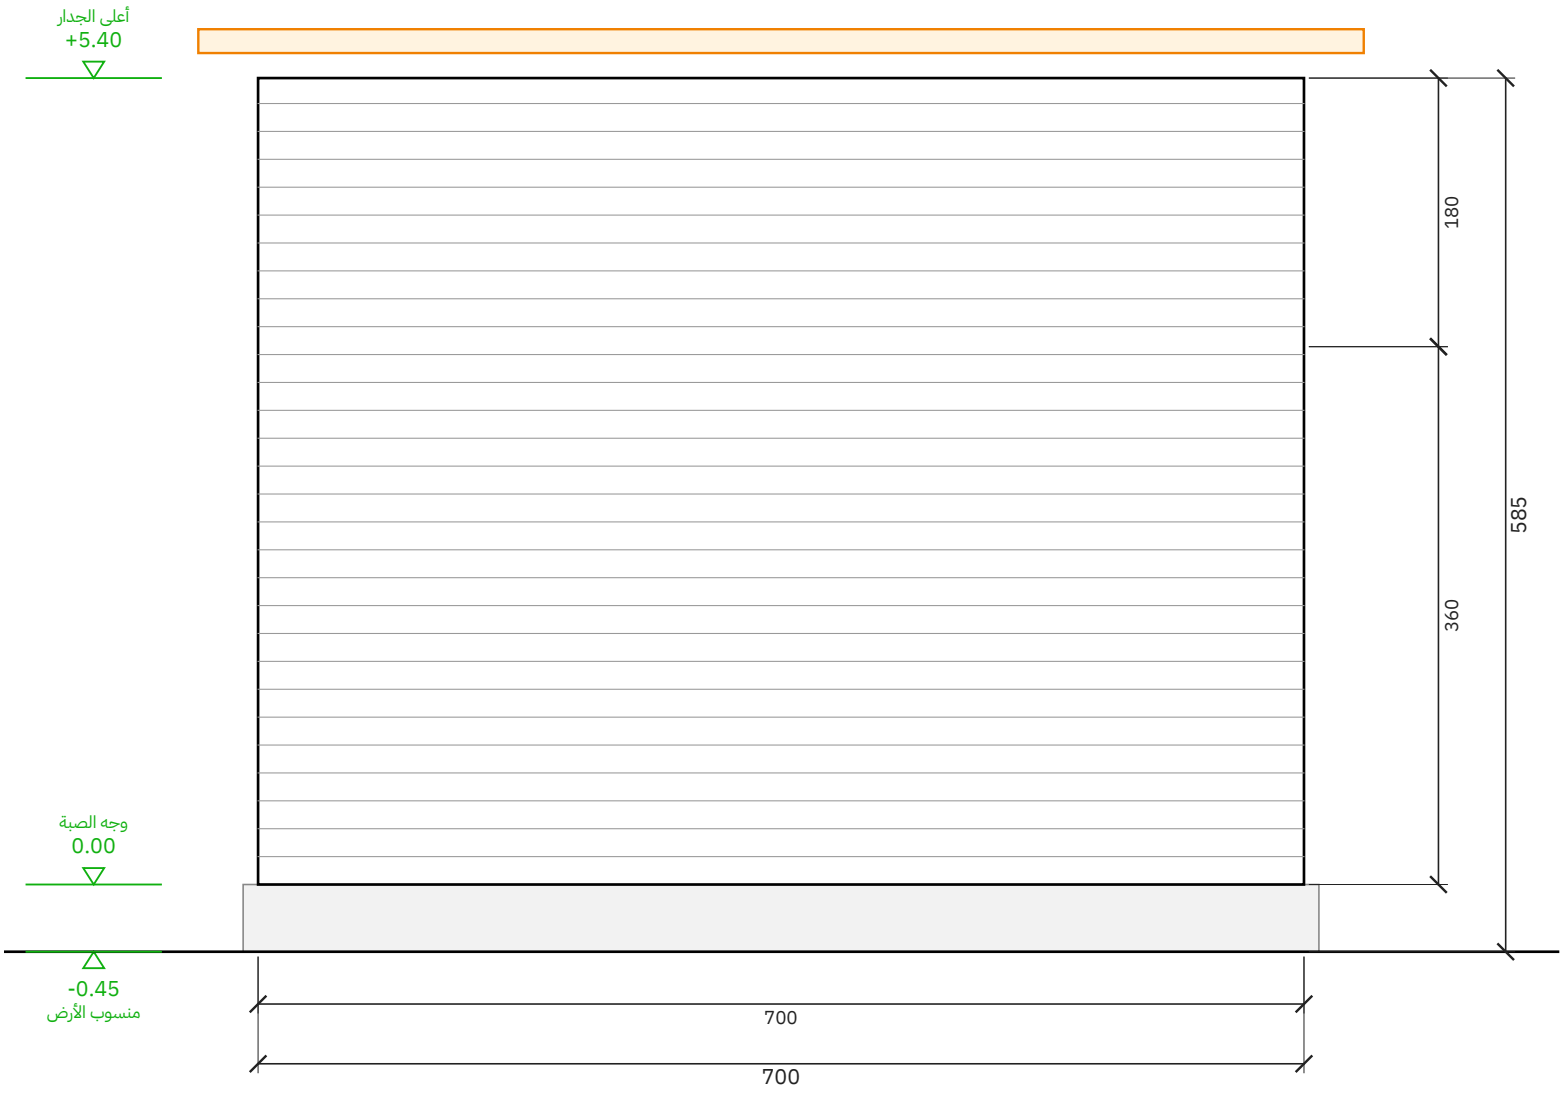

الواجهة الخلفية

مقياس 1:50 | الوحدة: سم

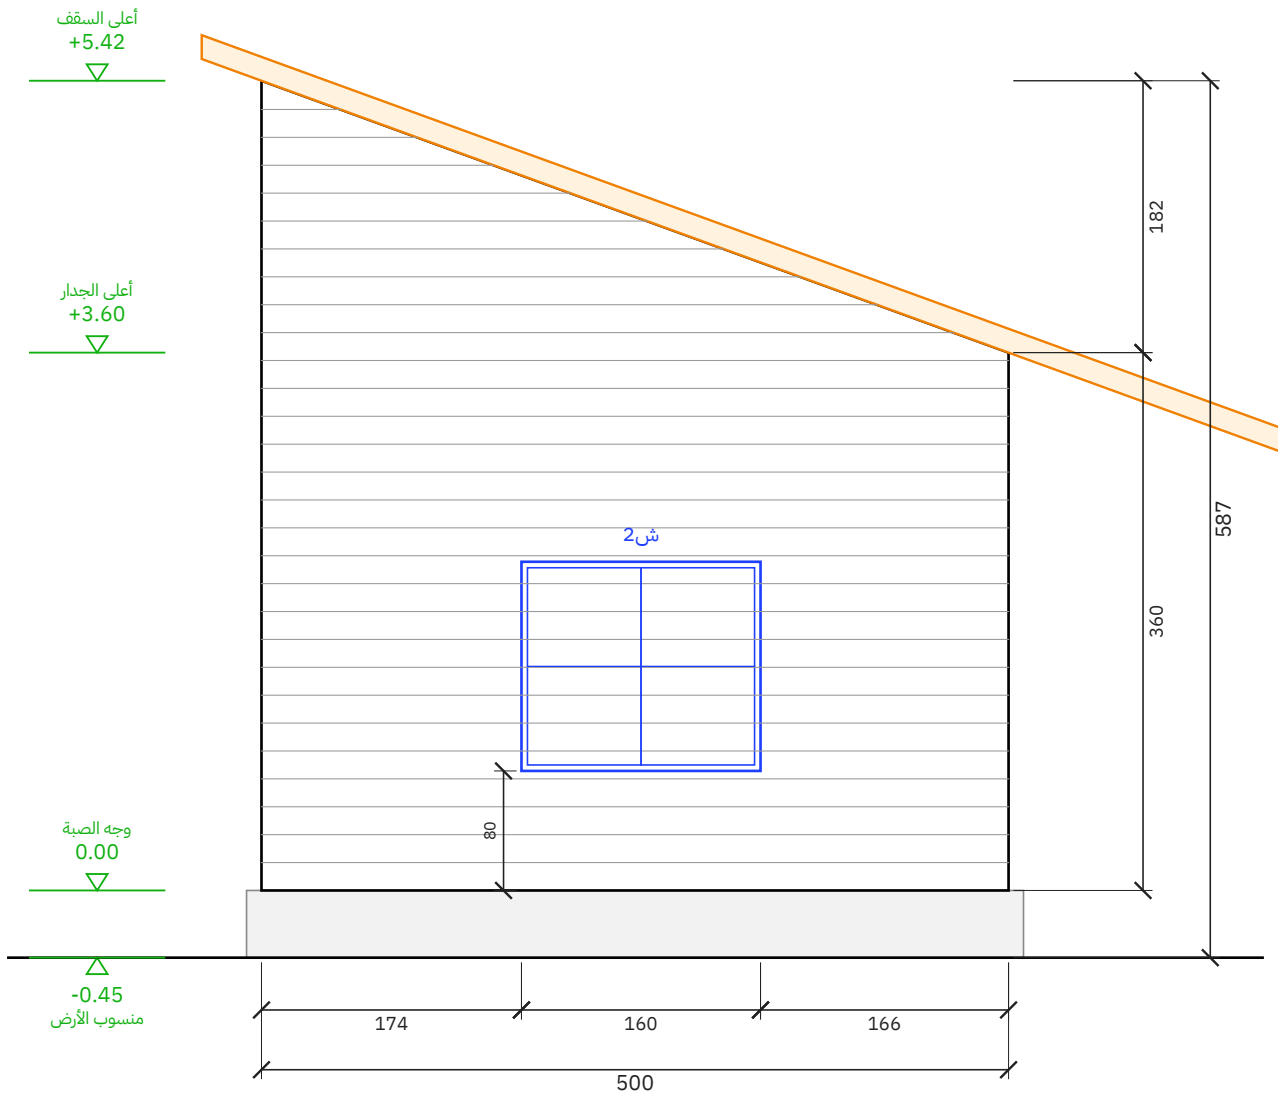

الواجهة الغربية


مقياس 1:50 | الوحدة: سم

المشروع / العميل	عنوان اللوحة	المقياس	التاريخ	رقم اللوحة
مجلس خشب 7.00 × 5.00 م – سقف مائل ممتد على جلسة خارجية عميل – مجلس 7×5	الواجهة الخلفية والواجهة الغربية	1:50	2026-10-29	W-04 (4/12)

مصنع وتد الأخشاب
Watad Wood Factory


مسقط السقف (مائل باتجاه واحد)

رفرف 40 سم من كل جهة | مقياس 1:50

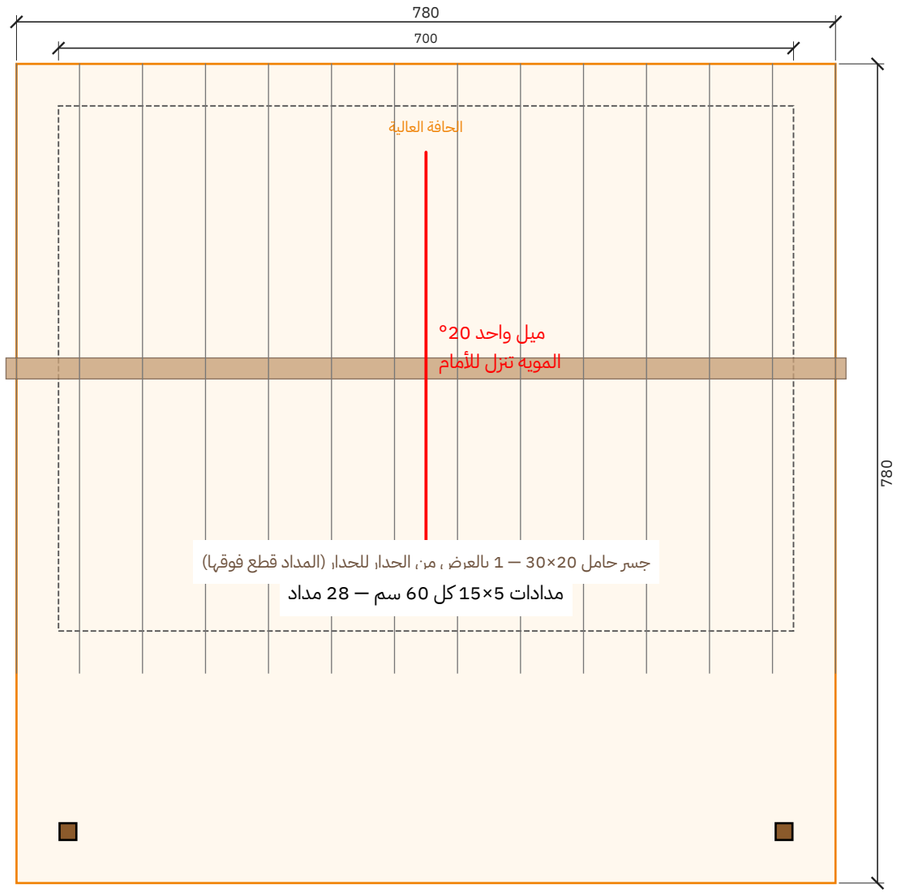


قطاع عرضي أ-أ

مقياس 1:50 | الوحدة: سم

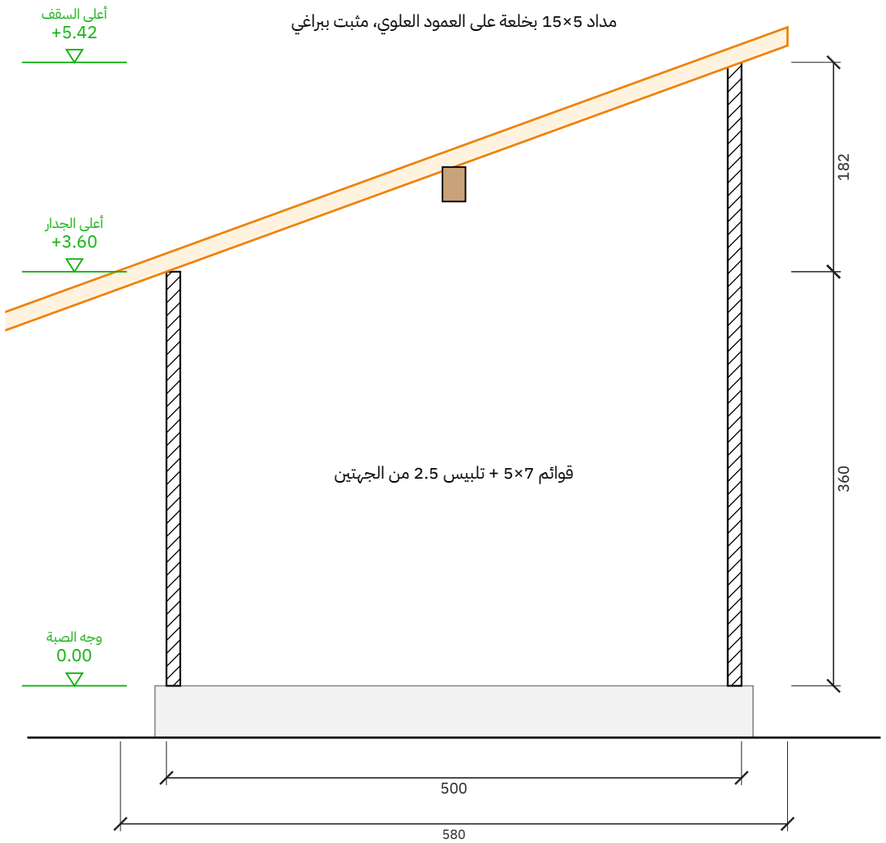

تفصيلة جلوس المداد على العلوي (1:5)

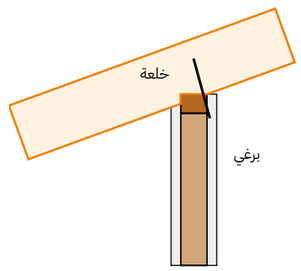

علوي 7×5 على قائم 7×5

المشروع / العميل	عنوان اللوحة	المقياس	التاريخ	رقم اللوحة
مجلس خشب 7.00 × 5.00 م — سقف مائل ممتد على جلسة خارجية عميل — مجلس 7×5	مسقط السقف والقطاع	1:50	2026-10-29	W-05 (5/12)

مصنع وتد الأخشاب
Watad Wood Factory

جدول مقاسات الأبواب والشبابيك

مقاس الفتحة الصافي في الجدار - الوحدة: سم

الرمز	النوع	العرض (سم)	الارتفاع (سم)	ارتفاع الجلسة (سم)	العدد	الموقع
ب1	باب مزدوج	140	240	-	1	الأمامية (على الحوش)
ب2	باب	70	210	-	1	دورة المياه
ش1	شباك	180	170	60	2	الأمامية (على الحوش) 2
ش2	شباك	160	140	80	1	الغربية
ش3	شباك	50	50	170	1	الشرقية

الإجمالي: أبواب 2 - شبابيك 4

جدول المساحات وبيانات المشروع


بيانات المشروع

البند	البيان
المشروع	مجلس خشب 7.00 × 5.00 م — سقف مائل ممتد على جلسة خارجية
العميل	عميل — مجلس 7×5
الموقع	—
الاستخدام	مجلس ضيافة
التاريخ	2026-10-29
نظام البناء	هيكل خشب 7×5 + تلبيس 2.5 سم من الجهتين
السقف	مائل باتجاه واحد 20° — قرميد معدني


جدول المساحات

م	الفراغ	الأبعاد (م)	المساحة (م2)
1	المجلس	5.14 × 4.76	24.47
2	المدخل	1.50 × 3.04	4.56
3	دورة مياه	1.50 × 1.60	2.40
	المساحة الصافية الداخلية		**31.43**
	الجلسة الخارجية المسقوفة	**7.00 × 2.00**	**14.00**
	المساحة الإجمالية المبنية	**7.00 × 5.00**	**35.00**
	المساحة الكلية (المبنية + التراس)		**49.00**

تأطير جدار جنوب — الطول 688 سم، الارتفاع 360 سم

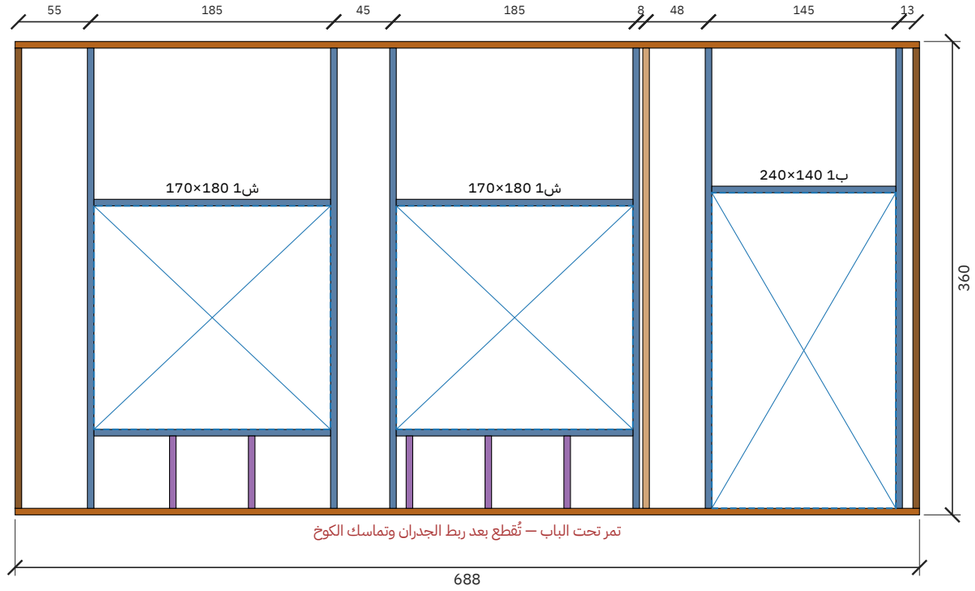

تأطير جدار شرق — الطول 488 سم، الارتفاع 360 سم

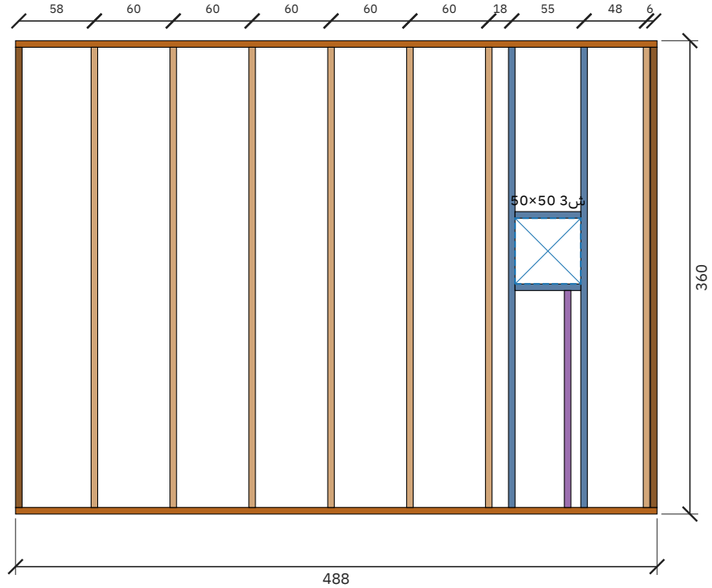


قاعدة سفلية | علوي | عمود | عمود زاوية | جنب فتحة | رأس فتحة | جلسة شباك | عمود قصير


المشروع / العميل	عنوان اللوحة	المقياس	التاريخ	رقم اللوحة
مجلس خشب 7.00 × 5.00 م — سقف مائل ممتد على جلسة خارجية عميل — مجلس 7×5	لوحات التأطير (للورشة)	—	2026-10-29	W-08 (8/12)

مصنع وتد الأخشاب
Watad Wood Factory

تأطير جدار شمال — الطول 688 سم، الارتفاع 542 سم

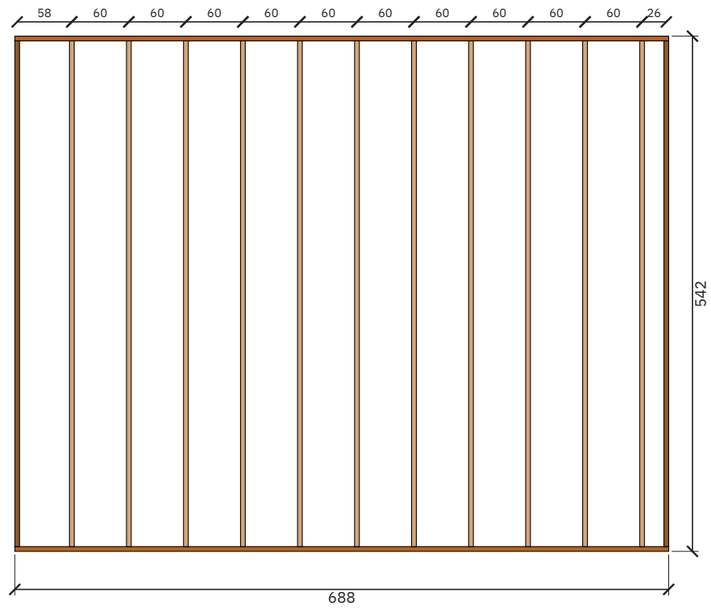

تأطير جدار غرب — الطول 488 سم، الارتفاع 360 سم

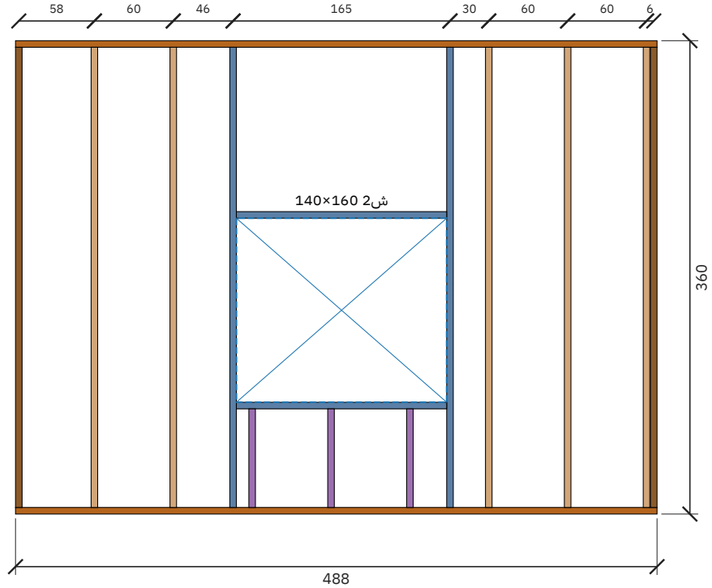


قاعدة سفلية | علوي | عمود | عمود زاوية | جنب فتحة | رأس فتحة | جلسة شباك | عمود قصير


المشروع / العميل	عنوان اللوحة	المقياس	التاريخ	رقم اللوحة
مجلس خشب 7.00 × 5.00 م — سقف مائل ممتد على جلسة خارجية **عميل — مجلس 7×5**	**لوحات التأطير (للورشة)**	**—**	**2026-10-29**	**W-09 (9/12)**

مصنع وتد الأخشاب
Watad Wood Factory

تأطير جدار جدار دورة المياه — الطول 162 سم، الارتفاع 360 سم (داخلي)

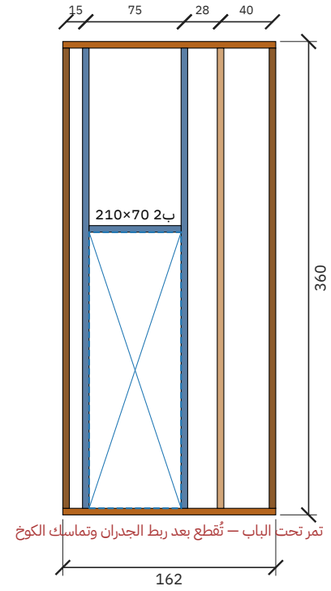

تأطير جدار جدار دورة المياه الغربي — الطول 172 سم، الارتفاع 360 سم (داخلي)

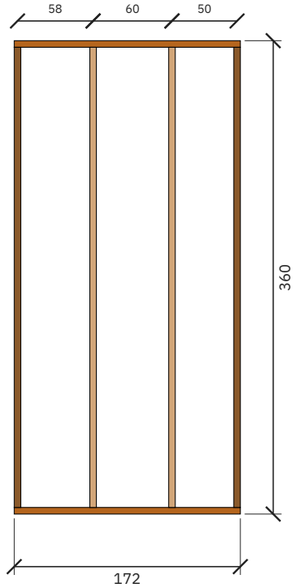

عمود قصير
جلسة شباك
رأس فتحة
جنب فتحة
عمود زاوية
عمود
علوي
قاعدة سفلية

مصنع وتد الأخشاب Watad Wood Factory	المشروع / العميل مجلس خشب 7.00 × 5.00 م — سقف مائل ممتد على جلسة خارجية عميل — مجلس 7×5	عنوان اللوحة لوحات التأطير (للورشة)	المقياس —	التاريخ 2026-10-29	رقم اللوحة W-10 (10/12)

جدول الكميات وخطة تقطيع الطبليات

البند	القيمة
الارتفاع المطلوب / المعتمد	360 / 360 سم
السقف	مائل باتجاه واحد 20° — أعلى نقطة 542 سم من وجه الصبة
المدادات 5×15	28 مداد (14 خط × قطعتين موصولة فوق الجسر الحامل بتراكب 60 سم) × حتى 340 سم — من طبلية 480
طبليات الطريقة الأولى (مداد + عمود)	28 طبلية × 480 سم
طبليات الطريقة الثانية (3 أعمدة)	15 طبلية × 320 سم
طبليات الطريقة الثانية (طويلة)	6 طبلية × 480 سم
إجمالي الطبليات 5×22.5	49
إجمالي قطع 5×7	82
قائمة تقطيع 5×7	688سم×4 | 532سم×13 | 488سم×4 | 350سم×38 | 180سم×4 | 172سم×2 | 165سم×1 | 162سم×2 | 160سم×2
	140سم×1 | 75سم×3 | 70سم×1 | 55سم×5 | 50سم×2
ألواح تلبيس 2.5 سم	292 لوح × 400 سم (مجموع الصفوف 922.6 م، 12 وجه)
أسمنت بورد 12 مم (122×244)	18 لوح (داخل دورات المياه)
العزل	134 لوح فوم صخري 80
الصبة	يجهزها العميل — 20 سم، مفرغة تحت دورات المياه

مراجعة التصميم مقابل قواعد المصنع

النوع	البند	التفاصيل	المقترح
ملاحظة	بحر المدادات	أطول بحر بدون جدار داخلي يحمل المداد: جهة أ: 500 سم. يحتاج رقم المصنع لأقصى بحر مسموح لتحديد المدادات اللي تُقوّى 20×5.	
ملاحظة	الصبة والدرج	ارتفاع الصبة 45 سم ← 3 درجة بقائمة 15.0 سم.	
ملاحظة	مناسيب رؤوس الفتحات	رؤوس الأبواب والشبابيك على مناسيب مختلفة: 210، 220، 230، 240 سم.	
سؤال	يحتاج تأكيد	أقصى بحر للمداد بدون جدار داخلي قبل إضافة تقوية 5×7 (مداد 20×5)؟	
سؤال	يحتاج تأكيد	التغطية الصافية للوح التلبيس بعد التعشيق (مستنتجة مؤقتاً 18.67 سم من 280/15)؟	
سؤال	يحتاج تأكيد	هل يوضع أعمدة قصيرة فوق رأس الشباك/الباب إلى العلوي؟	
سؤال	يحتاج تأكيد	مكان الوصلة في القاعدة والعلوي إذا الجدار أطول من الطبلية؟	