المنظور ثلاثي الأبعاد والمواد

النمط: جوزي غامق + إطارات سوداء — رندر واقعي بخامات حقيقية



جدول المواد والألوان

الخشب / الصبغة

صبغة عسلي / سيدر

القرميد

قرميد رمادي غامق

الزجاج

زجاج أزرق (بلو) عاكس

إطارات الشبابيك والأبواب

إطار ألمنيوم أسود

الكنار والزوايا

نفس الصبغة أغمق درجة


الصبة

خرسانة 0 سم


الدربزين: ألواح أفقية متقاربة (عصري)

تقسيم الشبابيك: شبكة | الباب الرئيسي: زجاج بتقسيمات (فرنسي)

أنواع الدربزين المعتمدة (من مشاريع المصنع)

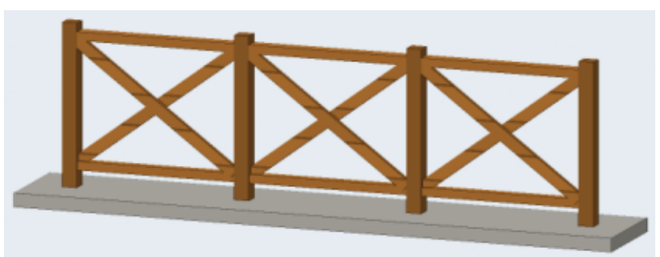

تقاطع X (صورة 5)

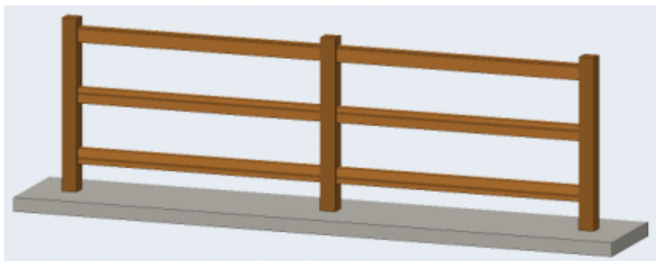

3 مرابيع أفقية (صورة 2)




قوائم رأسية متقاربة (صورة 1)

المشروع / العميل	عنوان اللوحة	المقياس	التاريخ	رقم اللوحة
مصنع وتد الأخشاب Watad Wood Factory **ملحق سطح – غرفة نوم + صالة – 4.75 × 9.00 م** **عميل – ملحق سطح**	**المنظور والمواد**	**1:50**	**2026-10-30**	**W-01 (1/11)**


المسقط الأفقي مع الفرش

الأبعاد بالسنتيمتر - الجدران: قوائم 5×7 + تلبيس 2.5 من الجهتين (12 سم)

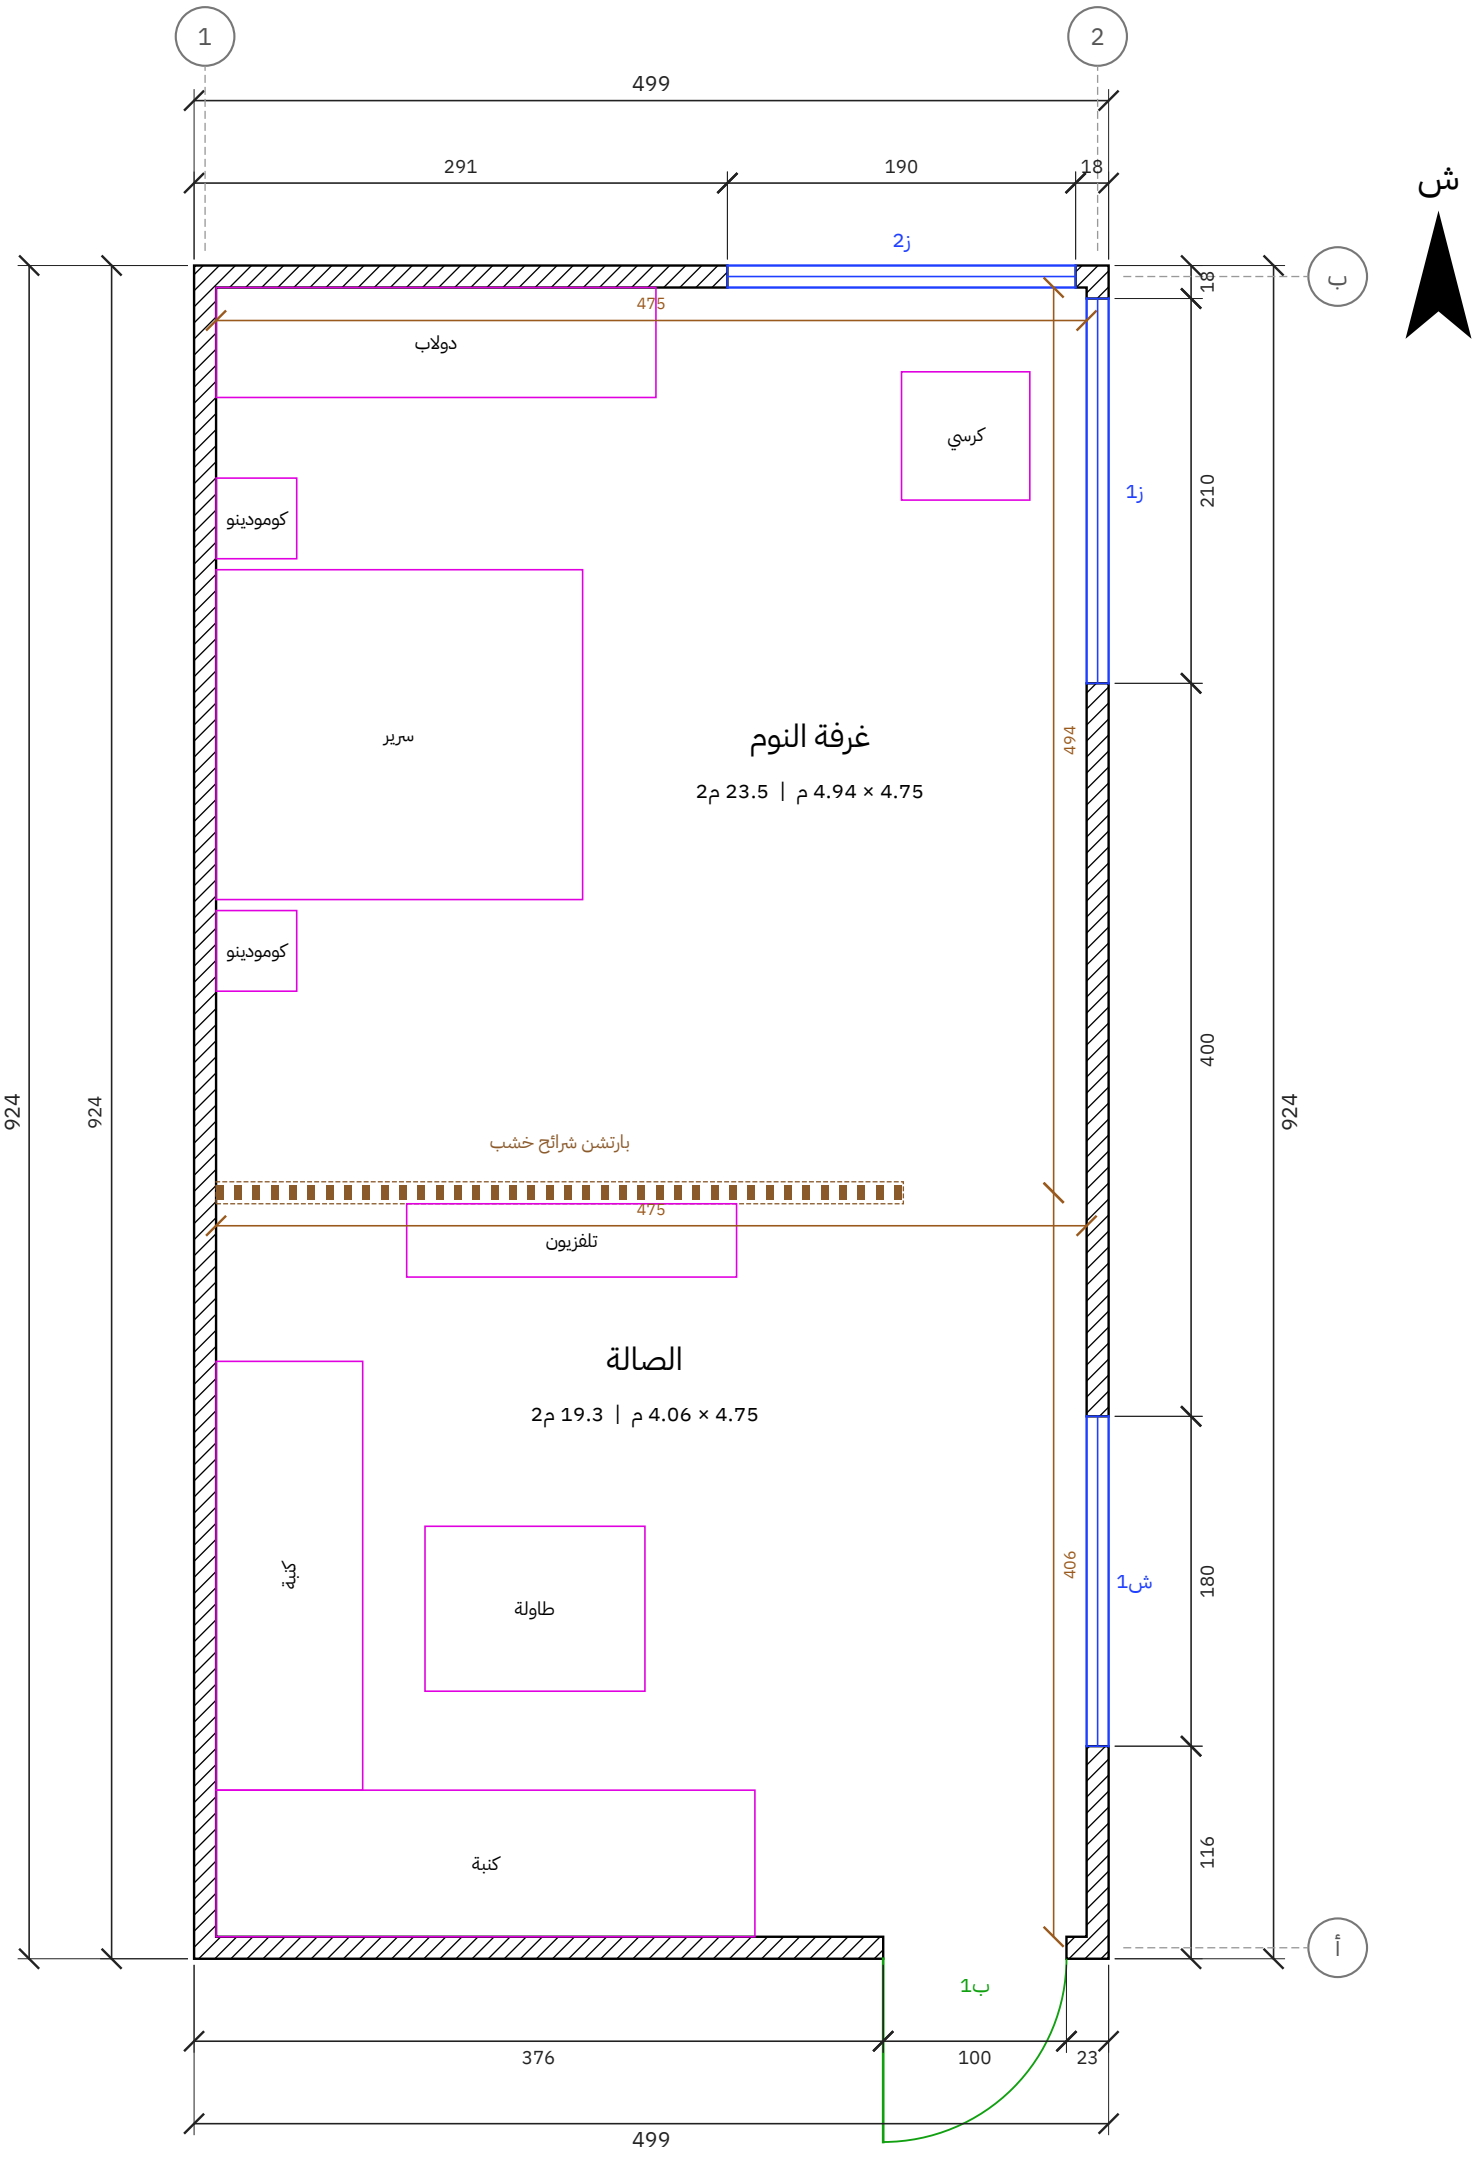


المشروع / العميل	عنوان اللوحة	المقياس	التاريخ	رقم اللوحة
ملحق سطح – غرفة نوم + صالة – 4.75 × 9.00 م عميل – ملحق سطح	المسقط الأفقي	1:50	2026-10-30	W-02 (2/11)

مصنع وتد الأخشاب
Watad Wood Factory

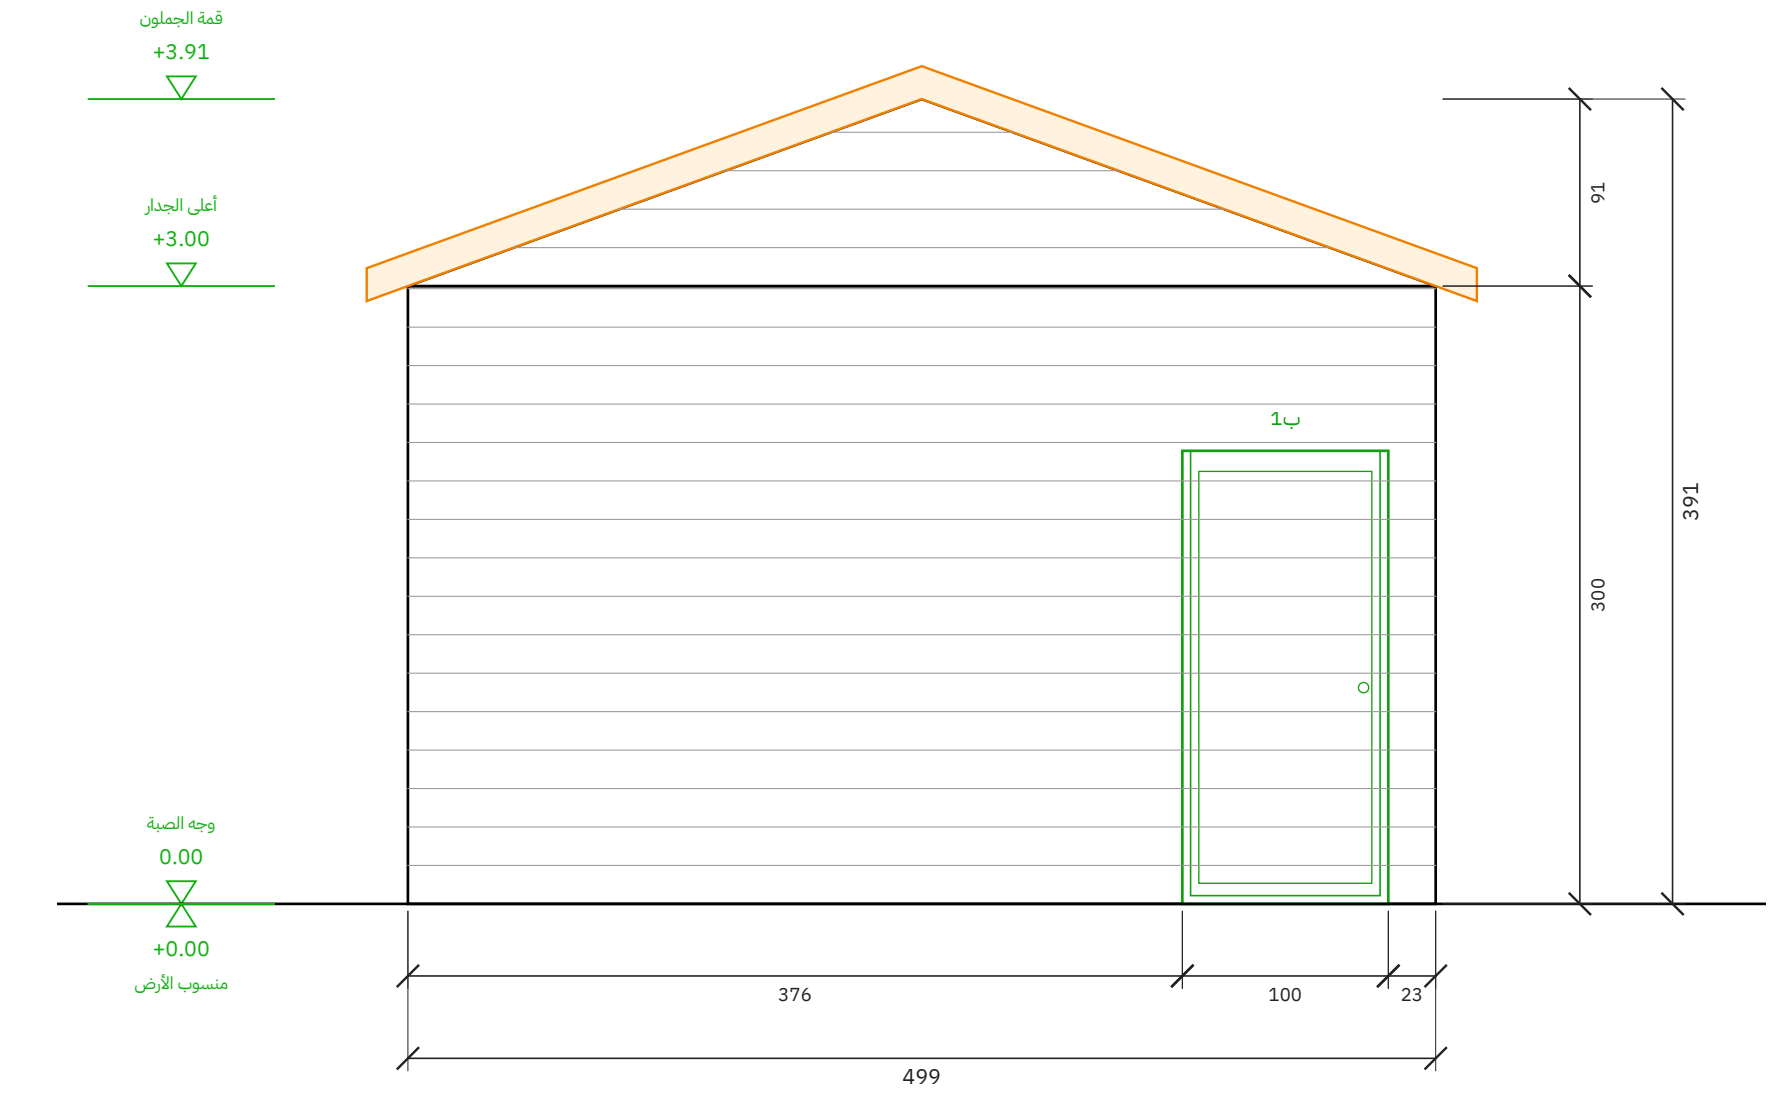

جدار المدخل (جهة السطح)

مقياس 1:50 | الوحدة: سم

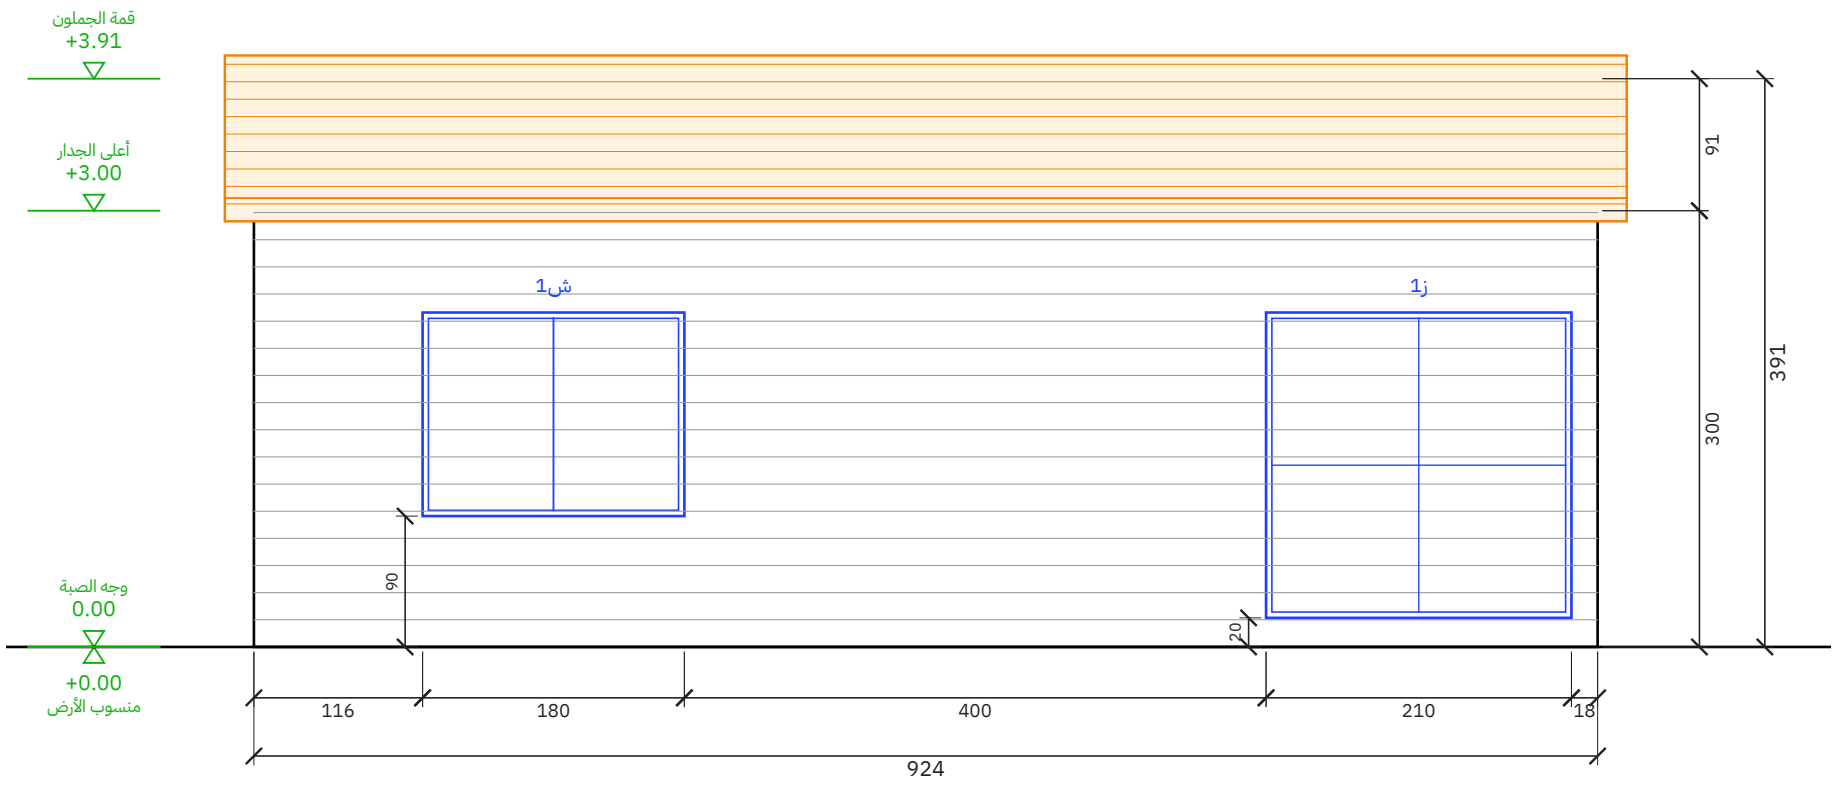


الجدار الأيمن (القائم + الرفع)

مقياس 1:50 | الوحدة: سم


المشروع / العميل	عنوان اللوحة	المقياس	التاريخ	رقم اللوحة
ملحق سطح – غرفة نوم + صالة – 4.75 × 9.00 م عميل – ملحق سطح	جدار المدخل (جهة السطح) والجدار الأيمن (القائم + الرفع)	1:50	2026-10-30	W-03 (3/11)

مصنع وتد الأخشاب
Watad Wood Factory

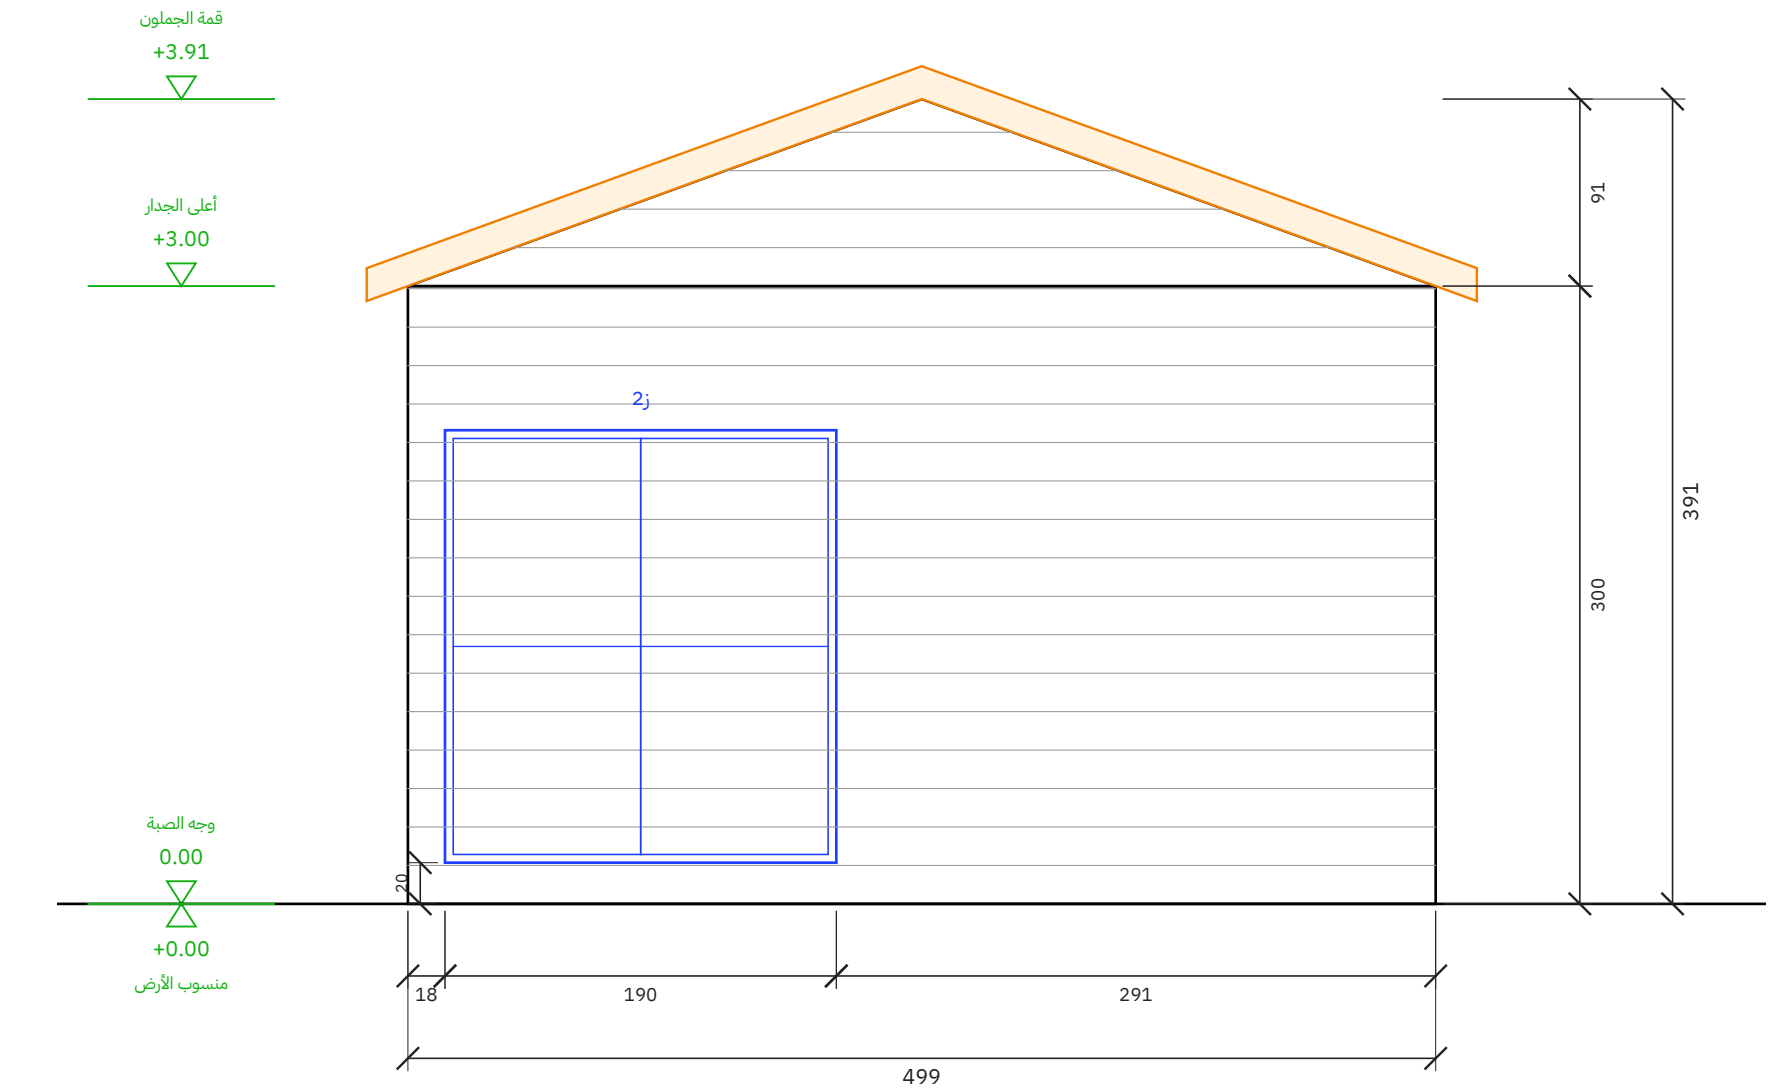

الجدار الخلفي (غرفة النوم)

مقياس 1:50 | الوحدة: سم

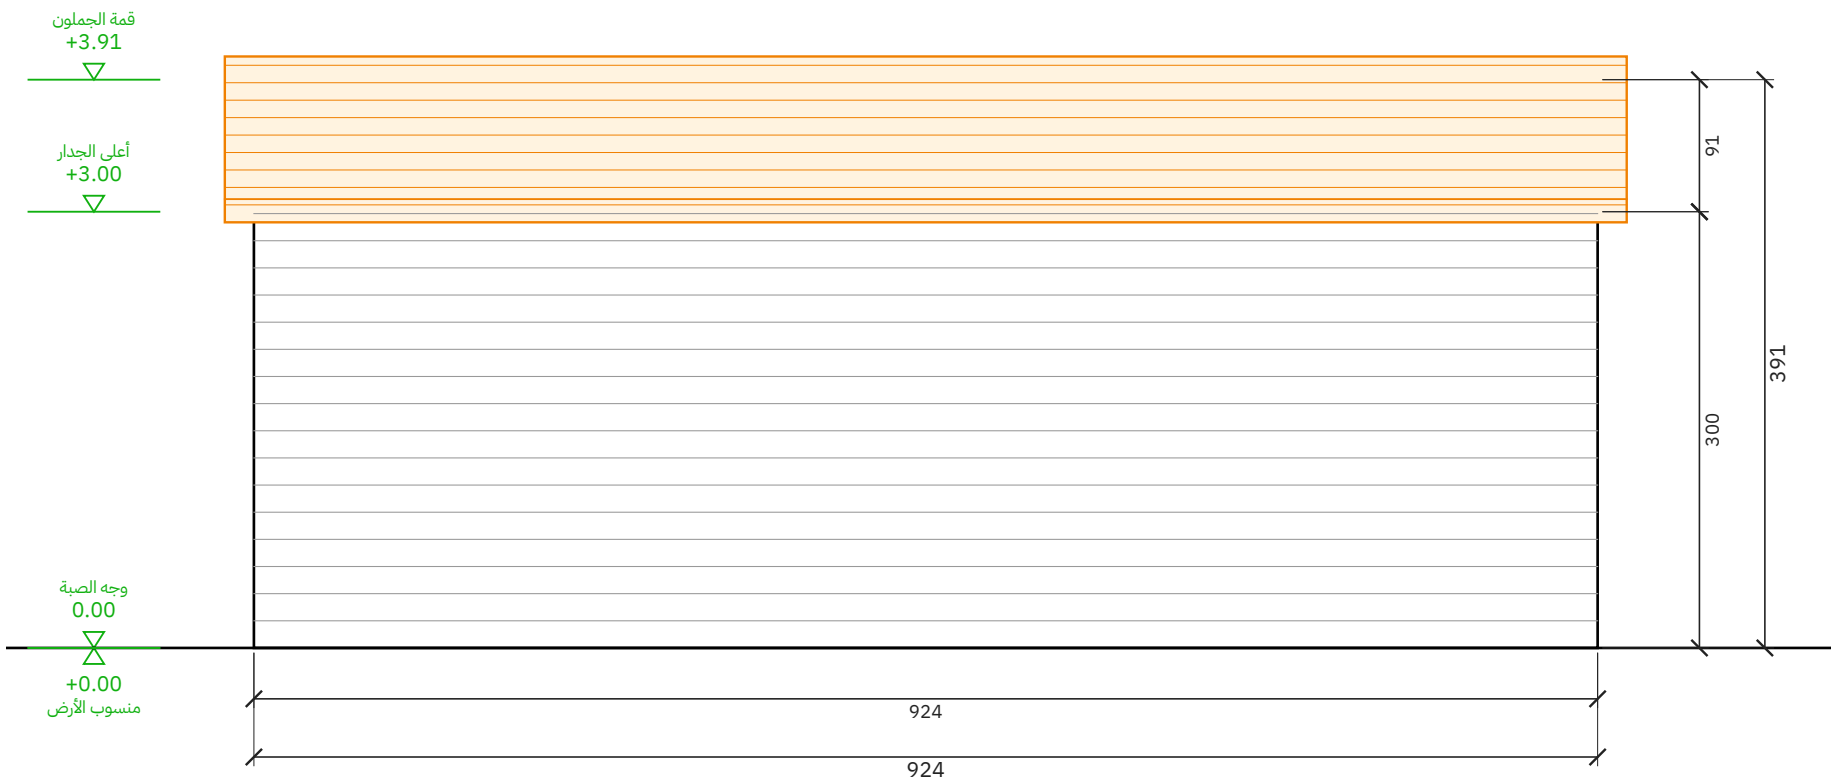

الجدار الأيسر (القائم + الرفع)


مقياس 1:50 | الوحدة: سم

المشروع / العميل	عنوان اللوحة	المقياس	التاريخ	رقم اللوحة
ملحق سطح – غرفة نوم + صالة – 4.75 × 9.00 م عميل – ملحق سطح	الجدار الخلفي (غرفة النوم) والجدار الأيسر (القائم + الرفع)	1:50	2026-10-30	W-04 (4/11)

مصنع وتد الأخشاب
Watad Wood Factory


مسقط السقف (جملون)

رفرف 20 سم من كل جهة | مقياس 1:50

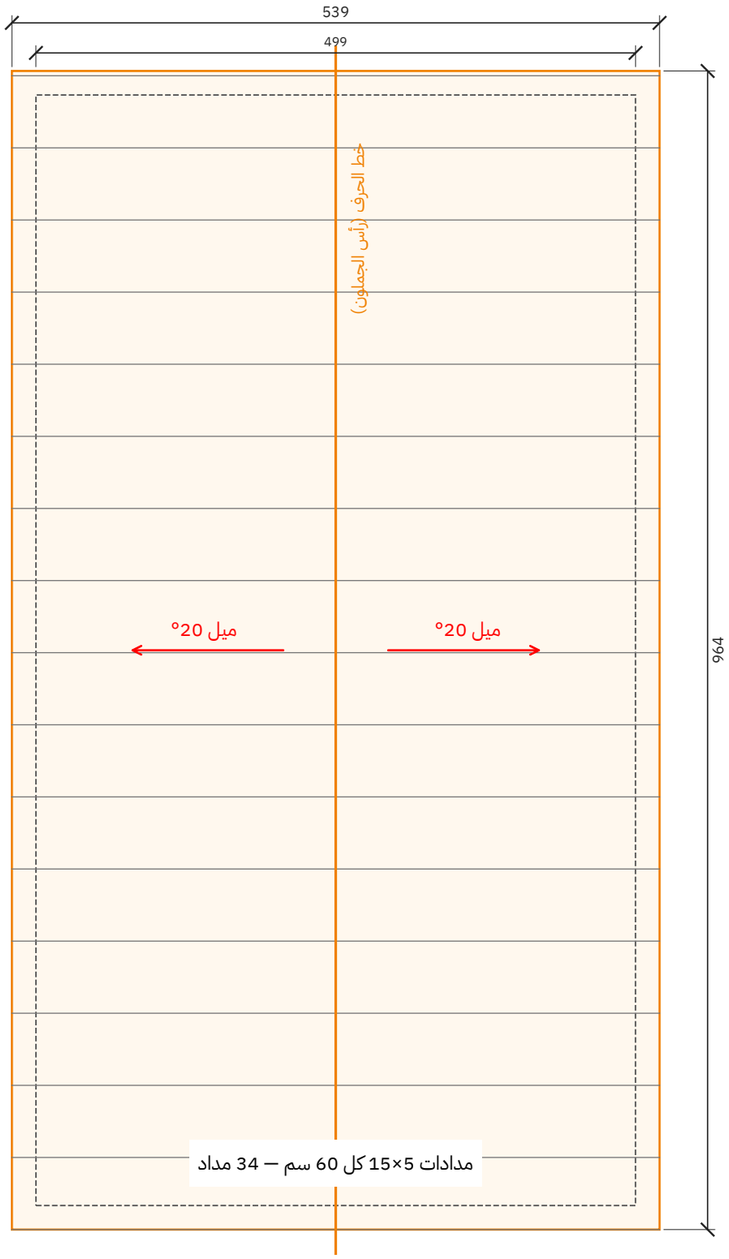


قطاع عرضي أ-أ

مقياس 1:50 | الوحدة: سم

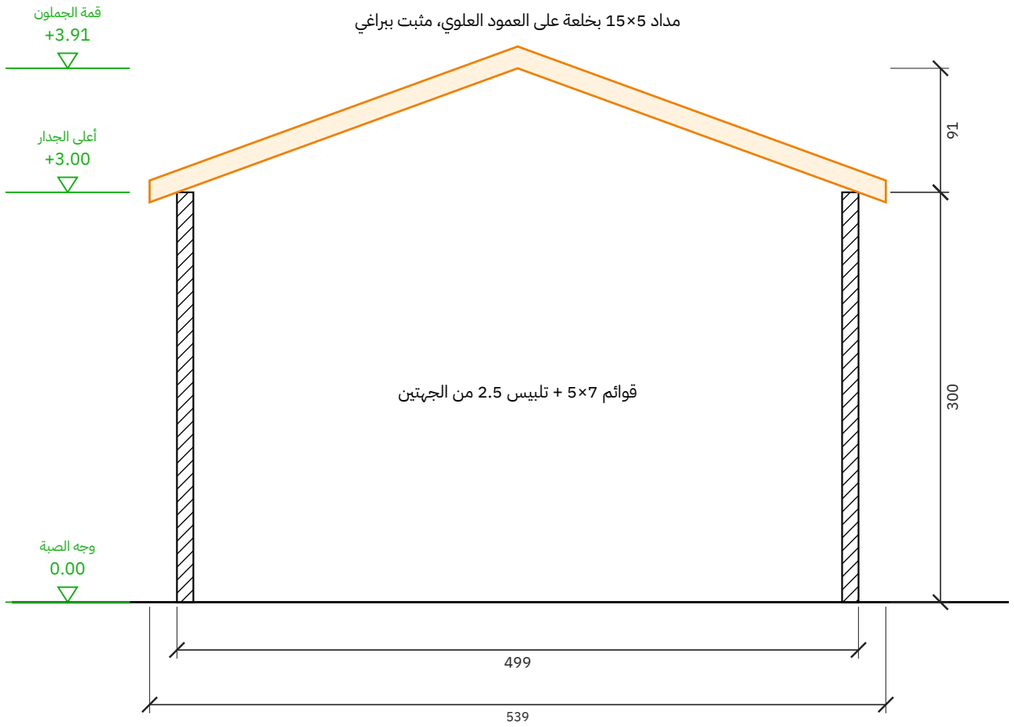

تفصيلة جلوس المداد على العلوي (1:5)

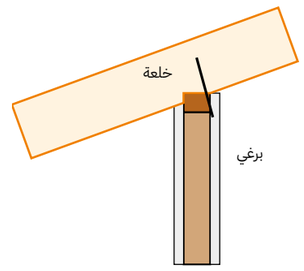

مصنع وتد الأخشاب Watad Wood Factory	المشروع / العميل ملحق سطح — غرفة نوم + صالة — 4.75 × 9.00 م عميل — ملحق سطح	عنوان اللوحة مسقط السقف والقطاع	المقياس 1:50	التاريخ 2026-10-30	رقم اللوحة W-05 (5/11)

جدول مقاسات الأبواب والشبابيك

مقاس الفتحة الصافي في الجدار - الوحدة: سم

الرمز	النوع	العرض (سم)	الارتفاع (سم)	ارتفاع الجلسة (سم)	العدد	الموقع
ب1	باب	100	220	-	1	جدار المدخل (جهة السطح)
ز1	شباك	210	210	20	1	الجدار الأيمن (القائم + الرفع)
ز2	شباك	190	210	20	1	الجدار الخلفي (غرفة النوم)
ش1	شباك	180	140	90	1	الجدار الأيمن (القائم + الرفع)

الإجمالي: أبواب 1 - شبابيك 3

جدول المساحات وبيانات المشروع


بيانات المشروع

البند	البيان
المشروع	ملحق سطح — غرفة نوم + صالة — 4.75 × 9.00 م
العميل	عميل — ملحق سطح
الموقع	—
الاستخدام	ملحق سكني على السطح
التاريخ	2026-10-30
نظام البناء	هيكل خشب 5×7 + تلبيس 2.5 سم من الجهتين
السقف	جملون 20° — قرميد معدني


جدول المساحات

م	الفراغ	الأبعاد (م)	المساحة (م2)
1	الصالة	4.75 × 4.06	19.29
2	غرفة النوم	4.75 × 4.94	23.46
	المساحة الصافية الداخلية		**42.75**
	المساحة الإجمالية المبنية	**4.99 × 9.24**	**46.11**

تأطير جدار جنوب — الطول 487 سم، الارتفاع 300 سم

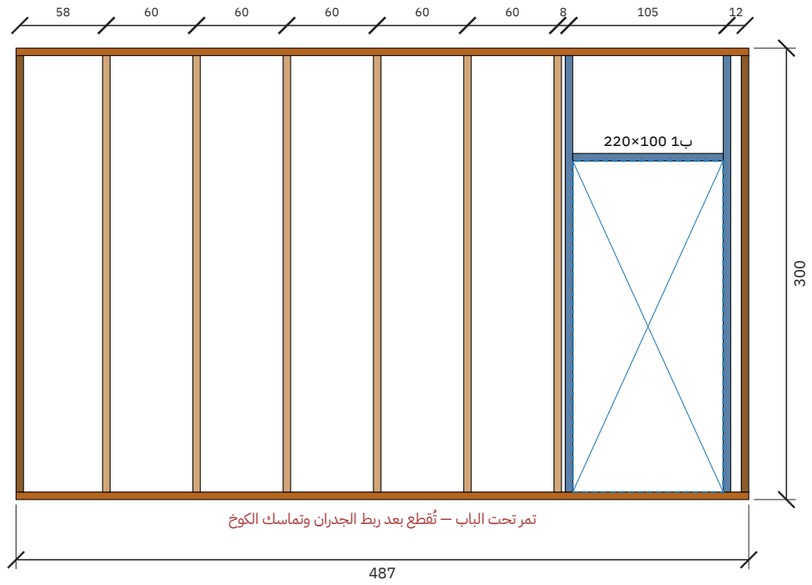

تأطير جدار شرق — الطول 912 سم، الارتفاع 300 سم

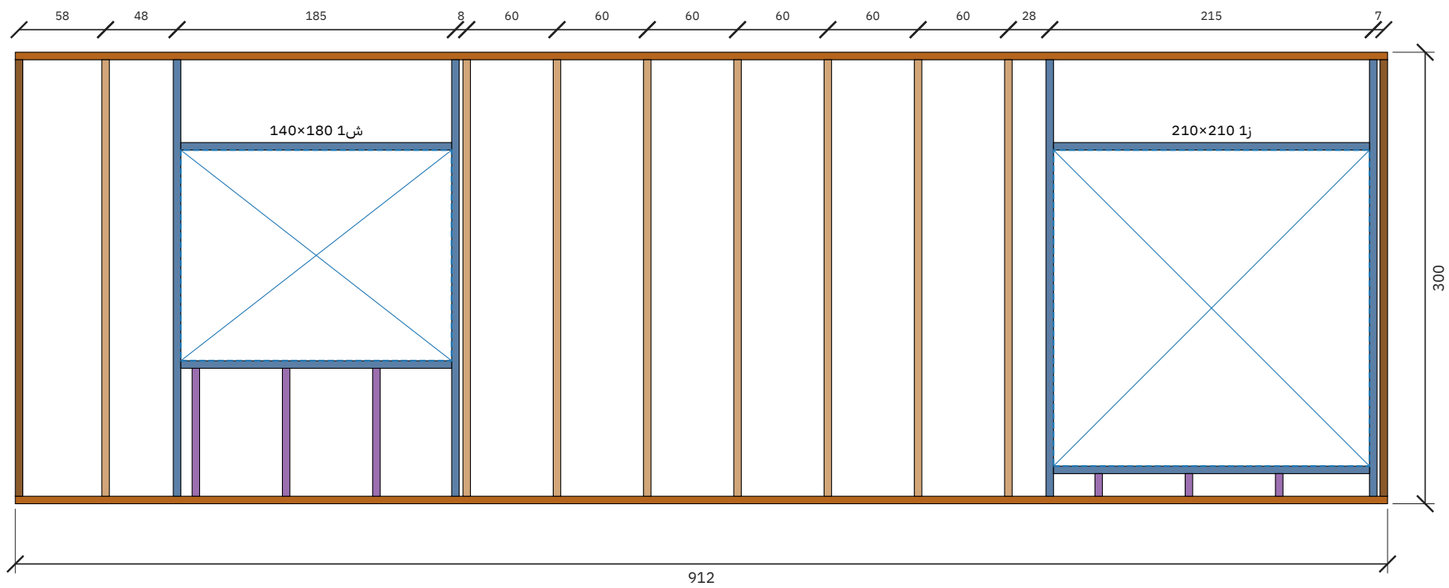


قاعدة سفلية | علوي | عمود | عمود زاوية | جنب فتحة | رأس فتحة | جلسة شباك | عمود قصير


المشروع / العميل	عنوان اللوحة	المقياس	التاريخ	رقم اللوحة
ملحق سطح — غرفة نوم + صالة — 4.75 × 9.00 م عميل — ملحق سطح	لوحات التأطير (للورشة)	—	2026-10-30	W-08 (8/11)

مصنع وتد الأخشاب
Watad Wood Factory

تأطير جدار شمال — الطول 487 سم، الارتفاع 300 سم

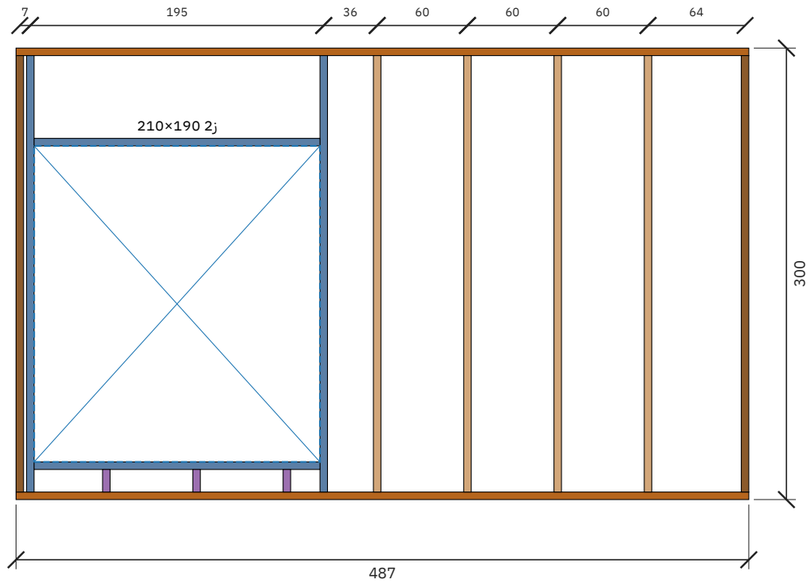

تأطير جدار غرب — الطول 912 سم، الارتفاع 300 سم

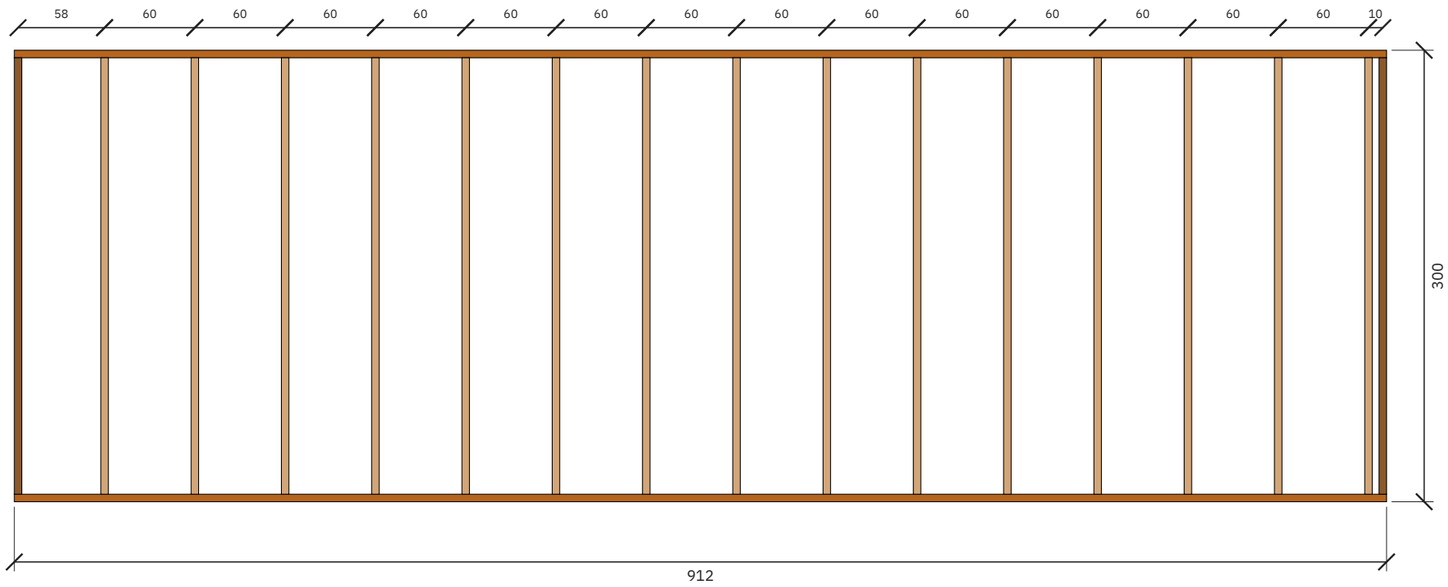

قاعدة سفلية | علوي | عمود | عمود زاوية | جنب فتحة | رأس فتحة | جلسة شباك | عمود قصير

المشروع / العميل	عنوان اللوحة	المقياس	التاريخ	رقم اللوحة
ملحق سطح — غرفة نوم + صالة — 4.75 × 9.00 م **عميل — ملحق سطح**	**لوحات التأطير (للورشة)**	**—**	**2026-10-30**	**W-09 (9/11)**

مصنع وتد الأخشاب
Watad Wood Factory

جدول الكميات وخطة تقطيع الطبليات

البند	القيمة
الارتفاع المطلوب / المعتمد	300 / 300 سم
السقف	جملون 20° — أعلى نقطة 391 سم من وجه الصبة
المدادات 5×15	34 مداد (17 لكل جهة) × حتى 287 سم — من طبلية 320
طبليات الطريقة الأولى (مداد + عمود)	34 طبلية × 320 سم
طبليات الطريقة الثانية (3 أعمدة)	14 طبلية × 320 سم
إجمالي الطبليات 5×22.5	48
إجمالي قطع 5×7	73
قائمة تقطيع 5×7	912سم×4 | 487سم×4 | 290سم×49 | 210سم×2 | 190سم×2 | 180سم×2 | 100سم×1 | 85سم×3 | 15سم×6
ألواح تلبيس 2.5 سم	250 لوح × 400 سم (مجموع الصفوف 800.5 م، 8 وجه)
أسمنت بورد 12 مم (122×244)	0 لوح (داخل دورات المياه)
العزل	80 لوح فوم صخري 99
الصبة	يجهزها العميل — 20 سم، مفرغة تحت دورات المياه

مراجعة التصميم مقابل قواعد المصنع

النوع	البند	التفاصيل	المقترح
ملاحظة	بحر المدادات	أطول بحر بدون جدار داخلي يحمل المداد: جهة أ: 250 سم، جهة ب: 250 سم. يحتاج رقم المصنع لأقصى بحر مسموح لتحديد المدادات اللي تُقوّى 20×5.	
ملاحظة	الصبة والدرج	ارتفاع الصبة 0 سم ← 1 درجة بقائمة 0.0 سم. بارتفاع 20 سم ما يطلع إلا درجة وحدة؛ للدكة المرتفعة 45 سم = 3 درجات.	
ملاحظة	مناسيب رؤوس الفتحات	رؤوس الأبواب والشبابيك على مناسيب مختلفة: 220، 230 سم.	
سؤال	يحتاج تأكيد	أقصى بحر للمداد بدون جدار داخلي قبل إضافة تقوية 7×5 (مداد 20×5)؟	
سؤال	يحتاج تأكيد	التغطية الصافية للوح التلبيس بعد التعشيق (مستنتجة مؤقتاً 18.67 سم من 280/15)؟	
سؤال	يحتاج تأكيد	هل يوضع أعمدة قصيرة فوق رأس الشباك/الباب إلى العلوي؟	
سؤال	يحتاج تأكيد	مكان الوصلة في القاعدة والعلوي إذا الجدار أطول من الطبلية؟	