

المسقط الأفقي مع الفرش

الأبعاد بالسنتيمتر - الجدران: قوائم 5×7 + تلبيس 2.5 من الجهتين (12 سم)

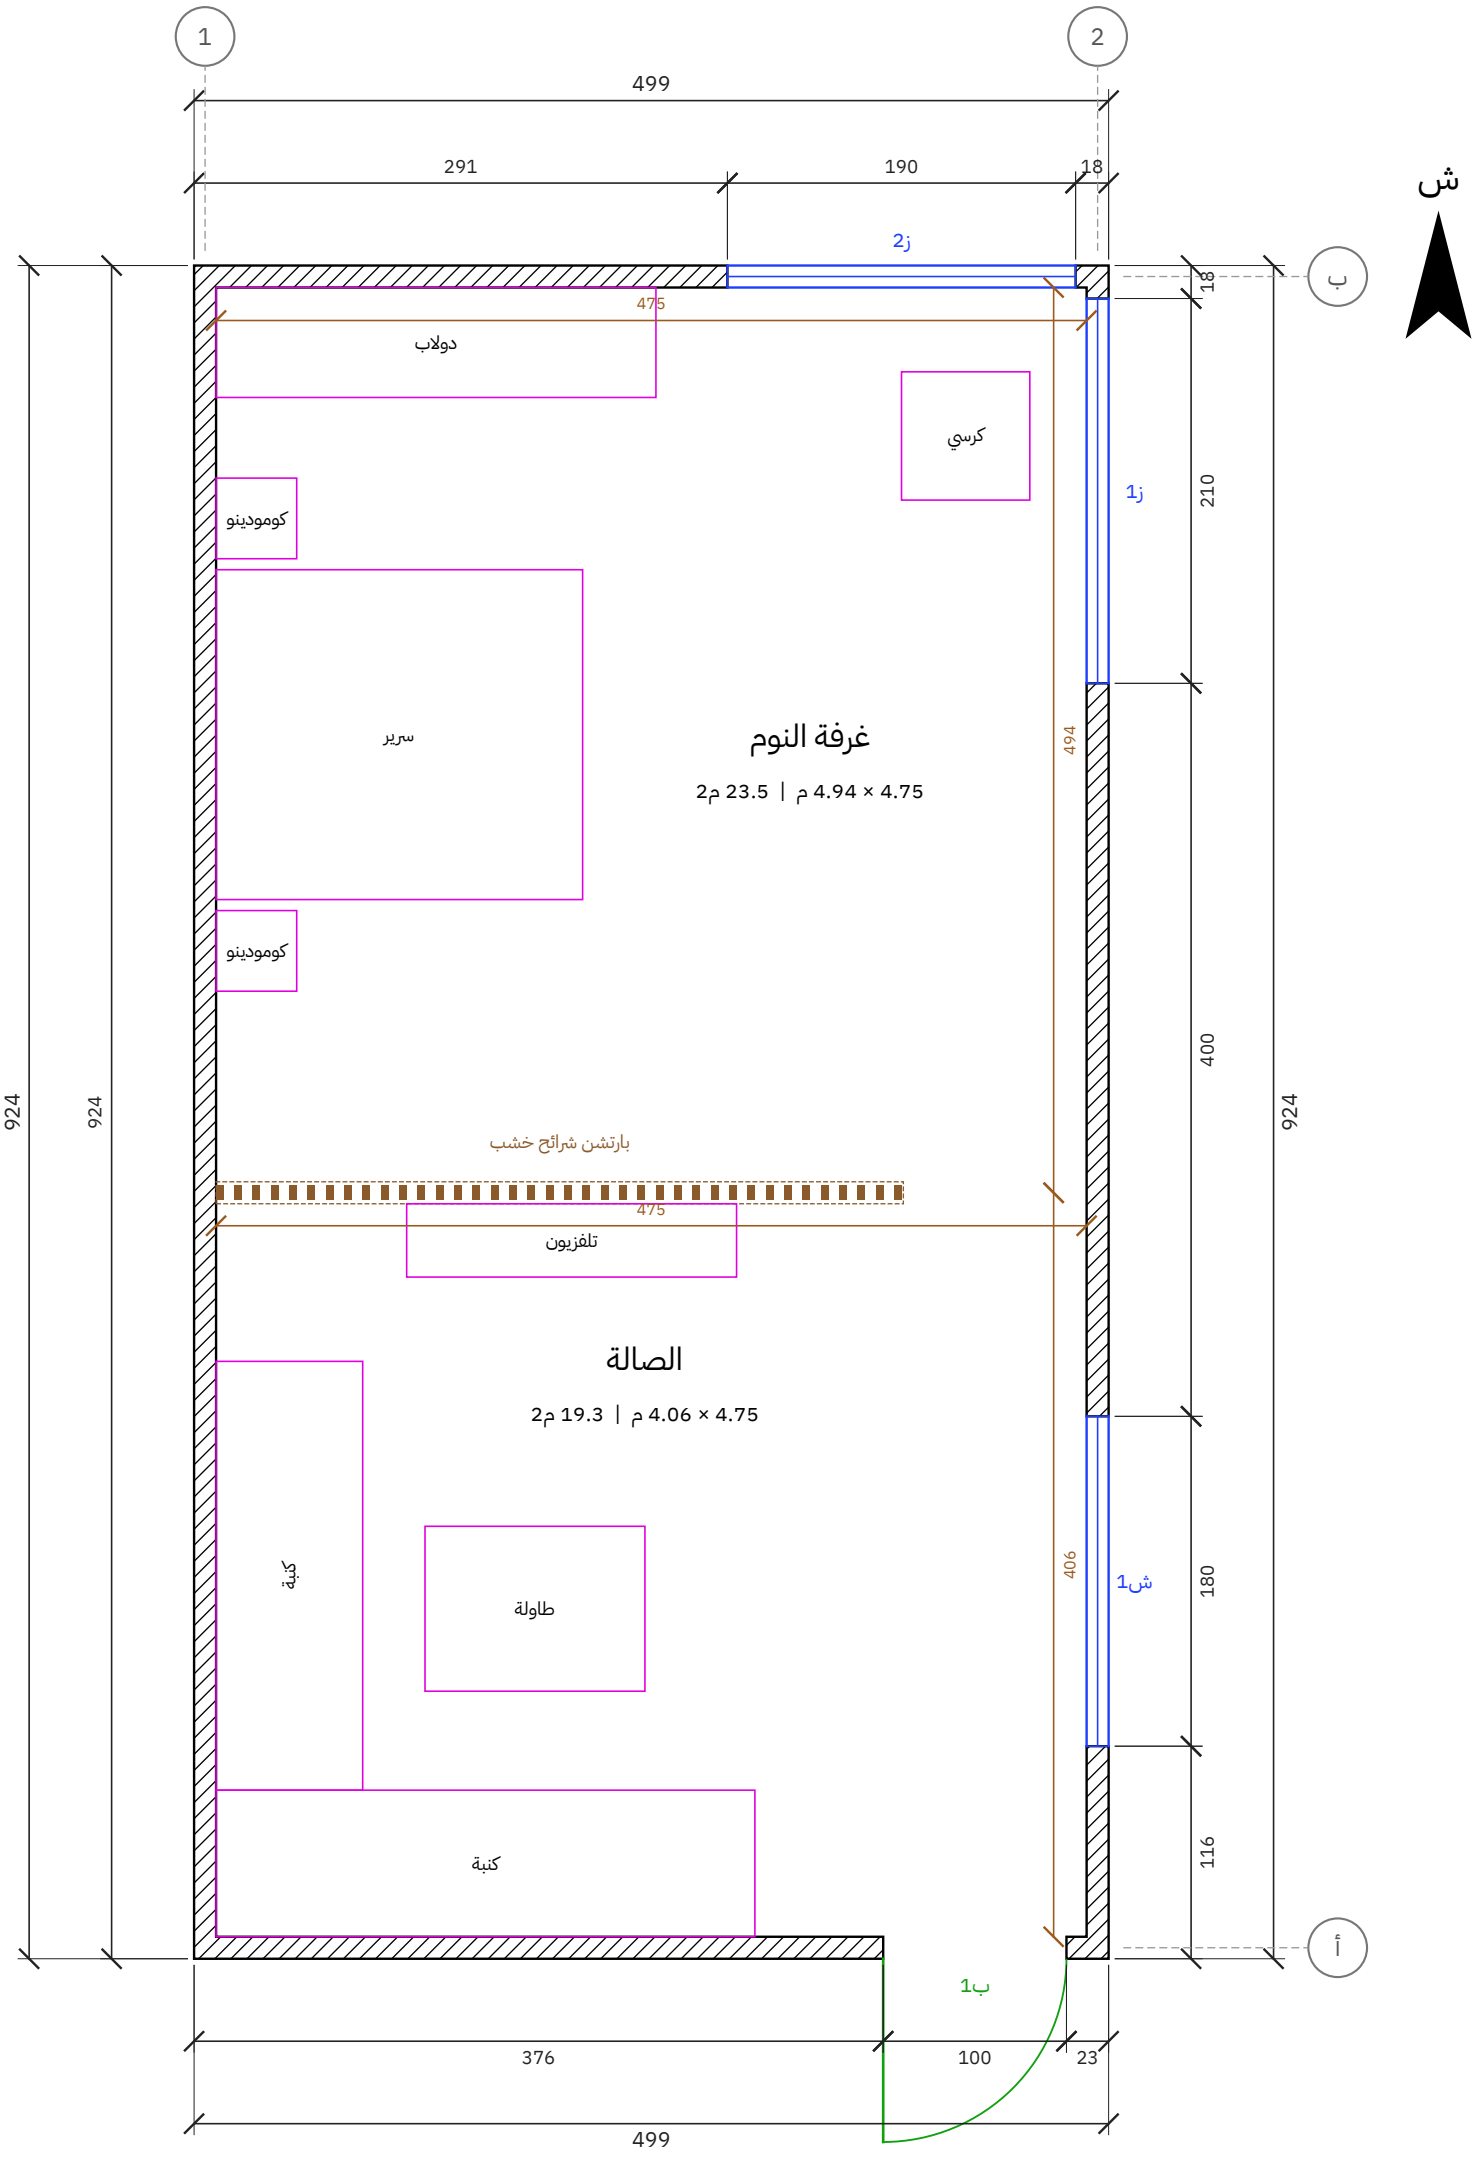


المشروع / العميل	عنوان اللوحة	المقياس	التاريخ	رقم اللوحة
ملحق سطح – غرفة نوم + صالة – 4.75 × 9.00 م عميل – ملحق سطح	المسقط الأفقي	1:50	2026-10-30	A-01 (1/9)

مصنع وتد الأخشاب
Watad Wood Factory

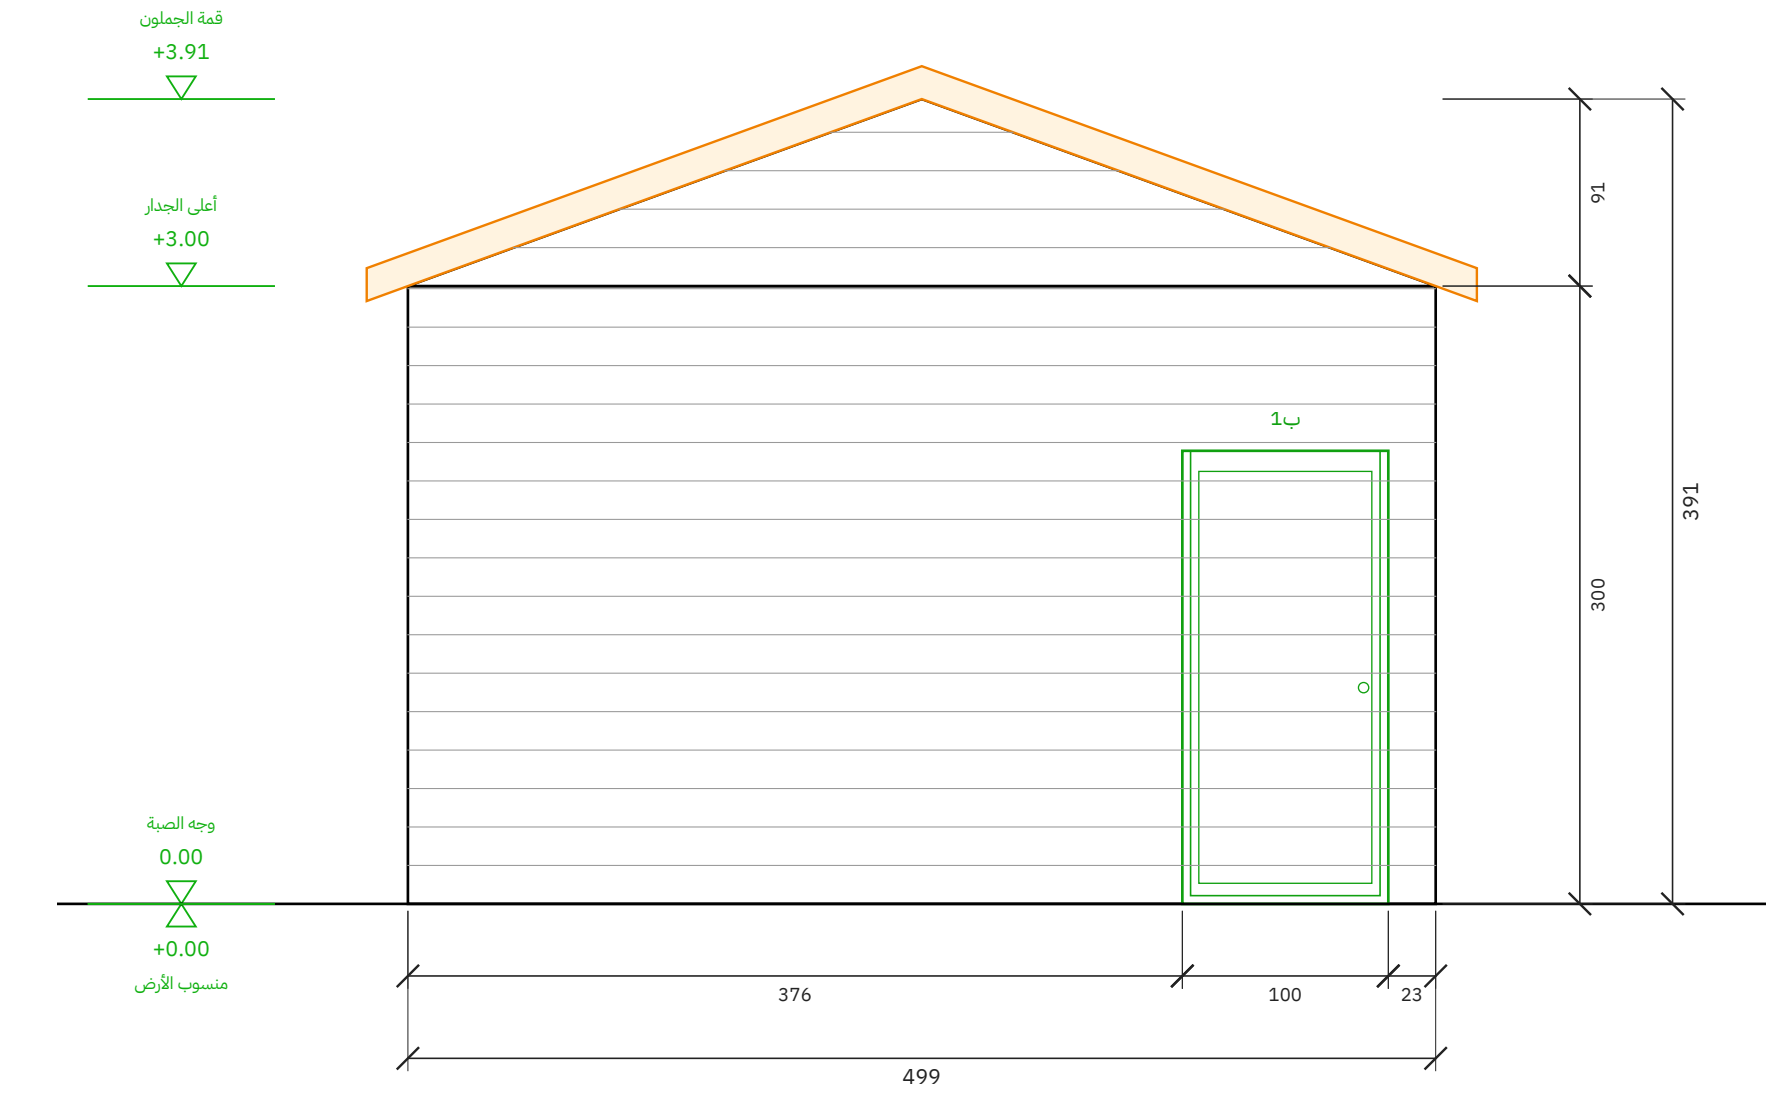

جدار المدخل (جهة السطح)

مقياس 1:50 | الوحدة: سم

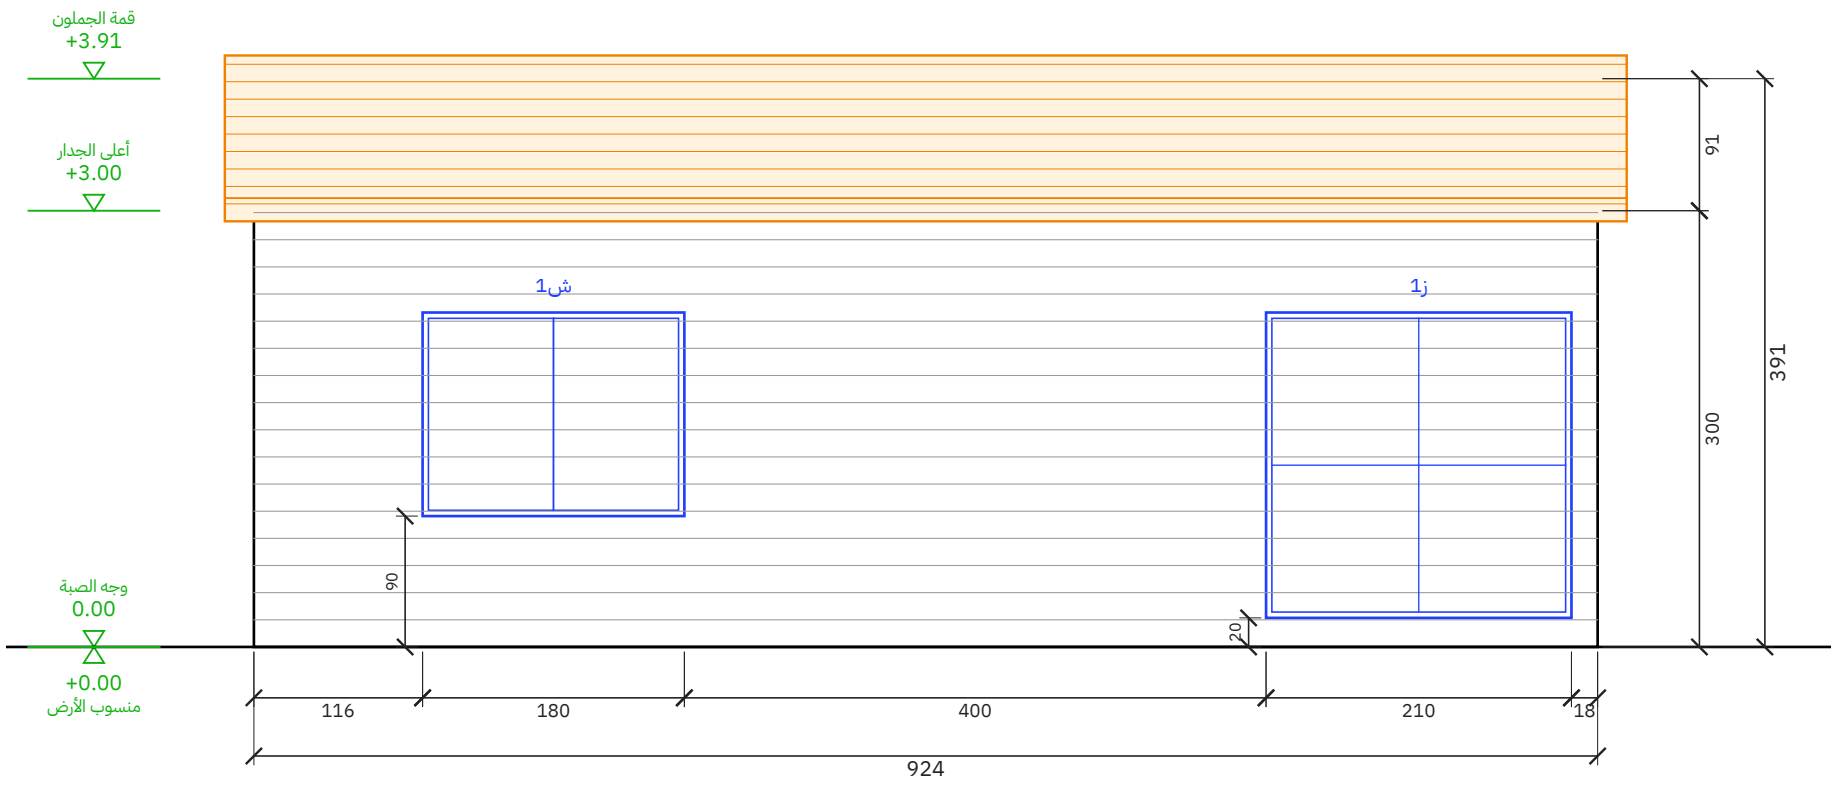


الجدار الأيمن (القائم + الرفع)

مقياس 1:50 | الوحدة: سم


المشروع / العميل	عنوان اللوحة	المقياس	التاريخ	رقم اللوحة
ملحق سطح – غرفة نوم + صالة – 4.75 × 9.00 م عميل – ملحق سطح	جدار المدخل (جهة السطح) والجدار الأيمن (القائم + الرفع)	1:50	2026-10-30	A-02 (2/9)

مصنع وتد الأخشاب
Watad Wood Factory

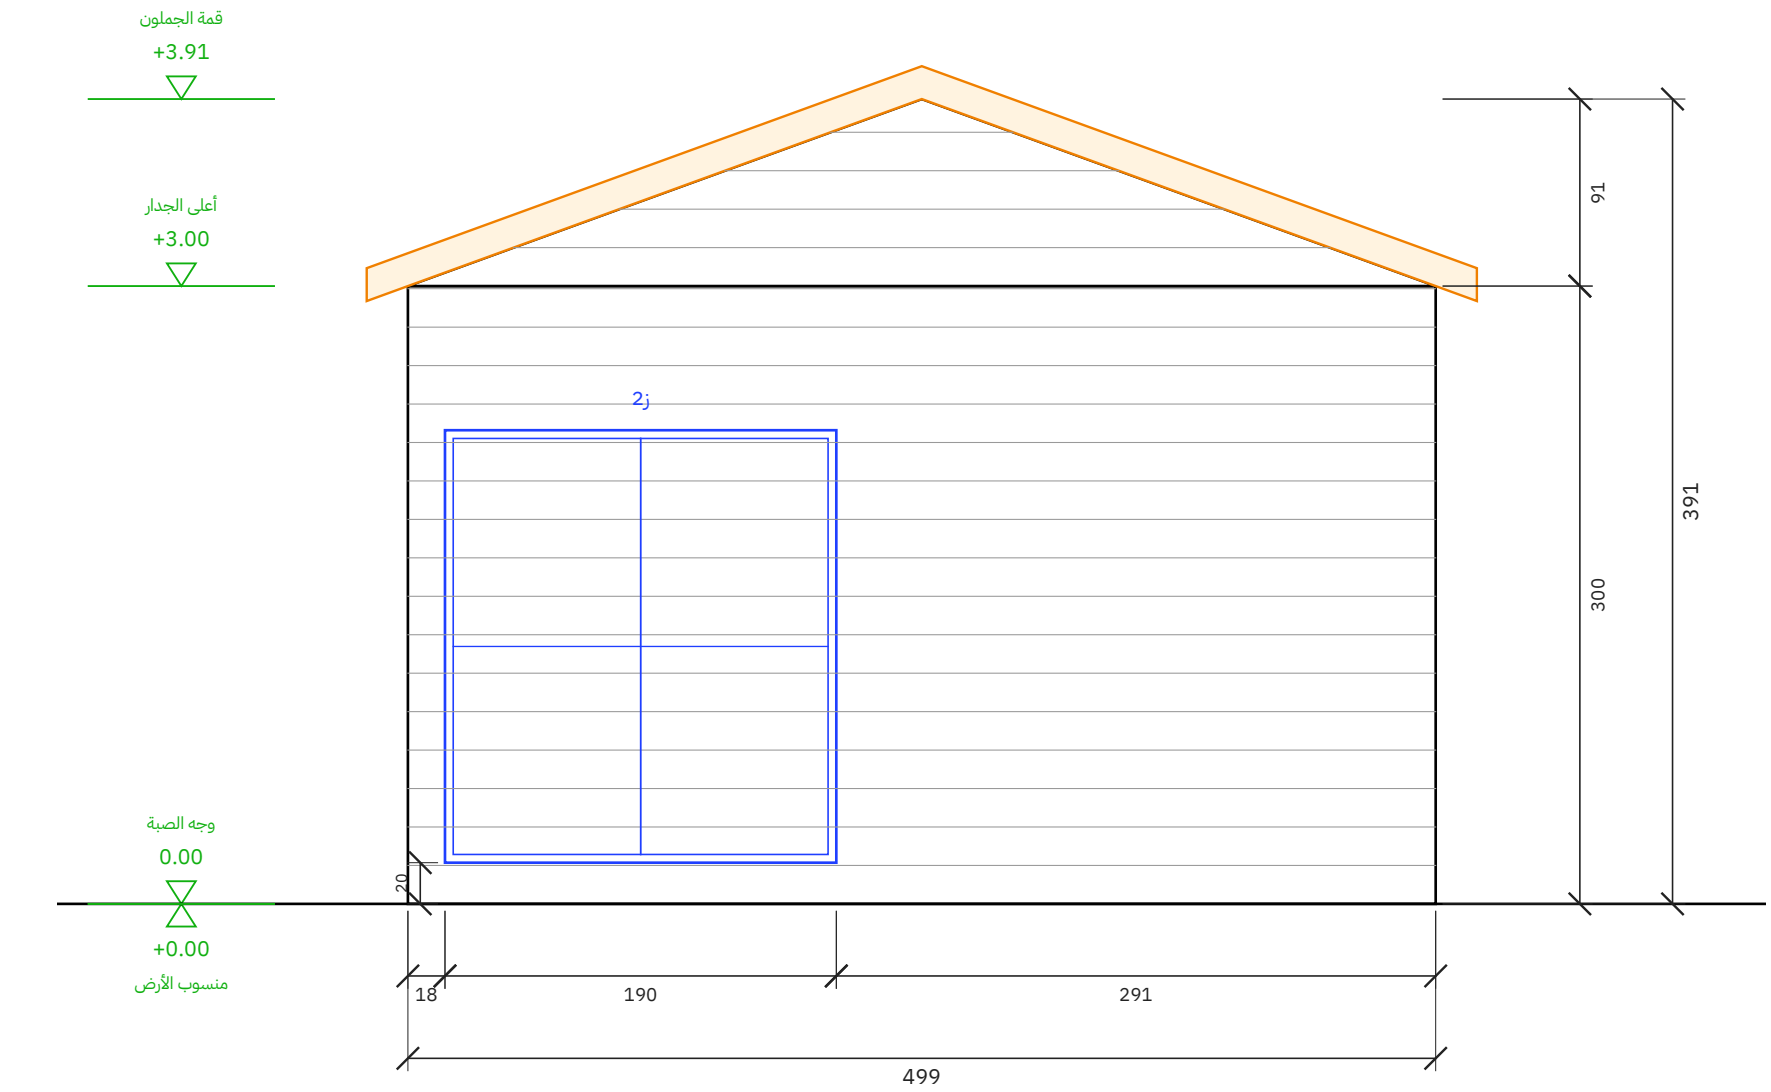

الجدار الخلفي (غرفة النوم)

مقياس 1:50 | الوحدة: سم

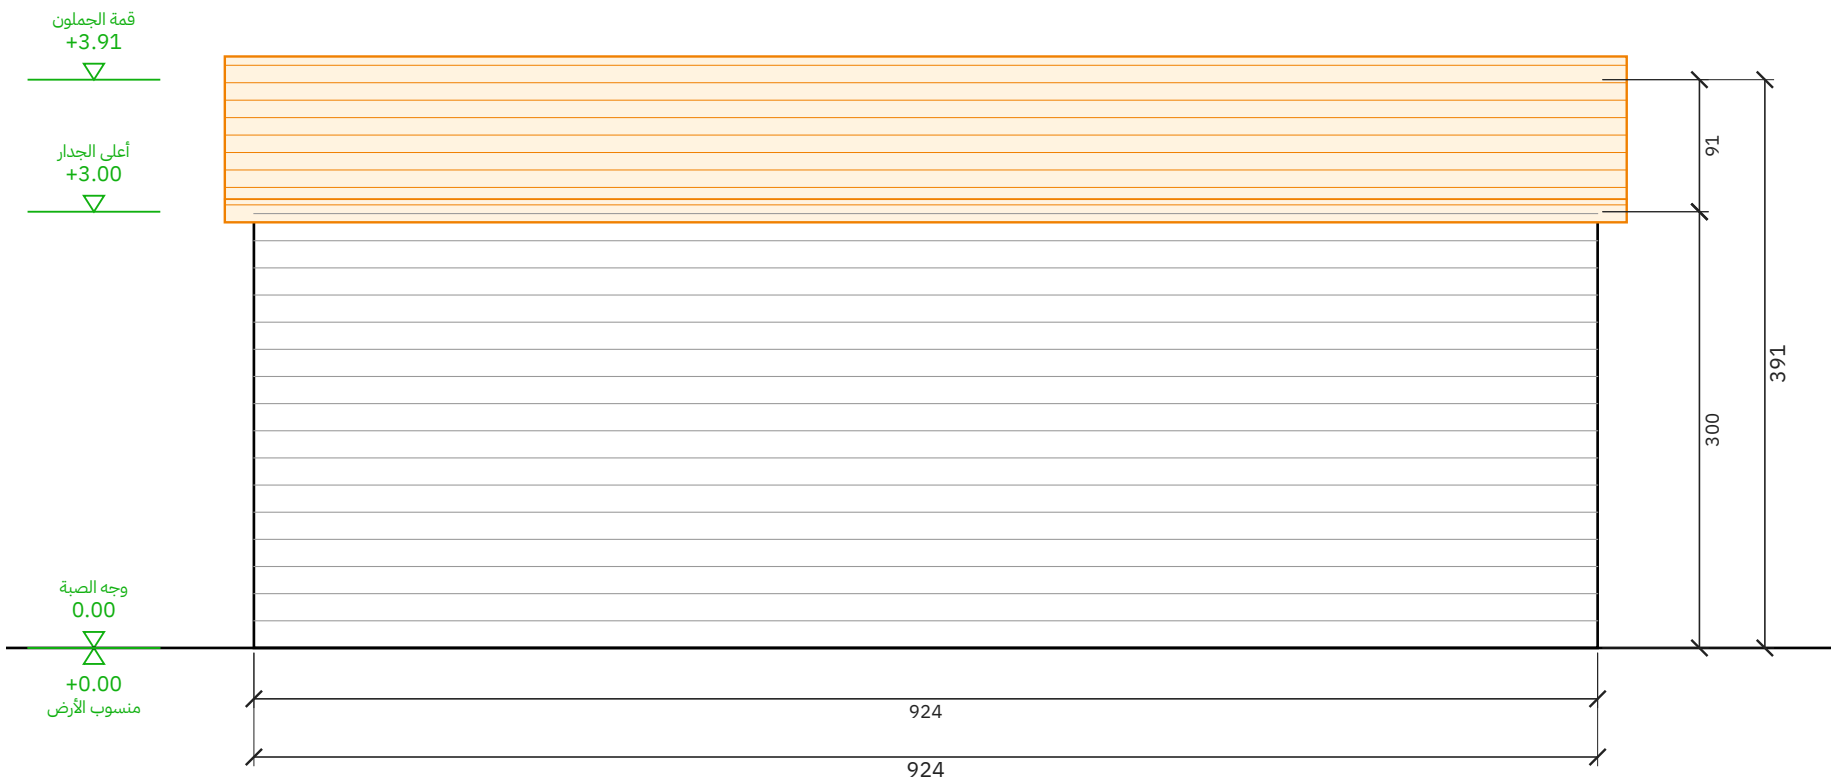

الجدار الأيسر (القائم + الرفع)


مقياس 1:50 | الوحدة: سم

المشروع / العميل	عنوان اللوحة	المقياس	التاريخ	رقم اللوحة
ملحق سطح – غرفة نوم + صالة – 4.75 × 9.00 م عميل – ملحق سطح	الجدار الخلفي (غرفة النوم) والجدار الأيسر (القائم + الرفع)	1:50	2026-10-30	A-03 (3/9)

مصنع وتد الأخشاب
Watad Wood Factory


مسقط السقف (جملون)

رفرف 20 سم من كل جهة | مقياس 1:50

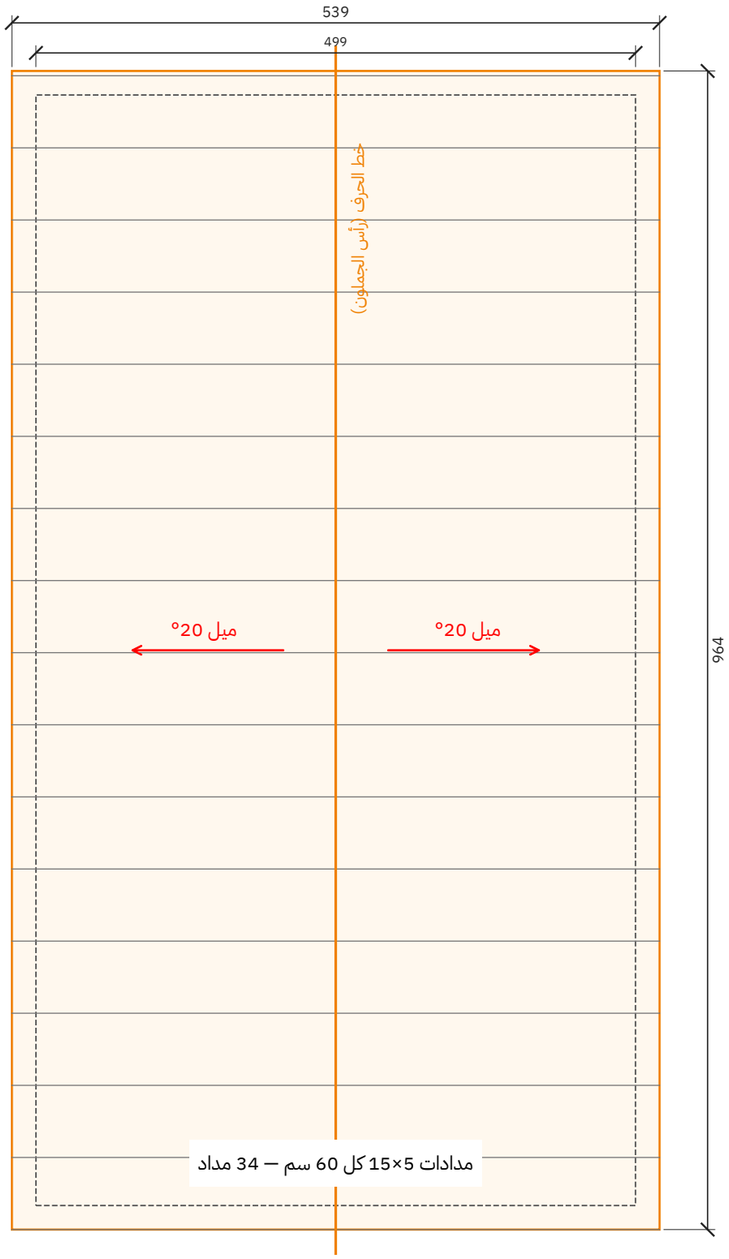


قطاع عرضي أ-أ

مقياس 1:50 | الوحدة: سم

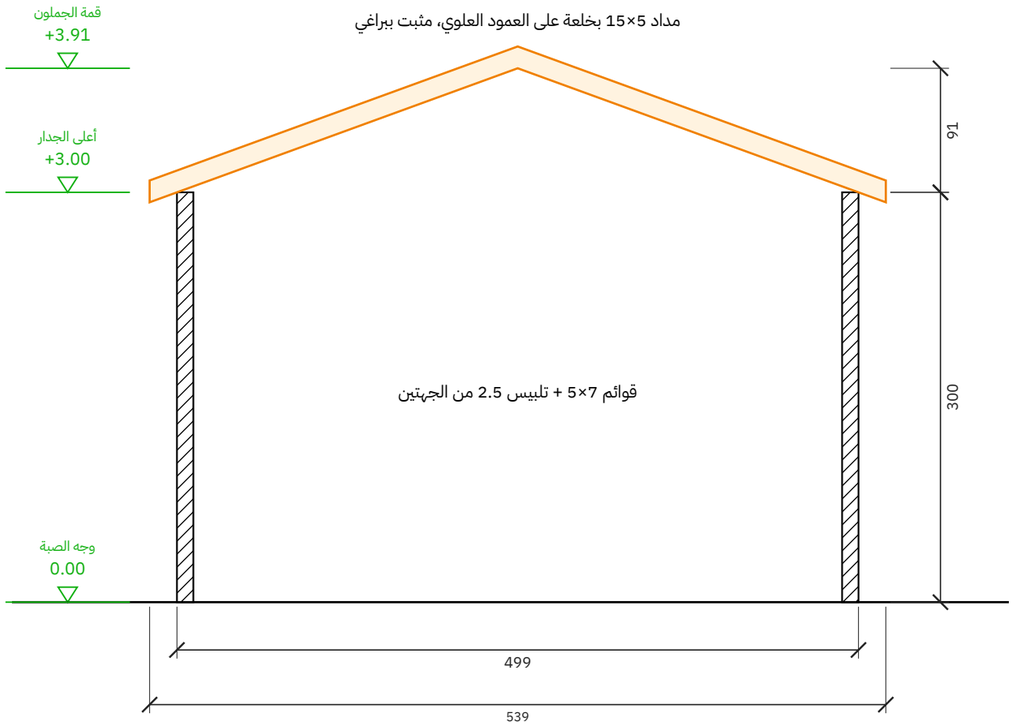

تفصيلة جلوس المداد على العلوي (1:5)

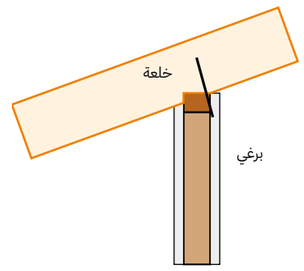

مصنع وتد الأخشاب Watad Wood Factory	المشروع / العميل ملحق سطح — غرفة نوم + صالة — 4.75 × 9.00 م عميل — ملحق سطح	عنوان اللوحة مسقط السقف والقطاع	المقياس 1:50	التاريخ 2026-10-30	رقم اللوحة A-04 (4/9)

جدول مقاسات الأبواب والشبابيك

مقاس الفتحة الصافي في الجدار - الوحدة: سم

الرمز	النوع	العرض (سم)	الارتفاع (سم)	ارتفاع الجلسة (سم)	العدد	الموقع
ب1	باب	100	220	-	1	جدار المدخل (جهة السطح)
ز1	شباك	210	210	20	1	الجدار الأيمن (القائم + الرفع)
ز2	شباك	190	210	20	1	الجدار الخلفي (غرفة النوم)
ش1	شباك	180	140	90	1	الجدار الأيمن (القائم + الرفع)

الإجمالي: أبواب 1 - شبابيك 3

جدول المساحات وبيانات المشروع

بيانات المشروع

البند	البيان
المشروع	ملحق سطح — غرفة نوم + صالة — 4.75 × 9.00 م
العميل	عميل — ملحق سطح
الموقع	—
الاستخدام	ملحق سكني على السطح
التاريخ	2026-10-30
نظام البناء	هيكل خشب 5×7 + تلبيس 2.5 سم من الجهتين
السقف	جملون 20° — قرميد معدني

جدول المساحات


م	الفراغ	الأبعاد (م)	المساحة (م2)
1	الصالة	4.75 × 4.06	19.29
2	غرفة النوم	4.75 × 4.94	23.46
	المساحة الصافية الداخلية		**42.75**
	المساحة الإجمالية المبنية	**4.99 × 9.24**	**46.11**

لقطات المنظور الخارجي


المنظور الأمامي



منظور أمامي من اليسار

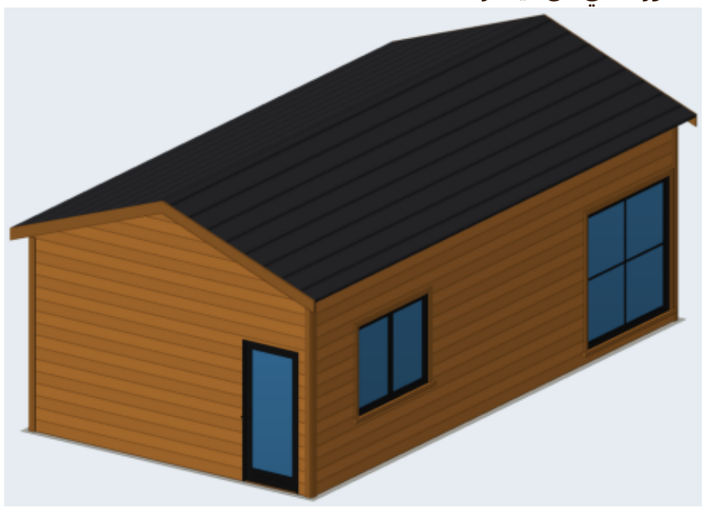


منظور أمامي من اليمين

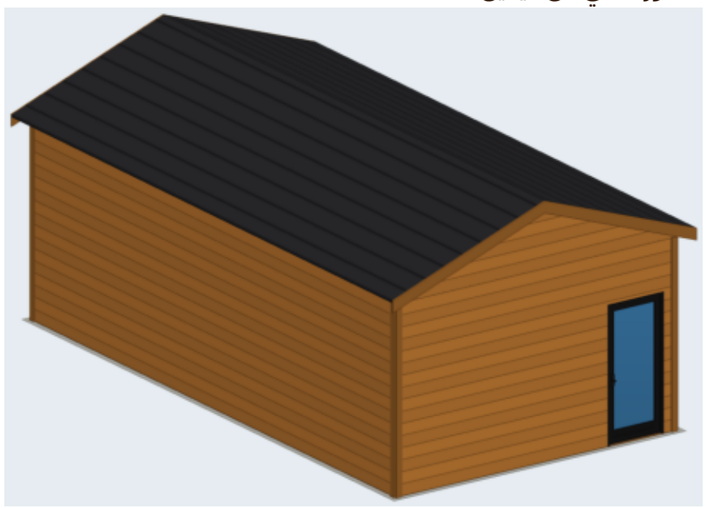

المنظور الخلفي



منظور خلفي من اليمين

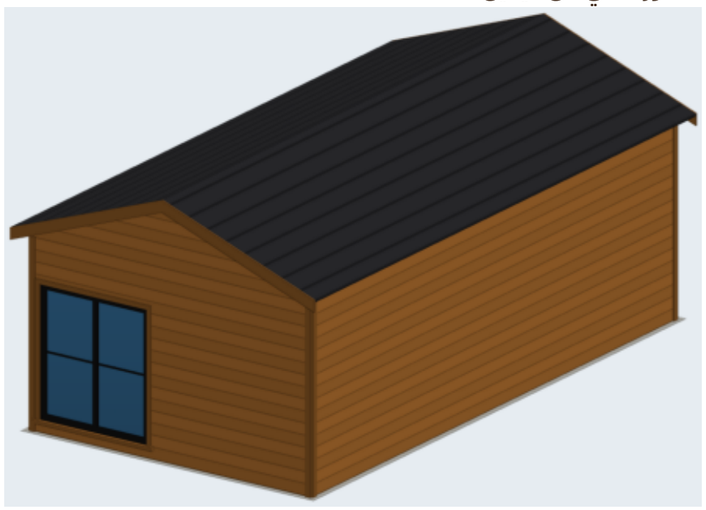

منظر علوي




المشروع / العميل ملحق سطح – غرفة نوم + صالة – 4.75 × 9.00 م عميل – ملحق سطح	عنوان اللوحة لقطات المنظور	المقياس –	التاريخ 2026-10-30	رقم اللوحة A-07 (7/9)

مصنع وتد الأخشاب
Watad Wood Factory

المقطع العلوي بالفرش

مقطع أفقي على ارتفاع 1.90 م — توزيع الفرش ومسار الحركة

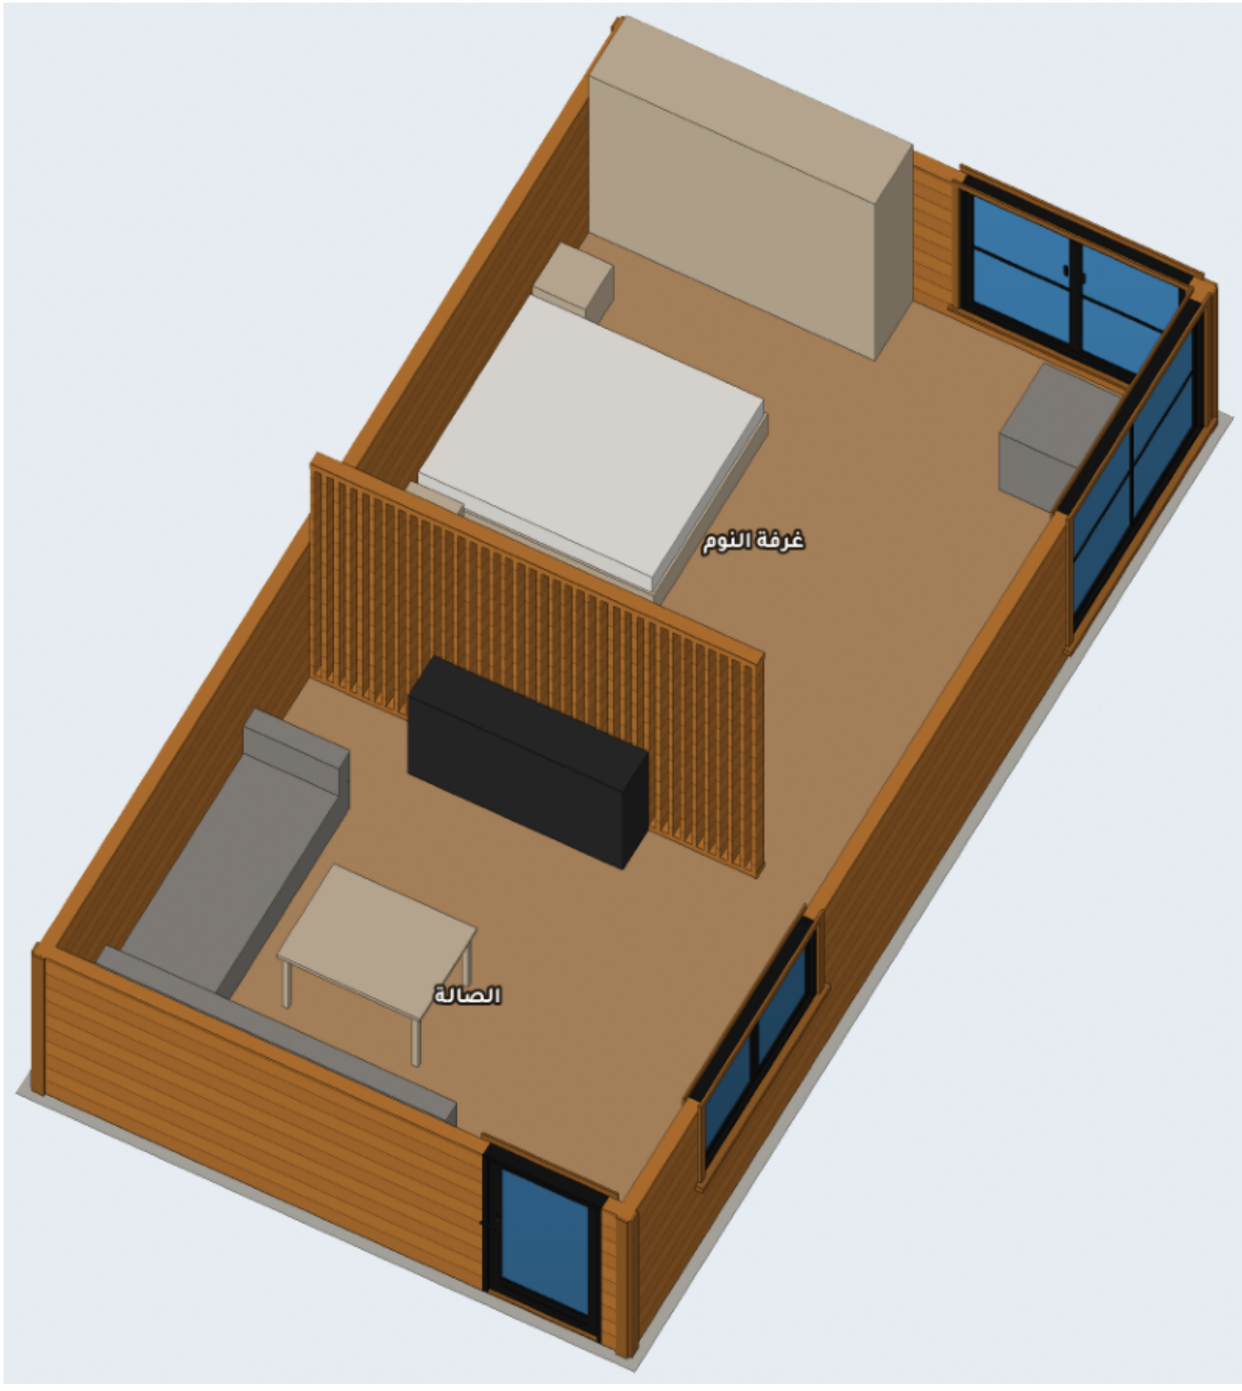

المشروع / العميل	عنوان اللوحة	المقياس	التاريخ	رقم اللوحة
مصنع وتد الأخشاب — Watad Wood Factory ملحق سطح — غرفة نوم + صالة — 4.75 × 9.00 م عميل — ملحق سطح	المقطع العلوي بالفرش	—	2026-10-30	A-08 (8/9)

المنظور ثلاثي الأبعاد والمواد

النمط: جوزي غامق + إطارات سوداء — رندر واقعي بخامات حقيقية



جدول المواد والألوان

الخشب / الصبغة

صبغة عسلي / سيدر

القرميد

قرميد رمادي غامق

الزجاج

زجاج أزرق (بلو) عاكس

إطارات الشبابيك والأبواب

إطار ألمنيوم أسود

الكنار والزوايا

نفس الصبغة أغمق درجة


الصبة

خرسانة 0 سم


الدربزين: ألواح أفقية متقاربة (عصري)

تقسيم الشبابيك: شبكة | الباب الرئيسي: زجاج بتقسيمات (فرنسي)

أنواع الدربزين المعتمدة (من مشاريع المصنع)

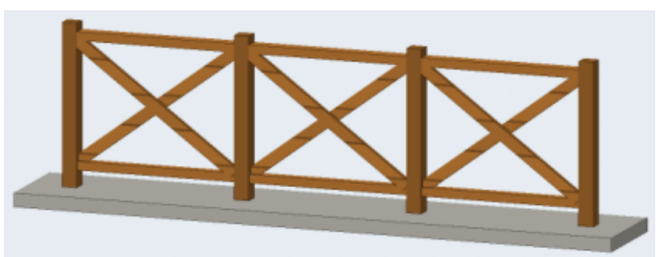

تقاطع X (صورة 5)

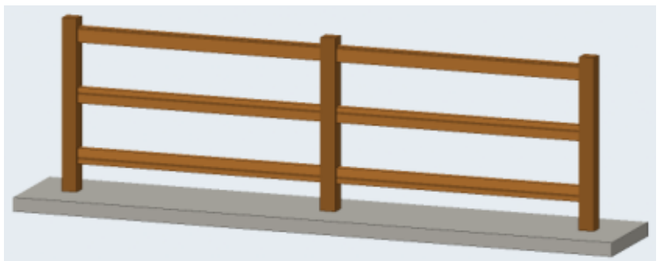

3 مرابيع أفقية (صورة 2)



قوائم رأسية متقاربة (صورة 1)

المشروع / العميل	عنوان اللوحة	المقياس	التاريخ	رقم اللوحة
مصنع وتد الأخشاب Watad Wood Factory **ملحق سطح — غرفة نوم + صالة — 4.75 × 9.00 م** **عميل — ملحق سطح**	**المنظور والمواد**	—	**2026-10-30**	**A-09 (9/9)**