المنظور ثلاثي الأبعاد والمواد

النمط: جوزي غامق + إطارات سوداء — رندر واقعي بخامات حقيقية



جدول المواد والألوان

الخشب / الصبغة

خشب طبيعي فاتح (بدون صبغة)

القرميد

قرميد رمادي غامق

الزجاج

زجاج عاكس غامق

إطارات الشبابيك والأبواب

إطار خشب بنفس الصبغة أغمق

الكنار والزوايا

نفس الصبغة أغمق درجة


الصبة

خرسانة 45 سم


الدربزين: ألواح أفقية متقاربة (عصري)

تقسيم الشبابيك: بدون | الباب الرئيسي: زجاج بتقسيمات (فرنسي)

أنواع الدربزين المعتمدة (من مشاريع المصنع)

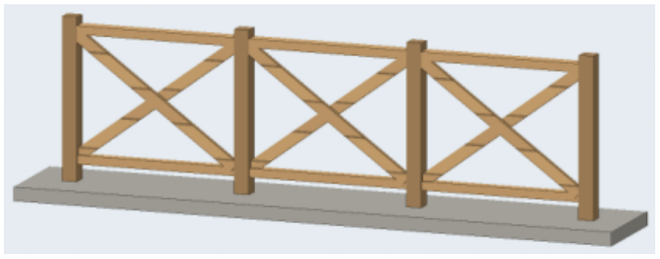

تقاطع X (صورة 5)

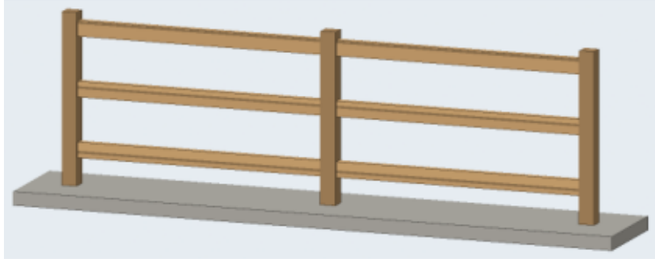

3 مرابيع أفقية (صورة 2)




قوائم رأسية متقاربة (صورة 1)

المشروع / العميل	عنوان اللوحة	المقياس	التاريخ	رقم اللوحة
مصنع وتد الأخشاب Watad Wood Factory **فيلا خشب دورين — مجلس + غرفتين — 7.00 × 9.00 م (63 م² للدور)** **عميل — تبوك**	**المنظور والمواد**	**1:50**	**2026-10-23**	**W-01 (1/20)**

المسقط الأفقي مع الفرش — الدور الأرضي

الأبعاد بالسنتيمتر - الجدران: قوائم 7×5 + تلبيس 2.5 من الجهتين (12 سم) | منسوب الأرضية +0.00

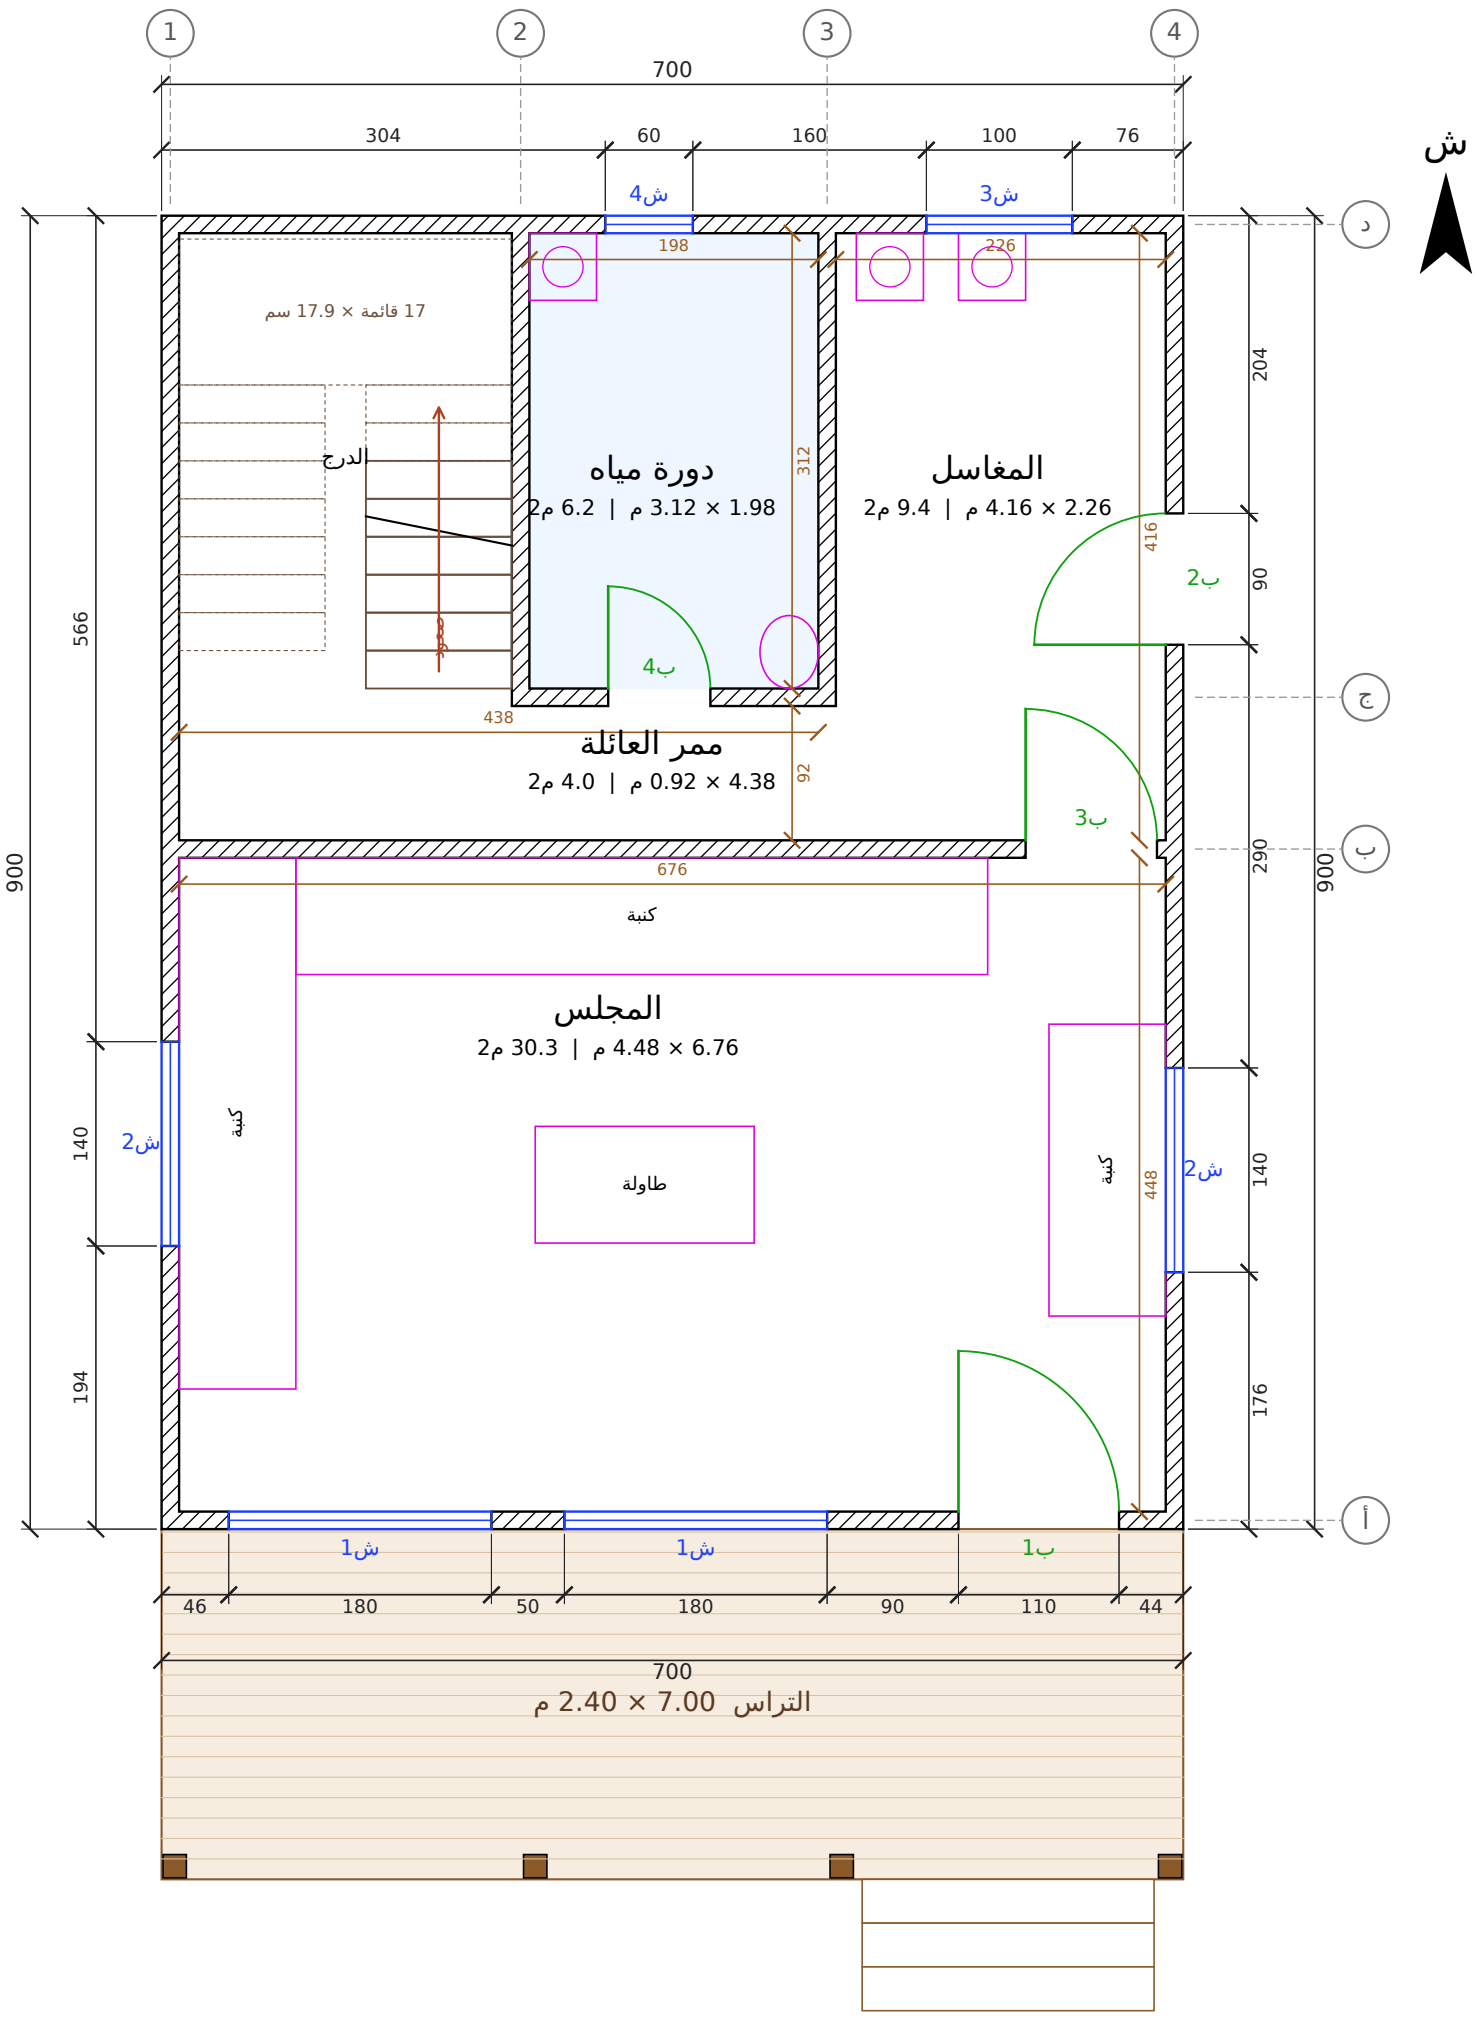


المشروع / العميل	عنوان اللوحة	المقياس	التاريخ	رقم اللوحة
فيلا خشب دورين — مجلس + غرفتين — 7.00 × 9.00 م (63 م² للدور) **عميل — تبوك**	**المسقط الأفقي — الدور الأرضي**	**1:50**	**2026-10-23**	**W-02 (2/20)**

مصنع وتد الأخشاب
Watad Wood Factory


المسقط الأفقي مع الفرش — الدور الأول

الأبعاد بالسنتيمتر - الجدران: قوائم 7×5 + تلبيس 2.5 من الجهتين (12 سم) | منسوب الأرضية +3.05

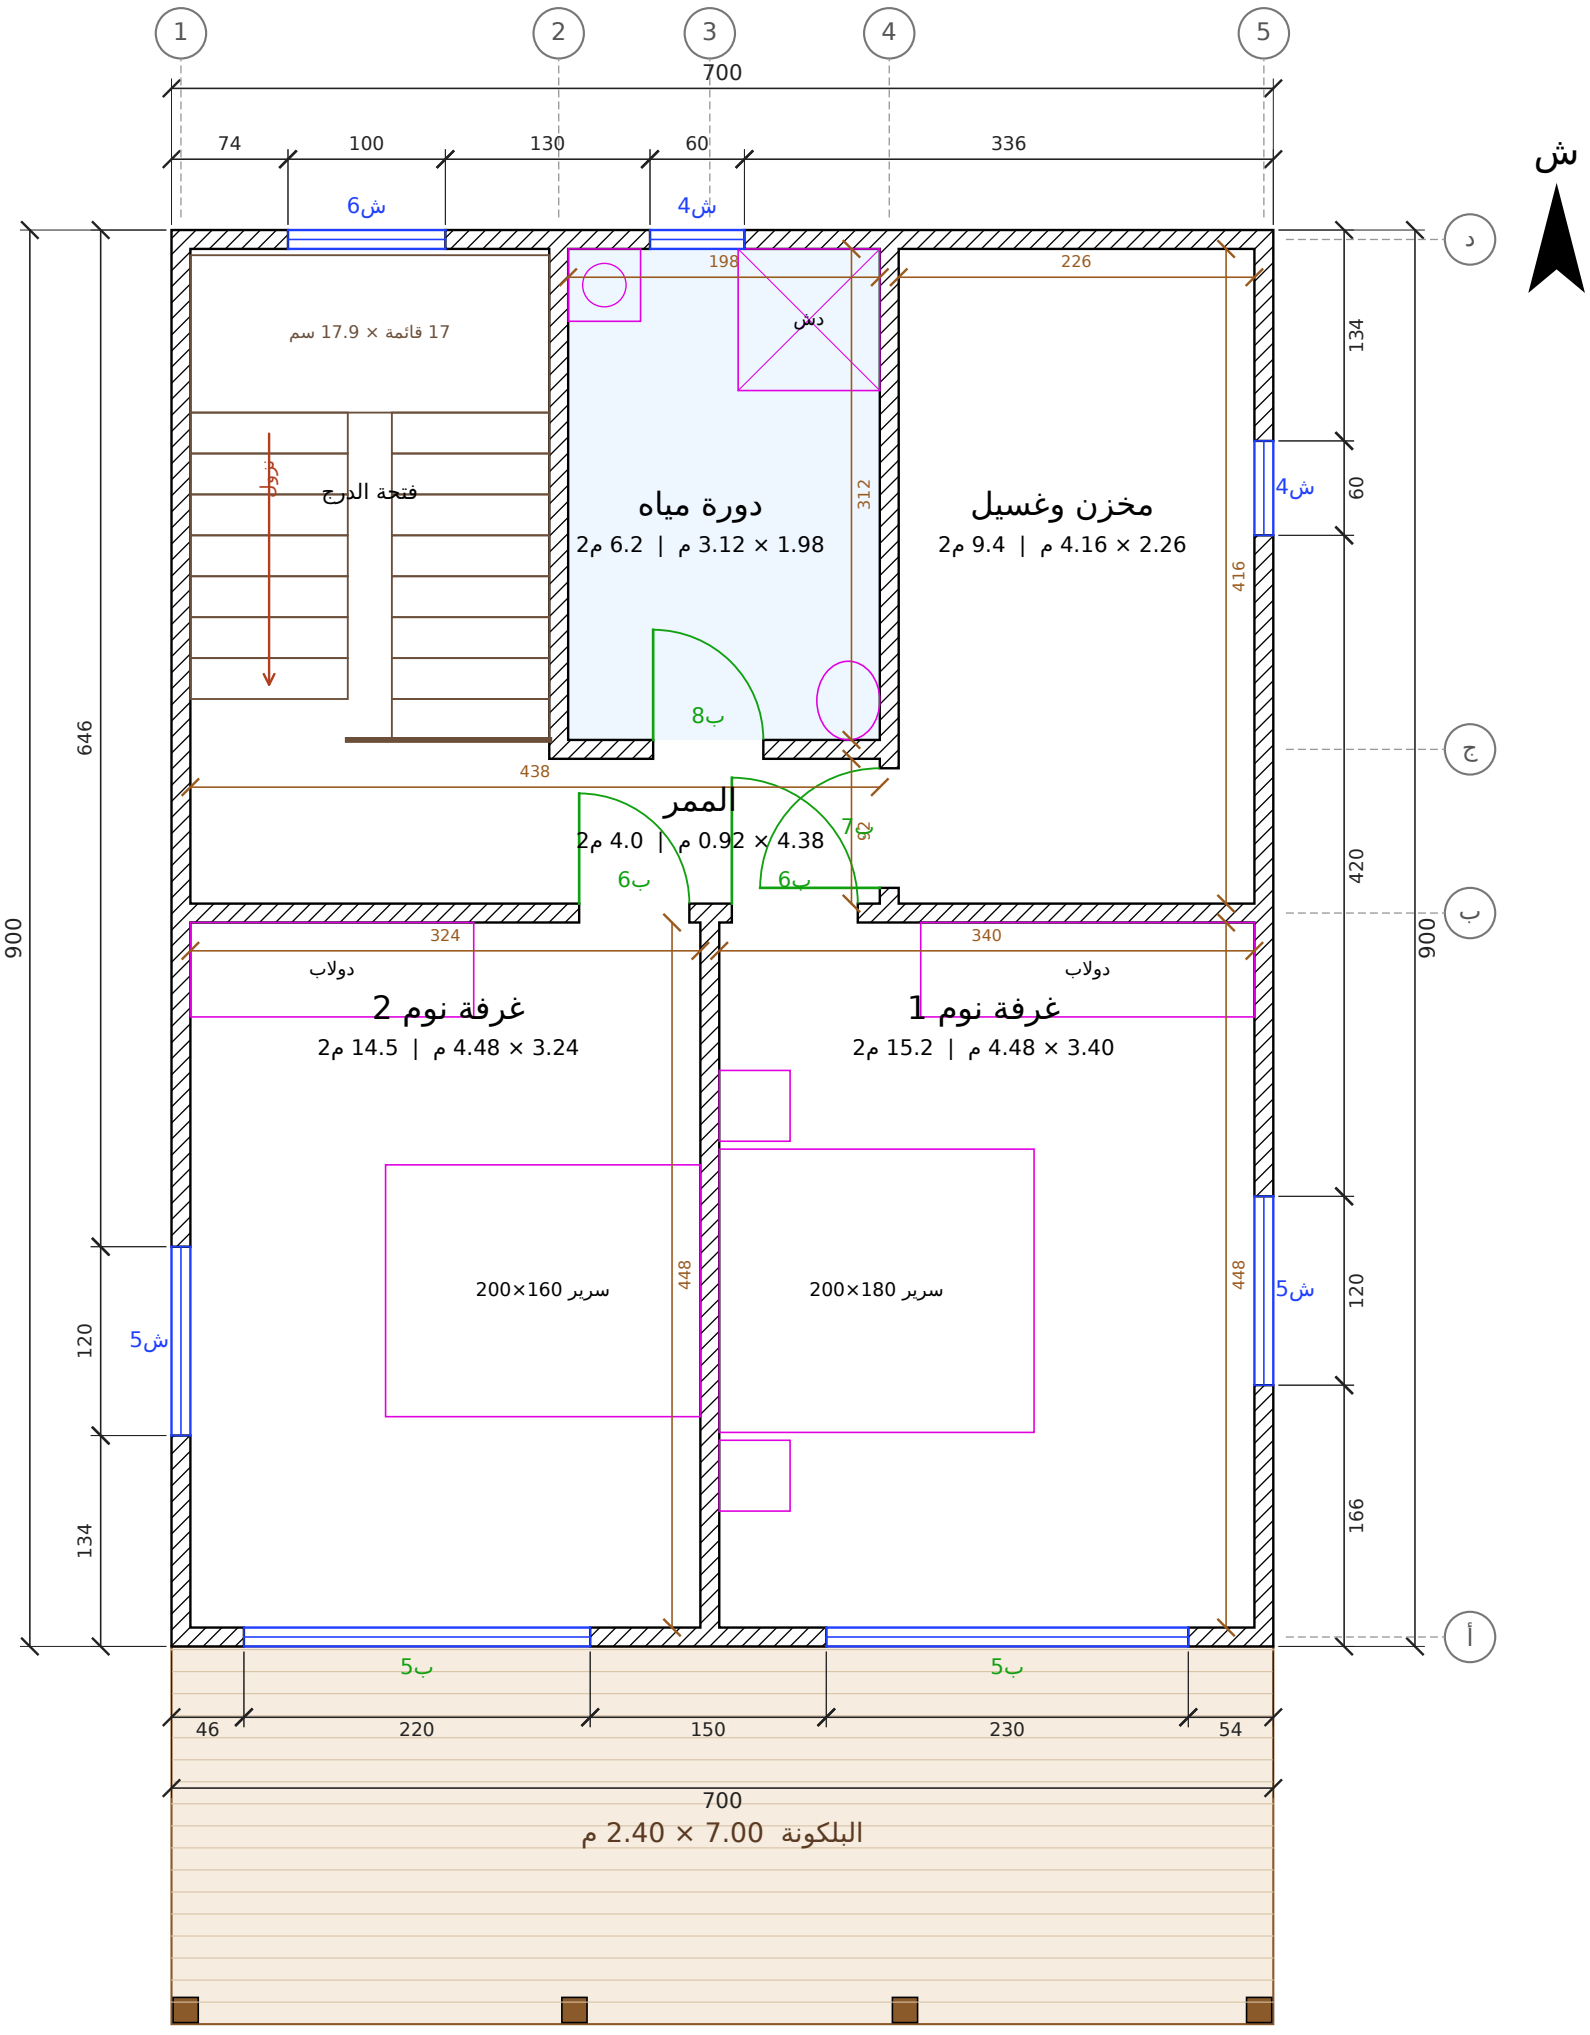


المشروع / العميل	عنوان اللوحة	المقياس	التاريخ	رقم اللوحة
فيلا خشب دورين — مجلس + غرفتين — 7.00 × 9.00 م (63 م² للدور) **عميل — تبوك**	**المسقط الأفقي — الدور الأول**	**1:50**	**2026-10-23**	**W-03 (3/20)**

مصنع وتد الأخشاب
Watad Wood Factory

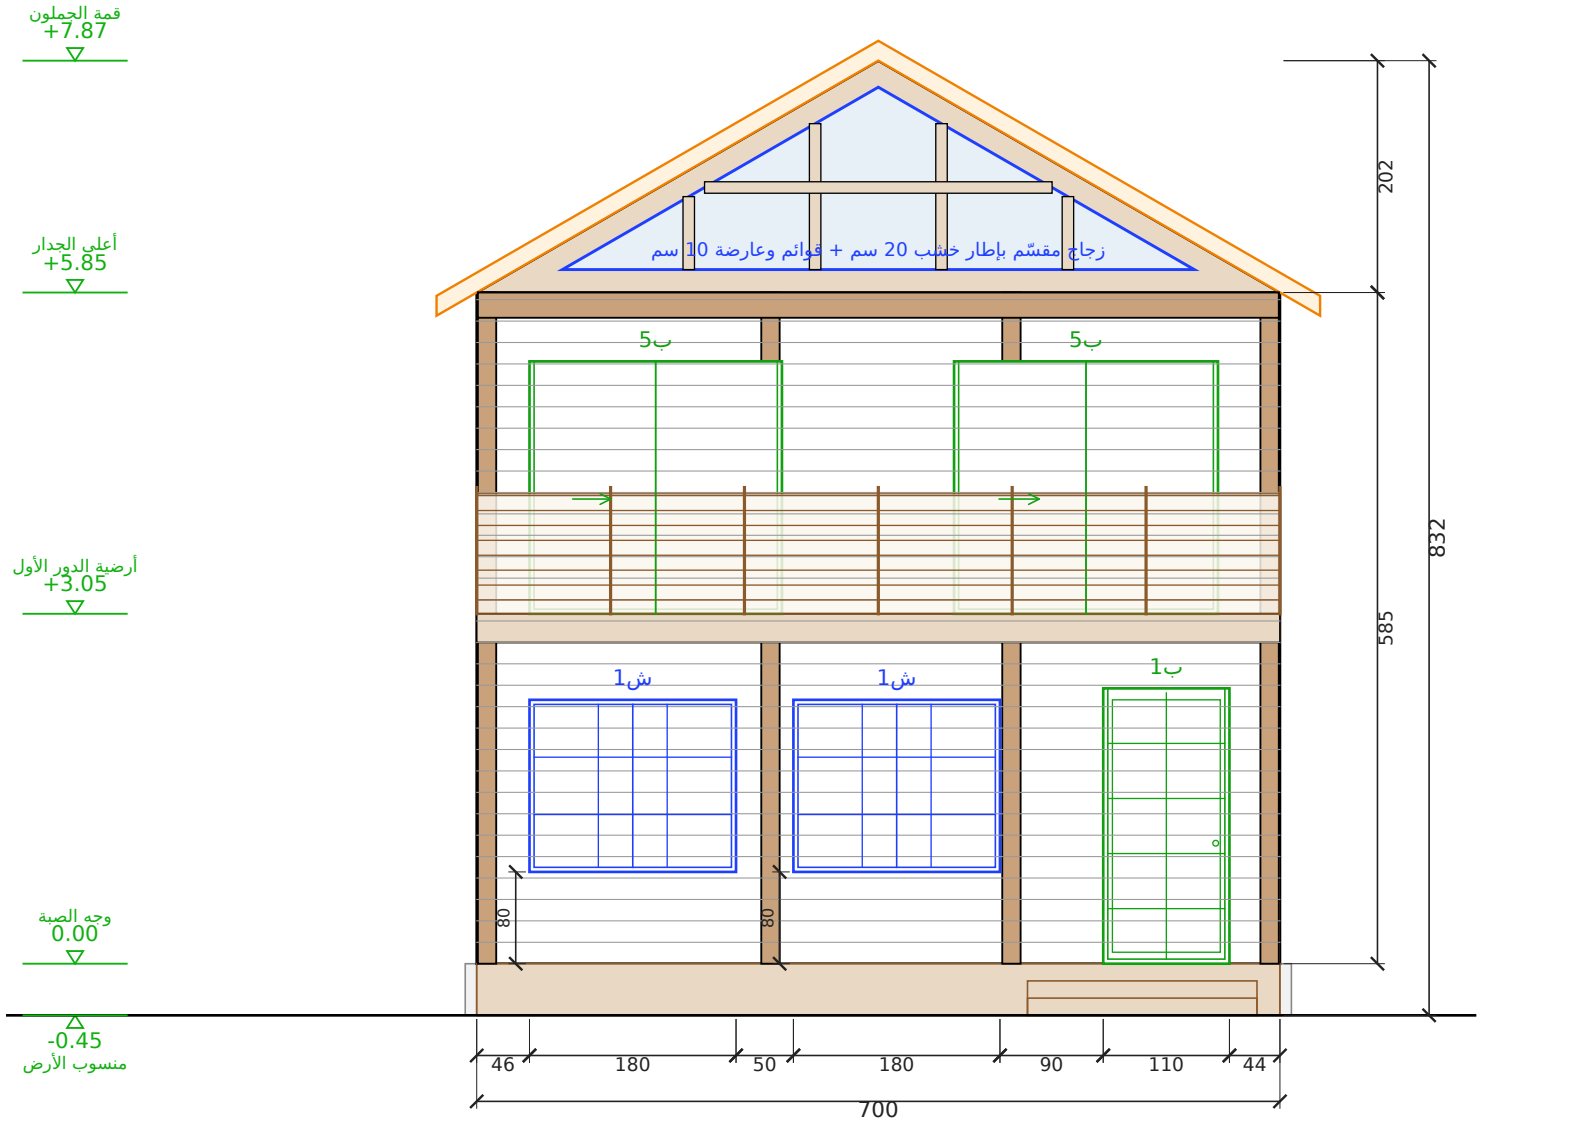

الواجهة الأمامية


مقياس 1:50 | الوحدة: سم

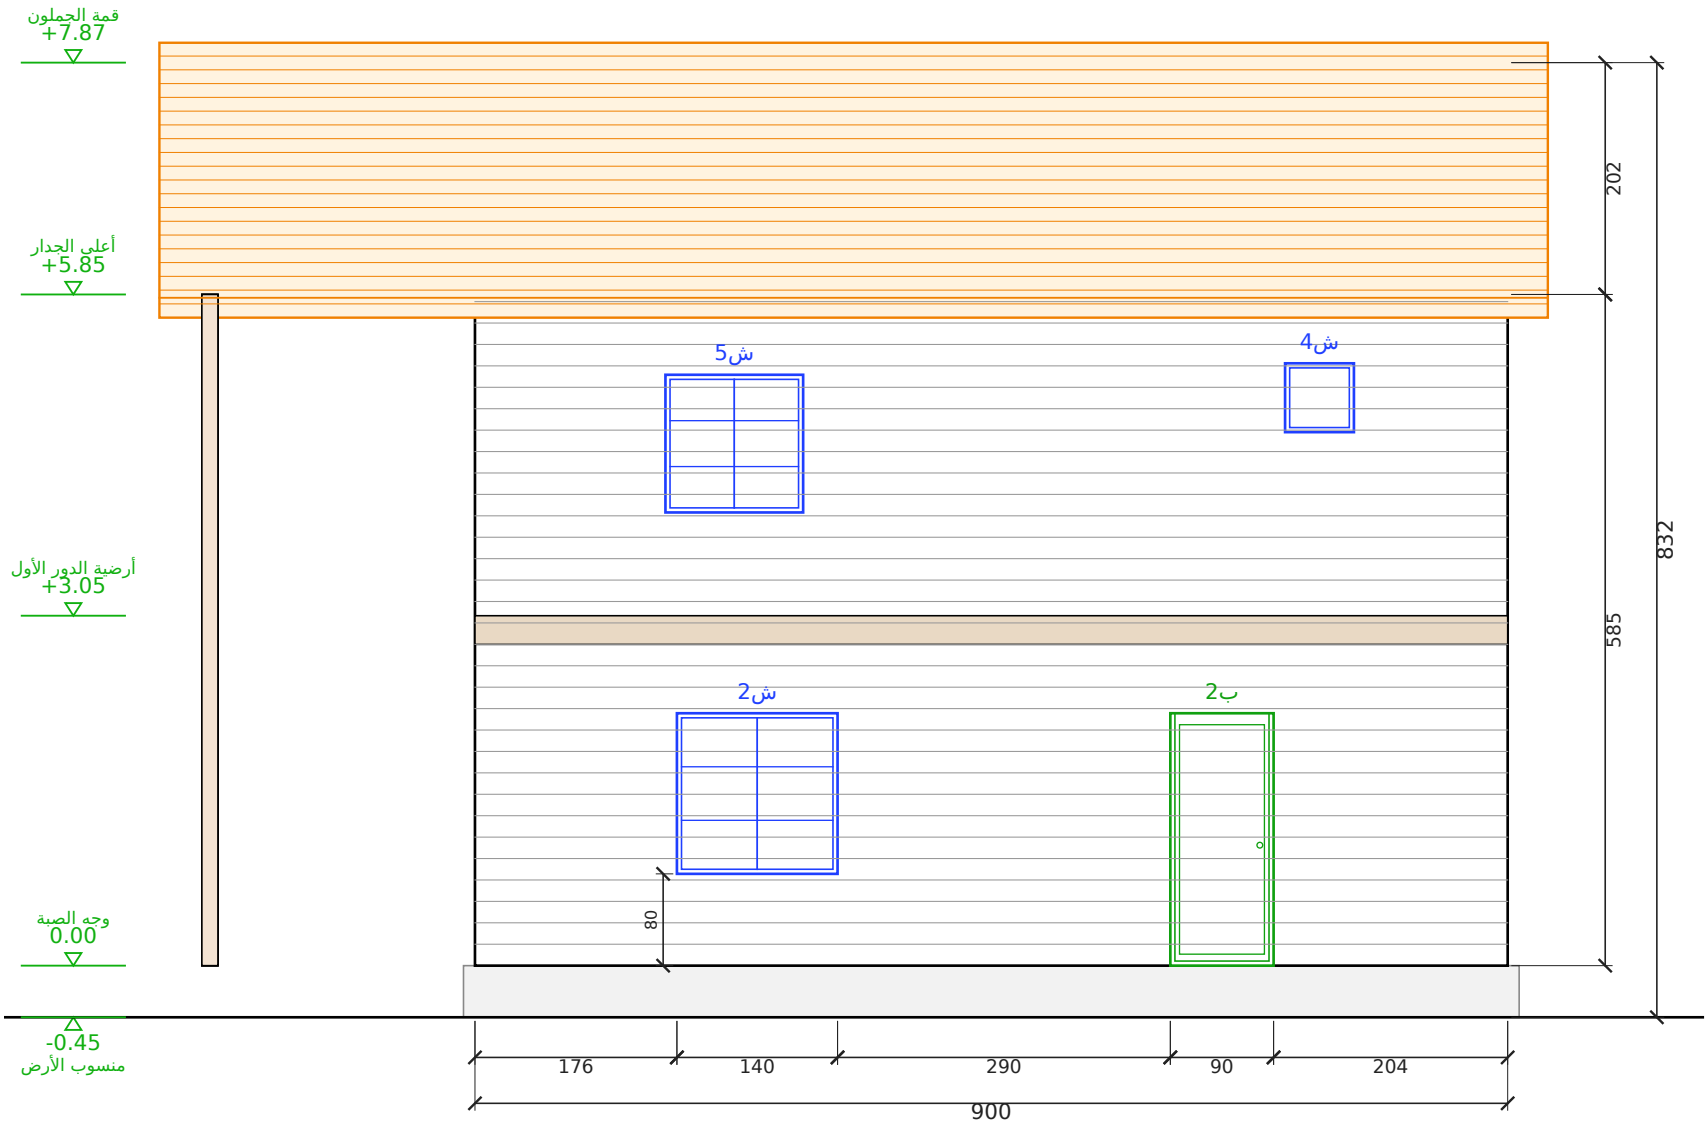

الواجهة الشرقية


مقياس 1:50 | الوحدة: سم

مصنع وتد الأخشاب Watad Wood Factory	المشروع / العميل فيلا خشب دورين — مجلس + غرفتين — 7.00 × 9.00 م (63 م² للدور) عميل — تبوك	عنوان اللوحة الواجهة الأمامية والواجهة الشرقية	المقياس 1:50	التاريخ 2026-10-23	رقم اللوحة W-04 (4/20)

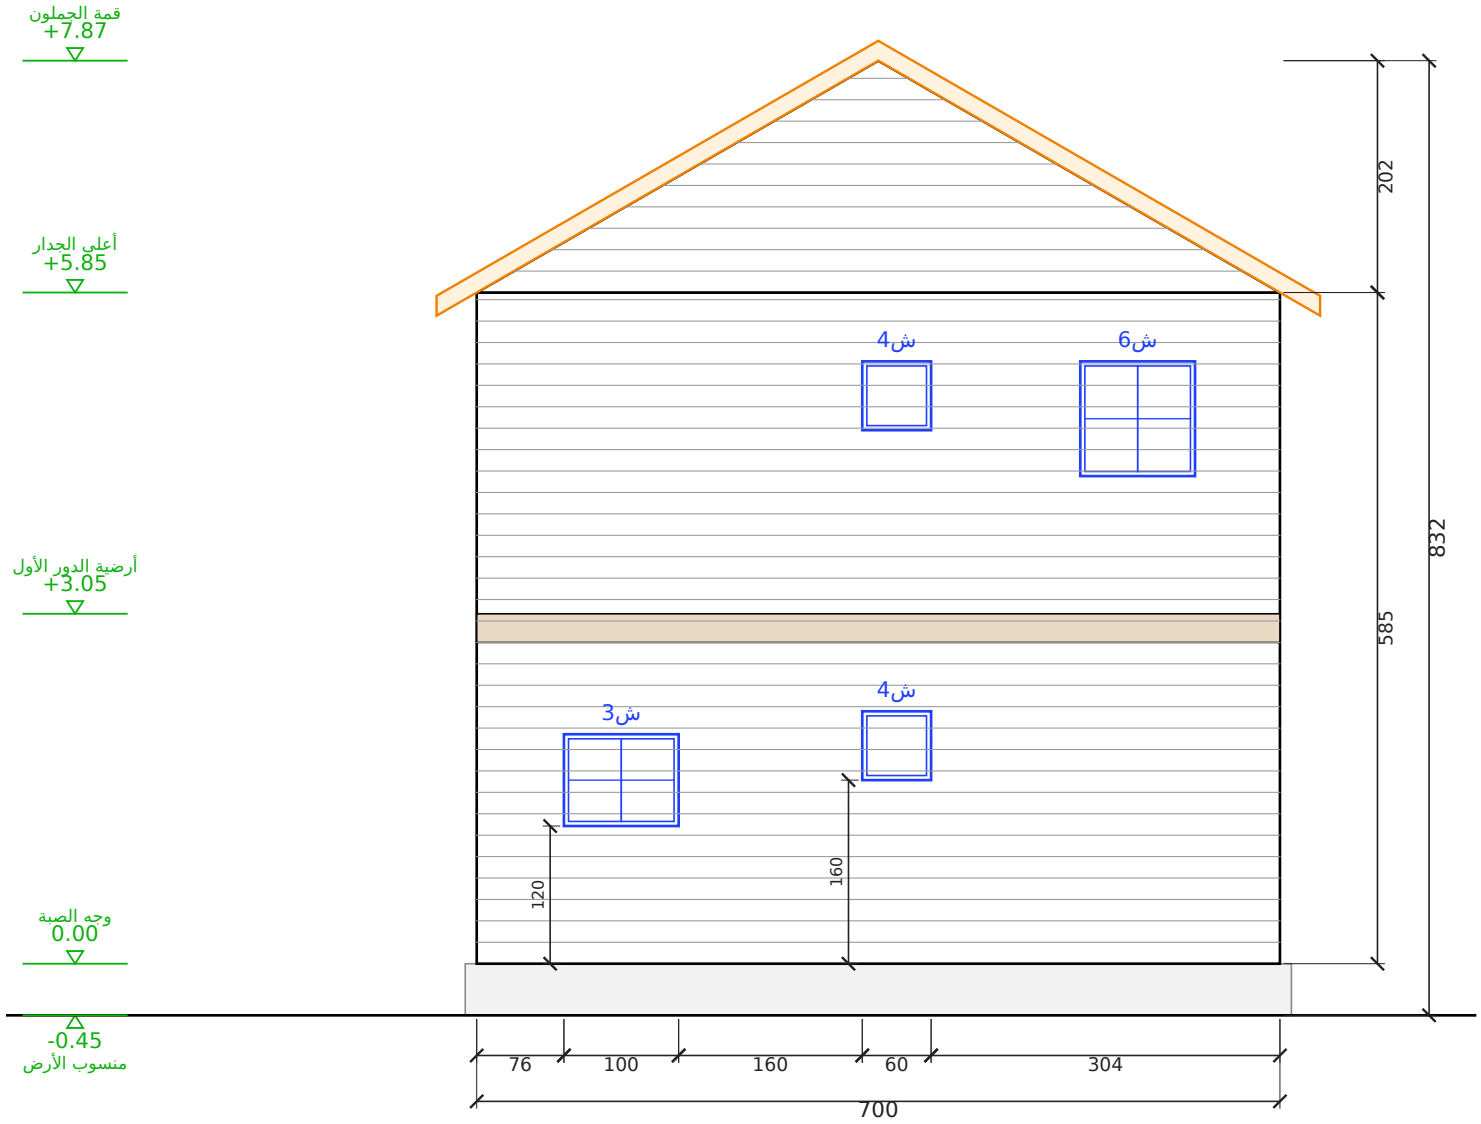

الواجهة الخلفية

مقياس 1:50 | الوحدة: سم

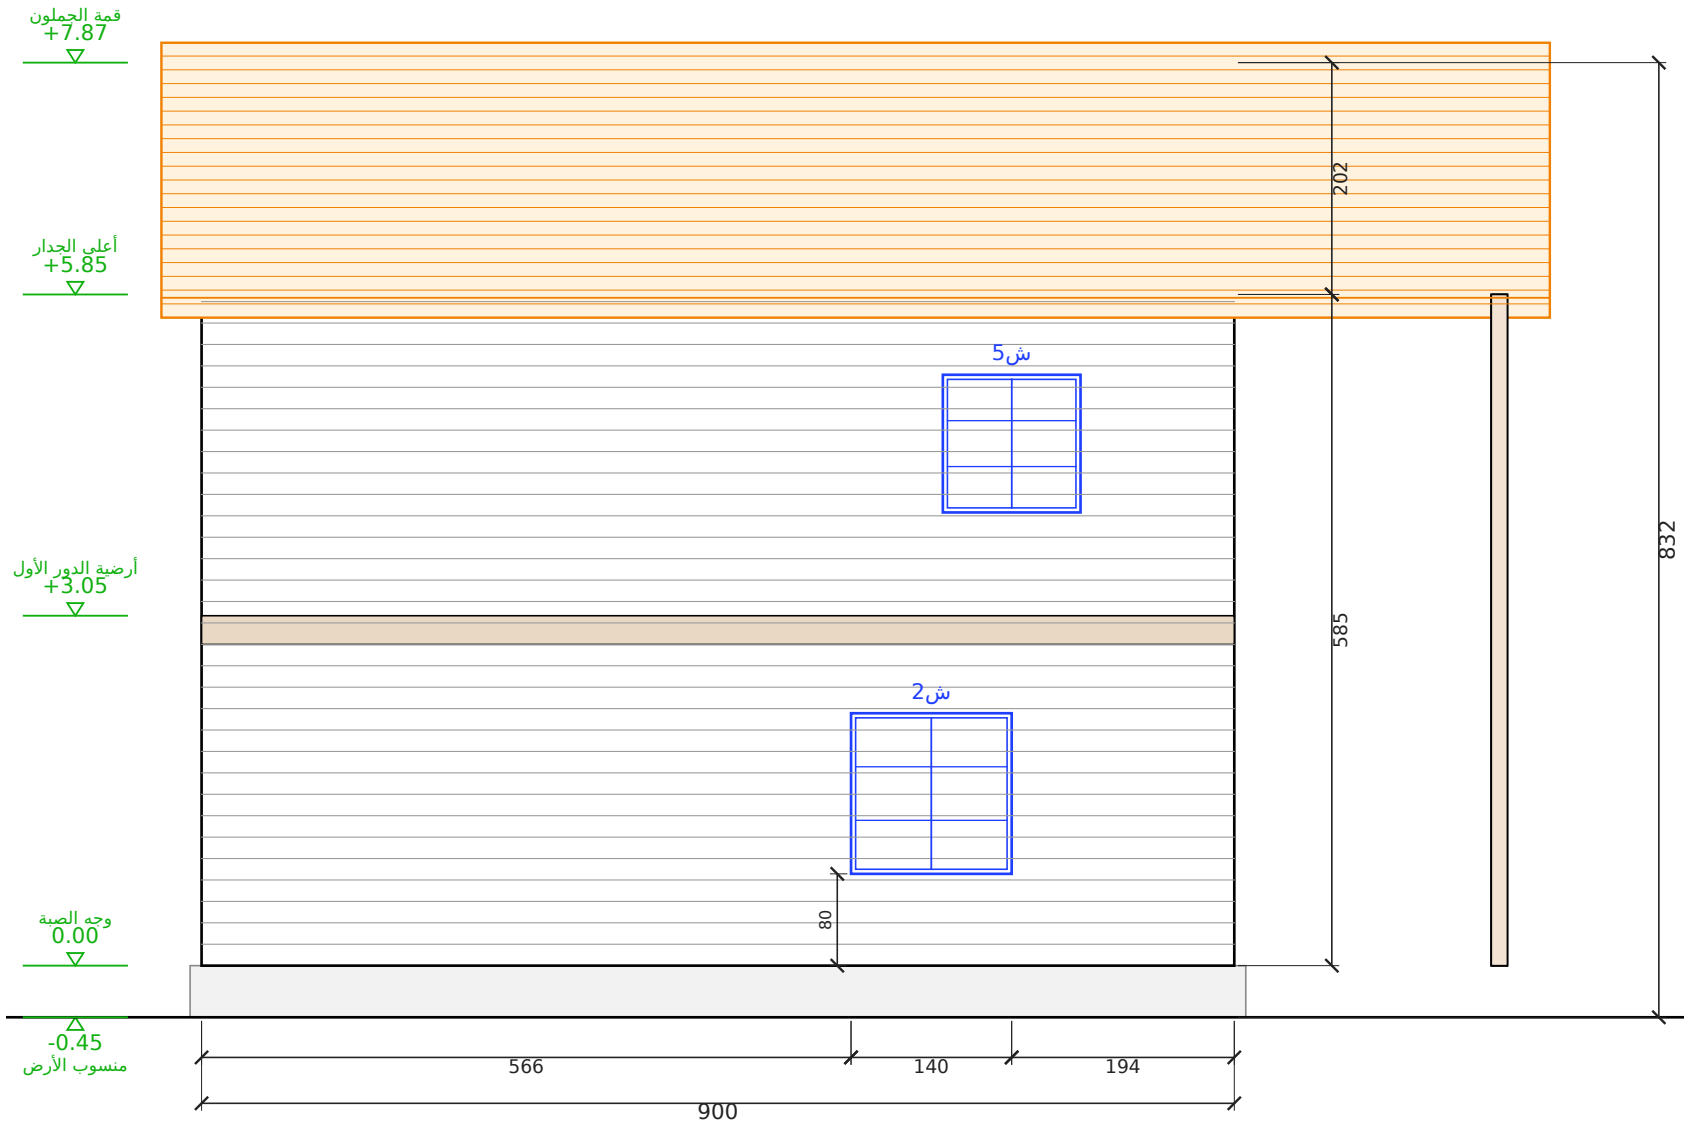


الواجهة الغربية


مقياس 1:50 | الوحدة: سم

المشروع / العميل	عنوان اللوحة	المقياس	التاريخ	رقم اللوحة
مصنع وتد الأخشاب Watad Wood Factory **فيلا خشب دورين — مجلس + غرفتين — 7.00 × 9.00 م (63 م² للدور)** **عميل — تبوك**	**الواجهة الخلفية والواجهة الغربية**	**1:50**	**2026-10-23**	**W-05 (5/20)**


مسقط السقف (جملون)
رفرف 35 سم من كل جهة | مقياس 1:50

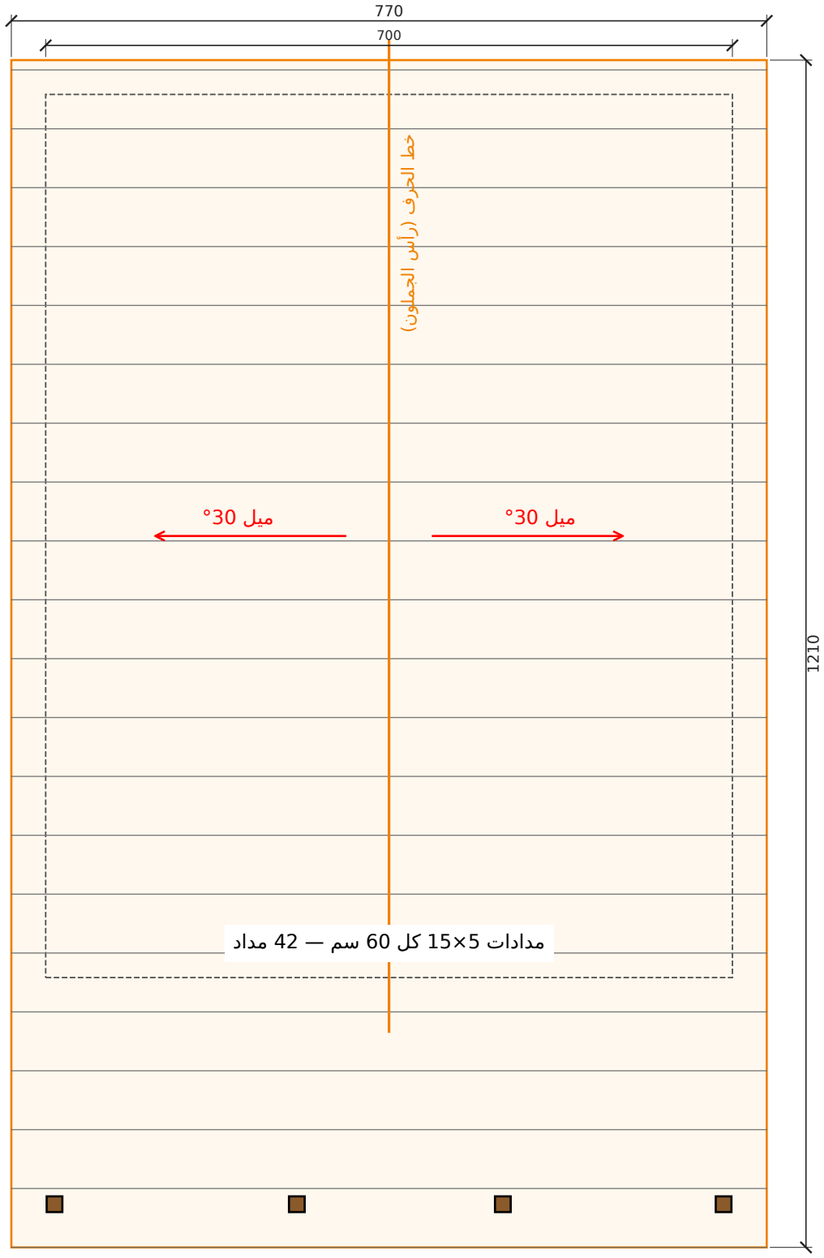

قطاع عرضي أ-أ
مقياس 1:50 | الوحدة: سم

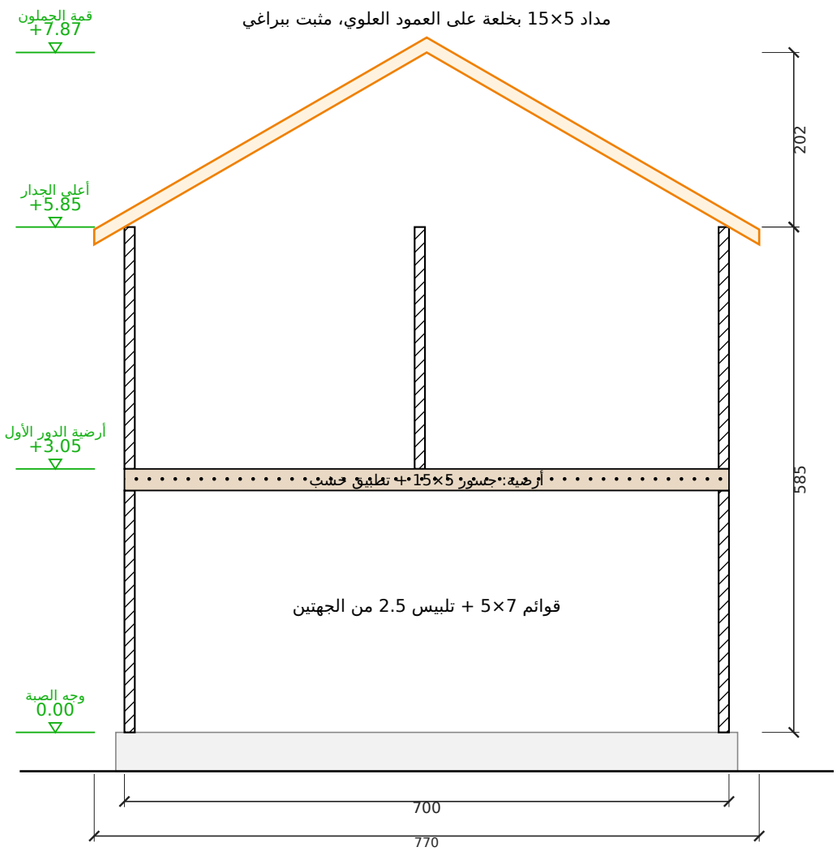

تفصيلة جلوس المداد على العلوي (1:5)

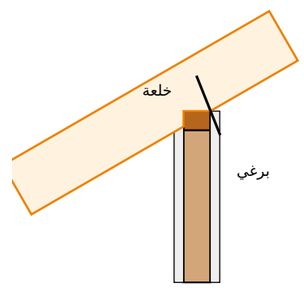

علوي 7×5 على قائم 7×5

المشروع / العميل	عنوان اللوحة	المقياس	التاريخ	رقم اللوحة
فيلا خشب دورين — مجلس + غرفتين — 7.00 × 9.00 م (63 م² للدور) **عميل — تبوك**	**مسقط السقف والقطاع**	**—**	**2026-10-23**	**W-06 (6/20)**

مصنع وتد الأخشاب
Watad Wood Factory

جدول مقاسات الأبواب والشبابيك
مقاس الفتحة الصافي في الجدار - الوحدة: سم

الرمز	النوع	العرض (سم)	الارتفاع (سم)	ارتفاع الجلسة (سم)	العدد	الموقع
ب1	باب	110	240	-	1	الأمامية
ب2	باب	90	220	-	1	الشرقية
ب3	باب	90	220	-	1	المجلس — المغاسل
ب4	باب	70	210	-	1	دورة المياه
ب5	باب مزدوج	220	220	-	1	الأمامية (على البلكونة)
ب5	باب مزدوج	230	220	-	1	الأمامية (على البلكونة)
ب6	باب	70	210	-	1	غرفة 2
ب6	باب	80	210	-	1	غرفة 1
ب7	باب	76	210	-	1	المخزن والغسيل
ب8	باب	70	210	-	1	دورة المياه
ش1	شباك	180	150	80	2	الأمامية 2
ش2	شباك	140	140	80	2	الشرقية - الغربية
ش3	شباك	100	80	120	1	الخلفية
ش4	شباك	60	60	160	3	الخلفية 2 - الشرقية
ش5	شباك	120	120	90	2	الشرقية - الغربية
ش6	شباك	100	100	120	1	الخلفية

الإجمالي: أبواب 10 - شبابيك 11

جدول المساحات وبيانات المشروع والتسعير

بيانات المشروع

البند	البيان
المشروع	فيلا خشب دورين — مجلس + غرفتين — 7.00 × 9.00 م (63 م² للدور)
العميل	عميل — تبوك
الموقع	تبوك
الاستخدام	سكن — مجلس ضيوف + غرفتين
التاريخ	2026-10-23
نظام البناء	هيكل خشب 7×5 + تلبيس 2.5 سم من الجهتين
السقف	جملون 30° — قرميد معدني

جدول المساحات

م	الفراغ	الأبعاد (م)	المساحة (م2)
1	أرضي — المجلس	6.76 × 4.48	30.28
2	أرضي — ممر العائلة	4.38 × 0.92	4.03
3	أرضي — الدرج	2.28 × 3.00	6.84
4	أرضي — دورة مياه	1.98 × 3.12	6.18
5	أرضي — المغاسل	2.26 × 4.16	9.40
6	أول — غرفة نوم 2	3.24 × 4.48	14.52
7	أول — غرفة نوم 1	3.40 × 4.48	15.23
8	أول — الممر	4.38 × 0.92	4.03
9	أول — دورة مياه	1.98 × 3.12	6.18
10	أول — مخزن وغسيل	2.26 × 4.16	9.40
	المساحة الصافية الداخلية		106.09
	التراس	**7.00 × 2.40**	**16.80**
	البلكونة	**7.00 × 2.40**	**16.80**
	المساحة الإجمالية المبنية	**7.00 × 9.00 × 2 دور**	**126.00**
	المساحة الكلية (المبنية + التراس والبلكونة)		**159.60**


التسعير المفصّل

البند	المبلغ (ريال)
الكوخ المبني 126.00 م² × 1,096	138,096
تراس الأرضي + بلكونة الأول (7.00 × 2.40 × 2) — 33.60 م² × 1,096	36,826
الإجمالي (ريال)	**174,922**


ملاحظات:

- السعر للدورين والتراس والبلكونة حسب المخطط المعتمد — التراس يُسعّر بنفس سعر متر الكوخ.
- الصبة والتمديدات الخارجية على العميل ما لم يُذكر غير ذلك.

تأطير جدار أ-جنوب — الطول 688 سم، الارتفاع 280 سم

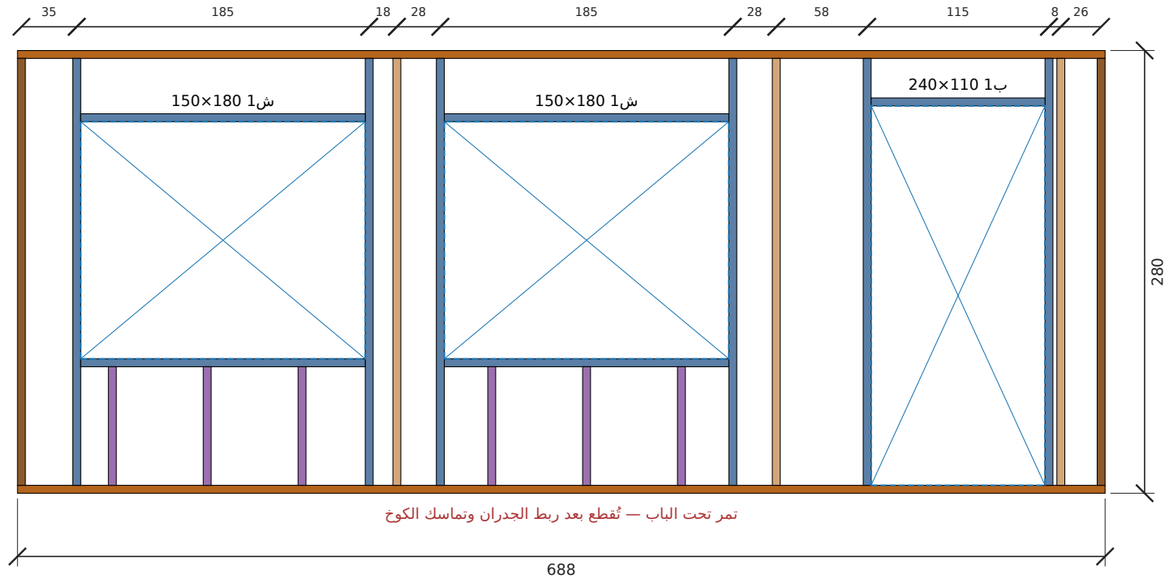


تأطير جدار أ-شرق — الطول 888 سم، الارتفاع 280 سم

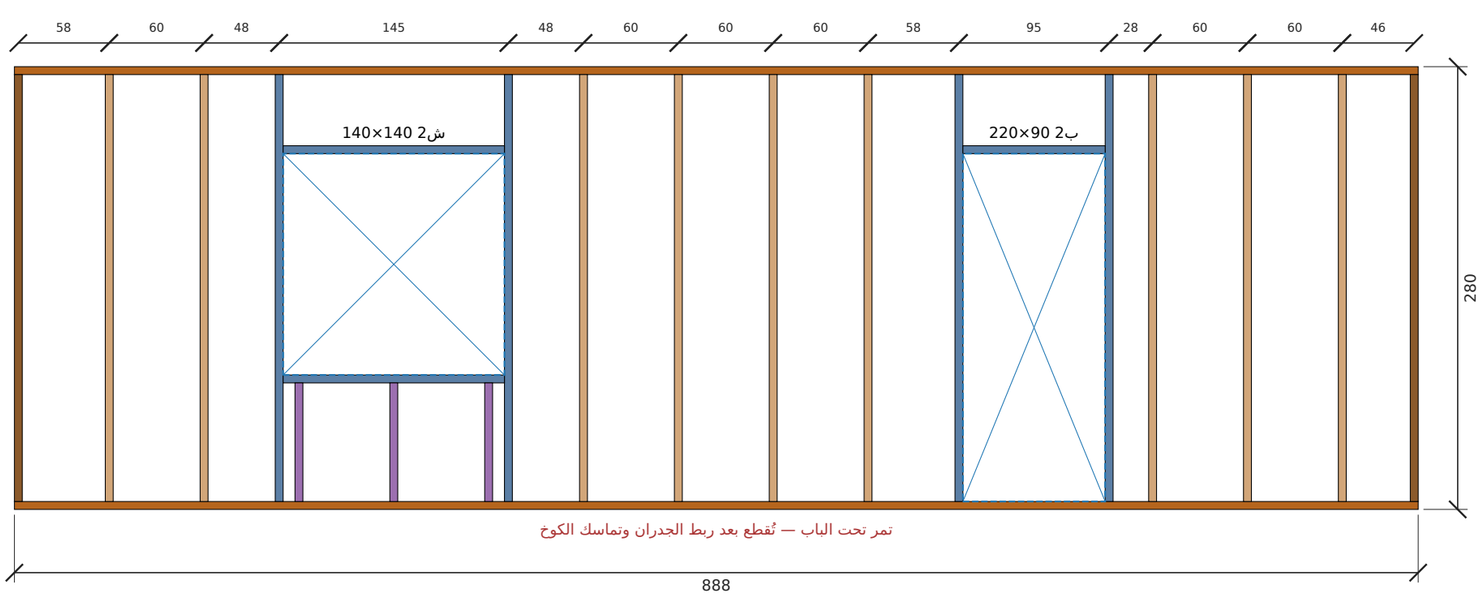


قاعدة سفلية | علوي | عمود | عمود زاوية | جنب فتحة | رأس فتحة | جلسة شباك | عمود قصير

مصنع وتد الأخشاب Watad Wood Factory	المشروع / العميل **فيلا خشب دورين — مجلس + غرفتين — 7.00 × 9.00 م (63 م² للدور)** **عميل — تبوك**	عنوان اللوحة **لوحات التأطير (للورشة)**	المقياس **—**	التاريخ **2026-10-23**	رقم اللوحة **W-09 (9/20)**

تأطير جدار أ-شمال — الطول 688 سم، الارتفاع 280 سم

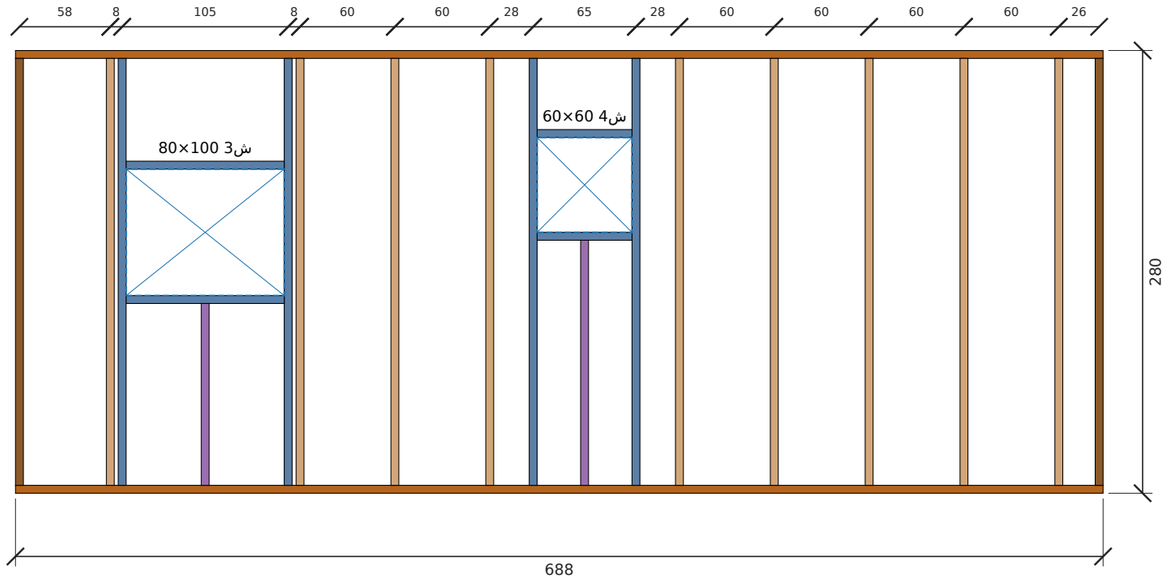

تأطير جدار أ-غرب — الطول 888 سم، الارتفاع 280 سم

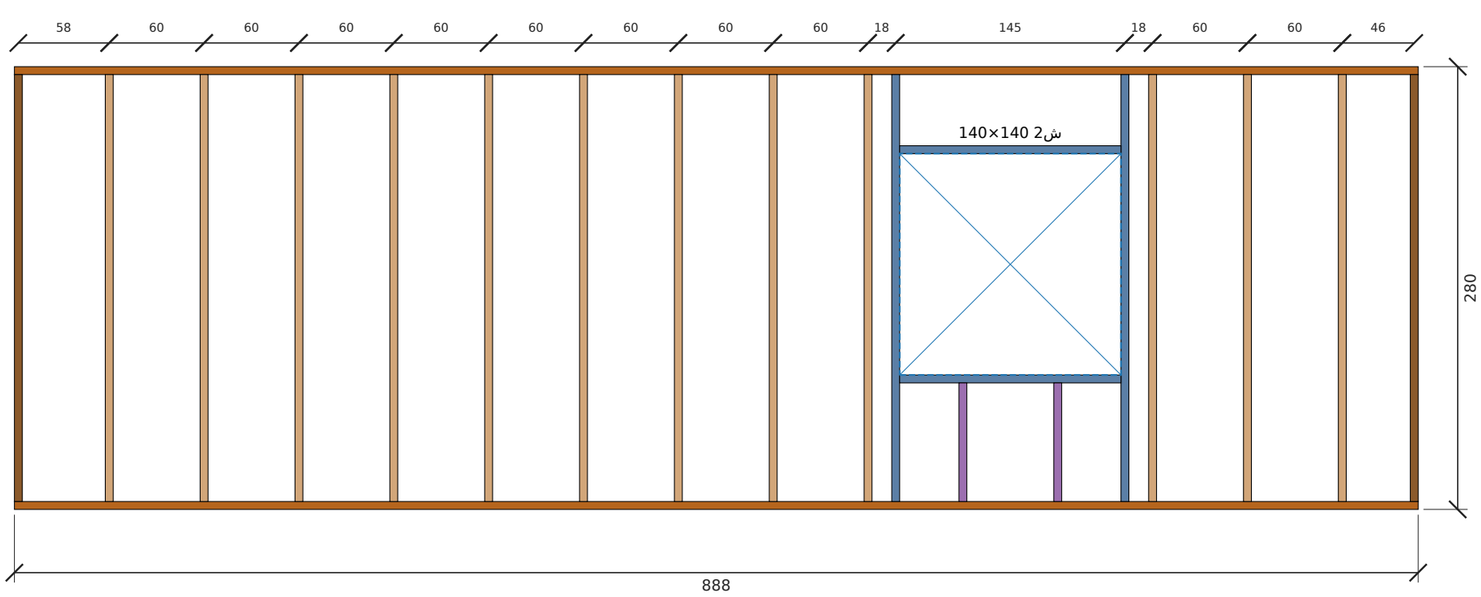


قاعدة سفلية | علوي | عمود | عمود زاوية | جنب فتحة | رأس فتحة | جلسة شباك | عمود قصير


المشروع / العميل	عنوان اللوحة	المقياس	التاريخ	رقم اللوحة
فيلا خشب دورين — مجلس + غرفتين — 9.00 × 7.00 م (63 م² للدور) **عميل — تبوك**	**لوحات التأطير (للورشة)**	**—**	**2026-10-23**	**W-10 (10/20)**

مصنع وتد الأخشاب
Watad Wood Factory

تأطير جدار أ-فاصل المجلس — الطول 688 سم، الارتفاع 280 سم (داخلي)

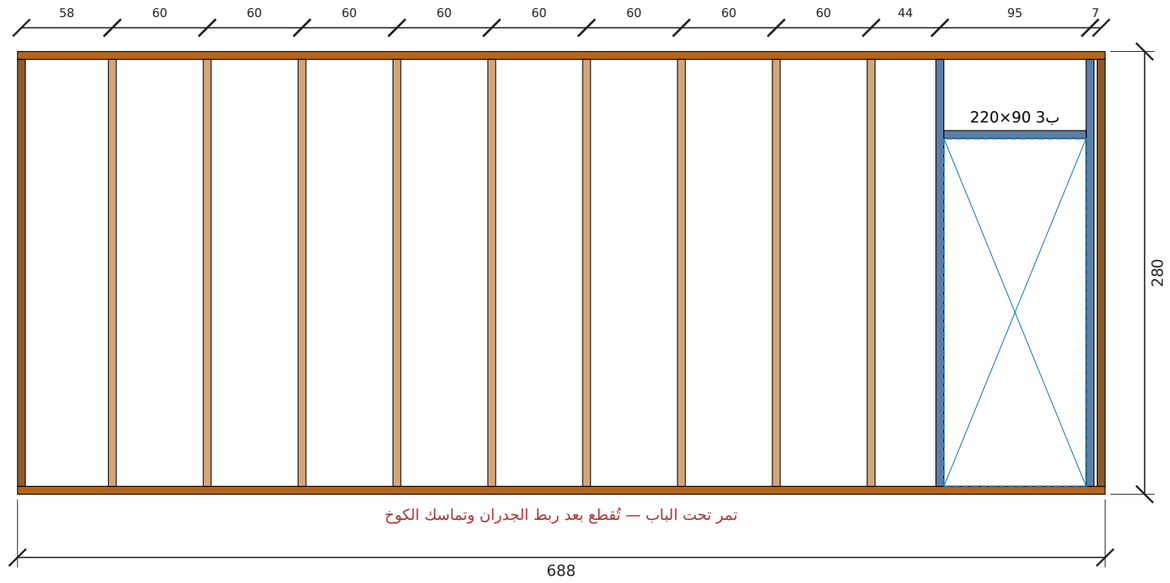


تأطير جدار أ-فاصل الدورة — الطول 210 سم، الارتفاع 280 سم (داخلي)

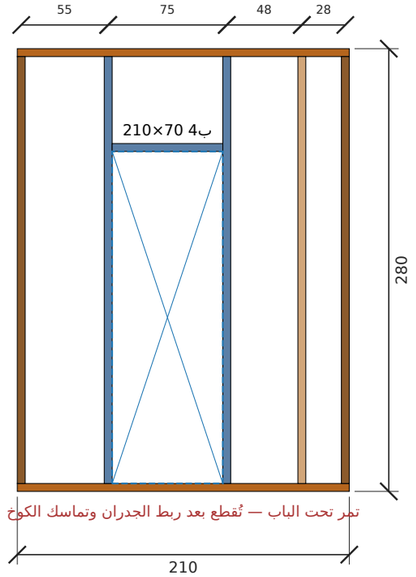


قاعدة سفلية | علوي | عمود | عمود زاوية | جنب فتحة | رأس فتحة | جلسة شباك | عمود قصير

مصنع وتد الأخشاب Watad Wood Factory	المشروع / العميل **فيلا خشب دورين — مجلس + غرفتين — 7.00 × 9.00 م (63 م² للدور)** **عميل — تبوك**	عنوان اللوحة **لوحات التأطير (للورشة)**	المقياس **—**	التاريخ **2026-10-23**	رقم اللوحة **W-11 (11/20)**

تأطير جدار أ-جدار الدرج — الطول 324 سم، الارتفاع 280 سم (داخلي)

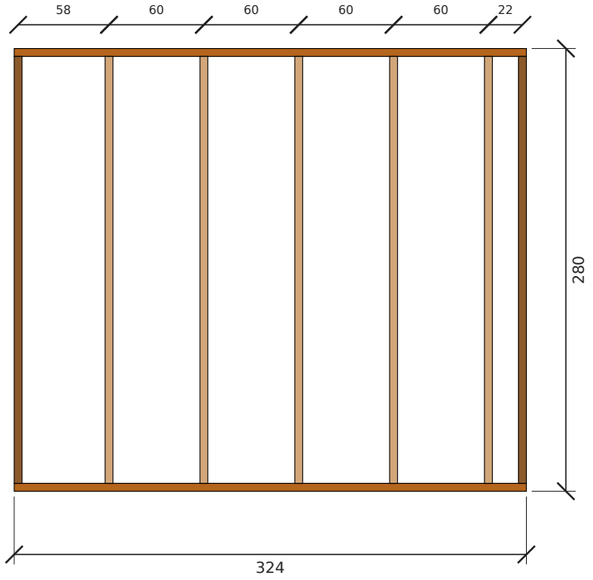


تأطير جدار أ-جدار الدورة — الطول 324 سم، الارتفاع 280 سم (داخلي)

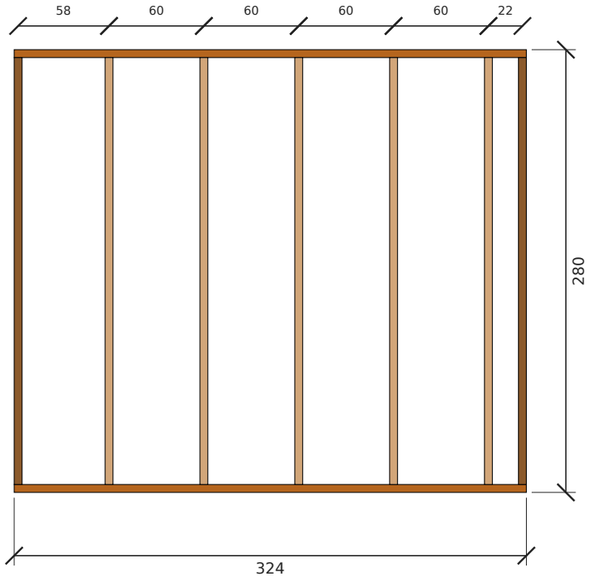


قاعدة سفلية | علوي | عمود | عمود زاوية | جنب فتحة | رأس فتحة | جلسة شباك | عمود قصير

مصنع وتد الأخشاب Watad Wood Factory	المشروع / العميل **فيلا خشب دورين — مجلس + غرفتين — 7.00 × 9.00 م (63 م² للدور)** **عميل — تبوك**	عنوان اللوحة **لوحات التأطير (للورشة)**	المقياس **—**	التاريخ **2026-10-23**	رقم اللوحة **W-12 (12/20)**

تأطير جدار ب-جنوب — الطول 688 سم، الارتفاع 280 سم

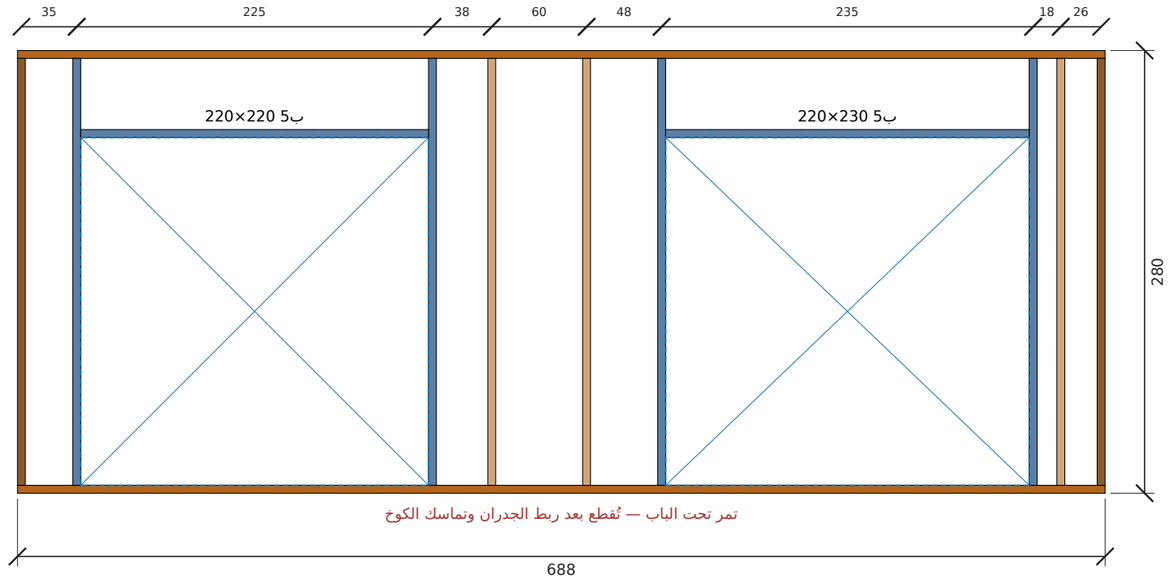

تأطير جدار ب-شرق — الطول 888 سم، الارتفاع 280 سم

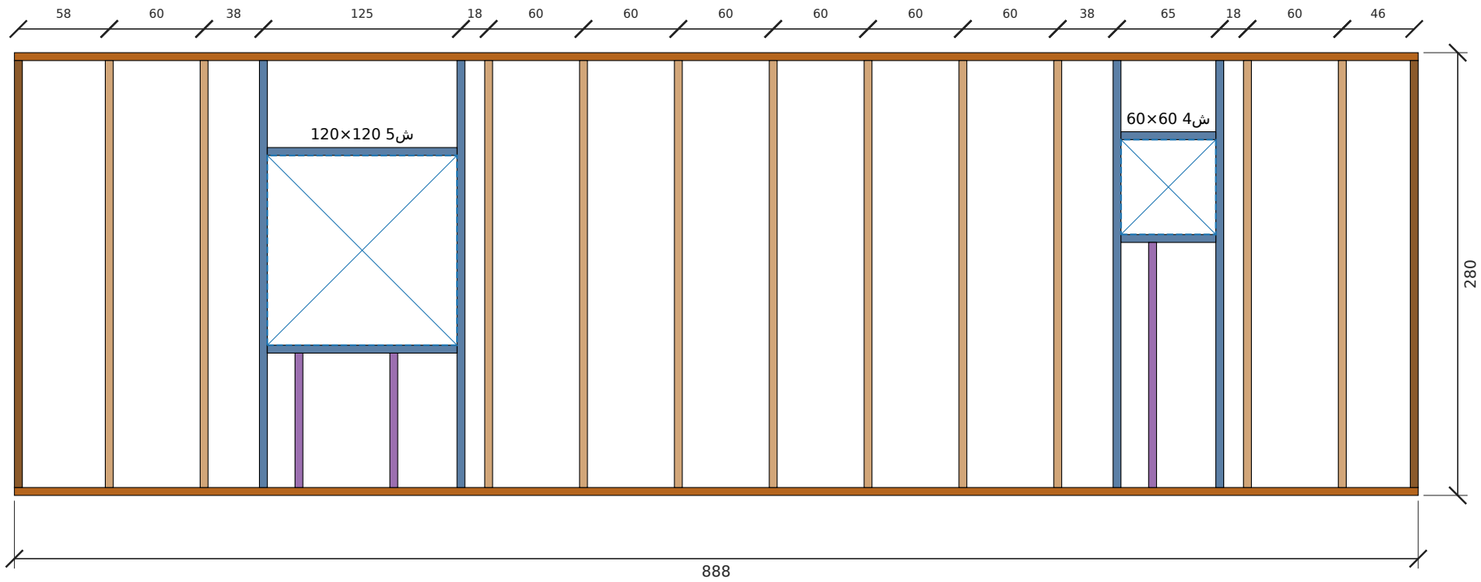


قاعدة سفلية | علوي | عمود | عمود زاوية | جنب فتحة | رأس فتحة | جلسة شباك | عمود قصير


المشروع / العميل	عنوان اللوحة	المقياس	التاريخ	رقم اللوحة
فيلا خشب دورين — مجلس + غرفتين — 9.00 × 7.00 م (63 م² للدور) **عميل — تبوك**	**لوحات التأطير (للورشة)**	**—**	**2026-10-23**	**W-13 (13/20)**

مصنع وتد الأخشاب
Watad Wood Factory

تأطير جدار ب-شمال — الطول 688 سم، الارتفاع 280 سم

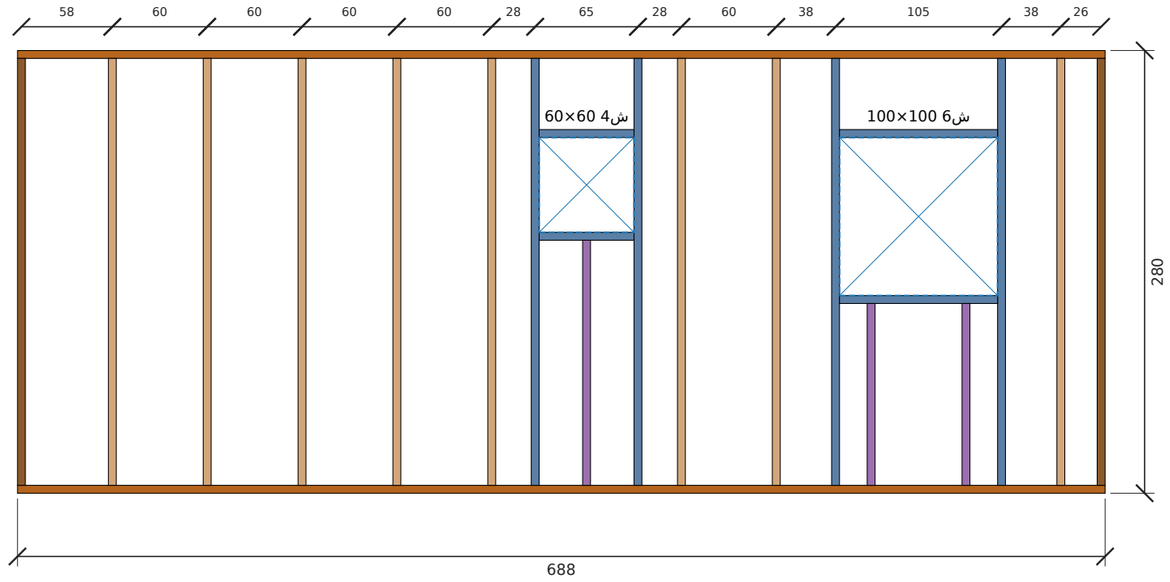

تأطير جدار ب-غرب — الطول 888 سم، الارتفاع 280 سم

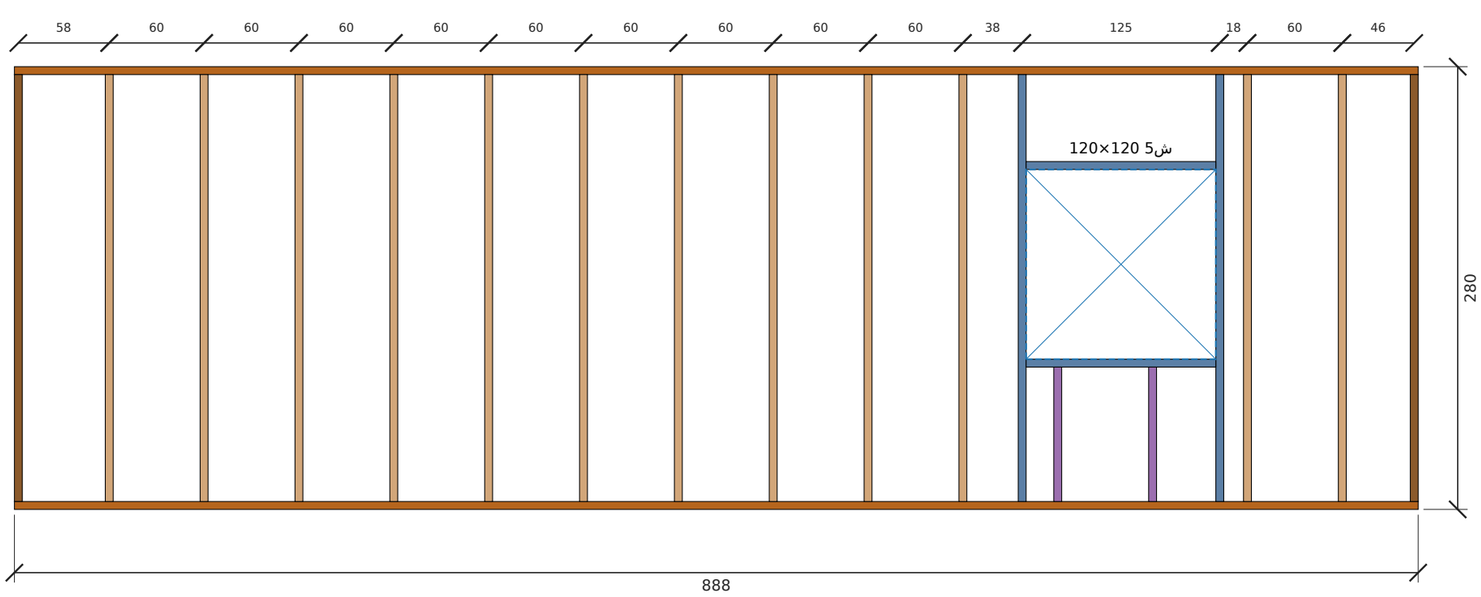


قاعدة سفلية | علوي | عمود | عمود زاوية | جنب فتحة | رأس فتحة | جلسة شباك | عمود قصير


المشروع / العميل	عنوان اللوحة	المقياس	التاريخ	رقم اللوحة
فيلا خشب دورين — مجلس + غرفتين — 9.00 × 7.00 م (63 م² للدور) **عميل — تبوك**	**لوحات التأطير (للورشة)**	**—**	**2026-10-23**	**W-14 (14/20)**

مصنع وتد الأخشاب
Watad Wood Factory

تأطير جدار ب-فاصل أمامي — الطول 688 سم، الارتفاع 280 سم (داخلي)

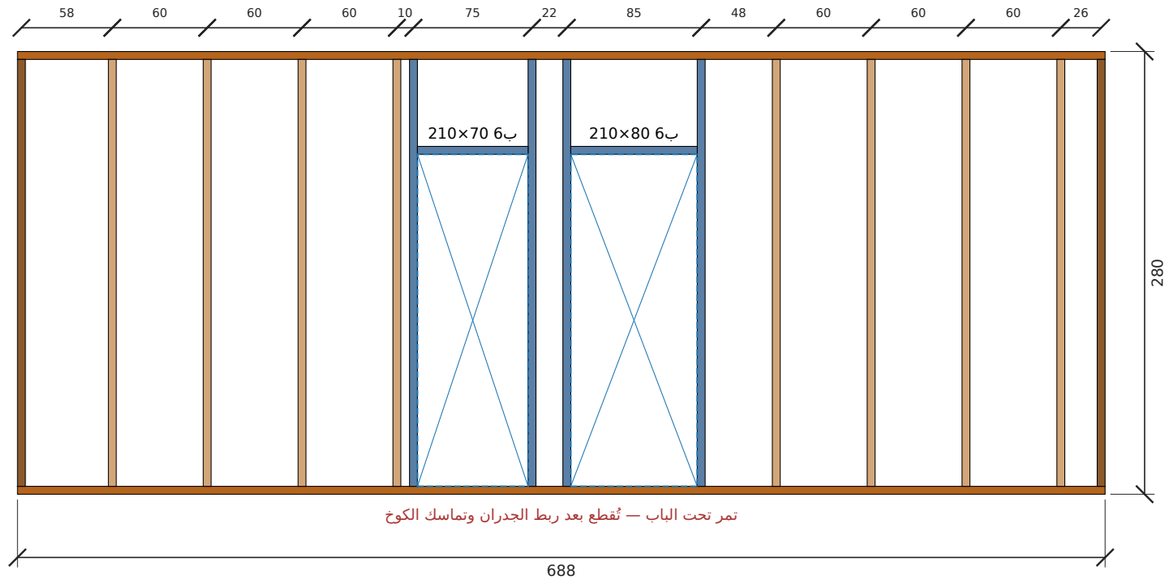

تأطير جدار ب-فاصل الغرف — الطول 460 سم، الارتفاع 280 سم (داخلي)

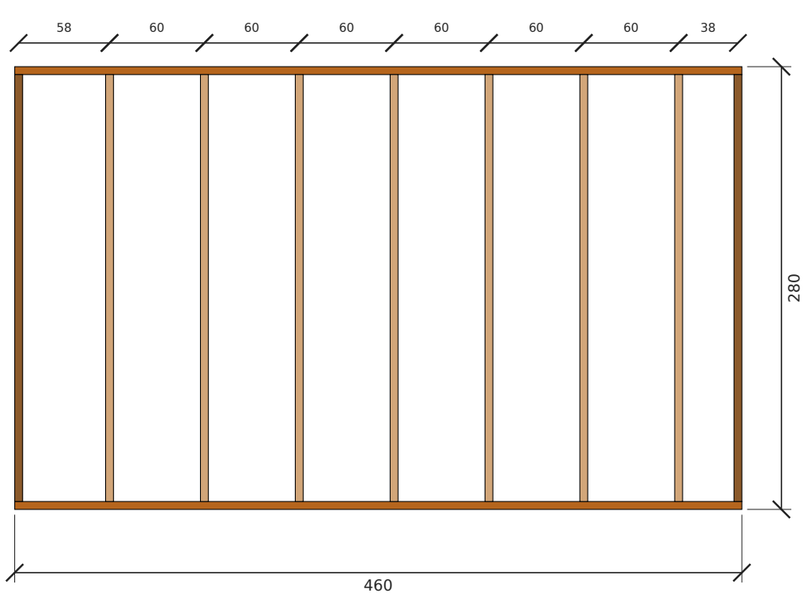


قاعدة سفلية | علوي | عمود | عمود زاوية | جنب فتحة | رأس فتحة | جلسة شباك | عمود قصير


المشروع / العميل	عنوان اللوحة	المقياس	التاريخ	رقم اللوحة
فيلا خشب دورين — مجلس + غرفتين — 7.00 × 9.00 م (63 م² للدور) **عميل — تبوك**	**لوحات التأطير (للورشة)**	**—**	**2026-10-23**	**W-15 (15/20)**

مصنع وتد الأخشاب
Watad Wood Factory

تأطير جدار ب-فاصل الدورة — الطول 210 سم، الارتفاع 280 سم (داخلي)

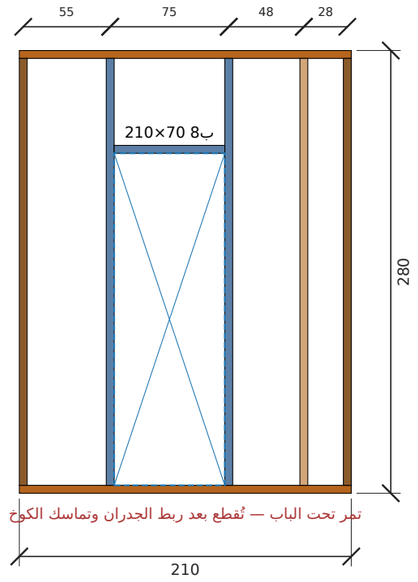

تأطير جدار ب-جدار الدرج — الطول 324 سم، الارتفاع 280 سم (داخلي)

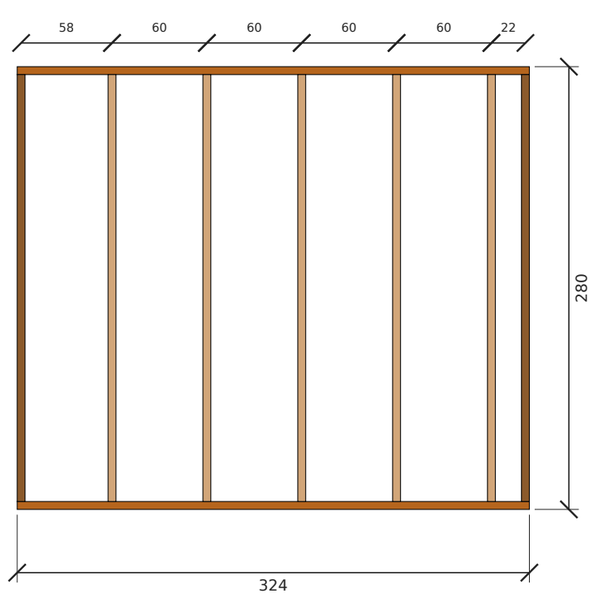


عمود قصير | جلسة شباك | رأس فتحة | جنب فتحة | عمود زاوية | عمود | علوي | قاعدة سفلية

المشروع / العميل	عنوان اللوحة	المقياس	التاريخ	رقم اللوحة
فيلا خشب دورين — مجلس + غرفتين — 7.00 × 9.00 م (63 م² للدور) **عميل — تبوك**	**لوحات التأطير (للورشة)**	**—**	**2026-10-23**	**W-16 (16/20)**

مصنع وتد الأخشاب
Watad Wood Factory

تأطير جدار ب-جدار المخزن — الطول 428 سم، الارتفاع 280 سم (داخلي)

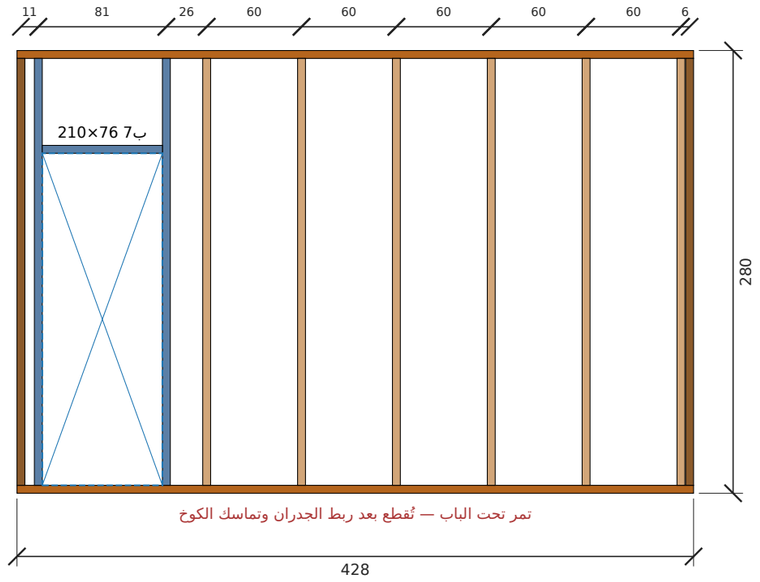

عمود قصير
جلسة شباك
رأس فتحة
جنب فتحة
عمود زاوية
عمود
علوي
قاعدة سفلية

مصنع وتد الأخشاب Watad Wood Factory	المشروع / العميل **فيلا خشب دورين — مجلس + غرفتين — 7.00 × 9.00 م (63 م² للدور)** **عميل — تبوك**	عنوان اللوحة **لوحات التأطير (للورشة)**	المقياس **—**	التاريخ **2026-10-23**	رقم اللوحة **W-17 (17/20)**

جدول الكميات وخطة تقطيع الطبليات

البند	القيمة
الارتفاع المطلوب / المعتمد	280 / 280 سم
السقف	جملون 30° — أعلى نقطة 787 سم من وجه الصبة
المدادات 5×15	42 مداد (21 لكل جهة) × حتى 445 سم — من طبلية 480
طبليات الطريقة الأولى (مداد + عمود)	42 طبلية × 480 سم
طبليات الطريقة الثانية (3 أعمدة)	68 طبلية × 320 سم
طبليات الطريقة الثانية (طويلة)	3 طبلية × 480 سم
مدادات أرضية الدور العلوي 5×15 كل 60 سم	45 مداد — 220سم×15، 248سم×15، 250سم×15 (طبلية 320 بالطريقة الأولى)
إجمالي الطبليات 5×22.5	158
إجمالي قطع 5×7	277
قائمة تقطيع 5×7	888سم×8 | 688سم×12 | 460سم×2 | 428سم×2 | 324سم×6 | 270سم×190 | 230سم×1 | 220سم×1 | 210سم×4
	180سم×4 | 155سم×3 | 140سم×4 | 120سم×4 | 115سم×3 | 110سم×1 | 100سم×4 | 90سم×2 | 85سم×4
ألواح تلبيس 2.5 سم	662 لوح × 400 سم (مجموع الصفوف 2231.6 م، 34 وجه)
أسمنت بورد 12 مم (122×244)	40 لوح (داخل دورات المياه)
العزل	333 لوح فوم صخري 80

جدول الكميات وخطة تقطيع الطبليات

البند	القيمة
الصبة	يجهزها العميل — 20 سم، مفرغة تحت دورات المياه

مراجعة التصميم مقابل قواعد المصنع

النوع	البند	التفاصيل	المقترح
ملاحظة	بحر المدادات	أطول بحر بدون جدار داخلي يحمل المداد: جهة أ: 350 سم، جهة ب: 350 سم. يحتاج رقم المصنع لأقصى بحر مسموح لتحديد المدادات اللي تُقوّى 20×5.	
ملاحظة	الصبة والدرج	ارتفاع الصبة 45 سم ← 3 درجة بقائمة 15.0 سم.	
ملاحظة	مناسيب رؤوس الفتحات	رؤوس الأبواب والشبابيك على مناسيب مختلفة: 200، 210، 220، 230، 240 سم.	
سؤال	يحتاج تأكيد	أقصى بحر للمداد بدون جدار داخلي قبل إضافة تقوية 5×7 (مداد 20×5)؟	
سؤال	يحتاج تأكيد	التغطية الصافية للوح التلبيس بعد التعشيق (مستنتجة مؤقتاً 18.67 سم من 280/15)؟	
سؤال	يحتاج تأكيد	هل يوضع أعمدة قصيرة فوق رأس الشباك/الباب إلى العلوي؟	
سؤال	يحتاج تأكيد	مكان الوصلة في القاعدة والعلوي إذا الجدار أطول من الطبلية؟	